


京张铁路遗址公园 · 百年京张AI创新带城市设计概念方案

百年应答

The Century Answer

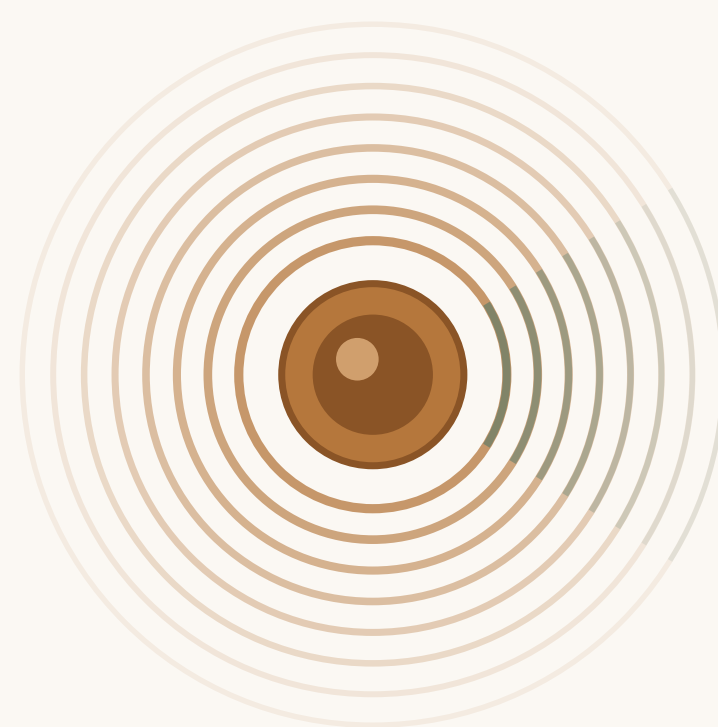


1909年，京张铁路回答了中国人能不能自己修铁路。
今天，同一条铁路腾出的9公里公园旁，正在回答中国能不能自己做AI。

把9公里遗址公园做成一份摊开在大地上的百年答卷——每一款海淀自主备案的大模型，在步道边缘钉下一颗铜道钉；市民蹲下来数道钉，就是在阅读中国自主创新的进度。

01 | 场地总览与总体结构（依据提交几何）

百年应答 · The Century Answer

九公里应答长卷 · 南问—中答—北跃：设计层读自 geometry/*_geojson，叠加真实地物锚点与实测偏差

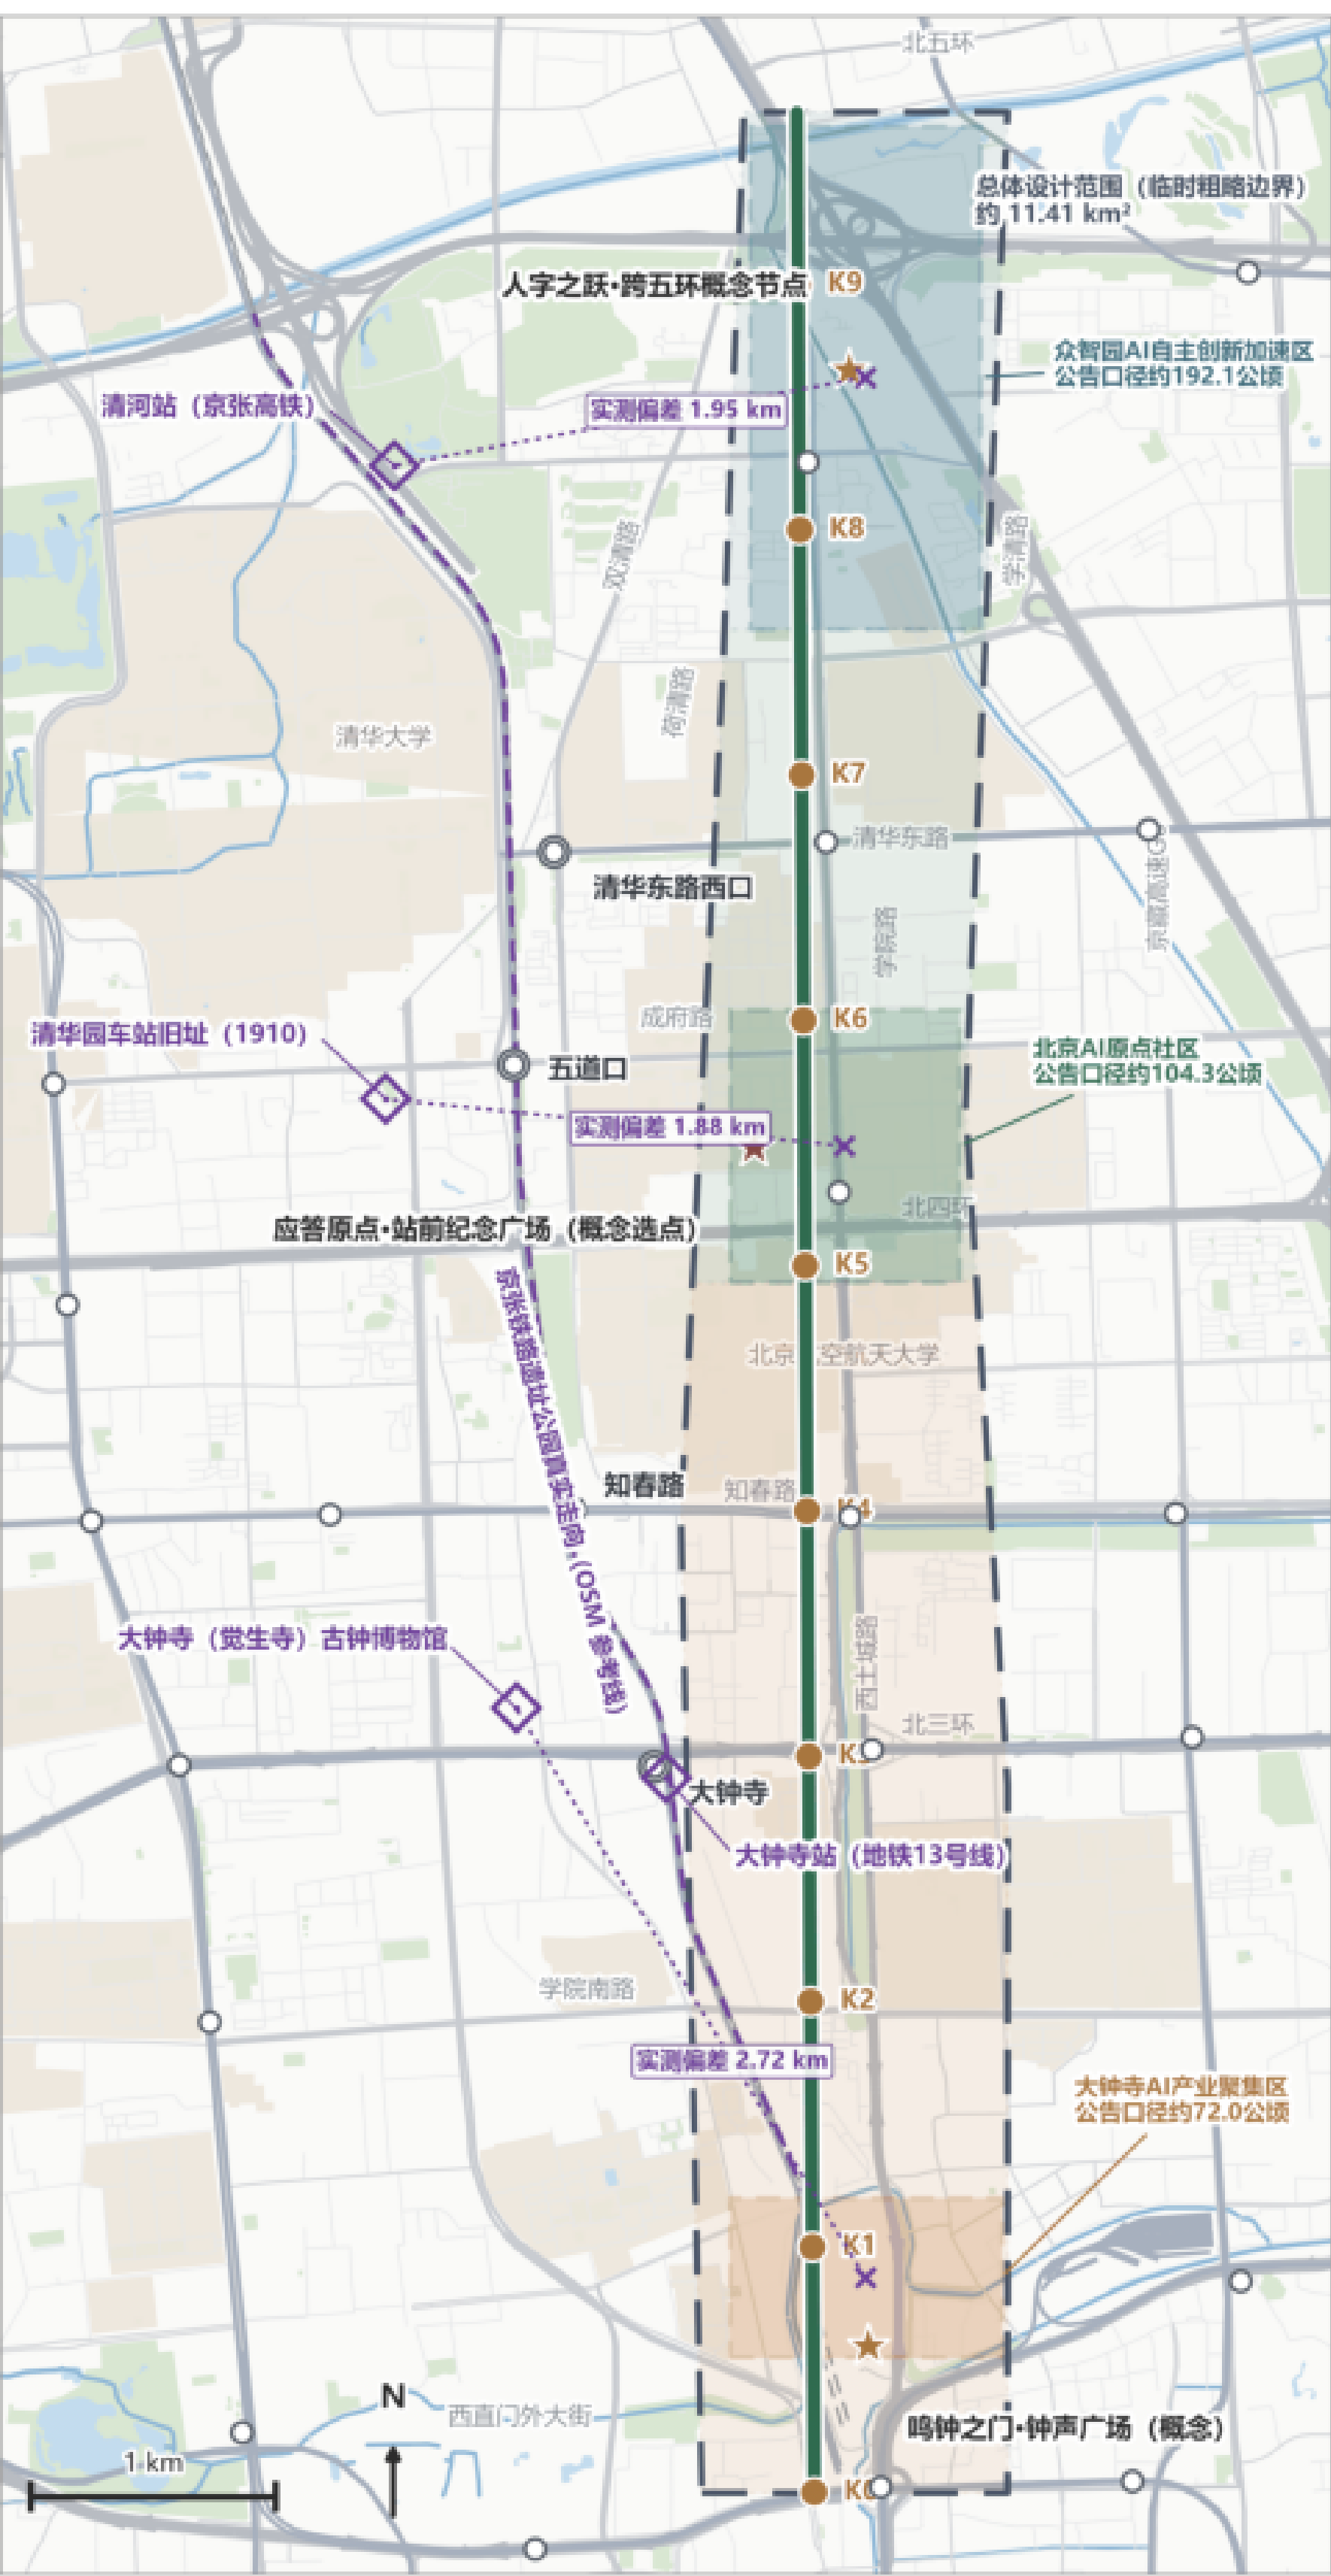

图例 LEGEND

设计层 (provisional 示意)

— 总体设计范围 (临时粗略边界)

— 九公里应答长卷慢行主线 (概念线)

● K0-K9 里程示意 (K0 = 主线南端)

★ 概念公共空间节点

■ 重点片区公告口径示范范围

■ 一期·南问段 (概念时序)

■ 二期·中答段 (概念时序)

■ 三期·北跃段 (概念时序)

真实地物锚点 (OSM 参考)

◇ 真实地物锚点 (OSM 核实)

— 京张真实走向参照线 (OSM)

····· 临时片区与真实地物实测偏差

底图 OSM

○ 地铁站

— 现状铁路

— 城市轨道交通

■ 水系

■ 现状公园绿地

■ 高校校园

坐标一致性与偏差说明 (必读)

临时边界说明 (provisional)：本图设计层依据维护者登记到临时粗略边界控制，非官方红线，非最终依据。实测该段时生量数据位于真实京张铁路以东——真实地物到临时慢行主线 (roads.geojson ROAD-001) 的最短距离约 0.6-1.7 公里 (清华园车站旧址约 1.70 公里，清华站约 1.65 公里)；三处临时重点片区质心与同名真实地物相距约 1.9-2.7 公里，其中大钟寺片区质心偏南约 2.3 公里。重点片区为公告口径示范范围，西至未公布。官方边界发布后，全部图层与标注须严格按校正复算。

1909 1910 1949 2019 2023 2024 2026

京张铁路建成通车 清华园车站建成 “进京赶考” 首站 京张高铁通车-老线腾退 遗址公园一期开放 二期开工 道钉带起笔 (概念)

百年时间线 (依据公开来源, 2026 为本方案概念动作)

底图数据: © OpenStreetMap contributors (ODbL, 检索日期 2026-08-18) | 设计图阅读自投稿 geometry/*_geojson, 为概念建议 (provisional, 虚线示意), 非官方边界, 非最终依据, 待专业团队深化核定
面积与比例读自 metrics.json 与 key_areas.geojson (公告口径) | 重点片区西至未公布, 位置为临时粗略示意 | 绘制: 百年应答项目组

题—答—阅：三带机制

百年京张文化带

1909年之问：题面与第一次作答；清华园车站保存最初的题面。



AI融合创新带

企业与模型作答：每款备案大模型钉一颗道钉，里程碑敲响应答钟。



都市AI生活体验带

阅卷现场：市民在9公里步道上数道钉、听钟声、看路演。

反馈回路：公众意见经城市进化档案馆归档并公开回应，重新成为下一年的“题”。

总体概念：一卷、三段、两翼

南问

鸣钟之门

大钟寺AI产业聚集区

72.0公顷口径

中答

应答原点

北京AI原点社区

104.3公顷口径

北跃

人字之跃

众智园AI自主创新加速区

192.1公顷口径

整个方案只讲一个故事，并把它讲进三个尺度：统筹研究范围决定“写什么”，总体设计范围决定“写在哪”，重点区域范围决定“怎么落笔”。空间上，这个故事落为一条9公里应答长卷主脊、南问—中答—北跃三段、东西46座应答门向近70个社区渗透的总体结构。长卷主脊对位已批控规“一带一轴两心多点”中的“一带”（法定“一轴”专指中关村大街创新发展轴，本方案骨架统一称主脊以示区分），鸣钟之门与应答原点分别落在“两心”——本方案是法定规划之上的概念深化建议，不与其并列、不替代、不引用其未公开控制指标。



应答钟与钟声广场（南问段·大钟寺）

AI 概念意象图，非实景照片；生成工具 LibTV / 模型 Lib Image。



人字之跃·人字天桥（北跃段·众智园）

AI 概念意象图，非实景照片；生成工具 LibTV / 模型 Lib Image。




道钉带与零公里桩（全线9公里）

AI 概念意象图，非实景照片；生成工具 LibTV / 模型 Lib Image。

一条铁路，问了两次同样的问题

1909 → 2026：从 “中国人能不能自己修铁路” 到 “中国能不能自己做AI”

设计不是从一张白纸开始的，是从1909年的一个问题开始的。那一年，京张铁路在关沟段爬不上天险的陡坡，詹天佑画了一个“人”字：列车驶入岔口、折返换向，用两段缓坡替代一段爬不动的陡坡。这条中国人自主勘测、自主设计、自主施工的铁路当年建成通车，回答了第一个百年之问。今天，铁路自己也交了卷——老线腾退，铁轨让位给公园；公园两侧，答题的人已经坐满考场。

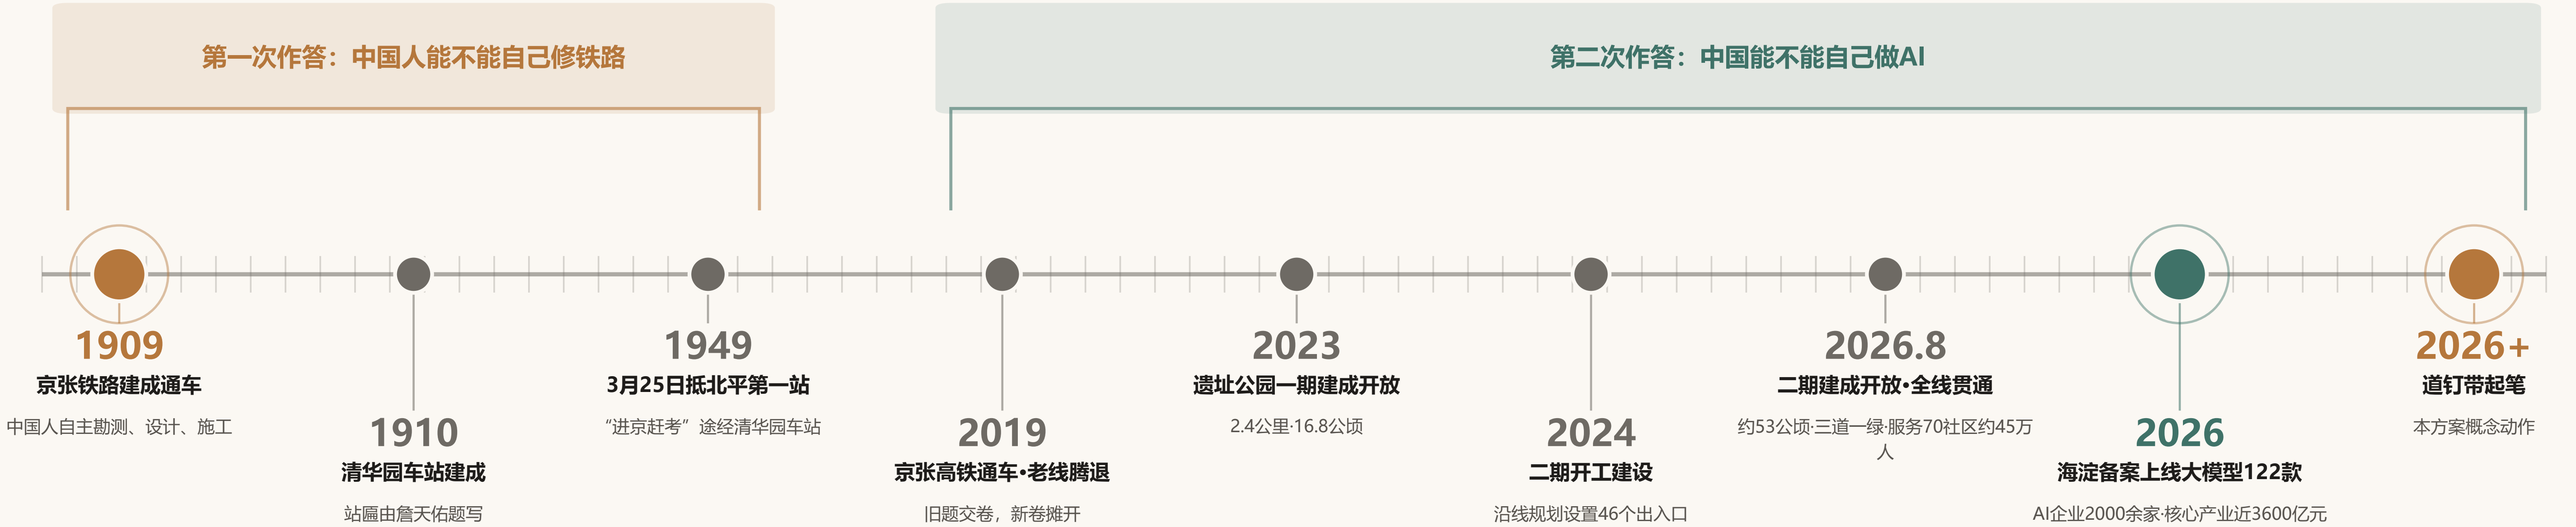

百年时间线依据已登记的公开来源；2026+ 为本方案概念动作，非政府计划或承诺。

两次自主创新，是同一道题的两次作答

京张文化不是AI的装饰背景，AI也不是京张的现代注脚——形式不是贴上去的符号，是解题解出来的结果。

	1909 · 京张铁路	今天 · 京张AI创新带
面对的问题	中国人能不能自己修铁路	中国能不能自己做AI
作答主体	詹天佑与中国工程师	沿线2000余家AI企业、高校与开发者
关键方法	人字形展线：用折返换高度，以有限长度解决无法直上的陡坡	全栈自主：从算力、框架到模型逐层补齐，以持续迭代解决无法一步到位的差距
留下的证物	铁路、车站、道钉	备案上线的大模型、专利、开源项目
公众如何验证	坐上火车，翻过关沟	蹲下来数道钉，听应答钟
本方案的动作	保存题面：车站文物本体不动一砖一瓦	记录作答：每款备案大模型钉一颗铜道钉

从“翻山”到“跨环”：同一个字，同一种用折返换高度的巧劲



方案设计：一卷、三段、四地标

题—答—阅三带机制落为9公里应答长卷；四大概念地标承担叙事、仪式、记录与界面四种角色。



应答钟与钟声广场

The Answer Bell & Bell Chime Plaza · 南问段 · 大钟寺AI产业聚集区（72.0公顷口径）

AI 概念意象图，非实景照片；生成工具 LibTV / 模型 Lib Image。

空间概念

一方开敞圆形广场，地面以同心声波环铺装向外扩散（Logo母题的地面放大）；圆心立取京张桁架清汇的钢结构钟架——工字钢、铆钉节点、道钉形收头，架下悬一口当代新铸的青铜应答钟。四条“声波径”从广场辐射进地铁站周边四个象限，缝合被道路切分的步行流线。

运行机制

带内企业完成大模型备案或IPO，可预约敲钟一响；敲钟资格与可公开核验事件绑定——记录事实、不背书企业。缝合的理由不是“修了路”，而是“广场值得绕过来”。

边界与铁律

应答钟为当代新铸之钟：与大钟寺古钟博物馆及其馆藏文物仅为文化呼应关系，绝不敲击、绝不移动、绝不商业化使用任何文物古钟。大钟寺为全国重点文物保护单位，钟架与广场一律退出文物保护单位范围及建设控制地带；具体选点、退让距离与体量控制均为待文物主管部门协商的概念建议，钟架高度以不高于周边行道树冠层为控制意向。



人字之跃 · 人字天桥

The Ren-Shaped Leap Footbridge · 北跃段 · 众智园AI自主创新加速区（192.1公顷口径）

AI 概念意象图，非实景照片；生成工具 LibTV / 模型 Lib Image。

空间概念

跨环路步行桥概念节点，回应官方“上跨环路标志性节点”的表述。主跨为一跨平直的步行桥概念；“人”字不做成桥面的平面造型，而落在两端的折返坡道上——每侧只设一处折返、贴地展开在绿地中，坡道形态克制、不做多层盘旋。桥下衔接清河蓝绿空间，主脊叙事与生态廊道在此形成十字交叠。

运行机制

用一个来回的坡长换取跨路所需的净空高度，坡度平缓可推轮椅——折返本身就是人字形展线的技术内核。众智园同时承担机器人测试与模型demo接入测试的“测试主场”职能。

边界与铁律

本方案不含线形、桥跨、结构等任何工程结论，工程可行性待专项研究。桥面栏板显示屏只显示按统计发布周期更新的少量核心数字，绝不实时、绝不广告。



道钉带与零公里桩

The Rail-Spike Band & Kilometre-Zero Post · 全线 · 9公里应答长卷（最细也最长的贯通要素）

AI 概念意象图，非实景照片；生成工具 LibTV / 模型 Lib Image。

空间概念

全线统一的步道边缘铜道钉带：每一款海淀自主备案的大模型，钉一颗铜道钉，刻备案事件与日期。沿已建成贯通的慢行系统连续铺陈，让“答卷”在地面上一路写通。零公里桩（K0+000）立于清华园车站站前素广场，柱脚嵌第0号道钉，刻“1909年京张铁路建成通车”这一事件本身。

运行机制

道钉数=备案大模型数，锚定政府既有公开口径（区政府正式口径122款，截至2026年2月）——道钉带因此是全场最可审计的城市KPI，每年赶考季新增道钉使公共空间成为活体纪念物。以钉代碑：不立高碑、不做名人墙，荣誉不供仰视、供蹲下来数。

边界与铁律

只刻事实不列排名、只记事件不背书主体、与主体存续脱钩——企业退出不拔钉，钉记录的是“某年某月某模型完成备案”这一历史事实。备案数逐月增长，“第N颗道钉”以安装时点的政府口径为准。零公里桩落位为待文物主管部门协商的概念选点。



应答门

The Answer Gates · 全线 · 依托二期规划46个出入口（以实际建成为准）

AI 概念意象图，非实景照片；生成工具 LibTV / 模型 Lib Image。

空间概念

每座门做成“一页翻开的考卷”——门外一面刻百年之问，门内一面刻今日之答。门是这条带最日常的界面：把被铁路隔开百年的东西两岸重新缝起来，靠的不是修一条路，而是给人一个穿过去的理由。

运行机制

由沿线近70个社区认领，居民口述史经三审进入门侧“社区一页”。门下坡道执行“机器人坡道=无障碍坡道”：一套改造两用，低速配送机器人与轮椅共用，合规成本变成通行福利；“轮椅优先、机器人强制停让”写入测试通过硬条件，无障碍指标为一票否决项。

边界与铁律


46个出入口为公园二期规划口径，以实际建成为准；社区认领机制、门体改造与任何测试试点均须经主管部门审批，本方案不含结论性工程与运营承诺。

用地结构与三层范围工作框架

一脊两翼十地块：沿真实走廊的概念用地分区示意（非法定用地边界）

02 | 用地结构与三层范围工作框架（概念）

一轴两翼十地块：全部图斑读自 geometry/land_use.geojson，非法定用地边界

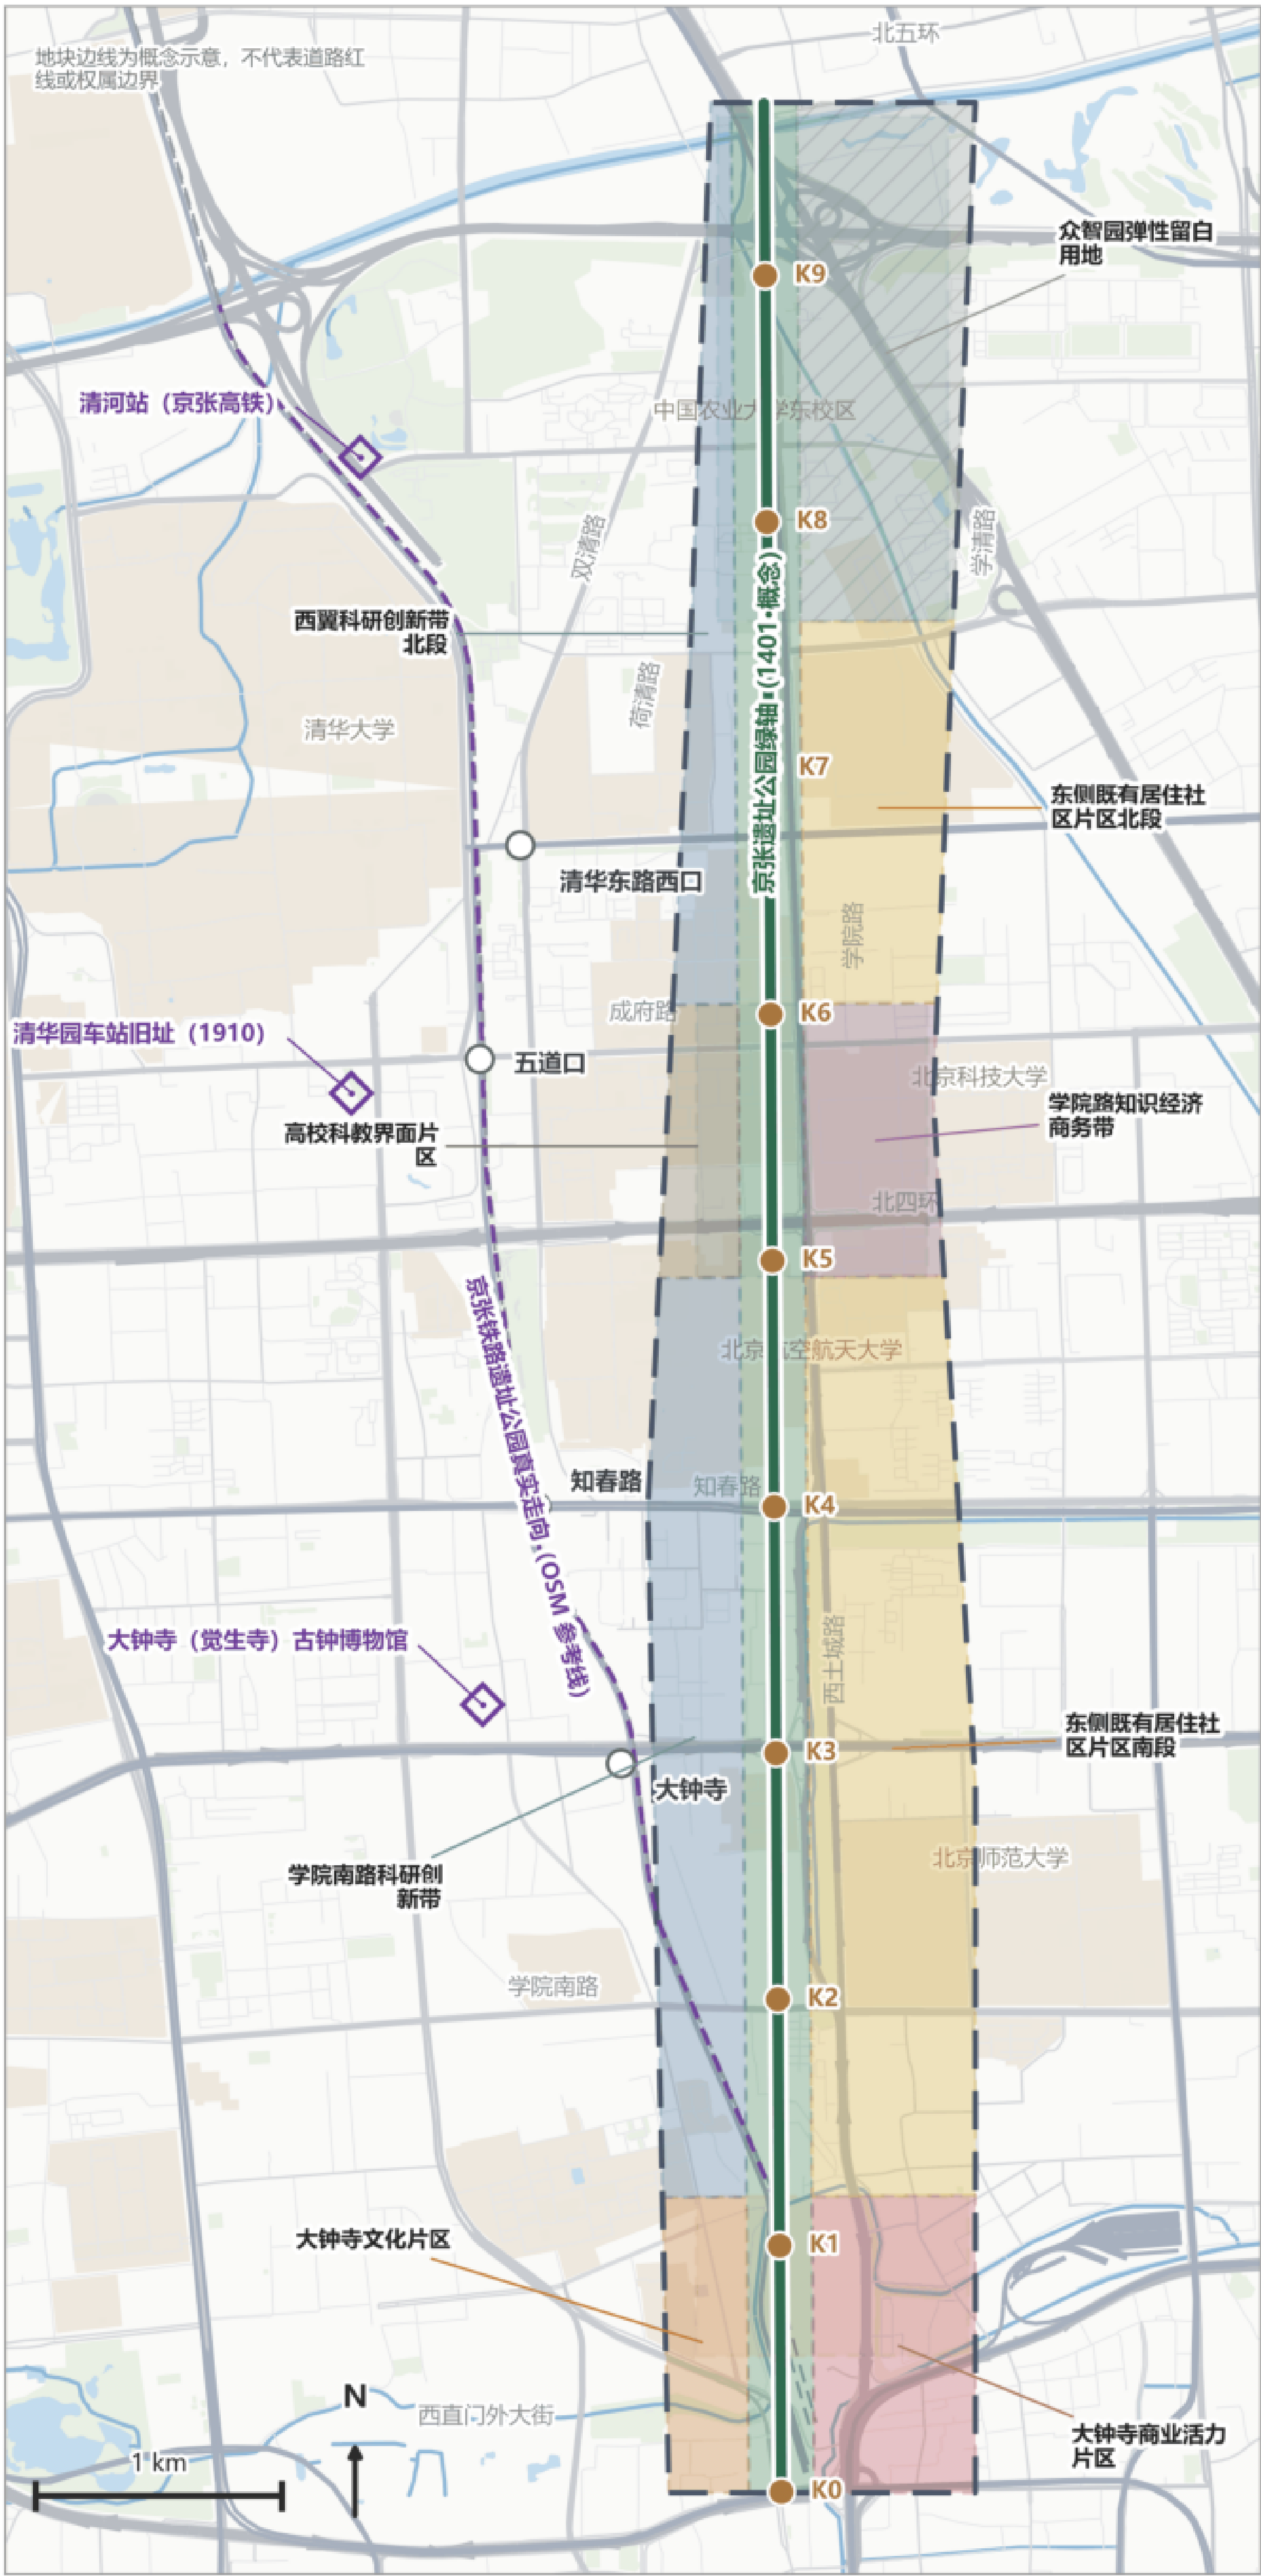

底图数据：© OpenStreetMap contributors (ODbL, 检索日期 2026-08-18) | 设计图层读自投稿 geometry/"

百年应答 · The Century Answer

图例 LEGEND

设计层·用地分区 (provisional)

- 公园绿地·绿轴 (1401)
- 文化设施 (0803)
- 商业 (0901)
- 商务 (0902)
- 科研 (0802)
- 高校科教 (0804)
- 既有居住延续 (0701)
- 弹性留白 (16)
- 总体设计范围 (临时边界)
- 重点片区示意图范围

真实地物锚点 (OSM 参考)

- 真实地物锚点 (OSM 核实)
- 京张真实走向参照线 (OSM)
- 临时片区与真实地物实测偏差

三层范围工作框架 (示意)



坐标一致性与偏差说明 (必读)

临时边界说明 (provisional)：本图设计层依据维护者登记的临时粗略边界绘制，非官方红线、非审批依据。实测该临时走廊整体位于真实京张廊道以东——真实地物到临时慢行主线 (roads.geojson · ROAD-001) 的最短距离约 0.6–1.7 公里 (清华园车站旧址约 1.70 公里、清河站约 1.65 公里)；三处临时重点片区质心与同名真实地物相距约 1.9–2.7 公里，其中大钟寺片区另偏南约 2.3 公里。重点片区为公告口径示意图范围，四至未公布。官方边界发布后，全部图层与指标须整体校正复算。

结构

9公里公园绿廊（1401）为长卷主脊，两翼按南向、中脊、北跃三段布置文化、商业、科研、居住、科教、商务与弹性留白等十个概念地块分区；北跃段专设弹性留白用地，为“未来之问”保留不被今日答案填满的余地。

复算

地块分区在EPSG:4548投影空间完成拓扑校验：覆盖缺口0.398平方米、最大重叠0.087平方米；用地代码全部取自场地包枚举。

边界

用地分区为概念建议，不替代法定控规；凡涉及建筑高度、开发强度、道路红线、退线与设施标准，本方案一律不给结论数值，统一表述为“待正式控规条件确认”。

9 公里 KM
应答长卷主脊

46 座 GATES
应答门以建成为准

70 个 COMMUNITIES
社区认领应答门

3 处 KEY AREAS
重点区域详细设计

122 颗 SPIKES
道钉 = 备案模型数

底图与图层说明

底图数据 © OpenStreetMap contributors (ODbL)，检索日期 2026-08-18；设计图层为概念建议（虚线示意），非官方边界、非审批依据。

全部空间内容为概念建议，待专业团队深化，不构成政府审定结论。

全部空间内容为概念建议，待专业团队深化，不构成政府审定结论。


用地结构板

三处重点区域索引与设计任务

南问—中答—北跃：三处重点区域在9公里长卷上各任一段叙事

03 | 三重点片区概念设计（放大·含实测偏差）

片区范围读自 key_areas.geojson；与同名真实地物的实测偏差在每幅内如实标注

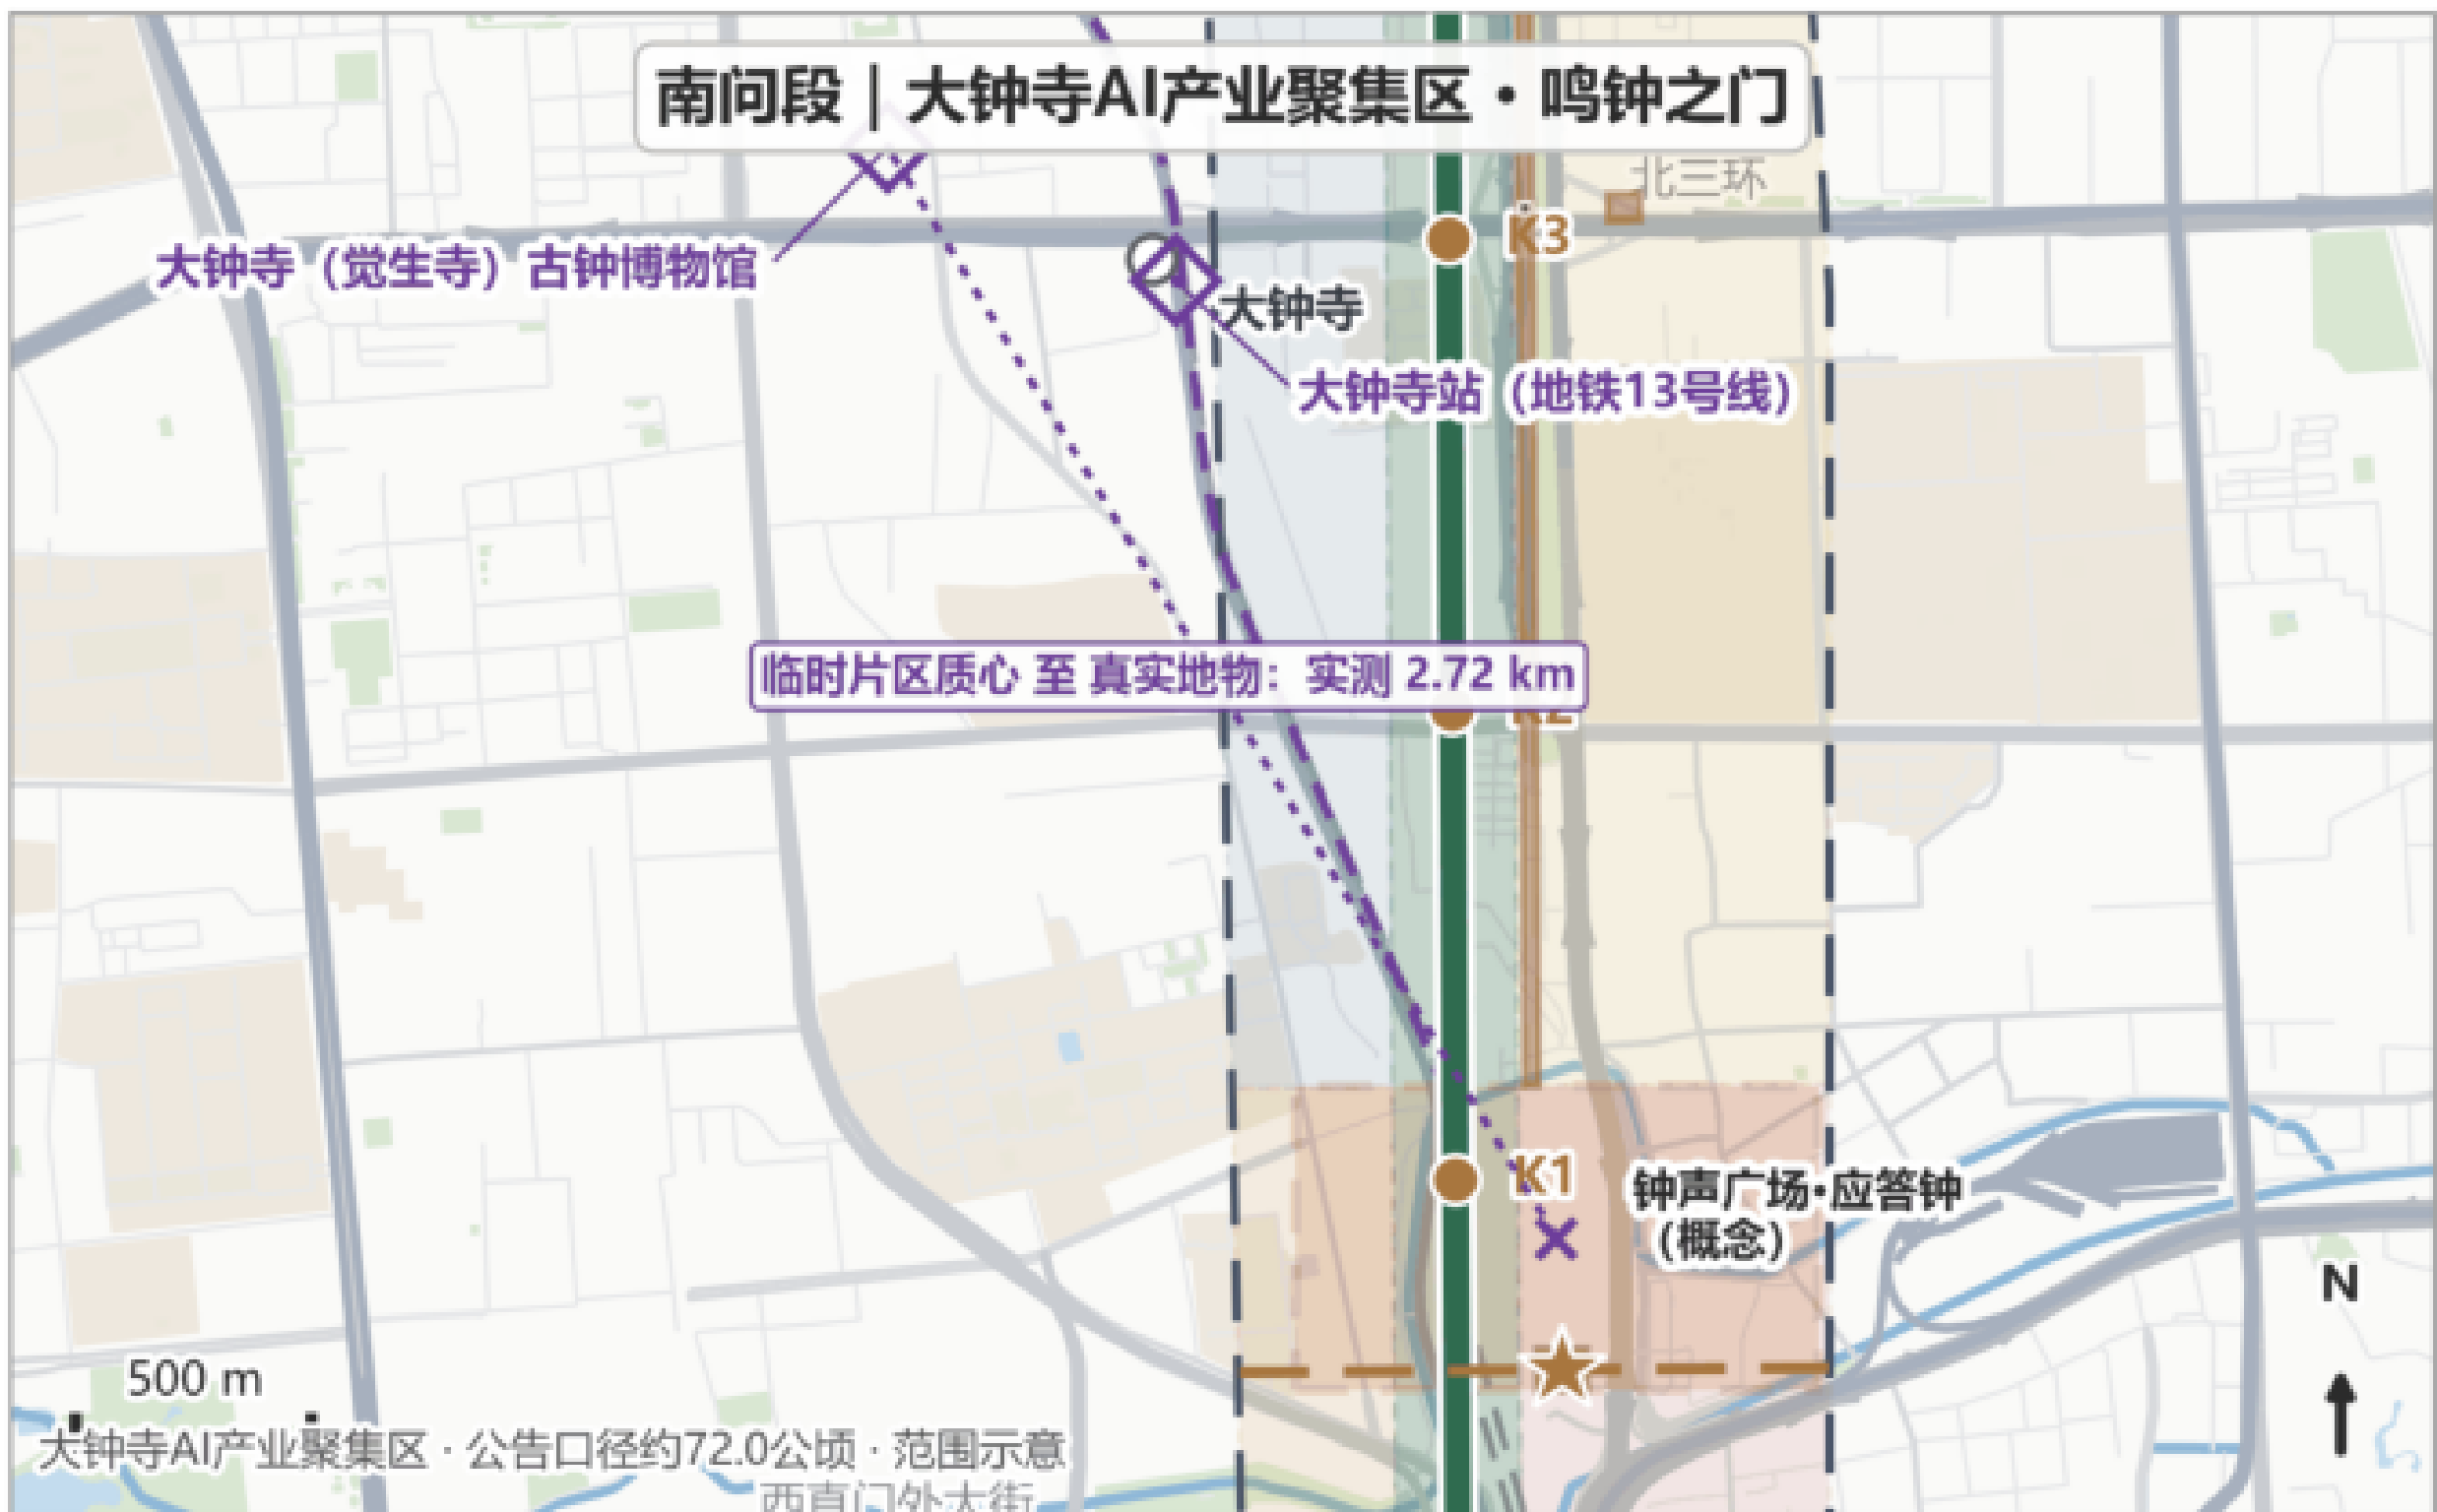

百年应答 · The Century Answer



图例 LEGEND

设计层 (provisional 示意)

- 总体设计范围
- 重点片区示意范围
- 慢行主线 (概念)
- 东西缝合慢行连线
- 低速物流测试通道
- 概念公共空间
- 概念建筑基底
- 概念绿地
- 概念节点

真实地物锚点 (OSM 参考)

- 真实地物锚点
- 京张真实走向参照
- 实测偏差连线

底图 OSM

- 地铁站
- 现状铁路
- 水系
- 公园绿地

坐标一致性 & 偏差说明 (必读)

临时边界说明 (provisional)：本图设计层依据维护者登记的临时粗略边界绘制，非官方红线、非审批依据。实测该临时走廊整体位于真实京张廊道以东——真实地物到临时慢行主线 (roads.geojson - ROAD-001) 的最短距离约 0.6~1.7 公里 (清华园车站旧址约 1.70 公里、清河站约 1.65 公里)；三处临时重点片区质心与同名真实地物相距约 1.9~2.7 公里，其中大钟寺片区另偏南约 2.3 公里。重点片区为公告口径示意范围，四至未公布。官方边界发布后，全部图层与指标须整体校正复算。

角色

大钟寺是南问 (鸣钟之门)，清华园车站是中答 (应答原点)，众智园是北跃 (人字之跃)。三段各有主场：大钟寺承接服务与仪式，原点段承接叙事，众智园承接测试。

口径

三区共用官方面积口径：众智园192.1公顷、AI原点社区104.3公顷、大钟寺72.0公顷；提交图层沿用临时粗略范围。

边界

临时范围不作为官方红线或精确面积依据；清华园车站文保范围GIS缺失，一切站前落位均为待文物主管部门协商的概念选点。

南问	中答	北跃
鸣钟之门	应答原点	人字之跃
大钟寺AI产业聚集区	北京AI原点社区	众智园AI自主创新加速区
72.0公顷口径	104.3公顷口径	192.1公顷口径
9 公里 KM 应答长卷主脊	46 座 GATES 应答门以建成为准	70 个 COMMUNITIES 社区认领应答门
3 处 KEY AREAS 重点区域详细设计	122 颗 SPIKES 道钉 = 备案模型数	

底图与图层说明

底图数据 © OpenStreetMap contributors (ODbL)，检索日期 2026-08-18；设计图层为概念建议（虚线示意），非官方边界、非审批依据。

全部空间内容为概念建议，待专业团队深化，不构成政府审定结论。

交通慢行与蓝绿公共空间复合系统

把主角让给走路的人：慢行主线、东西向断点客厅、蓝绿十字（概念建议）

04 | 交通慢行与蓝绿公共空间系统（概念）

慢行主线 · 三条东西缝合线 · 低速物流测试通道 · 概念绿地与公共空间，全部读自提交几何



底图数据：© OpenStreetMap contributors (ODbL, 检索日期 2026-08-18) | 设计图层读自投稿 geometry/*_geojson, 为概念建议（provisional, 虚线示意），非官方边界、非审批依据，待专业团队深化核定面积与比率读自 metrics.json 与 key_areas.geojson（公告口径） | 重点片区四至未公布，位置为临时粗略示意 | 绘制：百年应答方案组

百年应答 · The Century Answer

图例 LEGEND

设计层（provisional 示意）

- 总体设计范围（临时粗略边界）
- 九公里应答长卷慢行主线（概念线）
- K0-K9 里程示意（K0 = 主线南端）
- ★ 概念公共空间节点
- 重点片区公告口径示意范围
- 东西缝合慢行连线（概念）
- - 低速物流测试通道（概念）
- ◇ 应答门示意（实际建成为准）
- 概念公共空间
- 概念绿地（1401）
- 蓝绿协调带（1402）

真实地物锚点（OSM 参考）

- ◇ 真实地物锚点（OSM 核实）
- - 京张真实走向参照线（OSM）
- 临时片区与真实地物实测偏差

底图 OSM

- 地铁站
- - 现状铁路
- 城市轨道交通
- 水系
- 现状公园绿地
- 高校校园

坐标一致性与偏差说明（必读）

临时边界说明（provisional）：本图设计层依据维护者登记的临时粗略边界绘制，非官方红线、非审批依据。实测该临时走廊整体位于真实京张廊道以东——真实地物到临时慢行主线（roads.geojson · ROAD-001）的最短距离约 0.6-1.7 公里（清华园车站旧址约 1.70 公里、清华站约 1.65 公里）；三处临时重点片区质心与同名真实地物相距约 1.9-2.7 公里，其中大钟寺片区另偏南约 2.3 公里。重点片区为公告口径示意范围，四至未公布。官方边界发布后，全部图层与指标须整体校正复算。

慢行

9公里应答长卷慢行主线为全线连续概念线（约9.7公里）；三条应答门东西缝合概念示范线分别服务鸣钟之门段、应答原点段与人之跃段。全部标注概念属性、不代表道路红线。

蓝绿

一横一纵：主脊给叙事，清河给生态，交点给场景。绿地占提交范围约25%、公共空间约1.93%（临时边界口径）。

测试

低速配送机器人测试通道为概念线，建议先行于已开放的一期16.8公顷段划定测试环线与时段（物理隔离、安全员全程跟随、可随时急停撤回），验证达标后再研究逐级延伸、逐级报批。

9	公里 KM	应答长卷主脊
46	座 GATES	应答门以建成为准
70	个 COMMUNITIES	社区认领应答门
3	处 KEY AREAS	重点区域详细设计
122	颗 SPIKES	道钉 = 备案模型数

底图与图层说明

底图数据 © OpenStreetMap contributors (ODbL, 检索日期 2026-08-18; 设计图层为概念建议（虚线示意），非官方边界、非审批依据。

全部空间内容为概念建议，待专业团队深化，不构成政府审定结论。

设计说明：任务覆盖、指标、分期与合规

智能体开源征集任务书六项任务（agent.1–6）逐条挂接章节、图层、指标与图纸；合规矩阵登记23条要求，状态均为 addressed。

任务	本方案的回应	证据落点
agent.1 一带总体概念与功能统筹方案设计	命名主案“百年应答”统摄三大定位；9公里应答长卷主脊+南问—中答—北跃三段+一脊两翼十地块概念分区；对位已批控规“一带—轴两心多点”。	总体概念页·用地结构图·geometry/land_use.geojson
agent.2 AI全栈自主创新体系与世界级AI创新生态设计	“土地—空间—资金—人才—算力—数据—场景—政策”八要素×三区两翼配置；要素服务驿站（政策咨询、备案辅导、成果对接，非当场兑付）；国际对标六案提炼四种机制原型+一条数据治理红线。	正文统筹研究章·compliance_matrix.json
agent.3 AI+场景赋能新范式与智能化AI活力城市设计	12张AI场景卡挂接甲方标准场景ID，预设L1公开 / L2匿名汇总 / L3主动授权三档数据边界；全场景红线：不做人脸识别、不做个体轨迹追踪、不新增监控性采集。	正文场景章·设计说明页
agent.4 AI公共空间、智能原生新业态与朝圣地标设计	四大概念地标：应答钟与钟声广场、人字天桥、道钉带与零公里桩、应答门；全线共用10件标准化组件库，保证“一眼认得出、处处不重样”。	地标四页·geometry/public_space.geojson
agent.5 百年京张文化、中关村文化与AI新文化融合叙事设计	“题—答—阅”三带机制；以钉代碑五级荣誉载体（道钉 / 钟响 / 应答簿 / 认领铭牌 / 策展署名）；京张三色概念色卡与K0+000里程语汇导视。	灵感由来页·三带机制图
agent.6 一带全球AI创新活动体系与长期运营设计	春3月纪念开放日、夏6月毕业礼与青年道钉礼、秋9月《百年应答报告》与全球叙事联盟对话、冬12月进化日；城市进化档案馆公开归档迭代史与公众反馈。	分期与运营页·更新项目清单

核心指标与面积复算

指标	数值	状态	口径与说明
提交范围面积	约1141.28万平方米	known · high	polygon_area(submitted_site_boundary); 基于维护者登记的临时粗略边界
绿地率	约25.04%	known · medium	green_space_area / site_area
公共空间比例	约1.93%	known · medium	public_space_area / site_area
概念建筑基底合计	约3125平方米	known · medium	三处小型概念基底之和，均不含高度结论
重点区域数量	3处	known · high	count(key_detailed_design_areas)
容积率	未知	unknown	批准的强度控制与官方边界均缺失——不是缺项，而是“未知是合法终态”的诚实表达

复算前置条件

全部数值基于临时边界，不作为官方红线、审批依据或精确面积依据；官方边界发布后，全部图层与指标按登记的复算清单逐项重算。空间自检 spatial_review 结果 PASS：用地拓补覆盖缺口0.398平方米、最大重叠0.087平方米，面要素越界小于1平方米、概念线越界为0。

分期实施与长期运营

一期	南问段 · 依托既有建成界面先启动 道钉带首段 · 钟声广场研究 · 一期段机器人测试环线
二期	中答段 · 随公园二期建设推进 应答门认领 · 原点纪念空间协商 · 断点客厅
三期	北跃段 · 承接专项研究 人字天桥专项研究 · 清河蓝绿衔接 · 弹性留白

编号	更新项目	主要依赖
JZ-01	道钉带与零公里桩（含第0号钉）	文物部门协商、备案口径年审机制
JZ-02	应答钟与钟声广场	权属梳理、站城关系深化
JZ-03	46座应答门与社区认领	二期建设进度、社区动员
JZ-04	断点客厅（东西向穿越·先通后留）	穿越优化策略专业深化
JZ-05	要素服务驿站沿线布点	低效空间权属、运营主体确定
JZ-06	一期段机器人测试环线	管理许可、安全预案审批
JZ-07	人字天桥概念节点	工程可行性专项研究
JZ-08	城市进化档案馆	运营主体、归档规则制定

春 · 3月 百年应答纪念开放日 清华园车站；公益纪念性质，无企业冠名、无商业路演、无当场钉钉	夏 · 6月 毕业礼 + 青年道钉礼 青年策展权年度成果展示并署名，学生为主角	秋 · 9月 《百年应答报告》发布 备案清单、开源清单、场景开放清单三张可审计清单	冬 · 12月 进化日 档案馆年度归档展、Logo版本号演进发布、应答钟年度鸣响
--	--	--	---

空间表述边界

全部空间与开发内容均为概念建议，参考方案，供专业团队深化研究，不构成政府审定结论。本方案不提出容积率、建筑高度、道路红线、拆改留分类等任何结论性判断，不声称官方批准、审定控规或保证实施。

文物与工程

清华园车站文物本体不动一砖一瓦；文保范围GIS缺失，一切落位均为待文物主管部门协商的概念选点。应答钟为当代新铸之钟，与大钟寺文物古钟严格切割，绝不敲击、绝不移动、绝不商业化使用任何文物古钟。人字天桥不含任何工程结论；机器人测试以取得管理许可为前提。

图像与底图

全部效果图为AI概念意象图，非实景照片；生成工具 LibTV / 模型 Lib Image，规划图底图数据 © OpenStreetMap contributors (ODbL)，检索日期 2026-08-18；设计图层为概念建议（虚线示意），非官方边界、非审批依据。