



落位筛查 / A0 原尺寸 1:500

OSM 形态证据, 不是地块、红线、空地或可建性证明

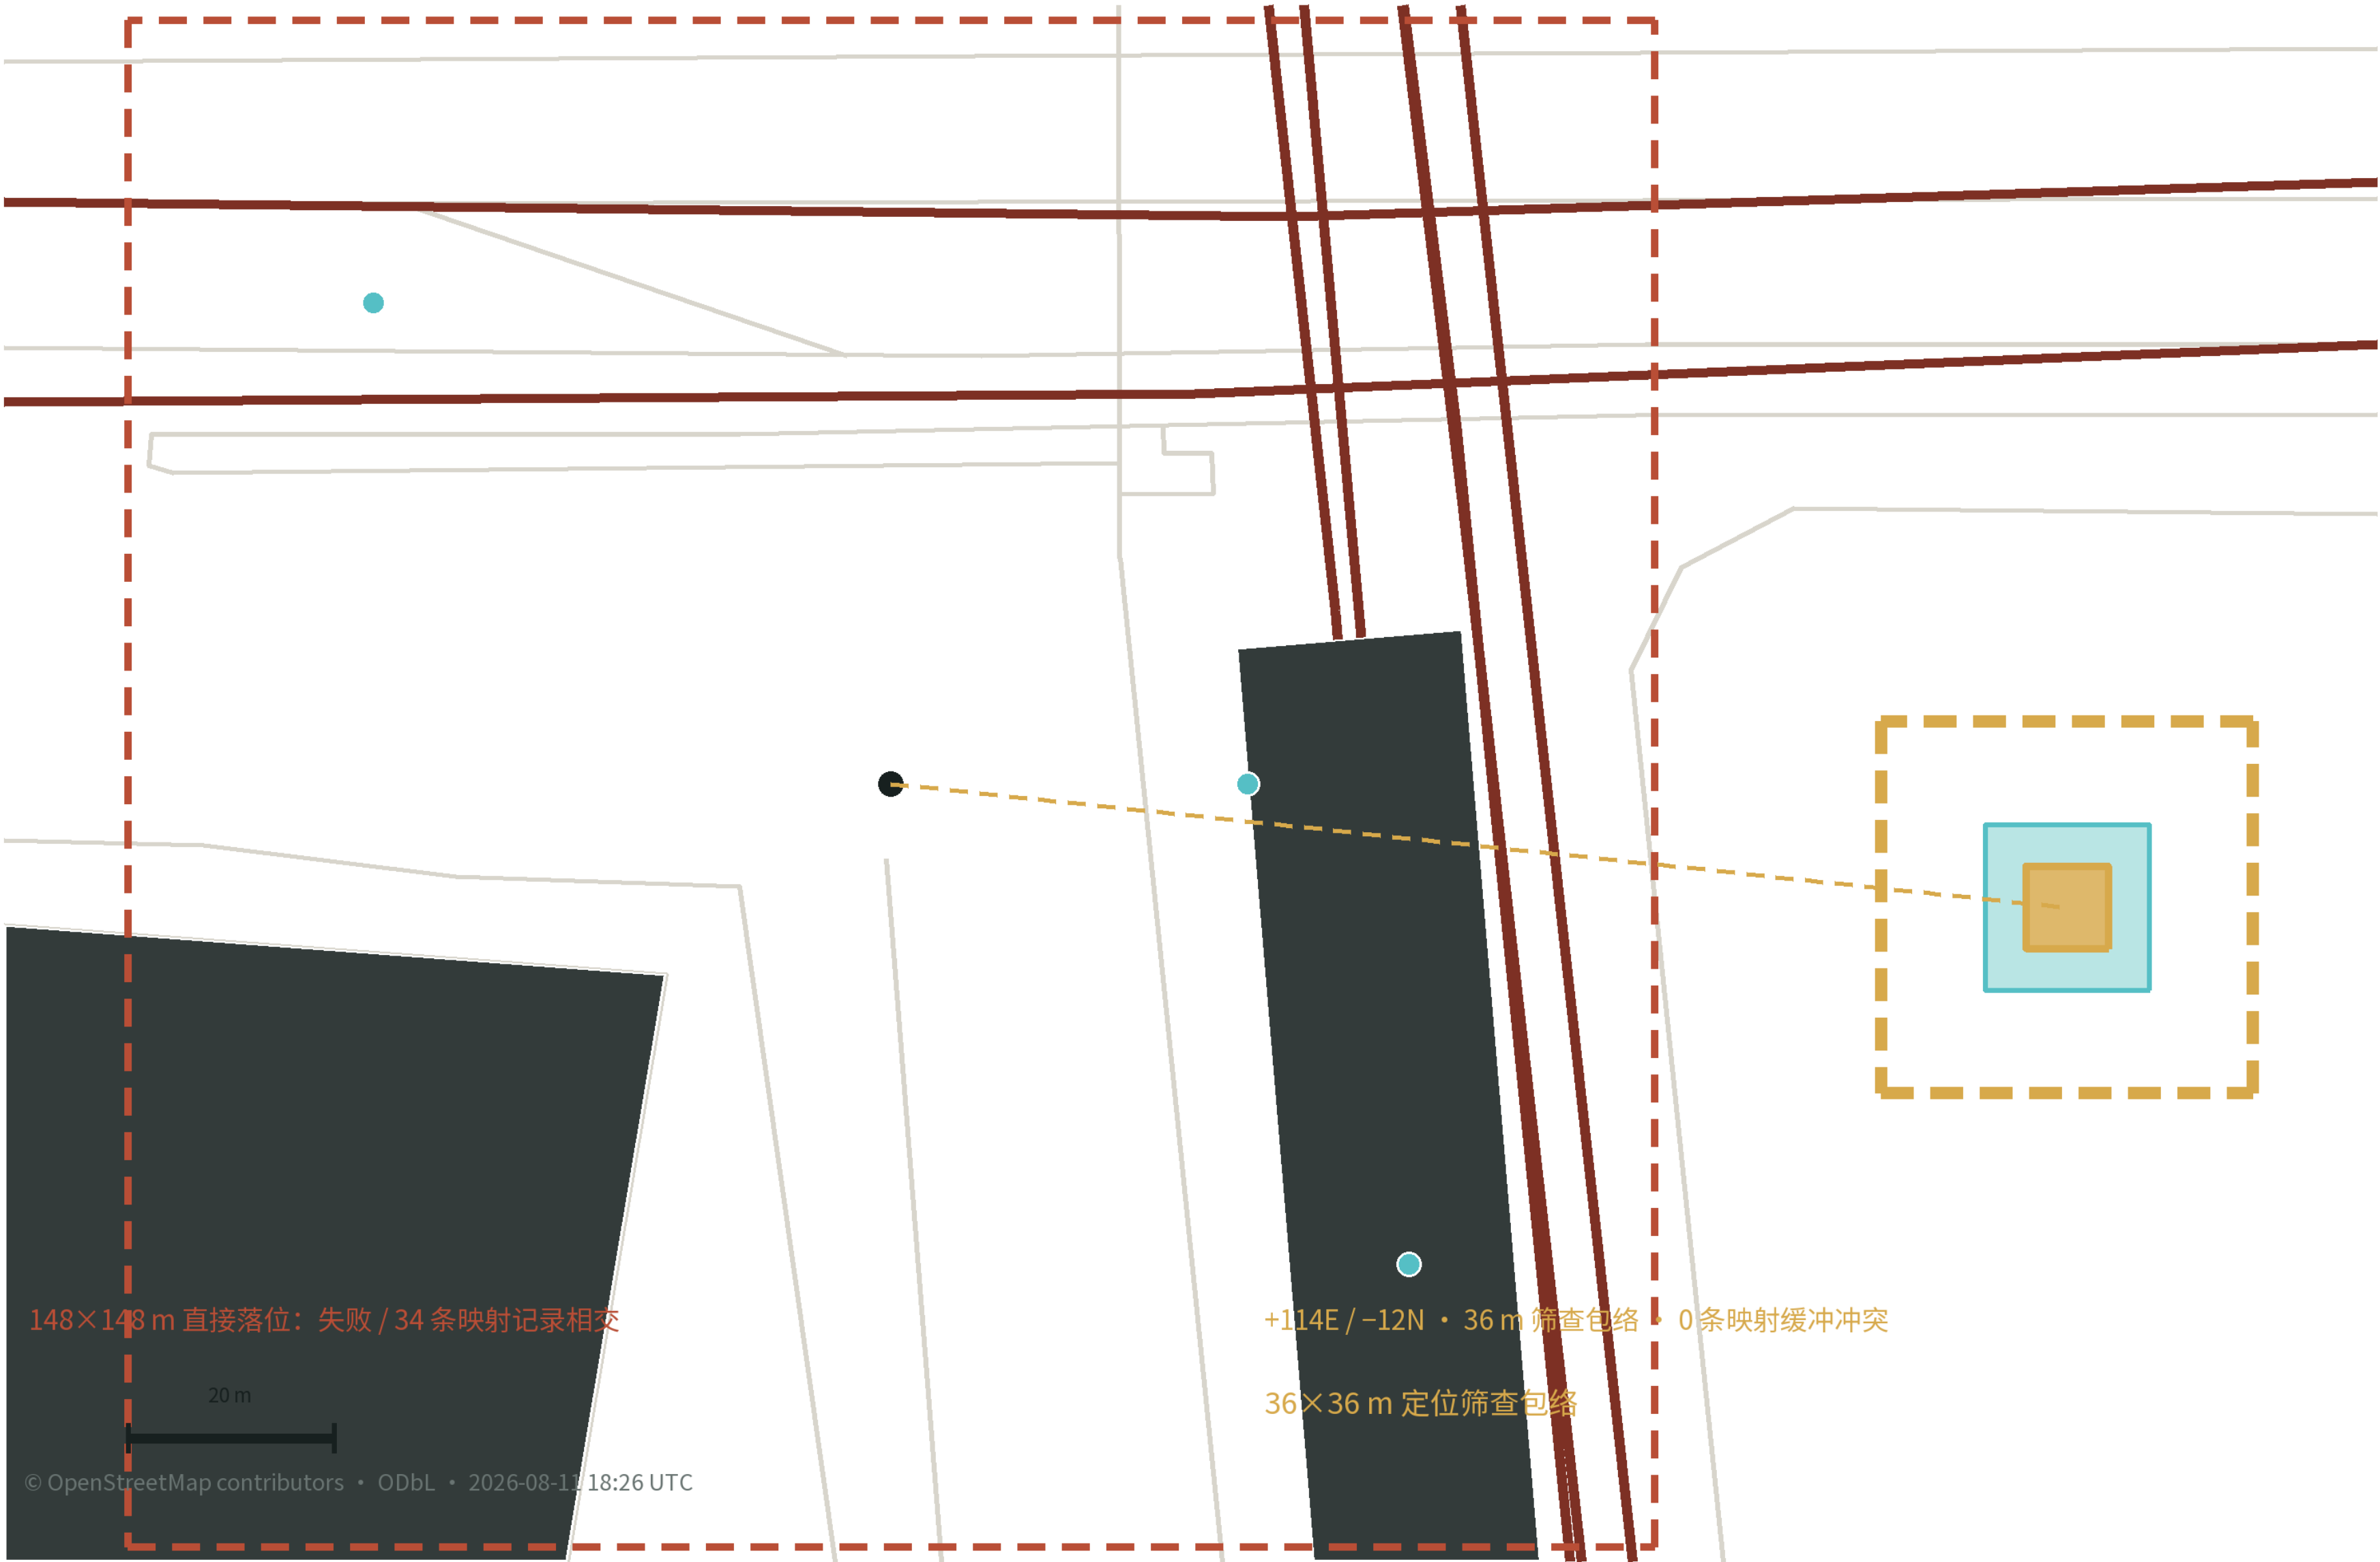


P0 平面 / A0 原尺寸 1:100

16 m 可逆地面内的一跨 8 m 支撑

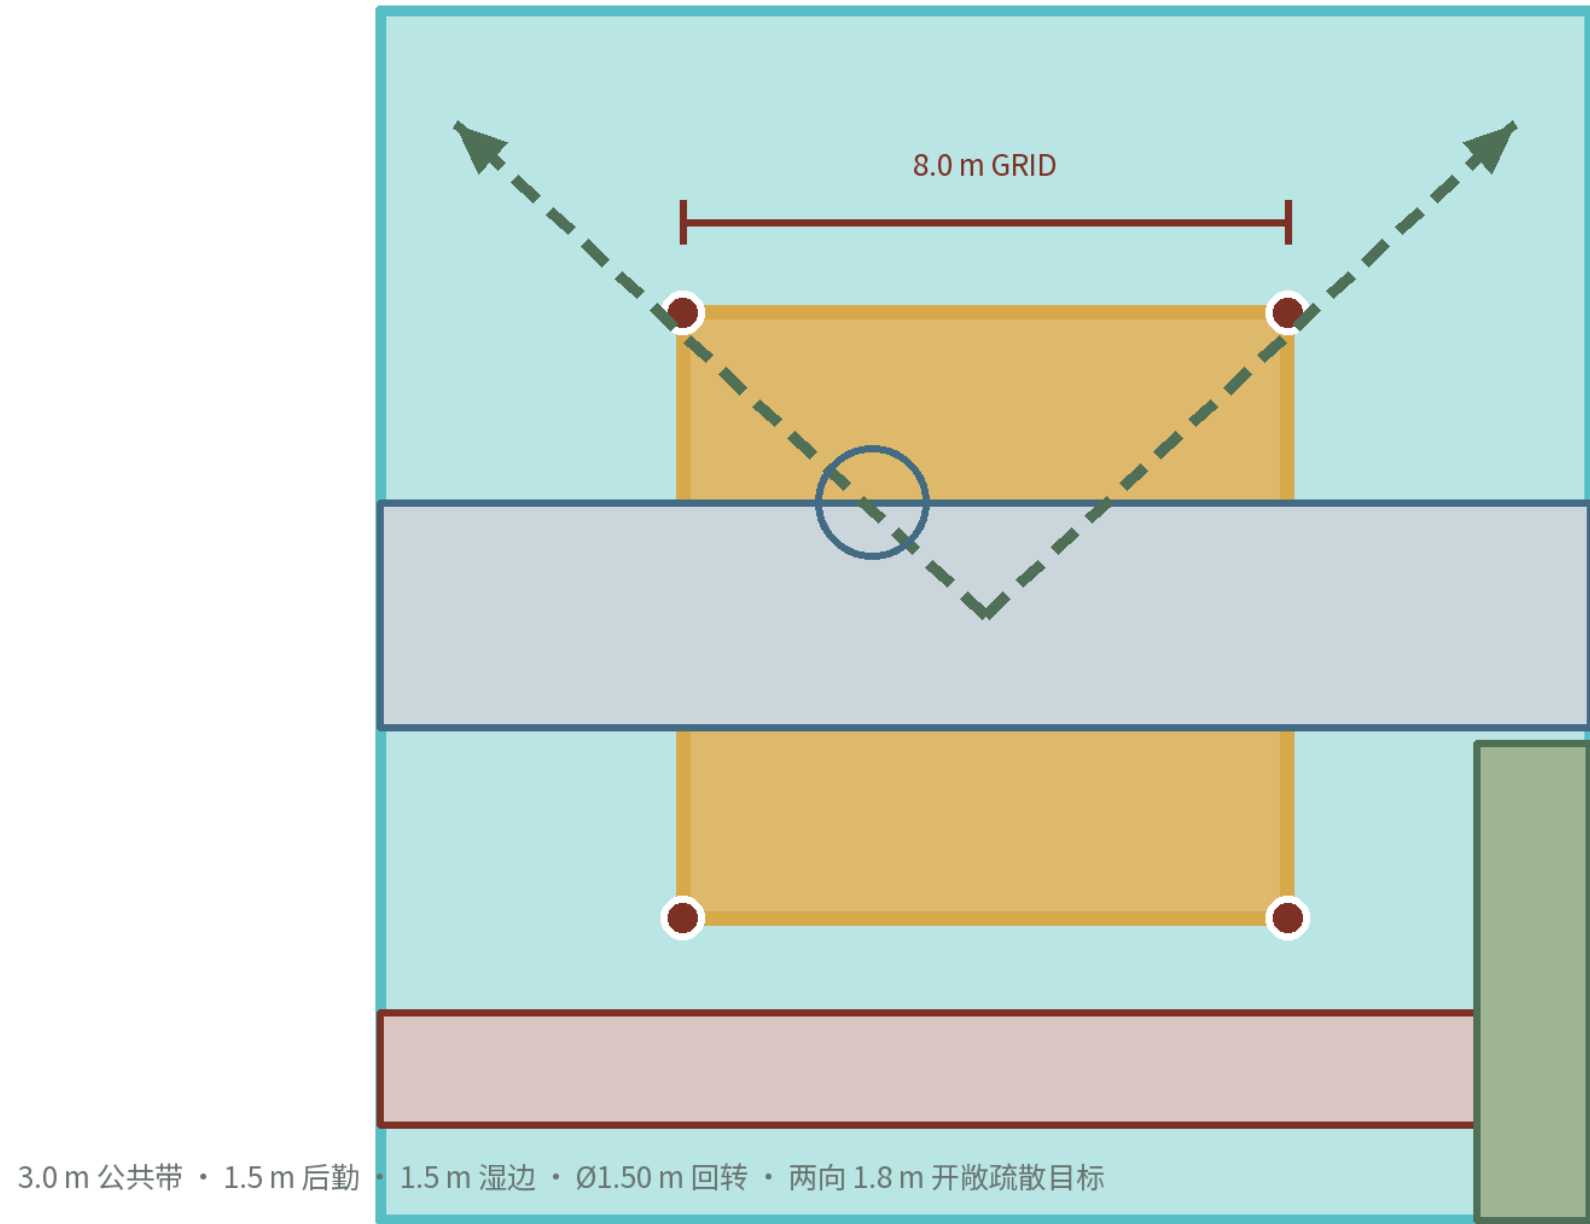

使用剖面 / A0 原尺寸 1:200


开放雨棚: 无烹饪、无动力电池充电; 消防与人数均待审

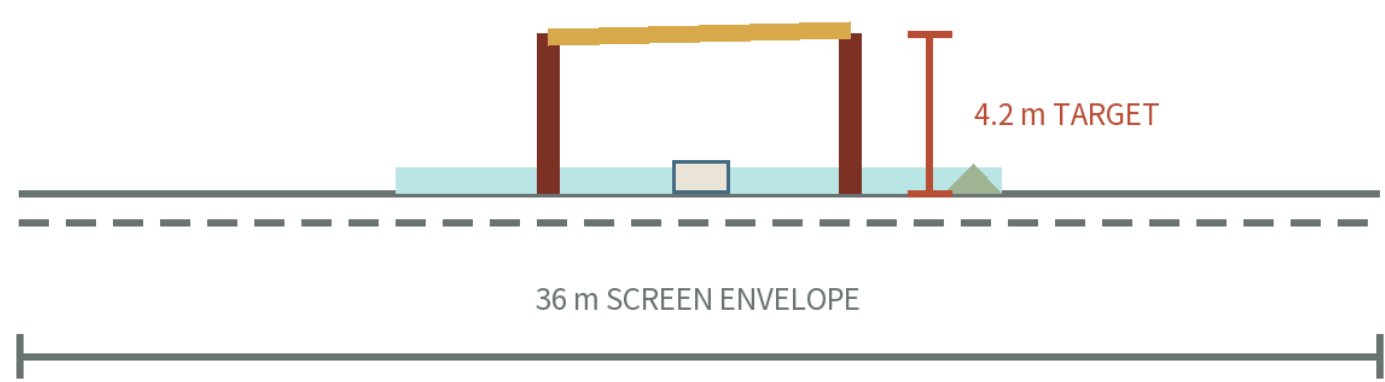

檐—水—服务接口 / A0 原尺寸 1:20

净几何按比例; 构件与产品厚度待结构/消防/机电确定


可拆屋面盒 / 2% 找坡假设

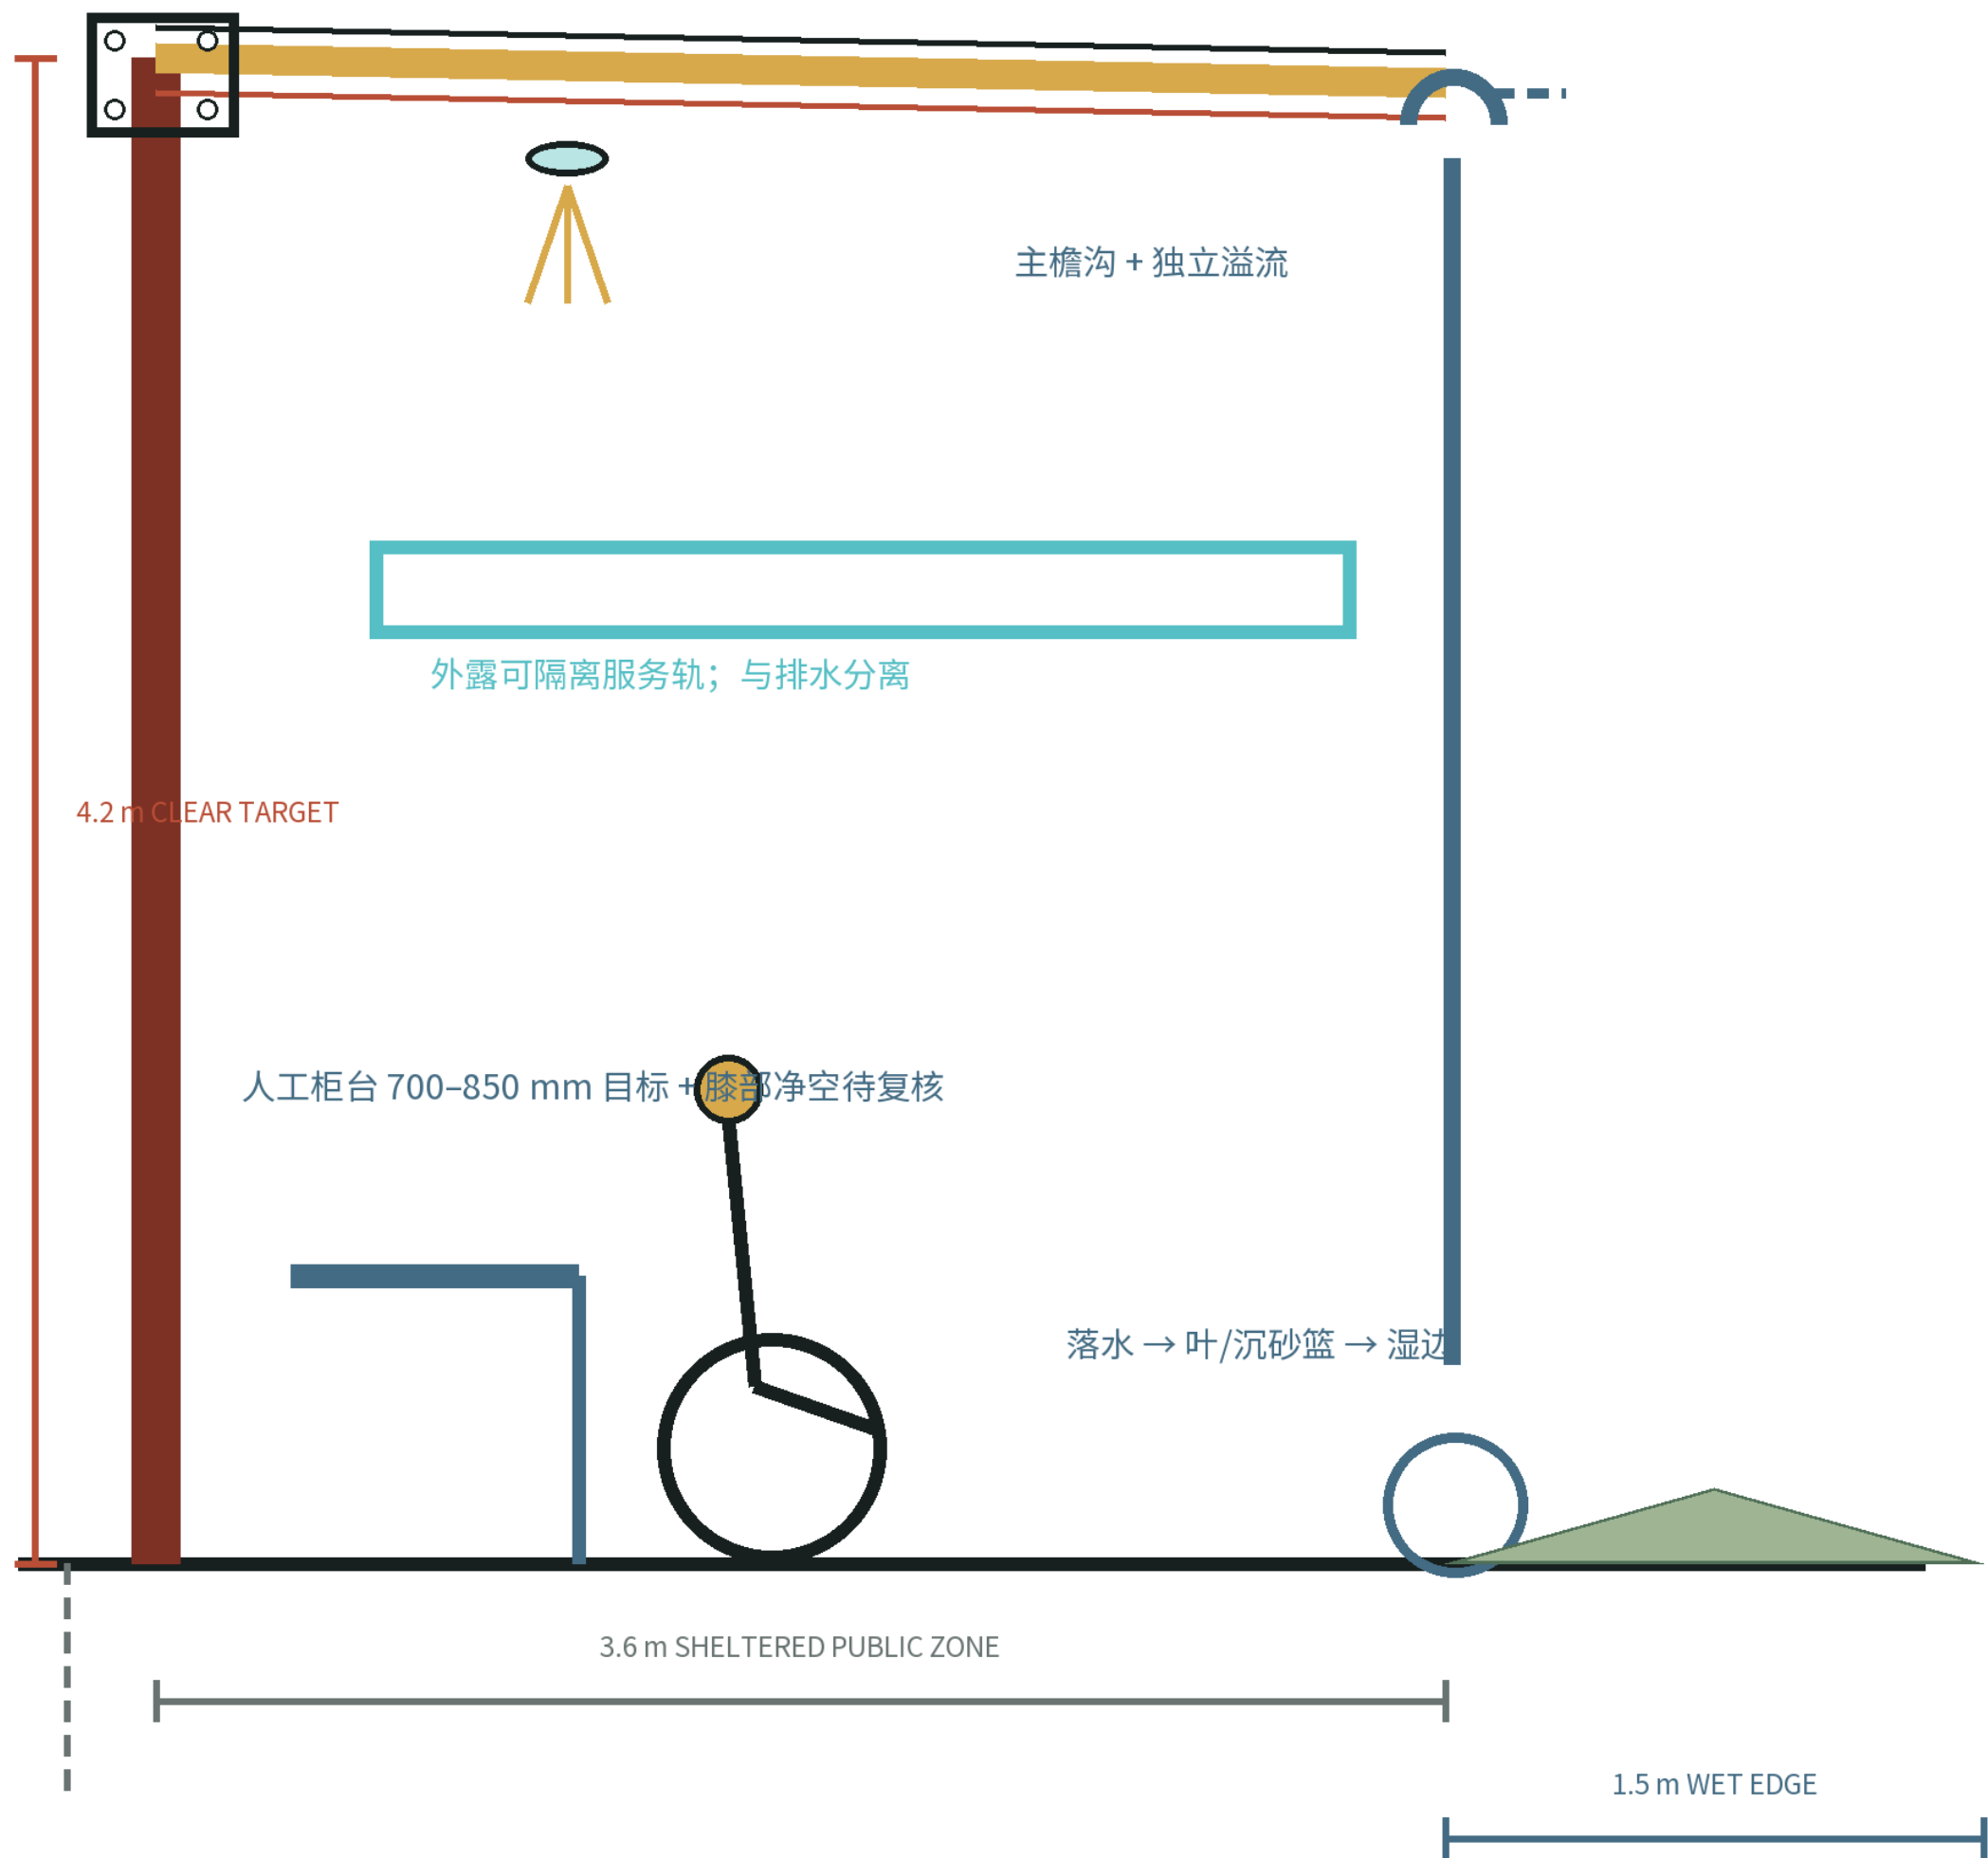

64 m² 屋面每 10 mm 雨 = 0.64 m³; 出口/蓄水/渗透待地形、土壤与市政排水。

同一几何的场地轴测

OSM 建筑仅作平面剪影; 没有高度、地块或权属证据

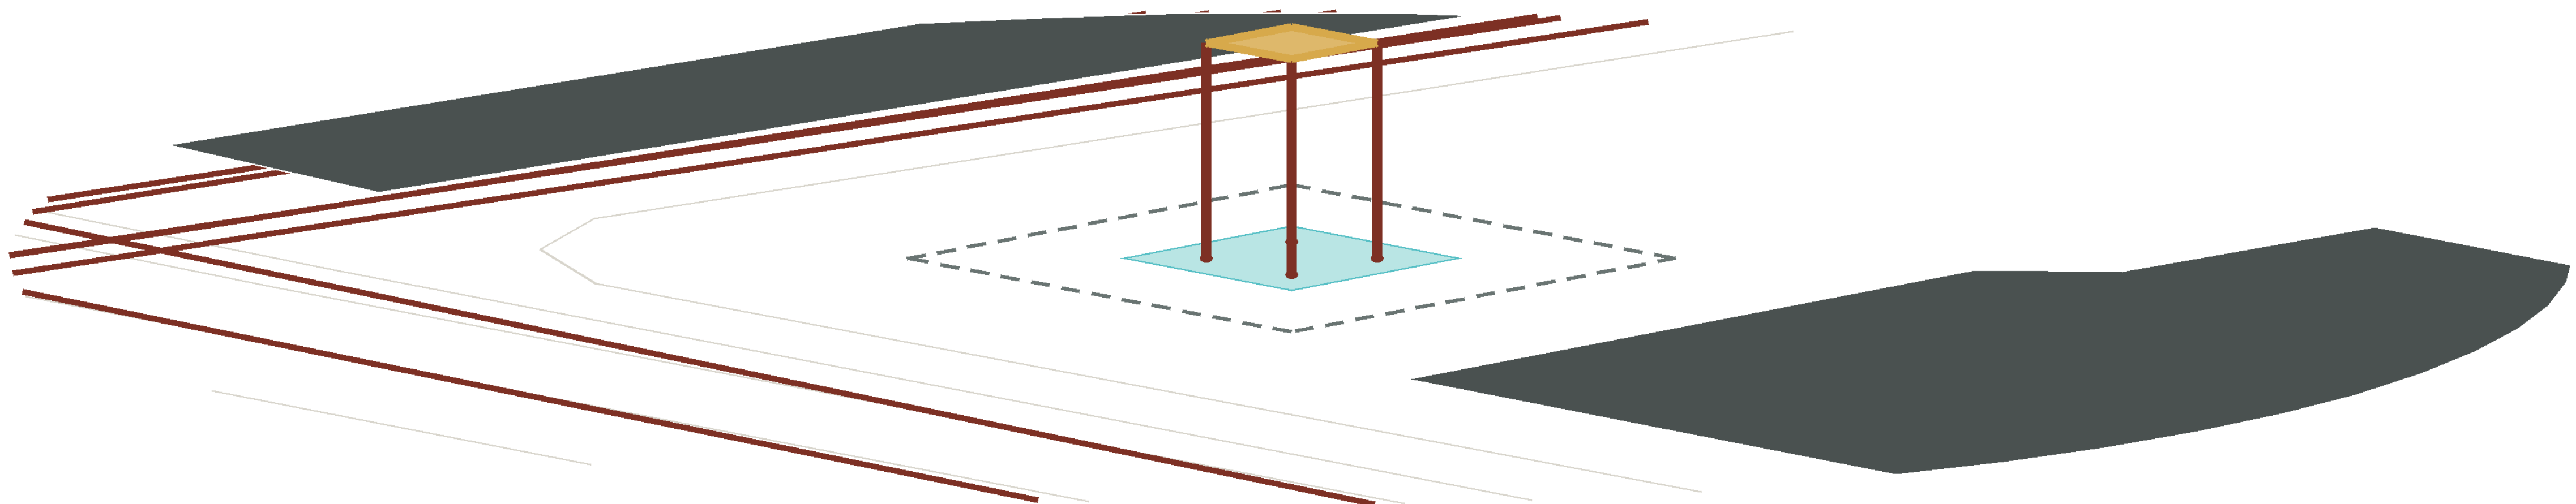

拟建 8×8 m 可拆第一跨

36×36 m 仅为定位筛查包络

材料性能表 / 参赛者参考规格

01	螺栓热镀锌框架 · 截面/钢级/耐火待定	¥1.9–3.8M
		参赛者概算 / 非投标价
02	可拆金属屋面盒 · 风雪/结露层待定	06:00–24:00 · 5 FTE 轮班
03	干铺可换地面 · 防滑/冻融/渗透待定	运维假设 ¥1.2–2.2M/年
04	外露排水 + 冬季排空; 落点在净路之外	运维假设 1.2–2.2M/年
05	明装可隔离服务轨 · 负荷/计量/防火待定	06:30 骑手/保洁饮水休息
		12:30 餐食交接; 不烹饪
		19:00 修理/学习/人工帮助

无权属/红线、具名运营者、12个月运维储备、通行协议、地铁/管线、消防/结构/机电审查与许可; 不建设、不开放。

01 / 07 · 从错误落位到第一跨

真实图底否决 148 米直接落位; P0 收缩为 8×8 米可拆一跨与 16×16 米可逆地面, 并把 T00 设为 T01-T11 / 第 1-15 周条件参考窗的文件前提

01 8×8 m / 可拆首跨

02 T00 / 文件前提

03 T01-T11 / W1-15 条件参考

04 12 类未来角色 / 单一 A

成对跨 · 差分廊 · 单队列


机制相同，建造与公众交接空间不同；参数平面和剖面把 H 路、可拆位与停止条件落到建筑

众智园 · 验证院

验证院

院 / 让公众看见受控验证


A/B 可拆可关 · H 旅行和人工服务不断

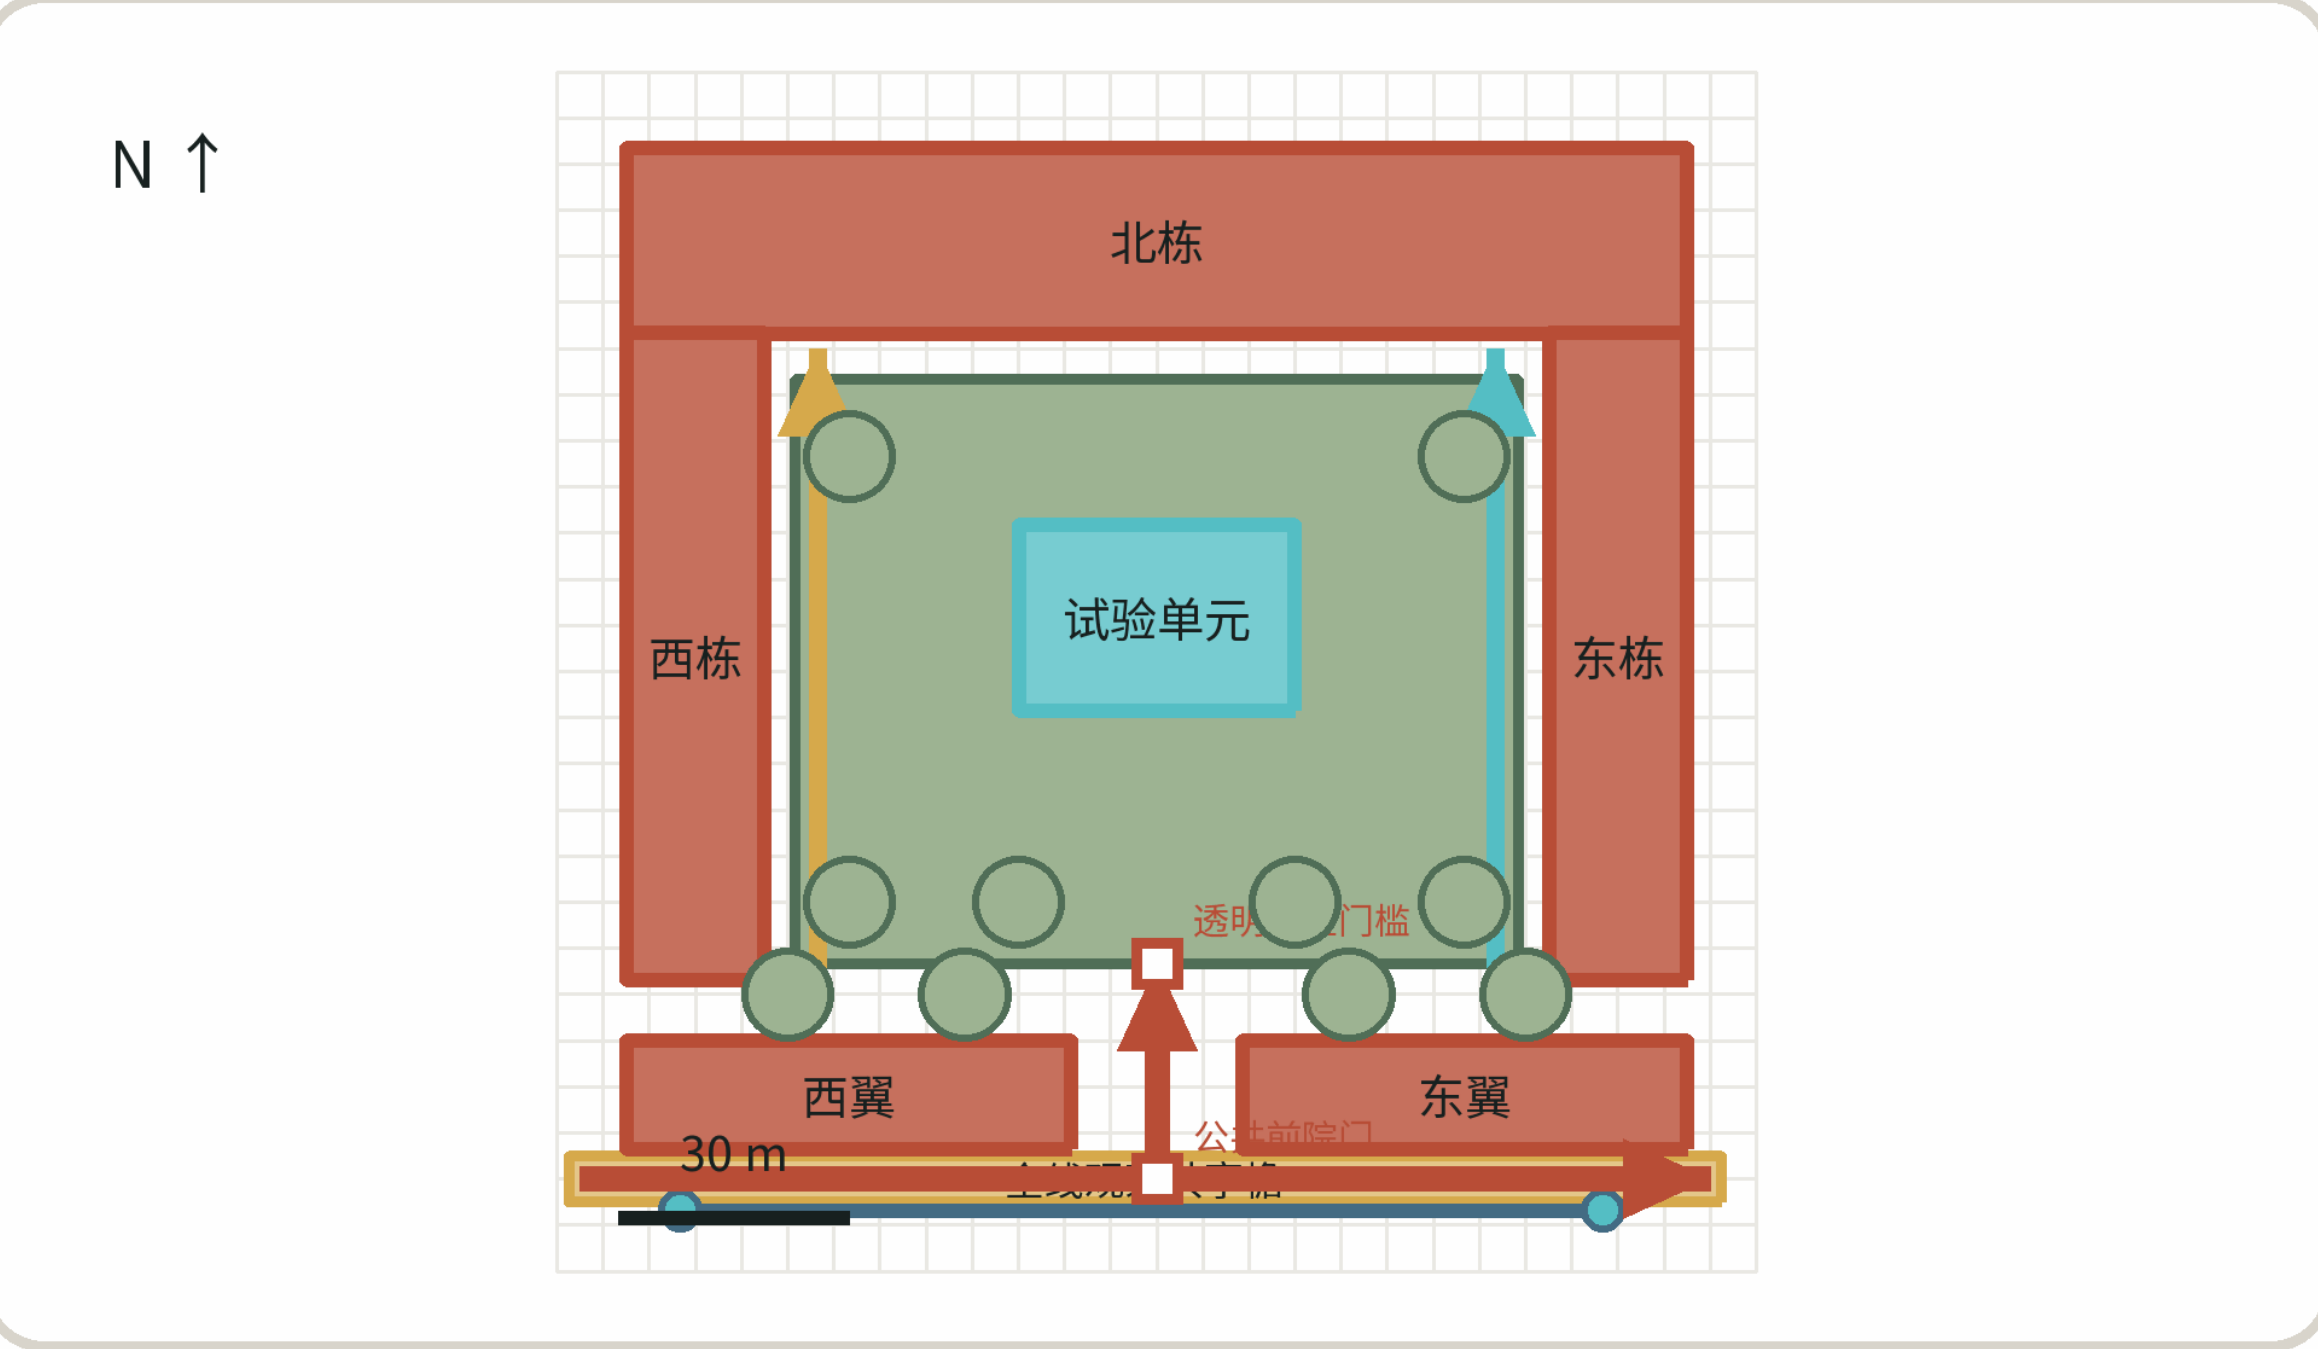

公共地面—气候边缘—长期支撑—可换填充

可拆共享檐 · 外露排水 · 冻融检修

CERTIFIED LONG-LIFE 6 M SUPPORT → BOLTED SECONDARY FRAME → DRY REPLACEABLE INFILL INSPECTABLE SERVICE BAND

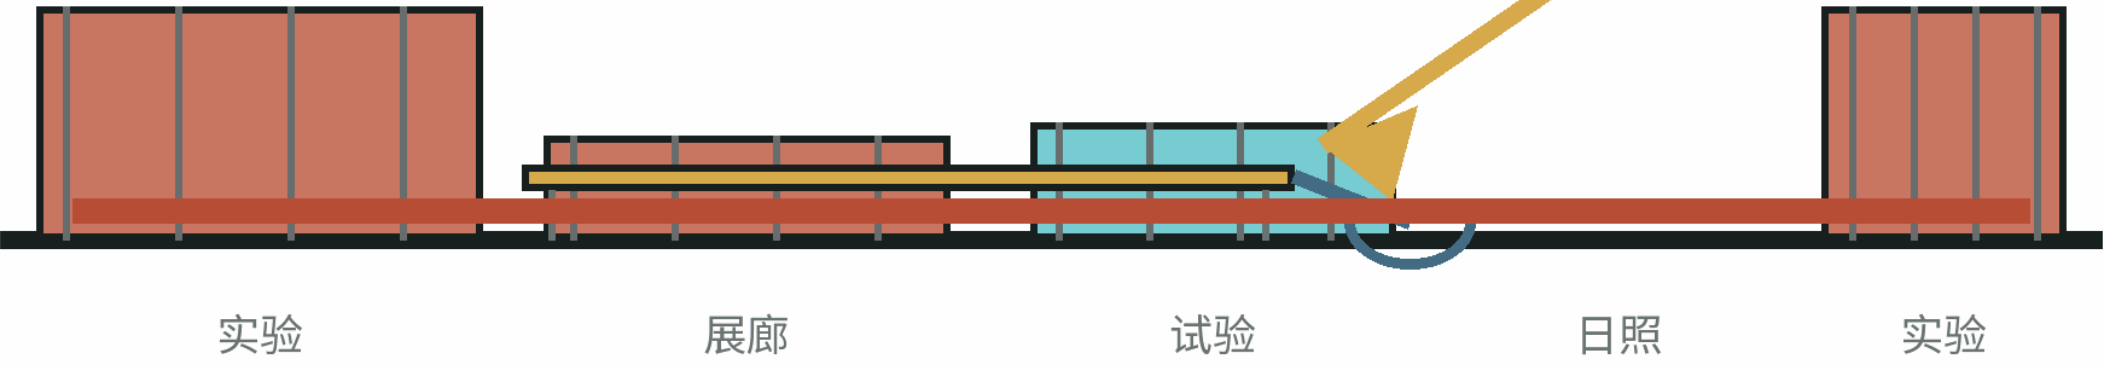

拆改留 保留可用框架 · 修复公共门檐 · 插入可撤第一跨

第一步 观察廊 · 隔离测试格

拟议责任 试验安全主管 · 独立校核者（角色类别）

停止规则 越界、不可复演或失联继续即停


候选落位 · 正式边界到位后统一复核并重新绑定

AI 原点 · 原点廊院

原点廊院

廊 / 改造优先的校园—社区编织


A/B 可拆可关 · H 旅行和人工服务不断

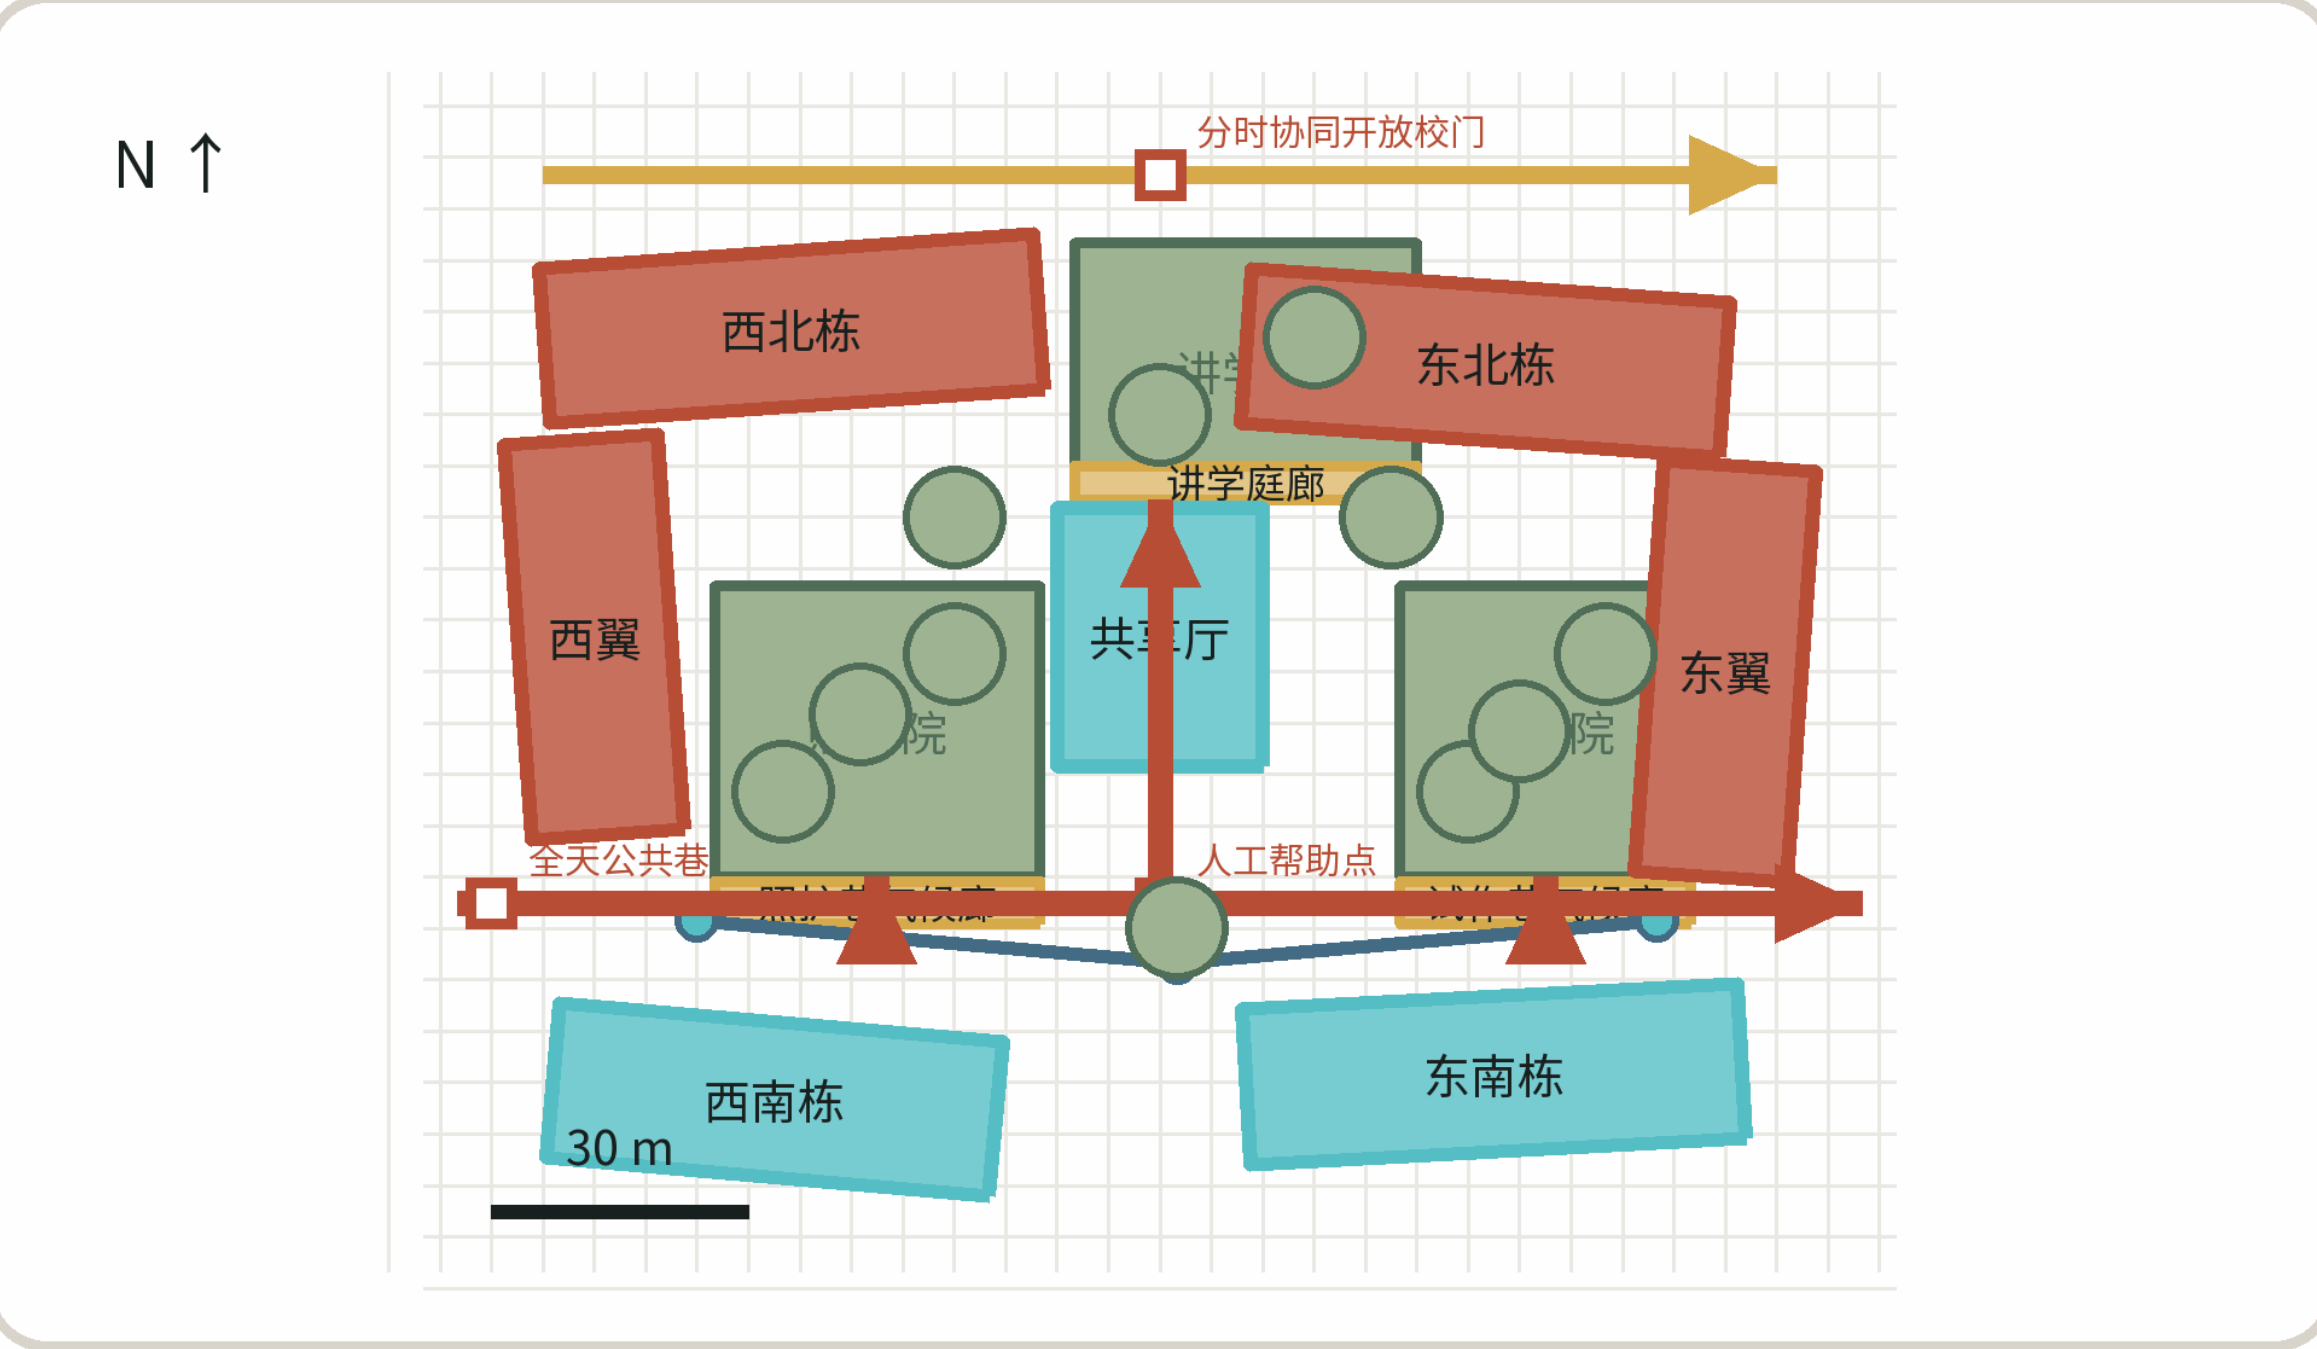

公共地面—气候边缘—长期支撑—可换填充

可拆共享檐 · 外露排水 · 冻融检修

RETAIN AND CERTIFY EXISTING FRAME FIRST → INDEPENDENT BOLTED PLUG-IN → DRY 1.2 M INFILL COORDINATION → EXPOSED MAINTAINABLE SERVICE STRIP

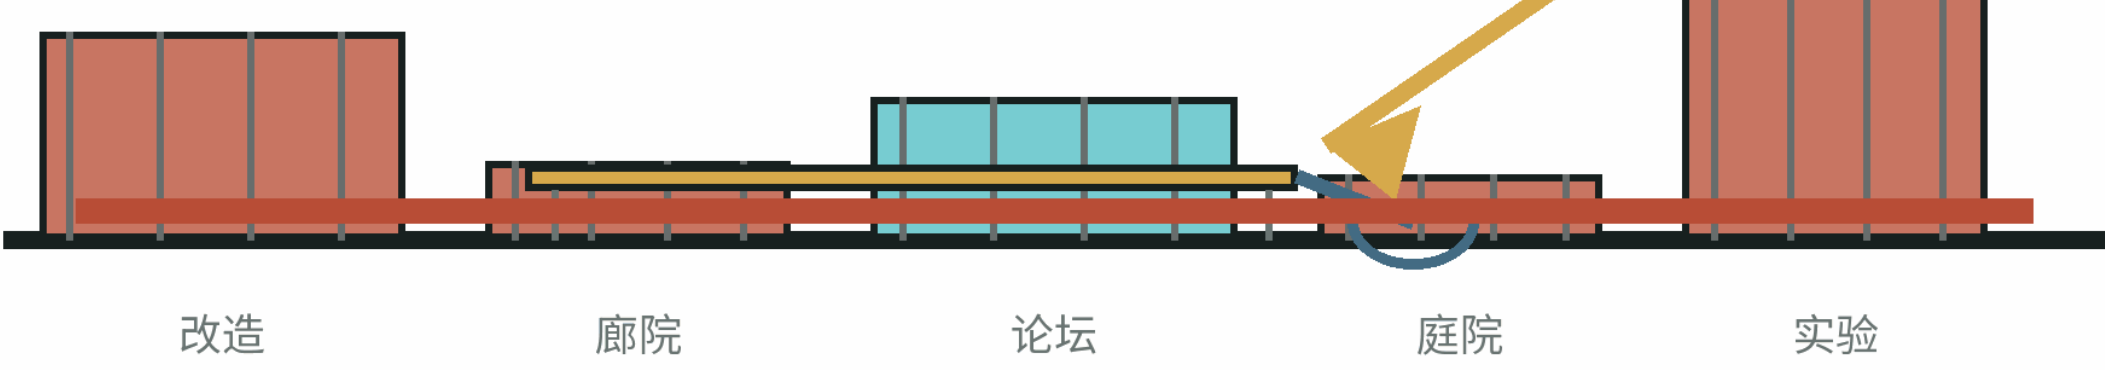

拆改留 保留校园/社区存量 · 修复通行 · 插入多孔廊院

第一步 分时协同开放校门 · 照护院

拟议责任 校园—社区联合运营（角色类别）

停止规则 无通行协议、无照护运营者即不建


候选落位 · 正式边界到位后统一复核并重新绑定

大钟寺 · 城市交汇厅

城市交汇厅

厅 / 四向公共入口与全天候城市客厅


A/B 可拆可关 · H 旅行和人工服务不断

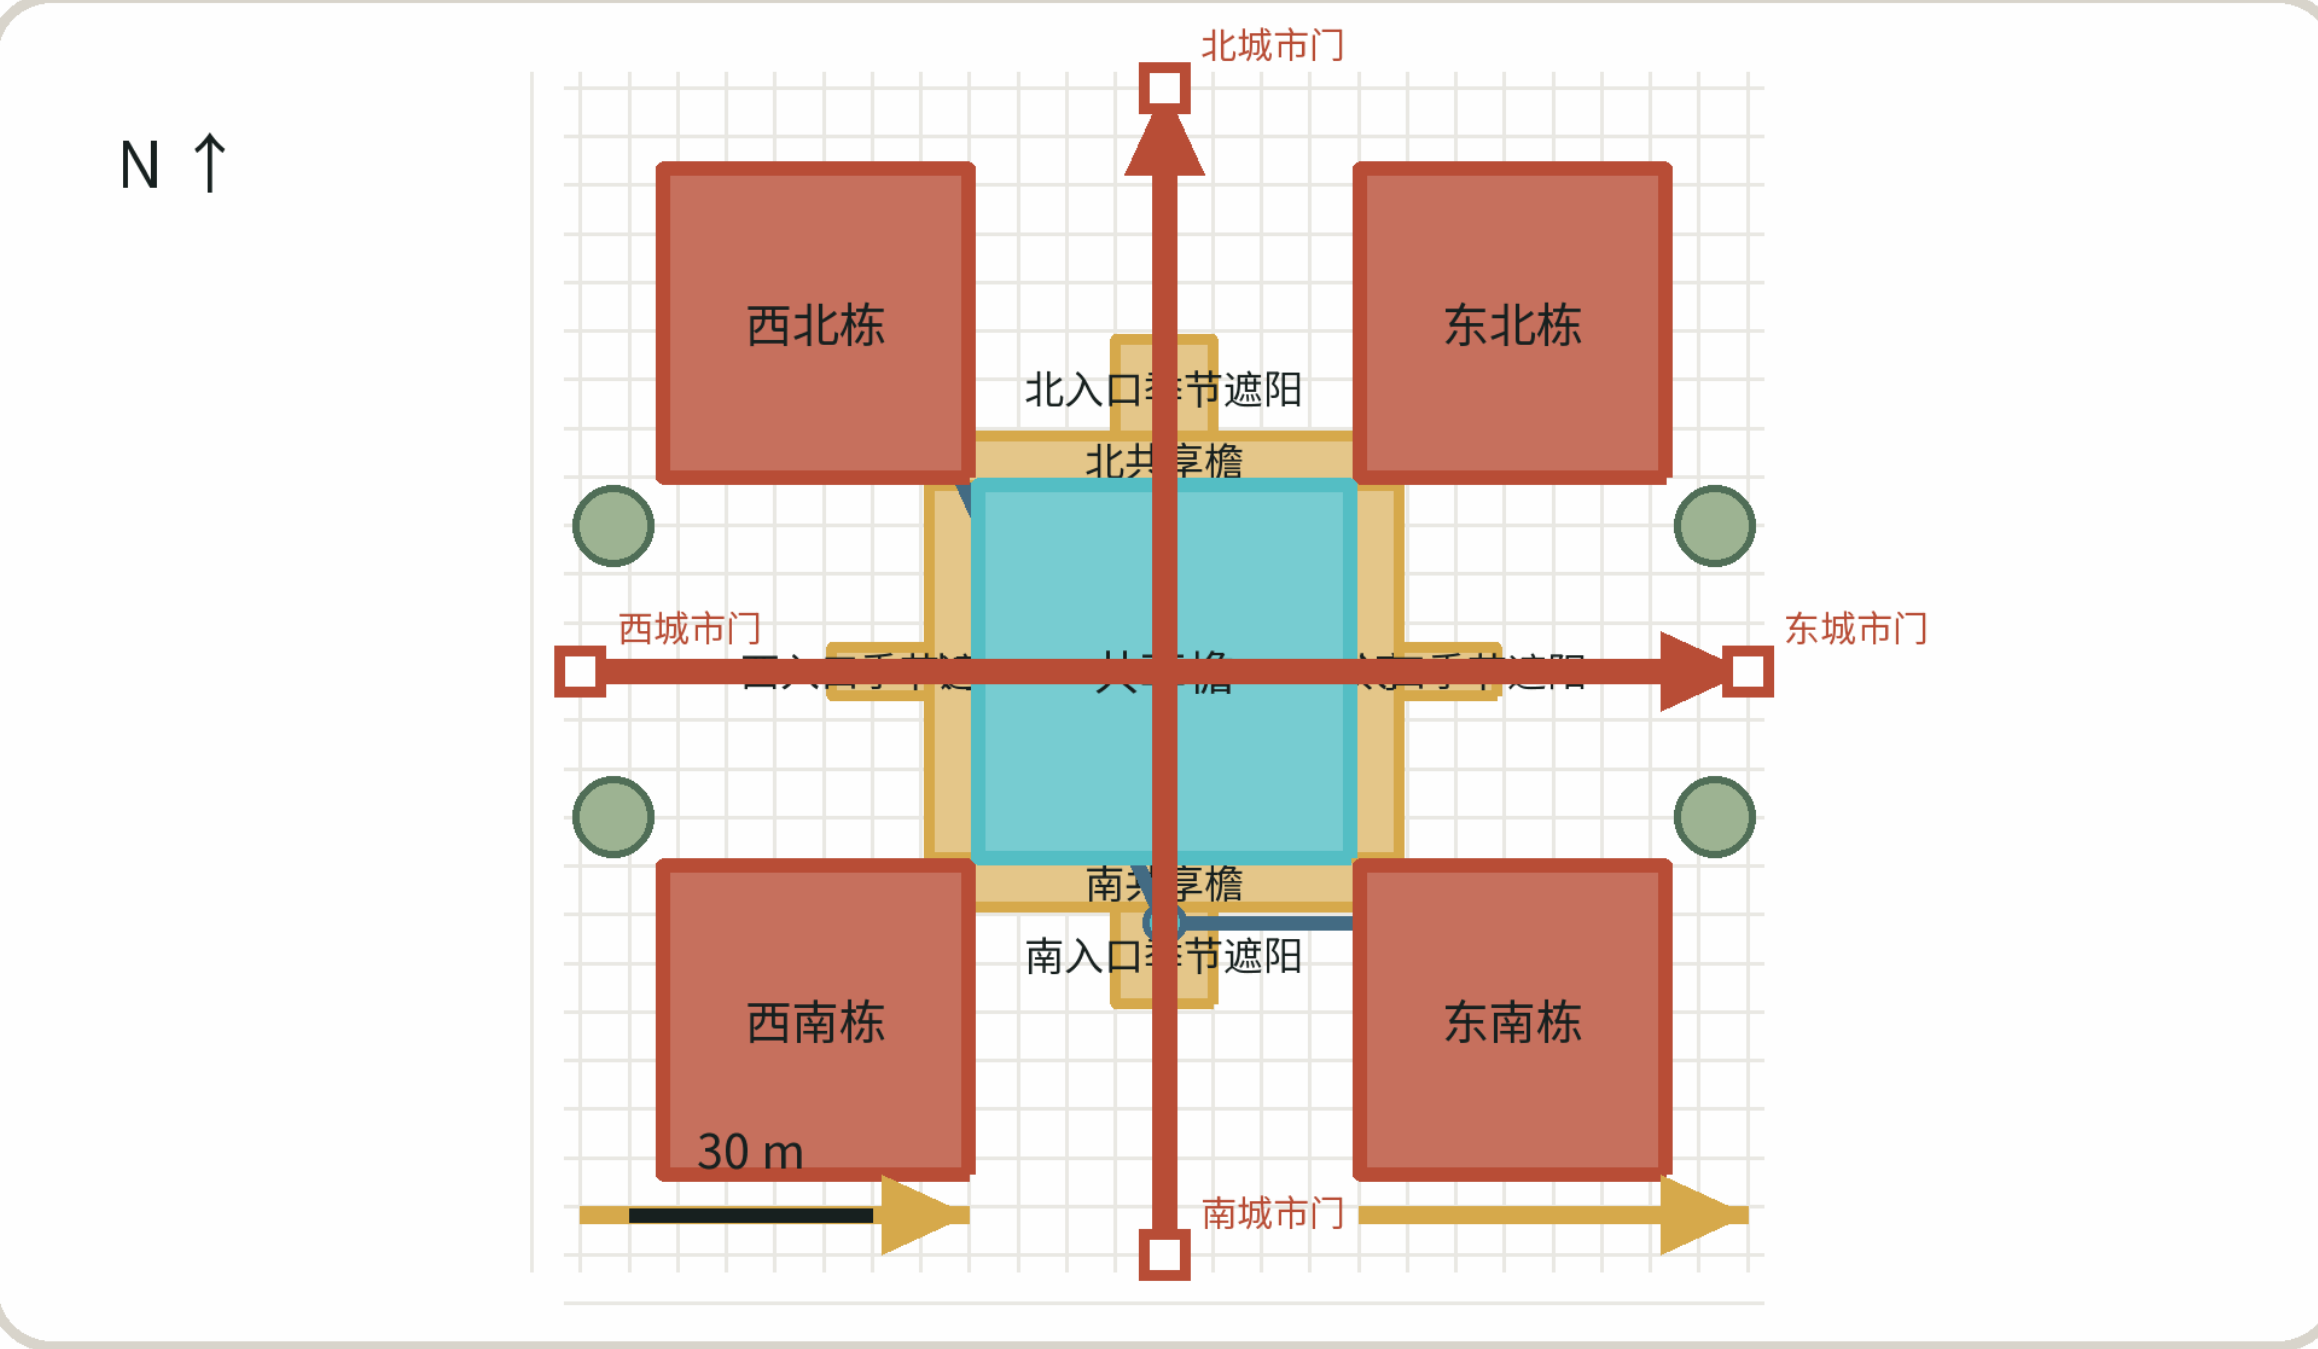

公共地面—气候边缘—长期支撑—可换填充

可拆共享檐 · 外露排水 · 冻融检修

LONG-LIFE 8 M PRIMARY FRAME → DEMOUNTABLE ROOF CASSETTES → REPLACEABLE MARKET/SERVICE INFILL → INSPECTABLE PERIMETER SERVICE BAND

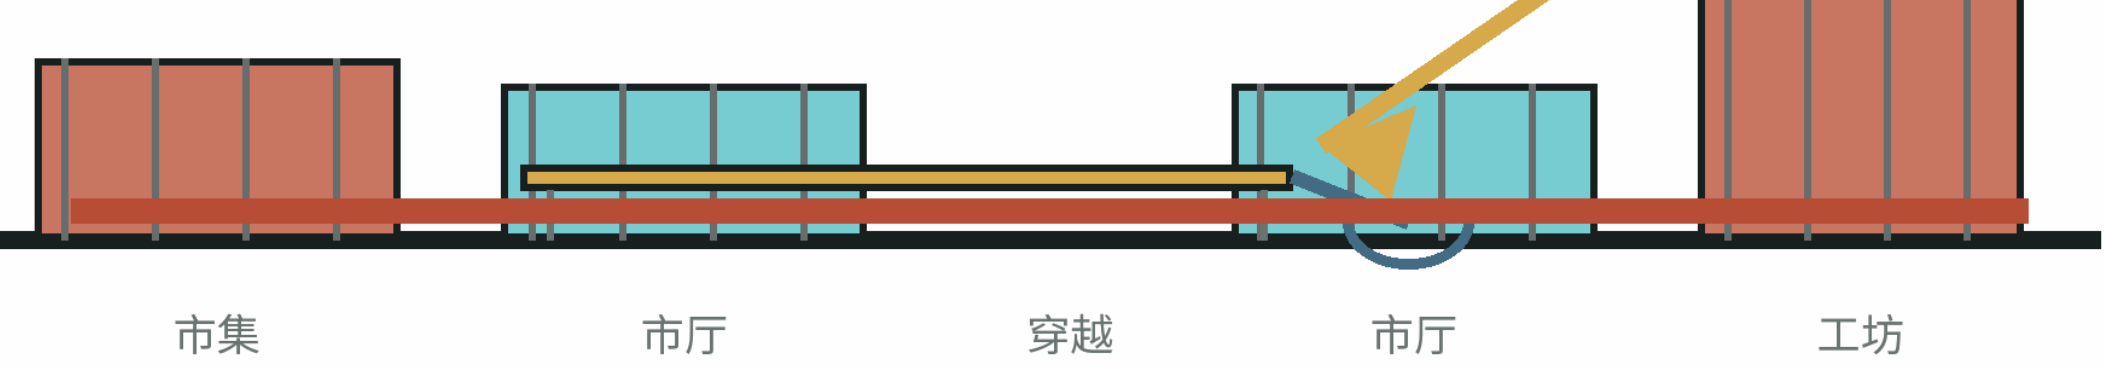

拆改留 先做拆改留调查 · 修复四象限步行 · 插入全天候共享檐

第一步 站点门廊 · 骑手驿站 · 人工帮助台

拟议责任 属地 · 交通 · 共地运营者（角色类别）

停止规则 未测人流、权属、消防或造价即不扩张

候选落位 · 邻近国保觉生寺；待套核保护规则，不骑缓冲线

让失败可见，让 H 桌留下

一次本地 BGE-M3 shadow 暴露 7 个分歧；4 个原点标签分歧把永久人工 H 桌与差分显示变成不可删减的空间配置

本地模型 Shadow

29 / 36

B 与参赛者 A/参考拓扑一致；A 不是独立真值

可见分歧

7 Δ

4 个非 hard-stop 分歧集中在原点任务

确定性 H

12 / 12

每个 hard-stop 均由确定性 H 门拦截

空间结果

H TABLE

永久人工复核 + 公开差分显示

一次真实本地推理：A/参考 × B/候选

BGE-M3 • 1 批 / 39 输入 • 1024 维 • 精确 tag/manifest/blob 哈希

A/ 参考	B=验证院	B=原点	B=交汇厅
验证院	10	0	2
原点廊院	3	7	2
城市交汇厅	0	0	12

非 hard-stop 的四个分歧：AI01-ambiguous • AI06-normal/ambiguous • AI08-ambiguous

空间改变 / KEEP B IN SHADOW

四项非 hard-stop 分歧均为原点标签：永久 H 桌与差分显示不得删减，B 不晋升；不虚构尺寸变化。

P0 / 从设计到决定

一条条件接力把前提、责任、数量和验收连起来

T00
文件前提

>

T01-11
第 1-15 周参考

>

12
未来角色 / RACI

>

16
数量行

>

12
验收指标

单一责任

12 项任务各有且仅有 1 个 A

数量可追溯

14 项设计/参考推导 + 2 项待实测或获授权复核

凭证交接

12 份模板：编制者 → 未来出具/责任角色 → 复核者 → 接收者

验收规则


8 条参赛者规则 + 4 项获授权基线后确定

边界 • 参赛者模板未签署 / 未批准 • 外部证据回执 0 • 外部放行 HOLD

分歧不是后台分数：它在原点留下人工复核的桌、公开可读的差分和不依赖 B 的 H 路。

京张共地 / 真实城市作底

七处局部图底关系：不以推测填补数据空白

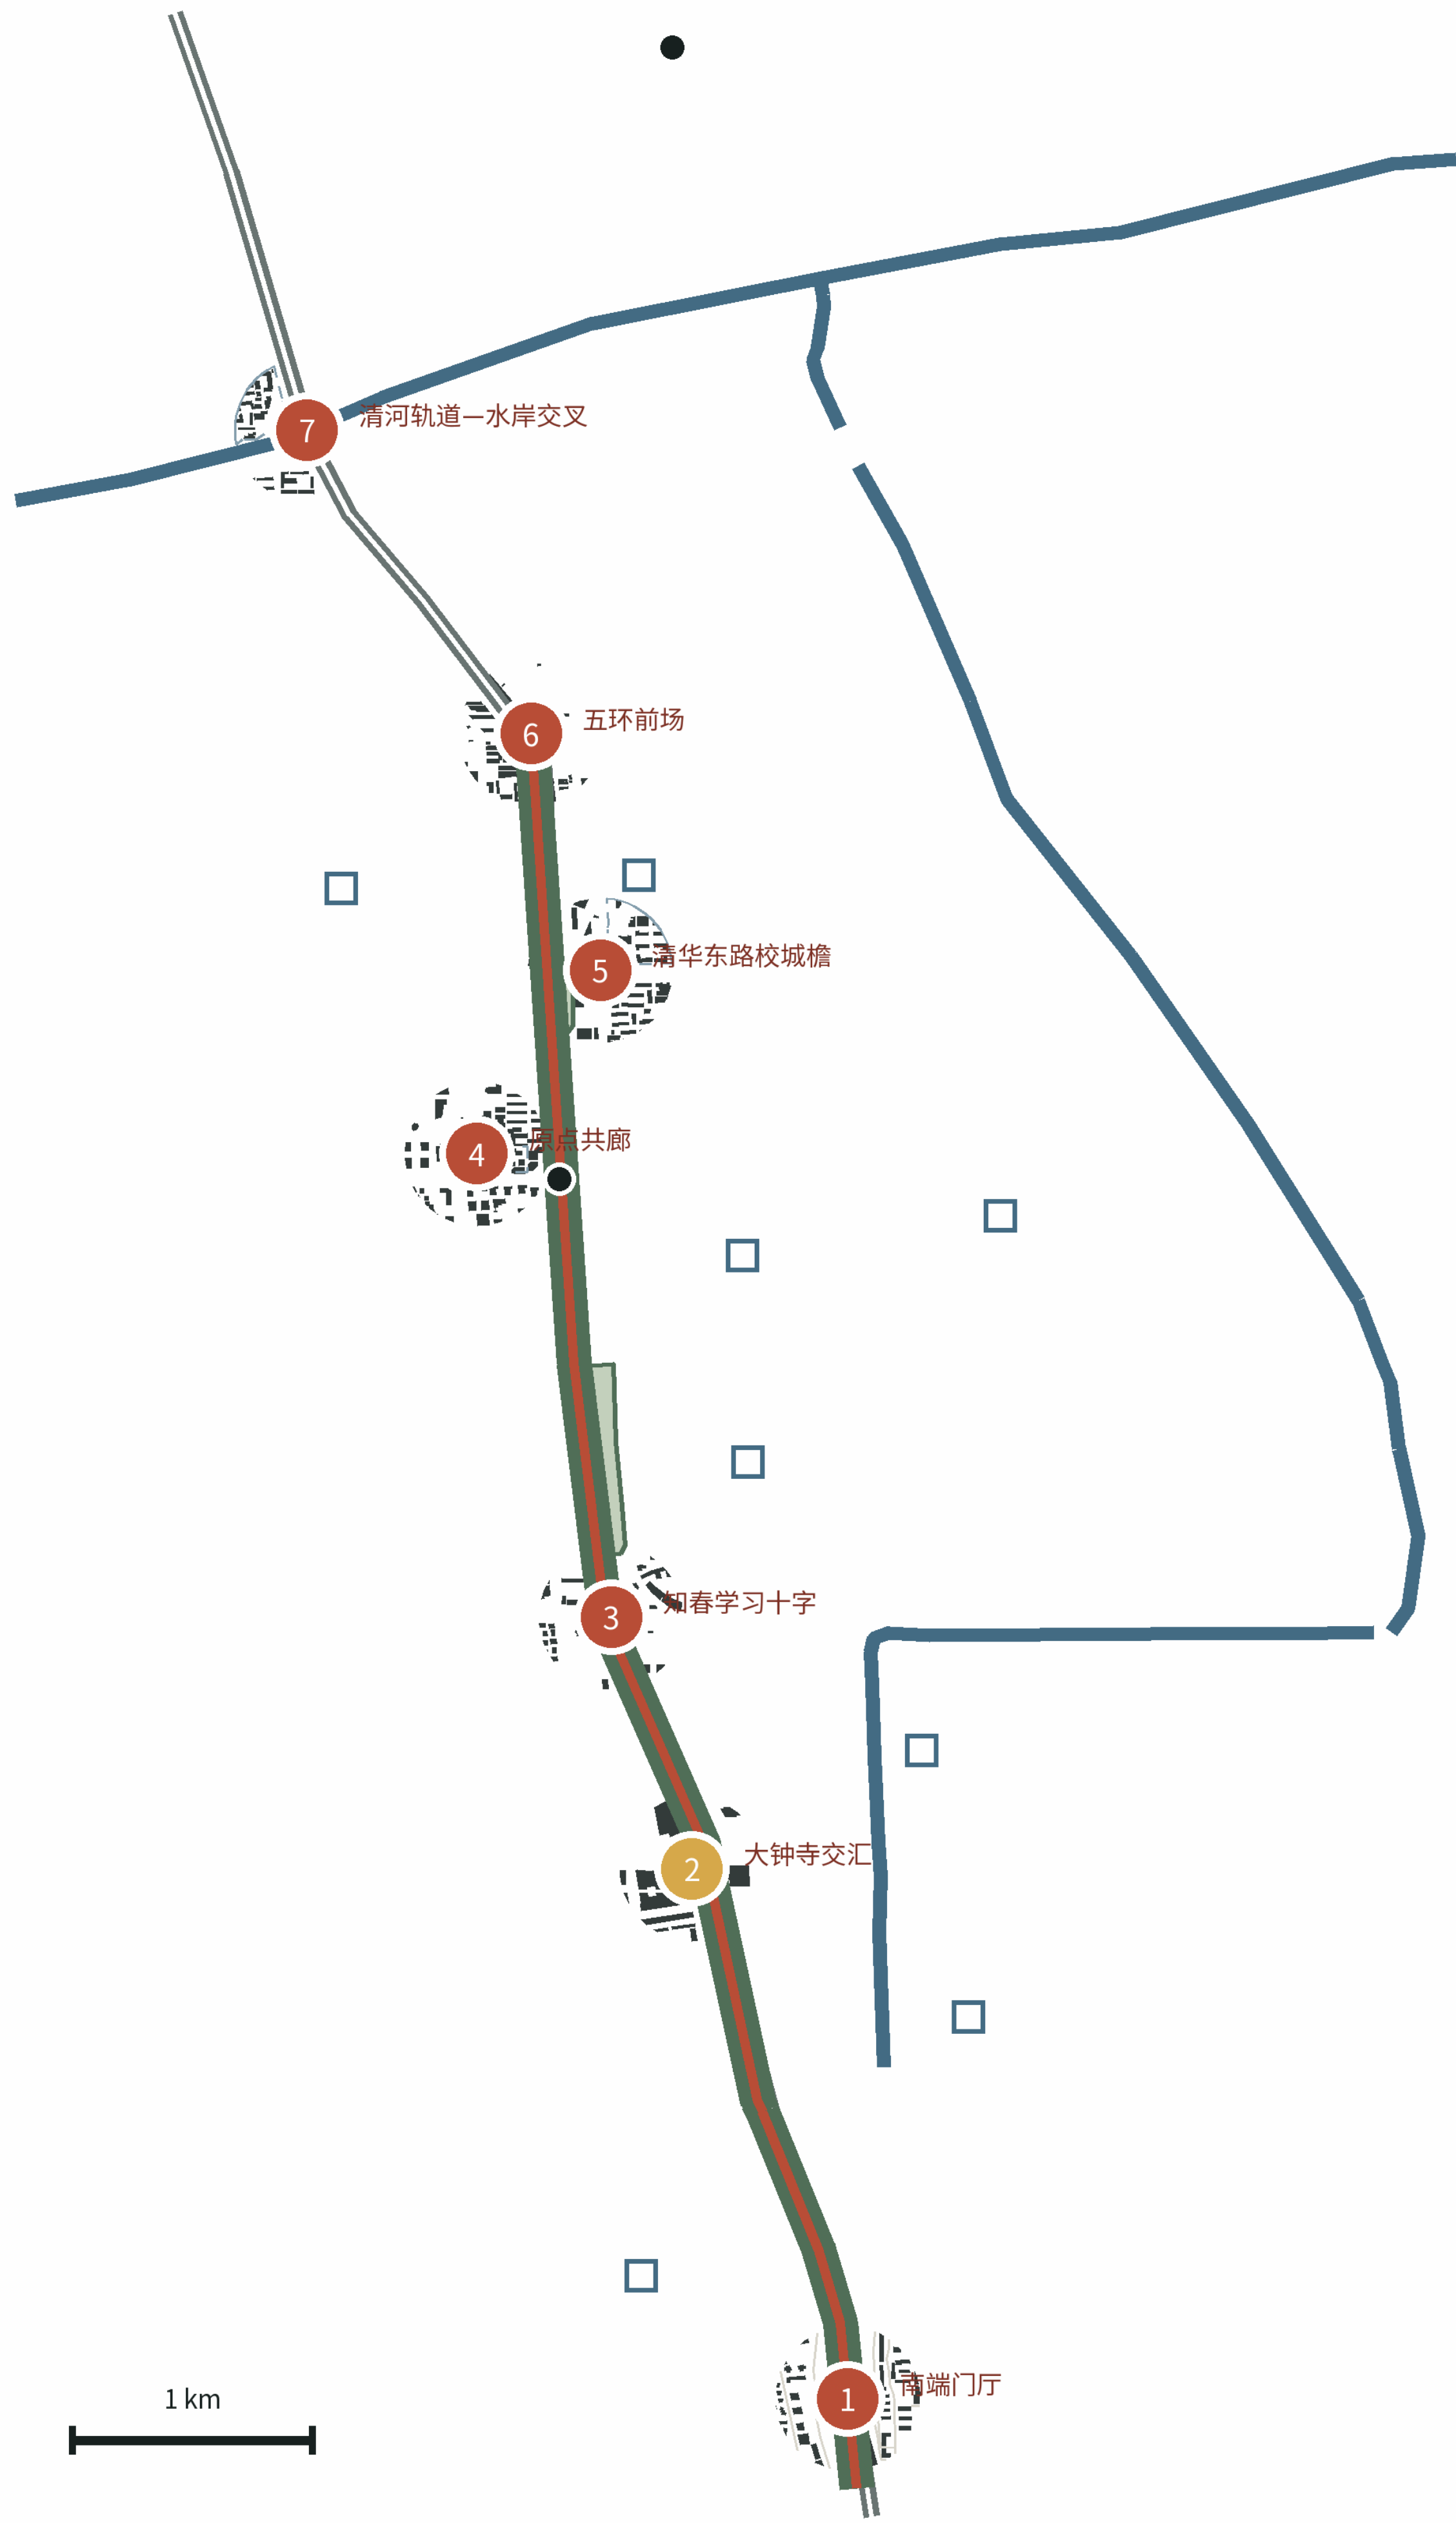

© OpenStreetMap contributors · ODbL 1.0 · 仅供形态与接口研判
不是法定地图、红线、地块、测绘、建筑清单、门禁协议或导航产品

范围与证据状态

43.6 km²

研究范围 / 官方约数

11.4 km²


总体设计 / 官方约数

368.4 ha

三处重点区 / 官方约数

深色=OSM建筑并集 · 细线=道路 · 红=轨道 · 蓝=水/门 · ●=站点 · □=校园中心 · 数字=候选

C1 · 南端门厅

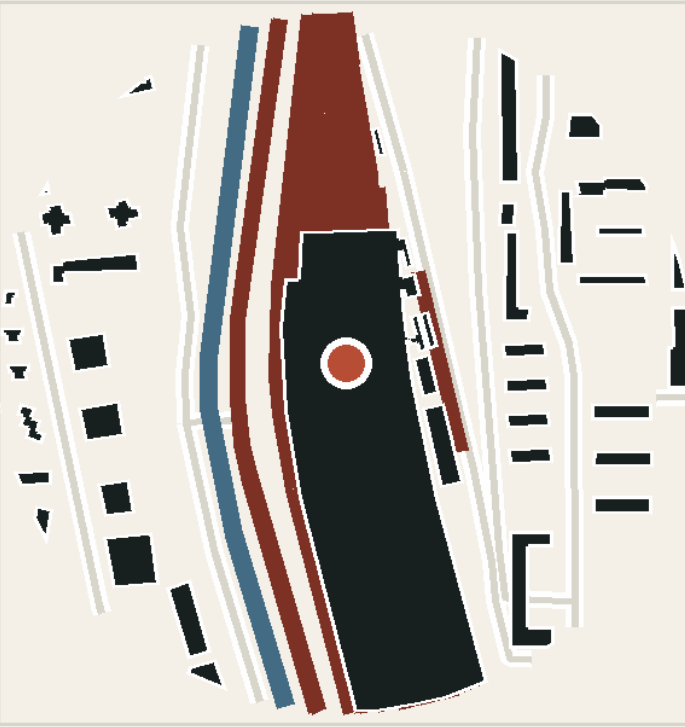

北京北站 + 现役/旧线端头


遗产门槛

站前界面、遗产与人流待实测

专 | 民 → 差异=修改

映射: 44 建筑记录 / 13 道路记录

C2 · 大钟寺交汇

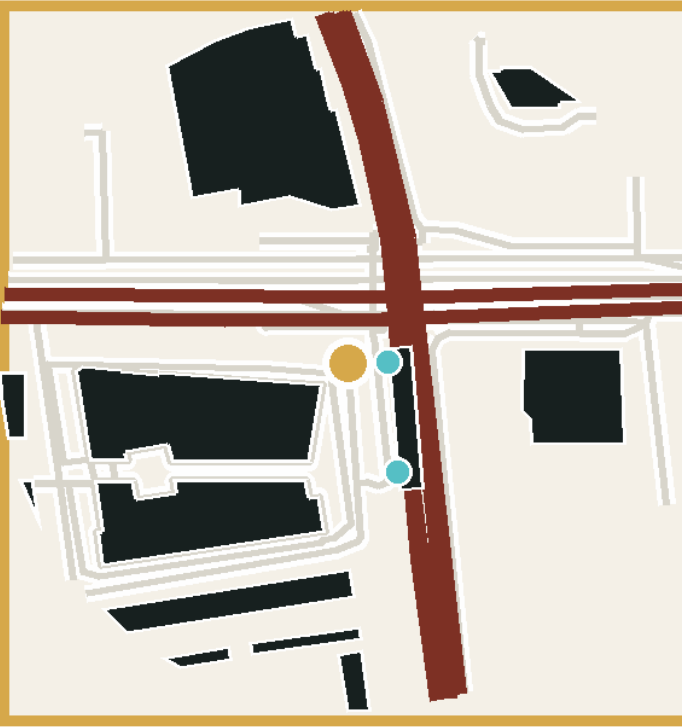

站点 + 轨道 + 四象限断裂


P0 站前共享檐；夜间房有条件

权属、地铁、消防与运营者

专 | 民 → 差异=修改

映射: 12 建筑记录 / 48 道路记录

C3 · 知春学习十字

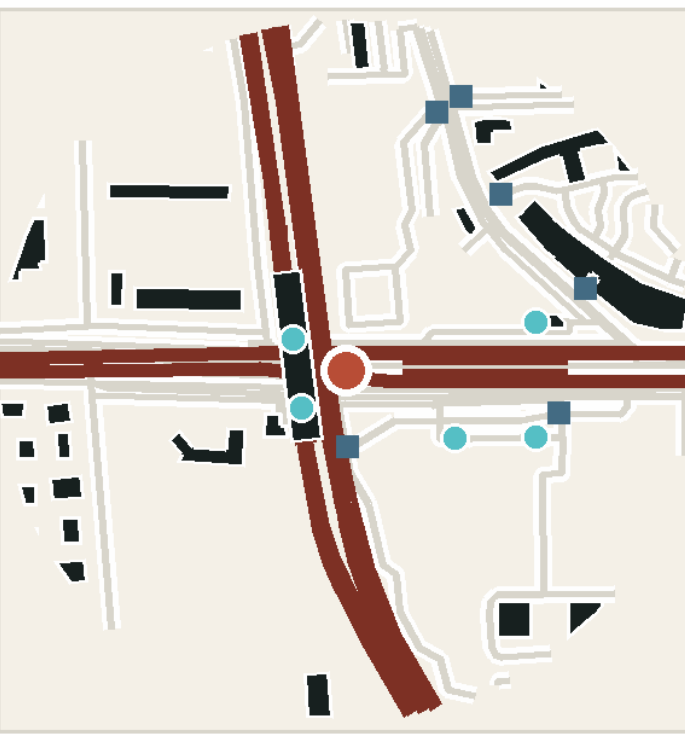

站点 + 轨道 + 学习街区

知春学习十字

七日流量、通行与街角实测

专 | 民 → 差异=修改

映射: 39 建筑记录 / 94 道路记录

C4 · 原点共廊



旧线/公园连接 + 社区日常

原点共廊 / 照护门廊

遗产、社区需求与运营协议

专 | 民 → 差异=修改

映射: 68 建筑记录 / 170 道路记录

C5 · 清华东路校城檐



站点 + 校园中心点；门位未捕获

分时协同开放校门

准确门位、安保与校方协议

专 | 民 → 差异=修改

映射: 51 建筑记录 / 90 道路记录

C6 · 五环前场



现役/旧线近五环；道路接口未核实

骑手驿站 / 服务前场

道路、装卸、消防与用地调查

专 | 民 → 差异=修改

映射: 49 建筑记录 / 128 道路记录

C7 · 清河轨道—水岸交叉



现役轨道 × 清河水岸

海绵穿越

水文、轨道、排水与防洪审批

专 | 民 → 差异=修改

映射: 31 建筑记录 / 48 道路记录

京张证据线



1909 工程影像，不是 C1-C7 现状证明

档案 / 记录

现场 / 实测

P0 / 可逆试用

同一指标 / 专+民

采用 · 修改 · 退出


传承方法，不复制造型 · 尚未开展评分

图源：同生照相馆《京张铁路摄影》，1909 · 原件：中国国家图书馆 · WDL/LOC · LCCN 2021668851

四种功能落地，五层寿命更新

概念用地不是法定分区；公共地面和支撑长期留下，服务、填充与设备按不同周期更换

N ↗ • 仅为版面阅读顺时针旋转 65°

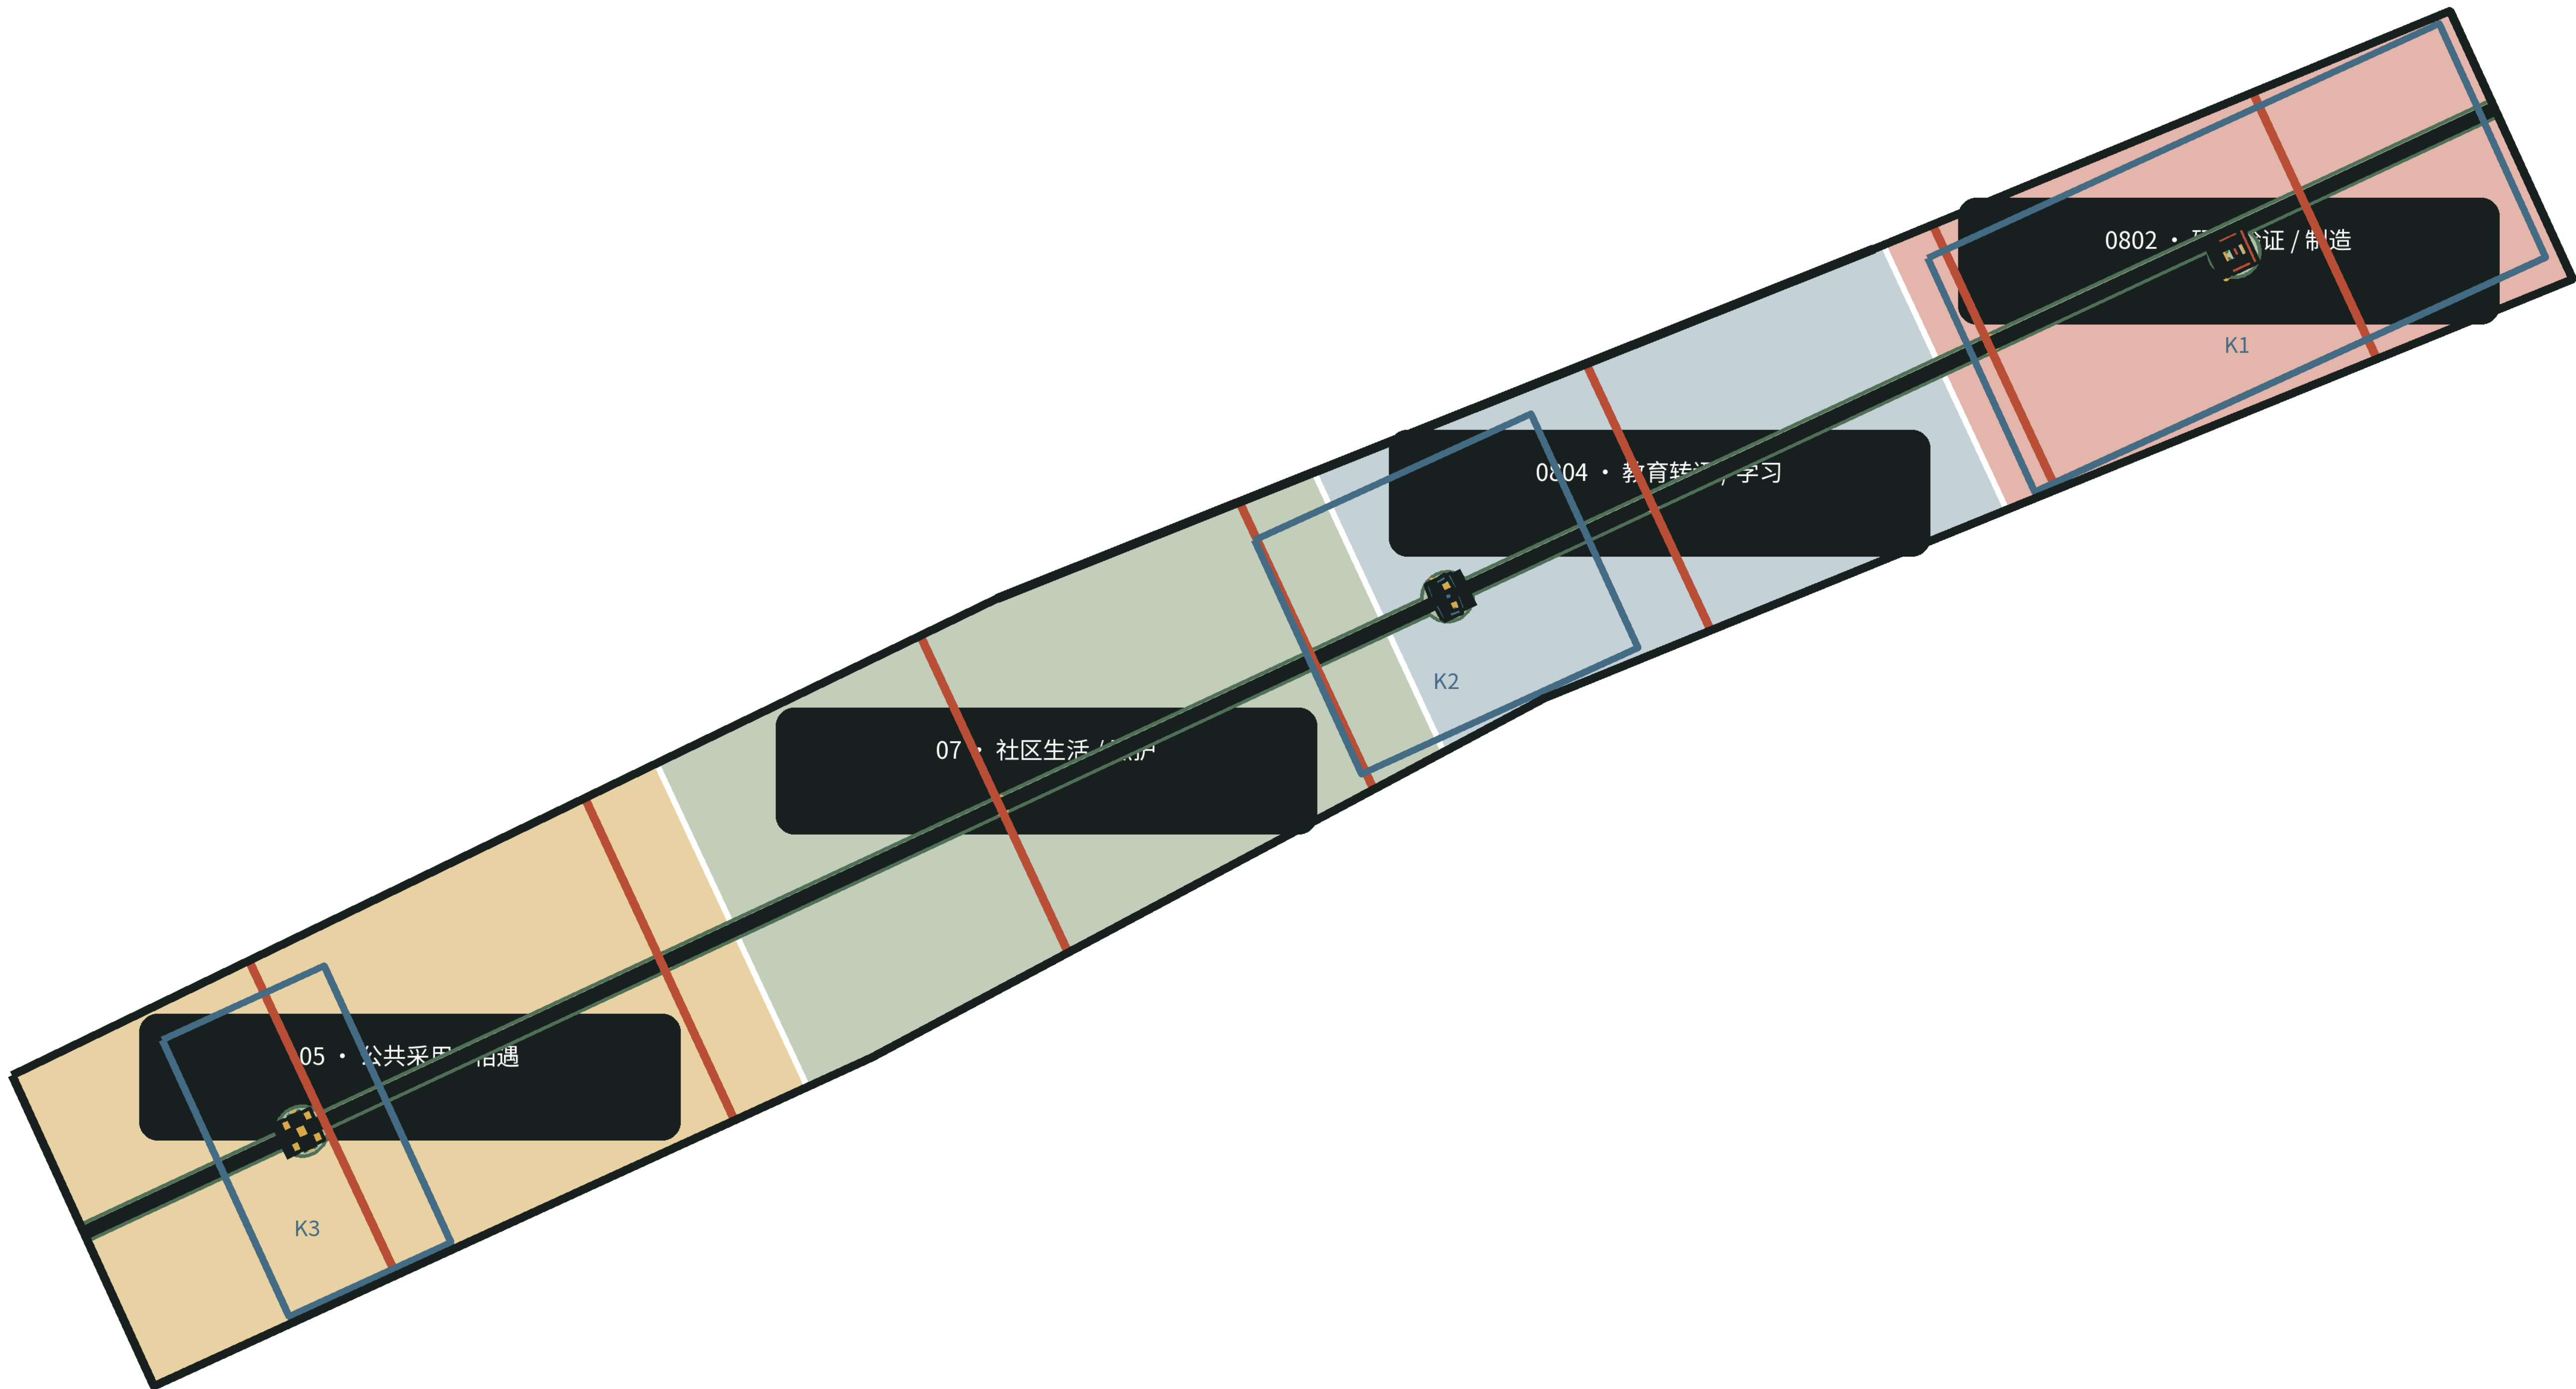

概念用地结构 • 非法定分区 • 正式控规到位后复核并重绑定

填色=四种功能带 • 深色=三种长期框架 • 金线=公共房间 • 红线=七处横向接口

功能 × 使用年限

0802	制造	0804	转译
07	生活	05	相遇

大钟寺 • 鼓励共享层

2F	规划鼓励
G	规划鼓励
B1	规划鼓励
B2	规划鼓励

鼓励 ≠ 已建成、已开放、通行权或 24H

地铁 / 业主 / 消防 / 结构 / 运营协议均为前置条件

五层更新速度

00	共地+气候边缘	100+
01	长期支撑	100
02	可维护机电底盘	25-40
03	可换填充	5-20
04	场景设备	≤5

留架、换芯、记录每次替换：寿命是目标，不是质保。

正式边界与控规触发统一复核、重算与重发。

05 / 07 • 城市留下，模型改变

公共地面、长期支撑与 H 服务底盘留下；A/B 模型、填充与设备可替换

01 100+ / 公共地面

02 100 / 支撑目标


03 H / 连续服务

04 A/B / 可换模型位


十二米共地：人行优先，机器人首先让行

大钟寺官方关系 + 12 米参考断面 · 计划不等于建成

大钟寺 · 官方规划关系（非 GIS）

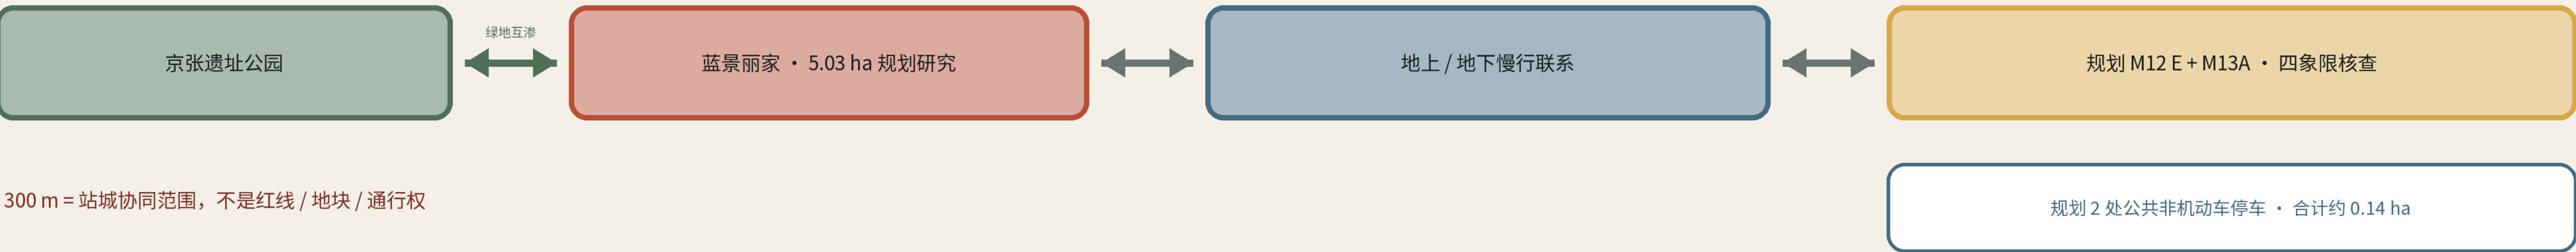

鼓励共享层与慢行联系 ≠ 已开放、已建成或已批准具体路线

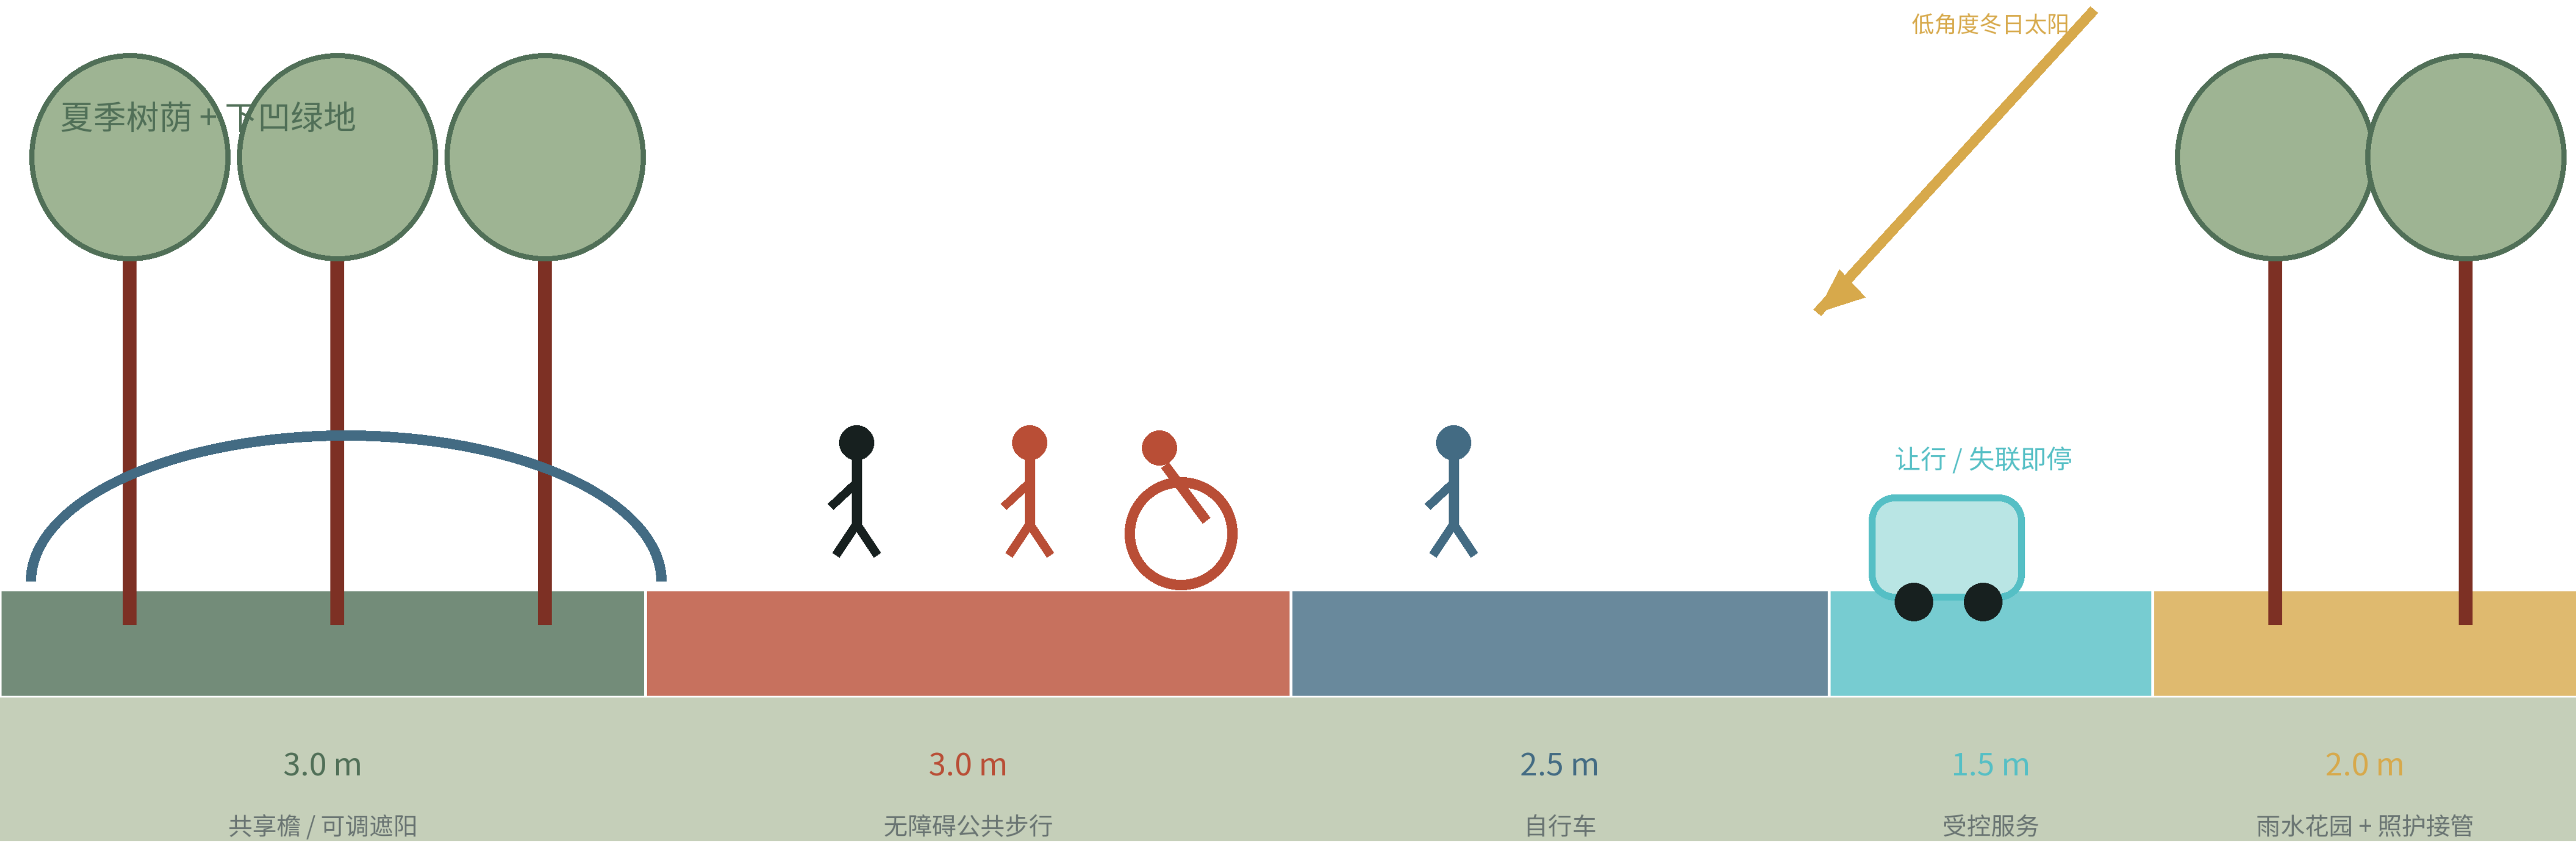

12.0 m 参考断面目标 · 不是法定道路红线

12 张 AI 场景卡 / 4 张示例

空间 · 拟议责任类型 · 人工兜底

AI01

无障碍换乘校核

七座城市房间 · 无障碍专员

故障→纸图+陪同

验证

AI02

低速配送验证

验证院 · 安全主管

故障→手推车+急停

验证

AI05

气候庇护运行提示

共享檐 · 场地管家

故障→人工巡检

验证

AI12

多语种人工帮助台

人工帮助点 · 城市管家

故障→人工翻译

验证

S01-S15 日常生活情景推演


7 类人物 · 24H × 四季

七处城市房间均需七天现场基线

完整卡片 ≠ 本地需求或绩效已经证实

机器人：低速、让行、失联即停；人工服务不中断


众智园 · 验证院

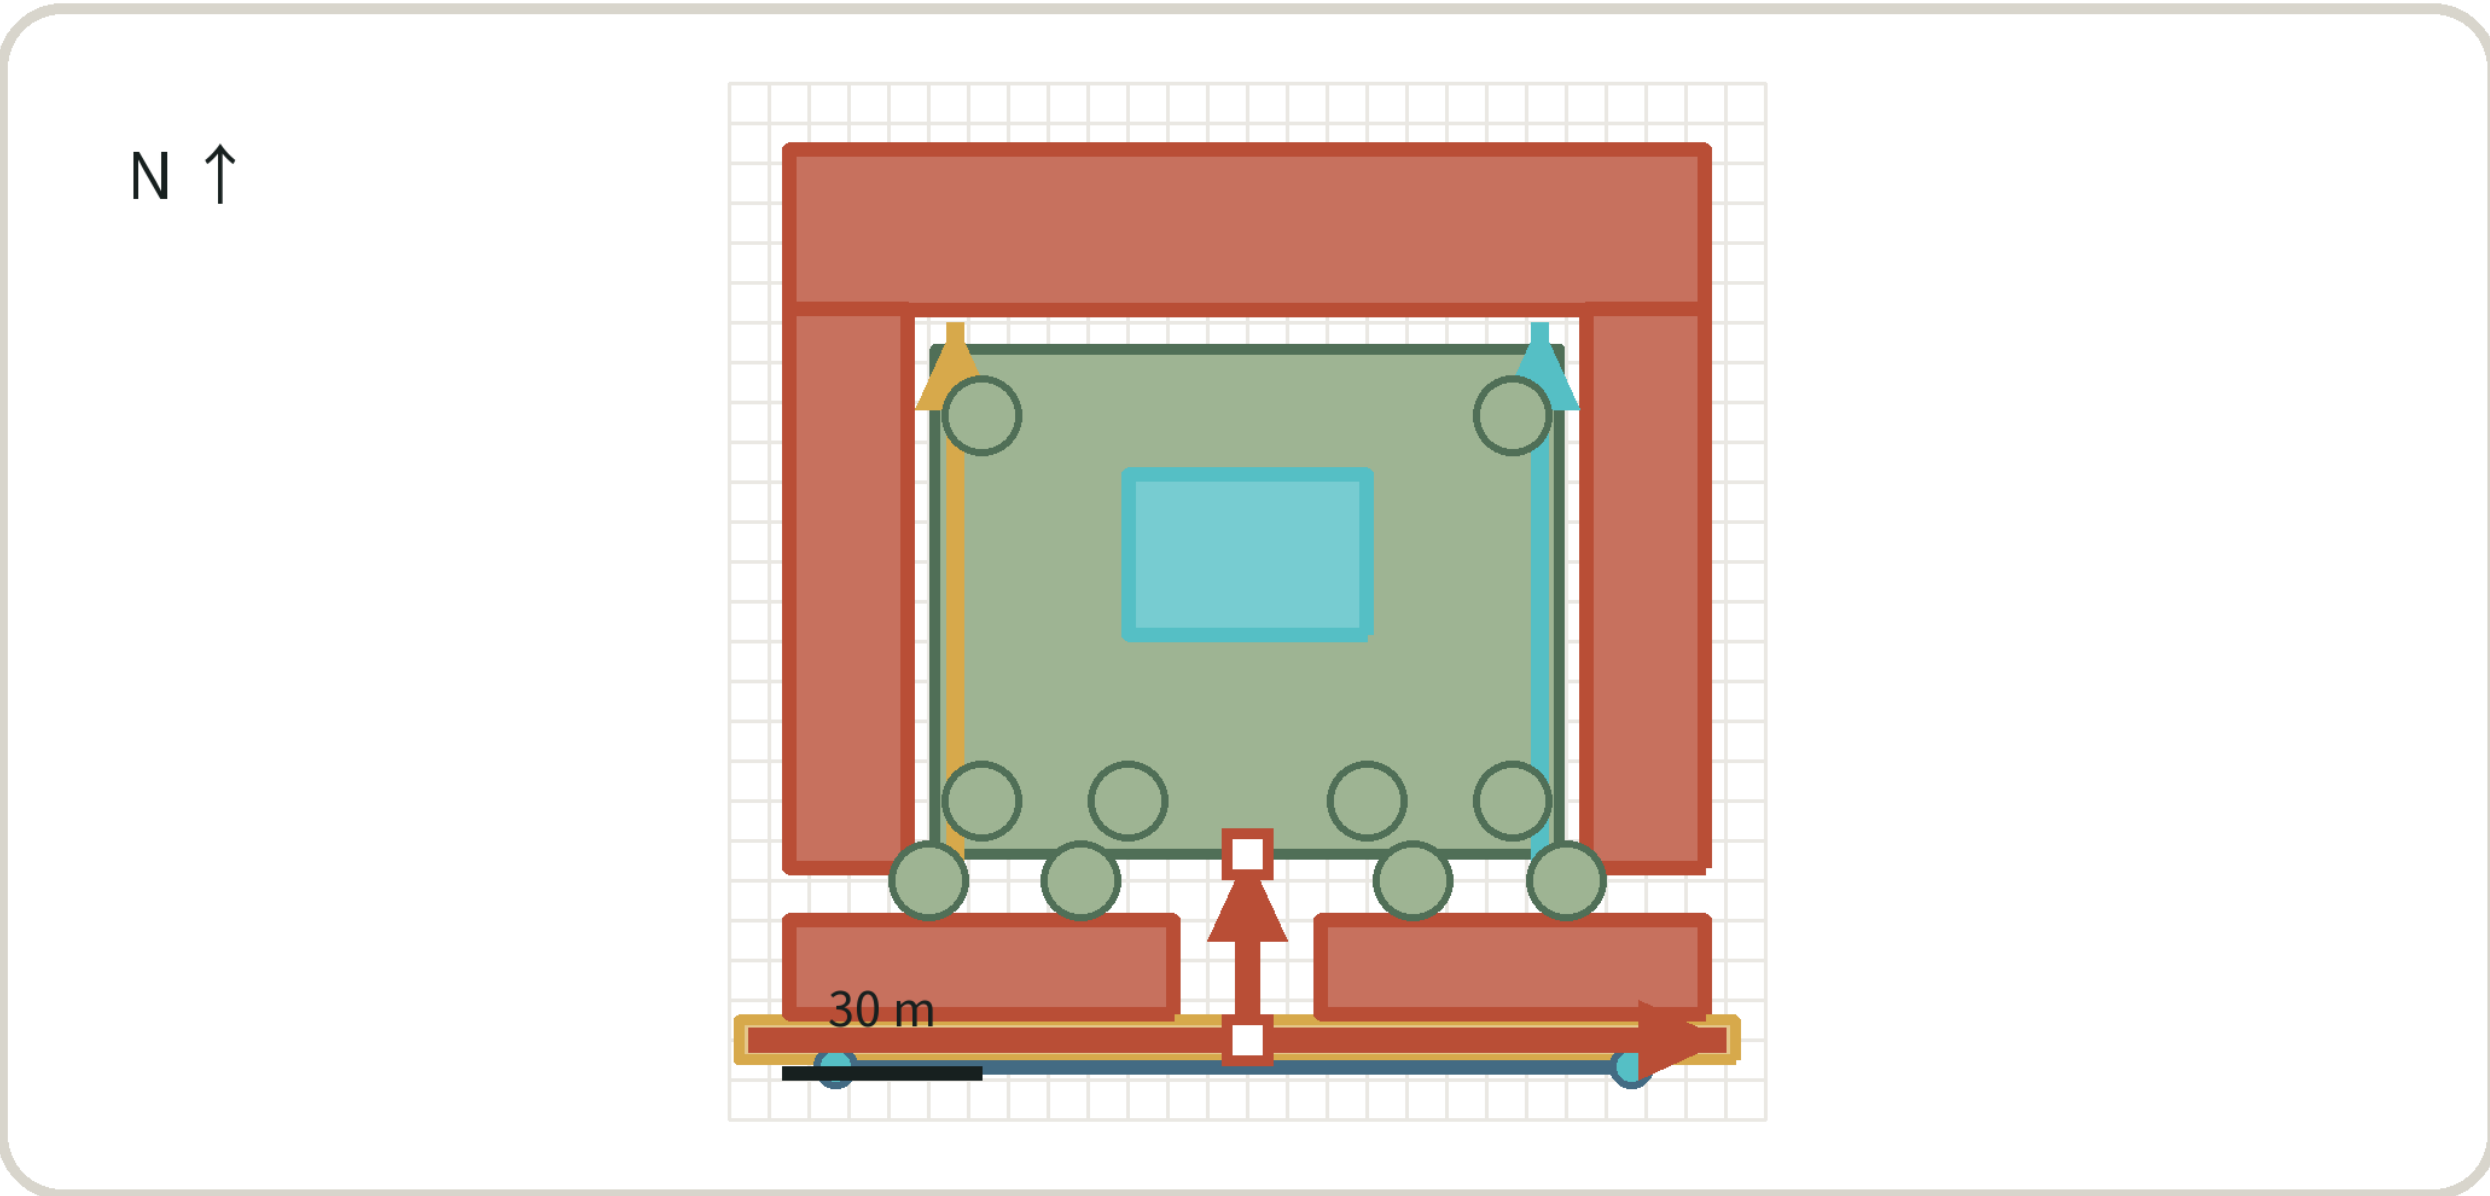

空间拓扑	双跨同测：A/B 同夹具；H 中带
契约	AI02 · AI05 · AI09 · AI11
见证换模	本地 shadow：全拓扑 29/36 一致
停止规则	关键回归、数据/工具扩张或任一钥匙拒绝

候选落位 · 正式 polygon/现状/权属到位后重绑定


AI 原点 · 原点廊院

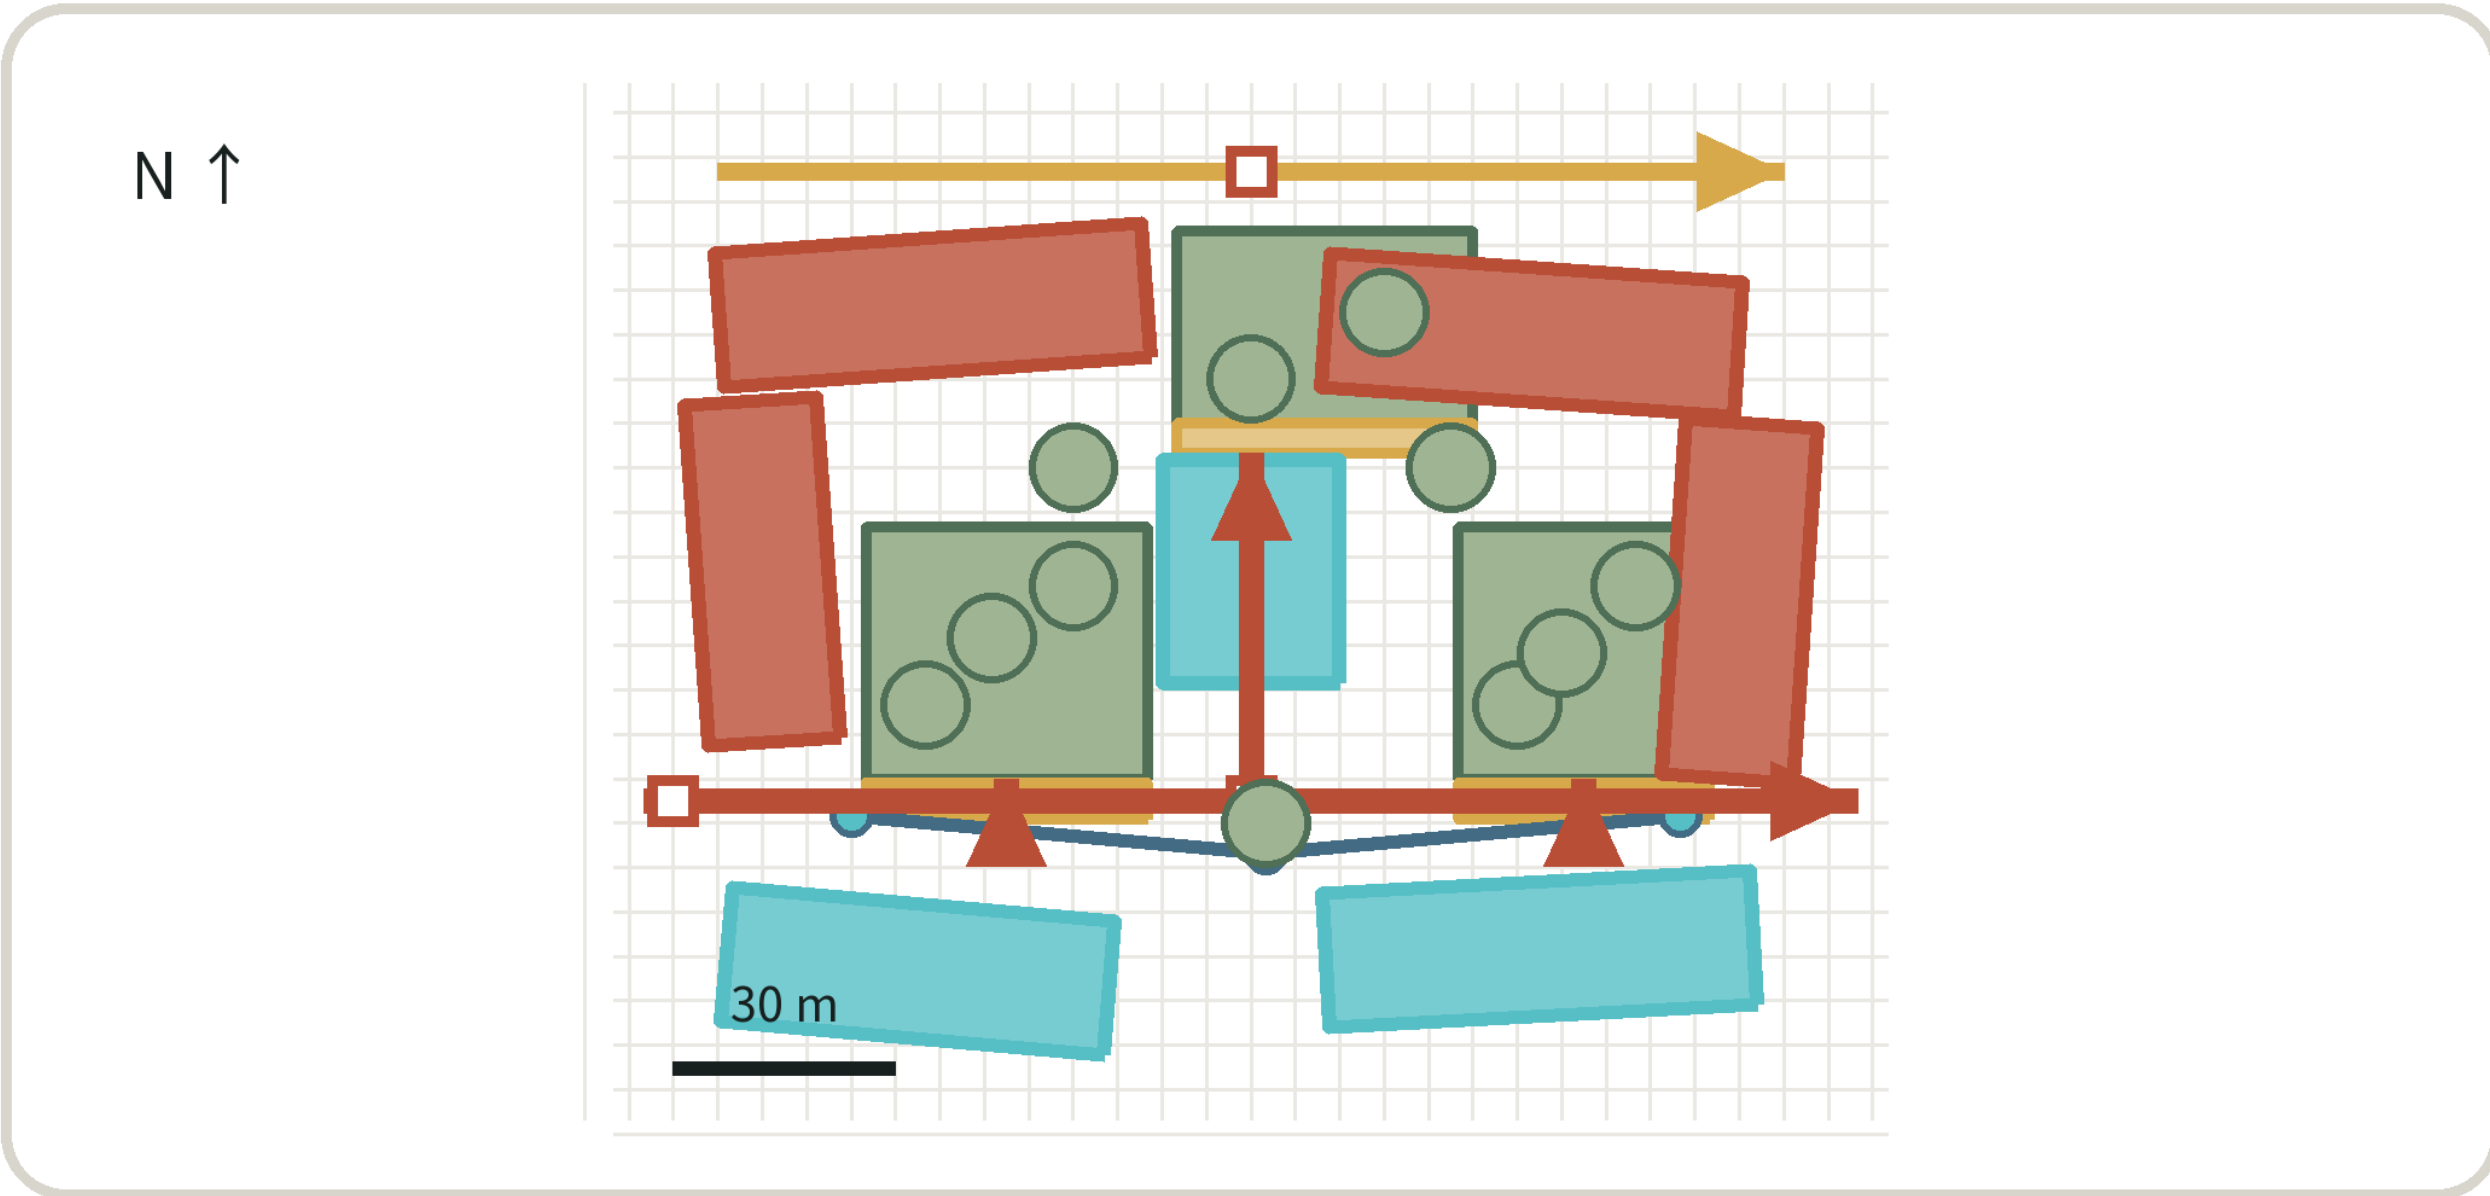

空间拓扑	差分回廊：A/B 并读；H 桌完成同任务
契约	AI01 · AI04 · AI06 · AI08
见证换模	4 项非 hard-stop 分歧集中于原点标签
停止规则	来源、权限或专业分歧未解决即转 H

候选落位 · 正式 polygon/现状/权属到位后重绑定

大钟寺 · 城市交汇厅

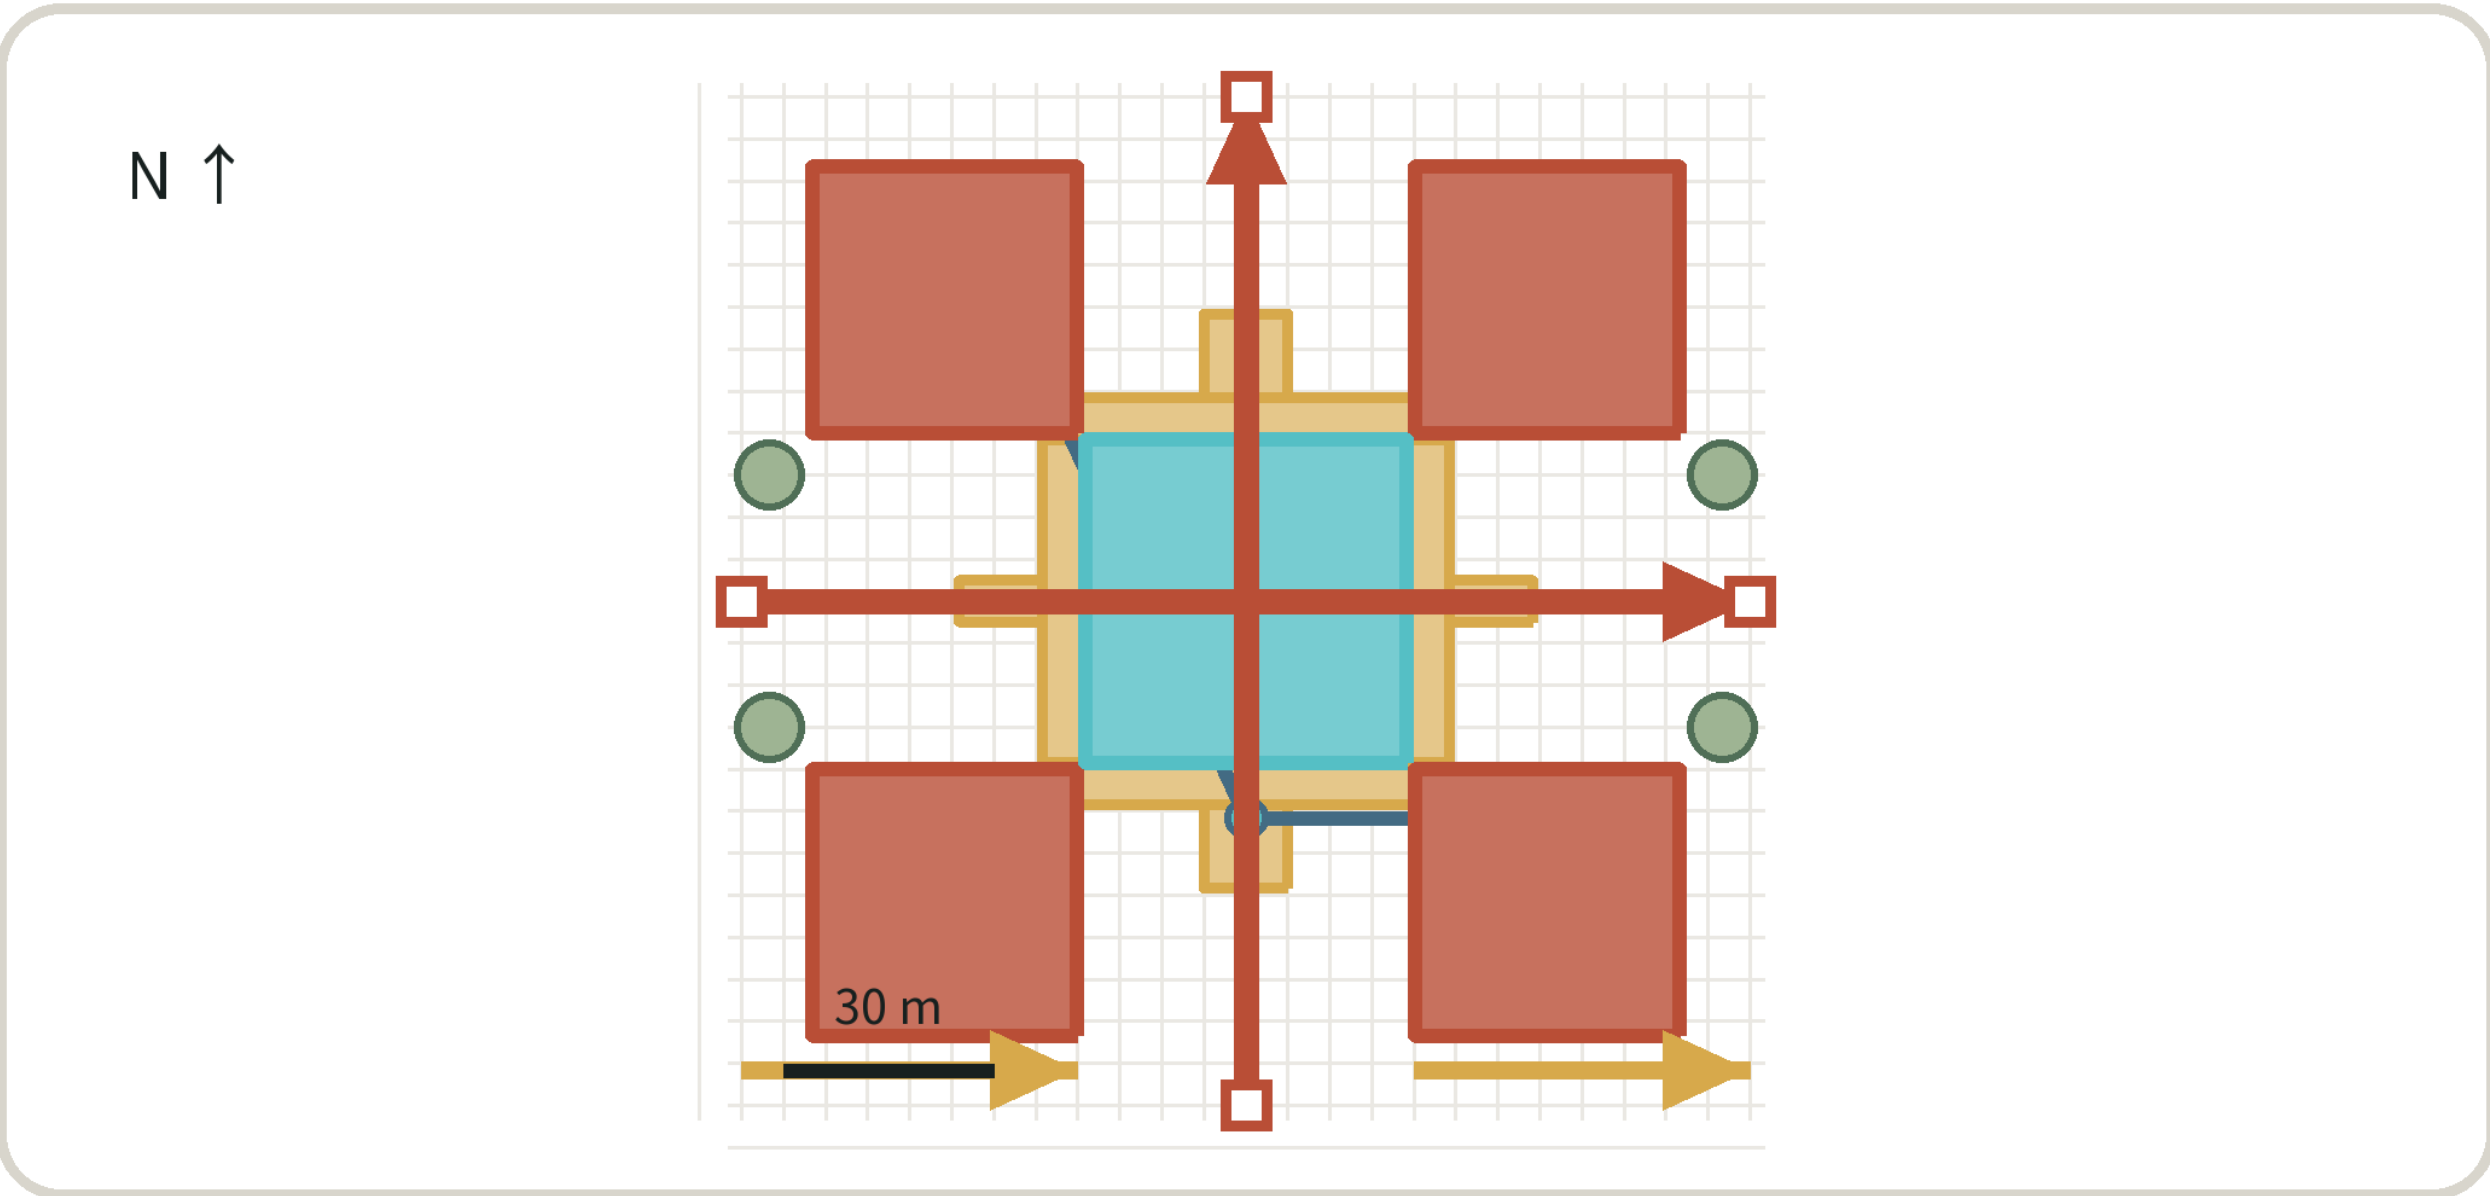

空间拓扑	单队列三出口：A / B / H 不得挑人
契约	AI03 · AI07 · AI10 · AI12
见证换模	12/12 hard-stop 全部由确定性 H 拦截
停止规则	困难用户负担上升或严重事件即全流回 A/H

候选落位 · 正式 polygon/现状/权属到位后重绑定

SAME TASK / FAIR COMPARISON

A/B 使用同一任务、夹具、数据边界与人群入口

单队列和 H 同任务路径防止 B 只挑容易用户；比较的是差值，不是漂亮的单项得分。

HUMAN AUTHORITY / TWO KEYS

服务责任人 + 权利/安全责任人；任何一钥匙可 HOLD

B 不能自我晋升。任何公众可直接选 H；高风险分歧只形成给 H 的建议。

SPATIAL CONSEQUENCE / ORIGIN H TABLE

29/36 一致；7 项分歧；4 项集中在原点；H 桌留下

原点把分歧变成公众可读的差分与永久人工复核空间；设计要求 B 变化时 H 同任务路线不断。

29/36 AGREE	7 DELTA	4 @ ORIGIN	H TABLE
-------------	---------	------------	---------

三种空间，一条不断的 H 路

概念体验图；空间权威仍为平面、剖面与 GeoJSON。图中人物与设备为概念示意，不是现场记录。



城市交汇厅 · 19:00

单队列三出口：配送机器人在路缘让行并可被物理停止；数字停机时由固定标识与现场人员接管。
换模发生在同一入口之后，公众不必知道今天用的是哪一个模型。



验证院 · 冬至正午

双跨同侧的公共一侧：轮椅使用者与同行者走在连续无高差的路线上。



原点廊院 · 夏日雨后

差分回廊的公共一侧：常设人工 H 桌不可删减，不用手机也能完成同一任务。