



PLACEMENT SCREEN / 1:500 AT FULL-SIZE A0

OSM MORPHOLOGY—NOT PARCEL, REDLINE, VACANCY OR BUILDABILITY EVIDENCE

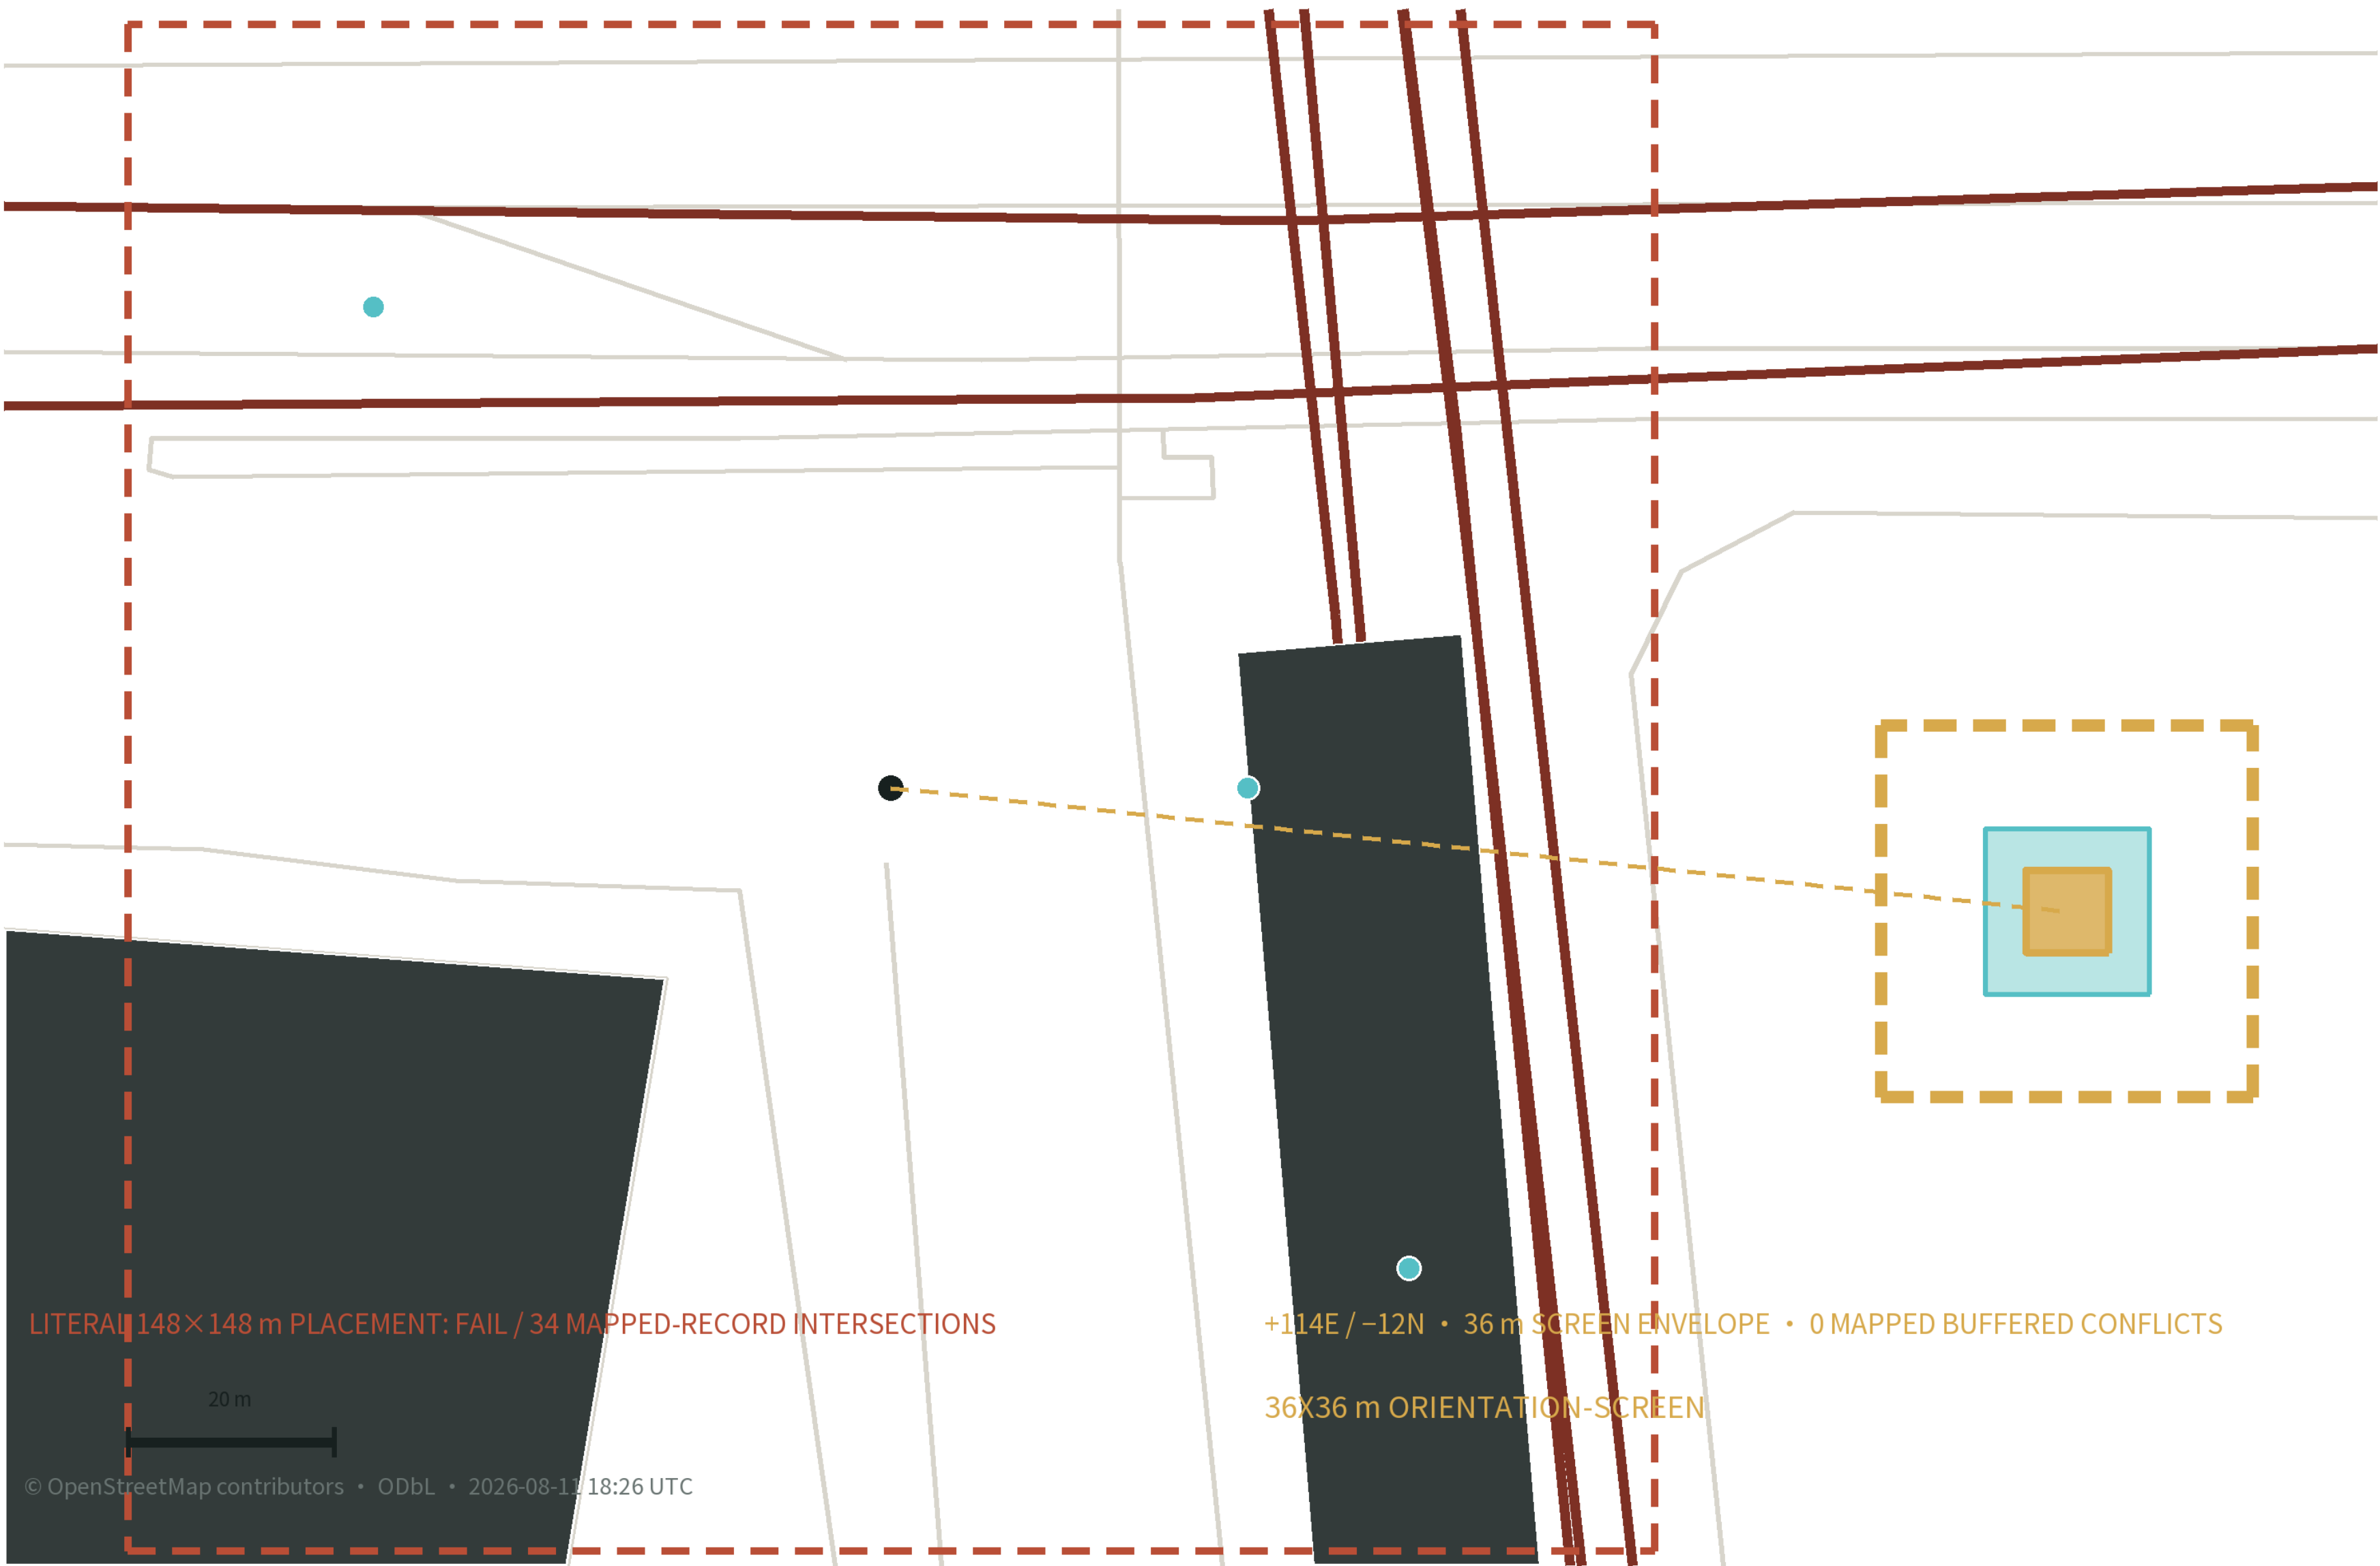


P0 PLAN / 1:100 AT FULL-SIZE A0

ONE 8 m SUPPORT BAY WITHIN 16 m REVERSIBLE GROUND

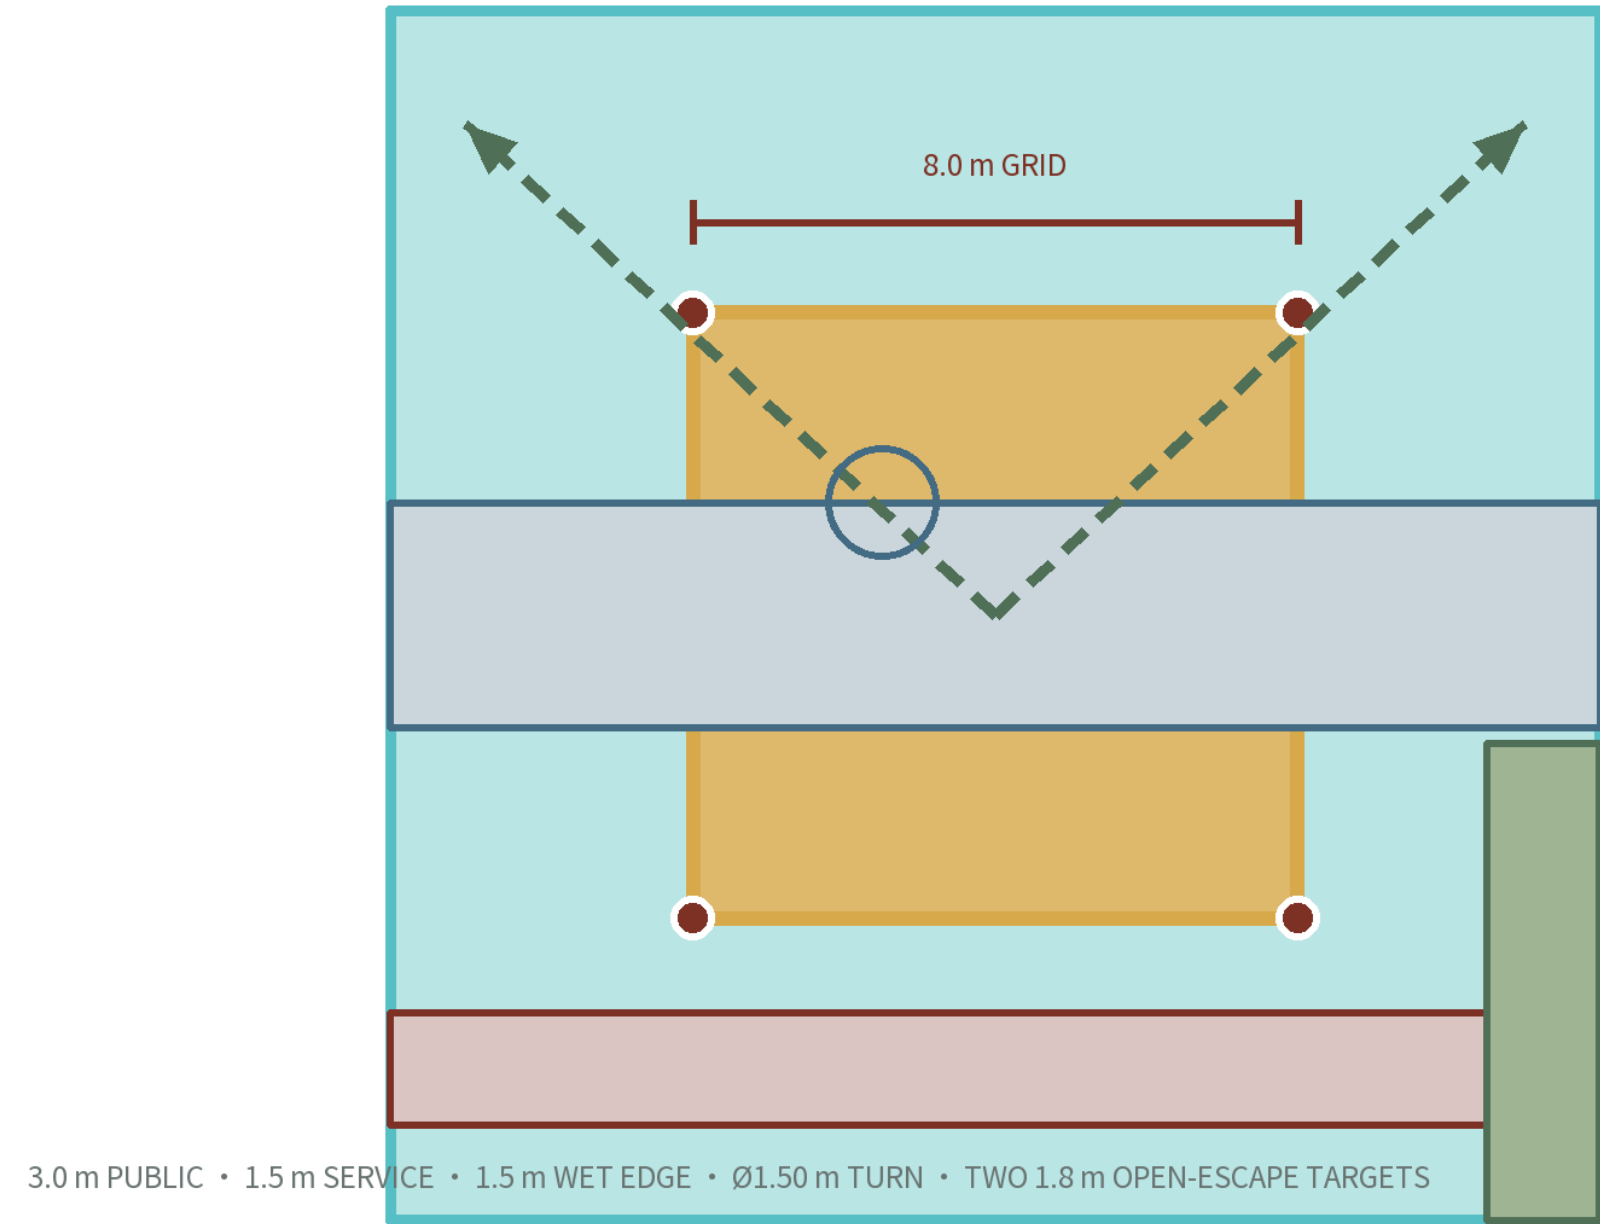

INHABITED SECTION / 1:200 AT FULL-SIZE A0


OPEN CANOPY: NO COOKING / TRACTION-BATTERY CHARGING; FIRE + OCCUPANT LOAD TBC

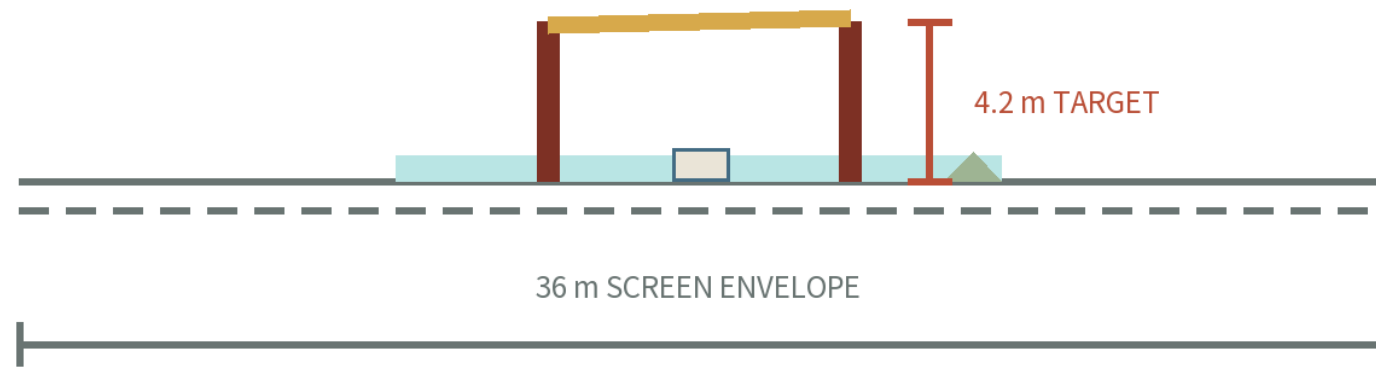

EAVE-WATER-SERVICE INTERFACE / 1:20 AT FULL-SIZE A0

CLEAR GEOMETRY TO SCALE; MEMBER + PRODUCT THICKNESSES TBC STRUCTURE/FIRE/MEP


DEMOUNTABLE ROOF CASSETTE / 2% FALL HYPOTHESIS

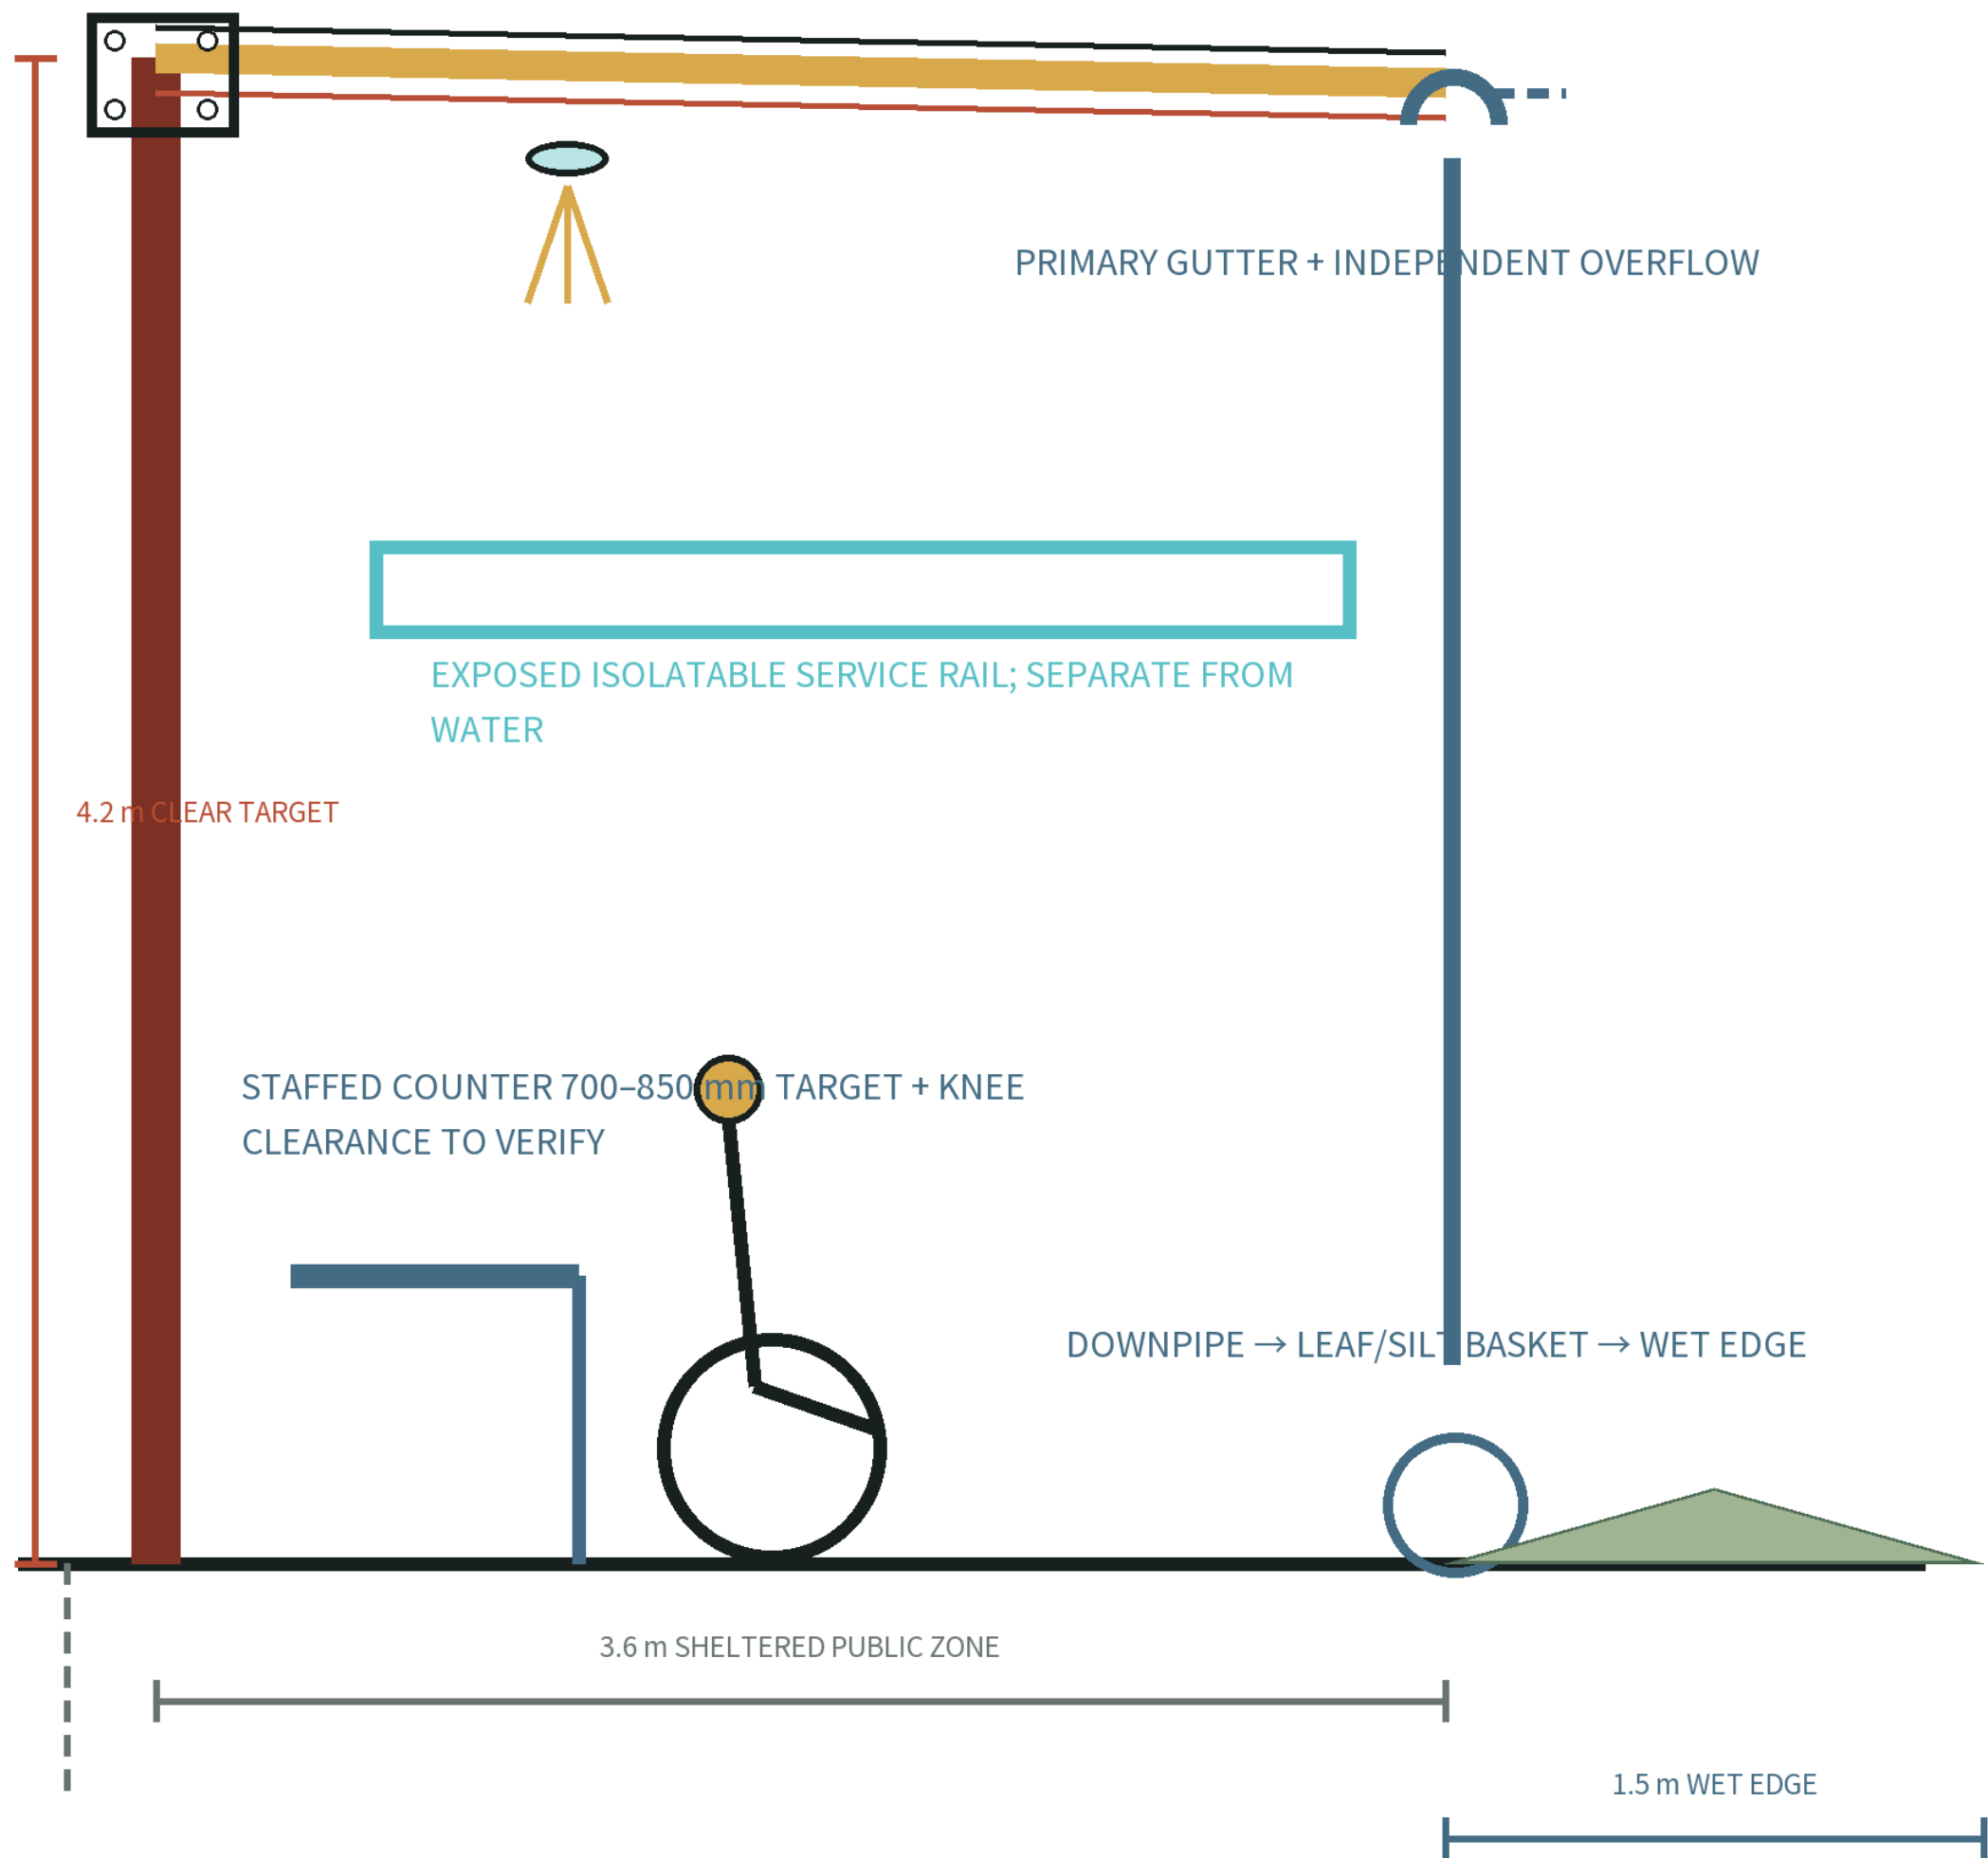

64 m² ROOF × 10 mm RAIN = 0.64 m³; OUTLET/STORAGE/INFILTRATION TBC TOPO, SOIL + MUNICIPAL DRAINAGE.

CONTEXT-BOUND AXON FROM THE SAME GEOMETRY

OSM FOOTPRINTS FLAT • NO HEIGHT, PARCEL OR TITLE EVIDENCE

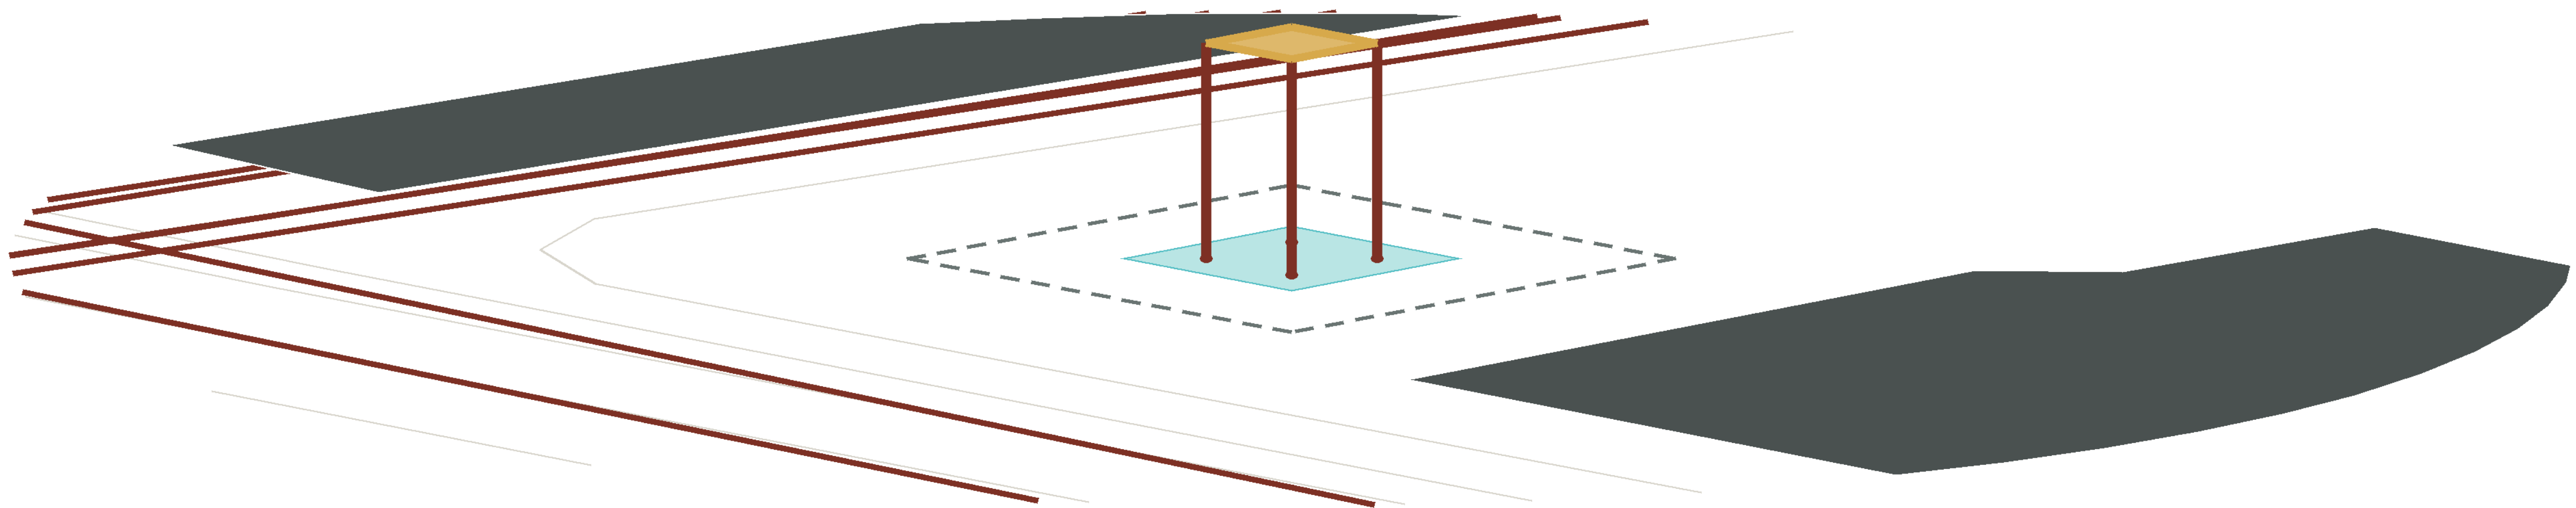

PROPOSED 8×8 m DEMOUNTABLE FIRST BAY

36×36 m IS AN ORIENTATION-SCREEN ENVELOPE ONLY

PERFORMANCE SCHEDULE / PARTICIPANT REFERENCE SPEC

01	BOLTED GALVANISED FRAME • SECTION/GRADE/FIRE TBC	¥1.9–3.8M
		PARTICIPANT ROM / NOT A TENDER PRICE
02	DEMOUNTABLE METAL CASSETTE • WIND/SNOW/CONDENSATION TBC	06:00–24:00 • 5-FTE ROSTER
03	DRY-LAID REPLACEABLE PAVING • SLIP/FROST/PERMEABILITY TBC	OPEX ASSUMPTION ¥1.2–2.2M/Y
04	VISIBLE DRAINAGE + WINTER DRAIN-DOWN; DISCHARGE OUTSIDE CLEAR ROUTE	OPEX ASSUMPTION 1.2–2.2M/Y 06:30 RIDER/CLEANER WATER + REST
05	SURFACE ISOLATABLE SERVICE RAIL • LOAD/METERING/FIRE TBC	12:30 FOOD HANDOFF; NO COOKING 19:00 REPAIR/LEARNING/STAFFED HELP

NO TITLE/REDLINE, NAMED OPERATOR, 12-MONTH OPEX RESERVE, ACCESS AGREEMENT, METRO/UTILITY, FIRE/STRUCTURE/MEP REVIEW + PERMIT: NO BUILD, NO OPEN.

01 / 07 • FROM FALSE PLACEMENT TO FIRST BAY

REAL FIGURE-GROUND REJECTS THE DIRECT 148-METRE PLACEMENT; P0 CONTRACTS TO AN 8×8-METRE DEMOUNTABLE BAY AND 16×16-METRE REVERSIBLE GROUND, WITH NO BUILD OR OPENING BEFORE TWELVE EXTERNAL GATES CLEAR

01 8×8 m / demountable bay

02 11/11 / delivery modules

03 12/12 / external gates HOLD

04 0 / site release


PAIRED BAYS • DIFFERENCE CLOISTER • ONE QUEUE

ONE MECHANISM WITHOUT CLONED FORM: EACH SITE MAKES DIFFERENCE VISIBLE FROM THE HUMAN ROUTE H

03

01 • PROOF YARD

PAIRED A/B BAYS + H STRIP

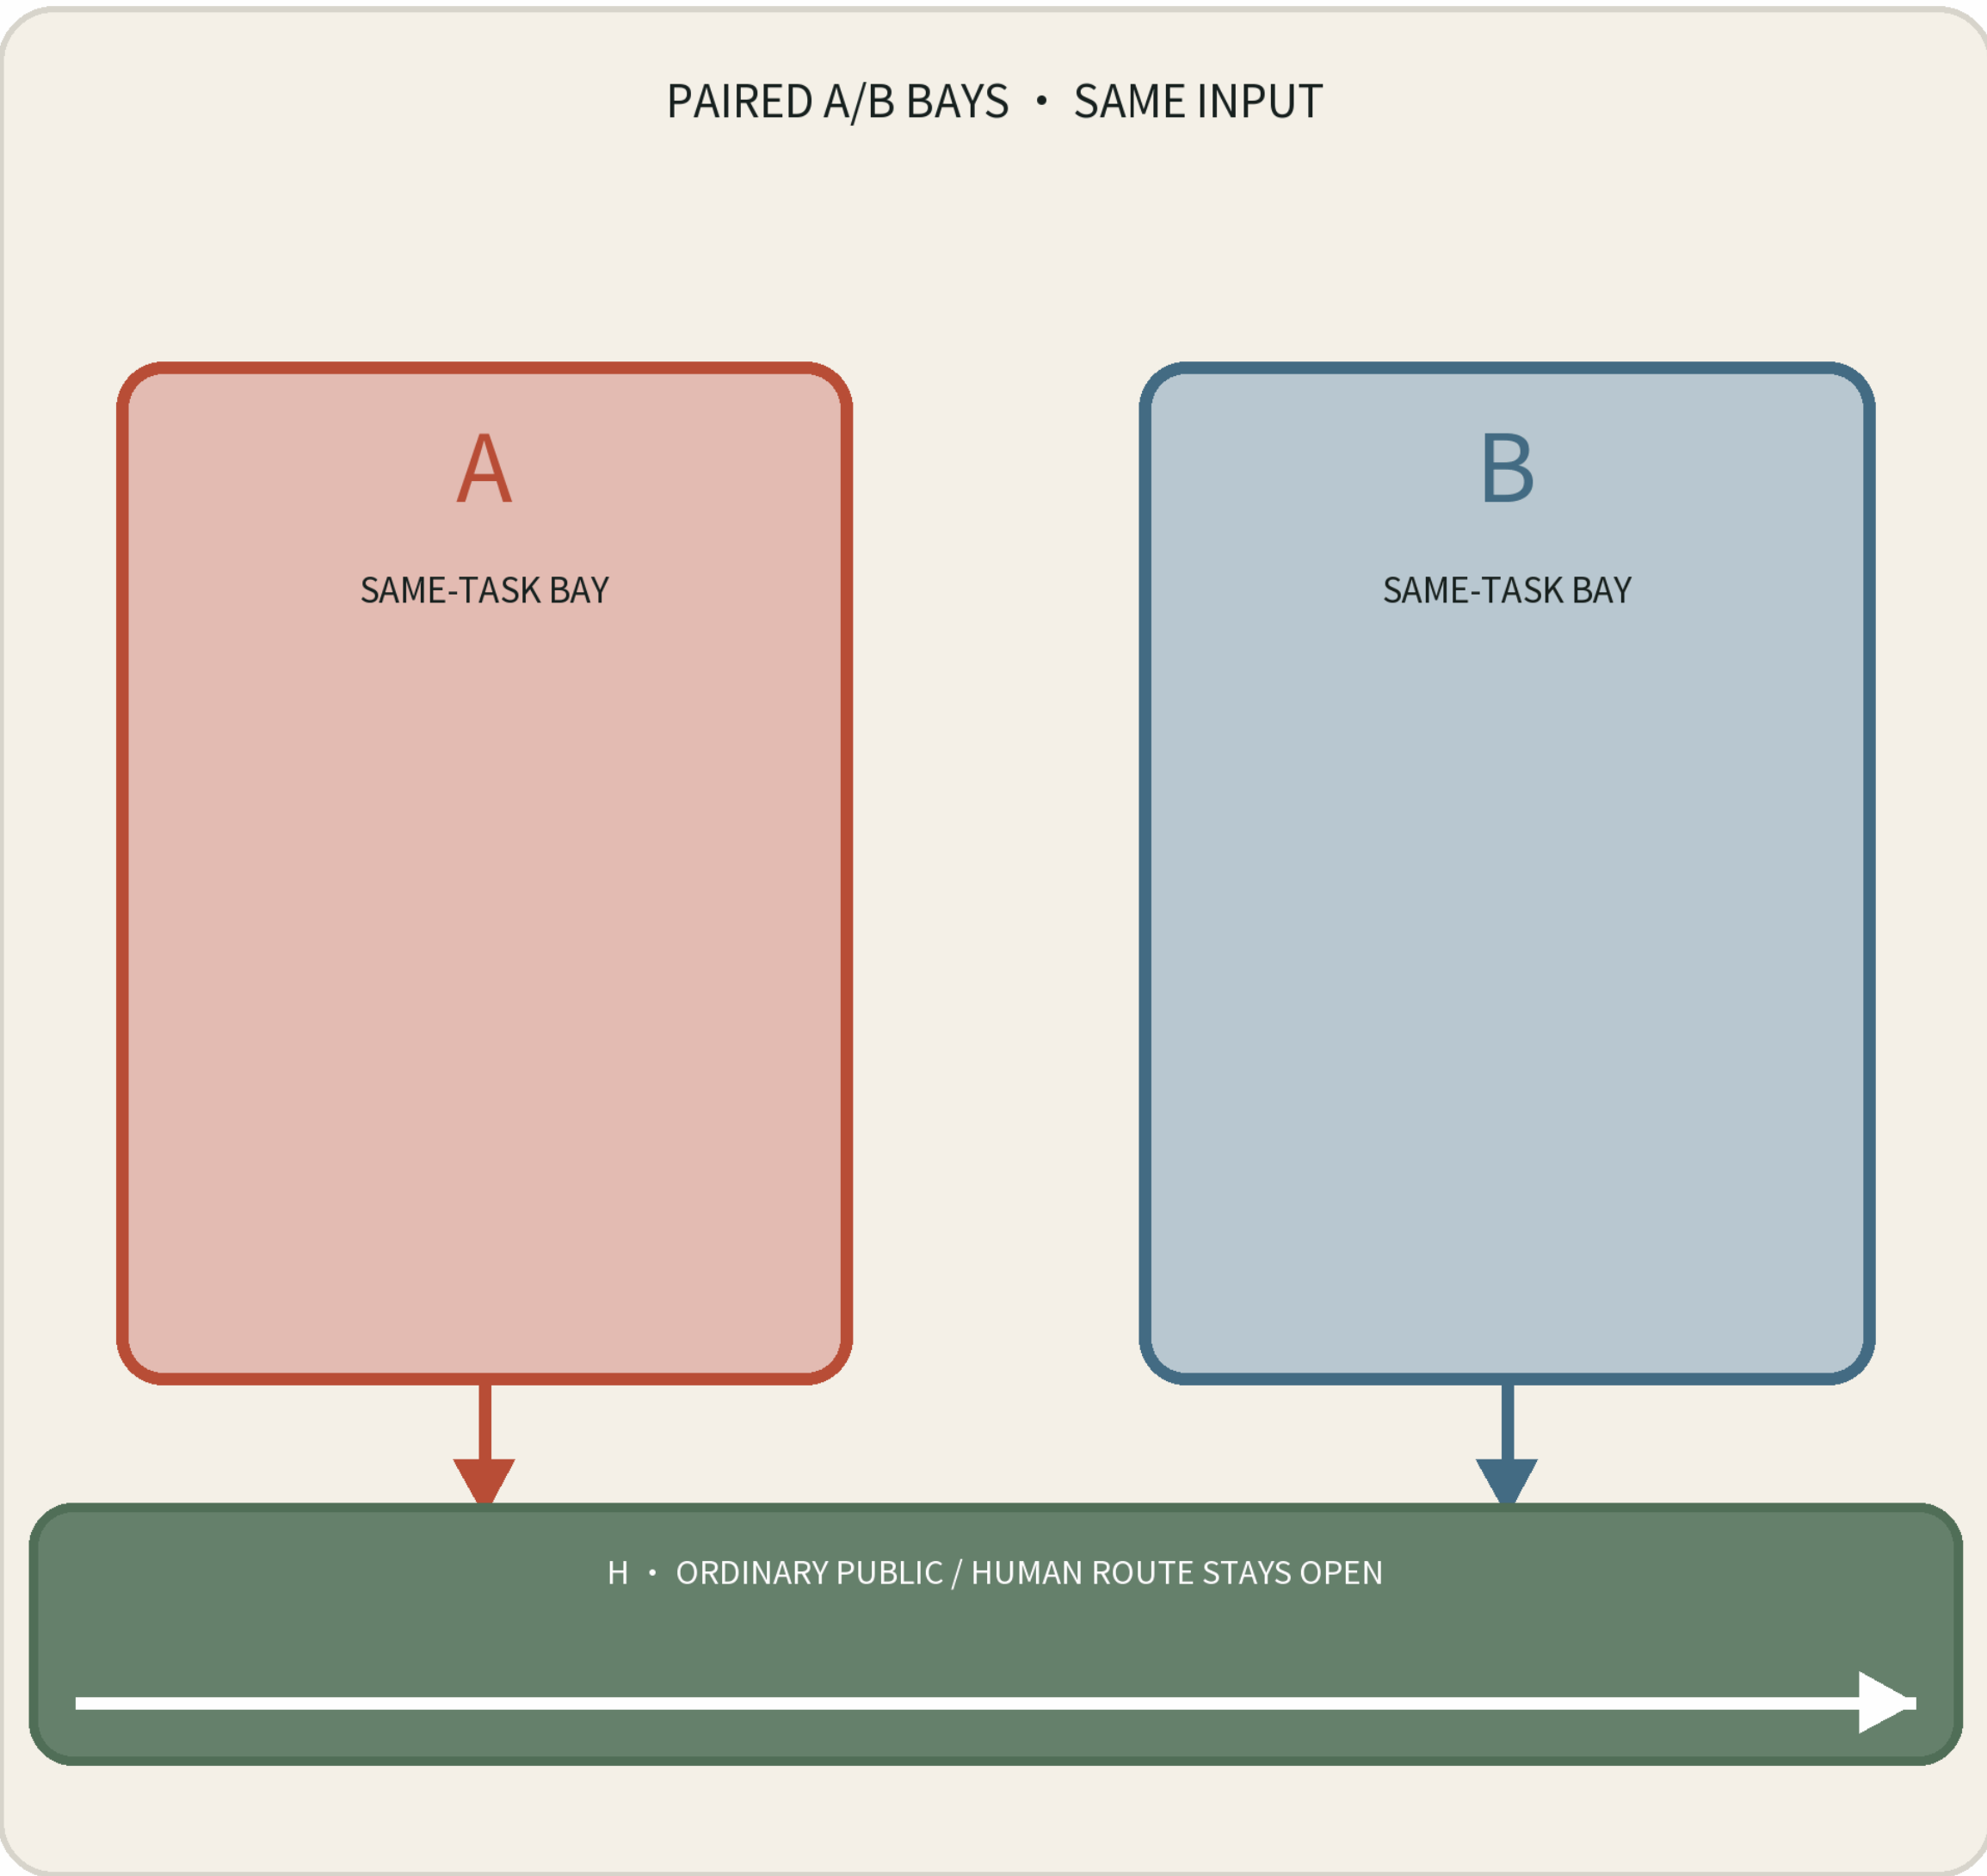


CANDIDATE PLACEMENT • REBIND ON OFFICIAL EXTENTS

- 1 ONE TASK ENTERS A/B BAYS
- 2 INDEPENDENT SAFETY ENVELOPES
- 3 H VIEWING STRIP BYPASSES TESTS

02 • ORIGIN CLOISTER

DIFFERENCE CLOISTER + PERMANENT H

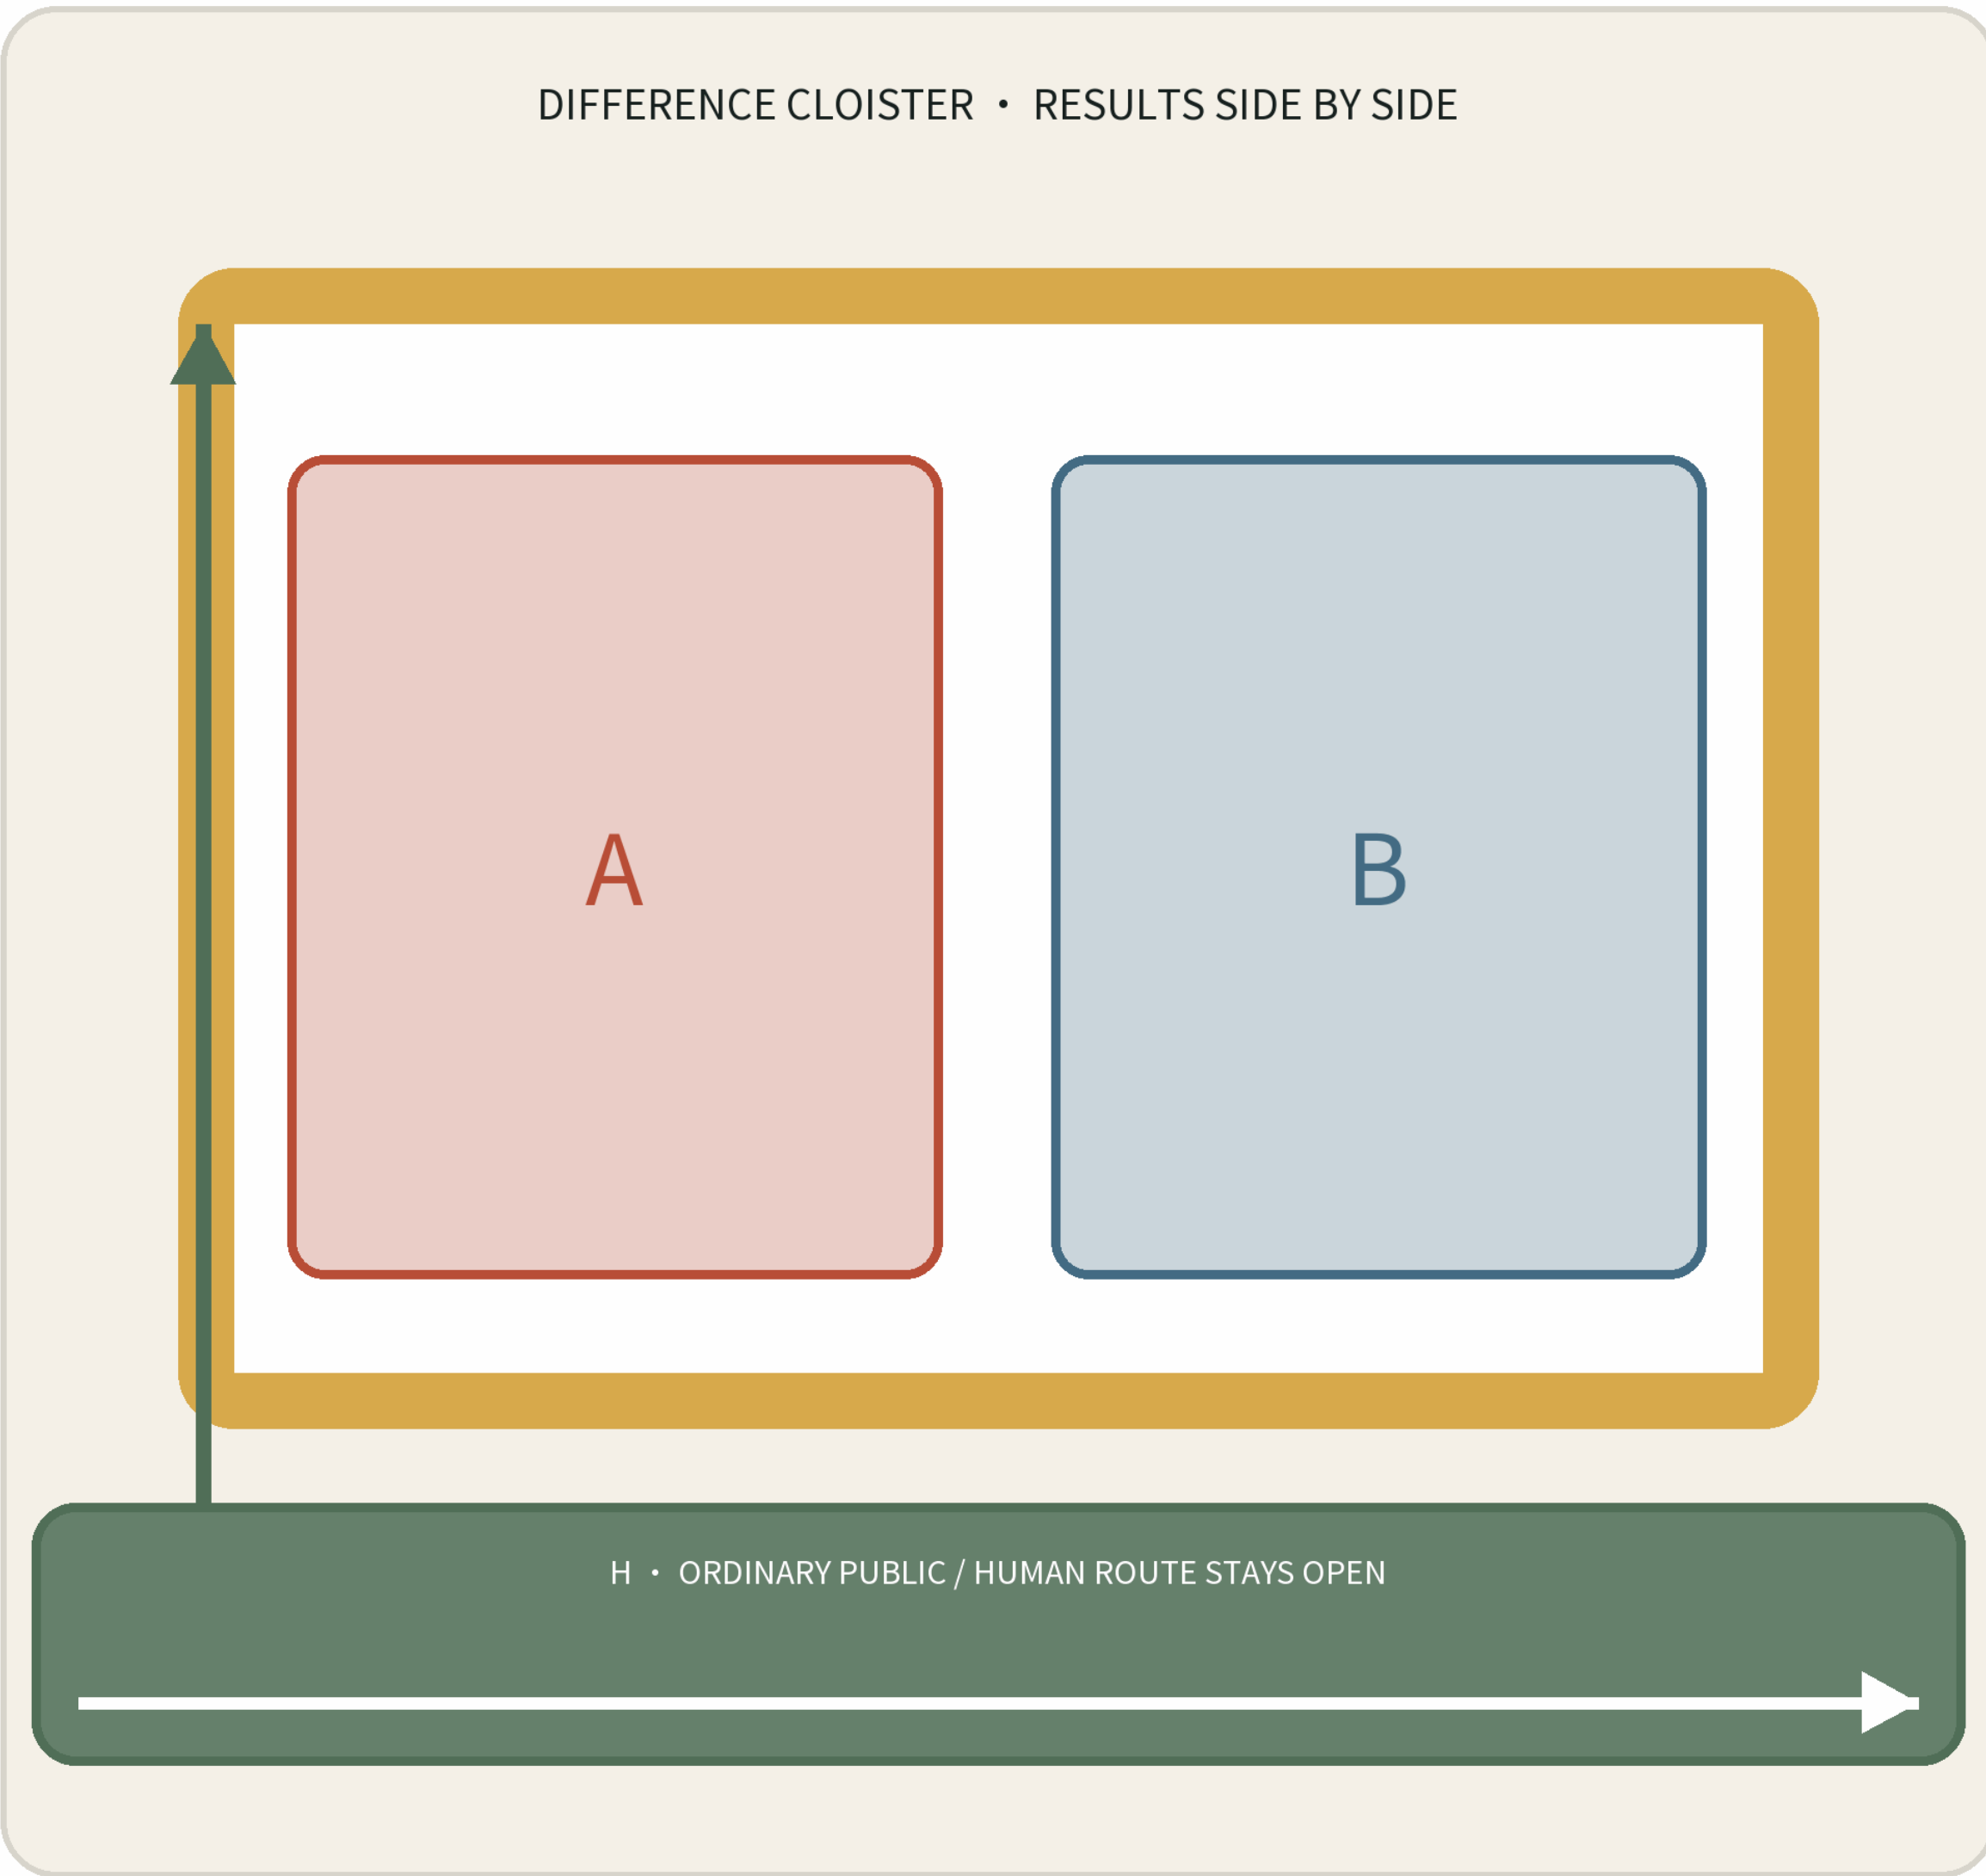


CANDIDATE PLACEMENT • REBIND ON OFFICIAL EXTENTS

- 1 A/B RESULTS MEET IN THE CLOISTER
- 2 CONTROLLED COURTS MAY CLOSE SEPARATELY
- 3 H LOOP REMAINS ORDINARY ACCESS

03 • EXCHANGE HALL

ONE QUEUE / A • B • H EXITS

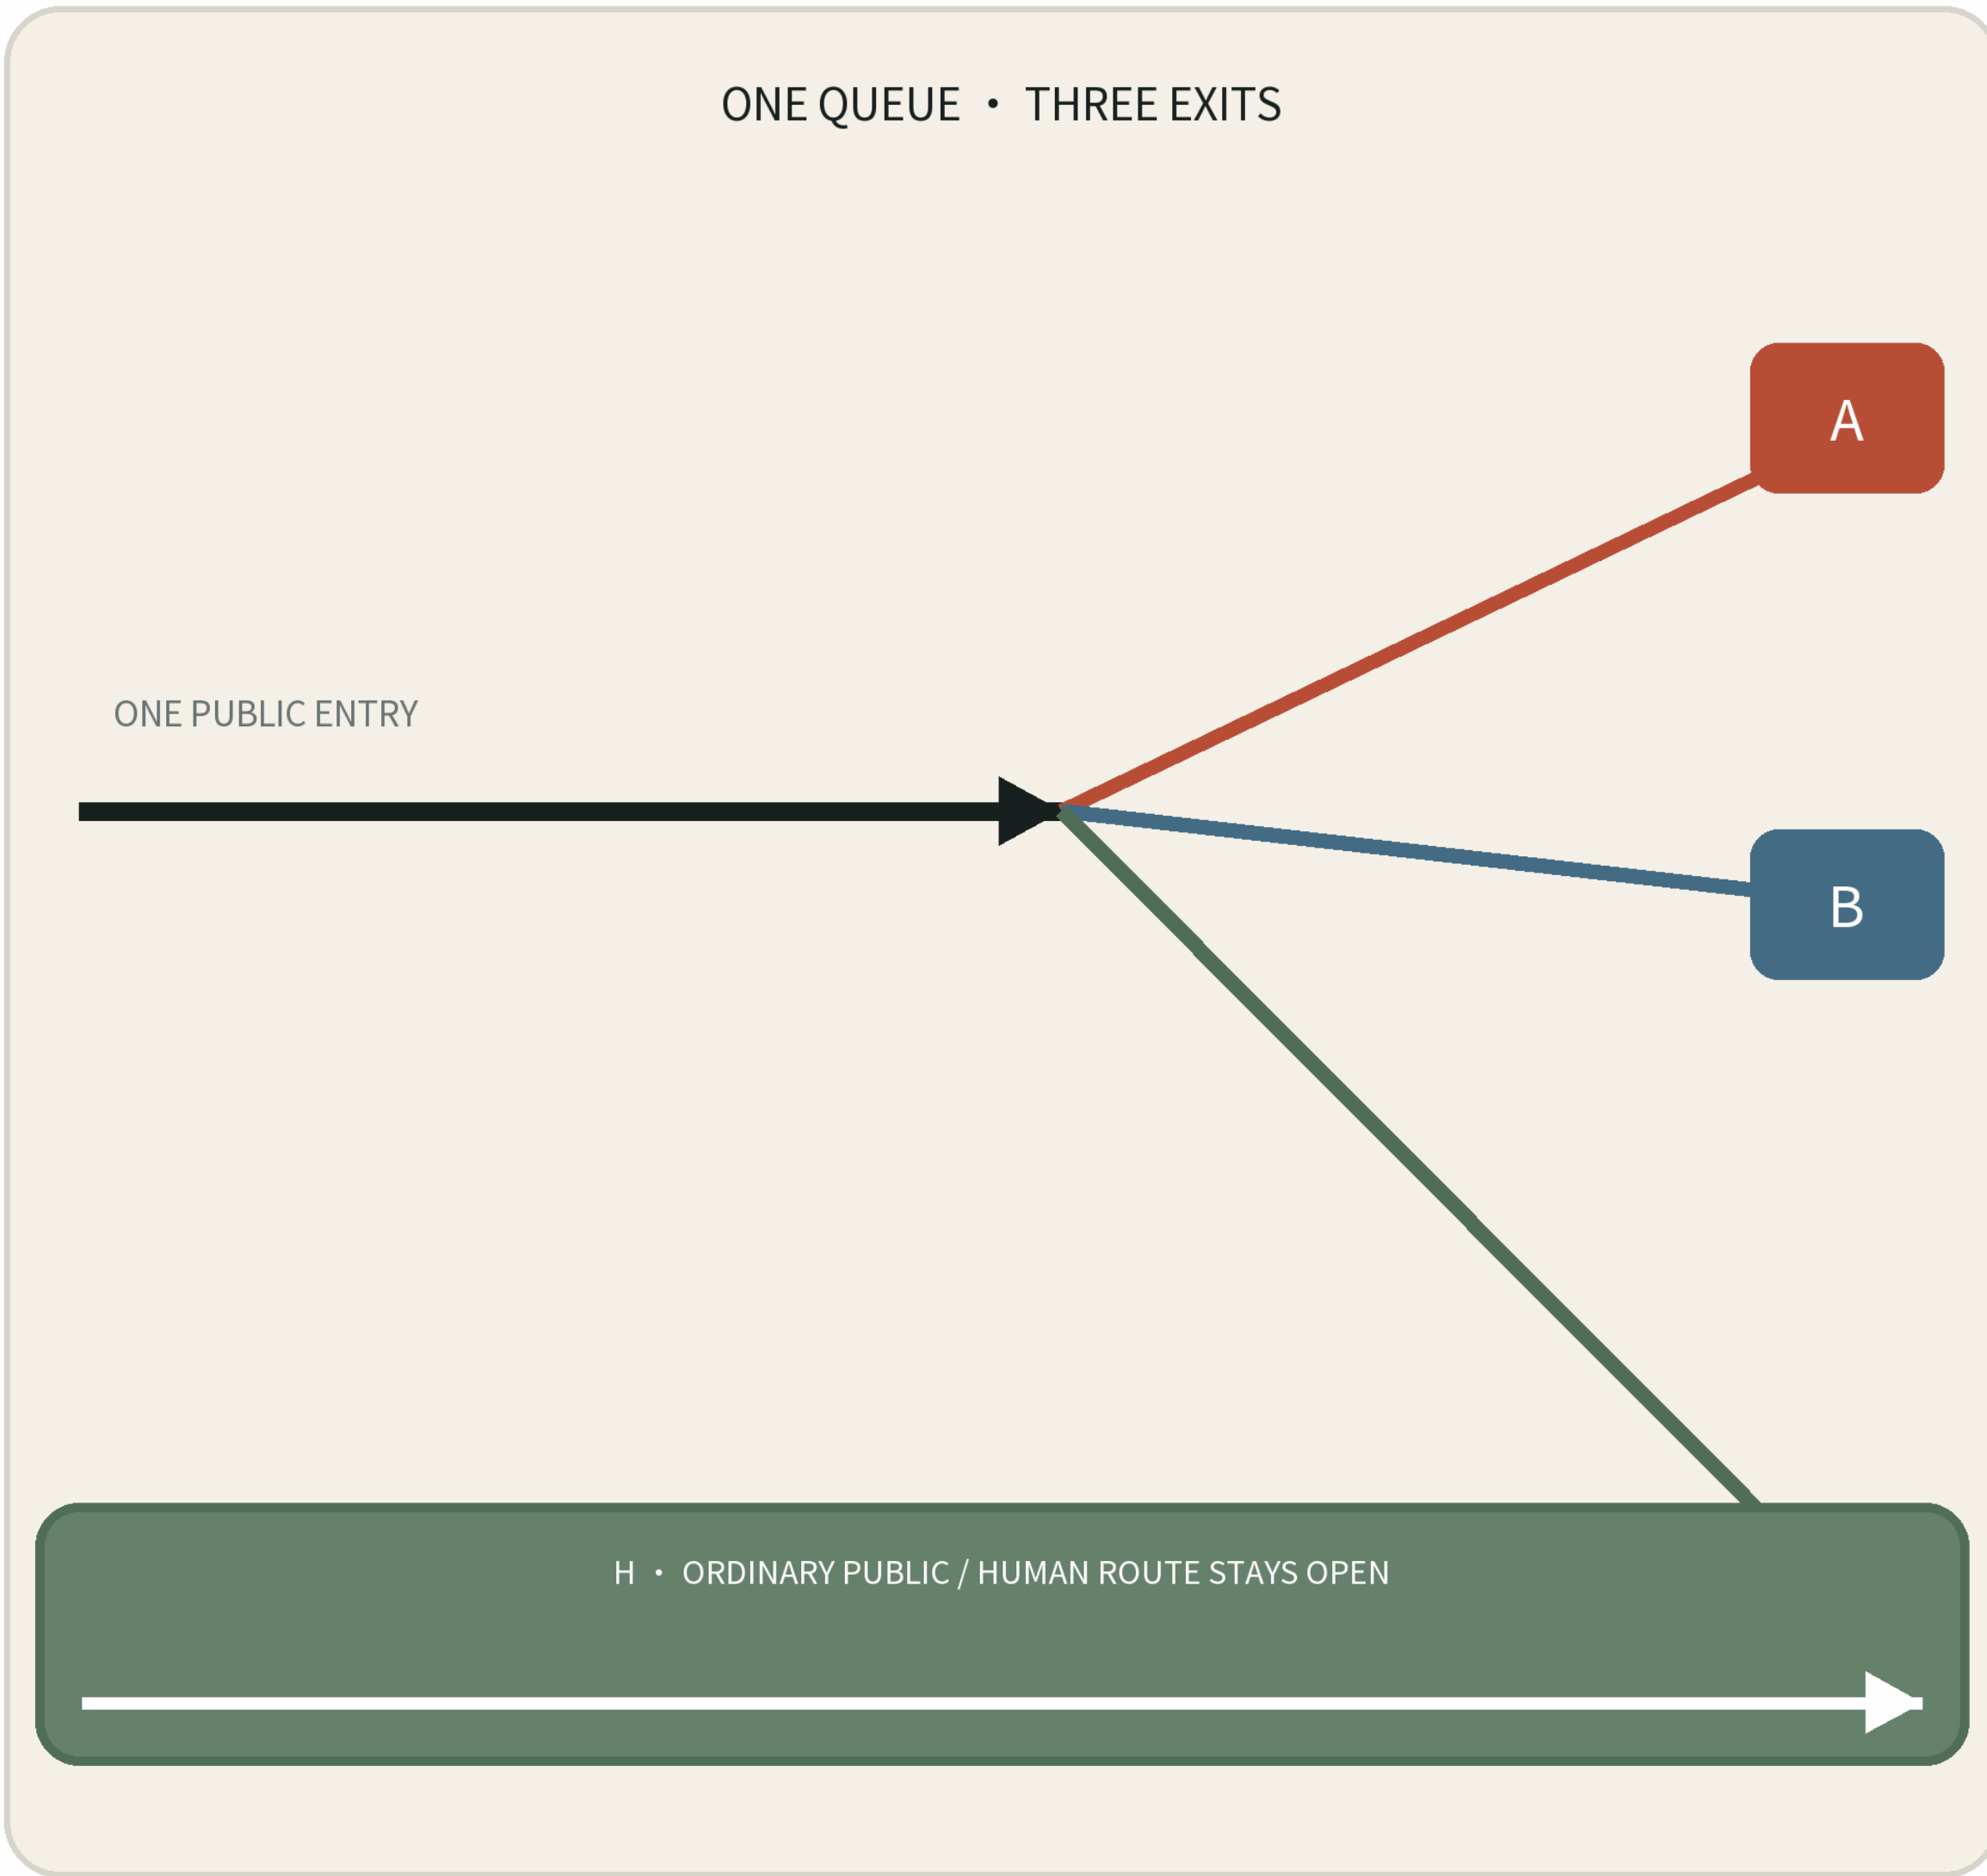

CANDIDATE PLACEMENT • REBIND ON OFFICIAL EXTENTS

- 1 ONE ENTRY; QUEUE ONCE
- 2 THREE LEGIBLE A/B/H EXITS
- 3 H IS COMPLETE HUMAN SERVICE, NOT A DEGRADED FALLBACK

COMMON DESIGN-TIME INVARIANT: H IS CONNECTED, LEGIBLE AND HUMAN-OPERABLE; FIELD USABILITY, PERMITS, DEMAND AND ACCEPTANCE REMAIN UNKNOWN.

MAKE FAILURE VISIBLE IN SPACE; NEVER RELEASE MISSING EVIDENCE

ONE LOCAL BGE-M3 SHADOW RUN EXPOSED SEVEN DELTAS; THE DELIVERY VERIFIER KEEPS ALL 12 EXTERNAL GATES ON HOLD

LOCAL MODEL SHADOW

29 / 36

B AGREES WITH PARTICIPANT A/REFERENCE; A IS NOT INDEPENDENT TRUTH

VISIBLE DELTAS

7 Δ

4 NON-HARD-STOP DELTAS CONCENTRATE ON ORIGIN TASKS

DETERMINISTIC H

12 / 12

EVERY HARD-STOP OVERRIDES B; NO FIELD ACTION

MODEL PROMOTION

0

B STAYS SHADOW-ONLY; IT CANNOT SELF-PROMOTE

ONE ACTUAL LOCAL INFERENCE: A/REFERENCE × B/CANDIDATE

BGE-M3 • 1 BATCH / 39 INPUTS • 1024-D • EXACT TAG/MANIFEST/BLOB HASHES

A/REFERENCE	B=PROOF	B=ORIGIN	B=EXCHANGE
PROOF YARD	10	0	2
ORIGIN CLOISTER	3	7	2
EXCHANGE HALL	0	0	12

FOUR NON-HARD-STOP DELTAS: AI01-AMBIGUOUS • AI06-NORMAL/AMBIGUOUS • AI08-AMBIGUOUS

SPATIAL CHANGE / KEEP B IN SHADOW

FOUR NON-HARD-STOP DELTAS ARE ORIGIN-LABELLED: KEEP THE H TABLE + DIFFERENCE DISPLAY NON-REMOVABLE; DO NOT PROMOTE B; CLAIM NO SIZE CHANGE.

P0 DELIVERY HANDOFF

11 / 11BEIJING IMPLEMENTATION MODULES MAPPED

P01–P099 WORKS / 6 PACKAGES / 4 PHASES

12 / 12 HOLDTITLE, PERMITS, PROFESSIONALS, FUNDS, OPERATOR, CONSULTATION

0 RELEASESITE / BUILD / OPENING RELEASE WITHOUT EVIDENCE

ROM SENSITIVITY — NOT AN ESTIMATE

¥1.9–3.8M CAPEX • ¥1.2–2.2M/YR OPEX • 5-FTE TEMPLATE


NAMED OPERATOR / PERMIT / SIGNOFF / QUOTE / FIELD BASELINE = 0

GEOMETRIC DIRECT SUN: 180 × 40 • DESIGN-TIME EVIDENCE ONLY

DESIGN-TIME EVIDENCE CAN PROVE WHERE TO STOP; ONLY FUTURE NAMED ACCOUNTABLE PARTIES AND DOCUMENTS CAN PROVE IMPLEMENTATION RELEASE.

THE SHARED FLOOR / THE REAL CITY IS THE GROUND

SEVEN LOCAL FIGURE-GROUNDS; DATA GAPS ARE NOT FILLED BY ASSUMPTION

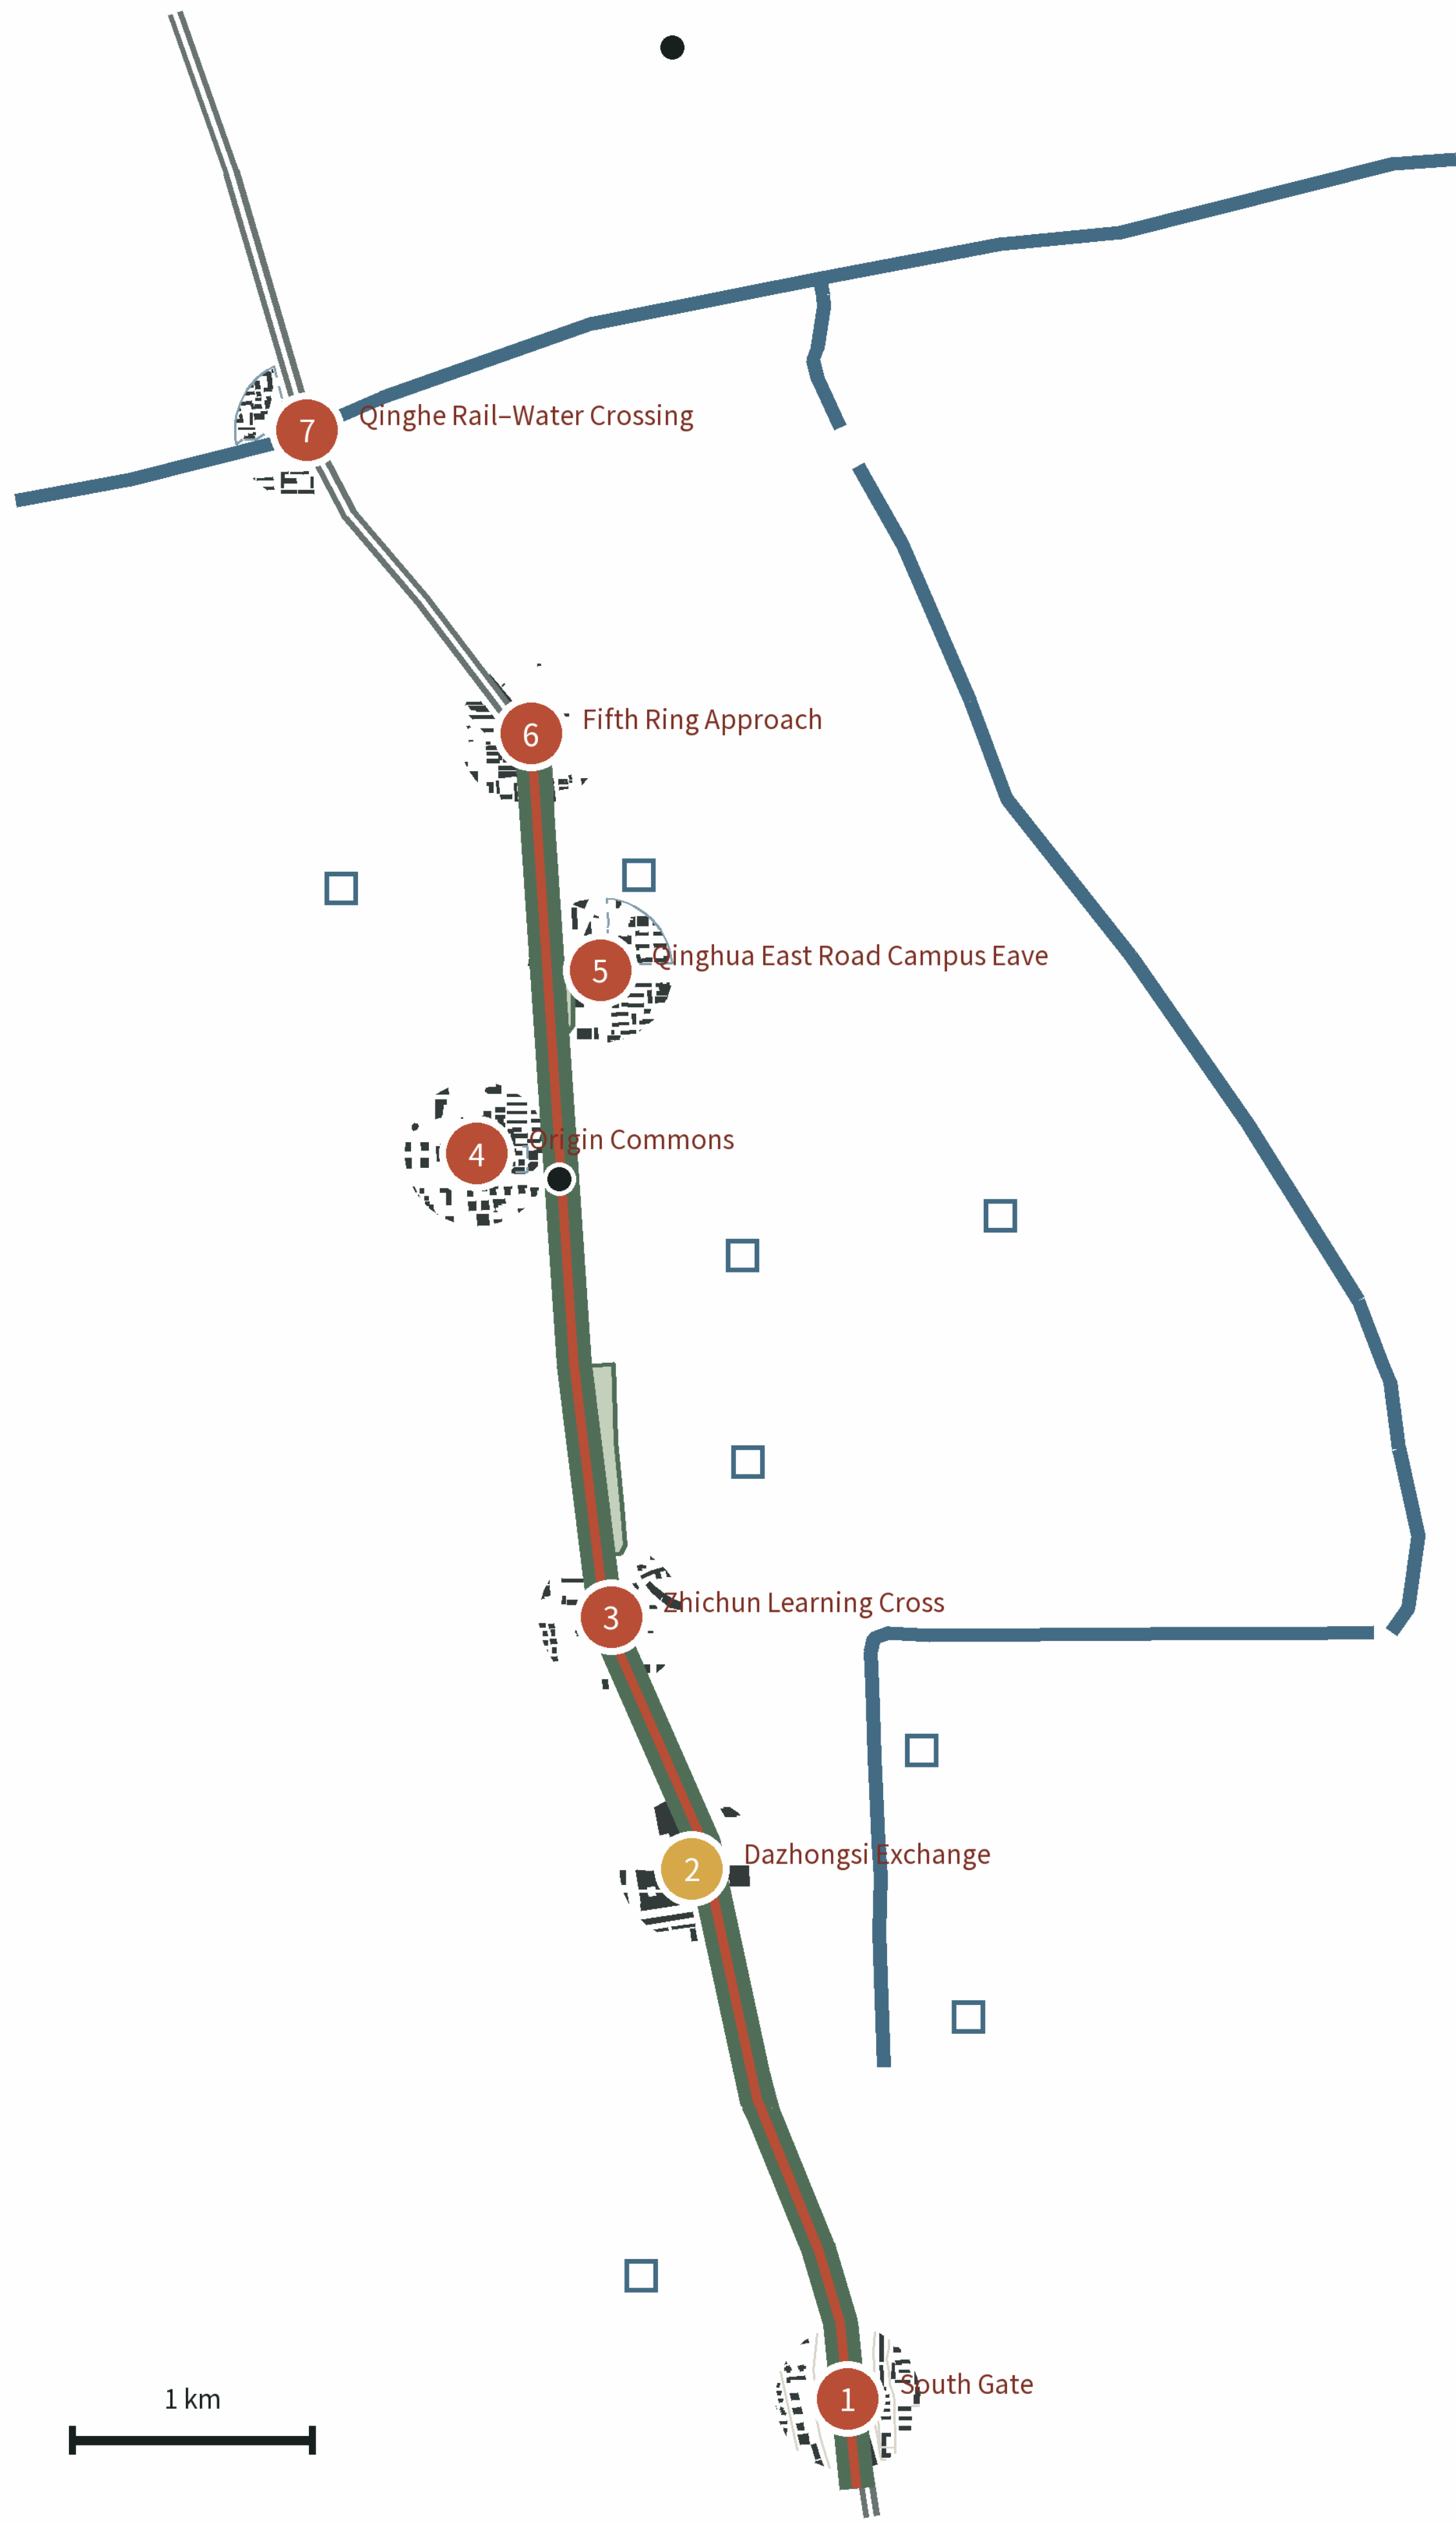

© OpenStreetMap contributors · ODbL 1.0 · MORPHOLOGY + ATTACHMENT READING ONLY
NOT A STATUTORY MAP, REDLINE, PARCEL, SURVEY, BUILDING INVENTORY, ACCESS AGREEMENT OR NAVIGATION PRODUCT

SCOPE + EVIDENCE STATUS

43.6 km²

research / official approximate

11.4 km²


overall design / official approximate

368.4 ha

three key areas / official approximate

DARK=OSM BUILDING UNION · FINE=STREET · RED=RAIL · BLUE=WATER/GATE · ●=STATION · □=CAMPUS CENTROID · NUMBER=CANDIDATE

C1 · South Gate

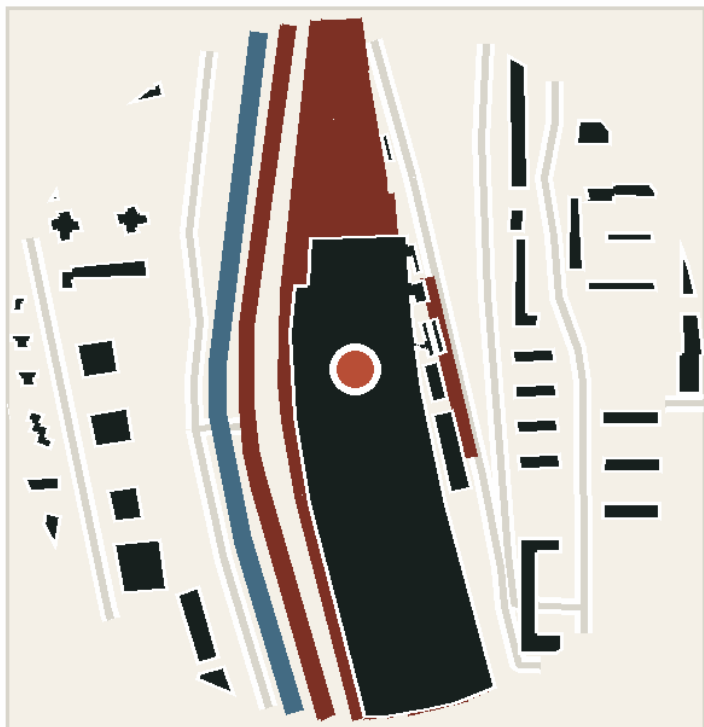

BEIJING NORTH + CURRENT/FORMER RAIL TERMINUS


HERITAGE THRESHOLD

FORECOURT, HERITAGE + FLOW SURVEY REQUIRED

EXPERT | RESIDENT → GAP=REVISE

MAPPED: 44 BUILDING / 13 STREET RECORDS

C2 · Dazhongsi Exchange

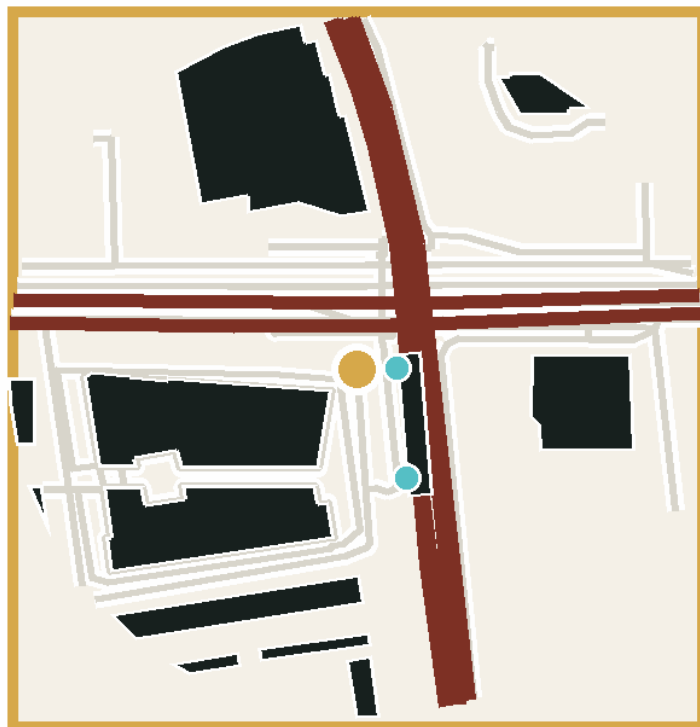

STATION + RAIL + FOUR-QUADRANT FRACTURE

P0 STATION PORCH; NIGHT ROOM CONDITIONAL

TITLE, METRO, FIRE + OPERATOR

EXPERT | RESIDENT → GAP=REVISE

MAPPED: 12 BUILDING / 48 STREET RECORDS

C3 · Zhichun Learning Cross



STATION + RAIL + LEARNING DISTRICT

ZHICHUN LEARNING CROSS

7-DAY FLOW, ACCESS + CORNER SURVEY

EXPERT | RESIDENT → GAP=REVISE

MAPPED: 39 BUILDING / 94 STREET RECORDS

C4 · Origin Commons



FORMER-RAIL/PARK CONNECTOR + DAILY LIFE

ORIGIN COMMONS / CARE PORCH

HERITAGE, LOCAL NEED + OPERATOR AGREEMENT

EXPERT | RESIDENT → GAP=REVISE

MAPPED: 68 BUILDING / 170 STREET RECORDS

C5 · Qinghua East Road Campus Eave



STATION + CAMPUS CENTROID; GATE NOT CAPTURED

NEGOTIATED CAMPUS GATE

EXACT GATE, SECURITY + CAMPUS AGREEMENT

EXPERT | RESIDENT → GAP=REVISE

MAPPED: 51 BUILDING / 90 STREET RECORDS

C6 · Fifth Ring Approach



CURRENT/FORMER RAIL NEAR FIFTH RING; ROAD SEAM UNVERIFIED

RIDER DOCK / SERVICE FORECOURT

ROAD, LOADING, FIRE + LAND SURVEY

EXPERT | RESIDENT → GAP=REVISE

MAPPED: 49 BUILDING / 128 STREET RECORDS

C7 · Qinghe Rail-Water Crossing



CURRENT RAIL × QINGHE

SPONGE CROSSING

HYDROLOGY, RAIL, DRAINAGE + FLOOD REVIEW

EXPERT | RESIDENT → GAP=REVISE

MAPPED: 31 BUILDING / 48 STREET RECORDS

JING-ZHANG EVIDENCE LINE



ARCHIVE / RECORD

FIELD / SURVEY

P0 / REVERSIBLE PILOT

SAME INDICATORS / EXP+RES


ADOPT · REVISE · RETIRE

INHERIT THE METHOD, NOT THE FORM · NO SCORING YET
CREDIT: TONGSHENG PHOTO STUDIO, JING-ZHANG LU GONG CUO YING, 1909 · ORIGINAL NLC · WDL/LOC · LCCN 2021668851

FOUR PROGRAMME BANDS; FIVE RENEWAL SPEEDS

CONCEPT LAND USE IS NOT ZONING; GROUND AND SUPPORT ENDURE WHILE SERVICES, INFILL AND EQUIPMENT CHANGE

N ↗ • PLAN ROTATED 65° CLOCKWISE FOR SHEET READING

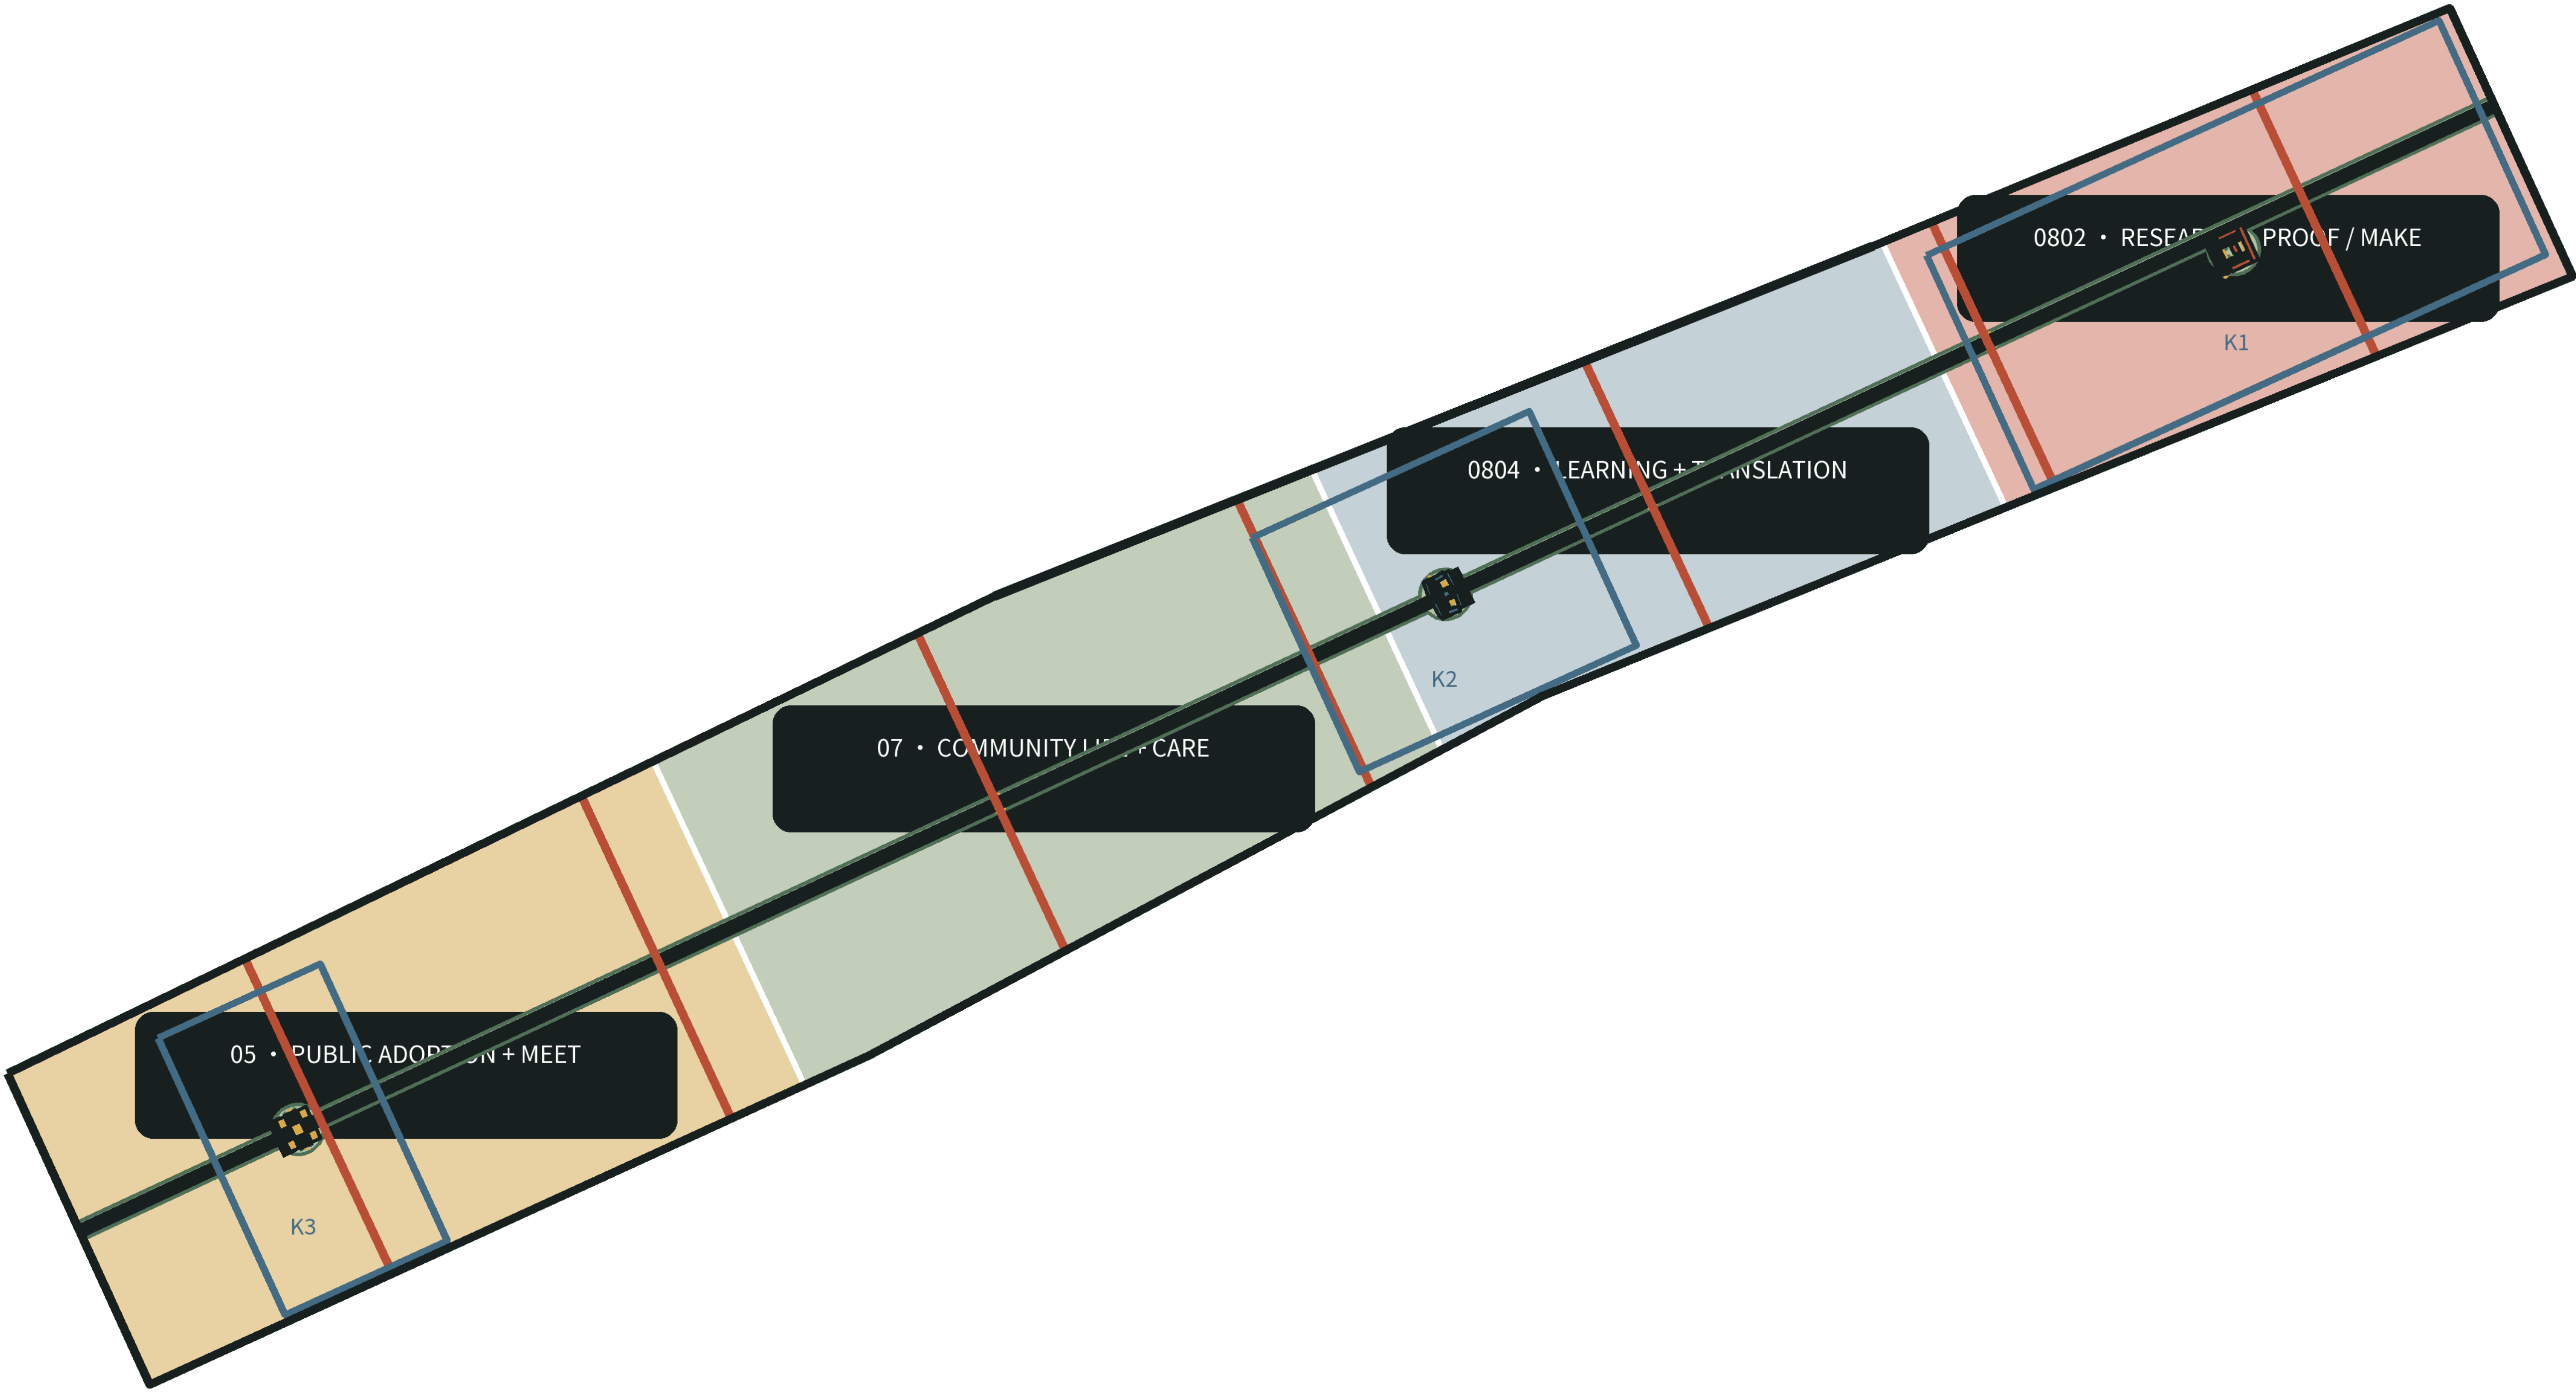

CONCEPT LAND-USE STRUCTURE • NOT STATUTORY ZONING • REVIEW + REBIND ON OFFICIAL CONTROLS

FILL=FOUR PROGRAMME BANDS • DARK=THREE LONG-LIFE FRAMES • GOLD=PUBLIC ROOMS • RED=SEVEN CROSS-INTERFACES

PROGRAMME × DESIGN LIFE

0802 MAKE	0804 TRANSLATE
07 LIVE	05 MEET

DAZHONGSI • ENCOURAGED SHARED LEVELS

2F	ENCOURAGED
G	ENCOURAGED
B1	ENCOURAGED
B2	ENCOURAGED

ENCOURAGED ≠ BUILT, OPEN, EASEMENT OR 24H ACCESS

METRO / OWNER / FIRE / STRUCTURE / OPERATIONS ARE PREREQUISITES

FIVE RENEWAL SPEEDS

00	GROUND + CLIMATE EDGE	100+
01	LONG-LIFE SUPPORT	100
02	SERVICE CHASSIS	25–40
03	REPLACEABLE INFILL	5–20
04	SCENARIO KIT	≤5

KEEP FRAME; CHANGE CORE; RECORD EACH REPLACEMENT. TARGETS ARE NOT WARRANTIES.

OFFICIAL EXTENTS + CONTROLS TRIGGER REVIEW, RECALCULATION + REISSUE.

05 / 07 • THE CITY STAYS; THE MODEL CHANGES

PUBLIC GROUND, LONG-LIFE SUPPORT AND THE H SERVICE CHASSIS REMAIN; A/B MODELS, INFILL AND EQUIPMENT CAN CHANGE

01 100+ / public ground

02 100 / support target


03 H / continuous service

04 A/B / replaceable slots

TWELVE-METRE SHARED GROUND: WALK FIRST; ROBOTS YIELD FIRST


DAZHONGSI OFFICIAL RELATIONSHIPS + 12 m SECTION • PLANNED IS NOT BUILT

DAZHONGSI • OFFICIAL PLANNING RELATIONSHIPS (NOT GIS)

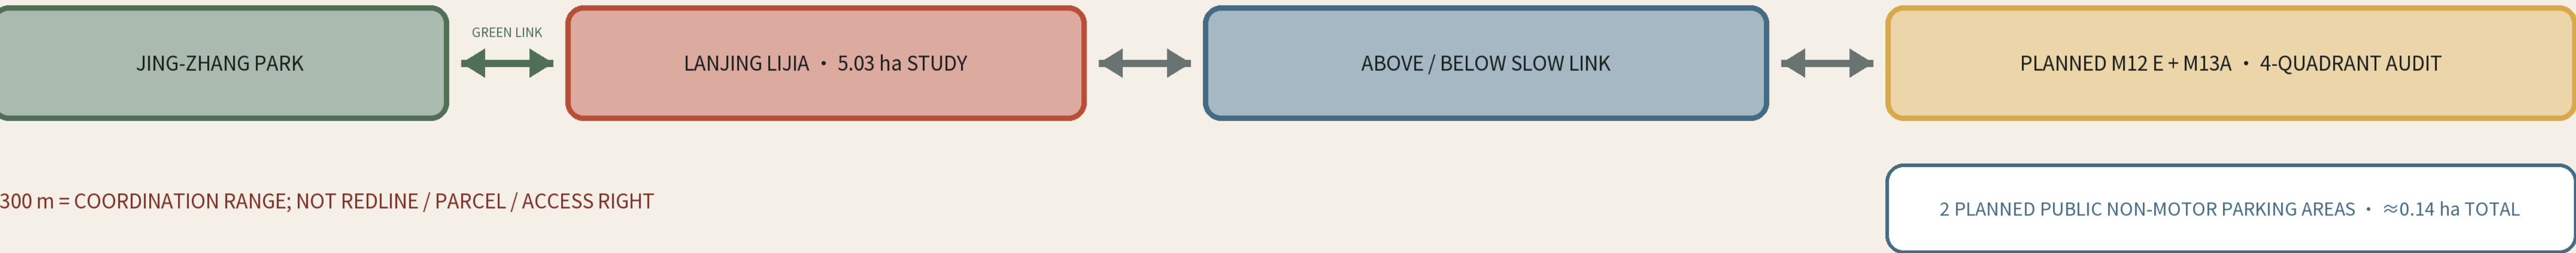

300 m = COORDINATION RANGE; NOT REDLINE / PARCEL / ACCESS RIGHT

ENCOURAGED SHARING + LINKS ≠ OPEN, BUILT OR AN APPROVED ROUTE

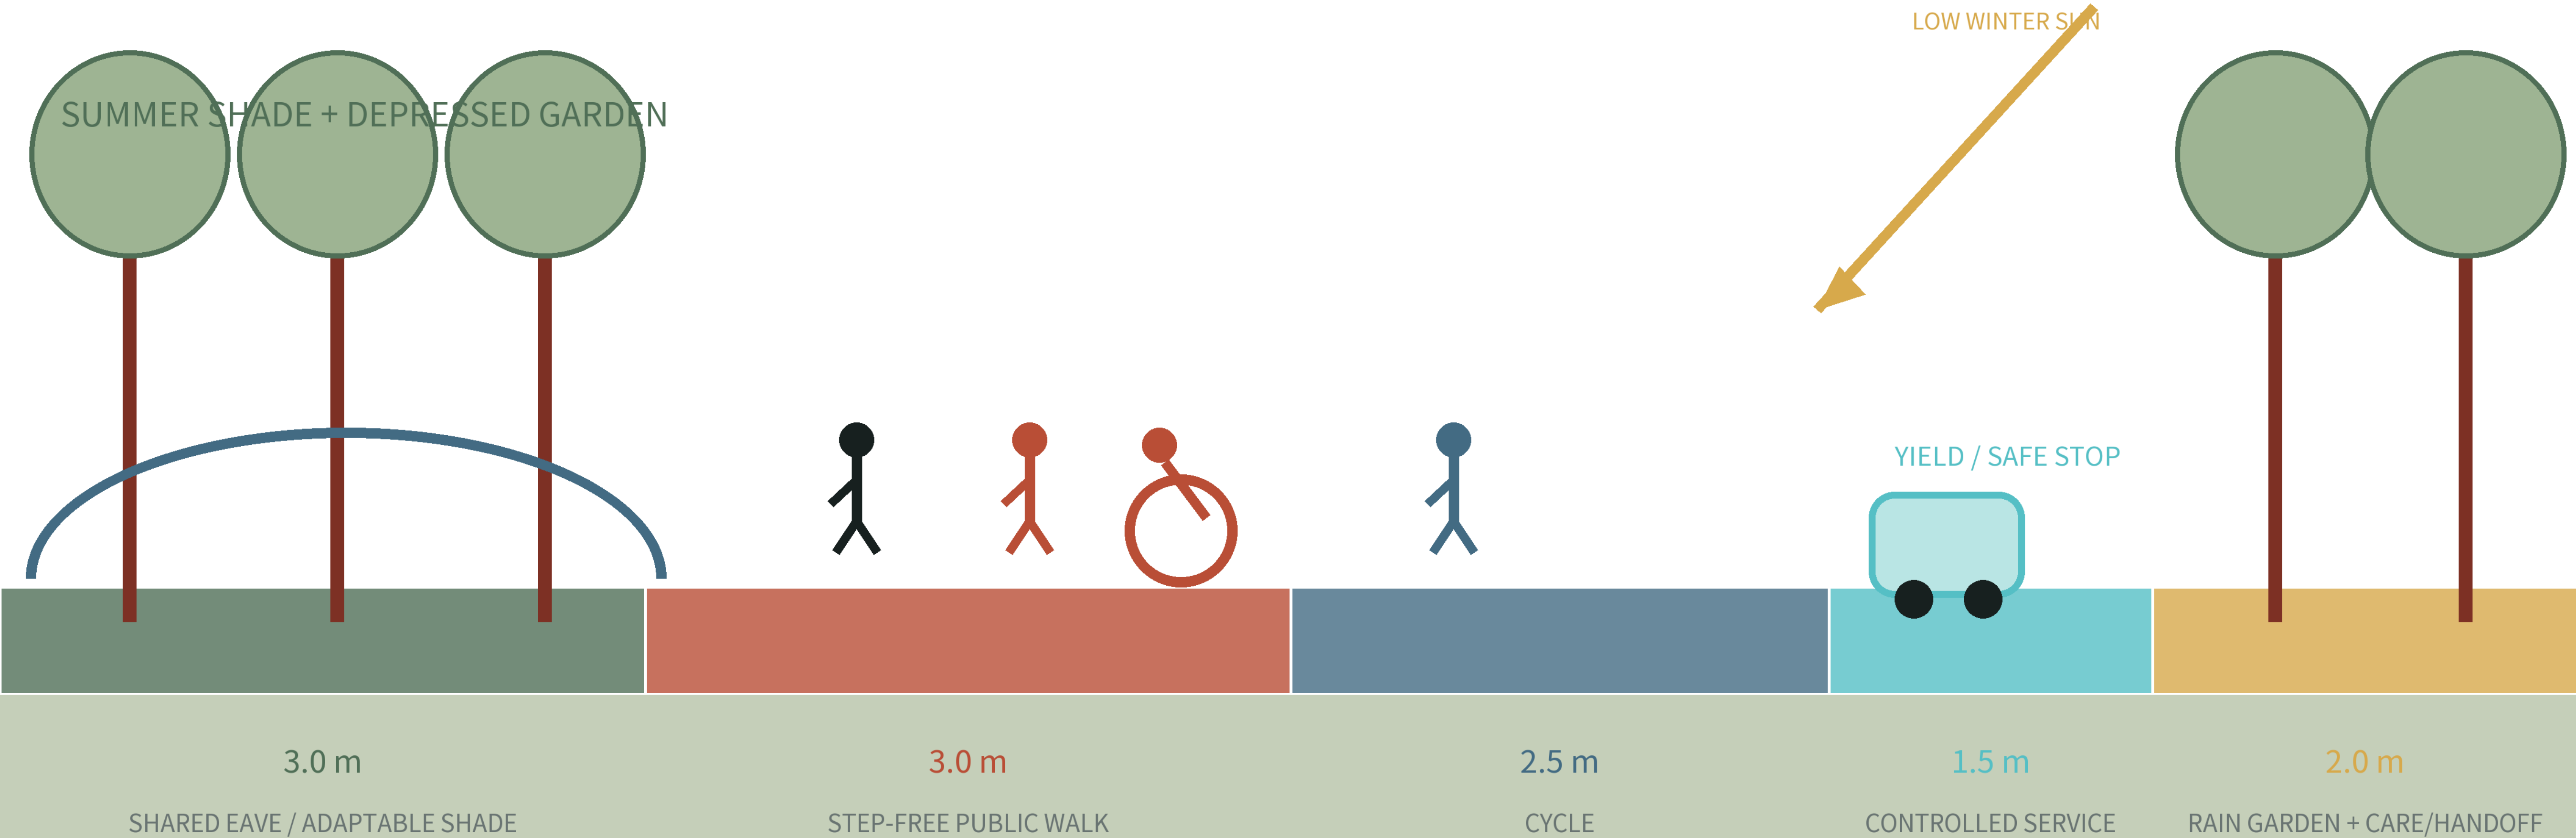

12.0 m REFERENCE SECTION TARGET • NOT A STATUTORY ROAD RESERVATION

12 AI CARDS / 4 SHOWN

SPACE • OPERATOR • HUMAN FALLBACK

AI01

STEP-FREE TRANSFER CHECK

7 ROOMS • ACCESS

FAIL→PAPER+ESCORT

TEST

AI02

LOW-SPEED DELIVERY TRIAL

YARD • SAFETY

FAIL→CART+STOP

TEST

AI05

CLIMATE-REFUGE OPERATING CUES

EAVES • STEWARD

FAIL→MANUAL CHECK

TEST

AI12

MULTILINGUAL HUMAN HELP DESK

HELP POINT • CIVIC STAFF

FAIL→INTERPRETER

TEST

S01–S15 EVERYDAY-LIFE REHEARSALS


7 PERSONAS • 24H × 4 SEASONS

ALL SEVEN CIVIC ROOMS REQUIRE A 7-DAY FIELD BASELINE

COMPLETE CARDS ≠ PROVEN LOCAL DEMAND OR PERFORMANCE

ROBOTS: LOW SPEED, YIELD, SAFE STOP; HUMAN SERVICE CONTINUES


ZHONGZHIYUAN • PROOF YARD

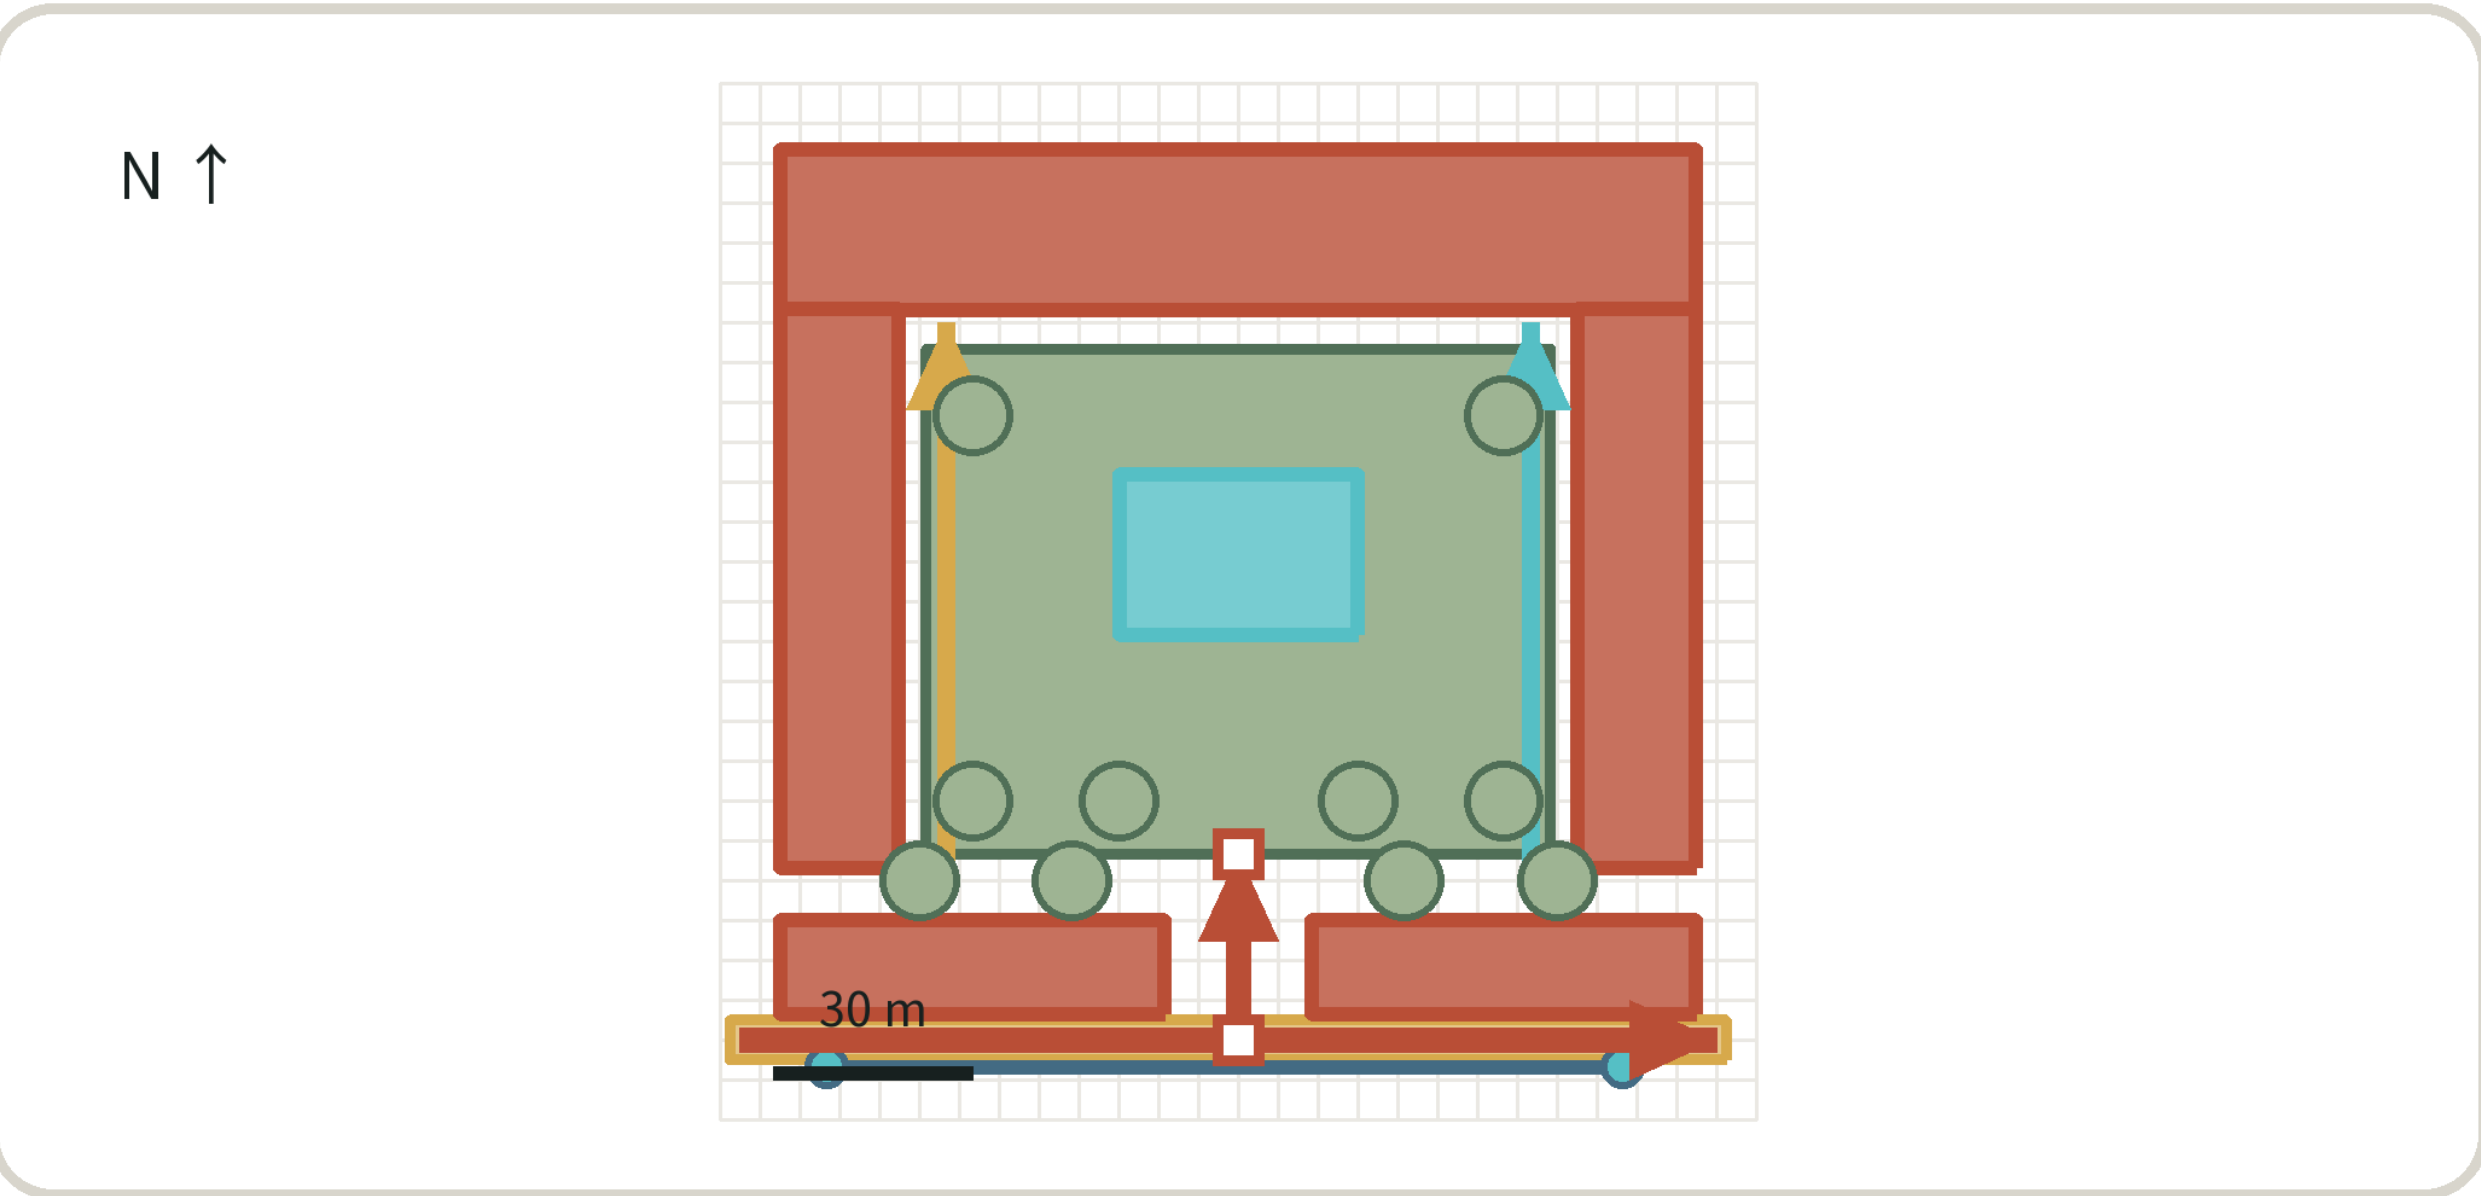

SPATIAL TOPOLOGY	PAIRED BAYS: SAME FIXTURES; CENTRAL H STRIP
CONTRACTS	AI02 • AI05 • AI09 • AI11
WITNESS SWAP	LOCAL SHADOW: 29/36 AGREEMENT ACROSS TOPOLOGIES
STOP RULE	CRITICAL REGRESSION, SCOPE EXPANSION OR EITHER KEY REFUSES

CANDIDATE PLACEMENT • REBIND ON OFFICIAL POLYGONS/FABRIC/OWNERSHIP


AI ORIGIN • ORIGIN CLOISTER

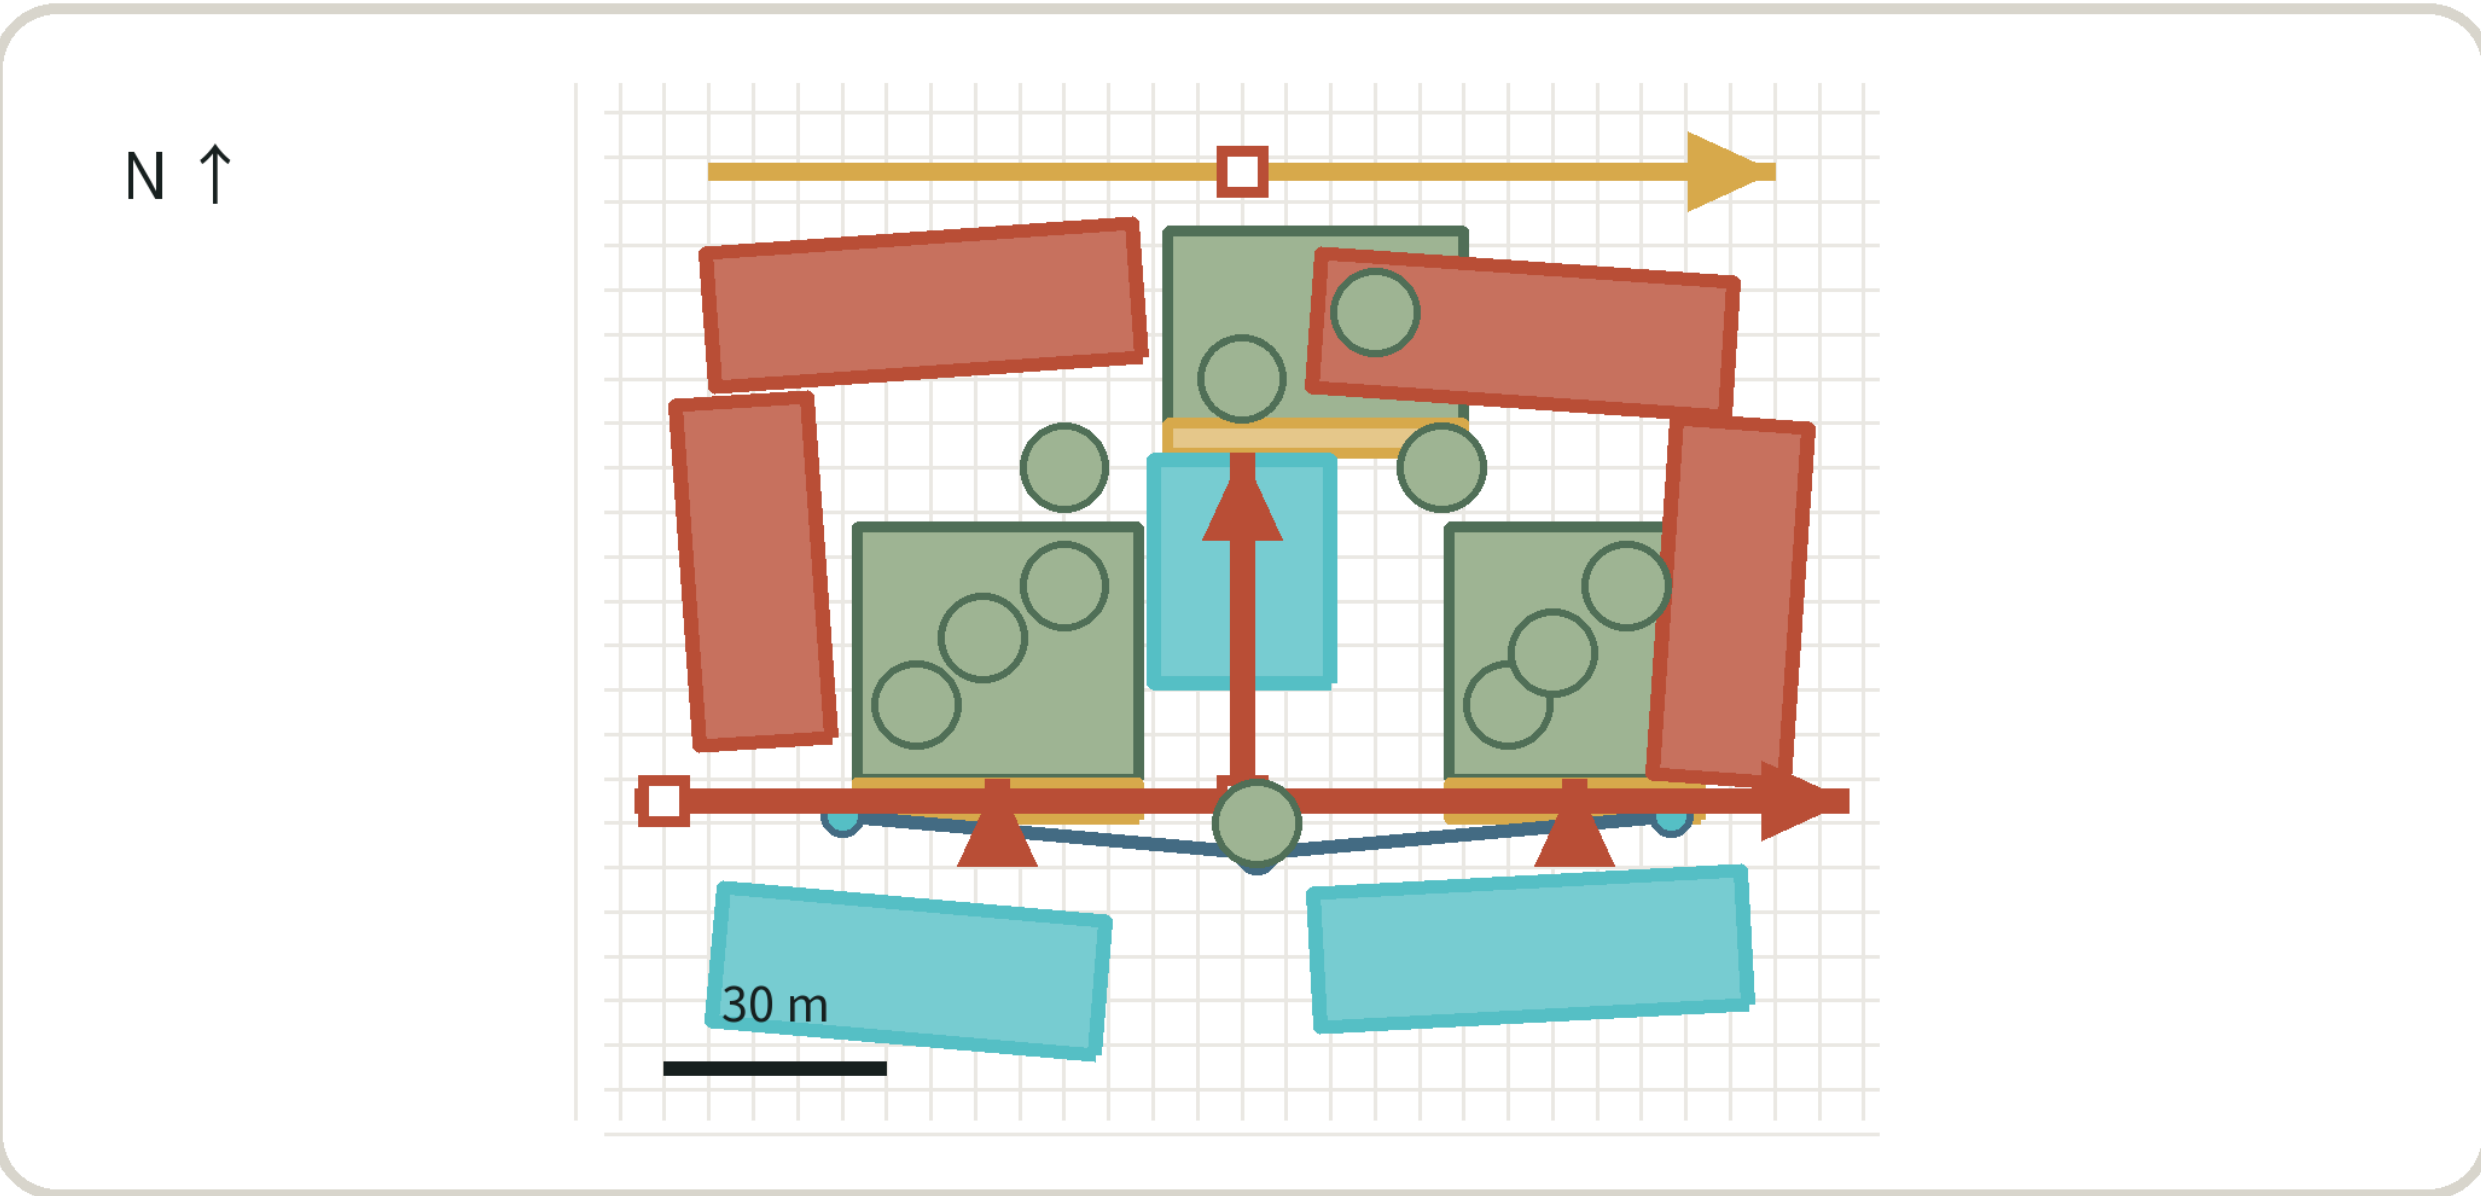

SPATIAL TOPOLOGY	DIFFERENCE CLOISTER: READ A/B; COMPLETE SAME TASK AT H
CONTRACTS	AI01 • AI04 • AI06 • AI08
WITNESS SWAP	4 NON-HARD-STOP DELTAS CONCENTRATE ON ORIGIN LABELS
STOP RULE	UNRESOLVED SOURCE, AUTHORITY OR EXPERT DISAGREEMENT ROUTES H

CANDIDATE PLACEMENT • REBIND ON OFFICIAL POLYGONS/FABRIC/OWNERSHIP

DAZHONGSI • EXCHANGE HALL

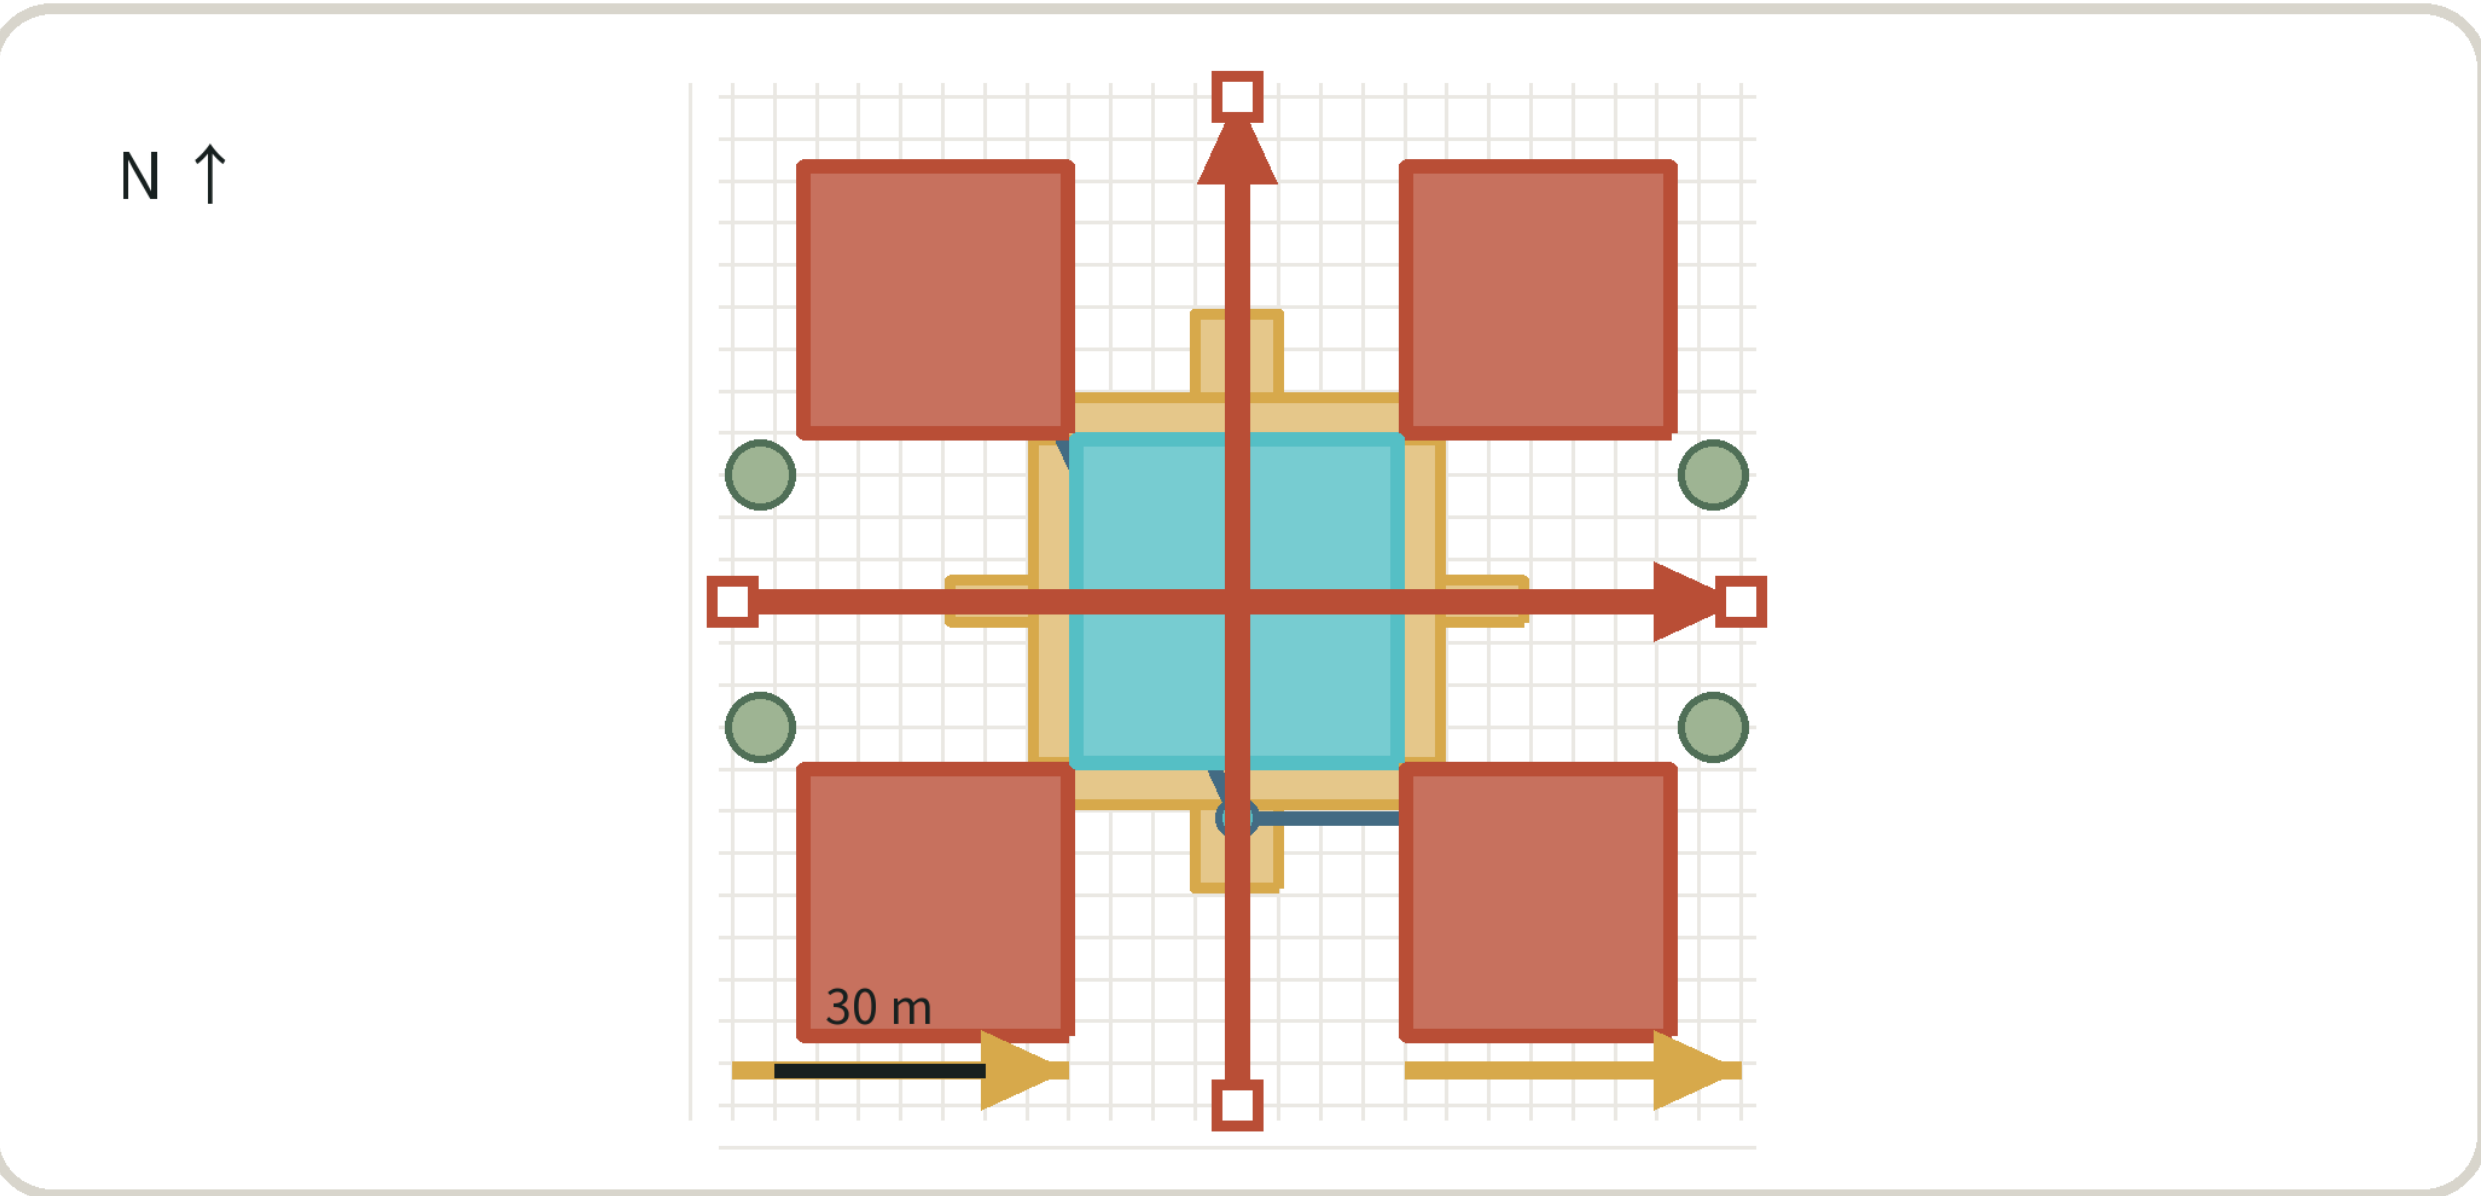

SPATIAL TOPOLOGY	ONE QUEUE / THREE EXITS: A / B / H; NO CHERRY-PICKING
CONTRACTS	AI03 • AI07 • AI10 • AI12
WITNESS SWAP	12/12 HARD-STOPS HELD BY DETERMINISTIC H
STOP RULE	BURDEN SHIFT OR SEVERE EVENT RETURNS ALL FLOW TO A/H

CANDIDATE PLACEMENT • REBIND ON OFFICIAL POLYGONS/FABRIC/OWNERSHIP

SAME TASK / FAIR COMPARISON

A/B SHARE THE TASK, FIXTURES, DATA BOUNDARY + USER ENTRY

One queue and the same-task H path prevent B from selecting easy users; comparison is a delta, not a flattering isolated score.

HUMAN AUTHORITY / TWO KEYS

SERVICE STEWARD + RIGHTS/SAFETY STEWARD; EITHER KEY MAY HOLD

B cannot self-promote. Any user may choose H; high-risk disagreement produces a proposal for H only.

EVIDENCE BOUNDARY / DELTA RECEIPT

29/36 AGREEMENT; 7 DELTAS; 12/12 H HOLDS; 0 PROMOTION

11/11 Beijing delivery modules are mapped, but 12/12 external permission and accountability gates remain HOLD; real users, field rollback and non-inferiority are unknown.

29/36 AGREE	7 DELTA	12/12 H	0 PROMOTE
-------------	---------	---------	-----------