


总体空间结构与公共服务骨架

一轴三片、多点支撑 | 真实图层沿廊道长轴展开

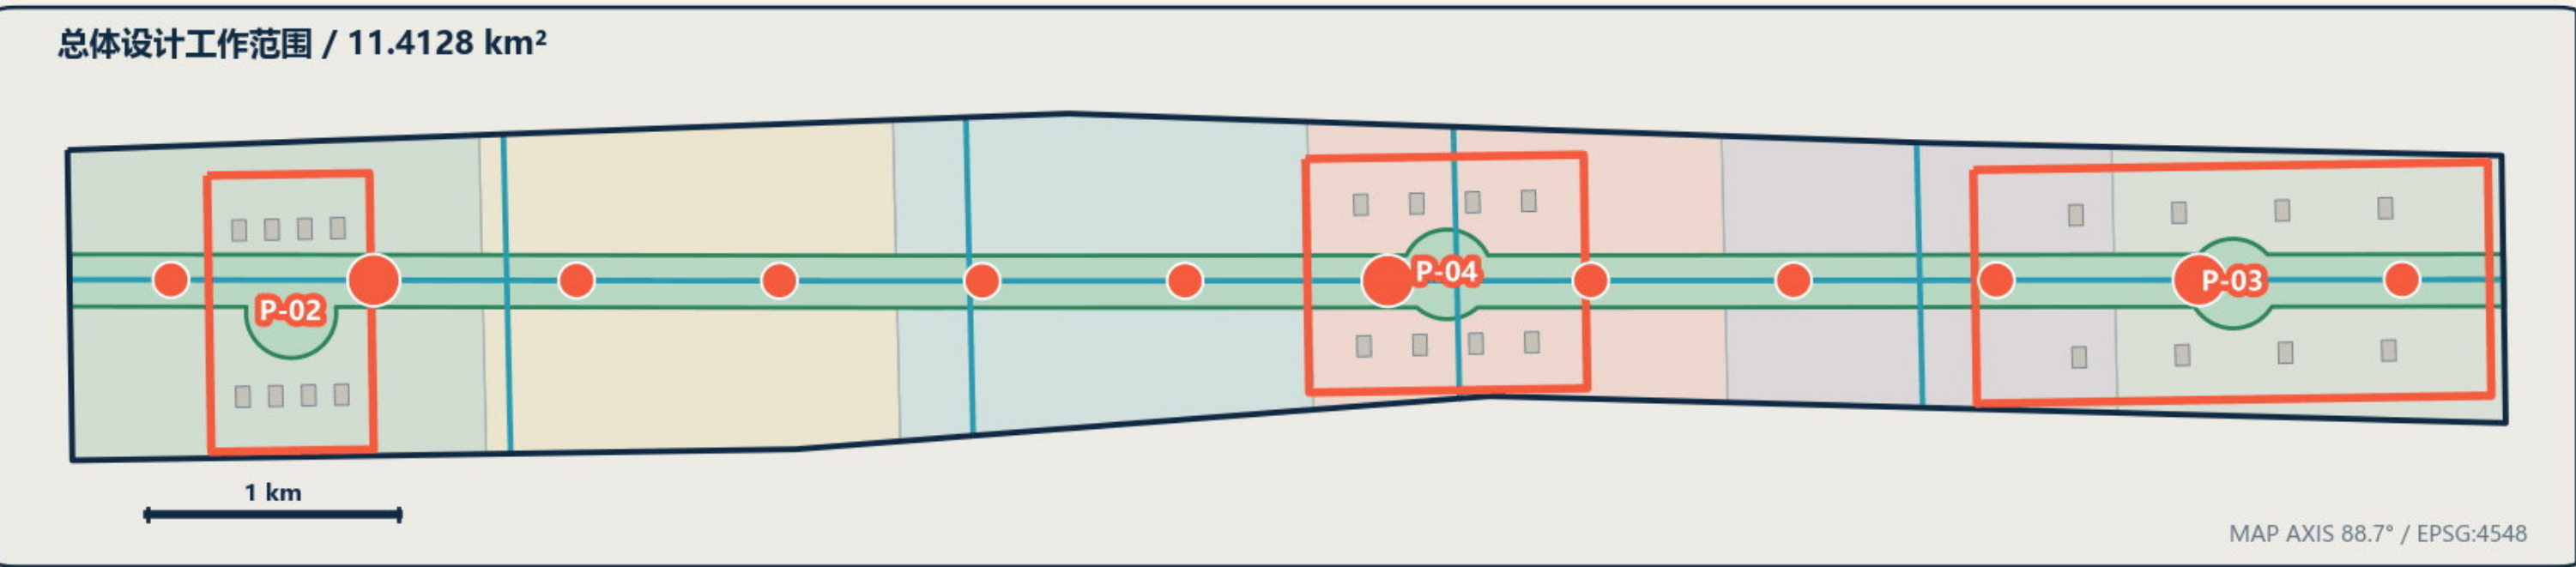

核心空间账本

11.41 km² 3

工作底图复算

重点片区

12

1 km

公共服务节点

首期示范段

图层图例

- 蓝绿公共空间
- 连续慢行主线
- 片区 / 服务节点
- 概念建筑体量

实施门控

- G0
- G1
- G2
- G3
- G4

资料—协商—审查—开放—复审

三处重点片区与首期项目

空间账本、首期入口、项目预算与开放条件



片区比较矩阵

P-03 众智园创新验证片区

192.1 ha / 192.9 ha

创新验证场

权属和场地许可、交通与消防、伦理与数据安全

P-04 北京 AI 原点社区协同创新片区

104.3 ha / 104.3 ha

共享首层计划

权属和租约、结构与消防、运营协议

P-02 大钟寺站城融合片区

72.0 ha / 72.0 ha


站城公共厅先导界面

客流和疏散、轨道安全、消防


公告面积与底图复算差异均小于 0.5%；正式四至仍由后续法定成果确定。

实施协议、负向测试与退出条件

十二项服务通过八条准入规则；八类缺陷由对应规则拦截

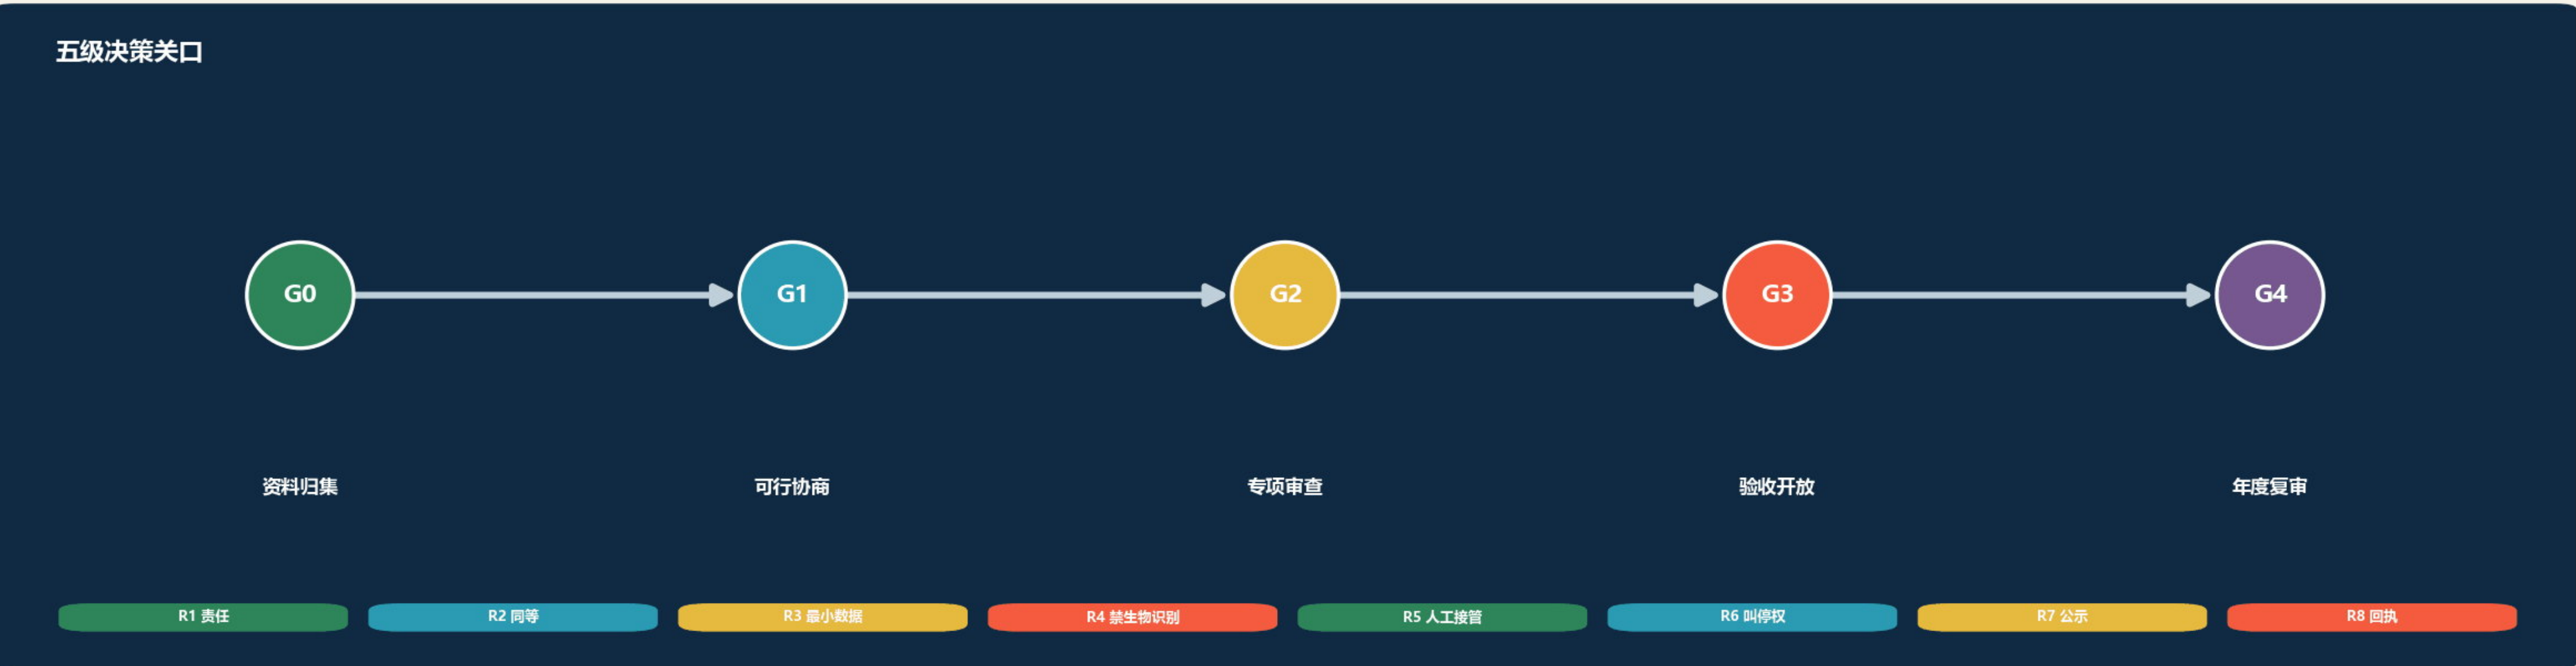

12 项服务 × 8 条规则：全部通过

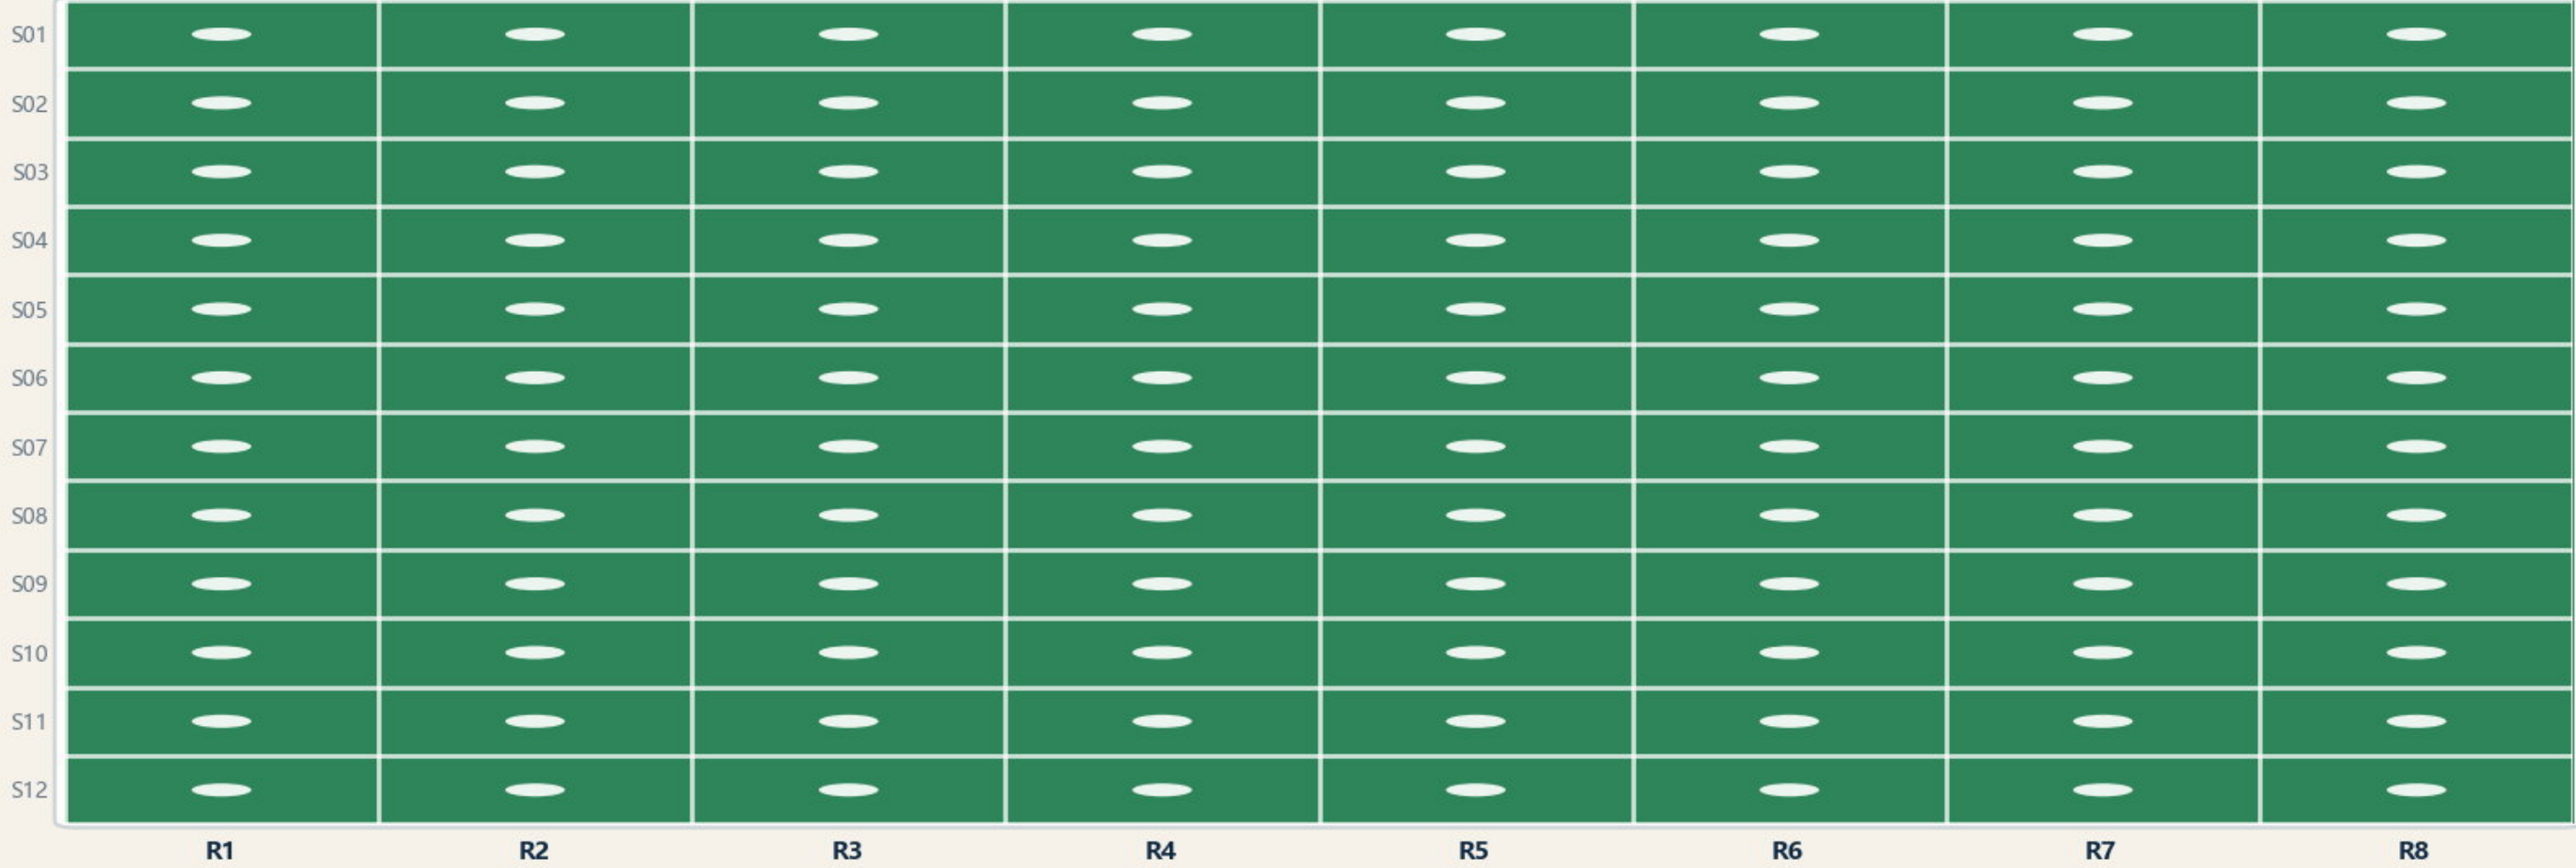

12/12

有效服务通过

8/8

缺陷被拦截


0

失效规则

负向测试 X01~X08 分别触发 R1~R8；结果来自可复算桌面协议，不代表项目授权或建成表现。


指标证据、建议目标与验收责任

九项实施指标按证据类型、测量方法和责任主体组织

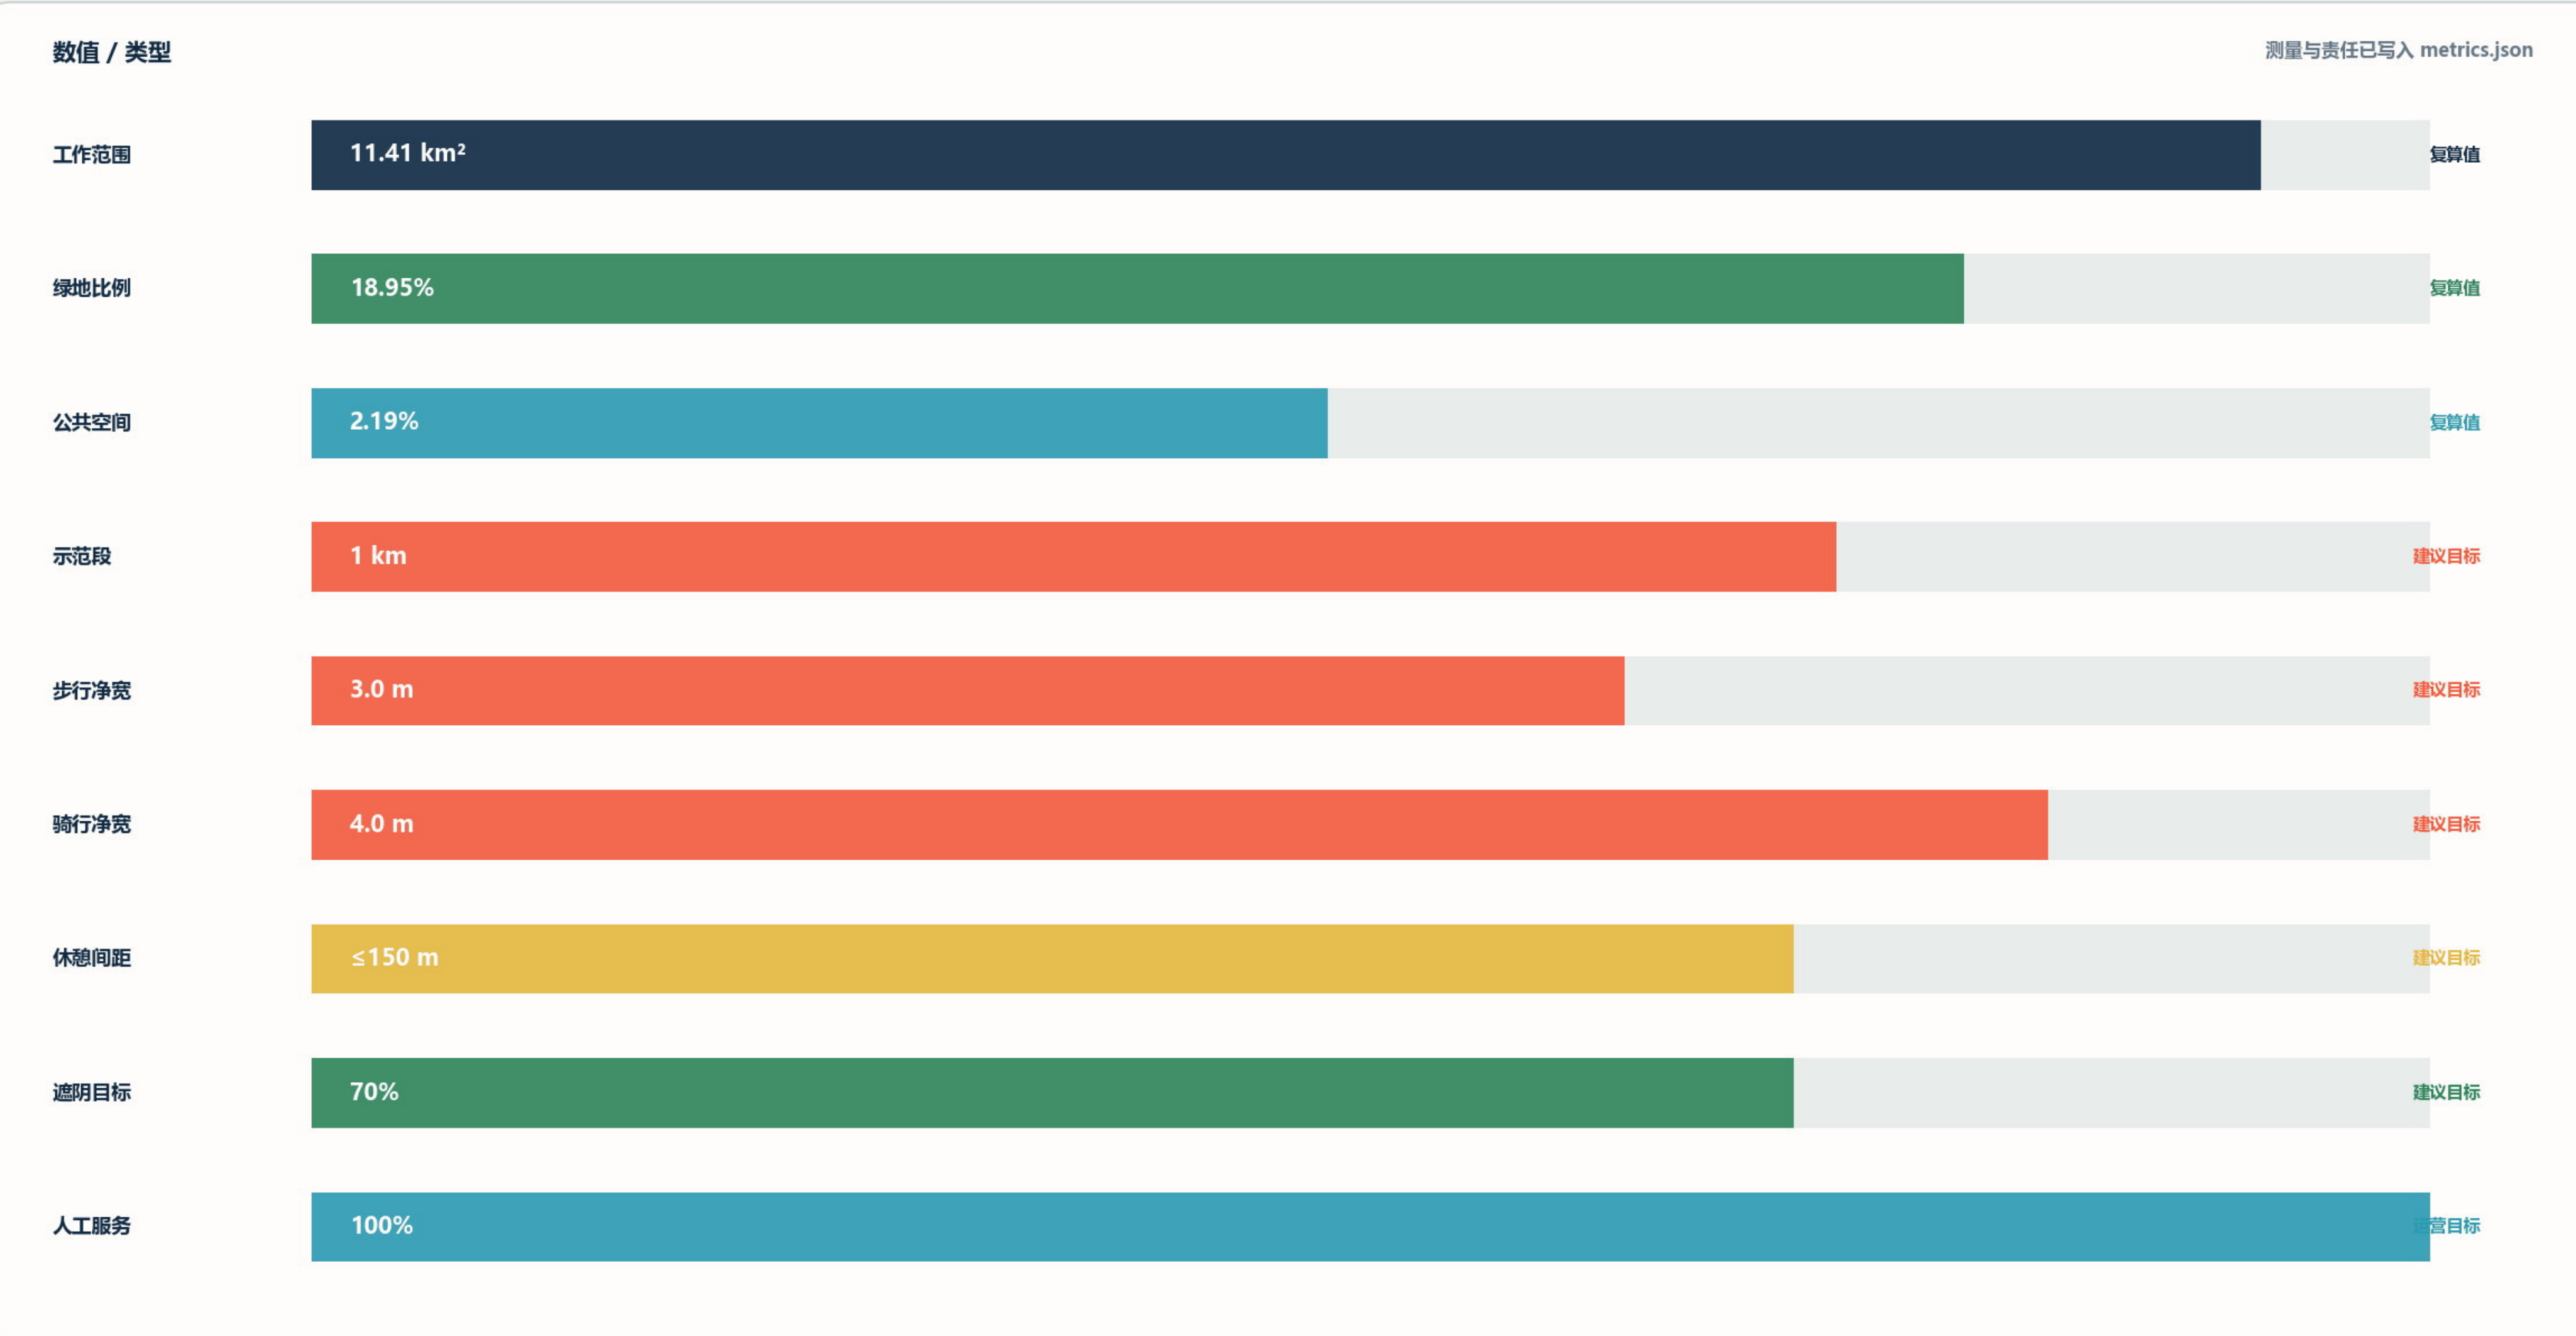

用地结构与复合功能组织

六类方案分区、面积平衡与实施边界

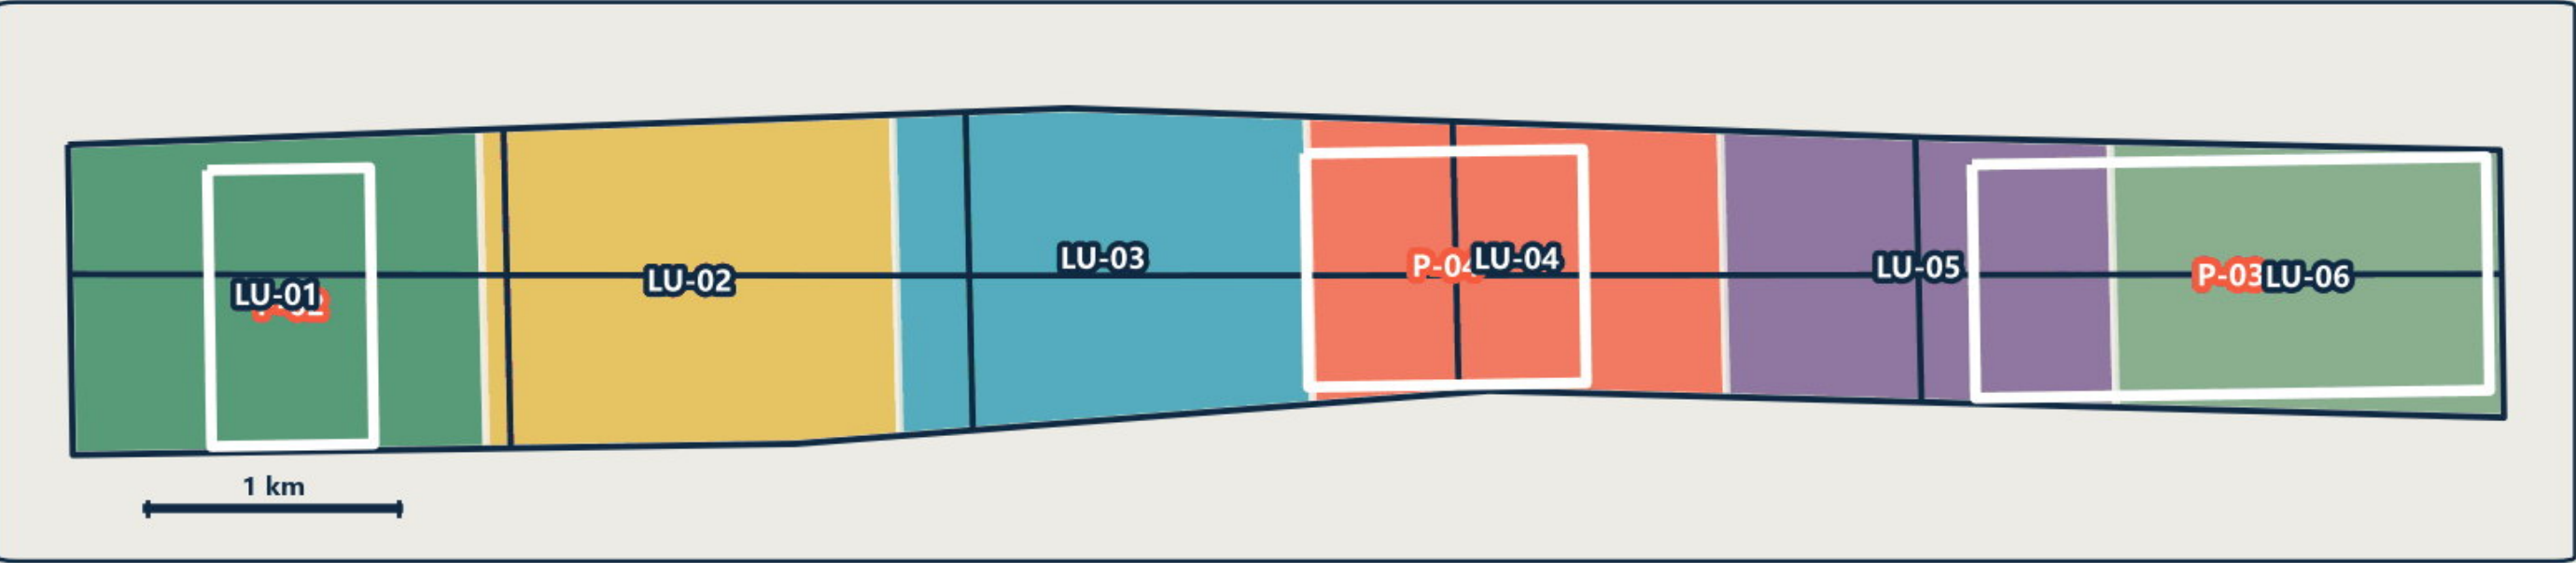

功能结构与实施提示

LU-01 研发与责任测试 208.6 ha / 18.3%	受控测试优先	LU-02 人才居住与照护 214.4 ha / 18.8%	照护设施协同
LU-03 共同学习与转化 204.9 ha / 17.9%	存量首层微改造	LU-04 铁路文化与公共服务 180.8 ha / 15.8%	铁路文化与服务
LU-05 AI 日常服务与商业 166.2 ha / 14.6%	日常服务融合	LU-06 蓝绿韧性基础设施 166.4 ha / 14.6%	海绵设施连续


1141.3 ha 六类方案分区完整覆盖：空白 0、重叠 0。

方案土地平衡

LU-01	208.6 ha	研发与责任测试
LU-02	214.4 ha	人才居住与照护
LU-03	204.9 ha	共同学习与转化
LU-04	180.8 ha	铁路文化与公共服务
LU-05	166.2 ha	AI 日常服务与商业
LU-06	166.4 ha	蓝绿韧性基础设施

慢行、蓝绿与气候适应一体化设计

连续网络、典型断面、气候基线与验收方法

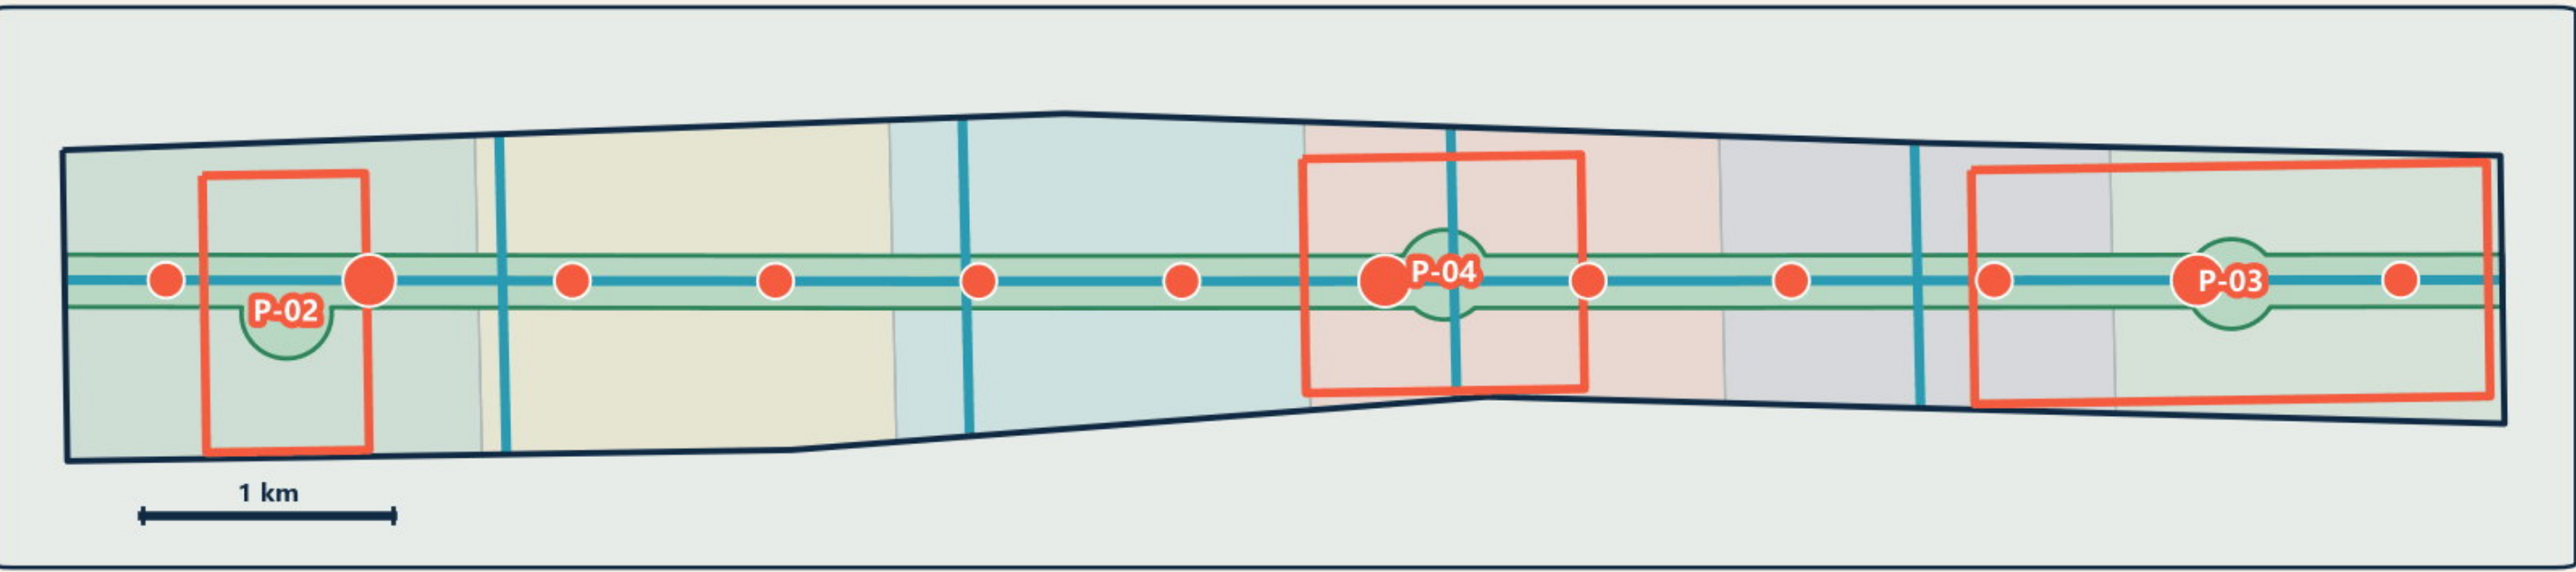

2015–2024 气候基线

35.58°C 日最高温 P95

22.3 d/y ≥35°C 日数

649.1 mm 年均降水

4.05 kWh/m²/日太阳辐射

连续步行

3.0 m

雨水花园

2.5 m

双向骑行

4.0 m

服务停留

2.5 m

验收要点


01 连续净宽实测

02 汇水—溢流—道水

03 遮阴与休憩间距

全龄包容性、负担与程序性权利

九类人群同时登记受益、负担、盲区、所需输入和暂缓权
登记议题关联强度 0–3（由台账文本复算）

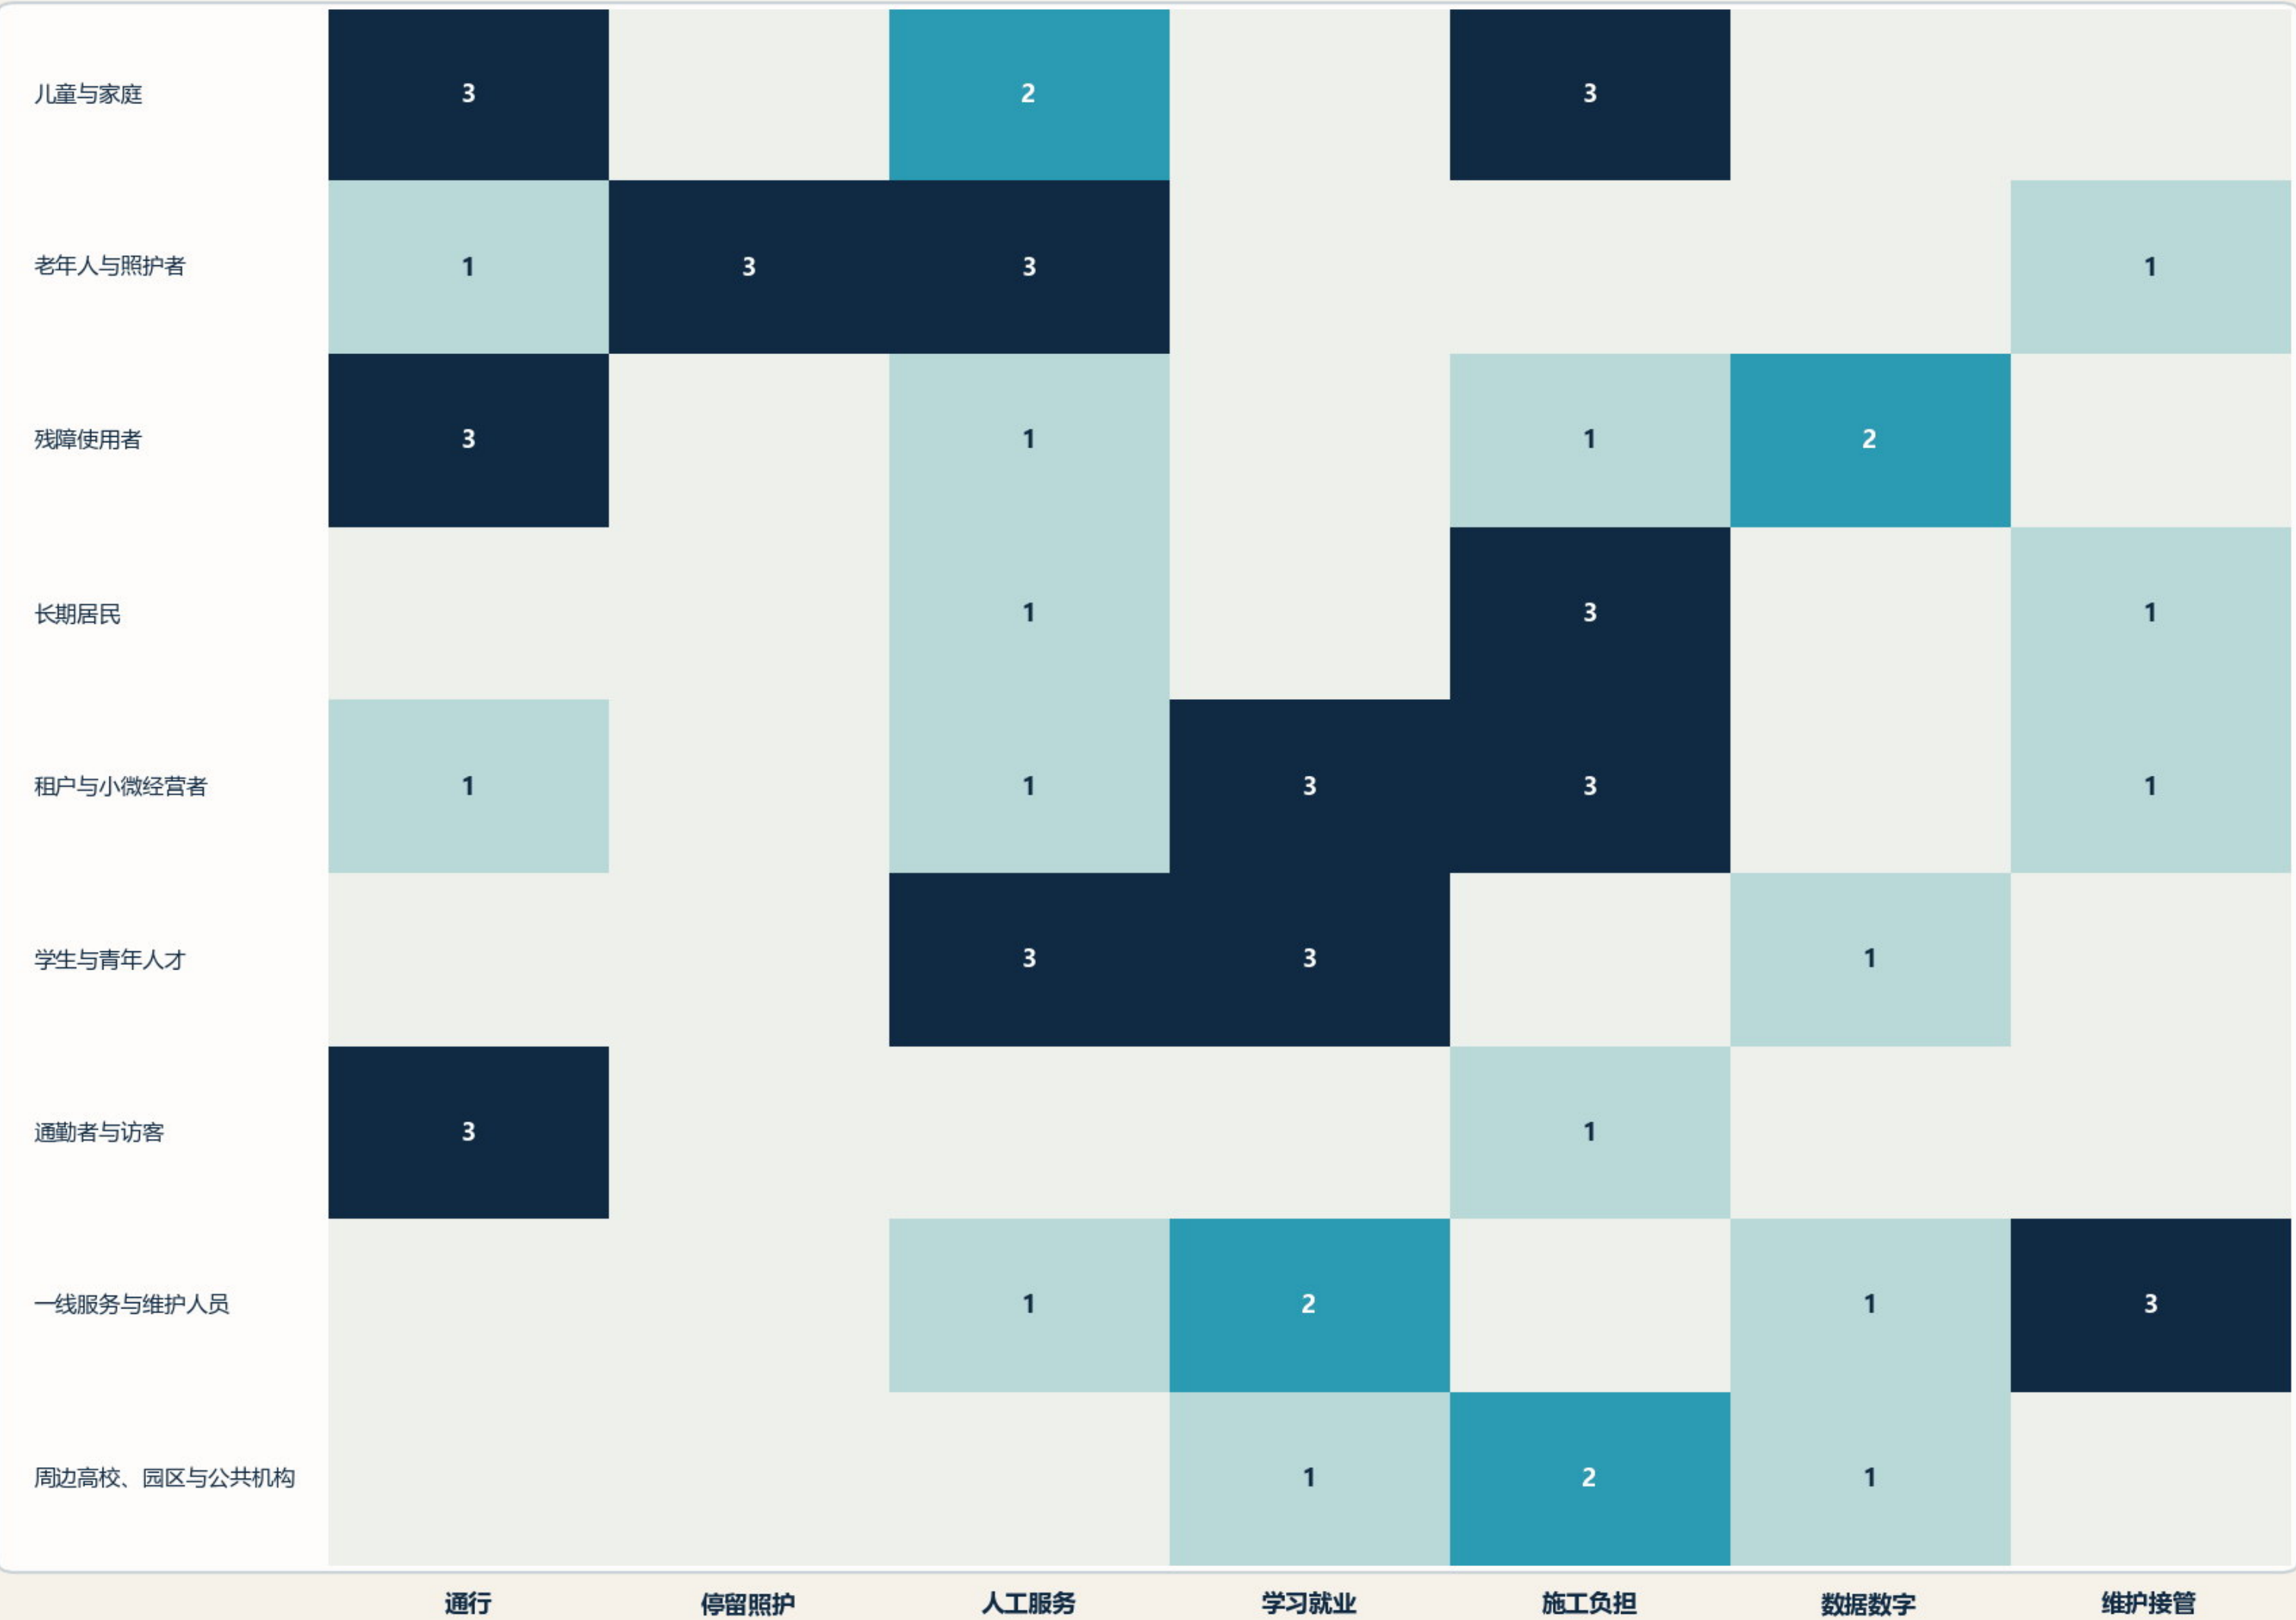

程序性权利

09

人群类别

09

暂缓 / 叫停权记录

00

人口覆盖率主张

缺少经授权的人口与客流分母时，
不计算覆盖率。总体效益须同时公布
分组受益、负担和盲区。

六项行动包：规模、周期与退出条件

以项目组合替代一次性总图承诺

项目组合：周期中值 × 概念成本级 × 时间弹性



交付责任账本

项目	级别	周期	前置	验收	退出
P-01	M	6–18m	3	3	•
P-02	L	12–24m	3	3	•
P-03	L	12–24m	4	3	•
P-04	M	9–18m	3	3	•
P-05	M	6–12m	4	3	•
P-06	S	3–9m	4	3	•

S <500 万 · M 500–2000 万 · L 2000–5000 万

京张创新发展轴典型断面与设施界面

真实尺度控制与空间效果并置



典型慢行断面意向 | 无障碍步行 + 雨水花园 + 双向骑行 + 人工服务

12.0 m 弹性组合

3.0 m

连续步行

2.5 m

雨水花园

4.0 m

双向骑行

2.5 m

服务停留

界面控制

- 01 轨道安全与检修通道
- 02 连续盲道与缘石坡道
- 03 汇水、溢流、退水路径
- 04 停电断网时实体导向

公共服务节点：可拆装构造与运行标准

320 m² 样板节点 | 人工服务、雨水花园、遮阴与基础设施



节点轴测意向 | 20 m × 16 m | 连续无障碍闭环

空间与运营账本

320 m²

样板节点

24–36 m²

人工服务空间

60 s

人工响应目标

24 h


常规故障工单

退场规则

维护经费或人员未落实时撤除设备，保留座椅、遮阴、纸质导向和人工公告。

区域协作接口与证据回执

五类接口均以输入、输出、准入、退出和证明材料定义

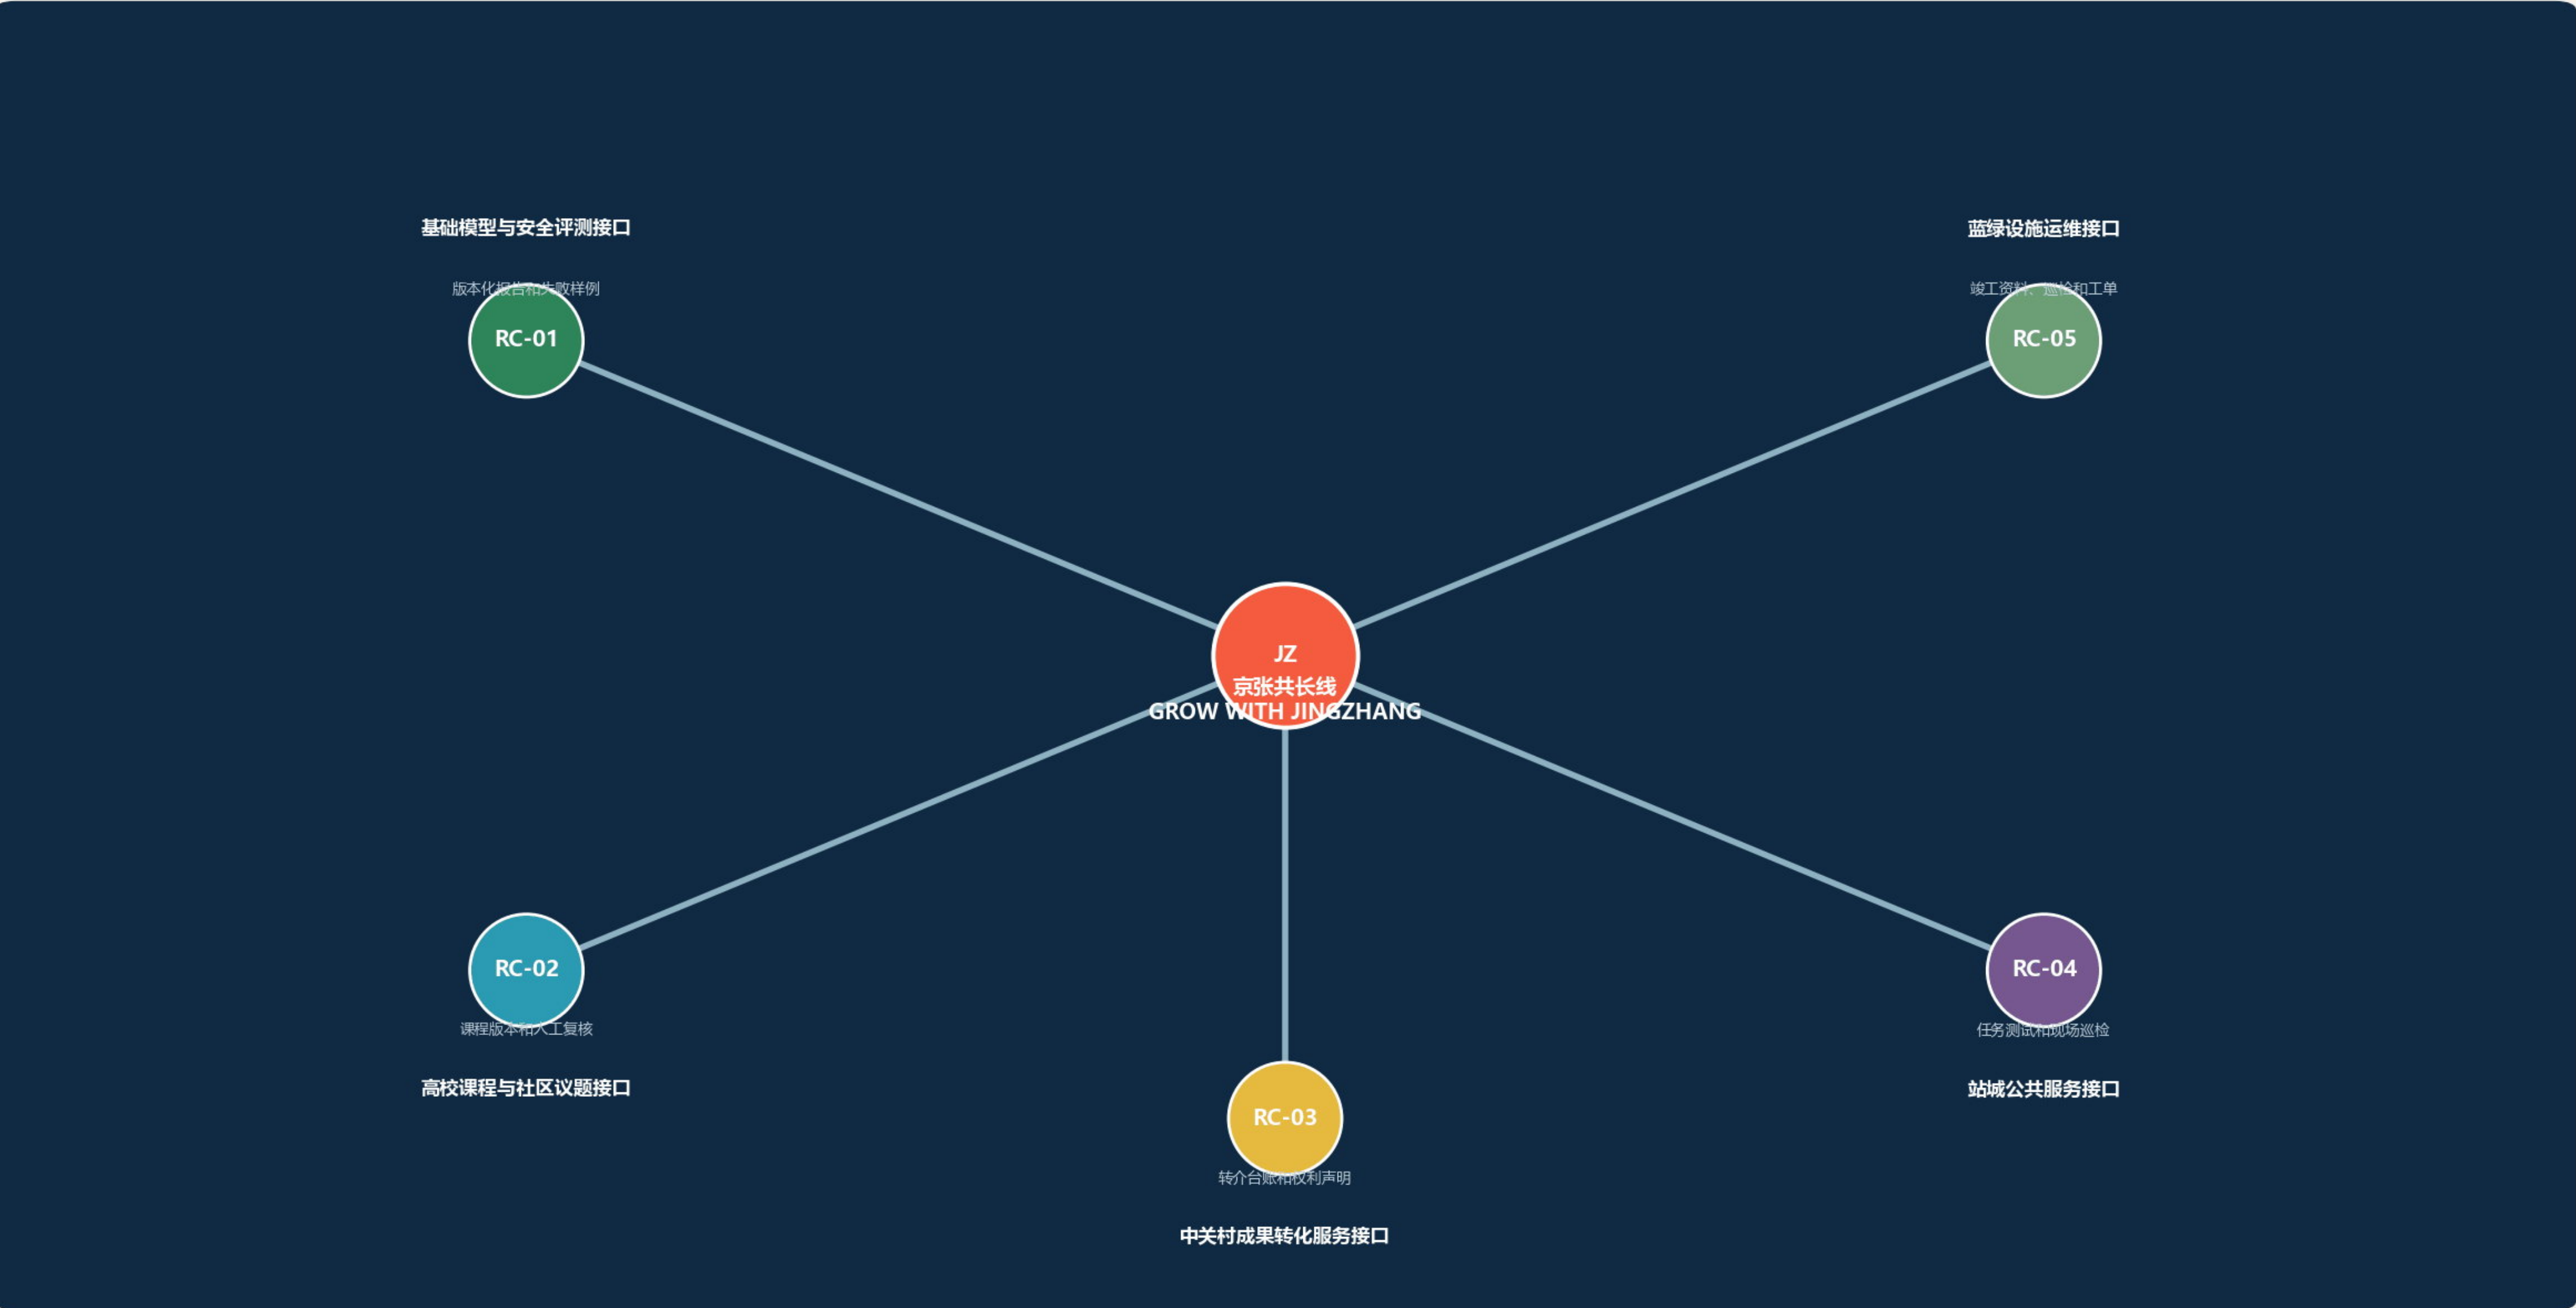

资料来源、权利边界与成果主张

八类资产逐项登记来源、用途和表达边界

资产	来源 / 权利	本方案用途	表达边界
方案文本与翻译	本方案原创文本	叙事与双活交付	政策与标准需要保留出处
技术图件	结构化数据本地生成	评审与公开讨论	示意图不作为法定图
OSM 背景	© OpenStreetMap contributors	网络与城市肌理背景	仅作城市肌理背景并标注来源
NASA 气候基线	NASA POWER 公开数据	2015–2024 概念基线	不替代本地专项模型
Blender 走廊渲染	概念体量本地生成	空间方案展示	不主张建成效果
五张概念场景	OpenAI 图像生成	场所气质参考	人物与材料仅作参考
Three.js 查看器	Three.js / MIT	离线三维浏览	保留 MIT 许可声明
系统字体	系统许可字体	图件与 PDF 嵌入	不单独分发字体文件