


总体空间结构与公共服务骨架

一轴三片、多点支撑 | 真实图层沿廊道长轴展开

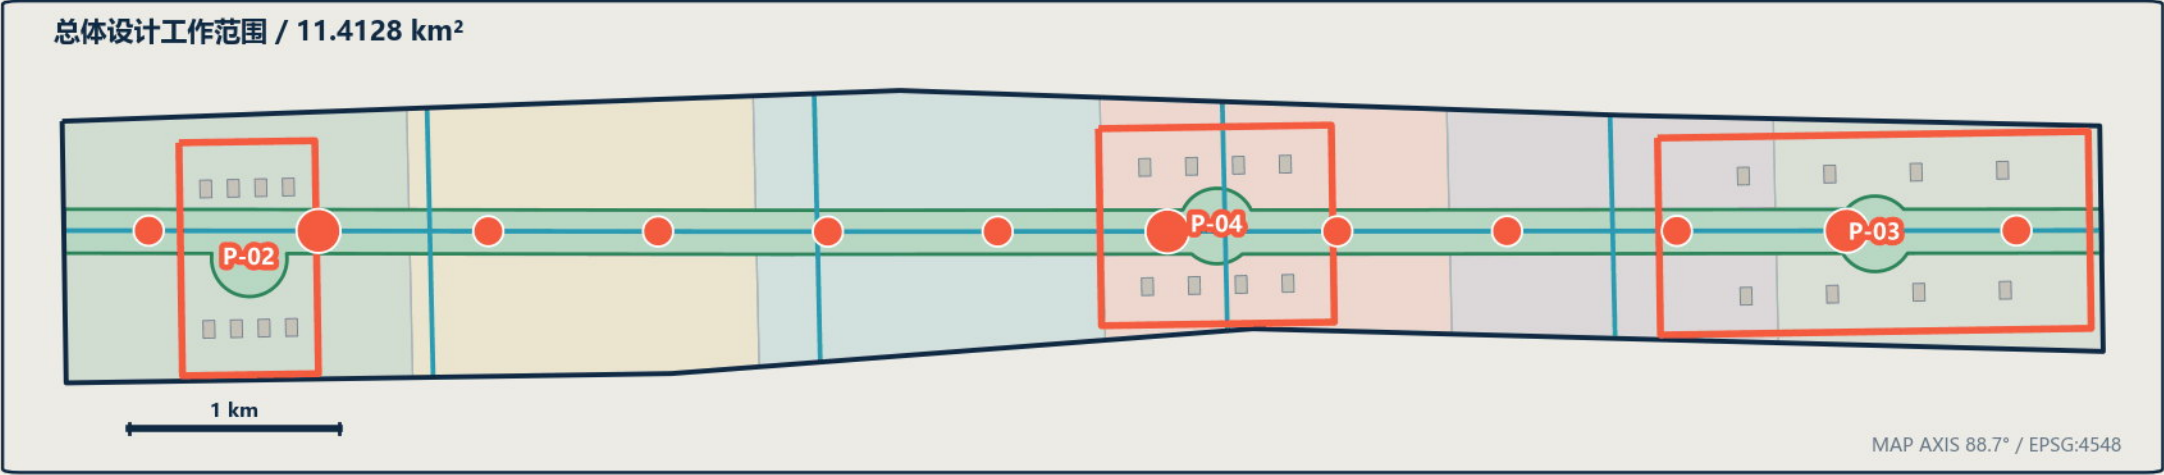

空间—服务—实施一体化摘要

首期动作

- 01 1 km 连续慢行示范段
- 02 3 处公共服务节点
- 03 3,000 m² 共享首层
- 04 1.5 ha 受控验证场

8-80 同等服务

- 01 无需账户、手机或人脸
- 02 人工或非数字路径同等可达
- 03 故障时基本公共服务持续
- 04 责任、接管和退出公开

实施前置

- 01 正式范围与权属
- 02 交通 / 轨道 / 消防
- 03 地下管线与水文
- 04 运营、采购与维护责任

核心空间账本

11.41 km² 3

工作底图复算 重点片区

12 1 km

公共服务节点 首期示范段

图层图例

- 蓝绿公共空间
- 连续慢行主线
- 片区 / 服务节点
- 概念建筑体量

实施门控

- G0 G1 G2 G3 G4

资料—协商—审查—开放—复审

三处重点片区与首期项目

空间账本、首期入口、项目预算与开放条件



共享公共空间意向

可逆构筑、雨水花园、人工服务与全年龄慢行共同构成公共界面。

片区比较矩阵

P-03 众智园创新验证片区

192.1 ha / 192.9 ha

创新验证场

权属和场地许可 · 交通与消防 · 伦理与数据安全

P-04 北京 AI 原点社区协同创新片区

104.3 ha / 104.3 ha

共享首层计划

权属和租约 · 结构与消防 · 运营协议

P-02 大钟寺站城融合片区

72.0 ha / 72.0 ha


站城公共厅先导界面

客流和疏散 · 轨道安全 · 消防

公告面积与底图复算差异均小于 0.5%；正式四至仍由后续法定成果确定。

实施协议、负向测试与退出条件

十二项服务通过八条准入规则；八类缺陷由对应规则拦截

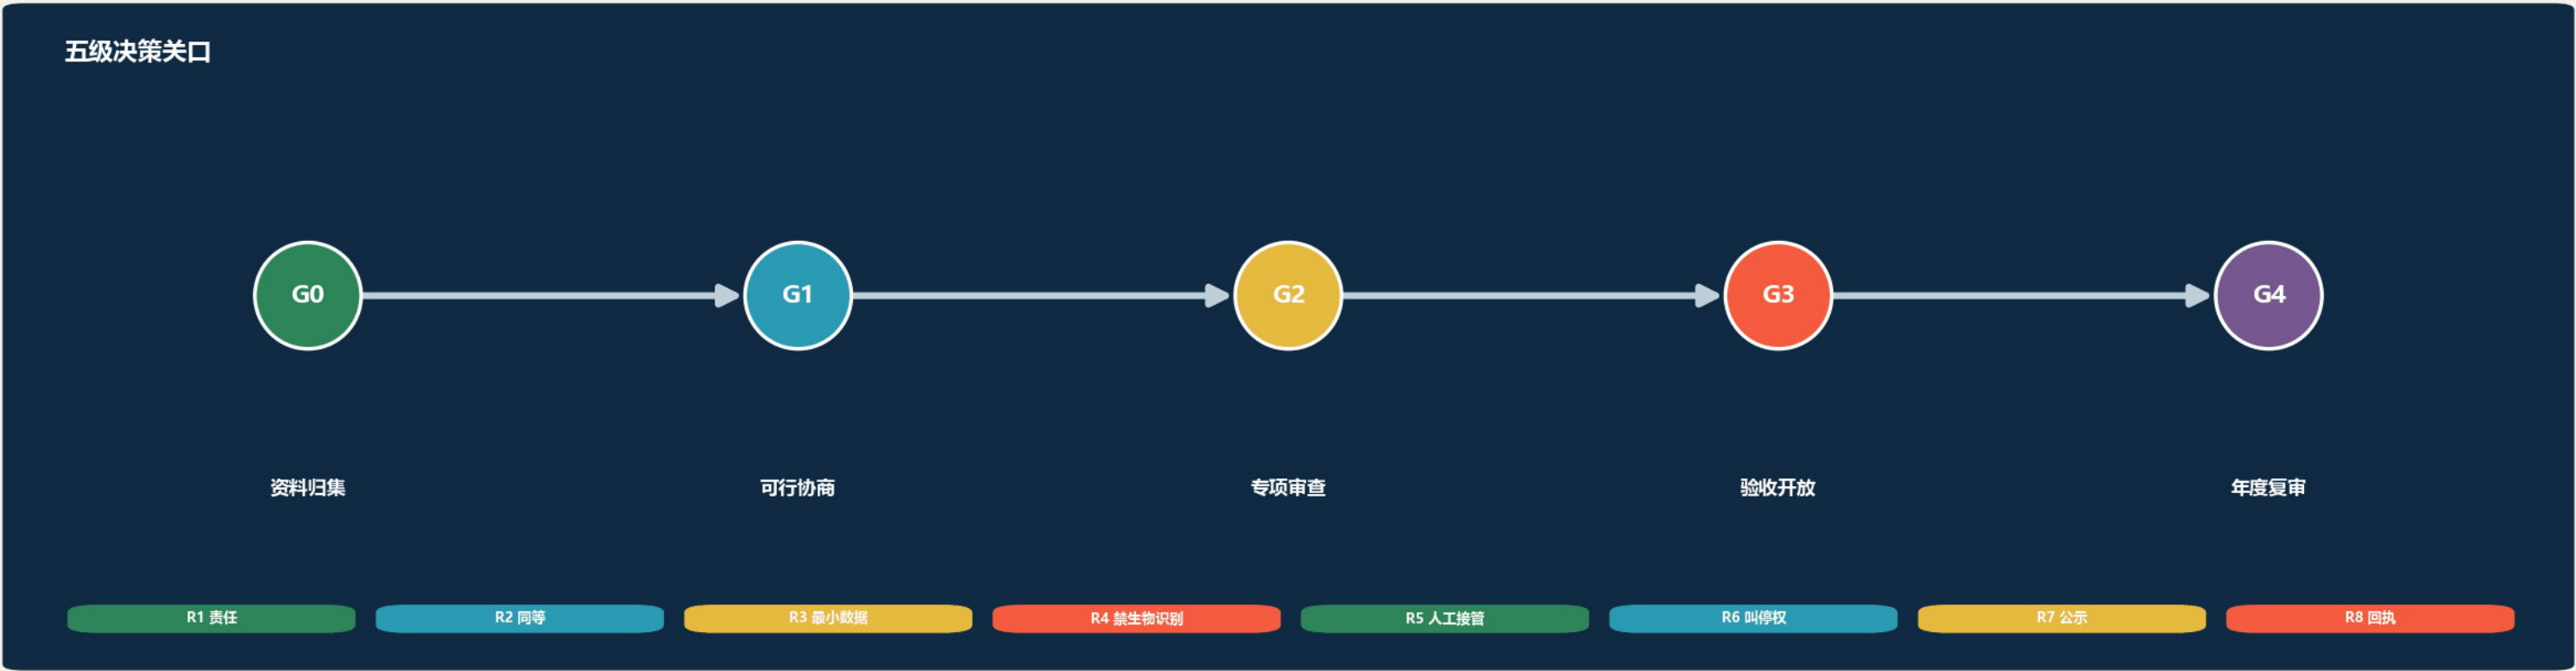

12 项服务 × 8 条规则：全部通过

S01								
S02								
S03								
S04								
S05								
S06								
S07								
S08								
S09								
S10								
S11								
S12								
	R1	R2	R3	R4	R5	R6	R7	R8

12/12

有效服务通过

8/8

缺陷被拦截


0

失效规则

负向测试 X01-X08 分别触发 R1-R8；结果来自可复算桌面协议，不代表项目授权或建成表现。

用地结构与复合功能组织

六类方案分区、面积平衡与实施边界

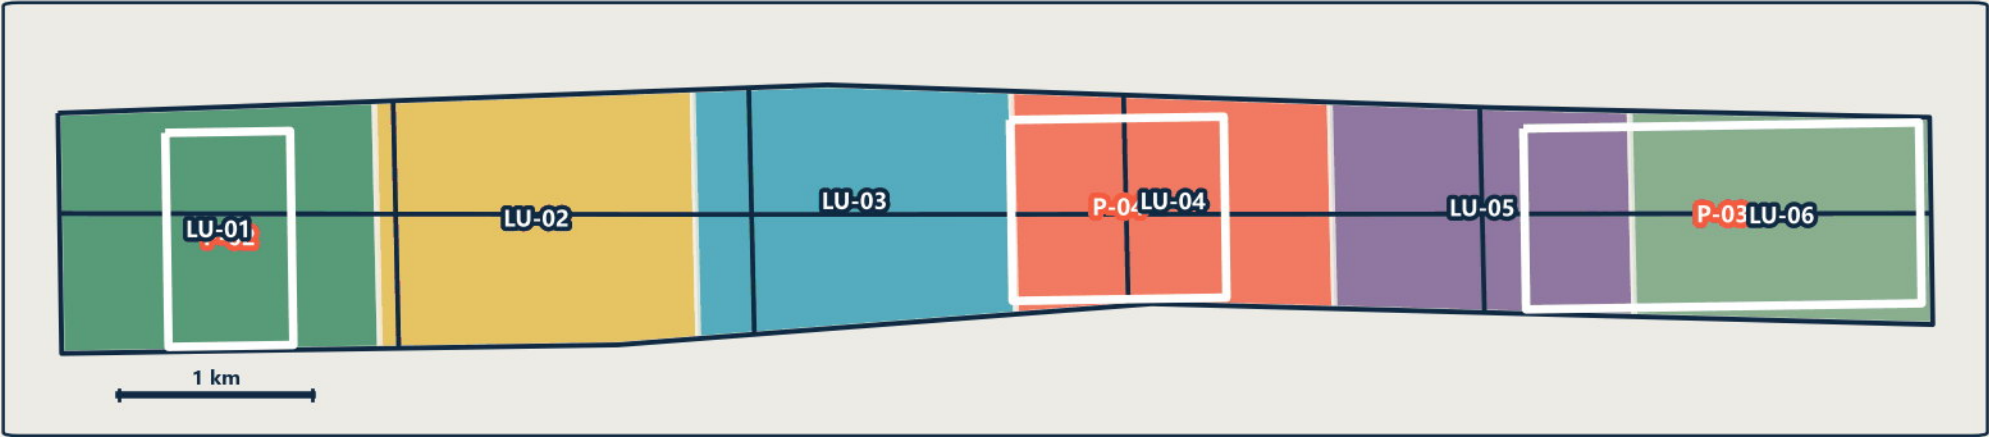

功能结构与实施提示

LU-01 研发与责任测试 208.6 ha / 18.3% 受控测试优先	LU-02 人才居住与照护 214.4 ha / 18.8% 照护设施协同
LU-03 共同学习与转化 204.9 ha / 17.9% 存量首层微改造	LU-04 铁路文化与公共服务 180.8 ha / 15.8% 铁路文化与服务
LU-05 AI 日常服务与商业 166.2 ha / 14.6% 日常服务混合	LU-06 蓝绿韧性基础设施 166.4 ha / 14.6% 海绵设施连续


1141.3 ha 六类方案分区完整覆盖；空白 0、重叠 0。

方案土地平衡

LU-01	208.6 ha	研发与责任测试
LU-02	214.4 ha	人才居住与照护
LU-03	204.9 ha	共同学习与转化
LU-04	180.8 ha	铁路文化与公共服务
LU-05	166.2 ha	AI 日常服务与商业
LU-06	166.4 ha	蓝绿韧性基础设施

慢行、蓝绿与气候适应一体化设计

连续网络、典型断面、气候基线与验收方法

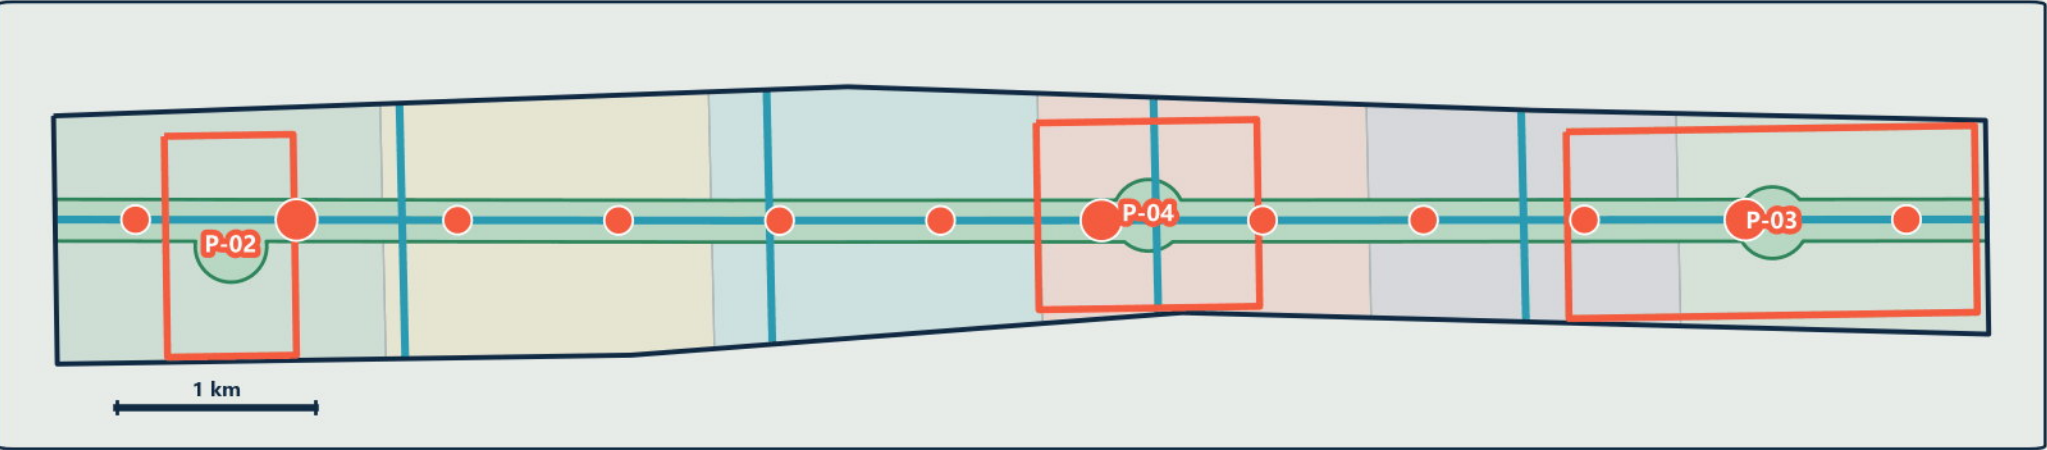


2015–2024 气候基线

35.58°C 日最高温 P95

22.3 d/y ≥35°C 日数

649.1 mm 年均降水

4.05 kWh/m²/日太阳辐射

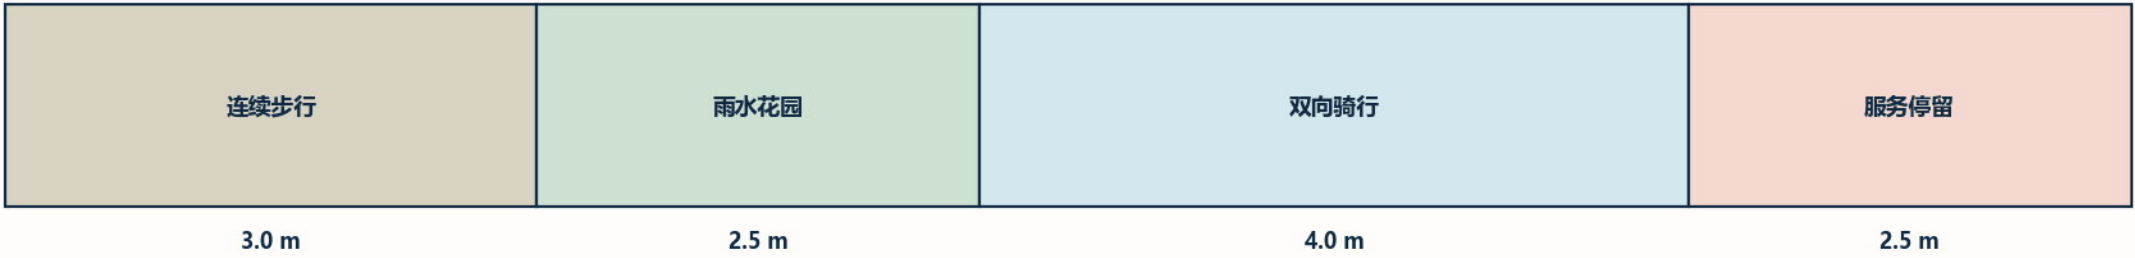


验收要点

- 01 连续净宽实测
- 02 汇水—溢流—退水
- 03 遮阴与休憩间距

指标证据、建议目标与验收责任

九项实施指标按证据类型、测量方法和责任主体组织

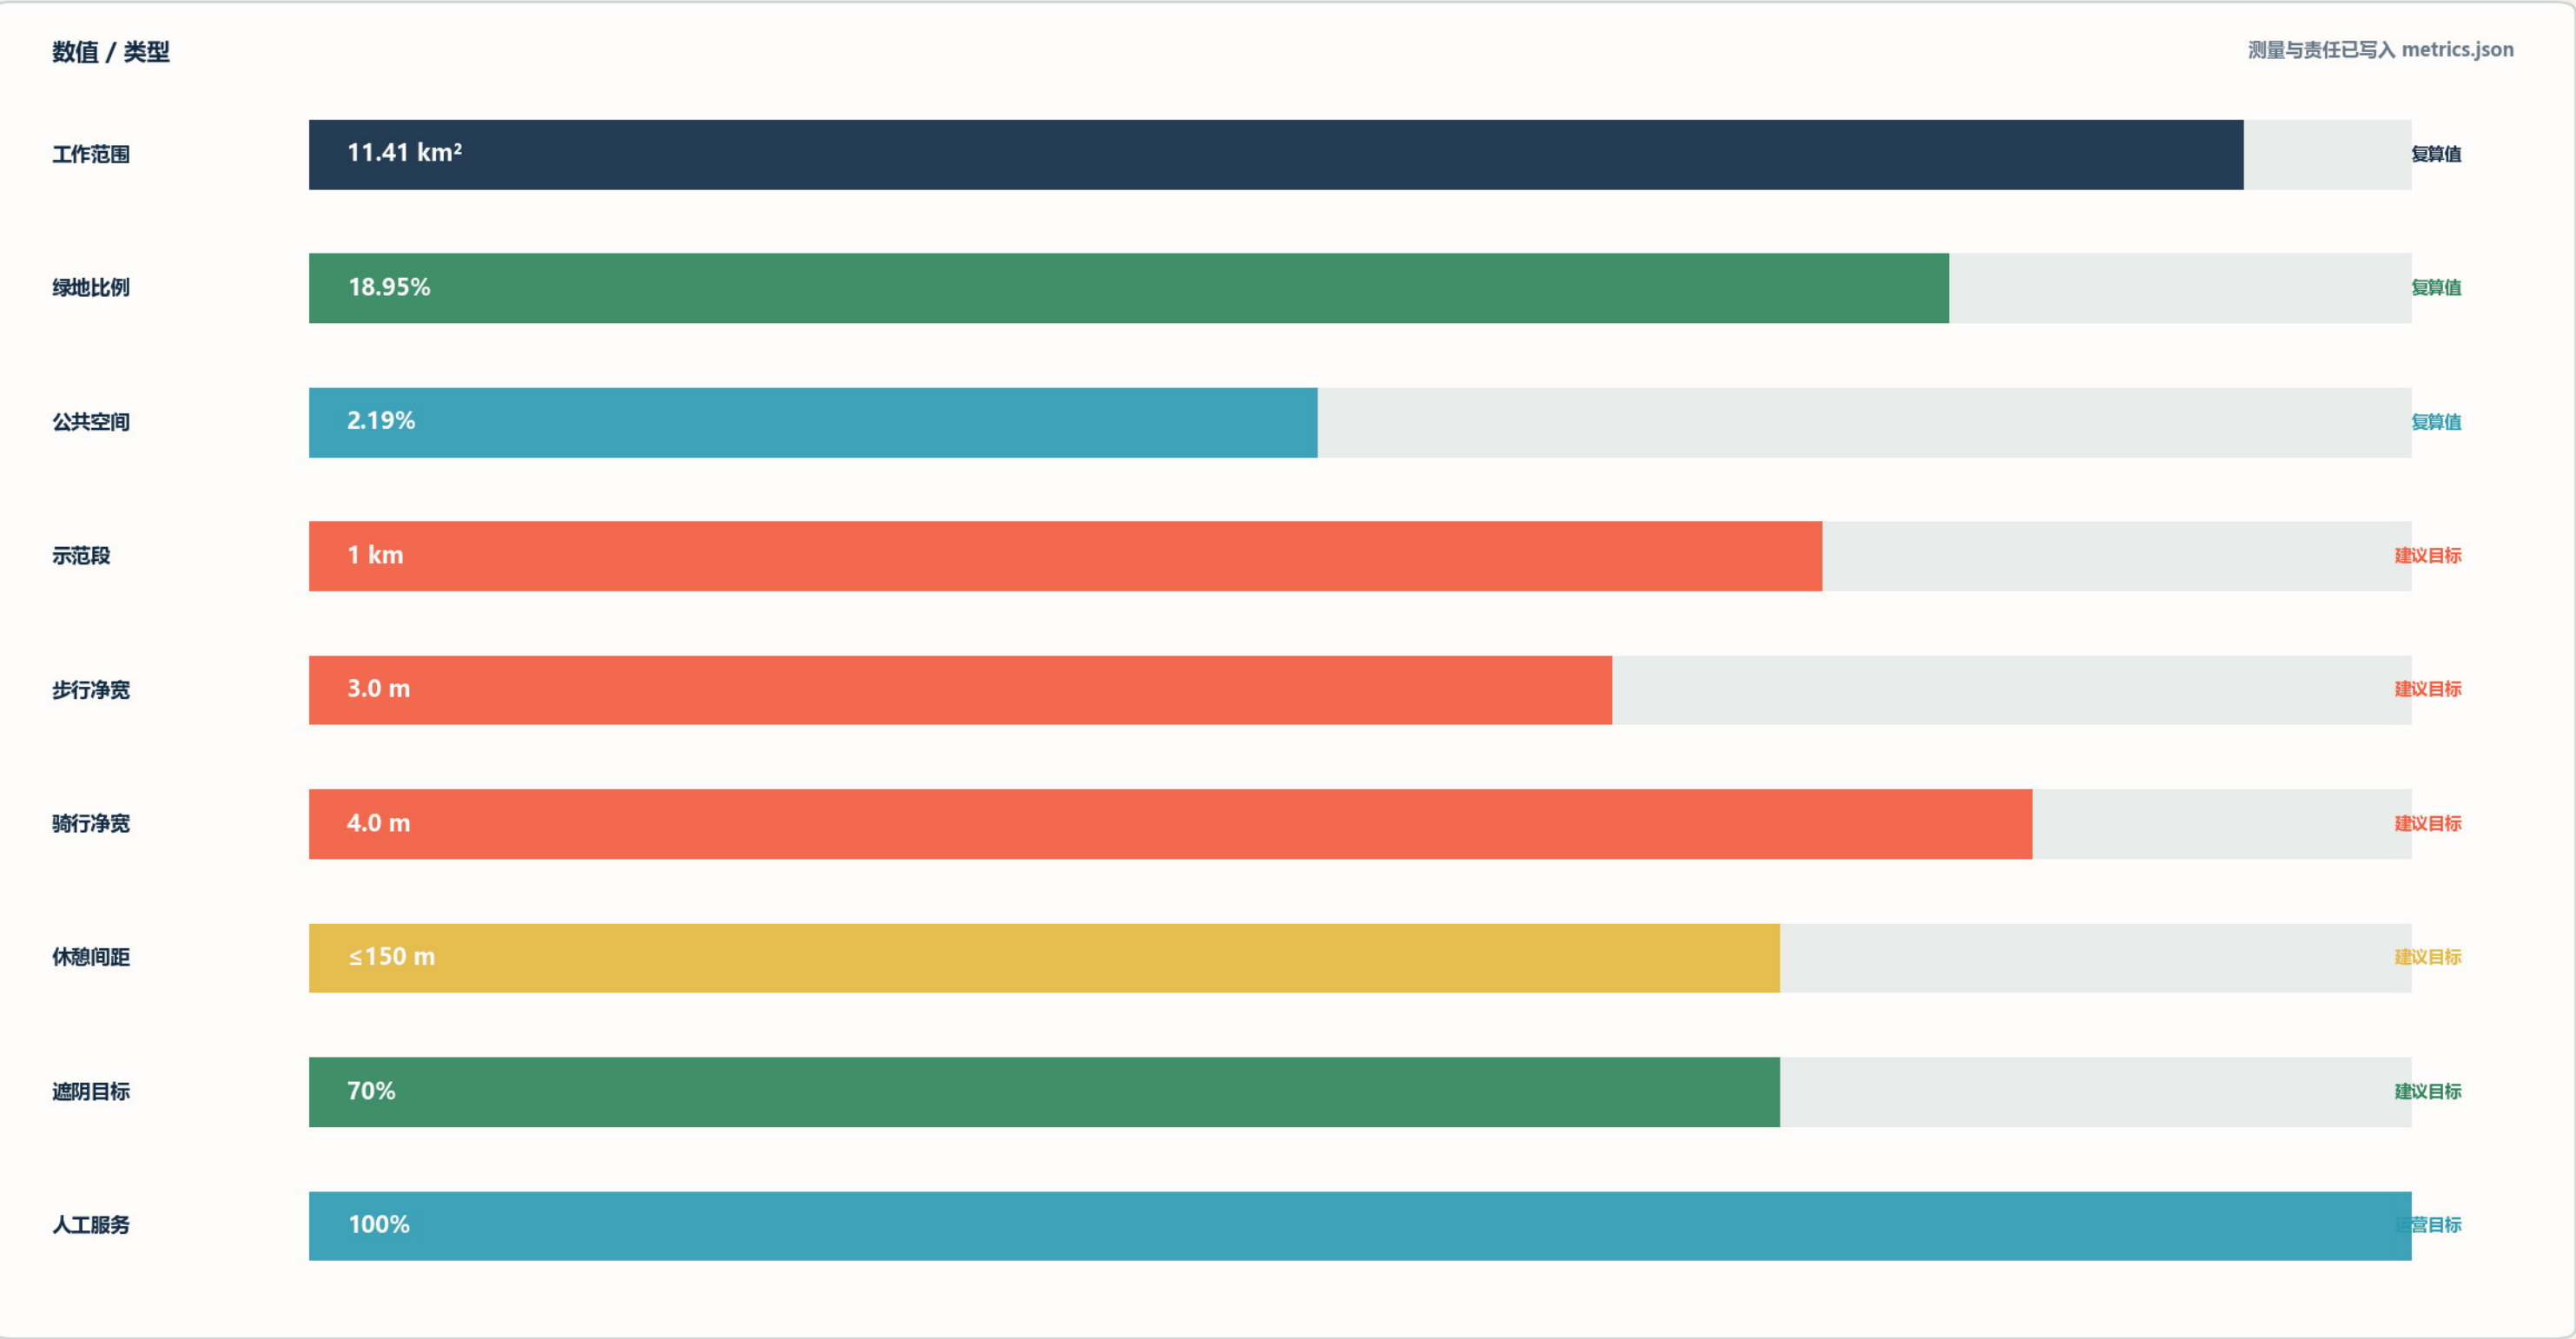

全龄包容性、负担与程序性权利

九类人群同时登记受益、负担、盲区、所需输入和暂缓权
登记议题关联强度 0-3（由台账文本复算）

儿童与家庭	3		2		3		
老年人与照护者	1	3	3			1	
残障使用者	3		1		1	2	
长期居民			1		3	1	
租户与小微经营者	1		1	3	3	1	
学生与青年人才			3	3		1	
通勤者与访客	3				1		
一线服务与维护人员			1	2		1	3
周边高校、园区与公共机构				1	2	1	
	通行	停留照护	人工服务	学习就业	施工负担	数据数字	维护接管

程序性权利

09

人群类别

09

暂缓 / 叫停权记录

00

人口覆盖率主张

缺少经授权的人口与客流分母时，
不计算覆盖率。总体效益须同时公布
分组受益、负担和盲区。

六项行动包：规模、周期与退出条件

以项目组合替代一次性总图承诺
项目组合：周期中值 × 概念成本级 × 时间弹性



交付责任账本

项目	级别	周期	前置	验收	退出
P-01	M	6-18m	3	3	●
P-02	L	12-24m	3	3	●
P-03	L	12-24m	4	3	●
P-04	M	9-18m	3	3	●
P-05	M	6-12m	4	3	●
P-06	S	3-9m	4	3	●

S <500 万 · M 500-2000 万 · L 2000-5000 万

京张创新发展轴典型断面与设施界面

真实尺度控制与空间效果并置



典型慢行断面意向 | 无障碍步行 + 雨水花园 + 双向骑行 + 人工服务

12.0 m 弹性组合

3.0 m

连续步行

2.5 m

雨水花园

4.0 m

双向骑行

2.5 m

服务停留

界面控制

- 01 轨道安全与检修通道
- 02 连续盲道与缘石坡道
- 03 汇水、溢流、退水路径
- 04 停电断网时实体导向

公共服务节点：可拆装构造与运行标准

320 m² 样板节点 | 人工服务、雨水花园、遮阴与基础设施



节点轴测意向 | 20 m × 16 m | 连续无障碍闭环

空间与运营账本

320 m²

样板节点

24–36 m²

人工服务空间

60 s

人工响应目标

24 h


常规故障工单

退场规则

维护经费或人员未落实时撤除设备，保留座椅、遮阴、纸质导向和人工公告。


区域协作接口与证据回执

五类接口均以输入、输出、准入、退出和证明材料定义

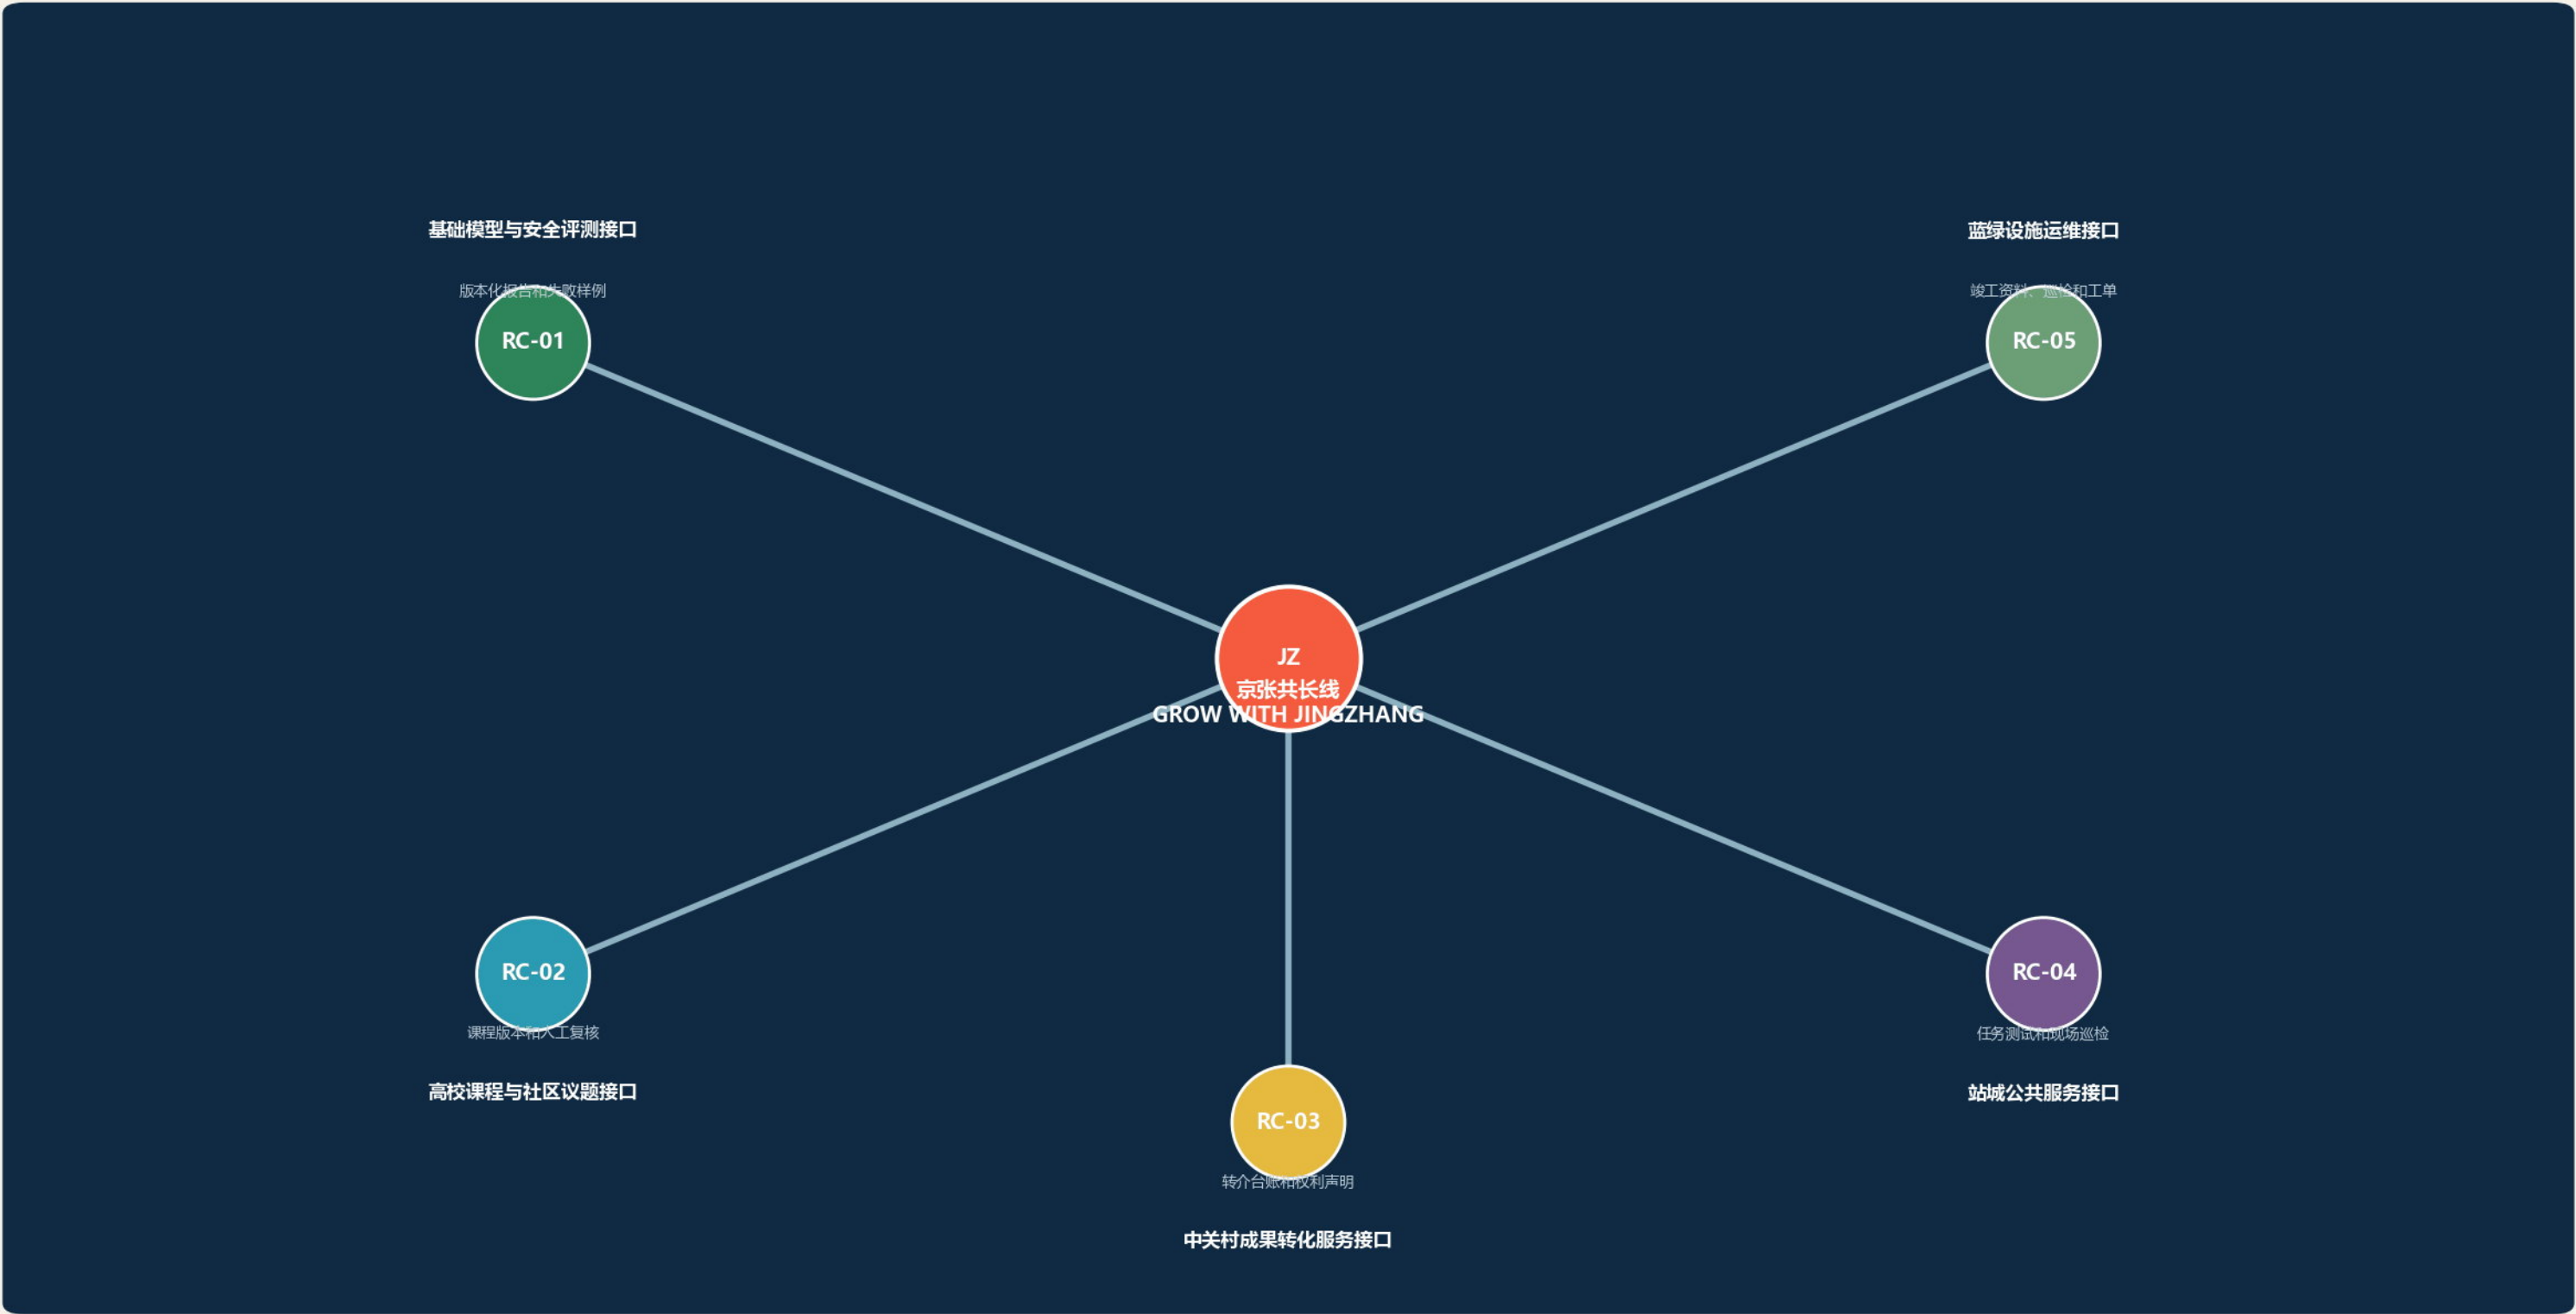

人工智能公共服务治理与人工接管


从提议、测试、公示到运行、复审和退出的责任链

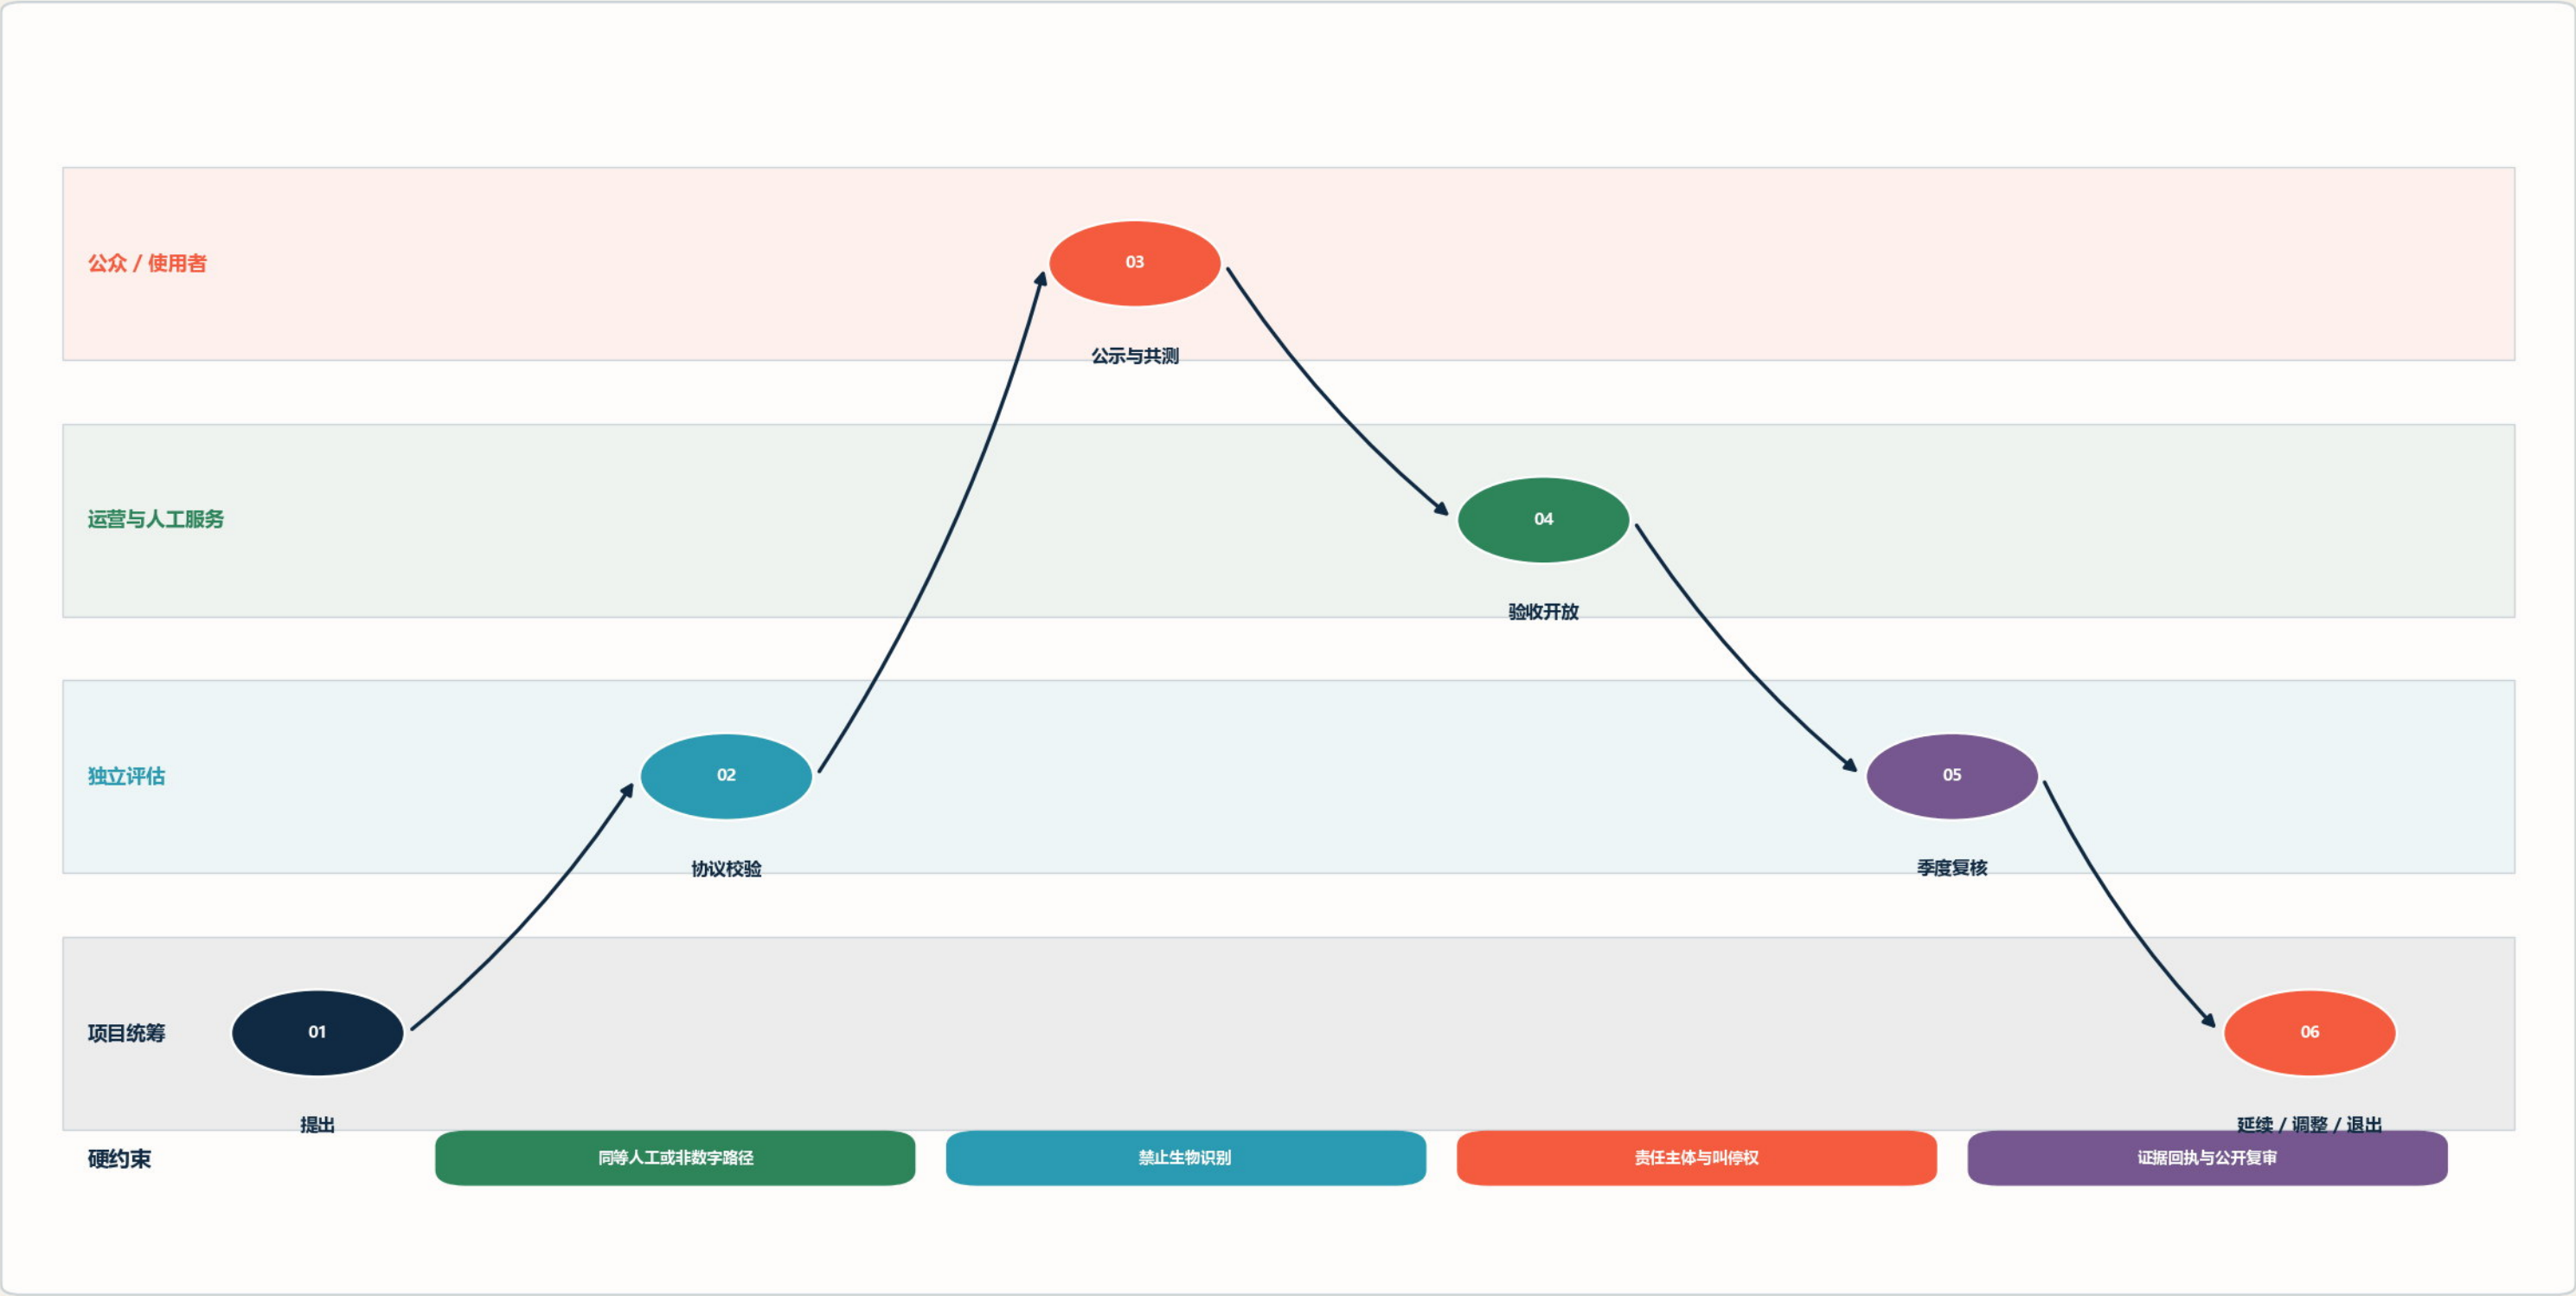

实施时序、决策关口与维护周期

先锁定证据和责任，再进入可逆试点、成段建设与年度复审

0-24 月建议实施窗口

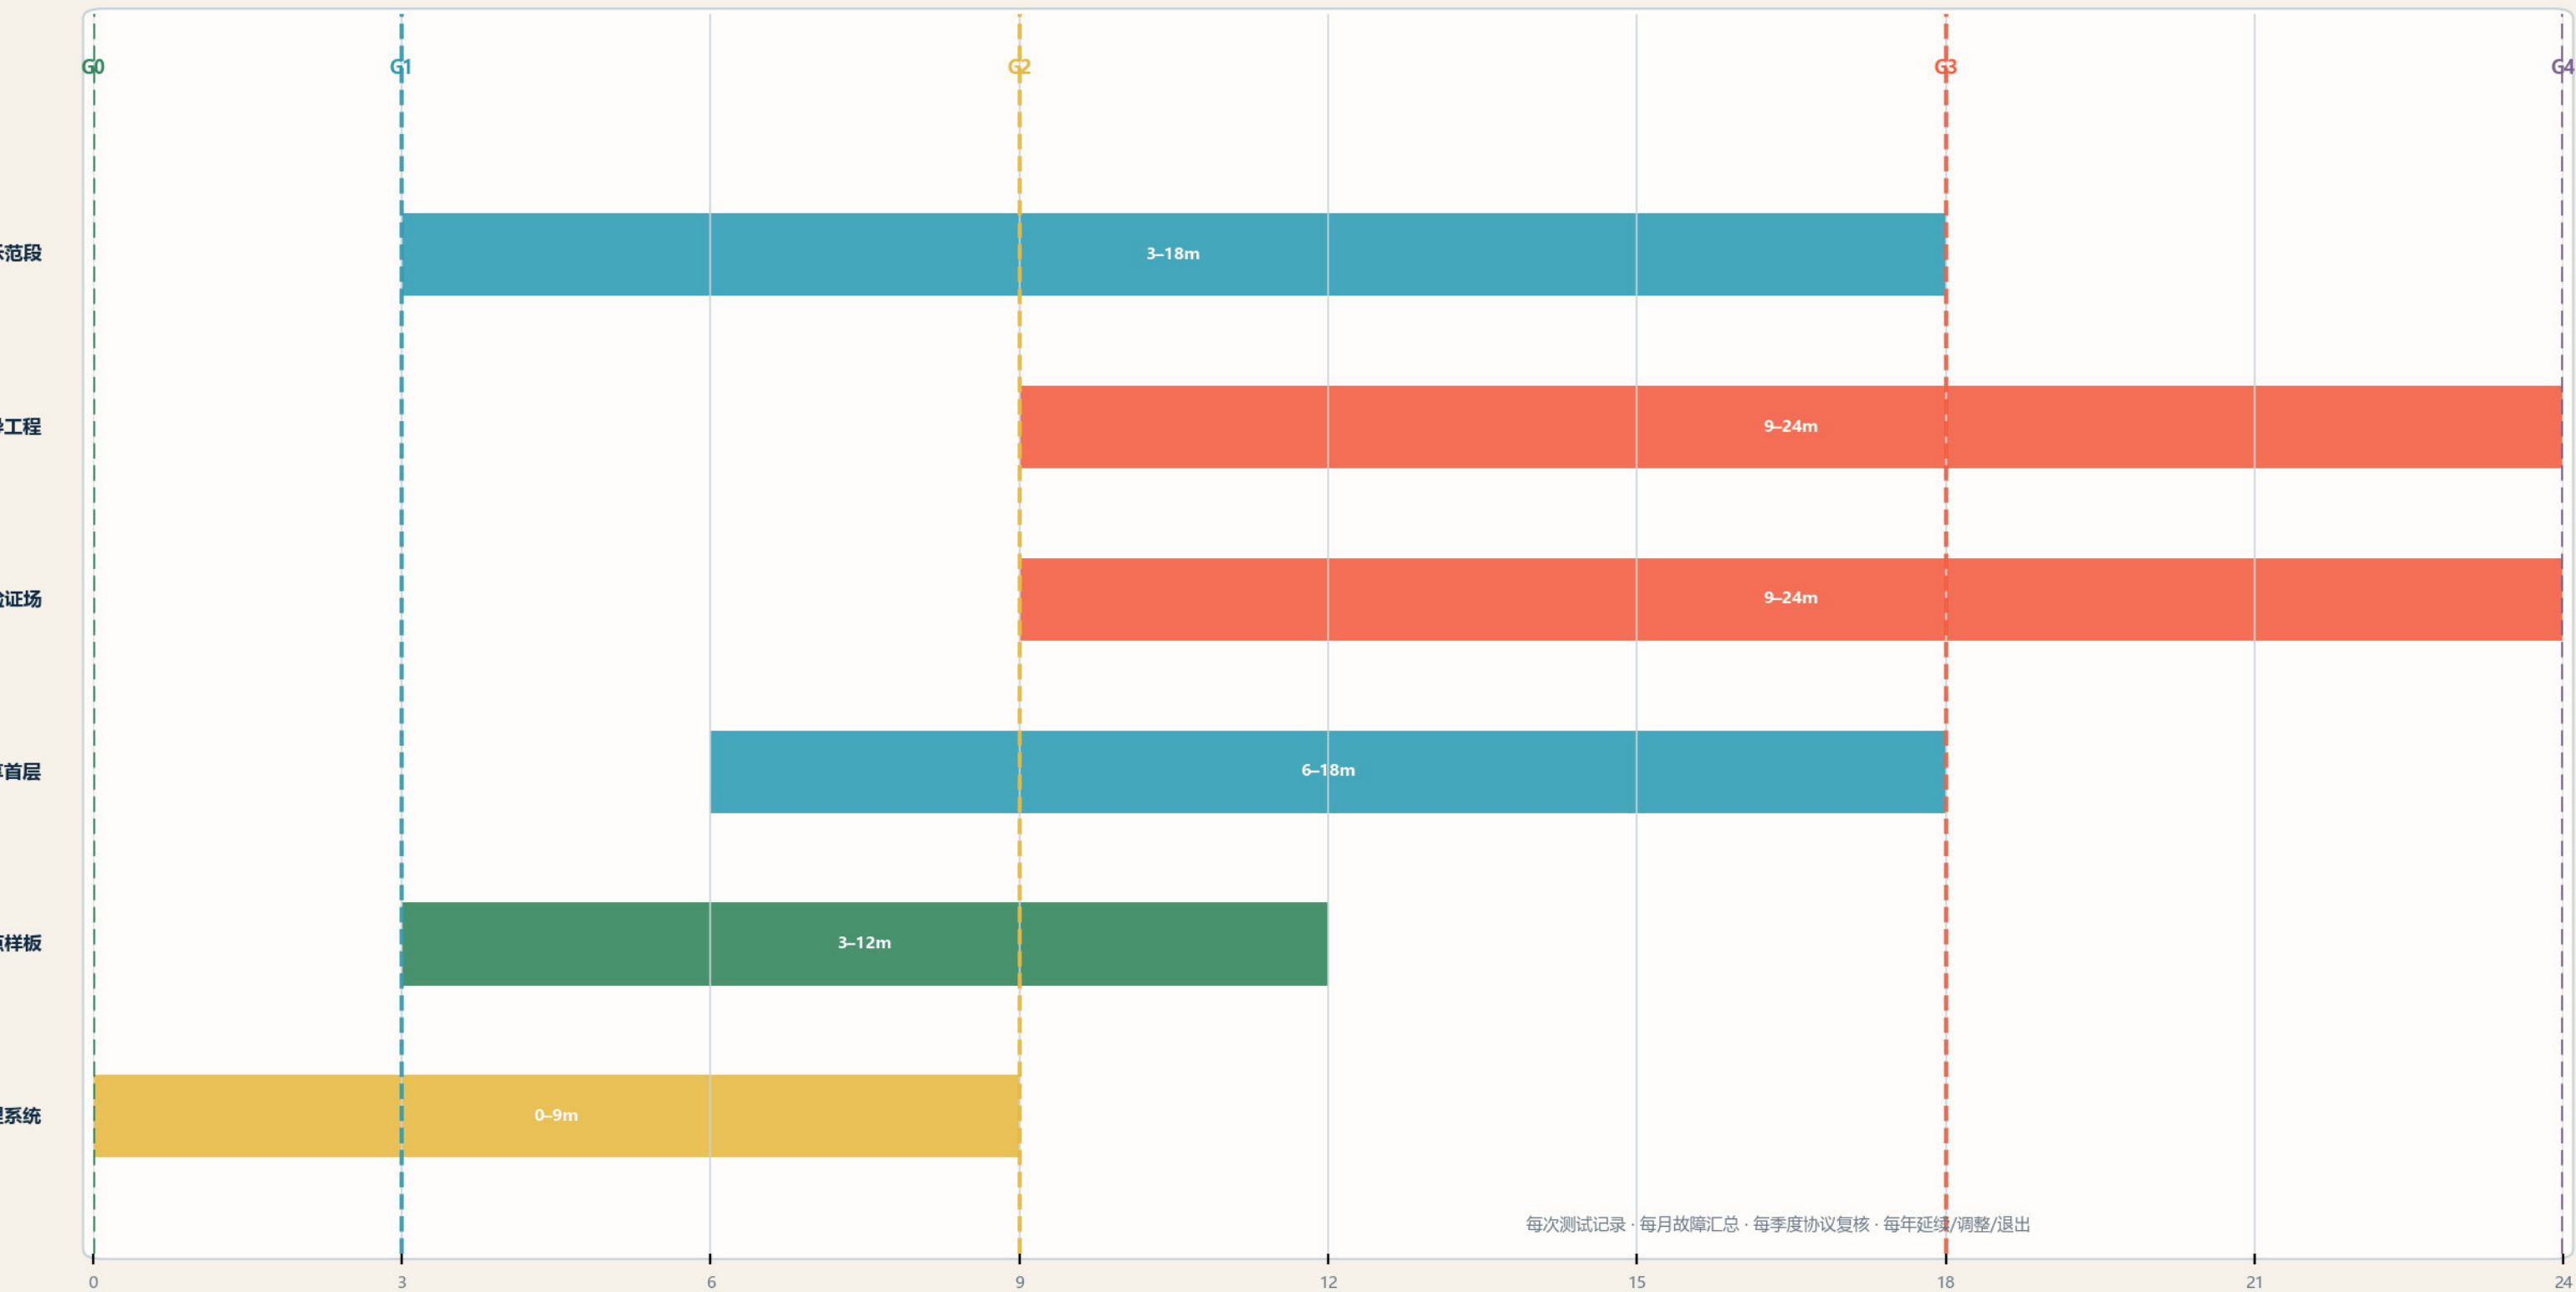

资料来源、权利边界与成果主张

八类资产逐项登记来源、用途和表达边界

资产	来源 / 权利	本方案用途	表达边界
方案文本与翻译	本方案原创文本	叙事与双语交付	政策与标准摘要保留出处
技术图件	结构化数据本地生成	评审与公开讨论	示意几何不作为法定图
OSM 背景	© OpenStreetMap contributors	网络与城市肌理背景	仅作城市纹理背景并标注来源
NASA 气候基线	NASA POWER 公开数据	2015–2024 概念基线	不替代本地专项模型
Blender 走廊渲染	概念体量本地生成	空间方案展示	不主张建成效果
五张概念场景	OpenAI 图像生成	场所气质参考	人物与材料仅作意向
Three.js 查看器	Three.js / MIT	离线三维浏览	保留 MIT 许可声明
系统字体	系统许可字体	图件与 PDF 嵌入	不单独分发字体文件

公共识别系统与信息使用规则

轨线、年轮与人工服务缺口构成统一识别



颜色与职责



轨道墨蓝

#102A43



叶绿 / 公共空间

#2F855A



市民青 / 信息流

#2B9BB3



公共橙 / 责任与停止

#F45B3F



审查金 / 门控

#E6B93F

使用规则

- 01 标识不得与政府机关标志组合使用
- 02 橙色仅用于责任、停止和公共服务提示
- 03 所有 AI 服务点同时显示人工服务符号