


京张向上 总体空间结构与用地规划

展板 01 / 03 · 一脉三台两翼双缝 | 三层范围 | 用地结构

统筹研究范围 43.6 km² | 总体设计范围约 11.41 km² | 三处重点区 369.3 ha | 脉—台—翼—缝

总体设计范围总览平面

范围、用地、绿地与三处重点区域均由本包 geometry/ 图层投影生成；边界为组织方临时粗略范围，不作红线依据。

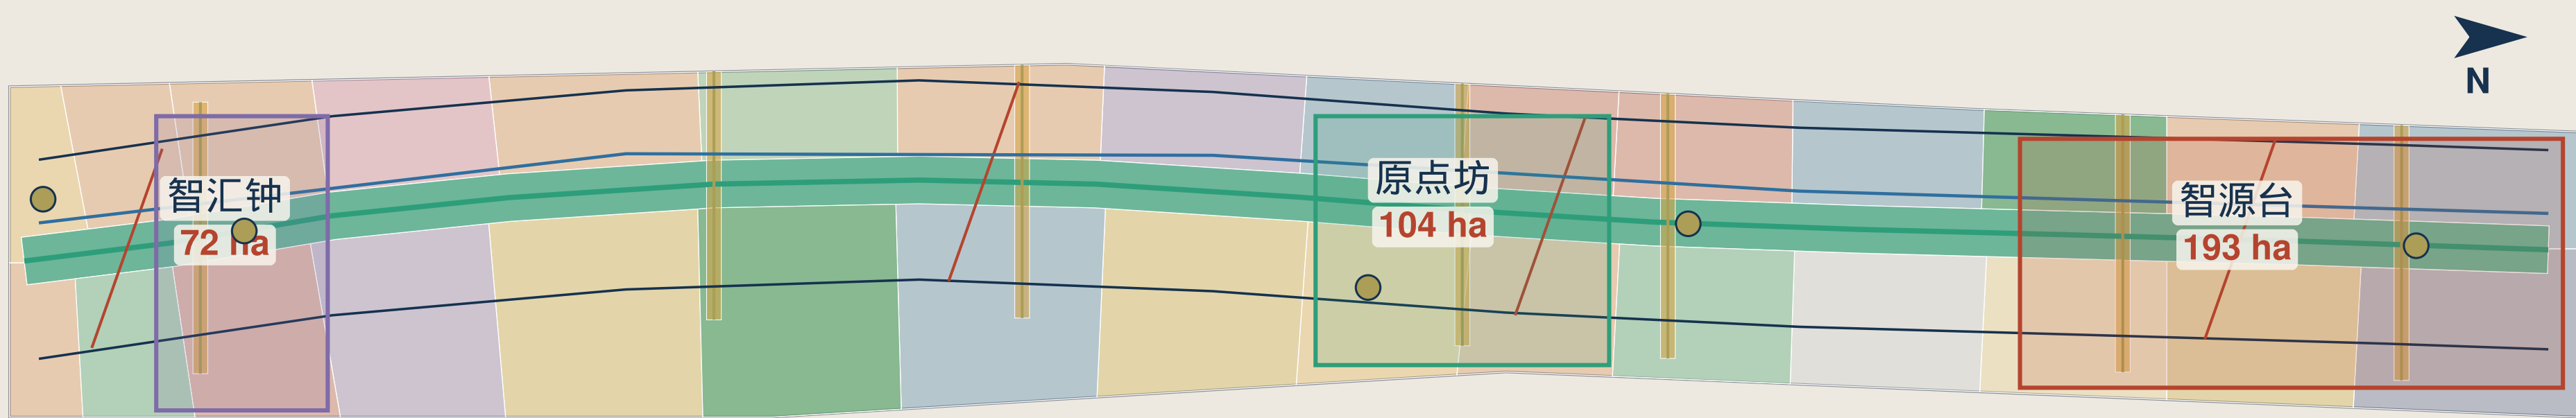

0 500 1000 1500 2000 m

□ 总体设计范围（临时粗略） ■ 重点区域 ■ 遗址公园主脉绿廊 — 主绿道（慢行主轴） — 通勤自行车道 — 东西缝合步行链 — 次干路
— 智站接驳线 ■ 朝圣地标

总体设计范围面积：约 11.41 km²（临时设计模型，随官方边界发布后重算）


site-overview

图 01 总体空间结构（一脉三台两翼）

- 历史母题：唐天佑 1909 年“人”字形展线的自主精神，转译为当代 AI 自主创新。
- 四处朝圣地标：人字台（1909）、赶考门（1949）、算力之钟（1980）、原点碑（2026）。
- 两翼：中关村科技服务翼（西）+ 小月河场景创新翼（东）。

用地结构平面（街区级）

31 个地块按用地代码着色，图例与面积统计均由 land_use.geojson 复算。

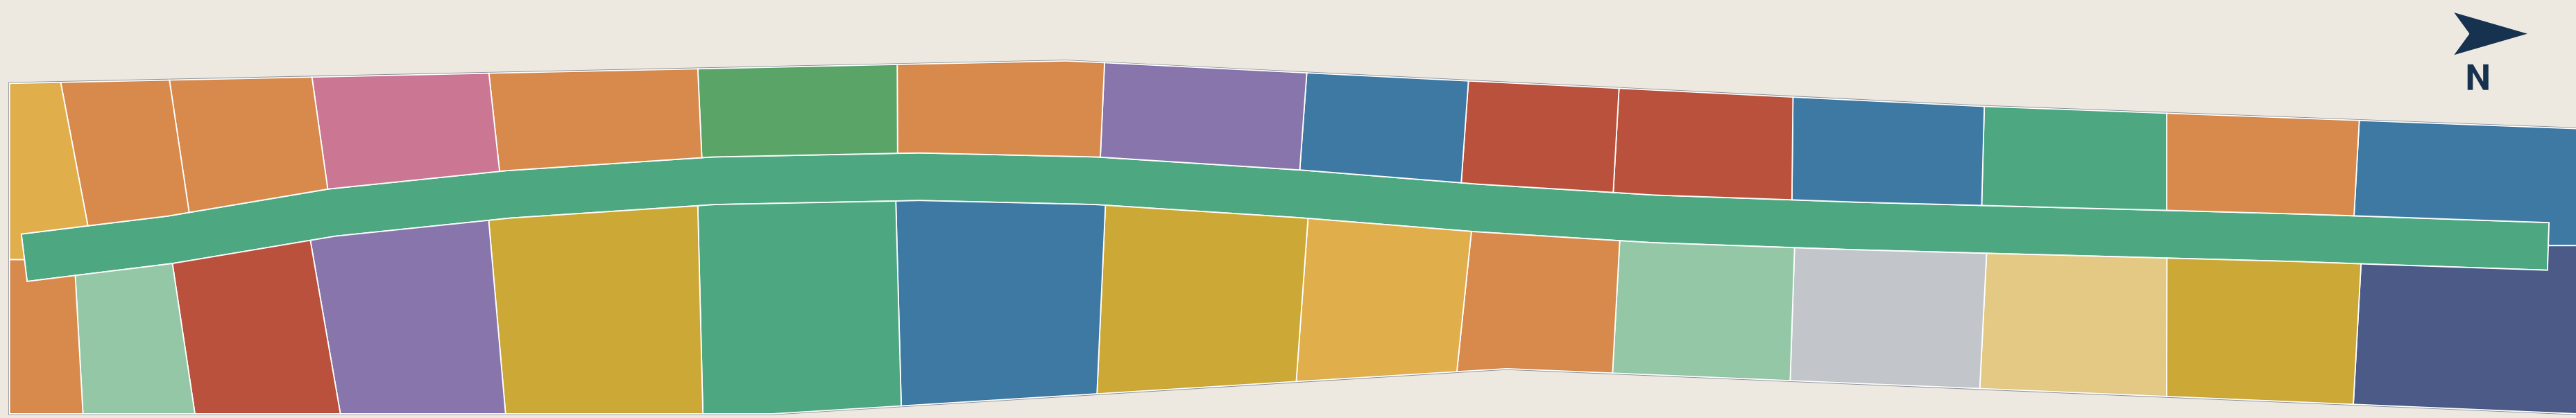

0 500 1000 1500 2000 m

■ 公园绿地 ■ 商业服务业用地 ■ 城镇住宅用地 ■ 科研用地 ■ 文化用地 ■ 教育用地 ■ 防护绿地 ■ 广场用地
■ 公共管理与公共服务用地 ■ 留白用地 ■ 城镇社区服务设施用地 ■ 医疗卫生用地 ■ 体育用地

用地面积统计（由 land_use.geojson 复算）

代码	用地类别	面积 (ha)	占比
1401	公园绿地	257.1	22.5%
05	商业服务业用地	169.7	14.9%
0701	城镇住宅用地	147.0	12.9%
0802	科研用地	138.7	12.2%
0803	文化用地	81.8	7.2%
0804	教育用地	73.1	6.4%
1402	防护绿地	55.1	4.8%

代码	用地类别	面积 (ha)	占比
1403	广场用地	49.4	4.3%
08	公共管理与公共服务用地	45.7	4.0%
16	留白用地	36.5	3.2%
0702	城镇社区服务设施用地	35.9	3.1%
0806	医疗卫生用地	26.4	2.3%
0805	体育用地	25.0	2.2%

合计 1141.3 ha (31 个地块)

land-use-structure

图 02 用地结构与锚点服务范围划分

- 完整划分：4 处智站 TOD 与 14 个创新锚点服务范围无缝划分约 11.41 km²。
- 功能平衡：研发创新实验室、教育协同、人才住房与连续蓝绿公园。
- 严格完整性：无缝隙、无重叠；依据 geometry 图层在 EPSG:4548 下复算。
- 31 个地块合计 1,141.3 ha，与 metrics.json 的 site_area_sqm 同源。

京张向上 三处重点区域详细设计


展板 02 / 03 · 智源台 193 ha | 原点坊 104 ha | 智汇钟 72 ha

15 个街区概念区间 | 容积率与限高建议 | 答卷亭布点

三处重点区域放大平面

街区轮廓=地块边界；公共空间、主要街道与答卷亭点位均落位于图上（点位示意）。


智源台 Origin Terrace

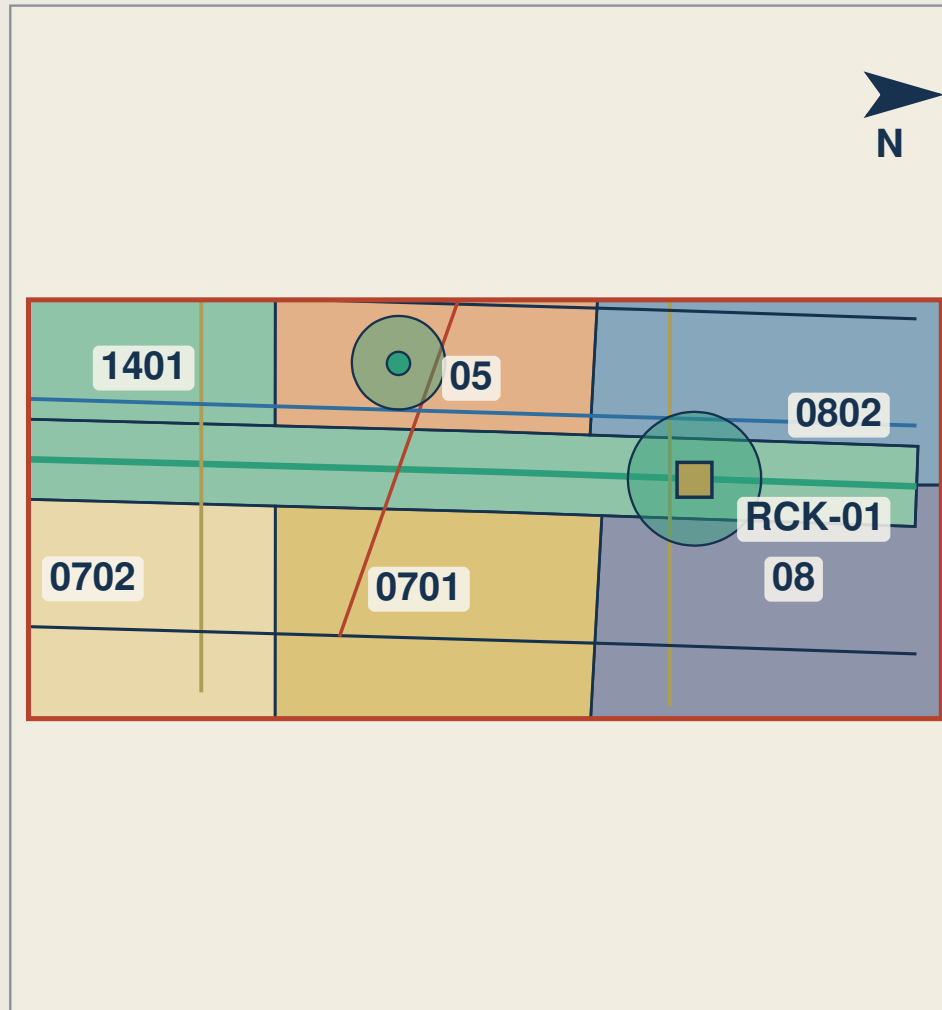

片区面积 192.92 ha

0 400 800 m


原点坊 Origin Works

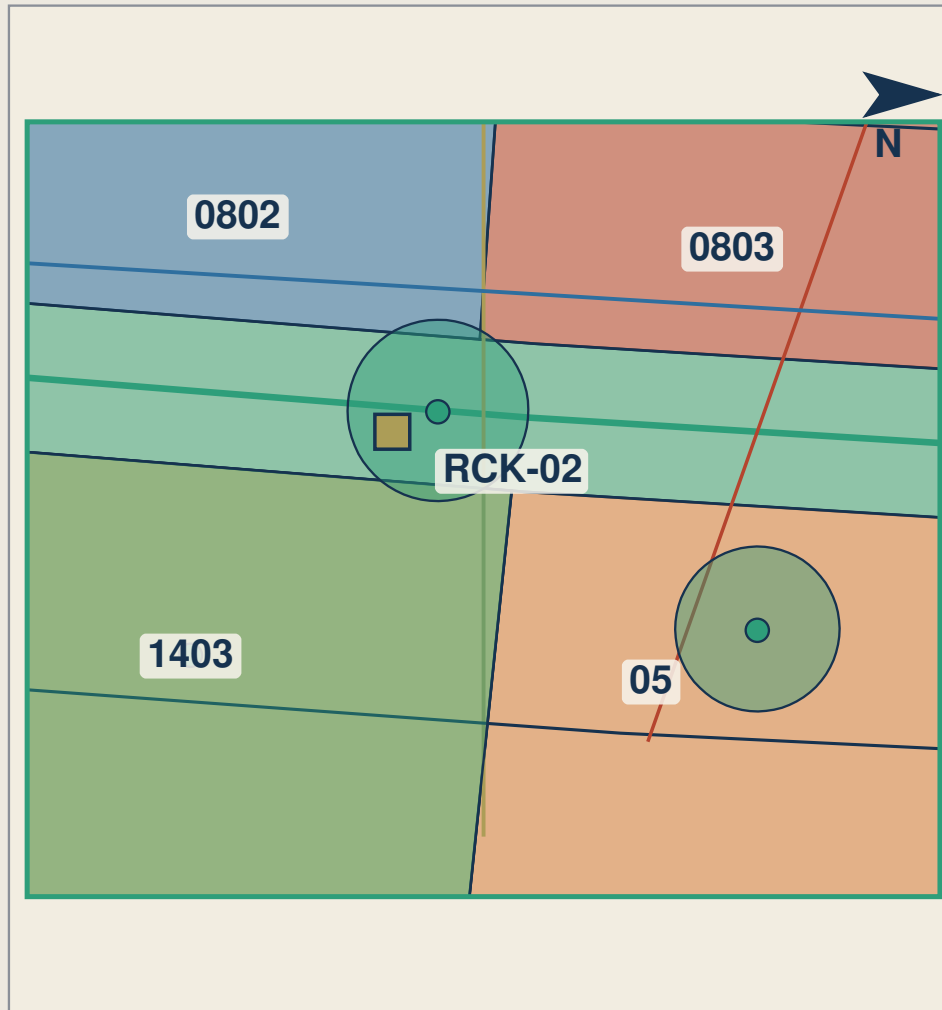

片区面积 104.32 ha

100 300

智汇钟 Bell Hub

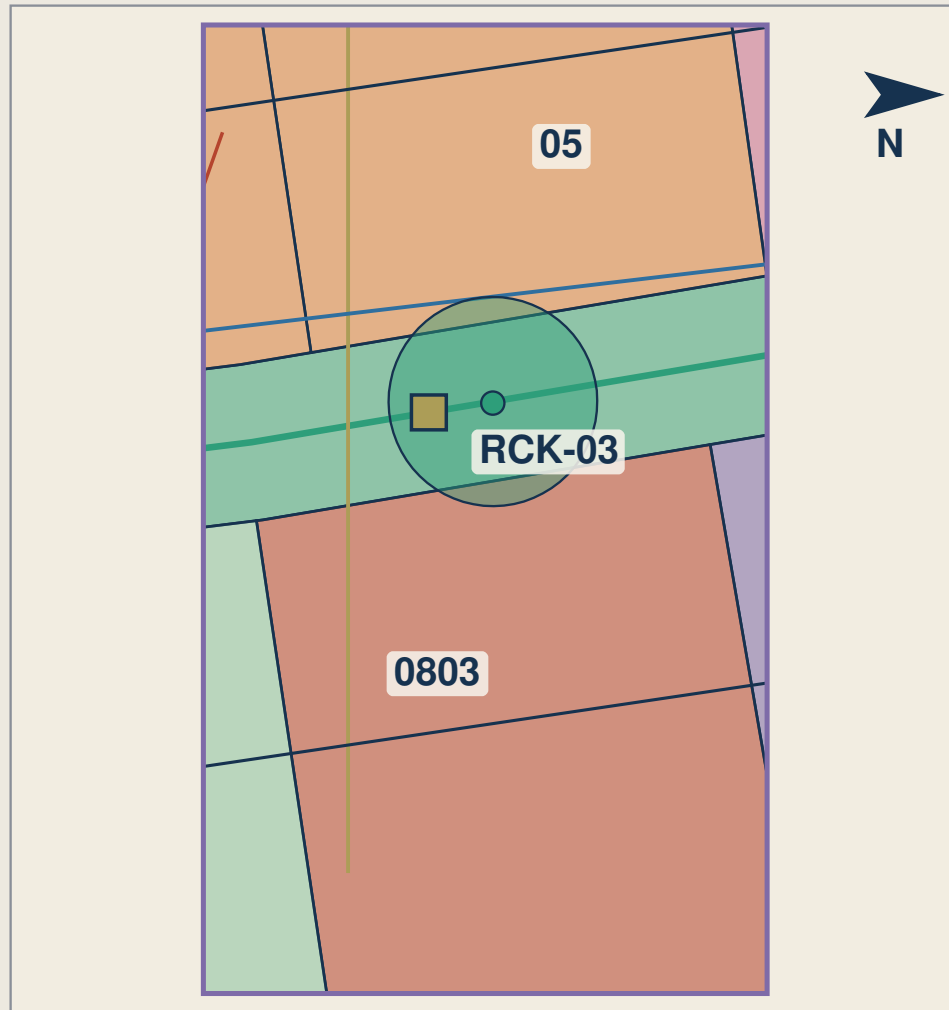

片区面积 72.05 ha

0 200 400 m


街区轮廓（地块） 公共空间节点 主要街道 答卷亭点位

街区轮廓标注为用地代码；答卷亭点位取自 proposal.md 部署计划表。

key-areas


片区平面（示意，非红线）

复算：片区 192.92 ha | 慢行 5,791 m | 密度 30.0 m/ha | 绿地率 29.9%

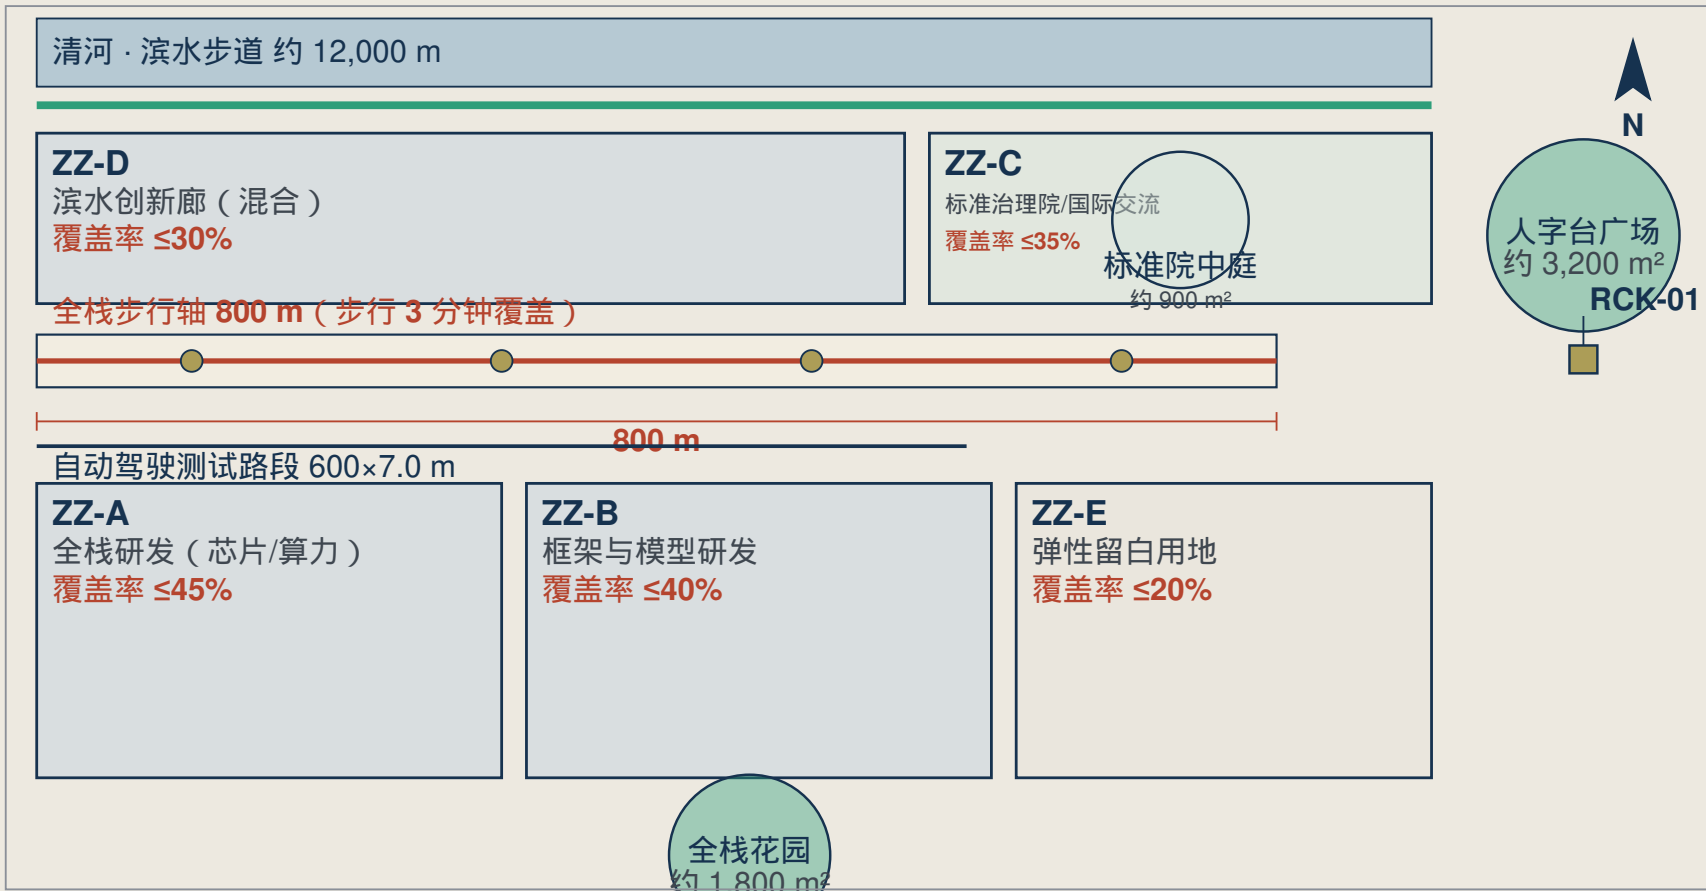

街区（含覆盖率上限） 慢行主轴 公共空间节点 答卷亭点位 水系

全栈步行轴断面（ZZ-A—ZZ-B 段）

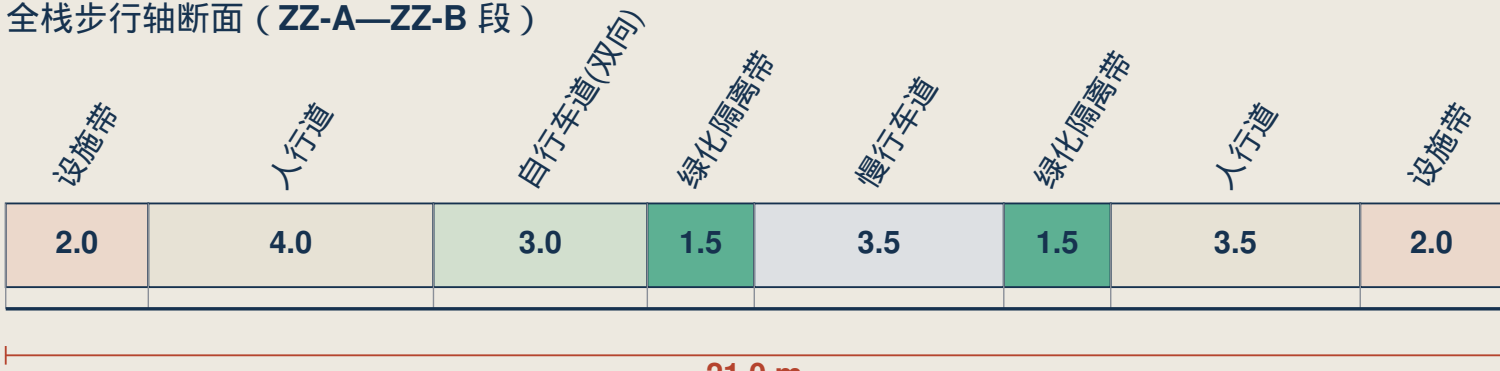

步行优先，非机动车主通道；服务车辆 ≤20 km/h，树冠覆盖 ≥70%。

边界为组织方临时粗略范围，仅概念建议，不作红线或精确面积依据。


key-areas-zhongzhiyuan

智源台（众智园，193 ha）

- 街区：ZZ-A 前沿实验室、ZZ-B 孵化、ZZ-C 人才住房、ZZ-D 服务、ZZ-E 绿地。
- 概念建议：容积率 1.6–3.5，限高 24–60 m，覆盖率 ≤35%。
- 公共锚点：人字台纪念 + 清河智站 TOD + RCK-01 答卷亭。
- 慢行：密度 30.0 m/ha，长度 5,791 m。


片区平面（示意，非红线）

复算：片区 104.32 ha | 慢行 3,092 m | 密度 29.6 m/ha | 公共空间占比 34.4%

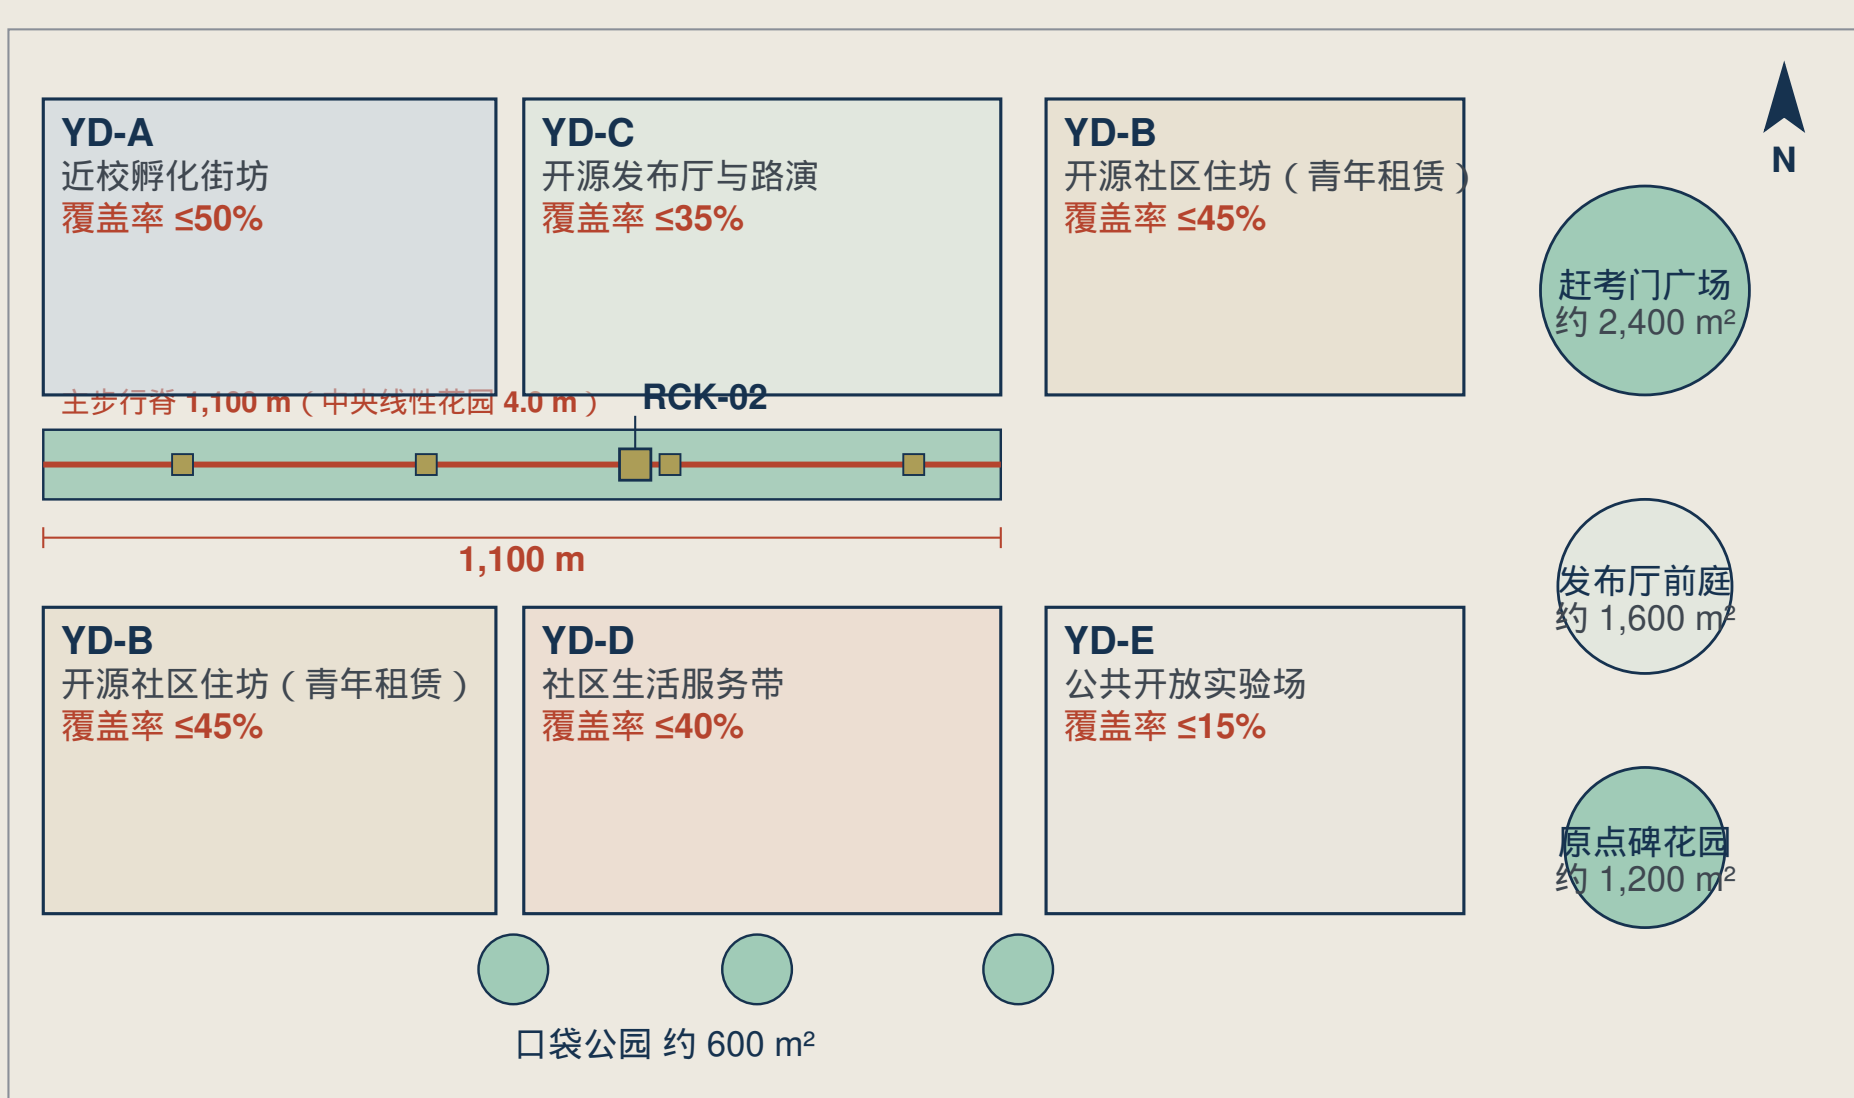

街区（含覆盖率上限） 慢行主轴 公共空间节点 答卷亭点位

原点社区主步行脊断面（YD-A—YD-C 段）

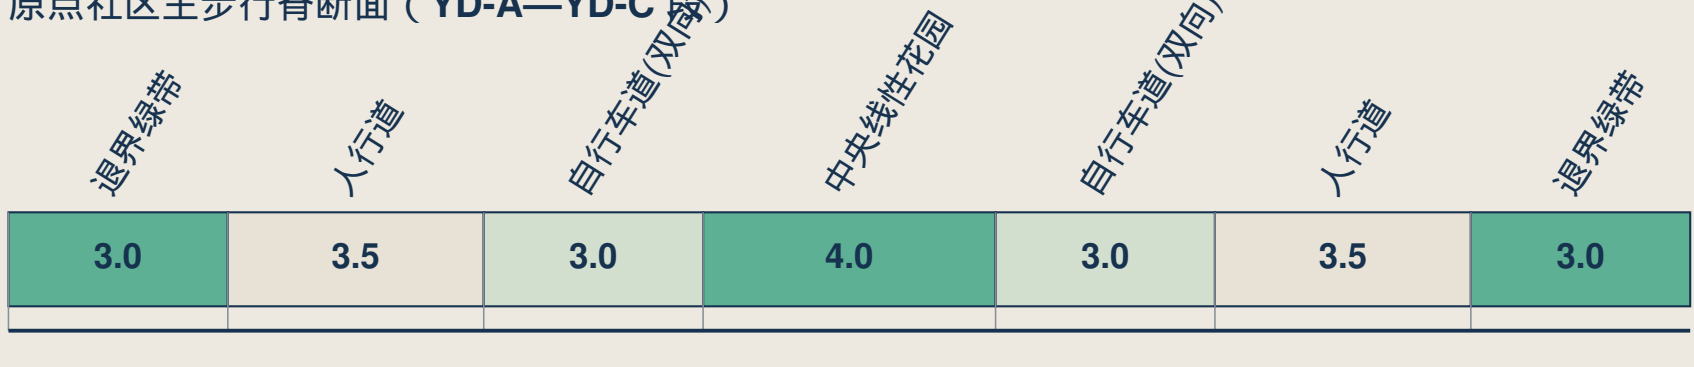


全段禁止社会机动车；自行车道彩色透水混凝土，中央花园含答卷亭。

key-areas-origin-works

片区平面（示意，非红线）

复算：片区 72.05 ha | 慢行 2,283 m | 密度 31.7 m/ha | 绿地率 30.2%

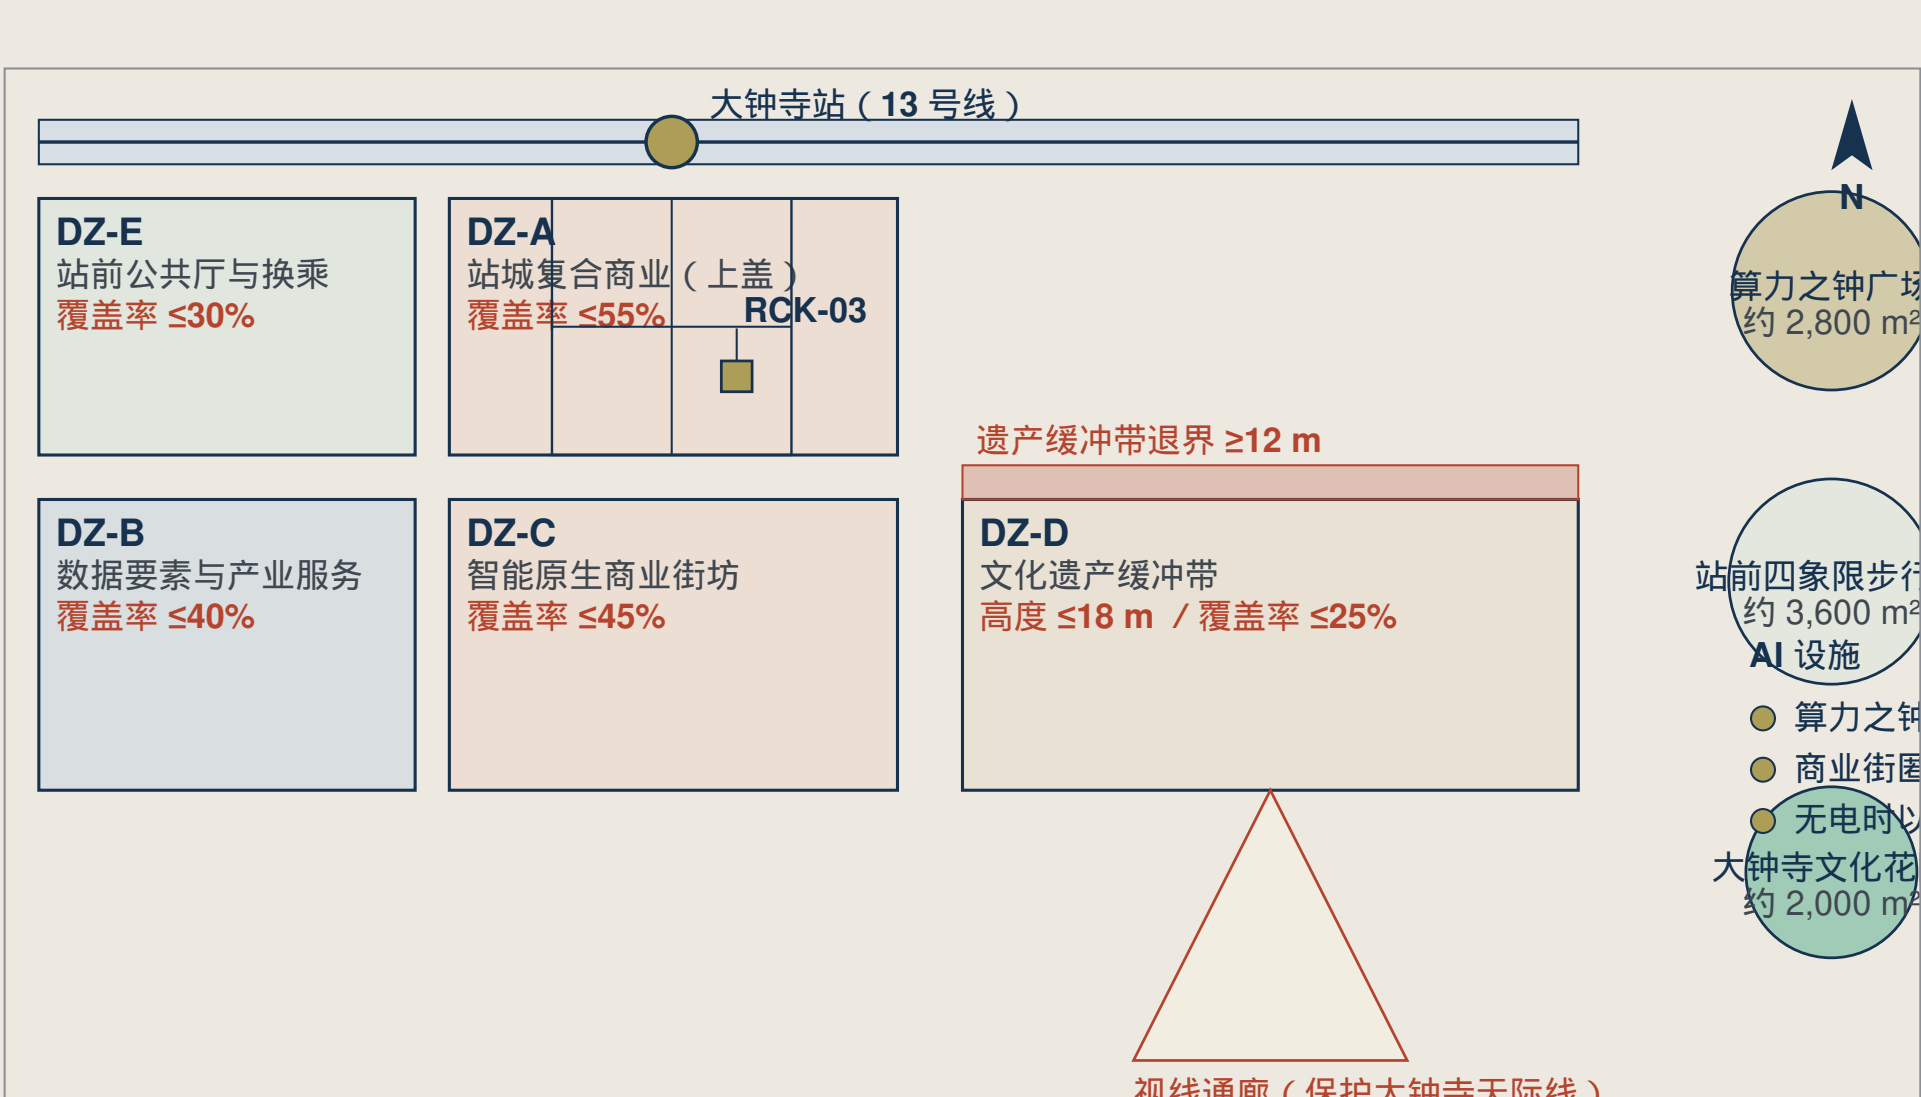

街区（含覆盖率上限） 公共空间节点 答卷亭点位 遗产缓冲带退界 ≥12 m

智能原生商业街断面（DZ-C 段）




公交+慢行模式，禁止社会车辆；外摆区可移动，夜间收回释放步行空间。

key-areas-dazhongzi

原点坊（104 ha）与智汇钟（72 ha）

- 原点坊街区：YD-A 开源发布厅、YD-B 校园连接、YD-C 公寓、YD-D 混合 TOD、YD-E 原点广场。
- 原点坊概念建议：容积率 1.2–2.8，限高 18–45 m，覆盖率 ≤35%；慢行密度 29.6 m/ha，长度 3,092 m。
- 智汇钟街区：DZ-A 绿色算力、DZ-B 产业引擎、DZ-C 商业、DZ-D 生活、DZ-E 四象限公园。
- 智汇钟概念建议：容积率 1.8–3.6，限高 24–60 m，覆盖率 ≤35%；慢行密度 31.7 m/ha，长度 2,283 m。
- 公共锚点：赶考门（清华园站）、五道口 TOD、算力之钟、大钟寺智站四象限站厅、RCK-02 与 RCK-03 答卷亭。

骑行网络、步行优先、绿廊与滨水四层叠加在同一底图上，各层图例分列于下。

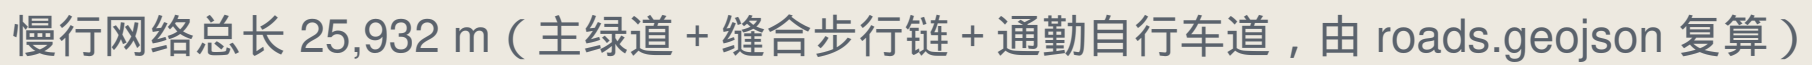

mobility-bluegreen



- 南北主脉：9.0 km 连续绿道 + 通勤自行车专用道。
- 东西缝合：7 条步行缝合走廊，跨越既有铁路割裂。
- 站城衔接：4 处智站，500 m 风雨连廊，50 m 内自行车停车枢纽，充电车位 $\geq 40\%$ 。
- 交叉口与停车：抬升过街平台 12 cm、1:12 坡道、分片区停车供给上限。

外轮廓 1,800 × 2,200 × 2,800 mm | 占地 3.96 m² | 独立基座、可拆移



report-card-kiosk

每个方形的边长按片区实际面积开方绘制，面积、慢行里程与比率均由本包 geometry/ 图层复算

口径：慢行 = 绿道 + 步行链 + 自行车道；比率 = 对应图层与片区边界求交后的面积比。边界为临时粗略范围。

metrics-evidence

- 33 项核心指标：30 项 known 指标确定性复算；3 项法定管控严格保持 unknown。
- 答卷亭（RCK）：占地 3.96 m²，1,800 × 2,200 × 2,800 mm，有电/无电双模式，具备实体兜底。
- 门禁校验：4 道确定性门禁与 30 项通用性质不变量 100% 通过。
- 三色治理：绿色全量放行、黄色 7 日整改、红色立即停用并切回人工服务。

范围与三处重点区均采用组织方发布的临时粗略替代边界（provisional），仅为概念建议，不得作为正式红线、审批依据或精确面积依据；官方 polygon 发布后必须整体重算几何、指标、图纸与 HTML。

提交包: cf3901646 | 作者: Charlie JIANG | 许可: COMMUNITY-DISPLAY-ONLY