


01 Overall structure: one spine, three key areas, two wings

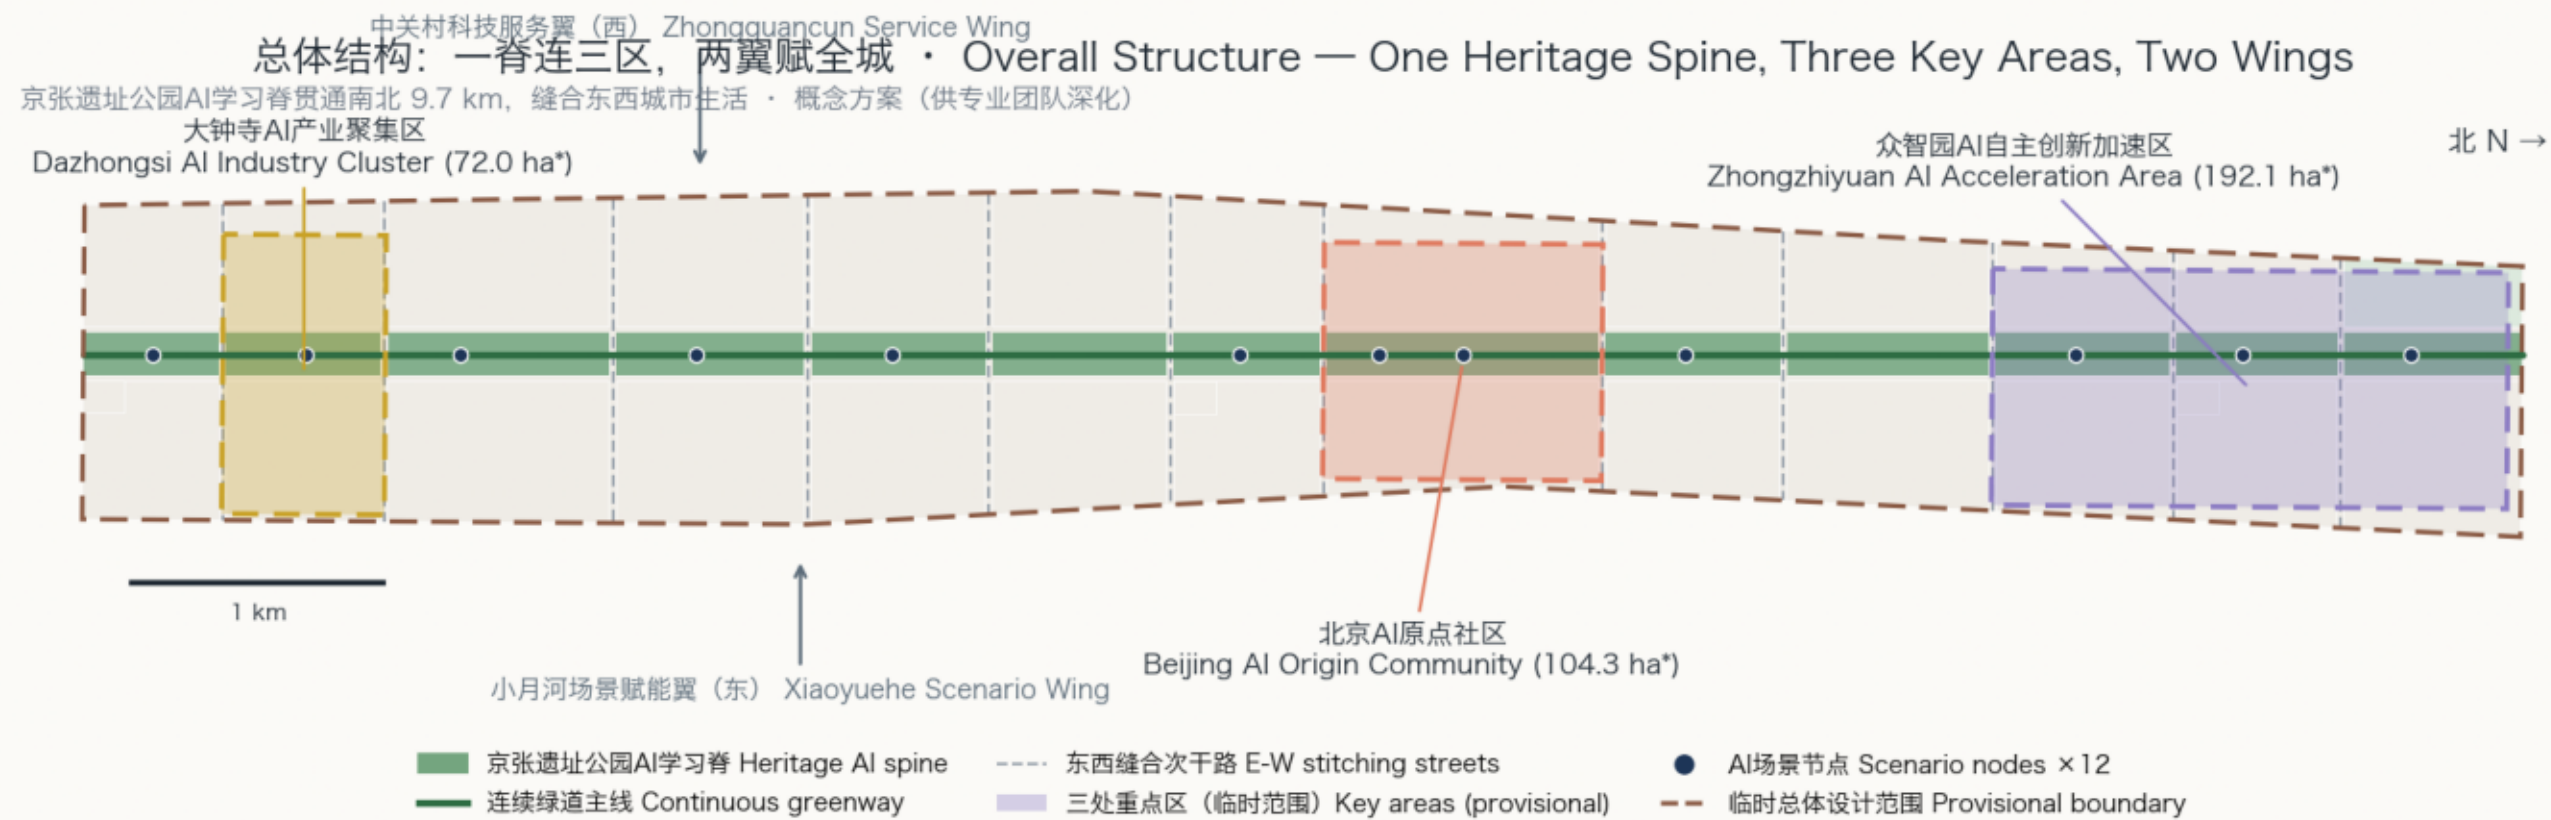

边界为临时约束范围（provisional，虚线），非官方红线；面积均为临时边界复算设计值。Provisional boundary (dashed), not an official redline; areas recomputed on provisional geometry. 来源 Sources: 官方公告 2026-05-09 · 仓库资料包 · 本包 geometry/*.geojson

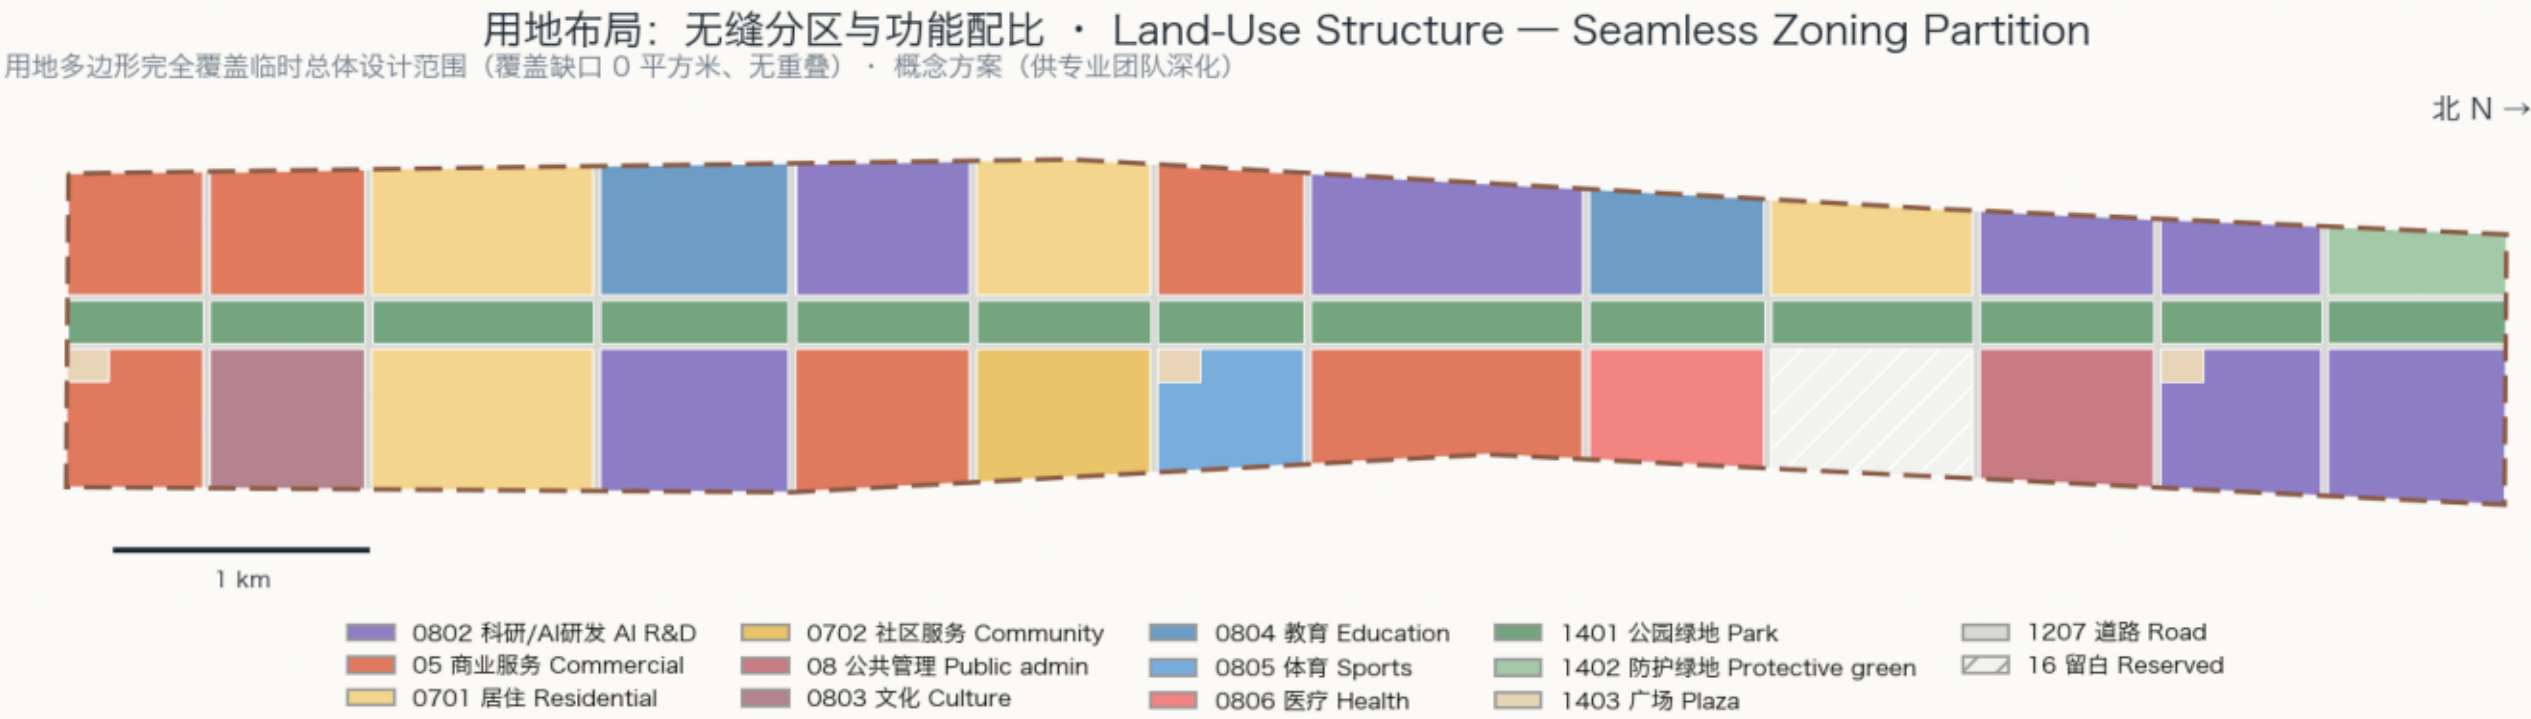


用地构成（公顷） · Land-use composition (ha) — 合计 total 1141 ha = 11.41 km²（临时边界复算 recomputed on provisional boundary）




边界为临时约束范围（provisional，虚线），非官方红线；面积均为临时边界复算设计值。Provisional boundary (dashed), not an official redline; areas recomputed on provisional geometry. 来源 Sources: 官方公告 2026-05-09 · 仓库资料包 · 本包 geometry/* .geojson

三处重点区详细设计索引 · Detailed Design Index of the Three Key Areas

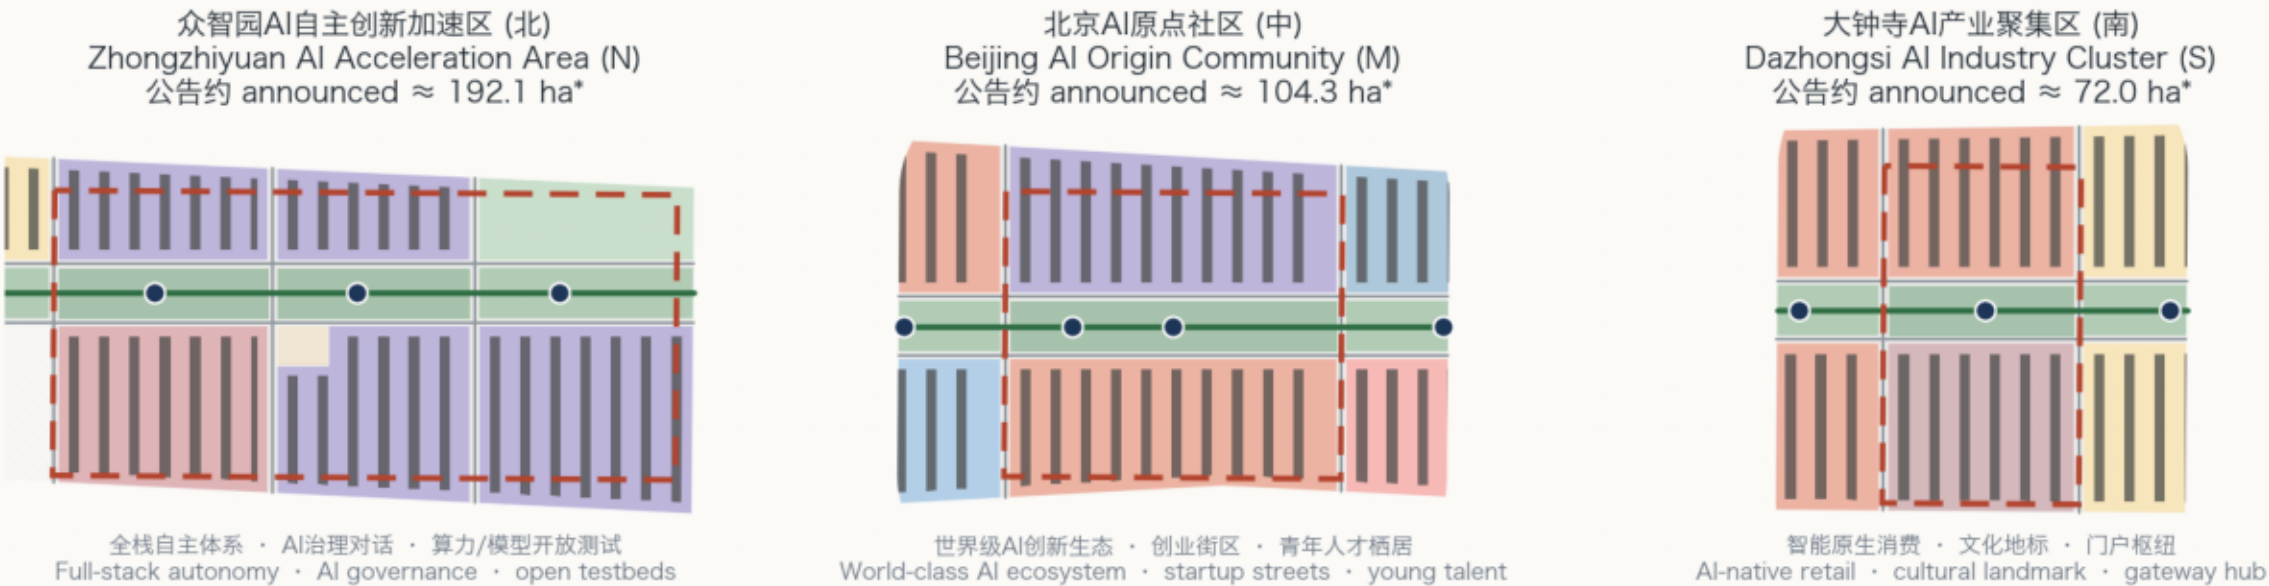

科研/AI研发 AI R&D 商业服务 Commercial 公园绿地 Park 概念建筑体量 Concept massing 绿道主线 Greenway AI场景节点 Scenario node 重点区临时范围 Provisional key-area

边界为临时约束范围 (provisional, 虚线), 非官方红线; 面积均为临时边界复算设计值。Provisional boundary (dashed), not an official redline; areas recomputed on provisional geometry. 来源 Sources: 官方公告 2026-05-09 · 仓库资料包 · 本包 geometry/*.geojson *面积为公告约数 announced approximate values

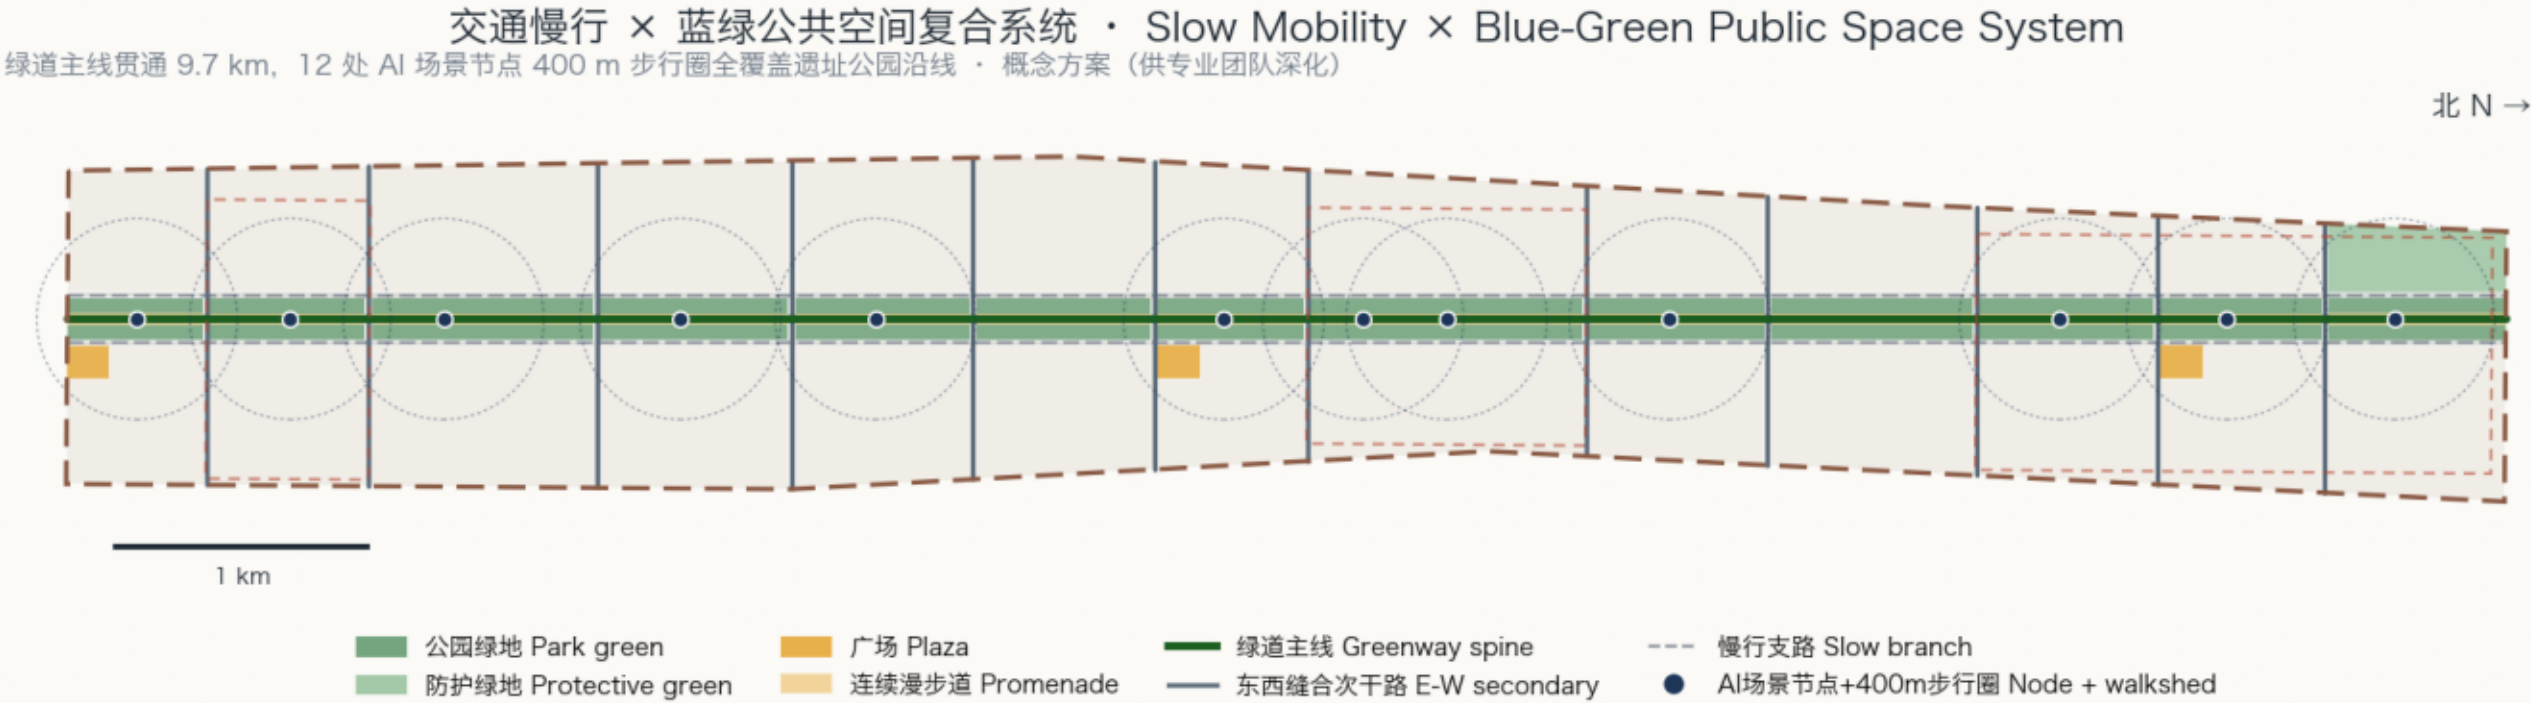

边界为临时约束范围 (provisional, 虚线), 非官方红线; 面积均为临时边界复算设计值。Provisional boundary (dashed), not an official redline; areas recomputed on provisional geometry. 来源 Sources: 官方公告 2026-05-09 · 仓库资料包 · 本包 geometry/*.geojson


核心指标复算与证据链 · Metrics Recalculation & Evidence Chain

全部数值由 geometry/*.geojson 在 EPSG:4548 投影下复算，与 metrics.json 完全一致；空间自检 PASS（用地覆盖缺口 0 m²、无重叠）。Recomputed from GeoJSON in EPSG:4548; identical to metrics.json; spatial self-check PASS.


① 面积总量 Headline areas

总体设计范围（临时复算） Site area*	11.413 km ²
绿地面积 Green space	177.8 ha
公共空间面积 Public space	51.6 ha
建筑基底（概念） Footprint*	226.9 ha
概念总建筑规模 Concept GFA*	18.39 M m ²


② 结构比例 Structural ratios (%)

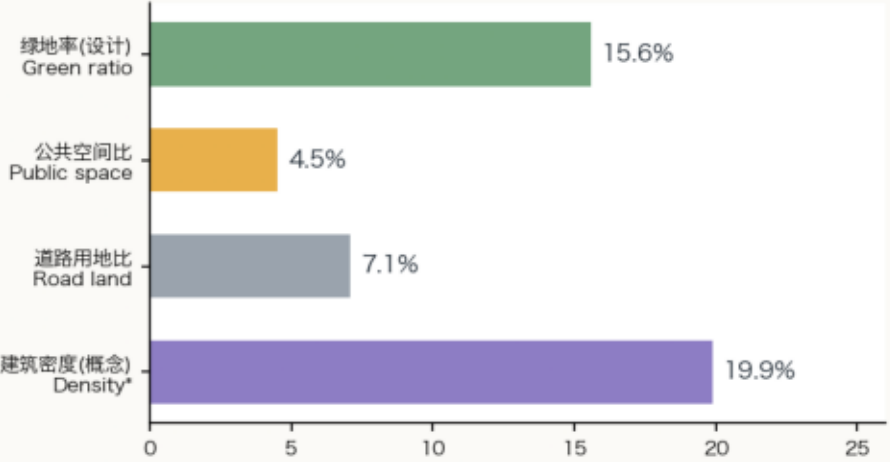

③ 重点区面积校核 Key-area check (ha)

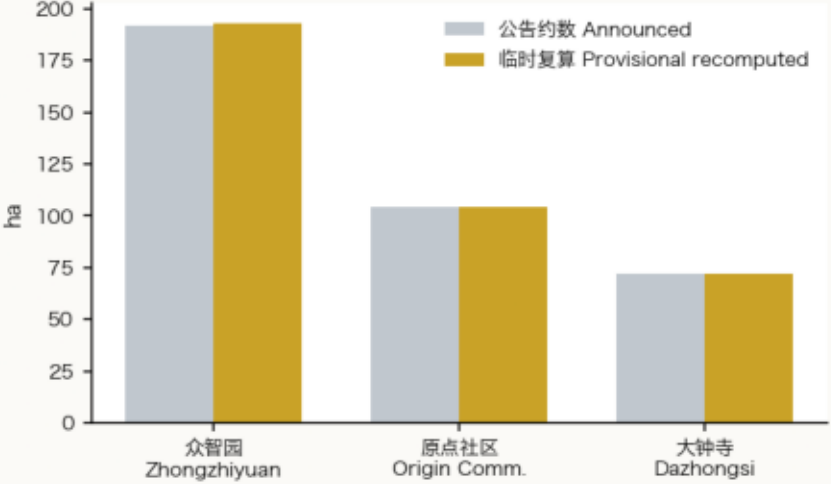


④ 概念分期 Concept phasing (km²)

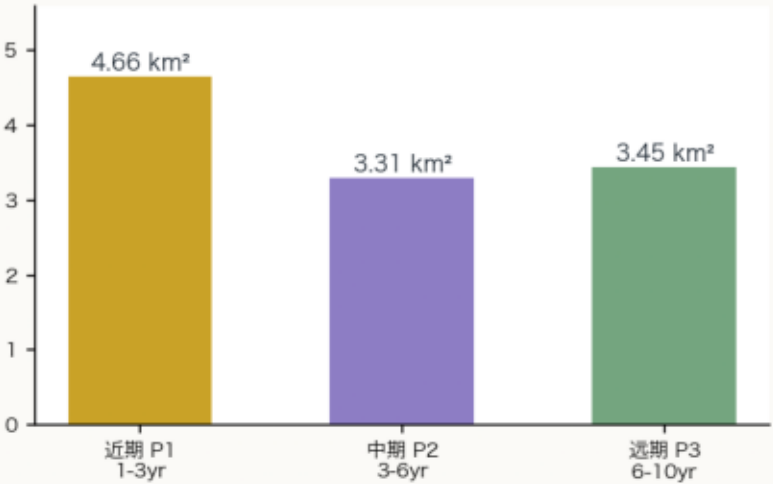

⑤ 待正式数据补齐 Pending official data

法定容积率 Statutory FAR	待控规条件 pending
法定建筑高度 Height control	待管控条件 pending
法定绿地率 Statutory green ratio	待控规条件 pending
官方精确边界 Official boundary	临时替代 provisional in use
管控/红线矢量 Constraint vectors	层有意留空 layer empty

⑥ 证据链 Evidence chain

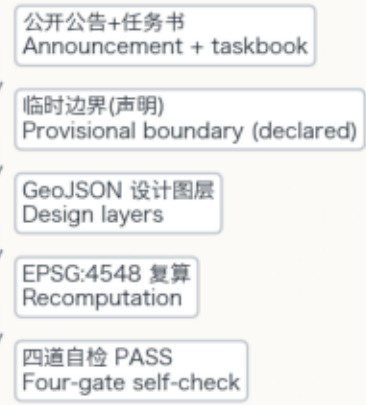

06 Scenario System & Implementation Outline

Twelve AI scenario cards (SN-01 to SN-12) line the heritage-park AI learning spine; SN-03 (compute & model open testbed), SN-07 (low-speed autonomous delivery loop) and SN-11 (Dazhongsi AI-native retail testbed) are the three industrial validation scenarios. All scenarios follow data minimization, visible on-site notice, and human reviewability.

Five personas: hardcore researchers / founders & engineers / AI-native youth / residents & elders / global visitors & developers.

Three AI pilgrimage landmarks: the Zhongzhiyuan Switchback Point governance tower · the Origin Community First Line of Code plaza · the Dazhongsi Bell-Sound Computing hall.

Concept phasing: near 4.66 km² (key areas + spine) → mid 3.31 km² (stitching + community renewal) → long 3.45 km² (reserve + rolling renewal); 14 concept renewal projects in total.

Long-term operations: annual Jing-Zhang AI Week global developer congress · quarterly scenario hackathons · standing AI-guided tours · two-tier governance of an operating company plus a developers' council. All items are conceptual suggestions, not established government arrangements.