




午饭走进公园：全线与清华东路西口的双尺度校验

500-600米是一期真实城市门周边的目标服务半径，不是已测步行路线

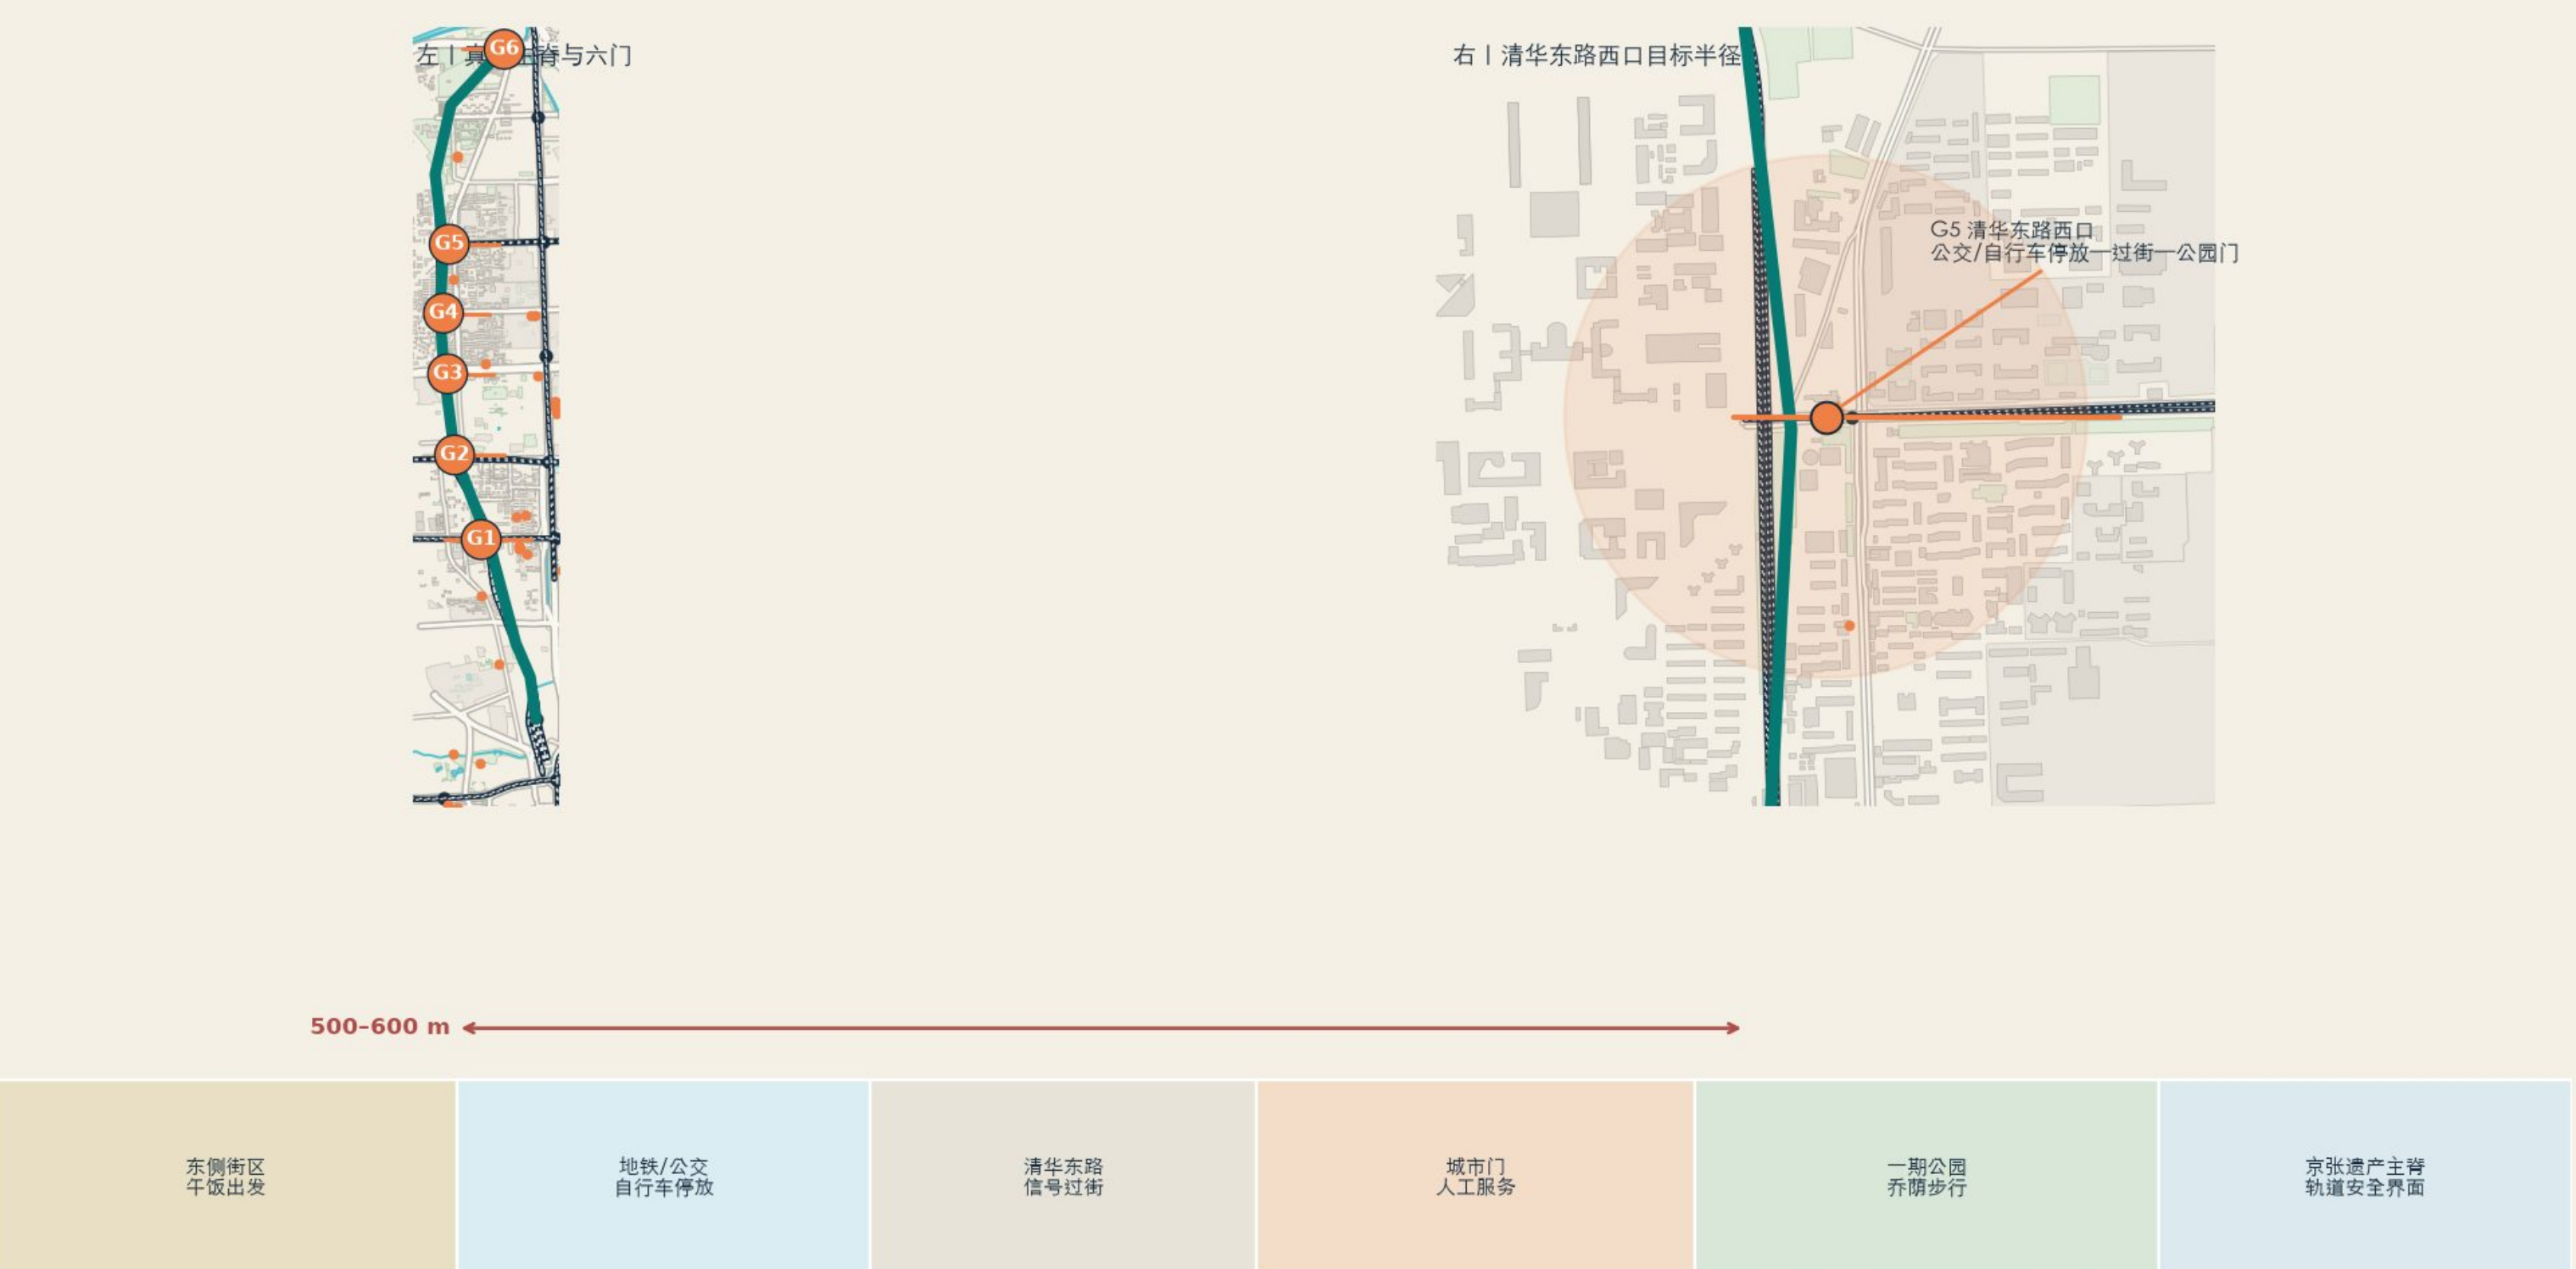

东西段是设计关系图，必须由现场步行记录、过街时间、净宽与无障碍审计替换。
概念设计、临时边界、非官方红线

JING-ZHANG COMMON VERANDA · CONCEPTUAL URBAN DESIGN

真实京张走廊与建设状态

总体设计四至：西直门外大街—北五环；大钟寺东路/荷清路—学院路/西土城路



概念设计 · 临时边界 · 非官方红线

01

一期已开放；知春路—清华东路，约2.5公里

02

一期已有足球、篮球及跑步设施：先审计，不重复建设

03

清华东路南侧公共空间项目已批：本案只补责任与服务层

04

二期仍在建；北五环连续性不可提前承诺

05

临时边界与重点区仍非官方矢量红线

JING-ZHANG COMMON VERANDA · CONCEPTUAL URBAN DESIGN

总体城市设计：真实主脊、六个真实接口、三种门廊

活动口袋离开直行流线；既有工程作基线；跨线只做核验，不画未经论证的捷径



概念设计 · 临时边界 · 非官方红线

G6 北五环—清河南缘

G5 清华东路西口

G4 成府路—五道口

G3 北四环遗产桥

G2 知春路南门

G1 大钟寺四象限

南→北状态

既有站点 / 一期开放 / 已批项目 / 二期在建

JING-ZHANG COMMON VERANDA · CONCEPTUAL URBAN DESIGN

三层真实范围：区域协同、总体设计、重点区详细设计

面积和四至来自官方公告；提交多边形仍是临时推导，不是官方矢量红线

01

43.6 km²

统筹研究范围

北：北五环 | 东：京藏高速
南：西直门外大街 | 西：万泉河路

02

≈11.4 km²

总体设计范围

北：北五环 | 东：学院路/西土城路等
南：西直门外大街 | 西：大钟寺东路/荷清路等

03

≈368.4 ha

重点区域范围

自北向南：众智园 192.1 ha
AI原点 104.3 ha | 大钟寺 72.0 ha

总体设计六段公共能力（自北向南）

01

自主创新与验证

02

清河蓝绿共享

03

开放学习与转化

04

社区维护与服务

05

智能生活与商业

06

铁路记忆与传播

范围关系：43.6 km²做战略协同；约11.4 km²做城市设计；三处重点区做场地级深化。任何临时几何到官方GIS/CAD到位后必须整包替换。

概念设计 · 临时边界 · 非官方红线

JING-ZHANG COMMON VERANDA · CONCEPTUAL URBAN DESIGN



现状建筑背景 ≠ 概念更新容量

OSM建筑只用于定位；22个研究单元只用于容量比较，不是拆建结论



灰=公开OSM建筑背景（非测绘） · 绿=90×64m概念研究单元 · 橙=临时重点区范围

概念设计 · 临时边界 · 非官方红线

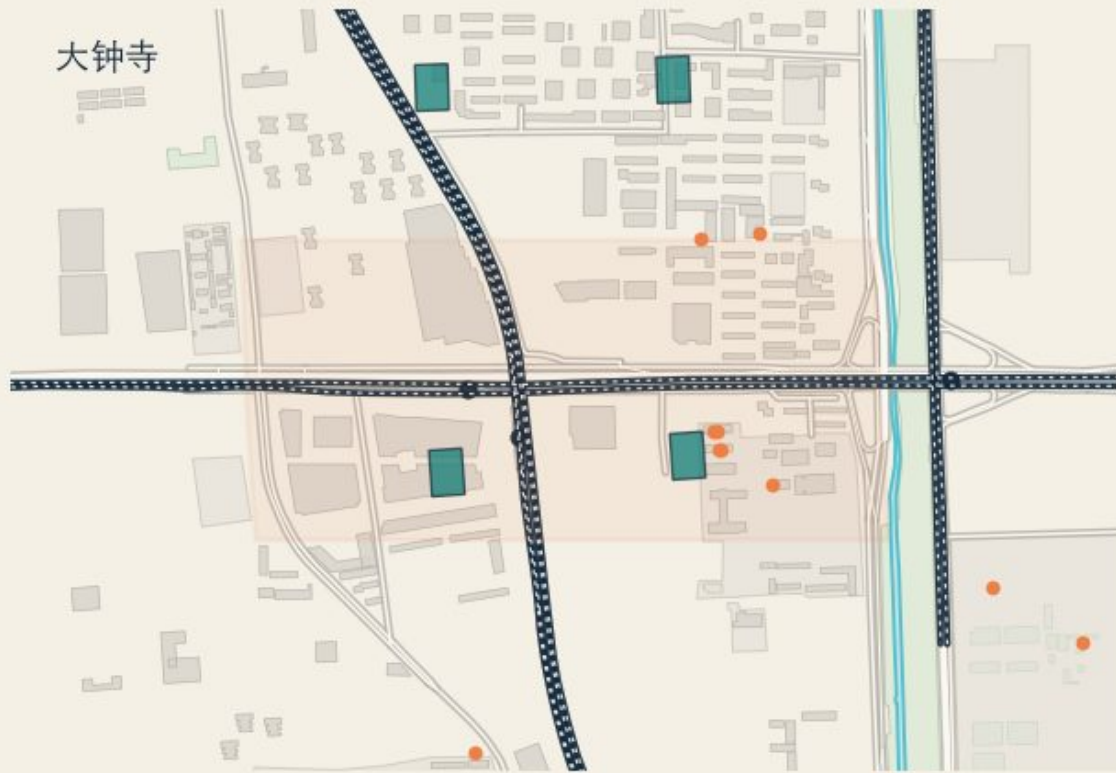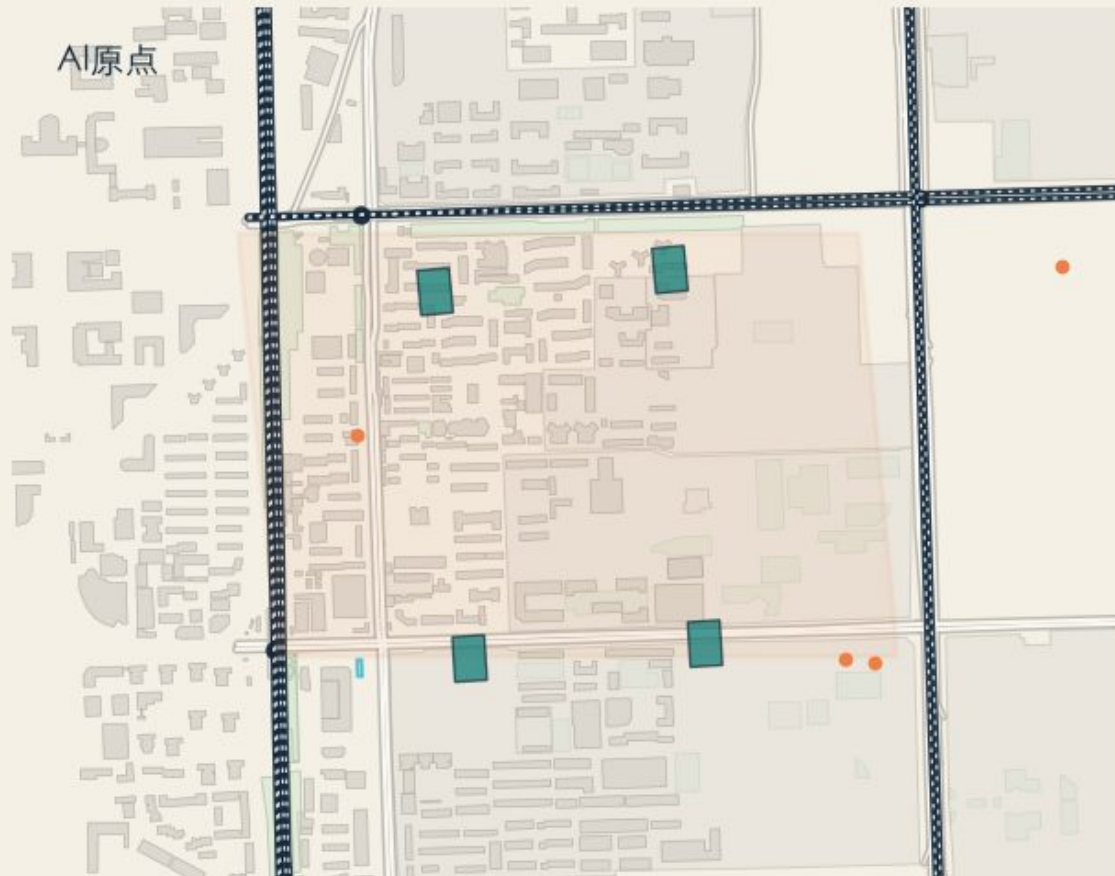


JING-ZHANG COMMON VERANDA · CONCEPTUAL URBAN DESIGN

三个重点区：真实位置、真实接口、概念动作

自北向南：众智园—AI原点—大钟寺；底图用于定位，彩色动作保持可替换

01 众智园实验门廊

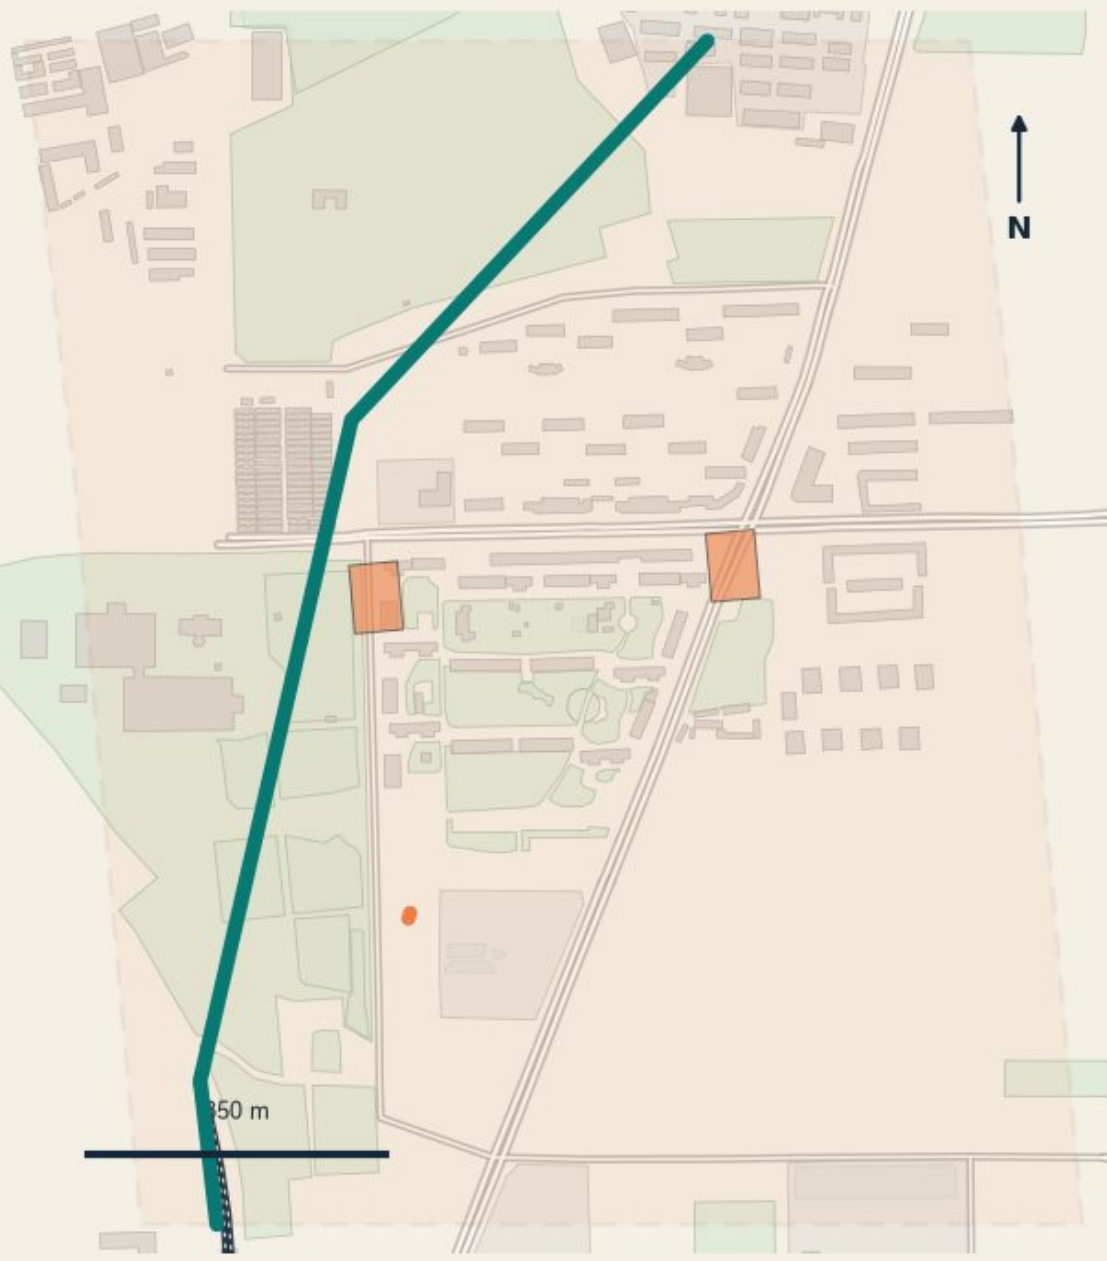

五环南侧的受控测试、清河生态与二期接口


概念设计 · 临时边界 · 非官方红线

02 AI 原点学习门廊



五道口—清华东路西口，真实站点、城市道路与一期公园

03 大钟寺生活门廊

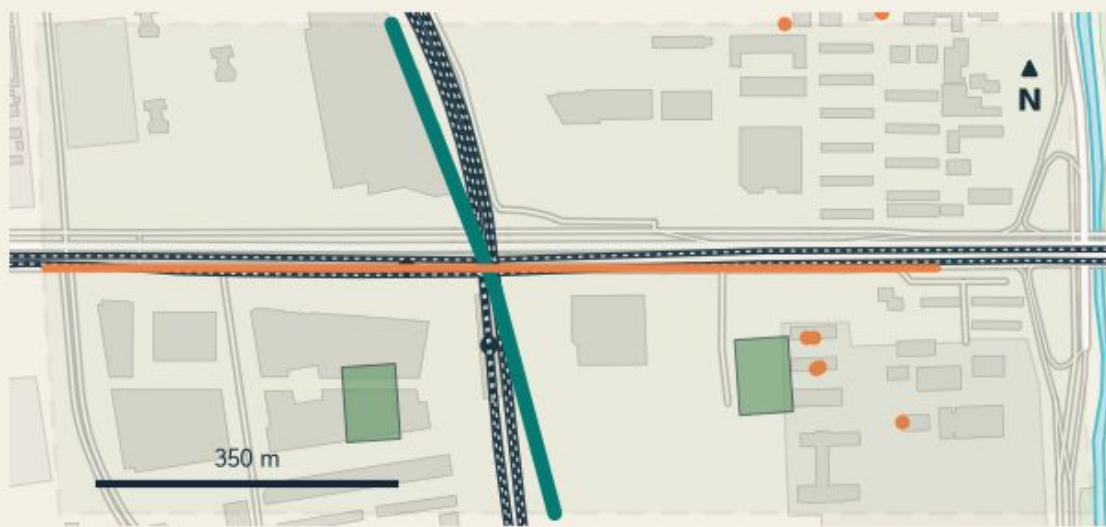


大钟寺站四象限：轨道换乘、商业首层与社区步行

JING-ZHANG COMMON VERANDA · CONCEPTUAL URBAN DESIGN

AI 原点学习门廊

五道口—清华东路西口：真实站点、城市道路与一期公园

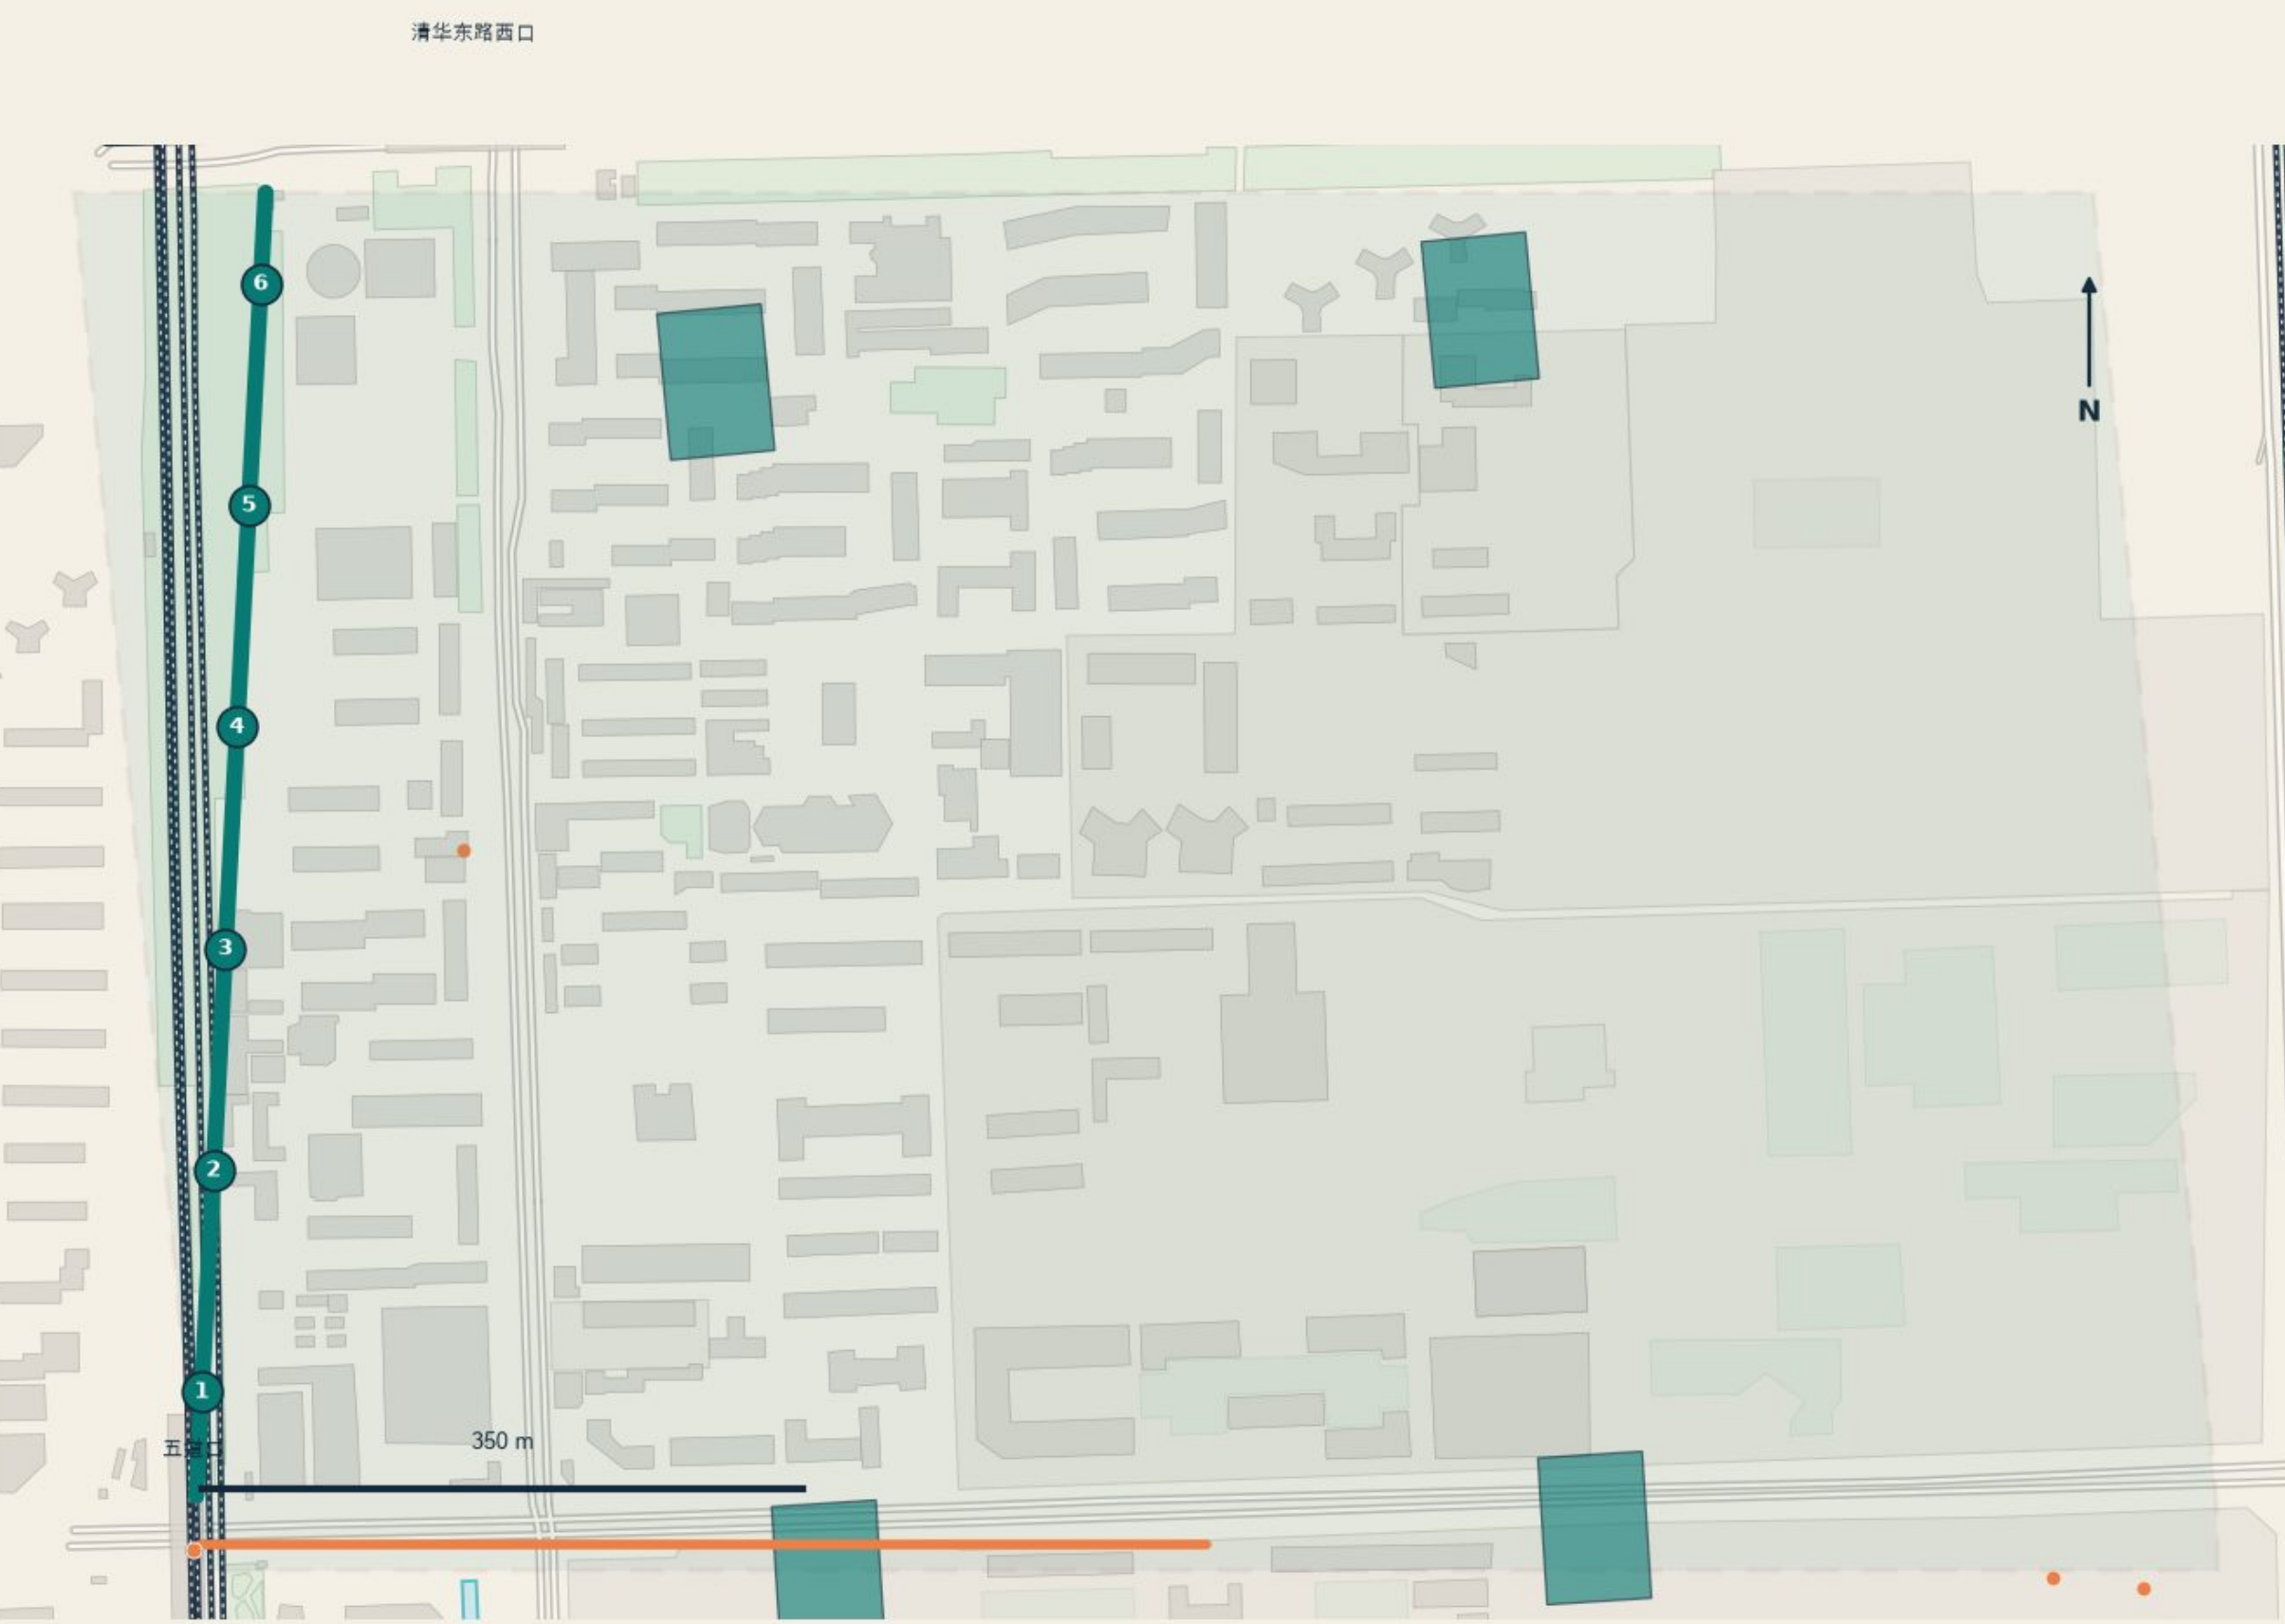

概念设计 · 临时边界 · 非官方红线

- 01 开源发布门
- 02 公共学习阶
- 03 研究转化桌
- 04 无障碍学习环
- 05 铁路雨洪花园
- 06 社区穿梭台

物理关系


东西向连接只沿成府路和清华东路等真实接口；运营轨道不做平面横穿。

灰=OSM背景（非测绘） | 深绿色=轨道 | 橙=真实道路接口 | 彩色块=概念容量单元

JING-ZHANG COMMON VERANDA · CONCEPTUAL URBAN DESIGN

众智园实验门廊

五环南侧的受控测试、清河生态与二期接口

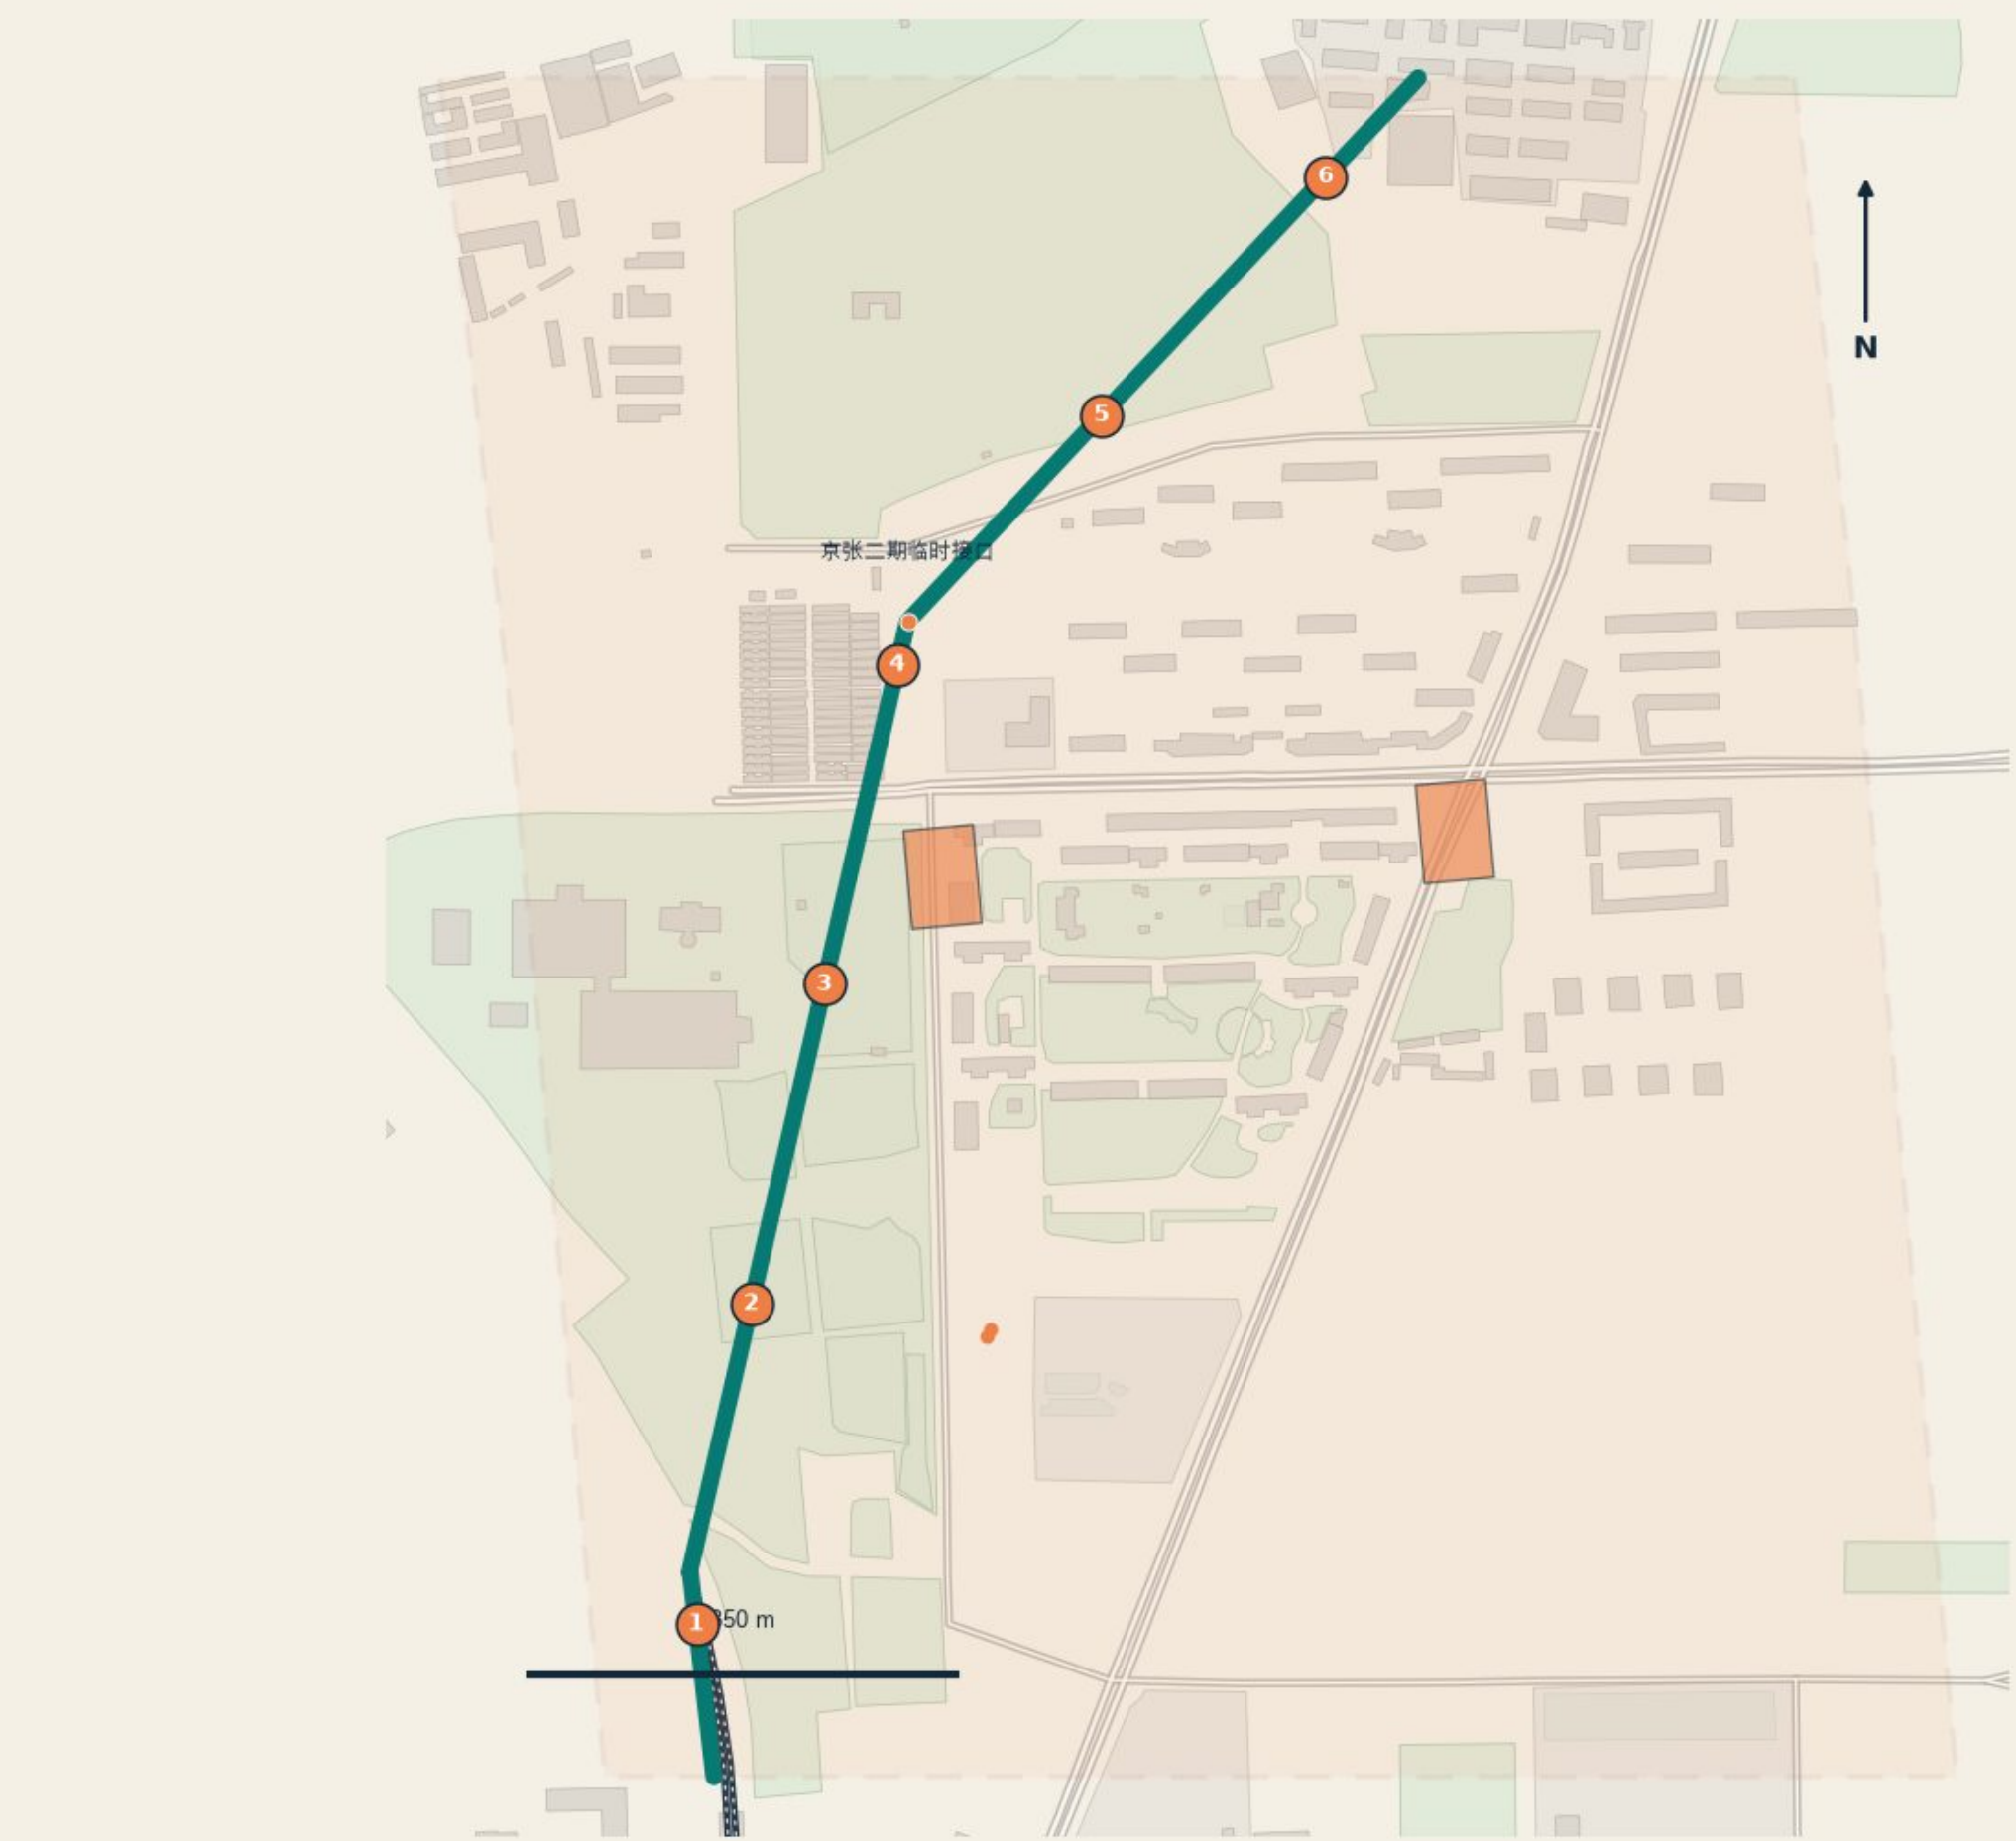

概念设计 · 临时边界 · 非官方红线

- 01 测试申请与解释厅
- 02 低速机器人沙盘
- 03 红队评测庭院
- 04 能源与安全审计亭
- 05 公众观察廊
- 06 人工接管台

物理关系


测试车与公众步行物理分开：越界、失联或无人工接管即停。

灰=OSM背景（非测绘） | 深绿色=轨道 | 橙=真实道路接口 | 彩色块=概念容量单元

JING-ZHANG COMMON VERANDA · CONCEPTUAL URBAN DESIGN

大钟寺生活门廊

大钟寺站四象限：轨道换乘、商业首层与社区步行

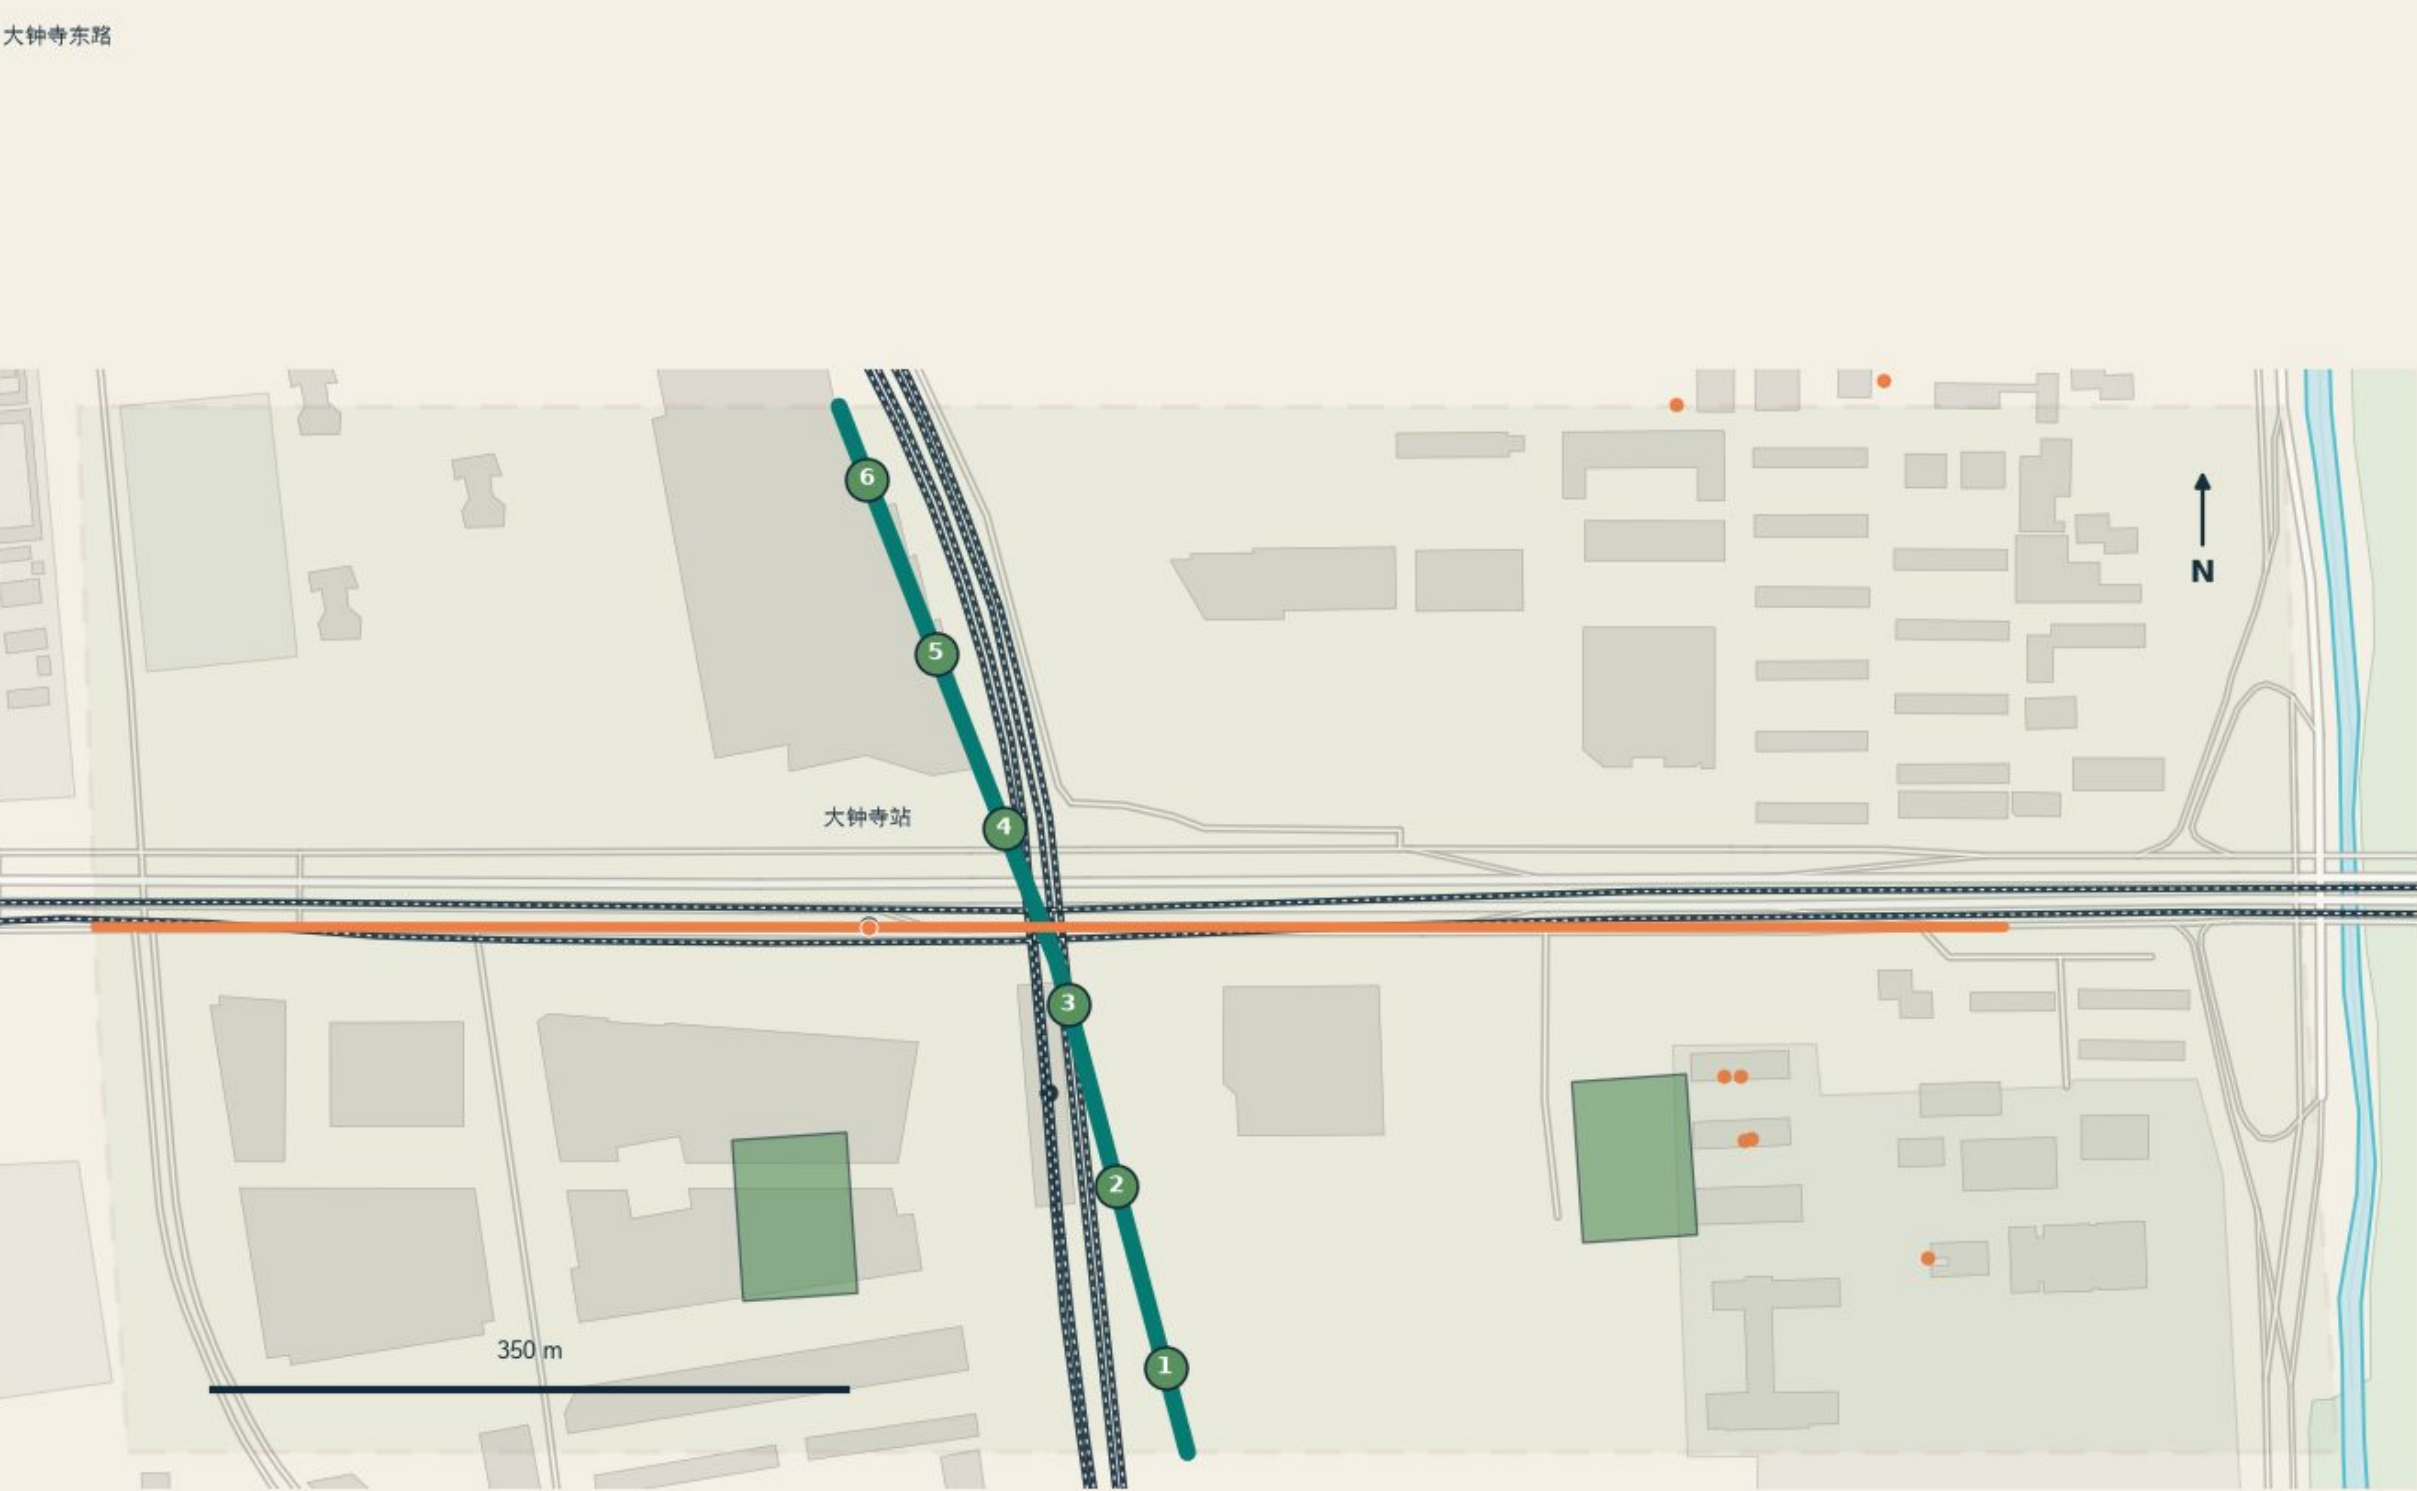

概念设计 · 临时边界 · 非官方红线

- 01 轨道到达客厅
- 02 责任零售柜台
- 03 长者服务导航
- 04 百年公共账本钟
- 05 夜间共治花园
- 06 社区申诉台

物理关系


先审计四象限既有骑行、出入口与非机动车停放；不虚构穿轨捷径。

灰=OSM背景（非测绘） | 深绿色=轨道 | 橙=真实道路接口 | 彩色块=概念容量单元

JING-ZHANG COMMON VERANDA · CONCEPTUAL URBAN DESIGN


午饭走进公园：全线与清华东路西口的双尺度校验

500-600米是一期真实城市门周边的目标服务半径，不是已测步行路线

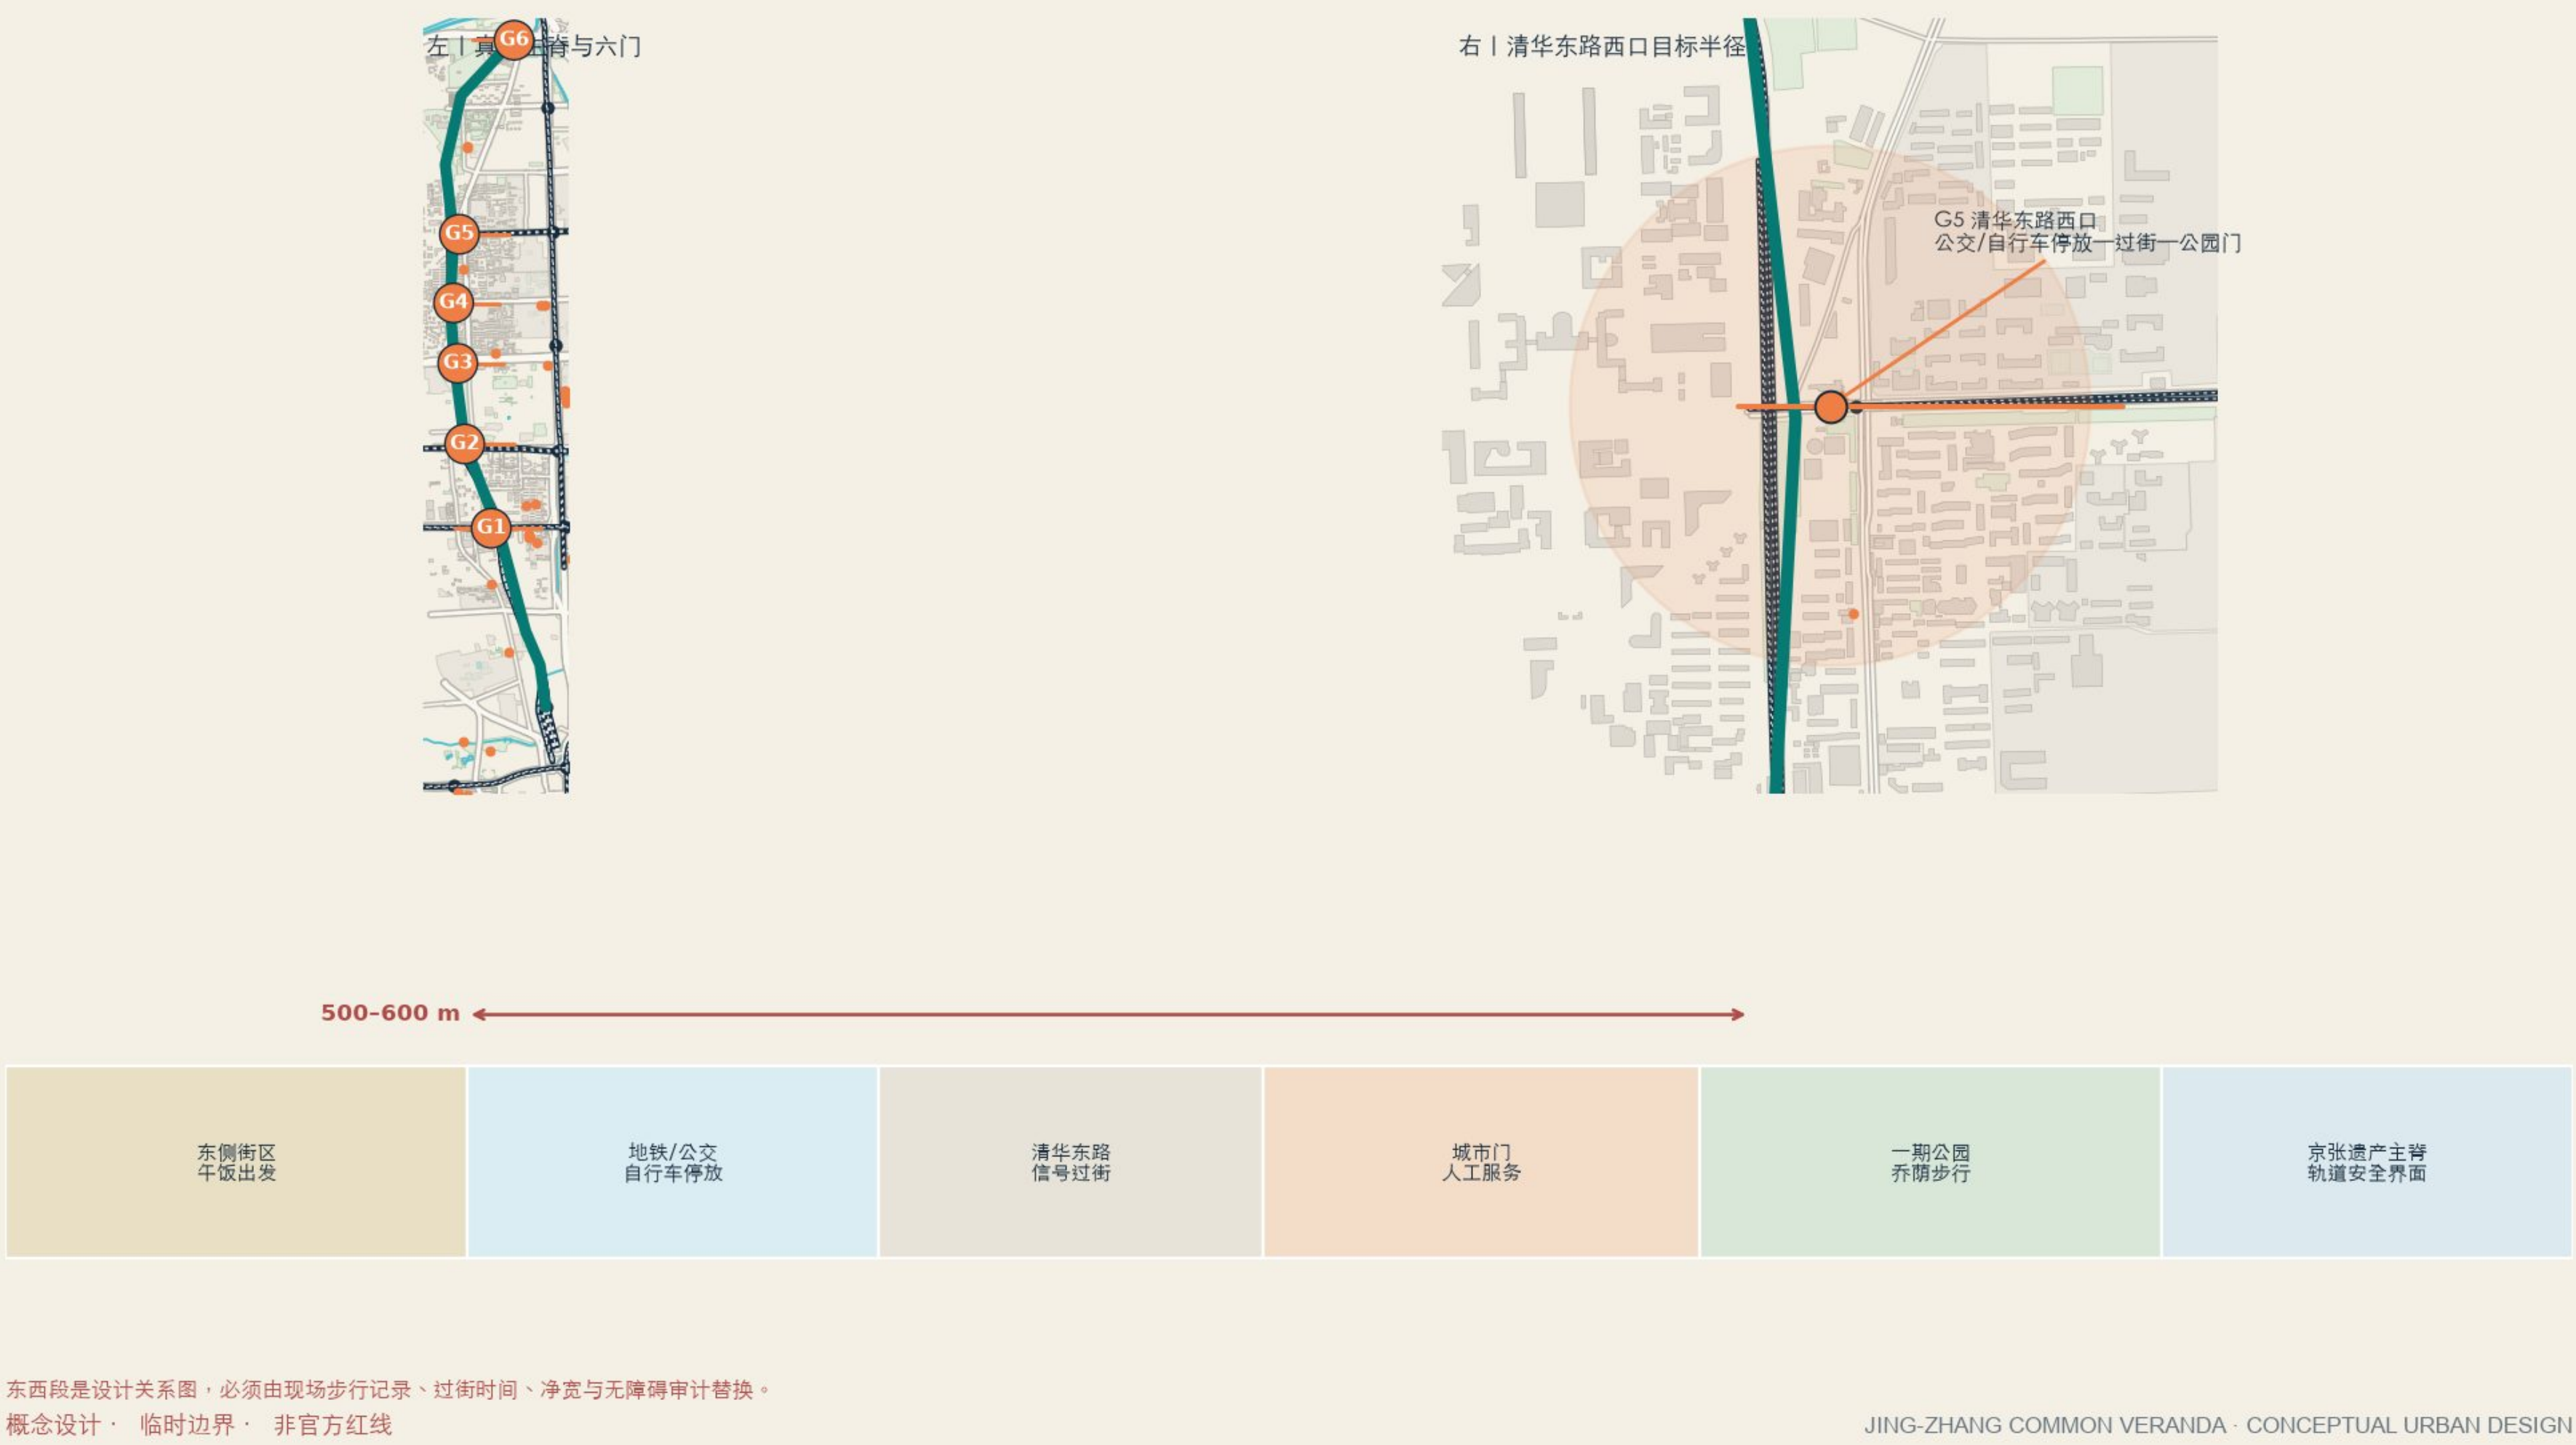

公共空间剖面：直行、活动与轨道安全互不打架

概念模块只表示关系与优先级；具体净宽、树木、市政、消防和轨道条件须现场复核

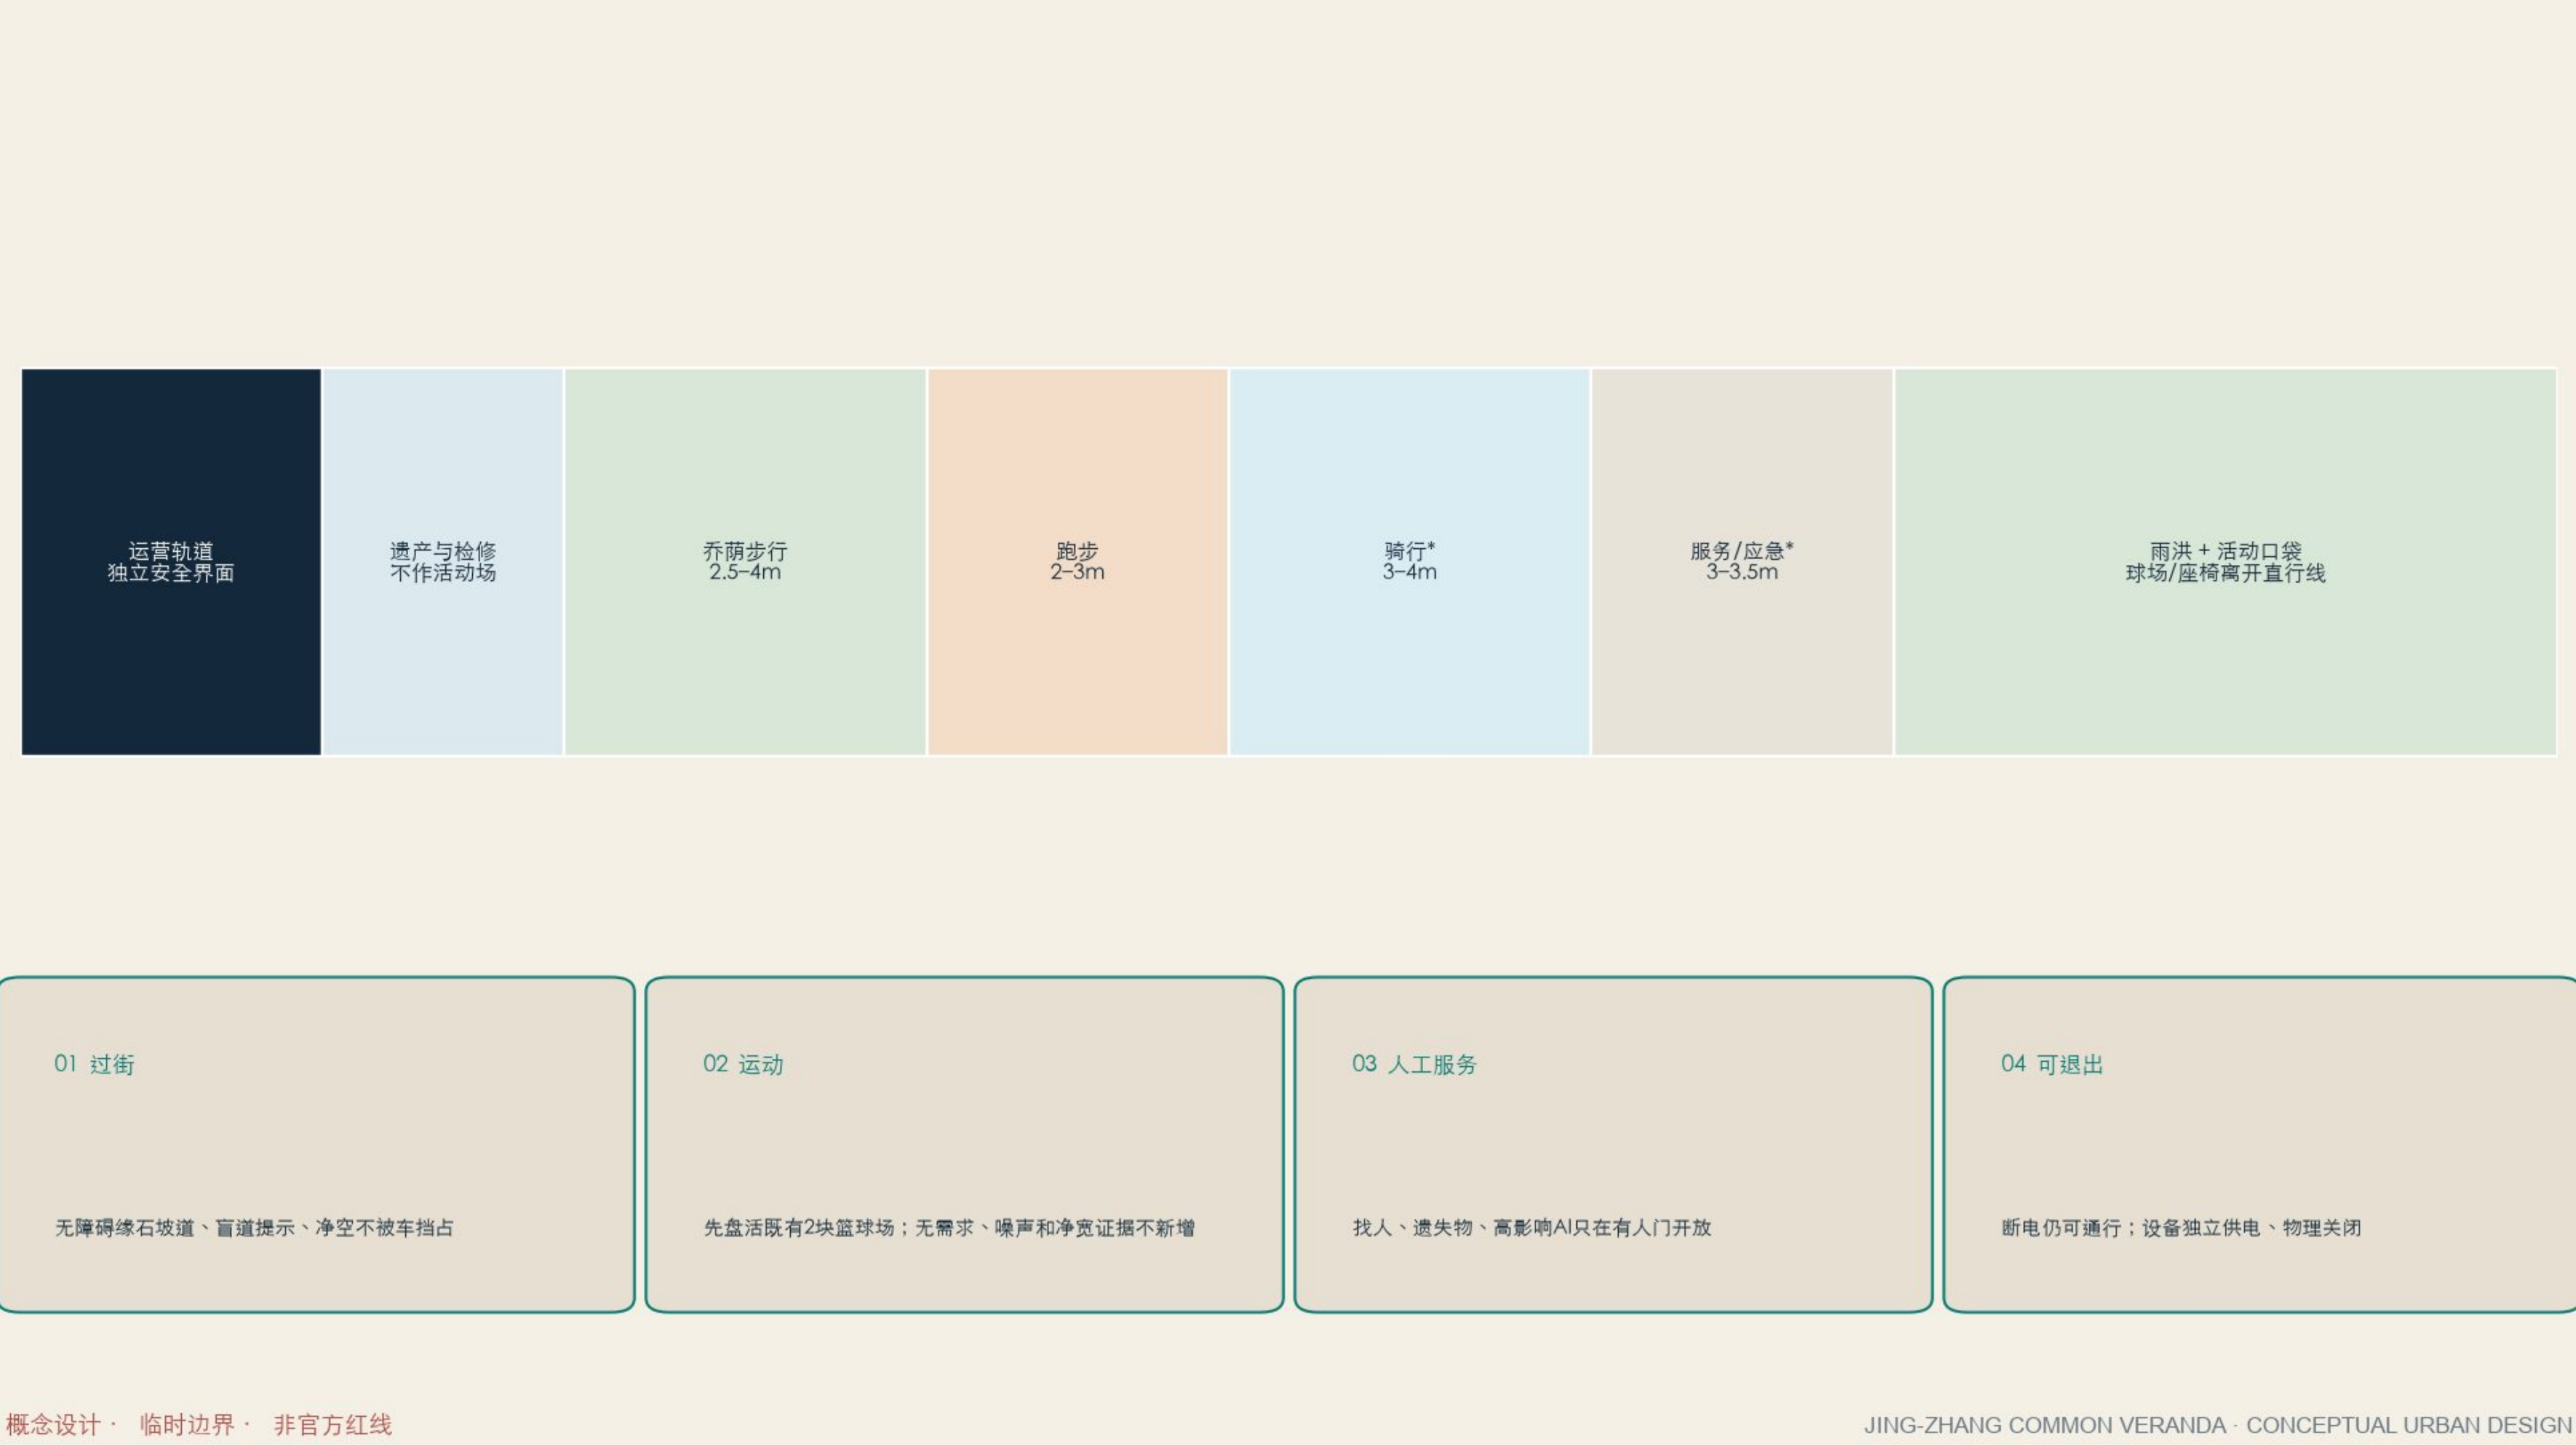

人、车、轨道：不靠一条路解决所有问题

走、跑、骑、服务车与轨道按风险和速度分层；宽度不足时骑行绕行城市道路



蓝绿公共空间：一条可遮阴、可滞蓄、可停留的遗产廊道

低技术基础层在断电时仍可使用，智能设施作为独立可关闭的服务层





十二个可感知场景：空间—数据—人工—退出四联表

场景不是功能清单，而是一组有空间、有责任人、有停机条件的公共服务契约




概念设计 · 临时边界 · 非官方红线

JING-ZHANG COMMON VERANDA · CONCEPTUAL URBAN DESIGN

文化与识别：从工程自强到开放责任

品牌不是装饰，而是一套让城市空间和 AI 服务可读的公共语法

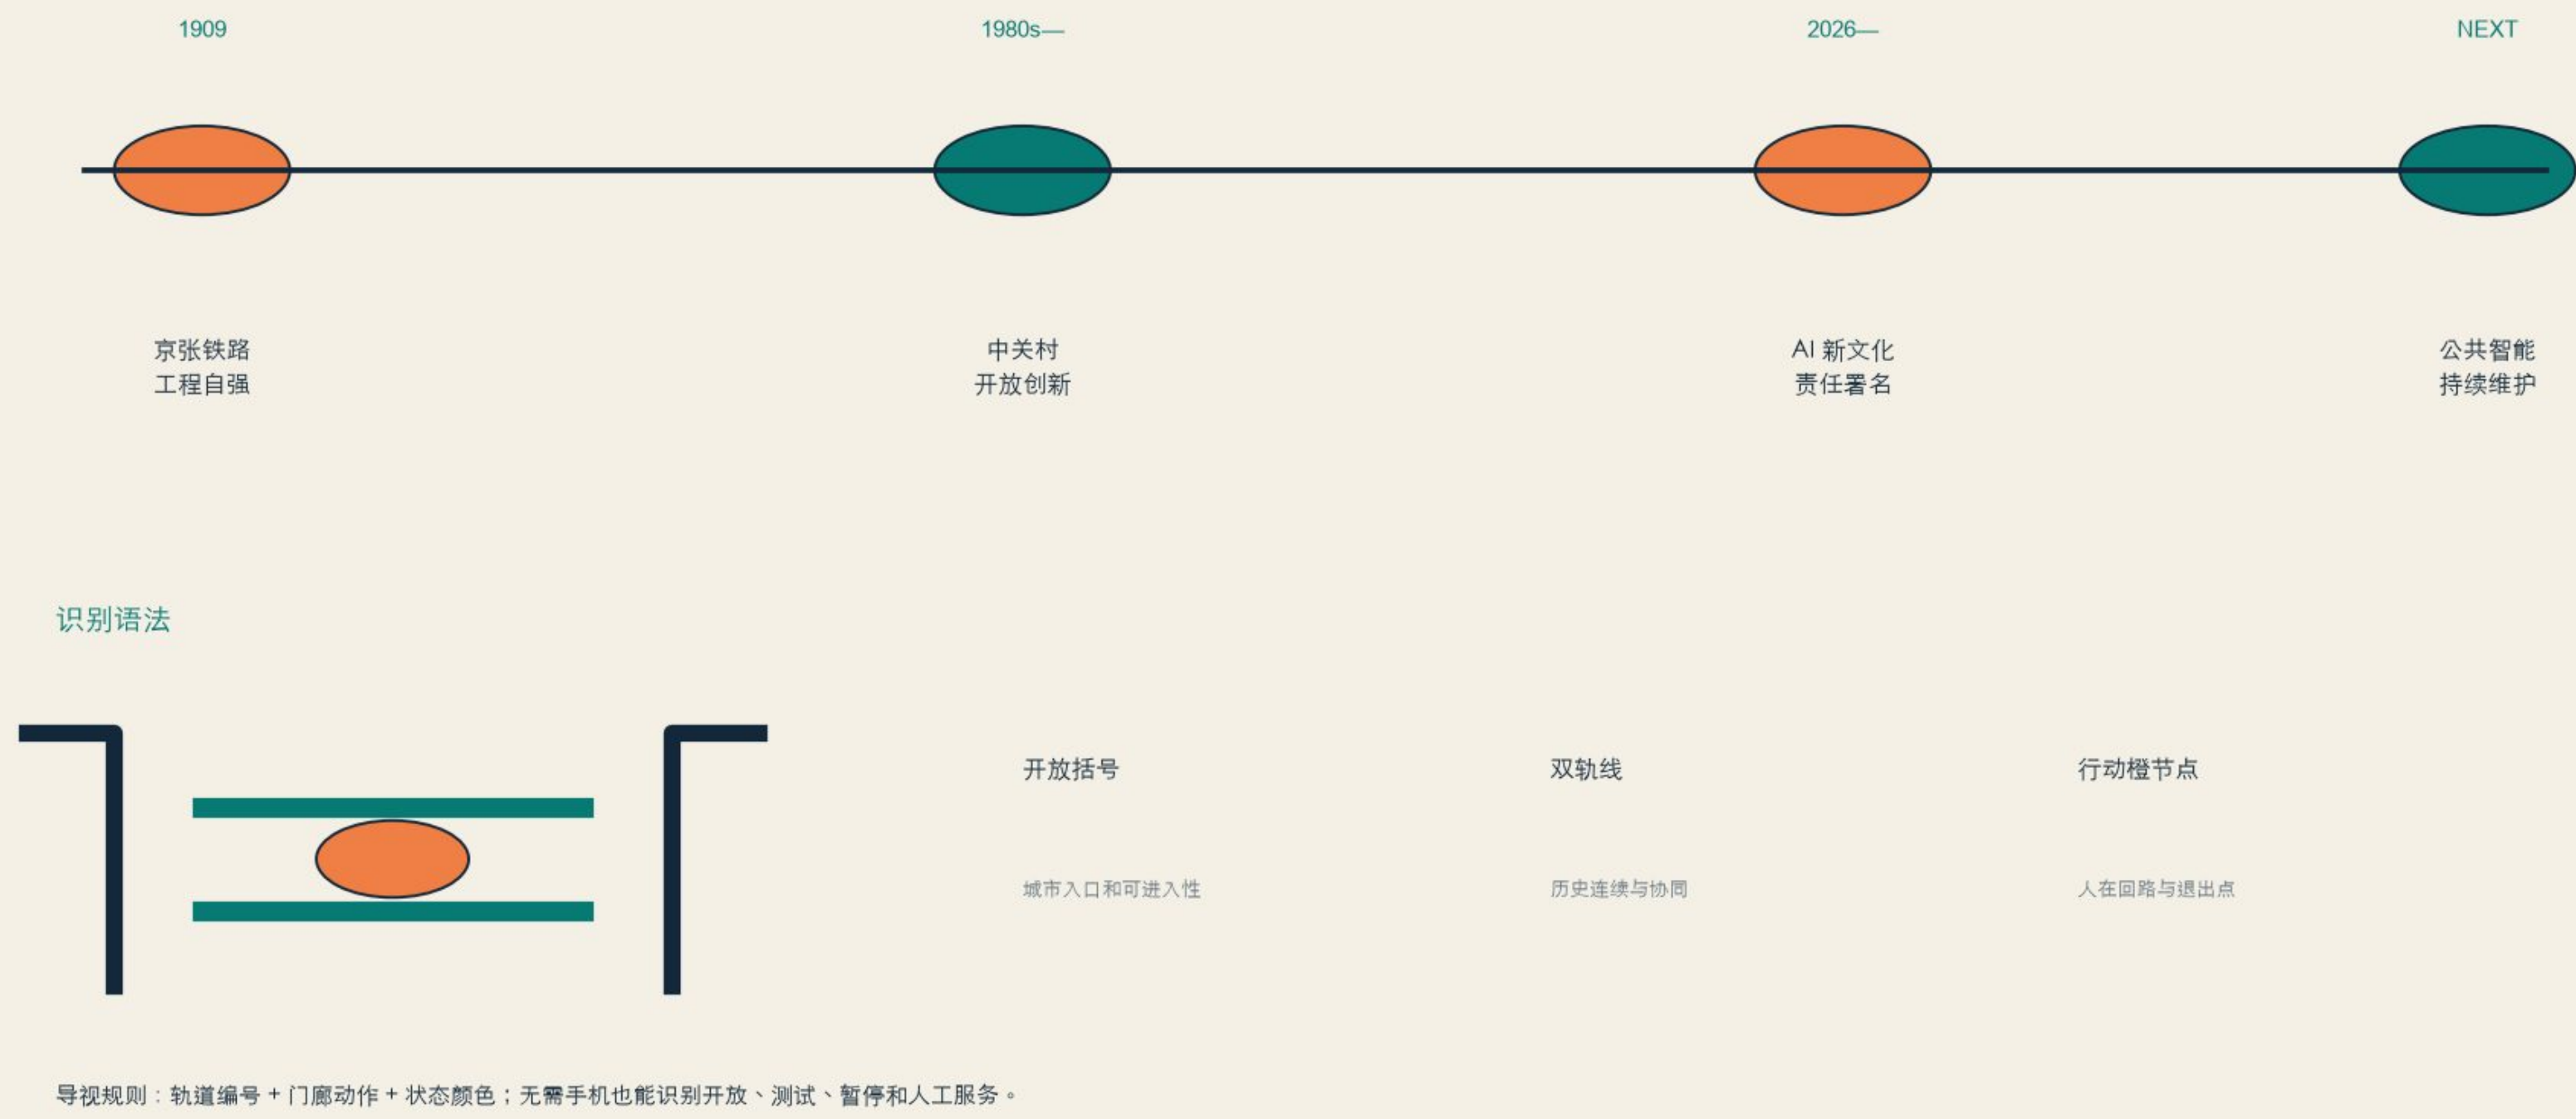


概念设计 · 临时边界 · 非官方红线

JING-ZHANG COMMON VERANDA · CONCEPTUAL URBAN DESIGN

AI 创新生态：研究—测试—采用—公共回报闭环

产业服务不只服务企业，也必须形成可见、可核验的城市公共收益

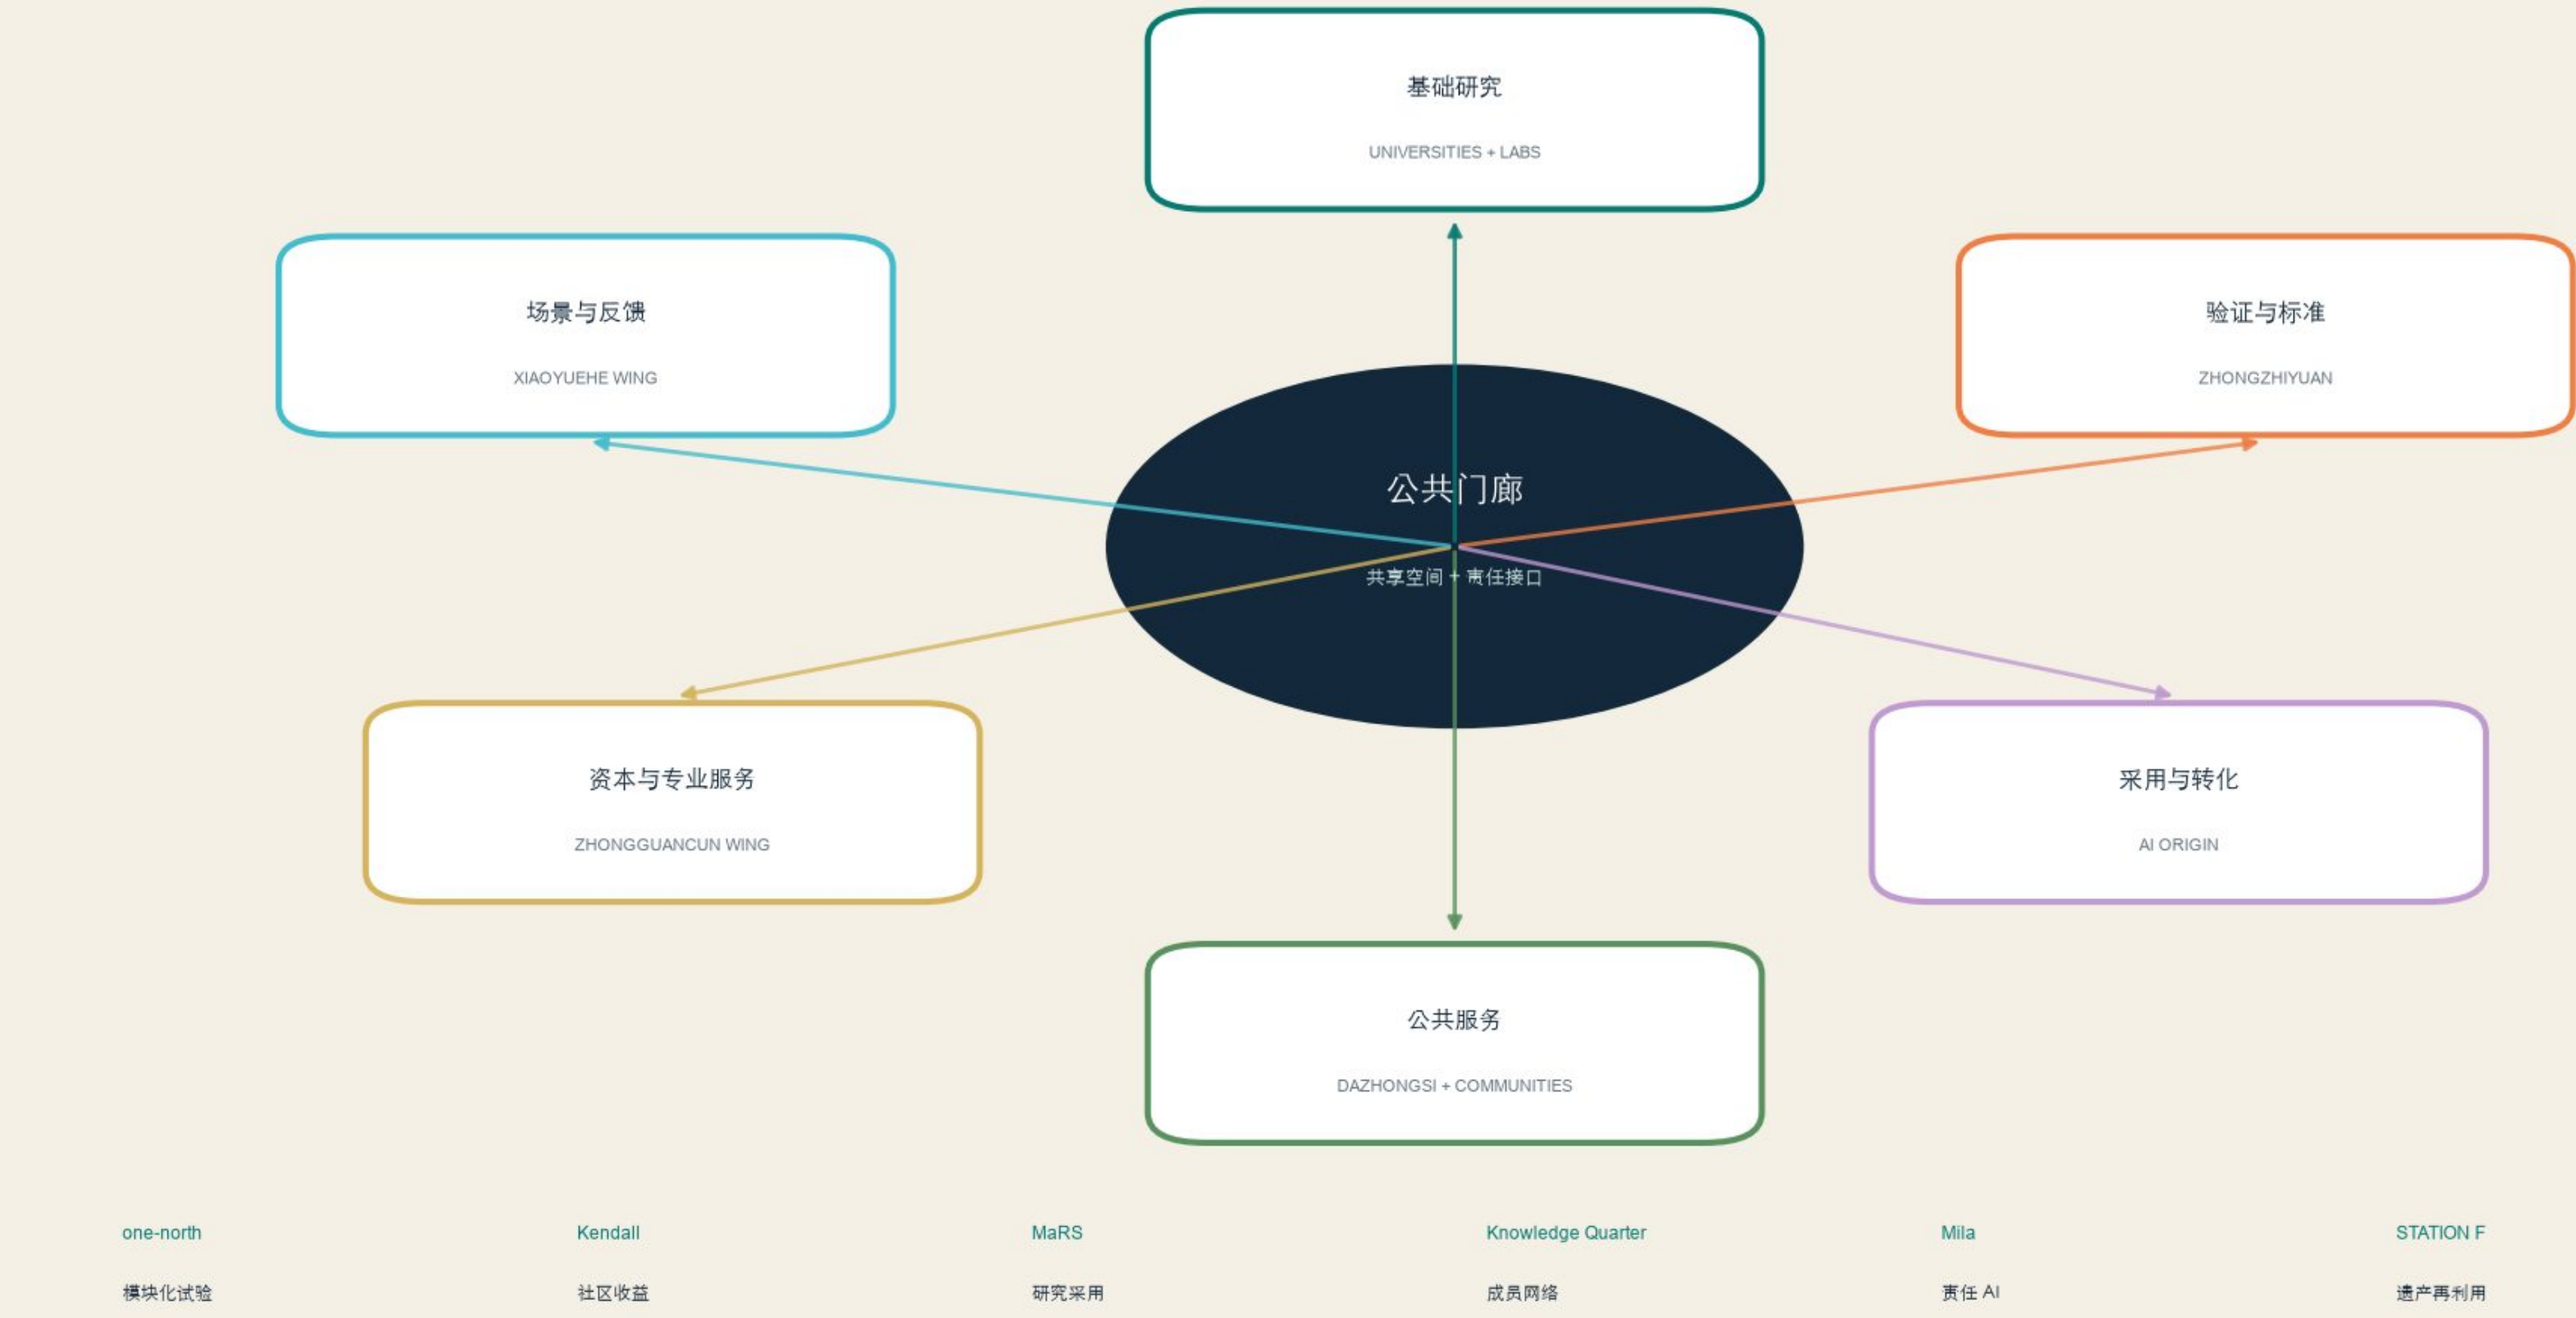

概念设计 · 临时边界 · 非官方红线

JING-ZHANG COMMON VERANDA · CONCEPTUAL URBAN DESIGN

门廊回执：一个可暂停的90天公共试验

只验证结构、停止与退出逻辑；尚未获批、未在现场运行



概念设计 · 临时边界 · 非官方红线

JING-ZHANG COMMON VERANDA · CONCEPTUAL URBAN DESIGN

可行性结论：先做公共基线，再做可逆试点

成熟度不是效果评分：它只表示当前证据离现场决策还有多远

现在 / NOW	0—6个月	6—18个月	取得官方资料后
方案与桌面证据	现场审计与公共基线	一处90天可逆试点	永久工程与跨线连接
01	既有公共空间与六门现场审计 可立即启动	责任：城市更新牵头＋无障碍共审 相对成本：S	前提：场地授权、现场测量 闸门：形成问题/权利/安全清单
02	遮阴、座椅、导视与人工服务基线 有条件可行	责任：场地运营＋公共空间专业 相对成本：S—M	前提：消防、市政、维护窗口 闸门：无维护责任则不开工
03	门廊回执90天桌面到现场试点 桌面可行 / 现场待授权	责任：试点发起者＋现场管家＋数据/IP 相对成本：M	前提：G0—G6全部签署 闸门：任一闸门失败即转人工并回滚
04	跨铁路、桥梁与永久建筑工程 当前不可实施	责任：主管部门＋权利人＋多专业总师 相对成本：L	前提：官方红线/GIS、权属、勘察、审批 闸门：资料未齐保持概念，不出工程结论

底线：没有官方几何、权属、勘察和专业审批，不把概念图变成施工图；没有运营、人工替代和退出资金，不开启智能层。

概念设计 · 临时边界 · 非官方红线

JING-ZHANG COMMON VERANDA · CONCEPTUAL URBAN DESIGN

十二个工程包：空间动作必须带着责任和退出

S/M/L为相对成本档，不是投资估算；真实金额等待工程量、权属和专业设计

众智园 · 实验	AI原点 · 学习	大钟寺 · 生活
4个可交接工程包	4个可交接工程包	4个可交接工程包
01 测试申请与解释厅 M G0-G3	05 开源发布厅 S G2-G3	09 轨道到达客厅 L G1-G5
02 低缝机器人沙盘 L G1-G4	06 门廊回执90天试验 M G0-G6	10 责任零售柜台 M G2-G6
03 红队评测庭院 M G2-G6	07 公共学习阶 S G1-G5	11 长者服务导航 M G1-G6
04 能源安全审计亭 S G3-G6	08 无障碍学习环 M G1-G6	12 百年公共账本钟 S G3-G6

每包必须补齐：牵头角色 · 专业依赖 · 相对成本 · 维护窗口 · 验收门槛 · 停止/撤除条件 · P1/P2/P3窗口

概念设计 · 临时边界 · 非官方红线

JING-ZHANG COMMON VERANDA · CONCEPTUAL URBAN DESIGN

实施与运营：先建立公共基线，再接入智能服务

每一期都设置进入条件、公开证据、责任主体和回退门槛



概念设计 · 临时边界 · 非官方红线

JING-ZHANG COMMON VERANDA · CONCEPTUAL URBAN DESIGN

长期运营：谁维护、谁响应、何时退出

没有维护窗口、人工等价服务和退出资金，智能层就不开启

每日 / DAILY 开放、无障碍、告知、人工、事件	每月 / MONTHLY 维护者会客厅、未结修复、异议	每季 / QUARTERLY 公开运行/暂停/申诉/修复回执	每年 / ANNUAL Open Veranda Week、资产与许可审计
资金前置 运营责任人 维护与备件窗口 人工服务排班 保险与退出资金	公共账本 OPEN / TEST / PAUSED状态 投诉与申诉 修复与复核 继续 / 修改 / 退役	开放品牌治理 标识可署名复用 状态断色不得删除 AI内容保持显式标识 所有变化有日期与版本	

季度未能公开责任、核算和退出证据时，相关场景默认进入PAUSED；两季仍未闭环则提交退场决定。

概念设计 · 临时边界 · 非官方红线

JING-ZHANG COMMON VERANDA · CONCEPTUAL URBAN DESIGN

六门证据表：不用虚构横跨轨道的捷径

每一门先说现状接口、物理冲突和设计规则

G1	大钟寺	站点四象限：停车、换乘、气口冲突	审计现有骑行：不靠平面穿轨
G2	知春路	一期南端：道路与轨道叠加	只用现有或专业论证过街
G3	北四环	桥下活动与通行混合	球场、排队、座椅退出直行带
G4	成府路一五道口	商业、地铁、骑行高峰	步行连接：骑行窄段设城市道路
G5	清华东路西口	已批公共空间与自行车停放	补责任和服务：不重复售票
G6	北五环—清河南缘	二期在建：开放条件未定	竣工验收前不承诺连续开放

概念设计 · 临时边界 · 非官方红线

JING-ZHANG COMMON VERANDA · CONCEPTUAL URBAN DESIGN

指标、证据与风险：能复算的才写数，不能确认的写触发条件

本轮数值只比较概念方案内部空间分配，不构成法定规划指标




质量结论：结构化校验通过只代表可进入内容评审；空间质量仍由真实底图、设计判断、图纸表达与专业团队复核共同决定。

概念设计 · 临时边界 · 非官方红线

JING-ZHANG COMMON VERANDA · CONCEPTUAL URBAN DESIGN

区域协作不是连线，而是可退出的证据接口

每个节点只承诺输入、最低输出、责任类型与停止条件

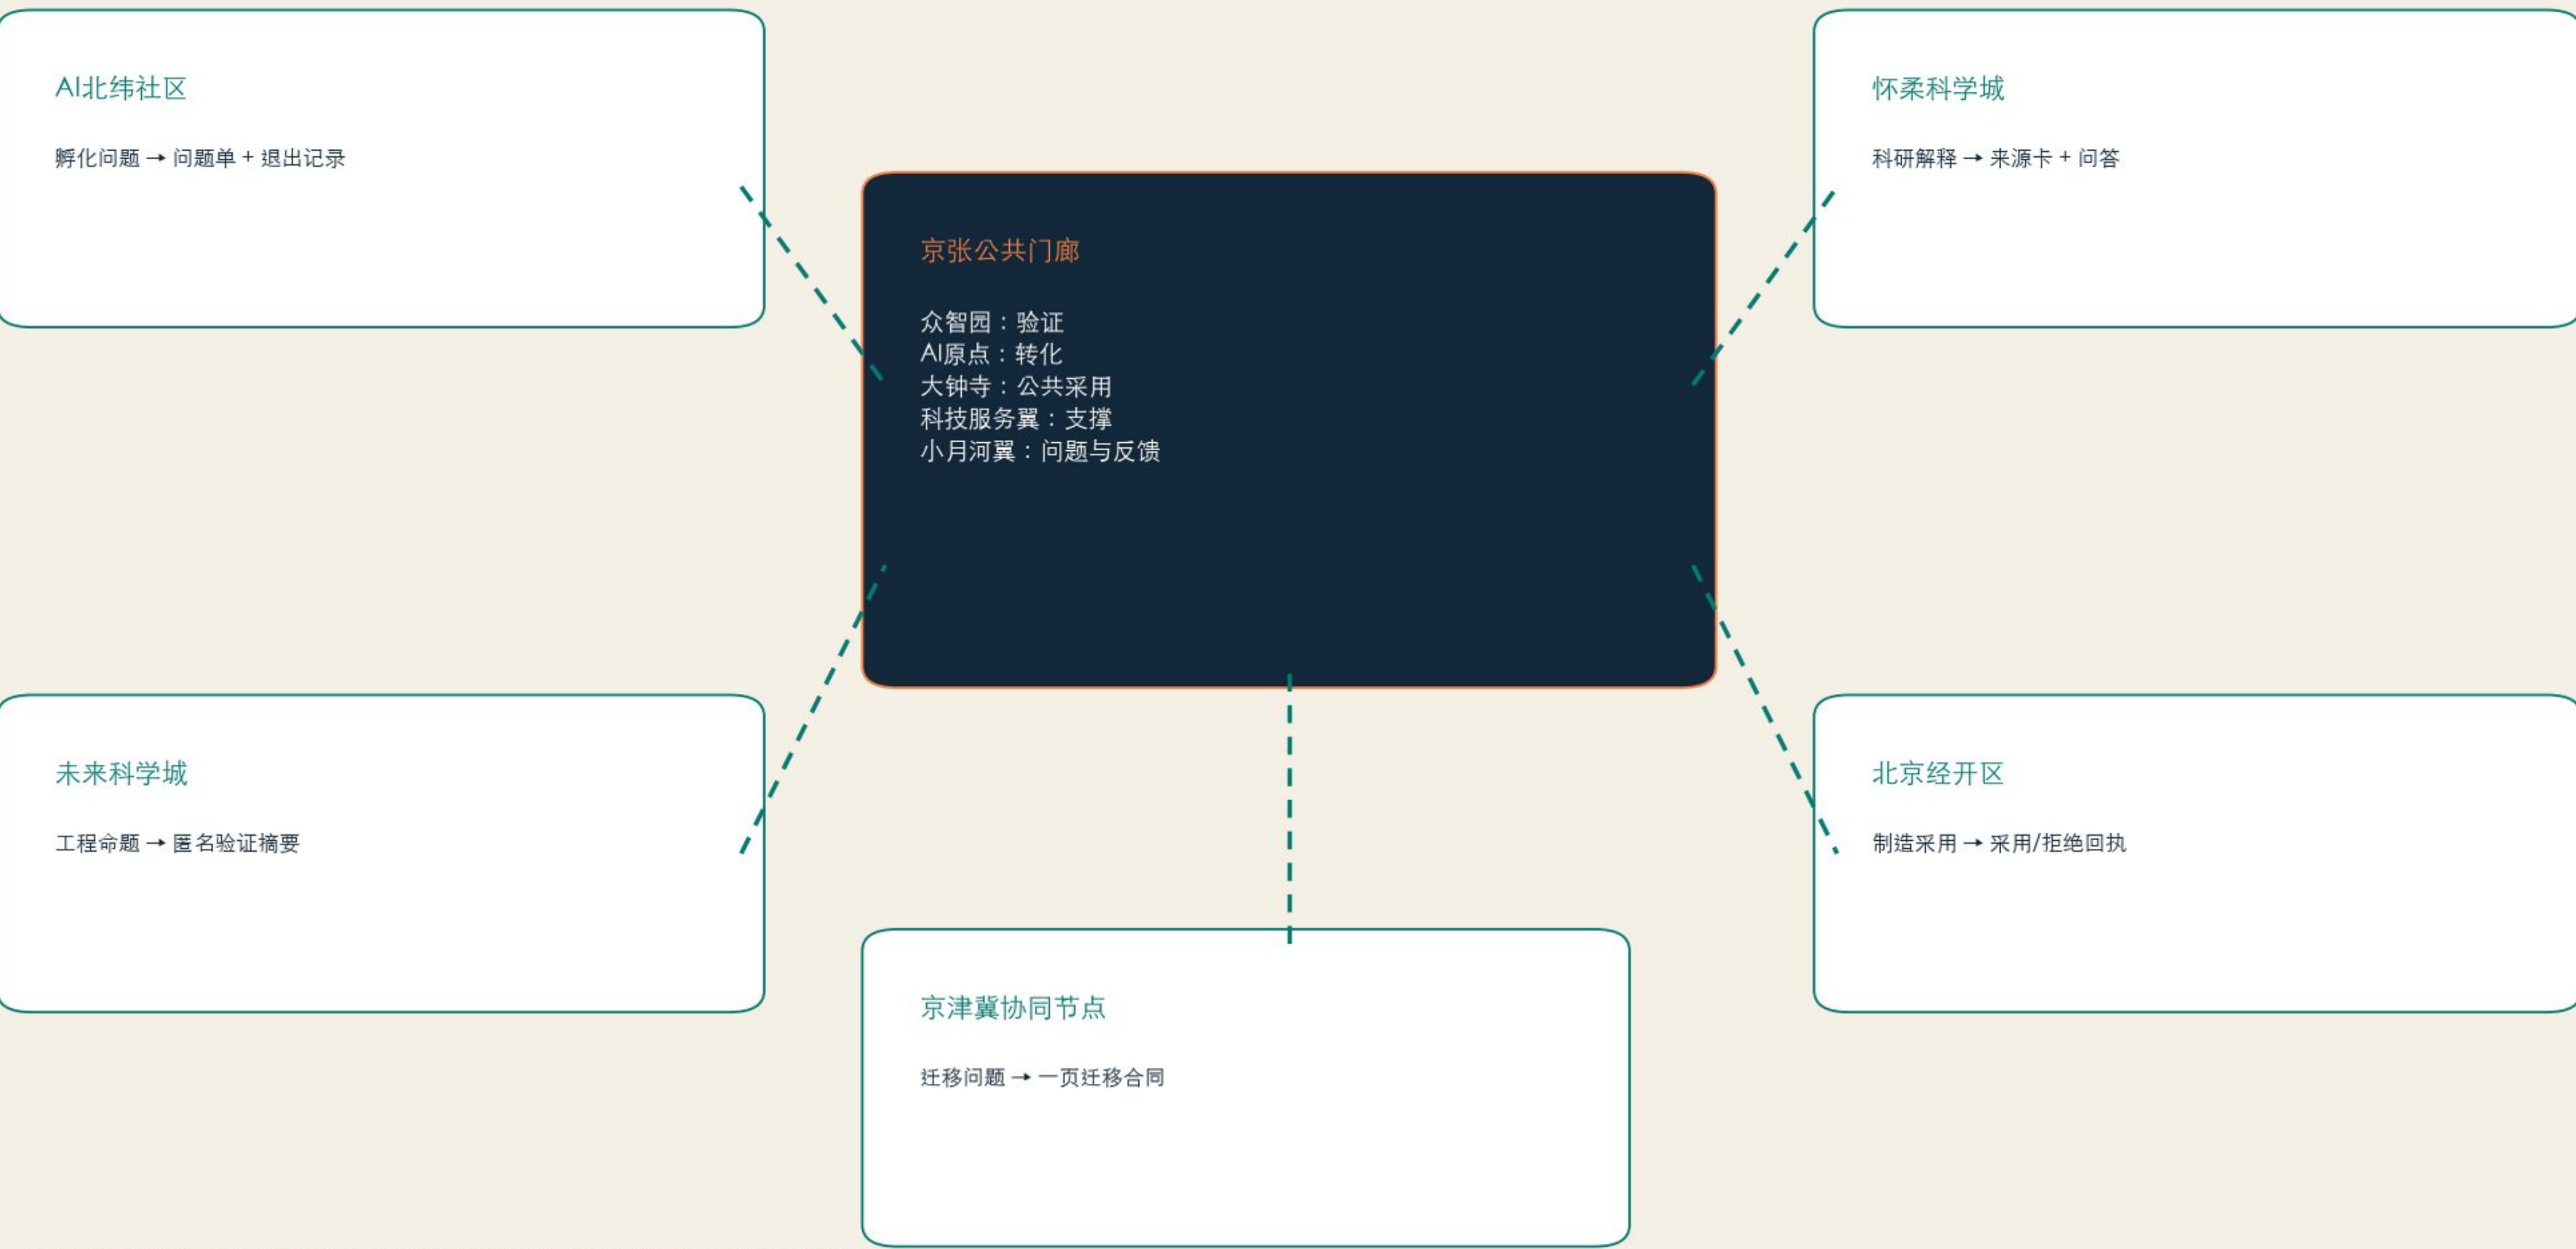


概念设计 · 临时边界 · 非官方红线

JING-ZHANG COMMON VERANDA · CONCEPTUAL URBAN DESIGN

设计结论：一条公共门廊、六个城市门、三层实施证据

现状基线、概念建议与待专业深化内容在图纸中明确分开

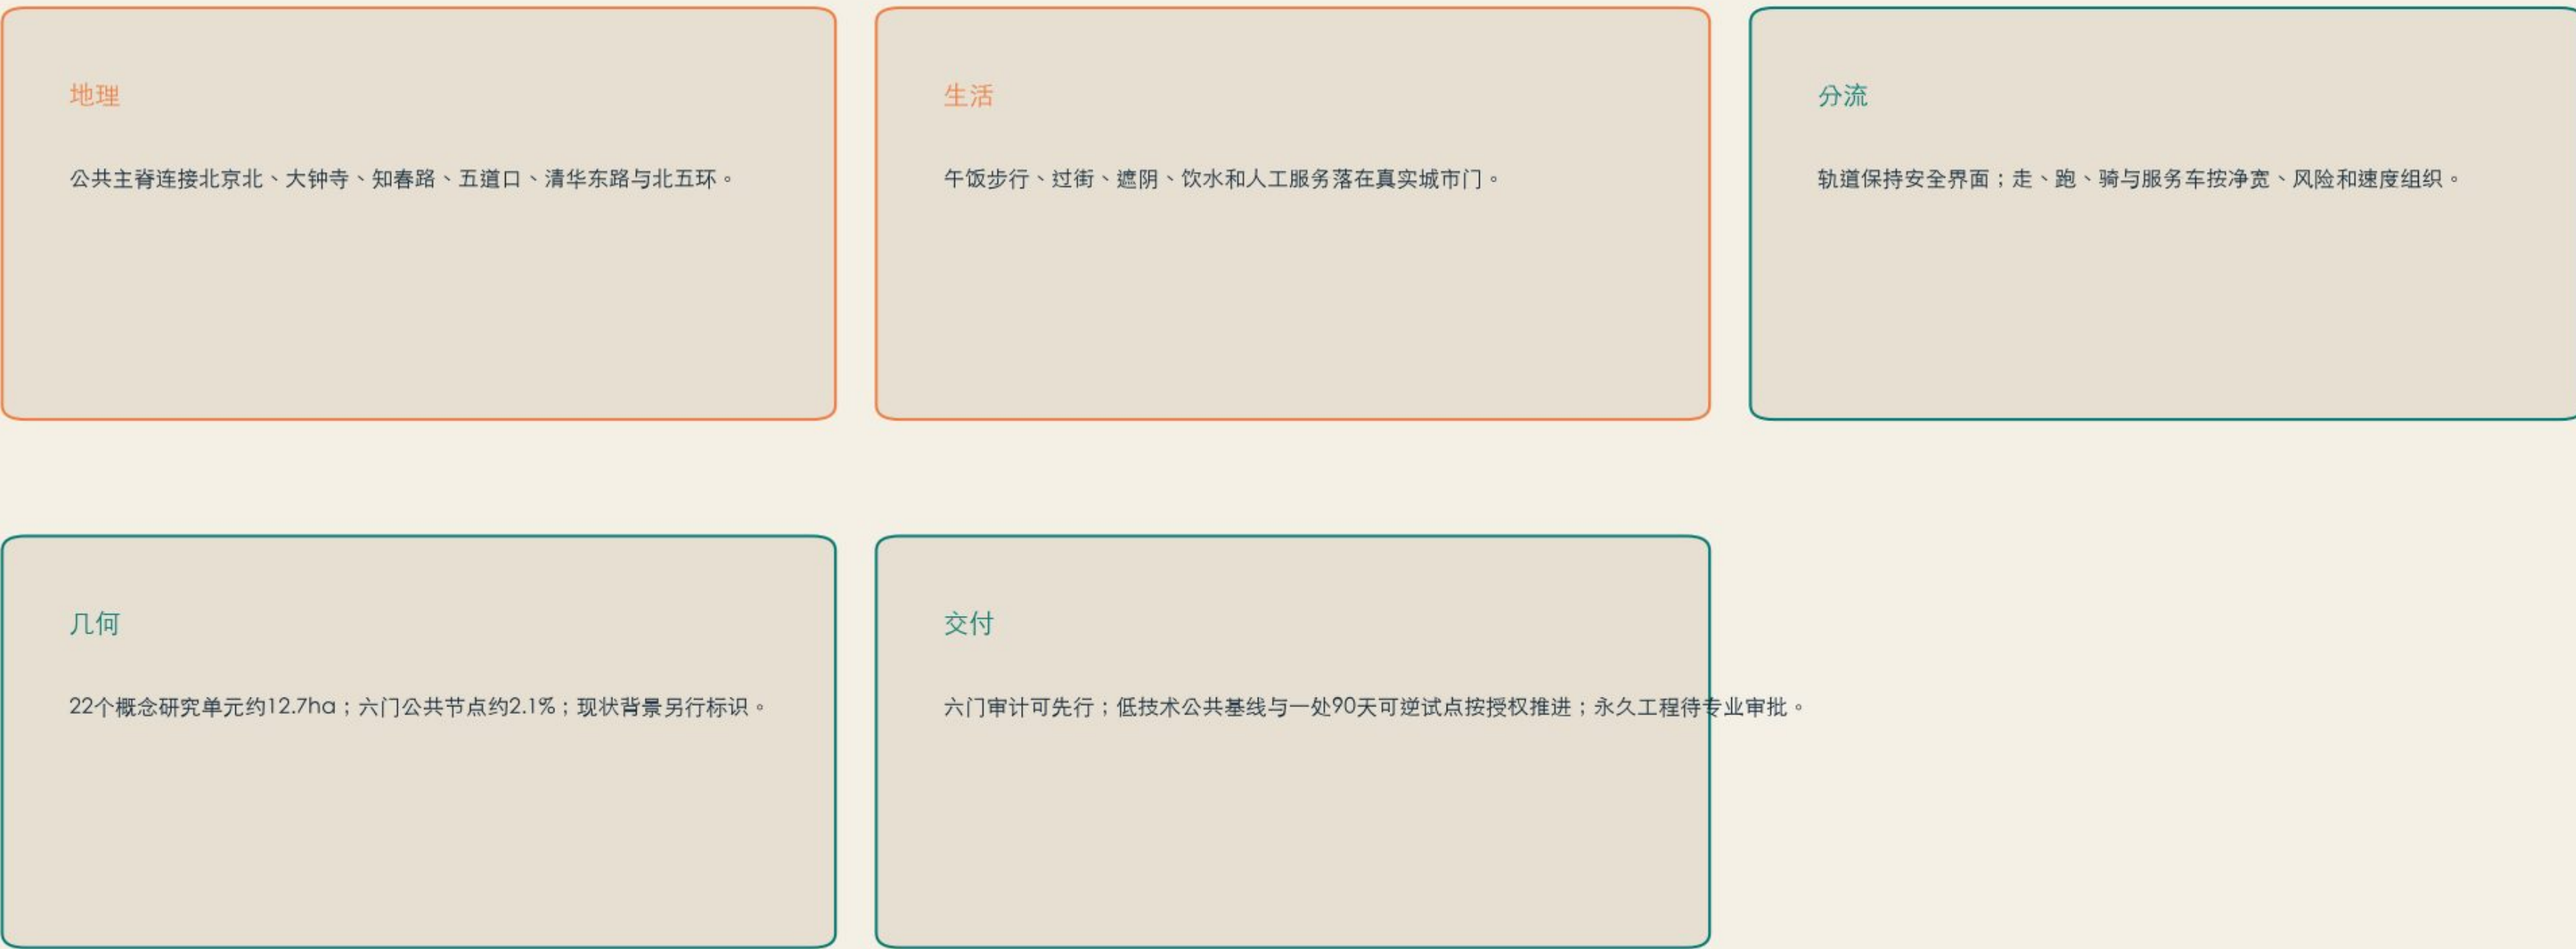

概念设计 · 临时边界 · 非官方红线

JING-ZHANG COMMON VERANDA · CONCEPTUAL URBAN DESIGN