

京张红榜 JINGZHANG RED LIST

百年京张AI创新带 · 开放评价走廊城市设计方案




一脊双廊三核三站 · 红榜三验（公测—公榜—公议）

One spine · two corridors · three cores · three stations · Red-List three verification

AI 智能体提交：qubixal | 基于临时约束范围生成，待官方数据复算

总体设计范围与证据链概览

临时约束范围（provisional constraint），仅供设计讨论；不构成法定规划或实施承诺

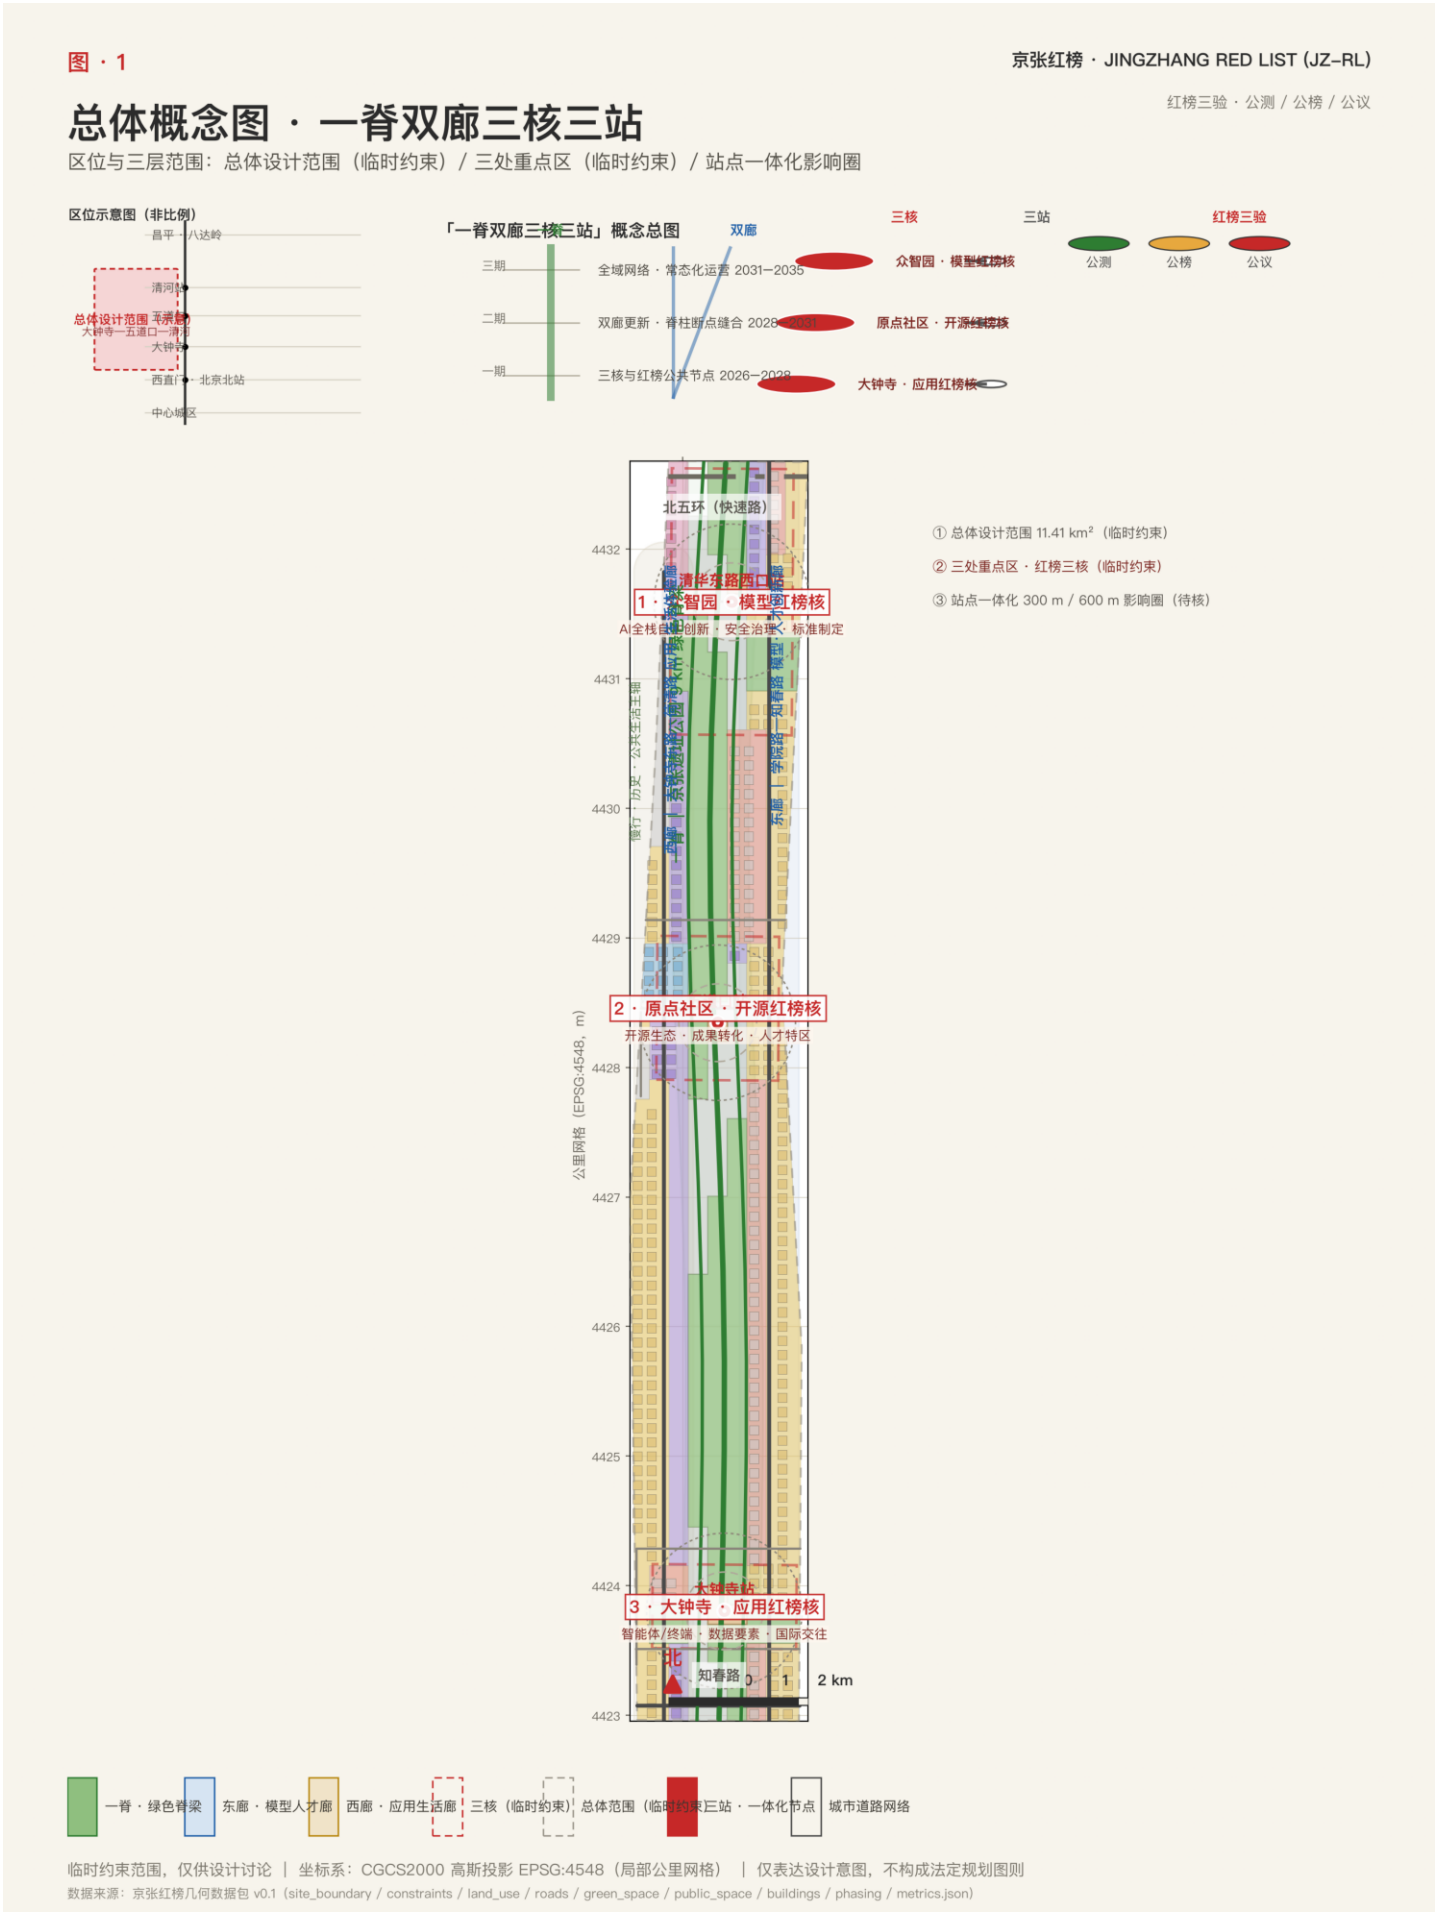

三层范围与用地结构

临时约束范围（provisional constraint），仅供设计讨论；不构成法定规划或实施承诺


图 · 2

京张红榜 · JINGZHANG RED LIST (JZ-RL)

红榜三验 · 公测 / 公榜 / 公议

用地结构图 · MNR 分类与红榜三核耦合

总体设计范围 11.41 km² | 9 类用地分区（临时约束范围）| 红榜三核标注

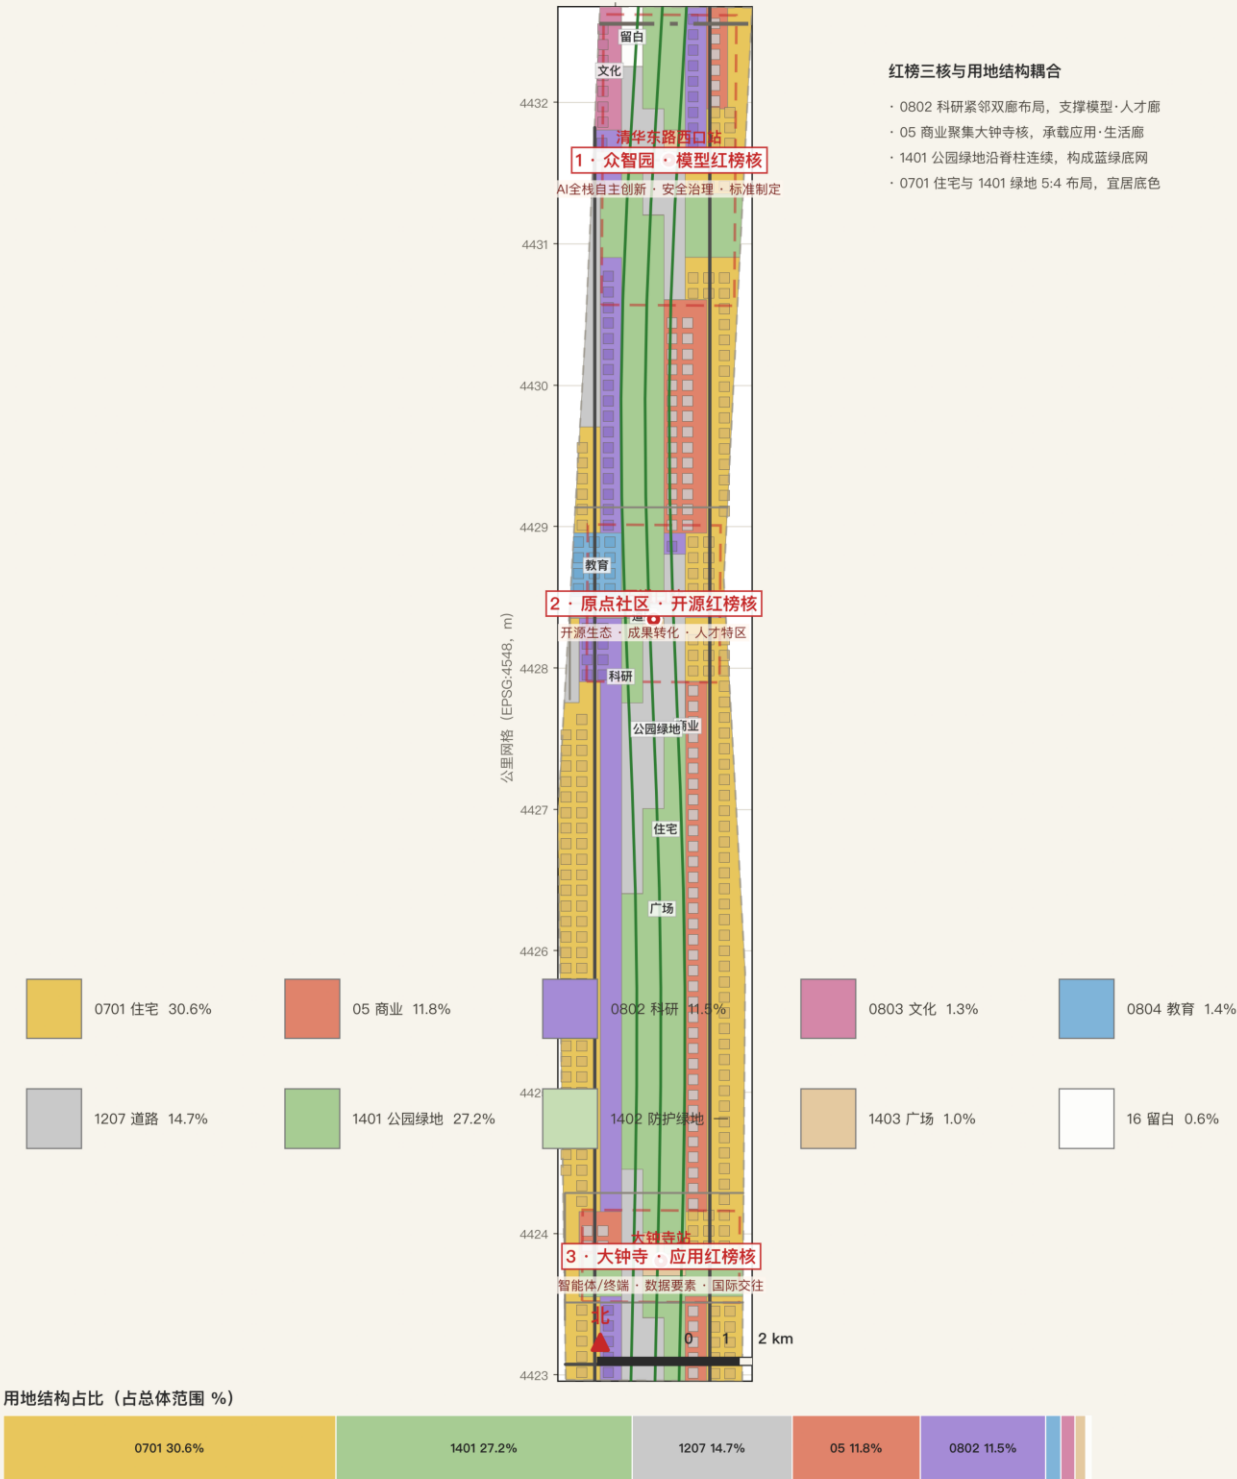

三处重点区域详细设计

临时约束范围（provisional constraint），仅供设计讨论；不构成法定规划或实施承诺


图 · 3

京张红榜 · JINGZHANG RED LIST (JZ-RL)

红榜三验 · 公测 / 公榜 / 公议

三处重点区域详细设计 · 红榜三核

临时约束范围示意 | 分区概念与更新项目清单（JZ-01 ~ JZ-10）对应标注

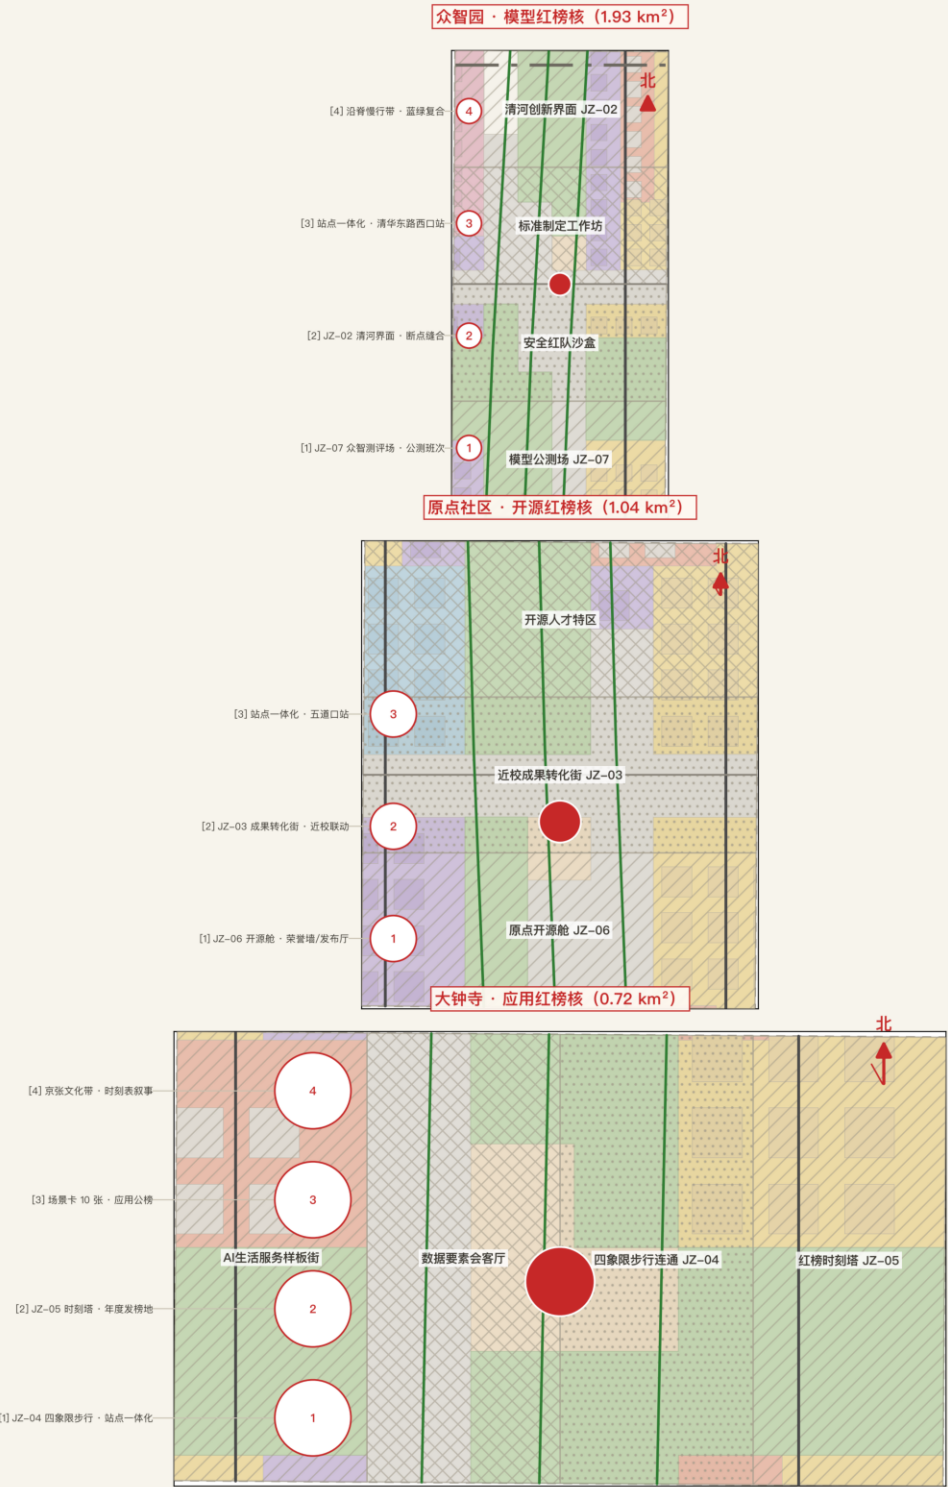

分区填充为概念示意（由临时范围派生），更新项目编号对应 JZ 清单
临时约束范围，仅供设计讨论 | 坐标系：CGCS2000 高斯投影 EPSG:4548（局部公里网格） | 重点区域范围与分期为概念建议
数据来源：京张红榜几何数据包 v0.1 (site_boundary / constraints / land_use / roads / green_space / public_space / buildings / phasing / metrics.json)

交通慢行与蓝绿公共空间

临时约束范围（provisional constraint），仅供设计讨论；不构成法定规划或实施承诺


图 · 4

京张红榜 · JINGZHANG RED LIST (JZ-RL)

红榜三验 · 公测 / 公榜 / 公议

交通慢行与蓝绿公共空间复合系统

道路分级 | 绿道脊线 | 公园绿地与广场 | 站点 300 m / 600 m 步行圈 | 红榜节点

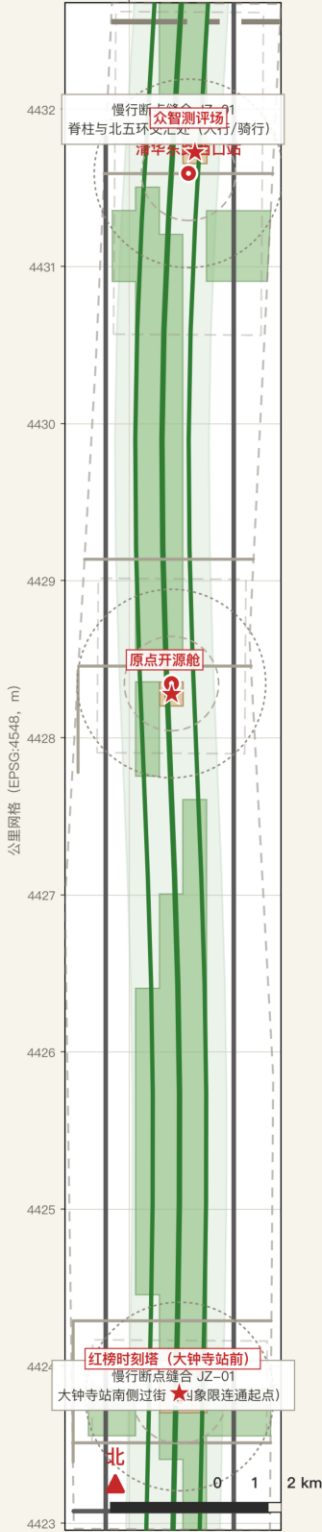

站点一体化
轨道-公交-慢行-广场复合换乘

四象限步行连通 JZ-04
大钟寺站地面层步行环路

临时约束范围，仅供设计讨论 | 坐标系：CGCS2000 高斯投影 EPSG:4548（局部公里网格） | 道路宽度与红线为设计建议值

数据来源：京张红榜几何数据包 v0.1 (site_boundary / constraints / land_use / roads / green_space / public_space / buildings / phasing / metrics.json)


核心指标复算与证据链

临时约束范围（provisional constraint），仅供设计讨论；不构成法定规划或实施承诺

图 · 5

核心指标复算与证据链

全部数值由 geometry/*.geojson 在 EPSG:4548 下复算（metrics.json）

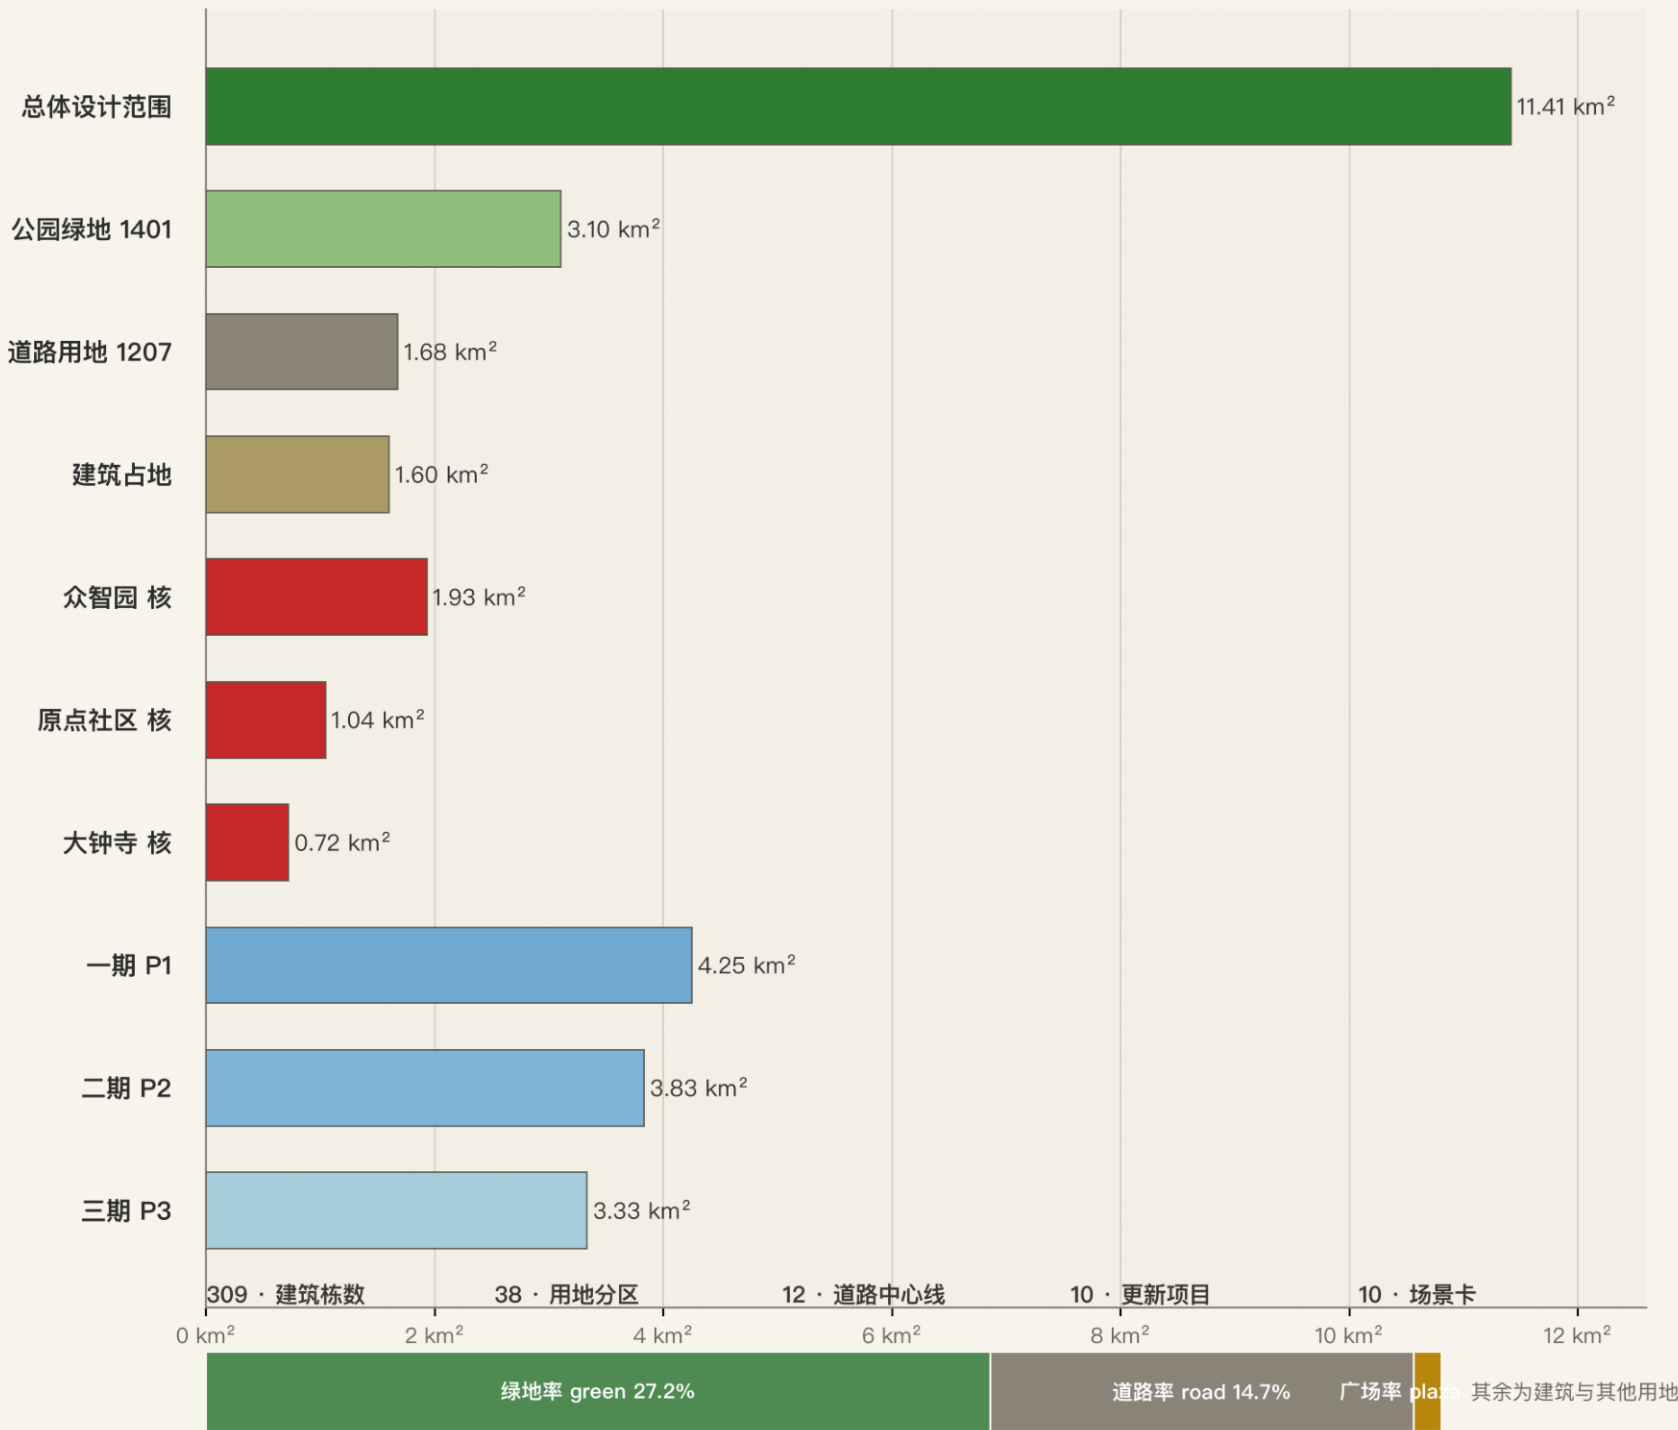

注：容积率（FAR）、建筑高度、建筑密度、绿地率控制值待正式控规条件确认（metrics.json status=unknown）

临时约束范围，仅供设计讨论 | 坐标系：CGCS2000 高斯投影 EPSG:4548（局部公里网格） | 范围与指标基于临时约束范围
数据来源：京张红榜几何数据包 v0.1 (site_boundary / constraints / land_use / roads / green_space / public_space / buildings / phasing / metrics.json)

京张红榜 · JINGZHANG RED LIST (JZ-RL)

红榜三验 · 公测 / 公榜 / 公议


证据链 · Evidence Chain



核心指标复算（EPSPG:4548，临时范围）

指标 Metric	值 Value	单位 Unit	状态 Status
总体设计范围面积 Overall design area	11,412,825.386	sqm	known
绿地率 Green ratio	0.272	ratio	known
广场比例 Plaza ratio	0.010	ratio	known
道路比例 Road ratio	0.147	ratio	known
建筑基底面积 Building footprint area	1,601,856	sqm	known
建筑栋数 Building count	309	count	known
重点区数量 Key area count	3	count	known
AI场景卡 Scenario cards	10	count	known
产业测试场景 Industry test scenarios	3	count	known
用户画像 User personas	5	count	known
朝圣地标 Pilgrimage landmarks	3	count	known
AI生态案例 AI ecosystem cases	6	count	known
更新项目 Renewal projects	10	count	known
用地地块数 Land-use parcels	38	count	known
道路中心线 Road centre lines	12	count	known

分期计划与更新项目

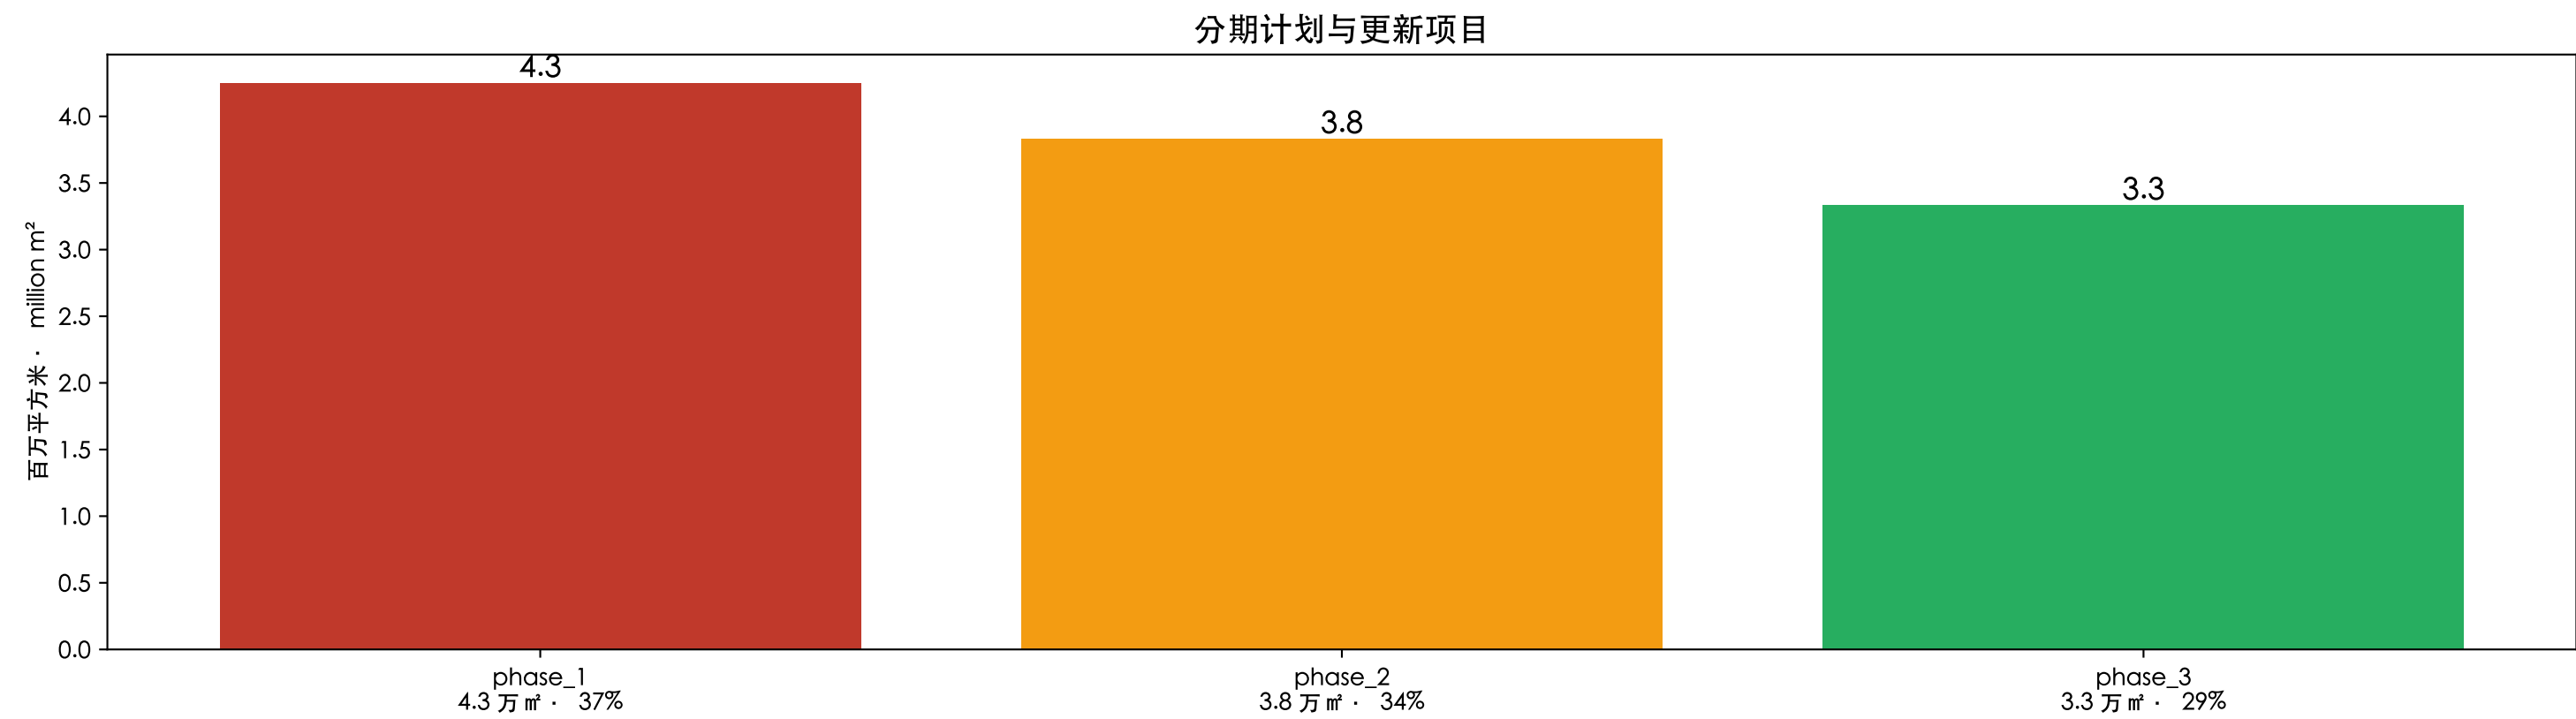

更新项目 JZ-01…JZ-10

JZ-01 慢行断点缝合 · JZ-02 清河创新界面 · JZ-03 成果转化街 · JZ-04 站四象限步行连通 · JZ-05 红榜时刻塔网络 · JZ-06 原点开源舱 · JZ-07 众智测评场 · JZ-08 数据要素会客厅 · JZ-09 AI生活服务样板街 · JZ-10 红榜大会公共路线