


Three-level scope: Coordinated Research Area approx. 43.6 km² (strategy and regional synergy), Overall Design Area approx. 11.4 km² (urban renewal at RDP depth), Key-Area Detailed Design Area approx. 368.4 ha (three archive stations). The levels are continuous: research explains why the belt exists, design turns judgments into recomputable land use and projects, key areas verify implementability.

Risk and compliance: full recalculation when official boundaries are released; control/redline/ownership/heritage gaps are listed as assumptions; archive facilities collect no personal trajectories; honors are human-final; no official approval or implementation commitment is claimed.

JZ Archive Belt · Concept Overview

Memory Spine · Three Archive Stations · Two Record Wings
Zhongguancun Technology Services Wing (Factor Record)

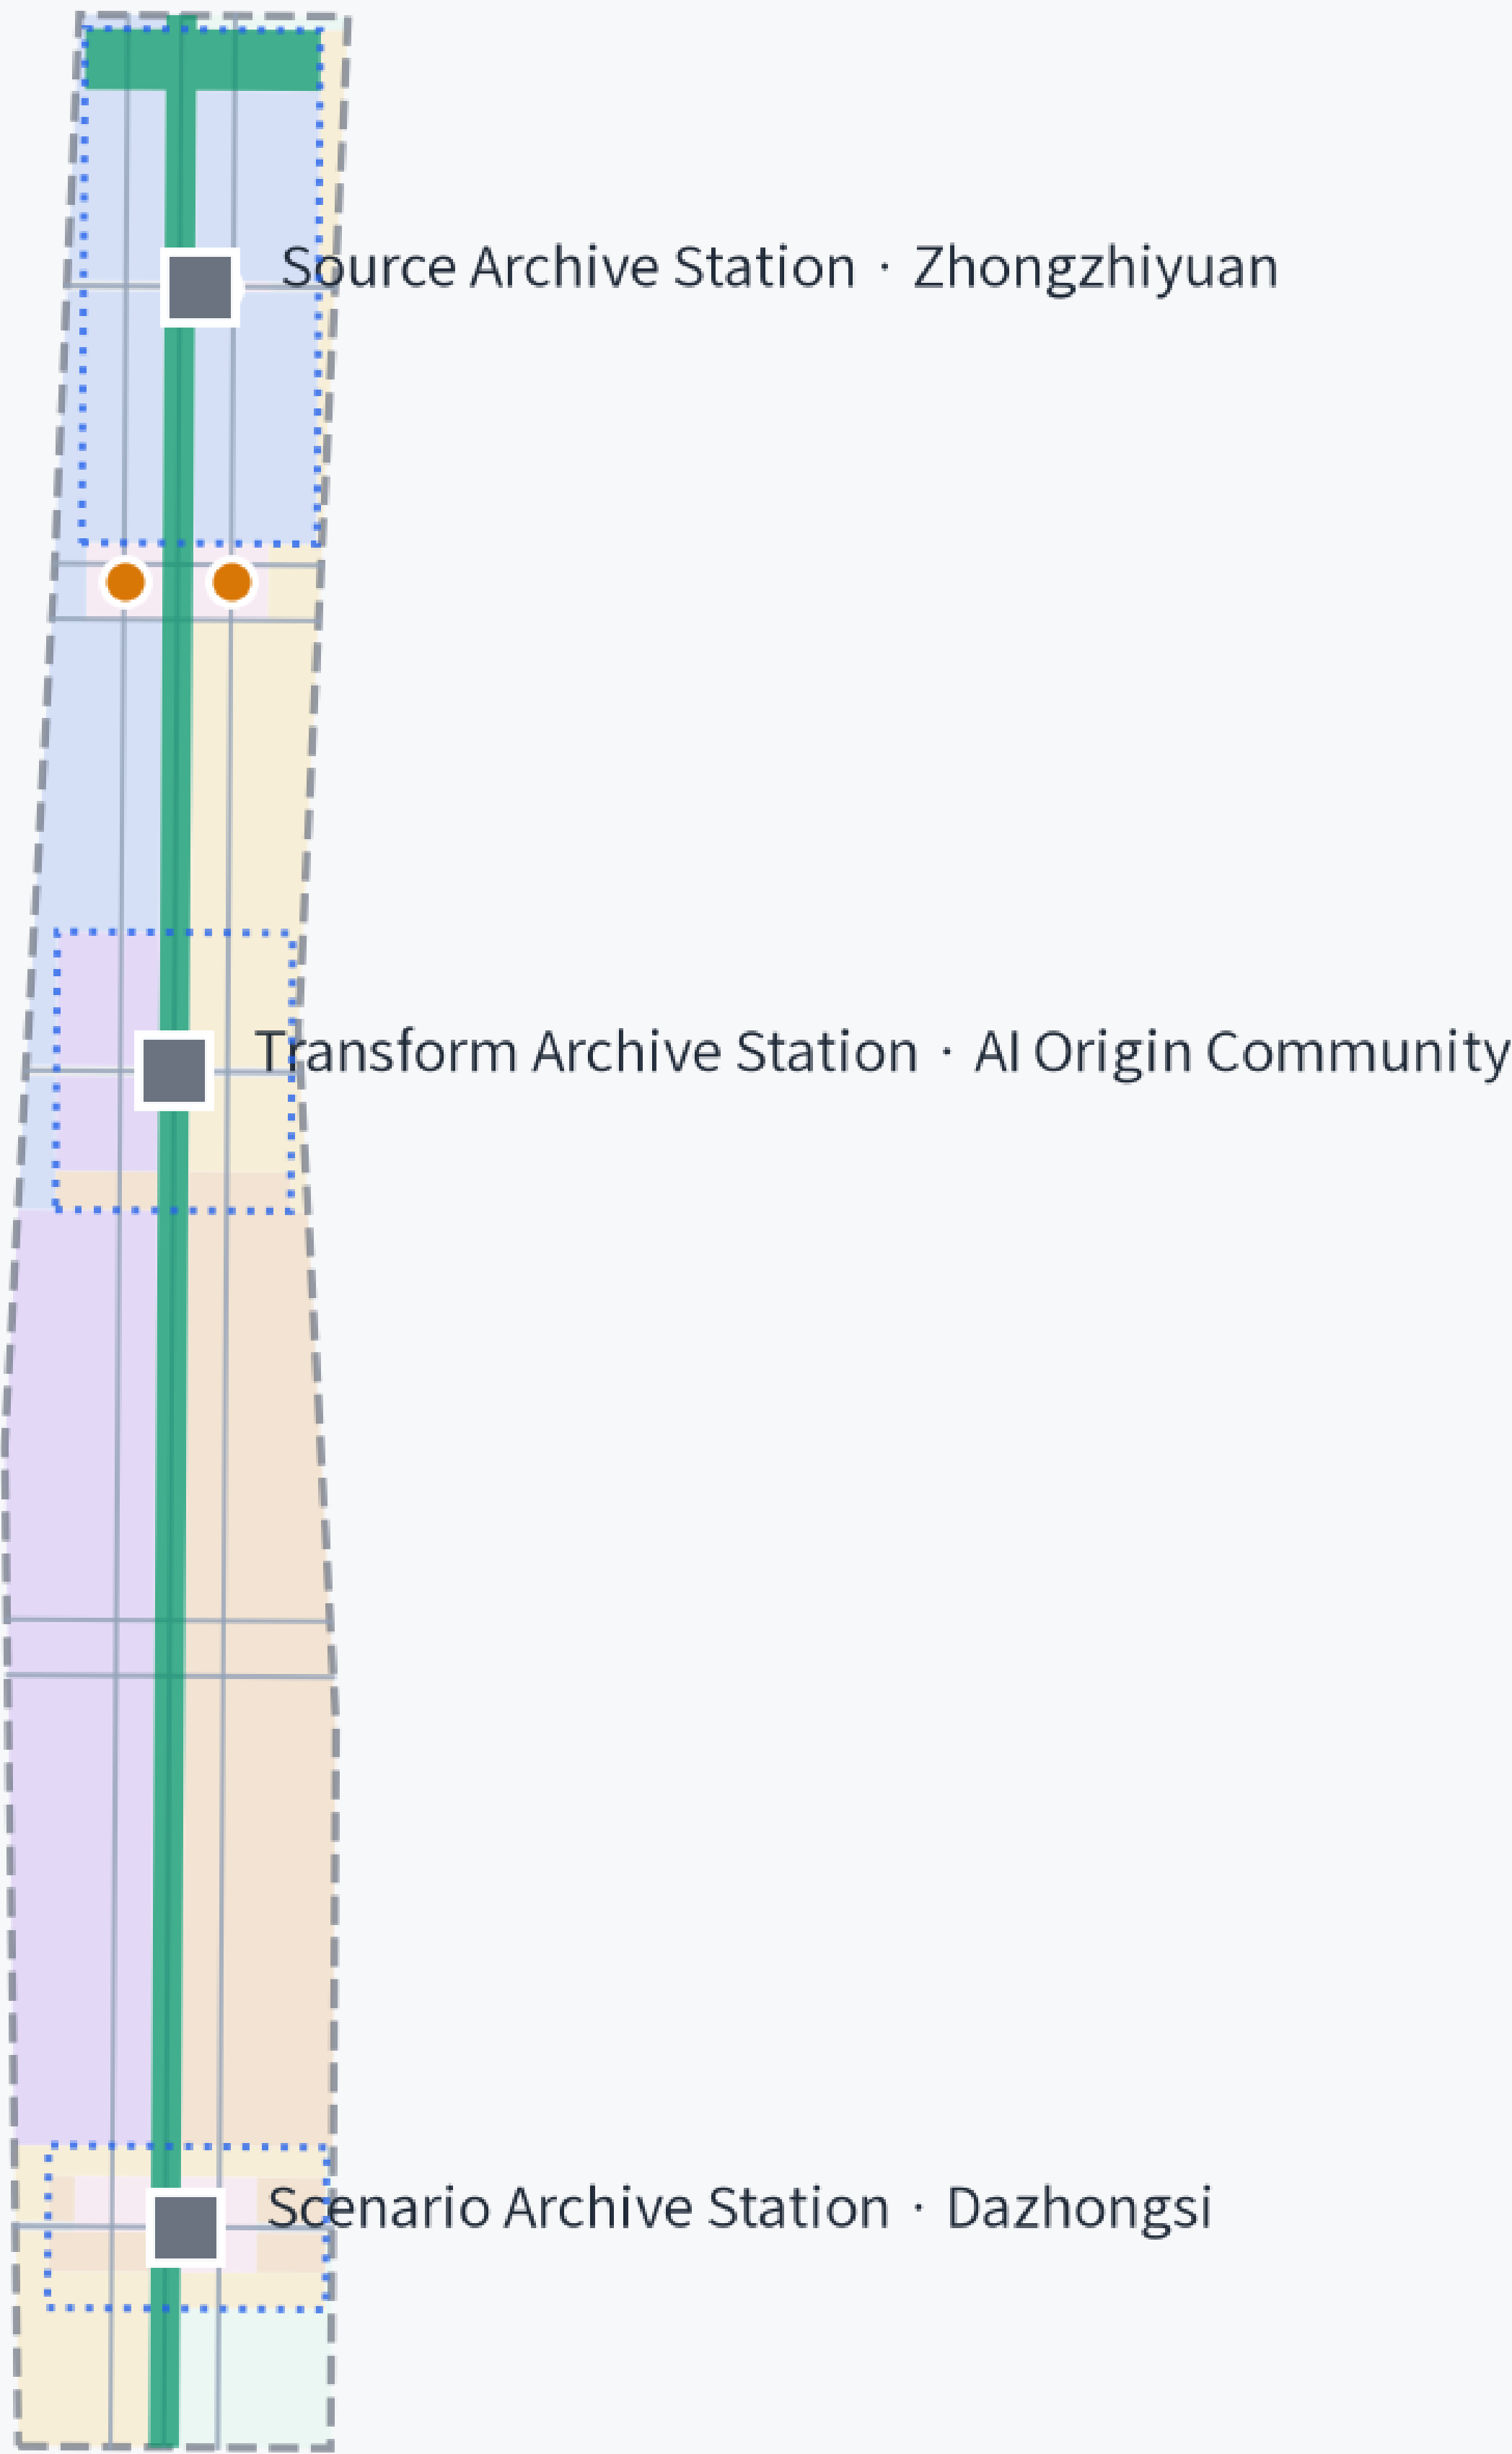

Write open co-creation into the city archive: contributions, services, corrections and honors all enter the archive

Three-level scope

- Coordinated Research Area 43.6 km²
- Overall Design Area 11.4 km²
- Key-Area Detailed Design Area 368.4 ha

01	Source Archive Station · Zhongzhiyuan Source / contribution
02	Transform Archive Station · AI Origin Community Transform / correction
03	Scenario Archive Station · Dazhongsì Scenario / public service

Xiaoyue River Scenario Enablement Wing (Scenario Record)


Boundaries are provisional, not official redlines; full recalculation required after official data release

Spatial structure: one belt (Memory Spine) · three stations (Source/Transform/Scenario) · two wings (Zhongguancun factor record, Xiaoyue scenario record) · multiple points (name wall/Honor Yearbook/commit stele) · two networks (blue-green slow traffic and archive retrieval). Renewal uses archive-based units: anchors + spine stitching + low-disturbance micro-renewal.

Risk and compliance: full recalculation when official boundaries are released; control/redline/ownership/heritage gaps are listed as assumptions; archive facilities collect no personal trajectories; honors are human-final; no official approval or implementation commitment is claimed.

JZ Archive Belt · Land Use and Spatial Structure

Research · Education · Commercial · Residential · Blue-Green · Reserve

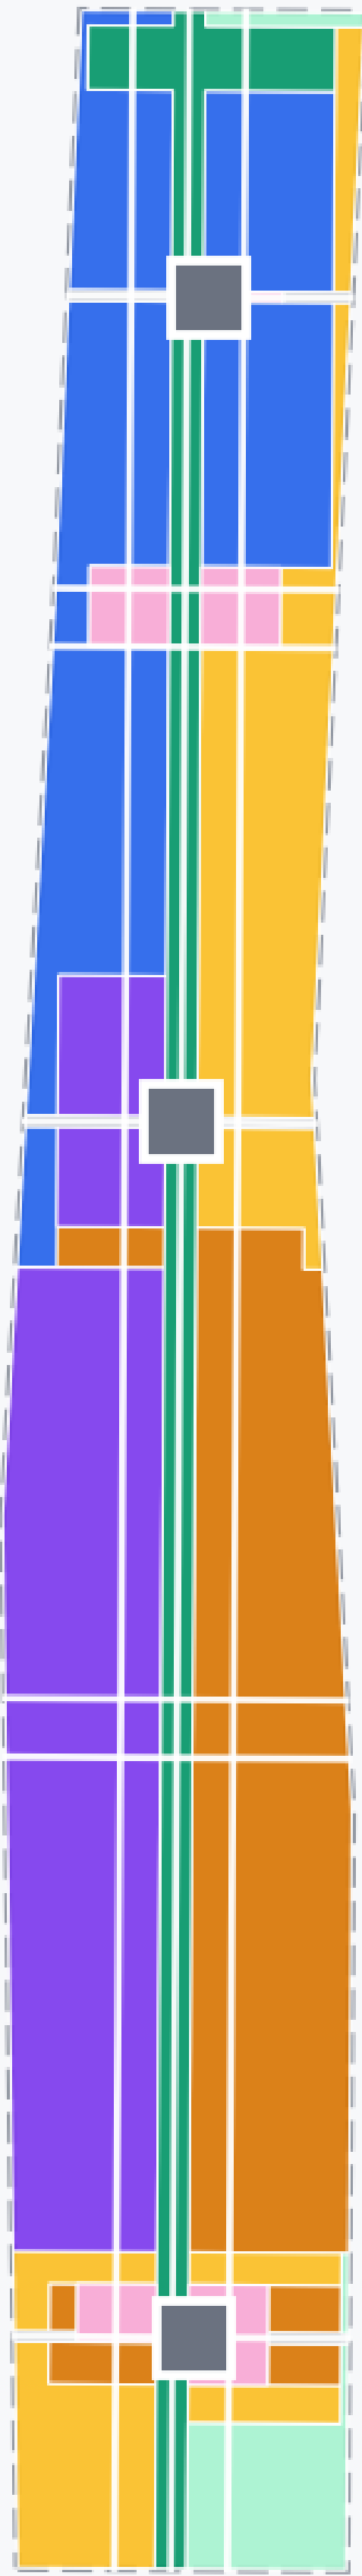

Land-use composition

- Research 0802 236 ha
- Education 0804 254 ha
- Commercial 05 244 ha
- Residential 0701 185 ha
- Park green 1401 135 ha
- Shelter green 1402 39 ha
- Plaza 1403 39 ha
- Road 1207 9 ha

Adjacent polygons share grid edges; union equals boundary


Boundaries are provisional, not official redlines; full recalculation required after official data release

13 conceptual renewal projects in three phases: Phase 1 spine stitching and archive anchors; Phase 2 test blocks and data platform; Phase 3 the two archive stations. Each item lists prerequisites, possible procedures subject to professional confirmation, resource-and-acceptance study items and rollback triggers (safety/privacy/heritage/ecology/economy), with no cost or performance commitment.

Risk and compliance: full recalculation when official boundaries are released; control/redline/ownership/heritage gaps are listed as assumptions; archive facilities collect no personal trajectories; honors are human-final; no official approval or implementation commitment is claimed.

JZ Archive Belt · Mobility, Blue-Green and Public Space

Memory Spine · Three stitch bands · Archive nodes

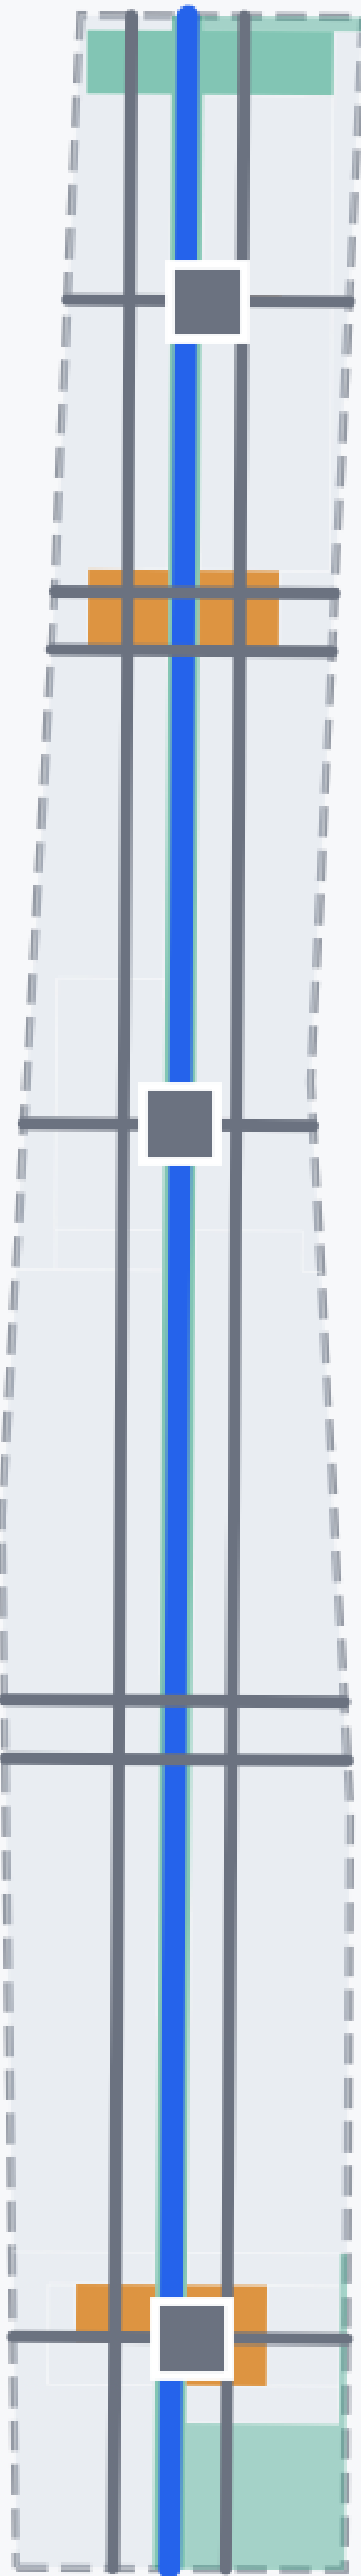

Mobility & blue-green

- Memory Spine (greenway)
 - 1 · north–south
- Stitch bands (branch)
 - 3 · to the three stations
- Total road centerline
 - 37.3 km
- Green area / ratio
 - 174 ha / 15.23%
- Public-space area
 - 394801 m²
- Transit connection
 - Dazhongsi / Wudaokou / Qinghua East Road West (conceptual)

Road redlines/rail alignments are conceptual; engineering conclusions await official data


Boundaries are provisional, not official redlines; full recalculation required after official data release

Three archive stations: Source - Zhongzhiyuan (full-stack innovation, model evaluation and standards hall); Transform - AI Origin Community (commercialization, commit stele and Honor Yearbook); Scenario - Dazhongsi (AI-native new business, four-quadrant pedestrian connection). All key-area content is directional concept design.

Risk and compliance: full recalculation when official boundaries are released; control/redline/ownership/heritage gaps are listed as assumptions; archive facilities collect no personal trajectories; honors are human-final; no official approval or implementation commitment is claimed.

JZ Archive Belt · Key-Area Detailed Design

Source · Transform · Scenario

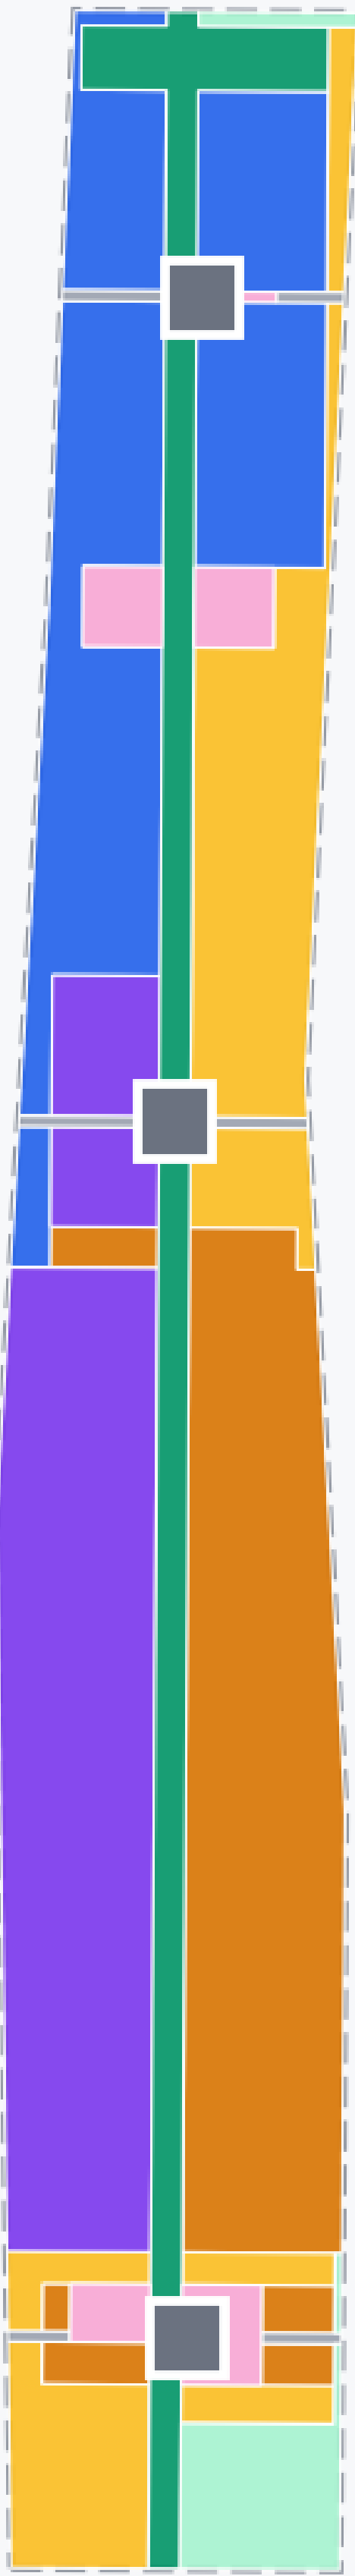

SOURCE Zhongzhiyuan · Full-stack innovation

Space: Shaded test court + slow loop

Public edge: Contribution intake desk

Manual fallback: Staffed intake / paper archive

TRANSFORM AI Origin Community · Commercialization

Space: Bookish courtyard + station stitch

Public edge: Yearbook node + commit stele

Manual fallback: Dual review for honors and corrections

SCENARIO Dazhongsi · AI-native new business

Space: Service street edge + four-way crossing

Public edge: Service archive panel

Manual fallback: Offline counter / conventional service

Key-area conclusions are conceptual; directional only until official polygons are published

Boundaries are provisional, not official redlines; full recalculation required after official data release

Spatial metrics (EPSG:4548): Overall Design Area 11,412,825 m²; green ratio 15.2%; public-space ratio 3.46%; building footprint 89,569 m²; roads 37.3 km. Statutory controls (FAR/height/density/setbacks) pending official data; operational metrics are definitions only.

Risk and compliance: full recalculation when official boundaries are released; control/redline/ownership/heritage gaps are listed as assumptions; archive facilities collect no personal trajectories; honors are human-final; no official approval or implementation commitment is claimed.

JZ Archive Belt · Metrics and Evidence

EPSG:4548 recomputation · three metric classes

Spatial recomputation metrics (status=known)

Overall Design Area 11,412,825 EPSG:4548 geometry recompute	Green ratio 15.23% EPSG:4548 geometry recompute	Public-space ratio 3.46% EPSG:4548 geometry recompute
Building footprint 89,569 EPSG:4548 geometry recompute	Road centerline length 37,308 EPSG:4548 geometry recompute	Key areas 3 EPSG:4548 geometry recompute

Sources & state

- OFFICIAL-ANNOUNCEMENT (formal)
- AGENT-TASKBOOK (formal)
- SITE-PACKAGE / SOURCE-REGISTRY
- PROVISIONAL-BOUNDARIES (provisional_only)
- Local standard snapshots ×5 (formal)

Self-check state

Spatial review: PASS

Professional evidence: PASS

Visual packaging: PASS

Deterministic validation: PASS

Statutory controls (FAR/height/density/setbacks) pending official data; no fabricated values

Operational metrics (archive entries / names / correction responses) are definitions only

Boundaries are provisional, not official redlines; full recalculation required after official data release