

01 · 总体结构

题—答—阅三带·一条9公里应答长卷





南问段·大钟寺片区鸟瞰 (AI 生成概念意象, 非实景照片)

百年应答

THE CENTURY ANSWER

把 9 公里遗址公园做成一份摊开在大地上的百年答卷。

1909 年，京张铁路回答了中国人能不能自己修铁路；今天，沿线 2000 余家 AI 企业在回答：中国能不能自己做 AI。

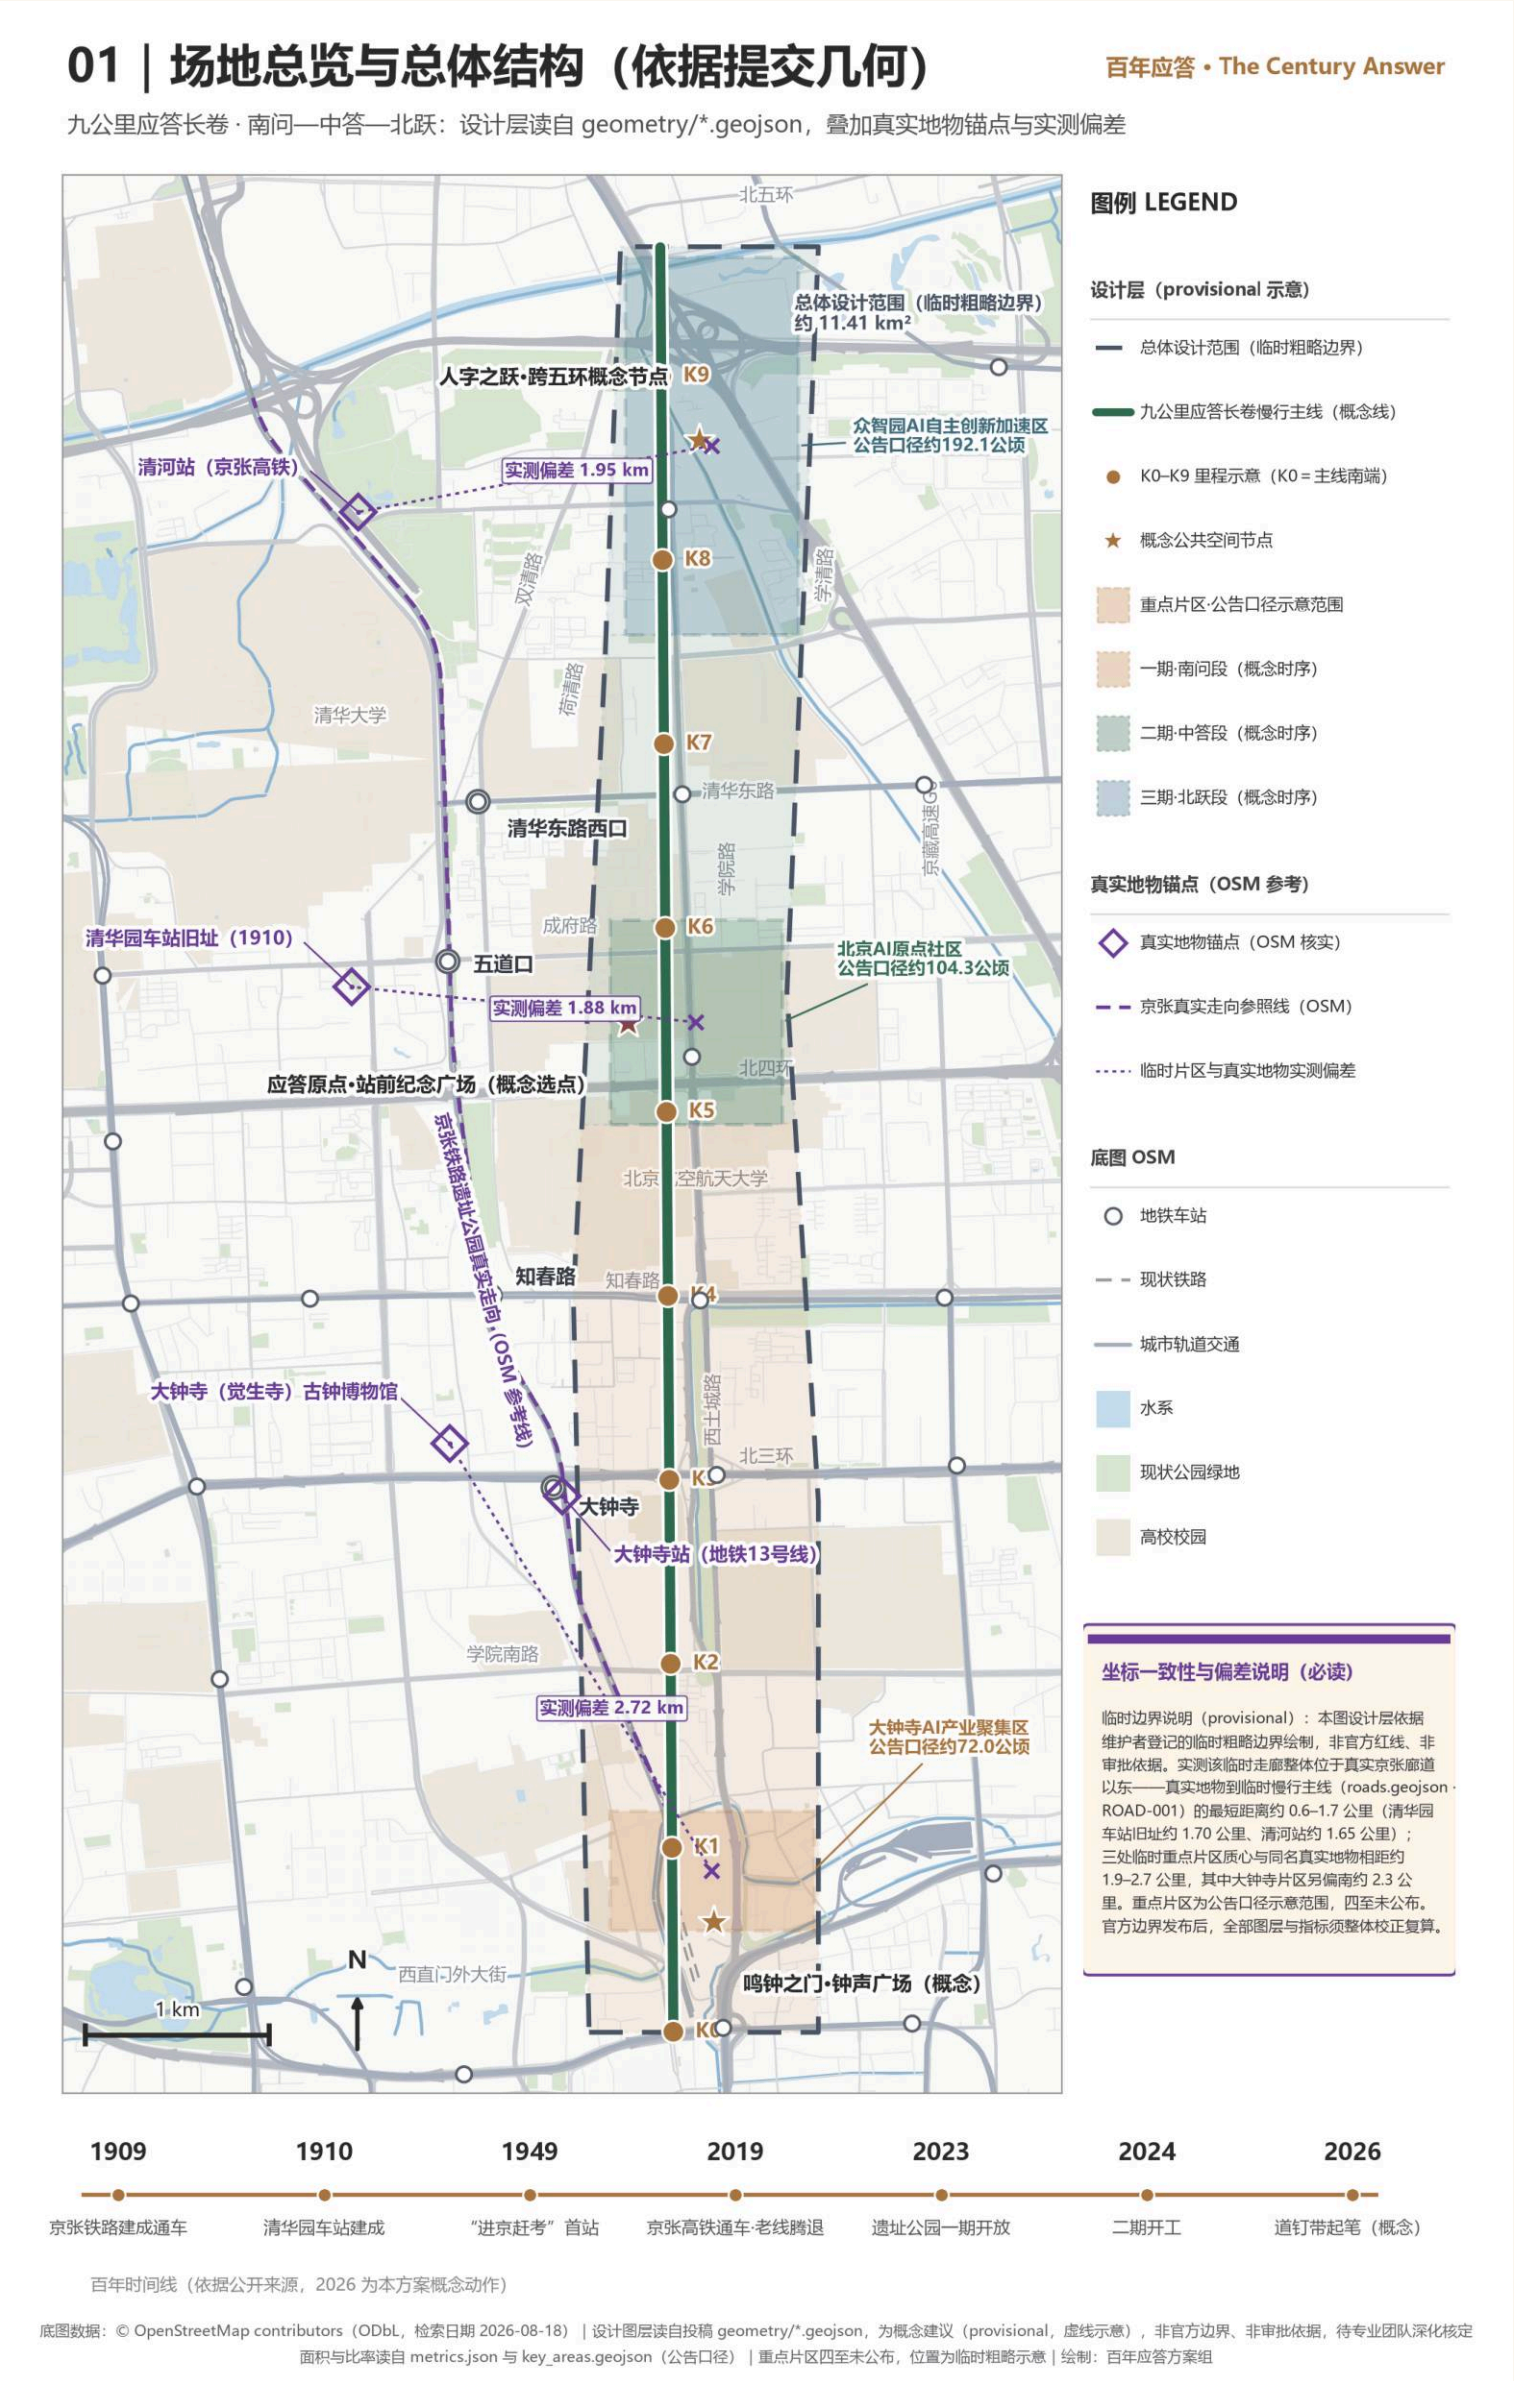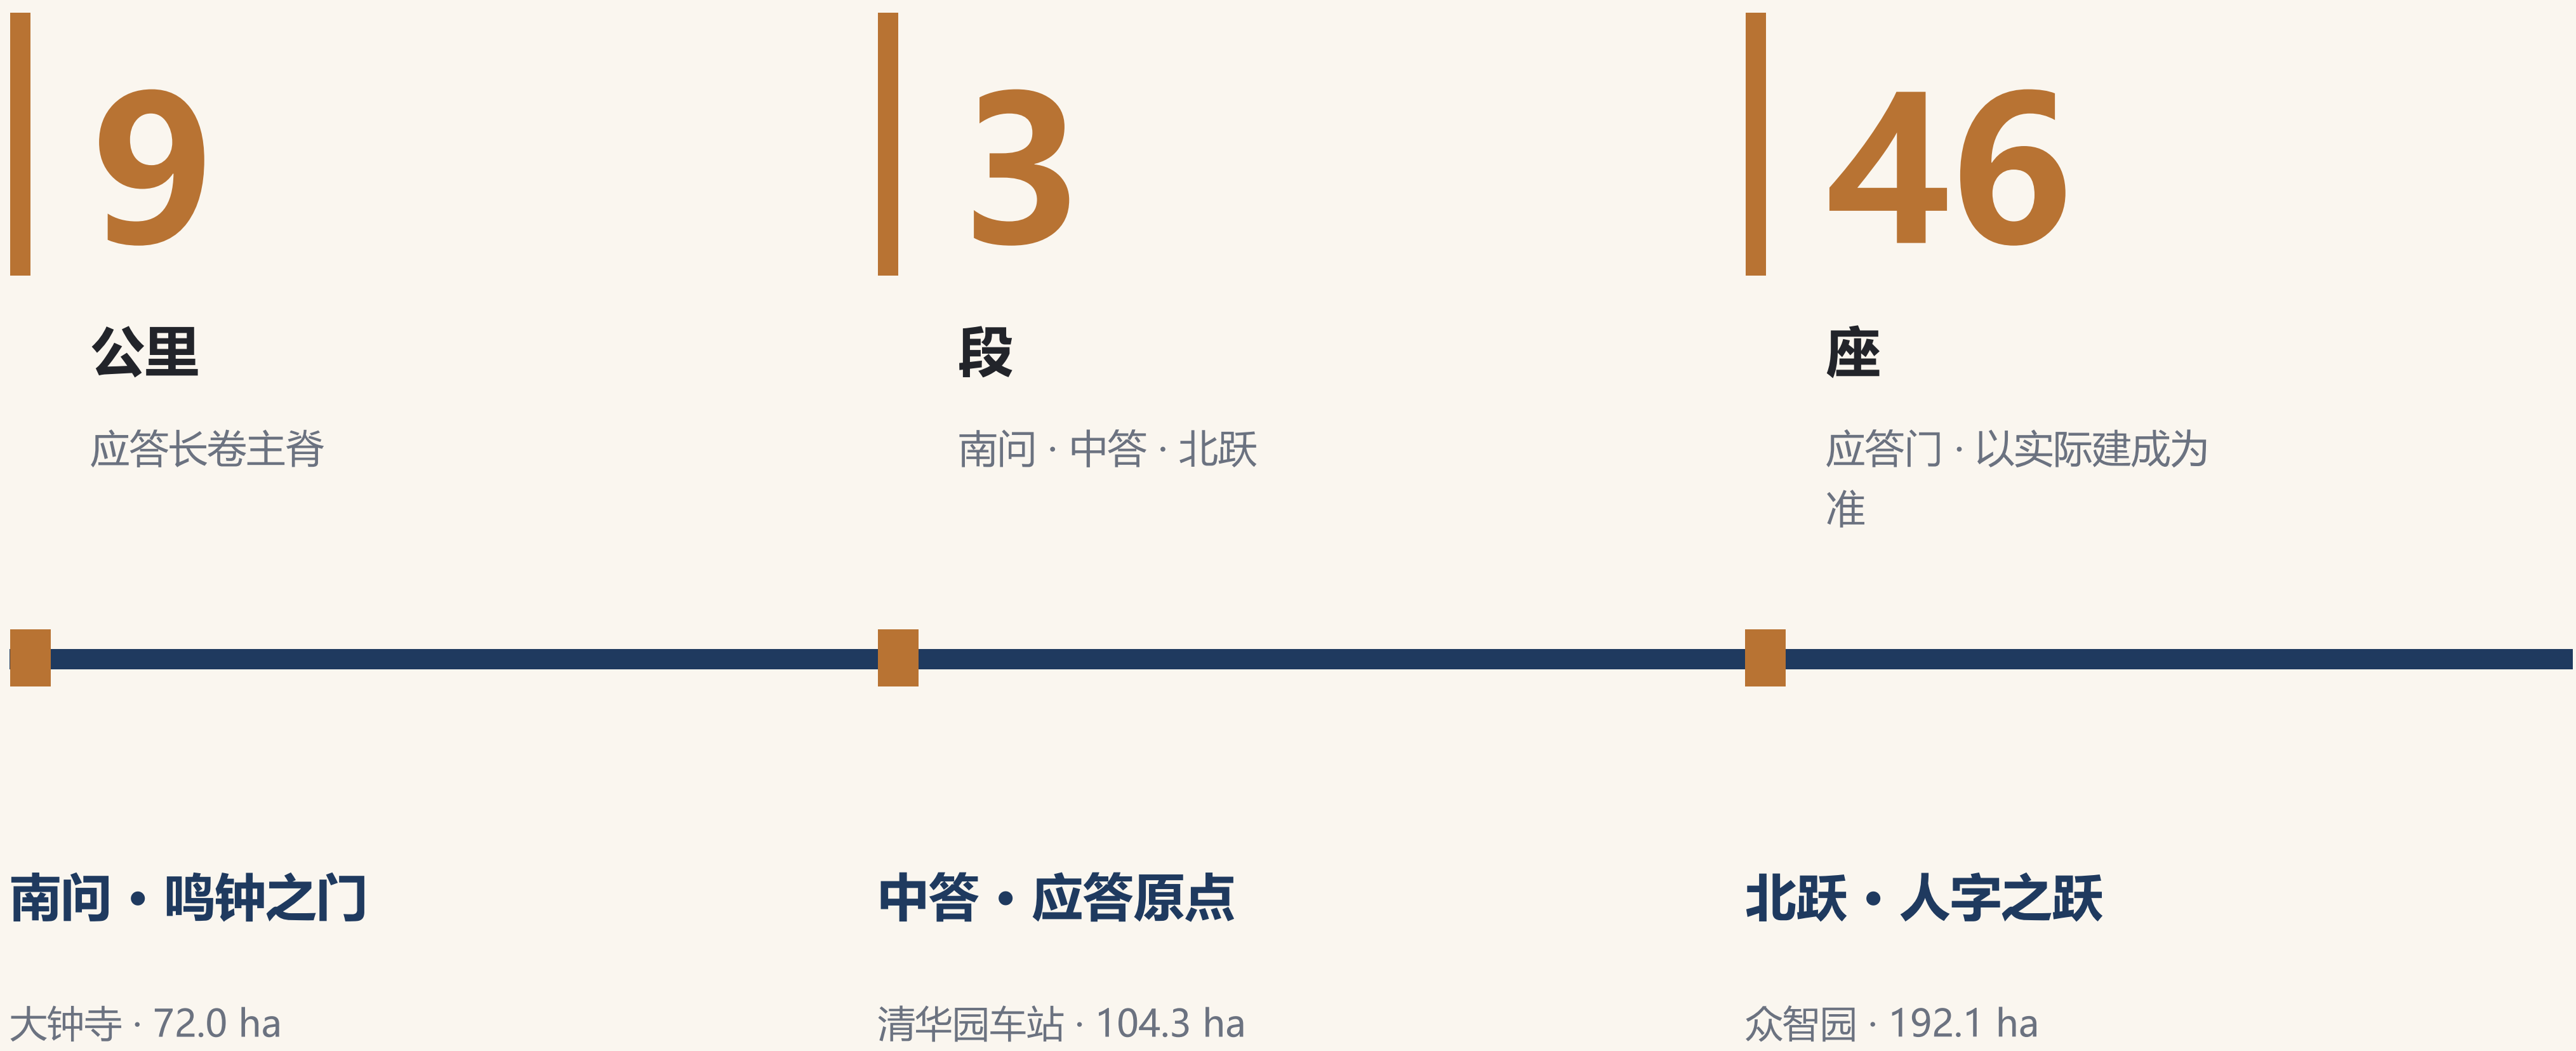

区位与总体结构 (概念示意)

02 · 用地与更新

轻介入 · 可逆化 · 复用优先（无拆改留结论）


9 km	1,141.3 ha	3	46	~70 / 45万	122
遗址公园主轴全长 · 约	报送范围 11,412,825 m² · metrics.json	重点设计片区 · 192.1 / 104.3 / 72.0 ha · 官方口径	二期规划出入口 · 以实际建成为准	沿线社区数 / 惠及人口 · 公开口径	海淀备案大模型 · 截至2026年2月区政府口径

策略

- 一切新增功能优先复用既有楼宇与低效空间，不以新增独立建筑为前提
- 要素服务驿站沿公园东西两侧低效空间布点：政策咨询/备案辅导/成果对接（非当场兑付）；离公园越近共享度越高——制造东西穿行理由，用功能回答缝合
- 驿站旗舰点建议靠近大钟寺段与众智园段；众智园接入测试工位复用既有楼宇
- 更新时序：一期16.8公顷已开放段为全部测试起点；二期建成一段、激活一段；不设依赖未批准事项的关键路径
- 用地底账（metrics.json）：报送范围 11,412,825 m²（约 1,141.3 ha）；建筑基底 3,125 m²；绿地率 25.0%；公共空间率 1.9%；容积率 unknown（官方控制指标未公开，不做推断）

02 | 用地结构与三层范围工作框架（概念）

一轴两翼十地块：全部图斑读自 geometry/land_use.geojson，非法定用地边界

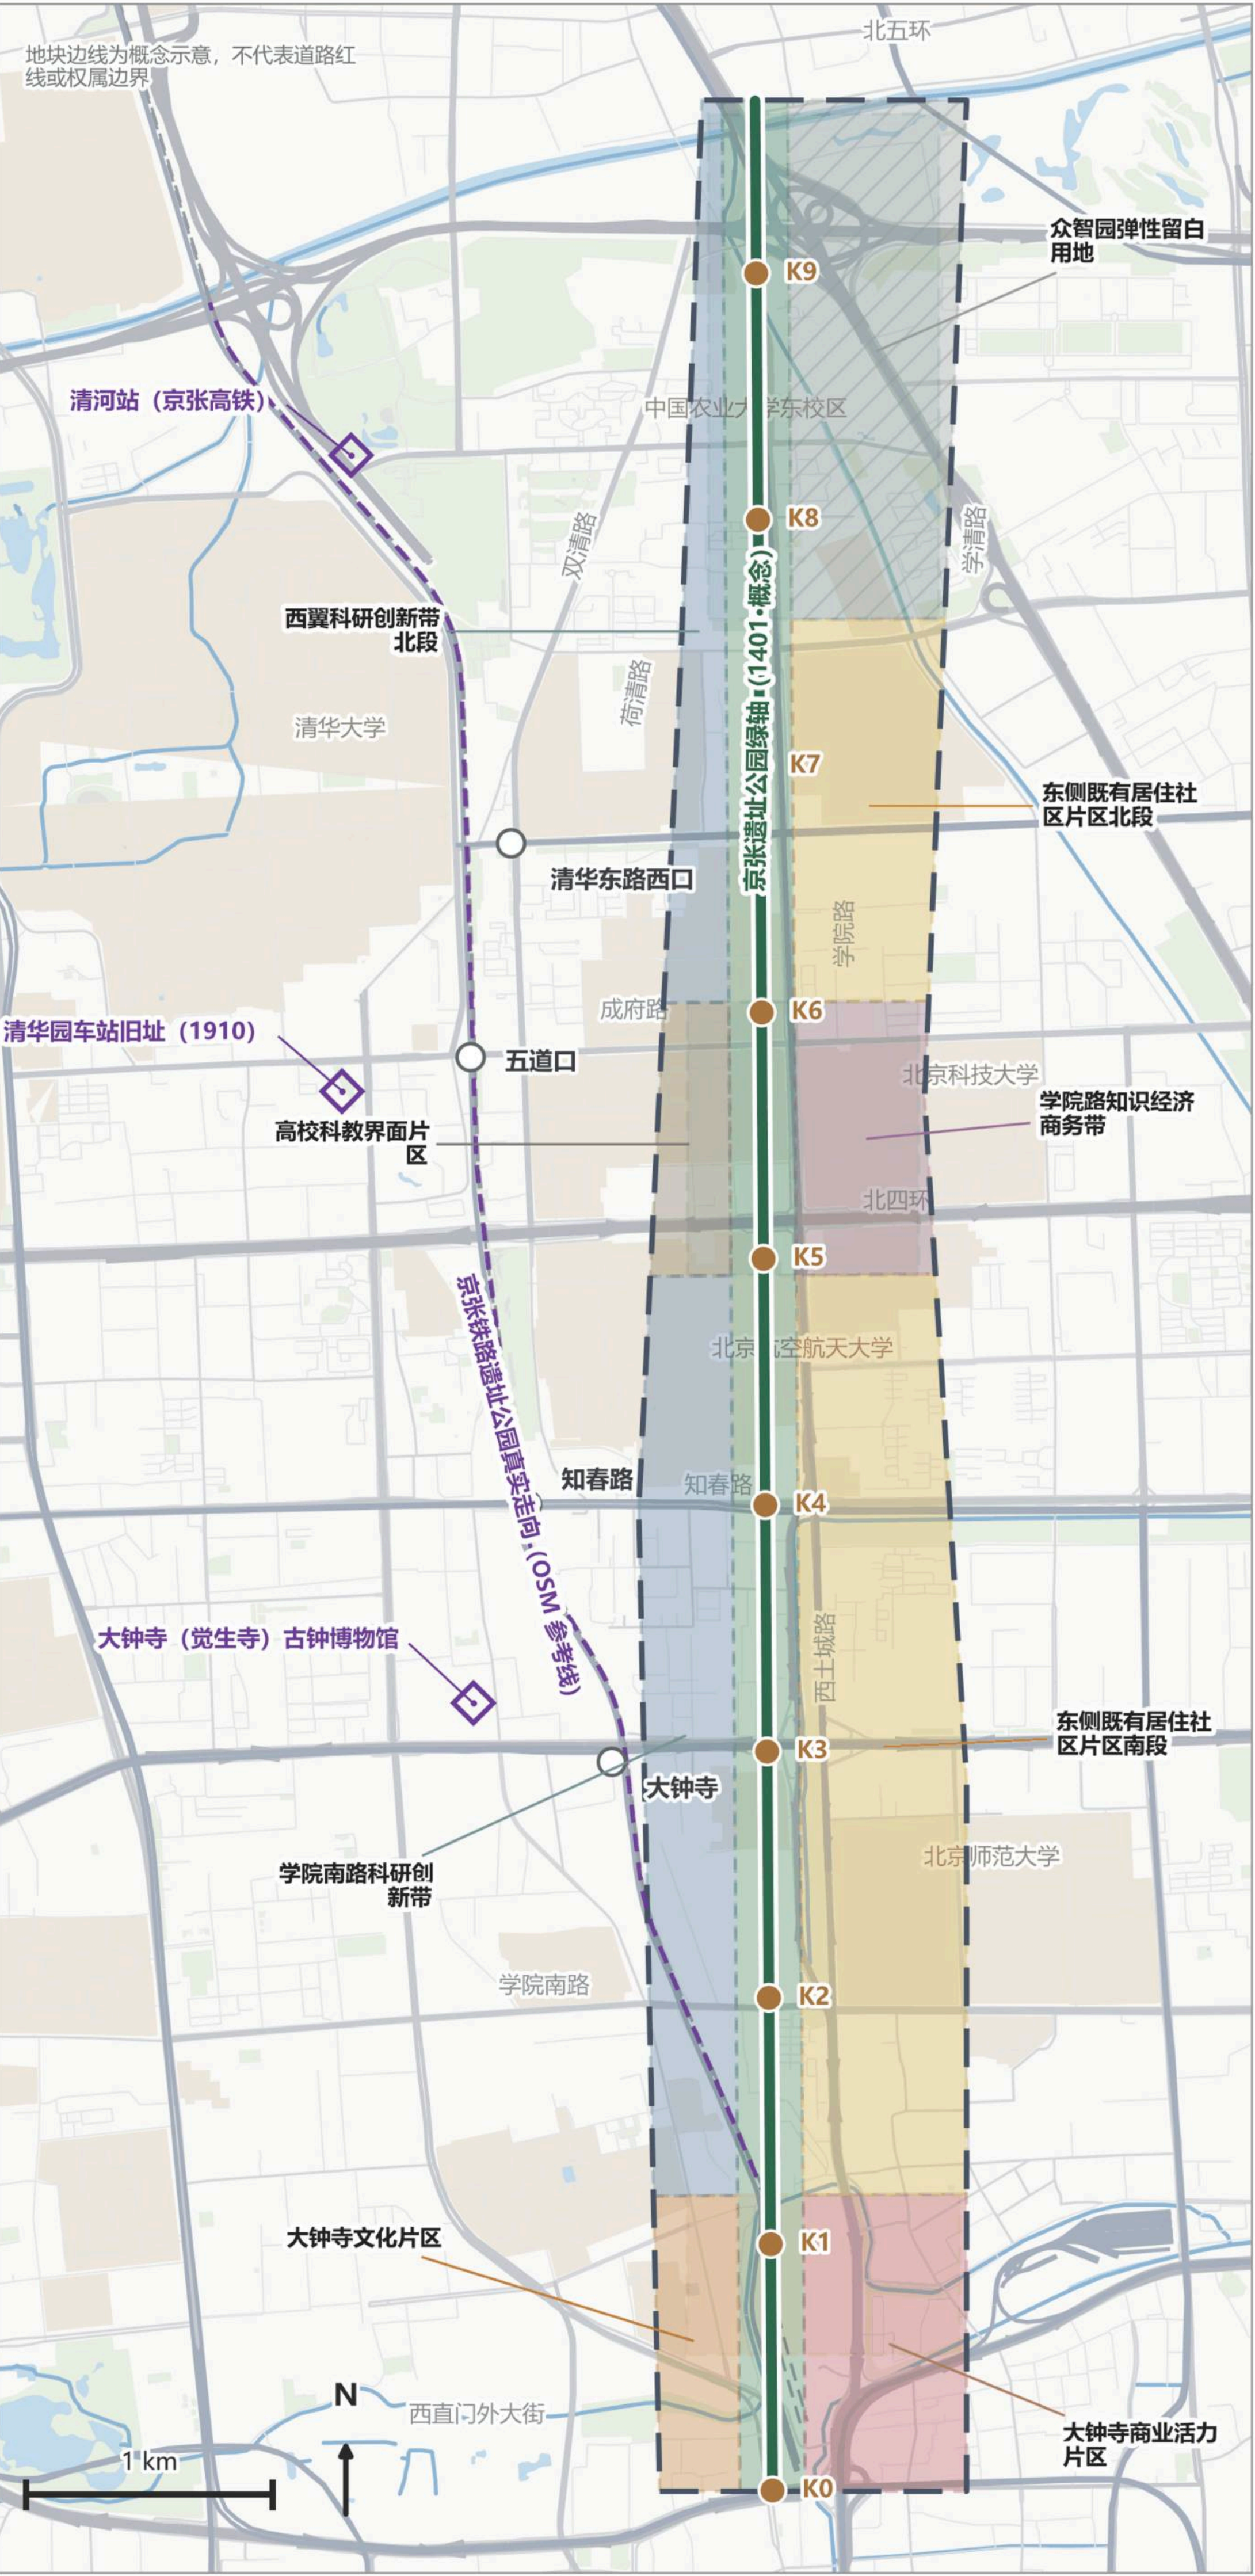

百年应答 · The Century Answer

图例 LEGEND

设计层·用地分区（provisional）

- 公园绿地·绿轴（1401）
- 文化设施（0803）
- 商业（0901）
- 商务（0902）
- 科研（0802）
- 高校科教（0804）
- 既有居住延续（0701）
- 弹性留白（16）
- 总体设计范围（临时边界）
- 重点片区示意范围

真实地物锚点（OSM 参考）

- 真实地物锚点（OSM 核实）
- 京张真实走向参照线（OSM）
- 临时片区与真实地物实测偏差

三层范围工作框架（示意）



坐标一致性与偏差说明（必读）

临时边界说明（provisional）：本图设计层依据维护者登记的临时粗略边界绘制，非官方红线、非审批依据。实测该临时走廊整体位于真实京张廊道以东——真实地物到临时慢行主线（roads.geojson · ROAD-001）的最短距离约 0.6–1.7 公里（清华园车站旧址约 1.70 公里、清河站约 1.65 公里）；三处临时重点片区质心与同名真实地物相距约 1.9–2.7 公里。其中大钟寺片区另偏南约 2.3 公里。重点片区为公告口径示意范围，四至未公布。官方边界发布后，全部图层与指标须整体校正复算。

用地结构引导（概念示意）

03 · 交通与市政

先通后留：断点连通在前，场景叠加在后

9 km	1,141.3 ha	3	46	~70 / 45万	122
遗址公园主轴全长 · 约	报送范围 11,412,825 m² · metrics.json	重点设计片区 · 192.1 / 104.3 / 72.0 ha · 官方口径	二期规划出入口 · 以实际建成为准	沿线社区数 / 惠及人口 · 公开口径	海淀备案大模型 · 截至2026年2月 区政府口径

04 | 交通慢行与蓝绿公共空间系统（概念）

慢行主线 · 三条东西缝合线 · 低速物流测试通道 · 概念绿地与公共空间，全部读自提交几何

百年应答 · The Century Answer



图例 LEGEND

设计层（provisional 示意）

- 总体设计范围（临时粗略边界）
- 九公里应管长卷慢行主线（概念线）
- K0-K9 里程示意（K0 = 主线南端）
- ★ 概念公共空间节点
- 重点片区公告口径示意图范围
- 东西缝合慢行连线（概念）
- - 低速物流测试通道（概念）
- ◇ 应管门示意（实际建成为准）
- 概念公共空间
- 概念绿地（1401）
- 蓝绿协调带（1402）

真实地物锚点（OSM 参考）

- ◇ 真实地物锚点（OSM 核实）
- - 京张真实走向参照线（OSM）
- 临时片区与真实地物实测偏差

底图 OSM

- 地铁站
- - 现状铁路
- 城市轨道交通
- 水系
- 现状公园绿地
- 高校校园

坐标一致性与偏差说明（必读）

临时边界说明（provisional）：本图设计层依据维护者登记的临时粗略边界绘制，非官方红线、非审批依据。实测该临时走廓整体位于真实京张铁道以东——真实地物到临时慢行主线（roads.geojson · ROAD-001）的最短距离约 0.6-1.7 公里（清华园车站旧址约 1.70 公里，清华东路约 1.65 公里）；三处临时重点片区质心与同名真实地物相距约 1.9-2.7 公里，其中大钟寺片区旁偏南约 2.3 公里。重点片区为公告口径示意图范围，西至未公布。官方边界发布后，全部图层与指标须整体校正复算。

交通与蓝绿系统（概念示意）


断面三 · 桥下空间由无序停车改为公共使用

大钟寺AI产业聚集区（南问段） | 以高架东端落地段为例 | 解决：把压在站厅通往西侧街区主流线上的桥下空间，改成为遮蔽、无台阶的连续走廊


京张·百年应答

断面 DZS-3

① 桥下横断面（桥墩间距与净高以实测为准）

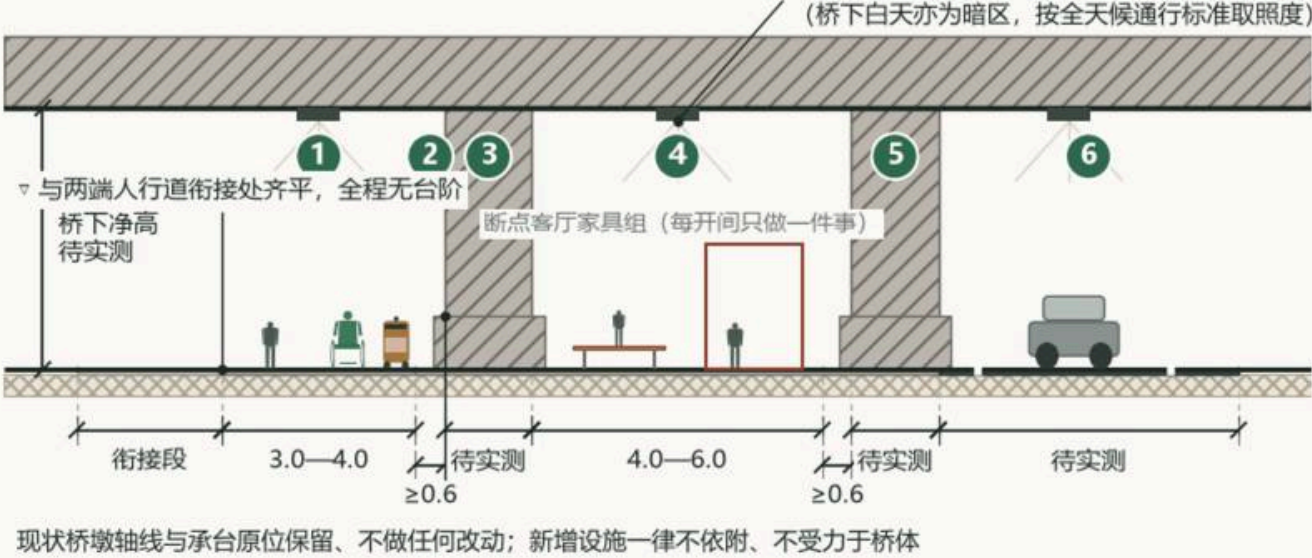

② 纵向示意（沿高架方向，左西右东；长度取自正文，竖向为示意，不按比例）

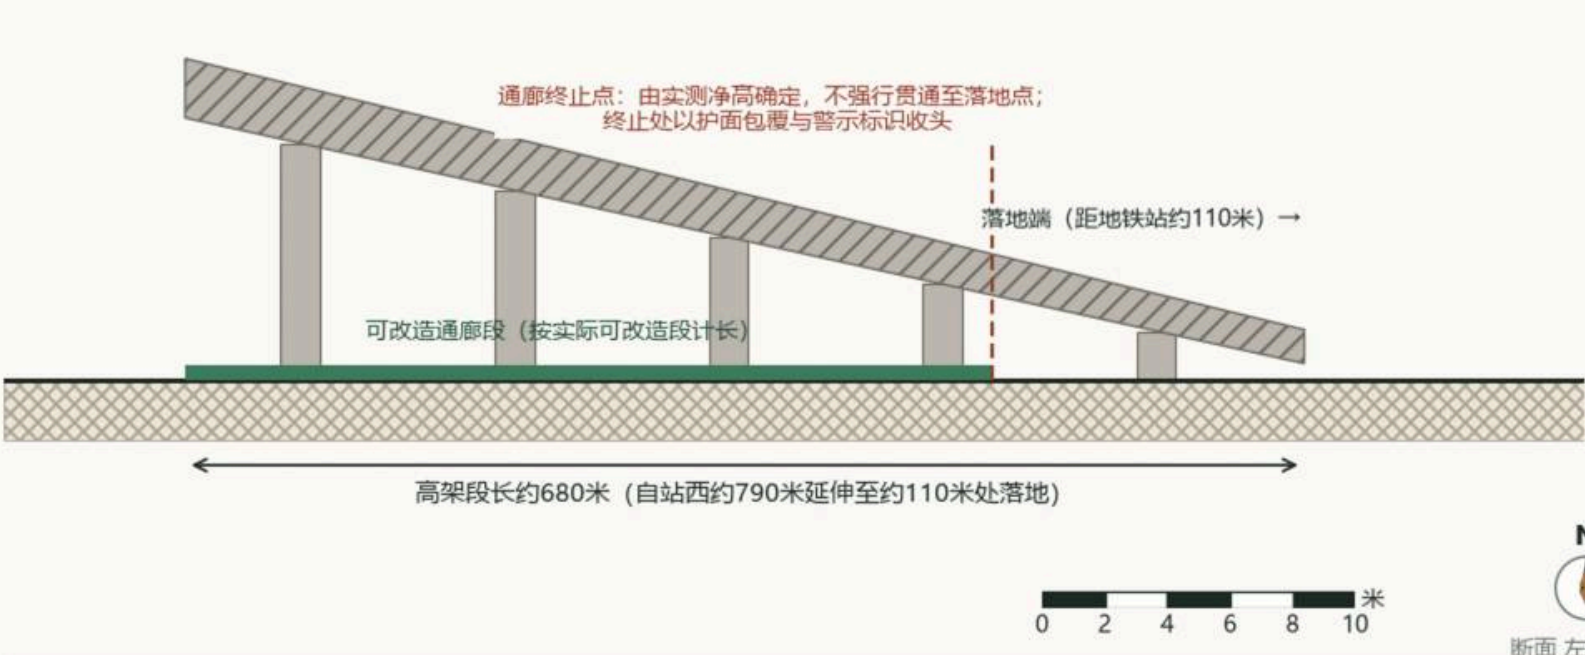

概念断面示意，不含工程结论；宽度为分配纵向而非道路红线；待专业团队按现行标准核定。

横向分带（自西侧街区向站厅侧）


- 通行区 3.0-4.0米：连续步行通道，全程无台阶、与桥下现状地面找平
- 检修间距≥0.6米：新增设施与墩柱之间必须留出
- 现状桥墩：桥墩与桥台部位保留，不做任何改动
- 活动区 4.0-6.0米：节点客厅家具组按散往开间或组布置，每开间只做一件事，不连续摆满
- 第二排墩柱与检修间距向前
- 停车处置：清得掉的先清，清不掉的先规范（划线、限位、纳入统一管理）

关键控制竖向（数字全部取自正文）

- 一律不依附、不受力于桥体：本方案不提出任何加固或改造结论
- 通廊从现有现状地面、控制高度不高于1.20，与两侧人行道衔接处齐平
- 面宽为遮蔽、防潮、易清洗的整体面层；桥板遮蔽、无雨水下渗需求，不用透水做法
- 定为低速机器人用需天气优先通行段；活动区一侧设充电与待机位

材料图例

- 混凝土结构 / 基础
 - 防腐防锈整体面层（非透水）
 - 浅色石材 / 预制块铺装
 - 沥青车行路面
 - 黄土 / 现状路基（示意）
- 待专业深化：桥梁管养单位使用许可与安全边界、现状停车权属与使用主体、消防与疏散、结构检测与限载

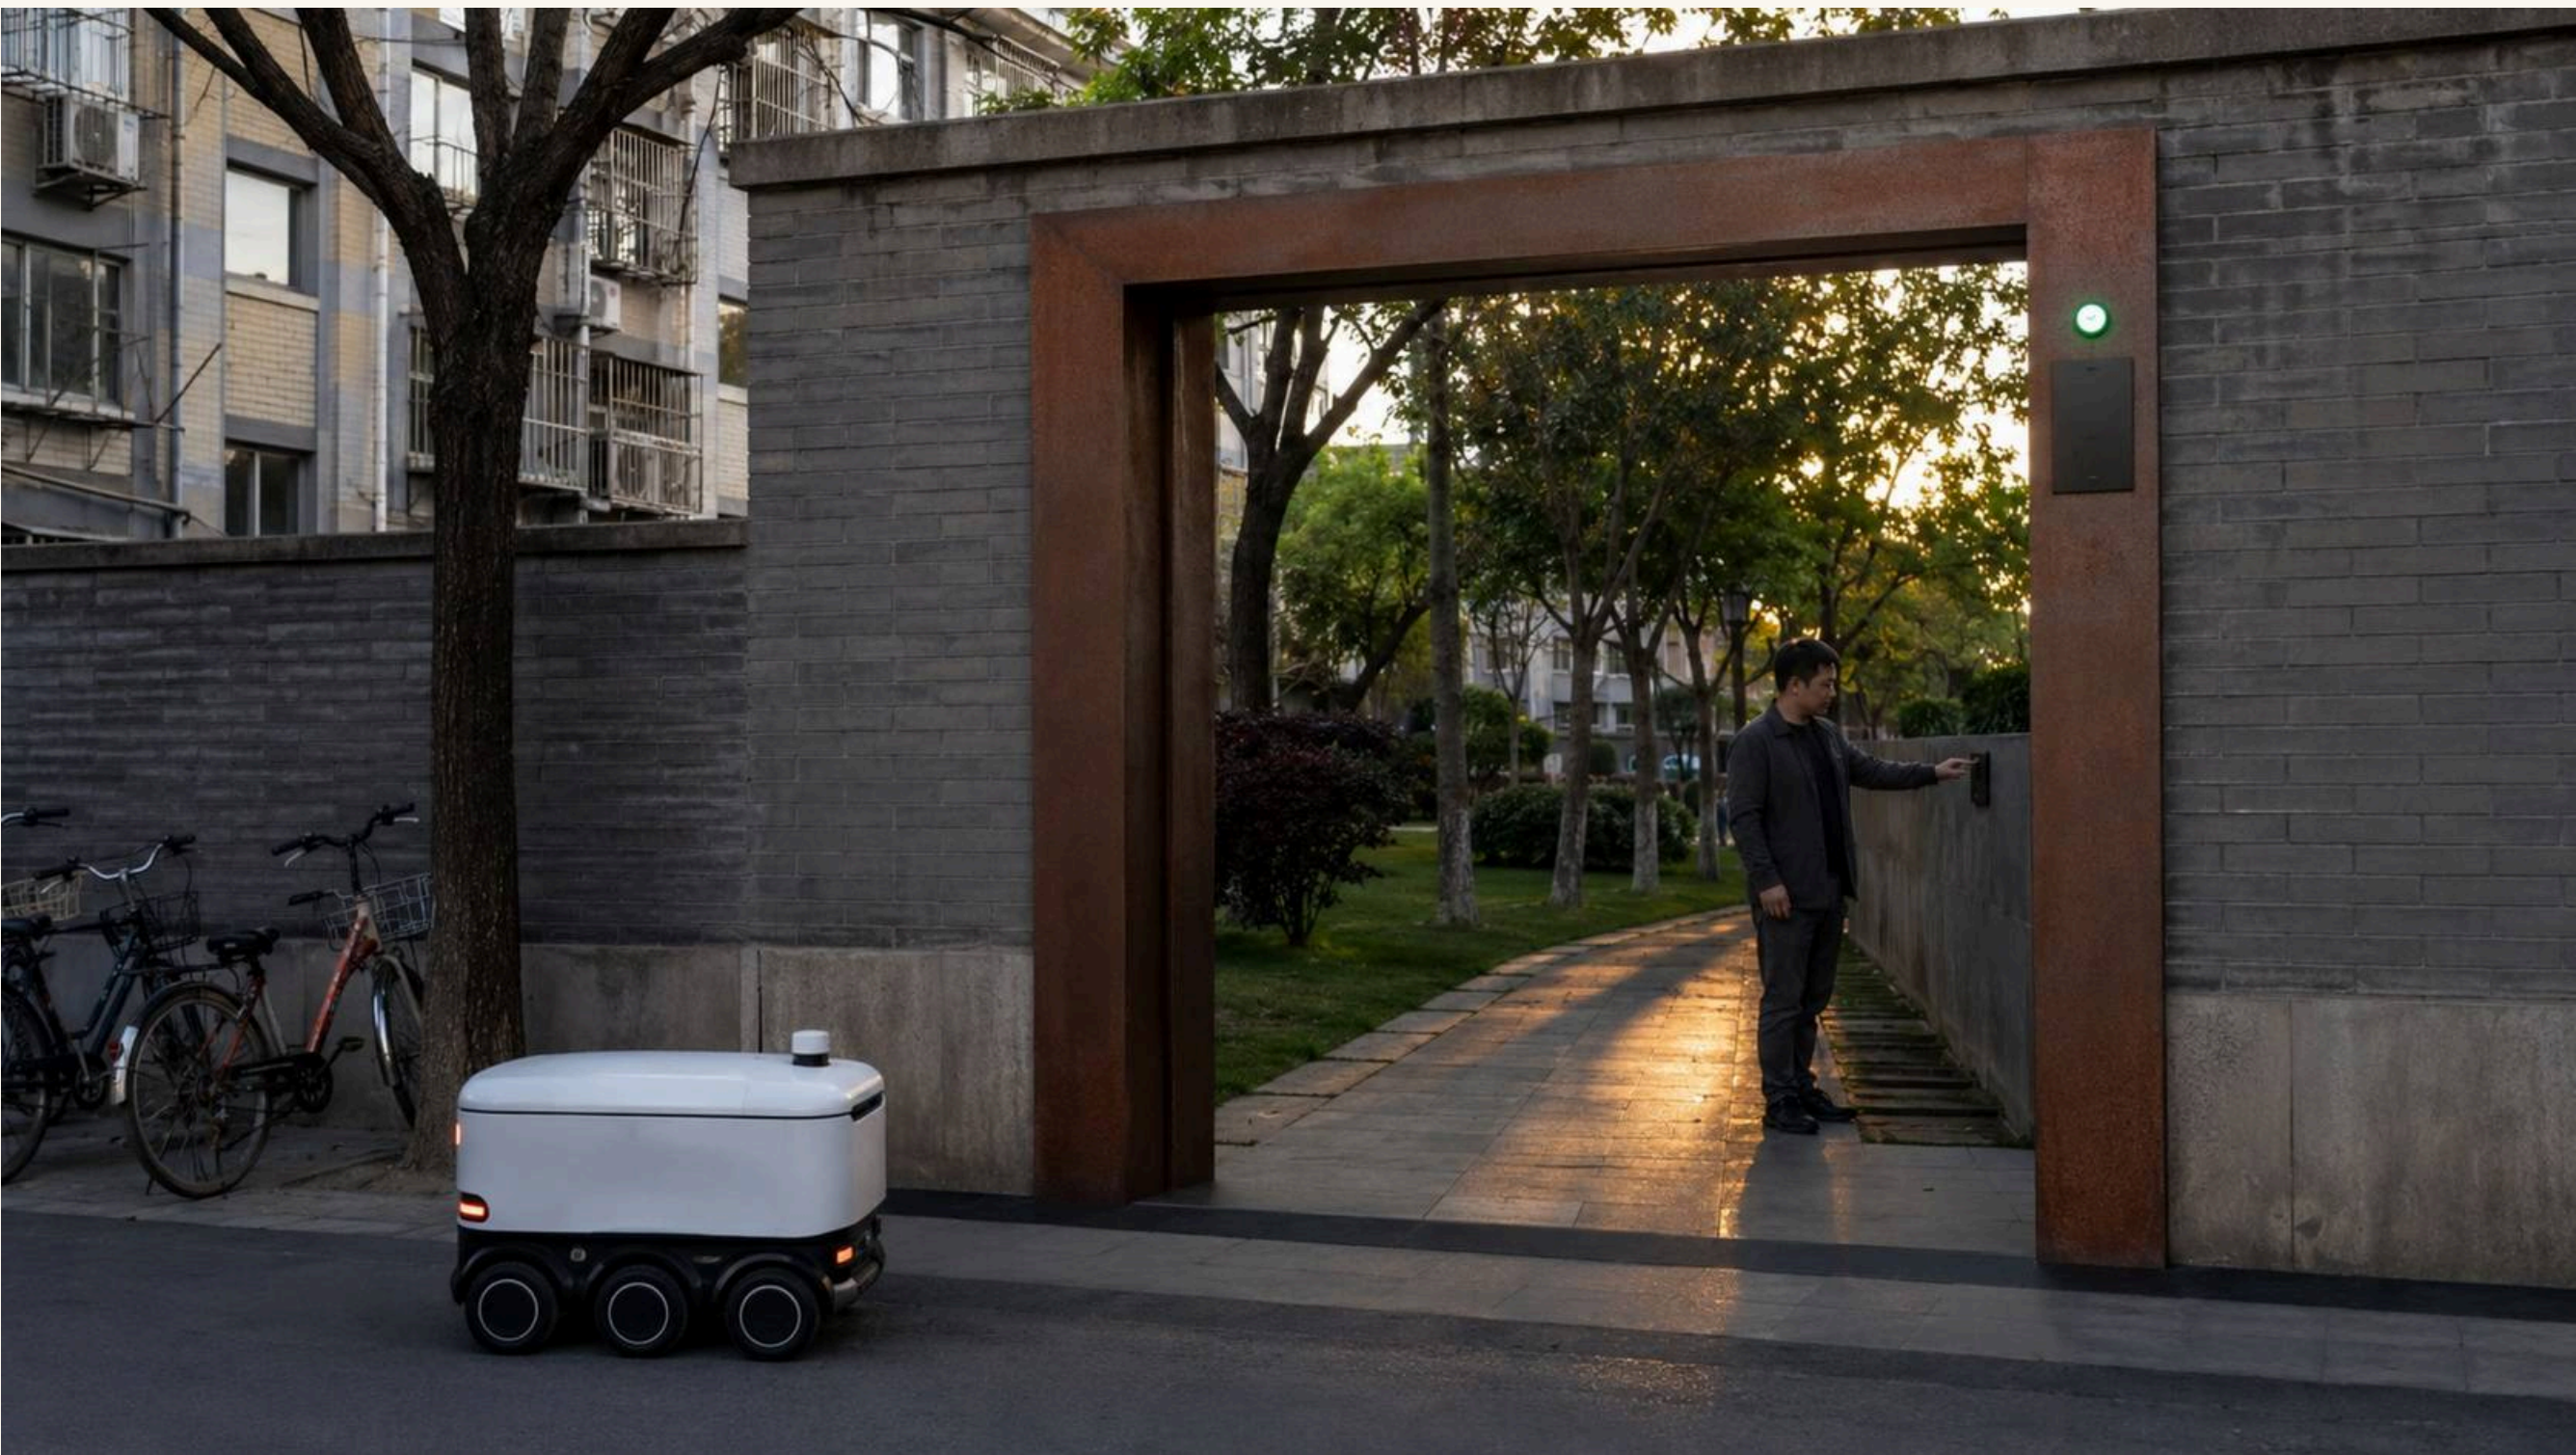

应答门-双用坡道：轮椅优先、机器人强制停让（AI生成概念意象）

04 · 活力带与蓝绿公共空间

把答案变成日子：清河 · 小月河 · 组件库 · 学年历

9 km	1,141.3 ha	3	46	~70 / 45万	122
遗址公园主轴全长 · 约	报送范围 11,412,825 m² · metrics.json	重点设计片区 · 192.1 / 104.3 / 72.0 ha · 官方口径	二期规划出入口 · 以实际建成为准	沿线社区数 / 惠及人口 · 公开口径	海淀备案大模型 · 截至2026年2月区政府口径

蓝绿与社区

- 底账（metrics.json）： 绿地率 25.0% / 公共空间率 1.9%（报送范围，中置信）
- 清河蓝绿空间衔接人字天桥概念节点，构成北段开放空间高潮（不含工程结论）
- 小月河场景赋能翼=场景的社区端出口：健康导航角首发布点、共创工具培训、机器人服务社区延伸评估（均为概念建议）
- 公共空间组件库10件：铜道钉/应答门套件/断点客厅家具组/信息桩/声波径铺装/驿站模块/双用坡道/策展点位/署名立牌/素广场
- 青年策展权：每季度固定比例点位由沿线10余所高校学生团队竞标策展并署名立牌
- 学年制活动年历：9月开学出发仪式 / 3月路演季（大钟寺段主场） / 3·25公益纪念开放日（清华园车站，无商业） / 6月毕业礼+青年道钉礼
- 城市进化档案馆：归档方案迭代史与公众反馈，Logo带版本号随年度进化



活力带的日常：钟声广场与声环铺装（AI 生成概念意象）



市民蹲下来数道钉（AI 生成概念意象）

05 · 三大重点区详细设计

官方面积口径：192.1 / 104.3 / 72.0 ha（±3%空间校验）

9 km	1,141.3 ha	3	46	~70 / 45万	122
遗址公园主轴全长 · 约	报送范围 11,412,825 m² · metrics.json	重点设计片区 · 192.1 / 104.3 / 72.0 ha · 官方口径	二期规划出入口 · 以实际建成为准	沿线社区数 / 惠及人口 · 公开口径	海淀备案大模型 · 截至2026年2月区政府口径

大钟寺 72.0 ha · 鸣钟之门

- 新铸应答钟：备案/IPO敲一响（绝不敲击1733年文物古钟）
- 钟声广场缝合地铁四象限步行流线（概念建议）
- 路演季主场+备案辅导旗舰驿站；商业活动与红色叙事绝不并联

AI原点社区 104.3 ha · 应答原点

- 清华园车站百年应答站：文物本体不动一砖一瓦；零公里桩为待文物部门协商的概念选点
- 道钉带起点：第0号钉讲1909年通车史；开钉即有122颗（区政府口径，差异如实脚注）
- 3·25公益纪念开放日：无企业冠名/无商业路演/无当场钉钉


众智园 192.1 ha · 人字之跃

- 跨五环人字天桥概念节点：回应官方'上跨环路标志性节点'，不含工程结论
- 桥面三个数字按统计发布周期更新（企业数/备案数/学者数），绝不实时
- demo接入测试工位（复用楼宇）+清河蓝绿空间+青年策展重点位

03 | 三重点片区概念设计（放大·含实测偏差）

片区范围读自 key_areas.geojson；与同名真实地物的实测偏差在每幅内如实标注

百年应答 · The Century Answer

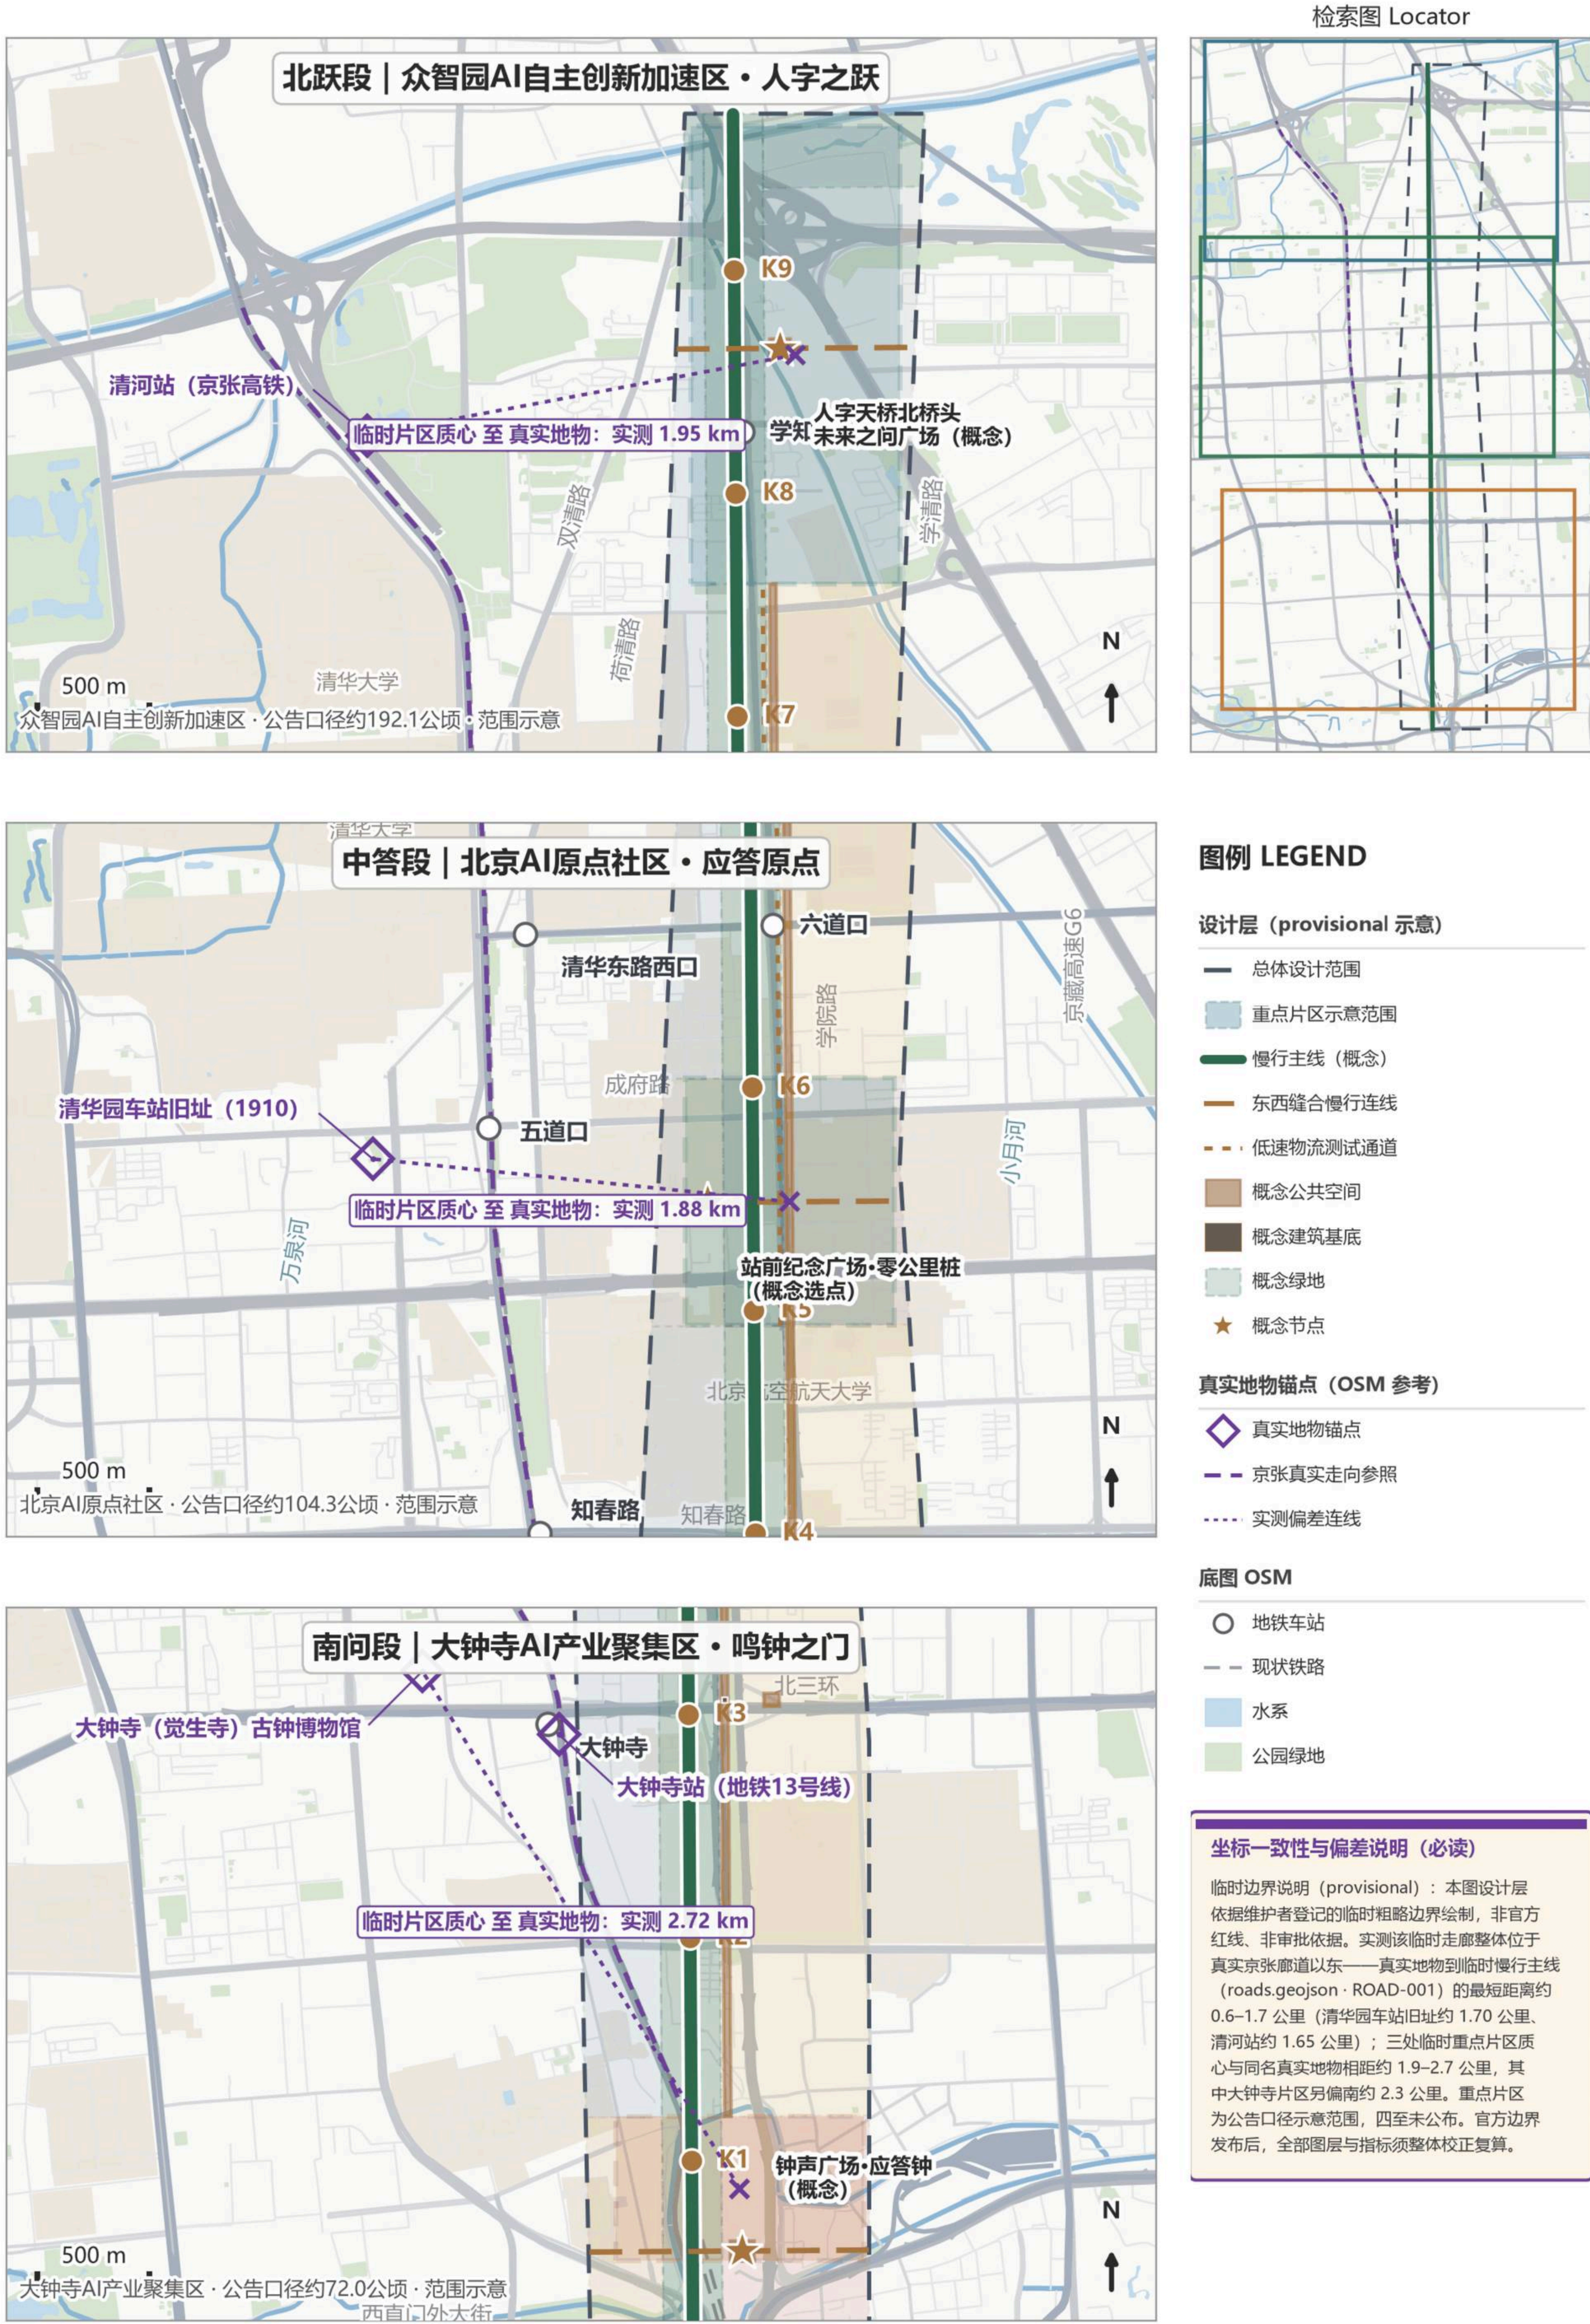

底图数据：© OpenStreetMap contributors (ODbL, 检索日期 2026-08-18) | 设计图层读自投稿 geometry/"*.geojson，为概念建议（provisional，虚线示意），非官方边界、非审批依据，待专业团队深化核定面积与比率读自 metrics.json 与 key_areas.geojson（公告口径） | 重点片区四至未公布，位置为临时粗略示意 | 绘制：百年应答方案组

三重点区详设底图（概念示意）

06 · AI场景与运营机制

19张场景卡 · 覆盖甲方点名的八类场景与三个概念 · 测试先于推广

9 km	1,141.3 ha	3	46	~70 / 45万	122
遗址公园主轴全长 · 约	报送范围 11,412,825 m² · metrics.json	重点设计片区 · 192.1 / 104.3 / 72.0 ha · 官方口径	二期规划出入口 · 以实际建成为准	沿线社区数 / 惠及人口 · 公开口径	海淀备案大模型 · 截至2026年2月区政府口径


场景卡	甲方场景类别	空间载体	边界与复核
S1 扫钉即应答	ai-cultural-guide	道钉带全线	L1公开·扫码仅匿名计数
S2 应答门社区导览	ai-cultural-guide	46出入口×近70社区	口述史需本人授权(L3)
S3 3·25开放日服务	ai-cultural-guide	清华园车站（概念选点）	内容审定锁版·零商业
S4 四象限换乘助手	ai-traffic-walkability	大钟寺钟声广场	非审定交通方案·季审
S5 断点客厅反馈站	ai-traffic-walkability	全线断点	匿名默认·结果公示
S6 健康服务导航	ai-health-service-navigation	小月河翼+驿站	只导航不诊疗·零健康数据
S7 备案辅导Copilot	enterprise-service-copilot	东西两侧驿站	非法律意见·材料即删
S8 青年策展助手	ai-cultural-guide	全线策展点位	评审全程人工
S9 机器人测试场	robot-delivery-low-speed	一期16.8ha环线	测试设想·安全员+急停
S10 双用坡道测试	robot-delivery-low-speed	2-3座应答门样段	无障碍一票否决
S11 demo接入测试	enterprise-service-copilot	众智园测试工位	通过≠政府背书
S12 活动日压力测试	ai-traffic-walkability	大钟寺—众智园廊道	安全判断始终在人
S13 无墙学期旁听	ai-cultural-guide	3-5座课门×邻校公开课	不登记身份；分档听者自选
S14 道钉微课	ai-cultural-guide	道钉带全线·零公里桩起读	与S1同源，不新增采集
S15 算法公示墙	ai-cultural-guide	三处重点区各一处集中墙	只公示部署方，无个人数据
S16 算法应答窗口	enterprise-service-copilot	要素服务驿站内	材料办结即删，人工复核后出具
S17 机器人敲门	robot-delivery-low-speed	46座应答门（先试3-5座）	社区认领人批准；拒绝可执行
S18 交接厅	robot-delivery-low-speed	两端桥头广场接驳组合	车不进带；交接需人工确认
S19 慢速街	ai-health-service-navigation	一期已开放段约800米	开关权在本人或家属，运营方无调阅权

运营机制

- 三张可审计清单：年度发布备案清单+开源清单+场景开放清单，汇成多语种《百年应答报告》，附全球AI街区叙事联盟倡议

场景开放闭环：申请—测试—验证—展示；接入与退出记录全部公开

隐私总边界：零监控增量/L1-L3三档数据分级/人在回路终审/可关停可回滚/测试非运营
- 国际对标 6 案例，每案标注可比与不可比点；Sidewalk Toronto 作为数据治理失败的反例，据此确立「数据治理先于技术部署」红线

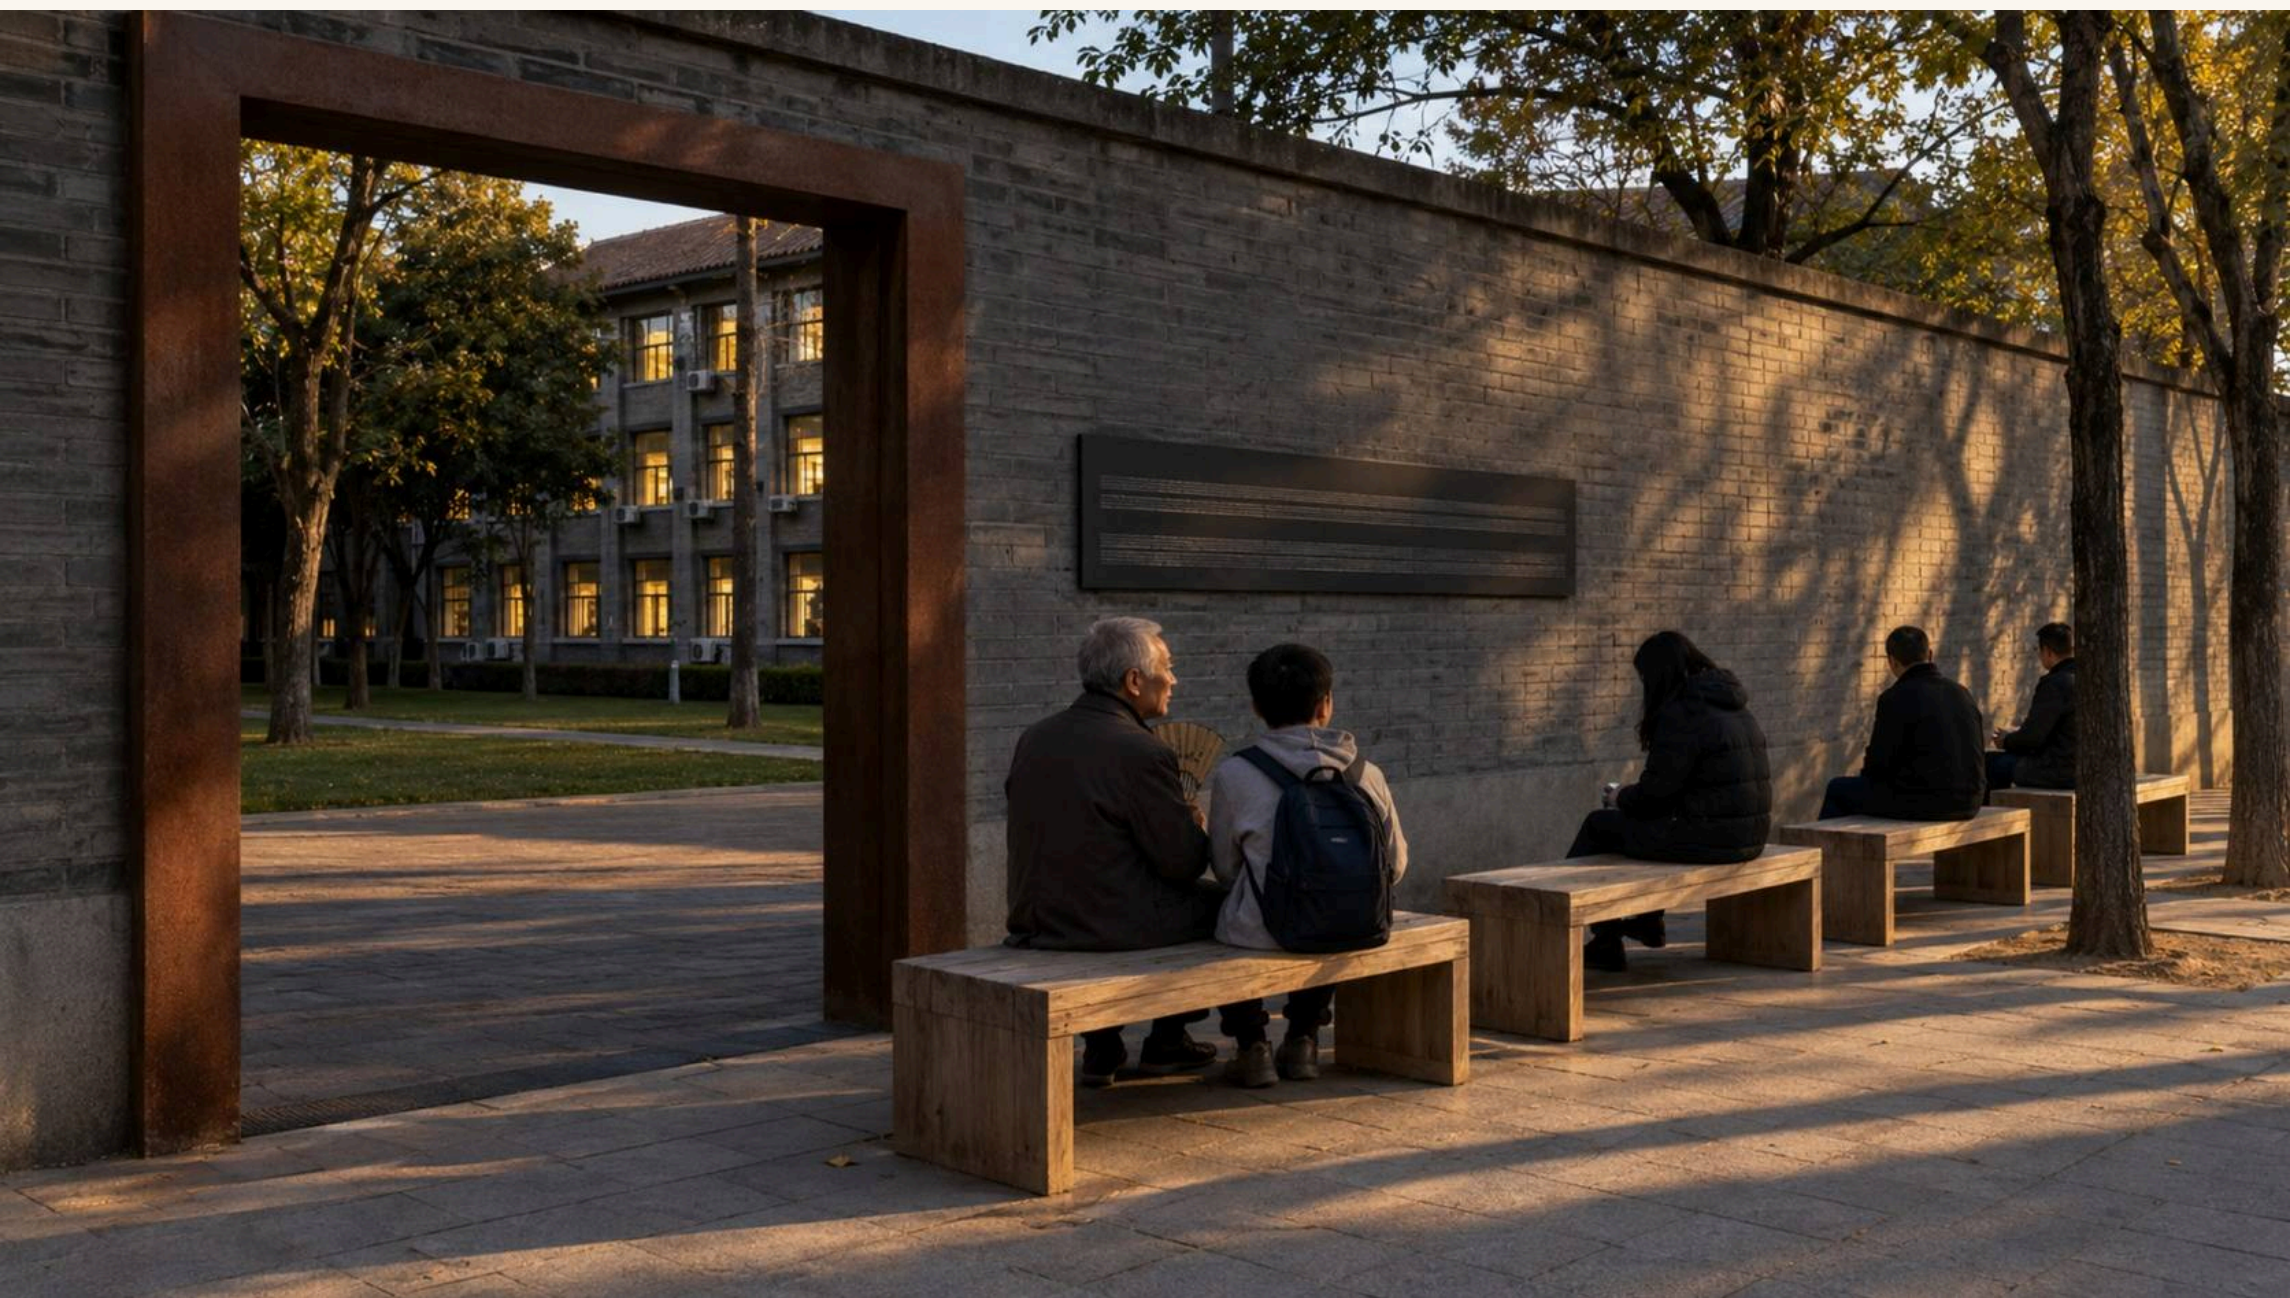

无墙学期·课门旁听席（AI 生成概念意象）

07 · 指标与合规

面积与 metrics.json 完全一致 · unknown 如实标注


9 km	1,141.3 ha	3	46	~70 / 45万	122
遗址公园主轴全长 · 约	报送范围 11,412,825 m² · metrics.json	重点设计片区 · 192.1 / 104.3 / 72.0 ha · 官方口径	二期规划出入口 · 以实际建成为准	沿线社区数 / 惠及人口 · 公开口径	海淀备案大模型 · 截至2026年2月区政府口径

指标	数值	状态/置信	来源
场地面积 site_area_sqm	11,412,825 m² (约 1,141.3 公顷)	known / 高置信	geometry/site_boundary.geojson
建筑基底 building_footprint_area_sqm	3,125 m²	known / 中置信	geometry/buildings.geojson
绿地率 green_ratio	25.0%	known / 中置信	geometry/green_space.geojson
公共空间率 public_space_ratio	1.9%	known / 中置信	geometry/public_space.geojson
容积率 floor_area_ratio	未知（官方控制指标未公开，不做推断）	unknown	planning_limits.json 缺失
重点片区数 key_area_count	3	known / 高置信	geometry/key_areas.geojson

合规与风险

- 场景卡覆盖甲方点名的八类场景与三个概念；轨道名称为本方案自定，不冒充官方编码
- 措辞纪律：全文'概念建议/参考方案/待专业团队深化'；无容积率、高度、红线、拆改留结论
- 事实纪律：企业名单/投资额/产值/政策承诺零虚构；所有数字带公开来源（sources.json）
- 口径纪律：备案数 122（区政府 2026-02）为统一口径，时点差异如实脚注
- 红色叙事边界：3-25开放日为唯一红色触点，无企业冠名/无商业路演/无当场钉钉

- 主要风险：文保范围 GIS 缺失、容积率未知、测试以许可为前提——均如实标注，不以估值充数

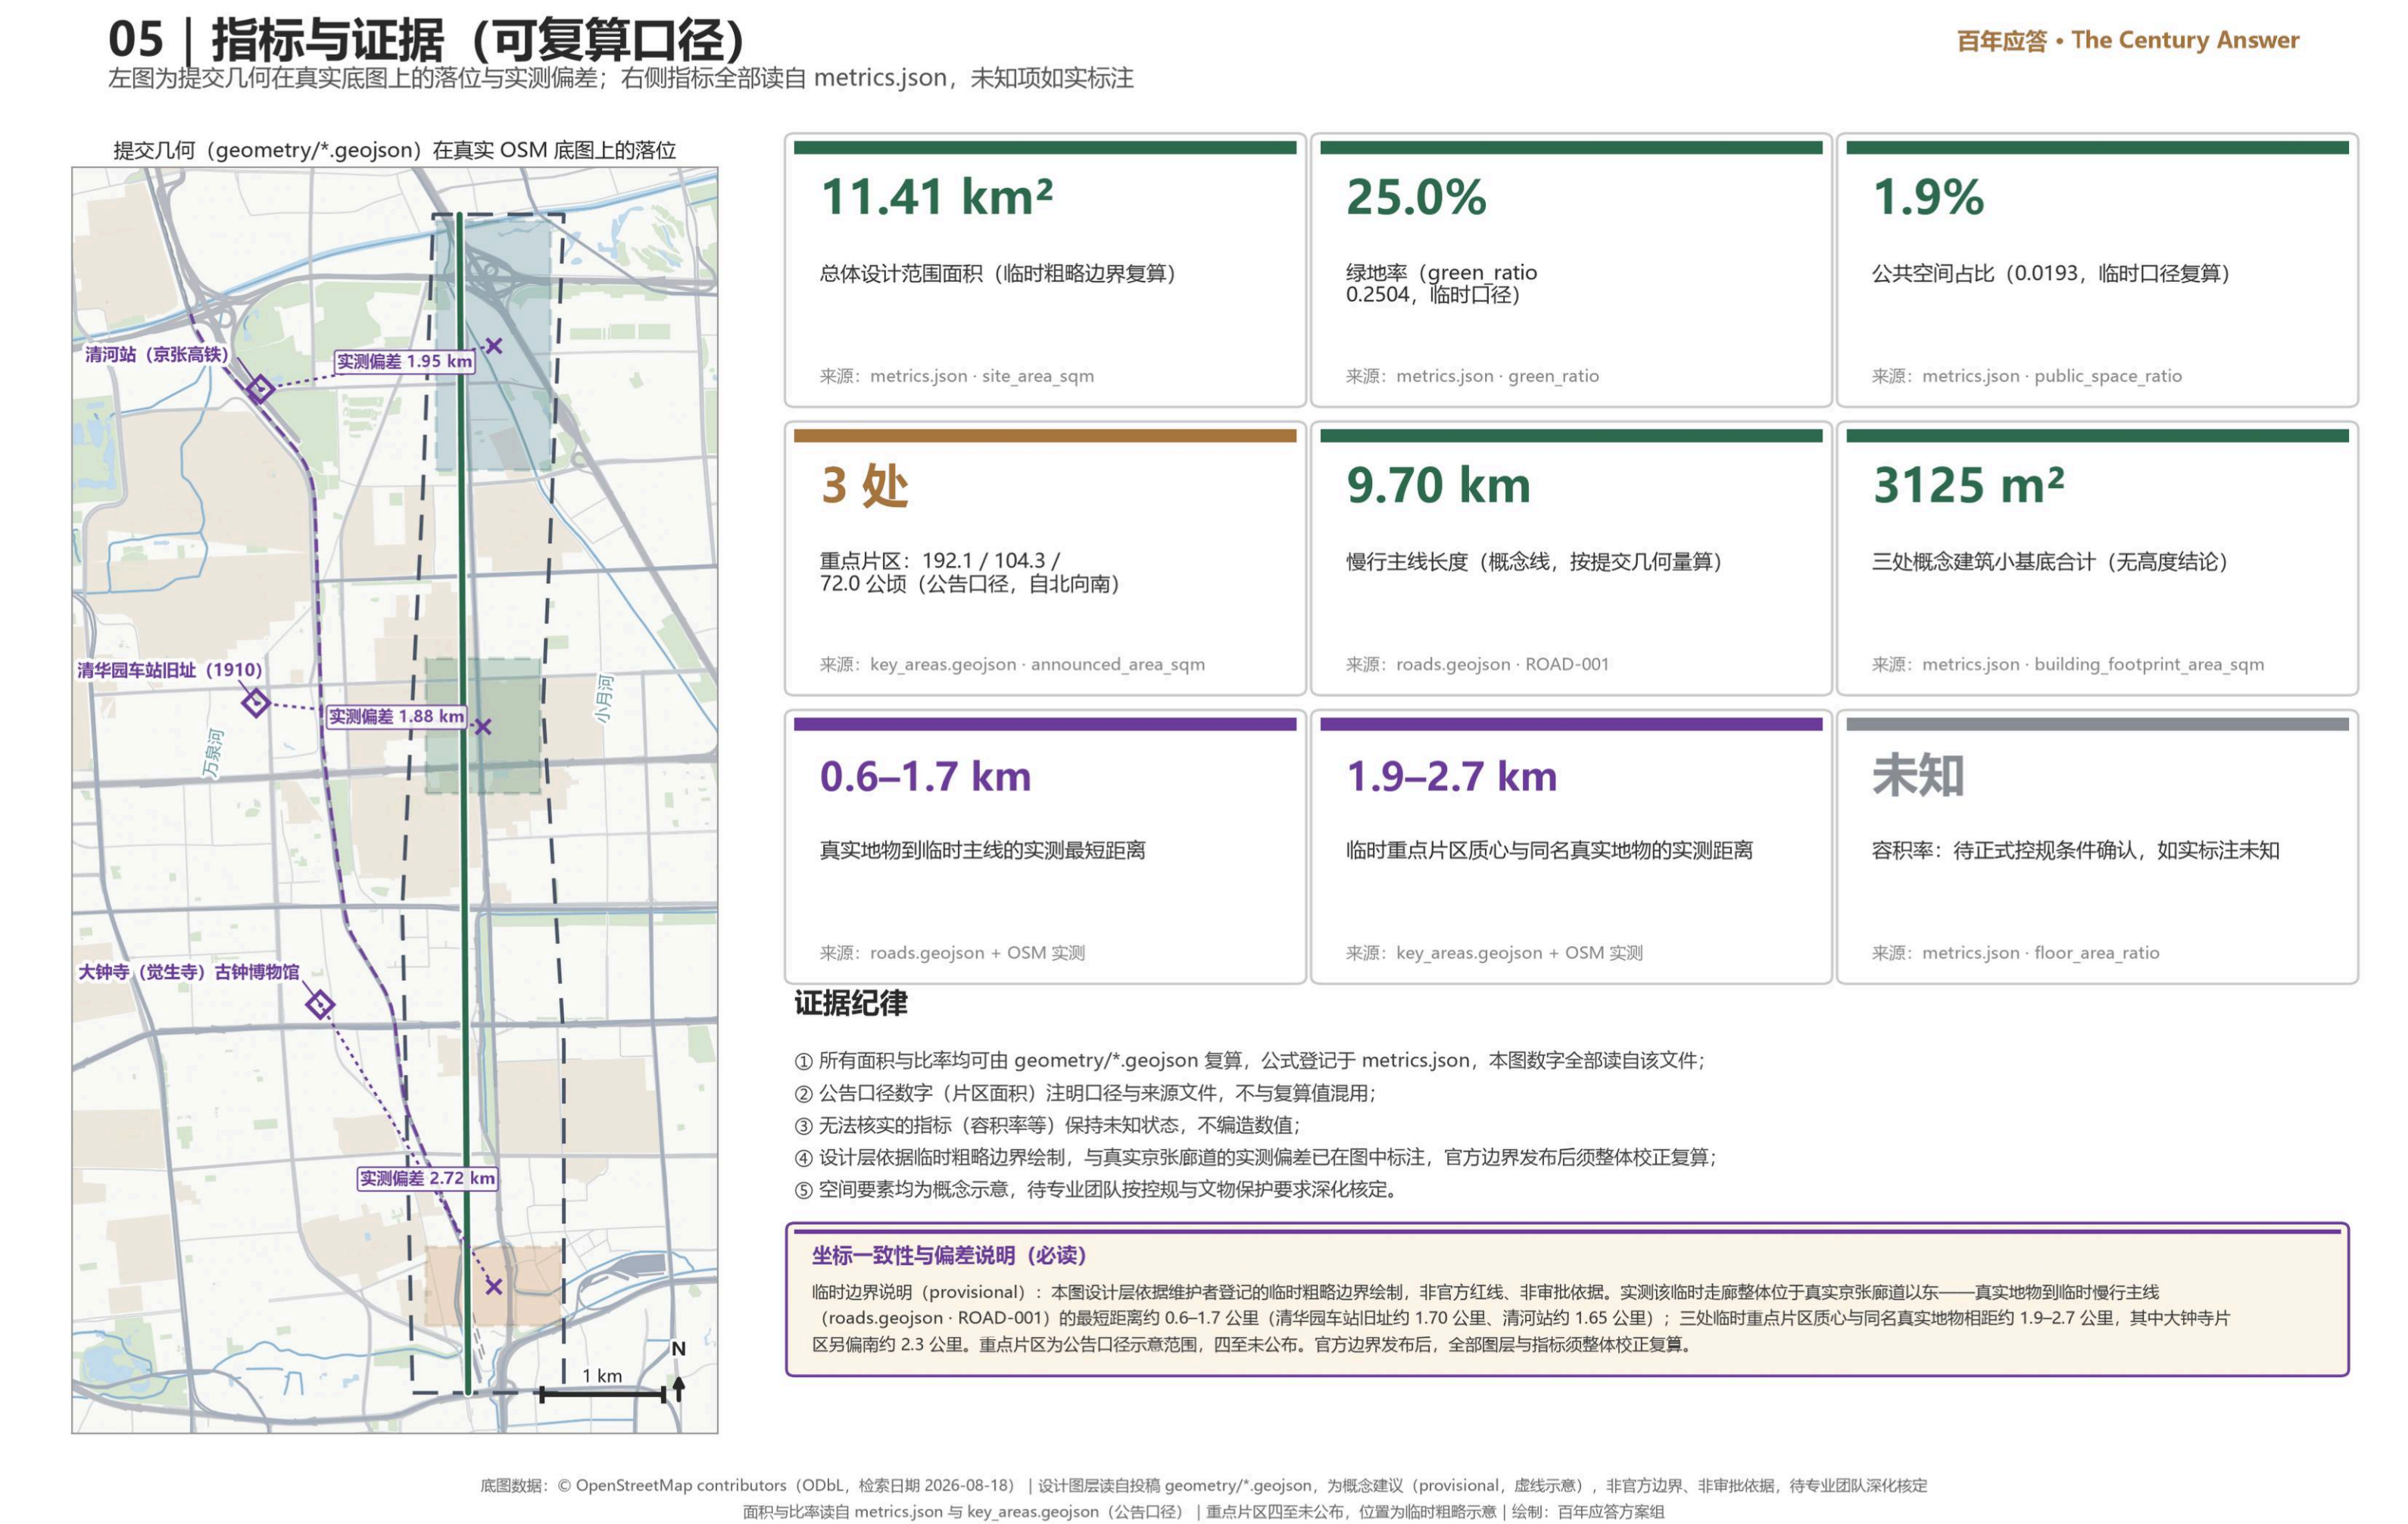

指标证据图（与本表同源）