

图 1 · 总体设计总平面：一线三折两翼七点（概念方案）









图2 · 三层范围传导与用地结构 (provisional 边界为虚线约束，重点在分区逻辑与职住判断)

图2a · 用地结构与 POI 动力分区 (概念)

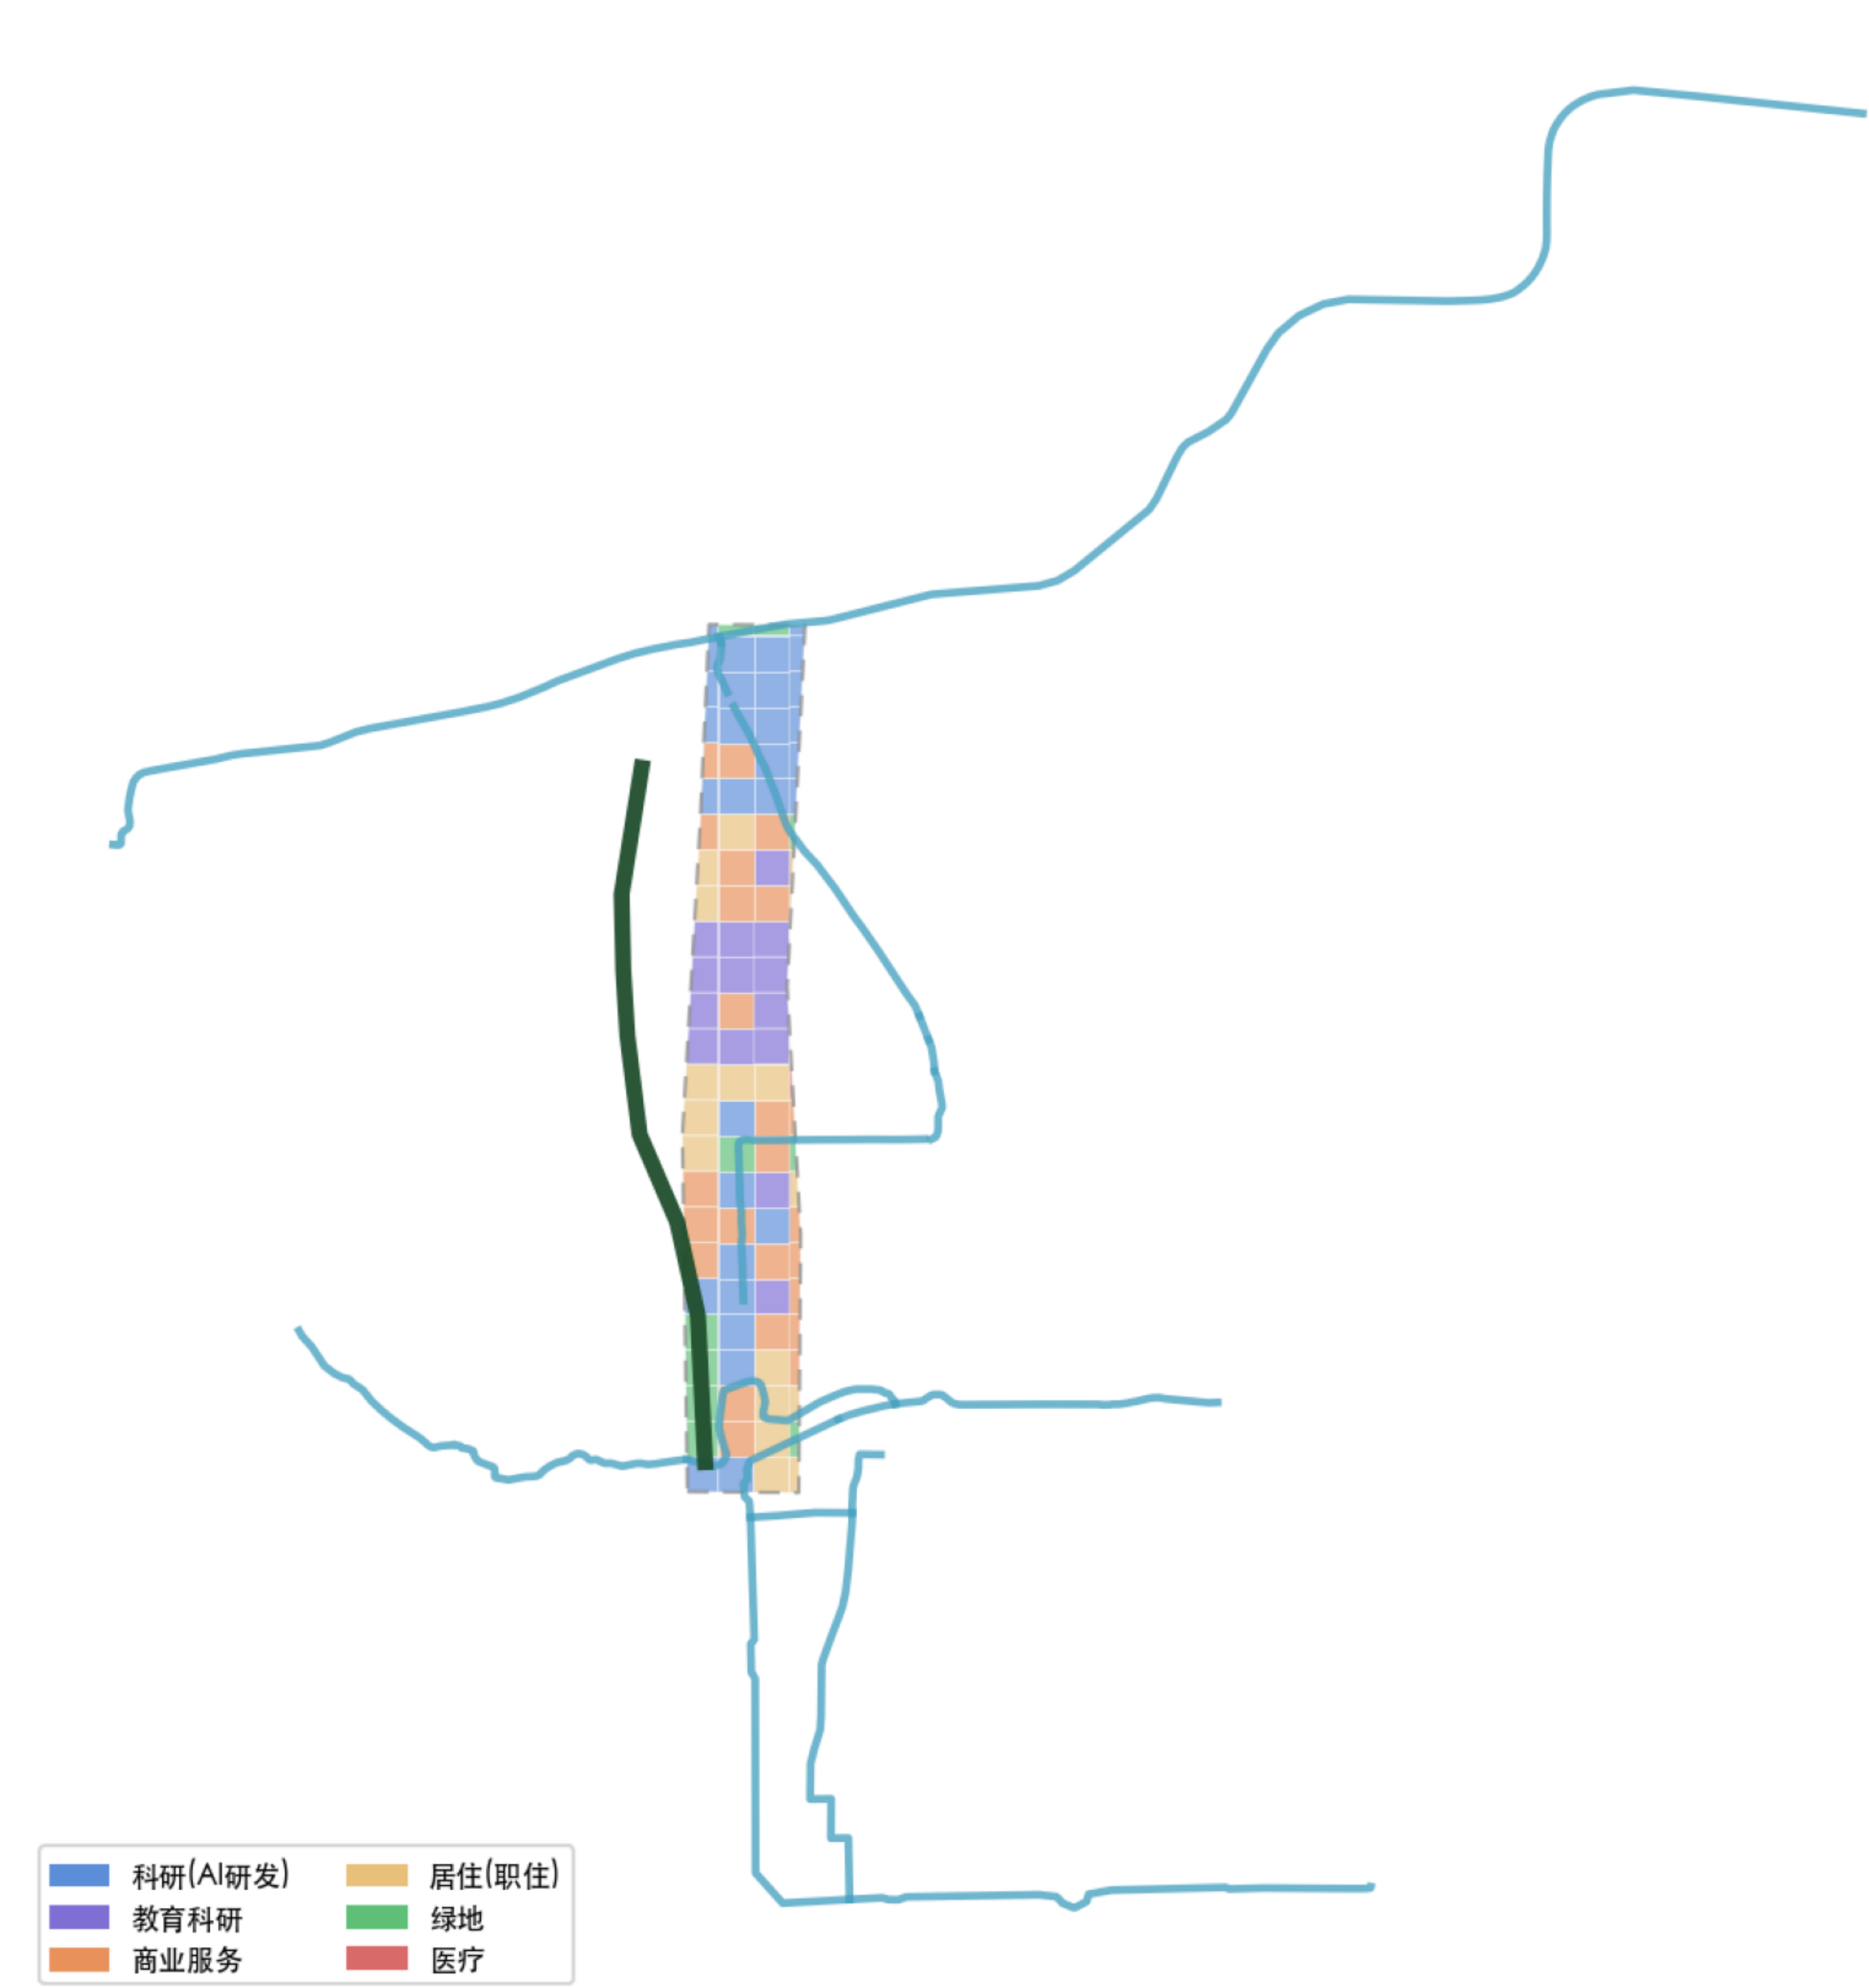


图2b · 用地构成 (万 m², 概念分区)



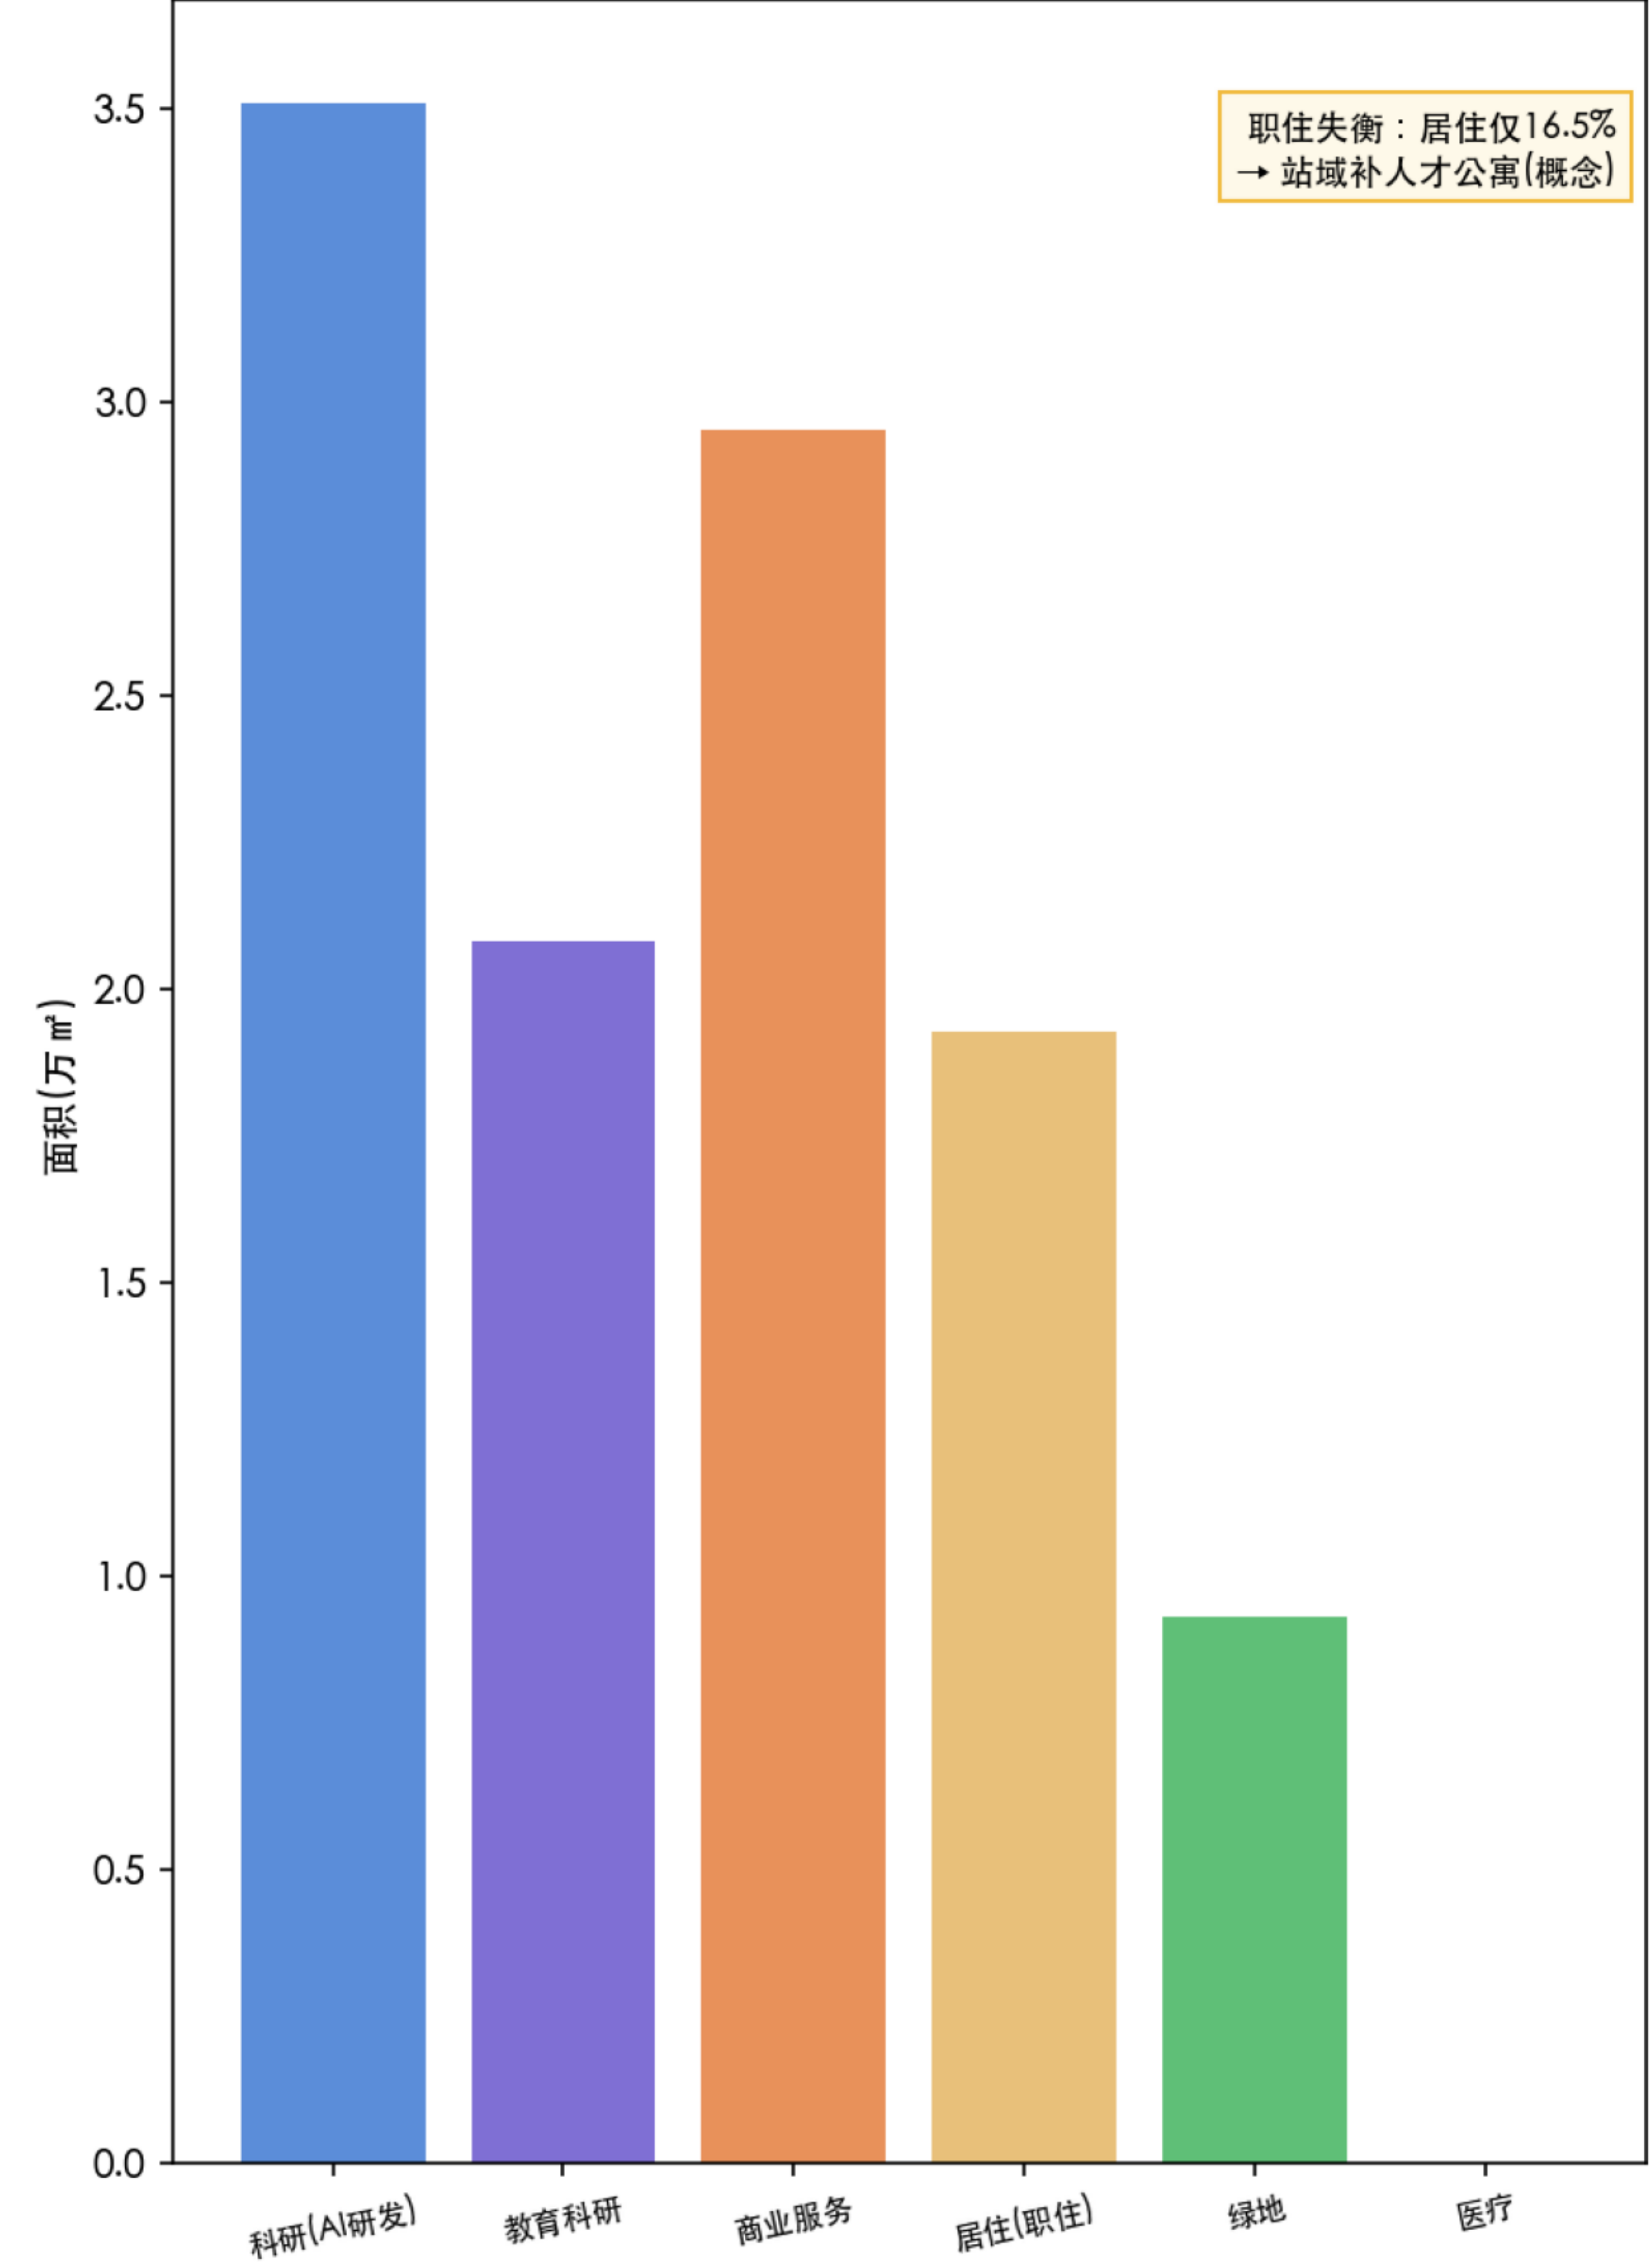




图4 · 交通慢行与蓝绿系统：七节点缝合

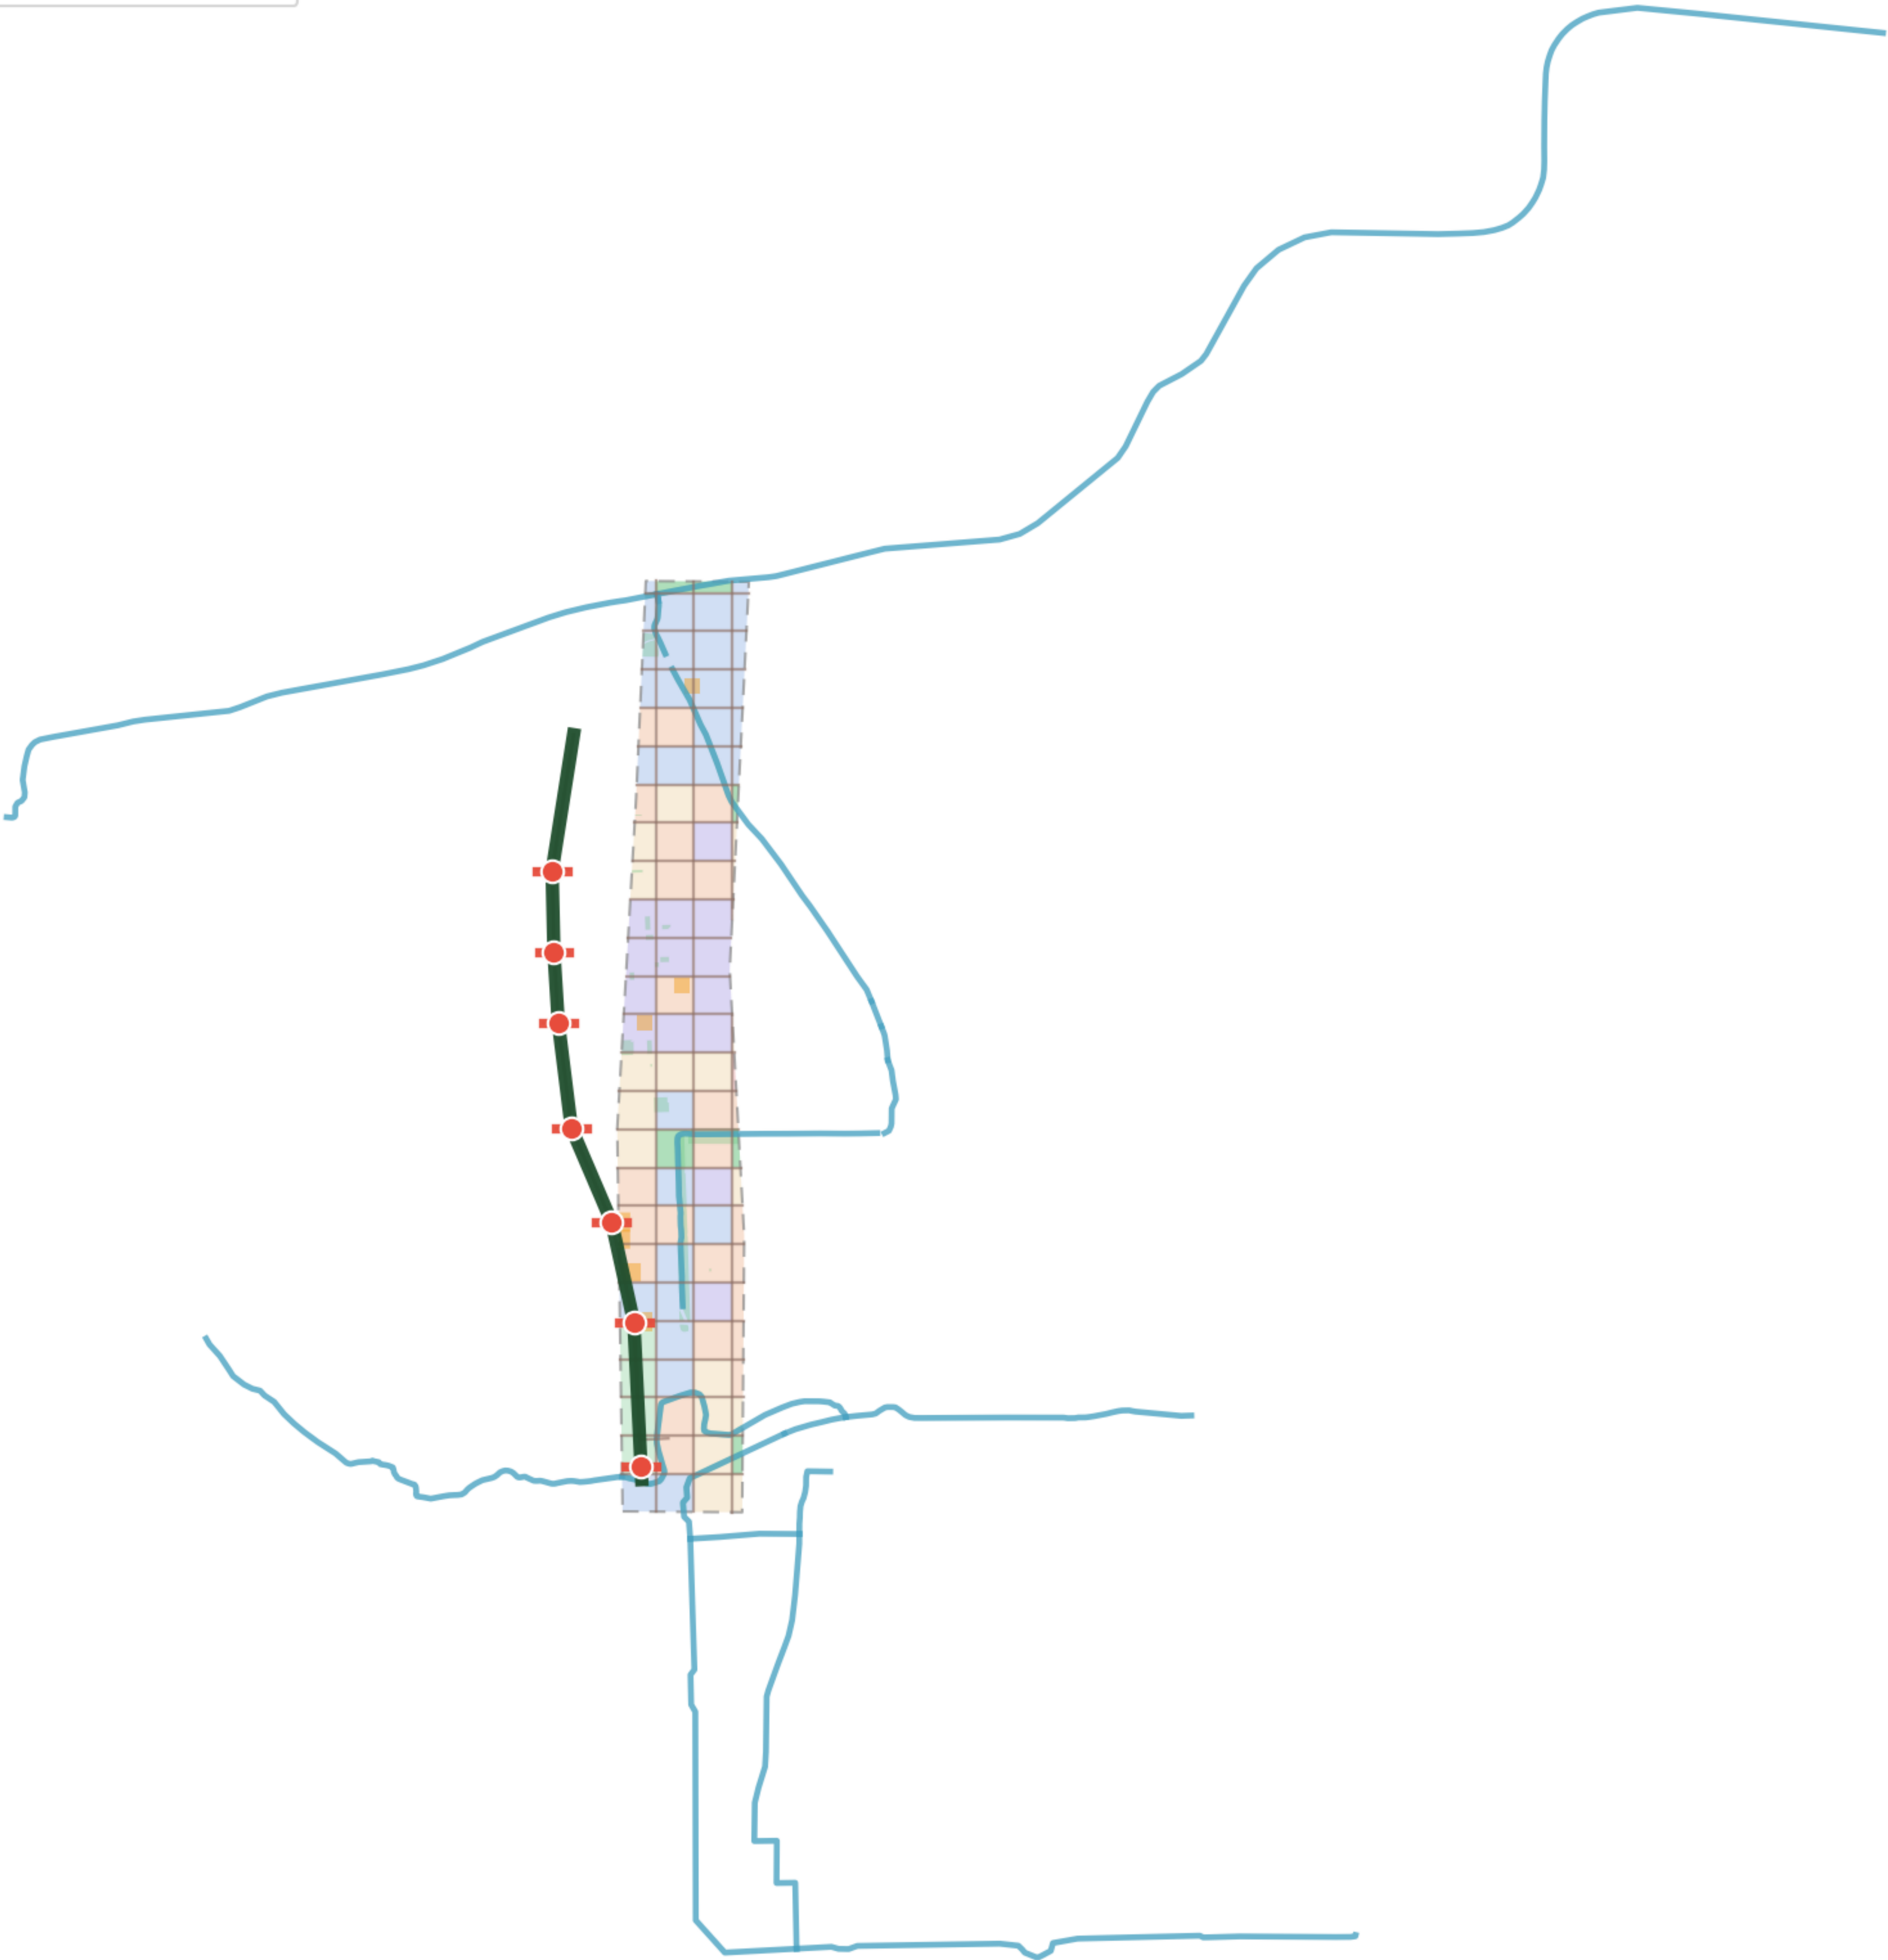

7处主干路断点→缝合步道(红线)；整合度提升：北京北+132% 大钟寺+102% 五道口+65%（空间句法实算）

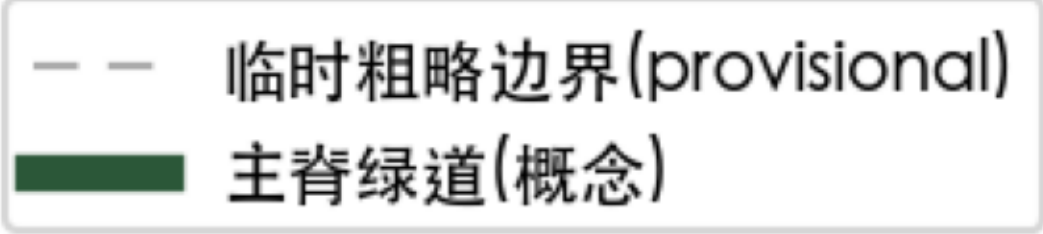

