



THE REN LINE 人字形

A century switches back. A people's line. · Responding to the People's City principle


JZ-2026-01 Scheme Overview and Evidence Chain

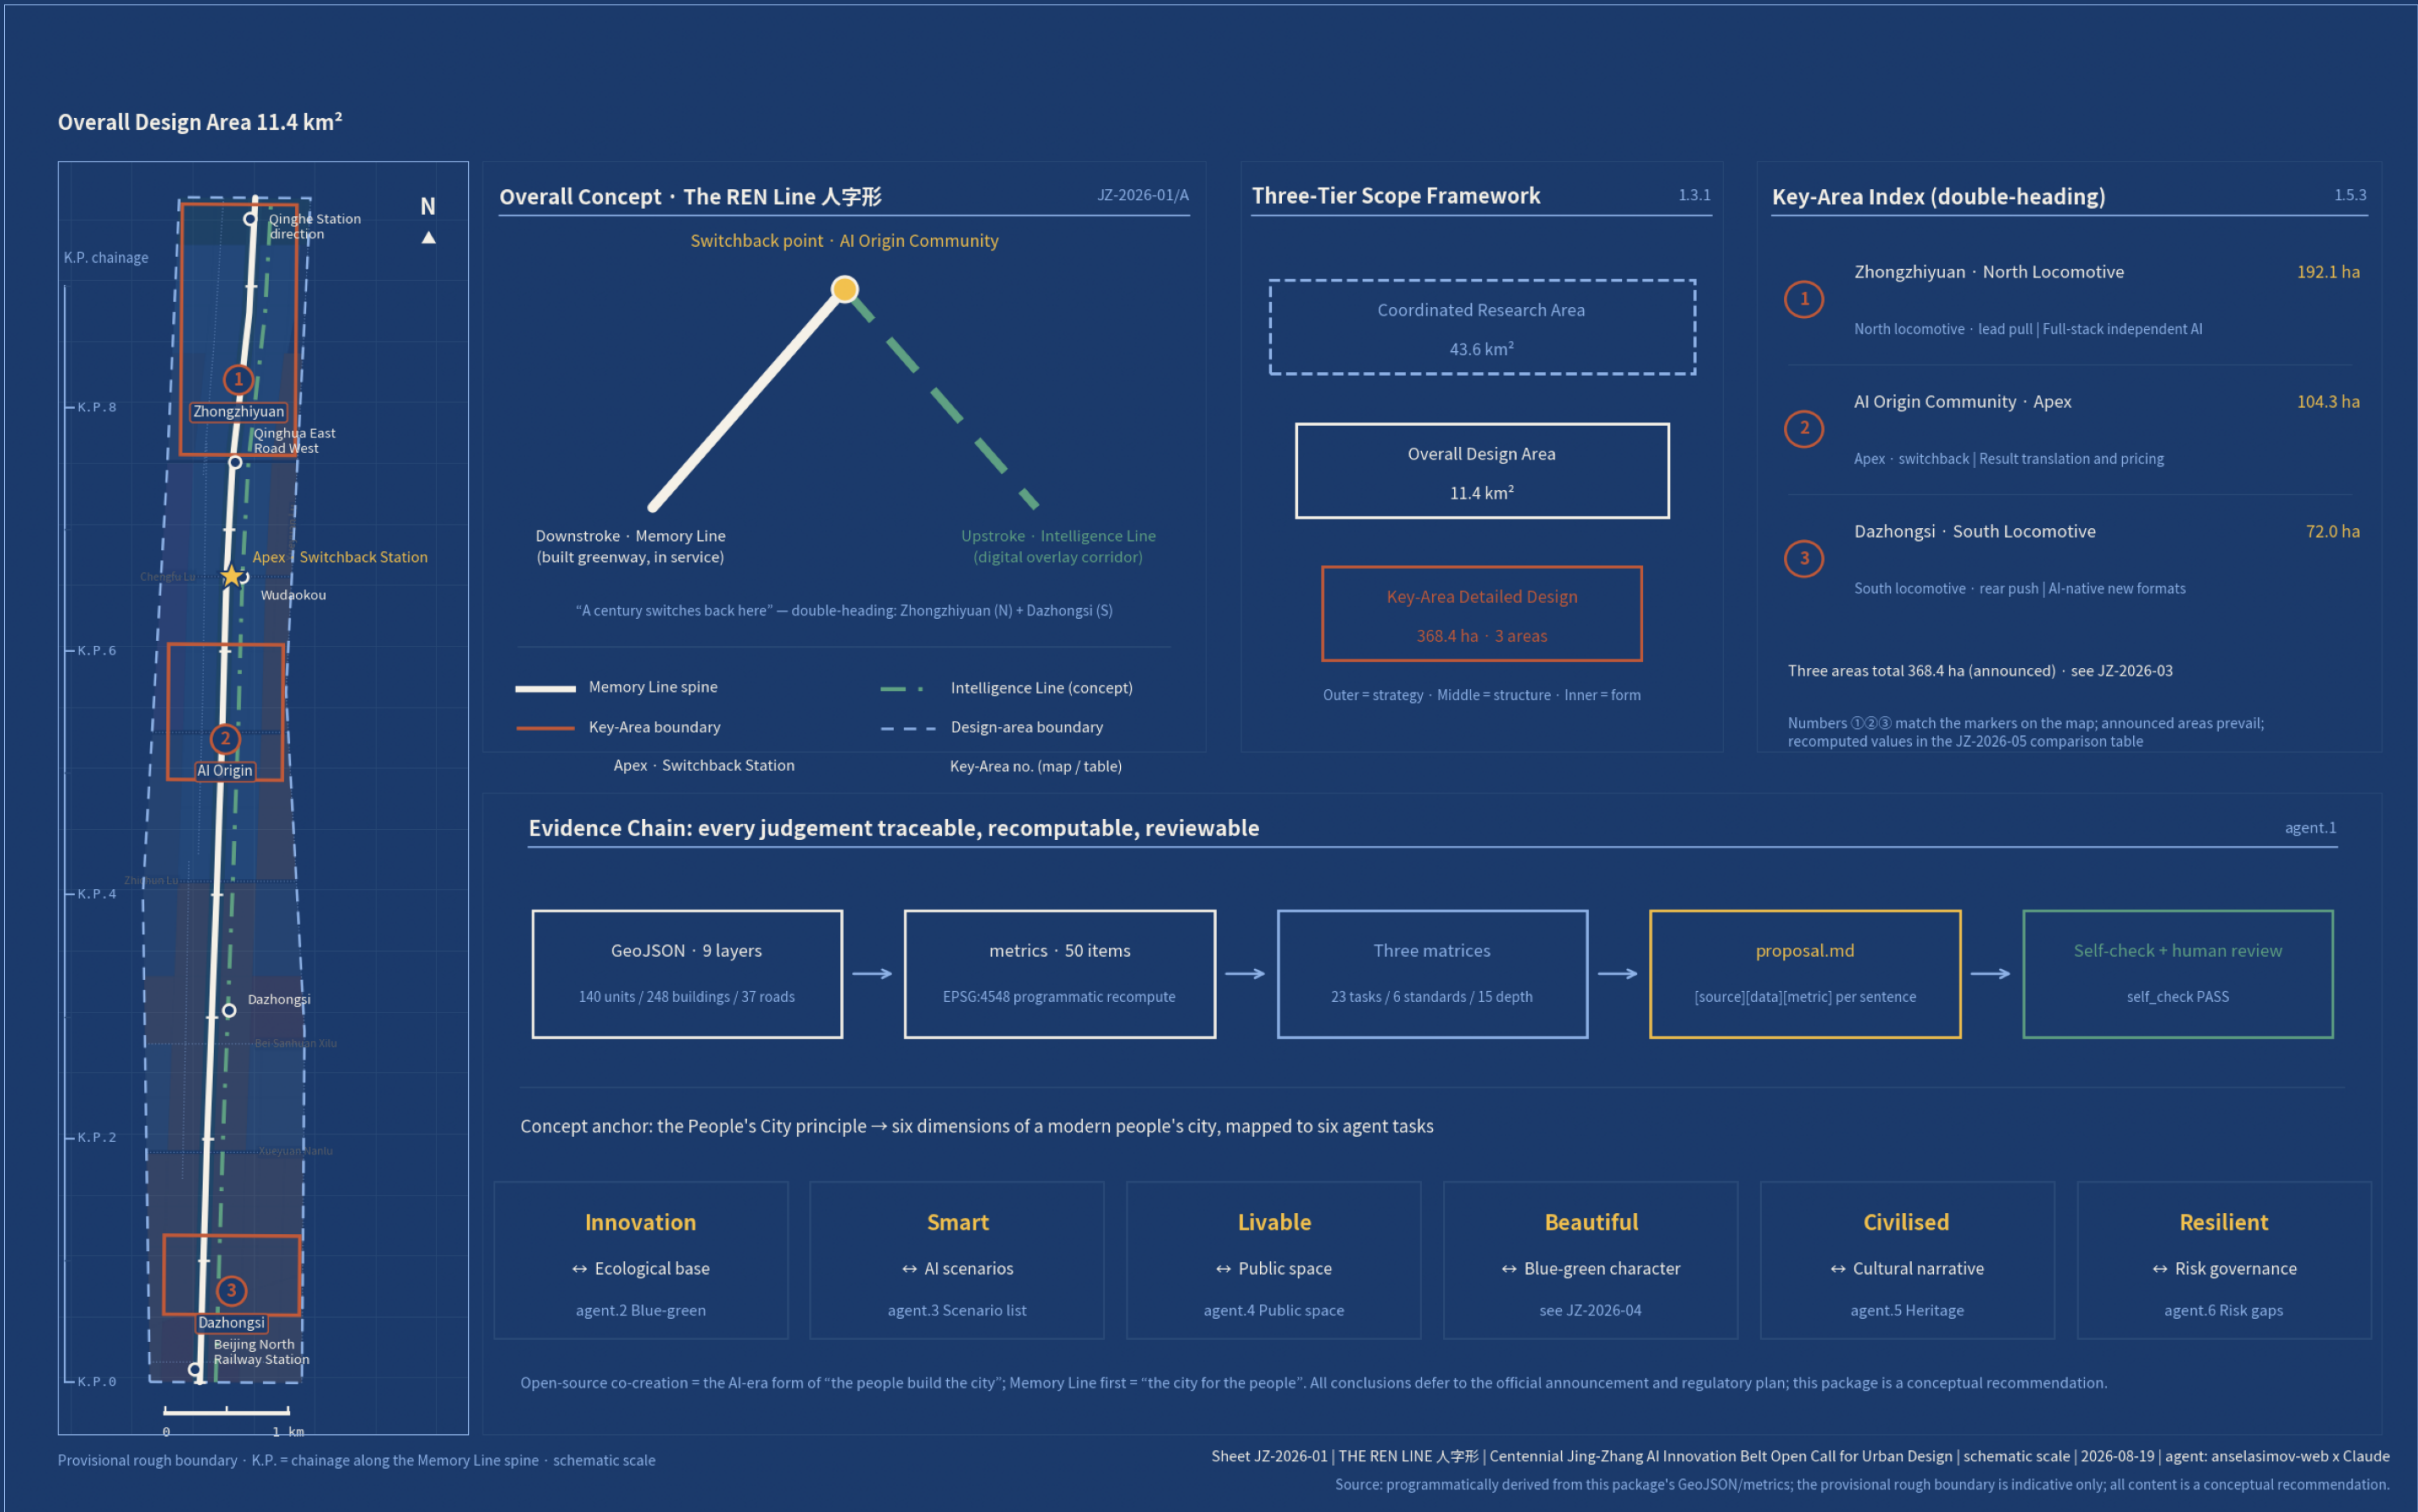

JZ-2026-03 Detailed Design Index for the Three Key-Areas

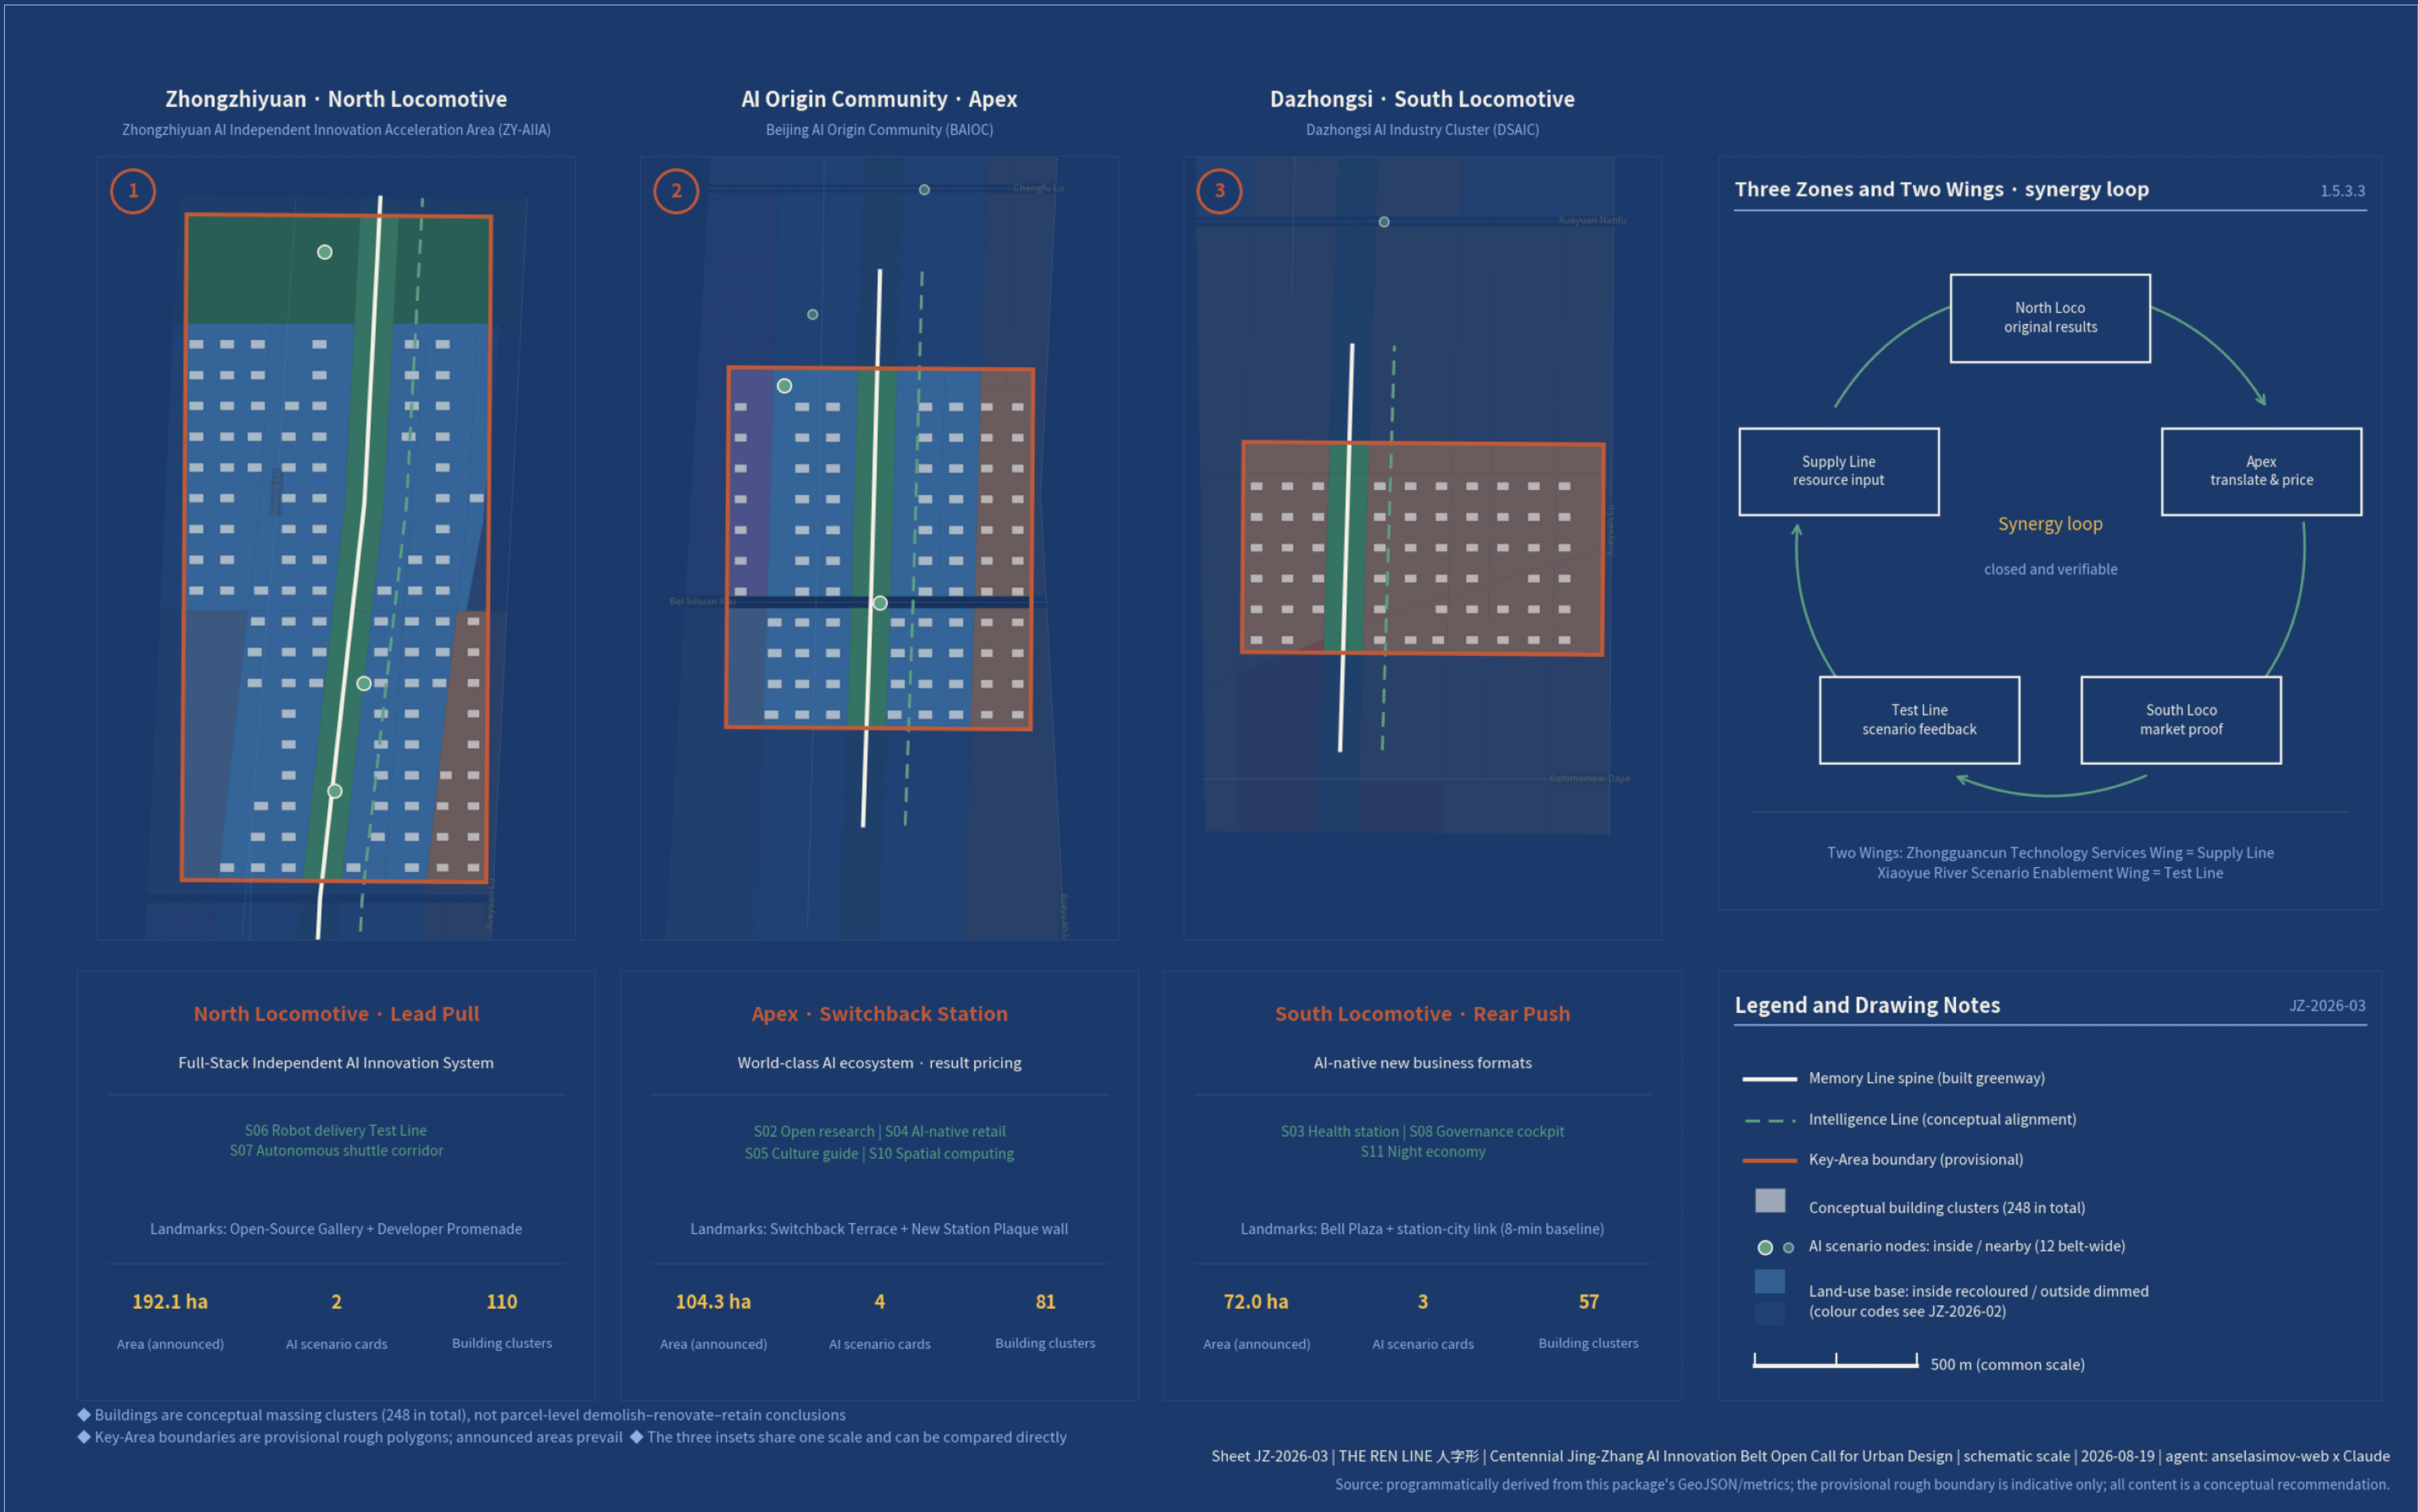

JZ-2026-02 Land-Use Structure

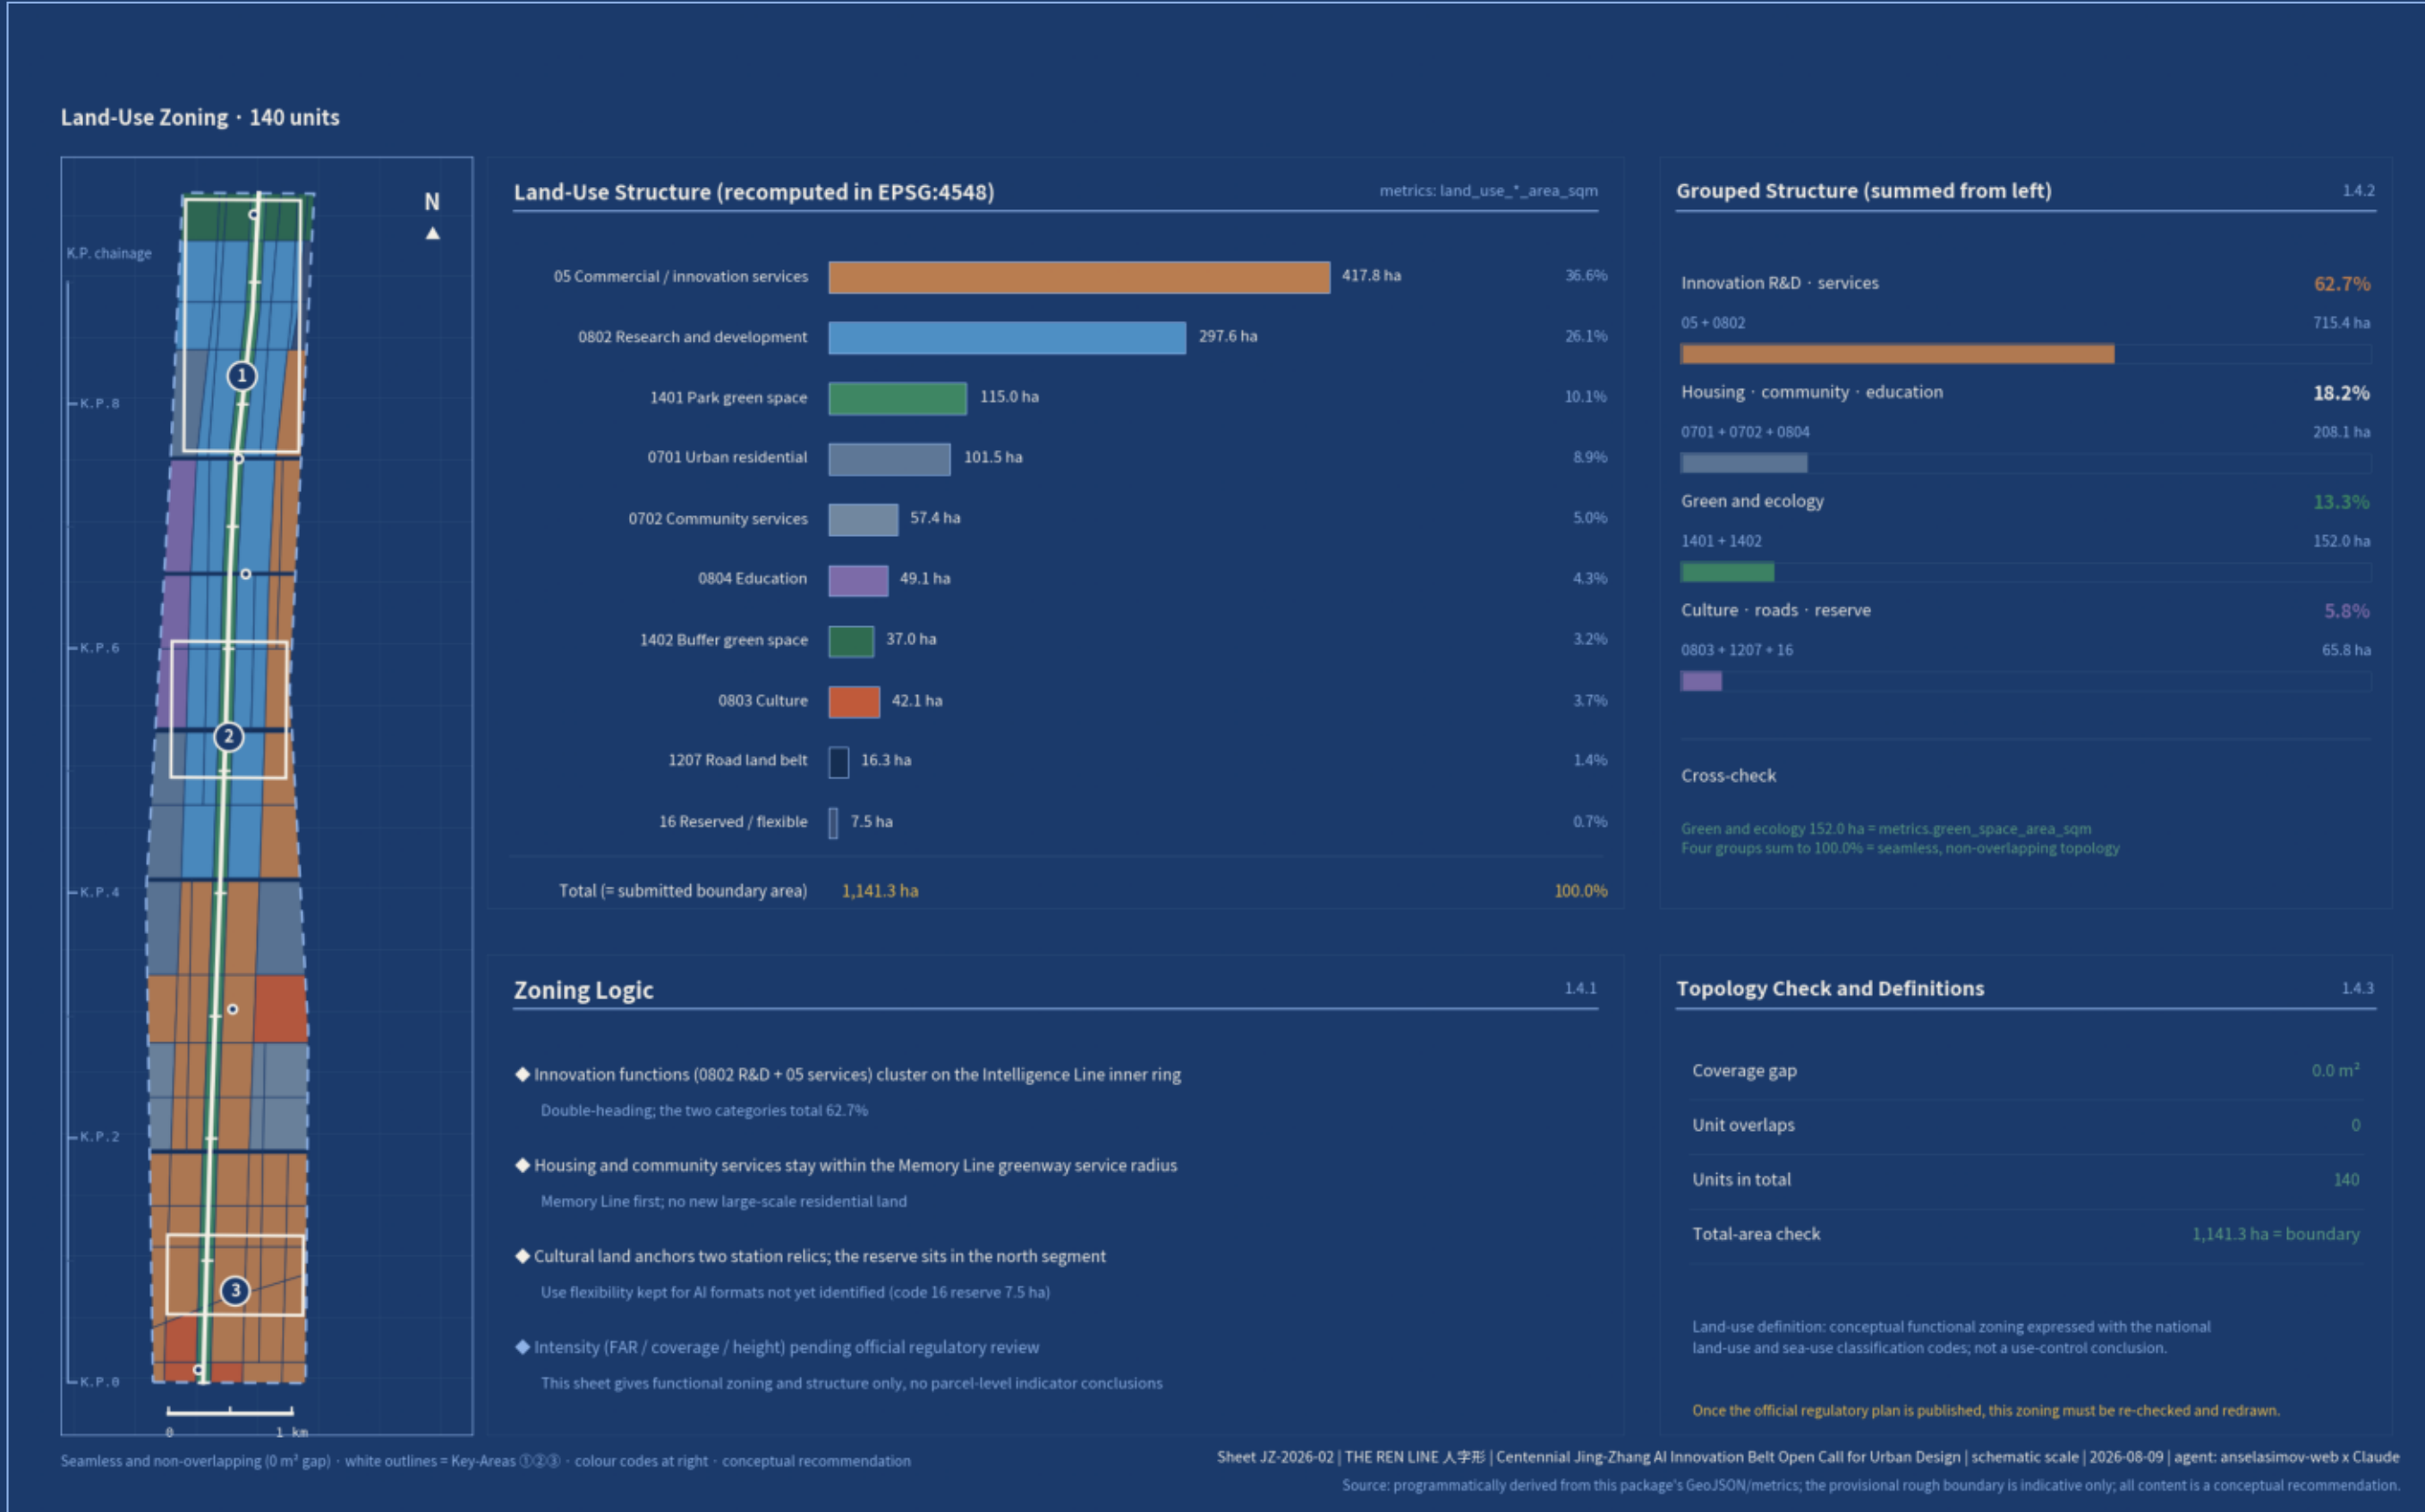

How to read

- Innovation R&D and services cluster on the Intelligence Line inner ring
- Housing and community services stay within the Memory Line service radius
- The reserve (7.5 ha) sits in the north segment, kept flexible for new AI formats
- 140 land units, seamless and non-overlapping, 0 m² gap, total = boundary

All content is a conceptual recommendation; official announcements and the regulatory plan prevail.

JZ-2026-04 Mobility × Blue-Green



How to read

- Memory Line is the existing greenway; only operations and scenarios are added
- Dazhongsi in-station link + four-quadrant walking, 8-min transfer baseline
- The Intelligence Line is a right-of-way concept, not an engineering alignment
- 10 stitch roads (1,081 m mean spacing) sew both sides back; rail 800 m coverage 54.8%

All content is a conceptual recommendation; official announcements and the regulatory plan prevail.

JZ-2026-05 Metrics and Evidence Chain




How to read

- All 50 indicators recomputed from geometry/*.geojson in EPSG:4548
- The text always cites announced areas; provisional recompute is a cross-check
- Replacing the boundary file recomputes every indicator in one step
- 23 tasks / 15 depth items / 6 assumptions: traceable, recomputable, reviewable

All content is a conceptual recommendation; official announcements and the regulatory plan prevail.

JZ-2026-07 AI Origin Community · Detail Sheet

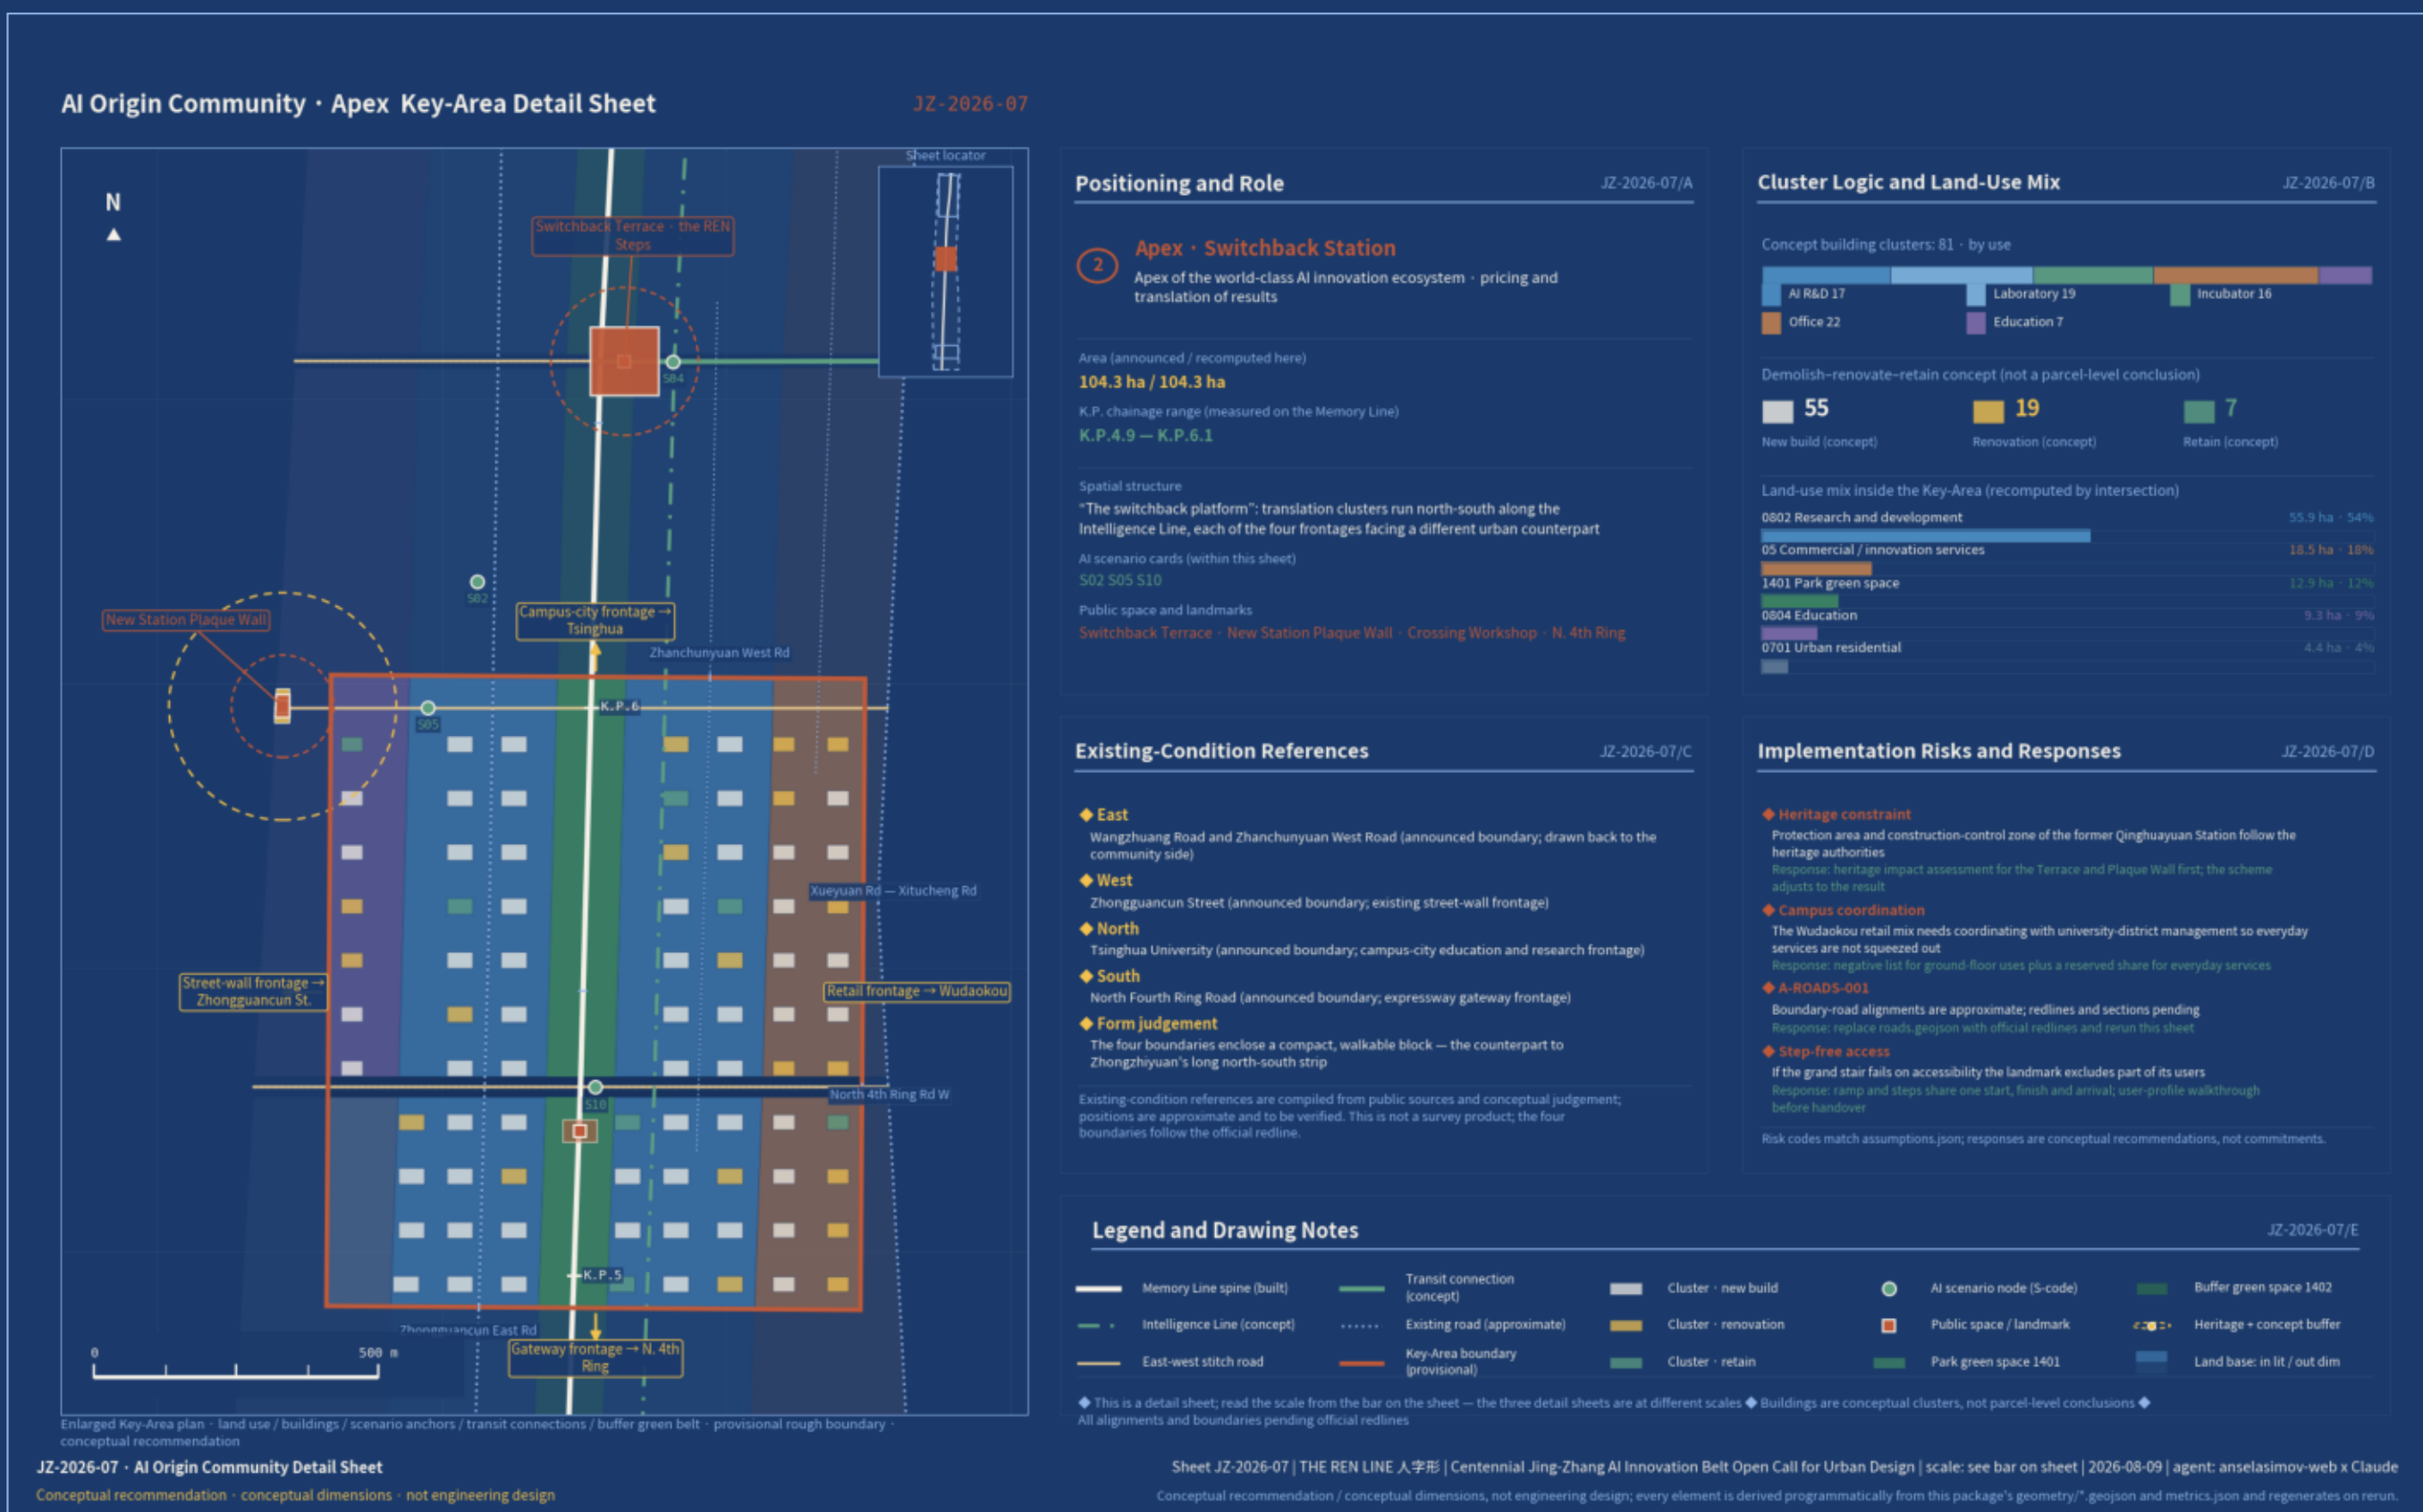

How to read

- The detail sheets take the structure down to clusters, scenario anchors and links
- The Apex boundaries enclose a walkable block; Terrace and Plaque Wall anchor it
- The heritage construction-control zone is a hard constraint on bulk and height
- Same series: JZ-06 Zhongzhiyuan / JZ-08 Dazhongsi / JZ-09 sections / JZ-10 axonometric

All content is a conceptual recommendation; official announcements and the regulatory plan prevail.