


总体设计与实施索引

一轴三片、多点支撑：总体结构、首期示范段、重点片区和图纸目录。

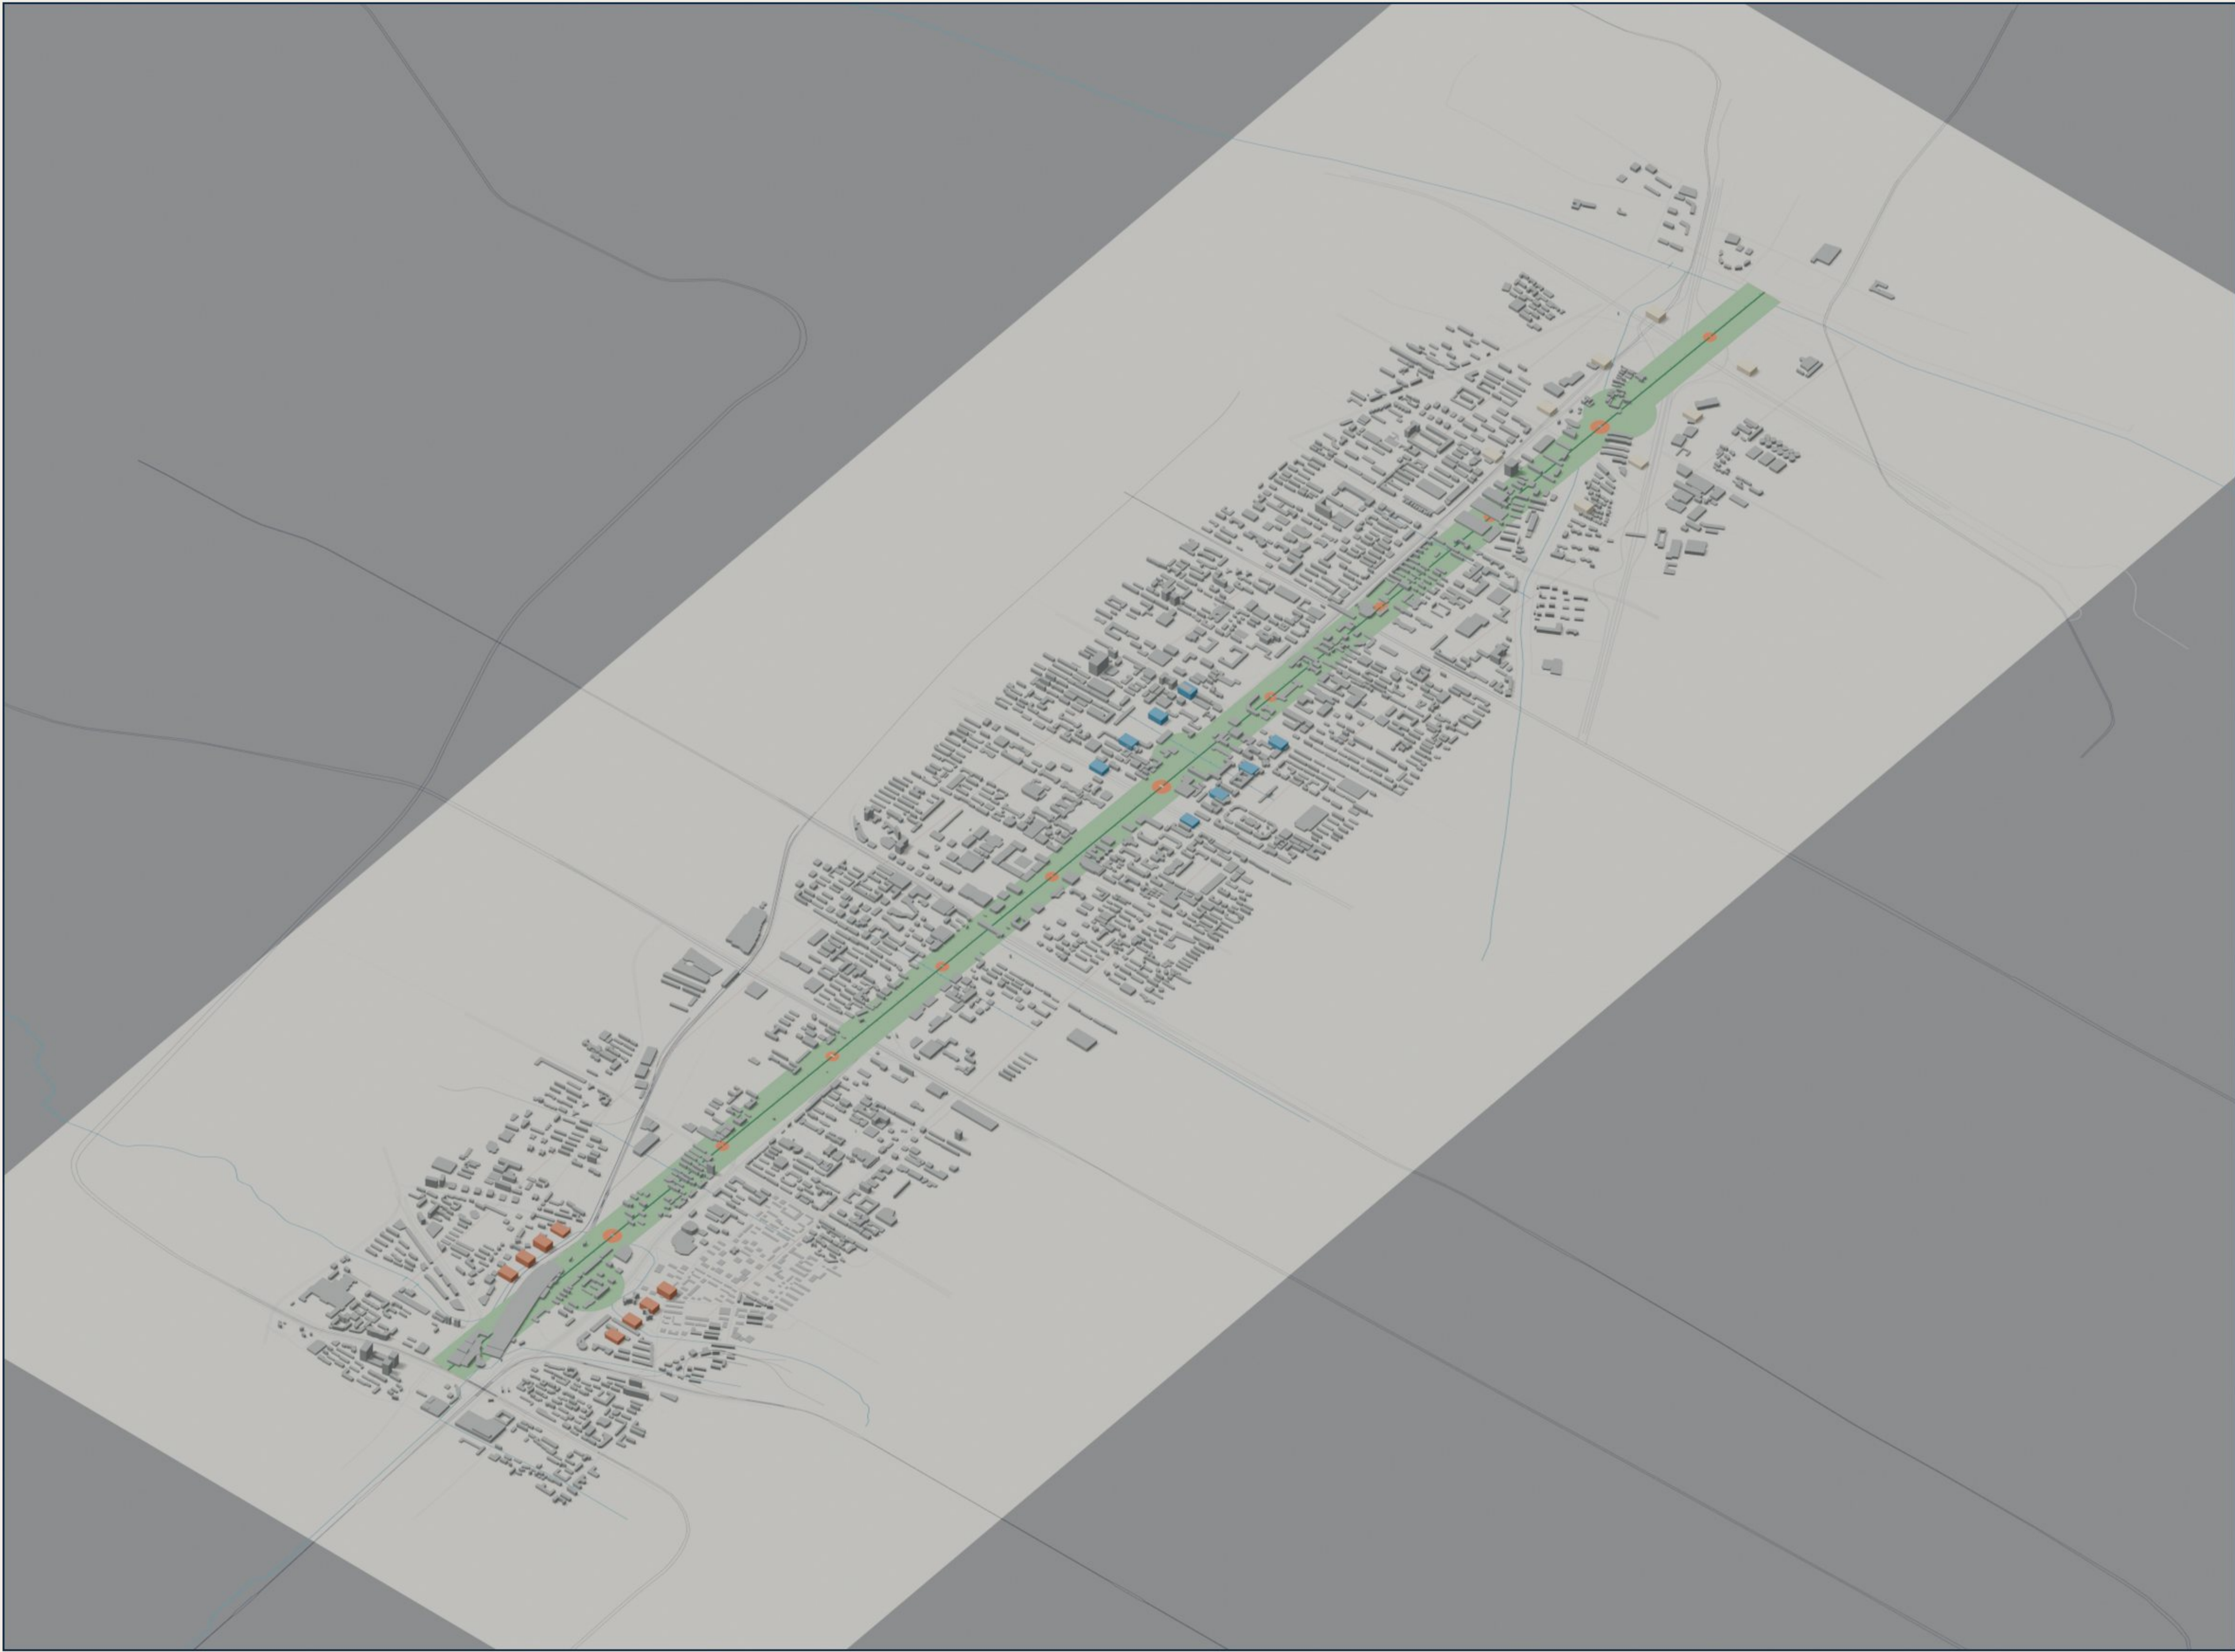

1.0 km 首期示范段

连续慢行与骑行系统贯通
雨水花园约 1,800 m²，新增遮阴约 2,400 m²
首期选择 3 处服务节点完成首件样板

C-01 总平 / C-02 断面 / C-03 节点

3 处 重点片区

众智园承担受控验证与公众审议
AI 原点社区导入共享首层与协同创新
大钟寺完善站城接驳与人工服务

P-03 受控验证 / P-04 共享首层 / P-02 站城服务

12 处 公共服务节点

单处建议 250—400 m²，首期样板 3 处
覆盖休憩、学习、维护、咨询和应急
连续无障碍与人工服务渠道同步保留

N01—N12 / M1—M5 / E1

6 项 近期项目

空间建设、片区更新、节点设施和治理系统
形成 6 个项目任务包与 5 个采购包
共用资料、审查、样板、验收、复审关口

P-01—P-06 / W-01—W-05 / G0—G4

成果索引

- 05

示范段总平
- 07

断面与构造
- 08

服务节点
- 12

项目交付
- 14

绩效验收
- 15

运营证据



众智园创新验证片区



北京 AI 原点社区协同创新片区




大钟寺站城融合片区

示范段总平与构造系统

一公里里程化总平 + 十二米断面 + 320 m² 服务节点 + 四类标准构造。



一公里示范段与十二处节点

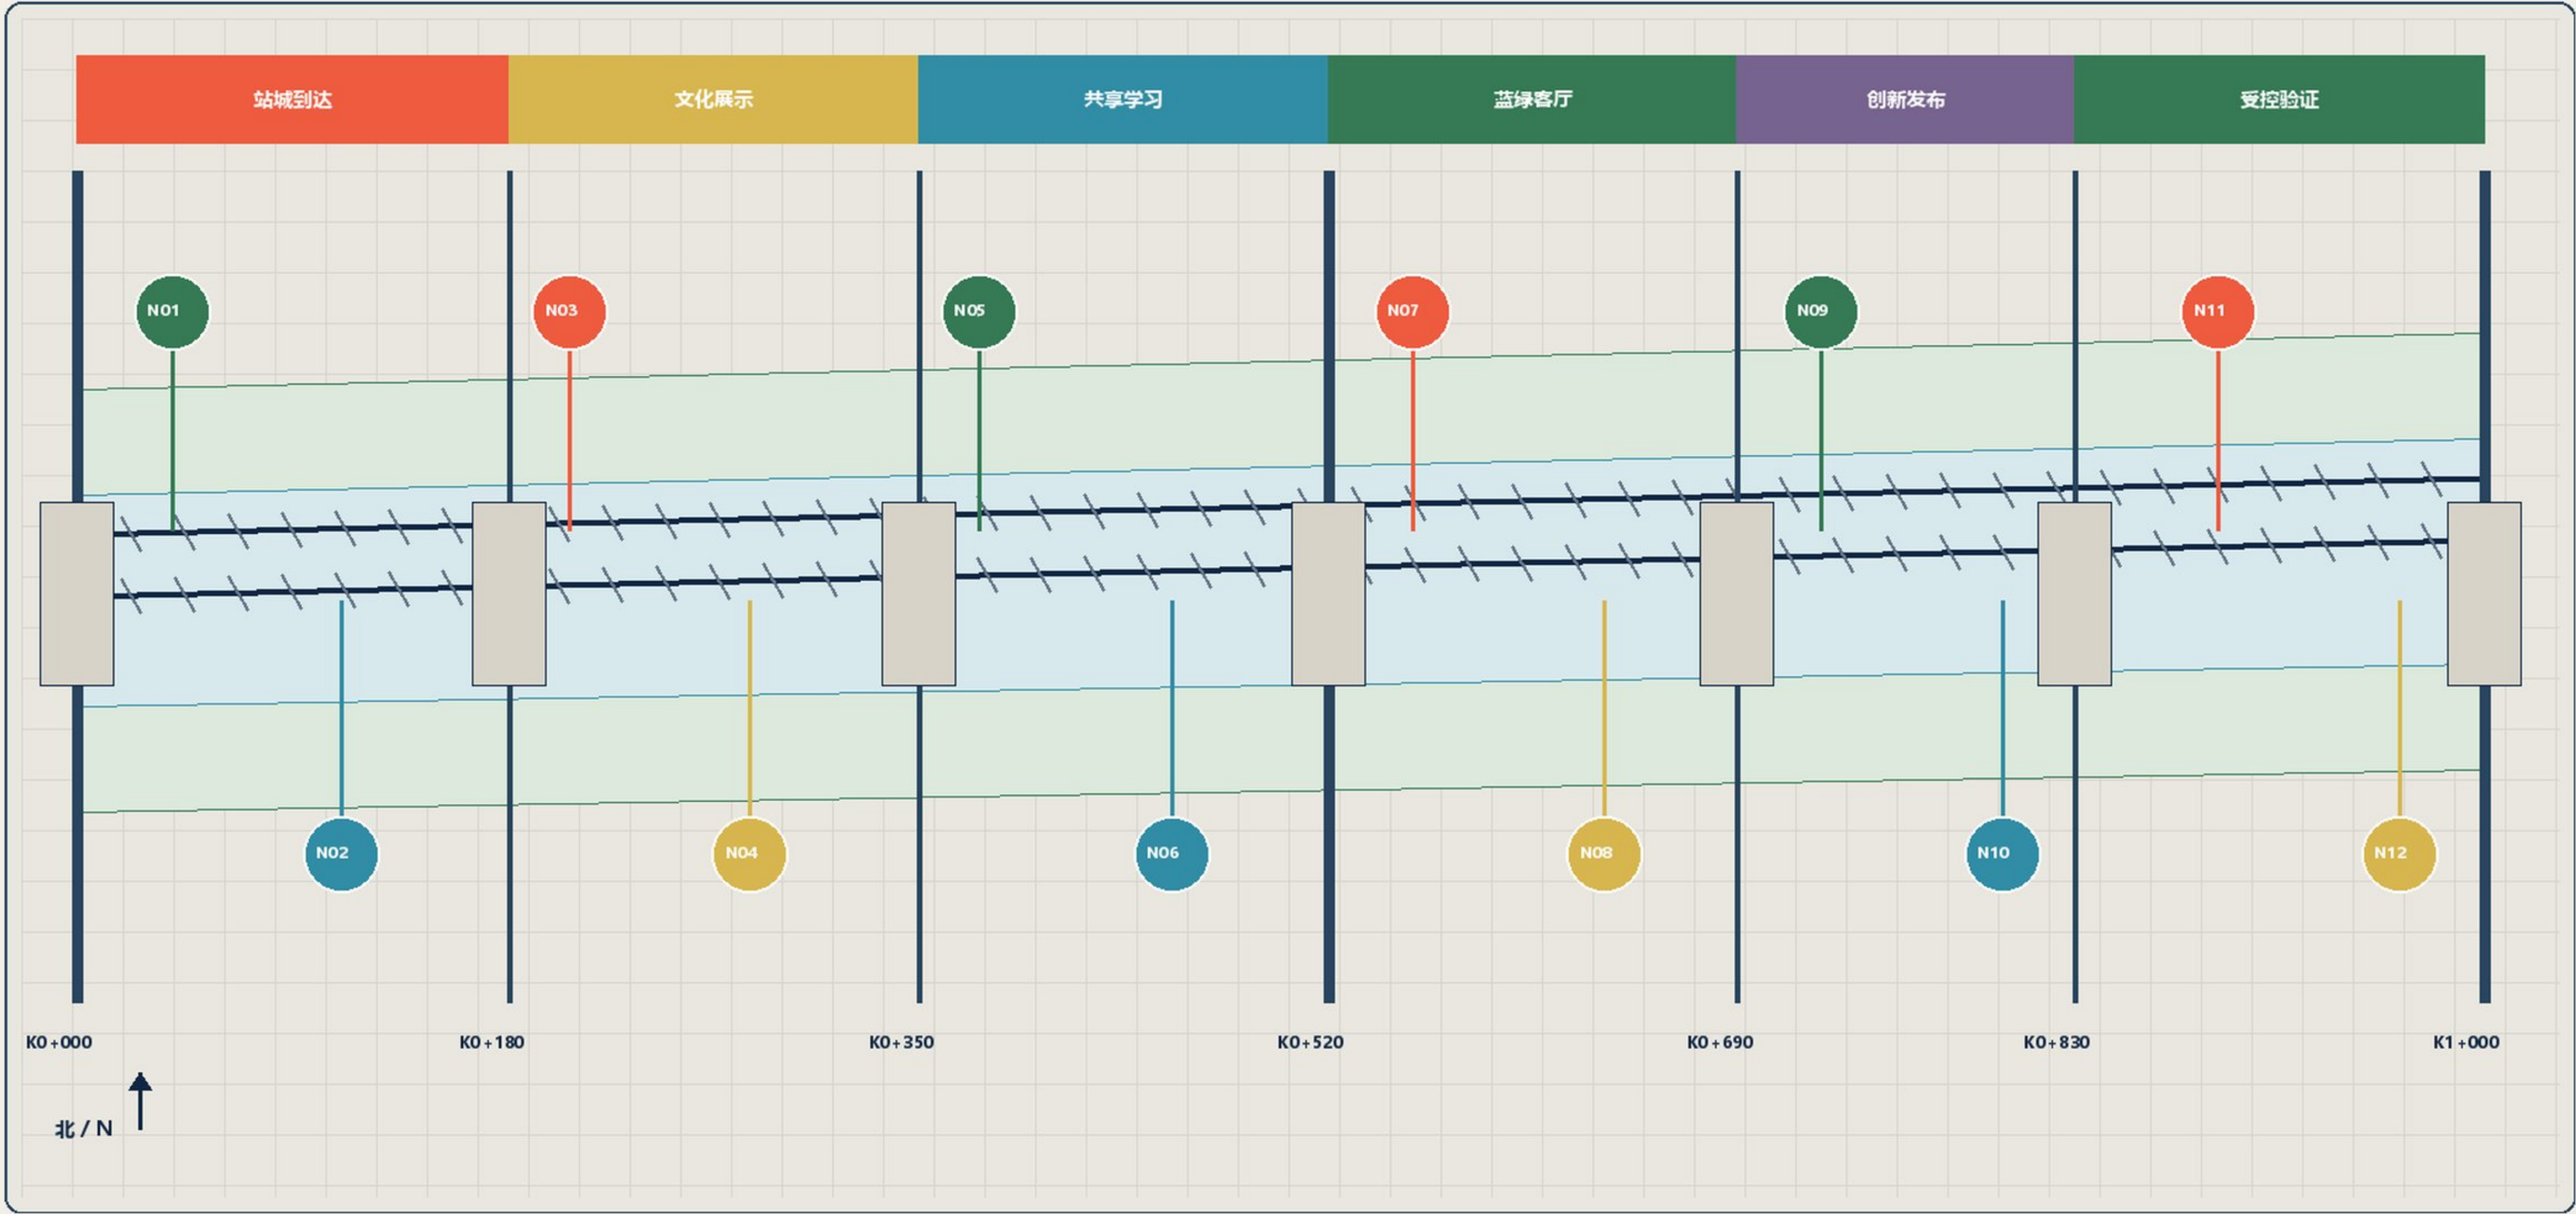




节点索引

编号	主功能	规模
N01	到达咨询	250-400
N02	全龄休憩	250-400
N03	文化导览	250-400
N04	雨水课堂	250-400
N05	共享学习	250-400
N06	维修服务	250-400
N07	公众议题	250-400
N08	饮水充电	250-400
N09	创新发布	250-400
N10	家庭支持	250-400
N11	测试观察	250-400
N12	运维实训	250-400

十二米原型断面与四处构造详图

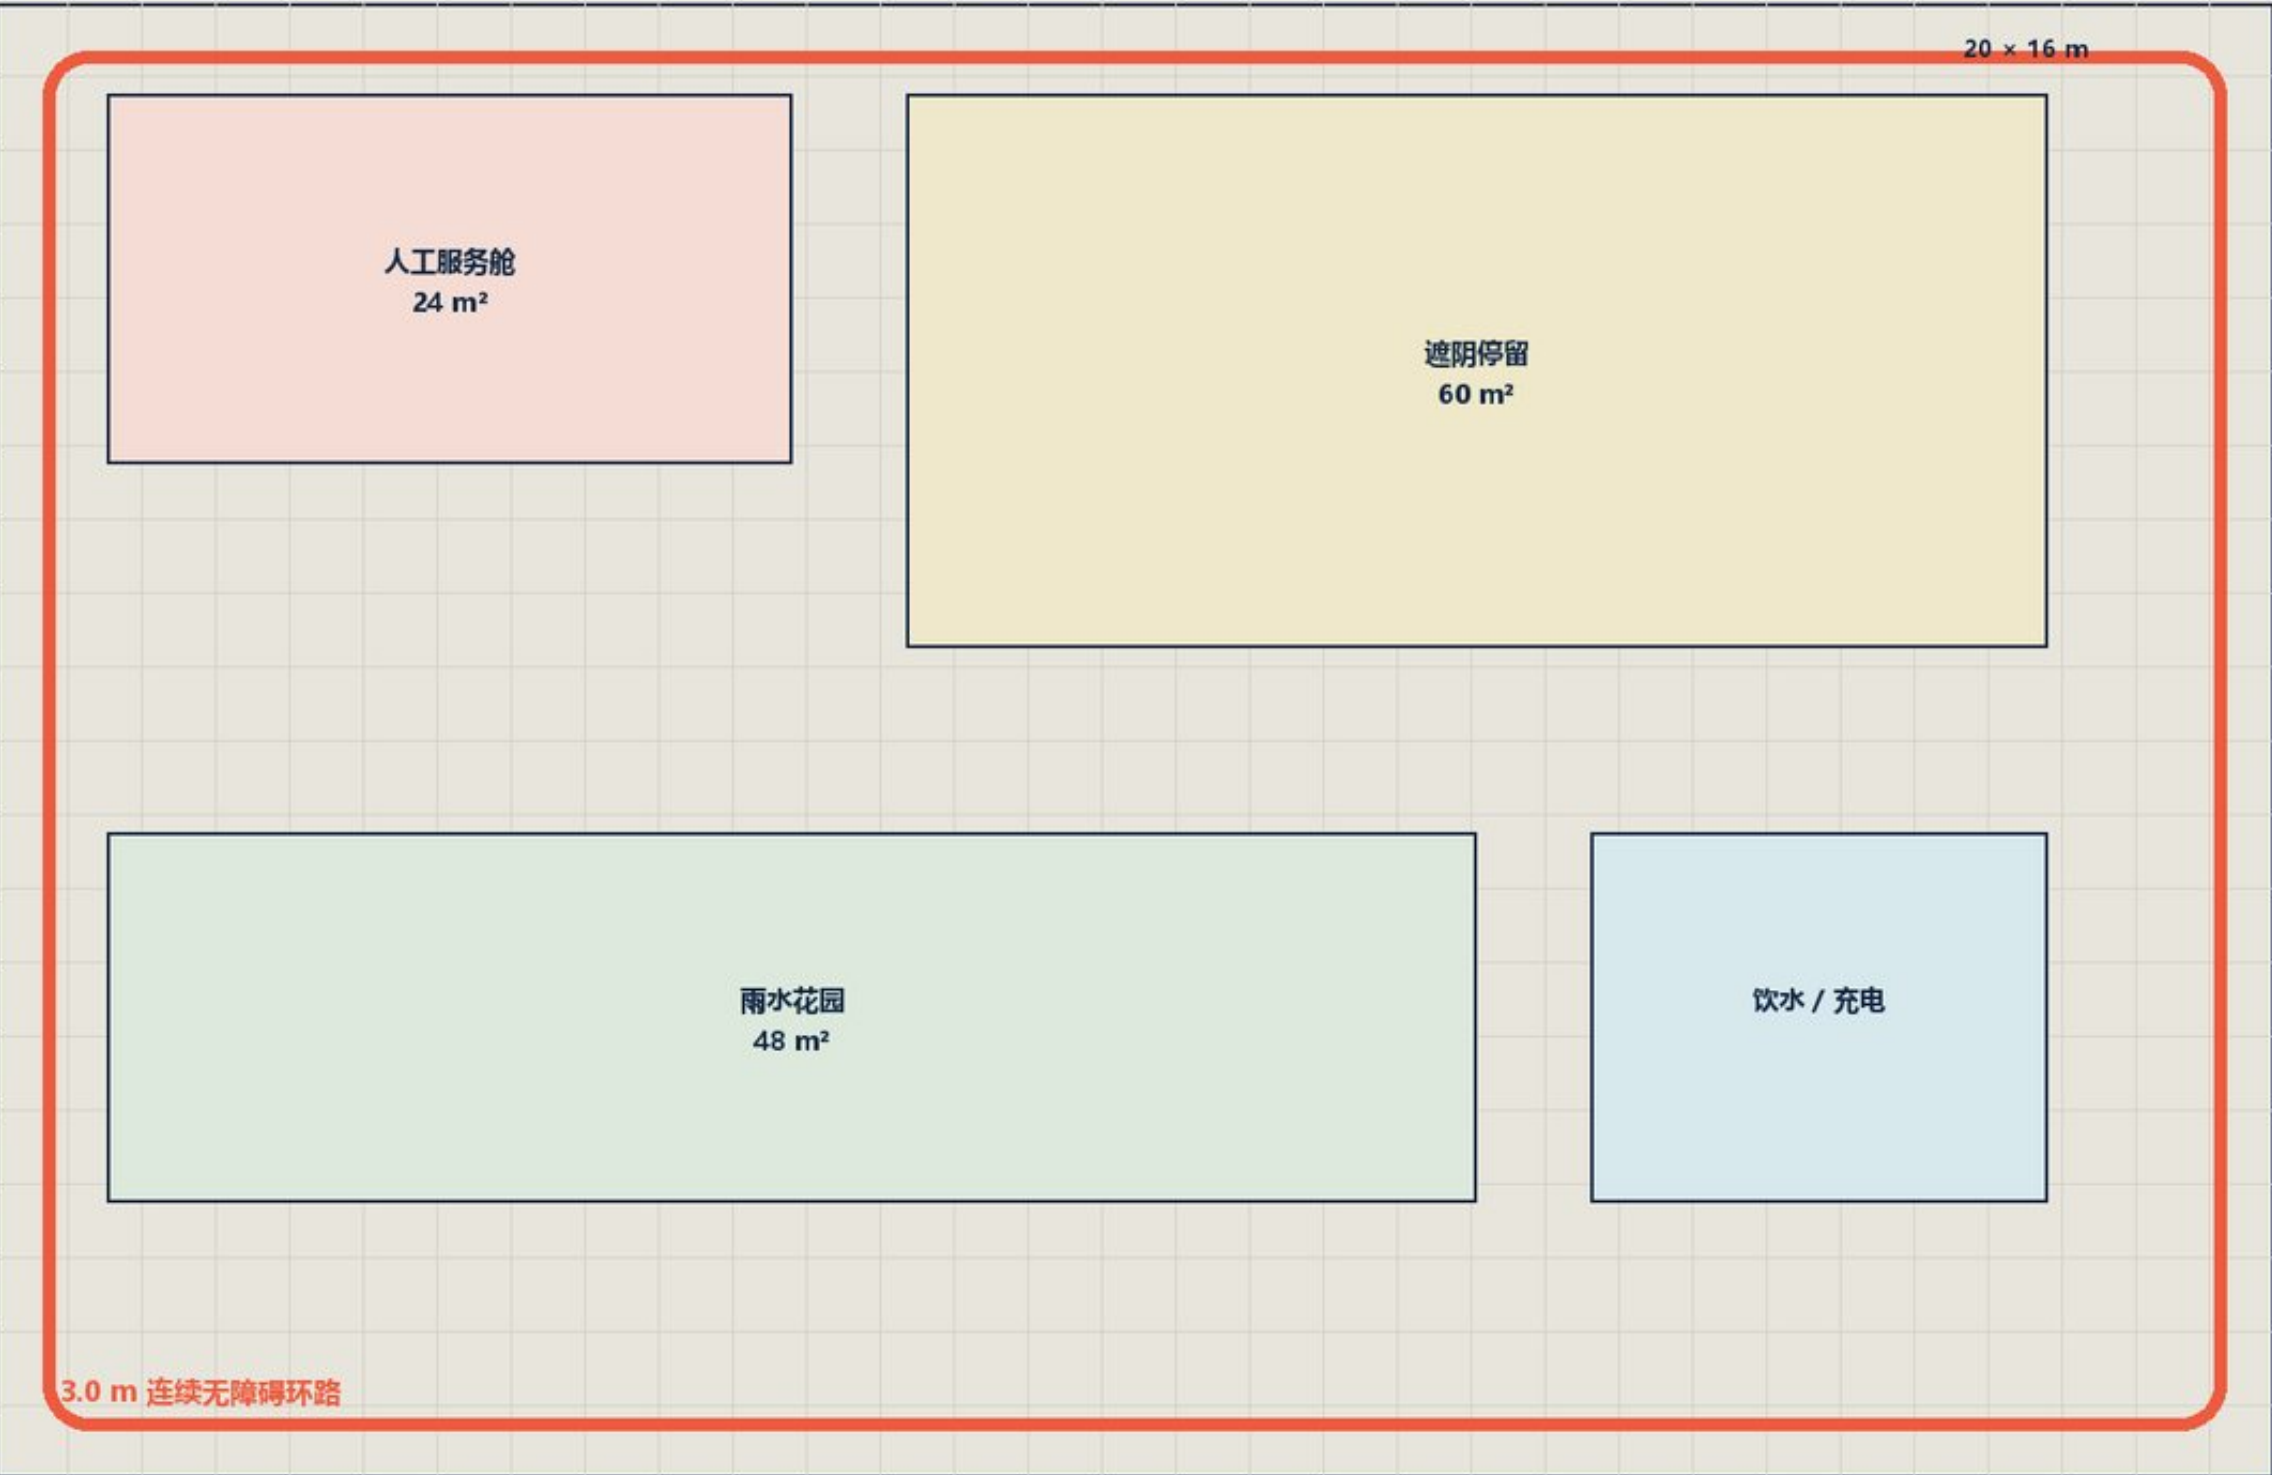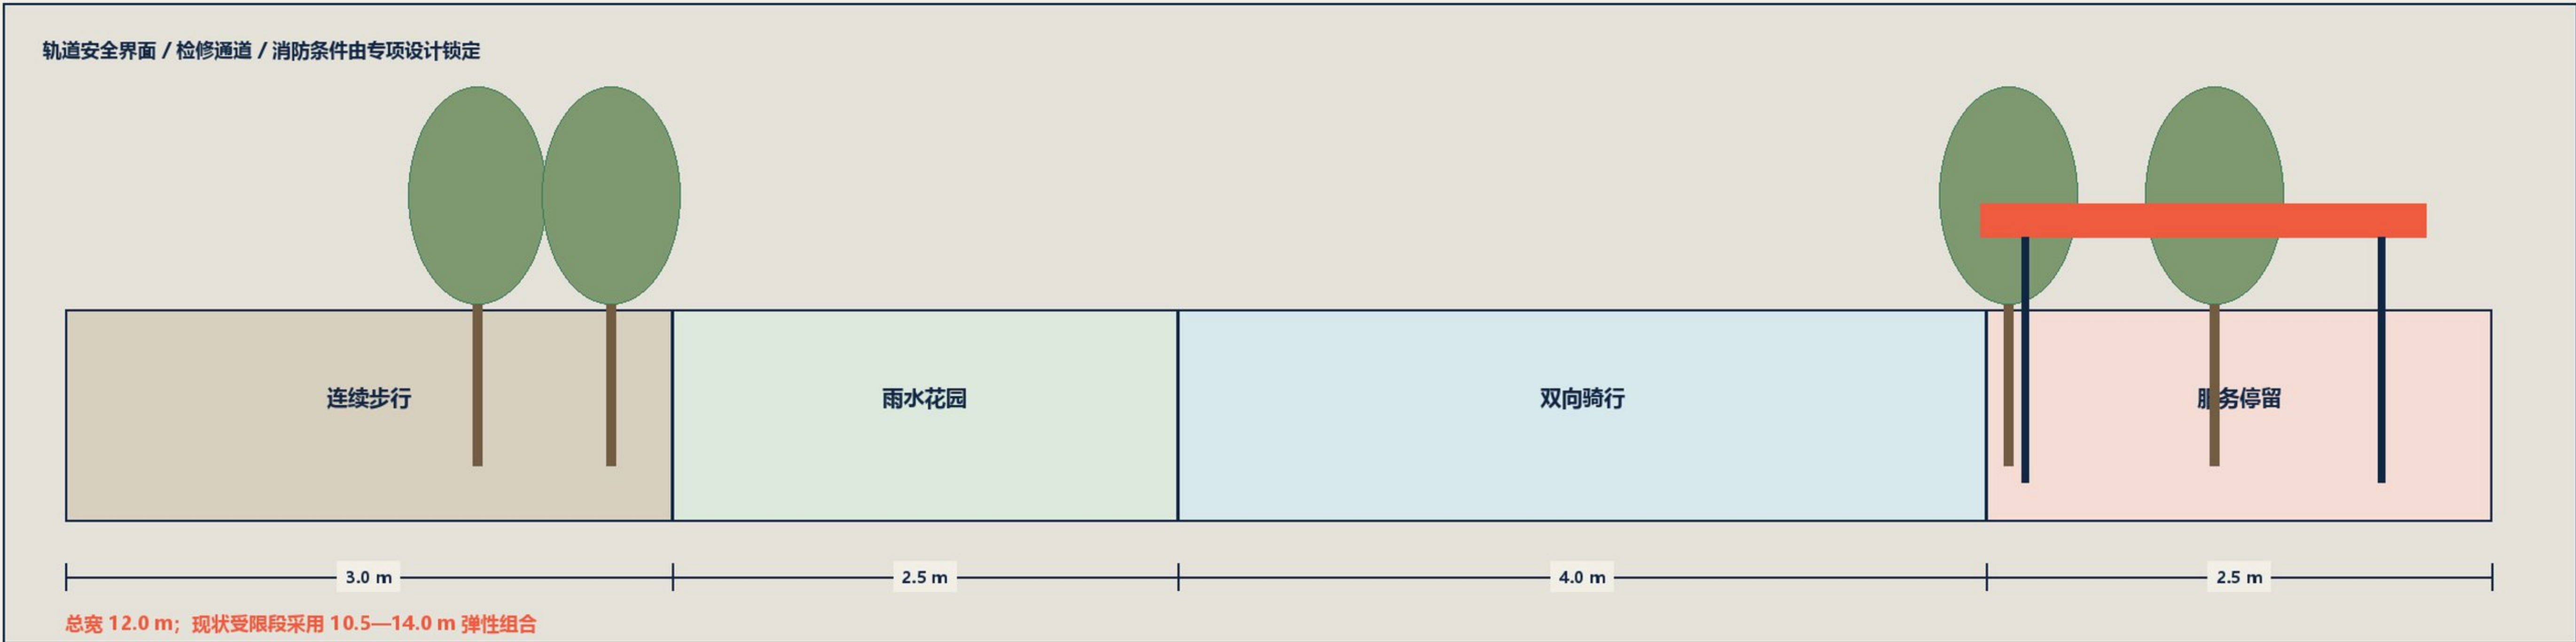

构造材料与维护索引

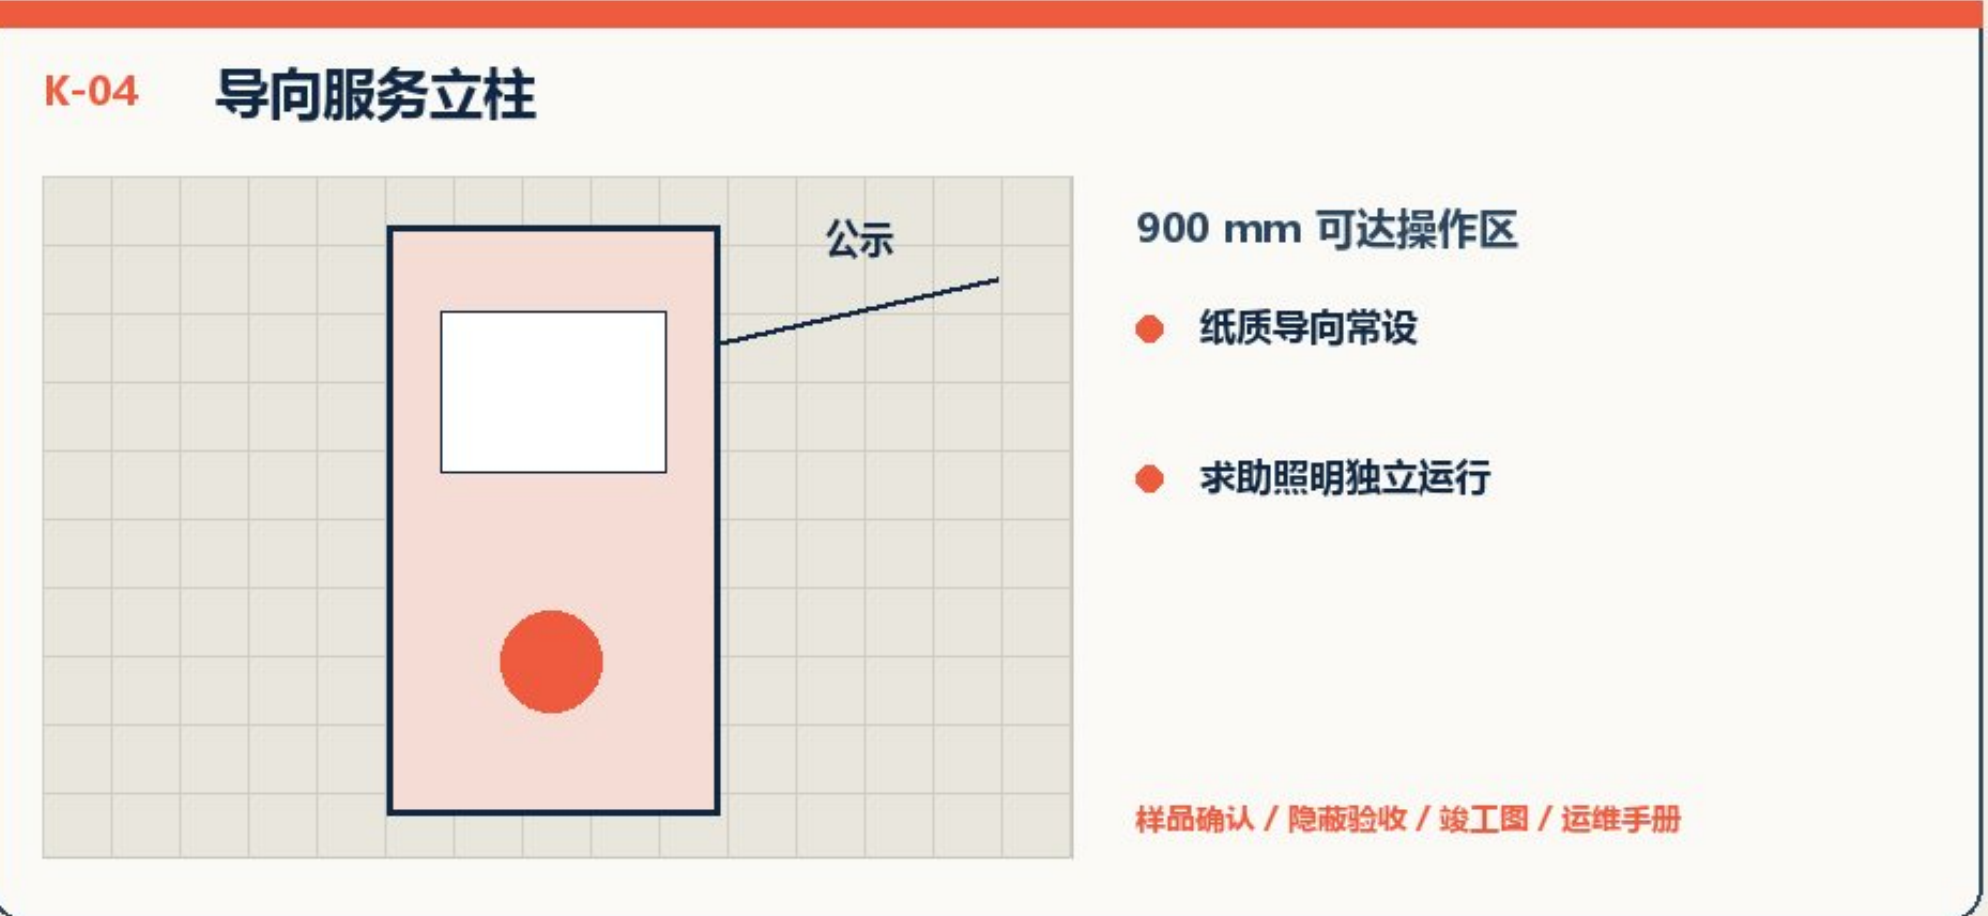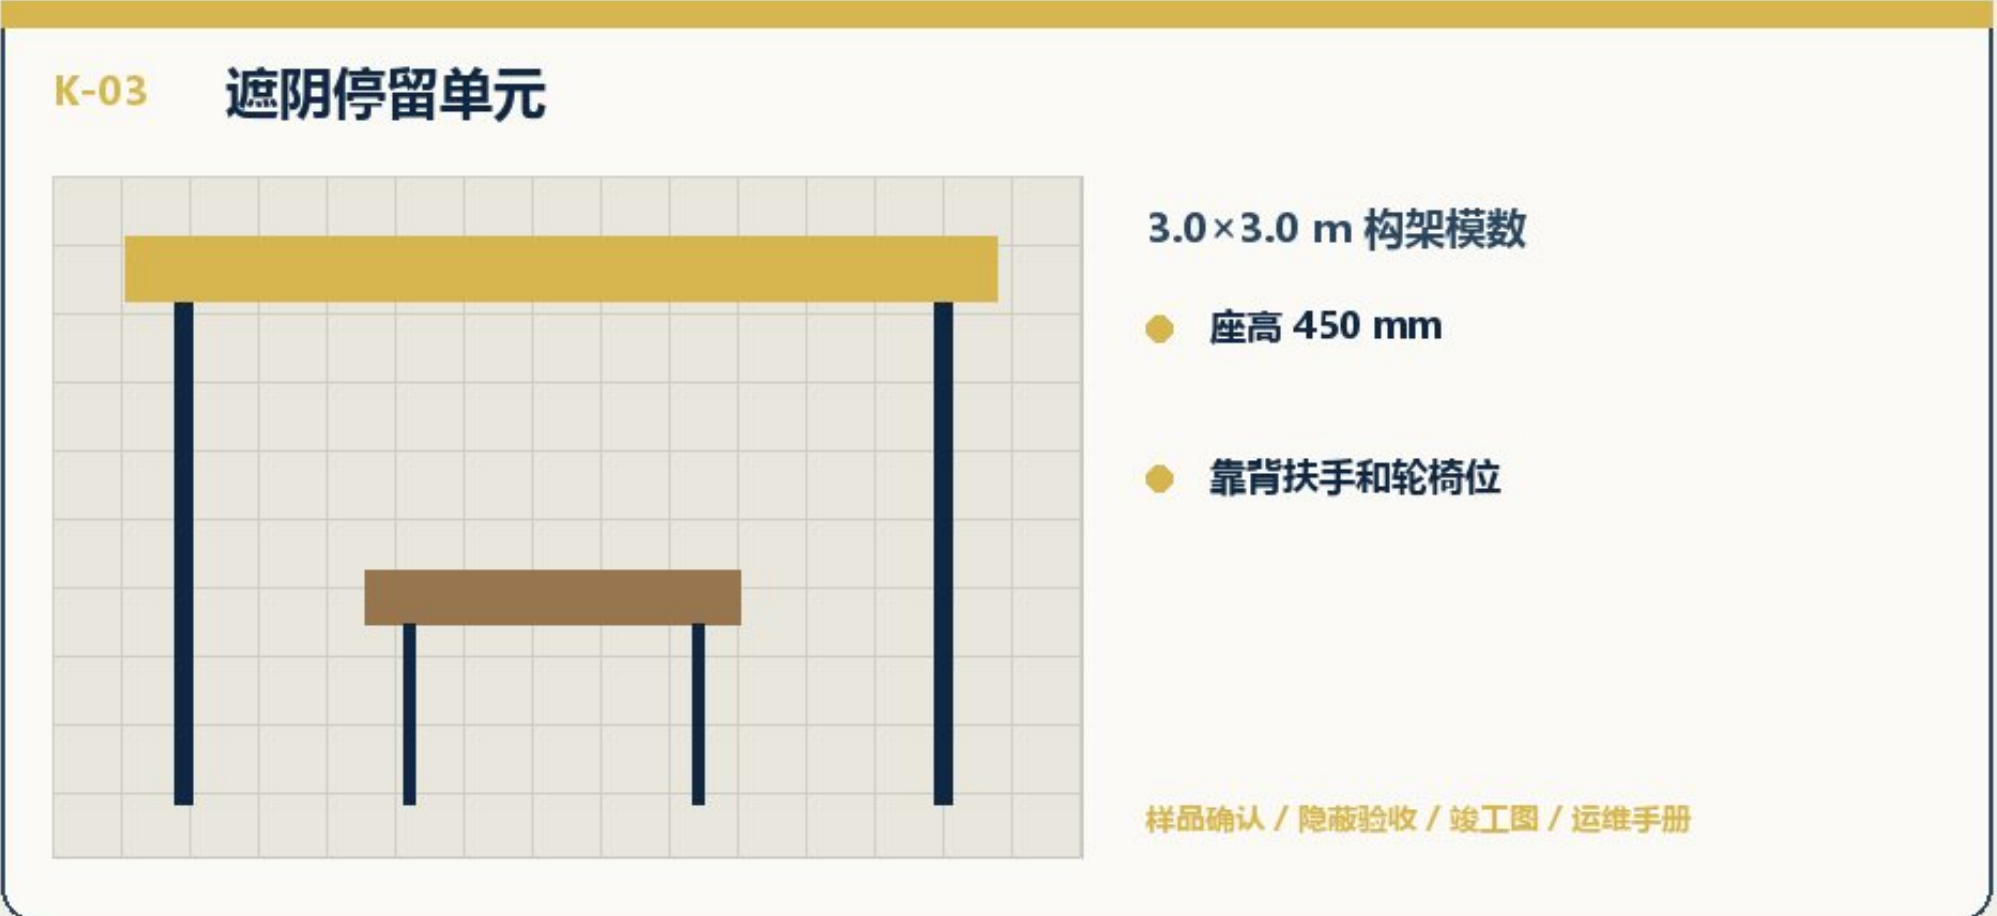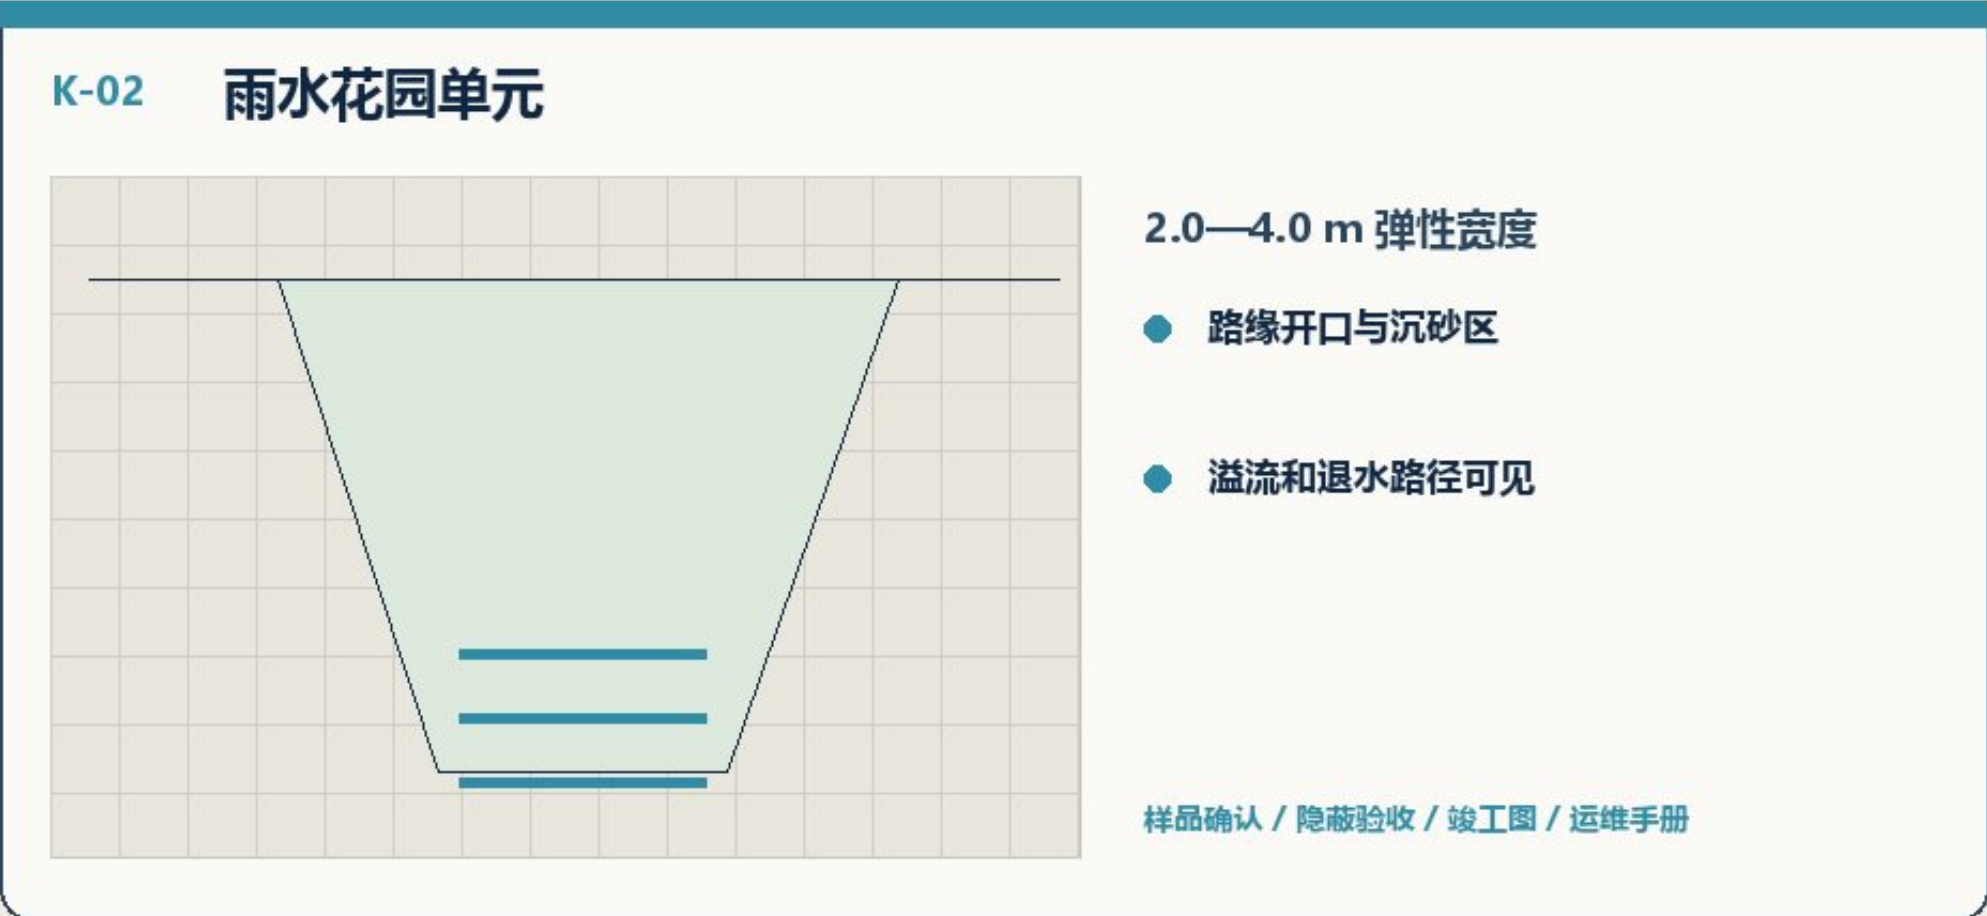

项目交付、运营治理与绩效证据

项目包、采购界面、二十四个月时序、人工智能治理、九项指标和责任台账。

近期项目包与采购界面

编号	项目	规模 / 交付	建议主体	前置条件	投资 / 工期	采购包
P-01	创新发展轴示范段	1 km / 3 节点	区级统筹 + 街道 + 产权	红线 / 轨道 / 市政 / 水评	M / 6—18 月	W-01
P-02	大钟寺站城融合	西向联系 / 2 服务点	街道 + 站区运营 + 交通	客流 / 通勤 / 产权	L / 12—24 月	W-02
P-03	众智园创新站证场	1.5 ha / 测试与审议	园区 + 高校企业 + 评估	权属 / 准入 / 数据安全	L / 12—24 月	W-03
P-04	AI 原点共享楼层	约 3000 m²	产权 + 街道 + 社区高校	结构 / 消防 / 运营协议	M / 9—18 月	W-04
P-05	三处服务节点样板	250—400 m²/处	街道 + 社区 + 运维	管线 / 接入 / 维护责任	M / 6—12 月	W-05
P-06	AI 公共服务治理	台帐 / 公示 / 接管 / 评价	区级统筹 + 运营 + 评估	数据分类 / 预案 / 投诉	S / 3—9 月	W-06

采购包拆分

