

京张共长线

GROW WITH JINGZHANG

从总体结构进入建设任务：

一公里示范段 · 三处重点片区 · 十二处公共服务节点

构造、成本、责任和证据同步落图。

总图 断面 构造 项目 运营

实施索引

01 空间骨架

05 示范段总平

07 构造详图


12 项目交付

15 运营证据



总体空间结构：一轴三片、多点支撑

把总体框架落实到首期示范段、重点片区行动和公共服务节点。

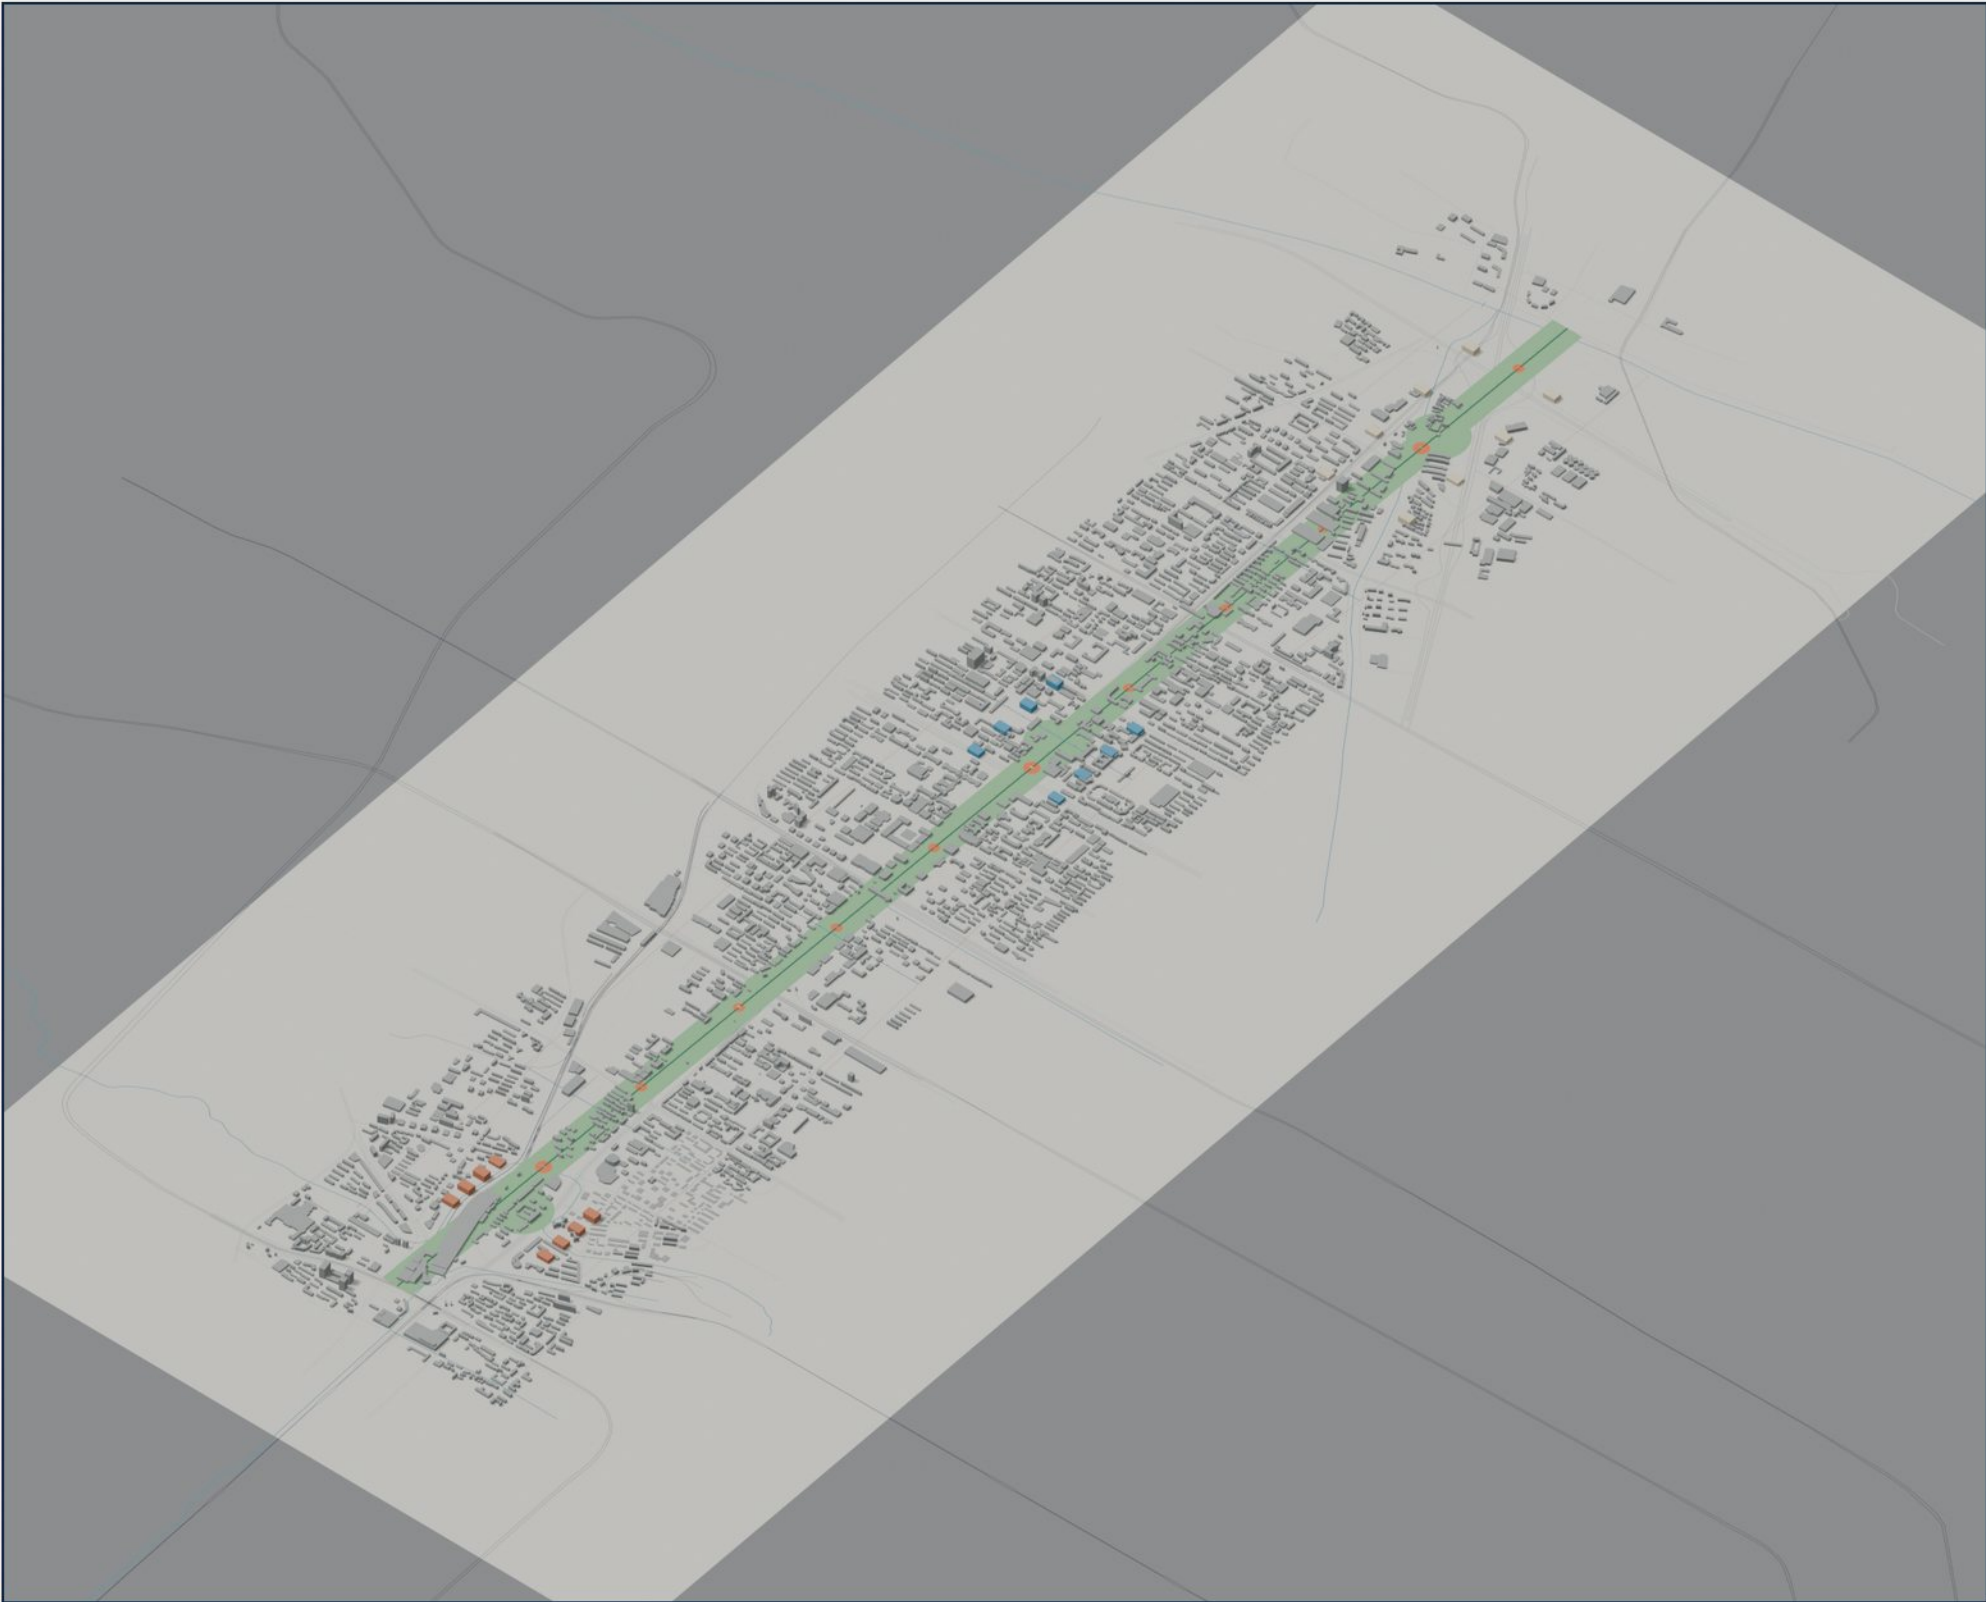

约 11.4 km²

京张创新发展轴

依托铁路遗产廊道组织连续慢行、蓝绿设施、创新展示与人工服务。

1.0 km

首期示范段

选择约 1.0 km 连续空间，优先实施 3 处样板节点和可逆公共空间改造。

3 处

三处重点片区

众智园创新验证、AI 原点社区协同创新、大钟寺站城融合形成差异化分工。

12 处

公共服务网络


十二处节点承担休憩、学习、展示、维修、饮水、充电和人工咨询。

实施顺序

资料与权属归集 → 可行性与公众协商 → 专项审查 → 建设验收 → 年度绩效评价。

用地组织：六类功能与更新接口

通过功能复合、首层盘活和蓝绿设施形成可分期实施的空间单元。

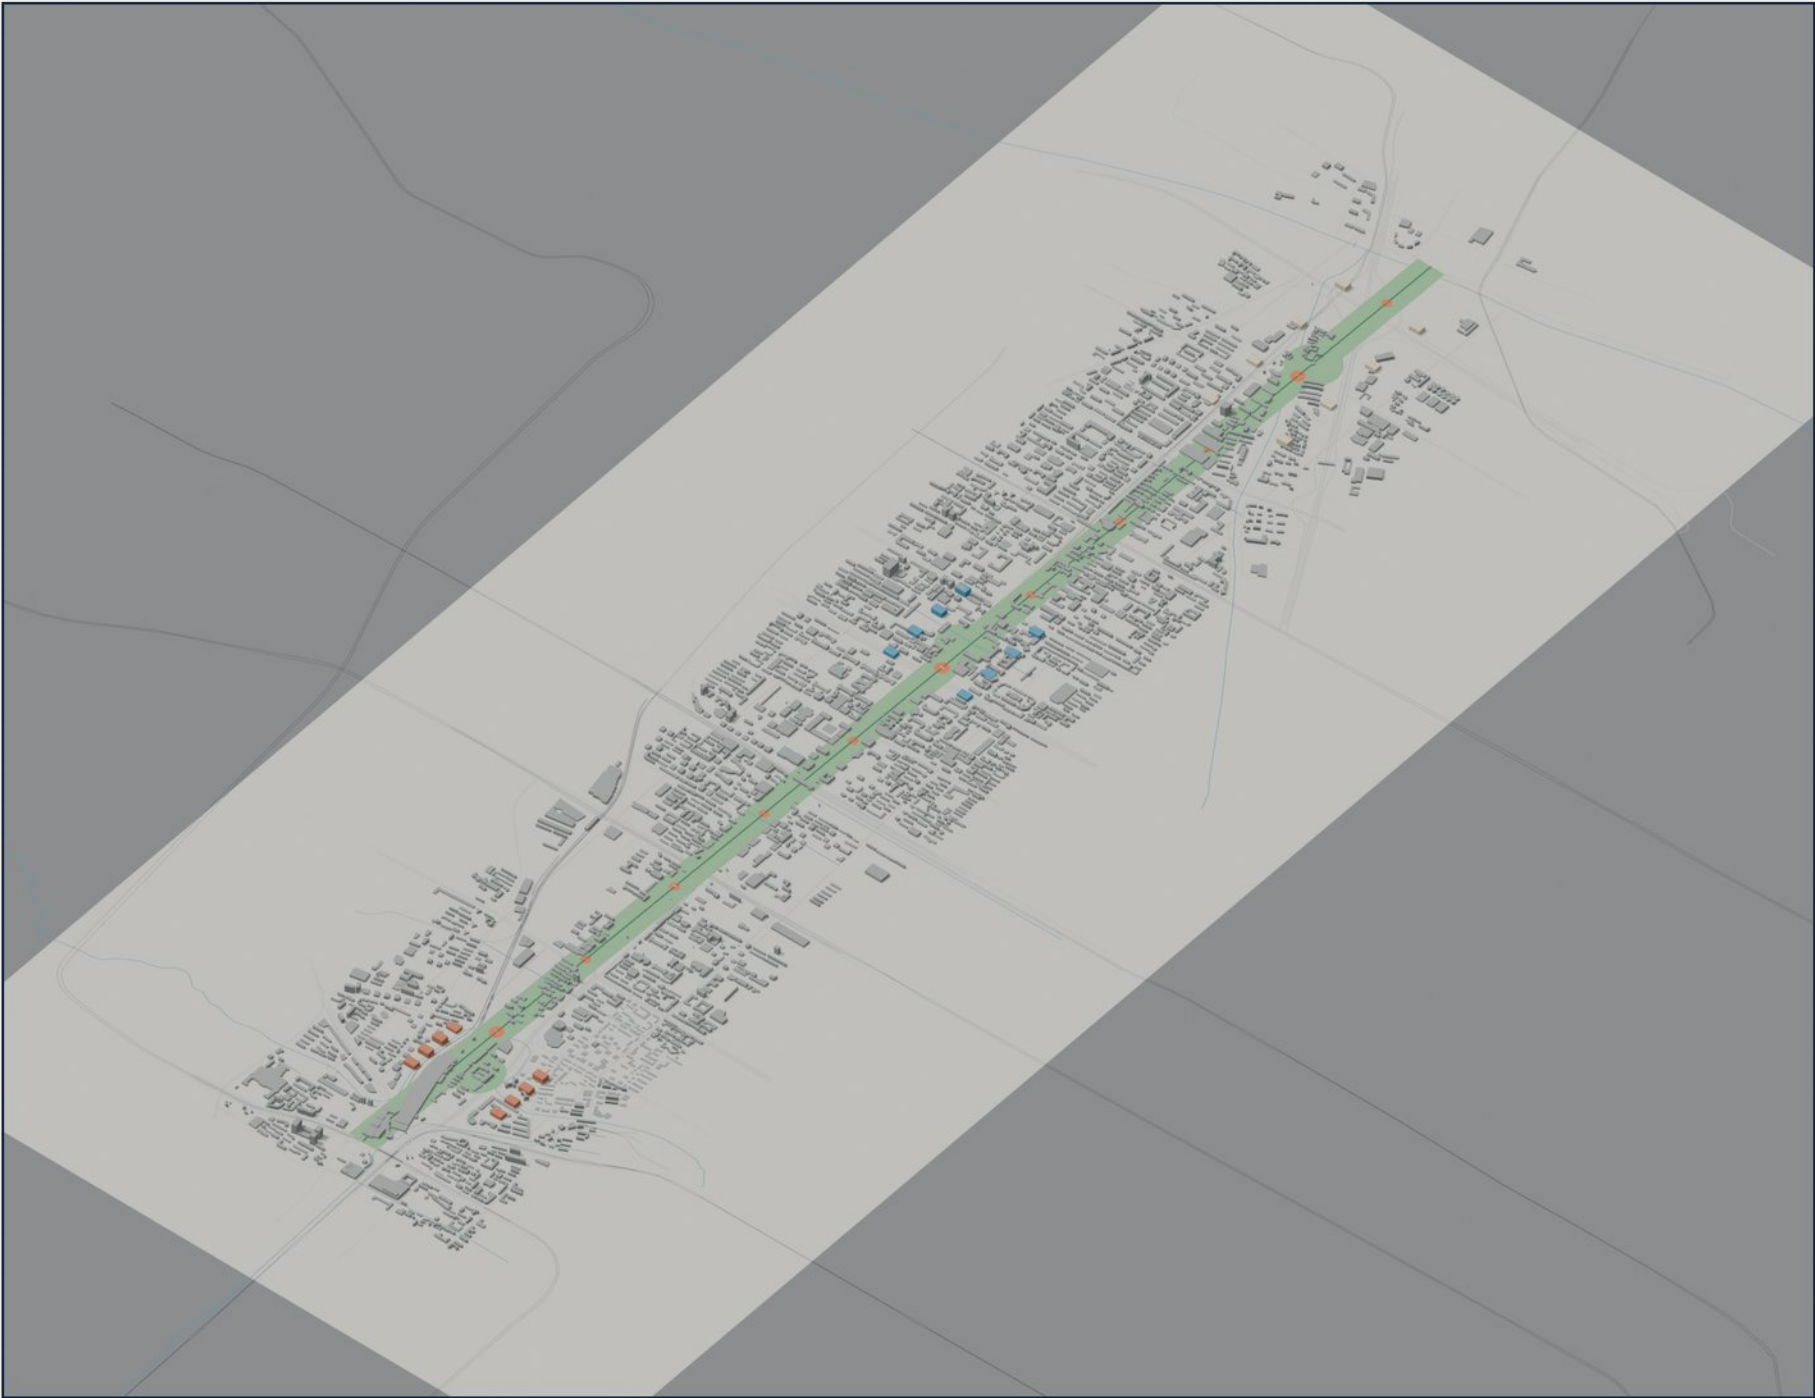

六类复合功能

创新验证 受控测试、责任评估、设施运维

协同创新 产学研协作、开源发布、人才服务

代际服务 无障碍、照护、人工服务渠道

文化公共 铁路遗产展示、公众议题交流

智慧生活 社区服务、学习与生活配套

蓝绿韧性 遮阳、雨水调蓄、生态教育

更新实施接口

共享首层先完成权属、结构、消防和运营协议；开发强度依据控规和专项论证确定。

三处重点片区：功能分工与近期抓手

每处片区设置可在 6-24 个月内启动的项目入口。



01 众智园创新验证片区

受控测试 + 责任评估

1.5 ha 验证场
全龄测试环 / 运维实训 / 公众审议

近期交付

1.5 ha 验证场；全龄测试环 / 运维实训 / 公众审议

L / 12-24 个月



02 AI 原点社区协同创新片区

共享首层 + 人才服务

首期盘活约 3000 m²
学习 / 发布 / 家庭支持 / 开源交流

近期交付

首期盘活约 3000 m²；学习 / 发布 / 家庭支持 / 开源交流

M / 9-18 个月



03 大钟寺站城融合片区

四向联系 + 人工服务

站区步行联系 / 2 处服务点
多语言导向 / 全龄停留


近期交付

站区步行联系 / 2 处服务点；多语言导向 / 全龄停留

L / 12-24 个月

一公里示范段：里程化总平与节点索引

以百米刻度组织慢行、蓝绿设施、服务节点、跨街联系和实施界面。

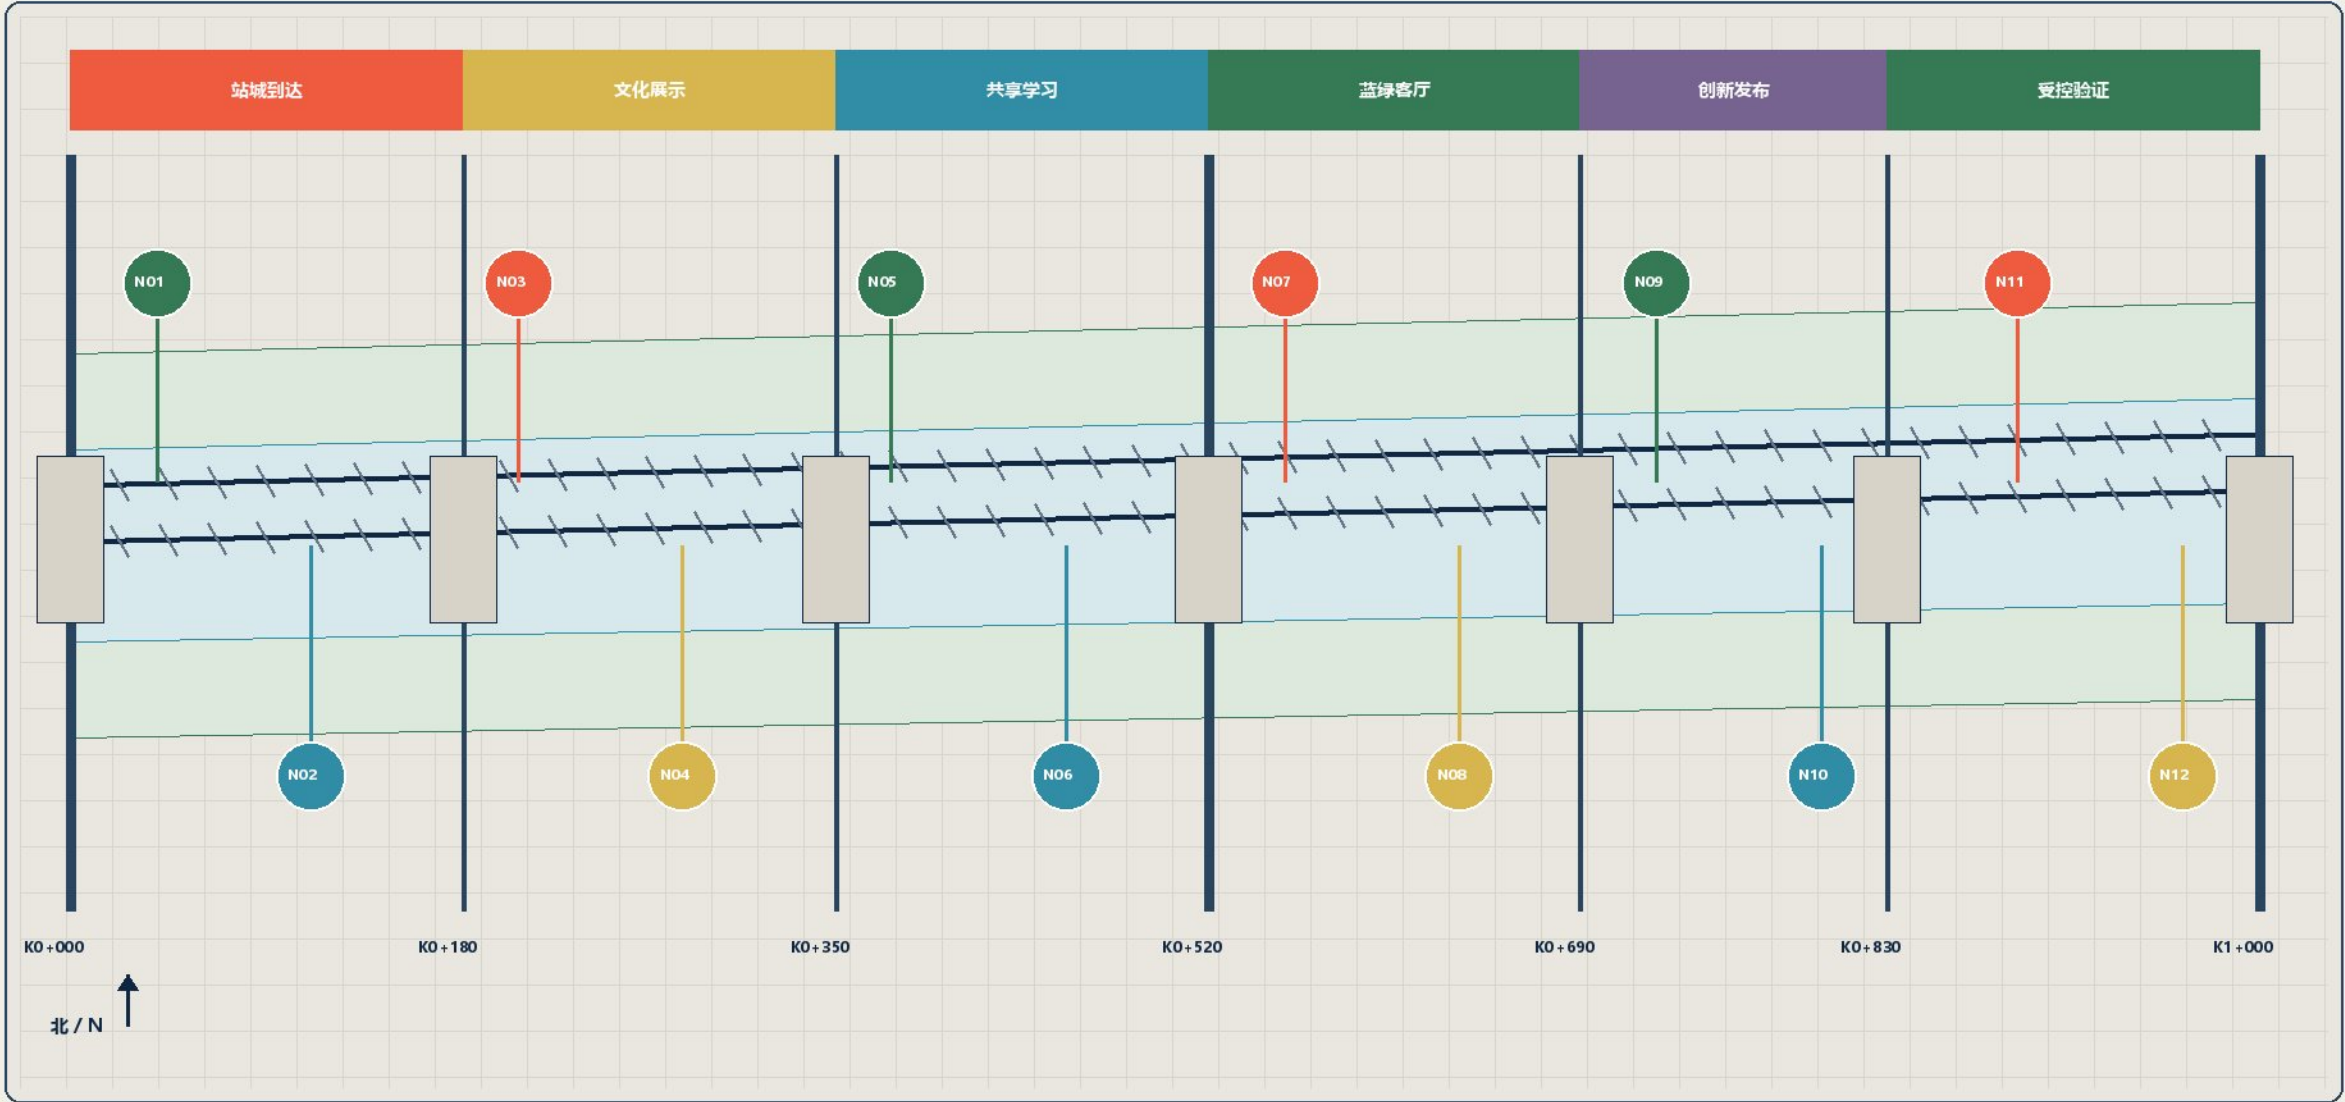

节点索引		
编号	主功能	规模
N01	到达咨询	250-400
N02	全龄休憩	250-400
N03	文化导览	250-400
N04	雨水课堂	250-400
N05	共享学习	250-400
N06	维修服务	250-400
N07	公众议题	250-400
N08	饮水充电	250-400
N09	创新发布	250-400
N10	家庭支持	250-400
N11	测试观察	250-400
N12	运维实训	250-400

P-01

首期工程量

连续改造 1.0 km
服务节点 3 处
雨水花园约 1,800 m²
新增遮阴约 2,400 m²
导向与求助设施 18 组

6 类

关键界面

轨道保护 / 消防通道 / 道路红线
既有树木 / 地下管线 / 商户出入口
过街冲突 / 夜间照明 / 冬季退水
各界面以专项审查图签闭环。

C-01—06

交付图纸索引

C-01 总平与放线坐标
C-02 12 m 原型断面
C-03 节点模块与设备表
C-04 铺装、雨水、遮阳构造
C-05 管线综合与检修界面
C-06 运营移交及责任清单

重点片区行动矩阵：空间、项目、主体与证据





三处片区均形成可立项的空间单元、责任组合、前置条件和移交证据。

	P-03 众智园创新验证片区 1.5 ha 受控验证场 空间交付 测试环 / 观察庭 / 运维实训 / 公众审议 移交证据 总平 / 准入清单 / 演练记录 / 年度复审	建议主体 园区运营主体 + 高校企业 + 独立评估 运营测量 预约批次 / 安全事件 / 公众审议	前置条件 权属、准入、数据安全、应急预案 评价节律 月度台账 + 季度复审
	P-04 北京 AI 原点社区协同创新片区 约 3000 m² 共享首层 空间交付 学习工作室 / 发布厅 / 家庭支持 / 人才服务 移交证据 竣工图 / 时段表 / 服务台账 / 意见闭环	建议主体 产权单位 + 街道 + 社区高校 + 运营方 运营测量 开放时长 / 服务人次 / 活动完成	前置条件 结构、消防、权属、分时运营协议 评价节律 月度报告 + 半年评估
	P-02 大钟寺站城融合片区 四向联系 + 2 处服务点 空间交付 步行接驳 / 多语言导向 / 全龄停留 / 人工咨询 移交证据 流线图 / 疏散图 / 导向清单 / 服务记录	建议主体 街道 + 站区运营 + 交通城管 + 商业主体 运营测量 客流 / 问询 / 无障碍协助	前置条件 客流、疏散、产权、交通衔接 评价节律 周报汇总 + 季度评价



十二米原型断面：构造节点与维护界面

断面尺度与铺装、排水、遮阴、坐凳、照明和管线接口同步表达。

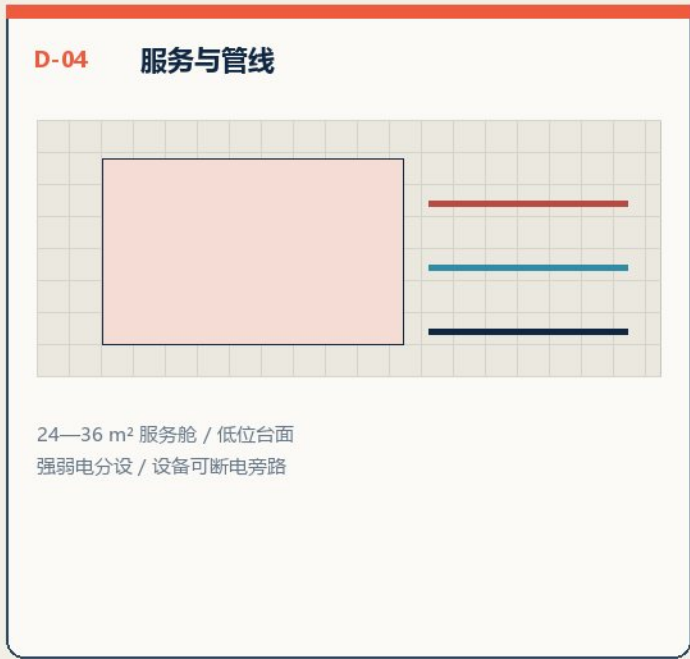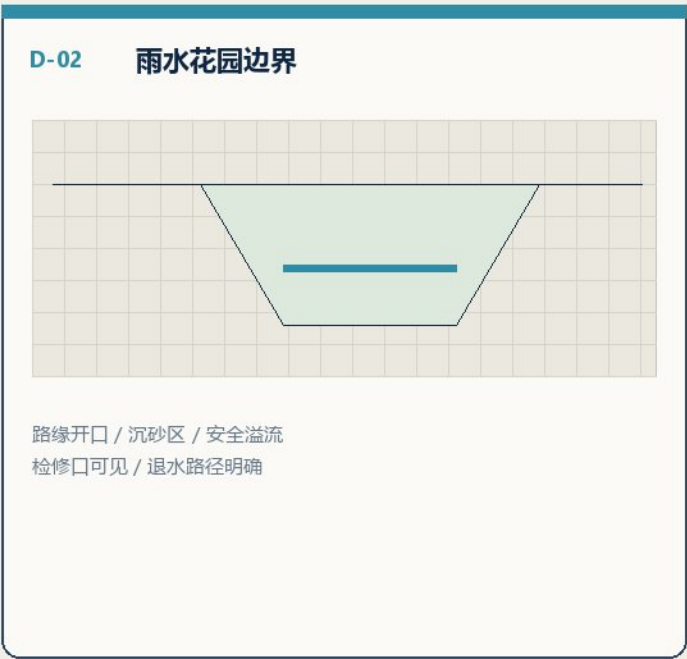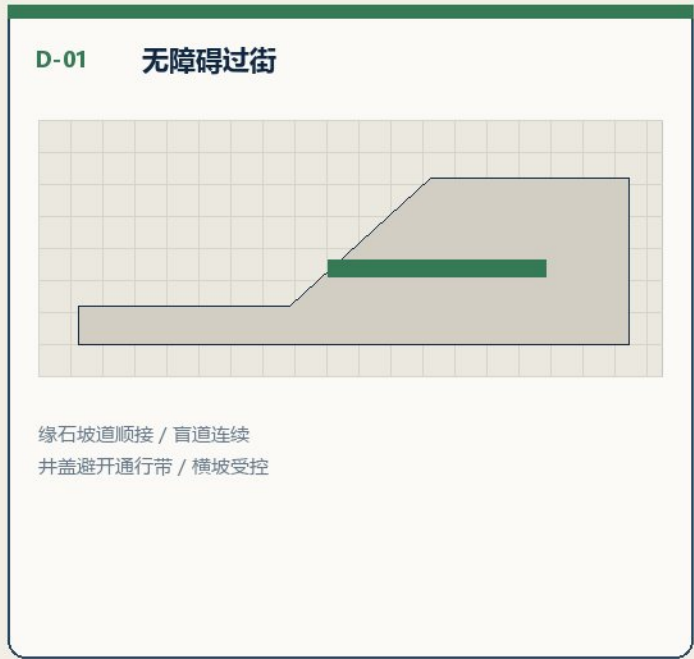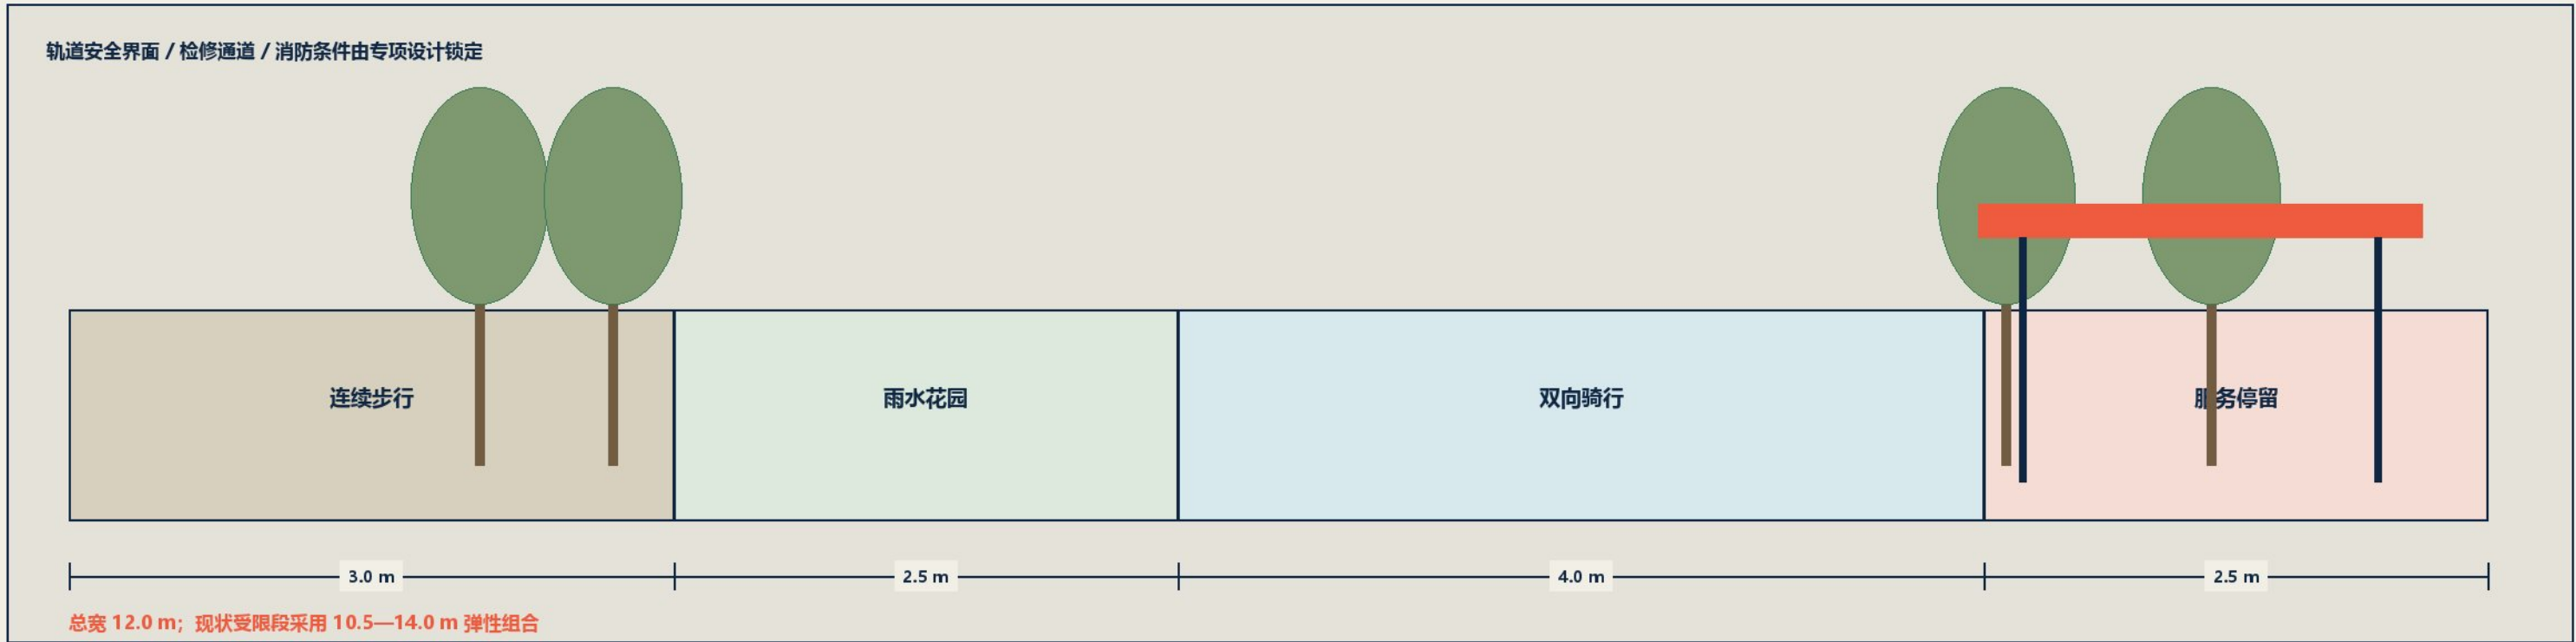


材料与维护索引

M01 透水铺装 防滑 / 低眩光 季度巡检	M02 耐候钢导向 圆角 / 可更换 半年紧固	M03 乡土植物 耐旱耐涝 雨后补植	M04 可拆装棚架 模块化连接 年度防腐	M05 低位服务台 高度双轨 月度检查
-------------------------------------	--------------------------------------	---------------------------------	-----------------------------------	----------------------------------

公共服务节点：平面、模块、设备与移交

以 20 m × 16 m 原型展示可拆装空间、全龄环路、蓝绿设施和服务设备。

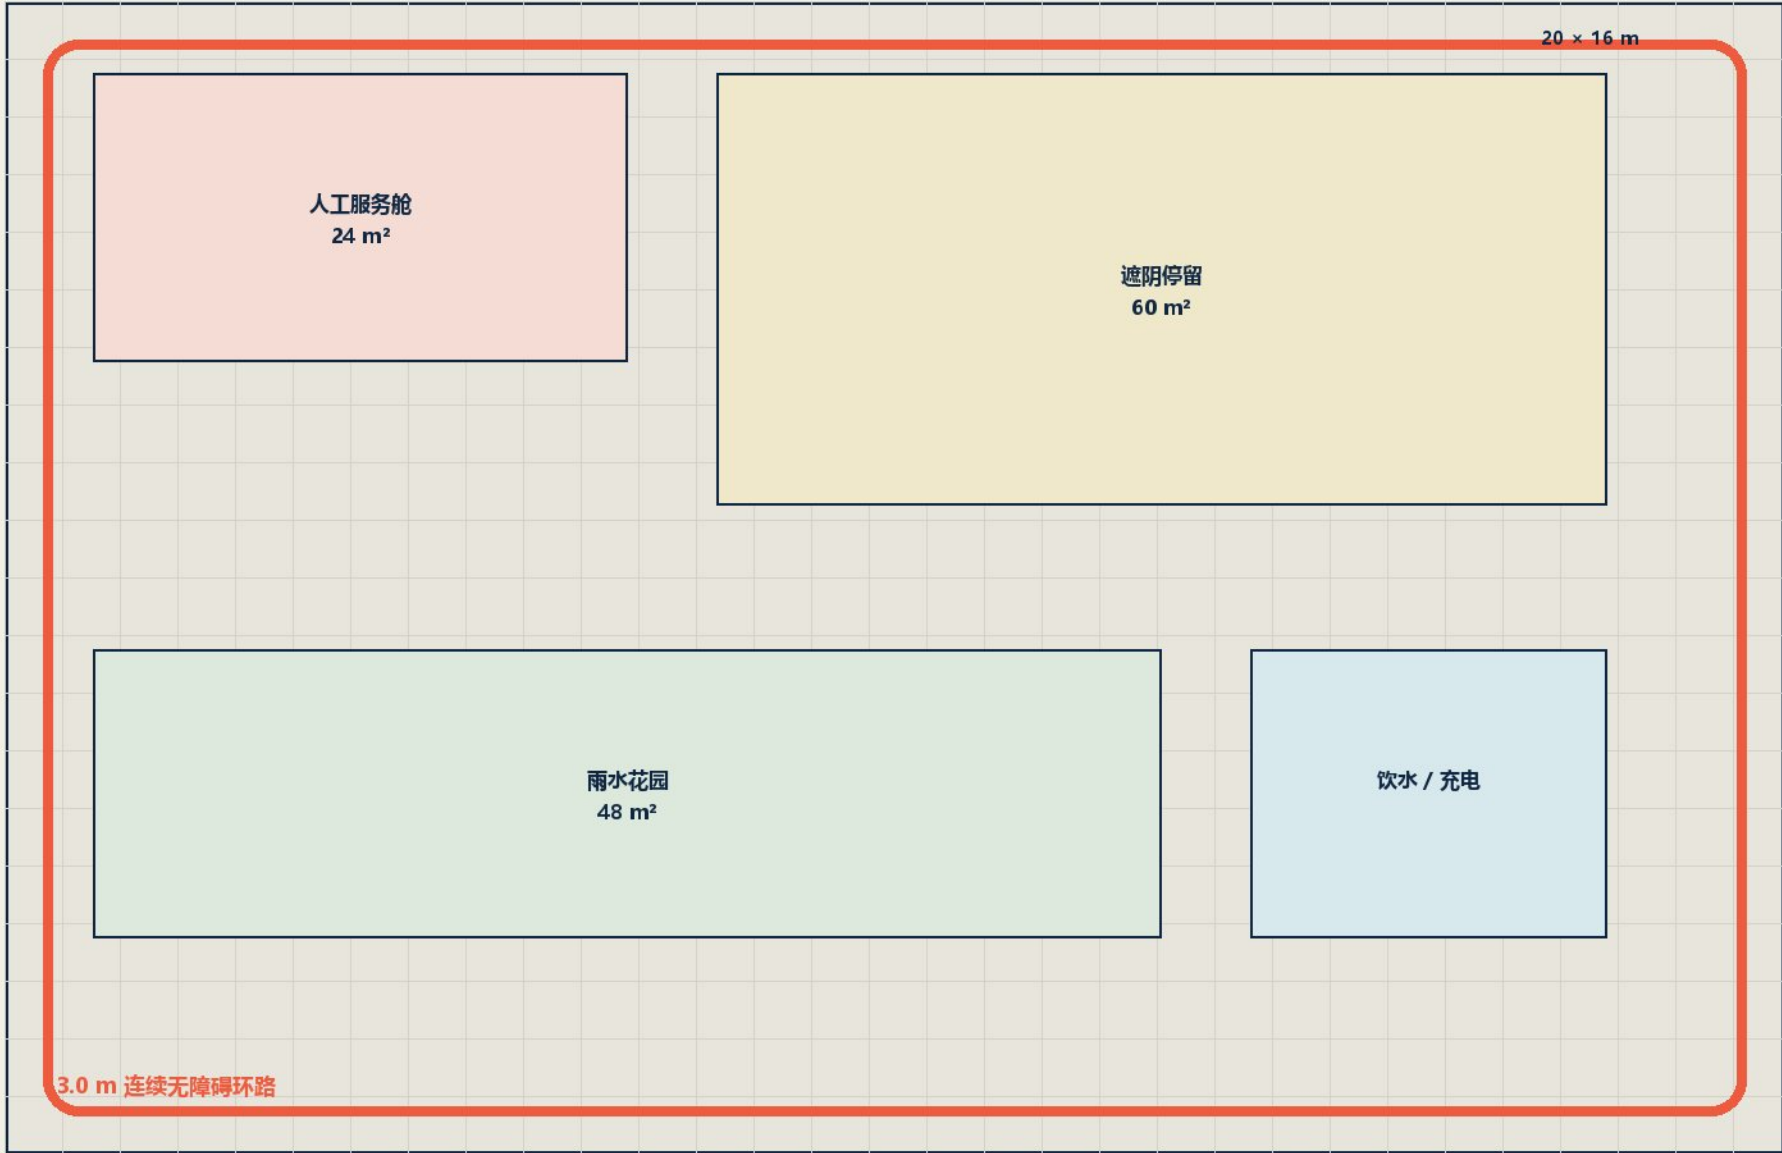

模块与设备表

M1	人工服务舱	双向开口 / 低位台面 / 储物急救
M2	遮阳停留	靠背扶手 / 轮椅与婴儿车位
M3	蓝绿设施	路缘开口 / 溢流 / 检修 / 补植
M4	基础服务	饮水 / 照明 / 充电 / 求助
M5	信息公示	用途 / 数据 / 责任 / 投诉 / 复审
E1	设备接口	强弱电 / 网络旁路 / 计量 / 断电

装配顺序与移交检查




构造与材料图谱：四类标准做法

将铺装、雨水、遮阳和信息设施拆解为可采购、可维护、可替换的构件。

K-01

连续通行铺装

600×300 mm 透水模块

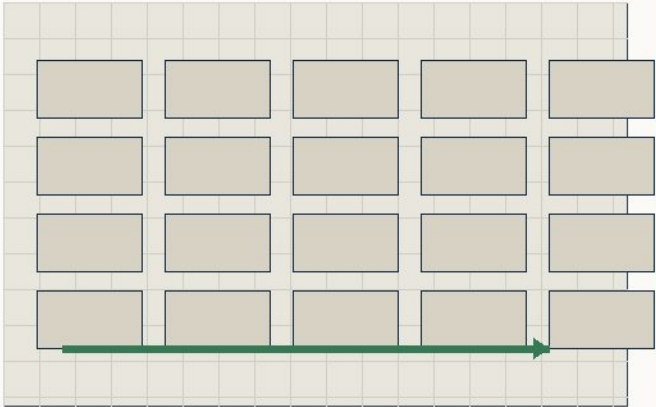

- 防滑等级按场所确定
- 缝宽统一并避开盲道
- 破损单元可独立更换


移交证据

样品确认 / 隐蔽验收 / 竣工图 / 运维手册

K-02

雨水花园单元

2.0—4.0 m 弹性宽度

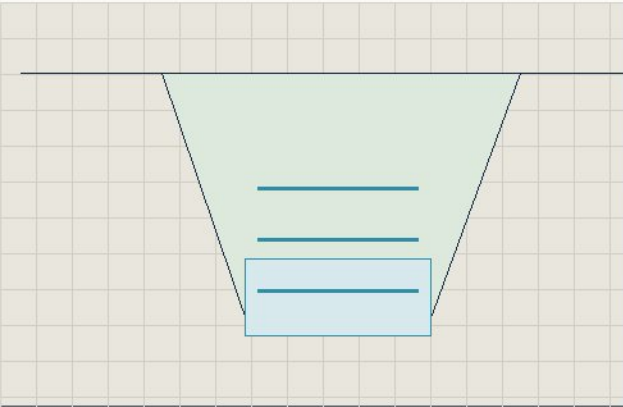

- 路缘开口与沉砂区
- 300 mm 表层调蓄
- 溢流与退水路径可见


移交证据

样品确认 / 隐蔽验收 / 竣工图 / 运维手册

K-03

遮阳停留单元

3.0×3.0 m 构架模数

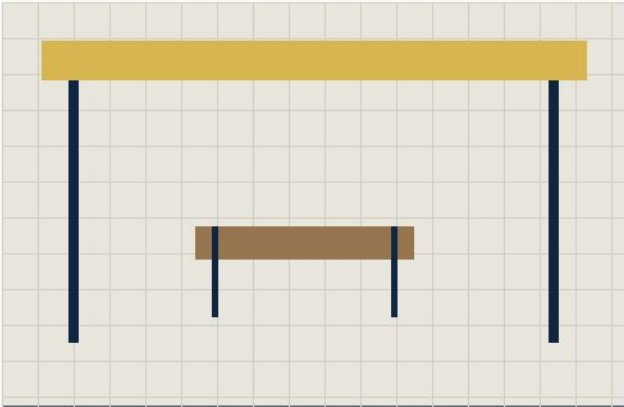

- 座高 450 mm
- 靠背扶手和轮椅位
- 构件可拆卸与复用


移交证据

样品确认 / 隐蔽验收 / 竣工图 / 运维手册

K-04

导向与服务立柱

900 mm 可达操作区

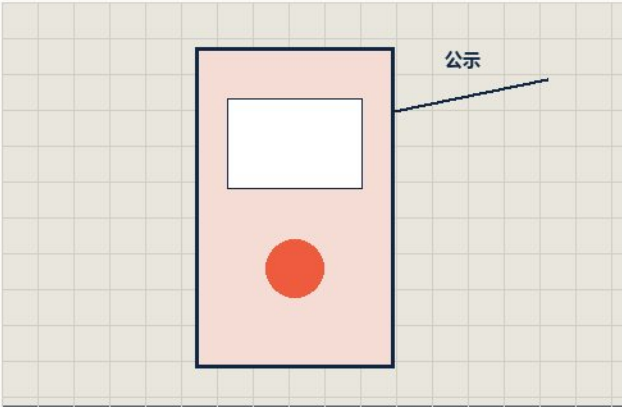

- 纸质导向常设
- 求助和照明独立运行
- 公示责任与报修方式

移交证据

样品确认 / 隐蔽验收 / 竣工图 / 运维手册

全生命周期维护矩阵

系统	日常巡检	季度维护	年度维护	责任主体	备件
K-01	破损、积水	缝隙清理	平整度抽检	道路运维	铺装 2%
K-02	堵塞、积水	沉砂清掏	植物补植	园林排水	苗木 5%
K-03	松动、锈蚀	紧固检查	防腐复涂	设施运维	连接件 3%
K-04	照明、求助	接口测试	电气检测	服务运营	模块 2 套

人工智能场景治理：准入、风险与退出


四项先导场景采用受控试运行、人工接管、信息公示和年度复审。



先导场景运行卡



风险矩阵

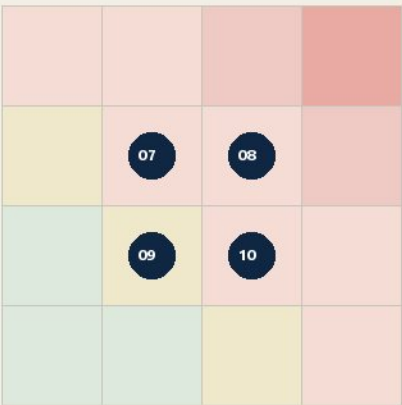

事件升级链



移动与蓝绿系统：气候压力转化为空间动作

以全龄连续通行和源头雨水控制作为示范段工程验收主线。



气候基线 / 空间响应

35.58°C 日最高温 P95	连续树冠 + 遮阳棚架 + 饮水休息
22.3 日/年 年均高温日	遮阳覆盖和热舒适监测纳入验收
649.1 mm 年均降水	源头消纳 + 可见溢流 + 安全退水
3.32 m/s 10 m 年均风速	冬季避风、夏季保留通风廊道

连续通行

无障碍路线不断点；交叉口、出入口、站点和轨道界面逐一核验。

慢行安全

步行、骑行、设施和机动车界面清晰；冲突点纳入交通专项审查。

海绵运维

汇水、调蓄、溢流、退水、检修和责任主体在竣工资料中——对应。

近期项目包：交付物、责任、前置条件与采购界面

六个项目按空间建设、片区更新、节点设施和运营治理拆分任务包。

编号	项目	规模 / 交付	建议主体	前置条件	投资 / 工期	采购包
P-01	创新发展轴示范段	1 km / 3 节点	区级统筹 + 街道 + 产权	红线 / 轨道 / 市政 / 水评	M / 6—18 月	W-01
P-02	大钟寺站城融合	四向联系 / 2 服务点	街道 + 站区运营 + 交通	客流 / 疏散 / 产权	L / 12—24 月	W-02
P-03	众智园创新验证场	1.5 ha / 测试与审议	园区 + 高校企业 + 评估	权属 / 准入 / 数据安全	L / 12—24 月	W-03
P-04	AI 原点共享首层	约 3000 m²	产权 + 街道 + 社区高校	结构 / 消防 / 运营协议	M / 9—18 月	W-04
P-05	三处服务节点样板	250—400 m²/处	街道 + 社区 + 运维	管线 / 接入 / 维护责任	M / 6—12 月	W-05
P-06	AI 公共服务治理	台账 / 公示 / 接管 / 评价	区级统筹 + 运营 + 评估	数据分类 / 预案 / 投诉	S / 3—9 月	W-06

采购包拆分




二十四个月交付时序与投资构成

以可数事件和可数百分点呈现项目推进、投资结构、决策门槛与支付条件。

六个项目错峰推进，24 个月完成首期交付

● 启动 / 交付 · ○ 审查 / 样板 / 试运行 · 虚线 = 跨阶段协同间隔 · 月份 1—24

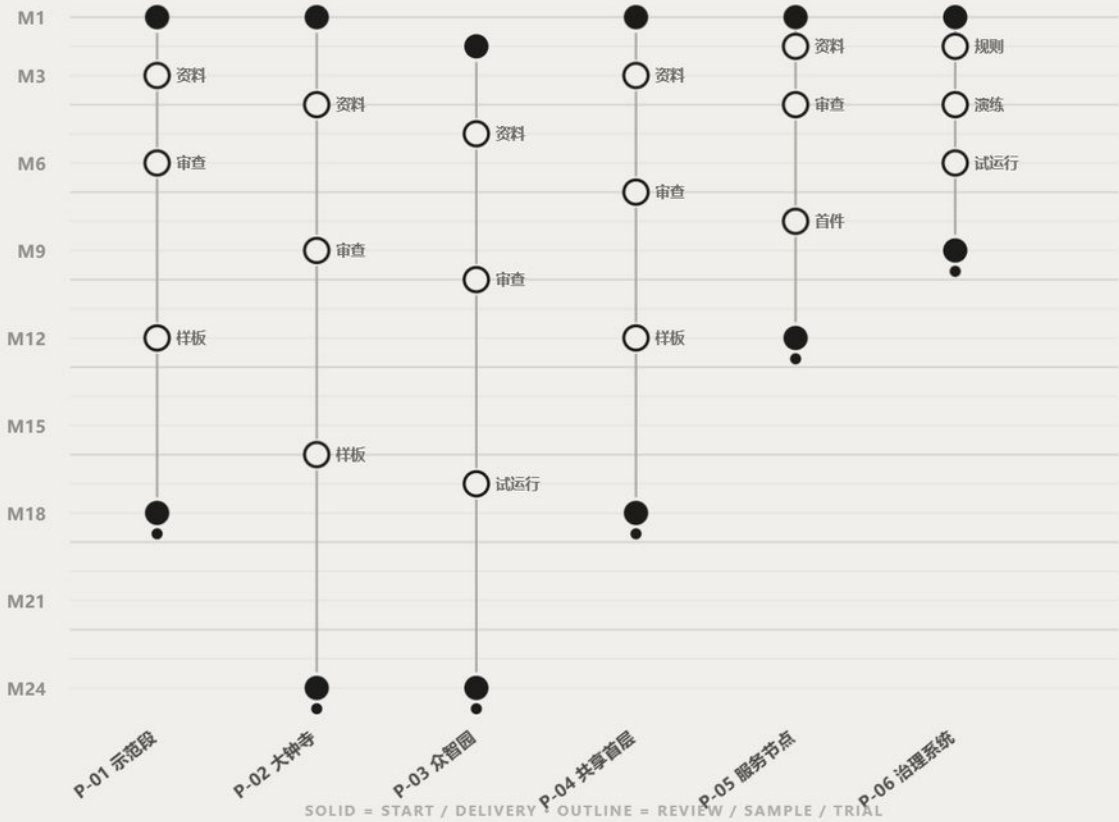

L11 TREND LINEAGE · MONO · JINGZHANG DELIVERY PROGRAMME

空间建设类投入占 87%，治理与预备费占 13%

一个点 = 方案阶段投资构成的 1 个百分点 · 六类费用合计 100%



L14 HUNDRED FIELD · MONO · STAGE-ONE COST COMPOSITION

五类决策门槛

G0 资料齐备 红线 / 权属 / 管线	G1 专项同审 交通 / 消防 / 水务	G2 首件样板 材料 / 构造 / 运维	G3 联合验收 工程 / 使用 / 证据	G4 运营复审 成本 / 绩效 / 退出
-----------------------------------	-----------------------------------	-----------------------------------	-----------------------------------	-----------------------------------

支付节点与成本控制



合同与保险 / 样板确认 / 主体完成 / 联合验收 / 缺陷期结束

首件样板锁定材料与构造；变更须同步核算工程量、工期和全生命周期运维费用。

九项验收指标：测量方法与证据编号

每项指标绑定测量方法、责任主体、检查频率和归档证据。


KPI-01 100% 无障碍连续通行率 方法 全线走查 主体 建设 + 运维 证据 E-01 检查	KPI-02 ≤150 m 主要休憩点间距 方法 GIS / 实测 主体 设计单位 证据 E-02 检查	KPI-03 ≥70% 停留空间遮阴建议值 方法 夏至投影 主体 园林单位 证据 E-03 检查
KPI-04 100% 人工服务渠道可用率 方法 现场抽测 主体 运营单位 证据 E-04 检查	KPI-05 100% AI 服务信息公示率 方法 公示核对 主体 场景主体 证据 E-05 检查	KPI-06 100% 季度应急演练完成率 方法 演练记录 主体 运营单位 证据 E-06 检查
KPI-07 ≥90% 设施故障 24h 闭环率 方法 工单统计 主体 运维单位 证据 E-07 检查	KPI-08 ≥90% 公众意见 5 日响应率 方法 台账统计 主体 属地街道 证据 E-08 检查	KPI-09 100% 蓝绿设施责任标识率 方法 设施普查 主体 园林排水 证据 E-09 检查

证据归档规则

工程类 测量记录 + 竣工图 + 隐蔽验收	运行类 工单 + 服务台账 + 演练记录	公众类 意见原文 + 办理过程 + 公开答复	AI 类 场景卡 + 版本号 + 事件与复审决定
---	--	--	--

运营证据台账：四类岗位与年度闭环

把公共服务、设施维护、AI 场景和公众意见纳入同一责任与证据体系。

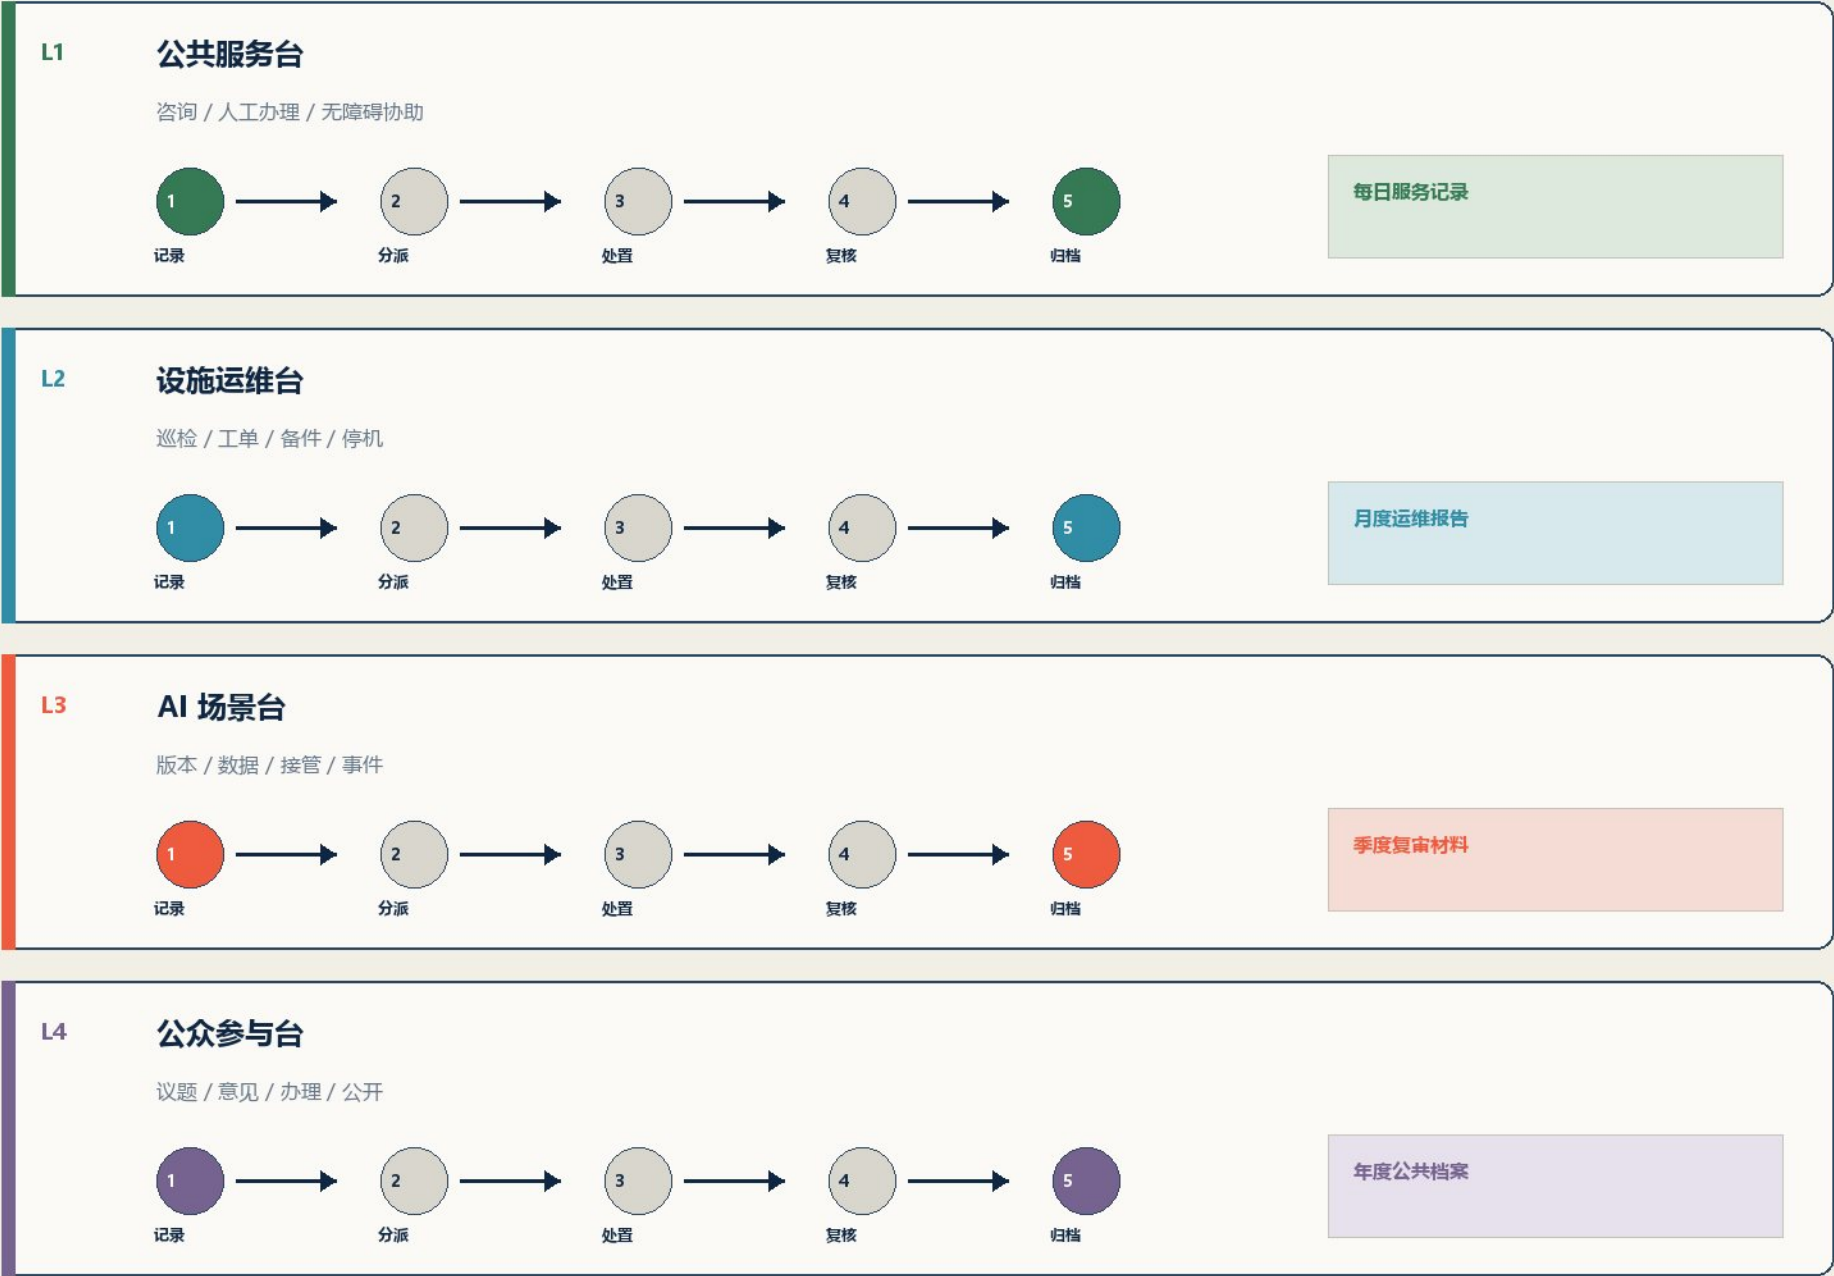

责任矩阵 / RACI

事项	街道	运营	运维	评估
服务	A	R	C	I
设施	A	C	R	I
AI	A	R	C	C
评价	A	C	I	R

R 执行 / A 负责 / C 协商 / I 知会