


ORIGIN LINE 原点·智轨

Centennial Jingzhang AI Belt · One Axis, Three Cores, Two Wings, One Loop

ORIGIN LINE | Overall Spatial Structure


One Axis · Three Cores · Two Wings · One Loop — Centennial Jingzhang AI Belt (approx. 11.4 km², provisional boundary)

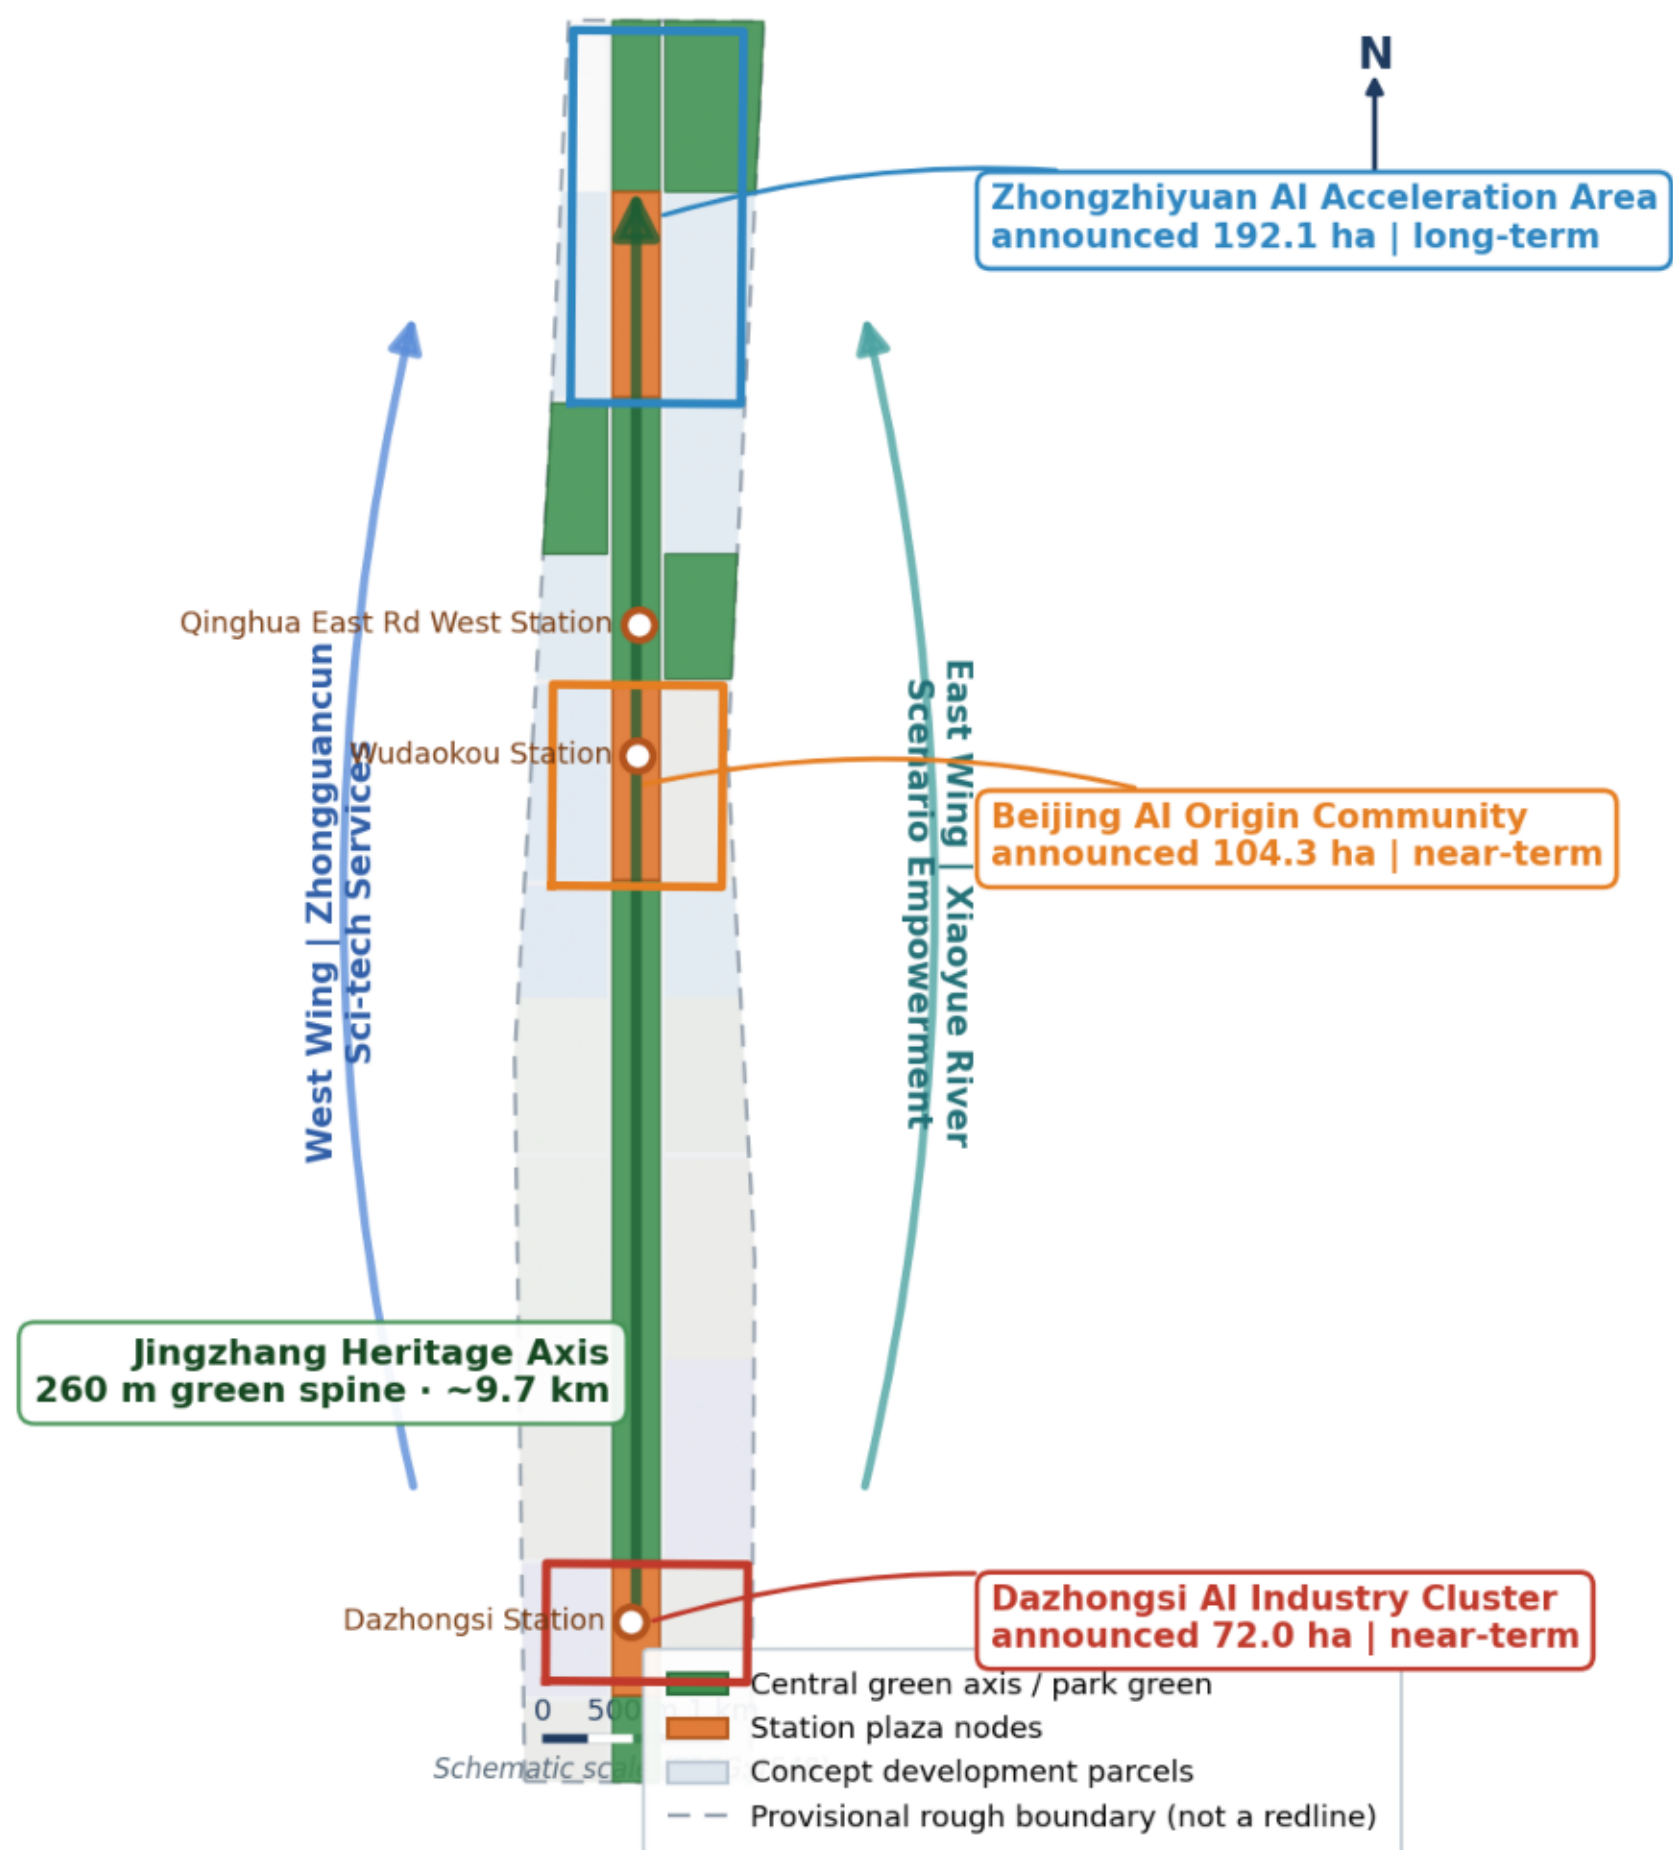

Note: overall boundary and key areas are provisional rough boundaries, pending official data; not valid as redlines. Areas recomputed from provisional geometry in EPSG:4548. Sources: call announcement (2026-05) + open site-package provisional geometry; AI-agent concept scheme ORIGIN LINE.

Three Cores | Key Detailed-design Areas

North to south: Zhongzhiyuan → AI Origin Community → Dazhongsi (provisional rough boundaries, announced-area comparison)

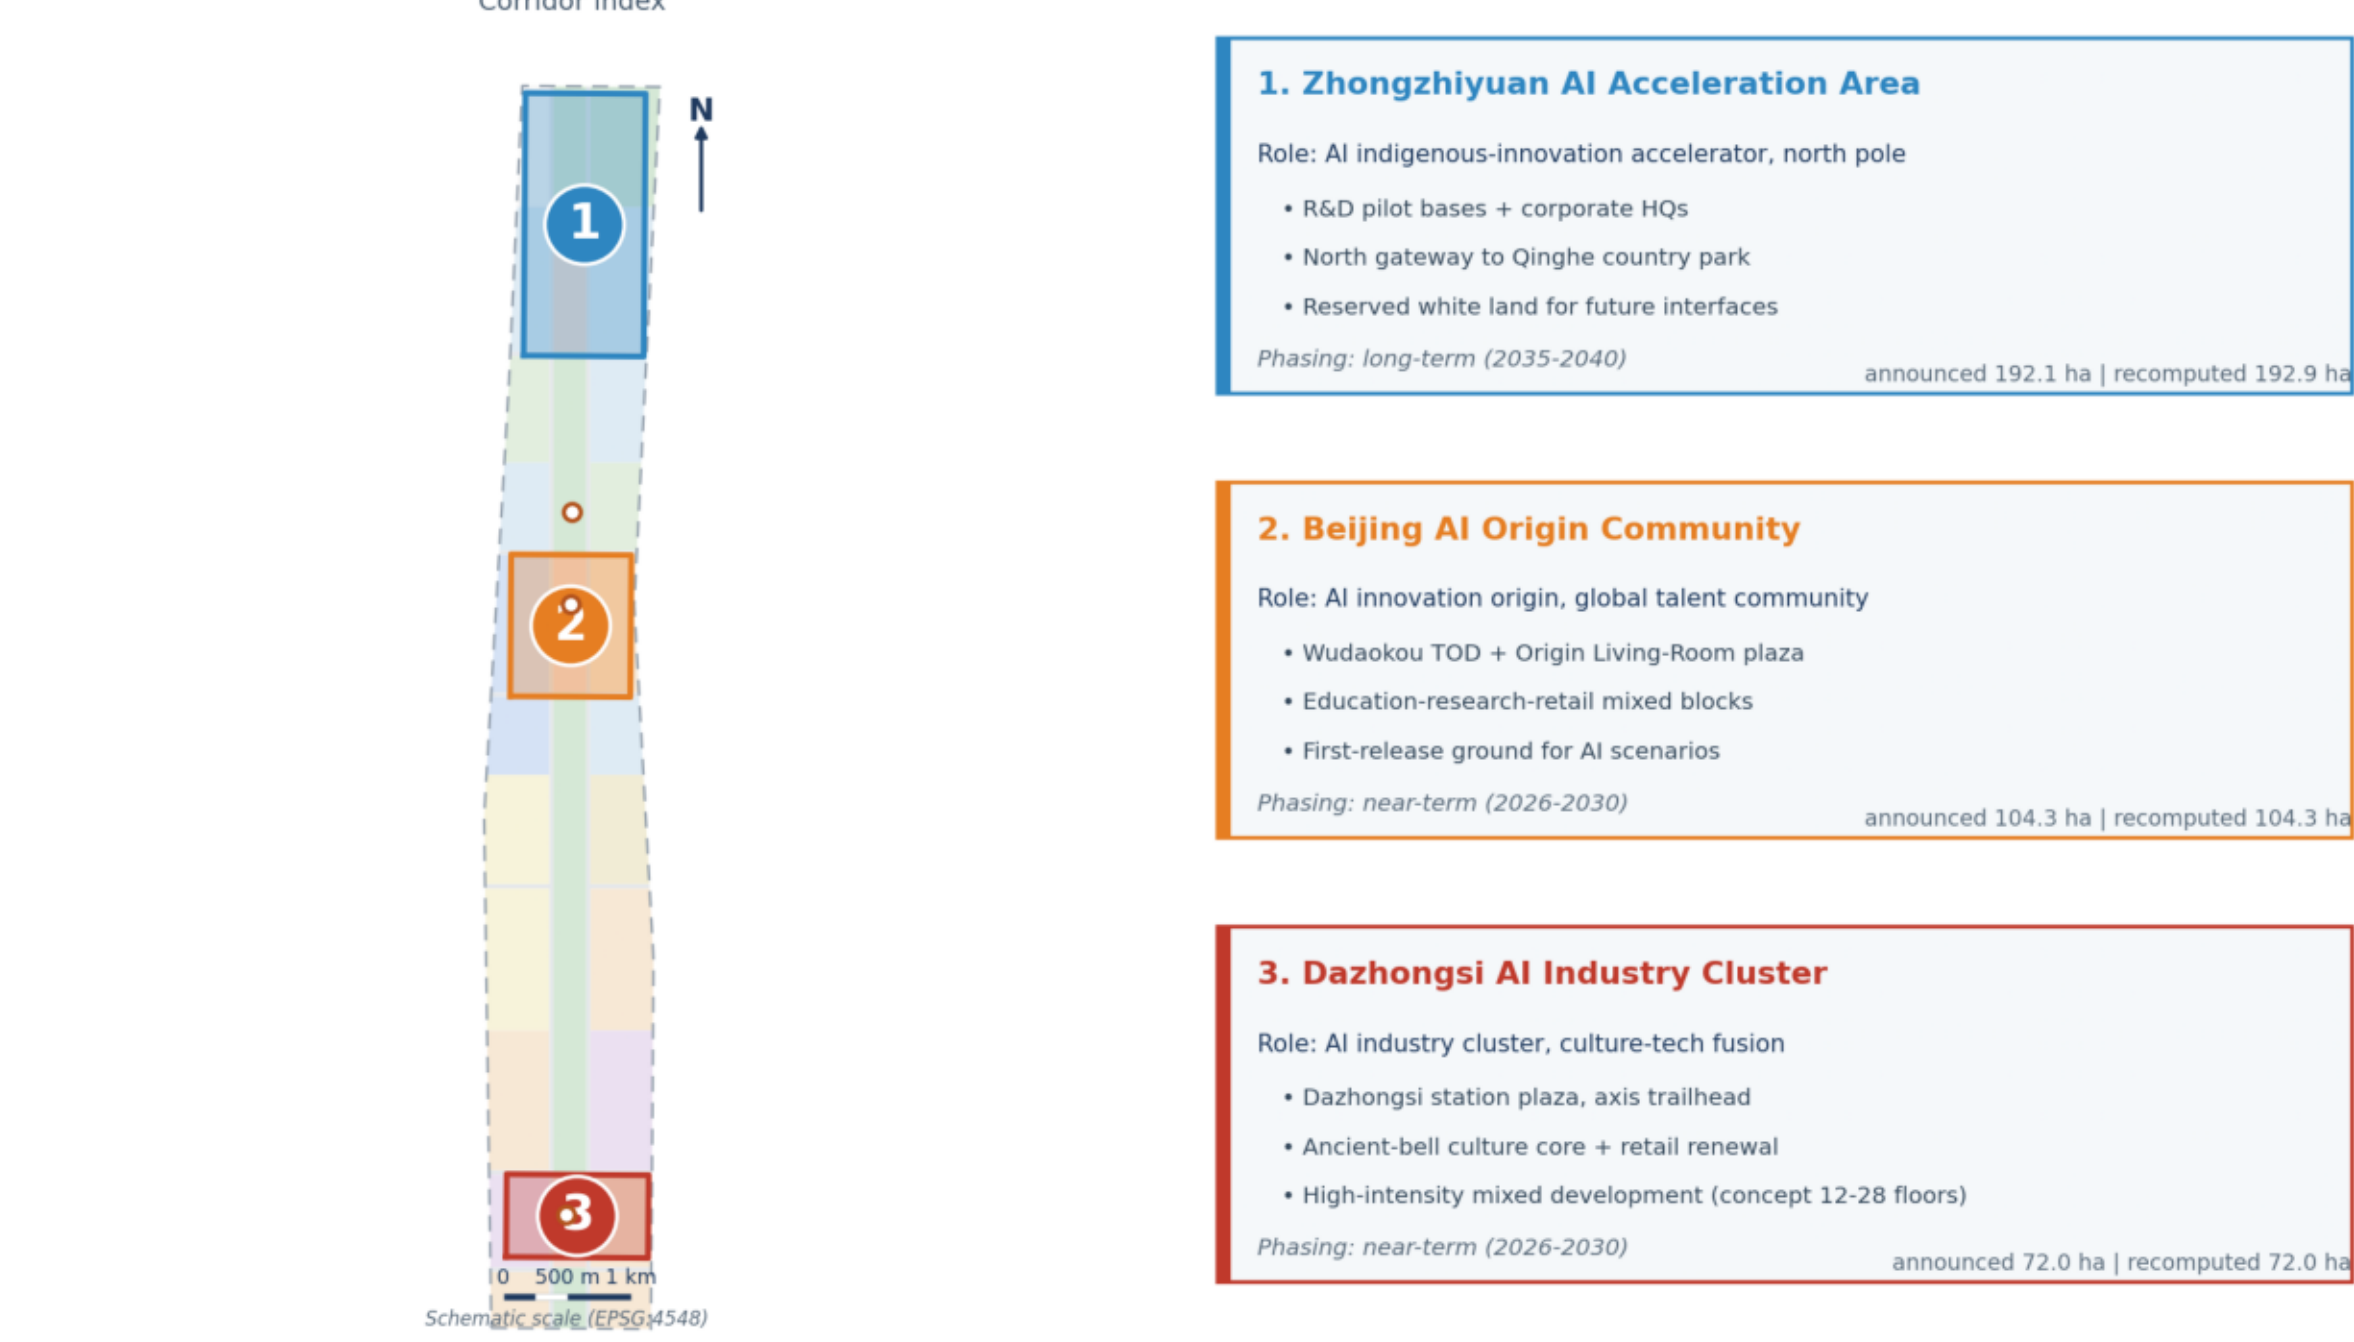

Note: overall boundary and key areas are provisional rough boundaries, pending official data; not valid as redlines. Areas recomputed from provisional geometry in EPSG:4548. Sources: call announcement (2026-05) + open site-package provisional geometry; AI-agent concept scheme ORIGIN LINE.

1,141.3 ha

Design area

24.4%

Green ratio

9.3%

Public space

3


Key areas

Systems & Metrics

Land use · mobility & blue-green · metrics evidence

Land-use Structure | Seamless Topological Partition


29 parcels tile SITE-001 without gaps or overlaps; shared edges share vertices; areas recomputed in EPSG:4548

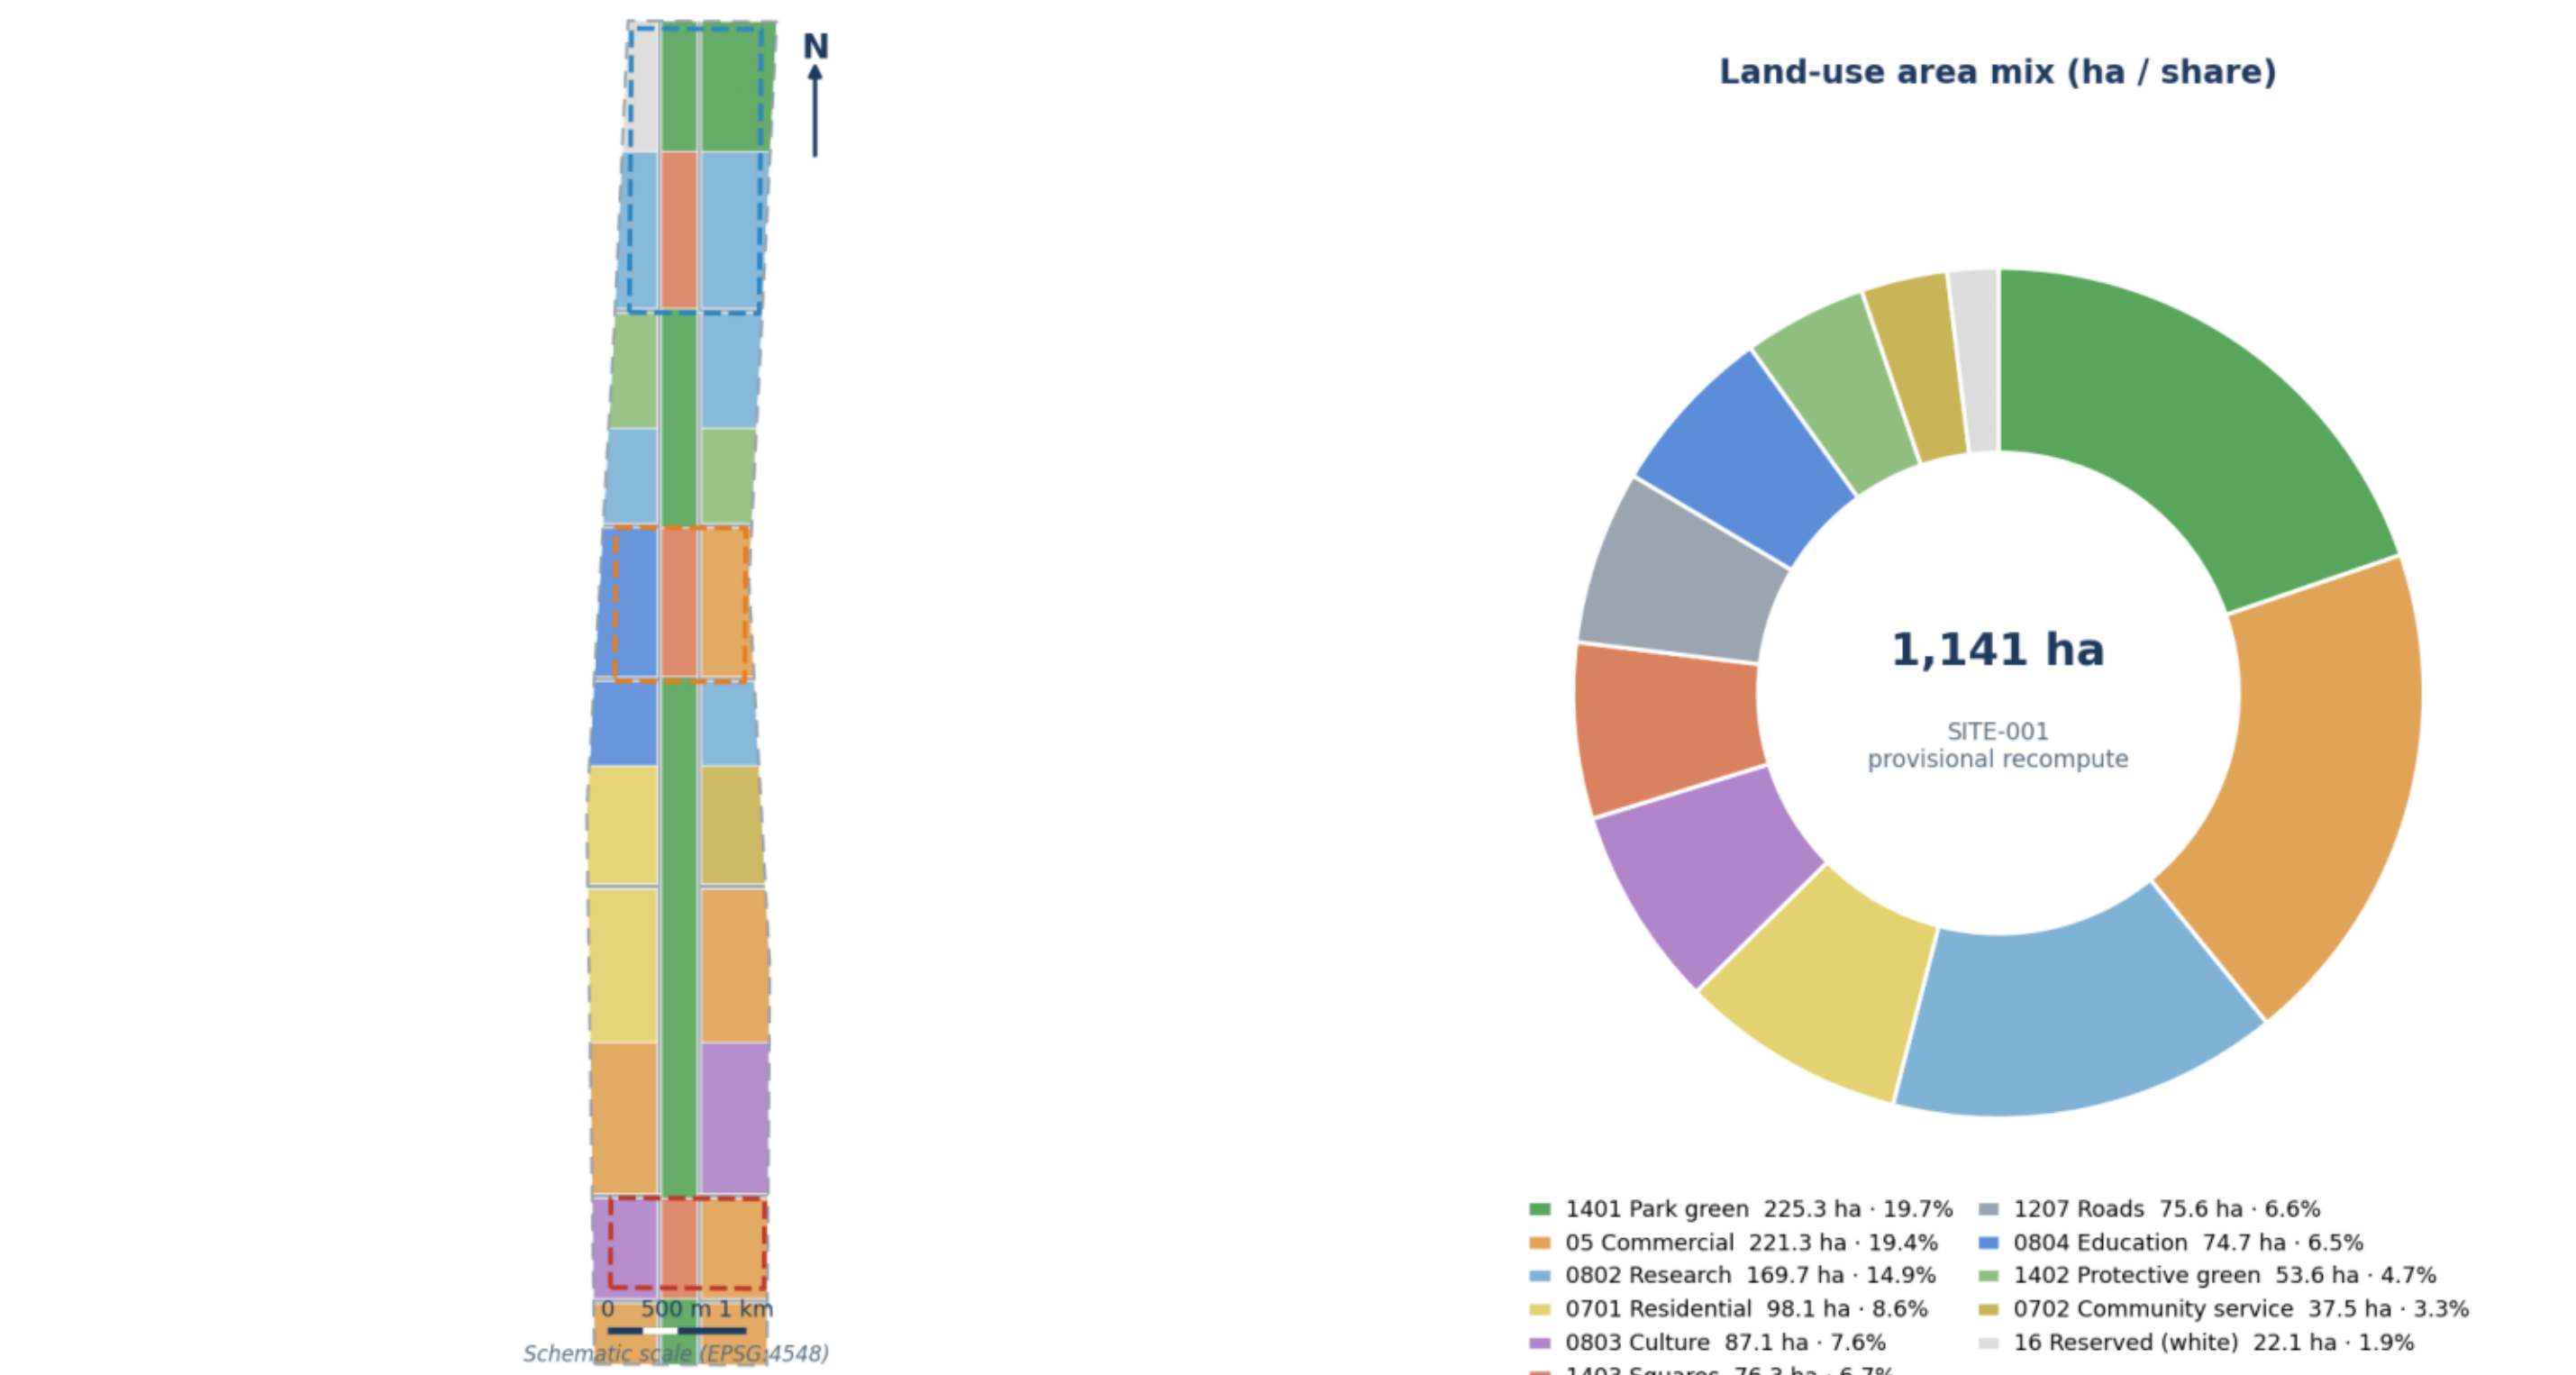

Note: overall boundary and key areas are provisional rough boundaries, pending official data; not valid as redlines. Areas recomputed from provisional geometry in EPSG:4548. Sources: call announcement (2026-05) + open site-package provisional geometry; AI-agent concept scheme ORIGIN LINE.

Mobility & Blue-green Network


Heritage axis + flanking service avenues + E-W links + slow-mobility loop; three metro stations (concept locations)

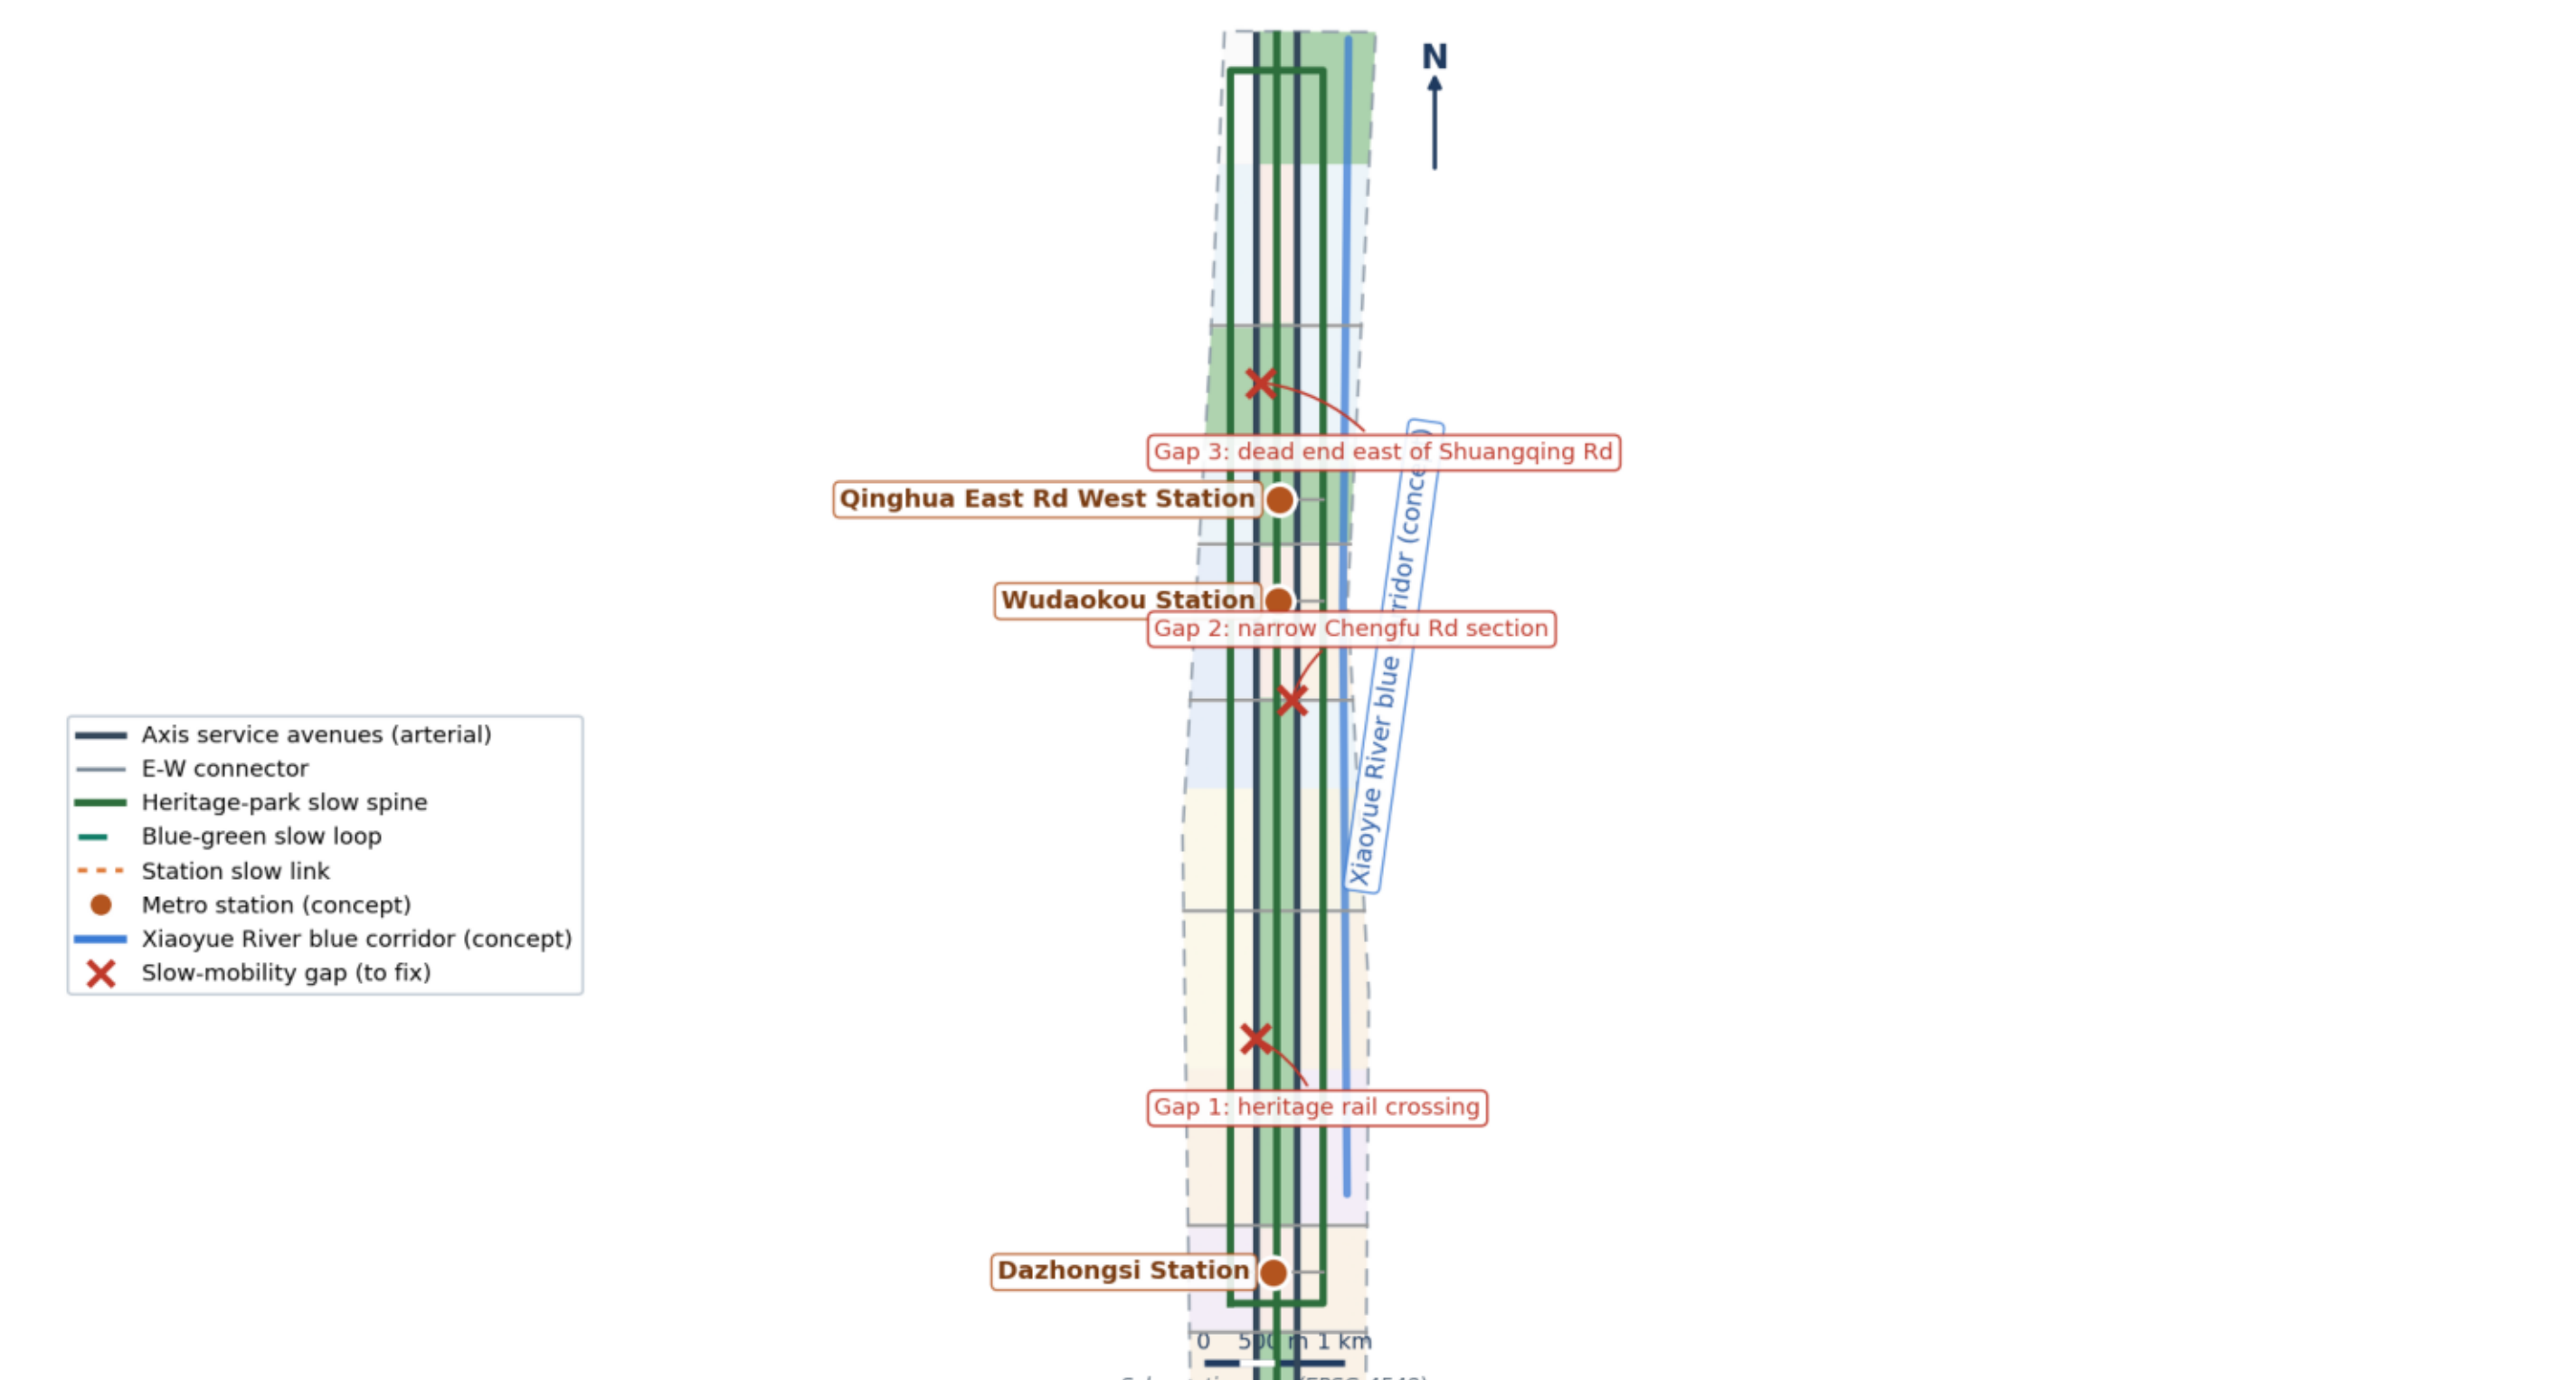

Note: overall boundary and key areas are provisional rough boundaries, pending official data; not valid as redlines. Areas recomputed from provisional geometry in EPSG:4548. Sources: call announcement (2026-05) + open site-package provisional geometry; AI-agent concept scheme ORIGIN LINE.

Metrics Evidence Dashboard

All metrics recomputed from design geometry in EPSG:4548; concept metrics are low-confidence design quantities, not statutory controls

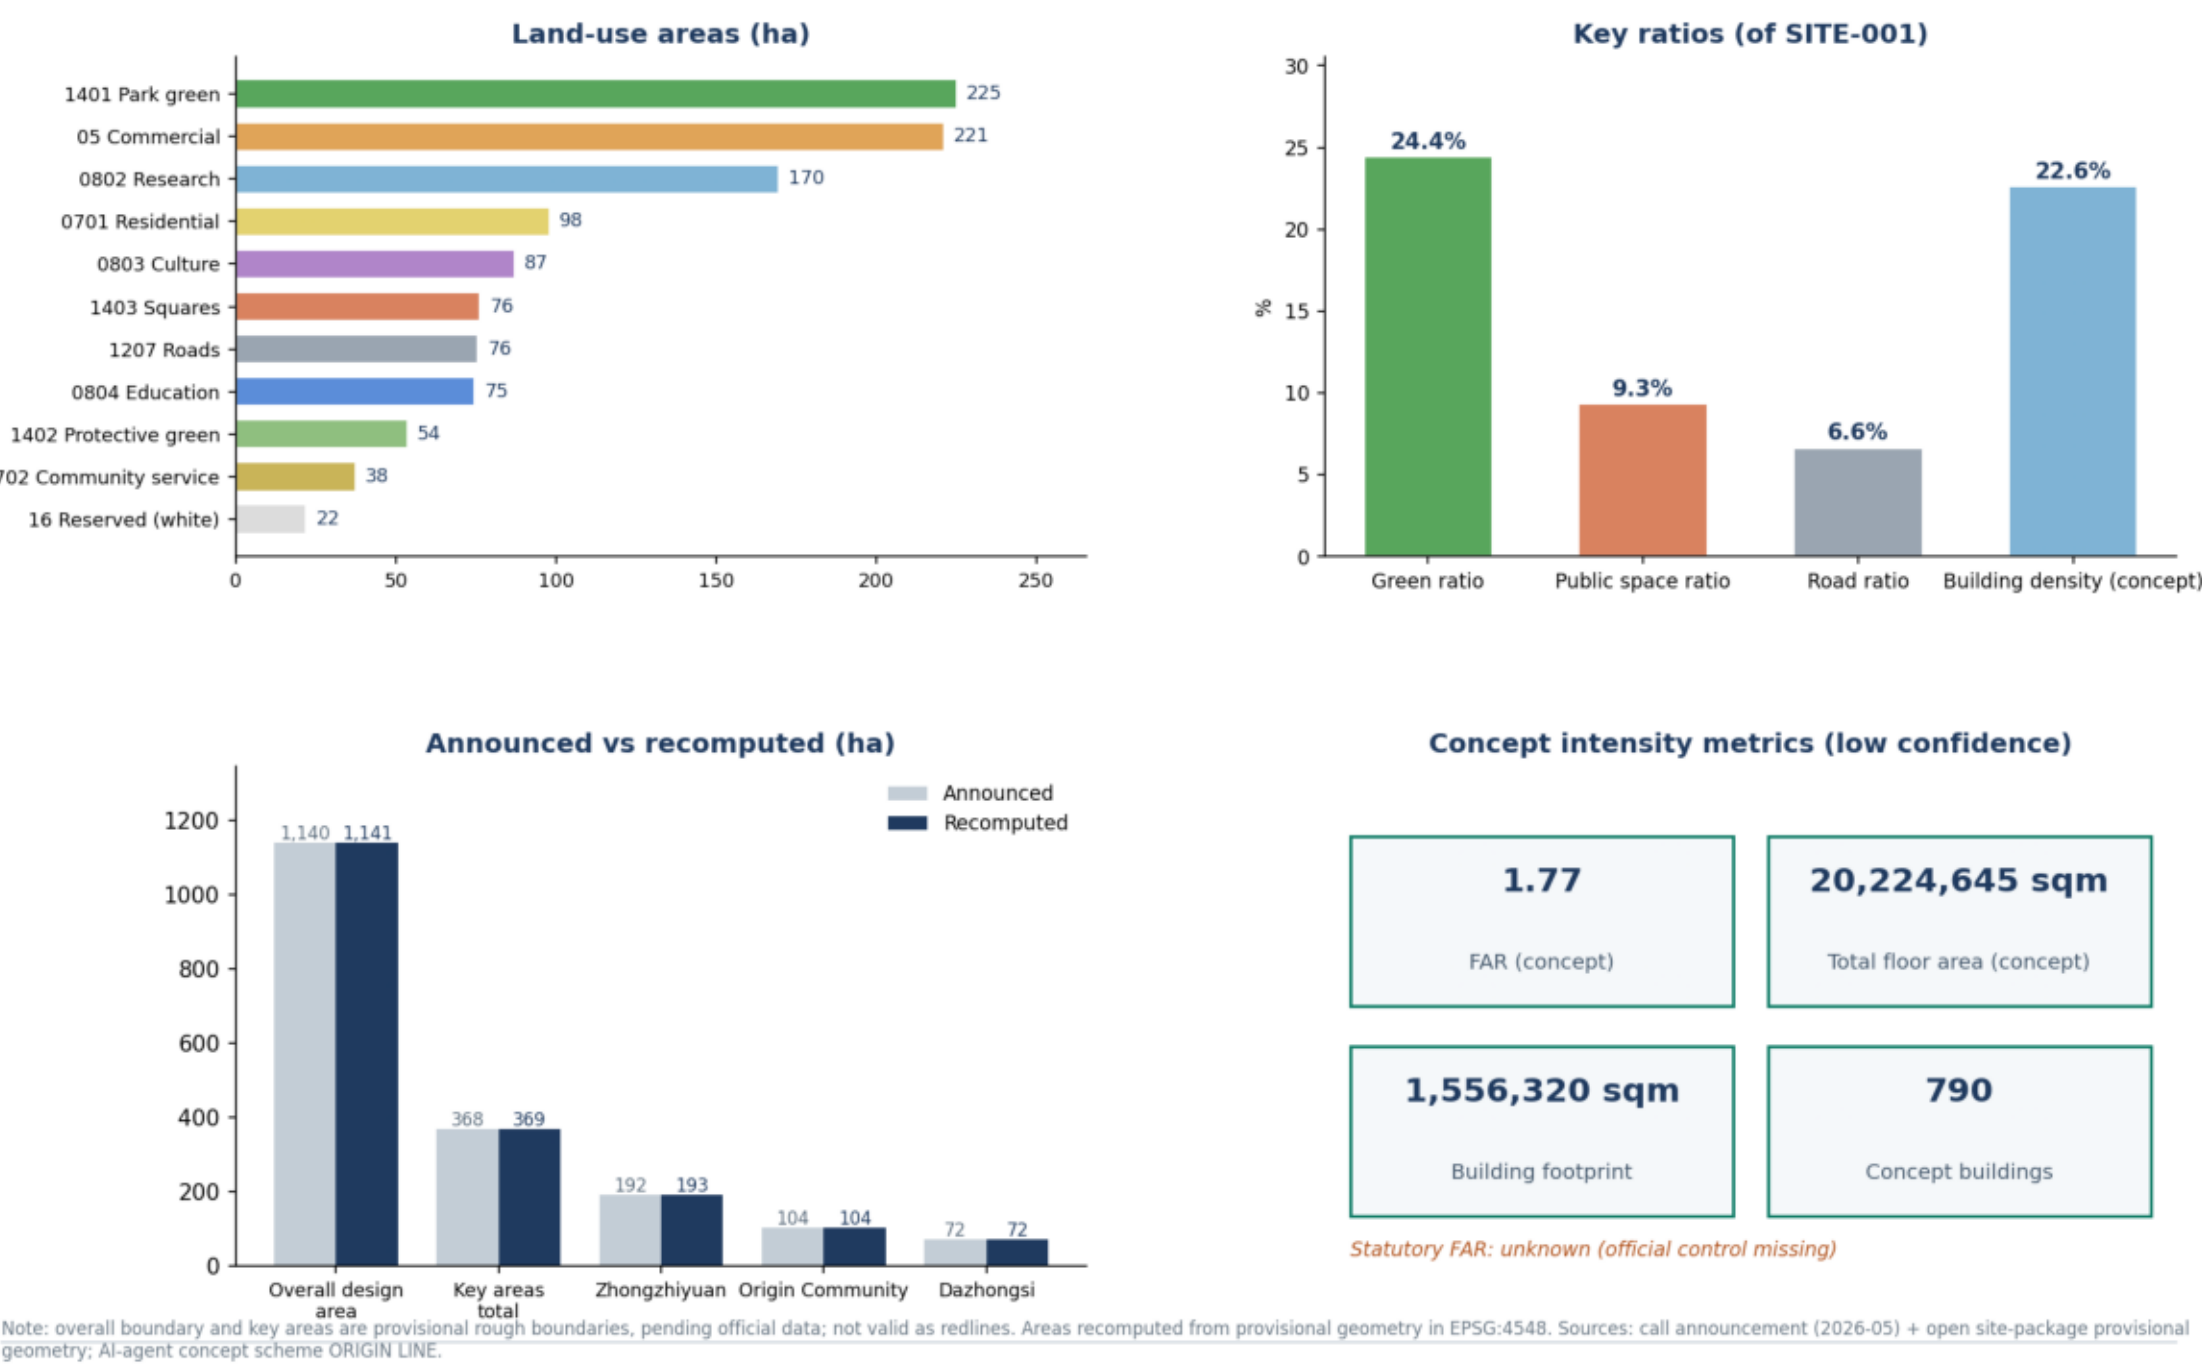

Note: overall boundary and key areas are provisional rough boundaries, pending official data; not valid as redlines. Areas recomputed from provisional geometry in EPSG:4548. Sources: call announcement (2026-05) + open site-package provisional geometry; AI-agent concept scheme ORIGIN LINE.

2,022 ×10⁴ m²

Total floor area (concept)

1.77

FAR (concept)

unknown

Statutory FAR

Concept metrics are low-confidence design quantities, not statutory controls.