
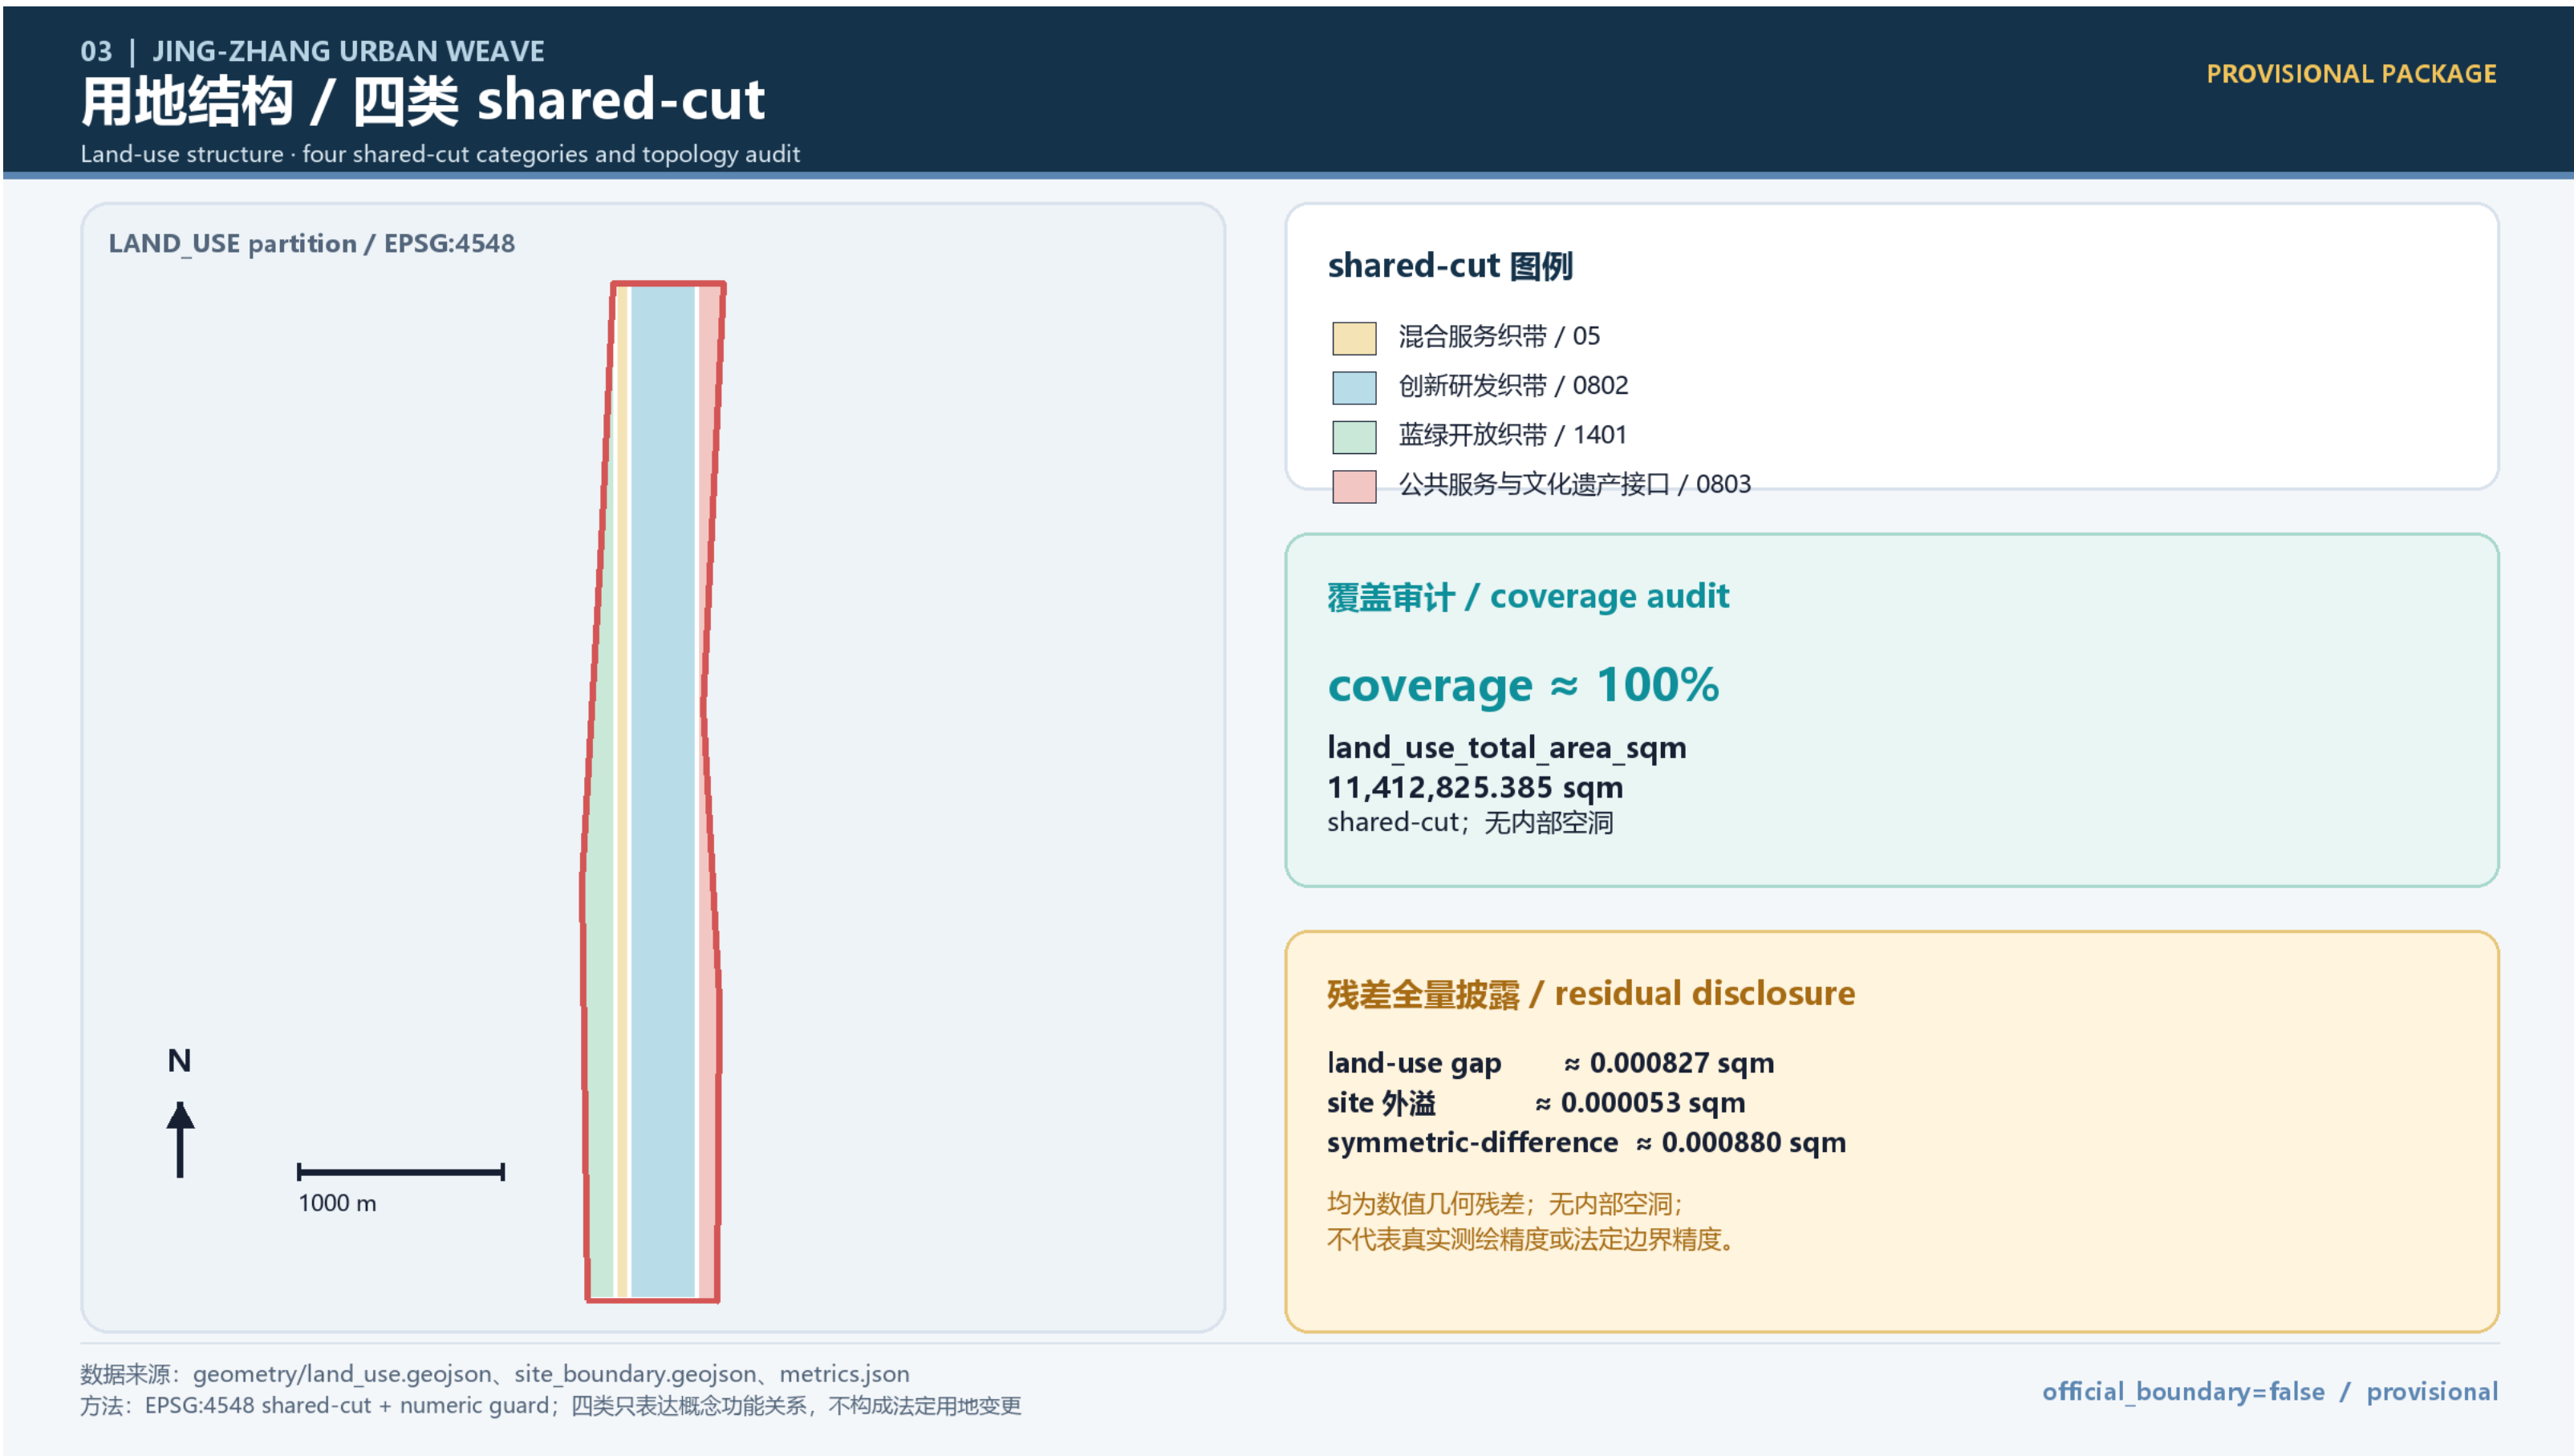


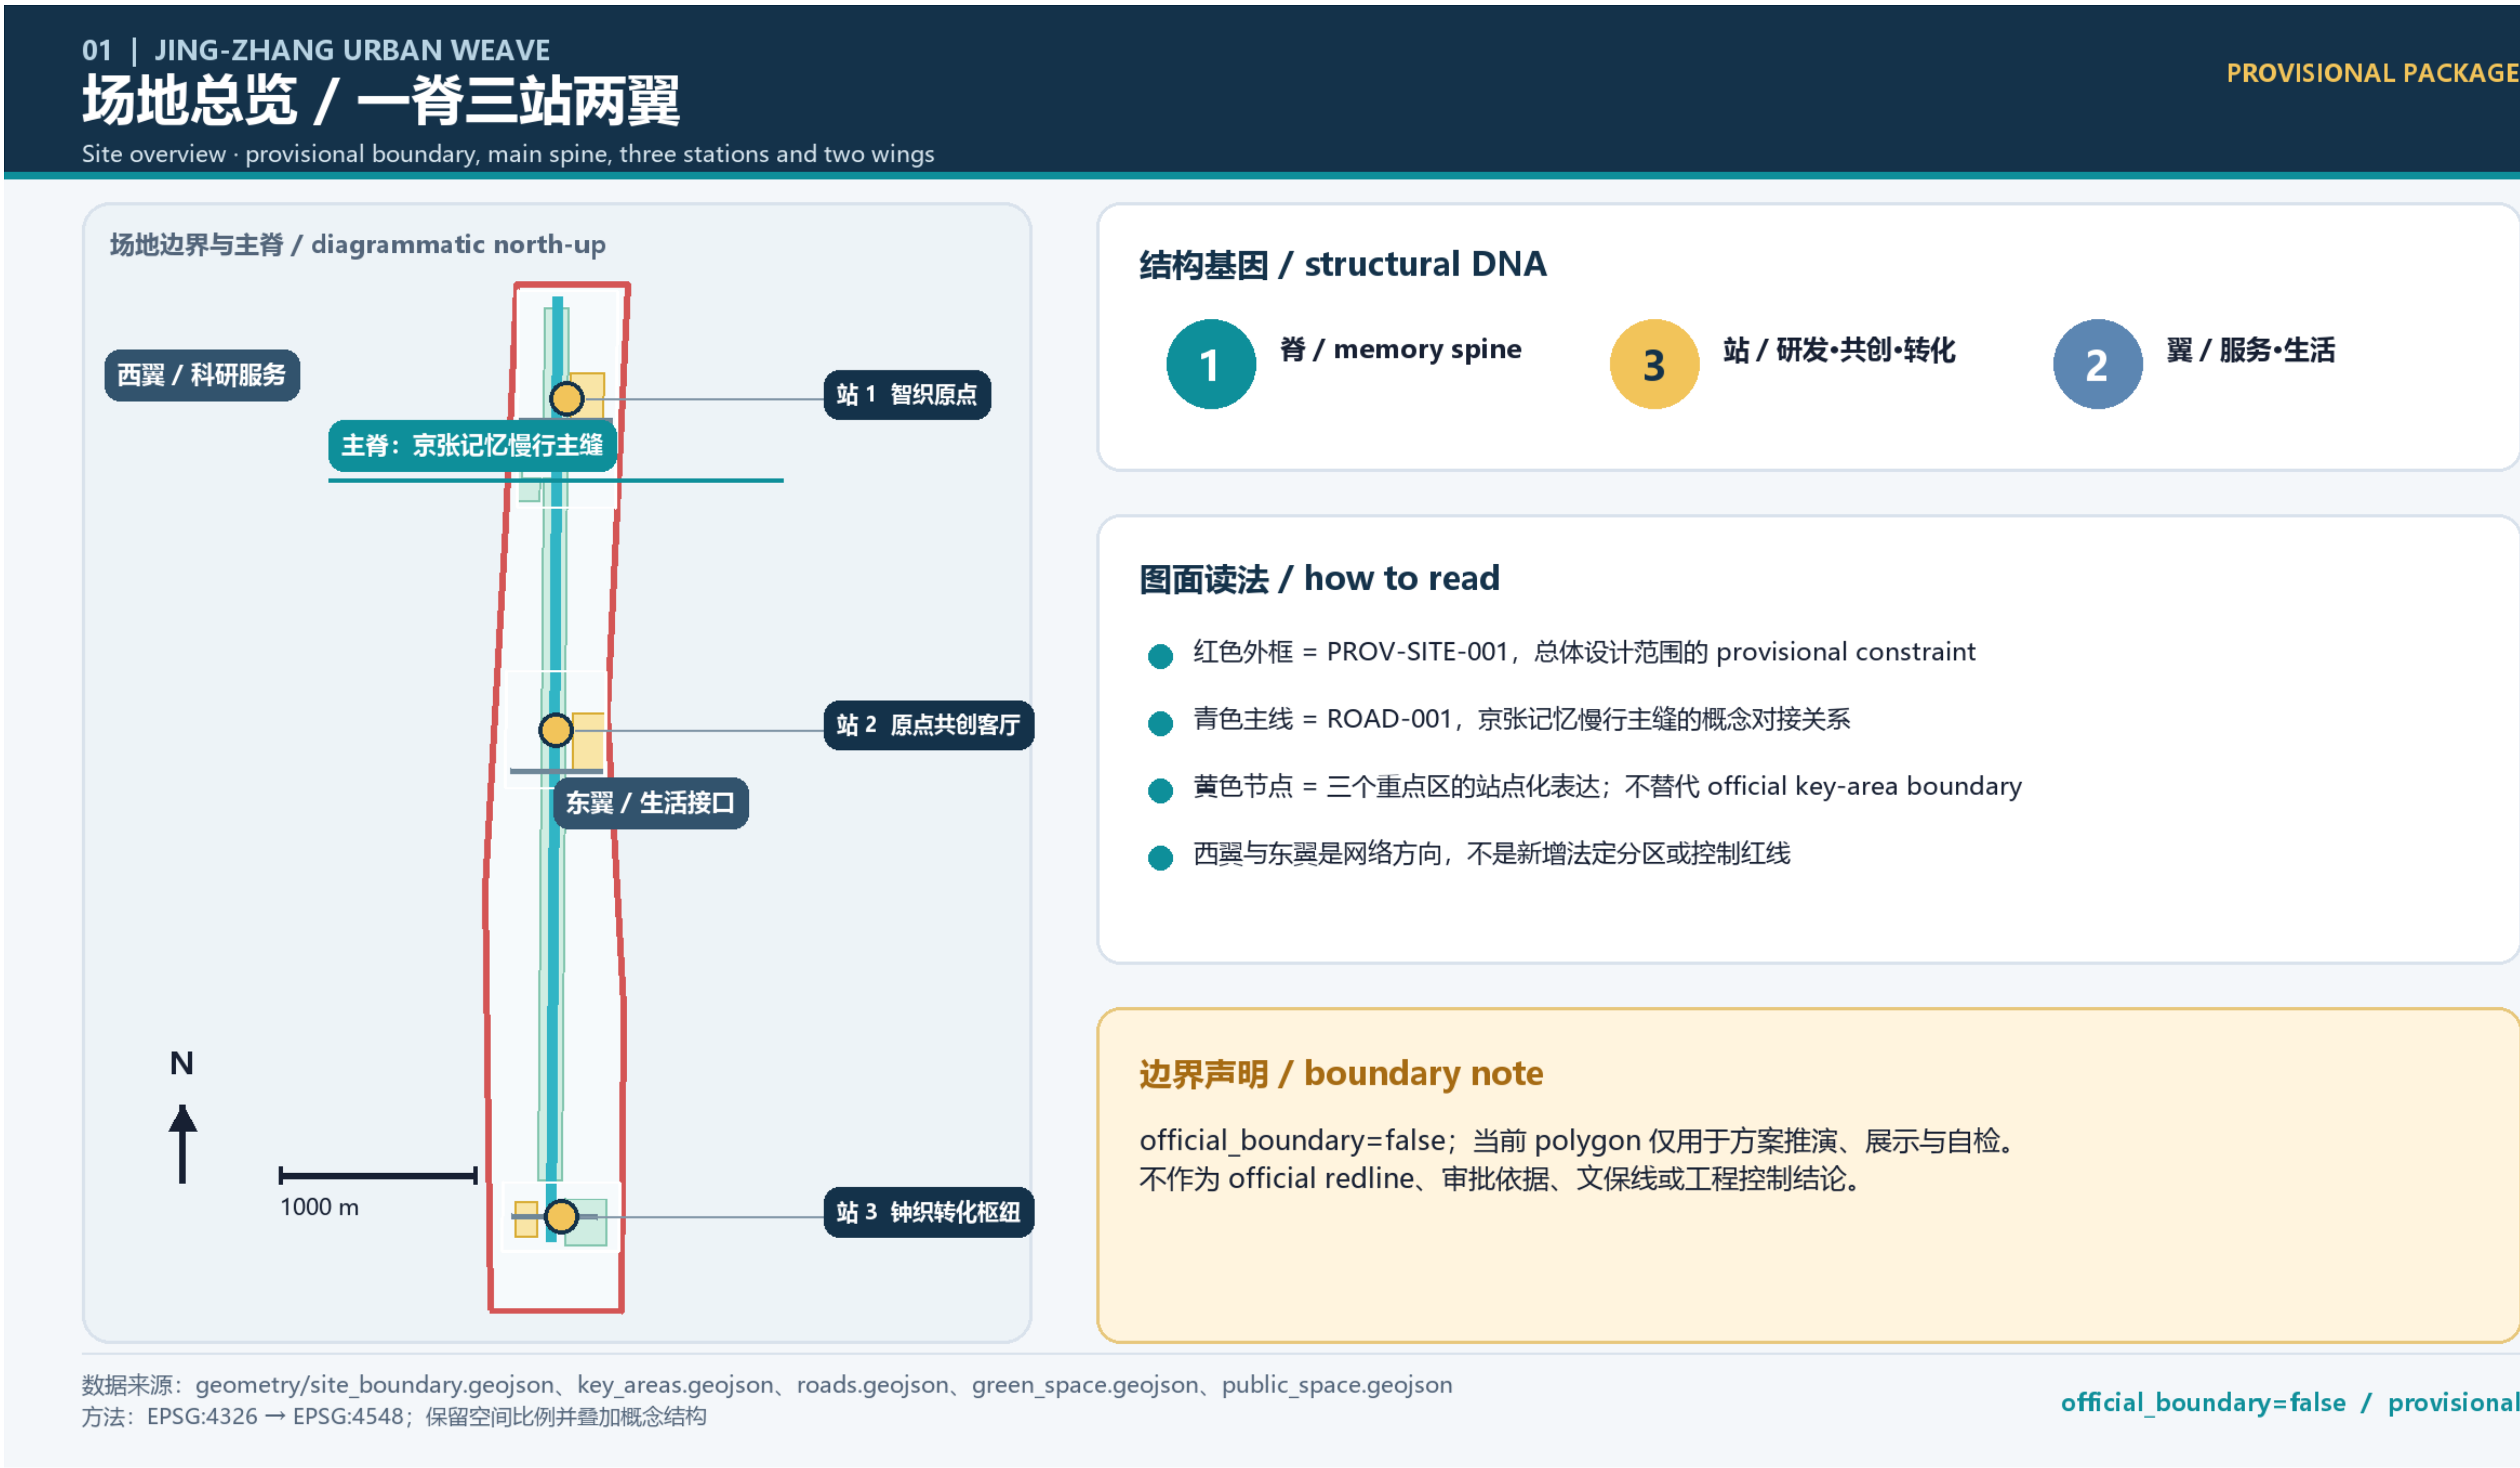

一脊三站两翼

主脊：京张记忆慢行主缝

三站：众智园研发、AI 原点共创、大钟寺应用转化

两翼：西翼科研服务、东翼生活接口

所有边界均为 provisional；方向性结构不等于法定分区。

用地与残差

四类 shared-cut：
混合服务 / 创新研发 / 蓝绿开放 / 公共服务文化遗产



coverage≈100%

land-use gap≈0.000827 sqm

site 外溢≈0.000053 sqm

symmetric-difference≈0.000880 sqm

无内部空洞；不代表 survey-level exact。

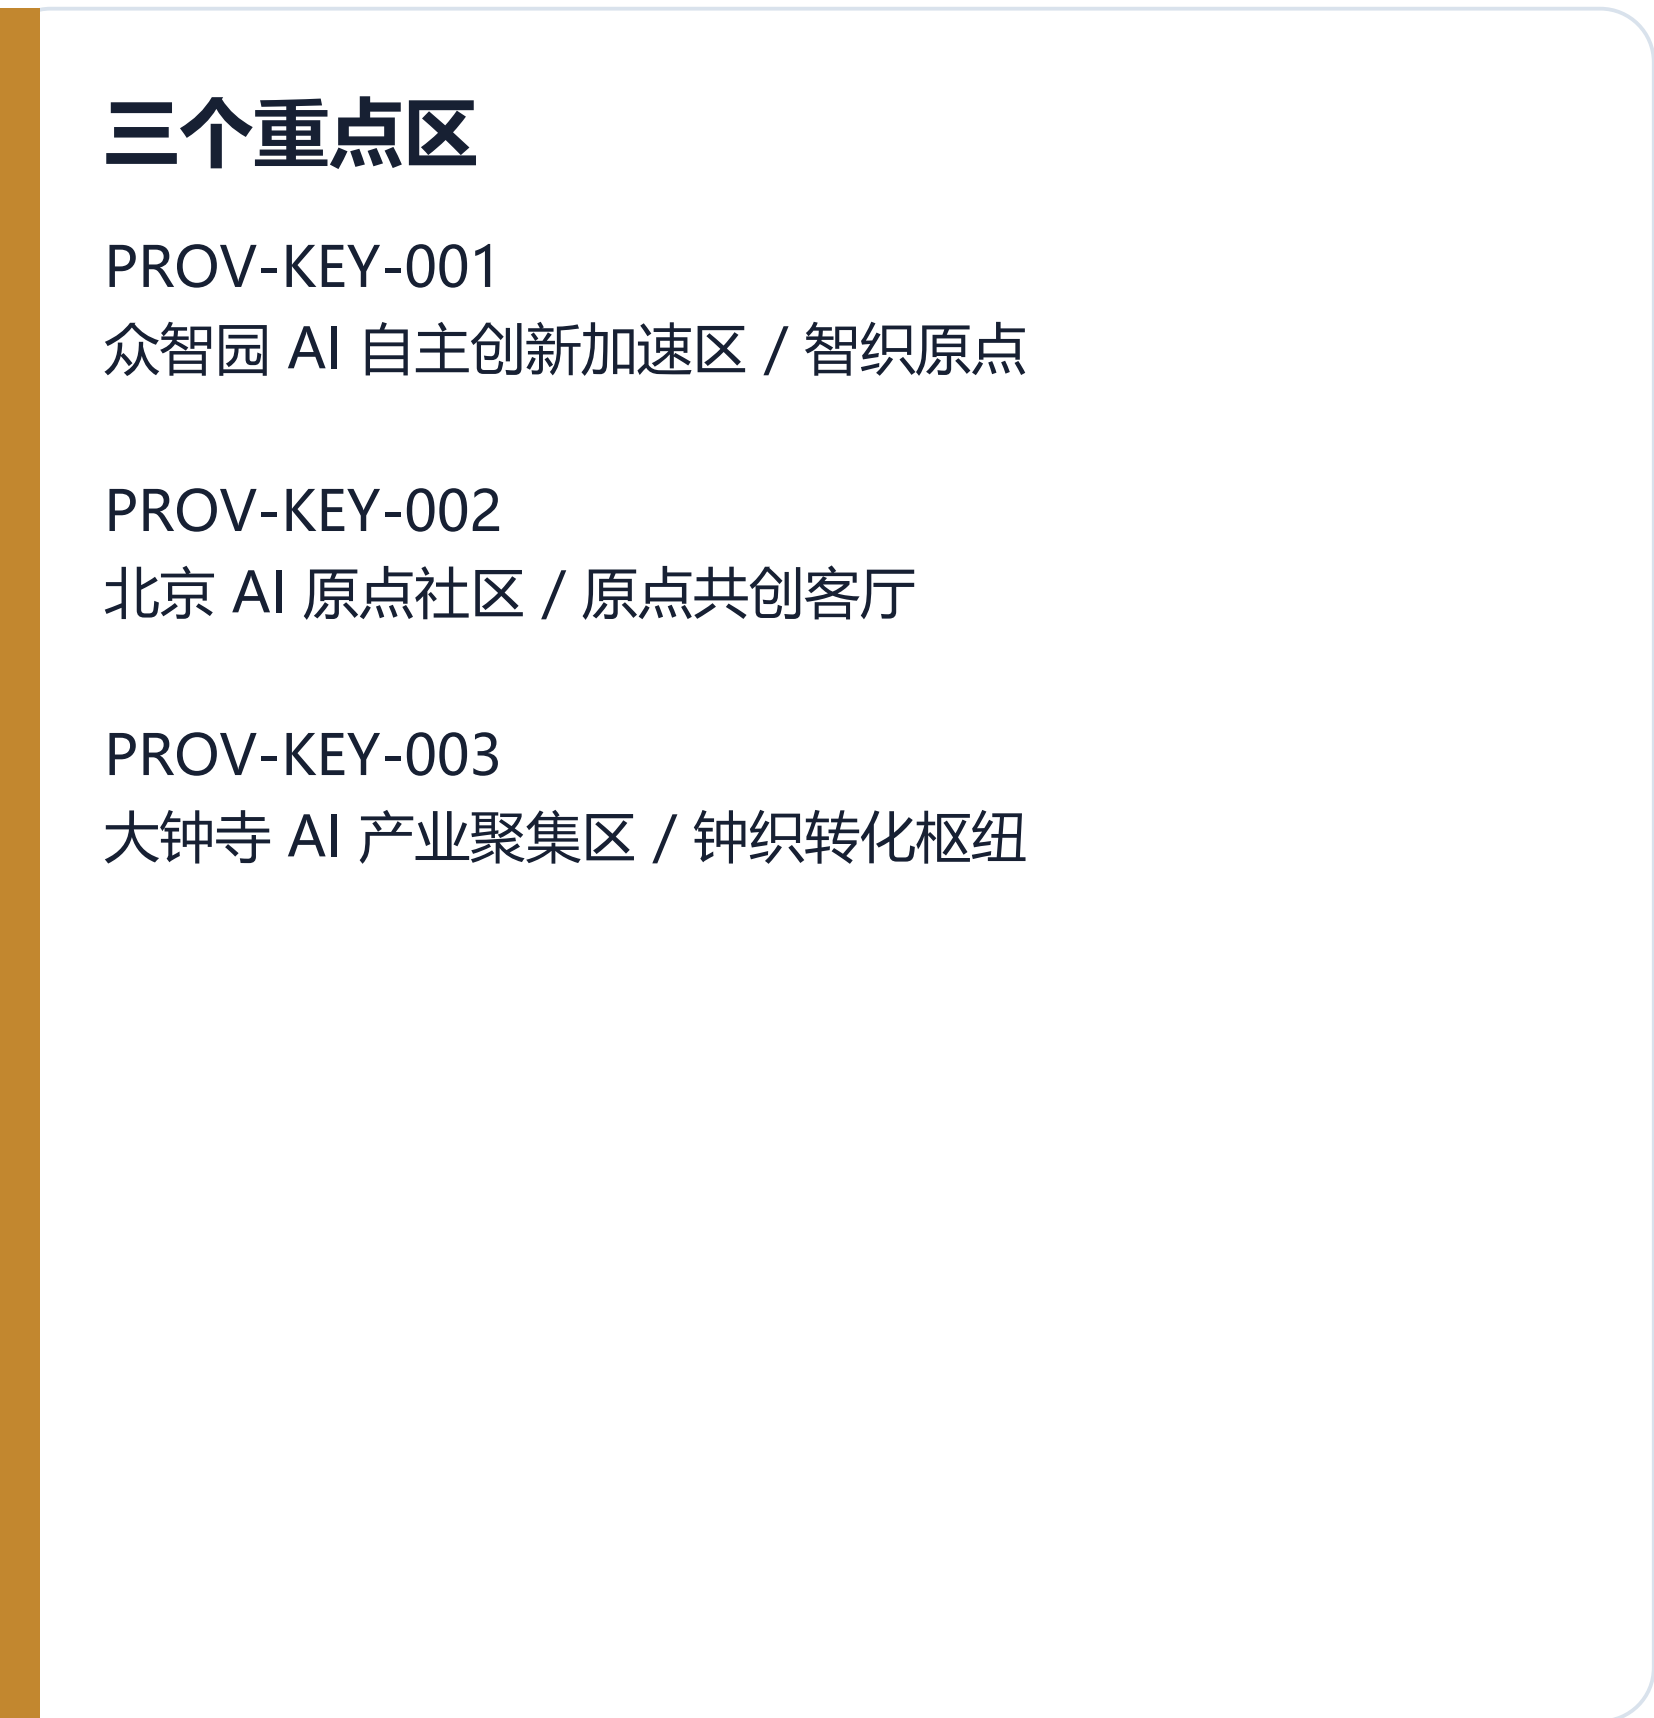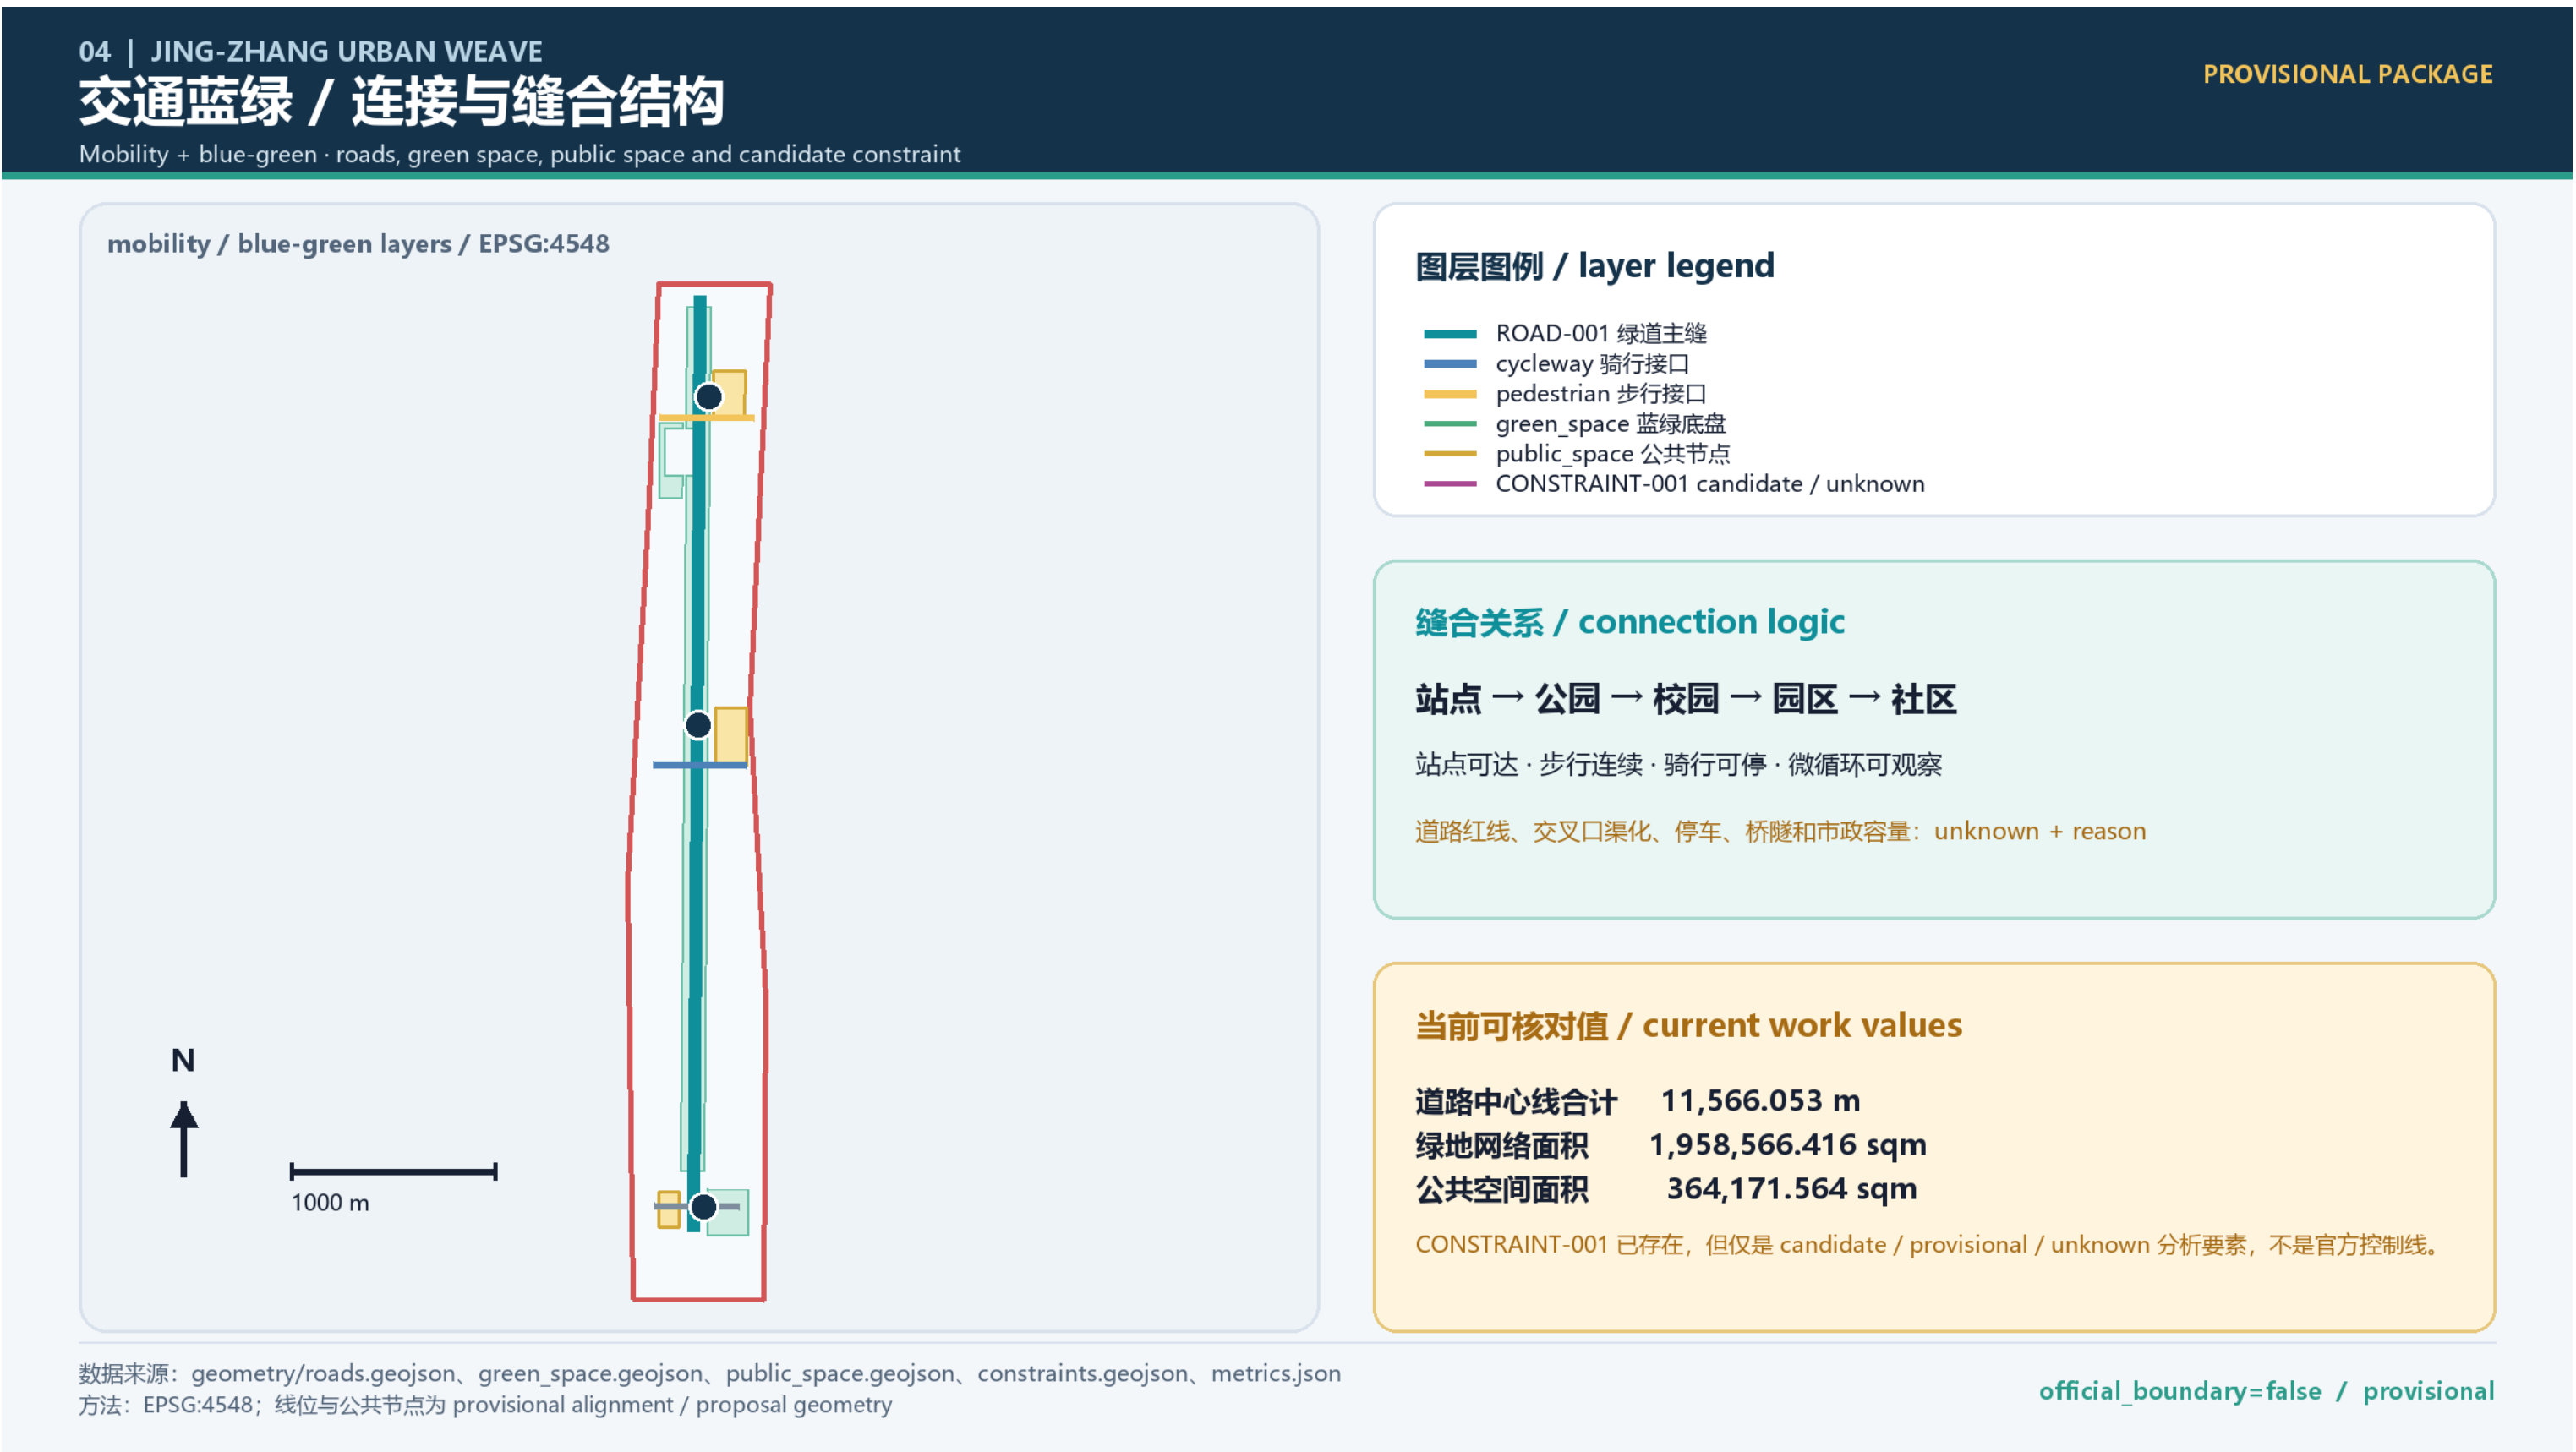


05 | JING-ZHANG URBAN WEAVE

指标证据 / 复算、未知与替换条件

Metrics evidence · current provisional values, unknown controls and audit trail

PROVISIONAL PACKAGE

evidence layers / EPSG:4548

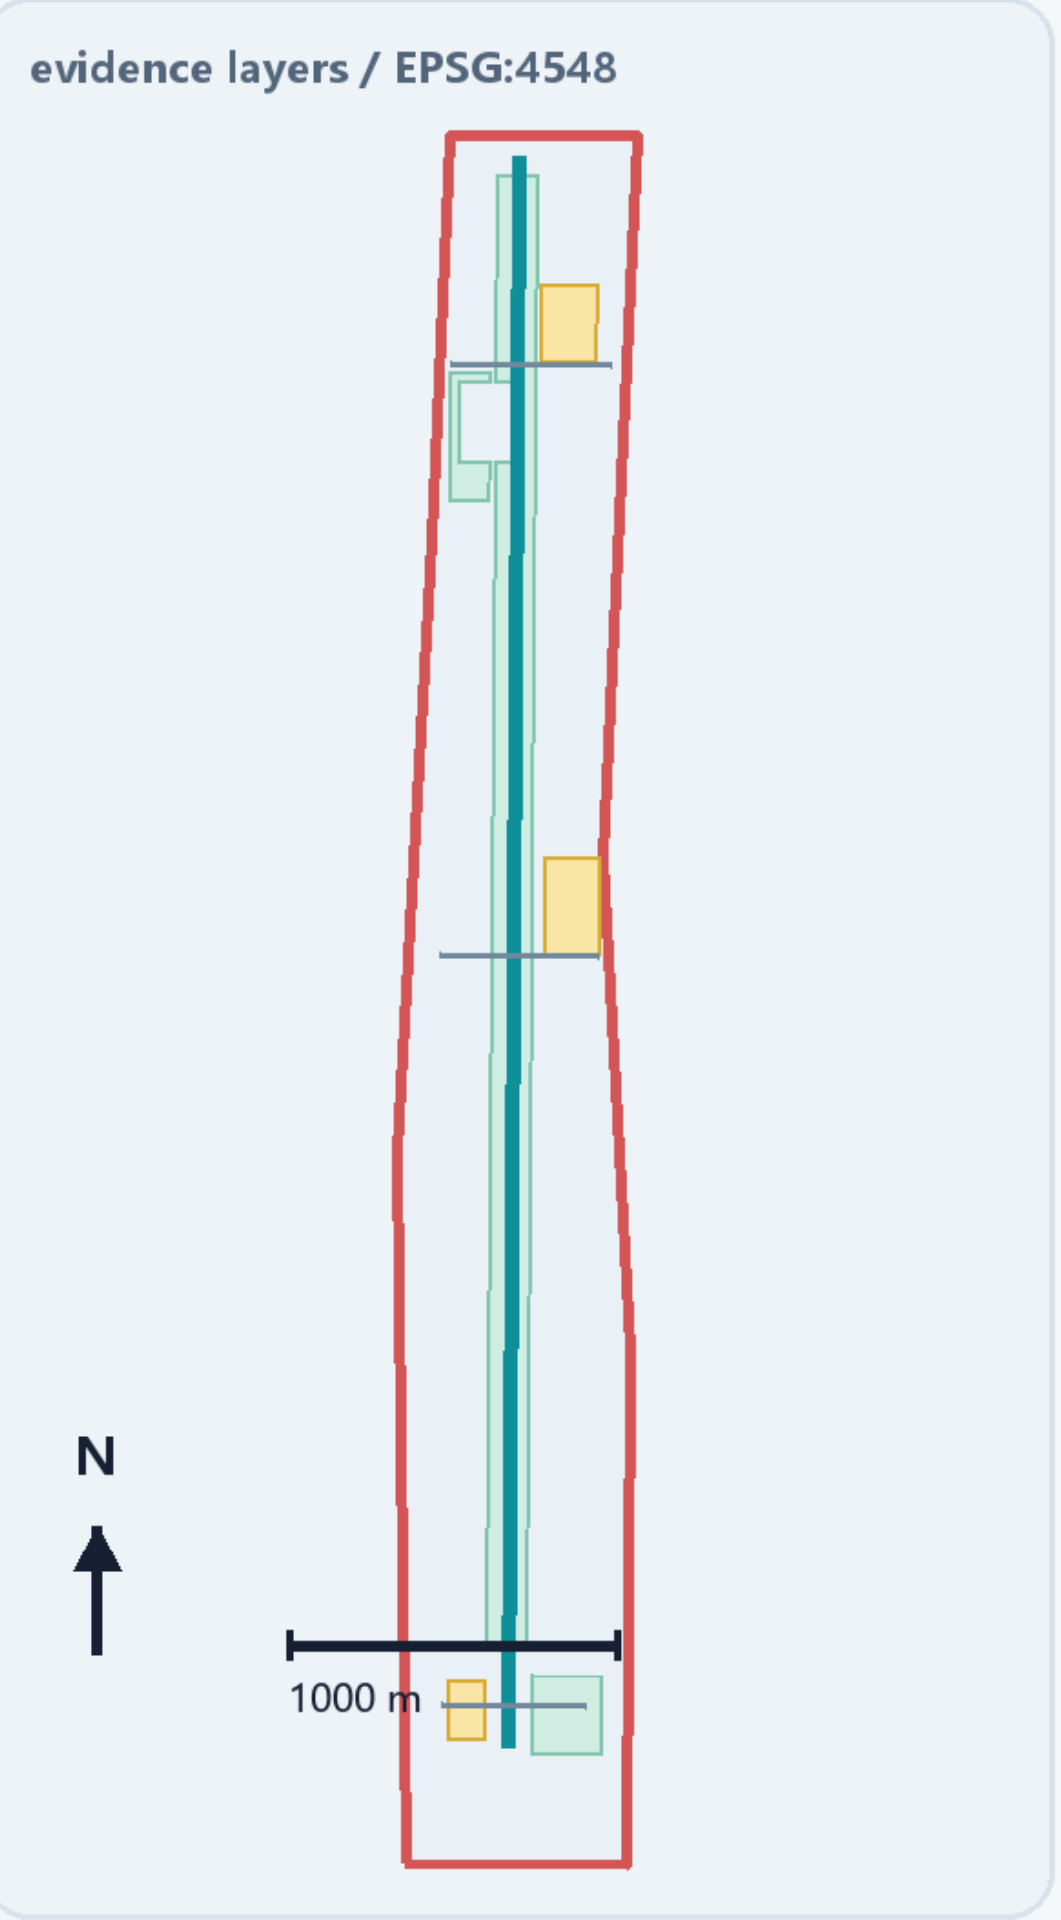

数据来源: metrics.json + geometry/*.geojson
方法: 当前几何由 EPSG:4326 转 EPSG:4548; unknown 控制项不以数值填充

当前结构化工作值

site 面积	11412825.386	sqm
绿地比例	17.16%	ratio
公共空间比例	3.19%	ratio
道路中心线	11566.053	m
shared-cut 类别	4	类
分期数量	3	期

残差审计 / geometry residuals

land-use gap
0.000827 sqm
site 外溢
0.000053 sqm
symmetric-difference
0.000880 sqm

待确认控制项 / unknown controls

FAR · 建筑高度 · 退线 · 建筑密度

原因: 官方控制条件、现场测绘、权属与专项资料未提供。

替换条件 / replacement rule

收到 official polygon 后, 整体替换 site/key areas, 重算面积、覆盖、道路、蓝绿、公共空间、分期, 并重跑: BOUNDARY_TRUST / KEY_AREAS_TRUST 以及 LAND_USE_TOPOLOGY。
数值残差不是 survey-level exact; 无内部空洞。

official_boundary=false / provisional

Phase 0 / 先缝合

历史—蓝绿—慢行主缝; 先做可达性、连续性和公众解释。

Phase 1 / 再试验

原点社区验证课堂—原型—展示—反馈; 人工复核与可退出。

Phase 2 / 后扩展

向两端重点区扩展创新与文化接口; 不承诺容量、投资或运营主体。

AI 场景底线

开源学堂、河岸实验室、智行生活剧场; AI 不做人脸识别、不自动执法、不替代规划/法律/医疗判断。

指标、未知与替换条件

当前结构化 work values: site 11,412,825.386 sqm · green 17.16% · public 3.19% · roads 11,566.053 m · 4 land-use classes · 3 phases。

未知控制项: FAR、建筑高度、退线、建筑密度、道路红线、停车/市政/算力容量、权属、投资、招商、政策与运营主体; 原因是官方控制条件、现场测绘、权属和专项资料未提供。

收到 official polygon 后, 整体替换 site boundary 与三个 key areas, 重算面积、覆盖、建筑、道路、蓝绿、公共空间和分期, 并重跑 BOUNDARY_TRUST、KEY_AREAS_TRUST、LAND_USE_TOPOLOGY。当前所有数值残差均是几何计算信号, 无内部空洞, 不代表真实测绘精度。