

智轨京张 The AI Line · 一脊十二站 · 三区两翼

总体概念：一脊十二站 · 三区两翼 —— 智轨京张 The AI Line

以京张遗址公园为“绿脊”，以十二座 AI 场景车站重构百年铁路站点记忆，串联三大重点区与两翼协同网络


百年京张文化带

都市AI生活体验带


AI融合创新带

五大功能：AI全栈自主创新体系 · 世界级AI创新生态 · AI+场景赋能新范式 · 智能化AI活力城市 · AI治理全球话语权

智轨京张 · The AI Line
图 1 · 总体概念结构 site-overview

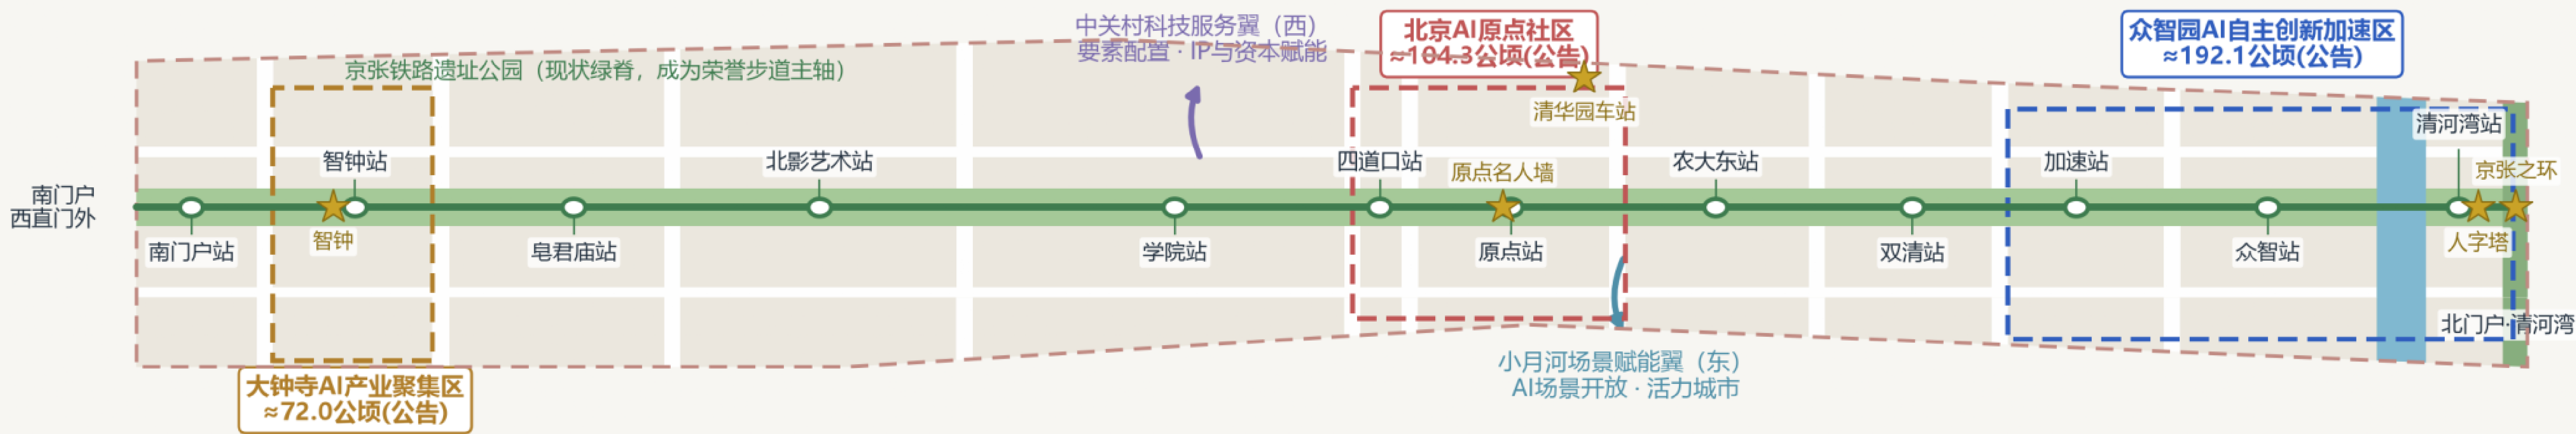


三层范围工作框架

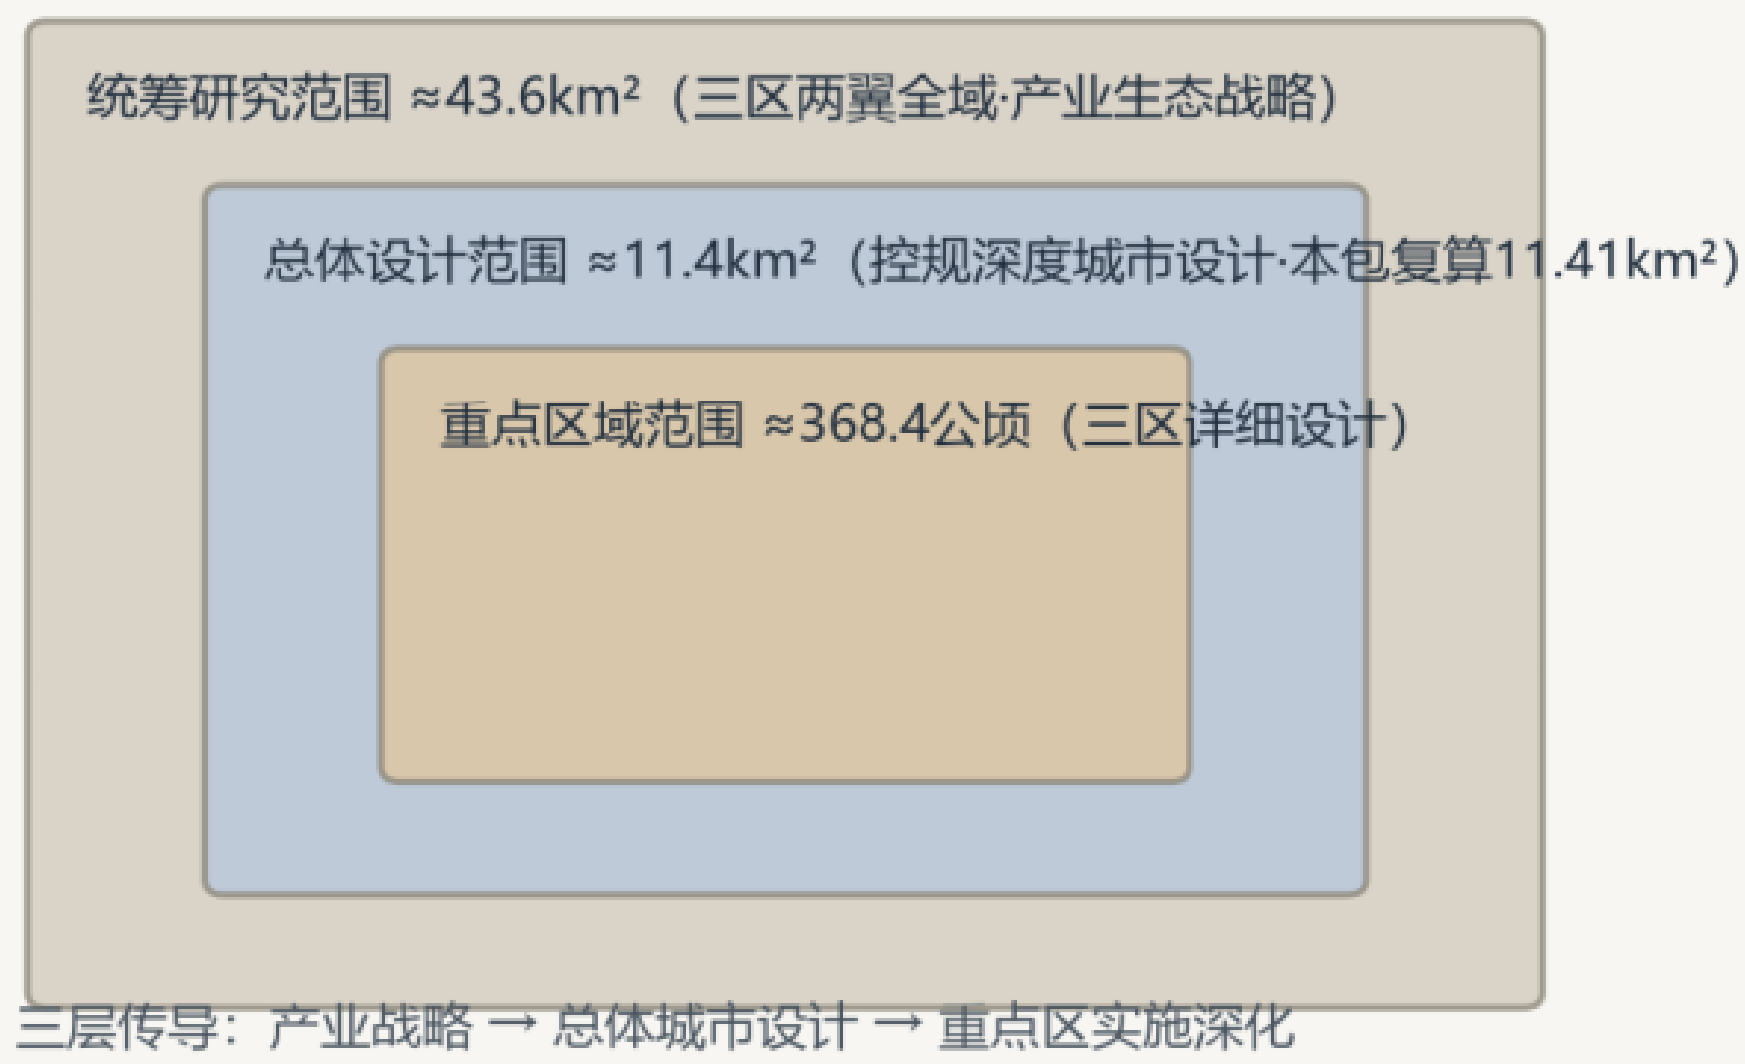


三层传导：产业战略 → 总体城市设计 → 重点区实施深化

结构模式：一脊 · 十二站 · 三区 · 两翼

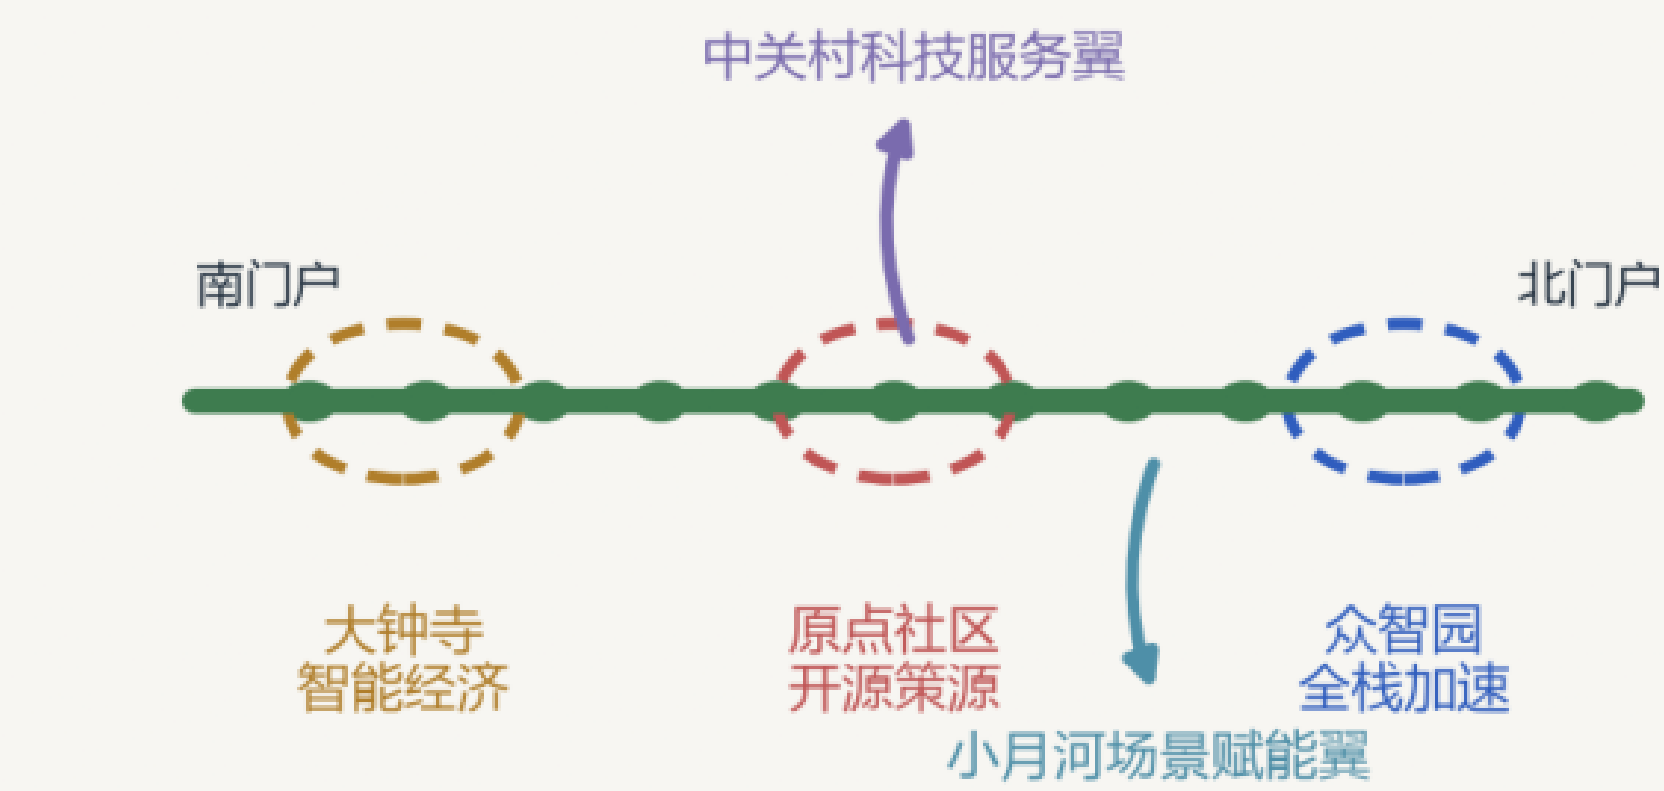

“站” = 站前广场 + AI场景 + 荣誉展示 + 社区运营单元
以百年铁路“车站”类型学重构 AI 时代公共空间

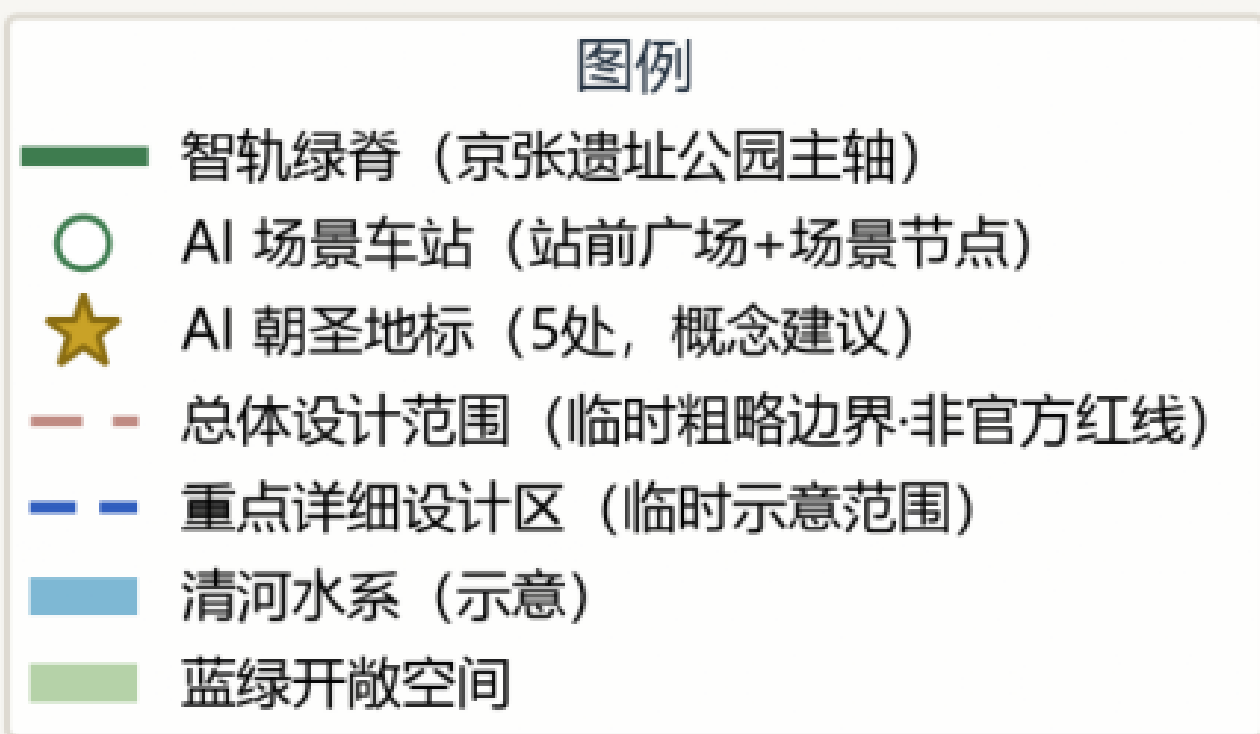

概念要点

- 纵向贯通：绿脊慢行主轴南起西直门外、北抵五环清河湾
- 东西缝合：车站单元向两侧社区/校区/园区开放
- 文化转译：铁路站点类型学 → AI 公共空间组件体系

总体概念

绿脊：京张遗址公园荣誉步道主轴

十二站：站前广场+AI场景+荣誉展示

+社区运营的复合单元

三区：众智园/原点社区/大钟寺

两翼：中关村科技服务翼

+小月河场景赋能翼

三大定位：百年京张文化带

都市AI生活体验带

AI融合创新带


临时粗略边界(provisional_rough)：范围线与重点区仅为公告文字四至推定的示意约束，非官方红线；官方矢量红线补齐后所有面积与图面需整体复算。

图1 · 总体概念结构 · geometry/*.geojson


168个概念地块全覆盖分区 · 站城织补 · 梯度更新

空间结构与用地布局：绿脊统领 · 站城织补 · 梯度更新

168个概念地块全覆盖分区（EPSG:4548复算）；主导功能自南向北：门户商务 — 智能消费 — 科教转化 — 开源策源 — 全栈加速

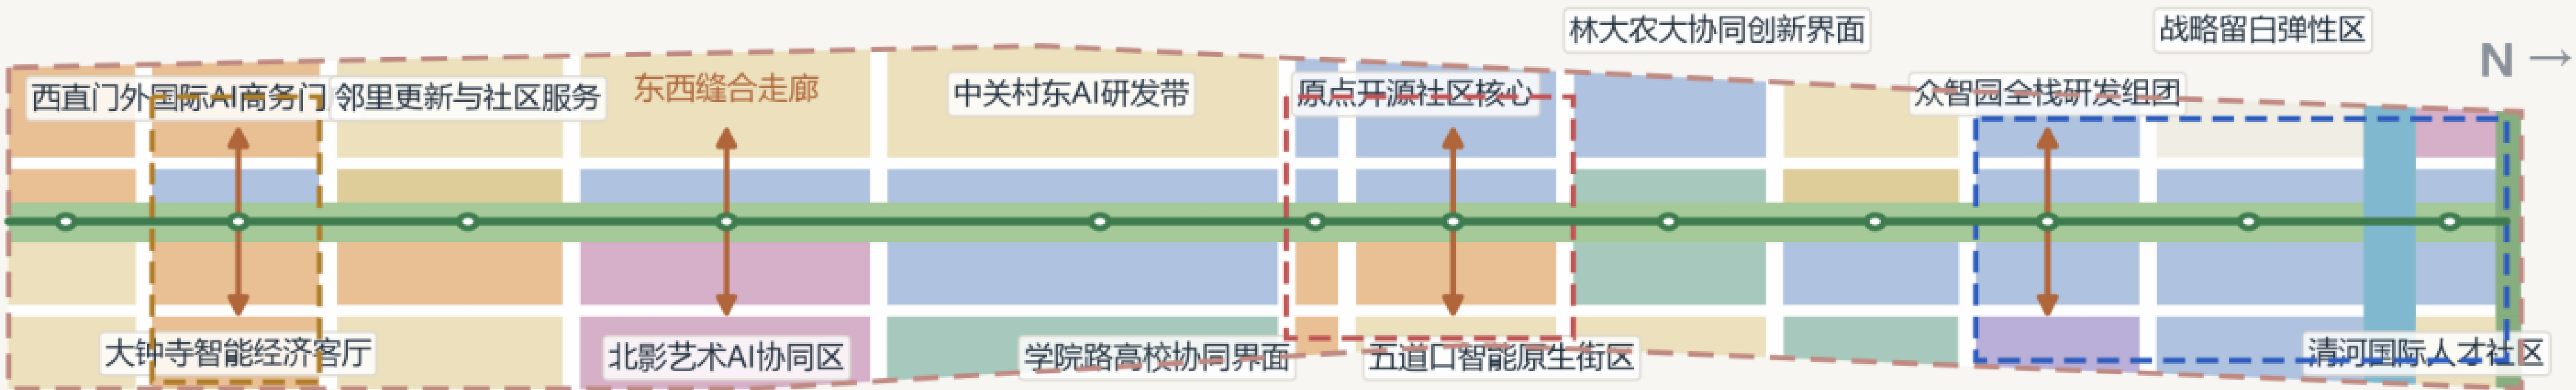


用地构成（复算面积 km²）

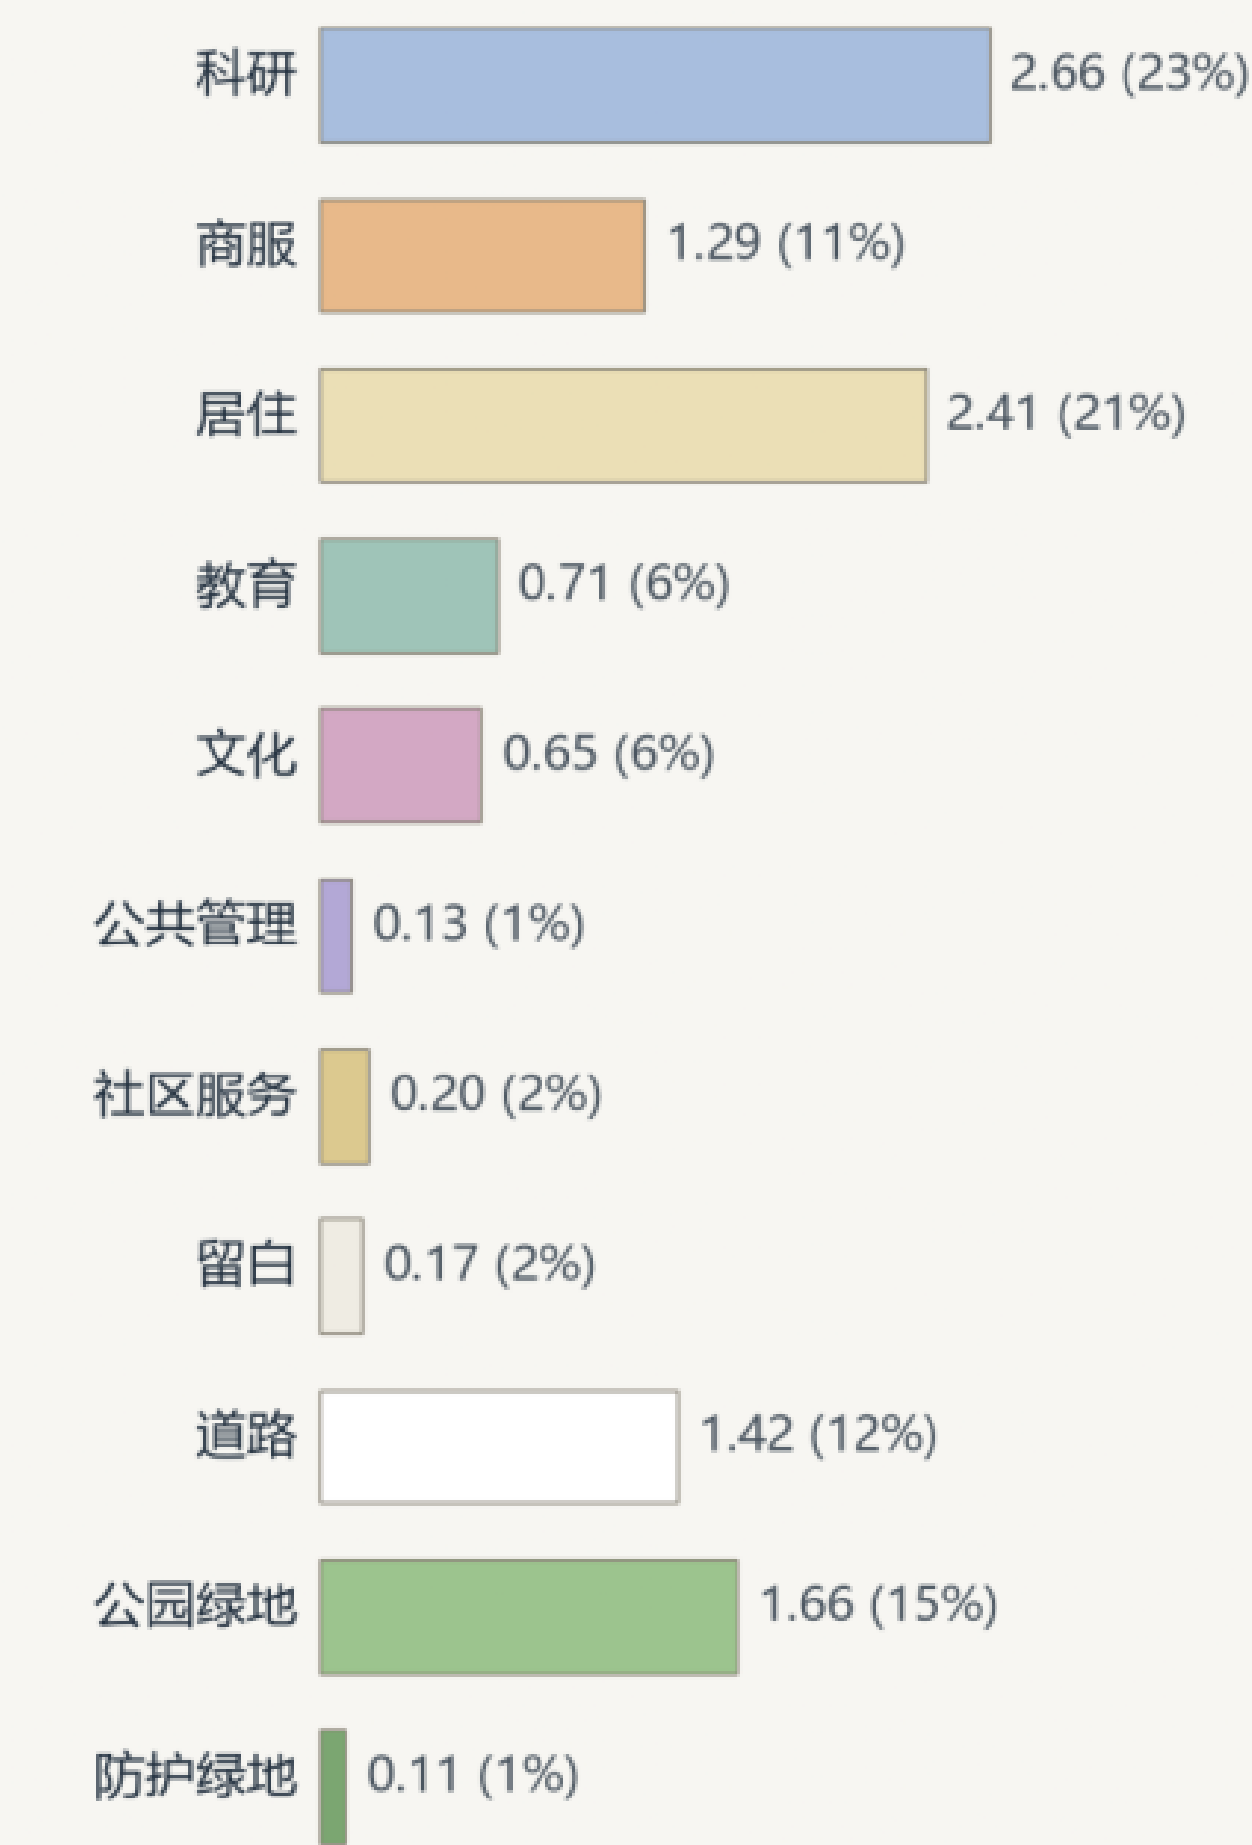

科研+商服+留白合计占比≈45%：
以产业空间供给回应“AI企业聚集”目标

东西向典型断面（原点社区段，西→东）

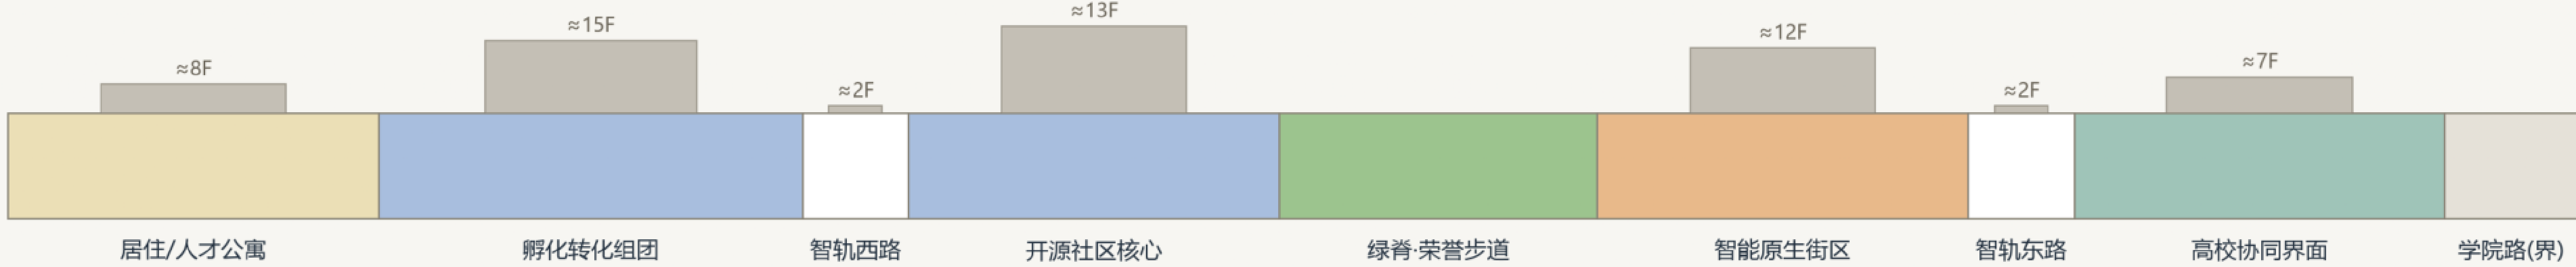

开发强度梯度：绿脊两侧低强度过渡 → 站点组团中高强度集聚；建筑高度体量的概念示意，正式指标以批准控规为准。

临时粗略边界(provisional_rough)：范围线与重点区仅为公告文字四至推定的示意约束，非官方红线；官方矢量红线补齐后所有面积与图面需整体复算。 数据来源：submissions/linzhuo606/the-ai-line/geometry/*.geojson · metrics.json （EPSG:4548 复算）

用地与更新

科研用地 2.66 km² （23%）
商服 1.29 km² · 居住 2.41 km²
公园绿地 1.66 km² · 留白 0.17 km²

更新框架：站点单元更新包
保留41% 改造26% 新建33%
（概念分类，待权属基数确认）

概念总建筑量 1615 万m²
概念毛容积率 1.42（非法定）

微循环+站城一体化+新型基础设施融合

交通慢行与蓝绿公共空间复合系统：贯通绿脊·缝合断点·站点即场景

南北贯通荣誉步道全线约9.7公里；东西向经知春路/北四环/成府路等走廊接驳两翼；12处站前广场即AI场景开放单元

智轨京张 · The AI Line
图 4 · 交通慢行与蓝绿系统 mobility-bluegreen

交通与市政


绿脊慢行贯通道全线约9.7公里
跨三环/四环下穿让行·跨清河慢行桥
跨五环上跨观景环（概念）

轨道接驳：大钟寺站四象限连通
五道口/清华东路西口双站接驳

市政：分布式能源+端侧算力舱
+城市传感数据治理框架
（容量测算待官方底数）



绿脊慢行贯通剖面（南→北）：断点缝合策略

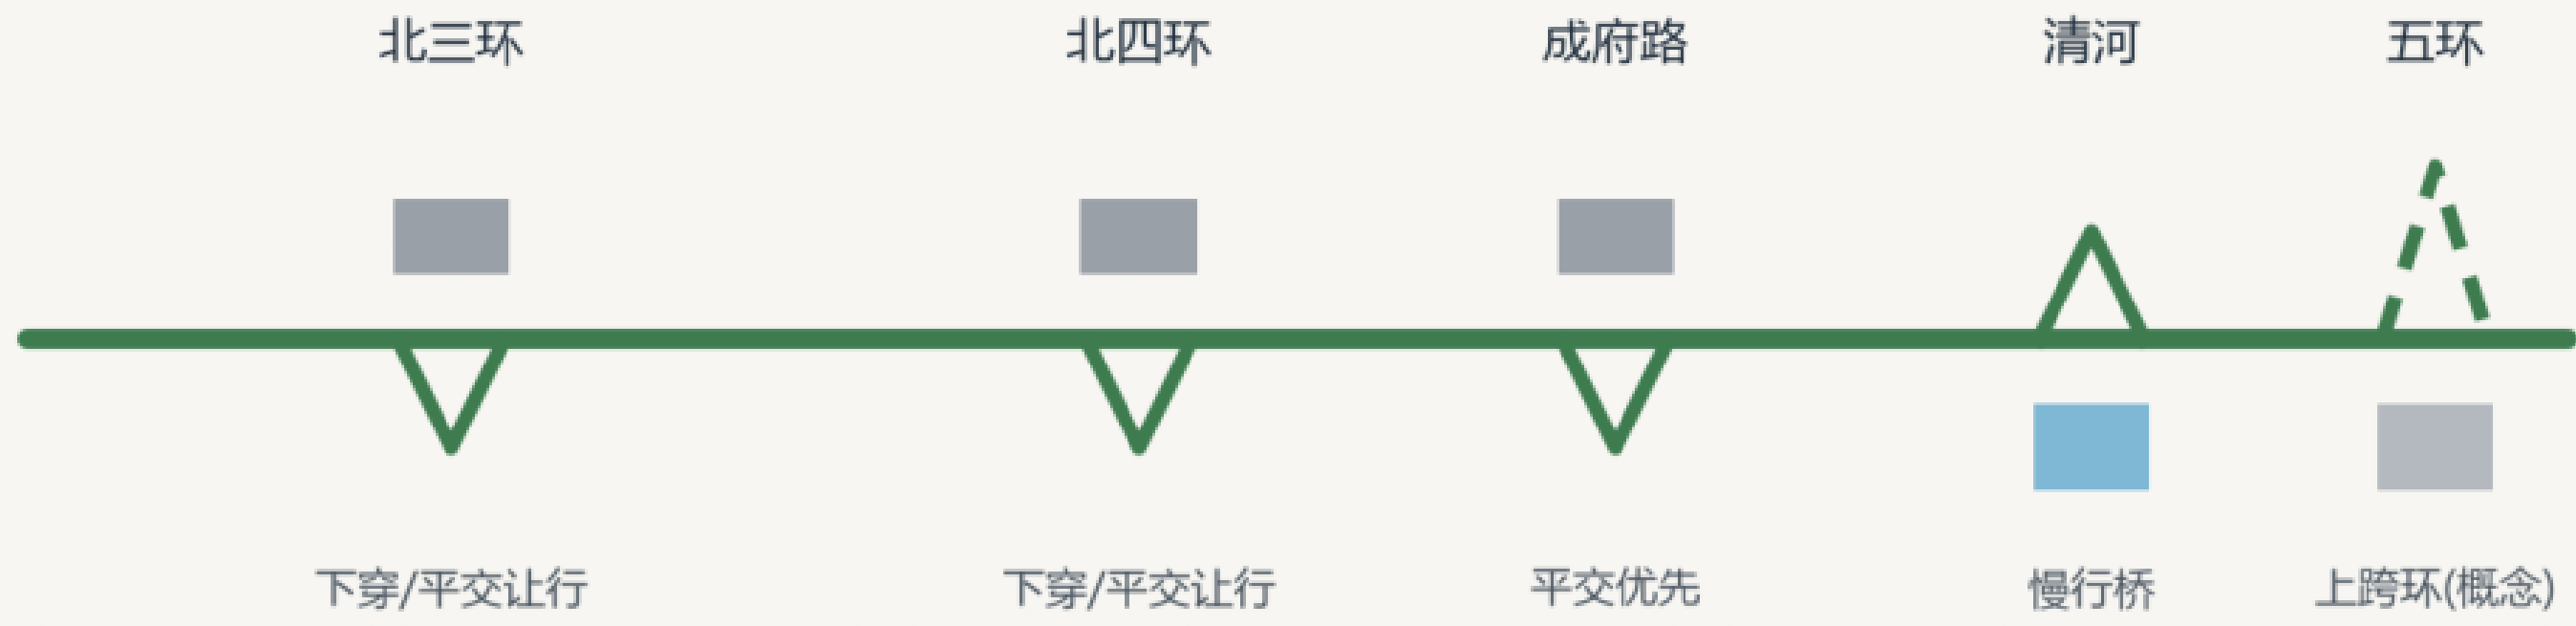

原则：慢行连续优先；车行走廊在绿脊处让行/立体分离。具体工程形式（桥/隧/下穿）均为概念建议，需专业论证。



站点 × AI 场景主题（南→北）

- | | |
|--------------------|-------------------|
| · 南门户站 · 城市AI问询与导览 | · 智钟站 · 智能终端/内容消费 |
| · 皂君庙站 · 社区健康哨点 | · 北影艺术站 · 生成式艺术展场 |
| · 学院站 · AI+教育实验舱 | · 四道口站 · 机器人配送测试道 |
| · 原点站 · 开源市集/名人墙 | · 农大东站 · 校园共创快闪 |
| · 双清站 · 能碳智能体试点 | · 加速站 · 自动驾驶接驳枢纽 |
| · 众智站 · 全栈中试展示 | · 清河湾站 · 低空物流试验窗口 |

临时粗略边界(provisional_rough): 范围线与重点区仅为公告文字四至推定的示意约束，非官方红线；官方矢量红线补齐后所有面积与图面需整体复算。 数据来源：submissions/linzhuo606/the-ai-line/geometry/*.geojson · metrics.json （EPSG:4548 复算）

临时粗略边界(provisional_rough): 范围线与重点区仅为公告文字四至推定的示意约束，非官方红线；官方矢量红线补齐后所有面积与图面需整体复算。

图4 · 交通慢行与蓝绿系统 · roads/constraints.geojson

贯通绿脊 · 荣誉步道 · 站前广场体系

交通慢行与蓝绿公共空间复合系统：贯通绿脊 · 缝合断点 · 站点即场景

南北贯通荣誉步道全线约9.7公里；东西向经知春路/北四环/成府路等走廊接驳两翼；12处站前广场即AI场景开放单元



智轨京张 · The AI Line
图 4 · 交通慢行与蓝绿系统 mobility-bluegreen

蓝绿与公共空间


绿地率（复算）15.7%
公共空间率（复算）5.3%
绿脊+清河绿廊+防护绿带
+六处口袋公园三级网络

荣誉步道：全线线性公共空间
十二处站前广场即场景开放单元

无障碍之线（盲人作者定义）：
导引带全线连贯约9.7公里
36处声响信号+9处安全岛
16处触觉模型+开源模型库

组件库V2（作者评审重构·五定律）：
站亭12座（五大站含卫生间）
座椅间隔≤50米（约130处）
问询柱/音频锚点（多语言）
店铺功能牌（首创·门侧1.35米）
智慧杆件/触觉模型台
贴标件已删除，只留标准接口

绿脊慢行贯通剖面（南→北）：断点缝合策略

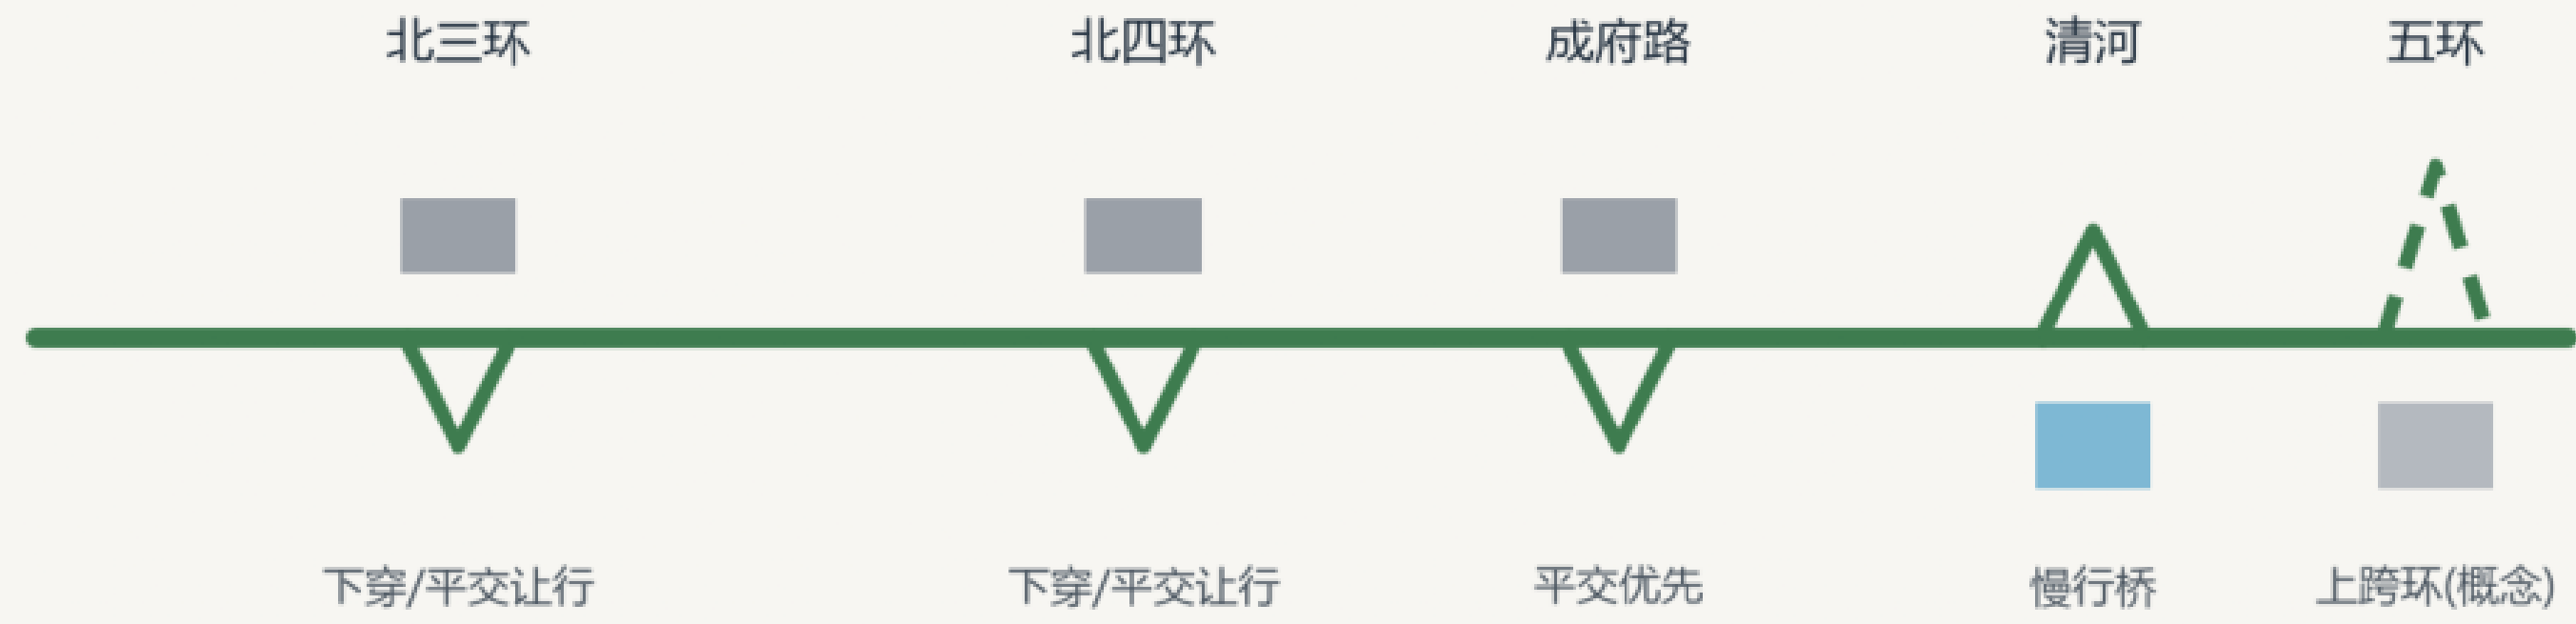

原则：慢行连续优先；车行走廊在绿脊处让行/立体分离。具体工程形式（桥/隧/下穿）均为概念建议，需专业论证。



站点 × AI 场景主题（南→北）

- | | |
|--------------------|-------------------|
| · 南门户站 · 城市AI问询与导览 | · 智钟站 · 智能终端/内容消费 |
| · 皂君庙站 · 社区健康哨点 | · 北影艺术站 · 生成式艺术展场 |
| · 学院站 · AI+教育实验舱 | · 四道口站 · 机器人配送测试道 |
| · 原点站 · 开源市集/名人墙 | · 农大东站 · 校园共创快闪 |
| · 双清站 · 能碳智能体试点 | · 加速站 · 自动驾驶接驳枢纽 |
| · 众智站 · 全栈中试展示 | · 清河湾站 · 低空物流试验窗口 |

临时粗略边界(provisional_rough): 范围线与重点区仅为公告文字四至推定的示意约束，非官方红线；官方矢量红线补齐后所有面积与图面需整体复算。 数据来源：submissions/linzhuo606/the-ai-line/geometry/*.geojson · metrics.json（EPSG:4548 复算）

临时粗略边界(provisional_rough): 范围线与重点区仅为公告文字四至推定的示意约束，非官方红线；官方矢量红线补齐后所有面积与图面需整体复算。

图4 · 蓝绿公共空间视角 · green_space/public_space.geojson

一区一策 · 站城一体 · 拆改留并举

三处重点区域详细设计索引：一区一策 · 站城一体 · 拆改留并举

众智园=全栈加速（国家级集聚区）· 原点社区=开源策源（近校型街区）· 大钟寺=智能经济（城市型街区）

智轨京张 · The AI Line
图 3 · 重点区域 key-areas



重点区域

① 众智园：花园型全栈加速
一枢四团+治理与标准中心
+清河创新湾+战略留白

② 原点社区：近校型开源策源
西转化中开源东活力
低扰动更新+双站接驳

③ 大钟寺：城市型智能经济
一厅两坊+四象限连通
+智钟古今对话

临时粗略边界(provisional_rough)：范围线与重点区仅为公告文字四至推定的示意约束，非官方红线；官方矢量红线补齐后所有面积与图面需整体复算。 数据来源：submissions/linzhuo606/the-ai-line/geometry/*.geojson · metrics.json（EPSG:4548 复算）

临时粗略边界(provisional_rough)：范围线与重点区仅为公告文字四至推定的示意约束，非官方红线；官方矢量红线补齐后所有面积与图面需整体复算。

图3 · 重点区域索引 · key_areas.geojson

14张场景卡 · 5处朝圣地标 · 年度活动体系 · 长期运营

总体概念：一脊十二站 · 三区两翼 —— 智轨京张 The AI Line

以京张遗址公园为“绿脊”，以十二座 AI 场景车站重构百年铁路站点记忆，串联三大重点区与两翼协同网络


百年京张文化带

都市AI生活体验带


AI融合创新带

五大功能：AI全栈自主创新体系 · 世界级AI创新生态 · AI+场景赋能新范式 · 智能化AI活力城市 · AI治理全球话语权

智轨京张 · The AI Line
图 1 · 总体概念结构 site-overview

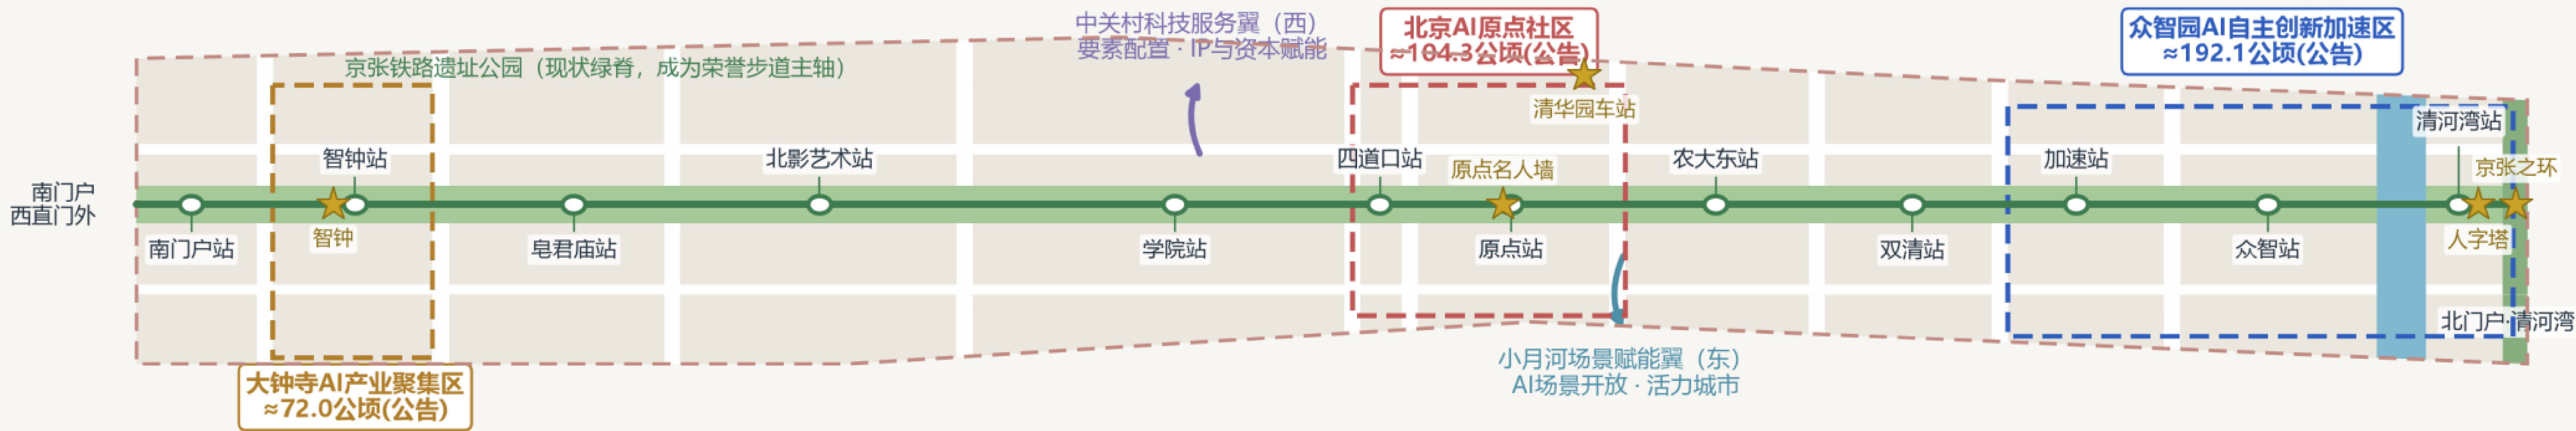


三层范围工作框架

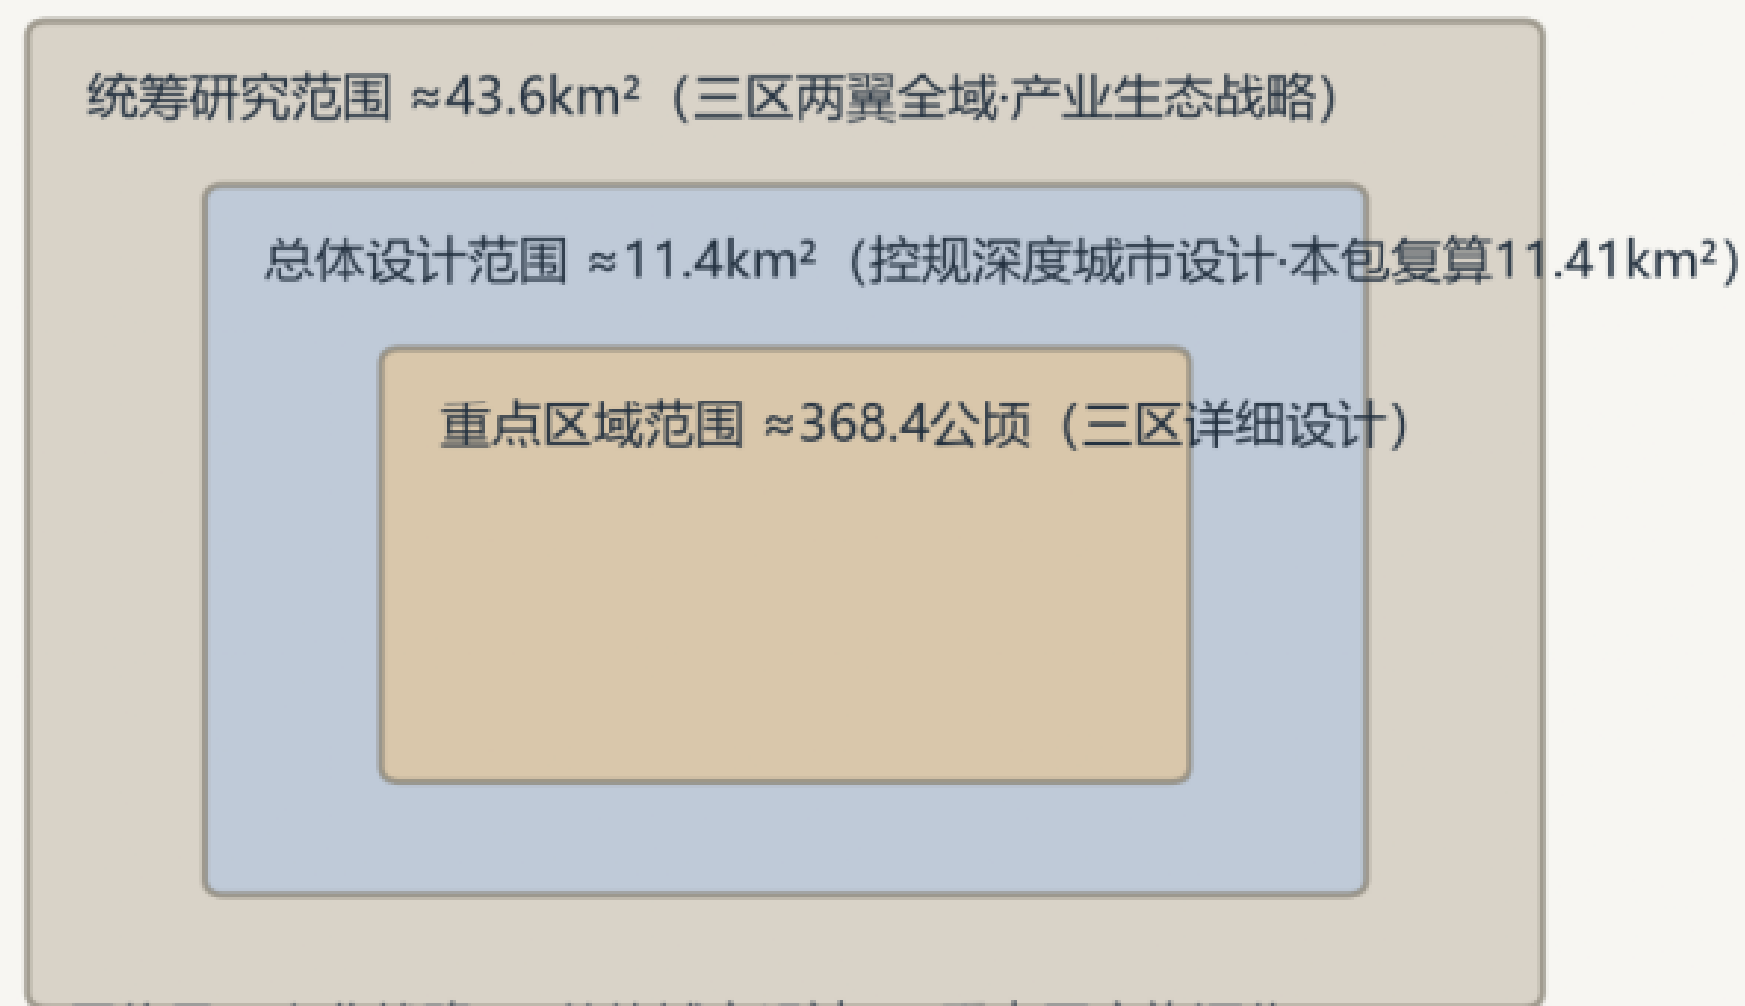


三层传导：产业战略 → 总体城市设计 → 重点区实施深化

结构模式：一脊 · 十二站 · 三区 · 两翼

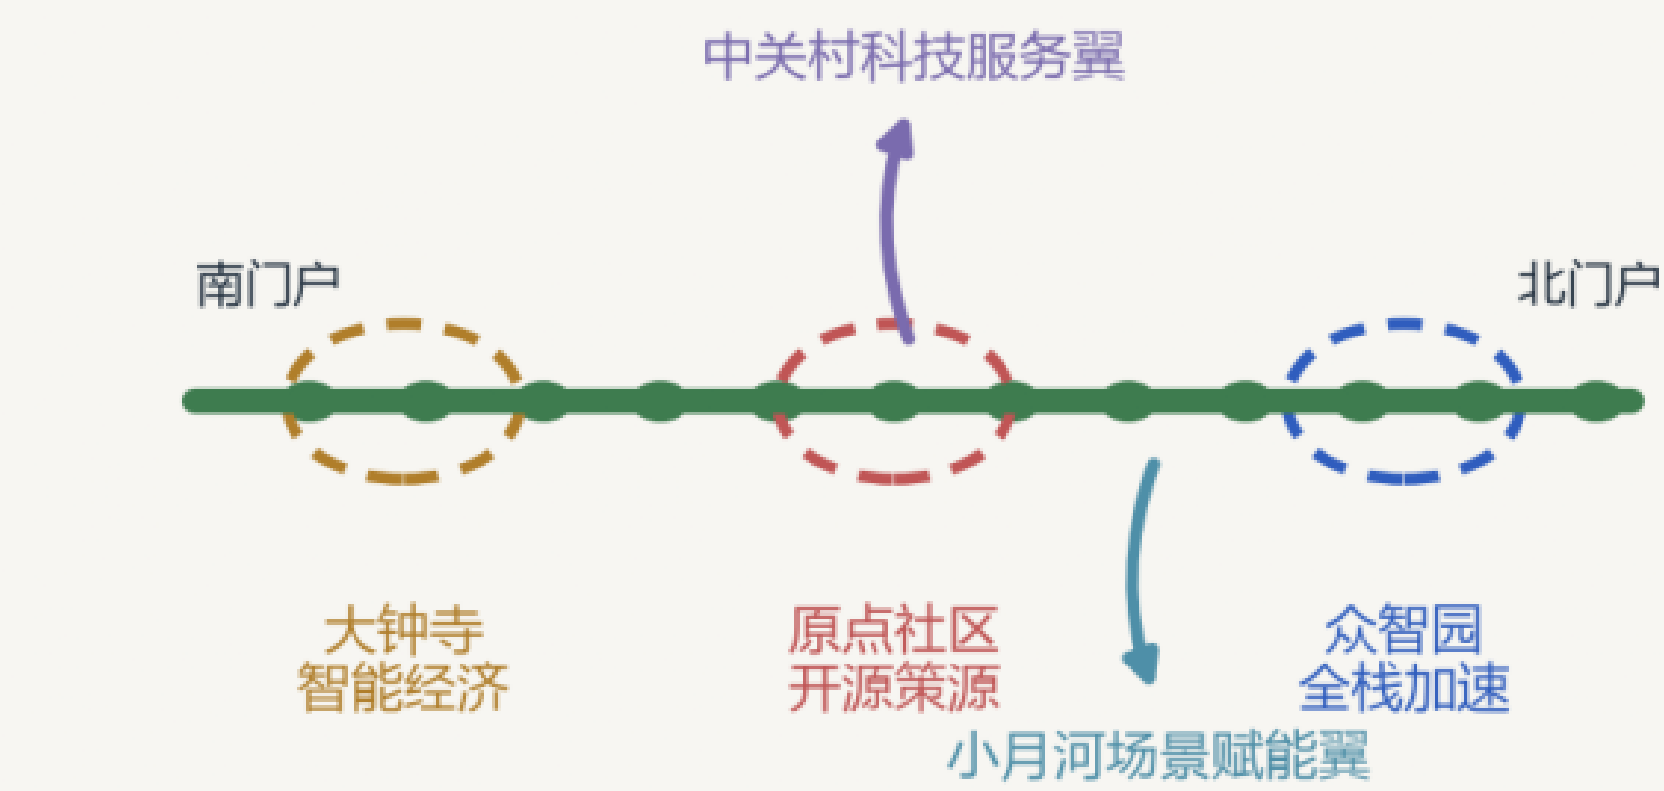

“站” = 站前广场 + AI场景 + 荣誉展示 + 社区运营单元
以百年铁路“车站”类型学重构 AI 时代公共空间

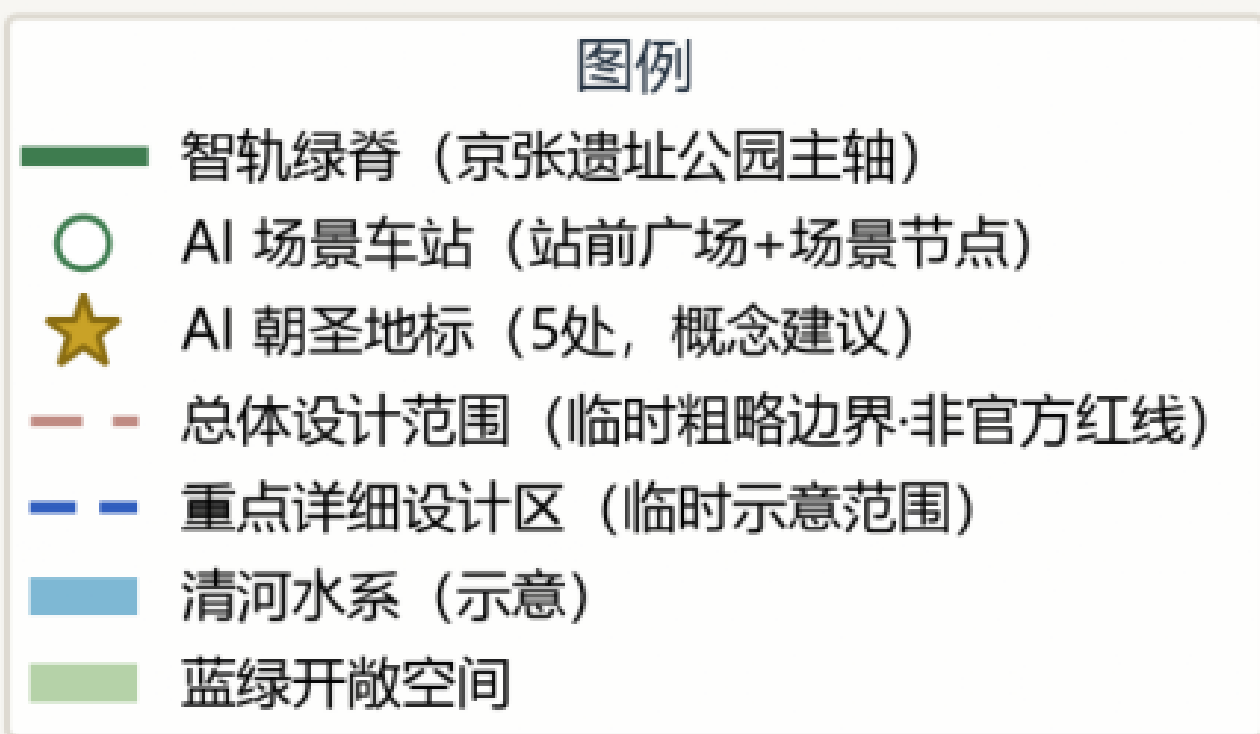

概念要点

- 纵向贯通：绿脊慢行主轴南起西直门外、北抵五环清河湾
- 东西缝合：车站单元向两侧社区/校区/园区开放
- 文化转译：铁路站点类型学 → AI 公共空间组件体系

场景与运营

14张场景卡（5个测试验证）：
问询导览/终端消费/健康哨点
艺术展场/教育实验舱/机器人测试道
开源市集/校园快闪/能碳智能体
自动驾驶接驳/全栈中试/低空物流
盲道连贯AI监测/无障碍伴行

五处地标：人字塔/原点名人墙
清华园车站时间机器/智钟/京张之环

运营：全球开发者大会+治理圆桌
+ 艺术双年展+开源之夜+鸣钟仪式

临时粗略边界(provisional_rough)：范围线与重点区仅为公告文字四至推定的示意约束，非官方红线；官方矢量红线补齐后所有面积与图面需整体复算。



场景节点见 public_space.geojson · SCENARIO_NODE

33项known指标可复算 · 23项任务全覆盖 · 四通道自检

指标复算与证据链：每个数字可回溯 · 每个结论可复核

全部空间指标由 GeoJSON 在 EPSG:4548 下复算并写入 metrics.json；矩阵与自检结果与正文互相引用

智轨京张 · The AI Line
图 5 · 指标证据 metrics-evidence

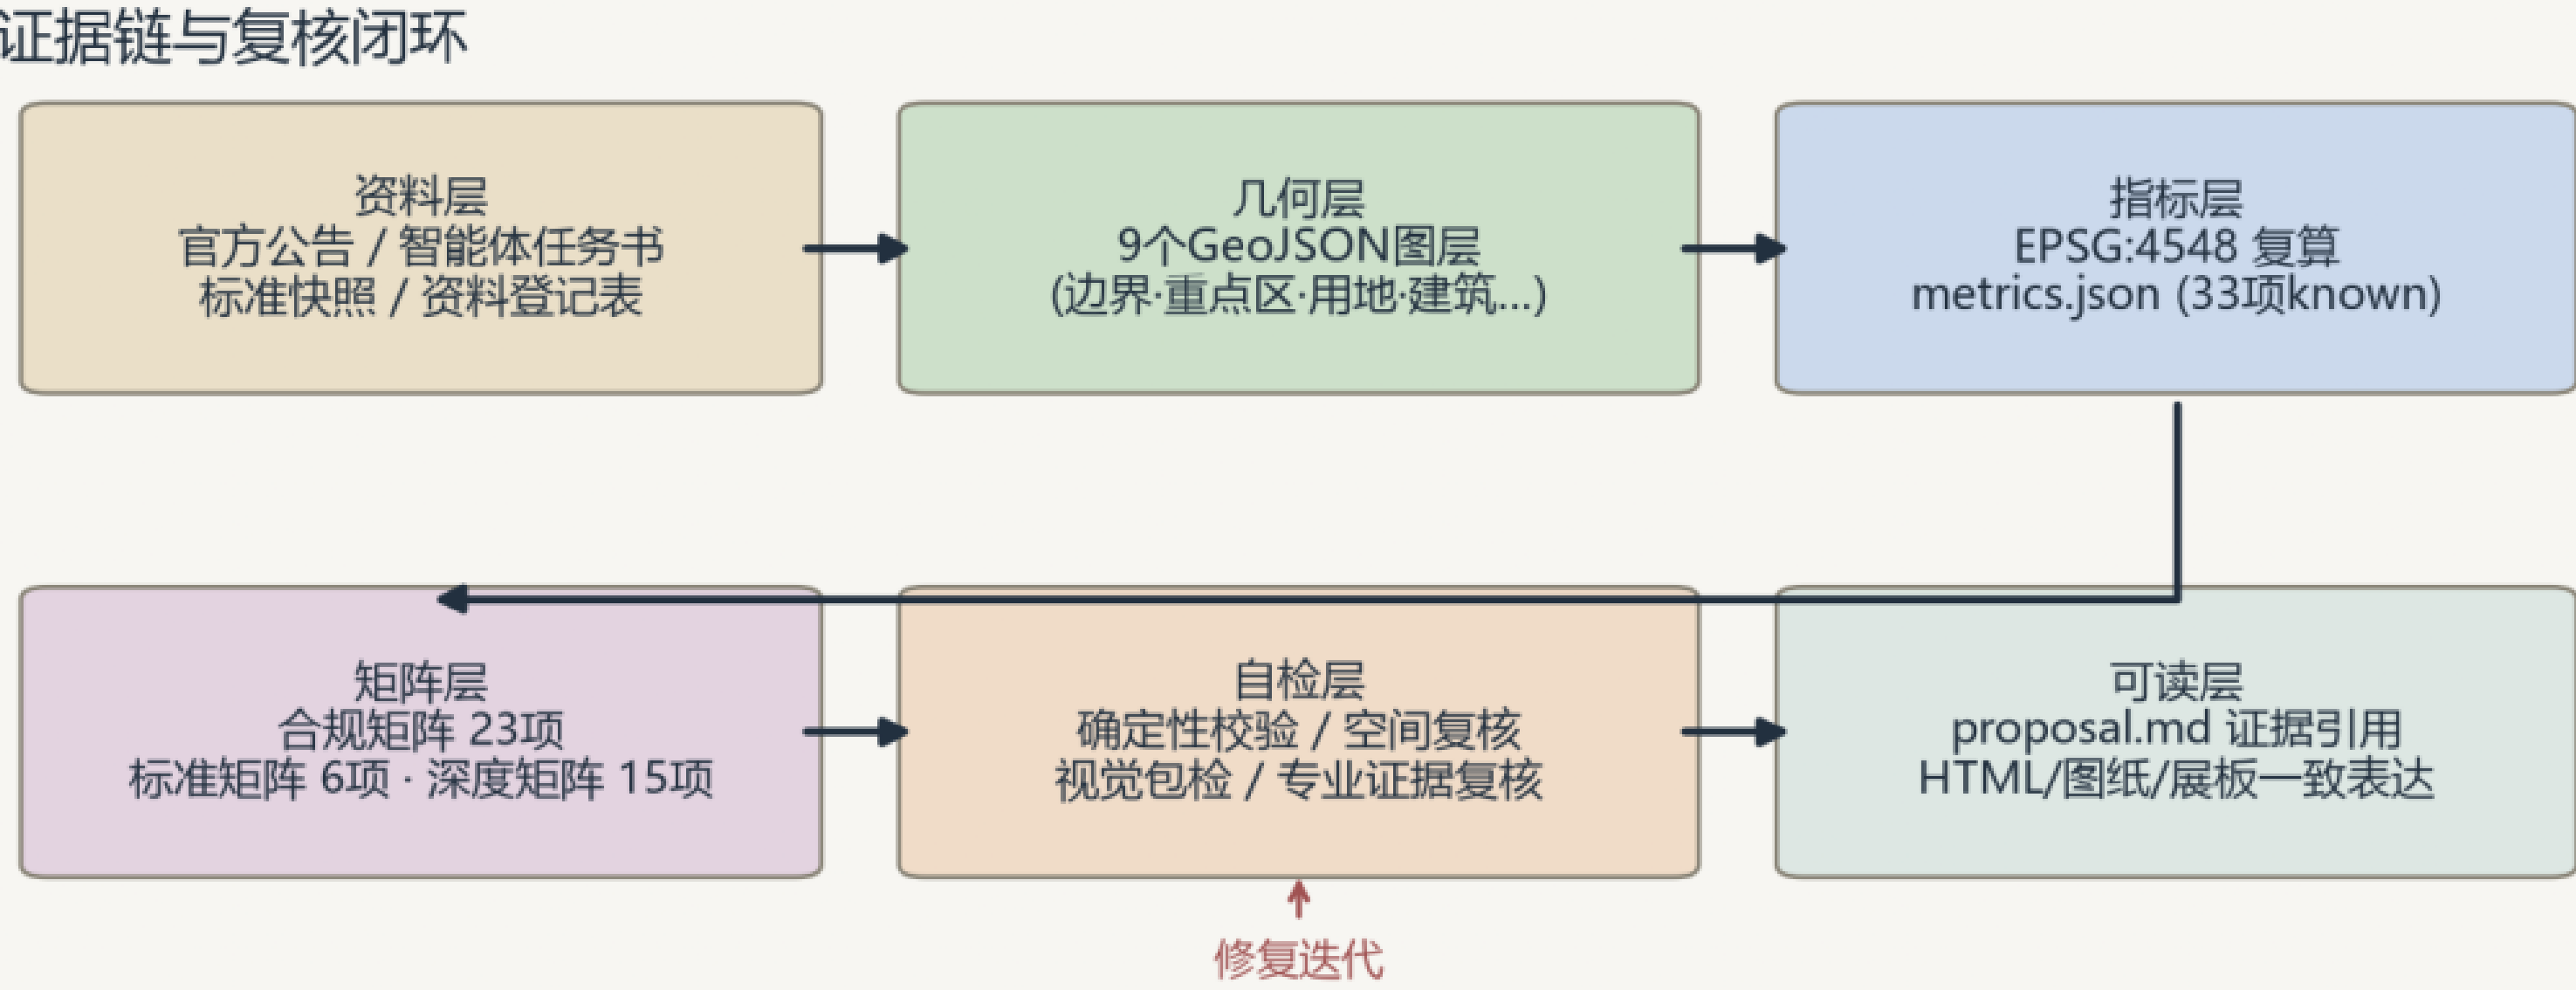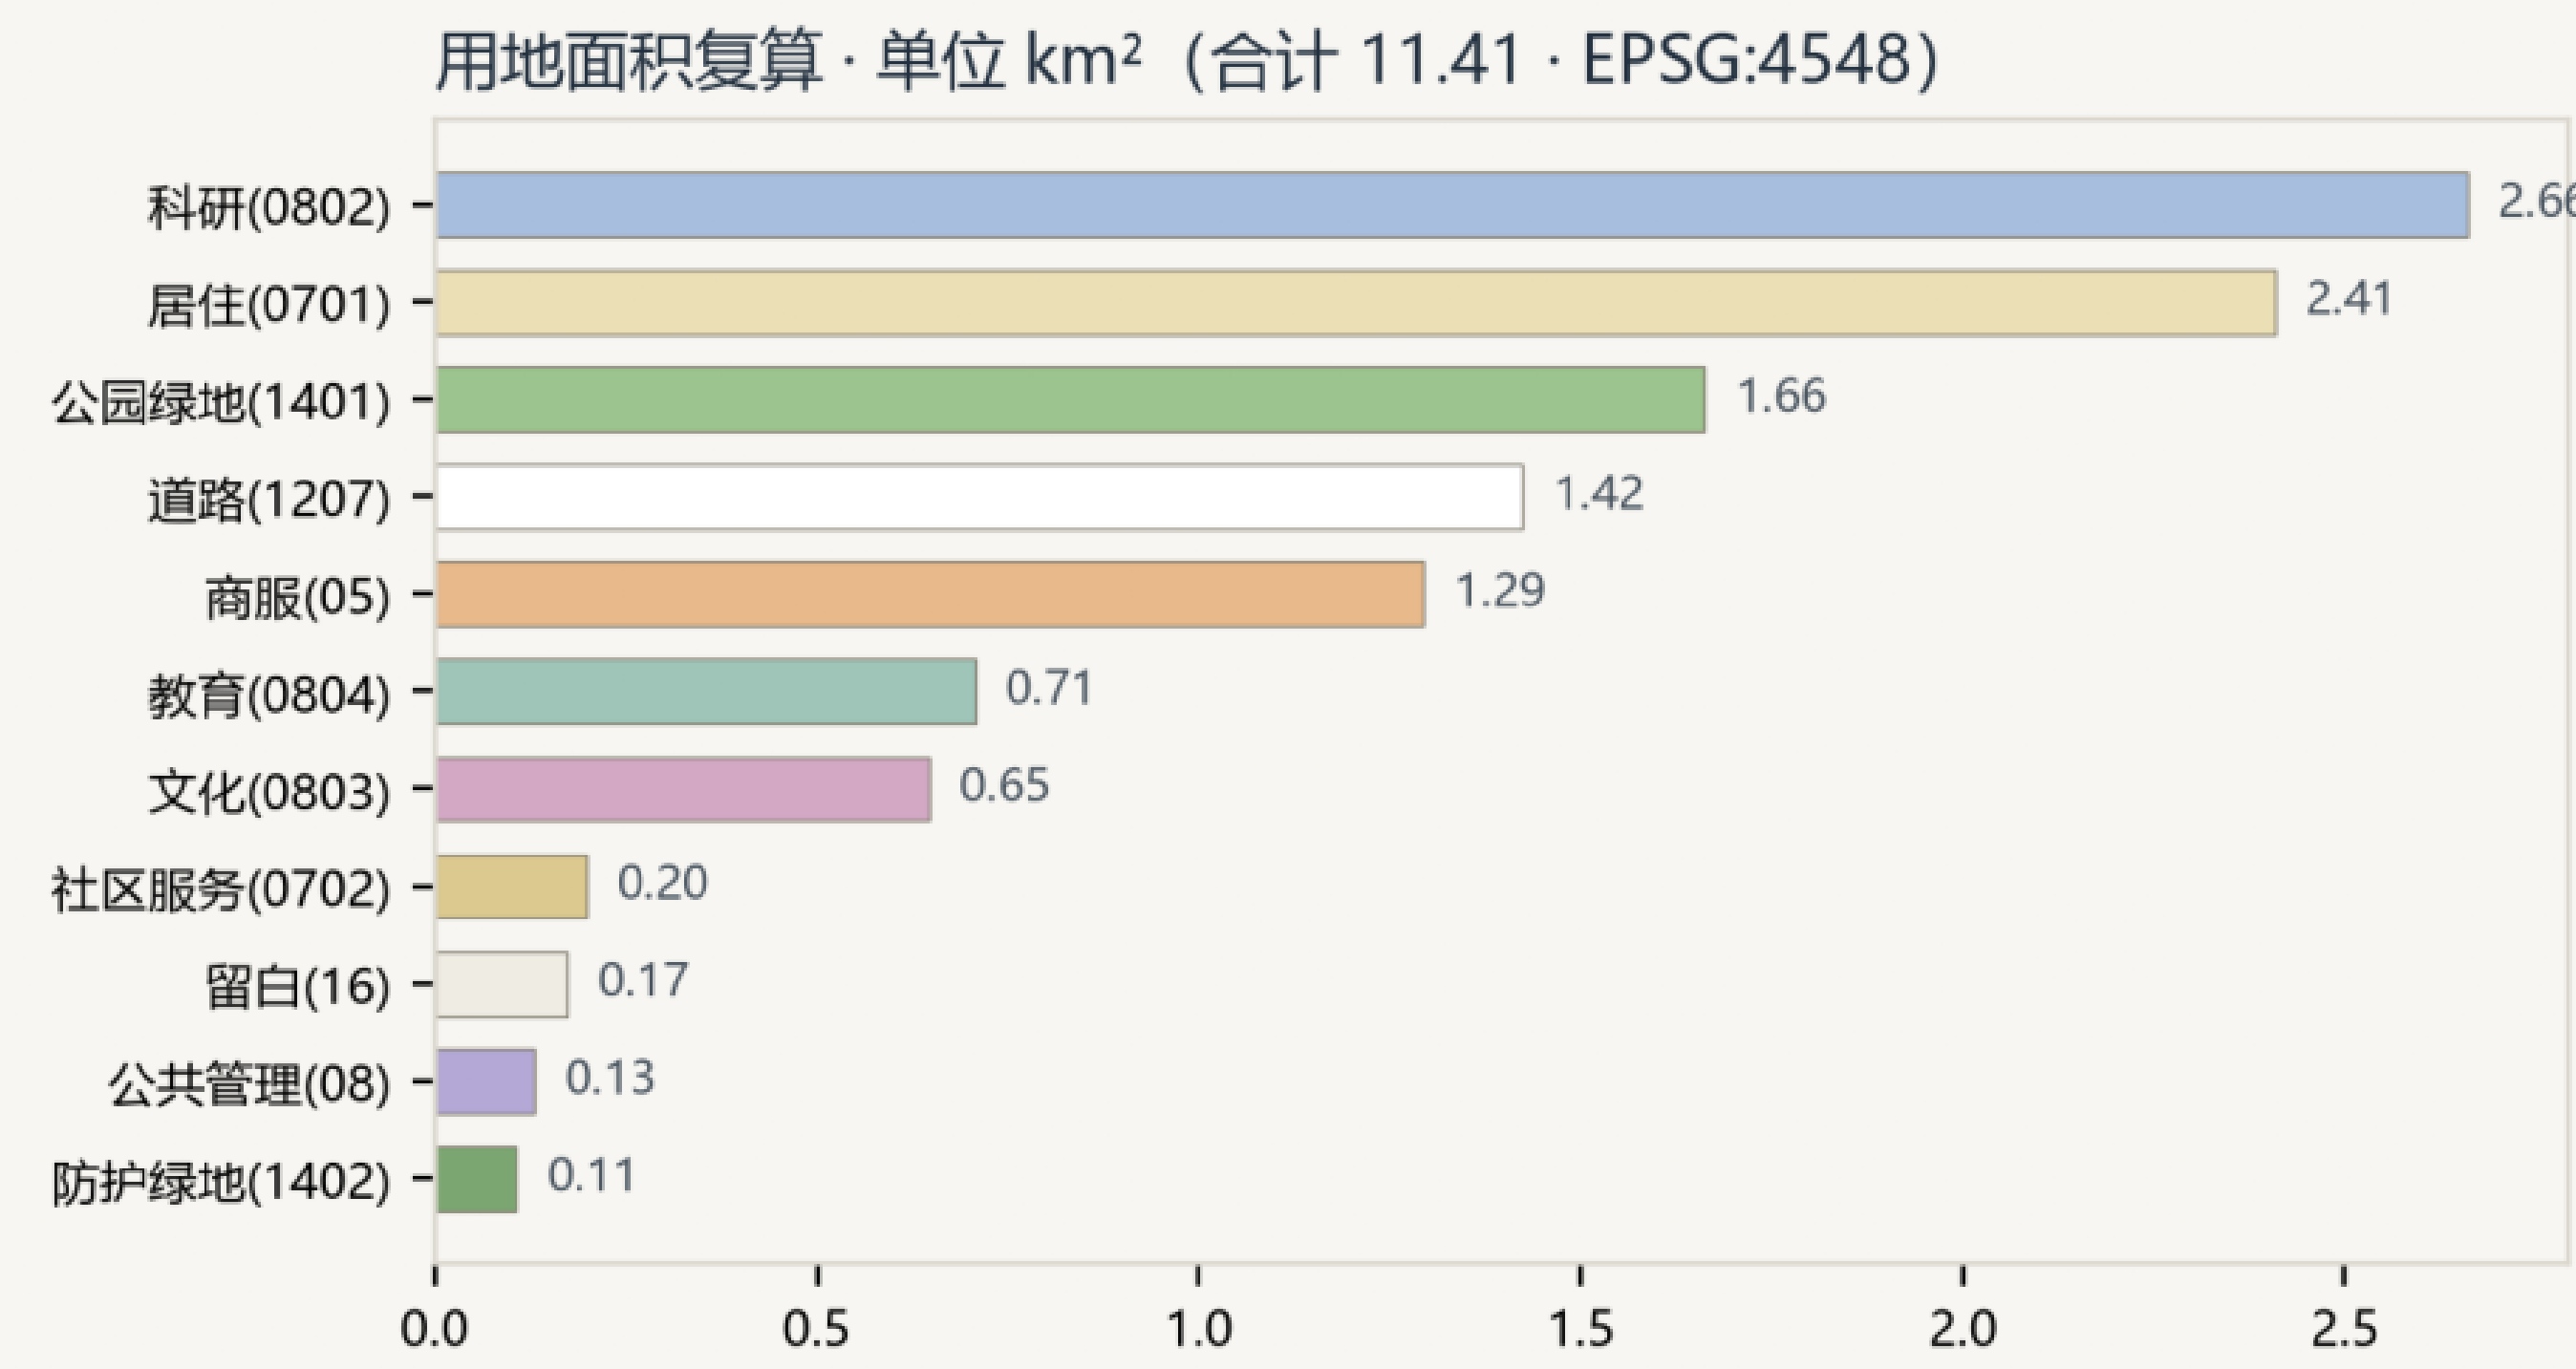

待确认官方控制条件（不伪装为审定指标）

指标/数据项	状态	补齐来源
法定容积率	待补	批准控规或正式任务书附件
建筑高度控制	待补	批准高度/航空/文保限高资料
现状建筑量底数	待补	官方测绘/权属数据
官方红线与三区精确范围	待补	资格预审文件图纸包(bkpmzb.com)

提交前自检状态

- ✓

确定性校验 · 结构/引用/矩阵
- ✓

空间复核 · 拓扑/面积/覆盖
- ✓

视觉包检 · 离线/指标一致
- ✓

专业证据复核 · 标准/深度

临时粗略边界(provisional_rough)：范围线与重点区仅为公告文字四至推定的示意约束，非官方红线；官方矢量红线补齐后所有面积与图面需整体复算。 数据来源：submissions/linzhuo606/the-ai-line/geometry/*.geojson · metrics.json （EPSG:4548 复算）

指标与合规

范围面积（复算） 11.41 km²
绿地率 15.7% · 公共空间率 5.3%

合规矩阵：公告1.3/1.4/1.5
+agent.1–6 共23项全覆盖
标准矩阵：5项强制标准 addressed
深度矩阵：15项全部 complete

自检：确定性/空间/视觉/专业
四通道全部通过

图5 · 指标证据 · metrics.json 与三矩阵

临时粗略边界(provisional_rough)：范围线与重点区仅为公告文字四至推定的示意约束，非官方红线；官方矢量红线补齐后所有面积与图面需整体复算。