


可建造的公共十字

一段可进入、可维护、可关闭、可恢复的建筑—公共空间

大钟寺剖切装配轴测 | 公共层先建，插件层可拆，证据层有人负责

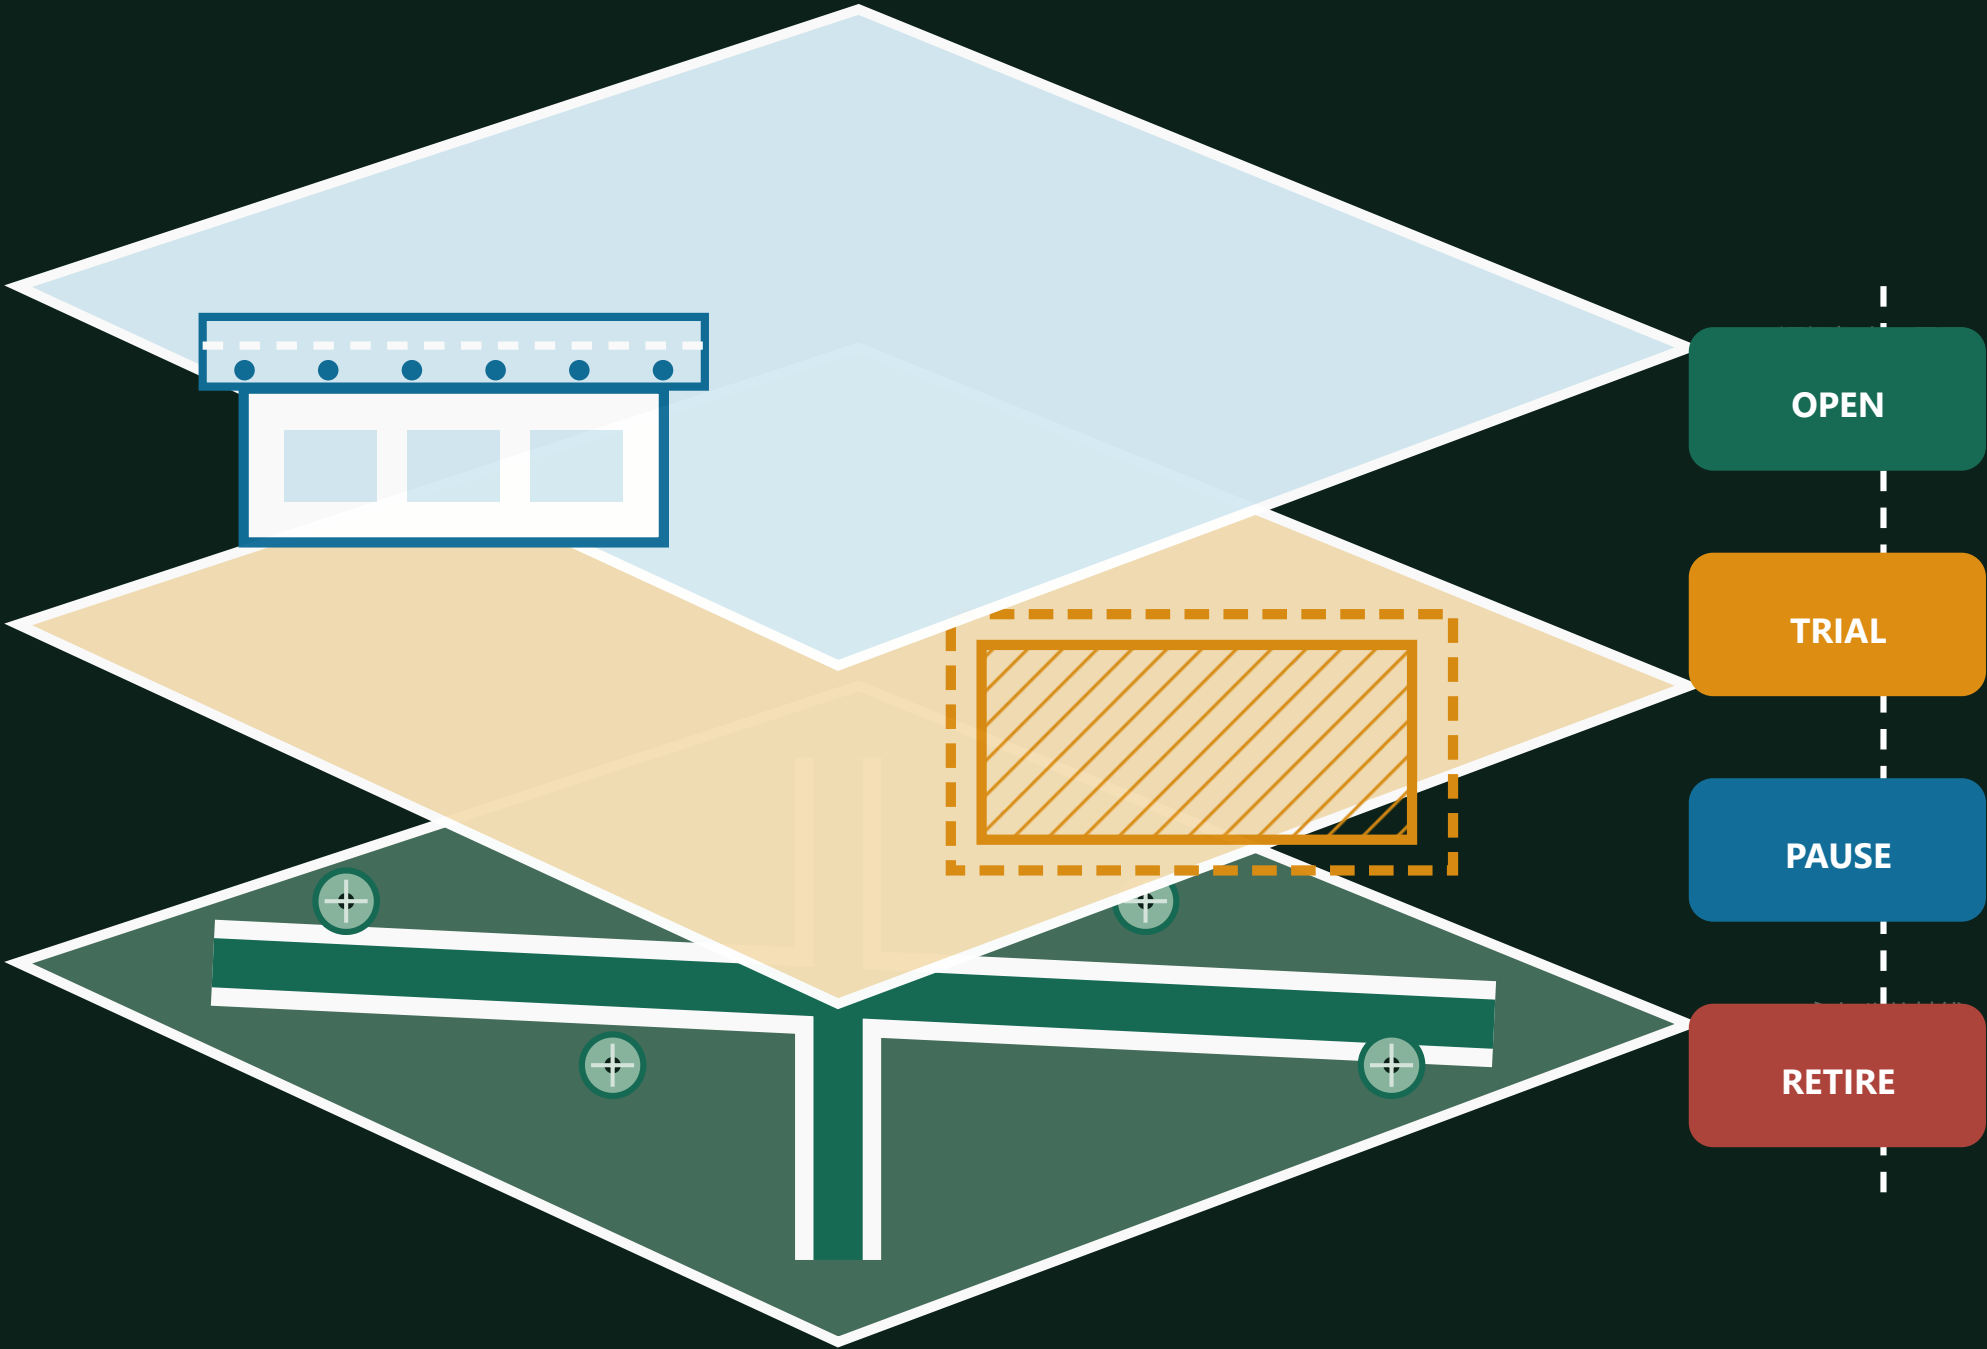


RETIRE: 设备沿独立后勤线撤出；公共十字、遮阴、蓝绿边界与人工门廊继续服务。

90秒评审路线

总体 → 三座地标 → 旗舰平面 → 节点 → 实施门

京张双答 | 不断线的公共十字

公共路线不被牺牲；AI只进入一侧；越线方案公开淘汰。

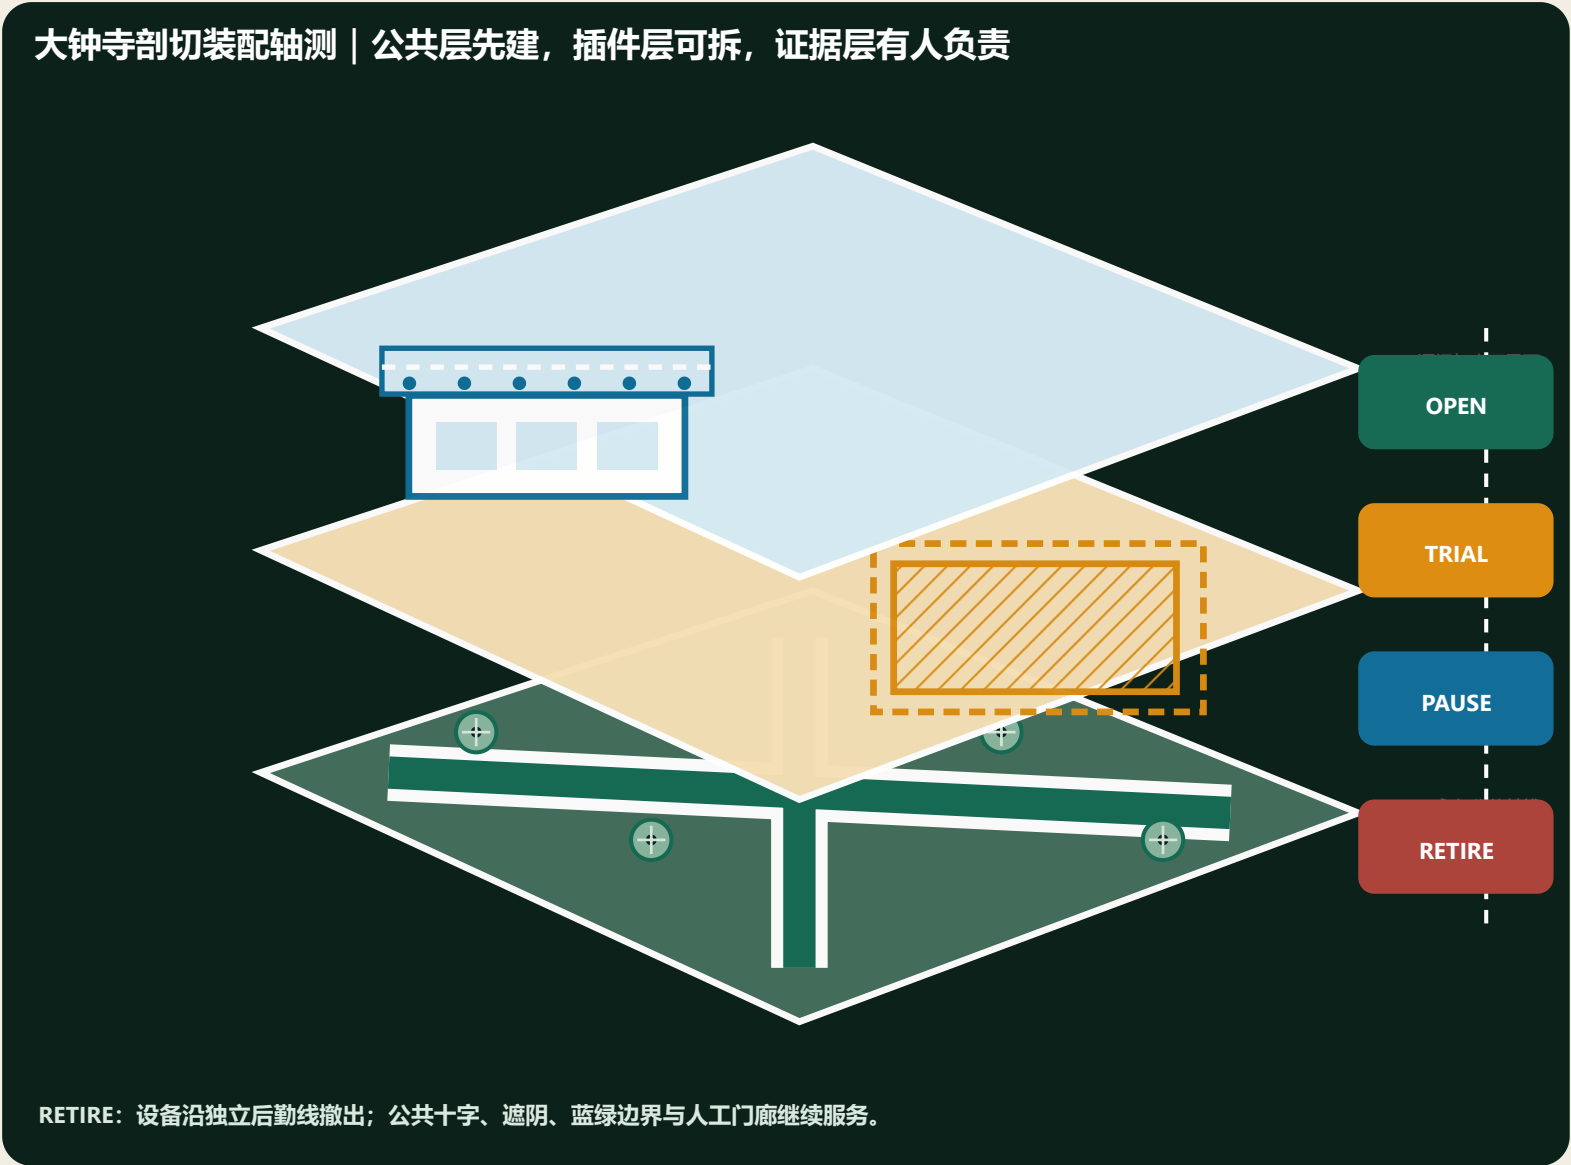

三个方案，一次否决

- ALT-A** **REJECT**
切断公共十字
- ALT-B** **REVISE**
监督与撤场碎片化
- ALT-C** **ADVANCE**
单侧可逆湾

GO NO-GO

0/8 PERMITS · 0/7 DAYS · 0/4 POSTS

设计原型完整，但试验不得开始。普通路线、候车和人工服务可独立运行。


T2	S2	S7	12/12	0
验真环	共译门	回执廊	测量契约	现场结果

资料、缺测与证据等级

公开城市关系可用；现状界面、结构与绩效待核验


可核验公开关系01

道路、轨道、水系、公园和已公开的京张背景；用于方向性关系，不替代测绘。

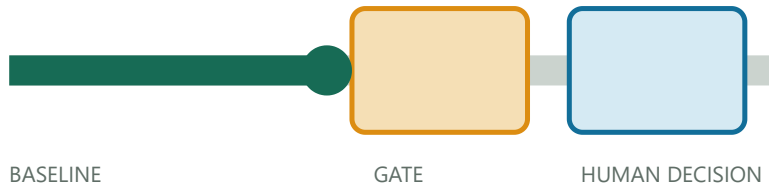


原型设计假设02

平面、剖面、材料、构件和尺寸由方案提出，待官方底图与专业计算。

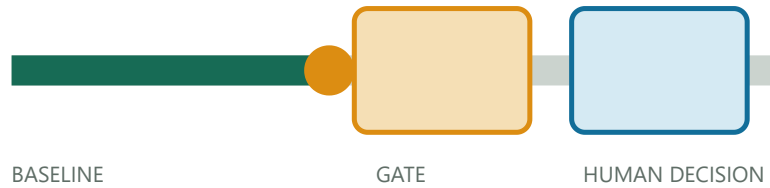


公开数据缺测03

大钟寺裁切仅含一个建筑要素；缺测处标为适配界面 / 待调查带。

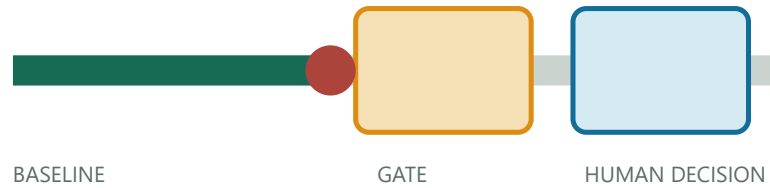


结构与许可状态04

结构、消防、基础、抗风、耐久和八类许可均待专业复核；当前0/8。

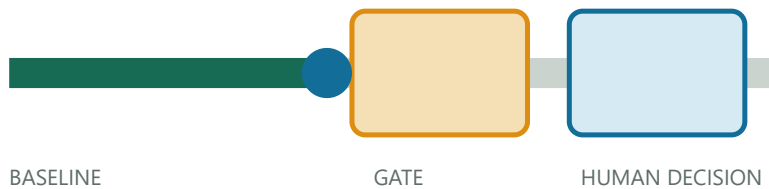


现场绩效未知05

客流、效率、满意度、成本、能耗和恢复时间不填虚构结果。

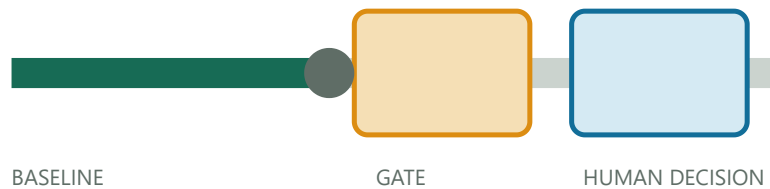

证据使用边界06

体验图只表达感知；专业判断以矢量图、结构化数据和来源为准。

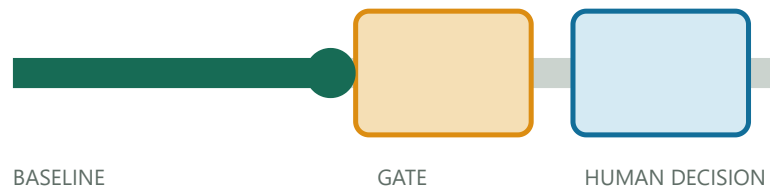


总体城市设计与区域协同

一脊三站两翼六缝合

总体城市设计 | 一条不断线的公共基线，三座不同的城市地标

公开城市肌理承担关系判断；所有边界和尺寸仍待官方底图与测绘复核

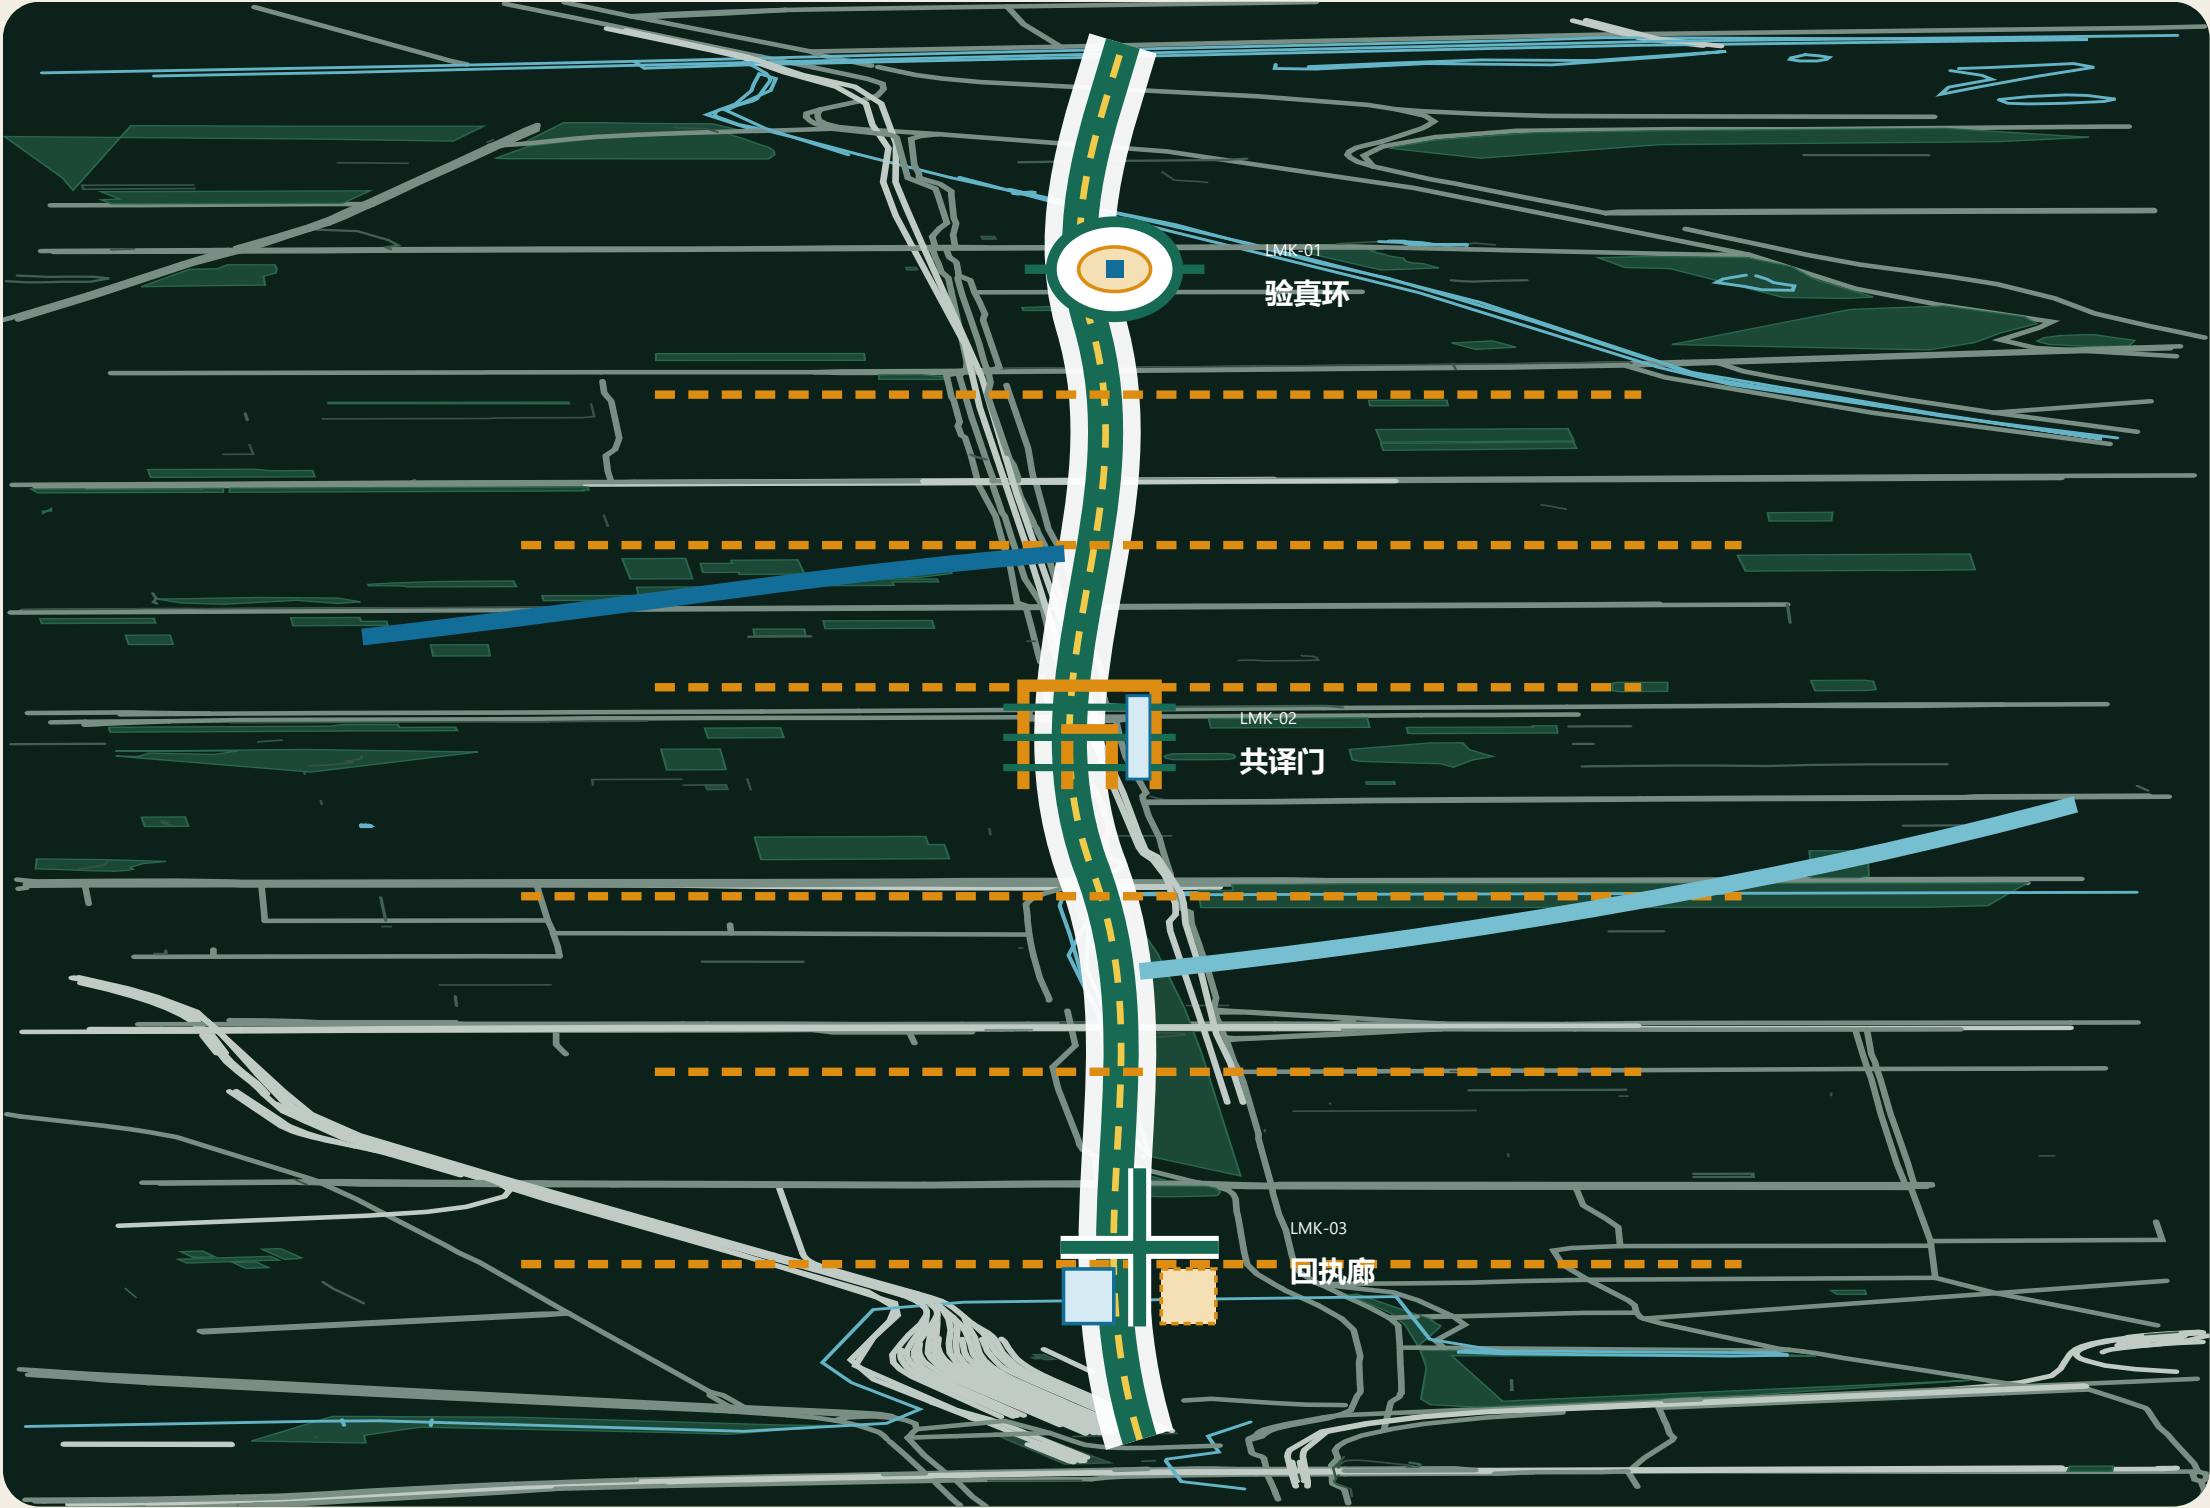

空间判断，不是图标目录

一脊

步行、自行车、无障碍、蓝绿与人工服务先连续

六缝合

每座地标两条东西公共接口，不推定道路红线

两翼

科技服务交换与社区问题进入同一证据链

第一眼结论

ALT-A REJECT

ALT-B REVISE

ALT-C ADVANCE


公共路线一旦被牺牲，空间方案立即出局。

公共基线、首层界面、交通与蓝绿

永久公共权利先于限时技术占用

首层、时间与维护界面 | 公共权利先于技术占用

这不是法定用地分类，而是永久 / 临时 / 人工 / 后勤的空间权利剖带

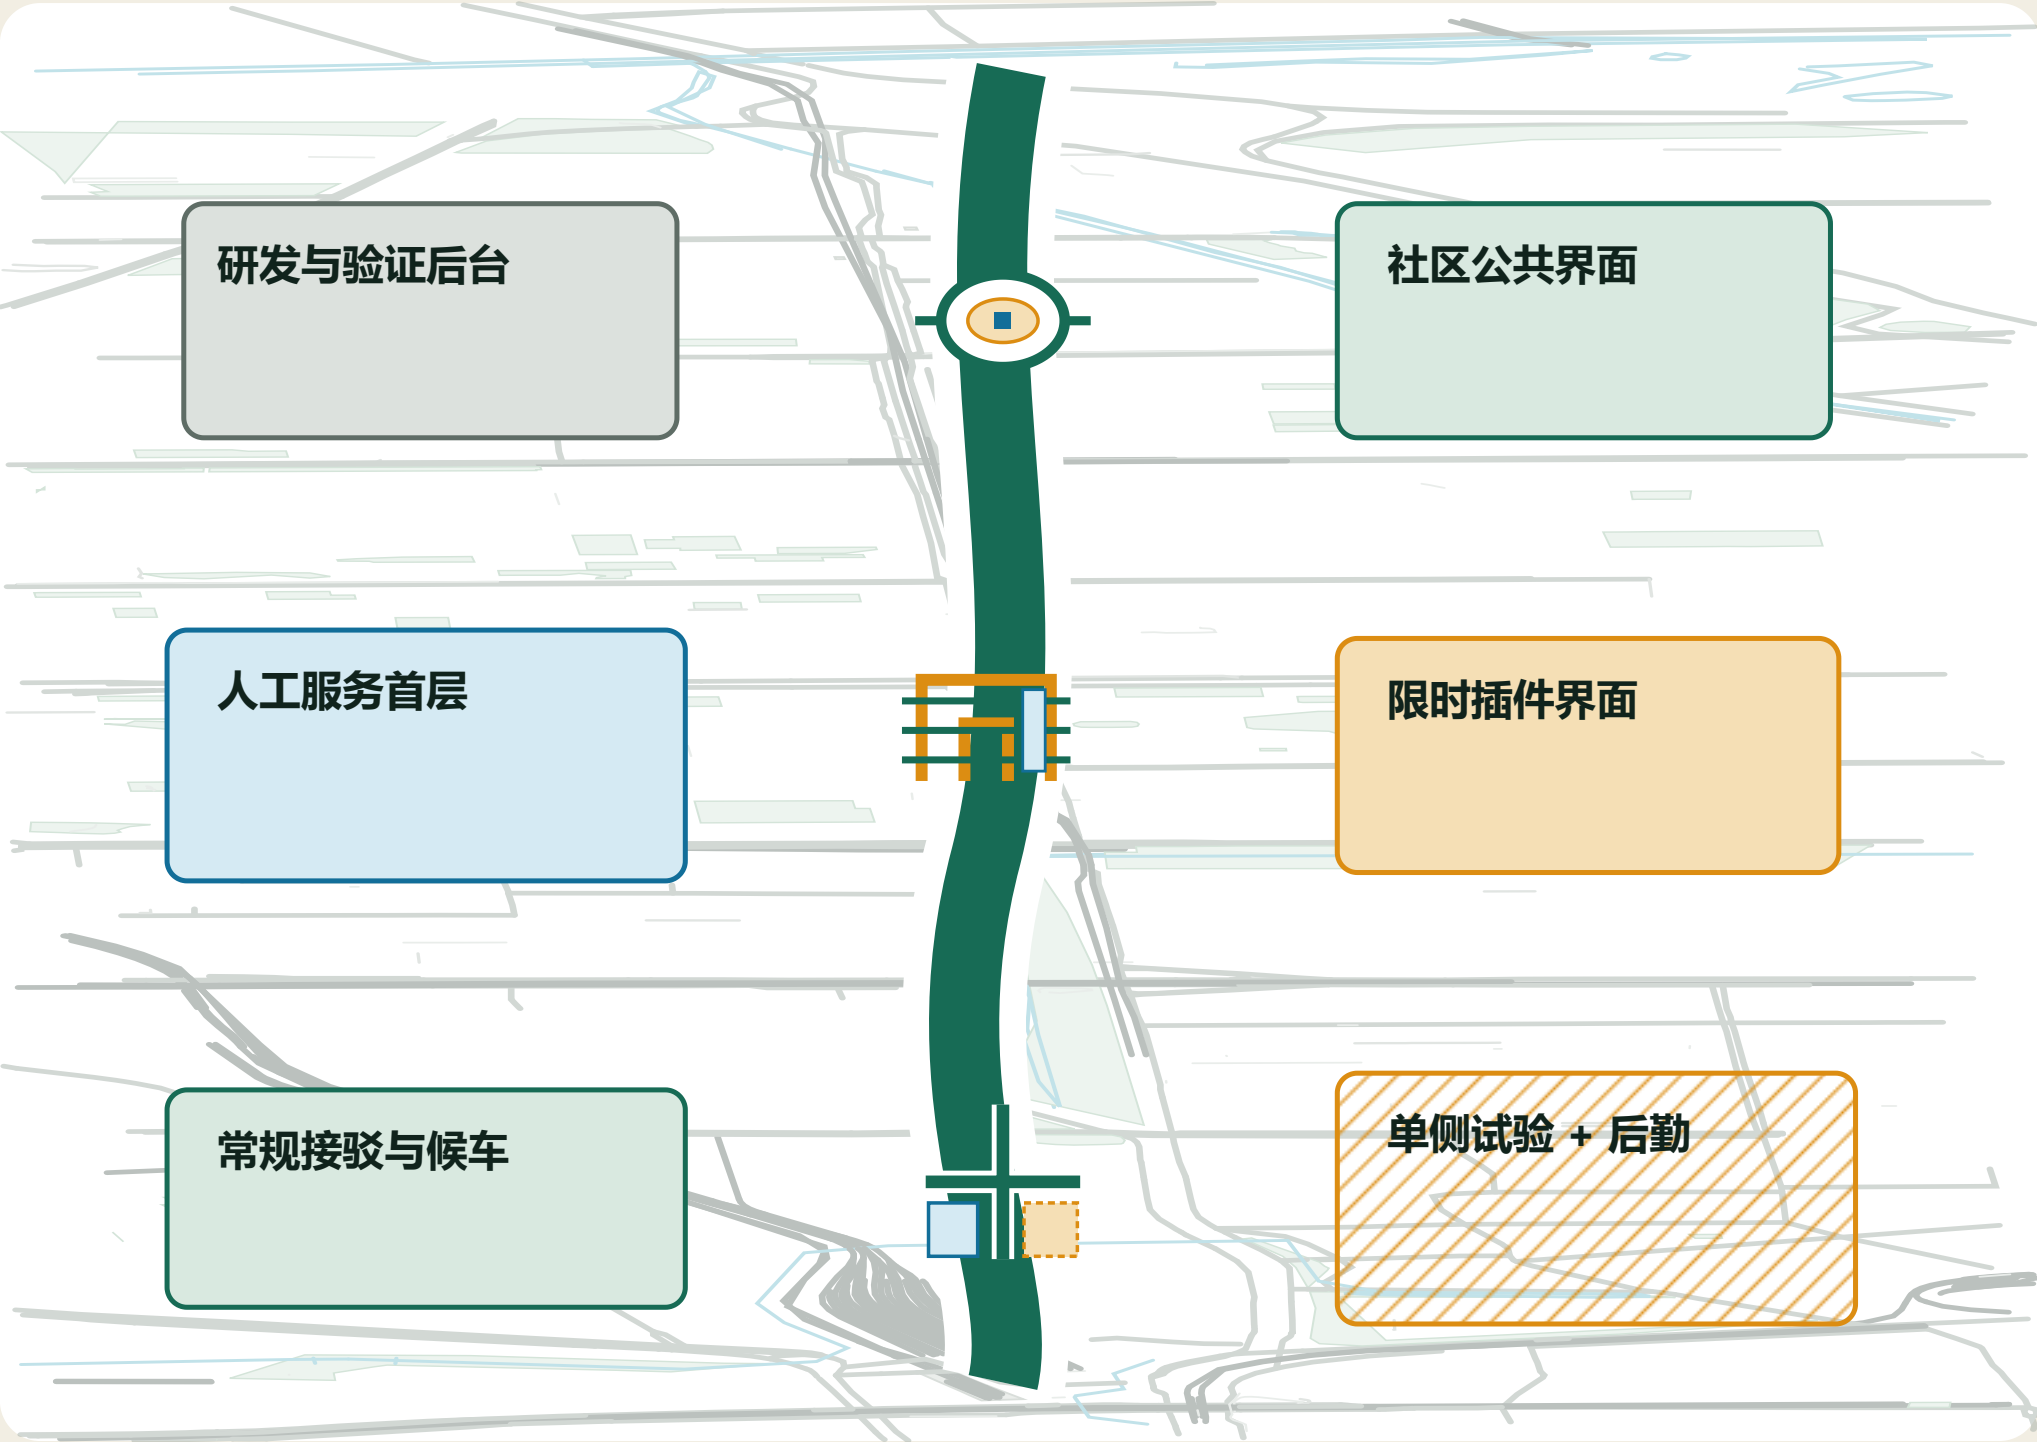

四种空间权利

PERMANENT
全天公共首层

STAFFED
有人值守证据界面

TIMED
限时可逆试验占用

SERVICE
独立维护与退役后场

GO NO-GO · 0/8 PERMITS
试验占用当前不得出现





永久公共层先建；人工层负责；AI层限时；后勤层独立。

三座地标、品牌与文化里程




环、门、廊共享材料，不共享轮廓

三座建筑地标 | 环、门、廊共享材料语言，却有不同空间骨架

同尺度平面—剖面—装配对照；关闭标题仍可凭轮廓、入口和后场辨认

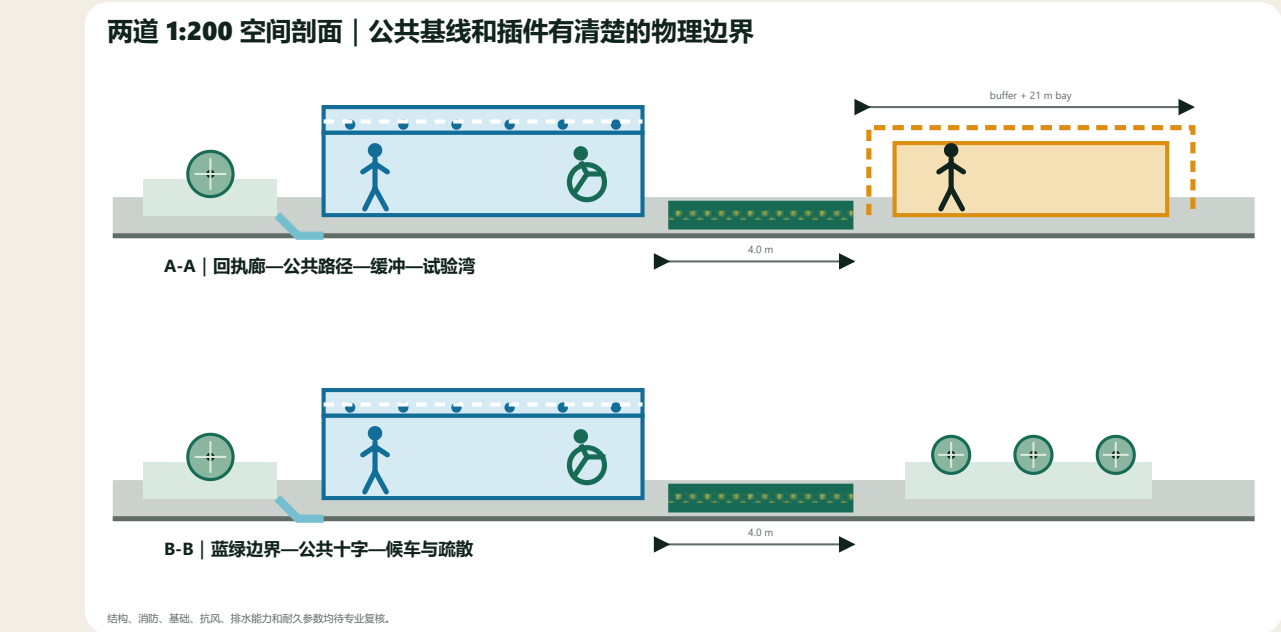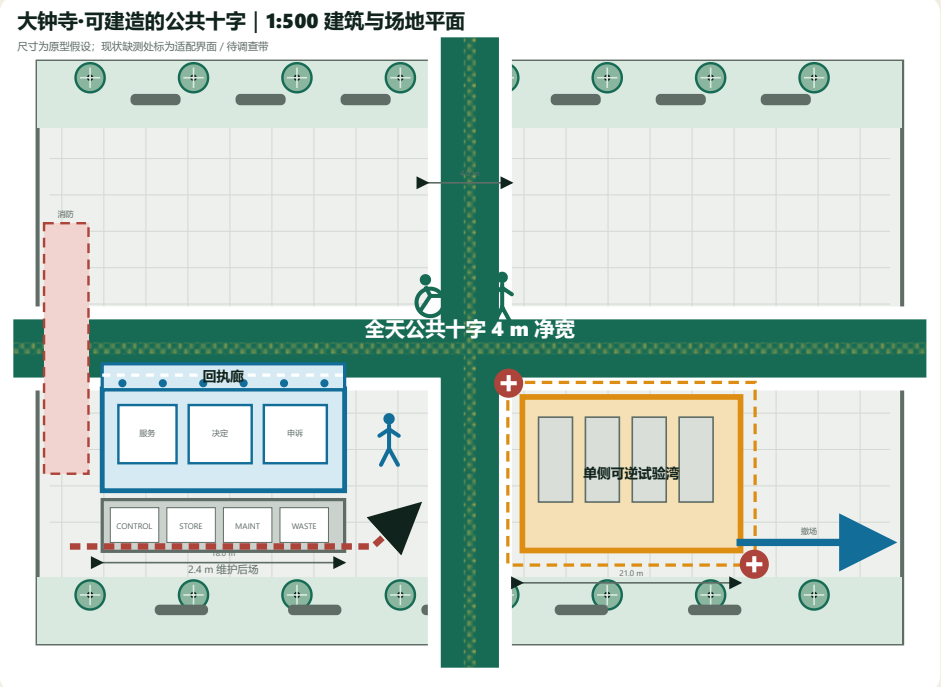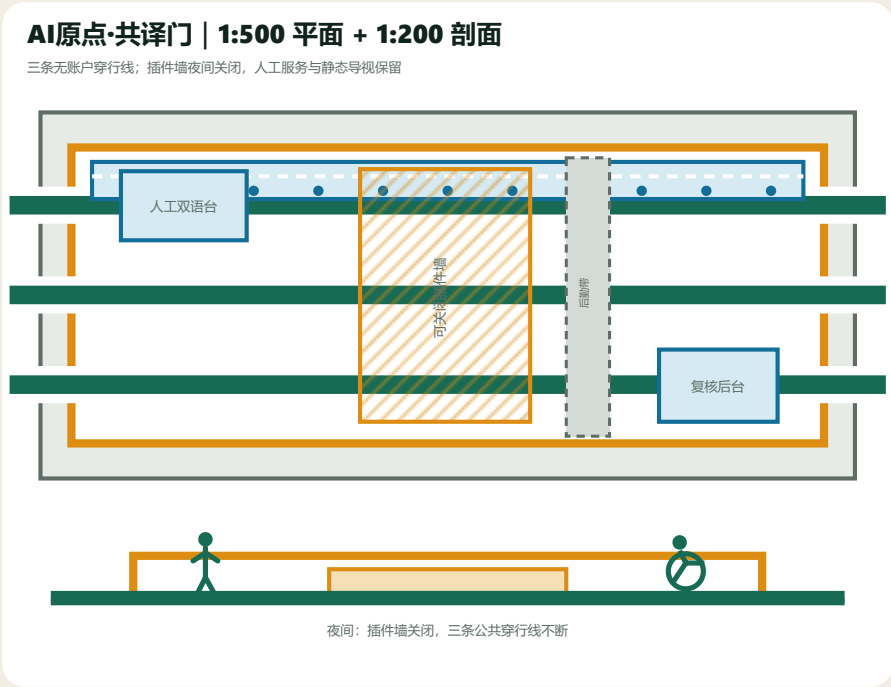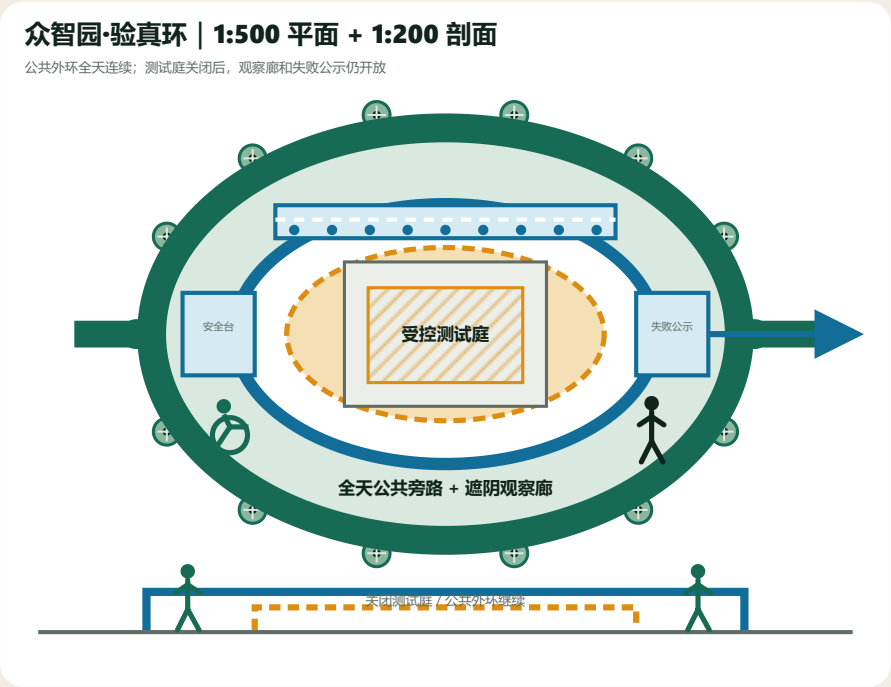

可逆建筑节点 | 干式装配、可维护、可恢复

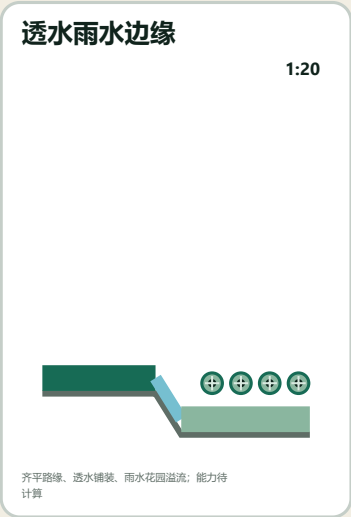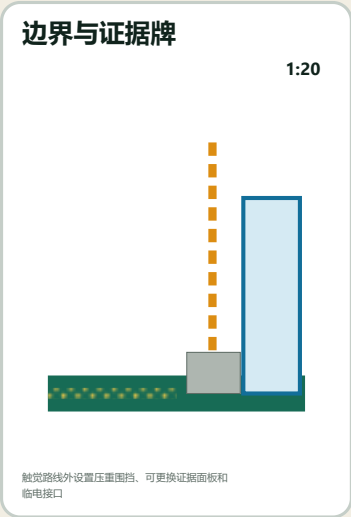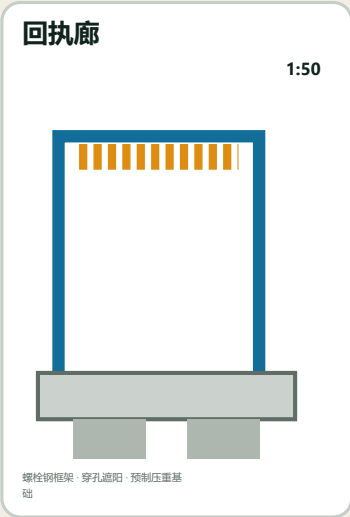


同一材料家族：镀锌钢框架·穿孔遮阳屏·预制压重基础·透水铺装·可更换证据面板。

国际机制、产业生态与两翼转化

只转化机制，不外推北京实施事实


公共问题进入 01

小月河、社区与日常服务提出可复述的问题；普通答案先定义。

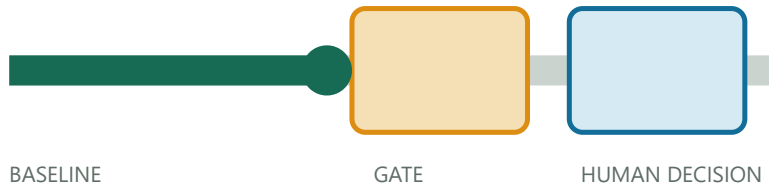


能力复现 02

开放模型、仪器和服务能力先记录输入、版本、许可与失败条件。

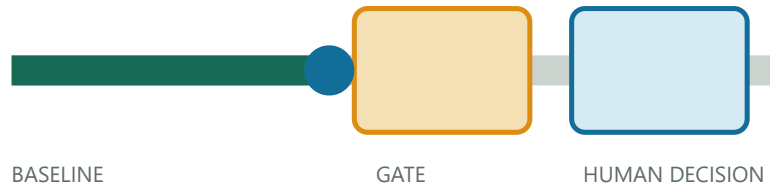


受控验证 03

环、门、廊只在许可、岗位和普通基线成立后接入可拆插件。

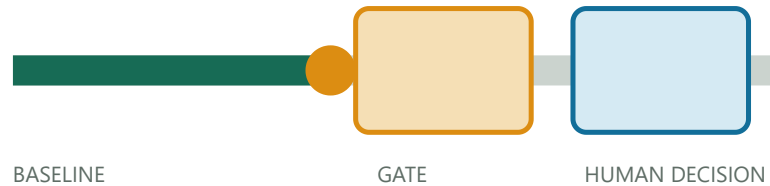


人工决定 04

场景委员会只能作出adopt / revise / stop，并留下回执和申诉入口。

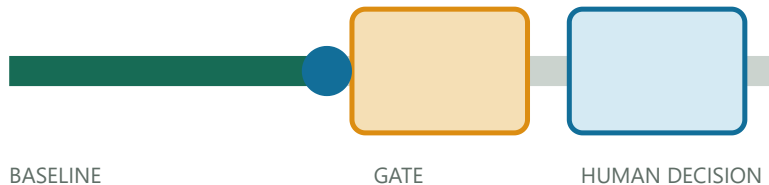


知识归档 05

问题、方法、失败、停止和资产去向归档，不以企业广告排名替代证据。

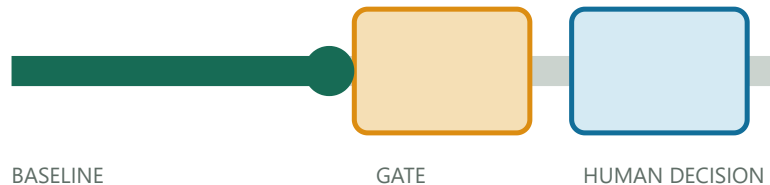

失败出口 06

许可、岗位、公共服务或安全硬门任一失败，回到普通服务并暂停插件。

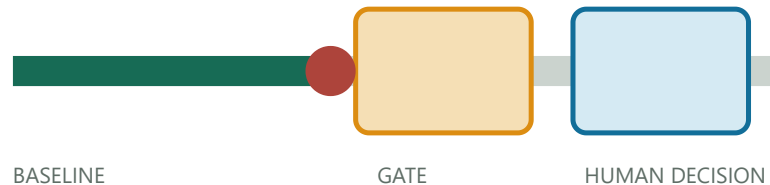


众智园·验真环建筑原型

1:500平面、1:200剖面、关闭状态与对应体验

众智园·验真环 | 1:500 平面 + 1:200 剖面

公共外环全天连续；测试庭关闭后，观察廊和失败公示仍开放

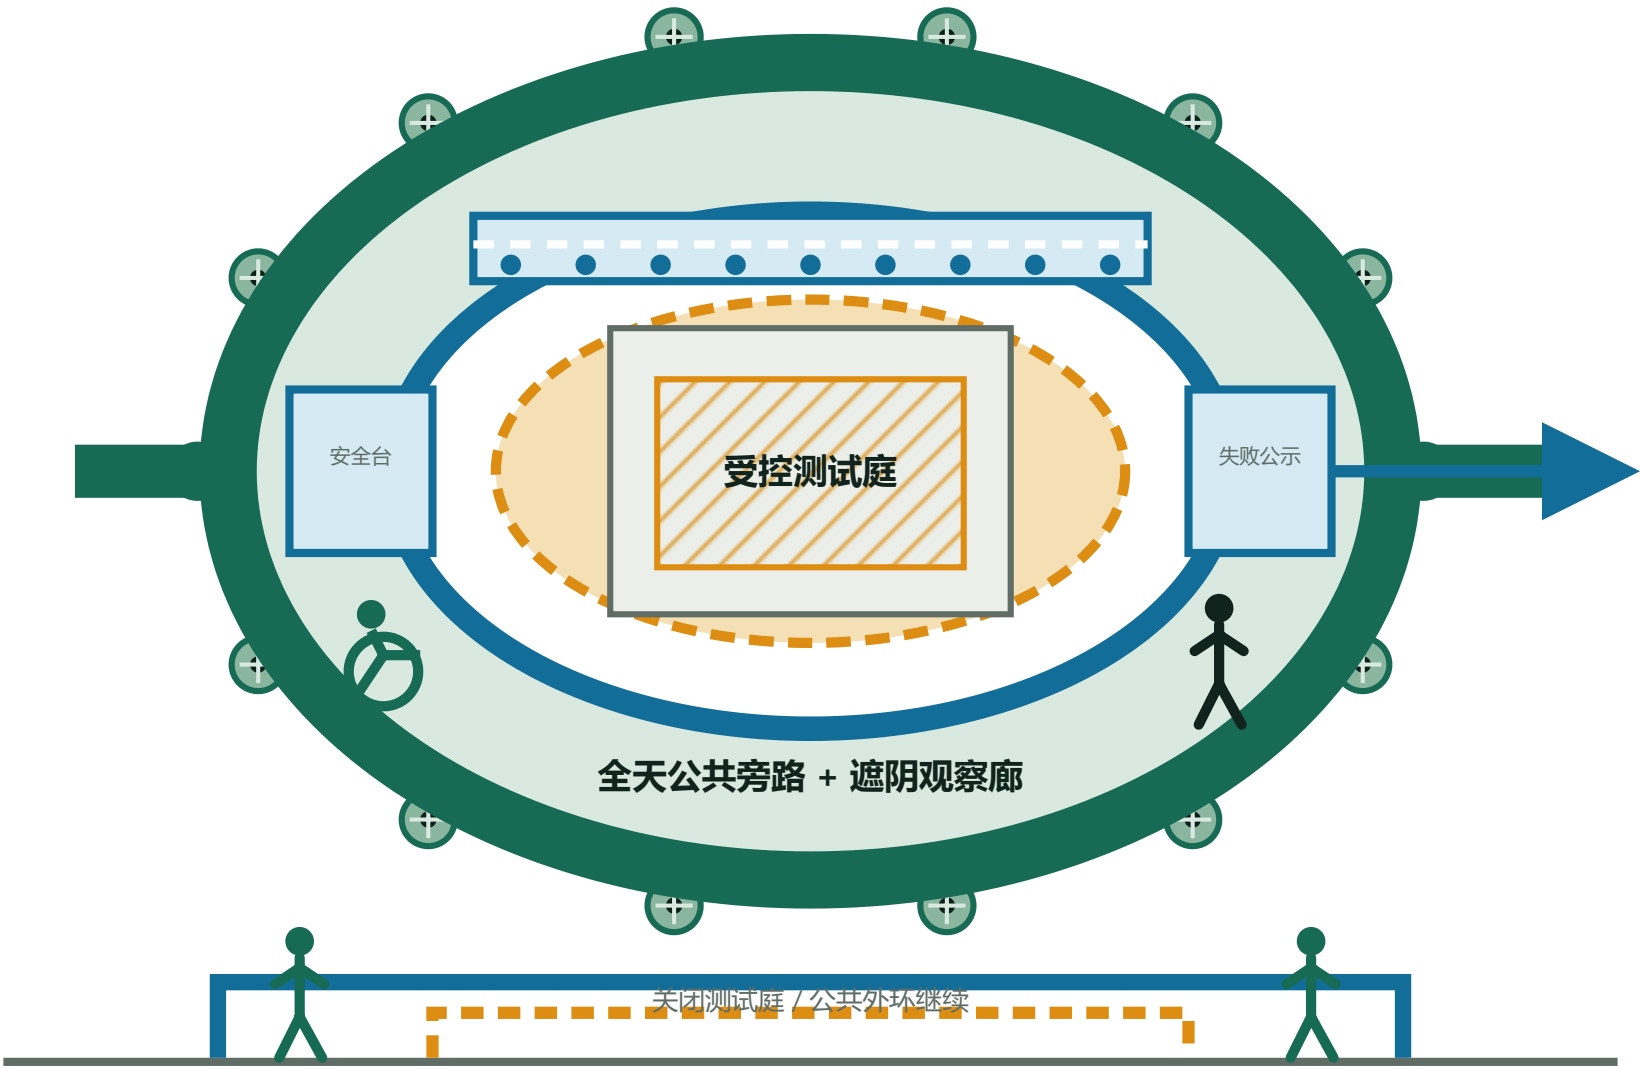

外环公共旁路围绕受控测试庭


概念生成图 / 非现场证据 空间与尺度判断以矢量平面、剖面 and 几何数据为准

AI原点·共译门建筑原型

三条无账户路径、可关闭插件墙与对应体验

AI原点·共译门 | 1:500 平面 + 1:200 剖面

三条无账户穿行线；插件墙夜间关闭，人工服务与静态导视保留

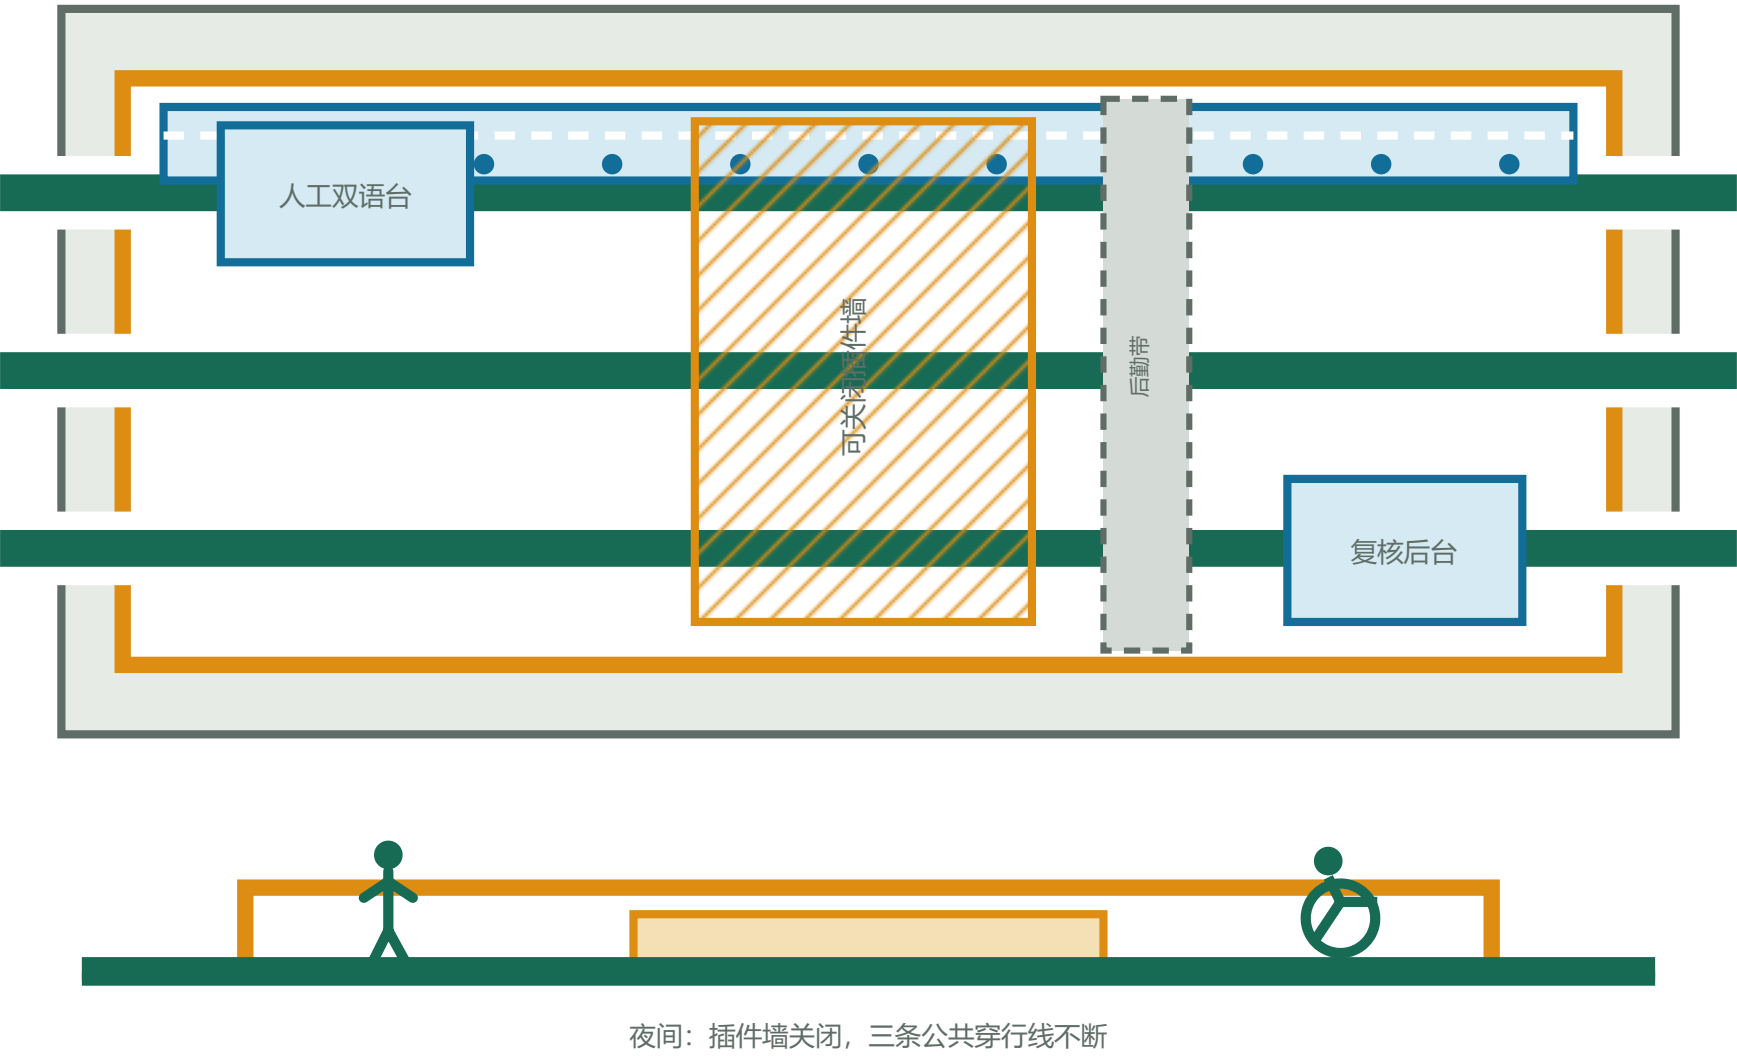

大钟寺城市联系与空间裁决

ALT-A拒绝、ALT-B修改、ALT-C进入建筑深化

实施闭环 | 空间裁决只出现一次，随后进入许可、建造、维护与退出

现场绩效仍未知；表单和图纸说明如何验证，不表示已经验证

01 同一把尺子的空间裁决

ALT-A

REJECT

切断公共十字

ALT-B

REVISE

消防/监督/撤场碎片化

ALT-C

ADVANCE

公共、试验、后勤三线独立

02 当前 G0：许可与岗位没有关闭

SITE

PENDING

TITLE

PENDING

FIRE

PENDING

ACCESS

PENDING

POWER

PENDING

NETWORK

PENDING

TRAFFIC

PENDING

DEVICE

PENDING

0 / 8 PERMITS · 0 / 7 BASELINE DAYS · 0 / 4 CONTRACTED POSTS

结论：NO-GO，试验湾不得装配

03 90天构件—责任—失败出口

0–15

测绘与八许可

失败 → 不进入下一阶段

16–30

只建公共基线

失败 → 不进入下一阶段

31–45

记录7日普通服务

失败 → 不进入下一阶段

46–75

限时装配插件

失败 → 不进入下一阶段

76–90

暂停演练与撤场

失败 → 不进入下一阶段

MAT-01–05 干式材料家族

RACI

资产/场地/普通服务/安全/数据/公众

RETIRE


设备撤出；公共层保留

ALT-C 1:500建筑与场地平面

公共、试验、消防与撤场路线互不占用

大钟寺·可建造的公共十字 | 1:500 建筑与场地平面


尺寸为原型假设；现状缺测处标为适配界面 / 待调查带

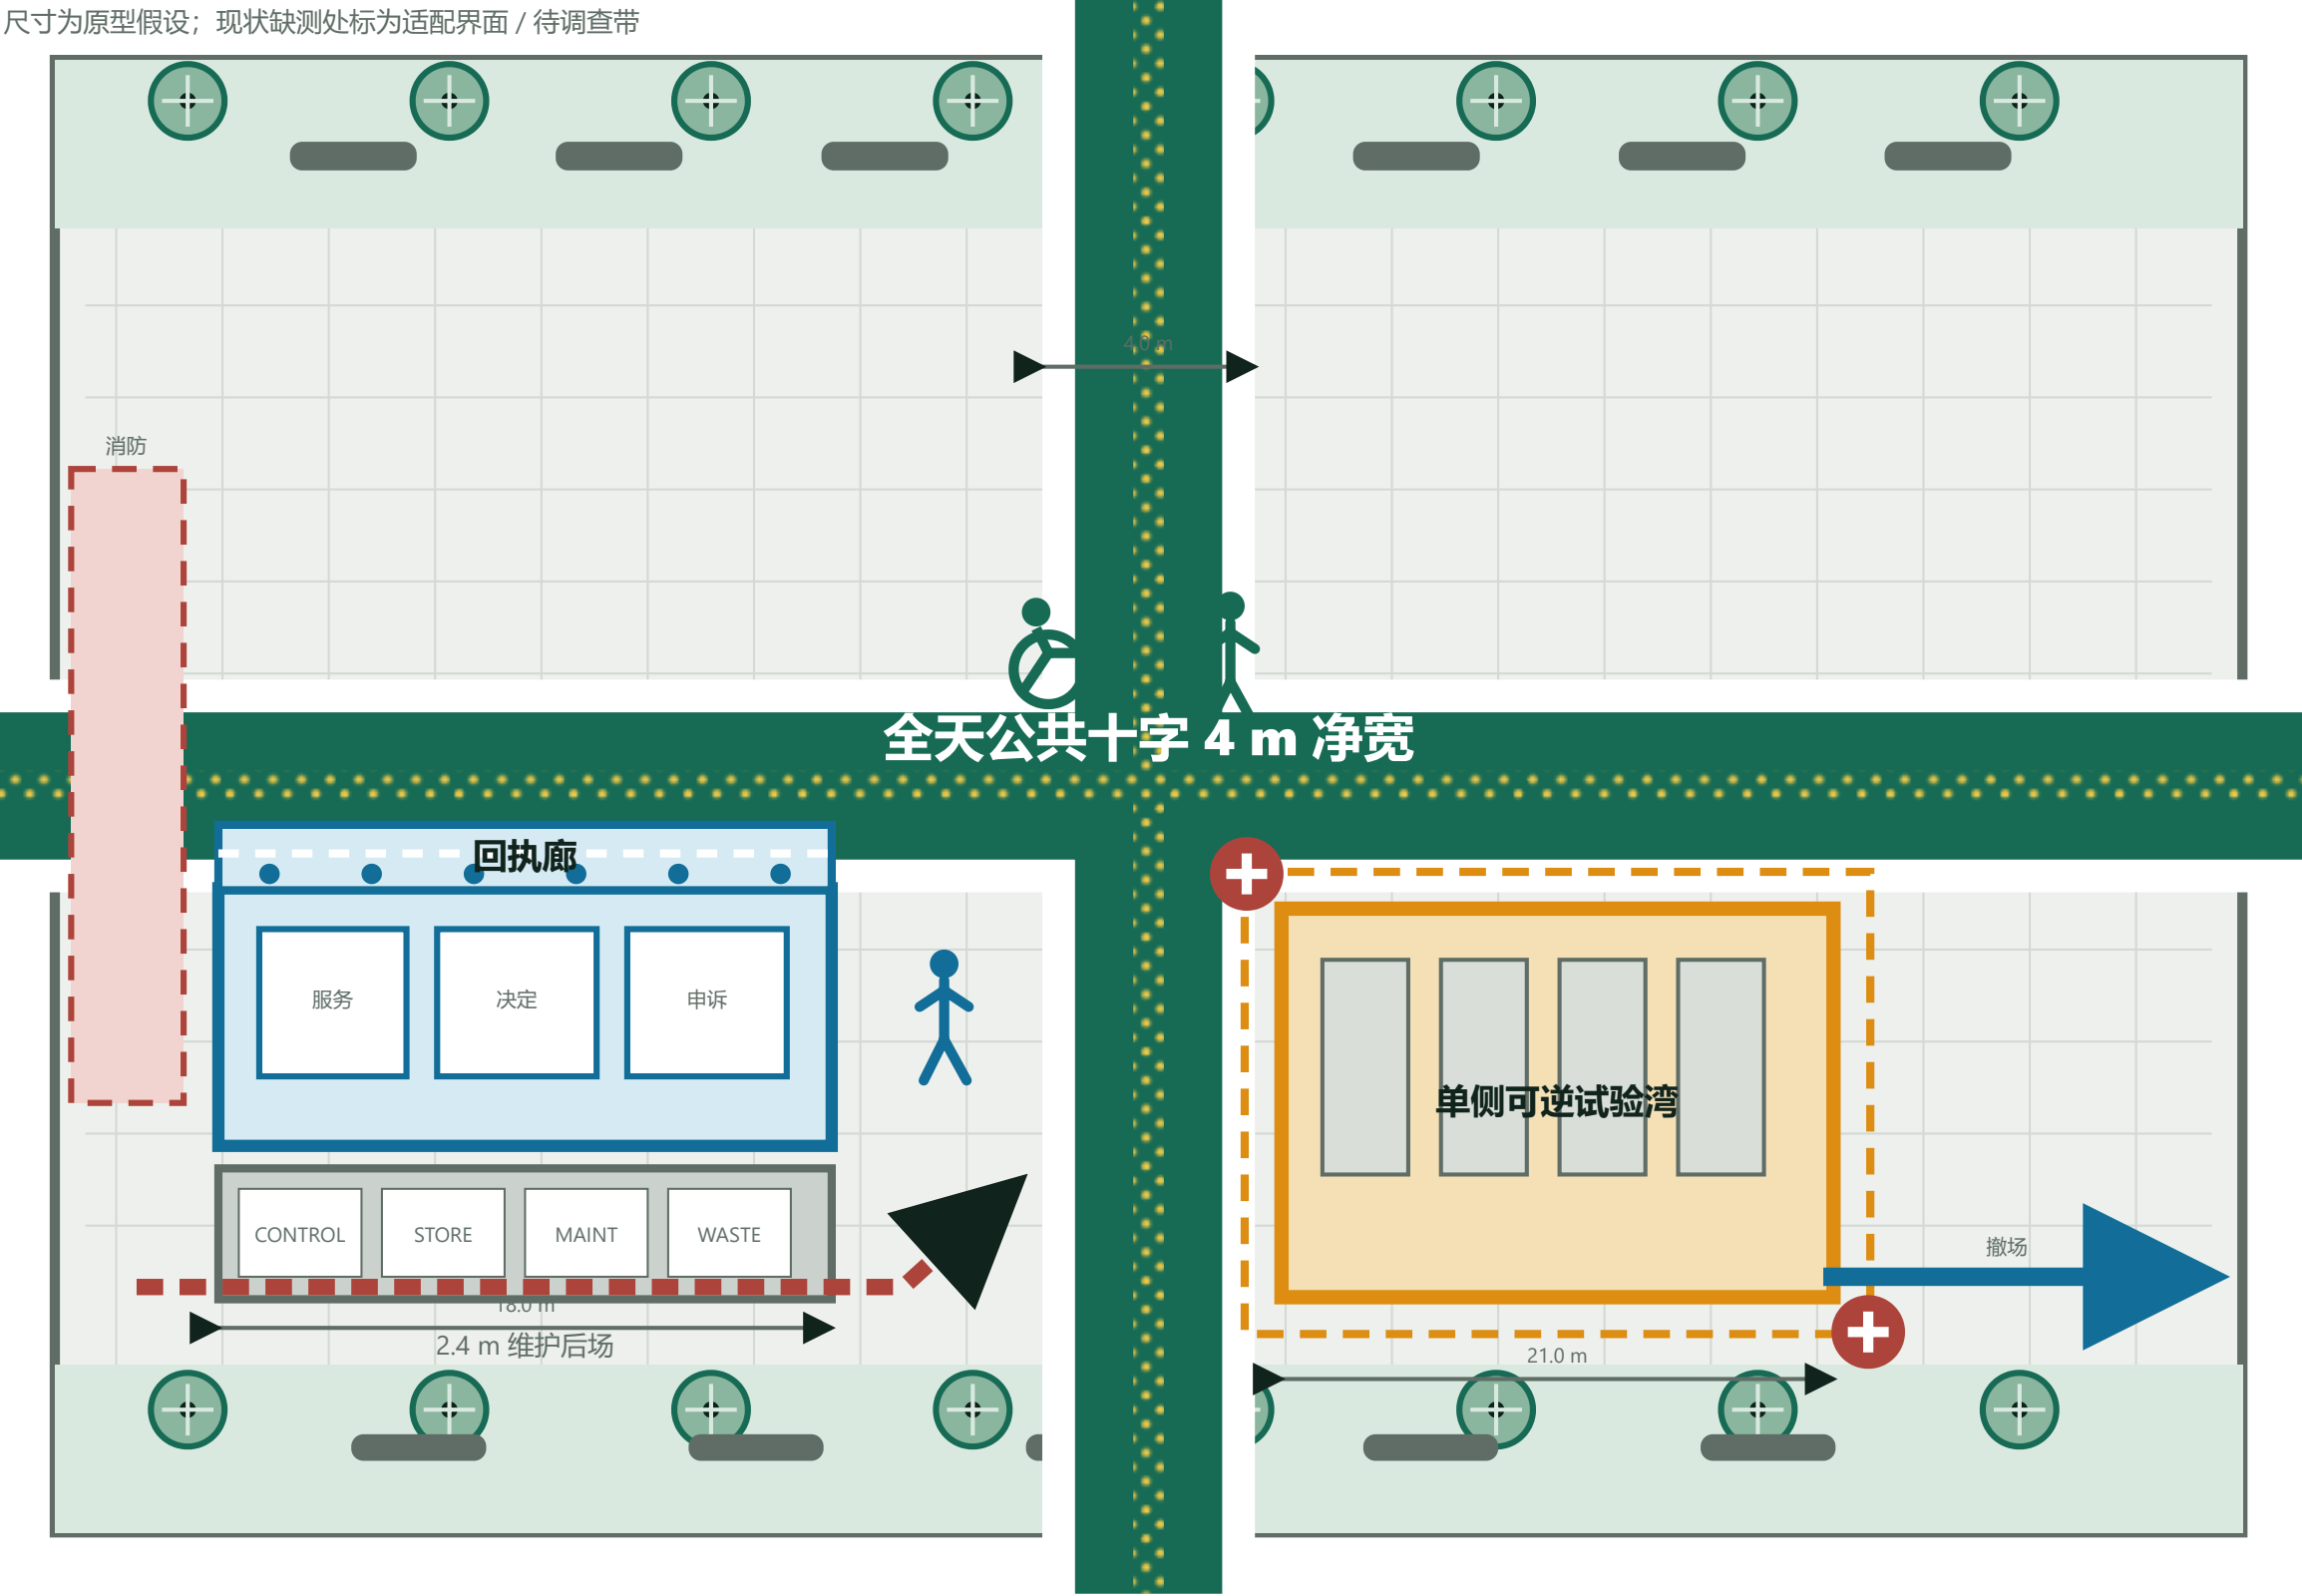

两道1:200剖面及1:50 / 1:20节点

物理边界、干式连接与雨水边缘

两道 1:200 空间剖面 | 公共基线和插件有清楚的物理边界

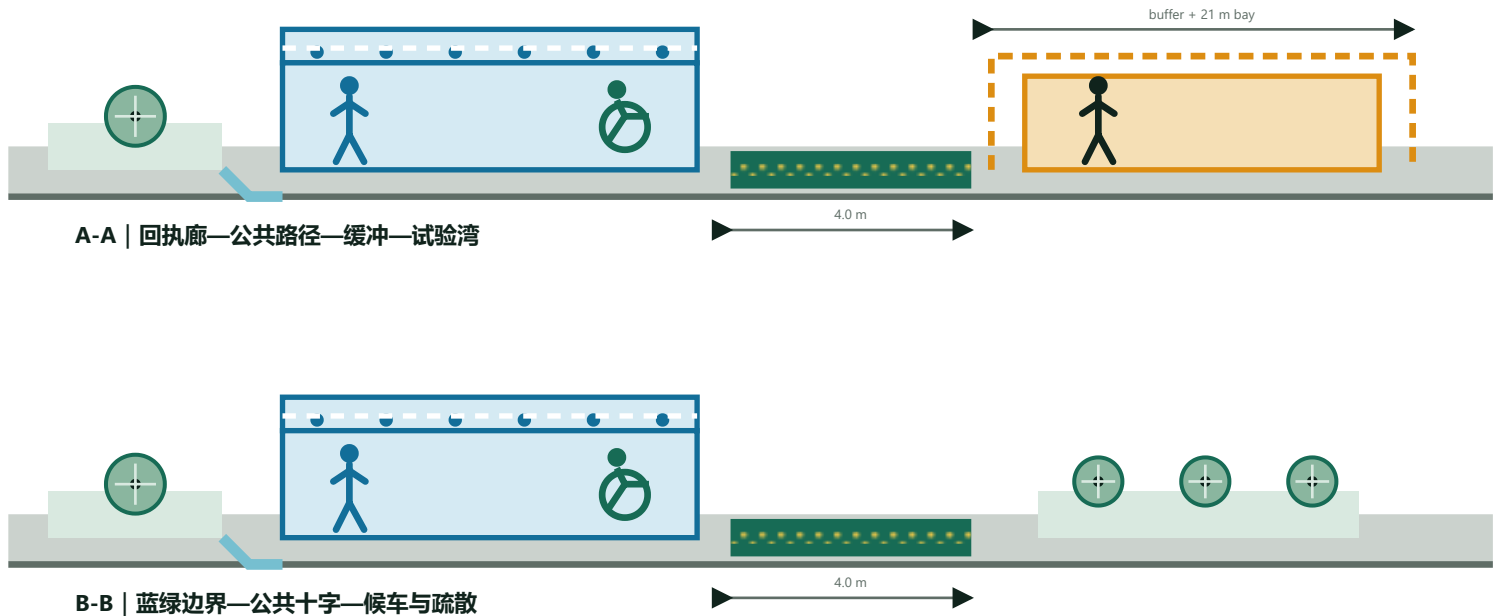

结构、消防、基础、抗风、排水能力和耐久参数均待专业复核。

可逆建筑节点 | 干式装配、可维护、可恢复

回执廊

1:50

螺栓钢框架·穿孔遮阳·预制压重基础

边界与证据牌

1:20

触觉路线外设置压重围挡、可更换证据面板和临电接口

透水雨水边缘


1:20

齐平路缘、透水铺装、雨水花园溢流；能力待计算

剖切轴测、四态运行与维护后场

公共层保留，插件层可拆，证据层有人负责

大钟寺剖切装配轴测 | 公共层先建，插件层可拆，证据层有人负责

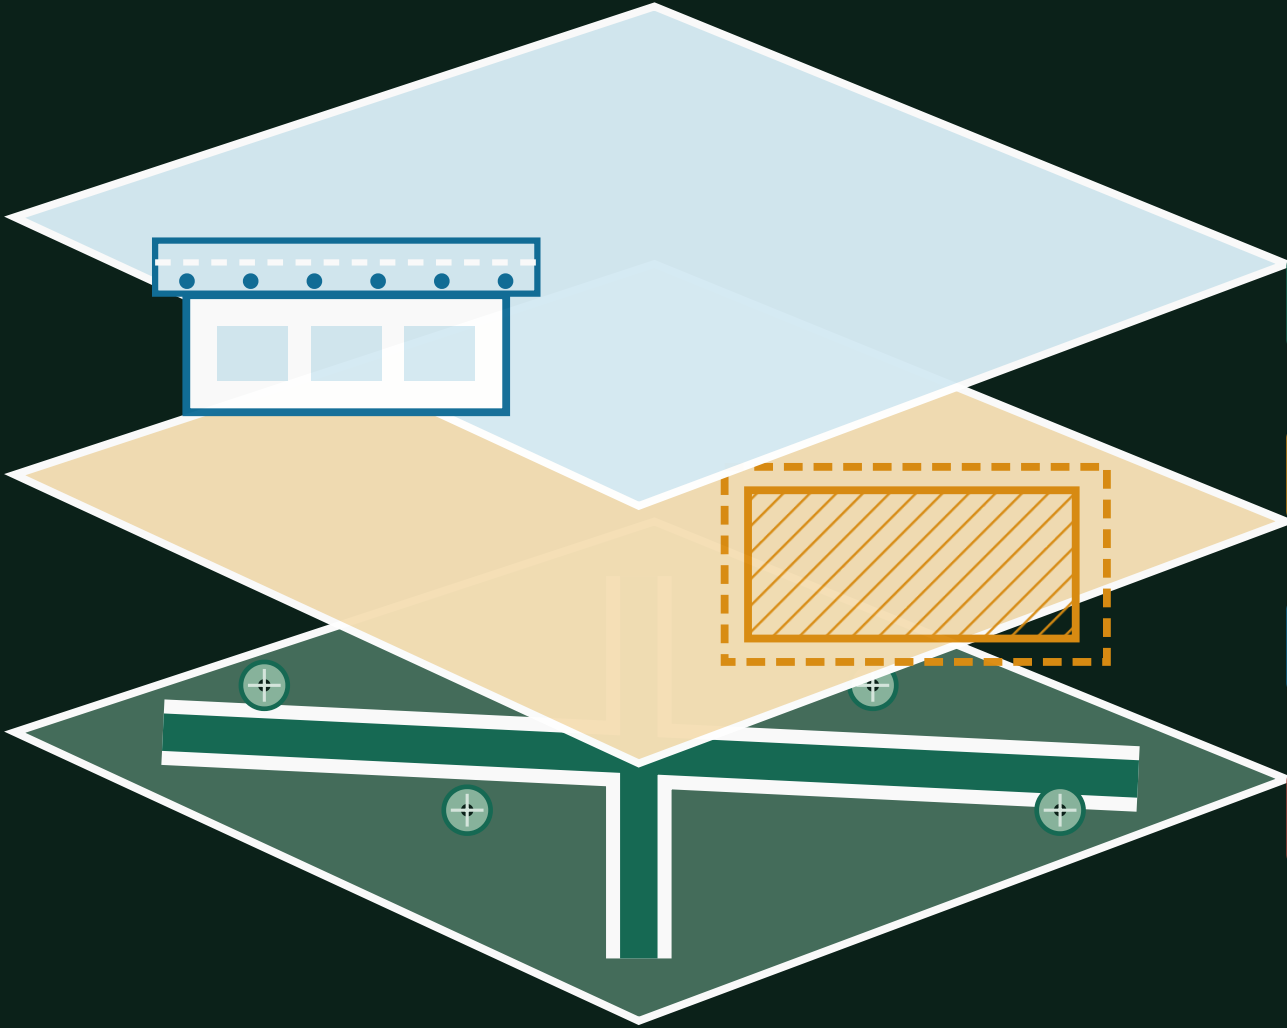

RETIRE: 设备沿独立后勤线撤出；公共十字、遮阴、蓝绿边界与人工门廊继续服务。



公共十字不断线，试验湾只在一侧

概念生成图 / 非现场证据：空间与尺度判断以矢量平面、剖面几何数据为准

十二场景、六类画像与城市采纳年

建筑原型承载协议复制，不增加场景数量

十二场景复制目录 | 空间、分母、责任、停止与恢复均可追踪

完整契约保留在结构化数据；图面突出英雄场景与失败回退

T1 · 模型与数据复现

复制目录 / 稳定ID

普通基线 + 人工责任 + 零容忍停止

现场结果：0 / NOT FIELD-RUN

T2 · 机器人通行

英雄契约 / 详图

普通基线 + 人工责任 + 零容忍停止

现场结果：0 / NOT FIELD-RUN

T3 · 端侧降级

复制目录 / 稳定ID

普通基线 + 人工责任 + 零容忍停止

现场结果：0 / NOT FIELD-RUN

S1 · 企业分诊

复制目录 / 稳定ID

普通基线 + 人工责任 + 零容忍停止

现场结果：0 / NOT FIELD-RUN

S2 · 国际抵达

英雄契约 / 详图

普通基线 + 人工责任 + 零容忍停止

现场结果：0 / NOT FIELD-RUN

S3 · 开源工作坊

复制目录 / 稳定ID

普通基线 + 人工责任 + 零容忍停止

现场结果：0 / NOT FIELD-RUN

S4 · 京张文化导览

复制目录 / 稳定ID

普通基线 + 人工责任 + 零容忍停止

现场结果：0 / NOT FIELD-RUN

S5 · 无障碍导航

复制目录 / 稳定ID

普通基线 + 人工责任 + 零容忍停止

现场结果：0 / NOT FIELD-RUN

S6 · 气候休息服务

复制目录 / 稳定ID

普通基线 + 人工责任 + 零容忍停止

现场结果：0 / NOT FIELD-RUN

S7 · 轨道接驳

英雄契约 / 详图

普通基线 + 人工责任 + 零容忍停止

现场结果：0 / NOT FIELD-RUN

S8 · 公共服务台

复制目录 / 稳定ID

普通基线 + 人工责任 + 零容忍停止

现场结果：0 / NOT FIELD-RUN

S9 · 活动客流

复制目录 / 稳定ID

普通基线 + 人工责任 + 零容忍停止

现场结果：0 / NOT FIELD-RUN

春：基线审计 夏：受控验证 秋：公众采纳 冬：回执与退出复盘；机构和活动均为建议角色。

构件、许可、RACI、90天实施与资产去向

数量可复算；报价和许可待确认

GO NO-GO | 90天不是承诺，而是五道进入条件

普通服务、许可、岗位、基线和撤场演练任一失败，不进入AI试验

DAY 0–15

测绘、权属、站口、消防、管线、无
障碍与交通核验

DAY 16–30

只搭公共路线、候车、遮阳、人工服
务和回执廊

DAY 31–45

记录7个连续普通运行日；不放AI
设备

DAY 46–75

8类许可 + 4独立岗位齐全后才
可限时试验

DAY 76–90

停止演练、撤场恢复、公众复核与回
执

八类许可 | 当前全部待办

SITE

场地使用与资产方书面同意

TITLE

权属、边界与现状测绘核验

FIRE

消防车道、疏散面与临时构筑物复核

ACCESS

无障碍路线、坡道、盲道和人工服务审计

POWER

临时用电、配电保护与断电责任

NET

隔离网络、数据最小化与日志保存规则

TRAFFIC

常规接驳优先、活动时窗与交通组织审批

EQUIP

设备安全、保险、急停与供应商撤场责任

四个岗位必须独立覆盖

01

场地负责人

待落实

02

普通服务人员

待落实

03

安全负责人

待落实

04

数据记录人员

待落实

关键安全岗位与普通服务岗位不得兼任。

单价、总价、合作和许可均未承诺。

16项构件、4个采购包、5类空白表单已登记；价格均为pending_market_quote，当前不构成采购或开工条件。

指标、回执、风险、来源与深化门槛

G0 NO-GO；现场绩效未知

实施闭环 | 空间裁决只出现一次，随后进入许可、建造、维护与退出

现场绩效仍未知；表单和图纸说明如何验证，不表示已经验证

01 同一把尺子的空间裁决

ALT-A

REJECT

切断公共十字

ALT-B

REVISE

消防/监督/撤场碎片化

ALT-C

ADVANCE

公共、试验、后勤三线独立

02 当前 G0：许可与岗位没有关闭

SITE

PENDING

TITLE

PENDING

FIRE

PENDING

ACCESS

PENDING

POWER

PENDING

NETWORK

PENDING

TRAFFIC

PENDING

DEVICE

PENDING

0 / 8 PERMITS · 0 / 7 BASELINE DAYS · 0 / 4 CONTRACTED POSTS

结论：NO-GO，试验湾不得装配

03 90天构件—责任—失败出口

0–15

测绘与八许可

失败 → 不进入下一阶段

16–30

只建公共基线

失败 → 不进入下一阶段

31–45

记录7日普通服务

失败 → 不进入下一阶段

46–75

限时装配插件

失败 → 不进入下一阶段

76–90

暂停演练与撤场

失败 → 不进入下一阶段

MAT-01–05 干式材料家族

RACI

资产/场地/普通服务/安全/数据/公众

RETIRE

设备撤出；公共层保留