



百年京张AI创新带 · 总体设计范围


11.41 km² · EPSG:4548 · 基于官方临时边界

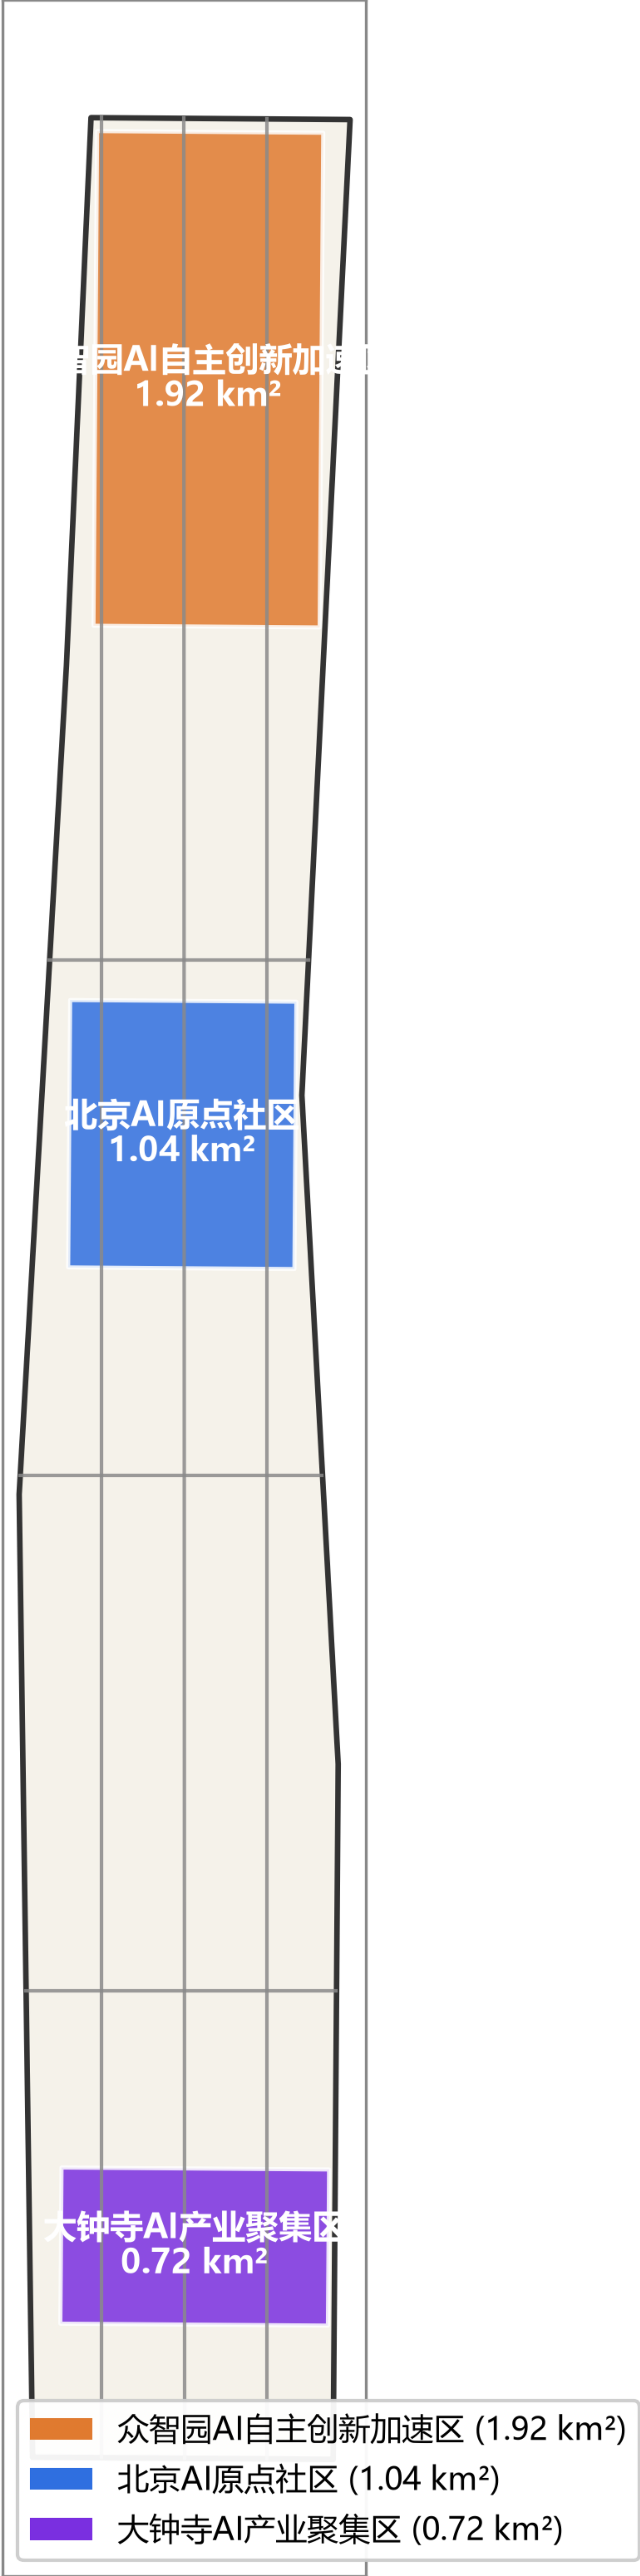


重点区域详细设计 / Key Detailed Design Areas

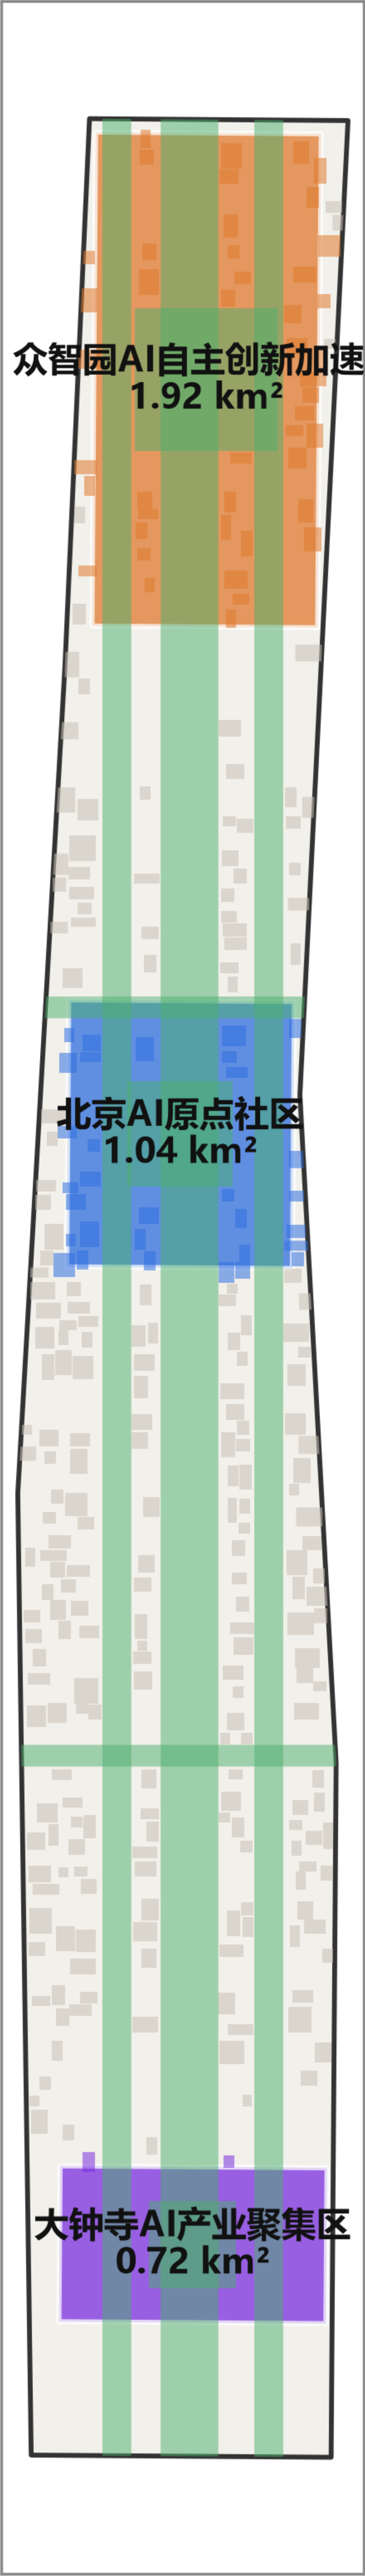

用地分区规划 / Land Use Plan

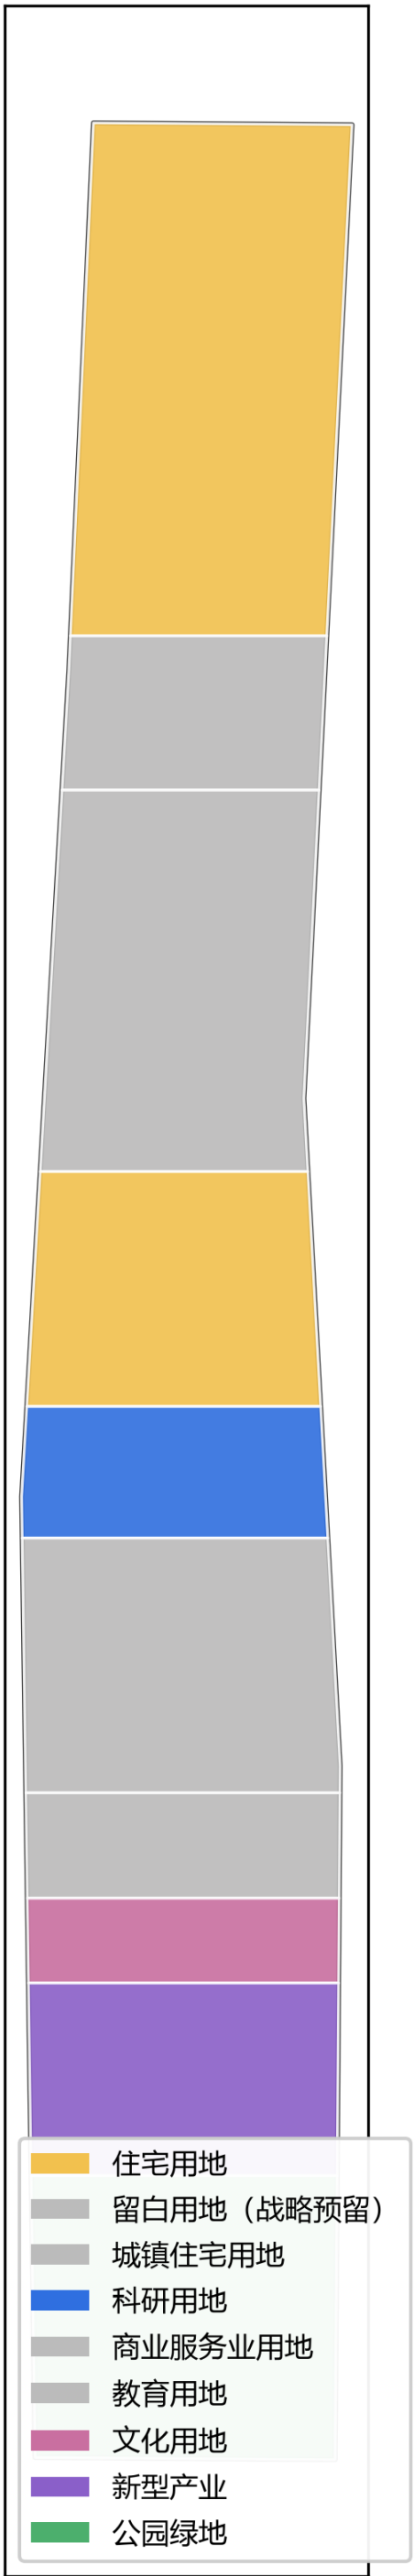


用地构成 / Land Use Mix

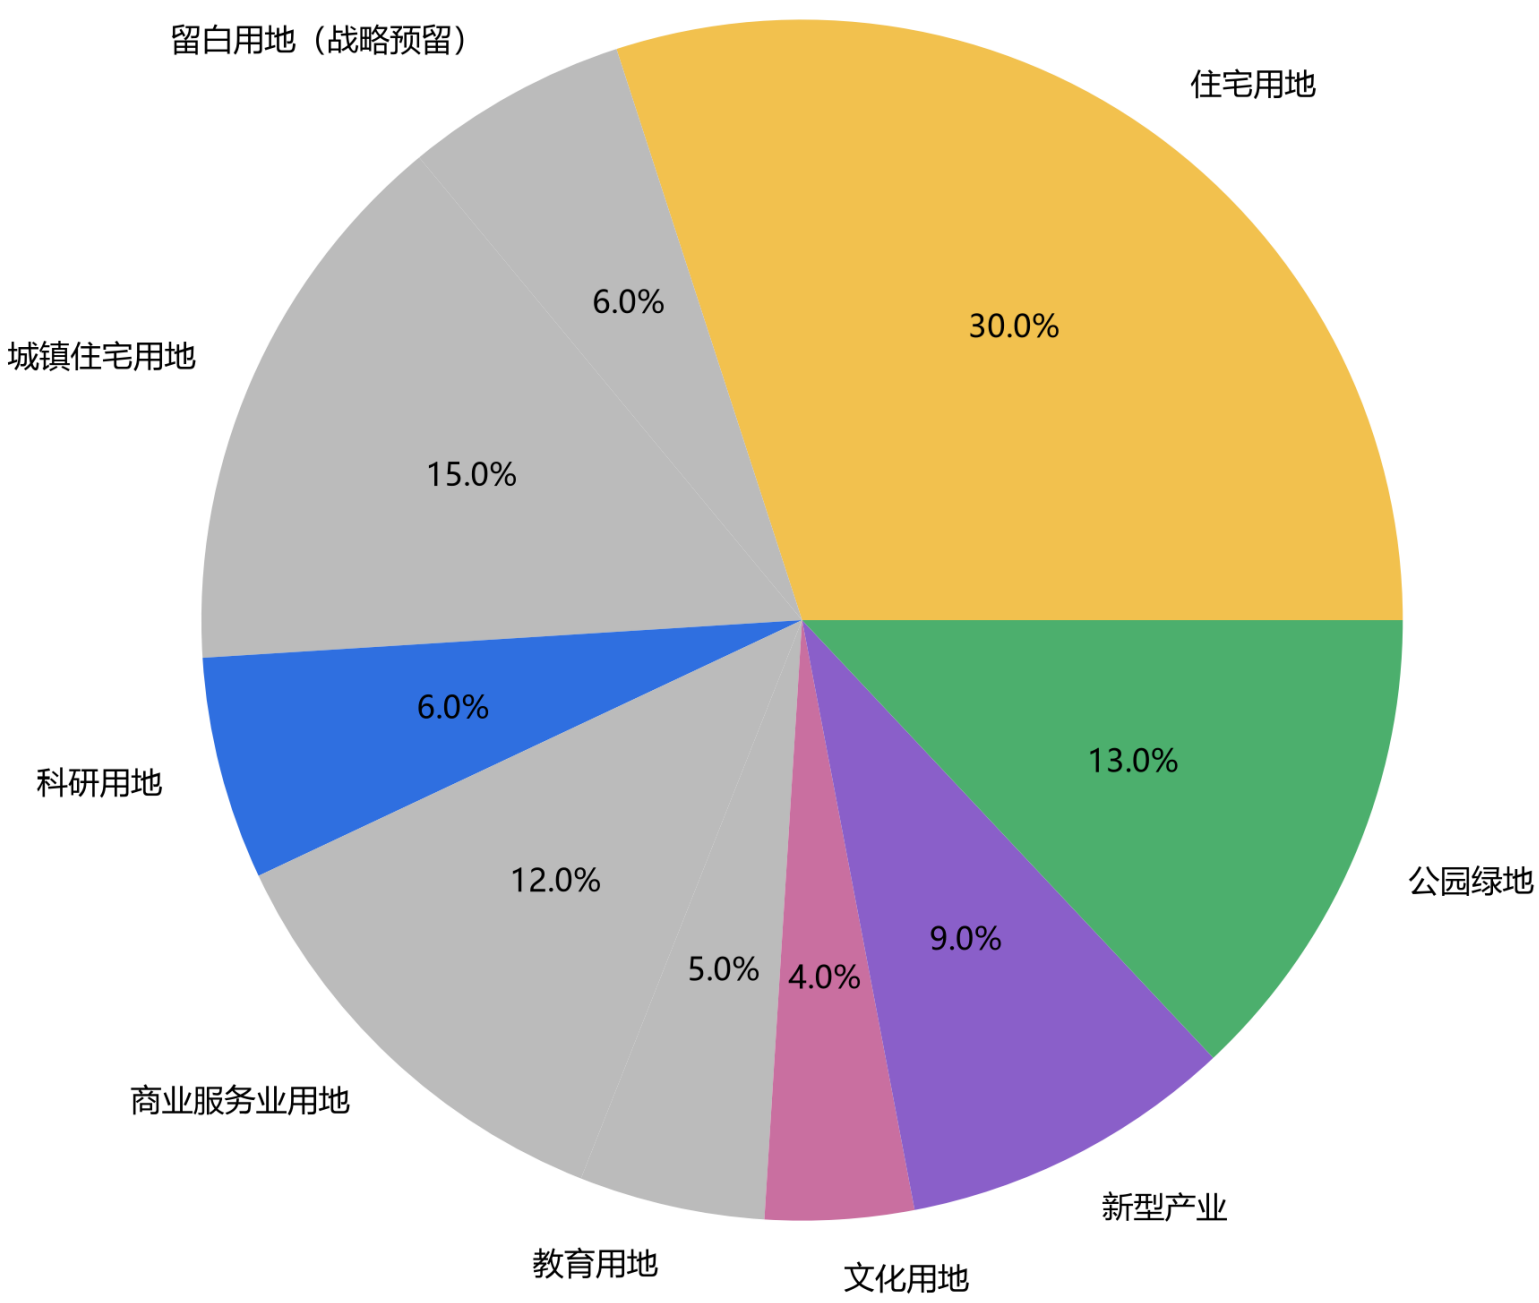


交通系统与蓝绿网络 / Mobility & Blue-Green Network

绿地率 green ratio 44.4% · 公共空间 public space 8.2%

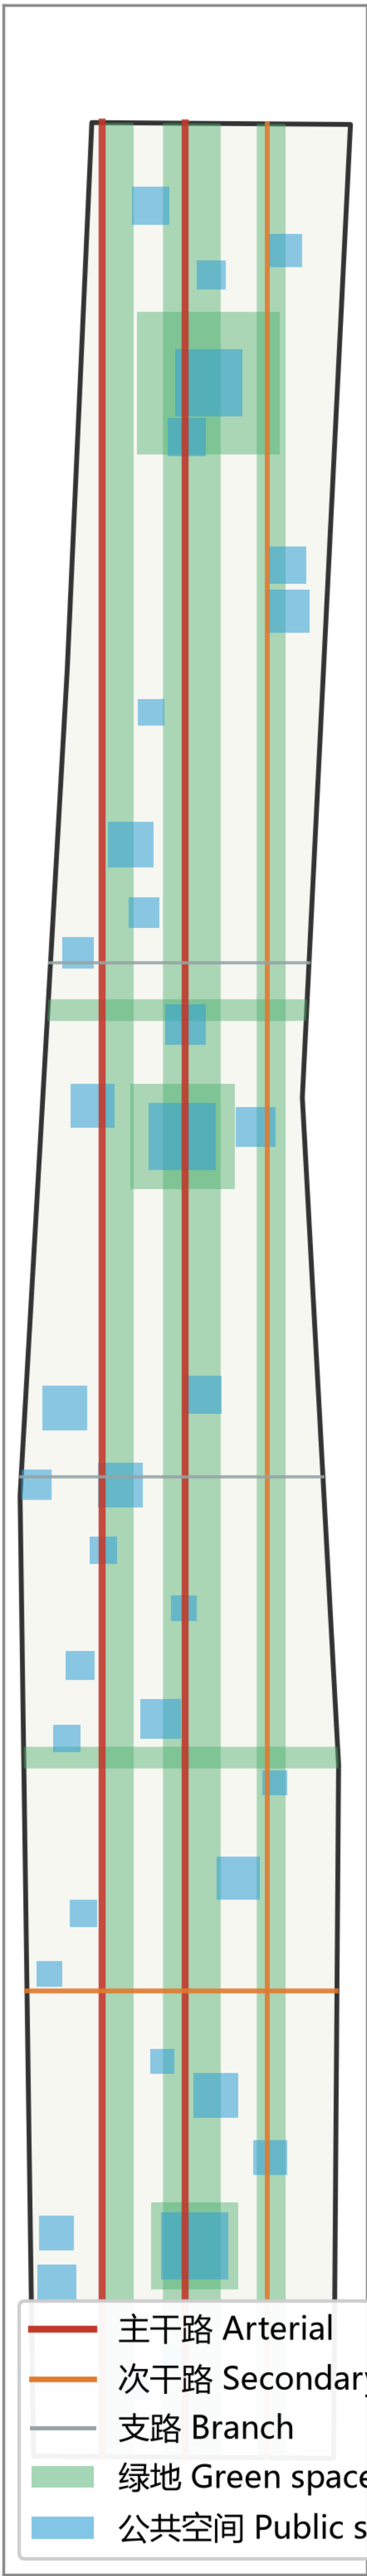

- 主干路 Arterial
- 次干路 Secondary
- 支路 Branch
- 绿地 Green space
- 公共空间 Public space

指标复算与证据 / Metrics Recalculation & Evidence

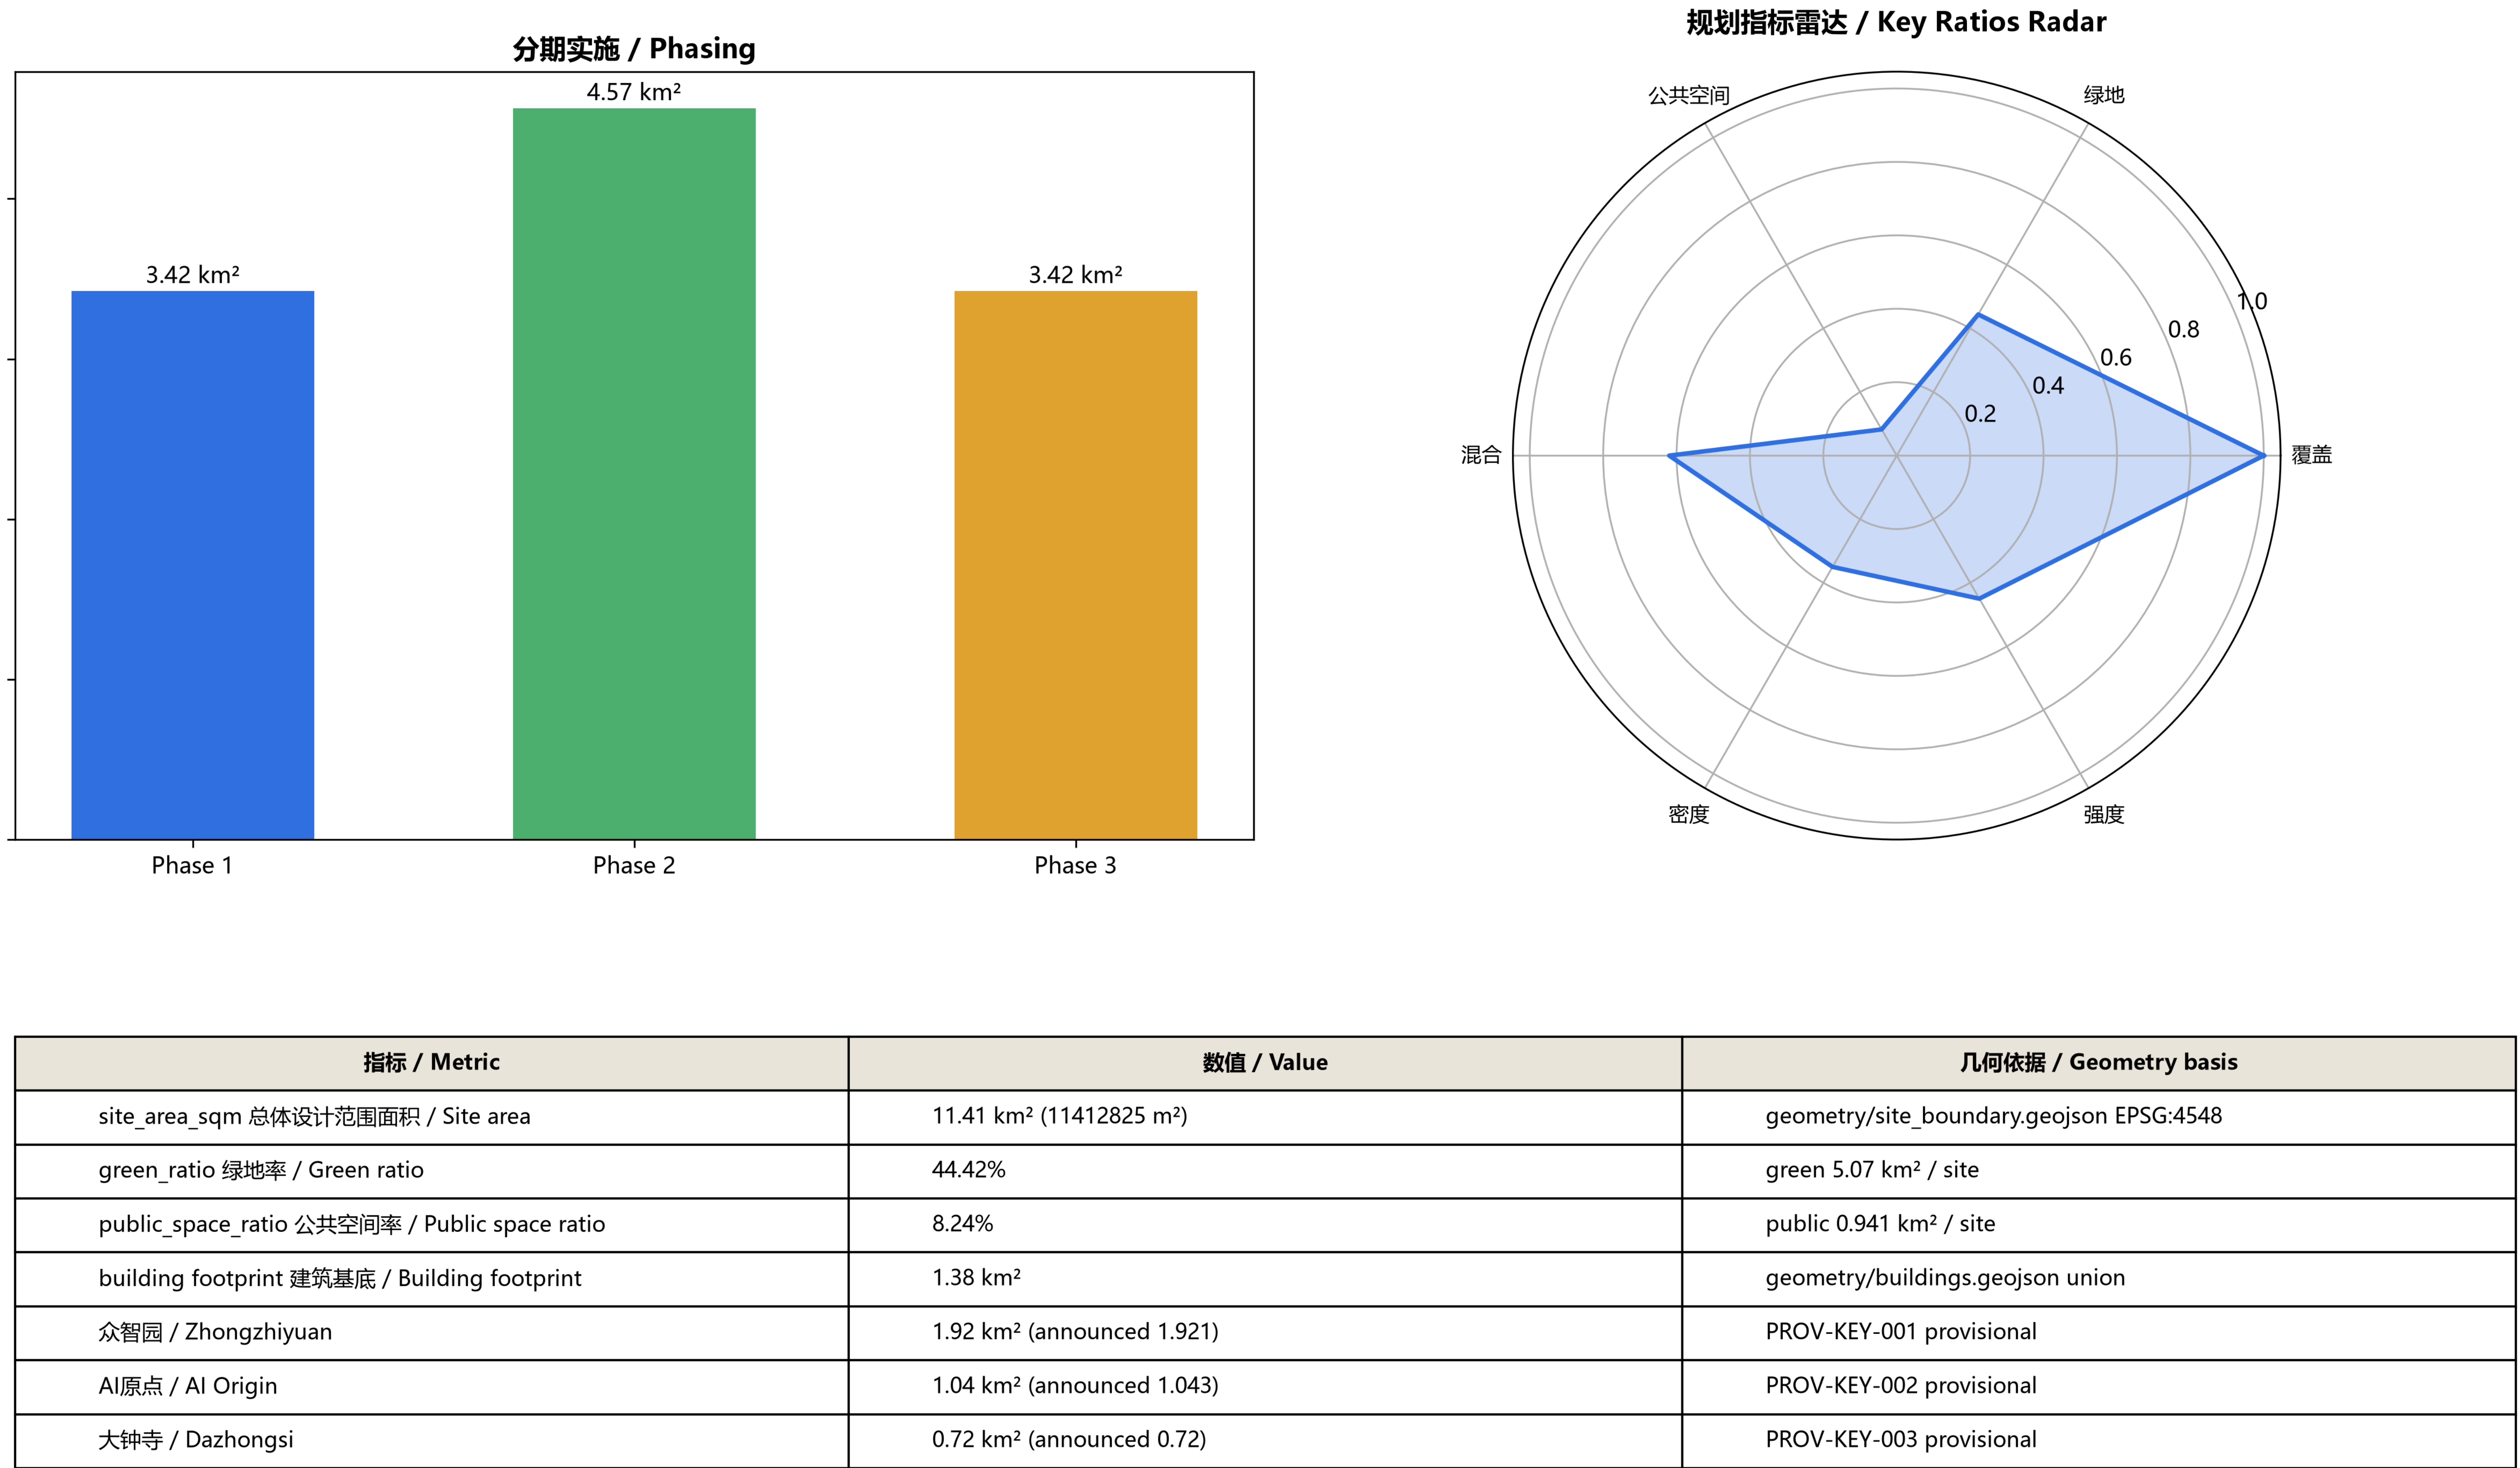

指标 / Metric	数值 / Value	几何依据 / Geometry basis
site_area_sqm 总体设计范围面积 / Site area	11.41 km² (11412825 m²)	geometry/site_boundary.geojson EPSG:4548
green_ratio 绿地率 / Green ratio	44.42%	green 5.07 km² / site
public_space_ratio 公共空间率 / Public space ratio	8.24%	public 0.941 km² / site
building footprint 建筑基底 / Building footprint	1.38 km²	geometry/buildings.geojson union
众智园 / Zhongzhiyuan	1.92 km² (announced 1.921)	PROV-KEY-001 provisional
AI原点 / AI Origin	1.04 km² (announced 1.043)	PROV-KEY-002 provisional
大钟寺 / Dazhongsi	0.72 km² (announced 0.72)	PROV-KEY-003 provisional