

JING-ZHANG FOR PEOPLE

人间京张

城市为人，AI为用。

百年京张AI创新带城市设计开源征集

Centennial Jing-Zhang AI Innovation Belt Open Call for Urban Design

概念性城市设计方案 | 2026



创新资源高度集聚，但人的生活更应当被关注

京张的关键不是继续堆叠技术资源，而是让创新能力转化为所有人共享的城市品质。



01 核心判断

创新机构、企业和人才的集聚只是起点。真正决定京张竞争力的，是知识、技术、资本和公共服务能否跨越园区、校园、社区、轨道与道路边界形成开放网络。

02 三类规划问题

- 创新协作** 为研发、测试、转化和企业成长提供适配空间。
- 城市适配** 以混合功能、存量更新和完整专项系统支撑高频协作。
- 生活品质** 让居民、儿童、老人、残障人士、服务人员和到访者共同受益。

03 统一成果体系

区域创新关系研究 → 主体与空间需求 → 总体空间系统 → 三处重点区域 → 公共文化体验 → 项目、分期与运营。

价值检验

既提高创新效率，也让更多人获得可达、可用、可感知的城市生活。



进地公园，开放空间骨架



二期建设，公共空间持续完善



交通基础设施，仍需缝合城市两侧

形成创新生产、公共服务、居住生活和蓝绿文化复合布局

功能分区服从三处重点区域的差异化定位，新增与更新空间按产业、生活、公共和基础支撑共同核算。

01 创新功能由北向南形成不同侧重

北部侧重共性技术与工程验证，中部侧重知识交流、早期研发和成果转化，南部侧重AI原生业态、商务交流、消费体验和城市服务。

02 用地分类与功能活动分层表达

概念用地建议遵循国土空间用地分类，创新交流、共享服务和AI场景作为功能属性叠加，不替代法定用地代码。


03 更新释放建筑量采用五类测试配比

当前推荐起点为创新研发40%、居住及阶段住宿20%、商业生活服务20%、公共文化与创新公共服务10%、共享技术与新型基础设施10%。

04 关键邻接关系决定混合质量

公共学习邻近校园与遗址，技术服务邻近研发与物流，居住邻近交通、社区服务与安静绿地。测试场景保持安全隔离。

总体功能与概念用地叠加

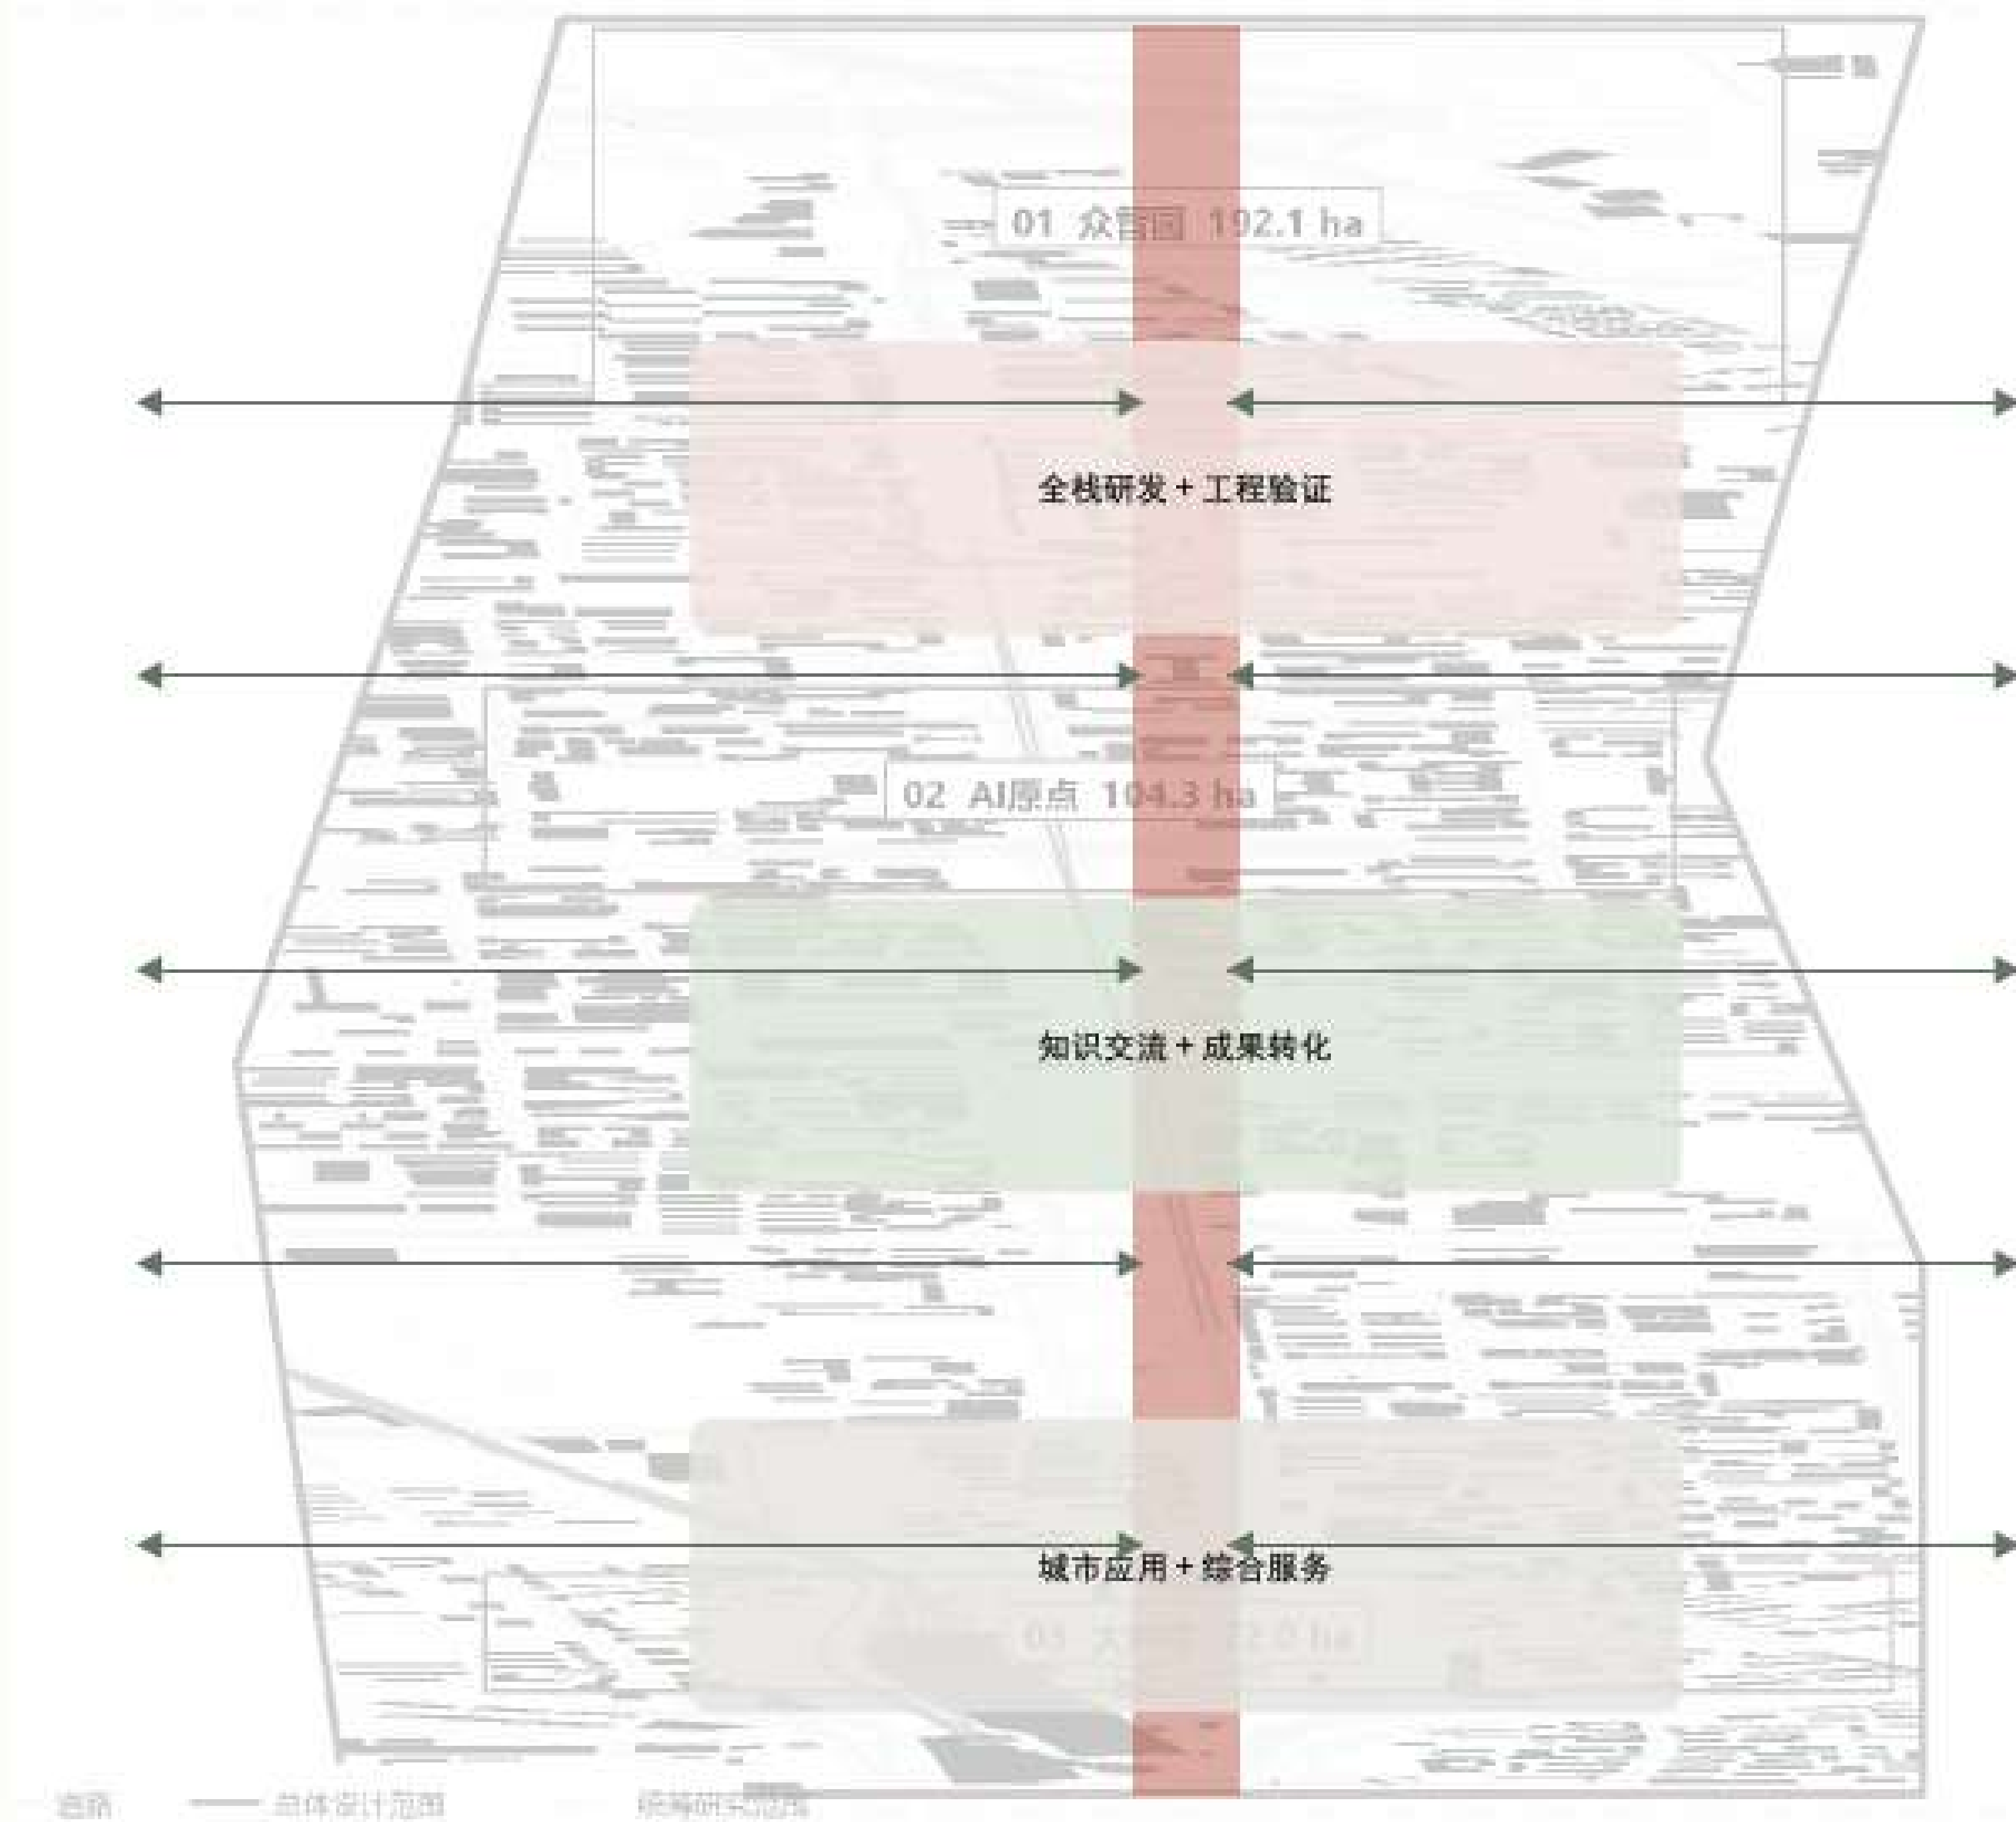

建议色系不代表法定用地

更新释放建筑量 | 推荐起点

创新研发与产业 40%

居住及阶段住宿 20%

商业及生活服务 20%

公共文化与创新服务 10%

共享技术与新基建 10%

关键邻接

公共学习	↔	校园 / 遗址
技术服务	↔	研发 / 物流
弹性创业	↔	轨道 / 生活
真实测试	↔	场景 / 隔离
居住	↔	交通 / 安静绿地

核心判断

用地保证可管理性，功能叠加支持创新协作，40:20:20:10:10用于检验产业、生活和公共服务是否同步。

概念用地

可管理

功能叠加

可协作

建筑容量

可承载

公共服务

可生活

蓝绿文化

可持续

众智园形成滨河公共界面与全栈创新单元复合布局

以清河和京张铁路遗址公园组织连续公共空间，将共享技术、成长研发、受控测试、成果交流和生活服务嵌入可步行街区。

01 双重蓝绿骨架组织建筑与公共空间

清河承担生态缓冲、雨洪和滨水慢行，遗址公园承担南北联系、历史展示和公共活动，横向公共联系进入建筑组团。

02 五类功能按创新过程相邻布局

共享技术位于多个组团共同到达位置，成长研发围绕共享庭院，受控测试邻近能源后勤，成果交流面向公共界面，生活服务靠近公交与安静绿地。

03 存量优先并形成向蓝绿空间递减的形态


临清河与遗址公园18—30米、普通更新24—45米、节点45—80米为概念测试；主要公共界面首层开放长度测试50%—70%。

核心判断


众智园以清河—遗址公园双重骨架为公共空间基础，以全栈过程组织功能相邻。以存量改造和分级开放形成花园型创新街区。

众智园概念总平 | 双重蓝绿骨架 + 全栈创新单元

所有线位、高度与边界均为概念建议

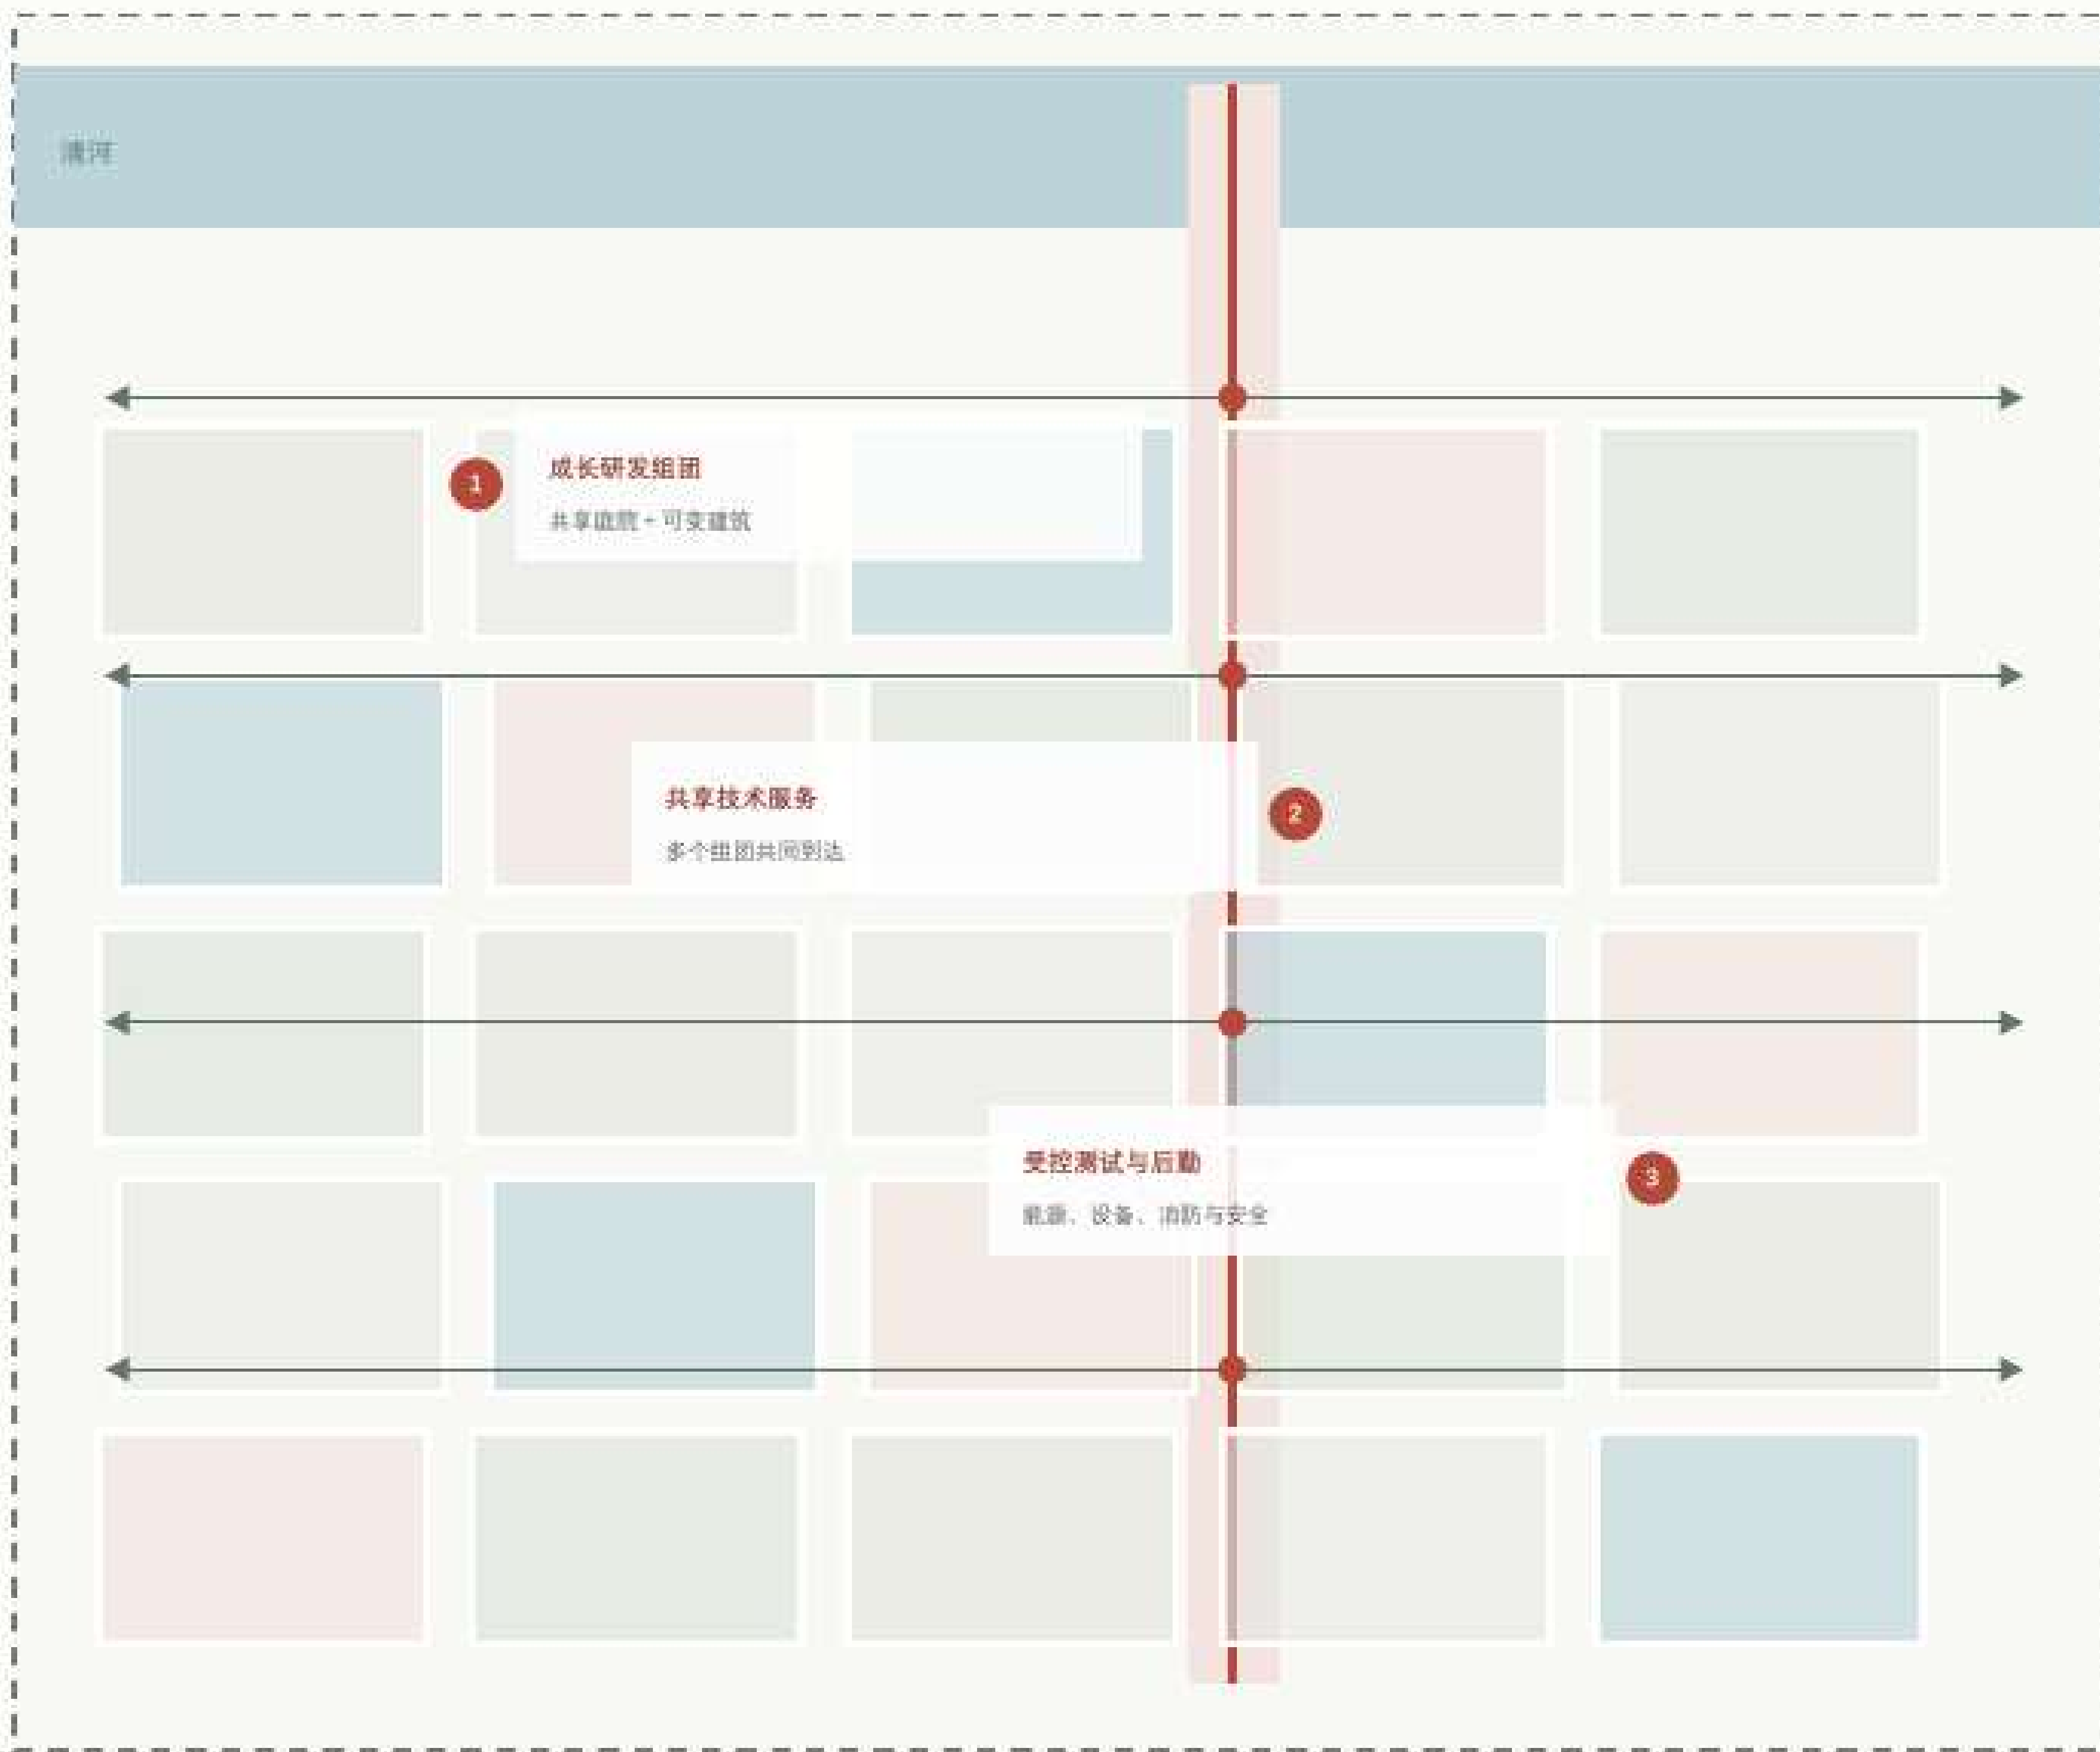

新增及更新释放建筑量 | 概念功能测试

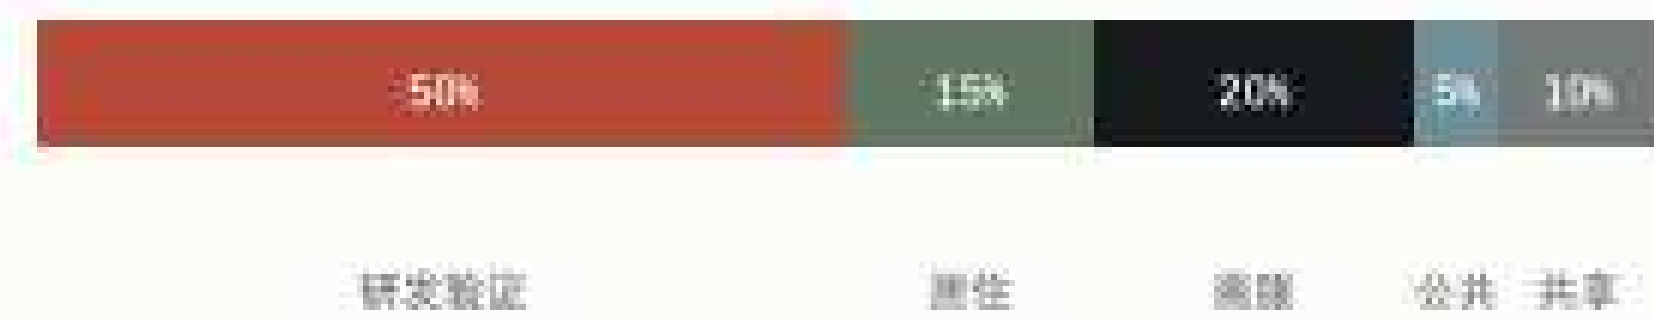

形态分级

清河 / 遗址 18—30m

普通更新 24—45m

交通 / 服务节点 45—80m


开放层级

公共开放 滨水 / 展示 / 生活

协作共享 技术 / 会议 / 设备

专业受控 测试 / 数据 / 后勤

清河—研发建筑—共享庭院典型关系

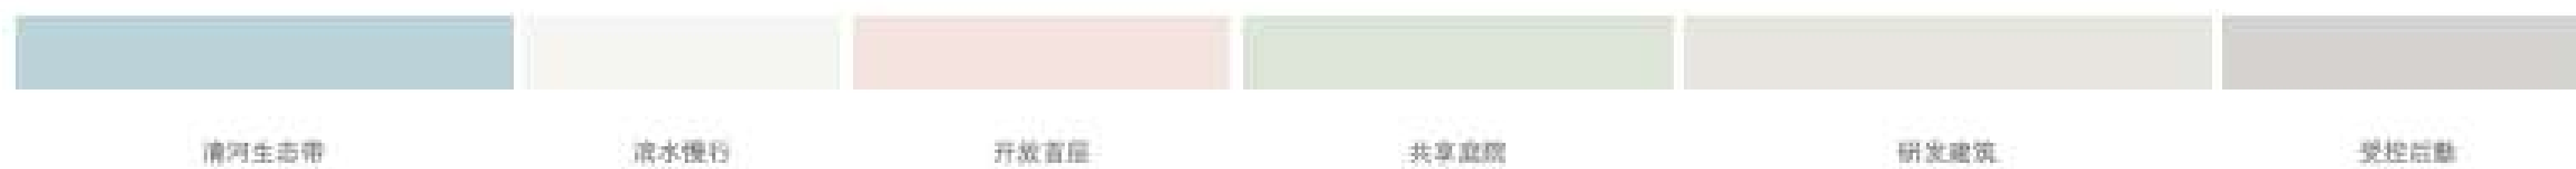

以人的实际任务组织场景设计与空间布局

设置10类日常场景与3类产业测试，分别检验城市服务和技术产品，并在三处重点区域及京张铁路遗址公园形成可到达、可运营、可评价的空间网络。

01 场景卡对应八项规划要素


每张场景明确人物、任务、地点、空间载体、运营者、时段、风险和指标；AI仅承担信息理解、资源匹配和辅助判断。

02 十类日常场景覆盖工作、学习与连续生活

工作学习进入共享技术、校城转化、遗产学习和共享首层；生活场景检验照护、办事、换乘、极端天气与夜间归家。

03 三类产业测试进入差异化空间

众智园承担专业验证，AI原点承担知识转化，大钟寺AI产业聚集区承担城市应用；全部测试须可停止并恢复正常使用。

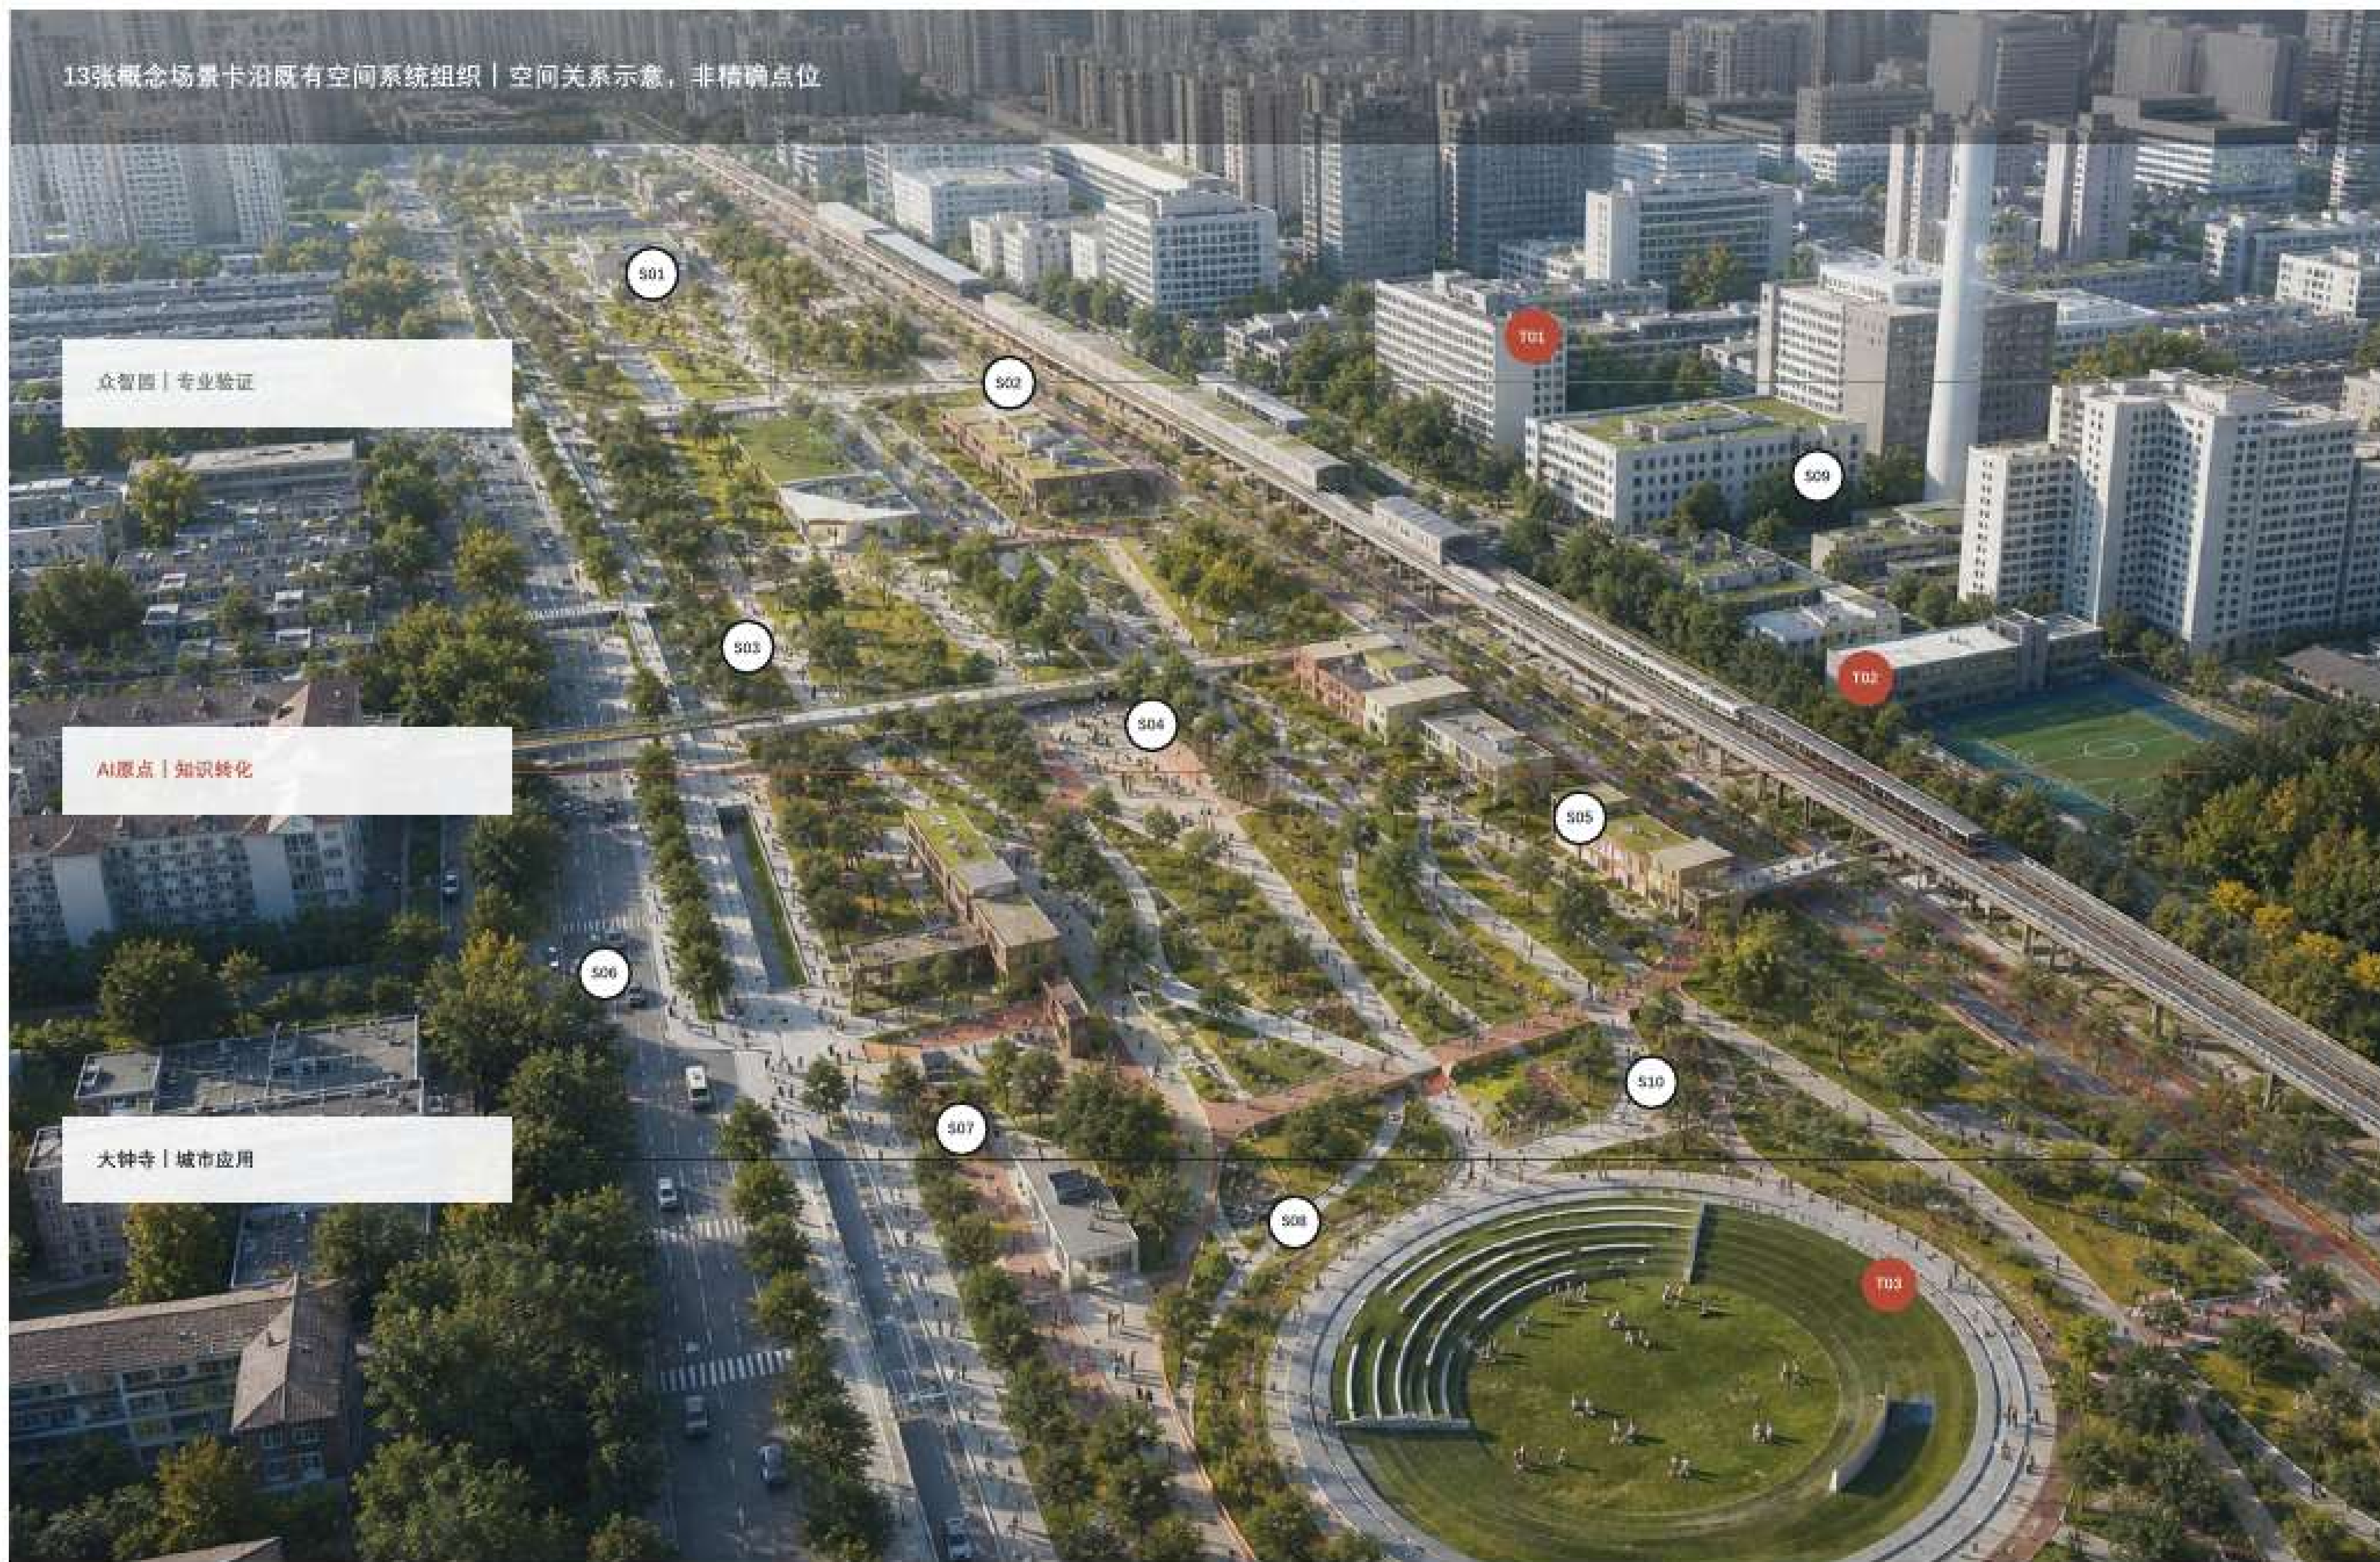

八项规划要素



人物



任务



地点



空间载体



运营者



时段



风险



指标

进入真实城市前的共同底线

● 人工服务并行

● 可以申诉纠正

● 最少必要数据

● 风险出现即停止

核心判断

AI场景不是设备清单，而是由具体空间承载、由责任主体运营，并接受不同人群压力测试的城市任务。

以十六项重点项目落实总体方案与分期建设

从公共骨架、交通蓝绿、生活服务和三处重点区域提取建设与运营单元，按照问题紧迫度、公共收益、前置条件和工程复杂度确定实施顺序。

01 项目库由空间方案直接生成


I2-01—16承接总体设计、三处重点区域及场景设计；ZY、OD、DZ局部编号与I2实施编号建立双向映射，避免重复统计。

02 三阶段表达实施条件而非确定年份

第一阶段推进调查、维护、连通和试行；第二阶段推进经论证的重点建设；第三阶段仅在法定、权属、资金和运营条件成立后实施。

03 规模和成本仅用于比较排序

S / M / L表示空间影响范围，成本I / II / III表示管理维护、一般更新与重大专项工程，不等同于投资估算或政府建设计划。

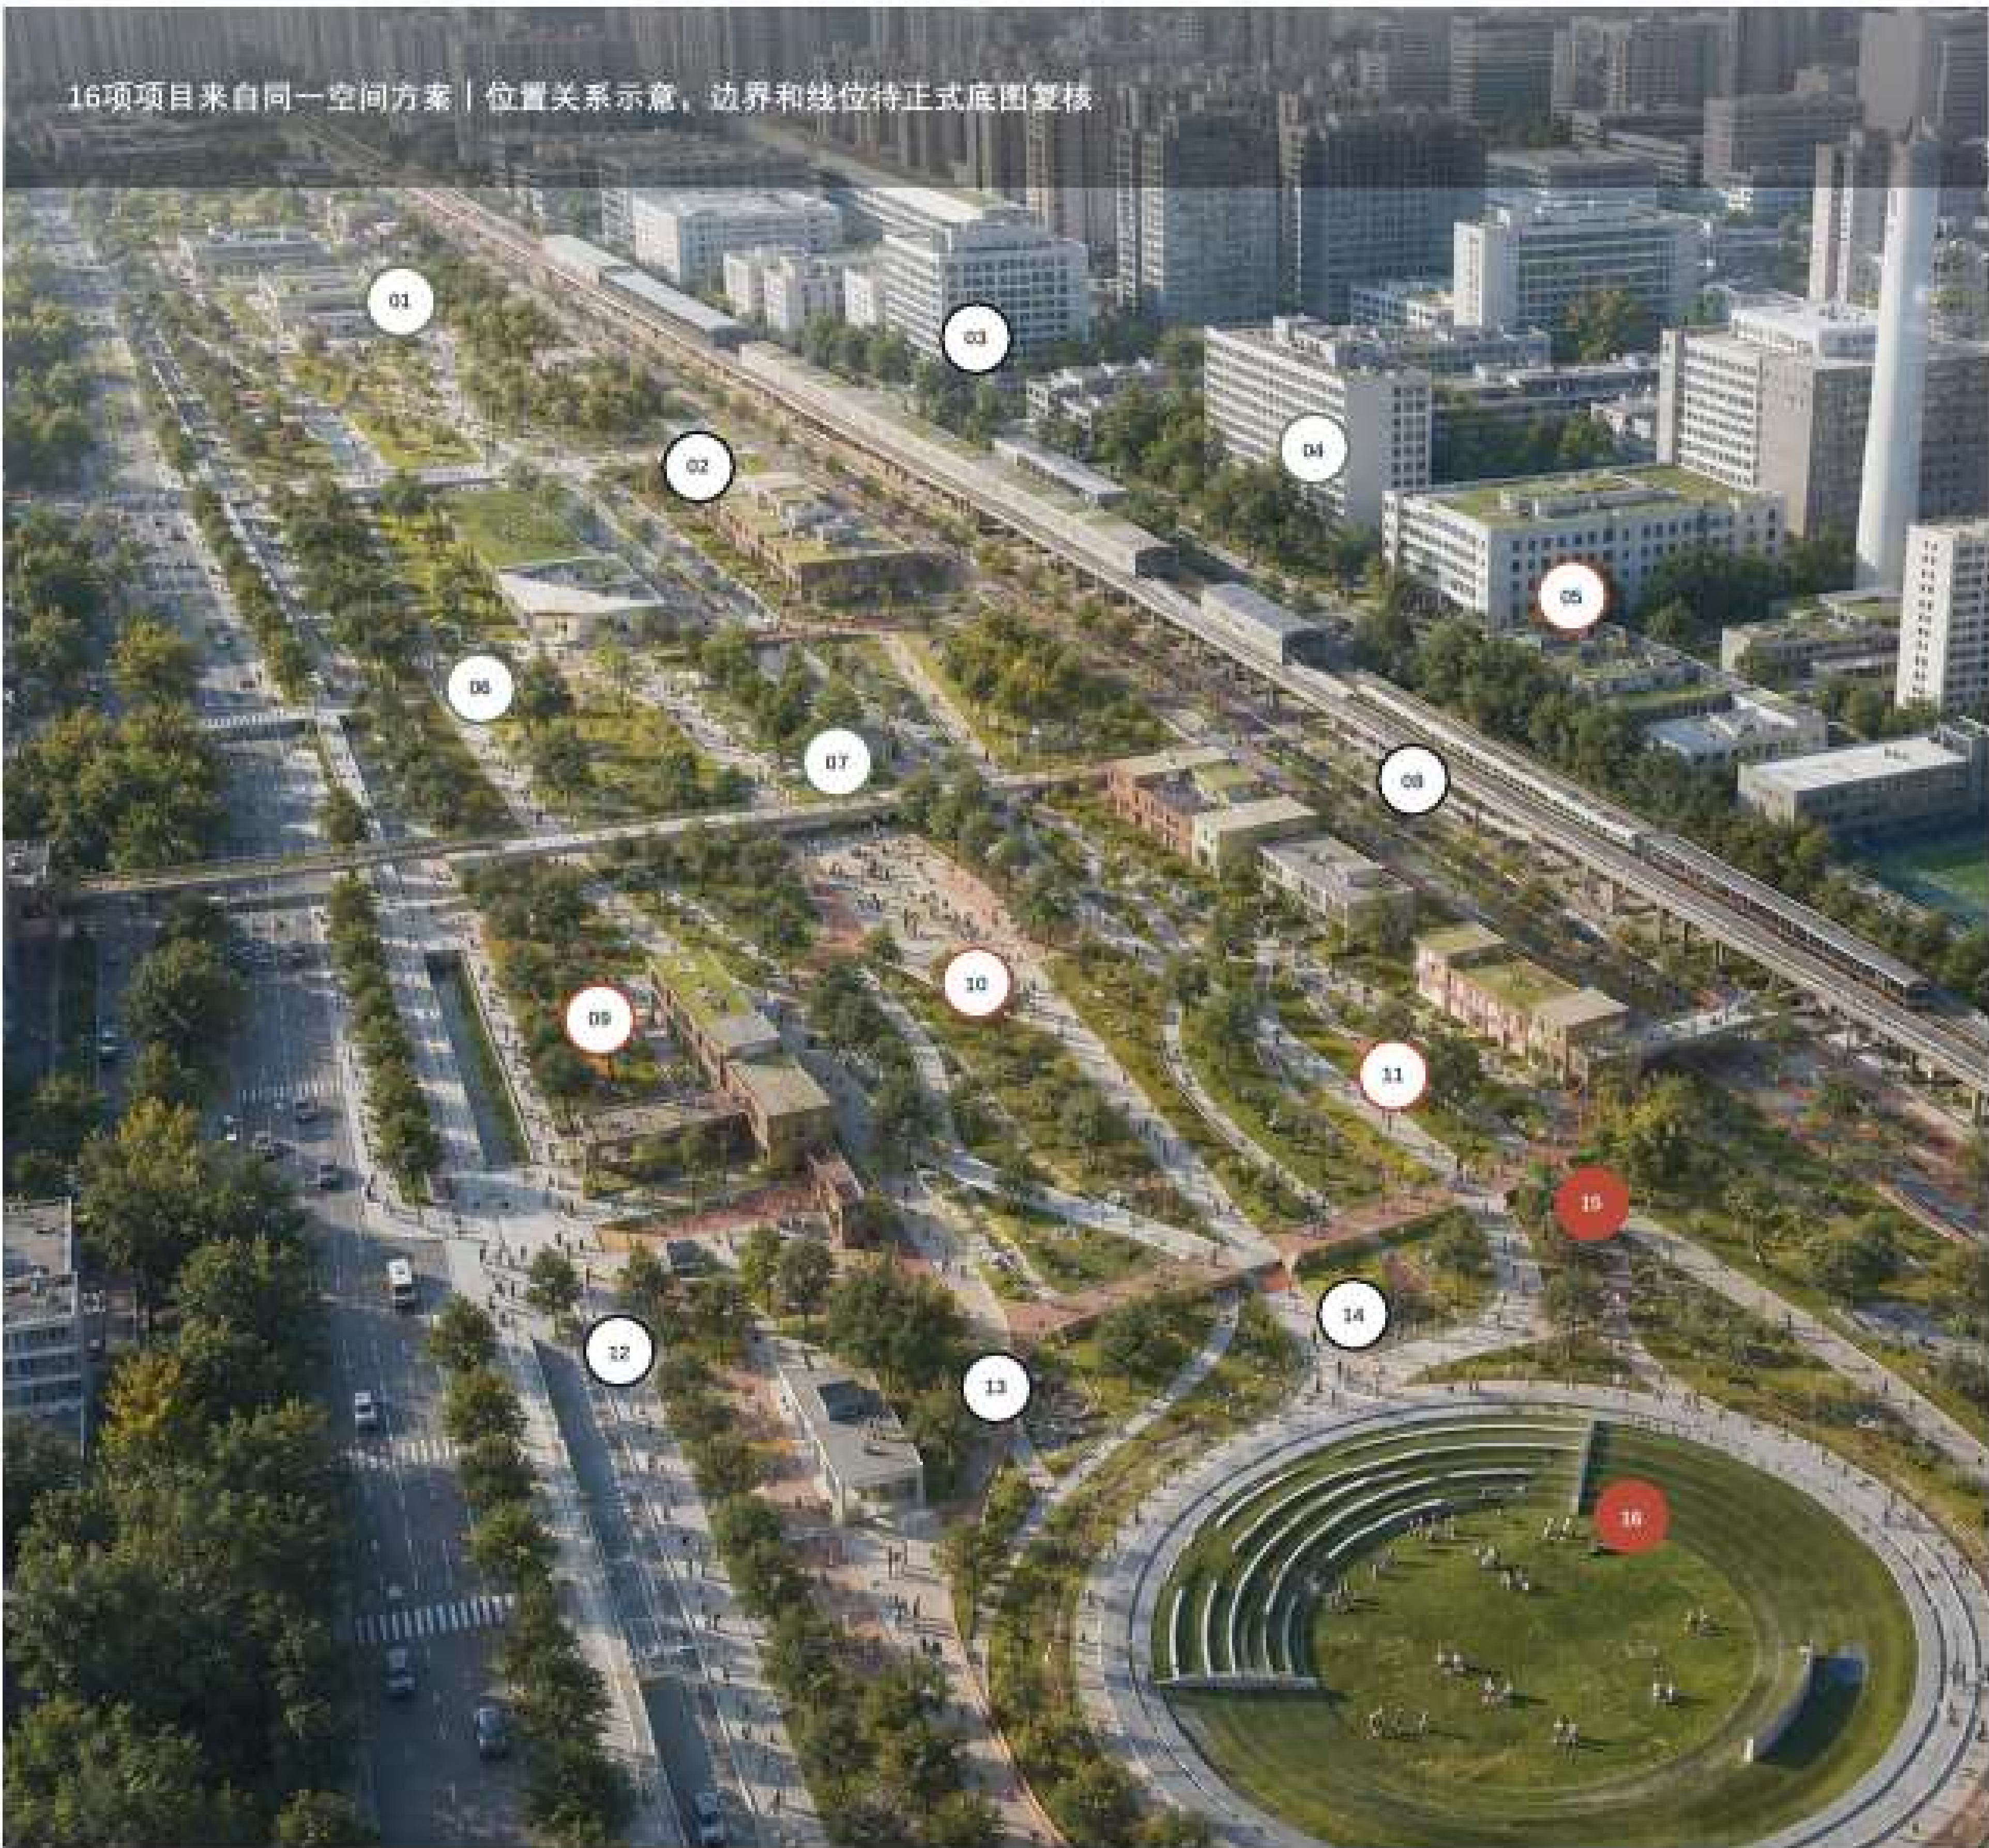

项目索引 | 阶段 / 规模—成本

- | | |
|----------------------------------|--------------------------------------|
| 01 I2-01 遗址公园骨柱
——二 L / III | 02 I2-02 东西断点修复
——三 L / III |
| 03 I2-03 六处轨道门户
——二 L / III | 04 I2-04 蓝绿雨洪网络
——三 L / III |
| 05 I2-05 生活服务补短
——二 L / III | 06 I2-06 清湾创新示范
——二 M / III |
| 07 I2-07 共享技术验证
——二 M / II | 08 I2-08 五环入口改善
——三 M / III |
| 09 I2-09 AI原点慢行
——二 M / II | 10 I2-10 铁路遗产学习
——二 M / II |
| 11 I2-11 创新与人才生活
——二 M / II | 12 I2-12 四象限步行
——三 M / III |
| 13 I2-13 活跃首层更新
——二 M / II | 14 I2-14 公园绿地复合
——二 M / II |
| 15 I2-15 三处贡献节点
——二 M / II | 16 I2-16 场景与受限测试
——三 S—M / I—II |

三阶段实施顺序 | 从获得授权时起计算

第一阶段

基础准备与低风险改善

调查摸底 / 维护修缮 / 路径连通 / 运营试行

第二阶段

重点建设与功能完善

经专业论证的公共空间 / 建筑更新 / 设施补短板

第三阶段

系统扩展与重大工程

法定 / 权属 / 资金 / 专项 / 长期运营条件同时成立

核心判断

先实施能够改善日常使用且风险可控的事项，再推进完成专业论证的重点建设。重大工程不得越过法定和工程条件。

编号映射：ZY-01/02/03→I2-06/07/08；ZY-04→I2-07/08；OD-01/02→I2-09/10；OD-03/04→I2-11；DZ-01→I2-12；DZ-04→I2-13；DZ-02/03→I2-14；DZ-05→I2-12/13；I2-15/16叠加对应节点与场景。