


图 6 · 综合索引图 —— 七类要素线性展开（北朝右）

Fig.6 Composite Index — linear unfolding along the Jingzhang heritage corridor (north to the right)

图件 FIGURE

▮ 边界为 provisional 临时边界（基于公告文字四至推定），非 official 边界；正式几何发布后整体重算

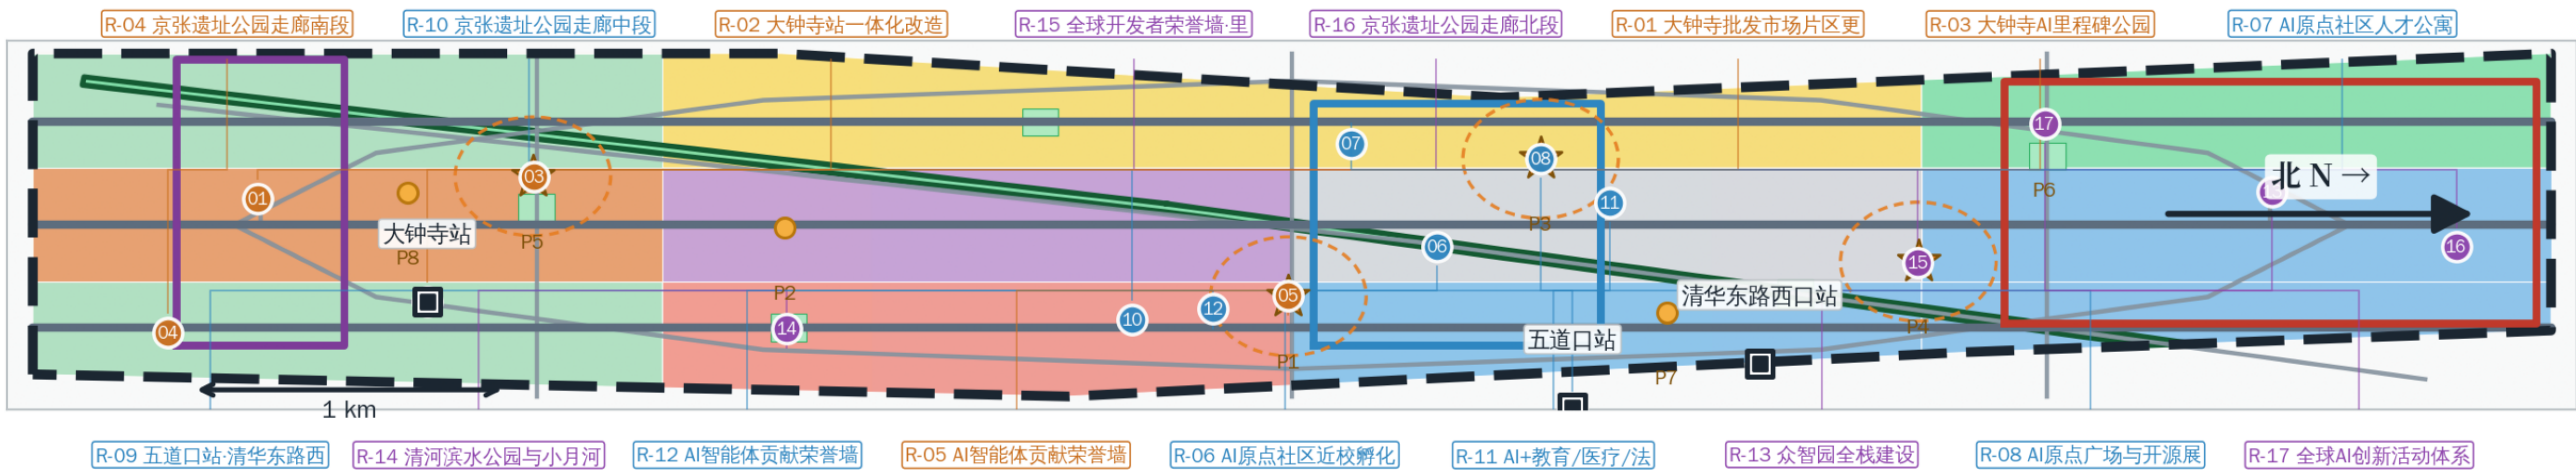

图例 · 七类索引要素

- 近期 2026-2028
- KA-1 众智园
- 京张遗产走廊 (约7km)
- 主干路 ×3
- AI 朝圣地标 ×4 (触点)
- 公共空间节点 ×8
- AI 场景服务半径 (300 m 概念)
- 轨道站 ×3 (示意位)
- 概念建筑基底 ×34
- 中期 2028-2030
- KA-2 AI 原点社区
- 次干路 ×3
- 蓝绿慢行环
- 远期 2030-2035
- KA-3 大钟寺
- 总体设计边界 (provisional)

项目索引 R-01~R-17 (17 项, 全部条件式)

- | 近期 2026-2028 | 中期 2028-2030 | 远期 2030-2035 |
|------------------|--------------------|-------------------|
| 01 大钟寺批发市场片区更新 | 06 AI 原点社区近校孵化带 | 15 众智园全栈建设 |
| 02 大钟寺站一体化改造 | 07 AI 原点社区人才公寓 | 14 清河滨水公园与小月河走廊 |
| 03 大钟寺AI里程碑公园 | 08 AI 原点广场与开展展示节点 | 15 全球开发者荣誉墙·里程碑公园 |
| 04 京张遗址公园走廊南段 | 09 五道口站·清华东路西口站一体化 | 16 京张遗址公园走廊北段 |
| 05 AI 智能体贡献荣誉墙一期 | 10 京张遗址公园走廊中段 | 17 全球AI创新活动体系 |
| | 11 AI+教育/医疗/法律场景铺开 | |
| | 12 AI 智能体贡献荣誉墙二期 | |

数据来源：六层 provisional 临时几何（公告四至推定）| 总体设计 11.413 km² · 重点区 3.693 km² · 12 用地多边形 · 道路 58.78 km · 绿地率 2.8958%（复算值）

aplaybox / jingzhang-ai-artery · P13 · 2026-08

核心指标 (metrics.json 复算)

11.413 km ²	3.693 km ²
总体设计范围 (公告 ≈11.4)	三处重点区合计 (≈368.4 ha)
12 块	58.78 km
用地多边形 (3x4 provisional)	道路中心线 (11 条复算)
2.8958%	0.80%
绿地率 green_ratio	公共空间率 public_space_ratio
4 个	17 项
AI 朝圣地标 (要求 ≥3)	条件式更新项目 (R-01-R-17)

校验与证据链

· 公告任务 1.3-1.5	17/17 PASS
· Agent 任务	6/6 PASS
· Mandatory 标准	5/5 PASS
· 设计深选项	15/15 PASS
· Provisional	已标注
· 法定控规条件	unknown → official

边界声明：全部边界与派生指标为 provisional（依公告四至推定），非 official；concept_furunknown；official
几何与控规条件发布后整体重算。开放共创建议，不替代正式规划与政府审批。

图 6 · 综合索引图：项目 R-01~R-17 / 遗产走廊 / 道路层级 / 三重点区 / 节点 / AI 触点 (含 300m 服务半径图) / 分期



图 1 · 总体场地与证据链概览

数据来源：六层 provisional 临时几何（公告四至推定）| EPSG:4326 (复算 EPSG:4548) | 全部数值与 metrics.json 一致 | aplaybox · 京张100-AI 大动脉



图 2 · 用地结构与三层范围 (12 块 3x4 provisional)

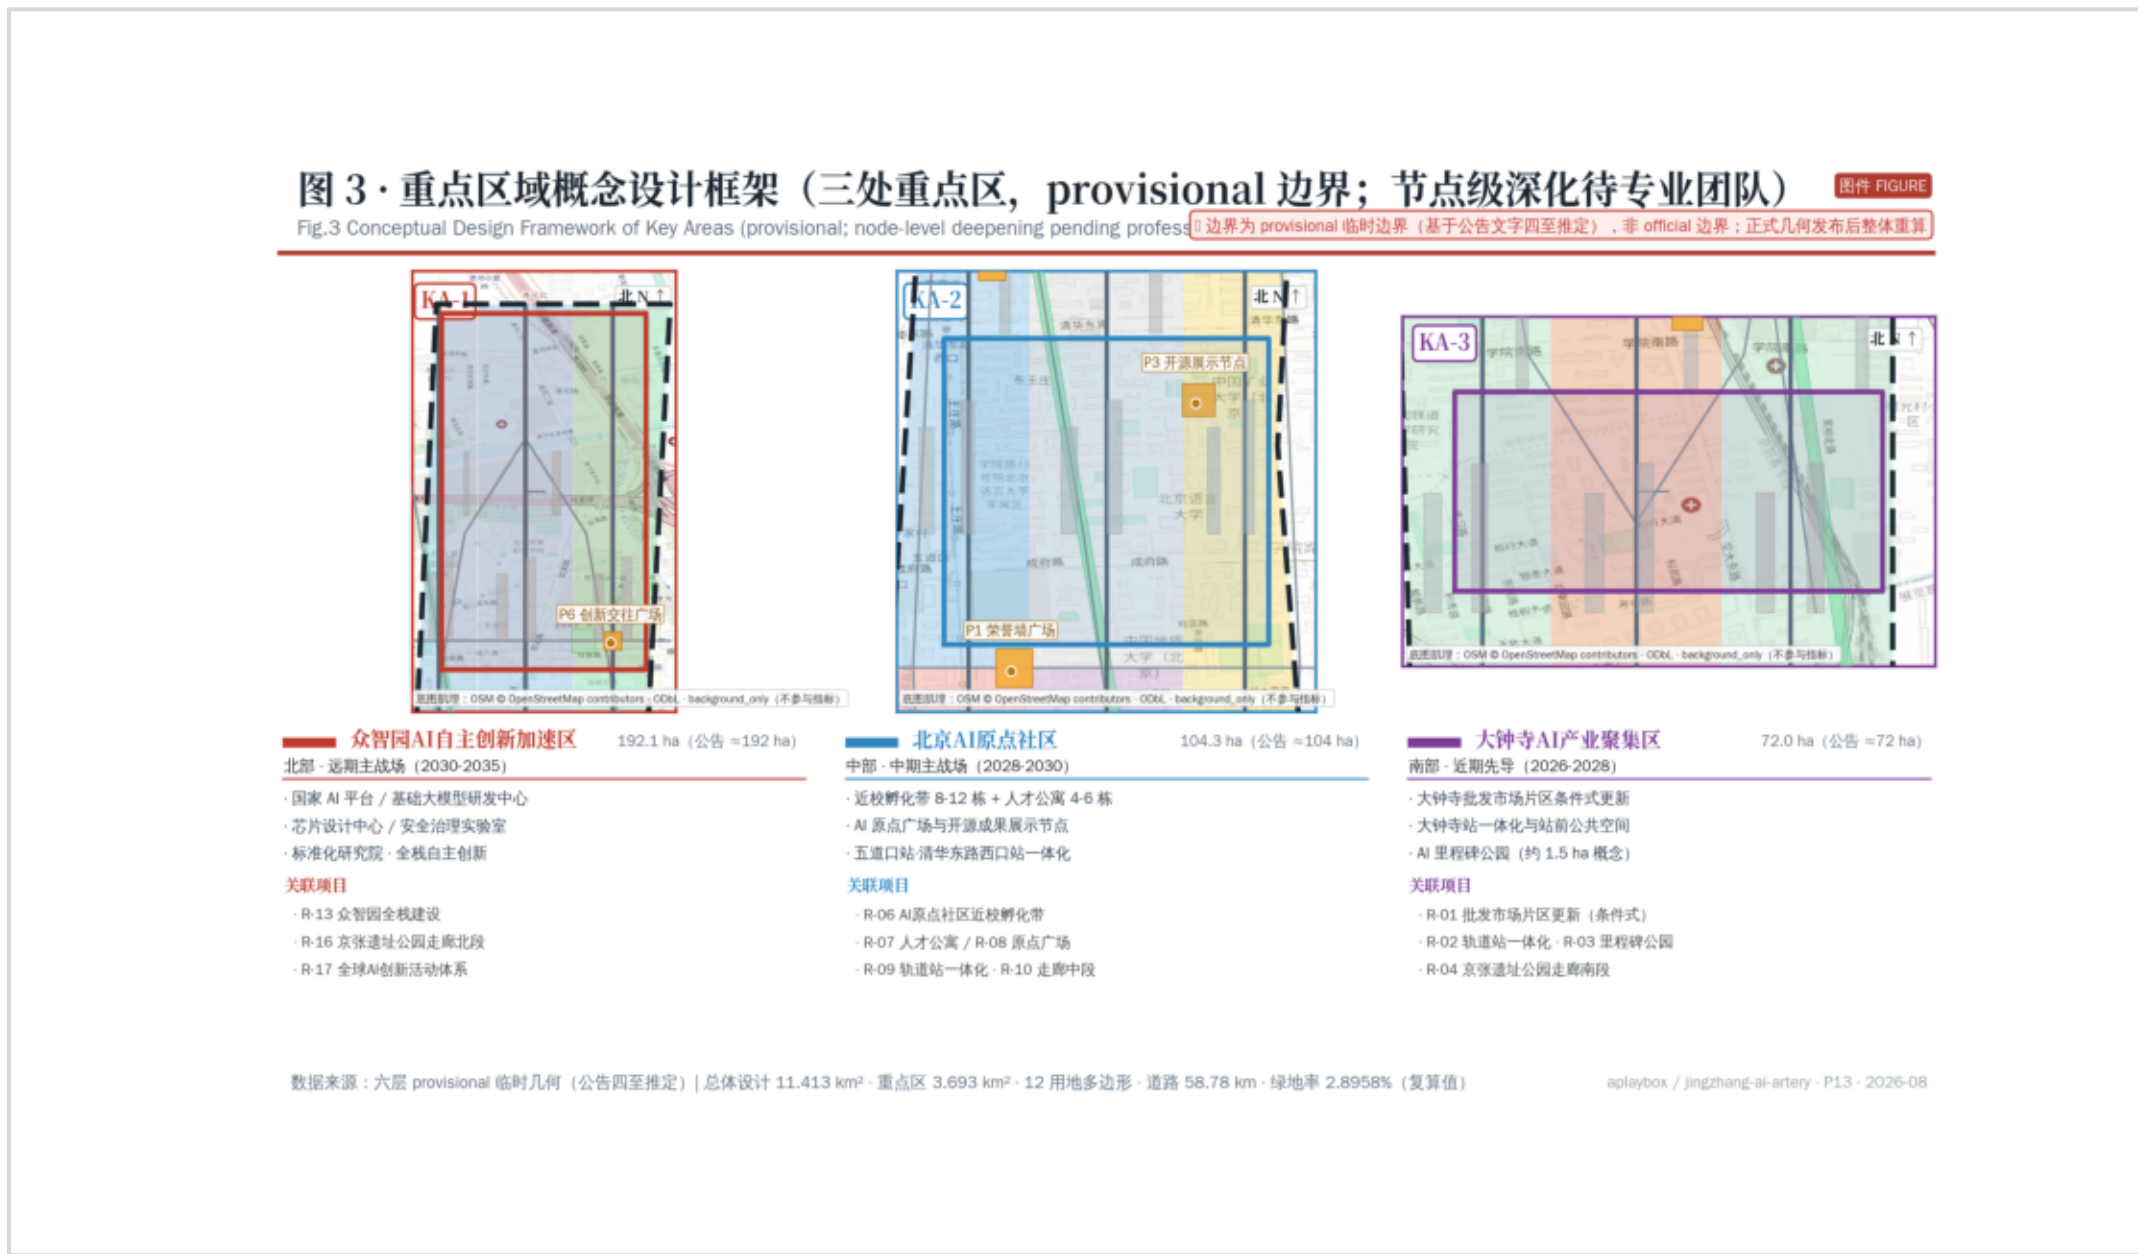


图 3 · 重点区域概念设计框架 (三处重点区, provisional 边界; 节点级深化待专业团队)



图 4 · 交通慢行与蓝绿公共空间复合系统