

# Why Jing-Zhang: The Openline 100


Urban design proposal for the Haidian Jingzhang heritage corridor • A3 plate book

This book collects 24 plates, all re-rendered on real OSM urban fabric and proposal geometry.


The full narrative lives in [proposal.md](#) / [proposal.en.md](#) and [report/proposal.html](#).

Graphic standard: Sasaki v1.2 (palette / type scale / scale bars / north arrows / title blocks).

Openline 100 Studio • kenshin-ai-101 • 2026-08 • v1.2

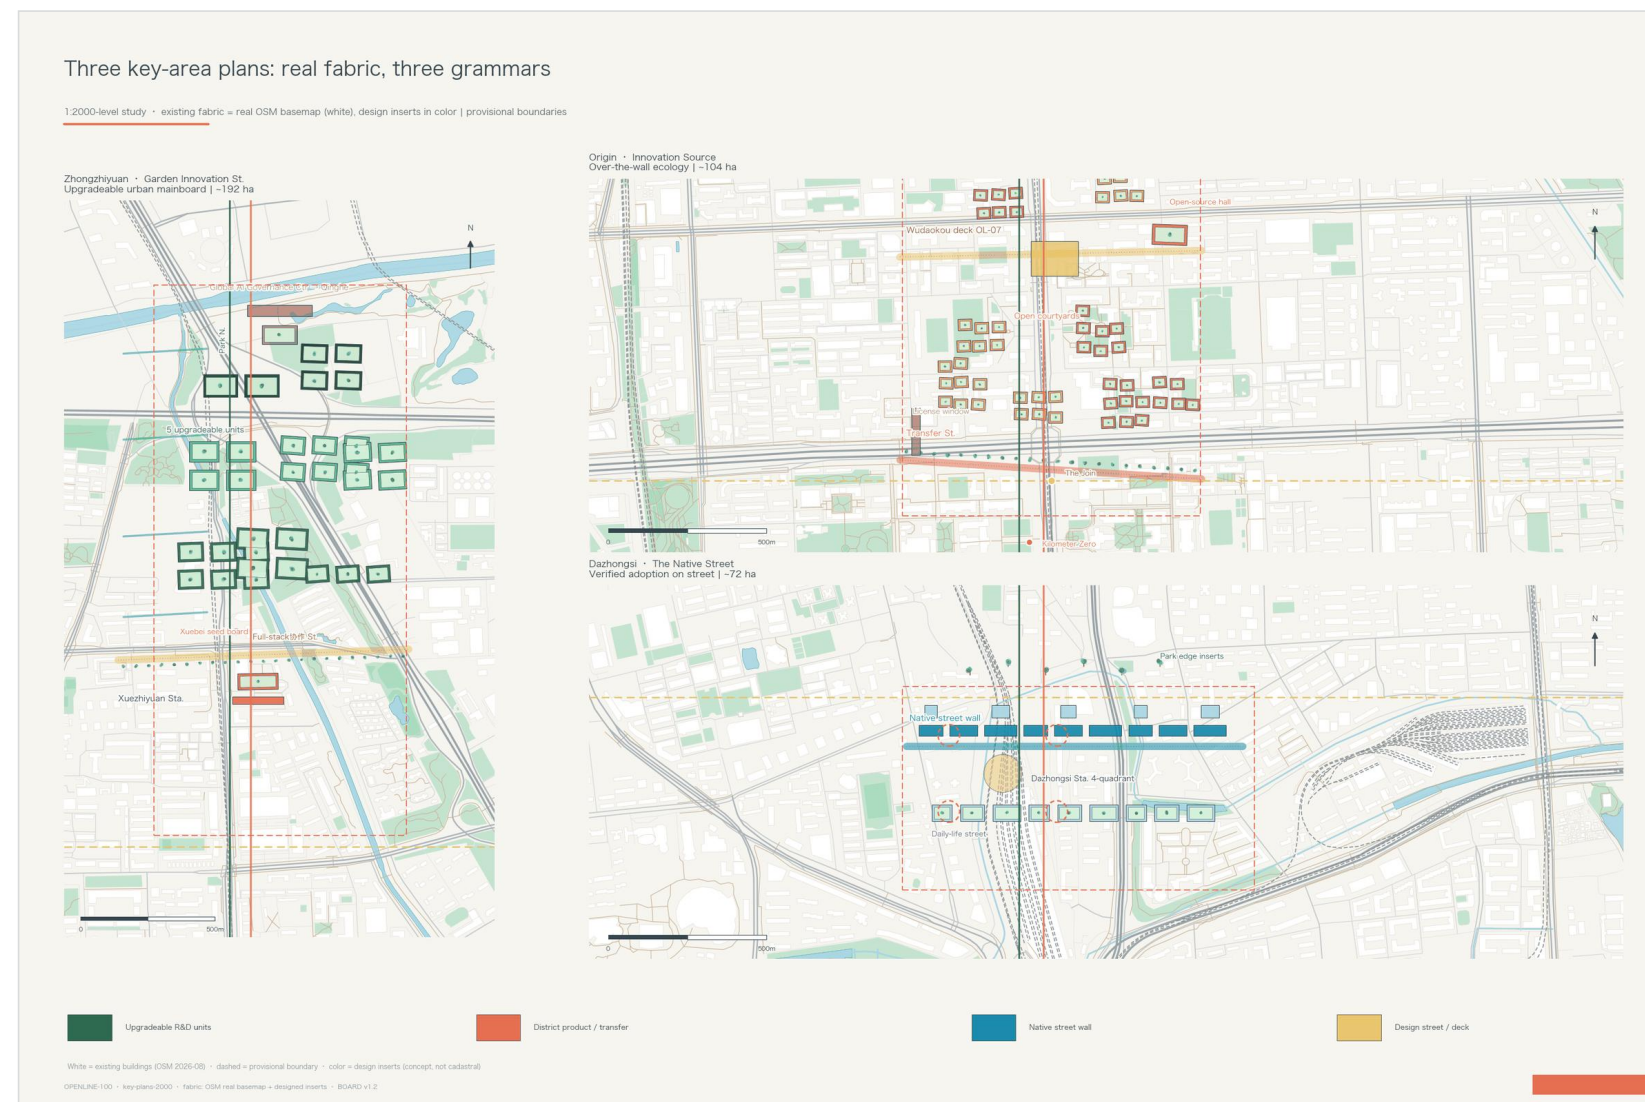




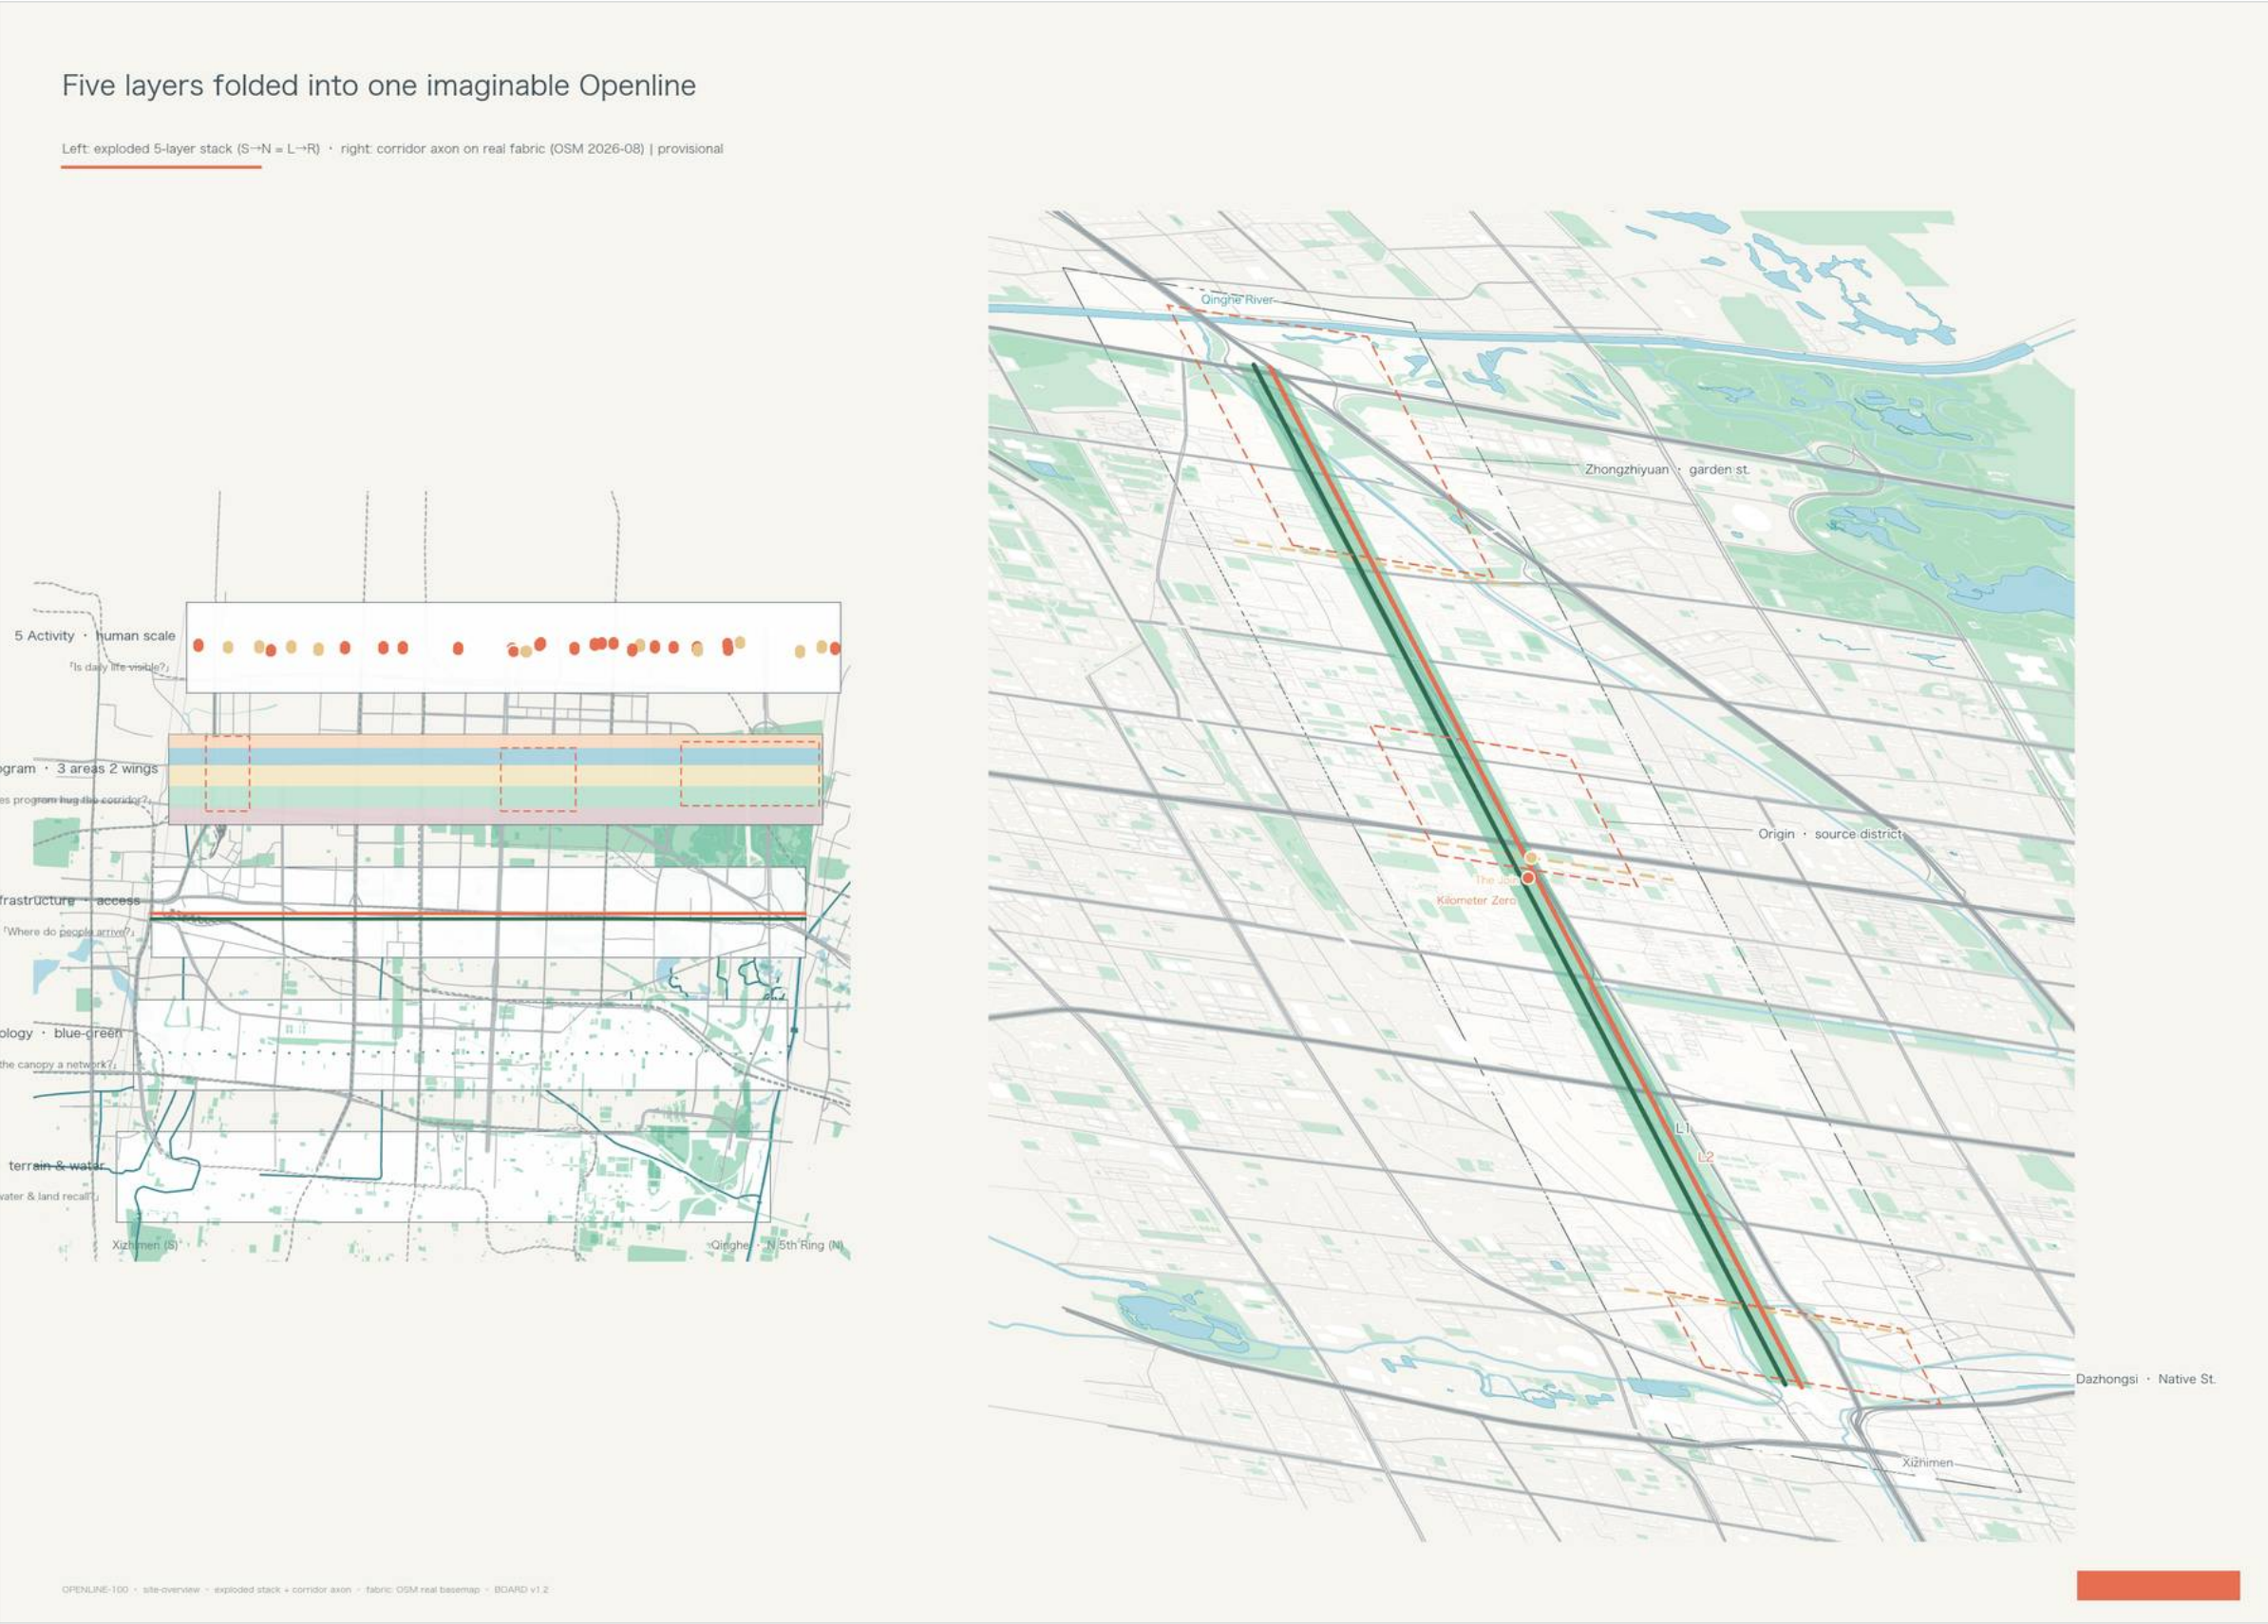


01 Site overview: five-layer structure and corridor axonometric



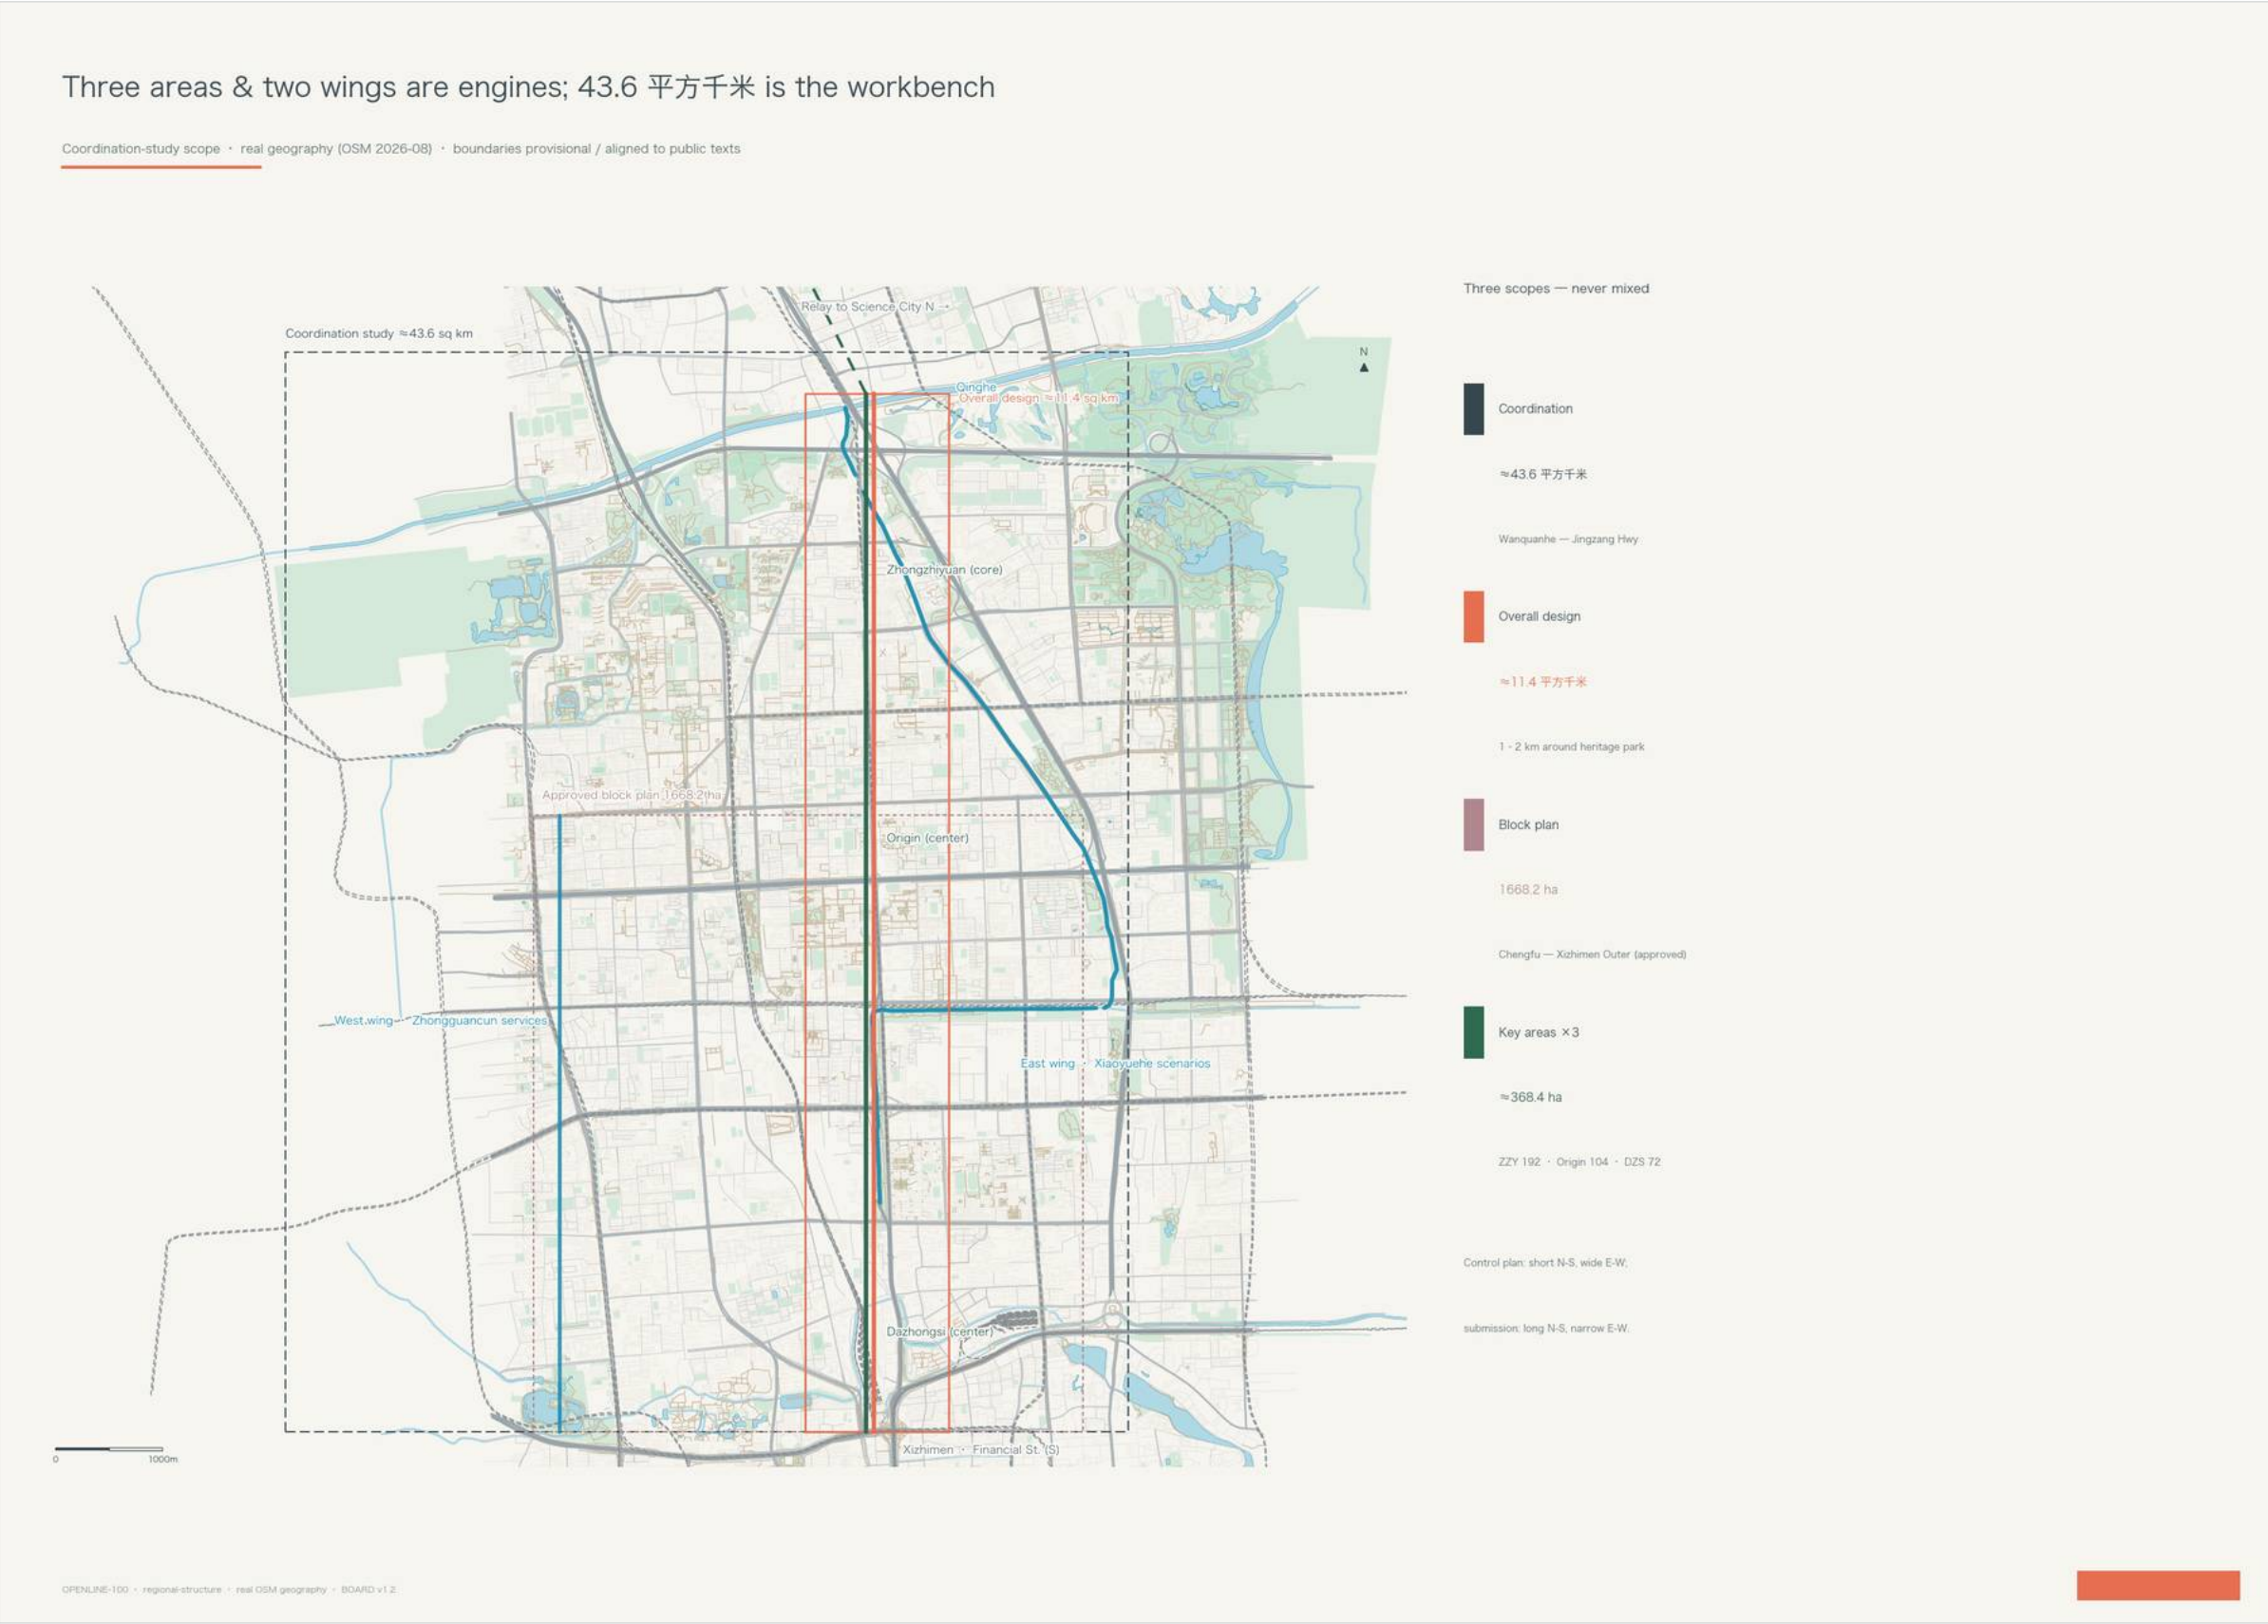

02 Regional structure: the corridor in northwest Beijing

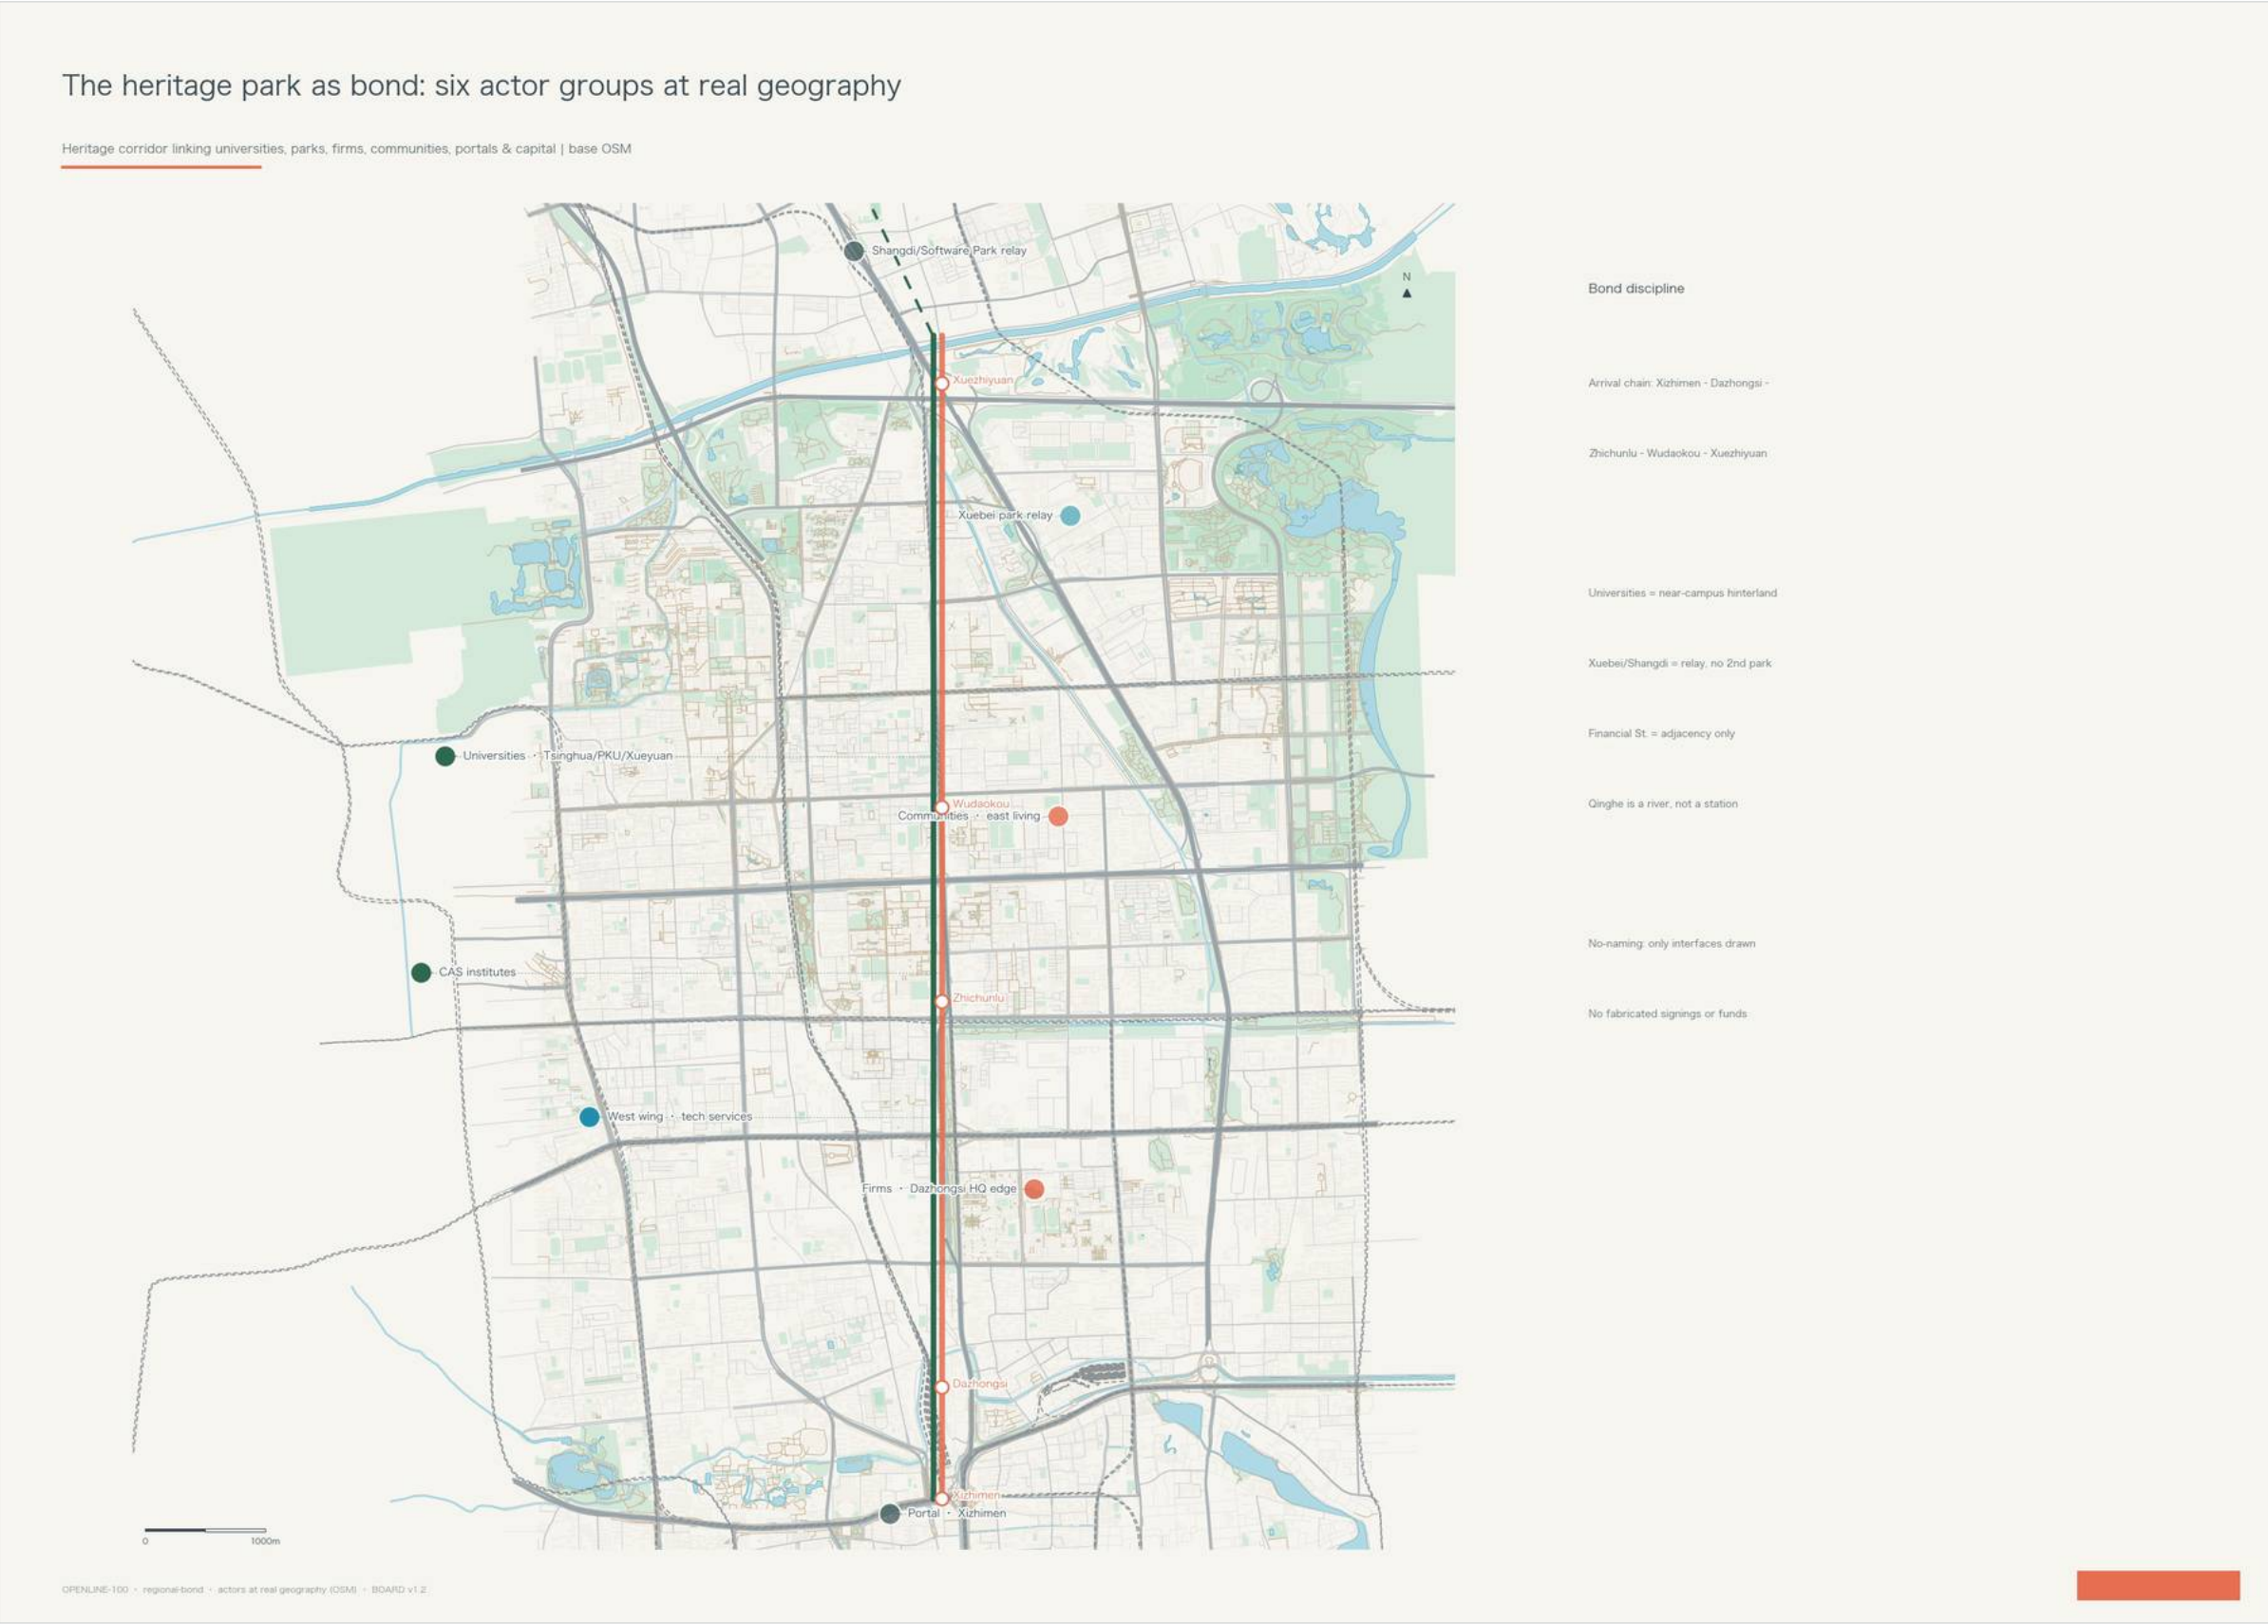

### 03 Regional bond: university, innovation and cultural ties





04 Land use and structure: one spine, three cores, five segments




05 Three key areas: Co-Wisdom Garden, Origin, Dazhongsi



Three key-area plans: real fabric, three grammars

1:2000-level study • existing fabric = real OSM basemap (white), design inserts in color | provisional boundaries

Zhongzhiyuan • Garden Innovation St.  
Upgradeable urban mainboard | ~192 ha

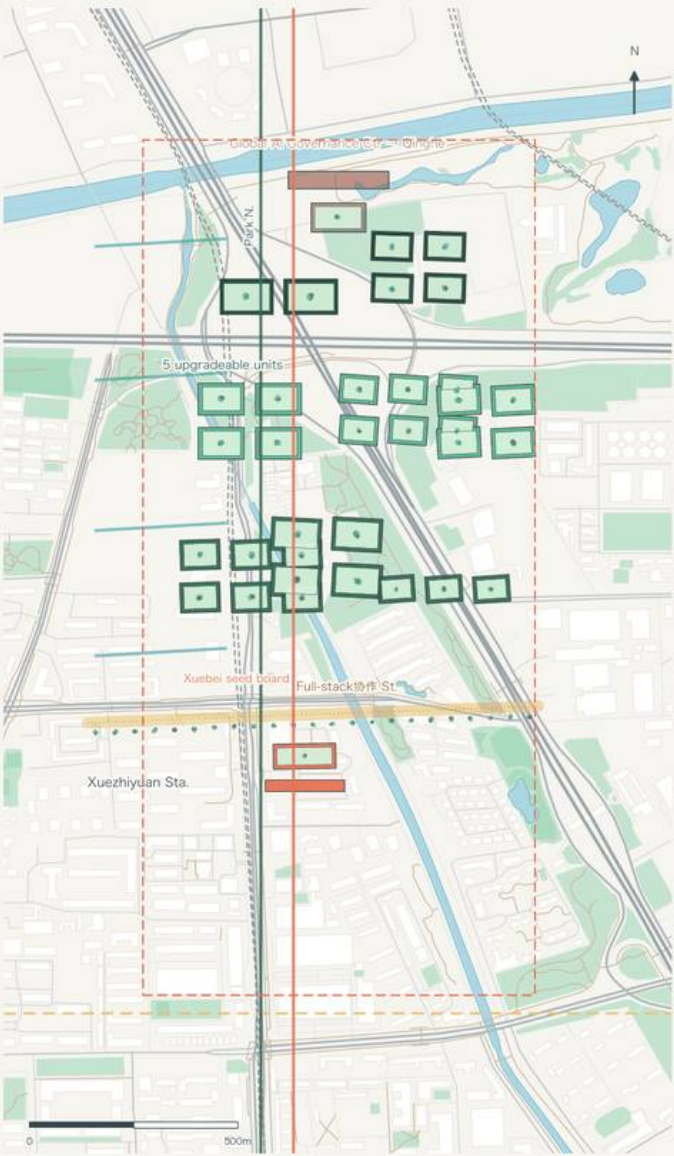

Origin • Innovation Source  
Over-the-wall ecology | ~104 ha



Dazhongsi • The Native Street  
Verified adoption on street | ~72 ha



Upgradeable R&D units

District product / transfer

Native street wall

Design street / deck

White = existing buildings (OSM 2025-08) • dashed = provisional boundary • color = design inserts (concept, not cadastral)

OPENLINE-100 • key-plans-2000 • fabric: OSM real basemap • designed inserts • BOARD v1.2

06 1:2000 key-area masterplans on real OSM urban fabric

Massing follows the block; the skyline grows no towers

Top: white-model axons per area (concept heights) · bottom: S→N skyline along the park



OPENLINE-100 · key-massing-skyline · concept heights, caps yield to official parcels · BOARD v1.2

## 07 Massing and skyline control




## Six typical streets, one Openline grammar

Section series A - F • not engineering • walking  $\geq 50\%$  at all times • robot band never becomes car lane

A • L1 Fact Line (walkable rail)



B • L2 Service Line (stations dock)

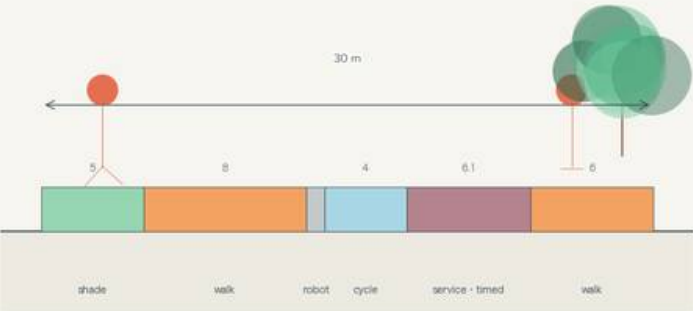


C • Collaboration St. (logistics behind)




D • Transfer St. (windows on edge)



E • Native St. (trial / life split)

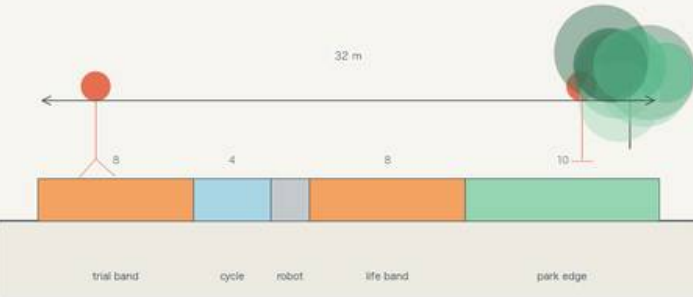

F • Deck (e-vehicle / people / view)

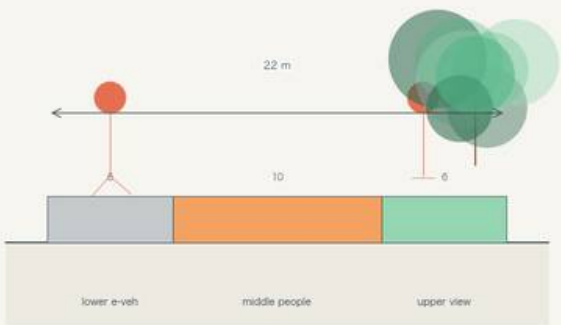


OPENLINE-100 • key-sections • walking  $\geq 50\%$  always • BOARD v1.2


## Five places — cut them open and you know them

Real place sections: courtyard / license window / deck / arrival / Qinghe edge


01 Zhongzhiyuan • courtyard & park

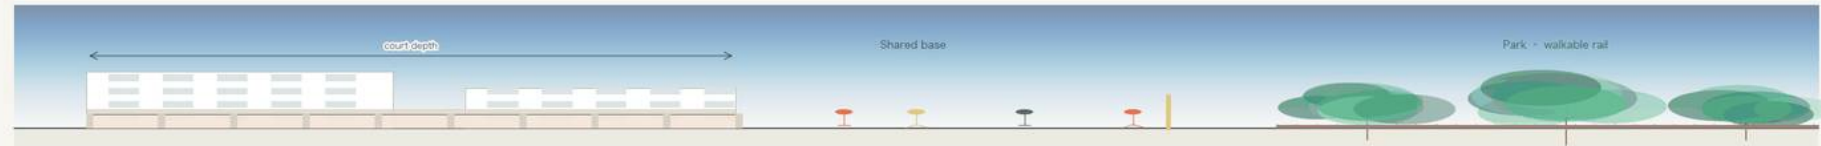


02 Origin • license window & KMO

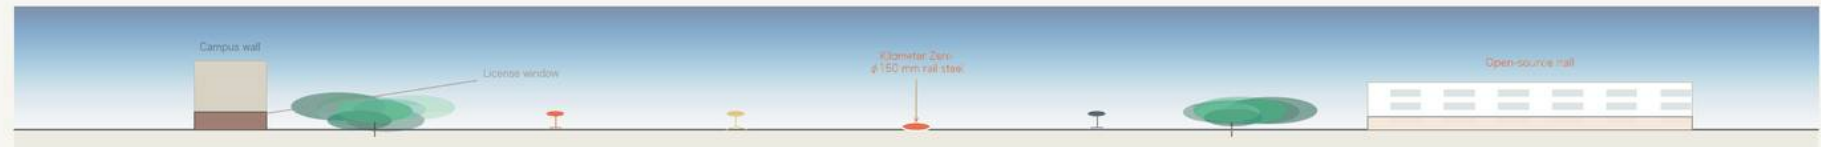


03 Wudaokou • 3-level stitch deck

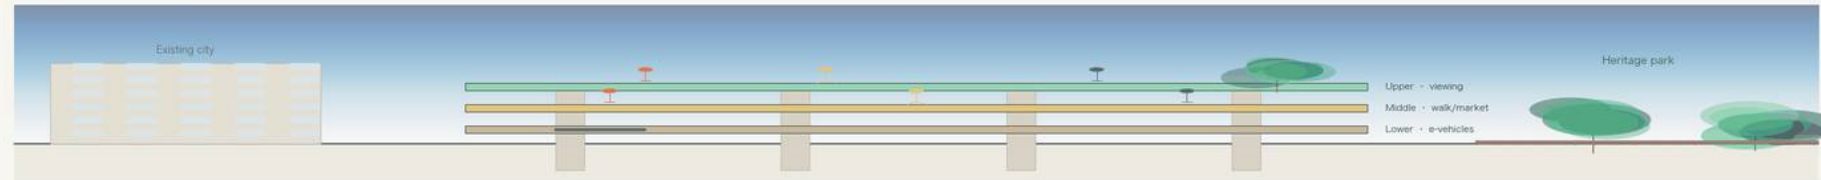

04 Dazhongsi Sta. • arrival only

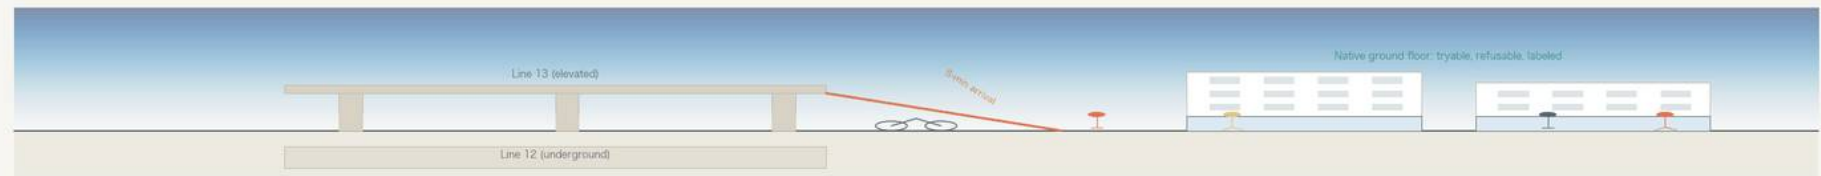

05 Qinghe • governance to river

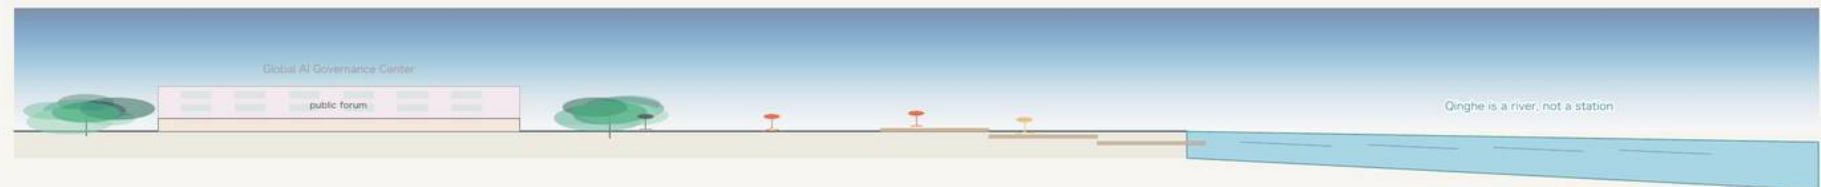

How to read

Each is a cut

through ground.

walls, rails,

water, people —

not a one-point

symbol street.

Depth = rules

hold in section:


join • verify

exit • inherit



## Wudaokou stitch deck: a reversible 3-level crossing

On existing pier logic · no unproven tunnels · pending red-line confirmation (concept, not construction)

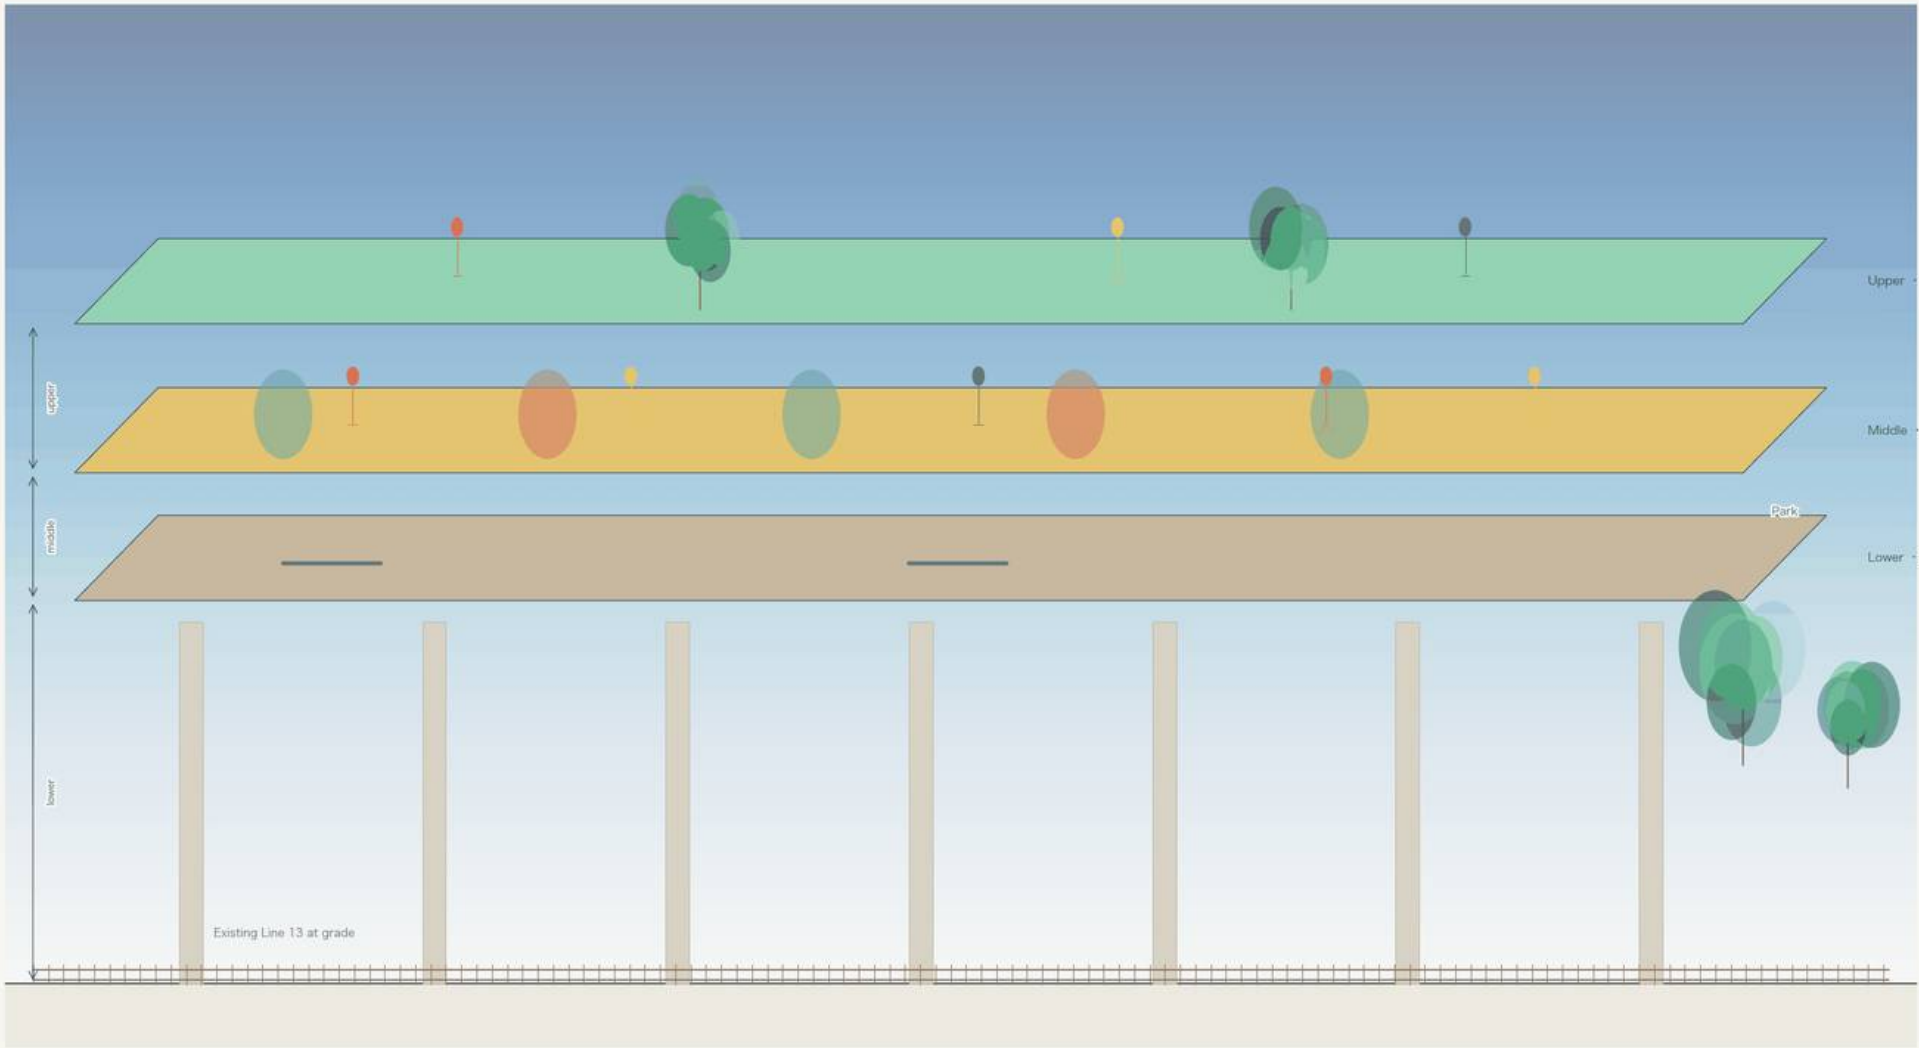


- Courage, bounded
- section logic &
- level relations
- concept tie-ins
- Upper · viewing deck
- Middle · walk & marl
- Lower · e-vehicles &
- × no spans/loads
- × no construction plan
- × not an approved alignment
- Plan B: no piers →
- independent columns →
- at-grade crossing +
- signal priority

OL-07 · pending red-line confirmation · concept, not for construction

## Wudaokou stitch deck: the boldest move drawn as credible everyday life

Section-perspective • material / level / real people • hand edges keep concept honest | OL-07

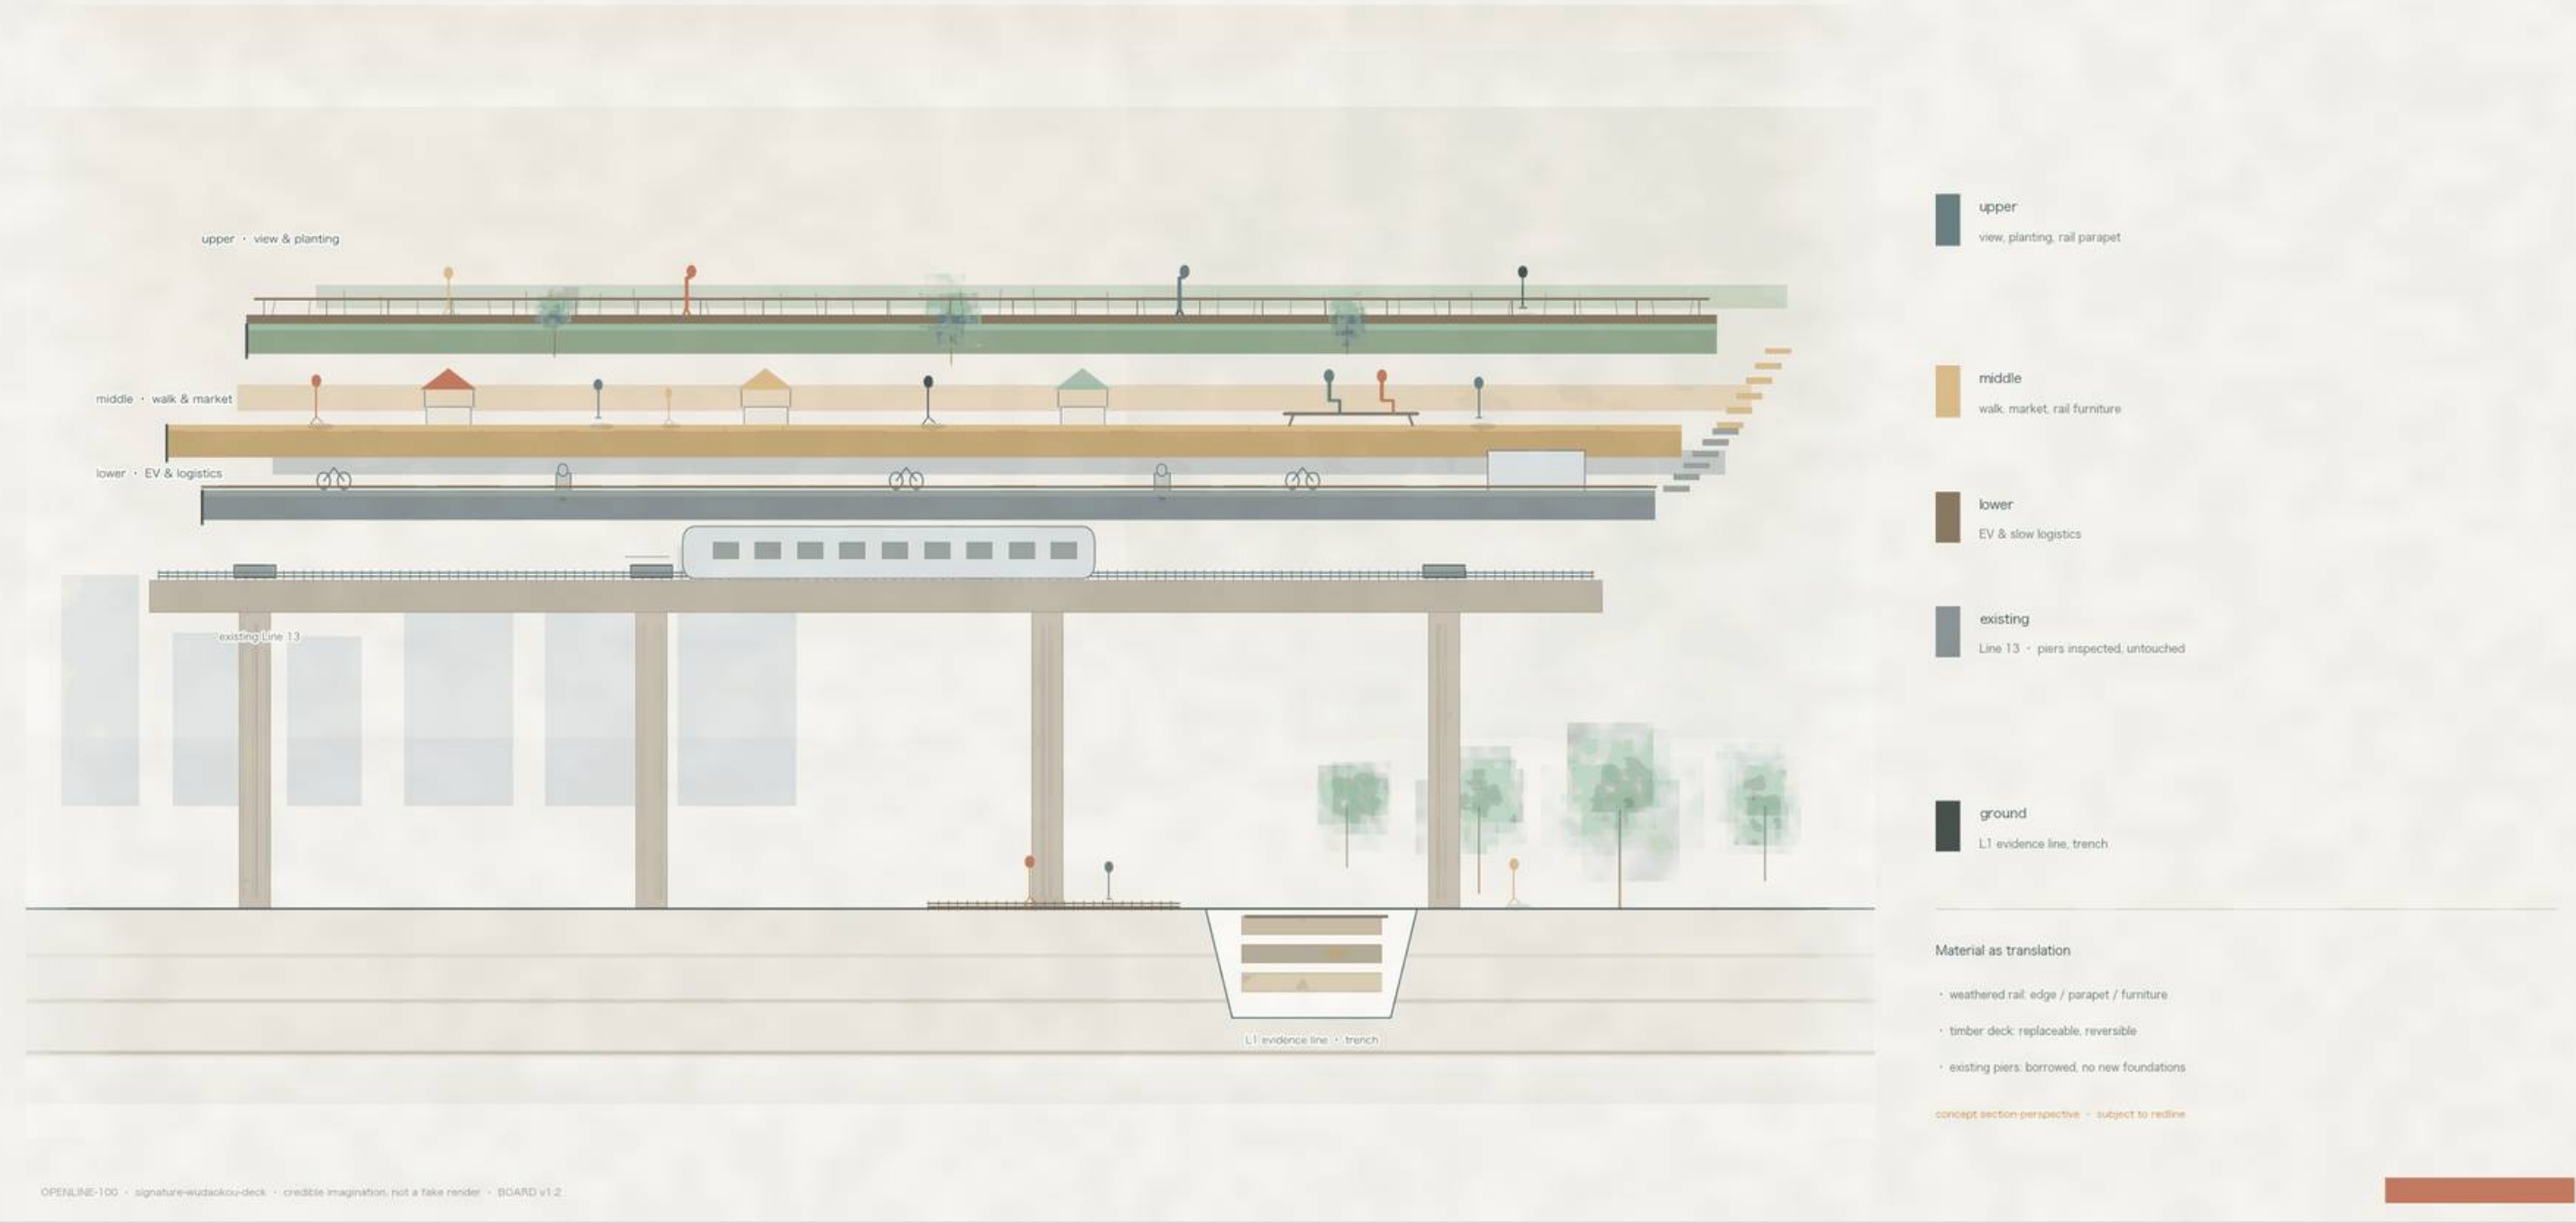

### 11 Signature: deck section-perspective • material, levels, real people





## Let the rails grow into the ground: five material translations


Components enter the public library, versioned via Inherit • sound & inscriptions pilot only after review

Ground • rail as paving



No unreachable exhibits

Section • archaeology trench

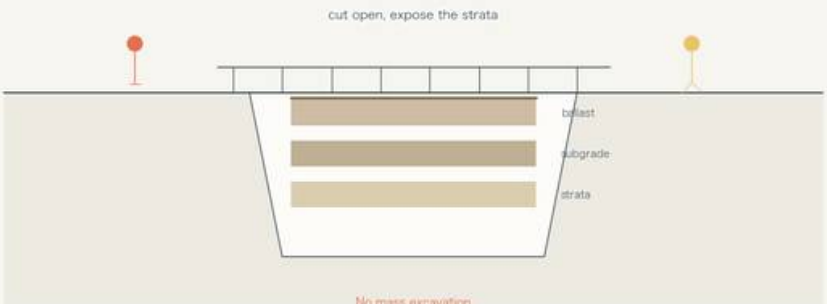


No mass excavation

Furniture • rails reused




No fake authenticity

Narrative • question stones

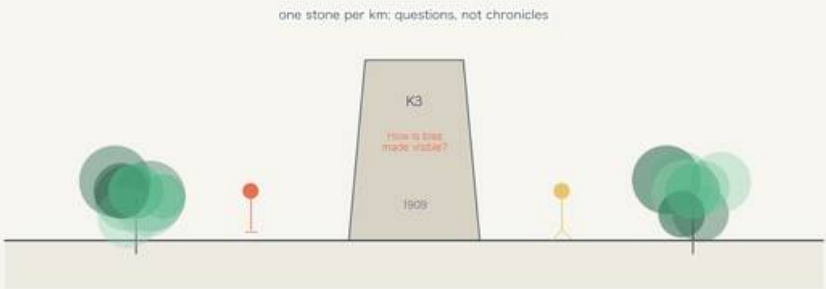

No trivializing history

Sound • steam × white-noise

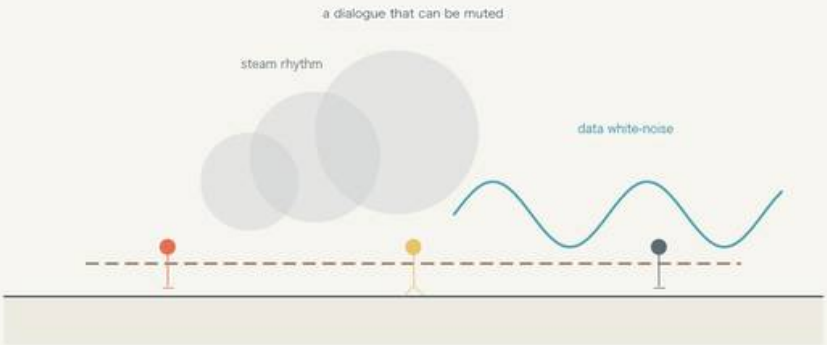

No noise nuisance

### Three rules before entering the library


- ① Reuse only after clearance & safety testing
- ② Versioned via Inherit: join / exit / inherit
- ③ Sound & inscriptions pilot after permit & review

All five share one ground: rails stay in the street.



## Heritage made soulful: grading • voices • rails of humanity

From preserving heritage to continuing Jing-Zhang | 3 grades × 3 voices × 3 turns | A-HERITAGE-001 framework

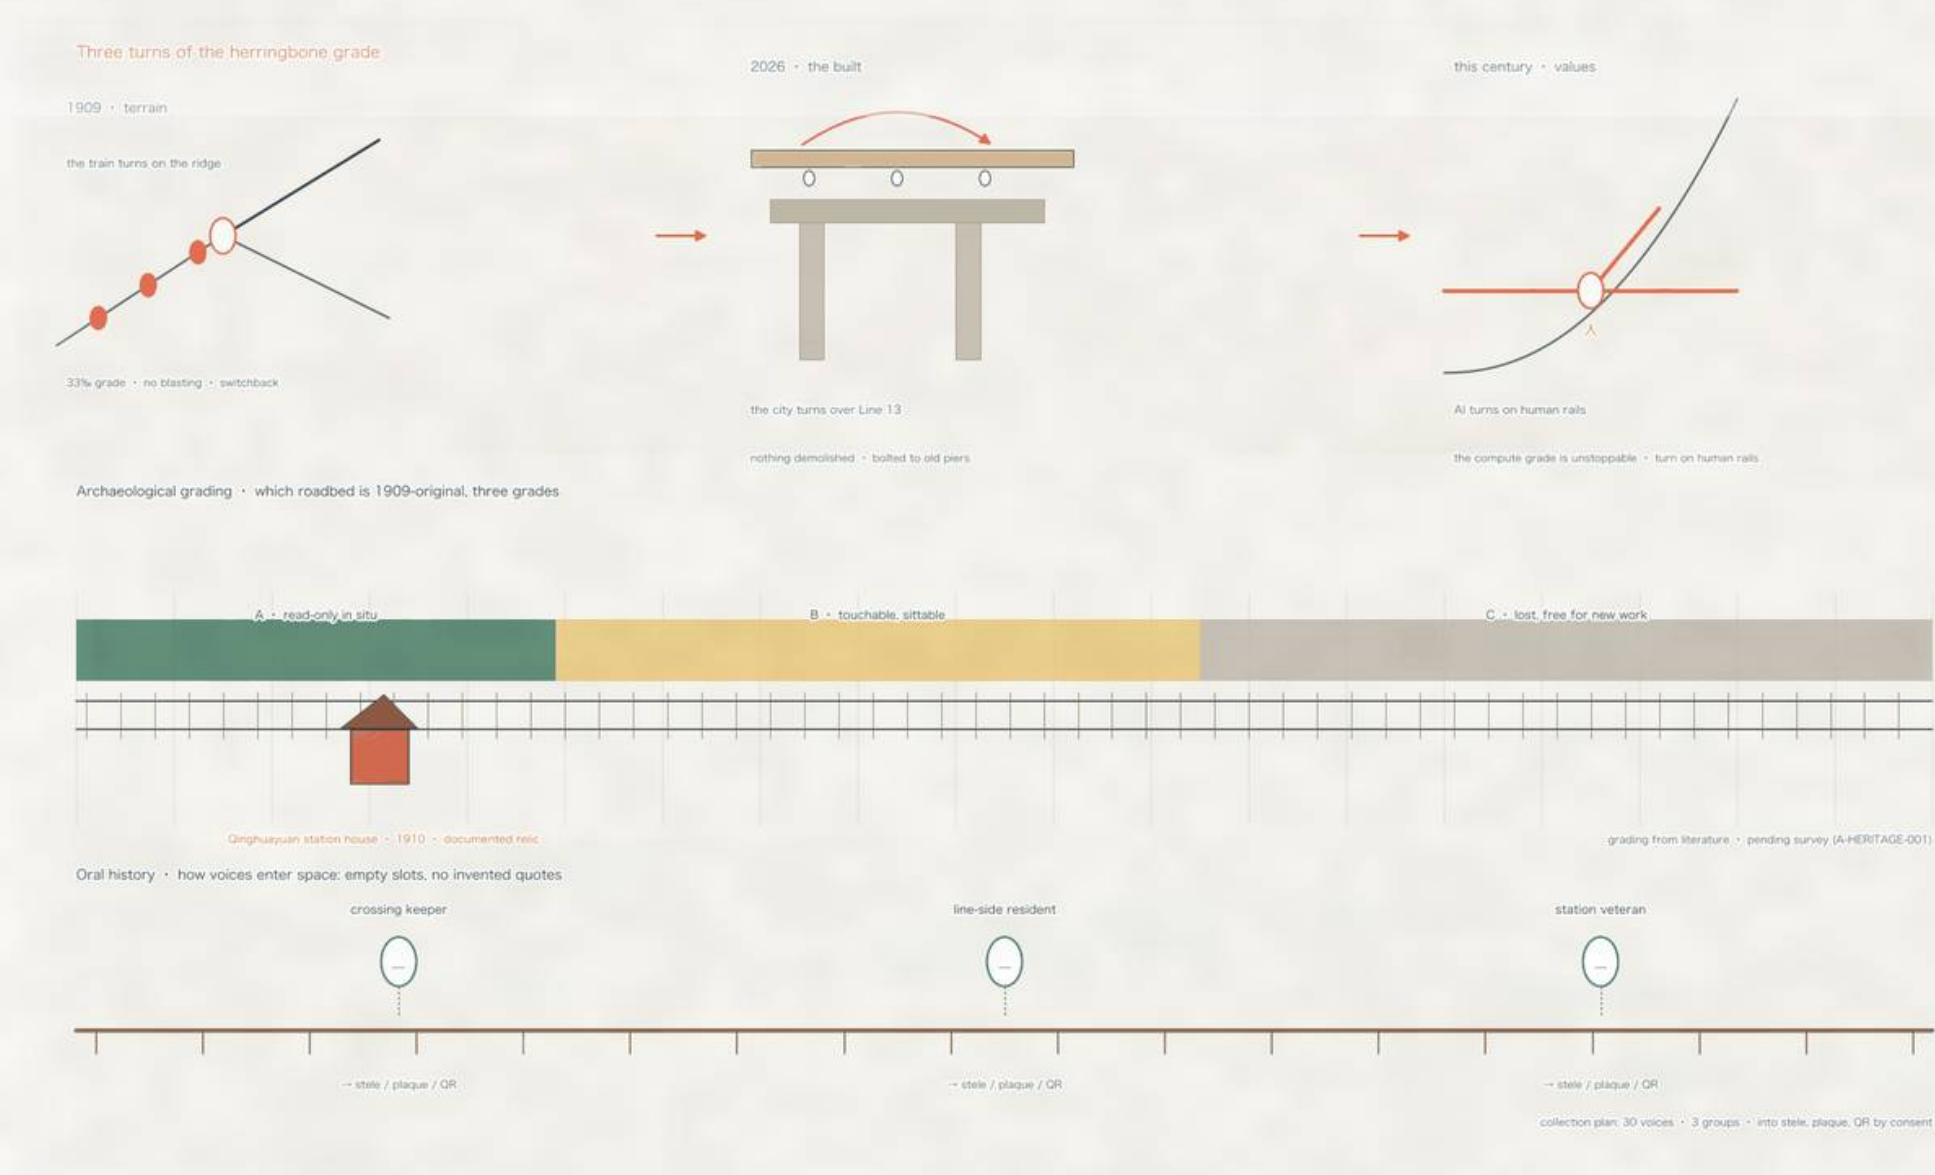

### 以人为轨

#### Rails of humanity

In 1909, the 「人」

drew the line's shape.

In this century, it names

whom the line belongs to.

Railway anatomy → today

switchback = Verify / Exit gates

safety siding = Failure Case Library

test track = governance sandbox

rail = human values, not compute

#### Each in its place


grading • for the fabric

voices • for the people

the turn • for the century

grading is a literature framework, pending survey

voice slots are empty, awaiting real collection

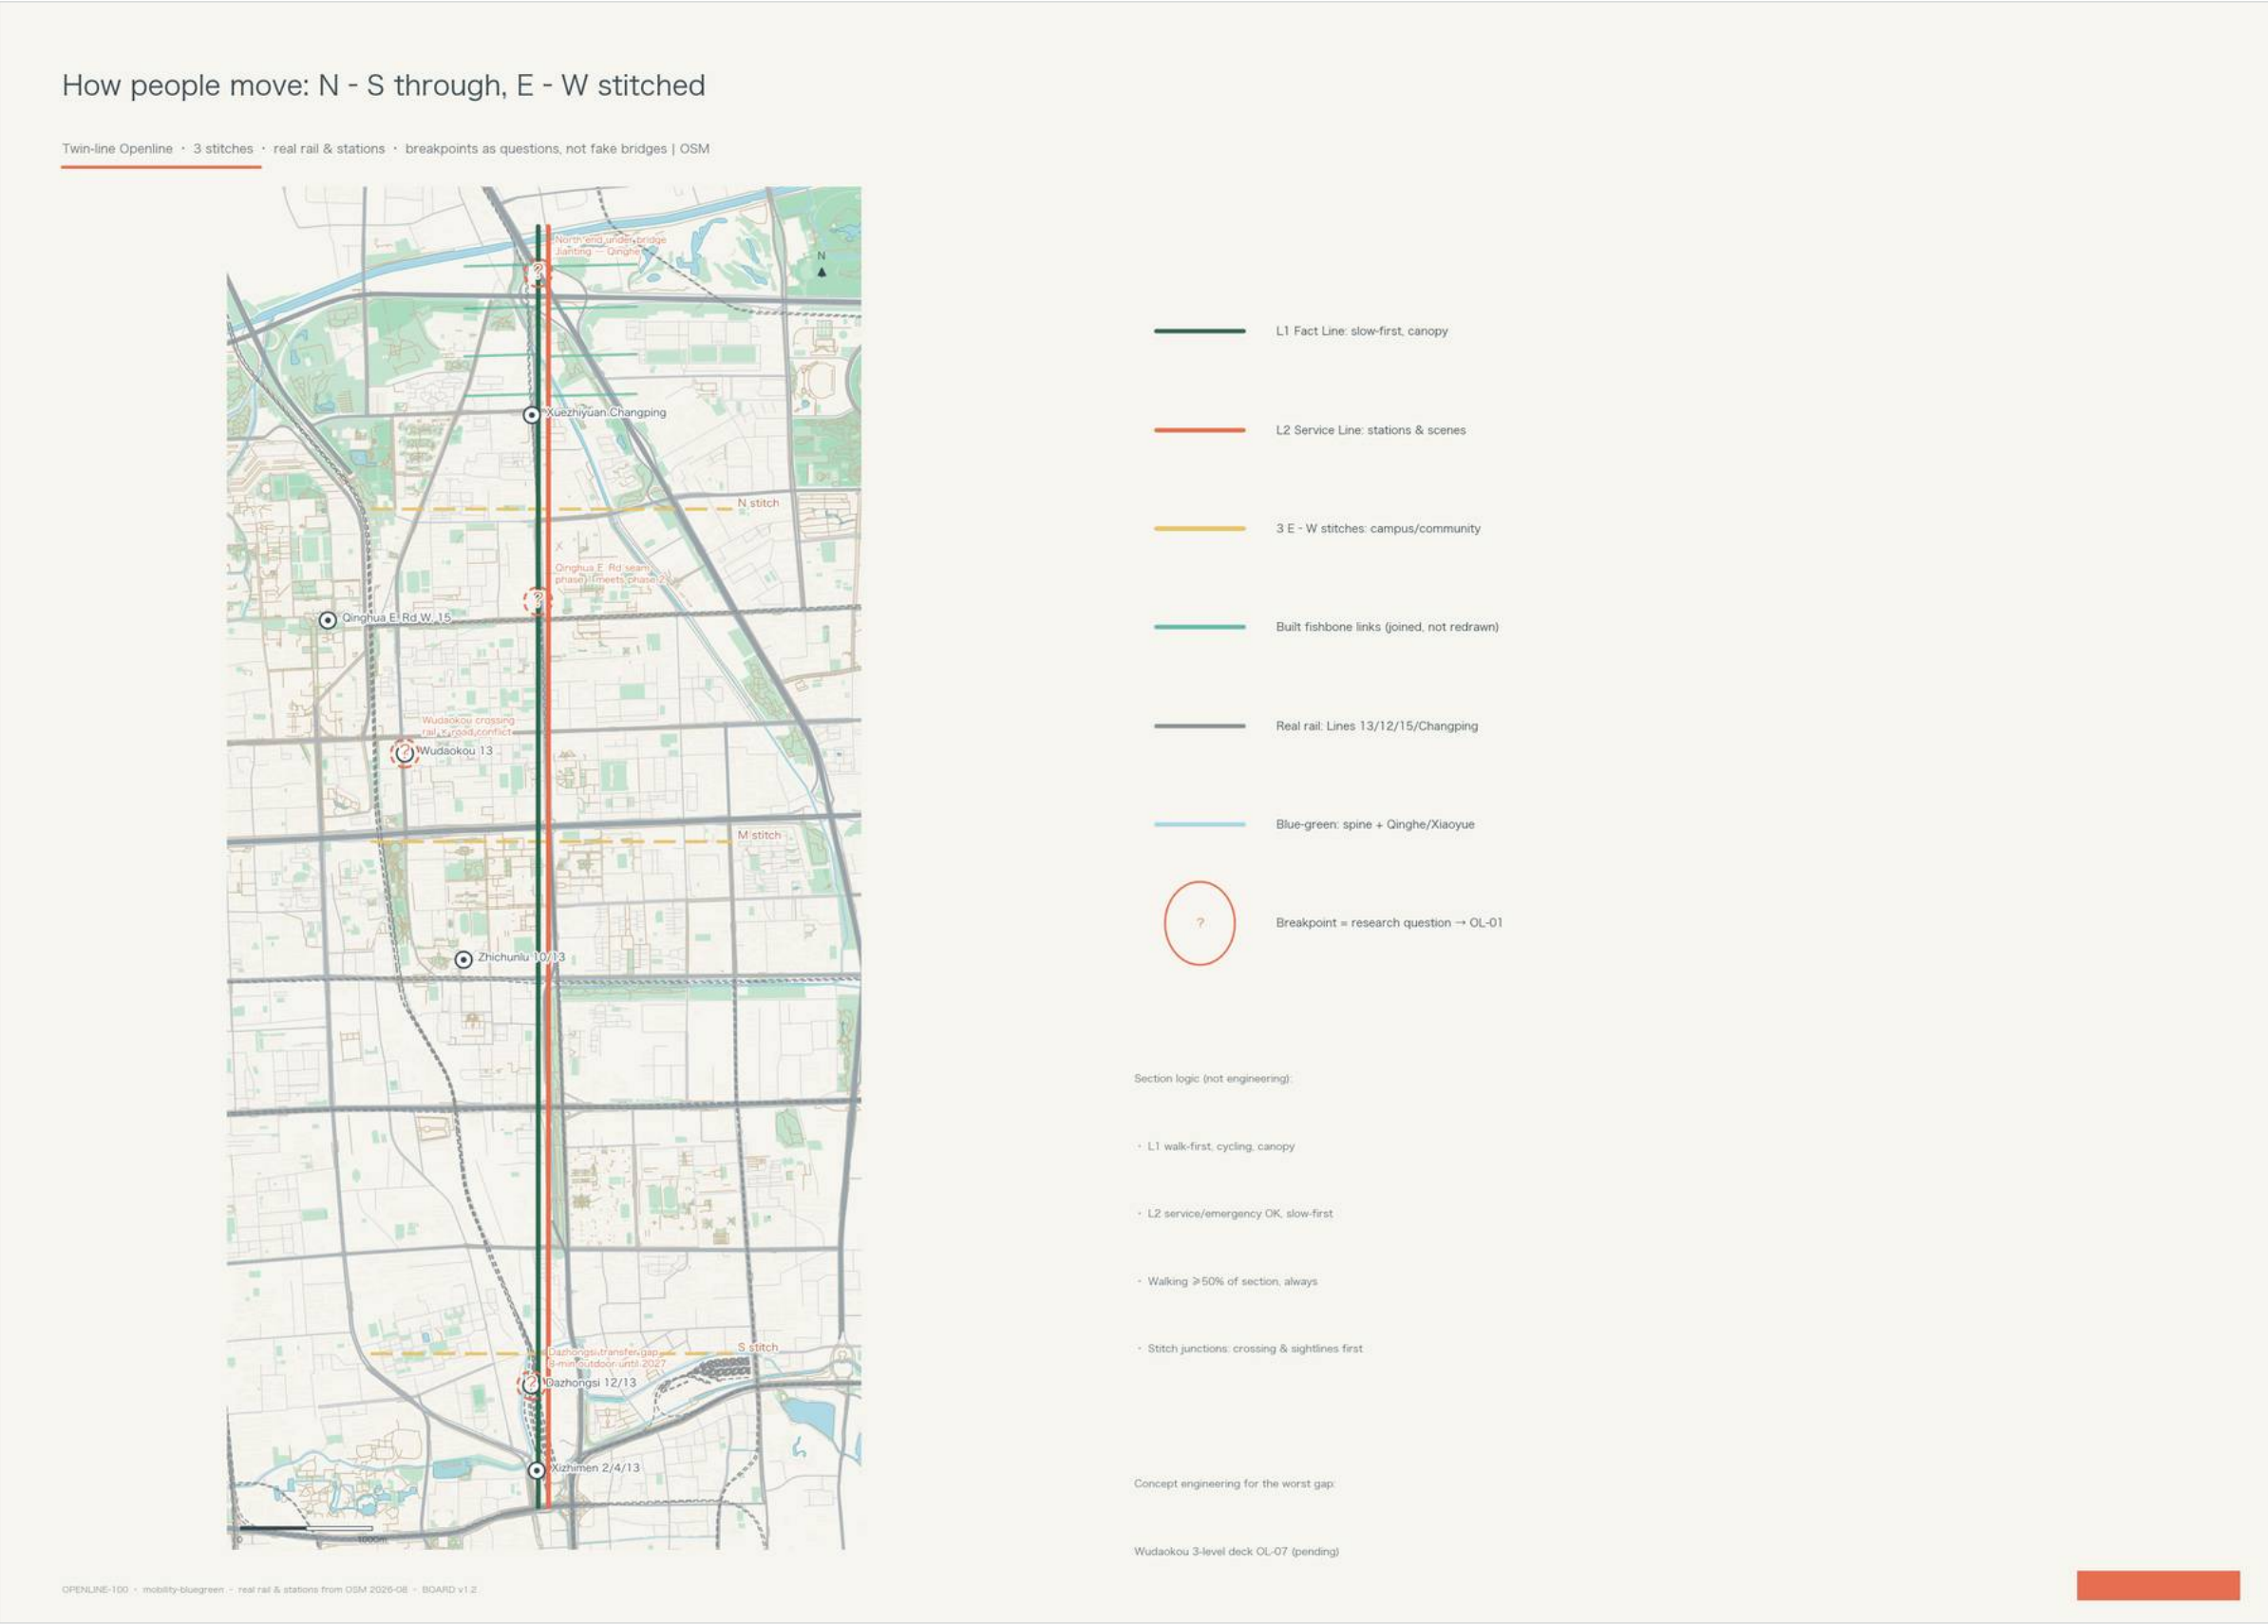


## 15 Slow mobility and blue-green network




Ecological commitments in numbers: verifiable targets each phase

Carbon budget • runoff capture • heat island • biodiversity net gain • canopy | sensors to trust, Verify gate publishes | targets per A-ECO-001

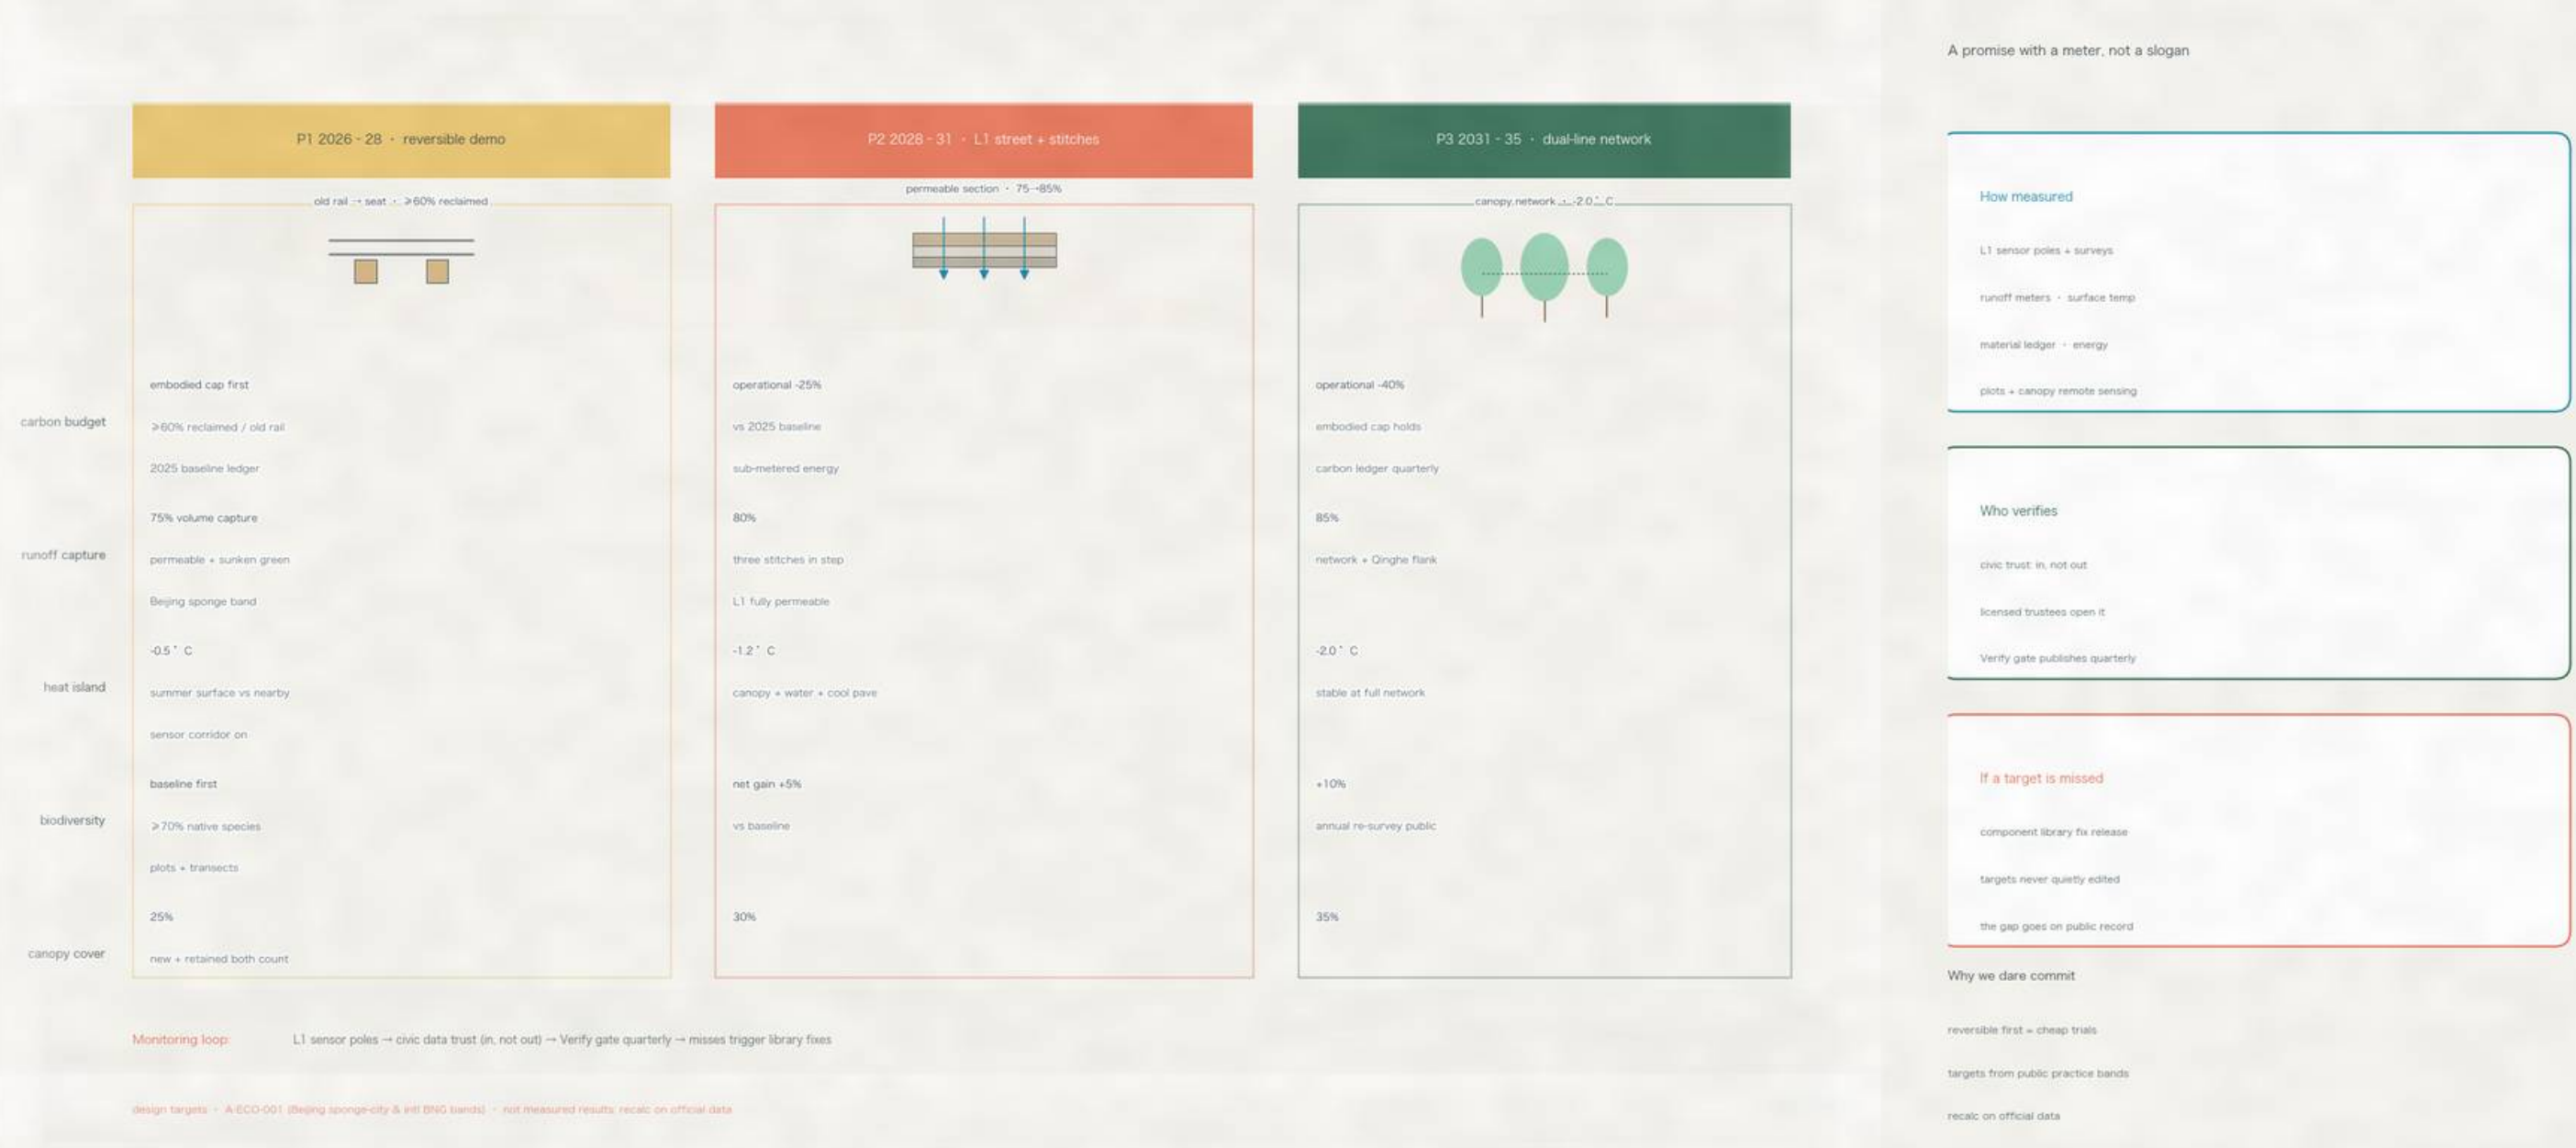


16 Ecological commitments in numbers: verifiable targets each phase

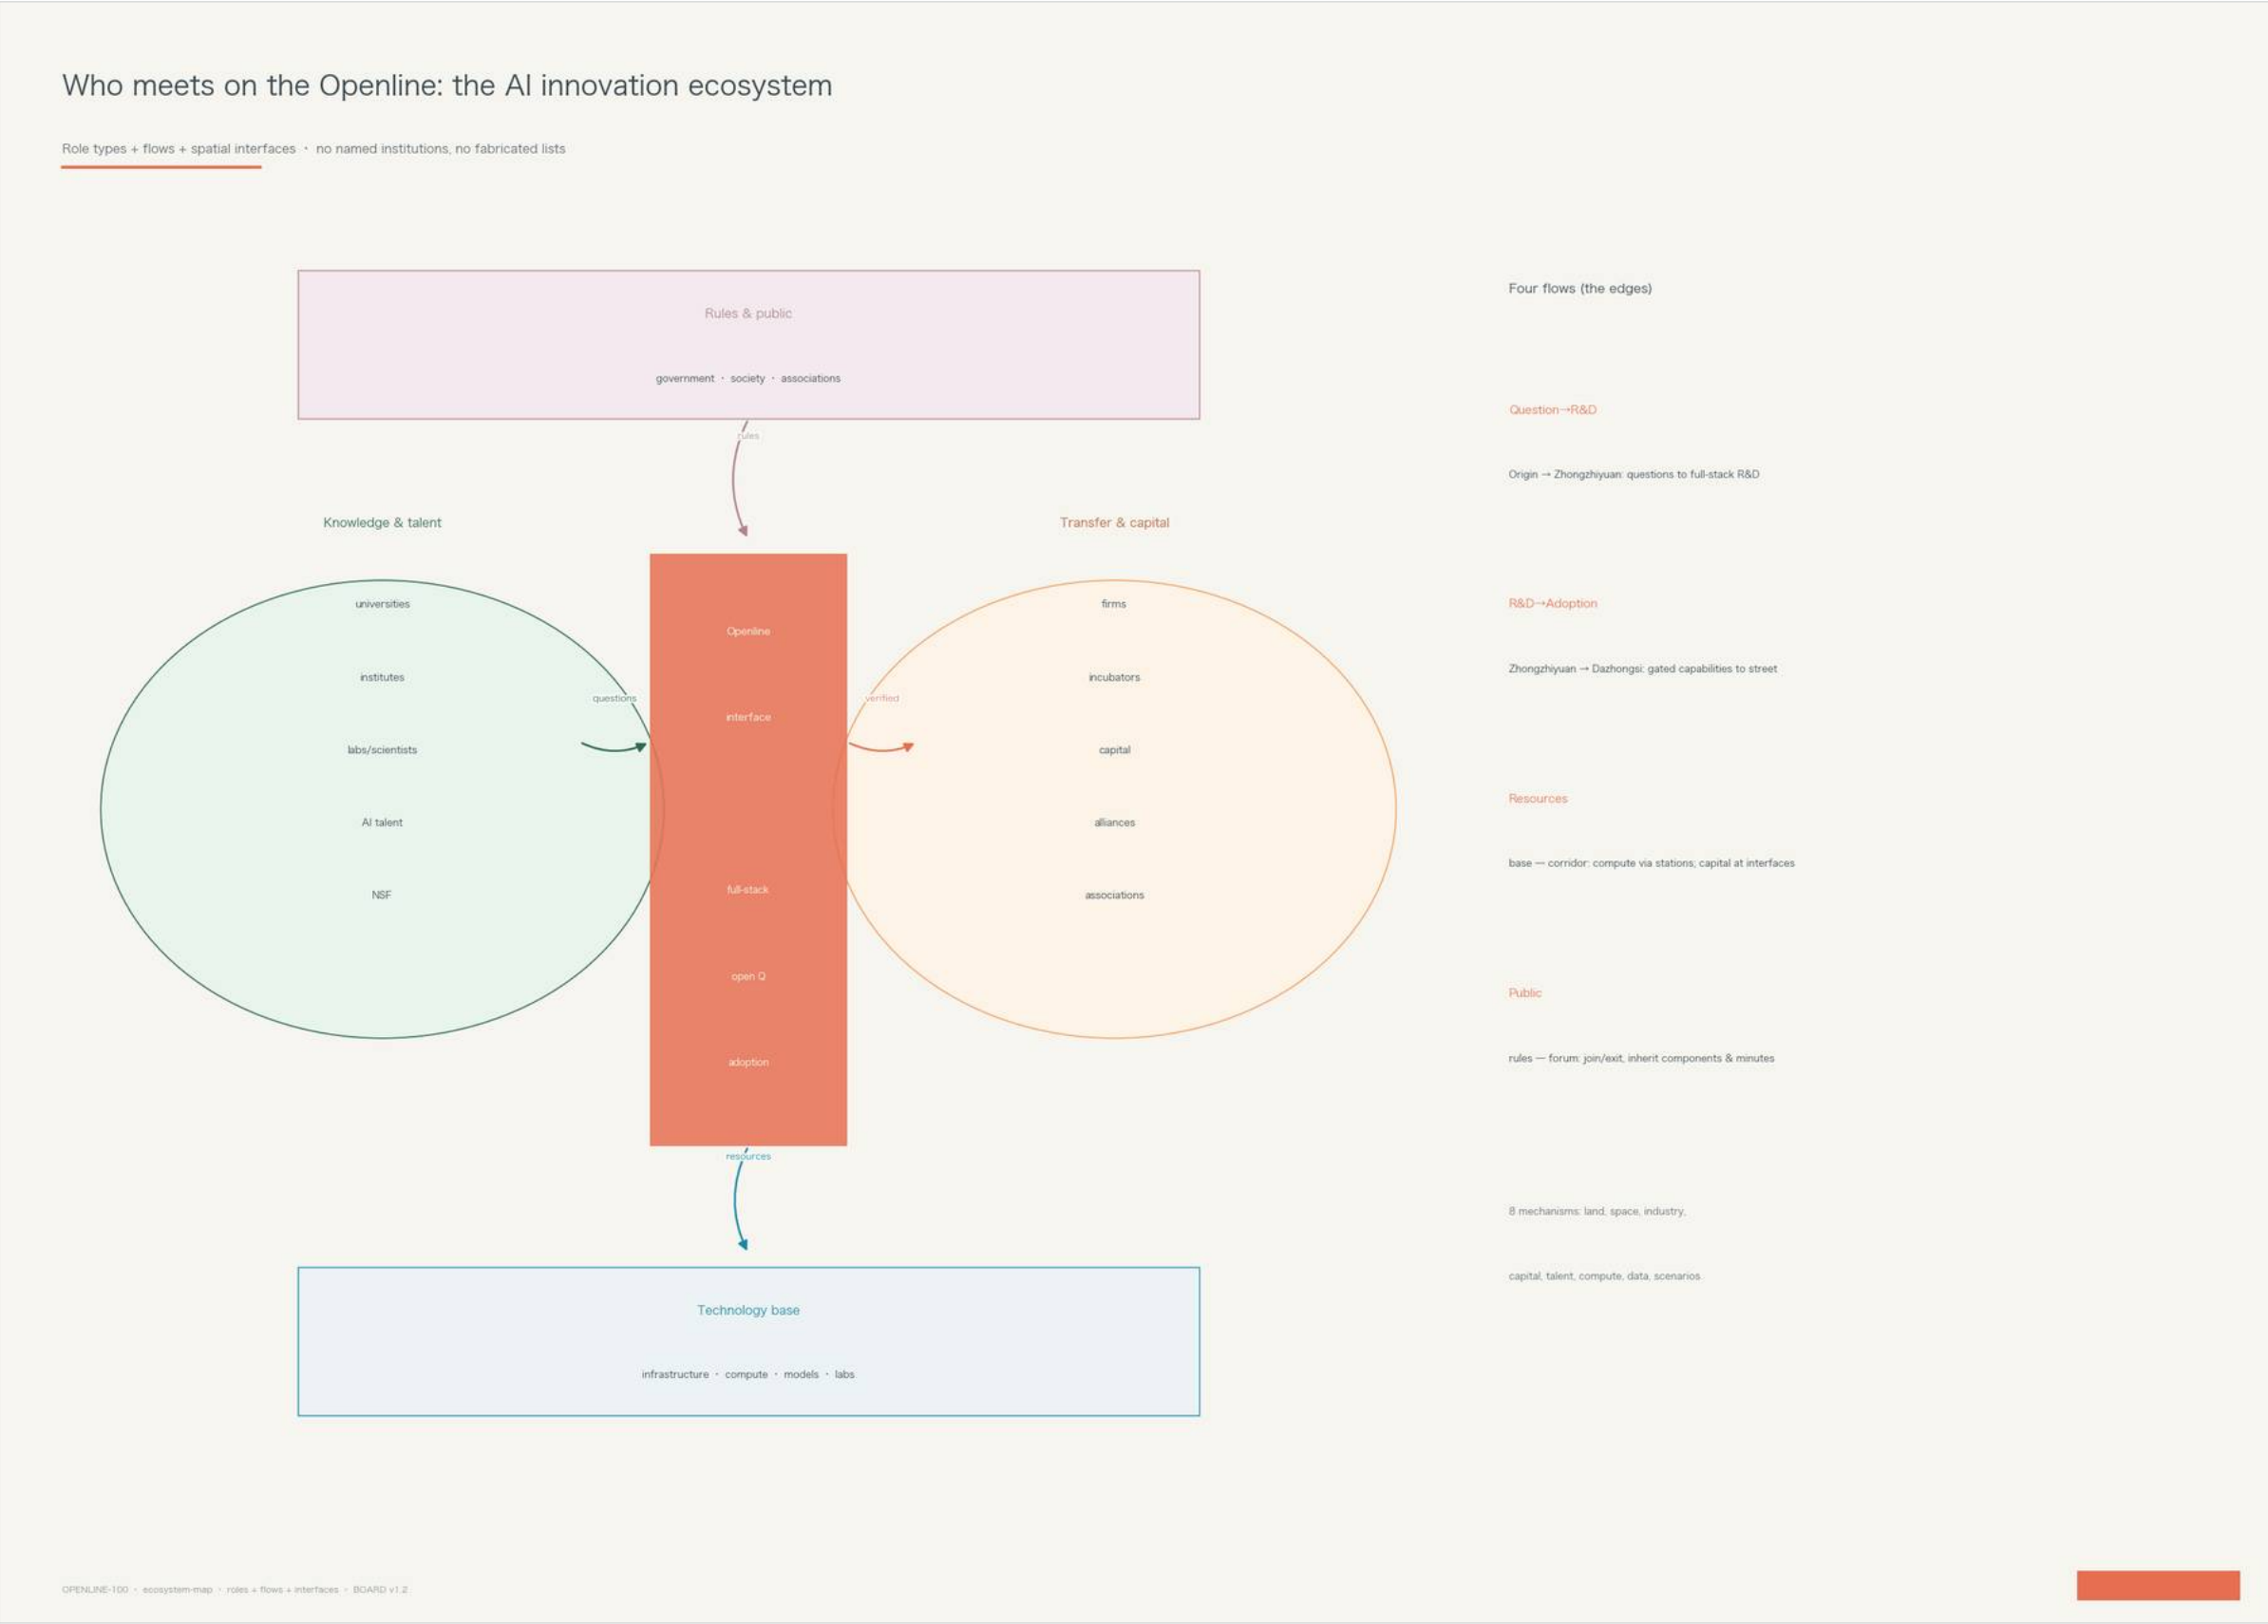

17 Ecosystem map: five habitat rings

## Open Ticket institutional section: the fare system of the Openline

The right-of-way rewritten for the digital century | Join • Verify • Exit • Inherit × govern / space / data / time | governance concept

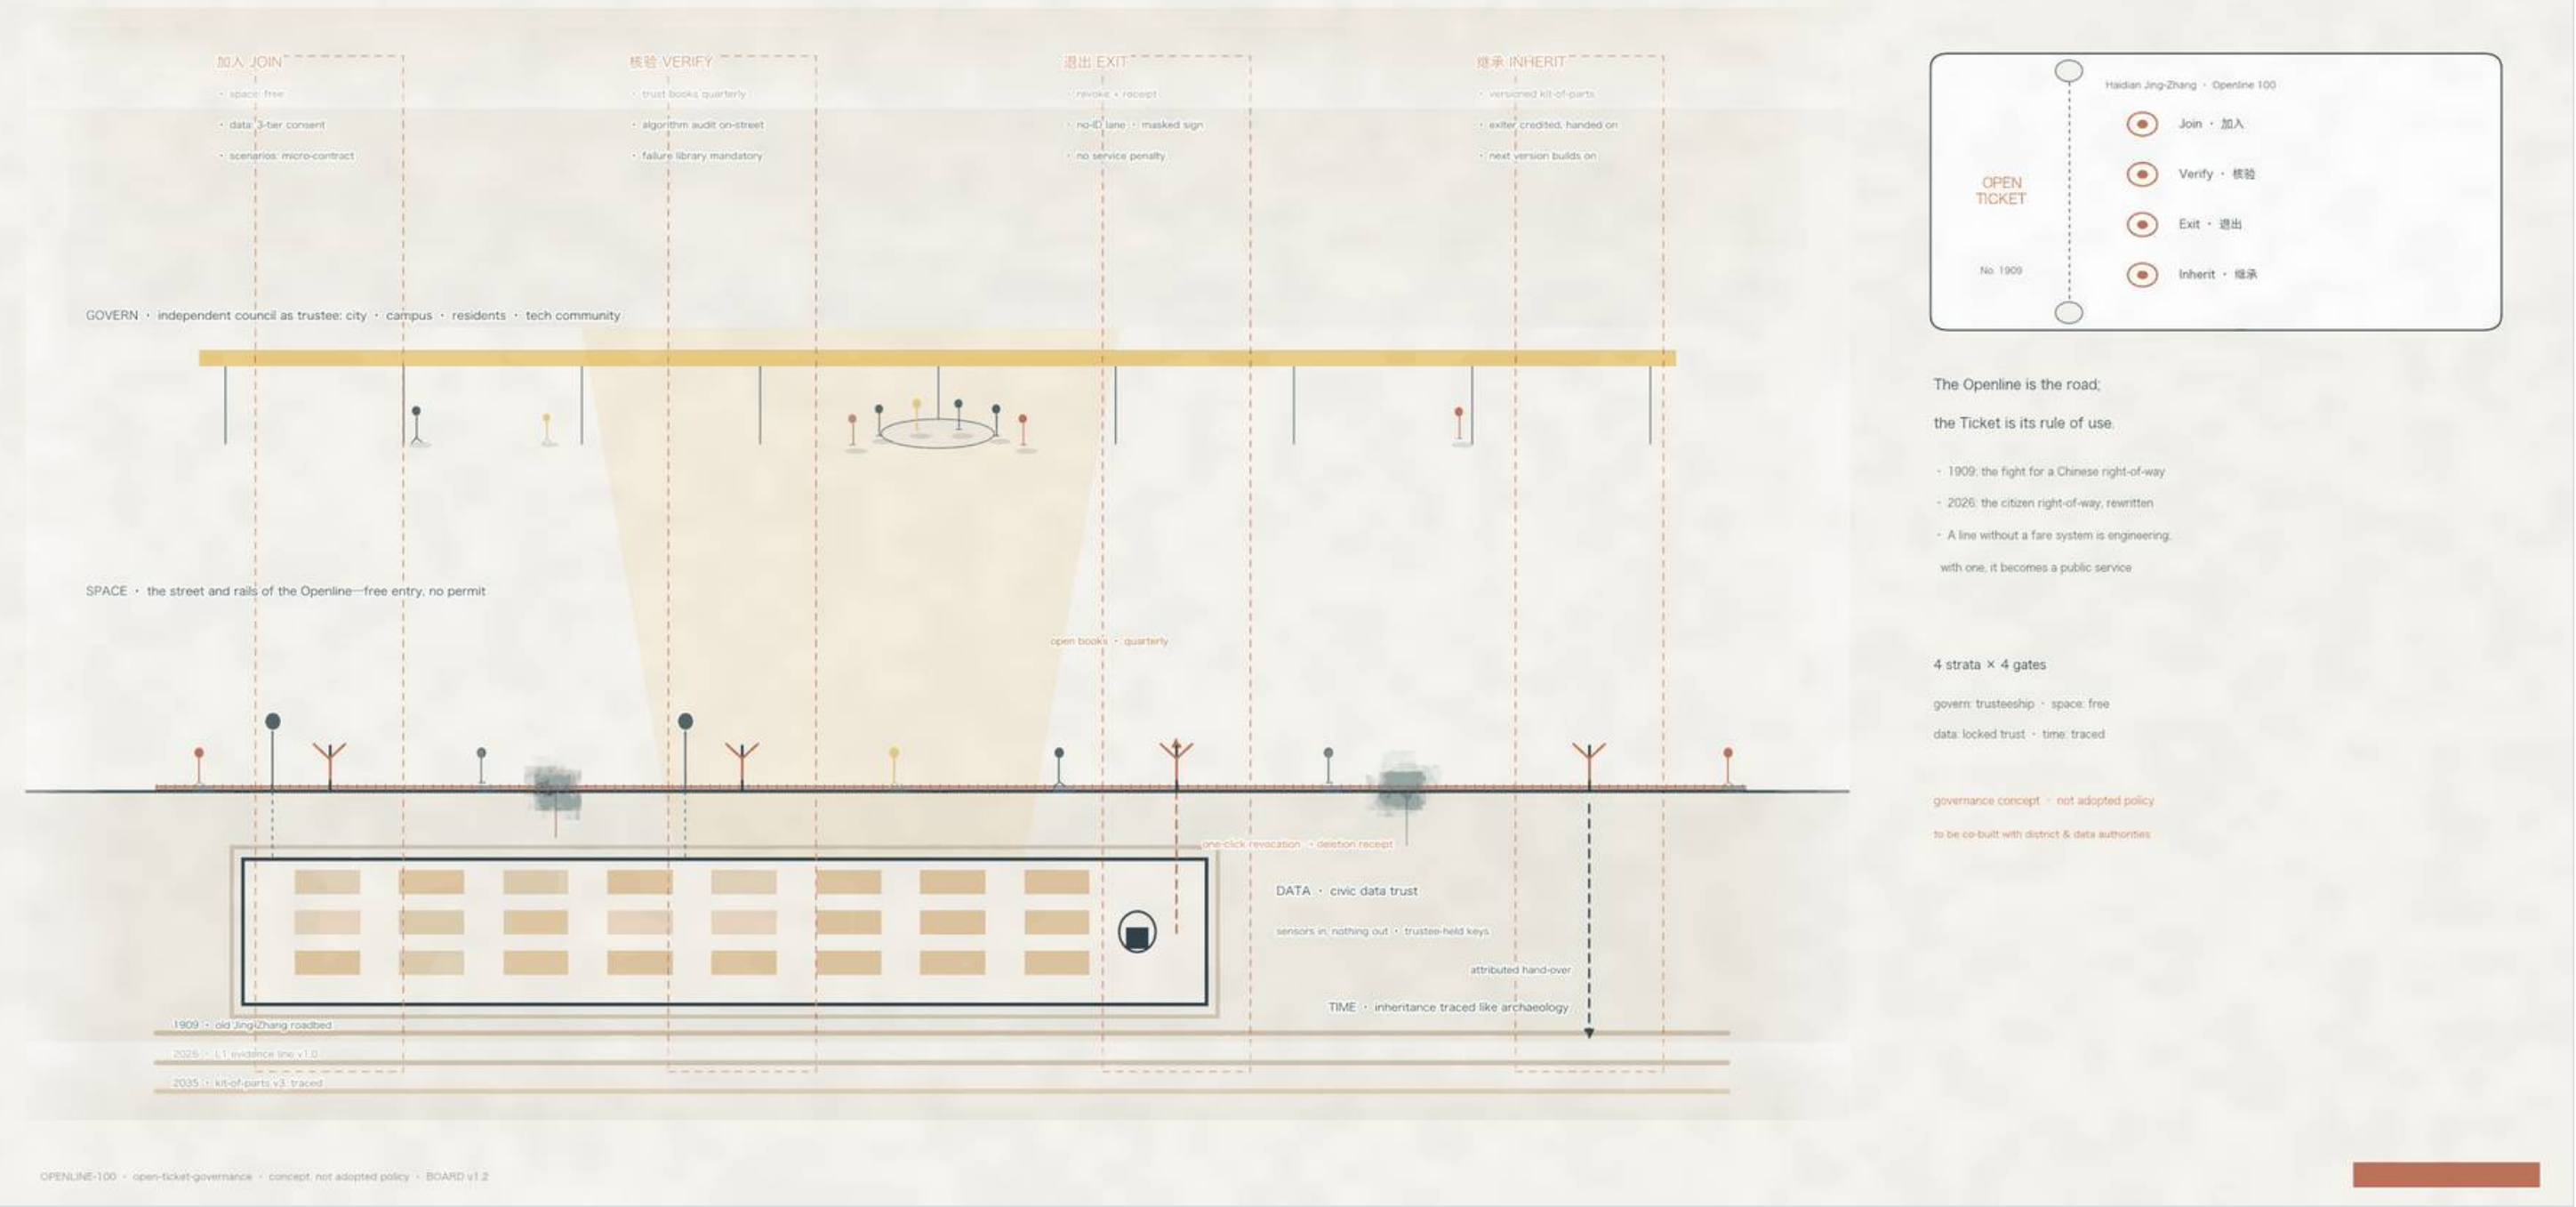


### 18 Open Ticket institutional section: Join • Verify • Exit • Inherit



## What is recalculated, what still awaits official data

Type 1 recalculated (provisional) • Type 2 structure known / intensity unknown • Type 3 performance in assumptions

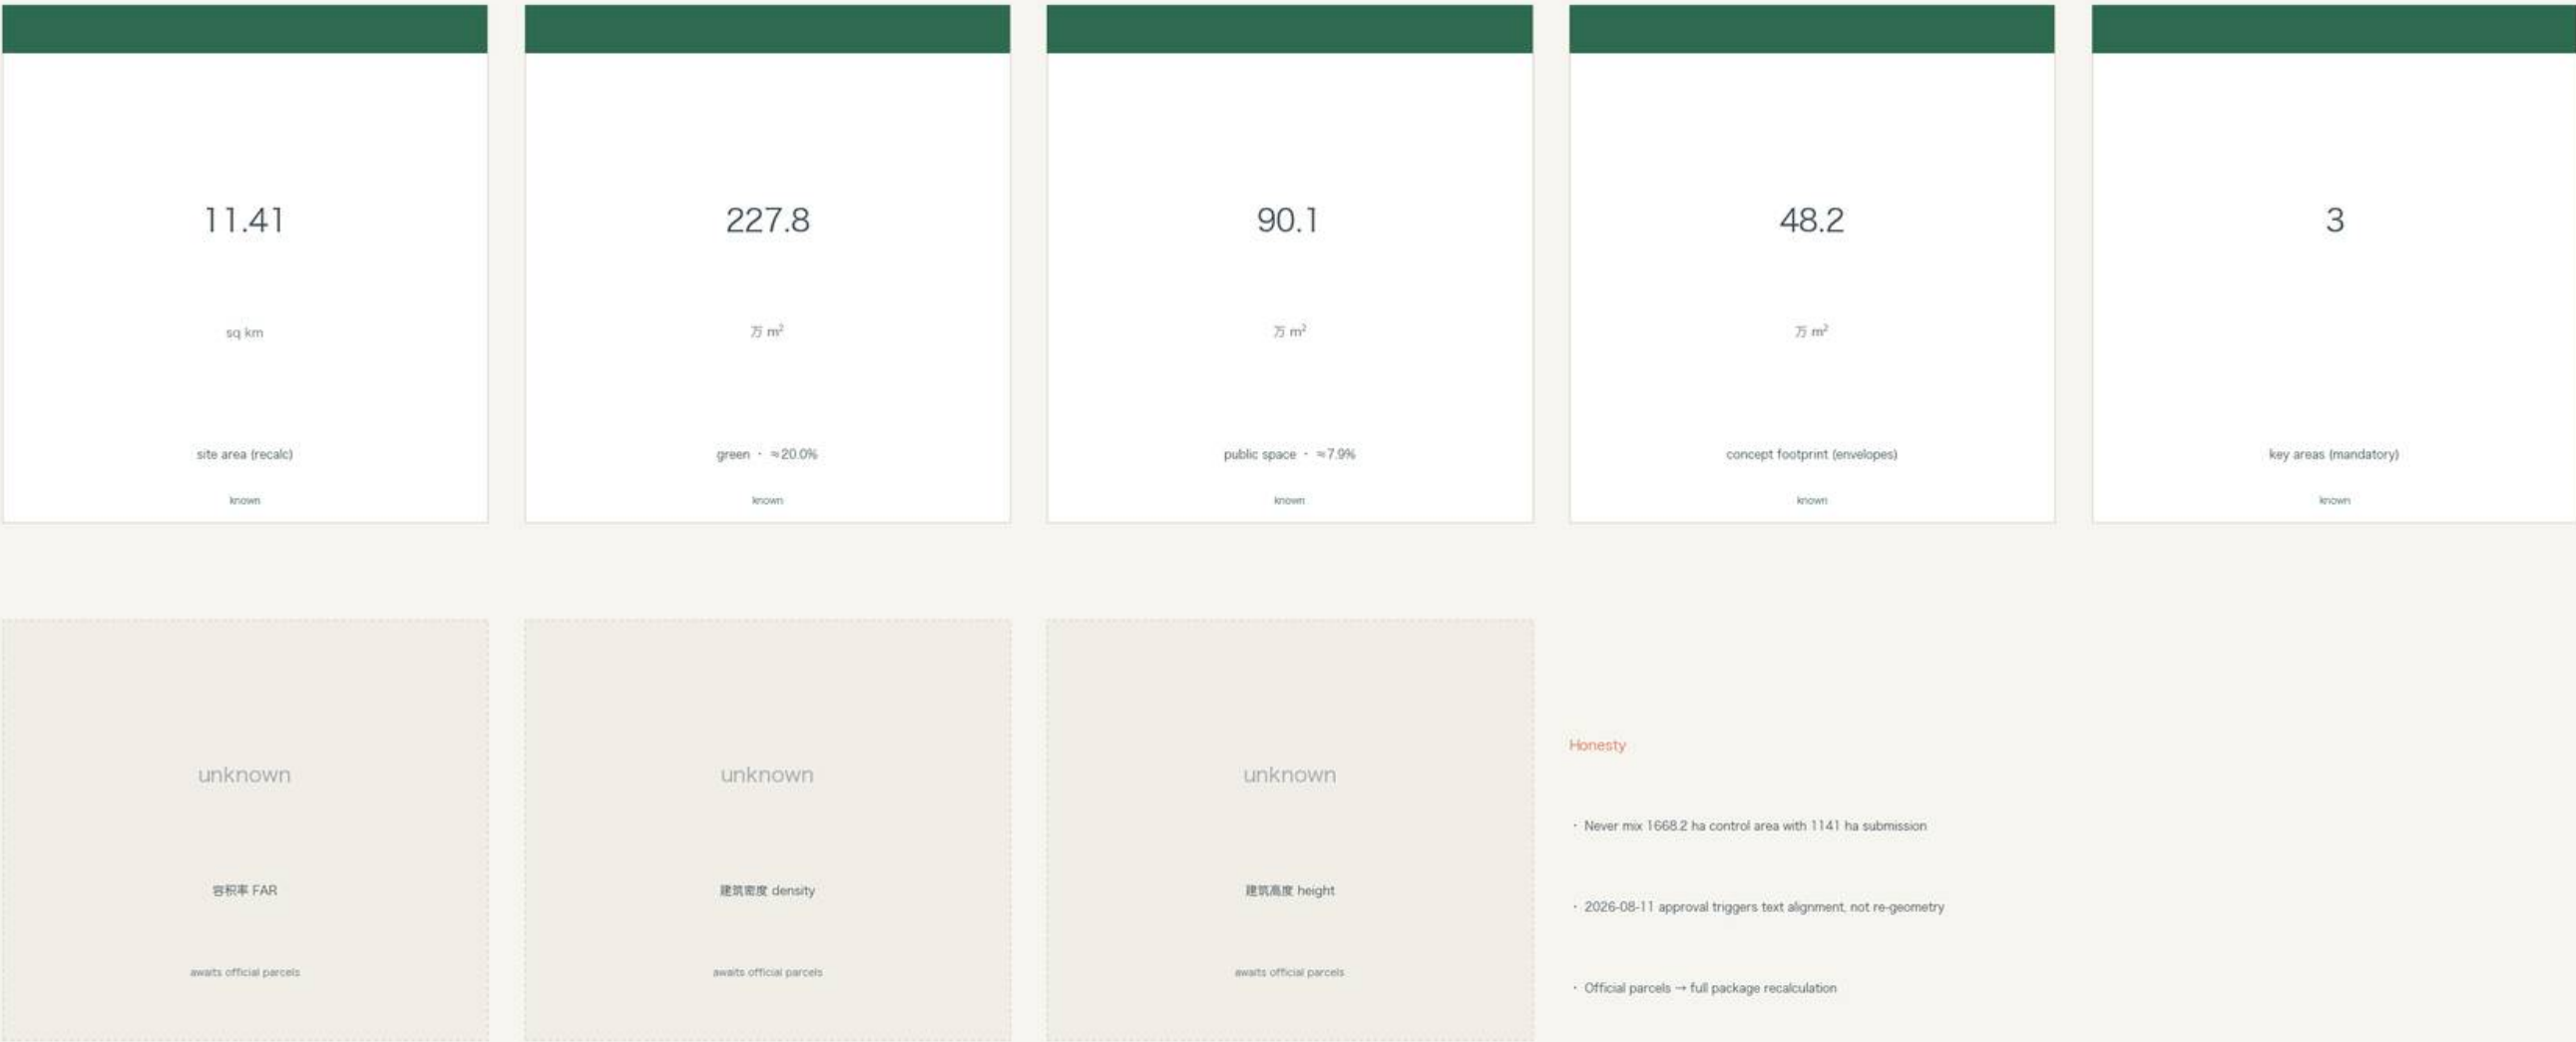

- Honesty
- Never mix 1668.2 ha control area with 1141 ha submission
  - 2026-08-11 approval triggers text alignment, not re-geometry
  - Official parcels → full package recalculation

Public space first, intensity follows: 0 - 1 • 1 - 3 • 3 - 10 yrs

Same actions as OL-01 - 10 • phasing is not a funding plan | real OSM fabric | dashed = not yet built

0 - 1 yr • prototype



0 - 1 yr • prototype

- Arrival first
- KMO + M-stitch sample
- Single station prototype

1 - 3 yr • streets



1 - 3 yr • streets

- One unit cluster opens
- Native street pilot
- License window & hall

3 - 10 yr • network




3 - 10 yr • network

- Three-area network
- OL-07 deck mid-term
- Governance center

OPENLINE-100 • key-phasing • 0 - 1 / 1 - 3 / 3 - 10 on real fabric • BOARD v1.2

Capital logic of phasing: reversibility is low risk

Each phase answers build / pay / operate / return | bond → pooling → adoption relay | magnitude only, A-CAPITAL-001

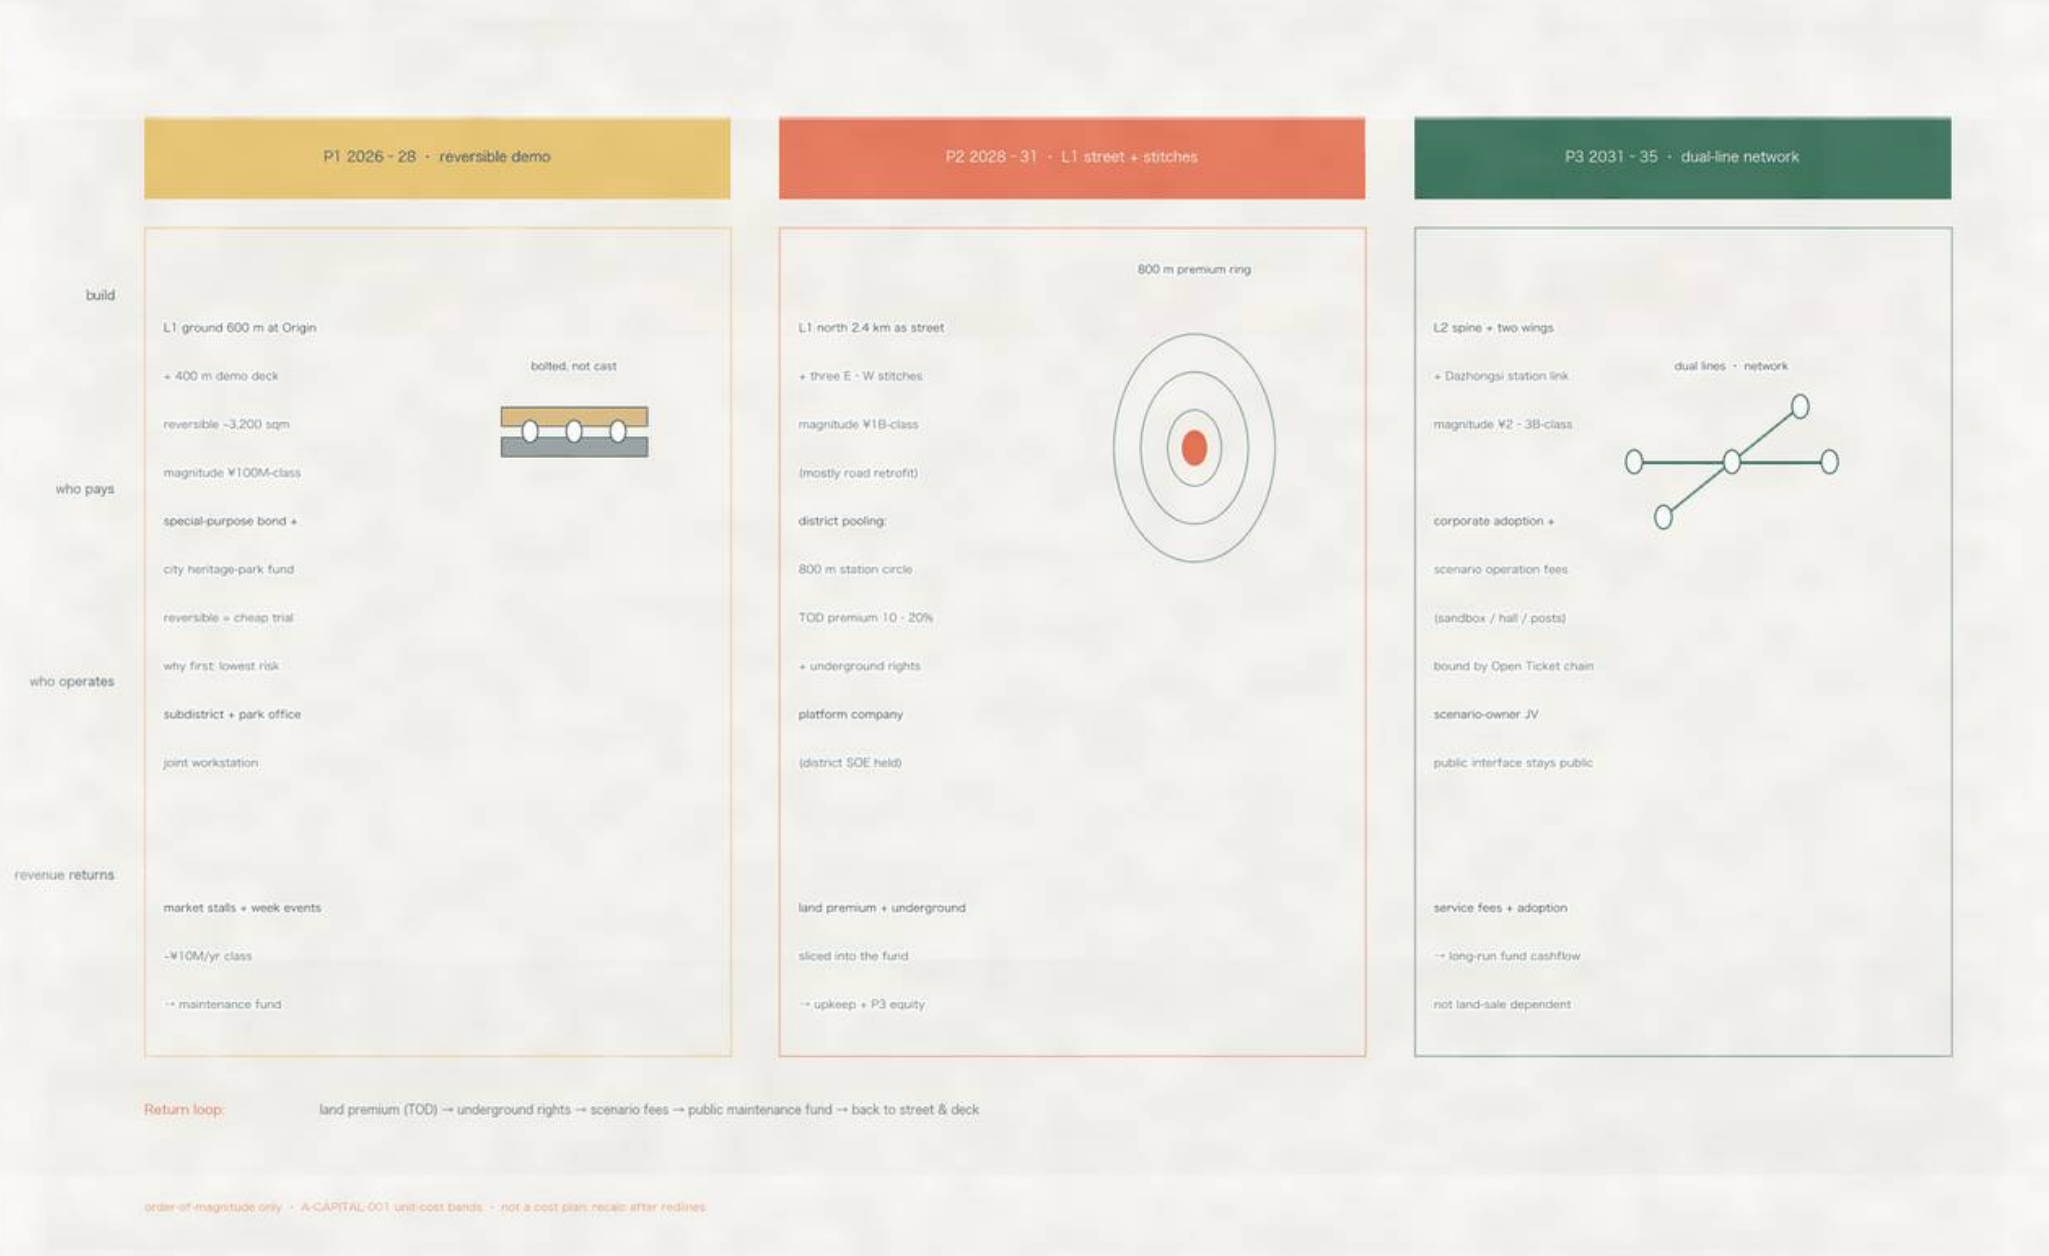

Three financing scenarios • relay, not either-or

A • special bond

fits P1 demo

fast, low cost

risk: no O&M source

B • district pooling

fits P2 street

TOD premium + underground

risk: land-market cycle

C • corporate adoption

fits P3 & long-run O&M

scenario fees • naming

risk: publicness ceded →

backstopped by Open Ticket


What reversibility buys

- deck unbolts → asset relocates
- a wrong demo is not sunk cost
- the real reason to go first





22 Immersive ①: morning on the L1 ground walk

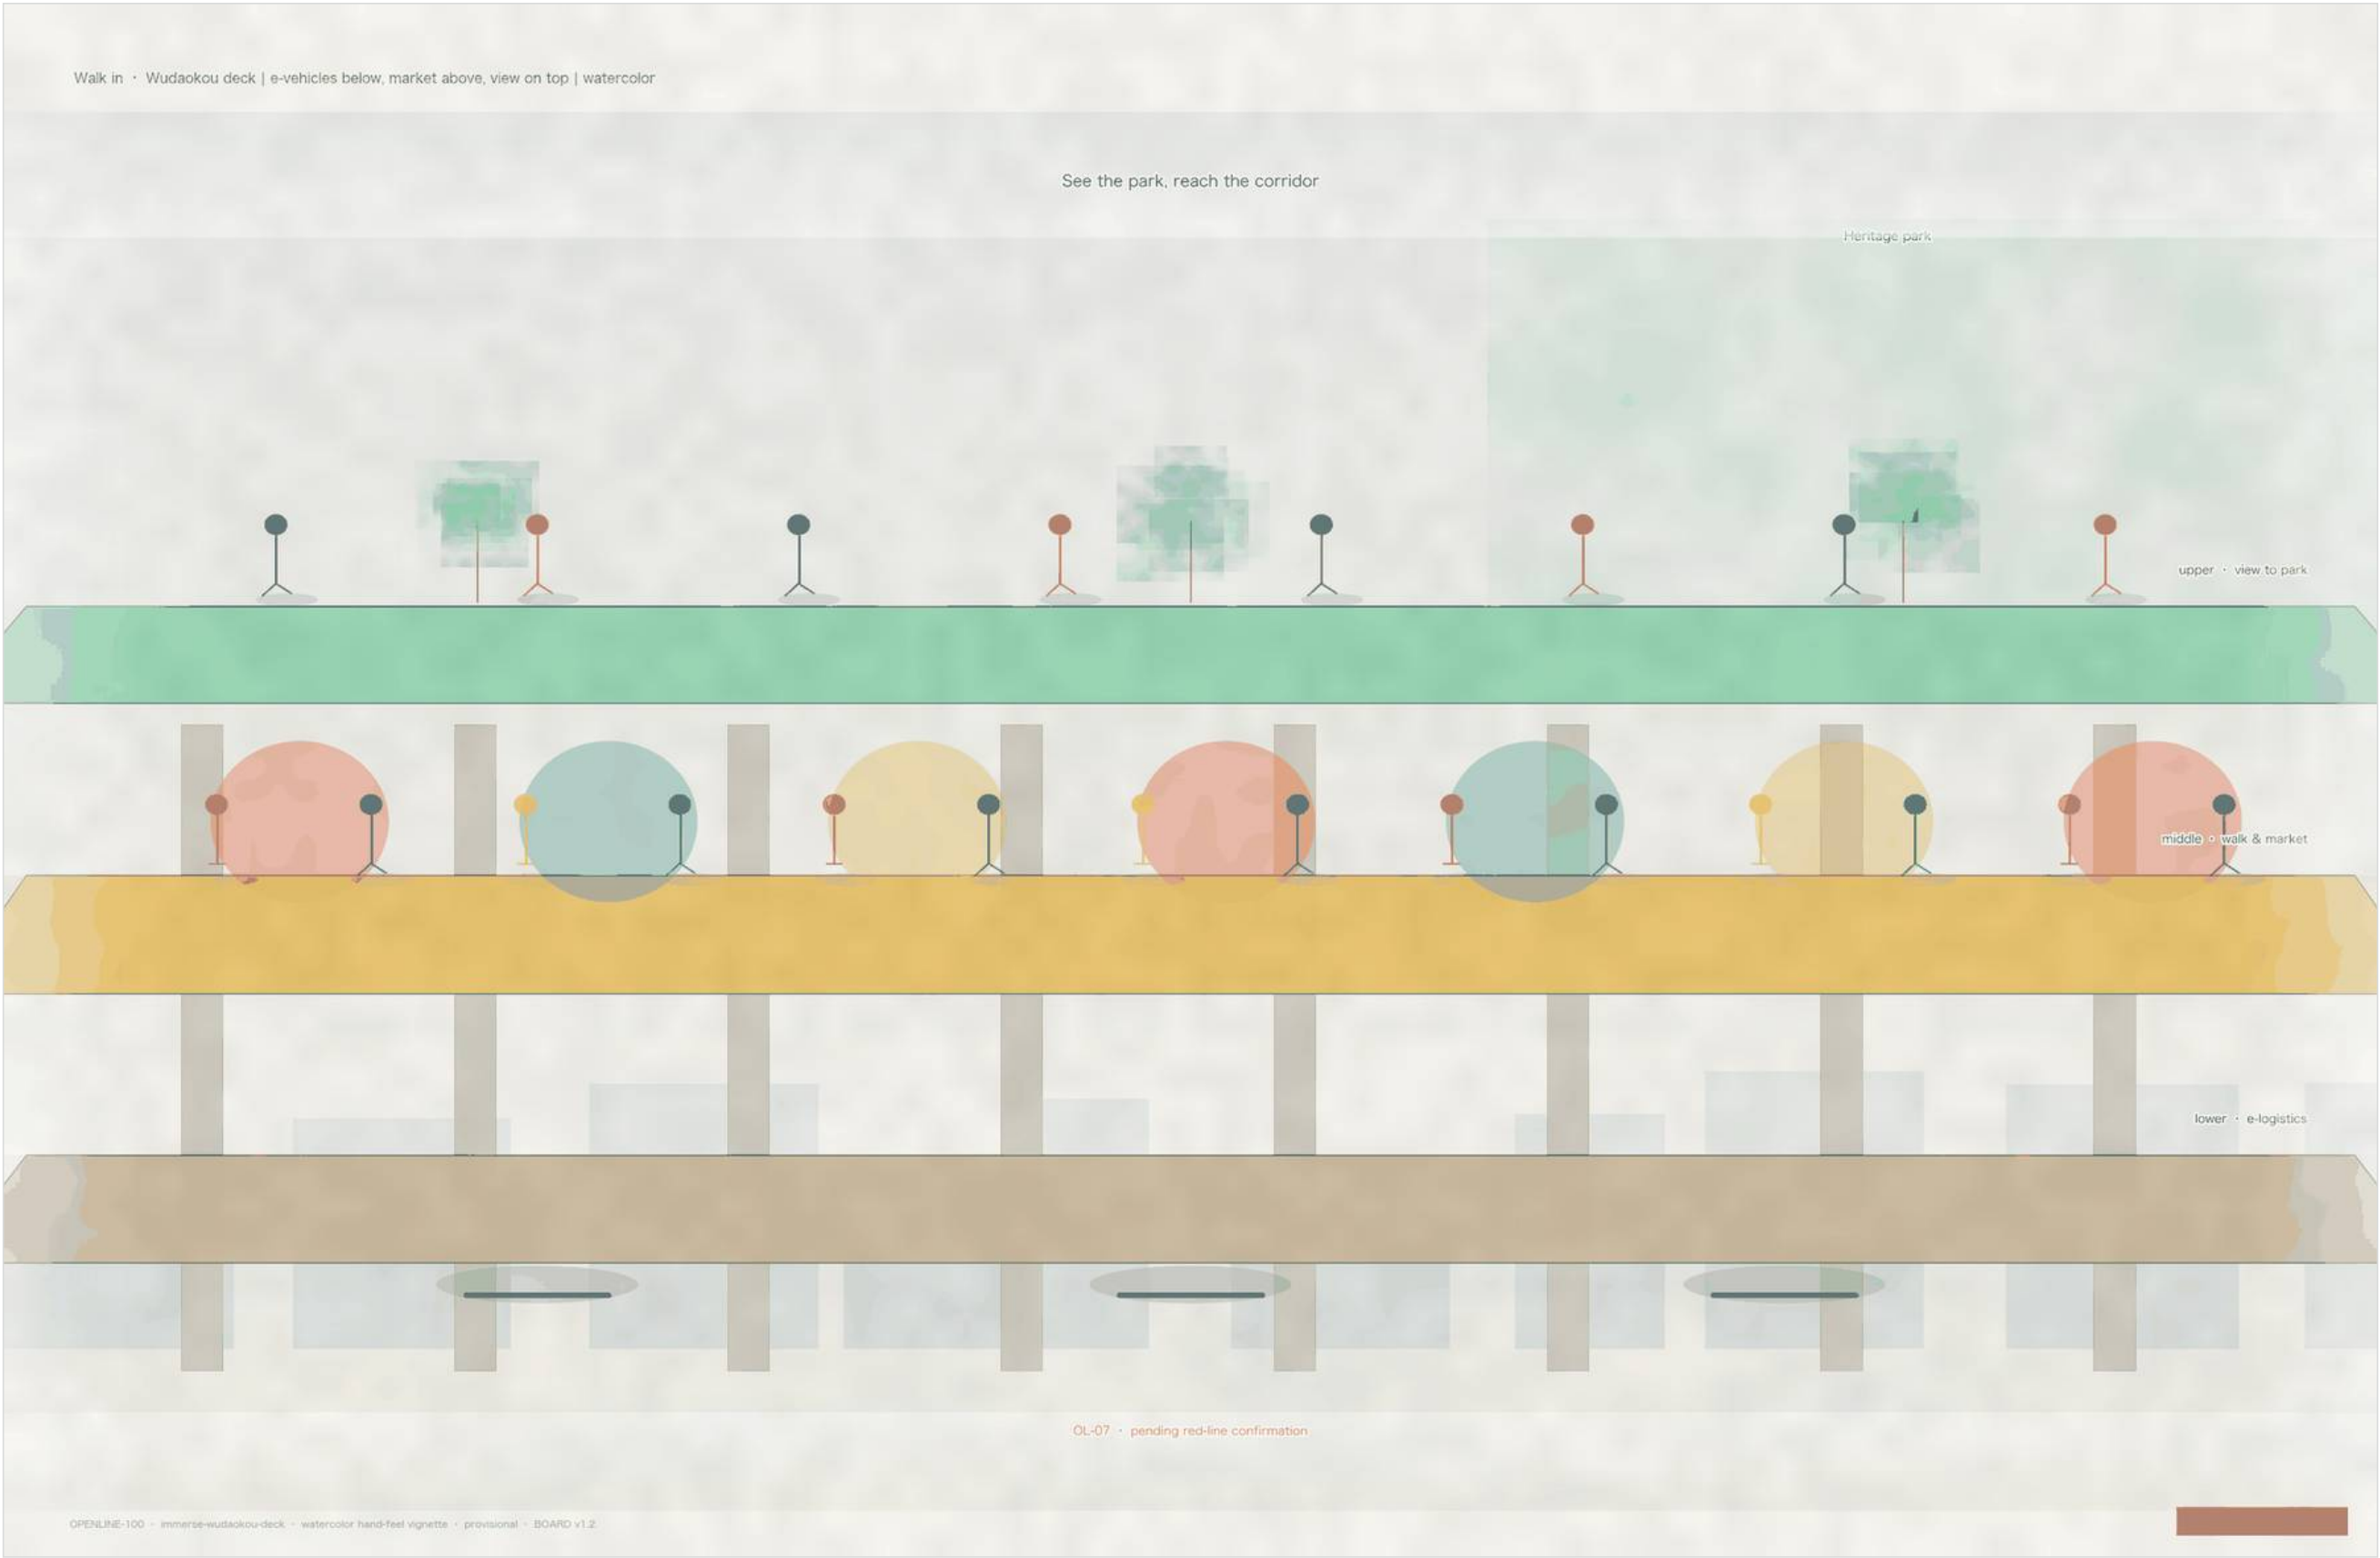

23 Immersive ②: afternoon on the Wudaokou deck



24 Immersive ③: dusk aerial over the Dazhongsi segment