


JINGZHANG RISING Overall Spatial Structure and Land-Use Planning

BOARD 01 / 03 · Spine, terraces, wings and stitches | three scope tiers | land use
Strategic scope 43.6 km² | overall design scope approx. 11.41 km² | three key areas 369.3 ha

Overall Design Area - Site Overview Plan

Boundary, land use, green space and the three Key Areas are projected from this package's geometry/ layers; the boundary is the organiser's provisional rough extent, not a red line.

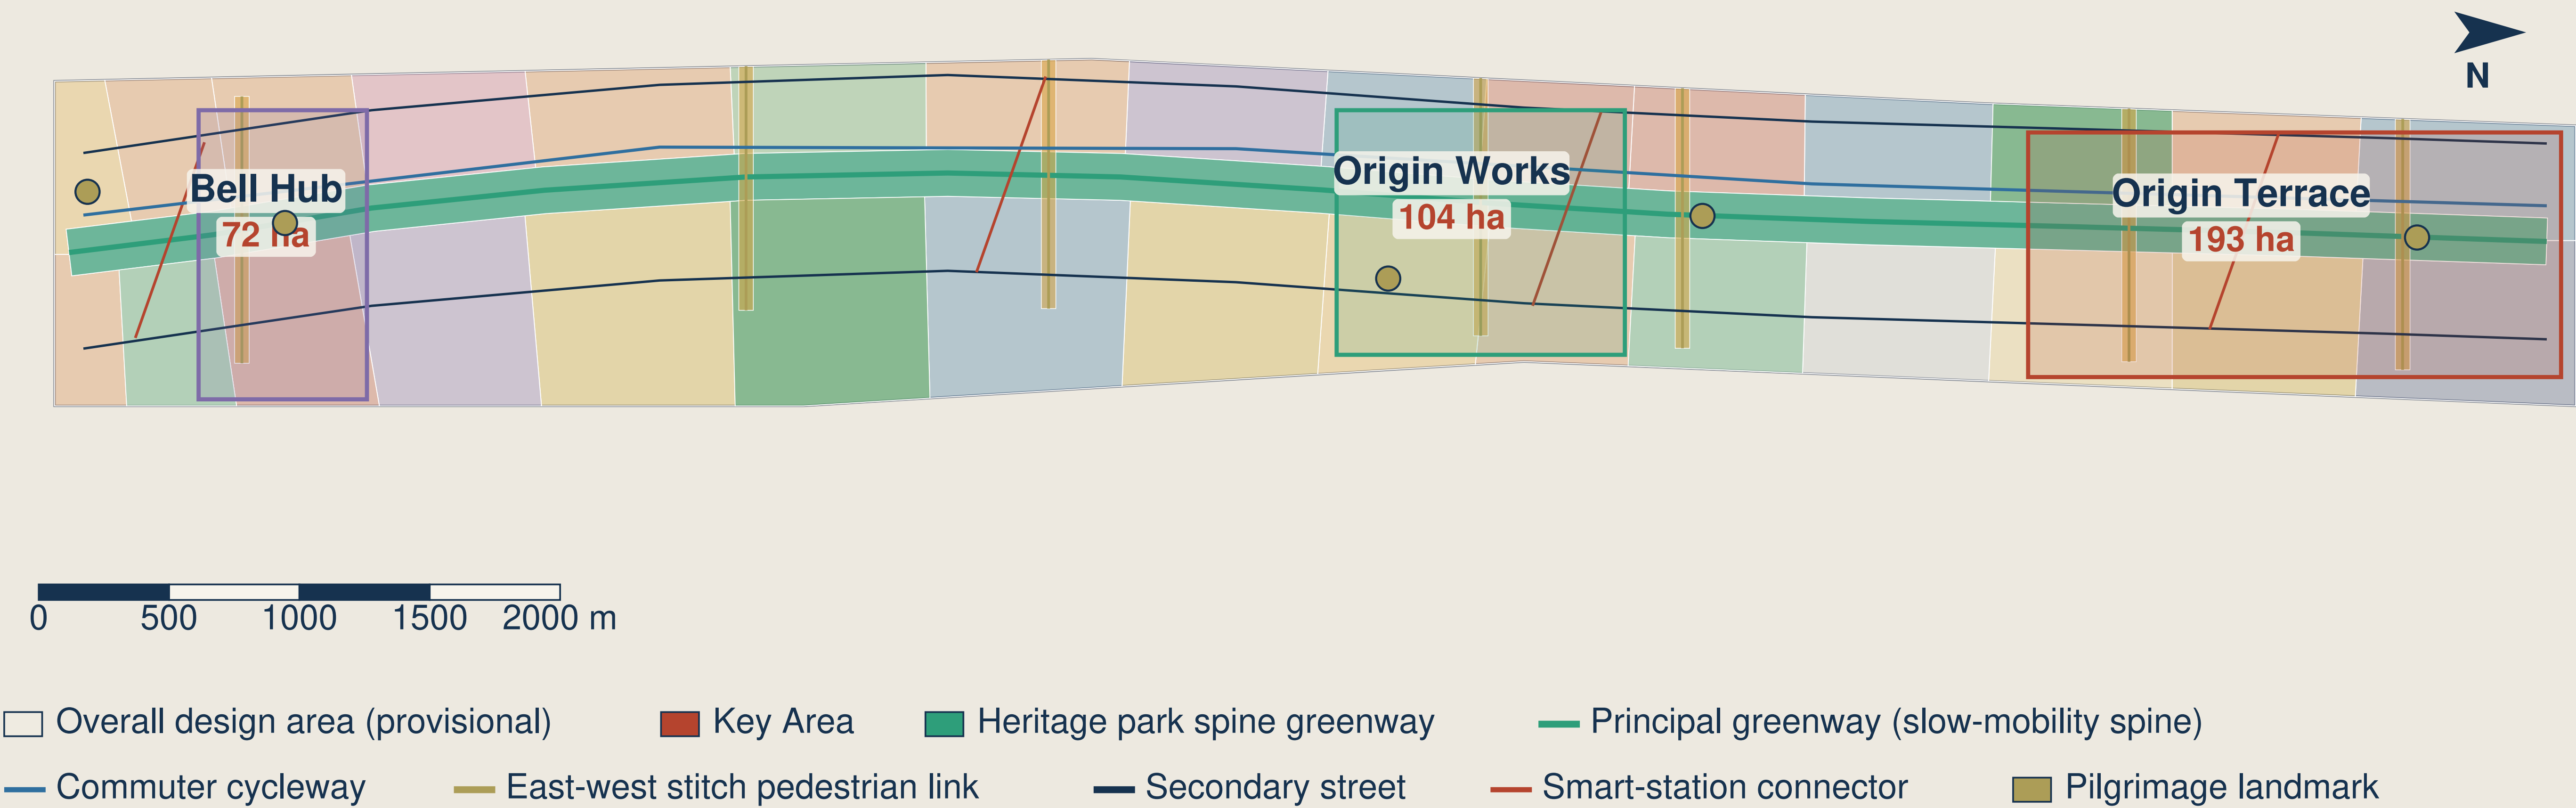

Design area: approx. 11.41 km² (provisional design model; recomputed when the official boundary is issued)

Three Key Areas | Street-Level Spatial Experience + Components

Generated from the package's concept sections and components; not a site photograph, approval rendering or engineering promise

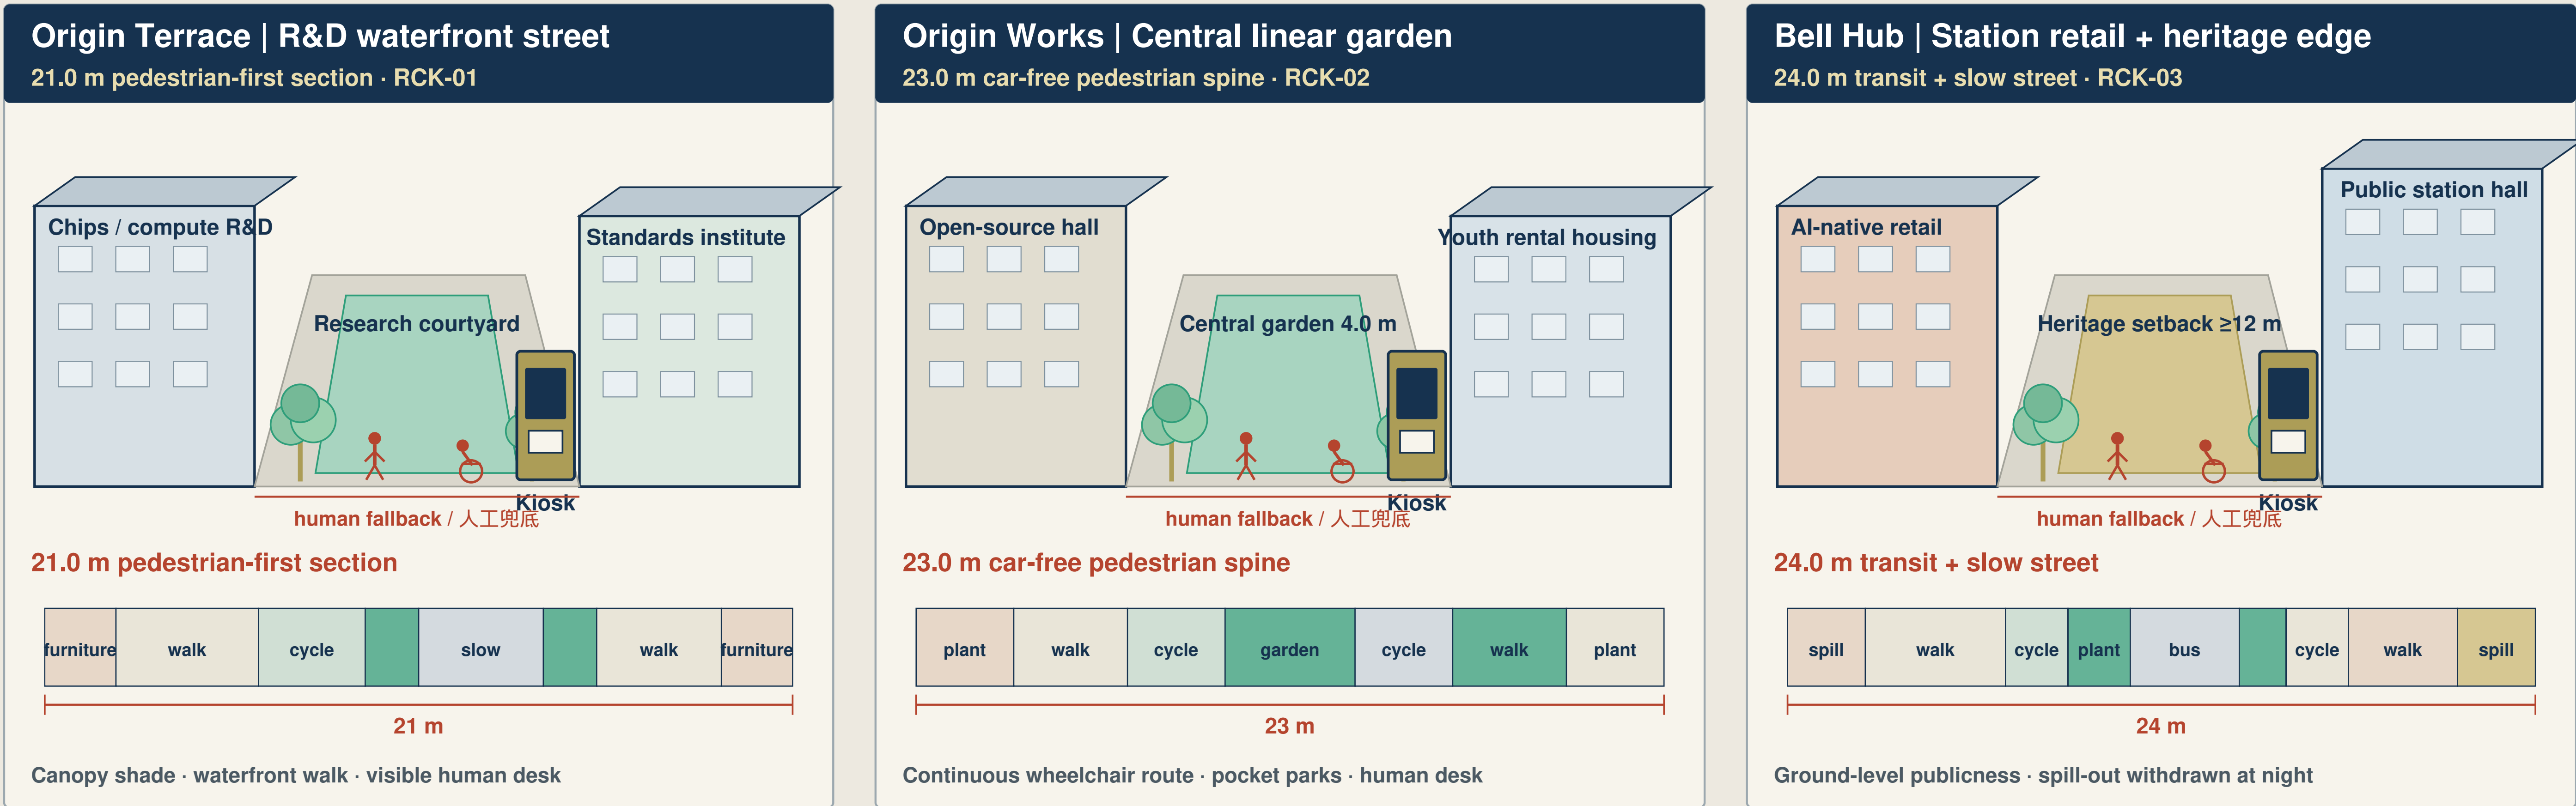


Figure 01: Overall spatial structure (one spine, three terraces, two wings)

- Historical motif: Zhan Tianyou's 1909 人-shaped switchback is a background_only narrative thread pending verification, translated into contemporary AI self-reliance and not used as formal historical evidence.

- 4 pilgrimage landmarks: Renzi Terrace (1909), Gaokao Gate (1949), Clock of Compute (1980), Origin Stele (2026).
- 2 wings: Zhongguancun Tech Service Wing (west) and Xiaoyuehe Scenario Innovation Wing (east).


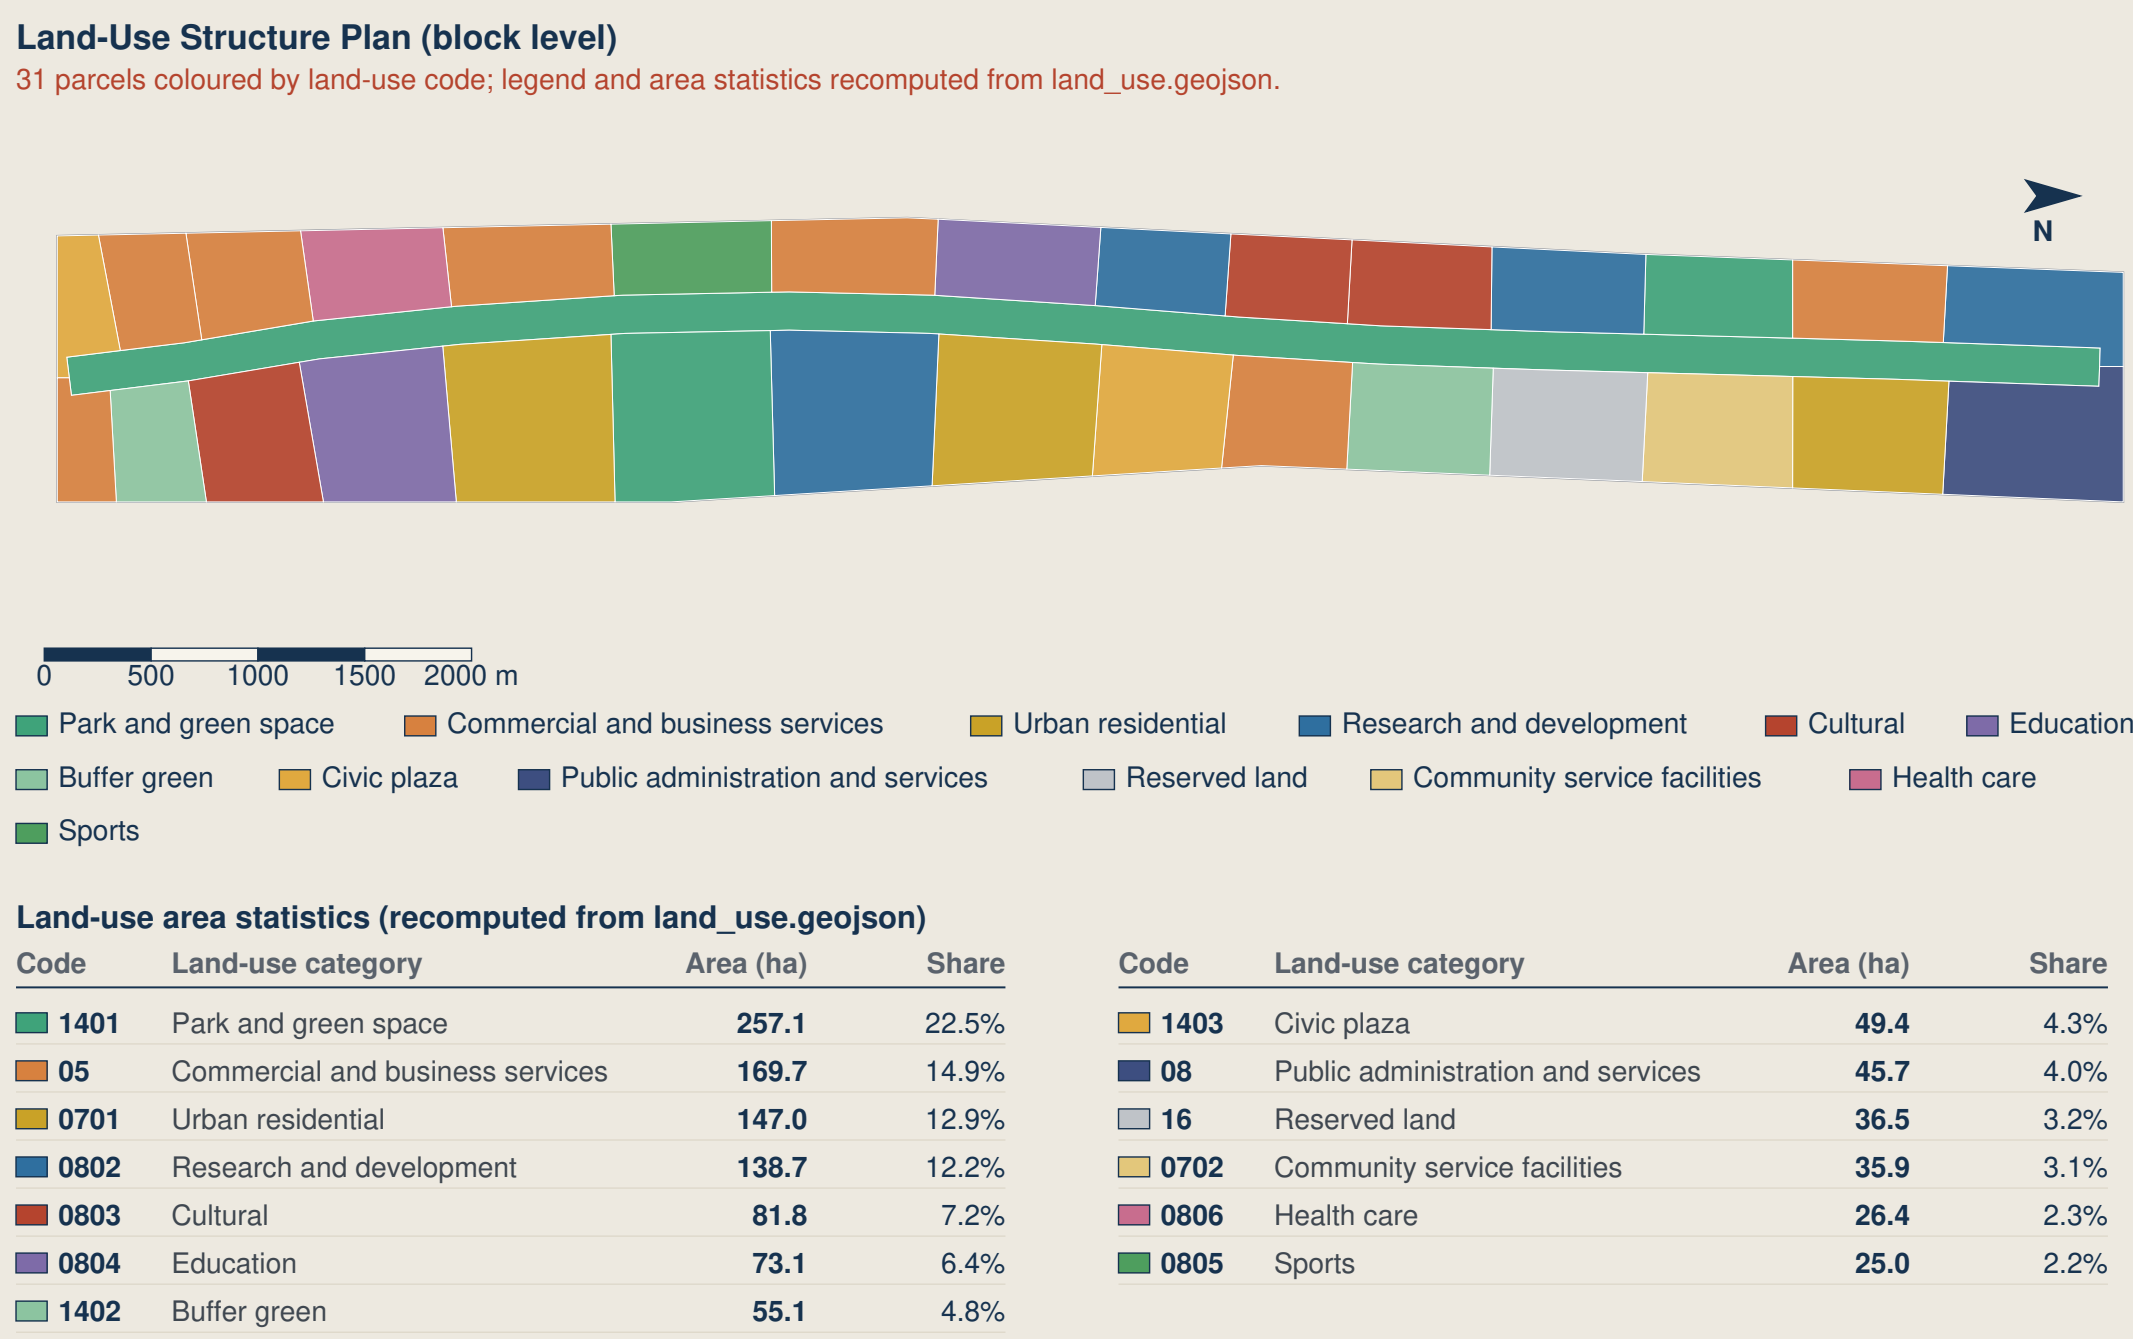


Figure 02: Land-use structure and anchor catchment partition

- Complete partition: 4 smart stations (TOD) and 14 innovation anchor catchments seamlessly partition approx. 11.41 km².
- Functional balance: R&D innovation labs, educational synergy, talent housing and continuous blue-green parks.
- Strict integrity: no gaps, no overlaps; recomputed against the geometry layers in EPSG:4548.
- 31 parcels total 1,141.3 ha, from the same source as metrics.json site_area_sqm.


JINGZHANG RISING Detailed Design of the Three Key Areas

BOARD 02 / 03 · Origin Terrace 193 ha | Origin Works 104 ha | Bell Hub 72 ha
15 blocks with concept ranges | FAR and height guidelines | Report Card Kiosk deployment

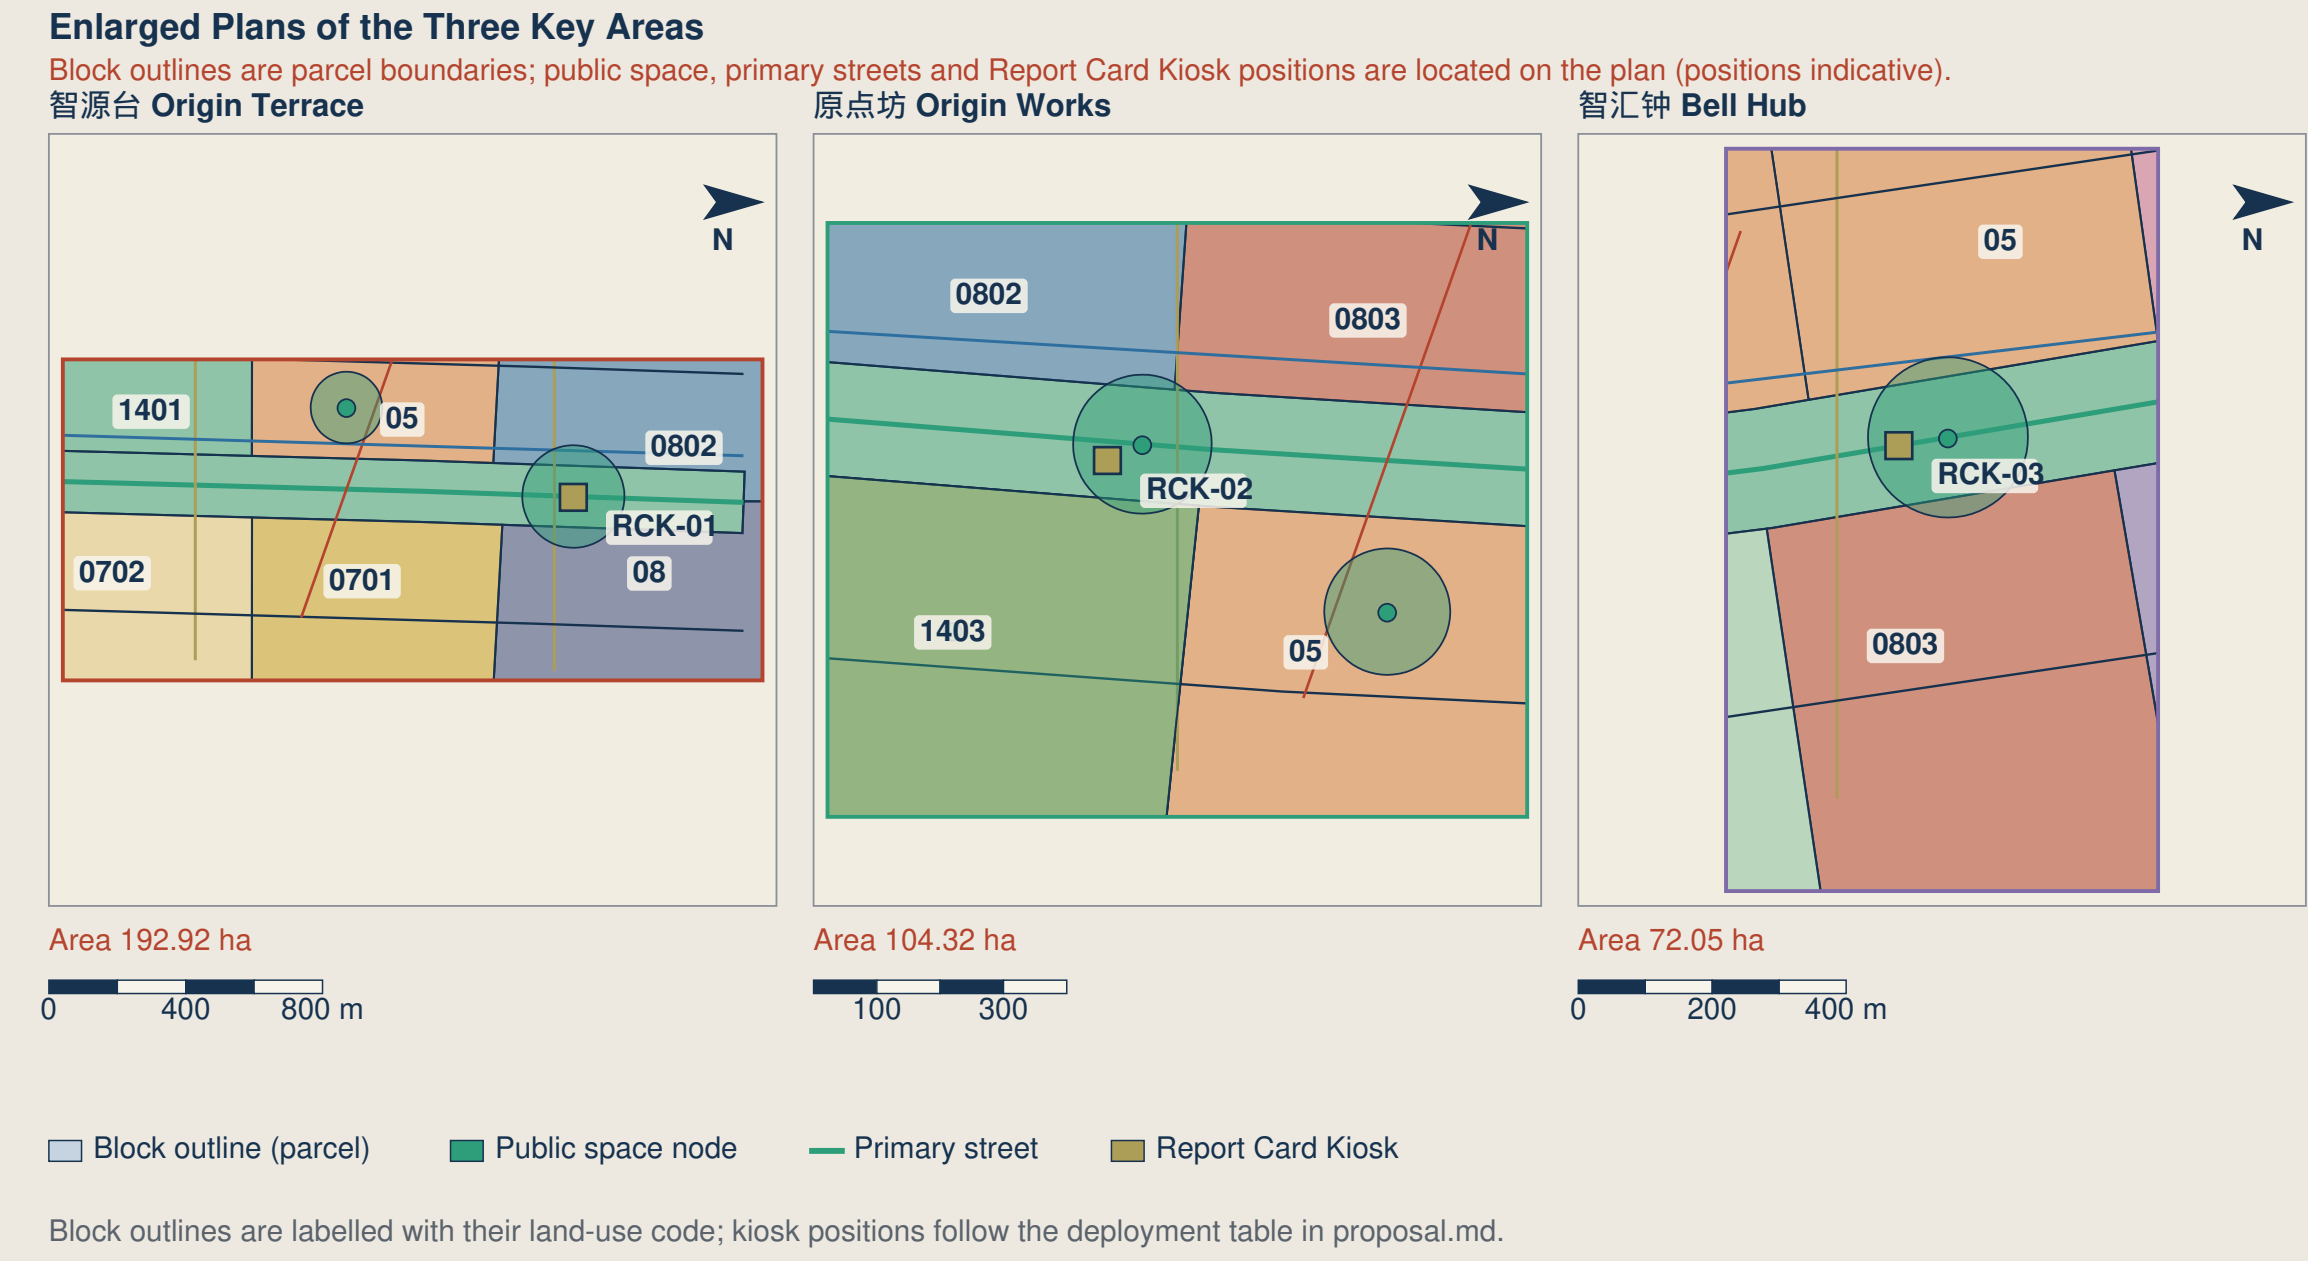


Three Key Areas | Street-Level Spatial Experience + Components


Generated from the package's concept sections and components; not a site photograph, approval rendering or engineering promise

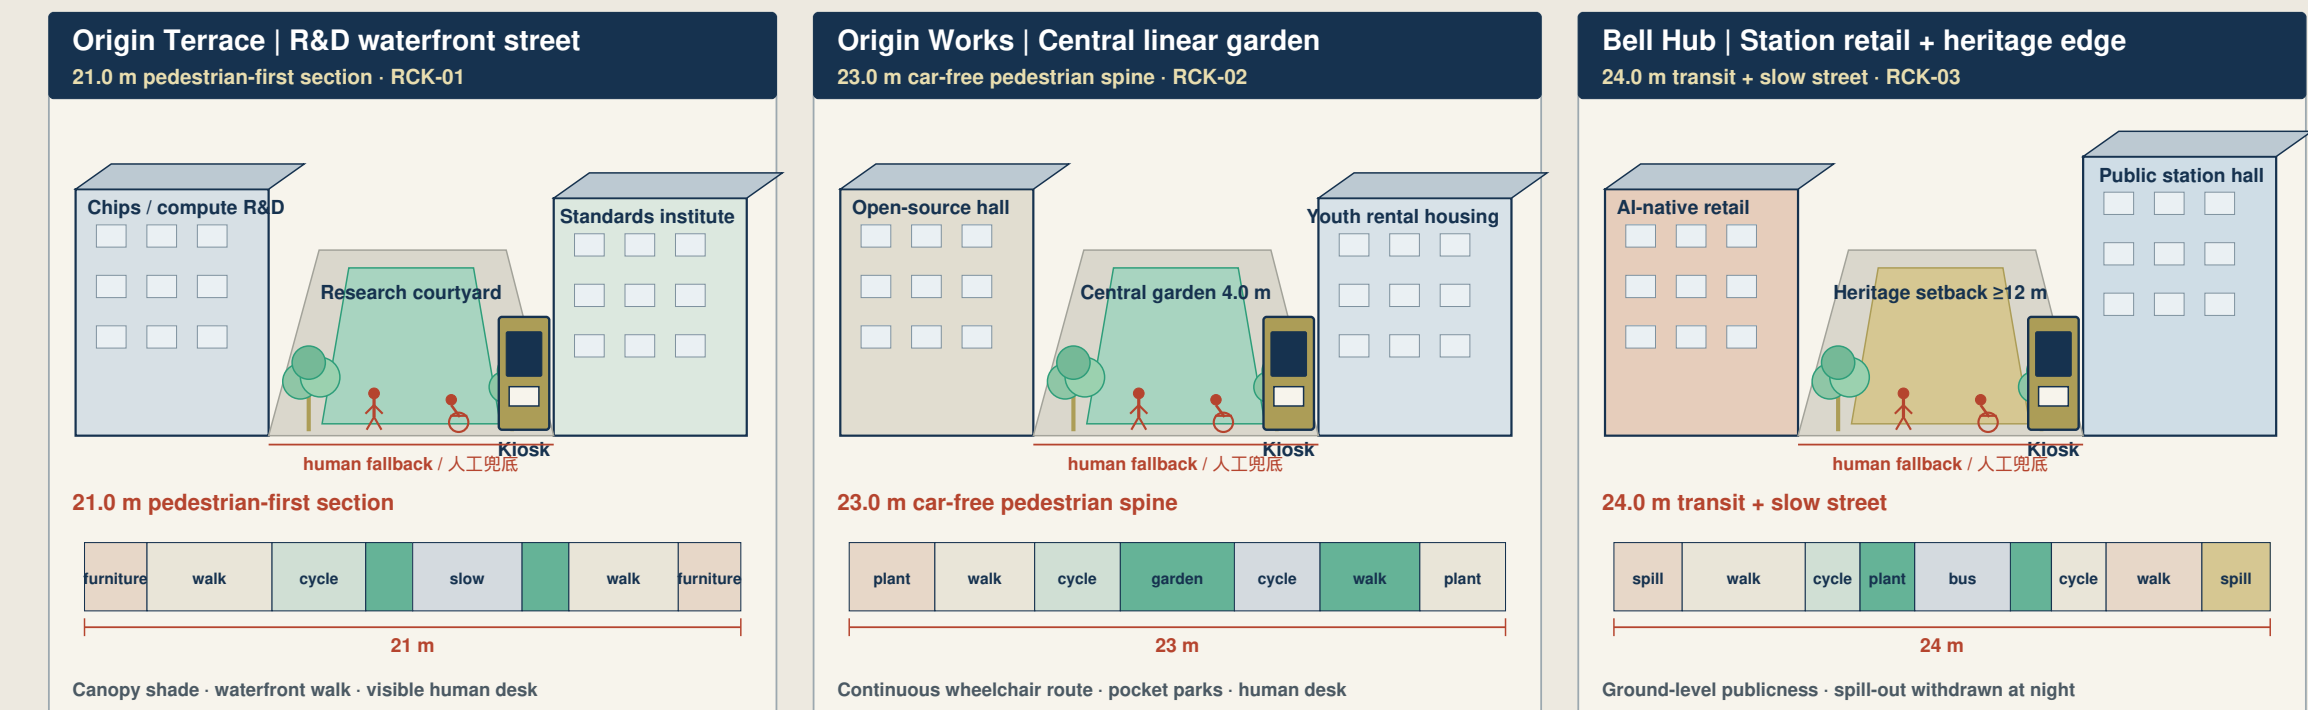


key-areas

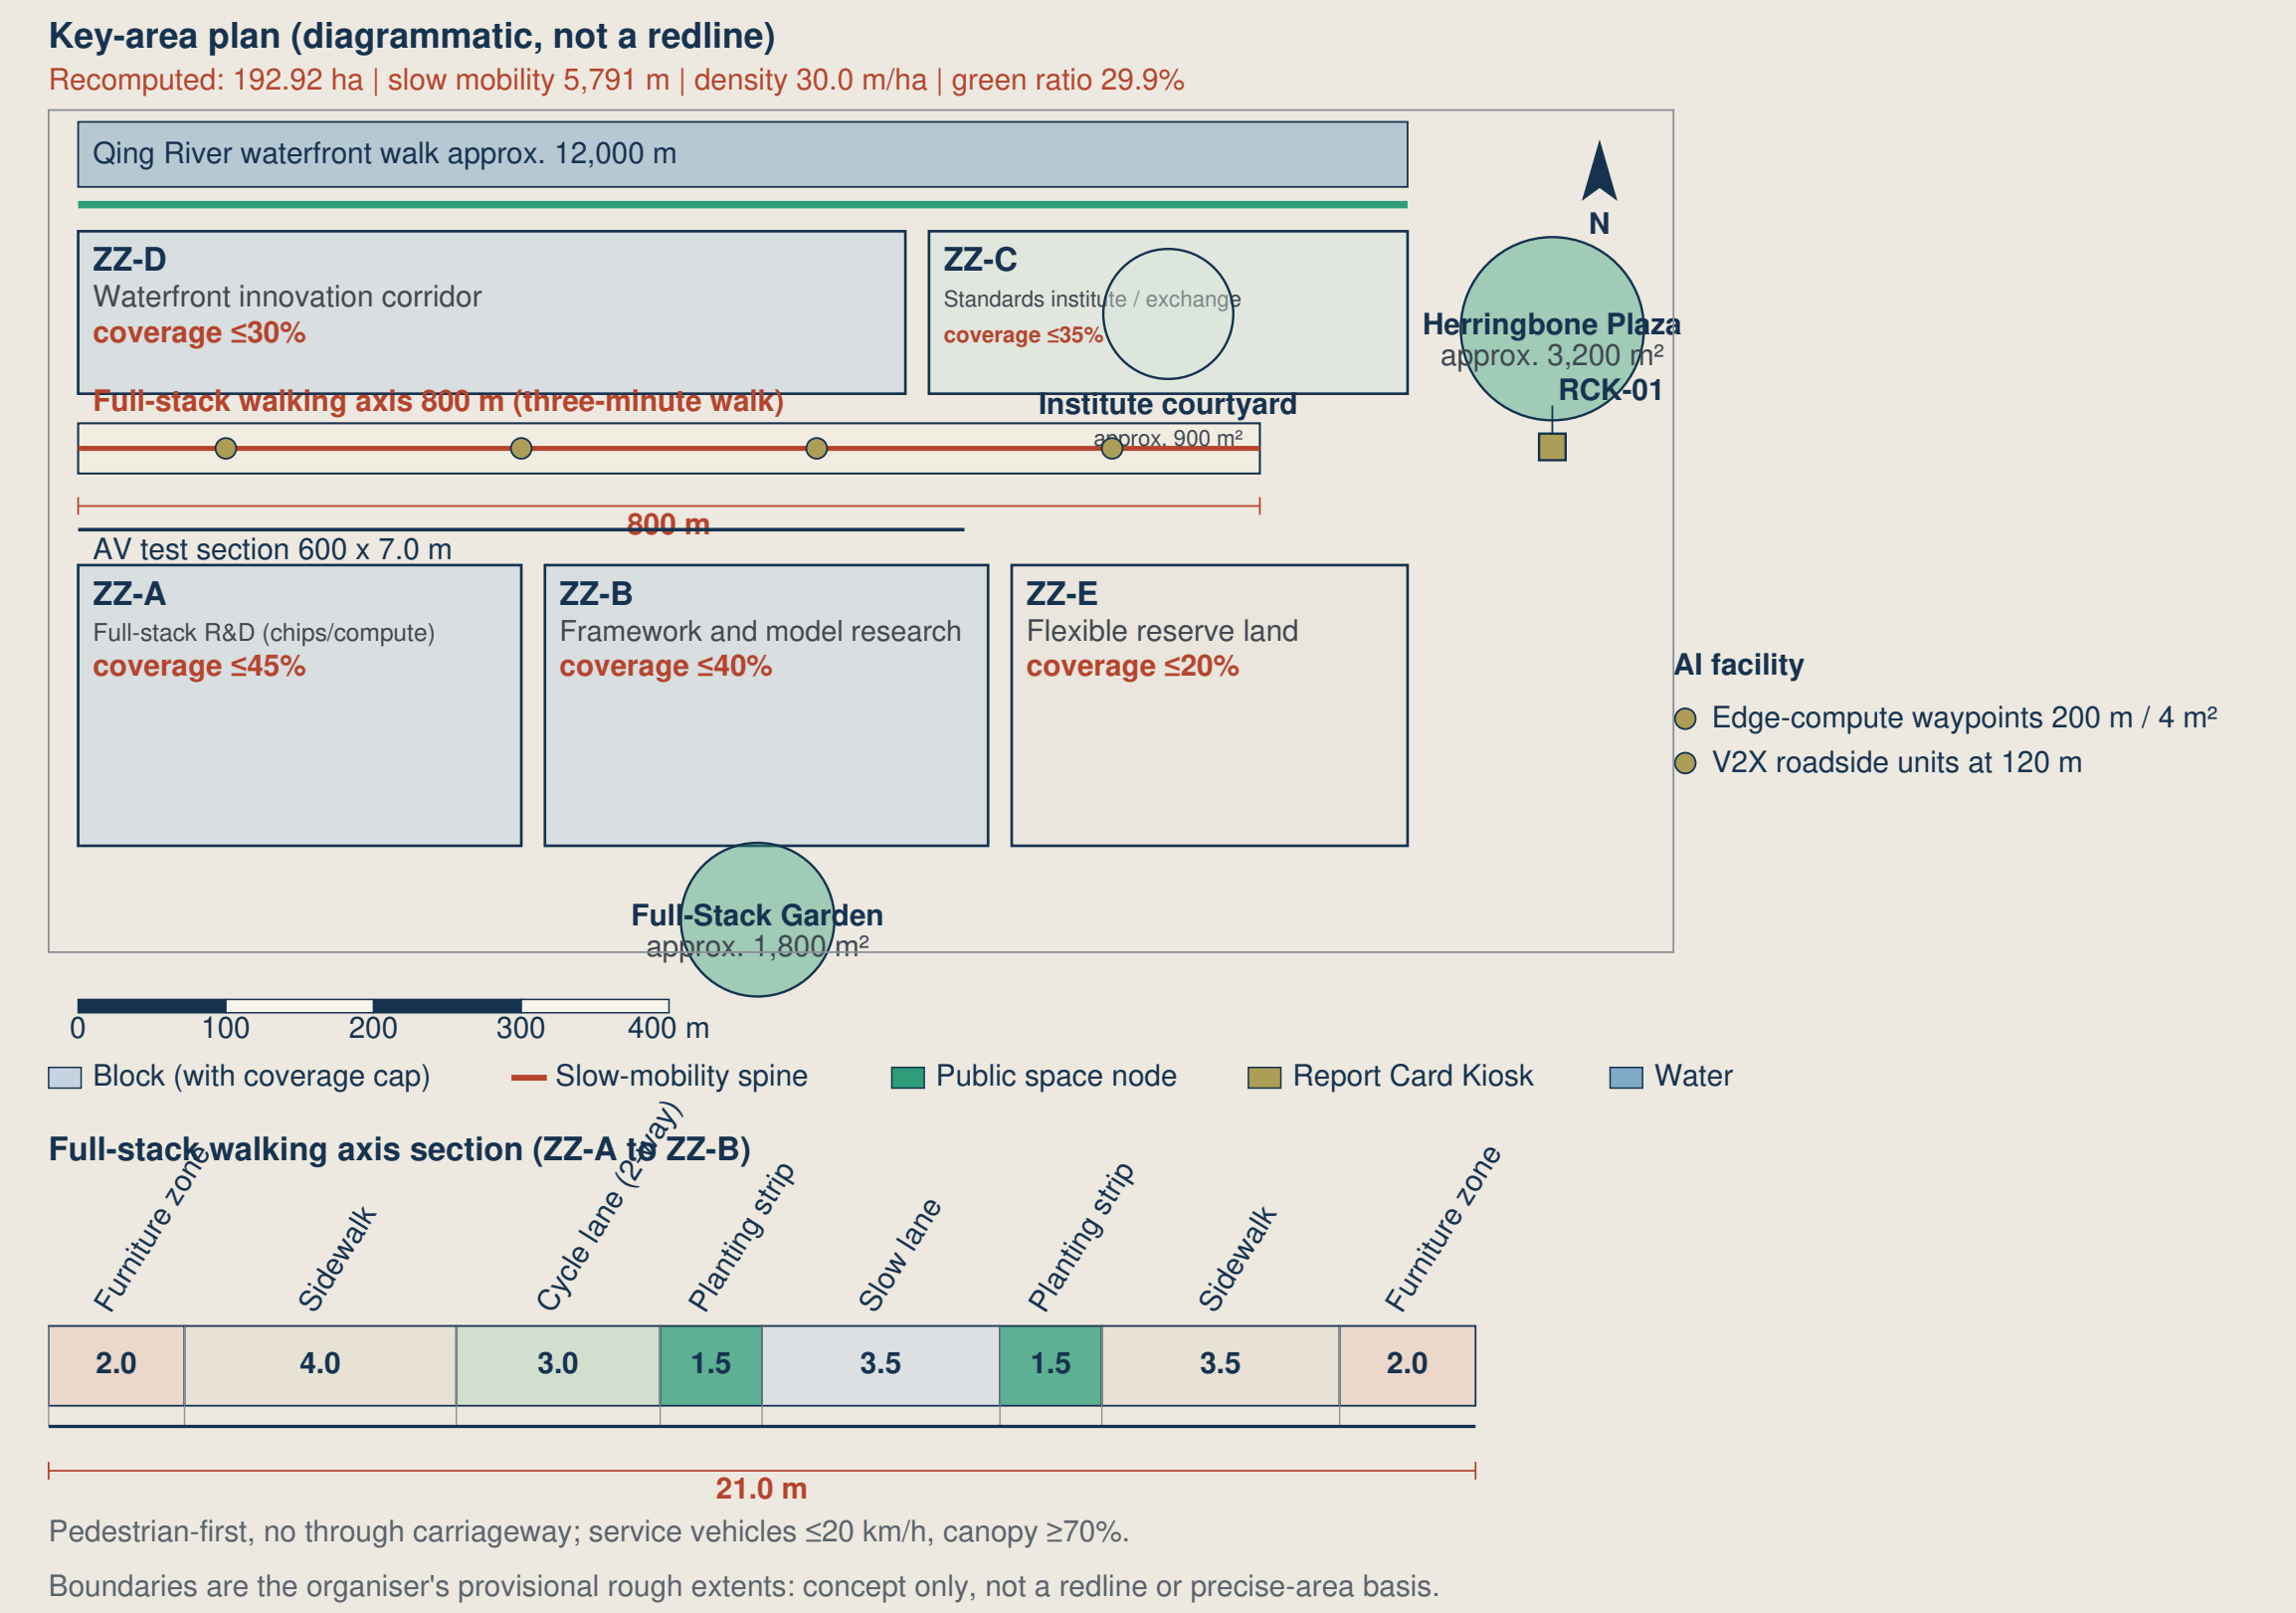

key-areas-zhongzhiyuan

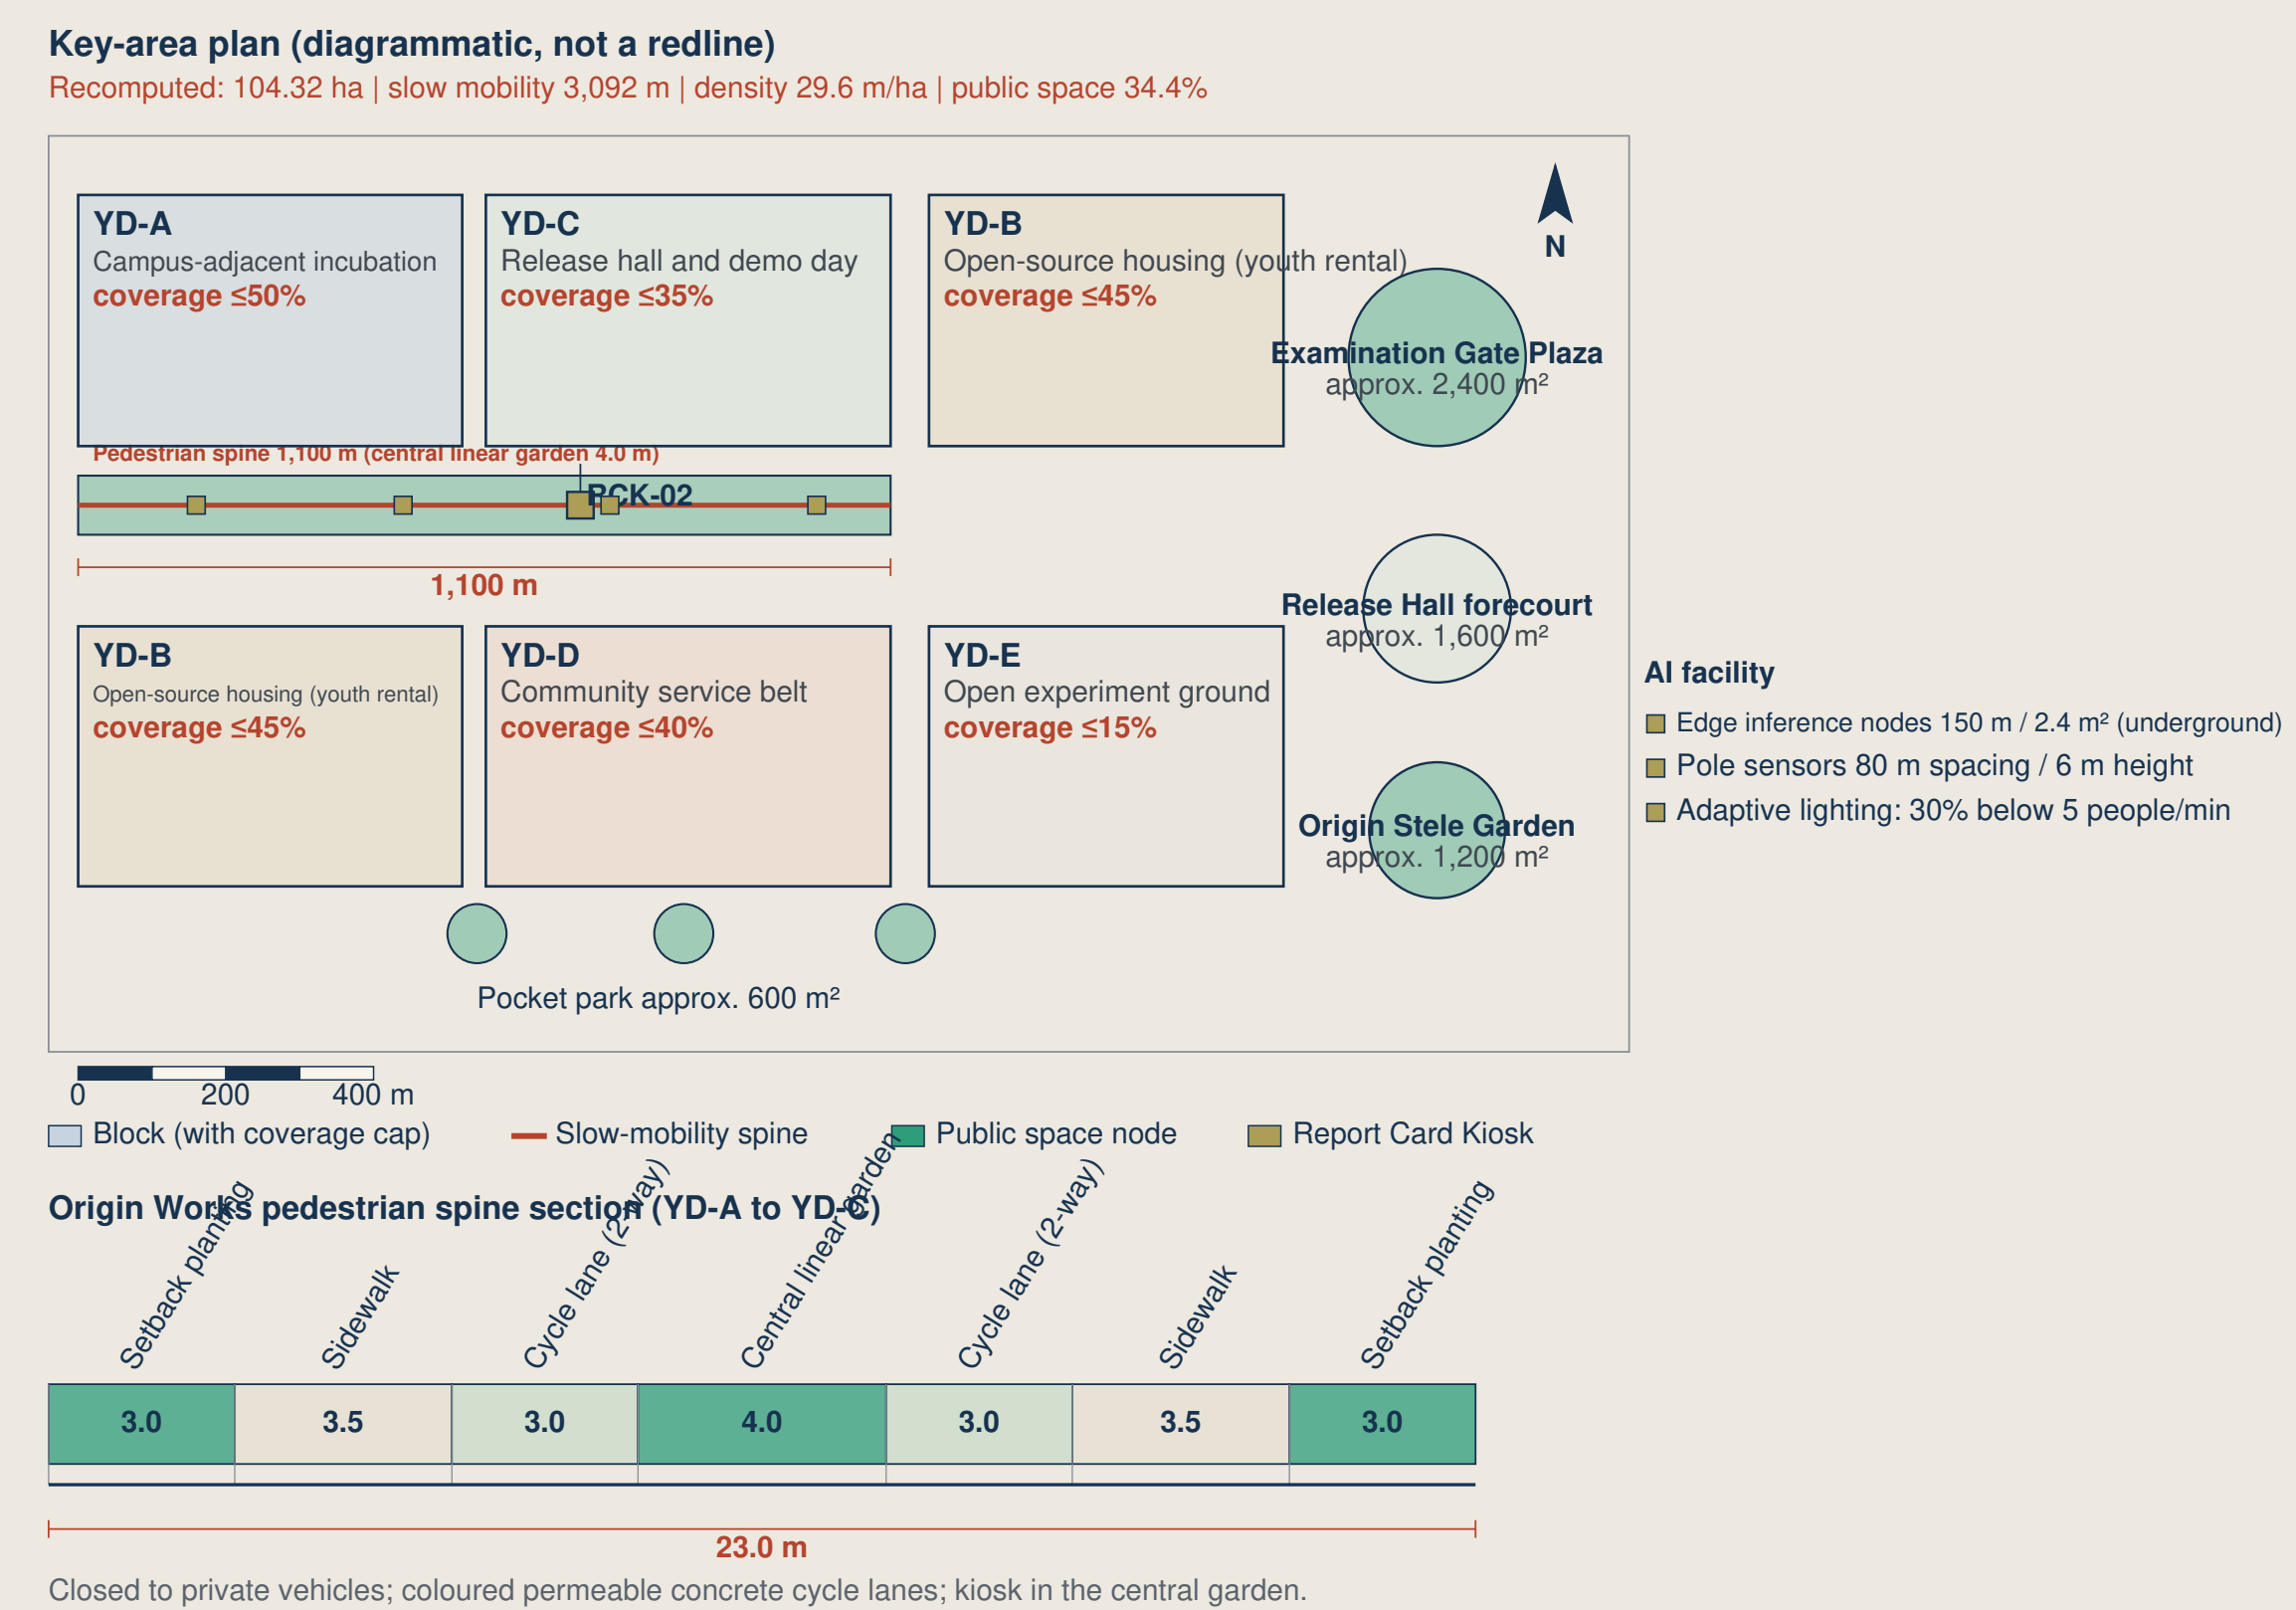

key-areas-origin-works

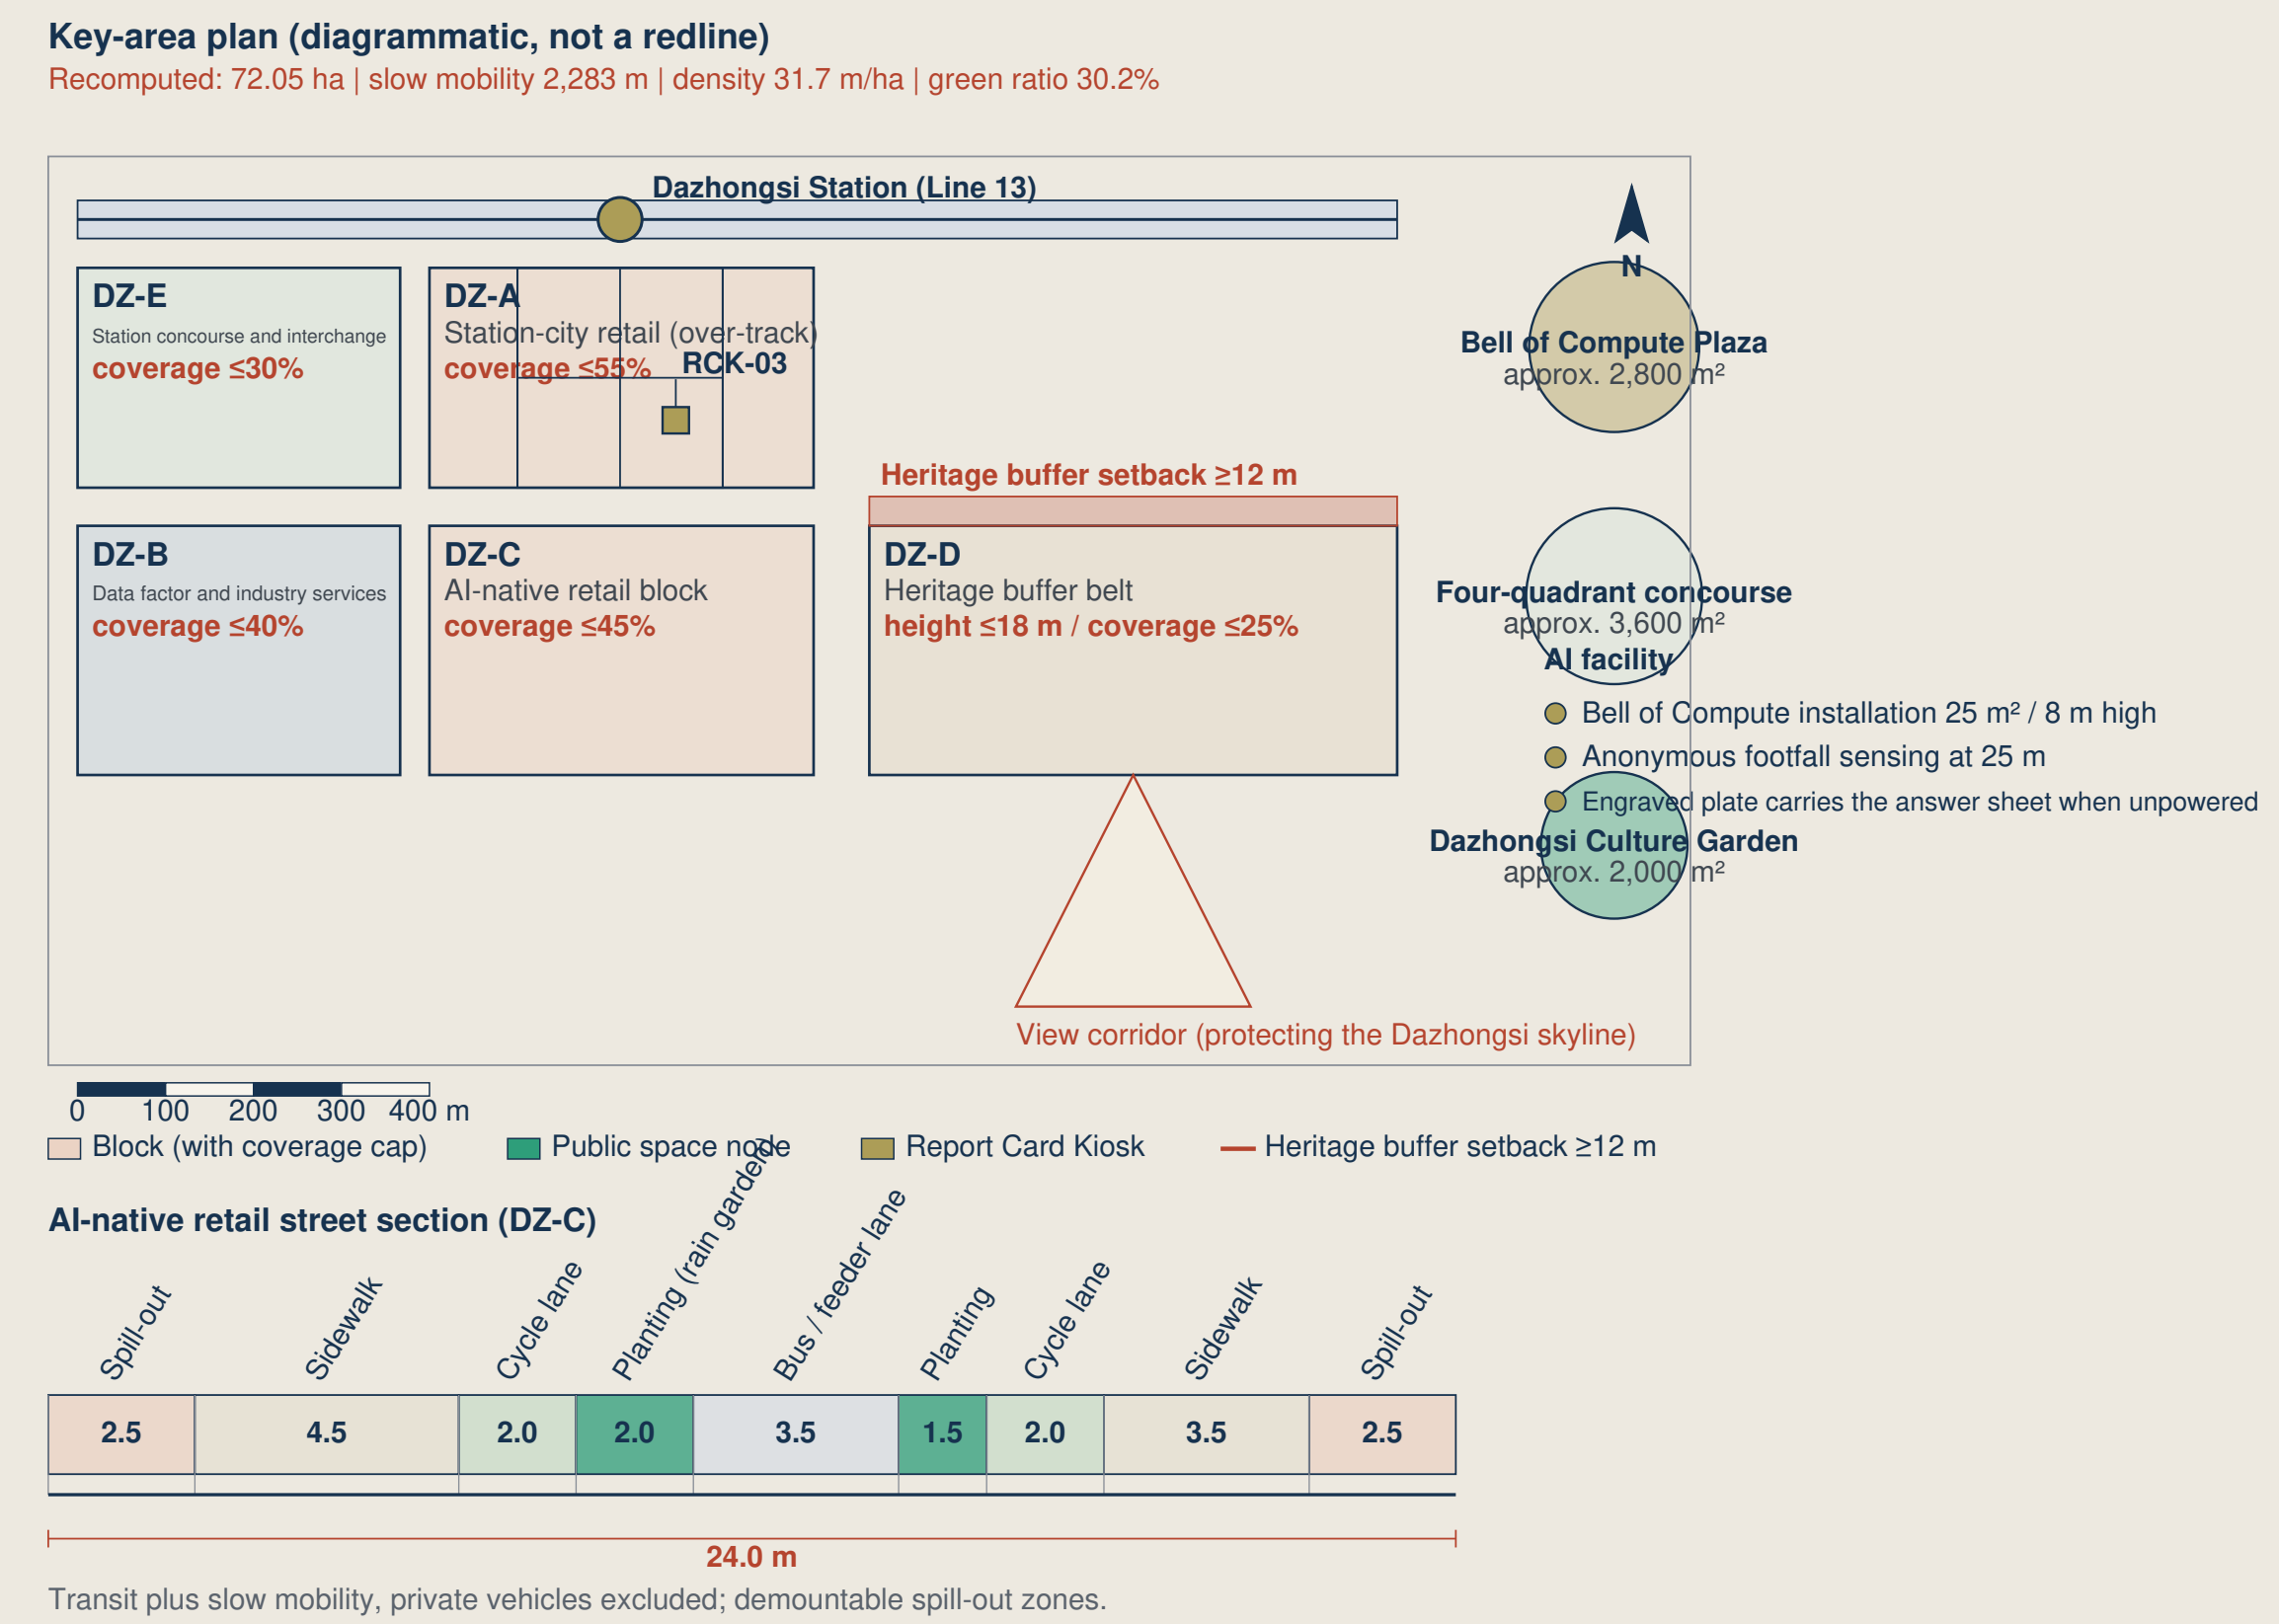

key-areas-dazhongsi

Origin Terrace / Zhongzhiyuan (193 ha)

- Blocks: ZZ-A frontier lab, ZZ-B incubation, ZZ-C talent housing, ZZ-D service, ZZ-E green space.
- Concept guidelines: FAR 1.6–3.5, height 24–60 m, building coverage ≤ 35%.
- Public anchor: Renzi Terrace memorial, Qinghe smart station TOD and the RCK-01 kiosk.
- Mobility: slow-mobility density 30.0 m/ha, length 5,791 m.

Origin Works (104 ha) and Bell Hub (72 ha)

- Origin Works blocks: YD-A open source hall, YD-B campus link, YD-C apartments, YD-D mixed TOD, YD-E origin plaza.
- Origin Works guidelines: FAR 1.2–2.8, height 18–45 m, coverage ≤ 35%; slow-mobility density 29.6 m/ha, length 3,092 m.
- Bell Hub blocks: DZ-A green compute, DZ-B industry engine, DZ-C commercial, DZ-D living, DZ-E quadrant park.
- Bell Hub guidelines: FAR 1.8–3.6, height 24–60 m, coverage ≤ 35%; slow-mobility density 31.7 m/ha, length 2,283 m.
- Public anchors: Gaokao Gate at Tsinghuayuan station, Wudaokou TOD, Clock of Compute, the Dazhongsi four-quadrant concourse, RCK-02 and RCK-03 kiosks.

The design scope and the three key areas use the organiser's provisional rough substitute boundary: concept recommendations only, never a statutory redline, an approval basis or a precise-area basis. Once official polygons are published the geometry, metrics, drawings and HTML must all be recomputed.


Submission package: cf3901646 | Author: Charlie JIANG | Licence: COMMUNITY-DISPLAY-ONLY

JINGZHANG RISING Mobility, Ecology, AI Scenarios and Metric Evidence

BOARD 03 / 03 · Continuous greenway | 7 stitch links | kiosk and 60 metrics
Greenway 9.0 km | 12 scenarios and 4 sandboxes | public report card governance | 100% self-check PASS

Slow Mobility, Blue-Green and Water Overlay Plan

Cycling network, pedestrian priority, green corridors and waterfront are overlaid on one base plan; each layer is listed in the legend below.

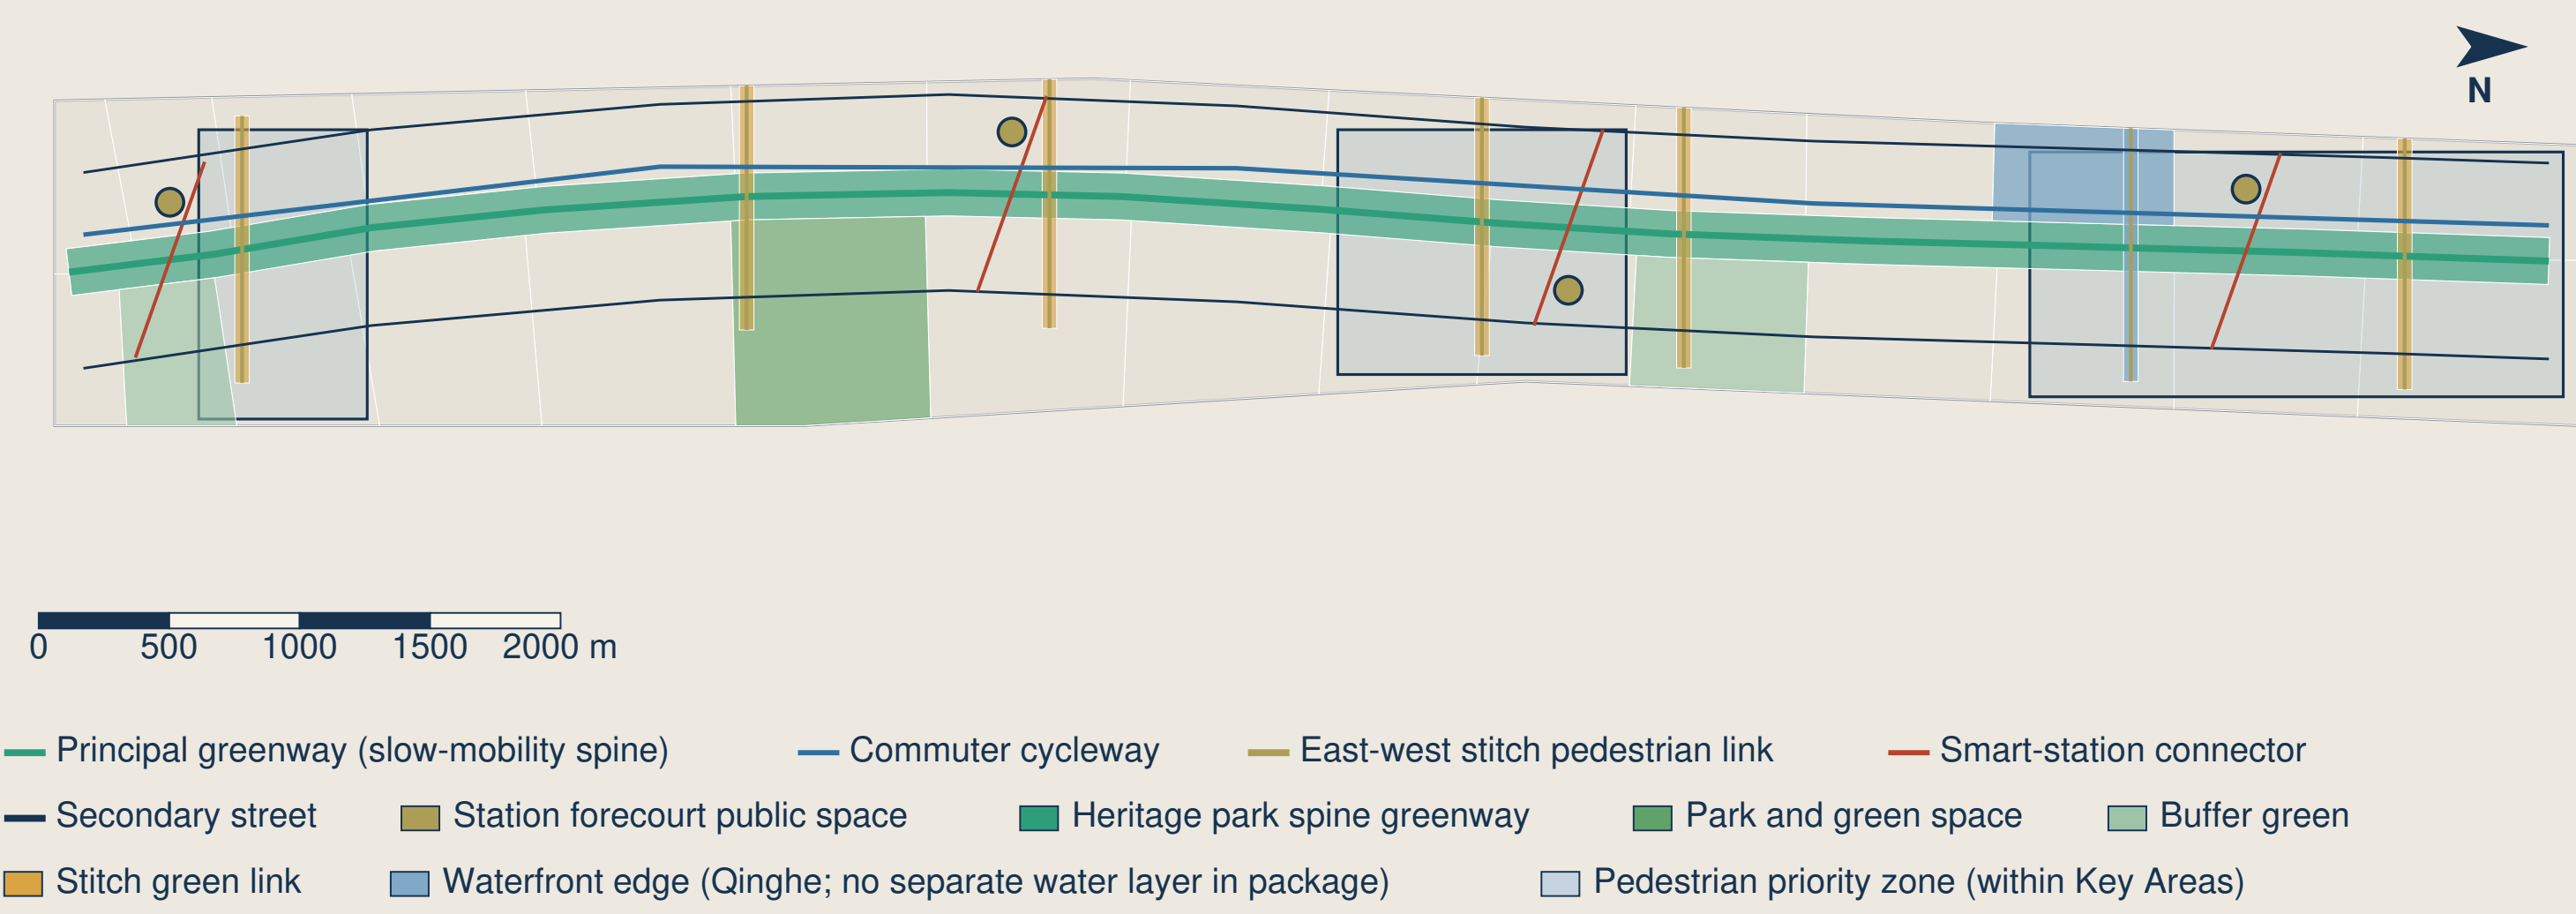


Slow-mobility network 25,932 m (greenway + stitch links + cycleway, recomputed from roads.geojson)

mobility-bluegreen

Slow-mobility network and station-area feeders (by key area)

Lengths and densities are recomputed from geometry/; sections and timings are concept proposals

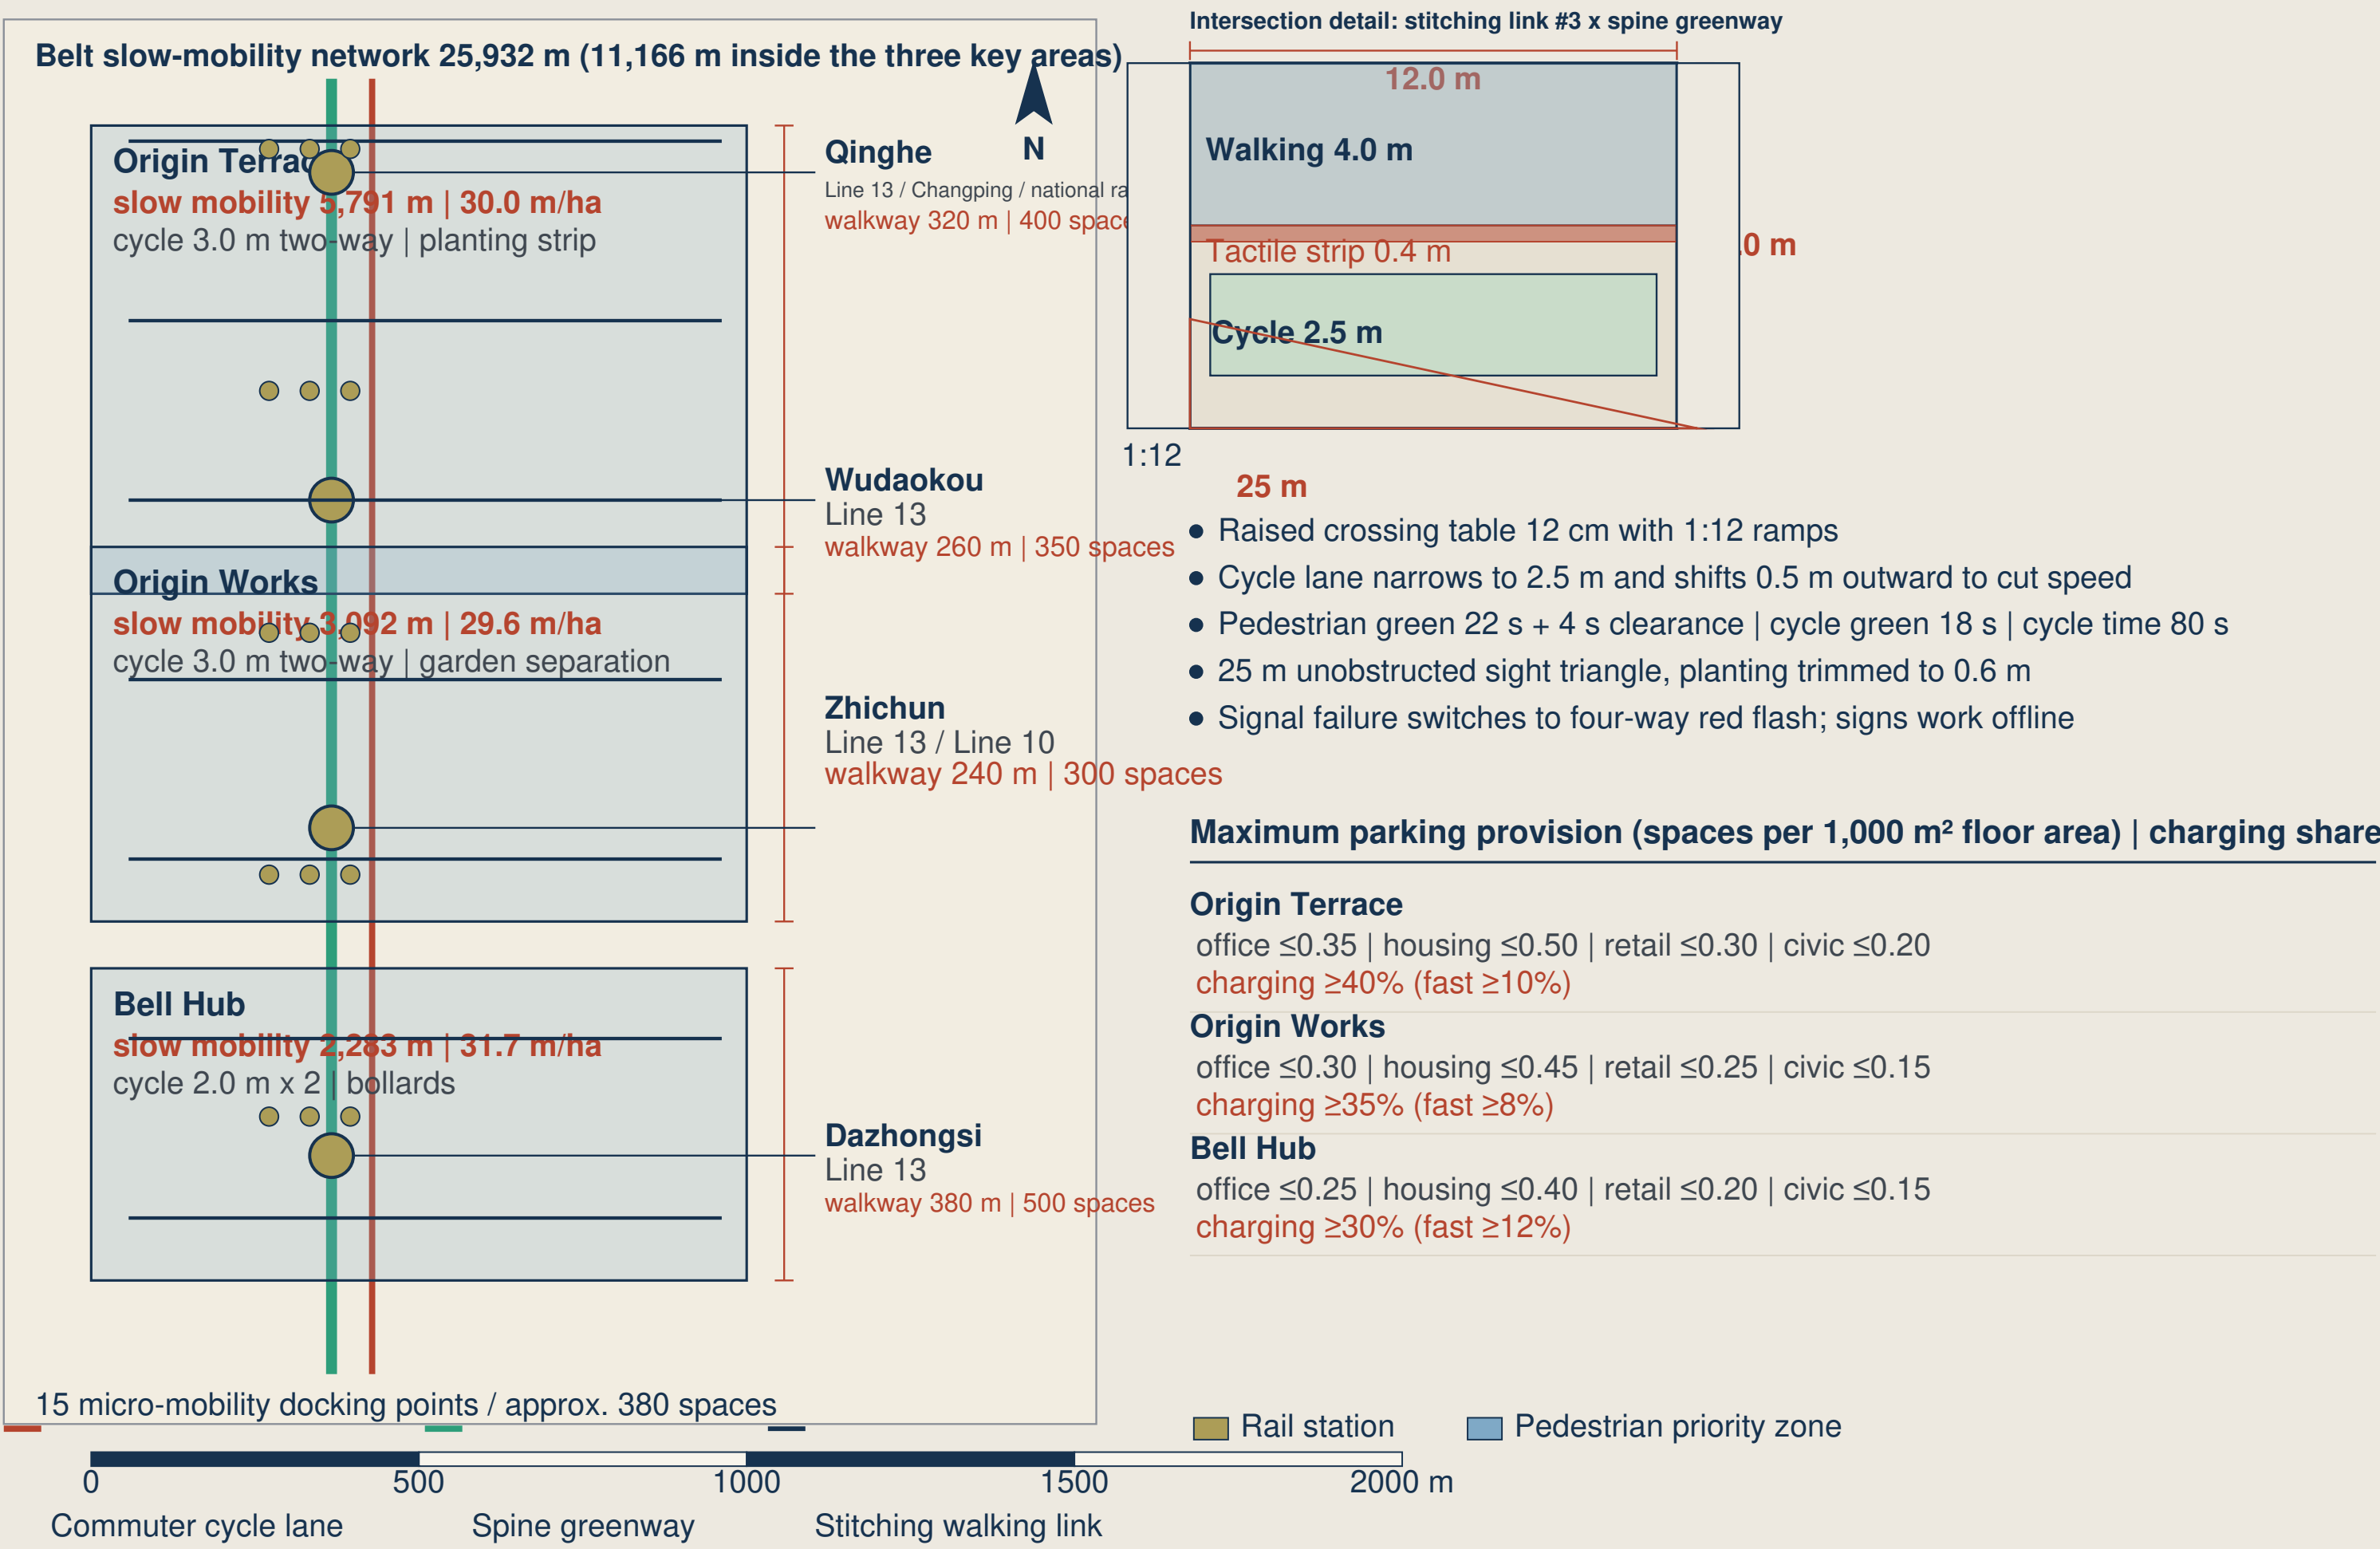


mobility-strategy

Figure 04: Mobility and blue-green public space system

- North-south spine: 9.0 km continuous greenway plus a commuter bike express lane.
- East-west stitch: 7 pedestrian stitch corridors overcoming the former railway severance.
- Station integration: 4 smart stations with 500 m covered walkways, bike hubs within 50 m and EV charging ≥ 40%.
- Intersections and parking: 12 cm raised crossing tables, 1:12 ramps and parking caps by key area.

Report Card Kiosk: elevations and footprint (front / side / clear zone)

Overall 1,800 x 2,200 x 2,800 mm | footprint 3.96 m² | freestanding, demountable

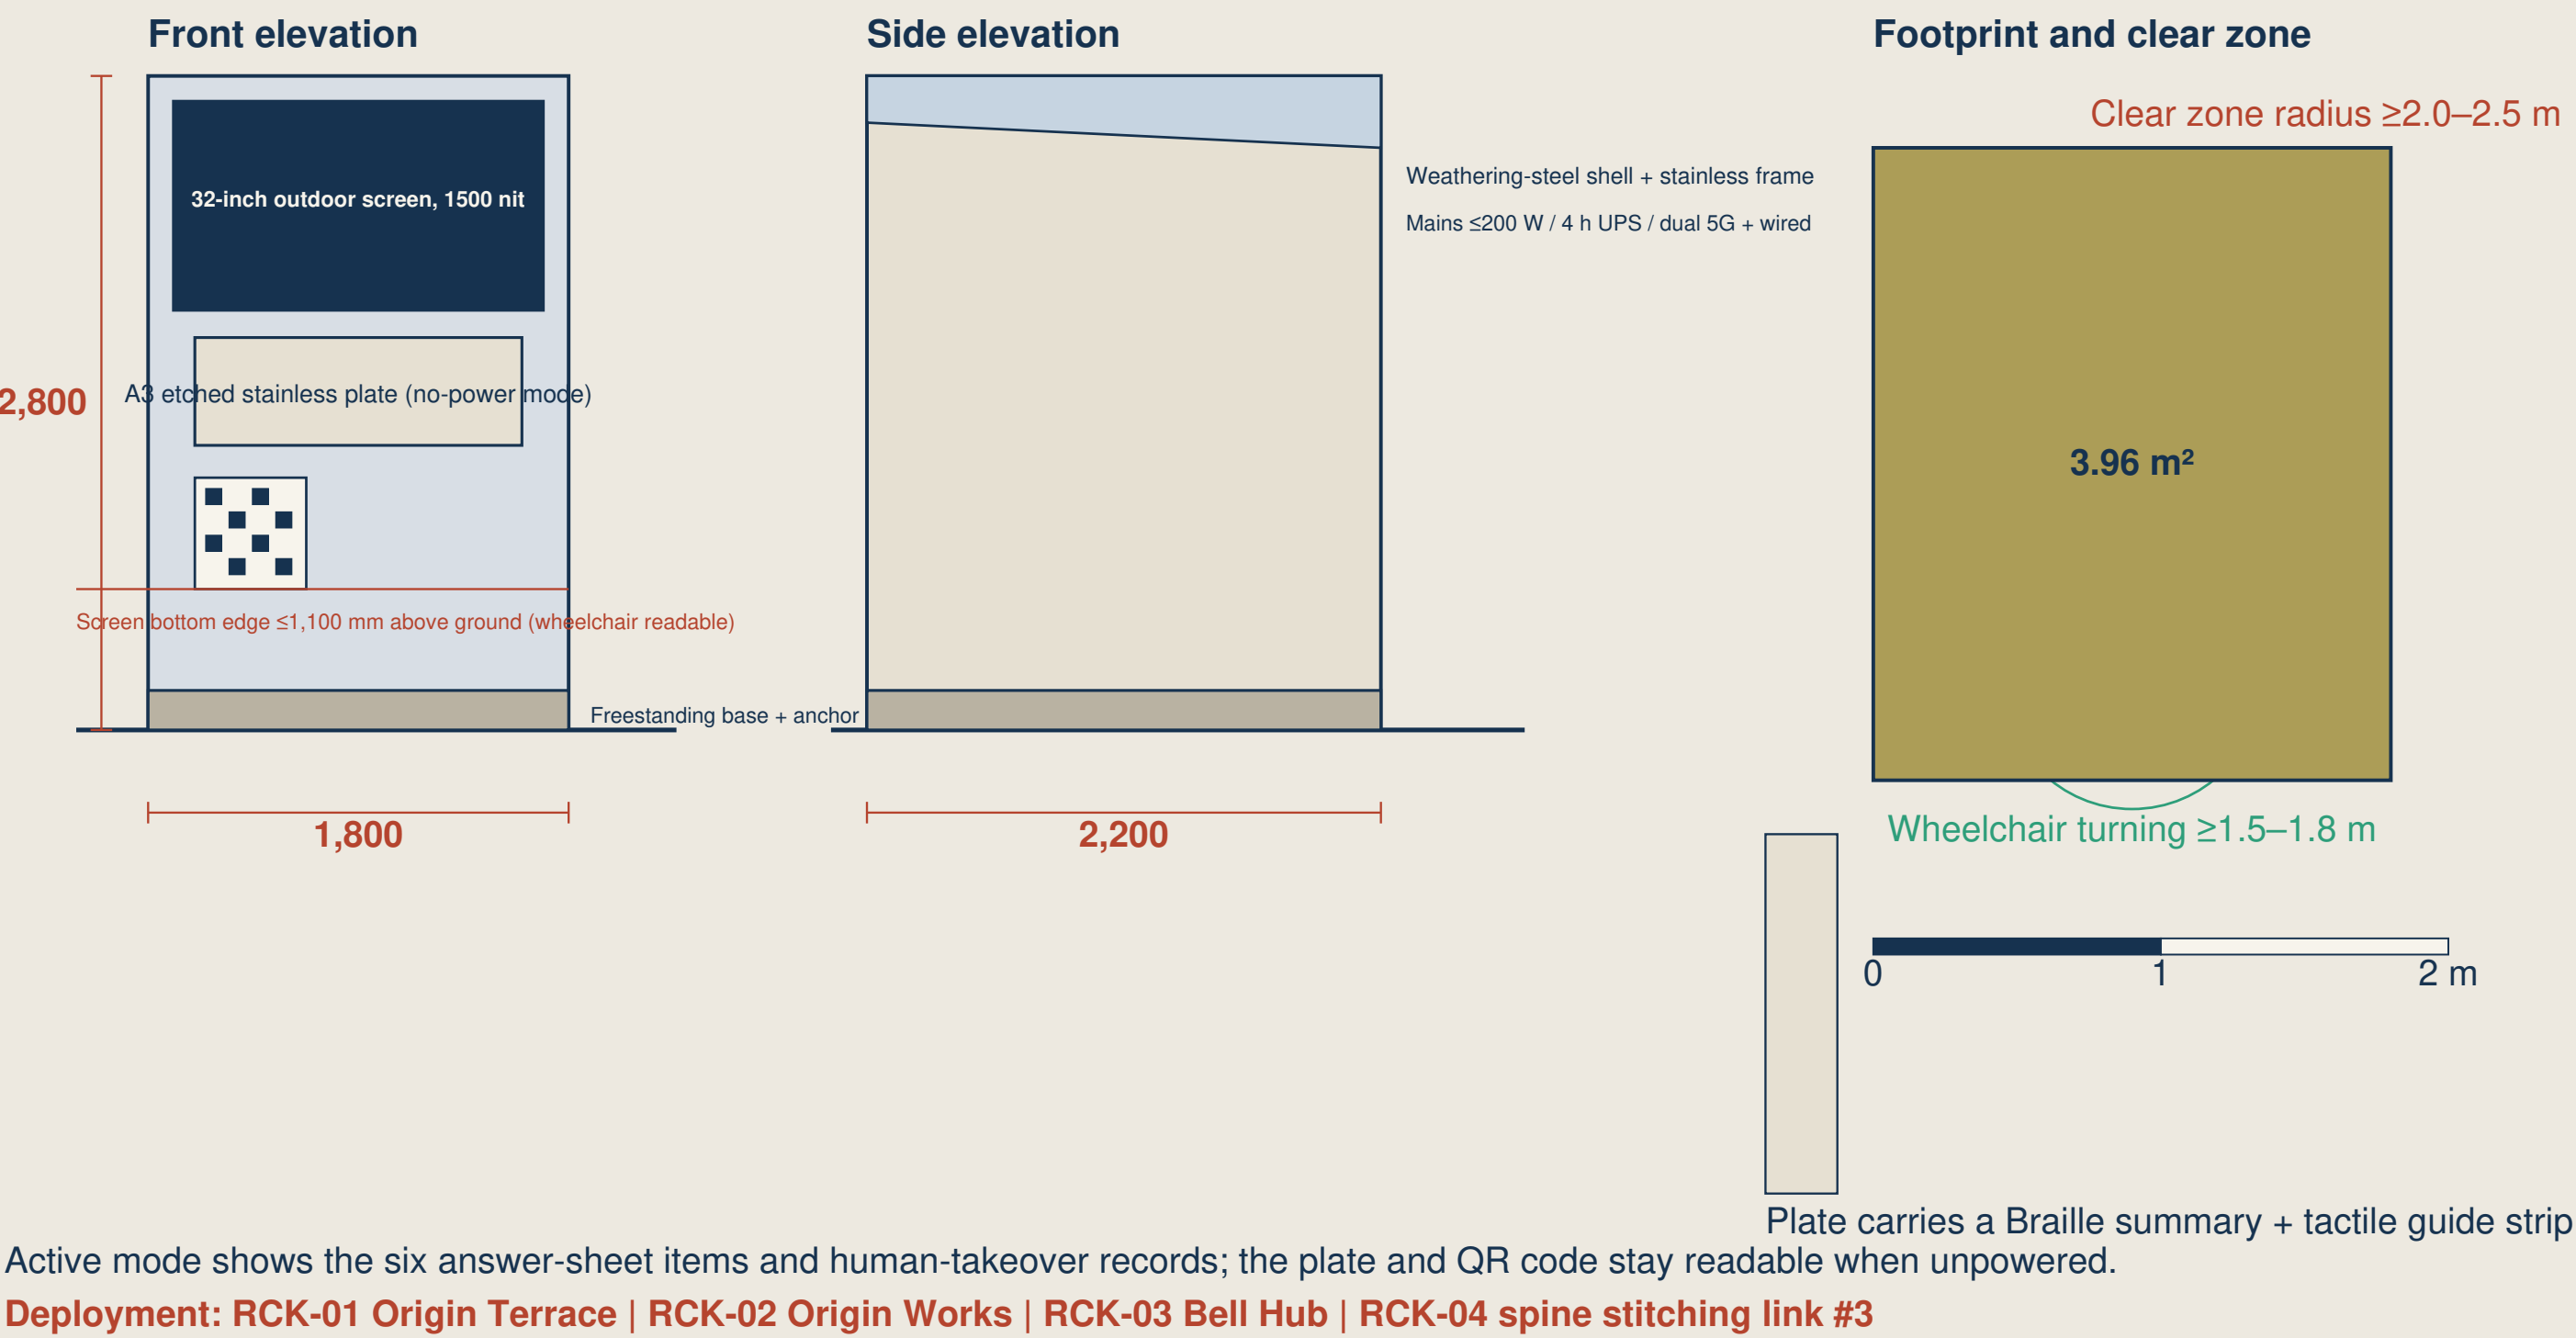


report-card-kiosk

Figure 05: Recomputed metrics and evidence chain

- 60 metrics: 57 known metrics recomputed deterministically; 3 statutory controls kept strictly 'unknown'.
- Report Card Kiosks (RCK): footprint 3.96 m², 1,800 × 2,200 × 2,800 mm, dual-mode operation with a physical fallback.
- Gate validation: all 4 verification gates and 30 universal property invariants 100% passed.
- Traffic-light governance: green for full access, yellow for 7-day rectification, red for immediate shutdown and a switch back to human service.

Metrics evidence: equal-area square diagrams of the three key areas

Each square is drawn with the side length of the key area's actual area; areas, lengths and ratios are recomputed from the geometry/ layers

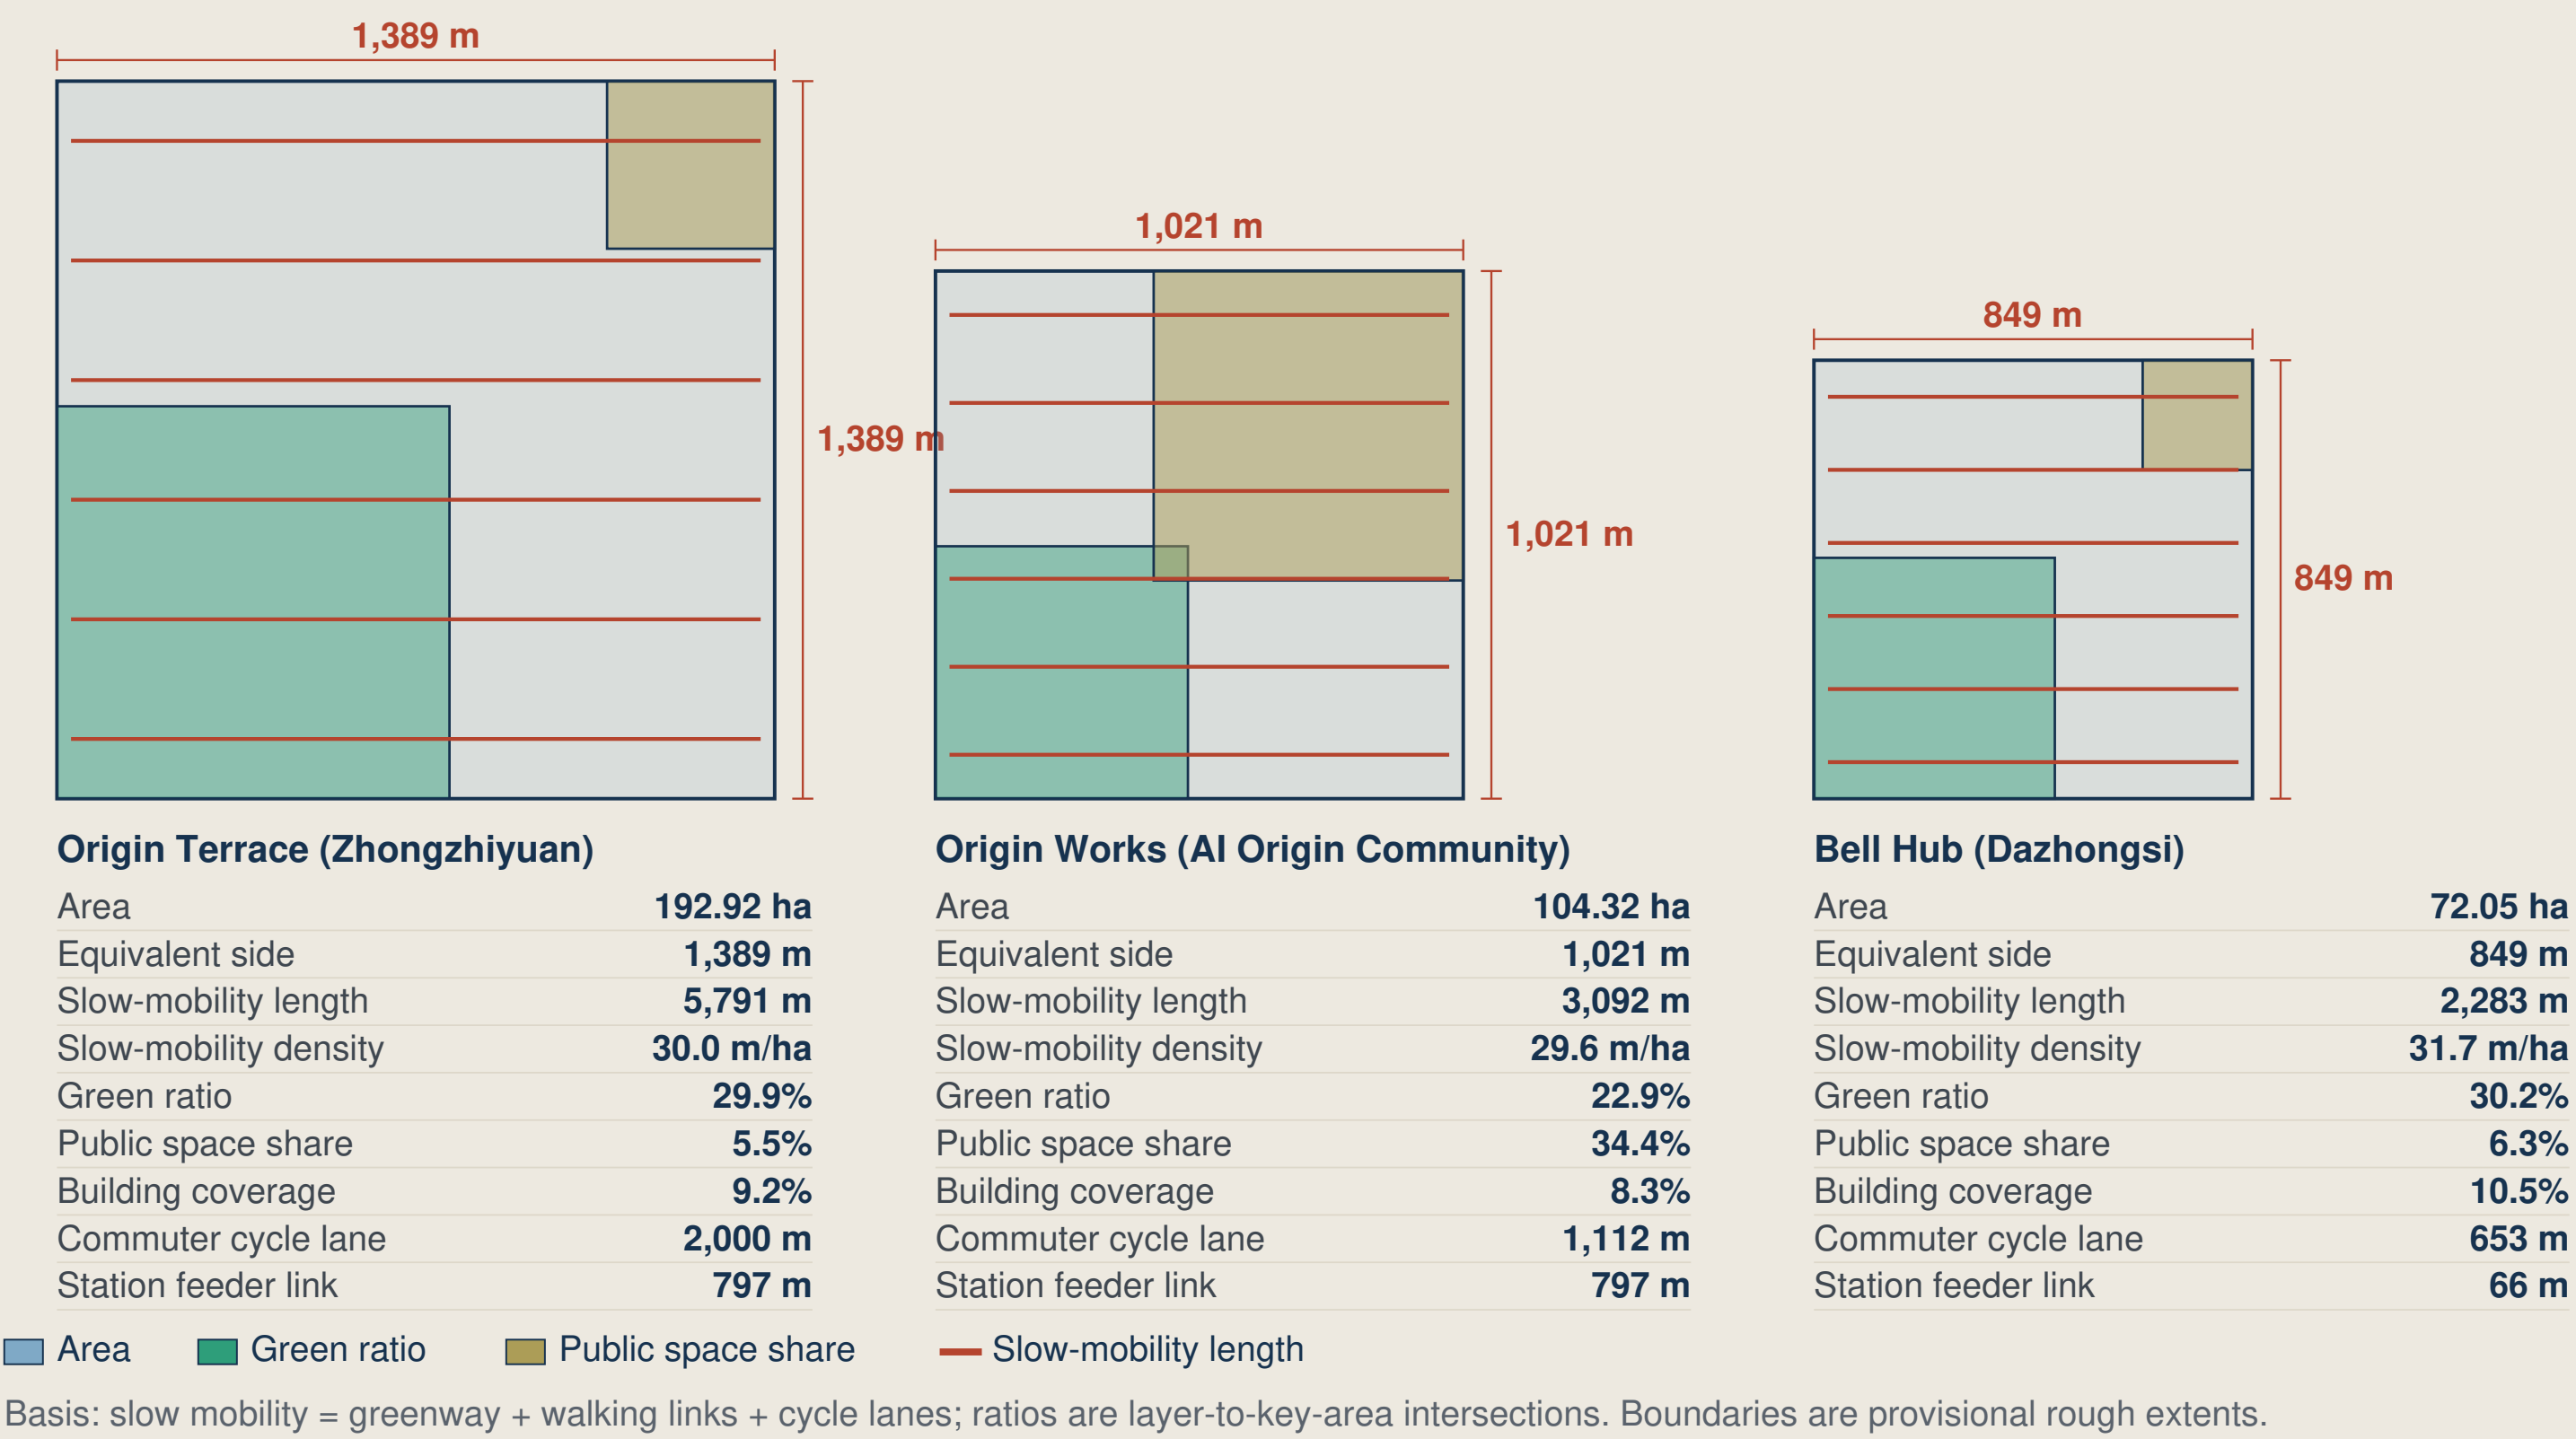

metrics-evidence

The design scope and the three key areas use the organiser's provisional rough substitute boundary: concept recommendations only, never a statutory redline, an approval basis or a precise-area basis. Once official polygons are published the geometry, metrics, drawings and HTML must all be recomputed.

Submission package: cf3901646 | Author: Charlie JIANG | Licence: COMMUNITY-DISPLAY-ONLY