


京张向上 总体空间结构与用地规划

展板 01 / 03 · 一脉三台两翼双缝 | 三层范围 | 用地结构

统筹研究范围 43.6 km² | 总体设计范围约 11.41 km² | 三处重点区 369.3 ha | 脉一台一翼一缝

总体设计范围总览平面

范围、用地、绿地与三处重点区域均由本包 geometry/ 图层投影生成；边界为组织方临时粗略范围，不作红线依据。

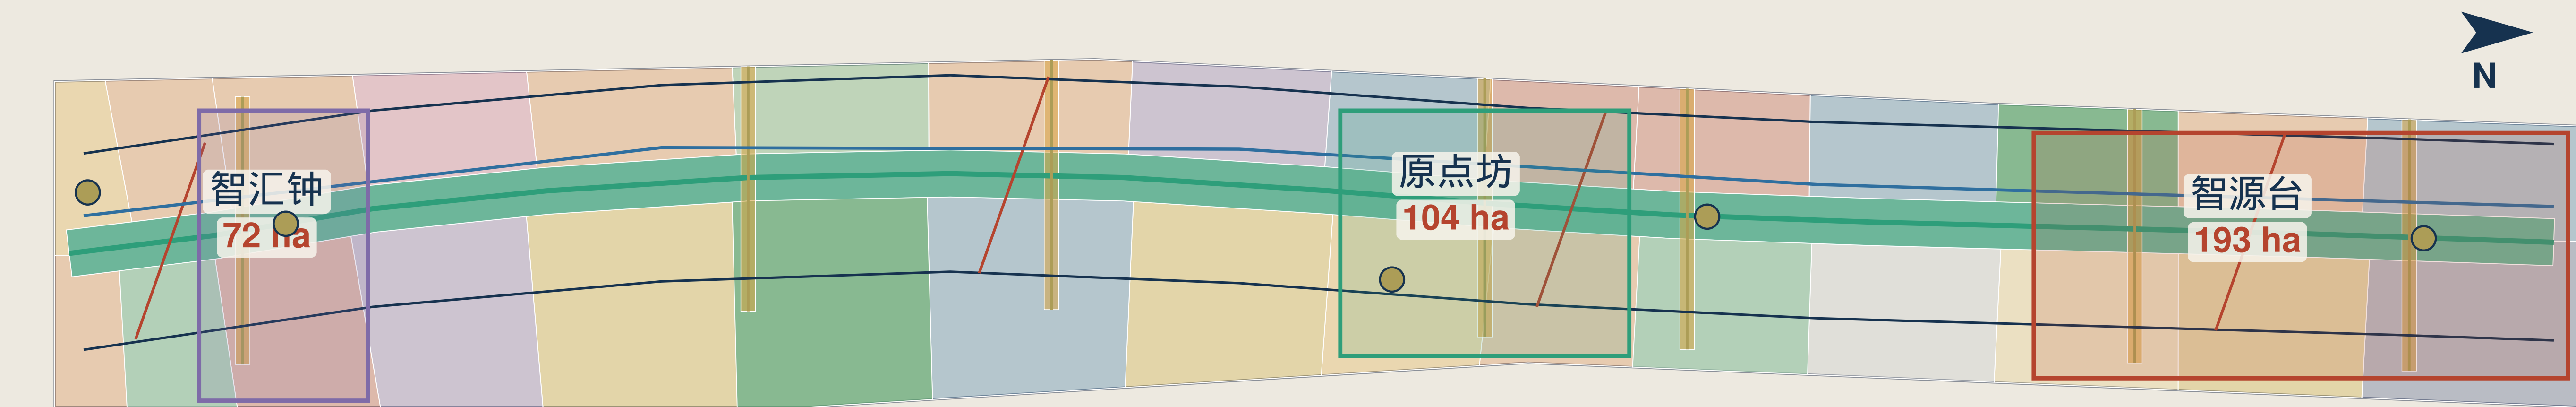

0 500 1000 1500 2000 m


□ 总体设计范围（临时粗略） ■ 重点区域 ■ 遗址公园主脉绿廊 — 主绿道（慢行主轴） — 通勤自行车道 — 东西缝合步行链 — 次干路
— 智站接驳线 ■ 朝圣地标

总体设计范围面积：约 11.41 km²（临时设计模型，随官方边界发布后重算）

site-overview

三处重点区 | 街道层级空间体验与构件落位

基于本包概念断面与空间组件生成；不是现状照片、审批效果图或工程承诺

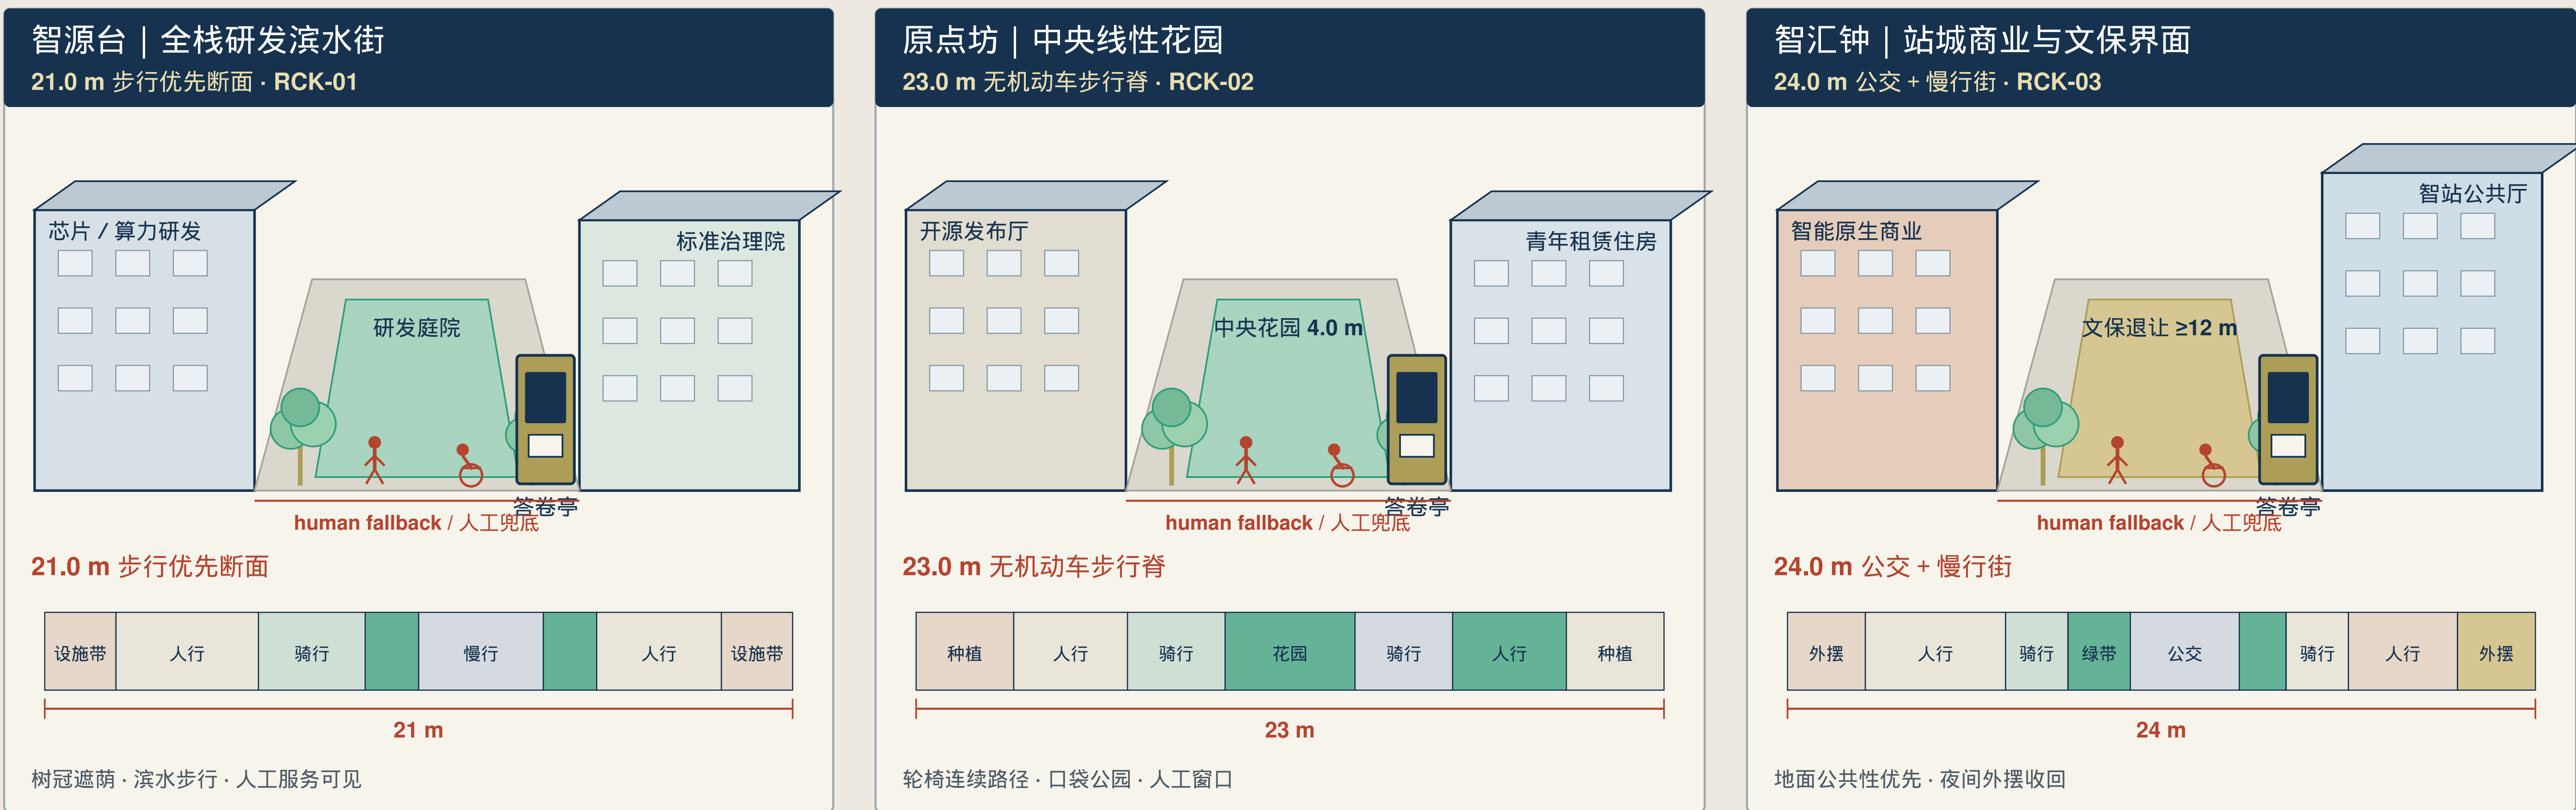


spatial-experience

图 01 总体空间结构（一脉三台两翼）

- 历史母题：詹天佑 1909 年“人”字形展线作为 background_only / 待核叙事线索，转译为当代 AI 自主创新，不作为正式历史证据。

- 四处朝圣地标：人字台（1909）、赶考门（1949）、算力之钟（1980）、原点碑（2026）。
- 两翼：中关村科技服务翼（西）+ 小月河场景创新翼（东）。

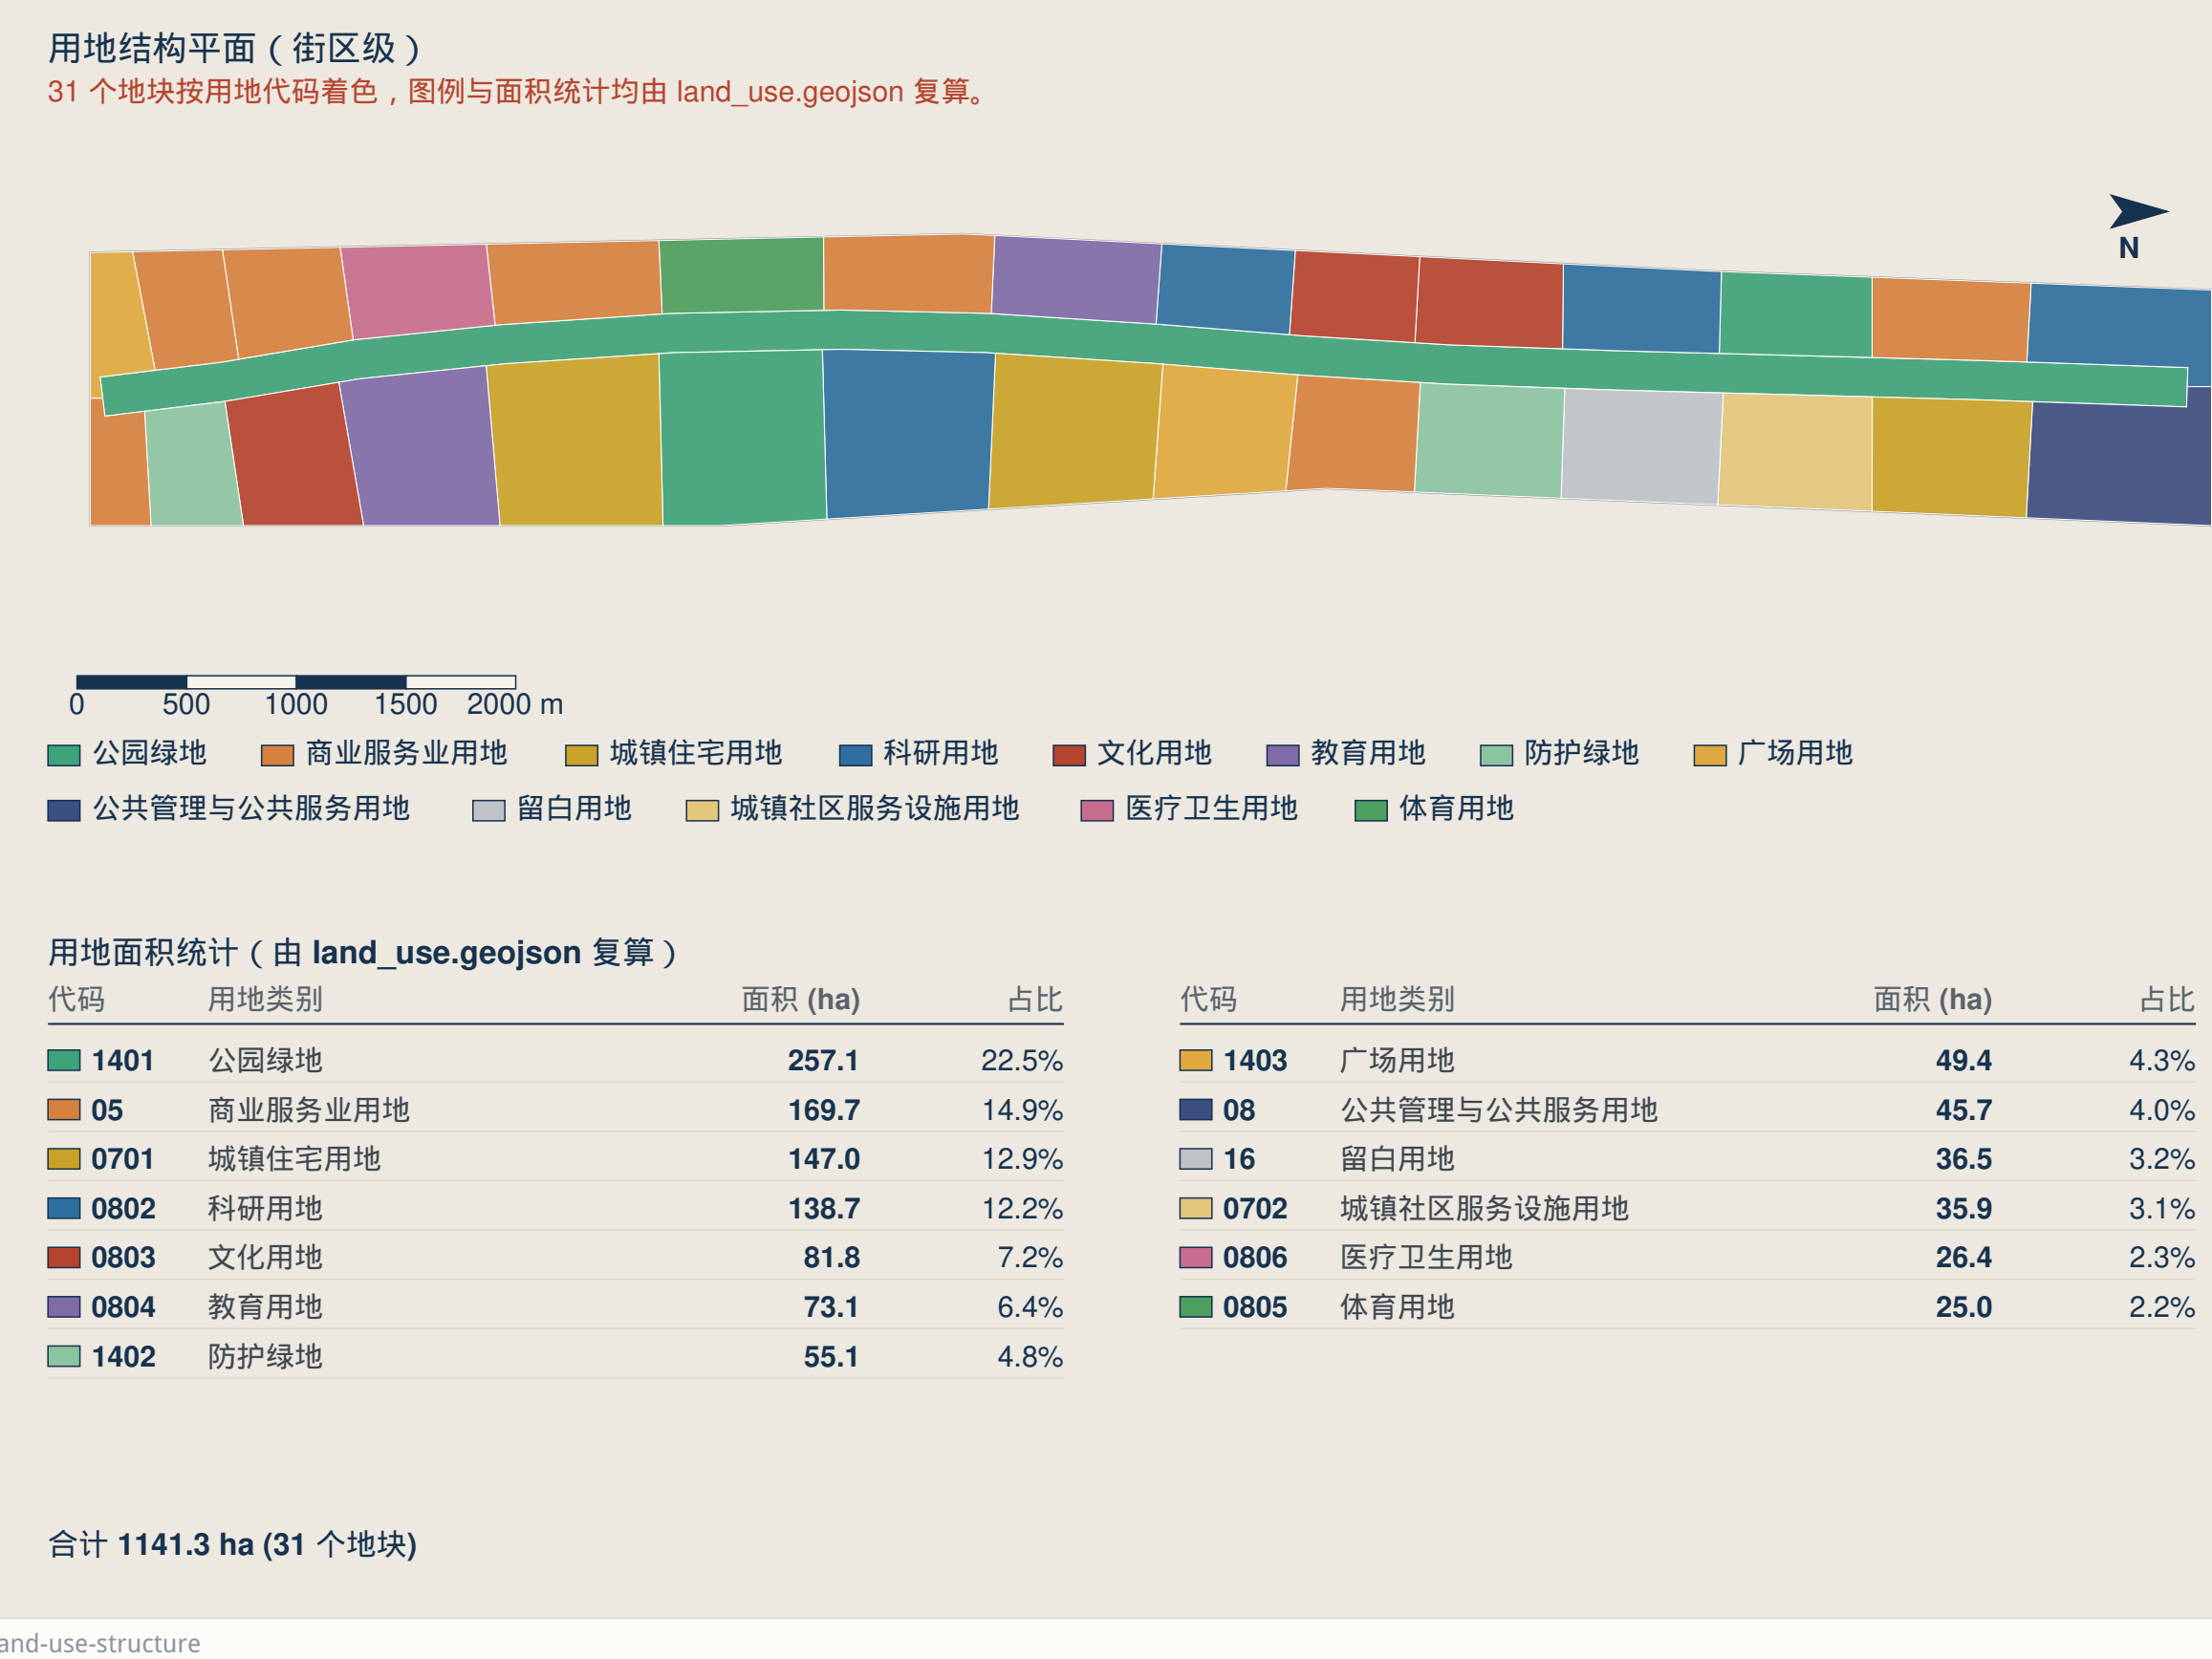

land-use-structure


图 02 用地结构与锚点服务范围划分

- 完整划分：4 处智站 TOD 与 14 个创新锚点服务范围无缝划分约 11.41 km²。
- 功能平衡：研发创新实验室、教育协同、人才住房与连续蓝绿公园。
- 严格完整性：无缝隙、无重叠；依据 geometry 图层在 EPSG:4548 下复算。
- 31 个地块合计 1,141.3 ha，与 metrics.json 的 site_area_sqm 同源。

范围与三处重点区均采用组织方发布的临时粗略替代边界（provisional），仅为概念建议，不得作为正式红线、审批依据或精确面积依据；官方 polygon 发布后必须整体重算几何、指标、图纸与 HTML。

提交包：cf3901646 | 作者：Charlie JIANG | 许可：COMMUNITY-DISPLAY-ONLY

展板 02 / 03 · 智源台 193 ha | 原点坊 104 ha | 智汇钟 72 ha
15 个街区概念区间 | 容积率与限高建议 | 答卷亭布点

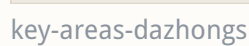


- 街区：ZZ-A 前沿实验室、ZZ-B 孵化、ZZ-C 人才住房、ZZ-D 服务、ZZ-E 绿地。
- 概念建议：容积率 1.6-3.5，限高 24-60 m，覆盖率 $\leq 35\%$ 。
- 公共锚点：人字台纪念 + 清河智站 TOD + RCK-01 答卷亭。
- 慢行：密度 30.0 m/ha，长度 5,791 m。

骑行网络、步行优先、绿廊与滨水四层叠加在同一底图上，各层图例分列于下。




mobility-bluegreen

里程与密度为 geometry/ 图层复算值；断面与配时为概念建议

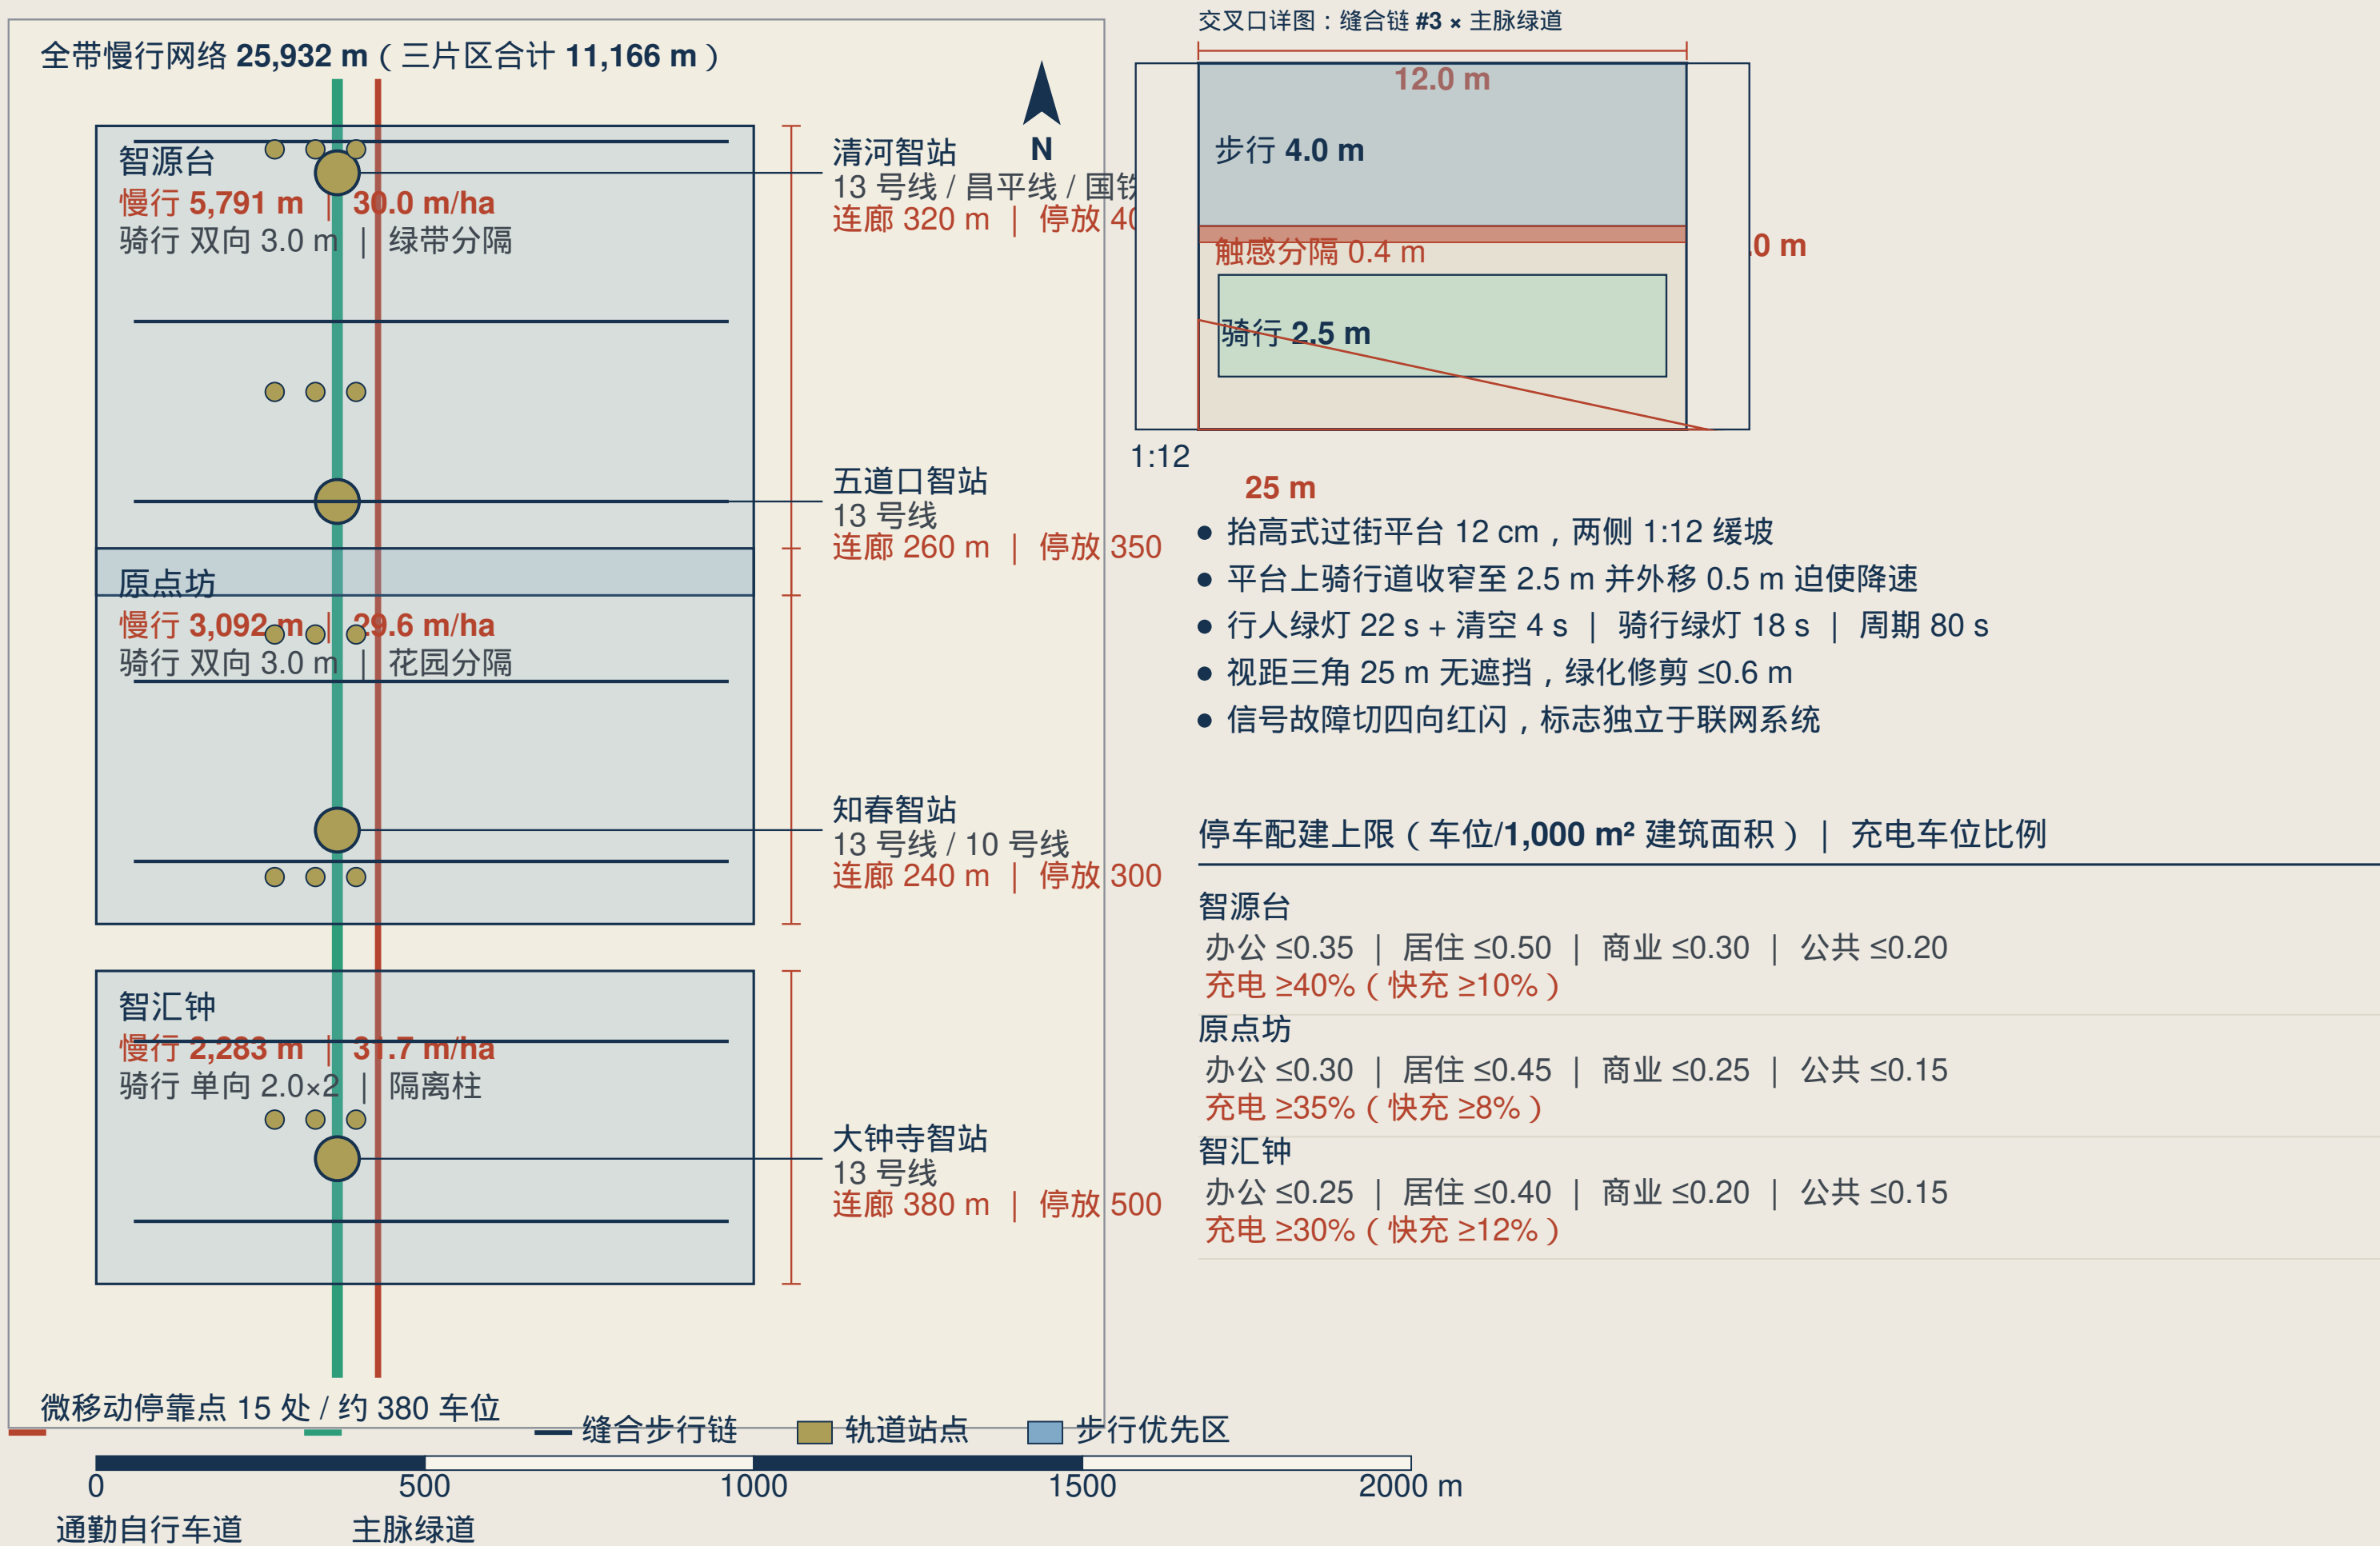


mobility-strategy

外轮廓 1,800 × 2,200 × 2,800 mm | 占地 3.96 m² | 独立基座、可拆移

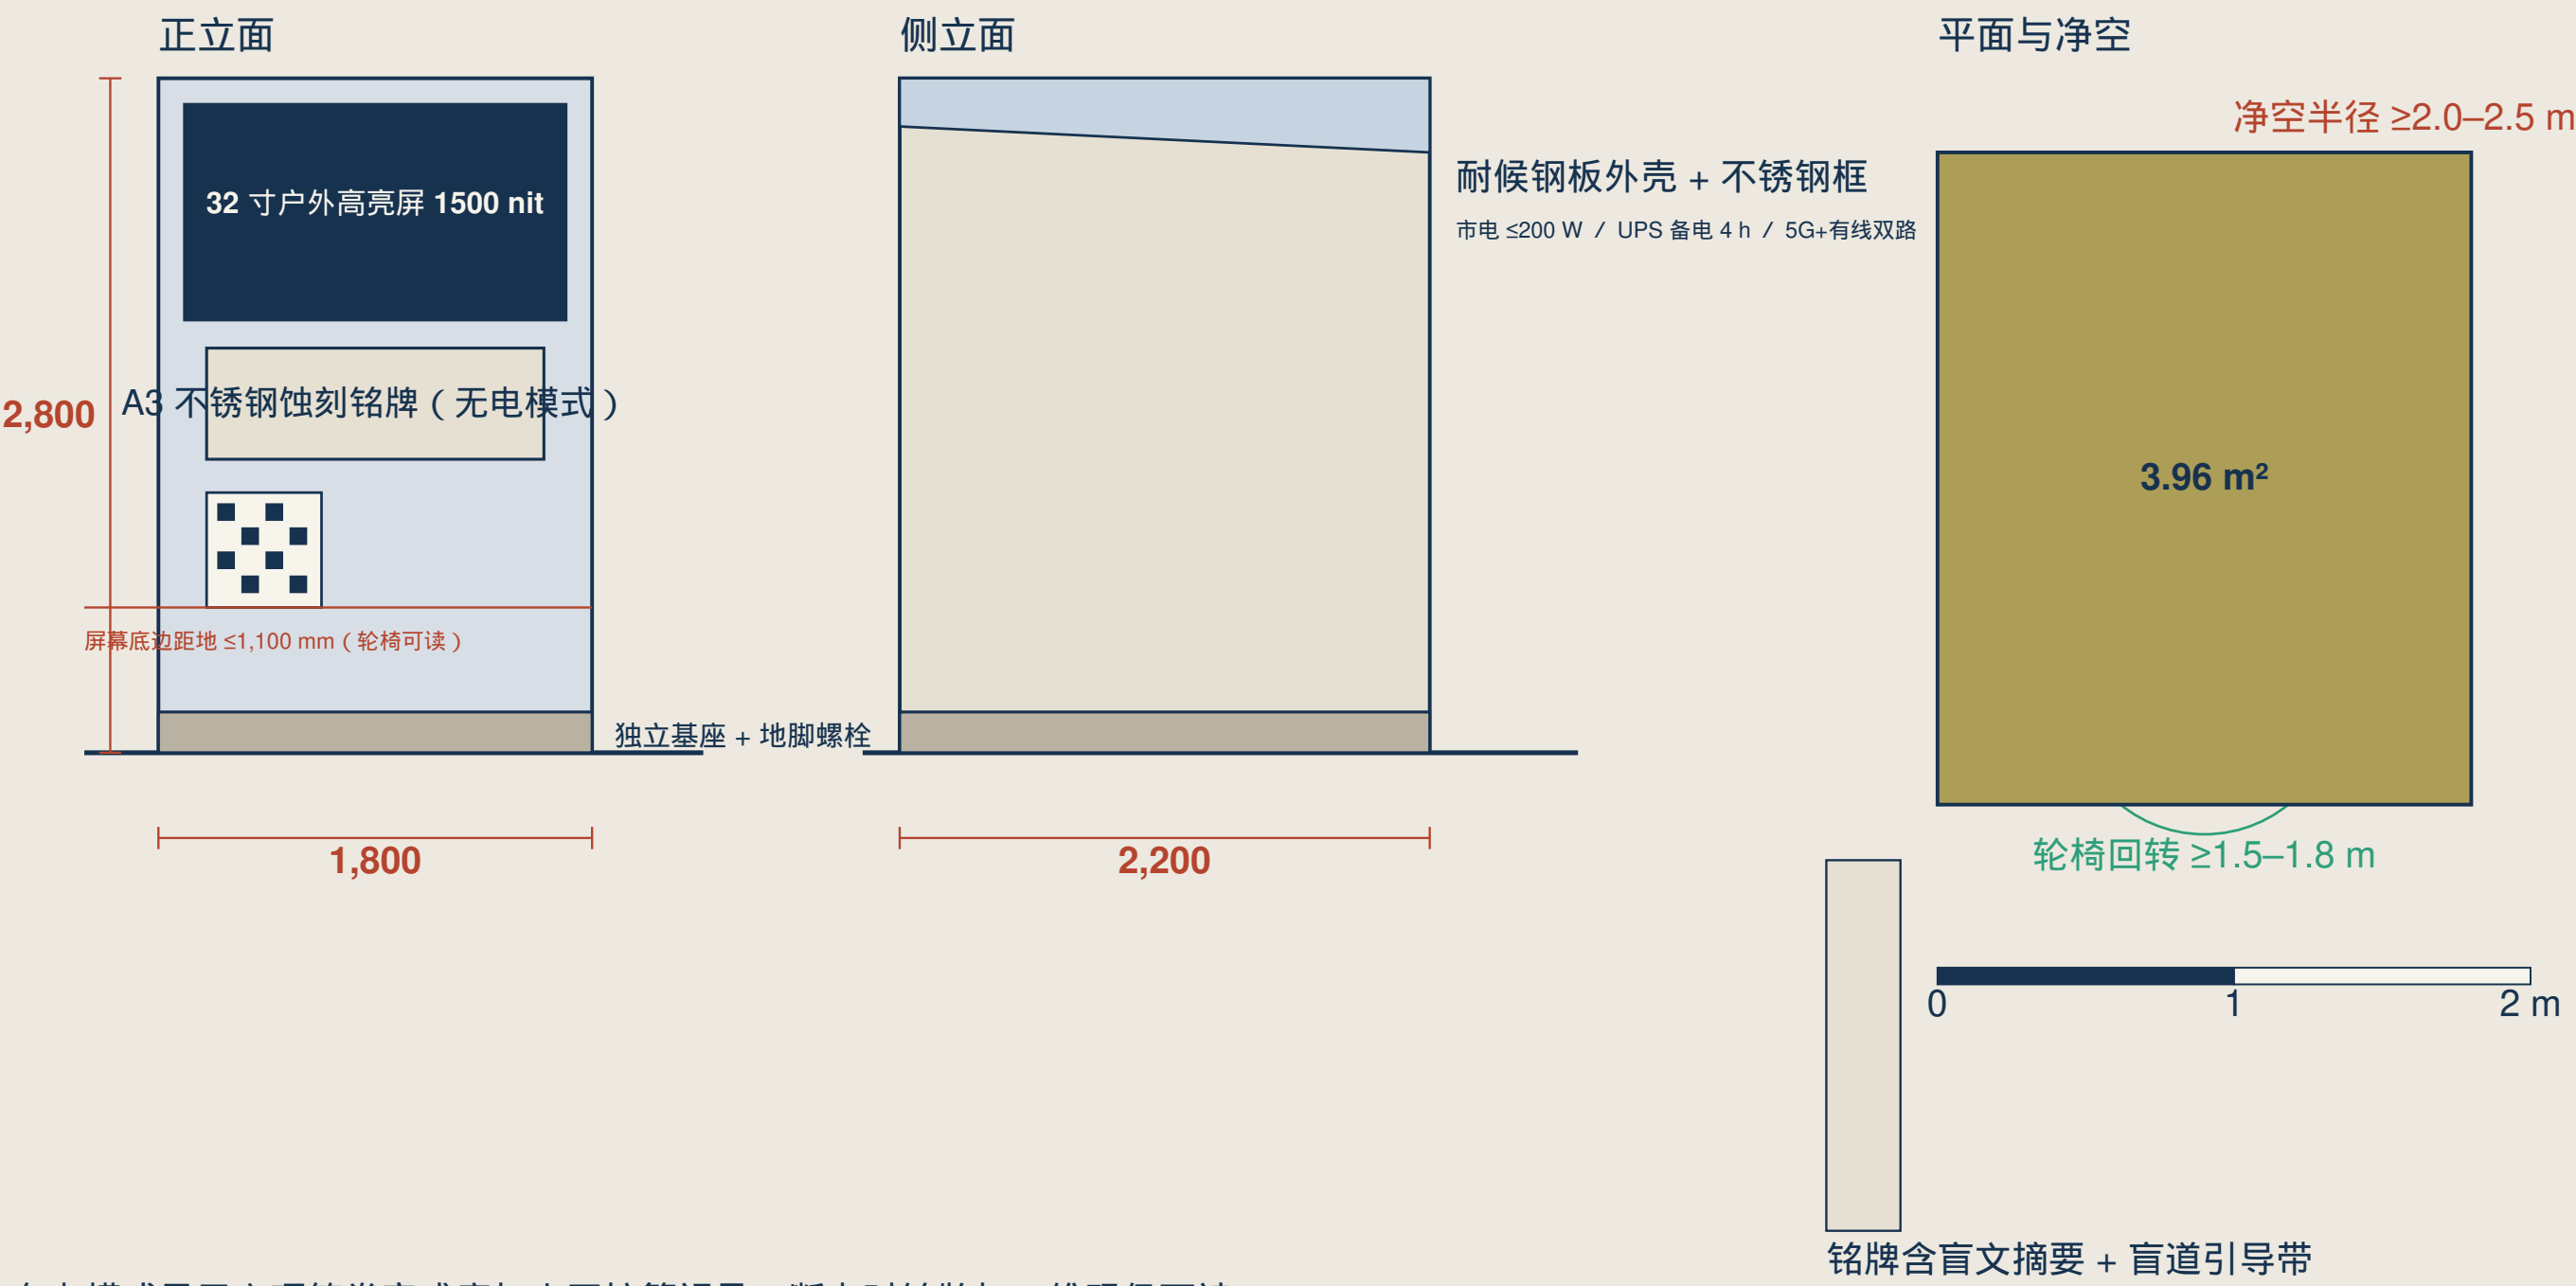

report-card-kiosk

每个方形的边长按片区实际面积开方绘制，面积、慢行里程与比率均由本包 geometry/ 图层复算

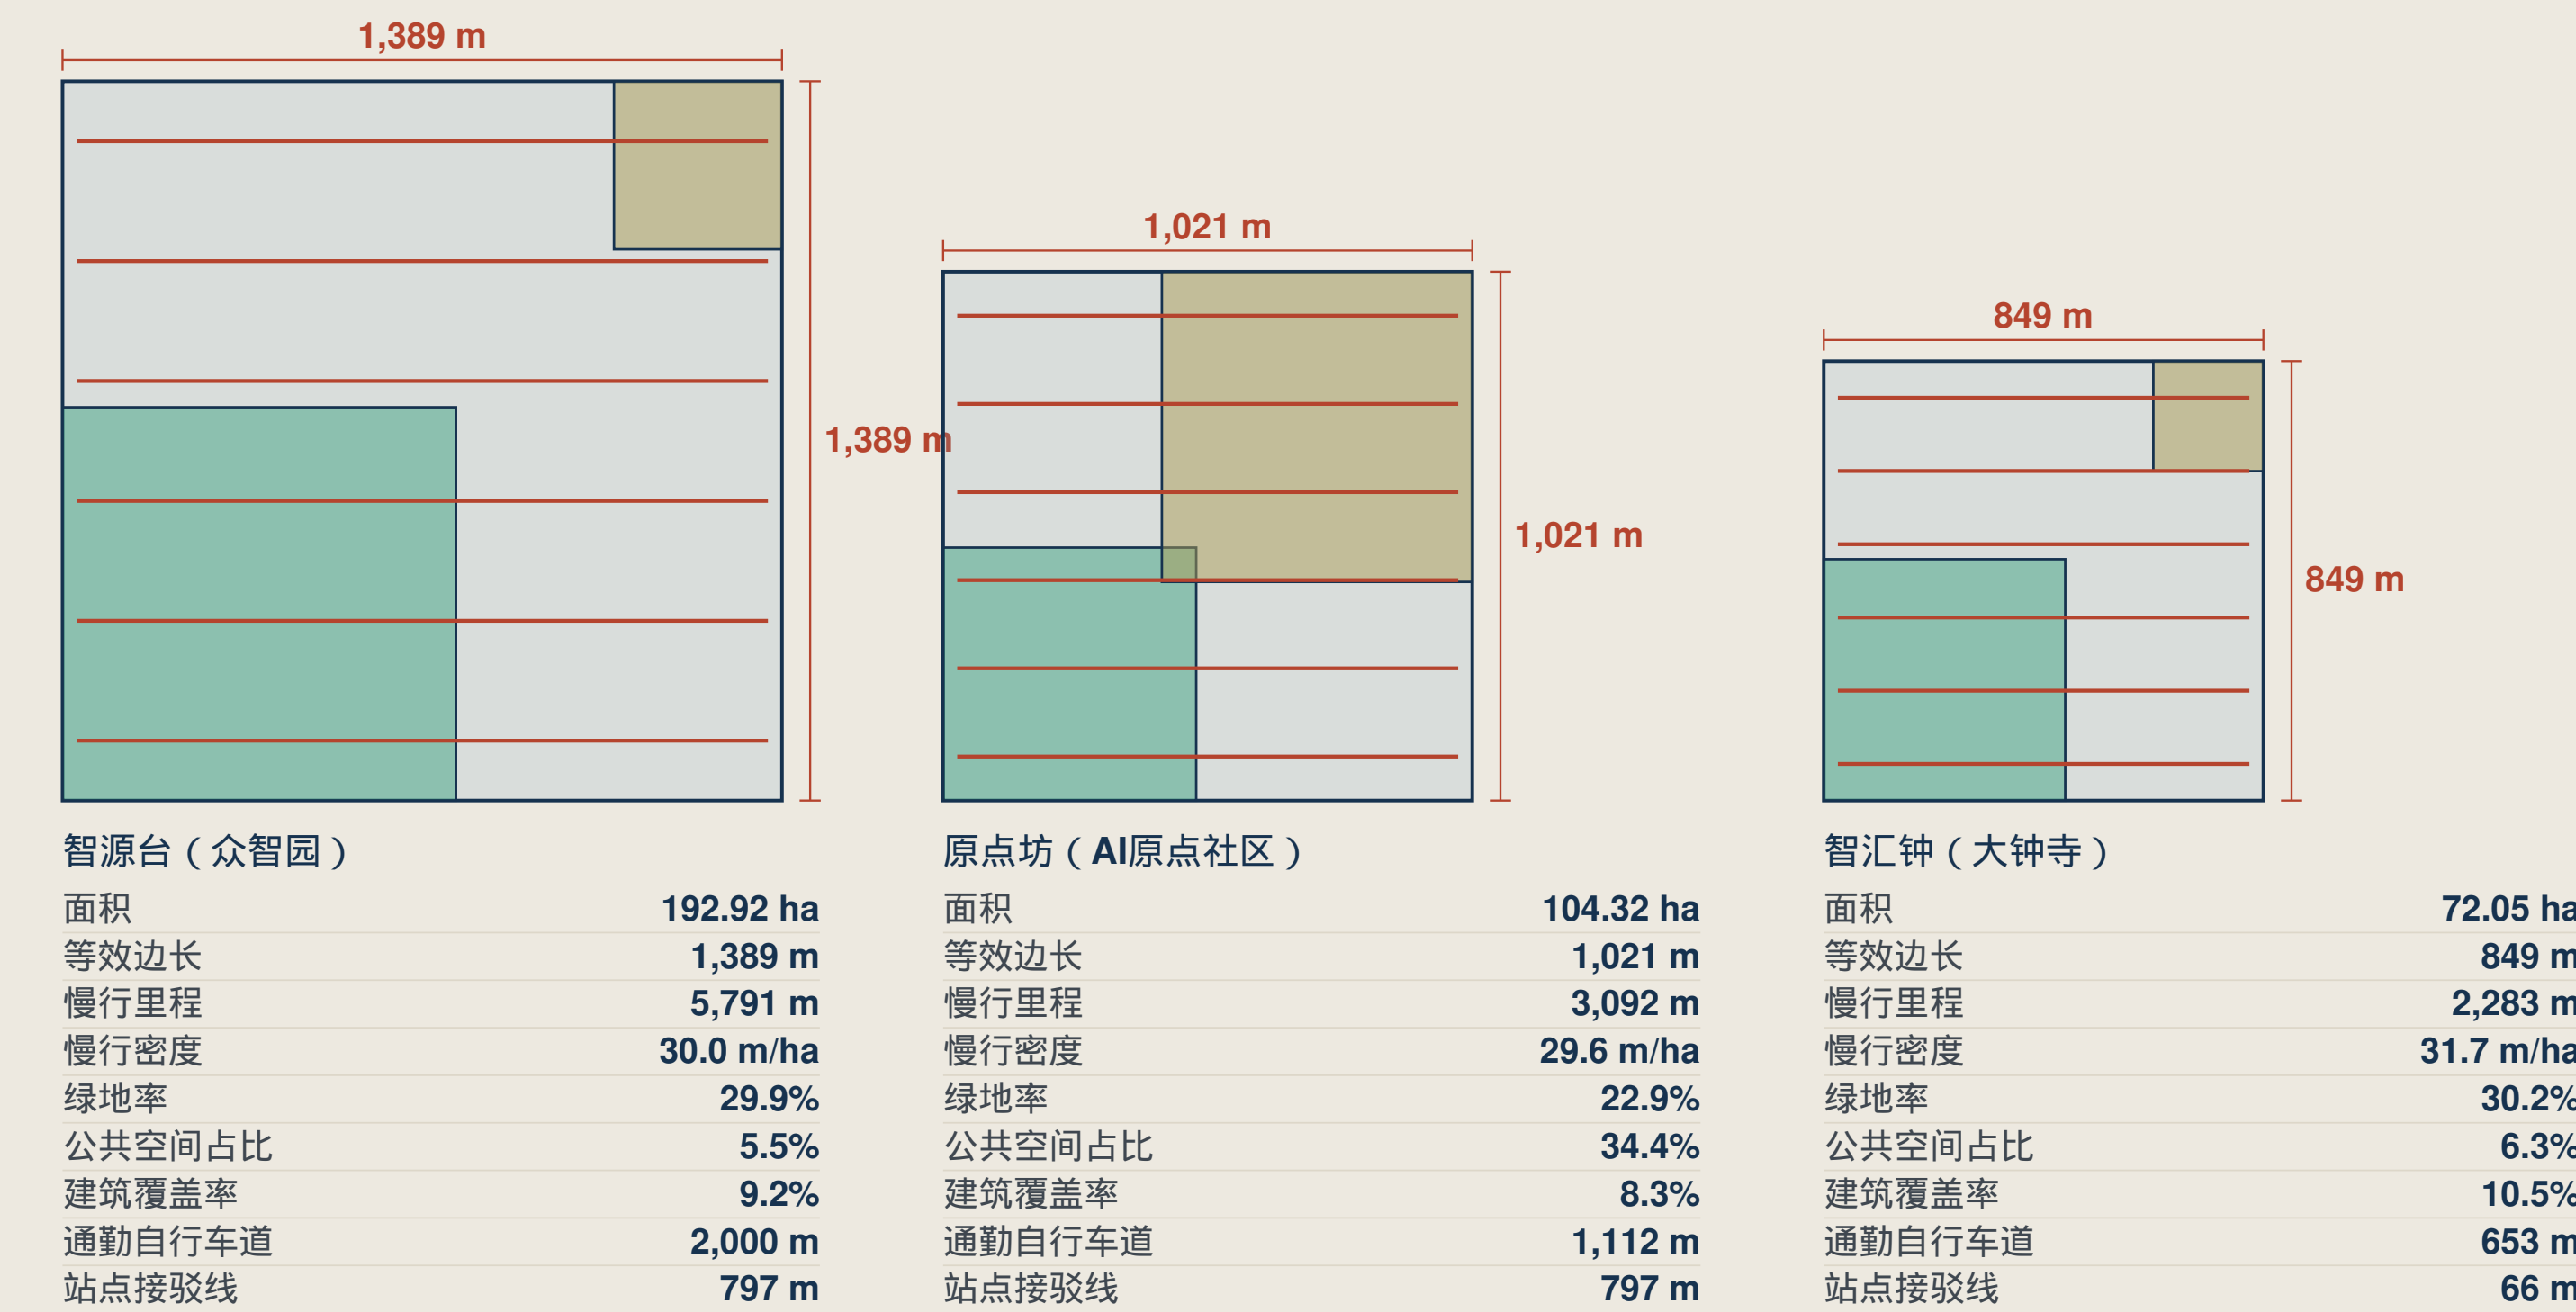

口径：慢行 = 绿道 + 步行链 + 自行车道；比率 = 对应图层与片区边界求交后的面积比。边界为临时粗略范围。

[metrics-evidence](#)

- 南北主脉：9.0 km 连续绿道 + 通勤自行车专用道。

- 南北主脉：9.0 km 连续绿道 + 通勤自行车专用道。
- 东西缝合：7 条步行缝合走廊，跨越既有铁路割裂。
- 站城衔接：4 处智站，500 m 风雨连廊，50 m 内自行车停车枢纽，充电车位 $\geq 40\%$ 。
- 交叉口与停车：抬升过街平台 12 cm、1:12 坡道、分片区停车供给上限。

- 60 项指标：57 项 known 指标确定性复算；3 项法定管控严格保持 unknown。

- 60 项指标：57 项 known 指标确定性复算；3 项法定管控严格保持 unknown。
- 答卷亭（RCK）：占地 3.96 m²，1,800 × 2,200 × 2,800 mm，有电/无电双模式，具备实体兜底。
- 门禁校验：4 道确定性门禁与 30 项通用性质不变量 100% 通过。
- 三色治理：绿色全量放行、黄色 7 日整改、红色立即停用并切入人工服务。

提交包：cf3901646 | 作者：Charlie JIANG | 许可：COMMUNITY-DISPLAY-ONLY