

京张向上

百年京张 AI 创新带城市设计 · 百年自主，人字向上

A3 设计图册 · A3 Design Booklet

百年京张 AI 创新带城市设计公开征集

提交包：cf3901646 | 作者：Charlie JIANG | 许可：COMMUNITY-DISPLAY-ONLY

- 核心判断：全部空间指标在 EPSG:4548 下由本包 geometry/ 图层复算得到。
- 边界性质：临时粗略替代边界，仅为概念建议，不构成法定管控。
- AI 公共治理：人工兜底通道 + 公开答卷，二者缺一不可。
- 授权状态：施工、传感、AI 试点、自动驾驶及资产再利用均为 NOT_AUTHORIZED。

范围与三处重点区均采用组织方发布的临时粗略替代边界（provisional），仅为概念建议，不得作为正式红线、审批依据或精确面积依据；官方 polygon 发布后必须整体重算几何、指标、图纸与 HTML。

百年京张 AI 创新带城市设计 | 提交包：cf3901646 | 临时粗略边界（provisional）

1. 正式命题：空间回路 + 公共 AI 准入

正式依据为组织方公告与面向智能体任务书：用作者自创的“人”字折角组织一脉三台两翼双缝，用“人工兜底 + 公开答卷”决定公共 AI 是否获准进入空间，用“时间公地”记录贡献、失败与修正。

品牌成立不依赖 1909、1949、中关村沿革或区域协同等待核历史线索。即使全部删除这些 background_only 内容，名称、空间结构、治理制度与G0—G5 证据门仍完整成立。

2. 核心结构：一脉、三台、两翼、七缝

- 一条主脉：9.0 km 连续的京张遗址公园主脉绿道，并行通勤自行车专用道。
- 三台：智源台（众智园，AI 加速）、原点坊（孵化与开源）、智汇钟（大钟寺，绿色算力集群）。
- 两翼：中关村科技服务翼（西，基础研究）与小月河场景翼（东，全域测试）。
- 七条缝合链：7 条东西向步行缝合链，弥合铁路割裂，重新连接高校校园。

3. 治理约定

- 任何 AI 公共服务上线前须完成算法备案、场景白名单与人工兜底演练。
- 答卷亭以实体方式公开 F1–F6 六项状态，断电亦可读。

百年京张 AI 创新带城市设计 | 提交包：cf3901646 | 临时粗略边界（provisional）

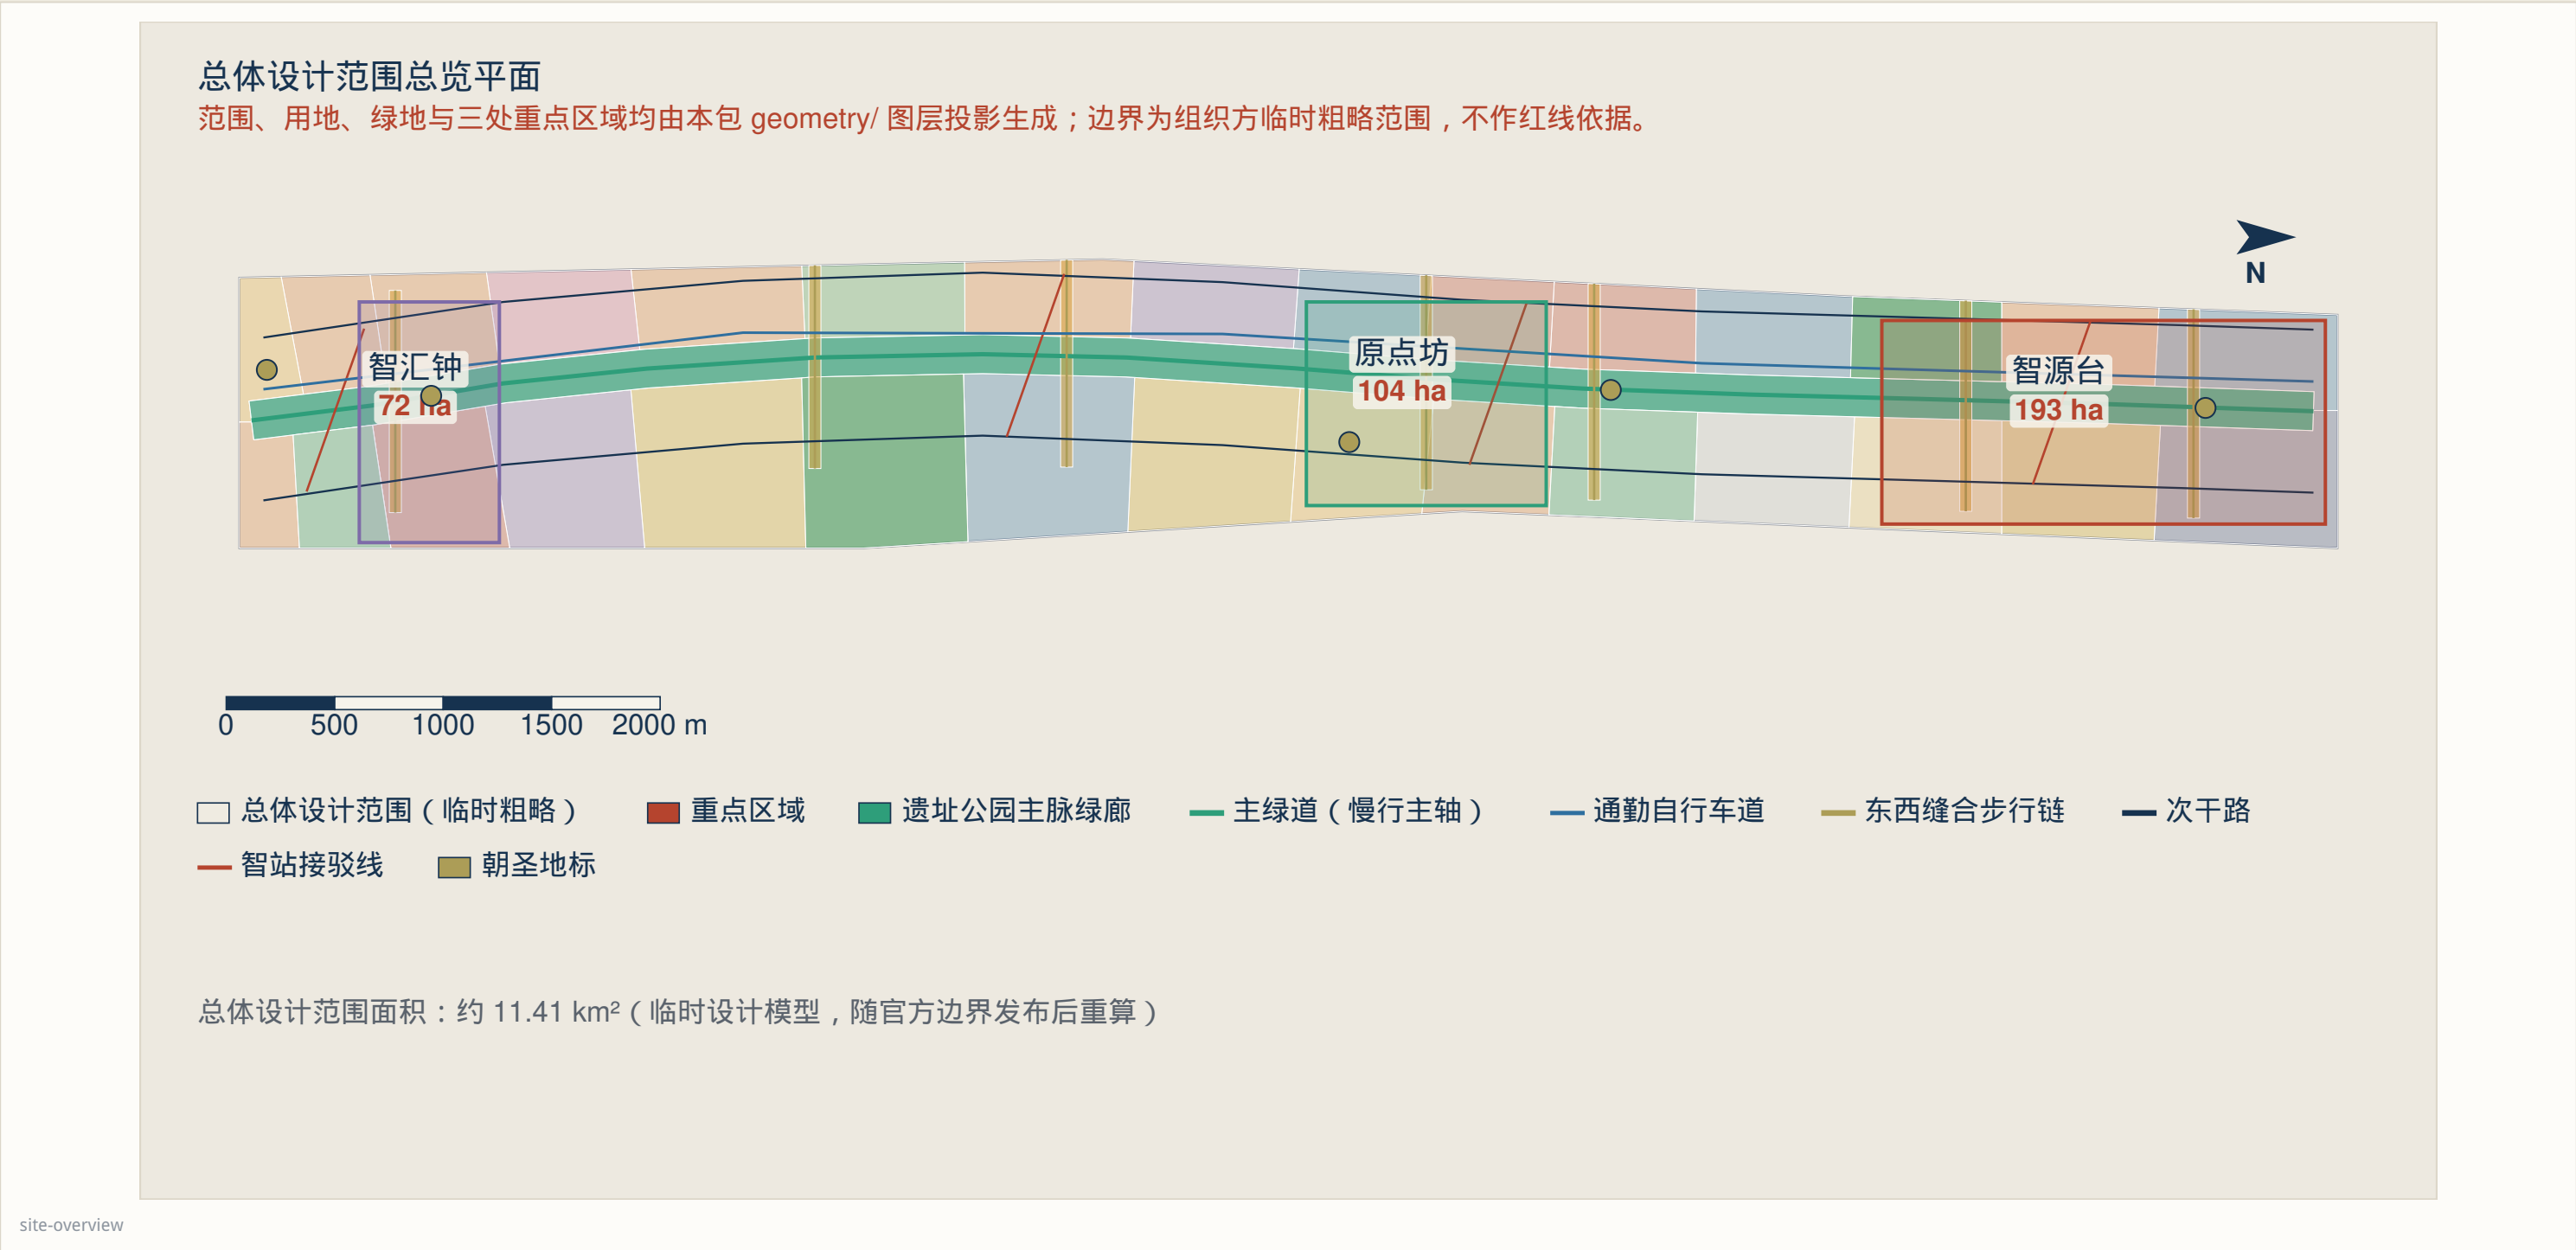



图 01 总体结构与地标

总体设计范围沿历史铁路走廊展开，面积约 11.41 km²（临时设计模型）。

关键要素


- 四处朝圣地标：
 - 人字台（1909，清河）
 - 赶考门（1949，清华园）
 - 算力之钟（1980，大钟寺）
 - 原点碑（2026，原点坊）

- 空间主脉：京张遗址公园主脉绿廊。
- 区域联动：衔接怀柔科学城、未来科学城与亦庄经开区。
面积口径以 metrics.json 的 site_area_sqm 为唯一来源，全部载体统一表述为约 11.41 km²。

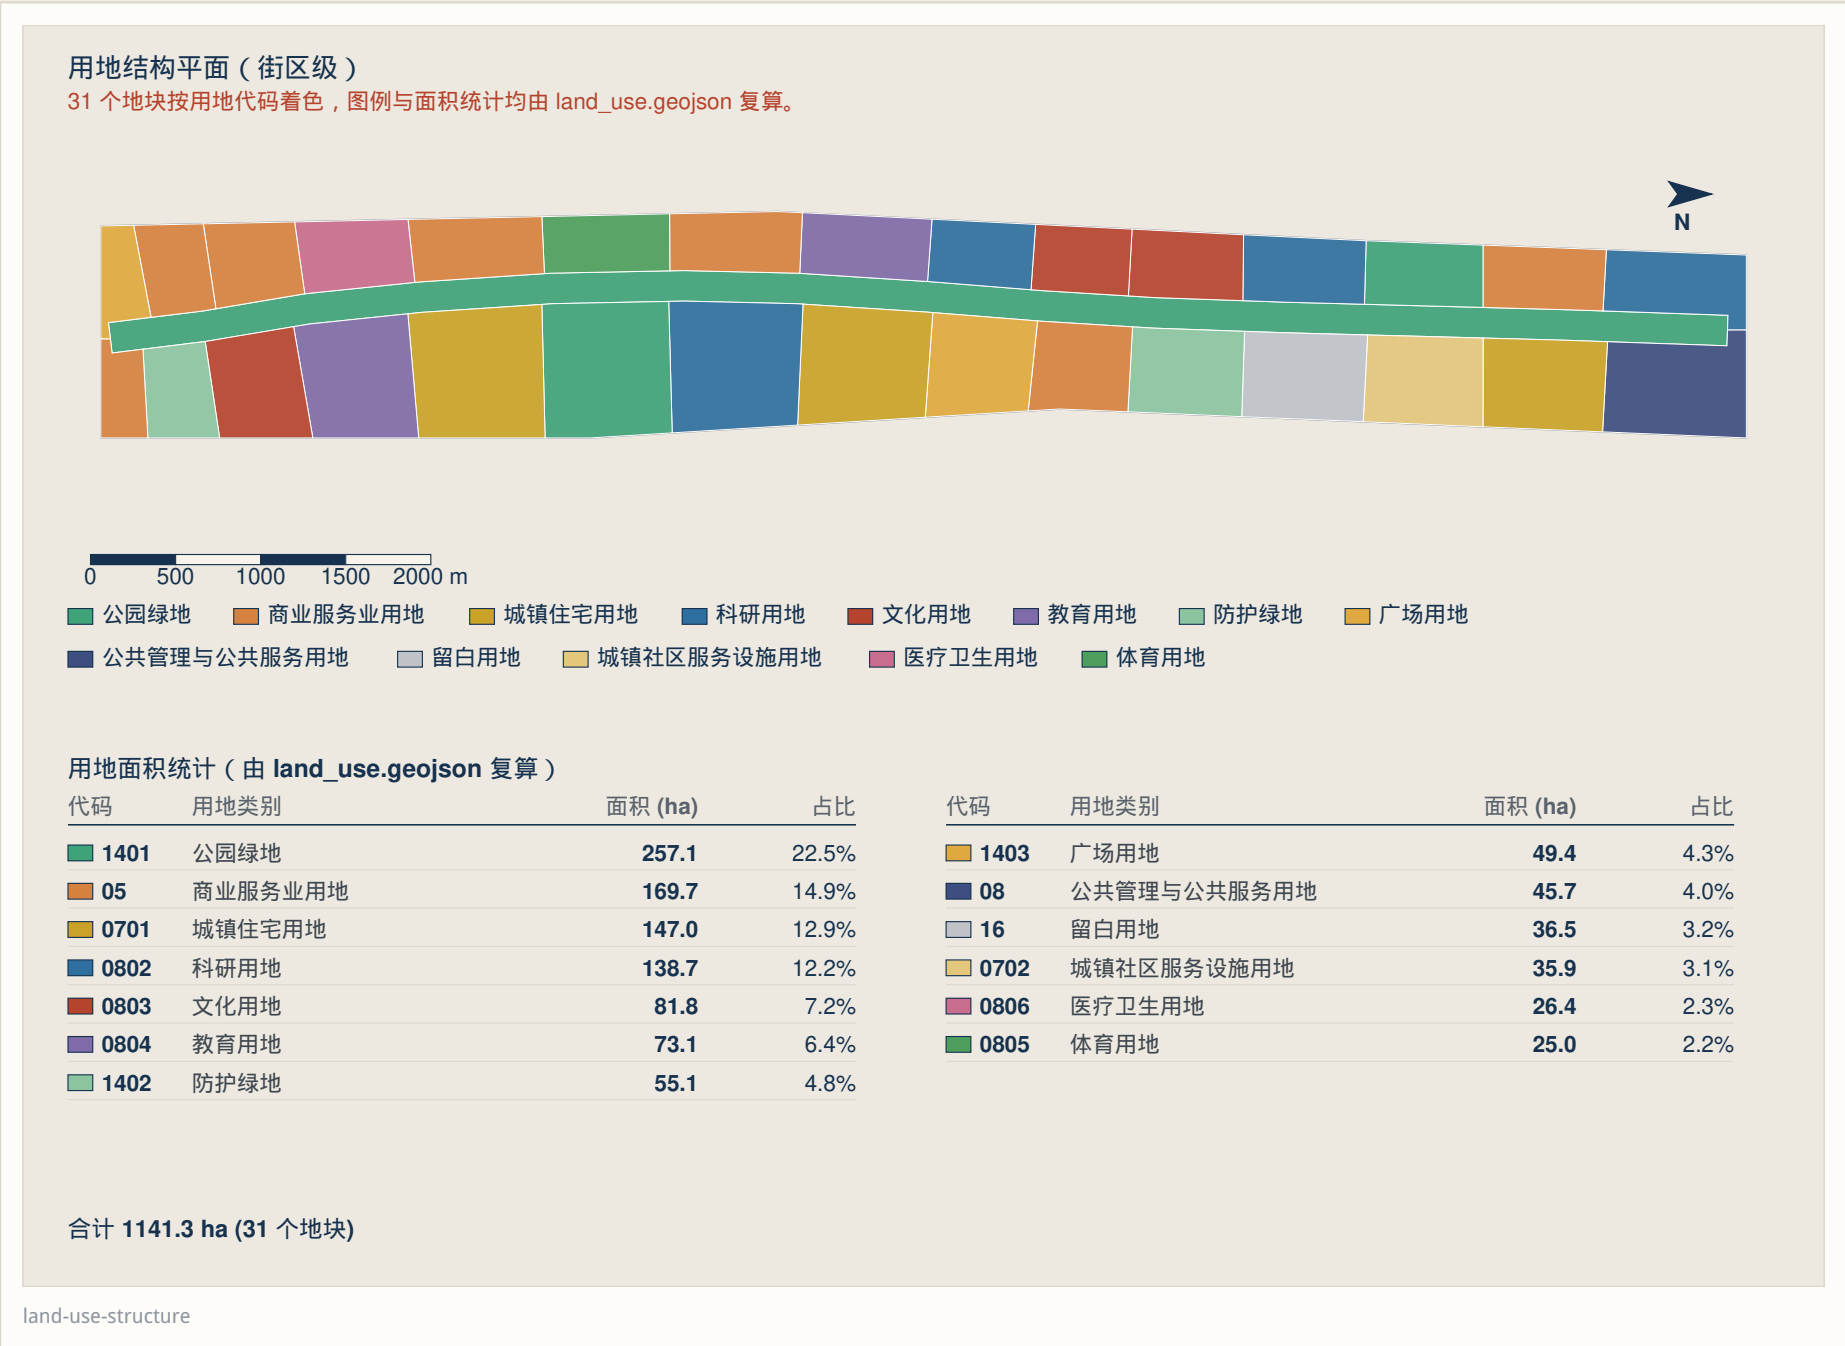


三处重点区域放大平面

街区轮廓 = 地块边界；公共空间、主要街道与答卷亭点位均落位于图上（点位示意）。
智源台 Origin Terrace

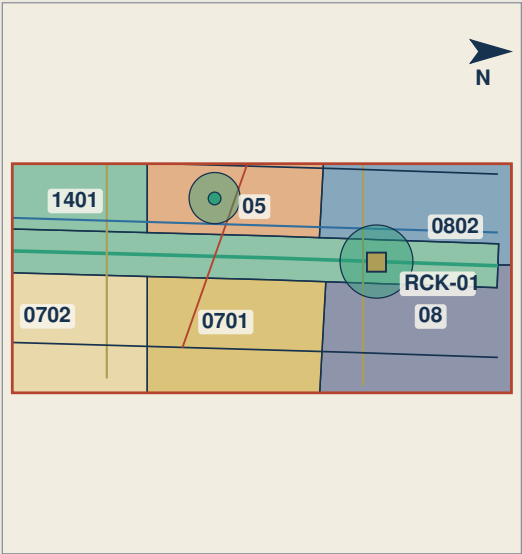


片区面积 192.92 ha
0 400 800 m

原点坊 Origin Works

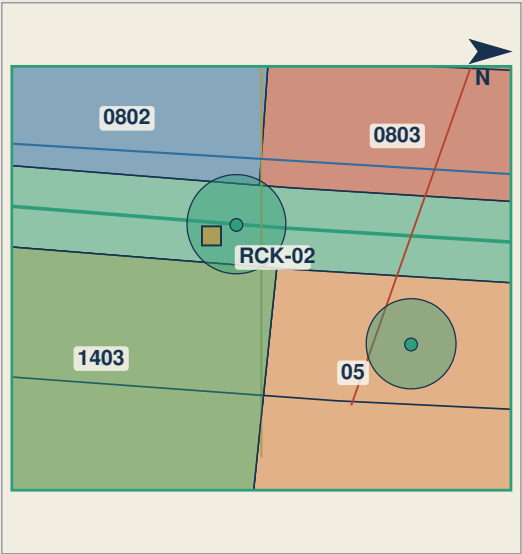

片区面积 104.32 ha
100 300

智汇钟 Bell Hub

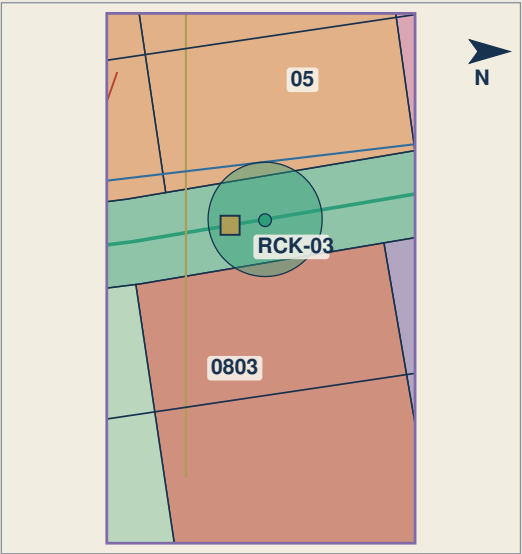

片区面积 72.05 ha
0 200 400 m


街区轮廓（地块） 公共空间节点 主要街道 答卷亭点位

街区轮廓标注为用地代码；答卷亭点位取自 proposal.md 部署计划表。


三处重点区 | 街道层级空间体验与构件落位

基于本包概念断面与空间组件生成；不是现状照片、审批效果图或工程承诺


智源台 | 全栈研发滨水街
21.0 m 步行优先断面 · RCK-01

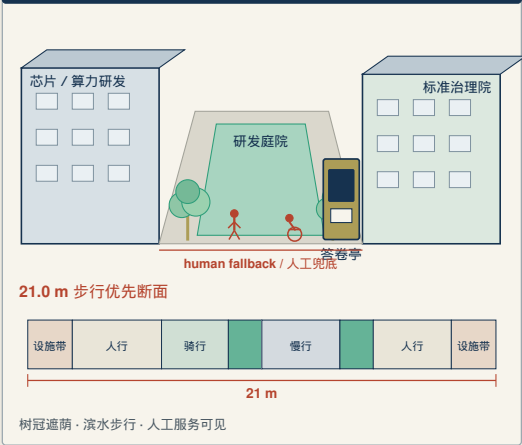

原点坊 | 中央线性花园
23.0 m 无机动车步行脊 · RCK-02

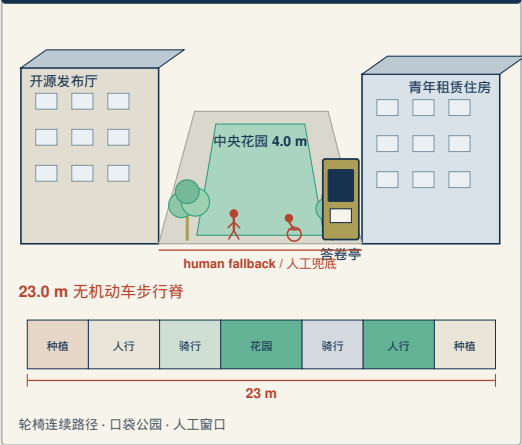

智汇钟 | 站城商业与文保界面
24.0 m 公交 + 慢行街 · RCK-03

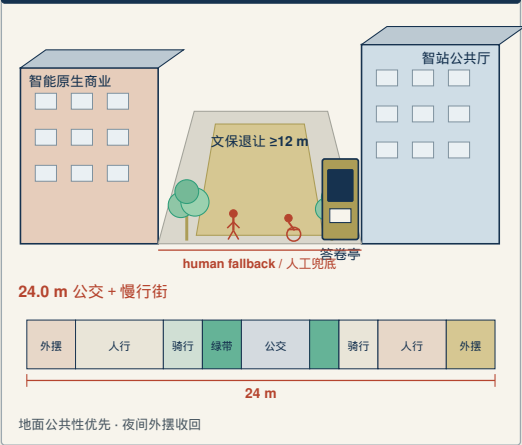

key-areas

图 03 重点区域与街区

三处重点区合计 369.3 ha，按街区尺度深化。

三台深度


- 智源台（众智园，193 ha）：ZZ-A—ZZ-E，容积率 1.6–3.5，限高 24–60 m，覆盖率 ≤ 35%。
- 原点坊（104 ha）：YD-A—YD-E，容积率 1.2–2.8，限高 18–45 m，覆盖率 ≤ 35%。
- 智汇钟（大钟寺，72 ha）：DZ-A—DZ-E，容积率 1.8–3.6，限高 24–60 m，覆盖率 ≤ 35%。
- 答卷亭布点：RCK-01、RCK-02、RCK-03 位于各片区中央步行广场。


上述强度与高度均为概念建议区间，须待正式控规、权属与建筑普查资料到位后由专业团队校准。

百年京张 AI 创新带城市设计 | 提交包：cf3901646 | 临时粗略边界（provisional）

三处重点区 | 街道层级空间体验与构件落位

基于本包概念断面与空间组件生成；不是现状照片、审批效果图或工程承诺

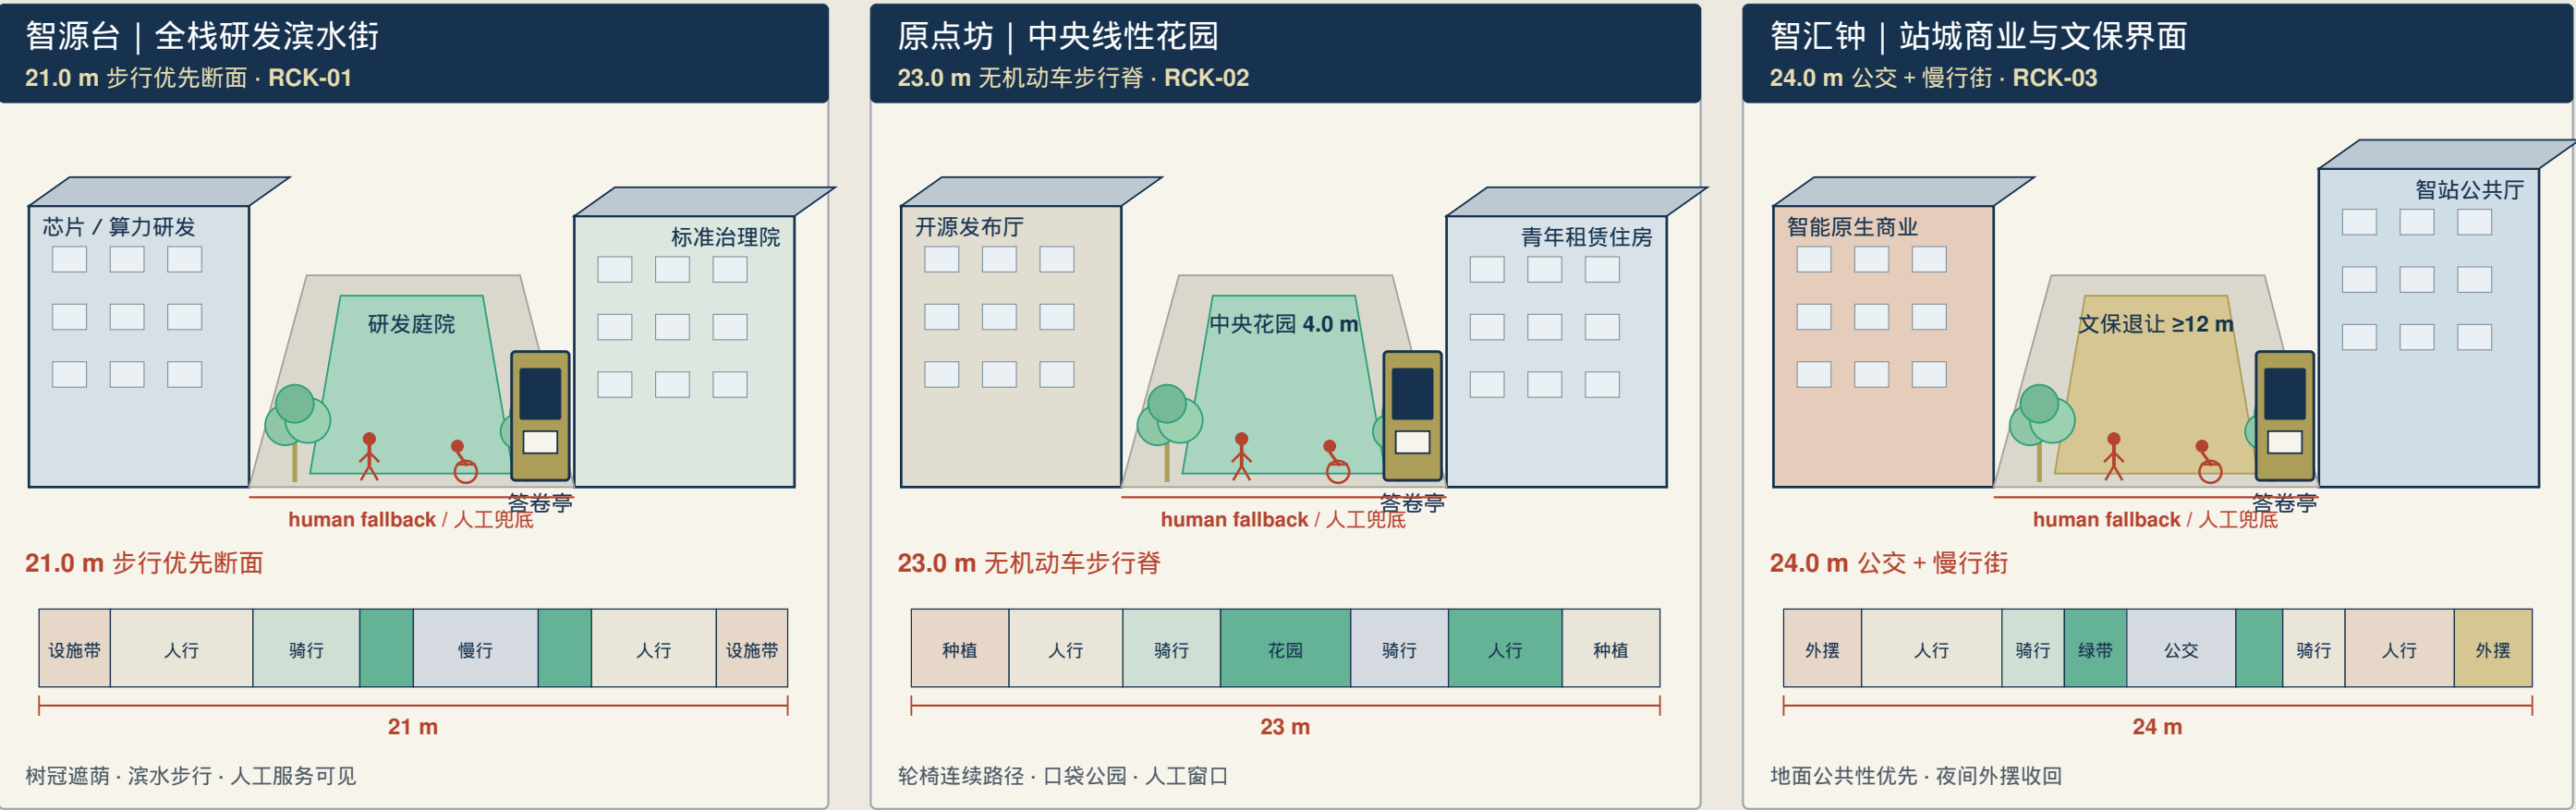

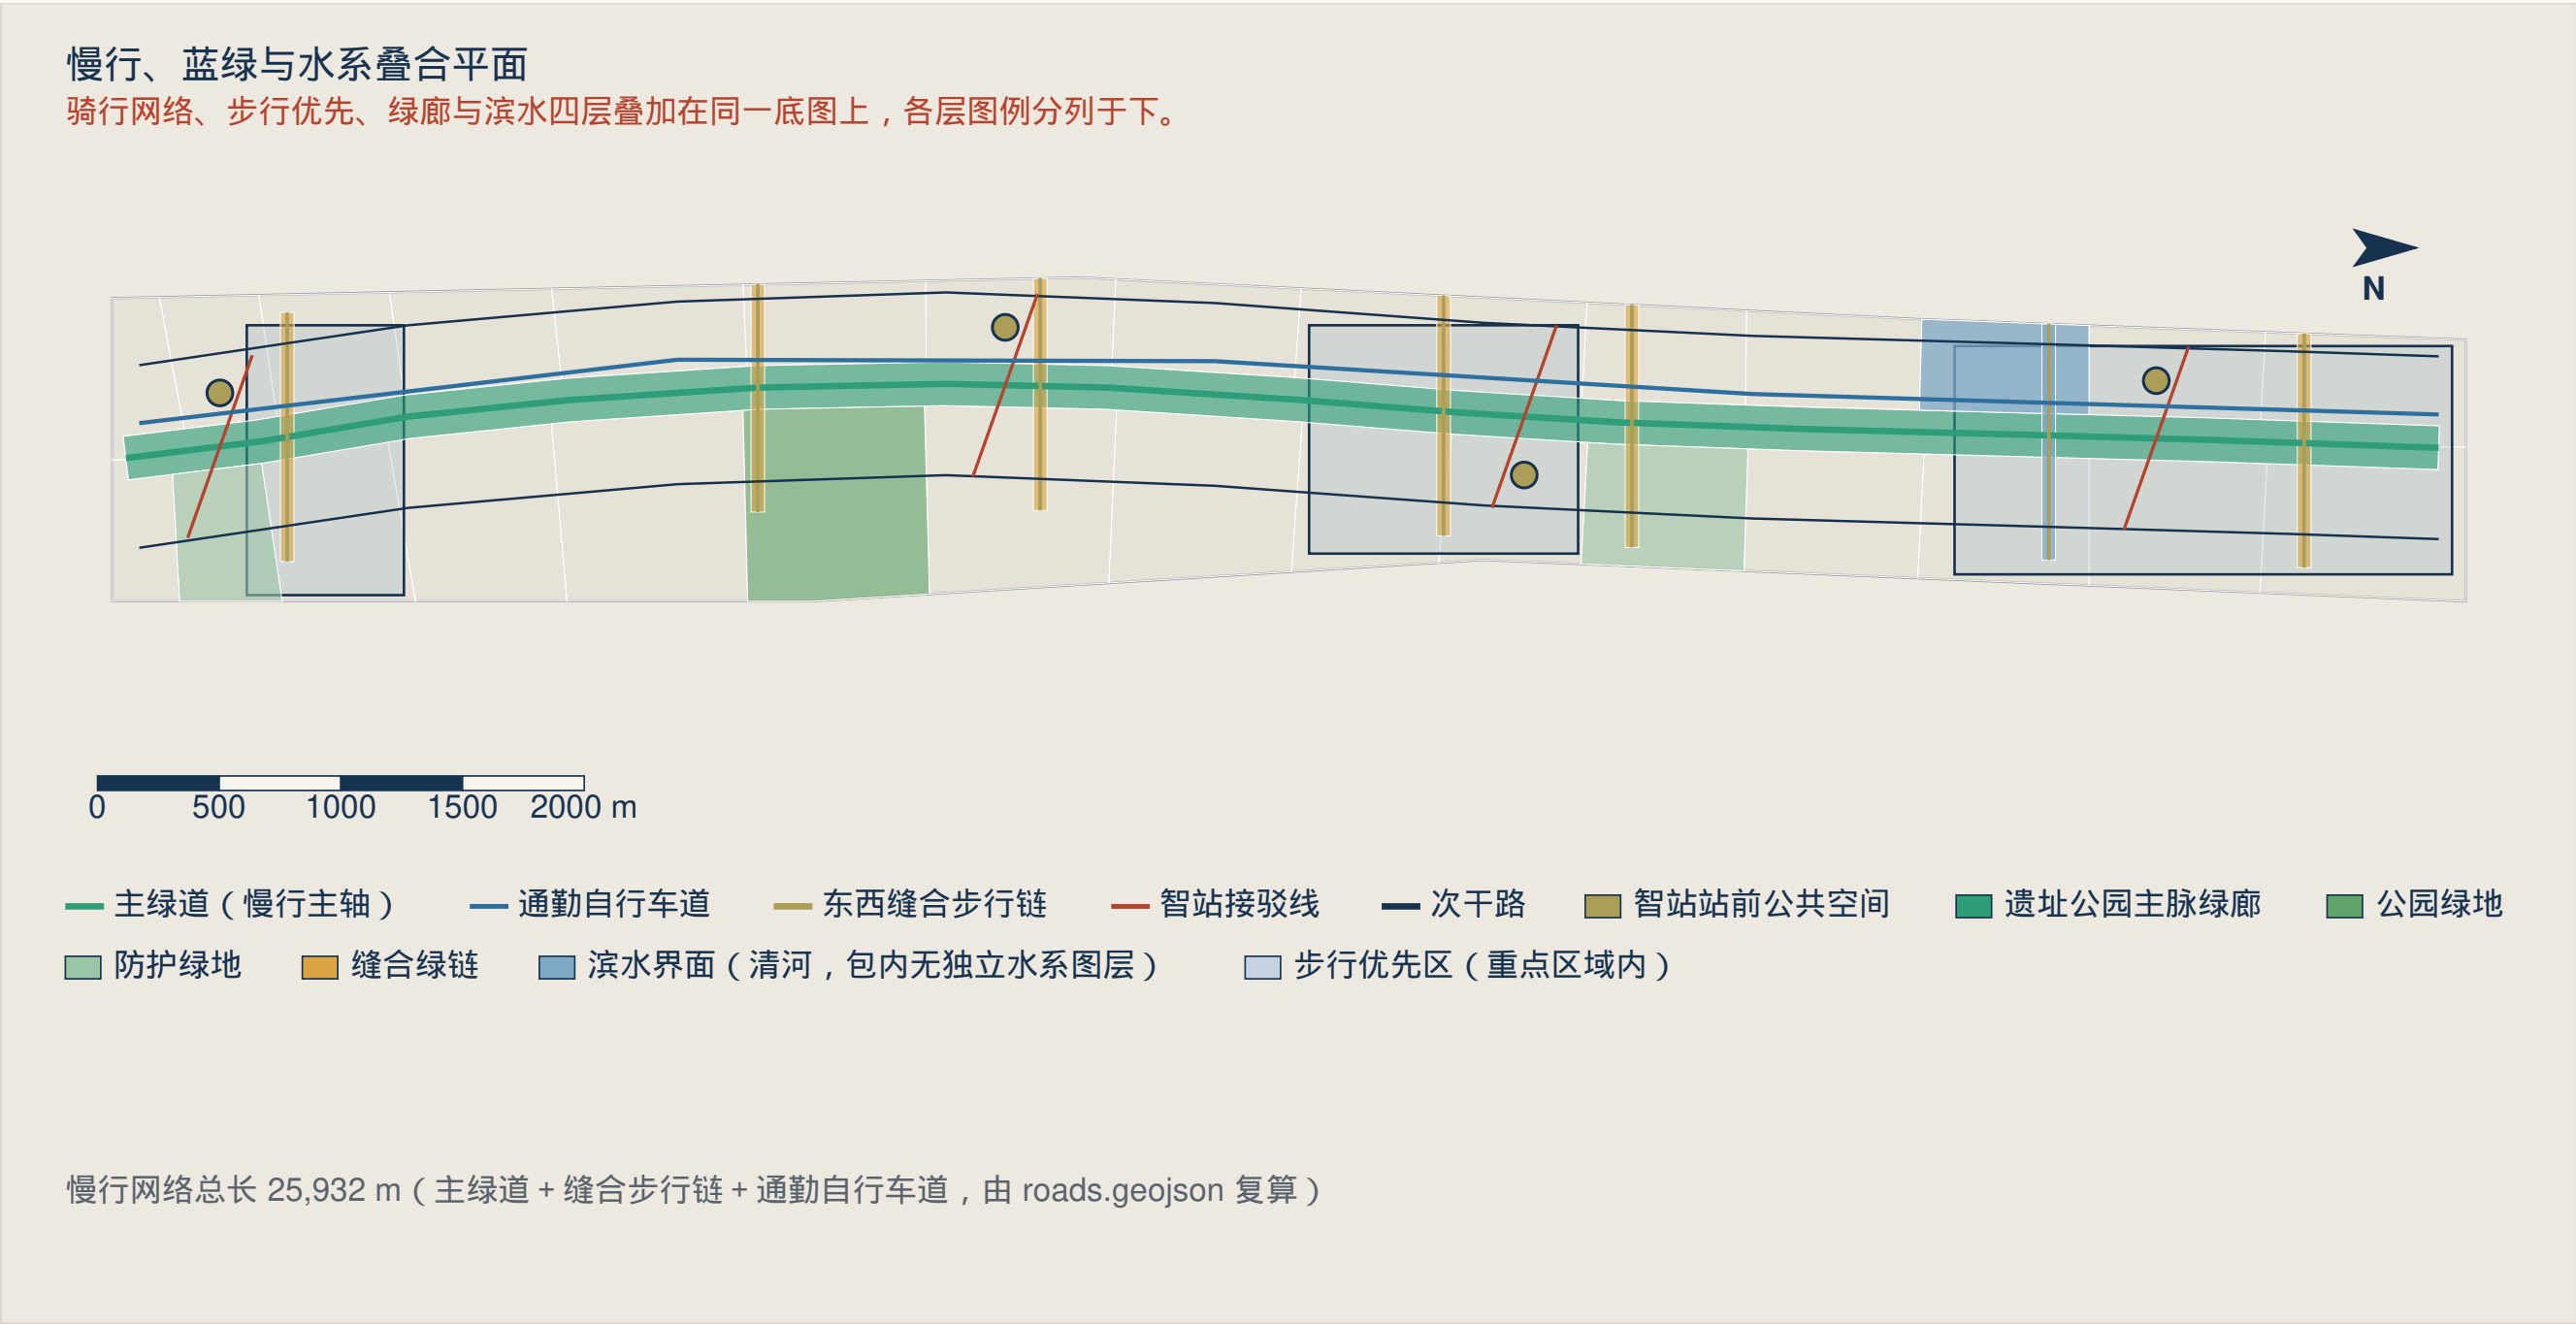

mobility-bluegreen

图 04 慢行与生态

步行、骑行与生态公园廊道的整体网络。


核心系统

- 9.0 km 主脉绿道，含 4.5 m 铺装复合游径。

- 7 条东西向缝合步行链，跨越既有铁路割裂界面。
 - 街道断面：步行 3-5 m、自行车 2.5-3 m，配置绿化带。
 - 智站路缘：分时动态分配，新能源充电车位比例 $\geq 40\%$ 。
- 慢行网络总长 25,932 m，由 roads.geojson 在 EPSG:4548 下复算。

指标图证：三片区等面积方形图解与复算值

每个方形的边长按片区实际面积开方绘制，面积、慢行里程与比率均由本包 geometry/ 图层复算

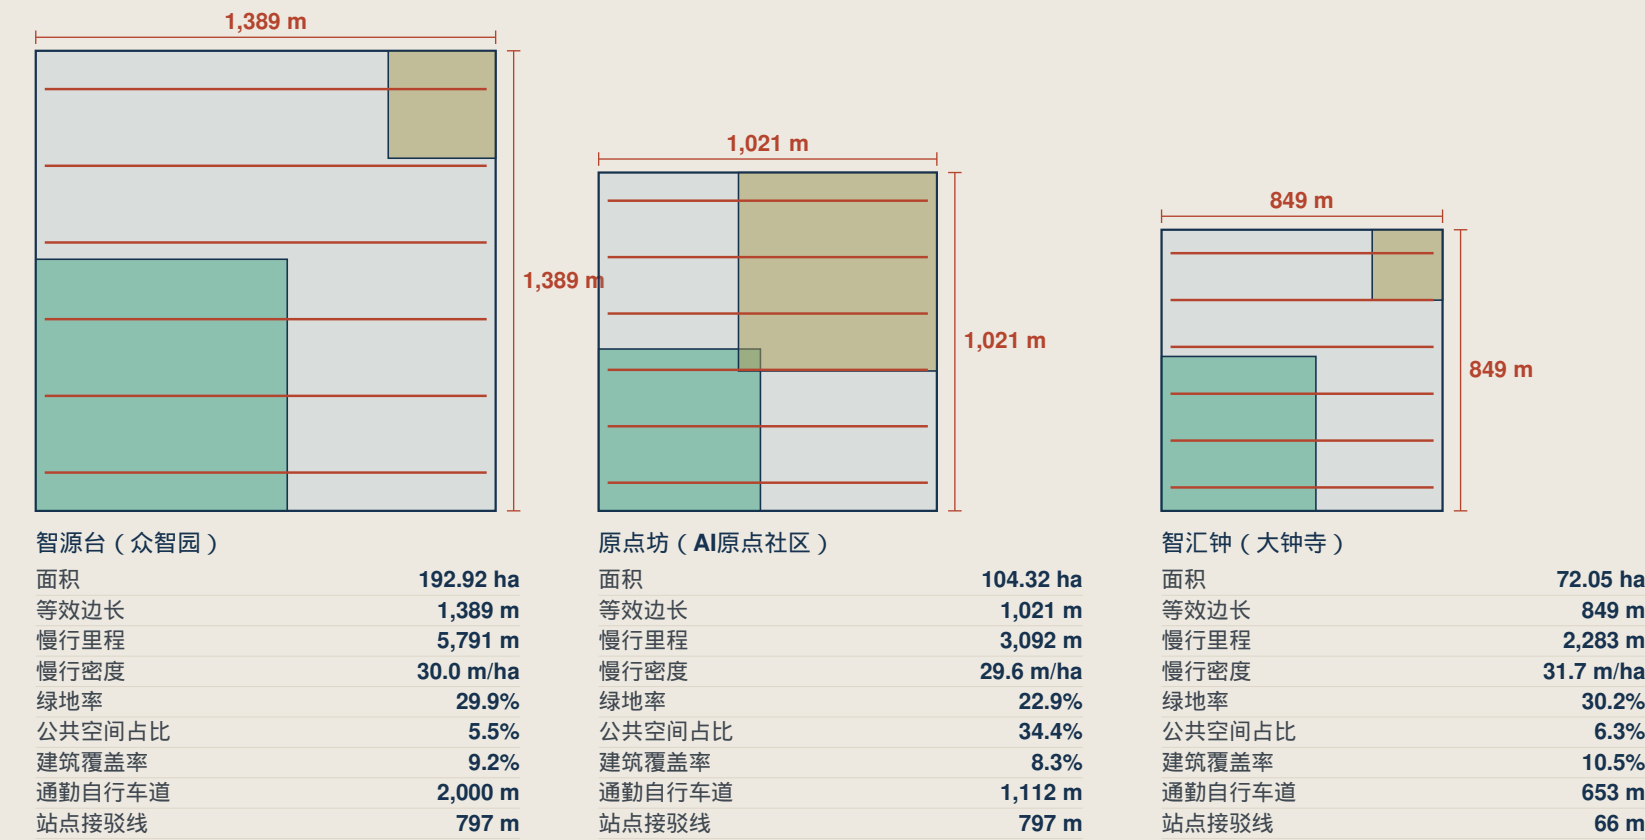

口径：慢行 = 绿道 + 步行链 + 自行车道；比率 = 对应图层与片区边界求交后的面积比。边界为临时粗略范围。

metrics-evidence

图 05 指标与治理

60 项指标在 EPSG:4548 下结构化复算。

指标不变量

- 57 项 known 指标：正文陈述值 = 自动复算值。
- 3 项法定管控：容积率、建筑限高、总建筑面积严格保持 unknown。
- 答卷亭概念设计目标：占地 3.96 m²（1,800 × 2,200 × 2,800 mm），净操作区 ≥ 2.0 m，轮椅回转半径 ≥ 1.5 m；须经适用标准与专业核验。
- 校验：全部确定性门禁 100% PASS。

百年京张 AI 创新带城市设计 | 提交包：cf3901646 | 临时粗略边界（provisional）

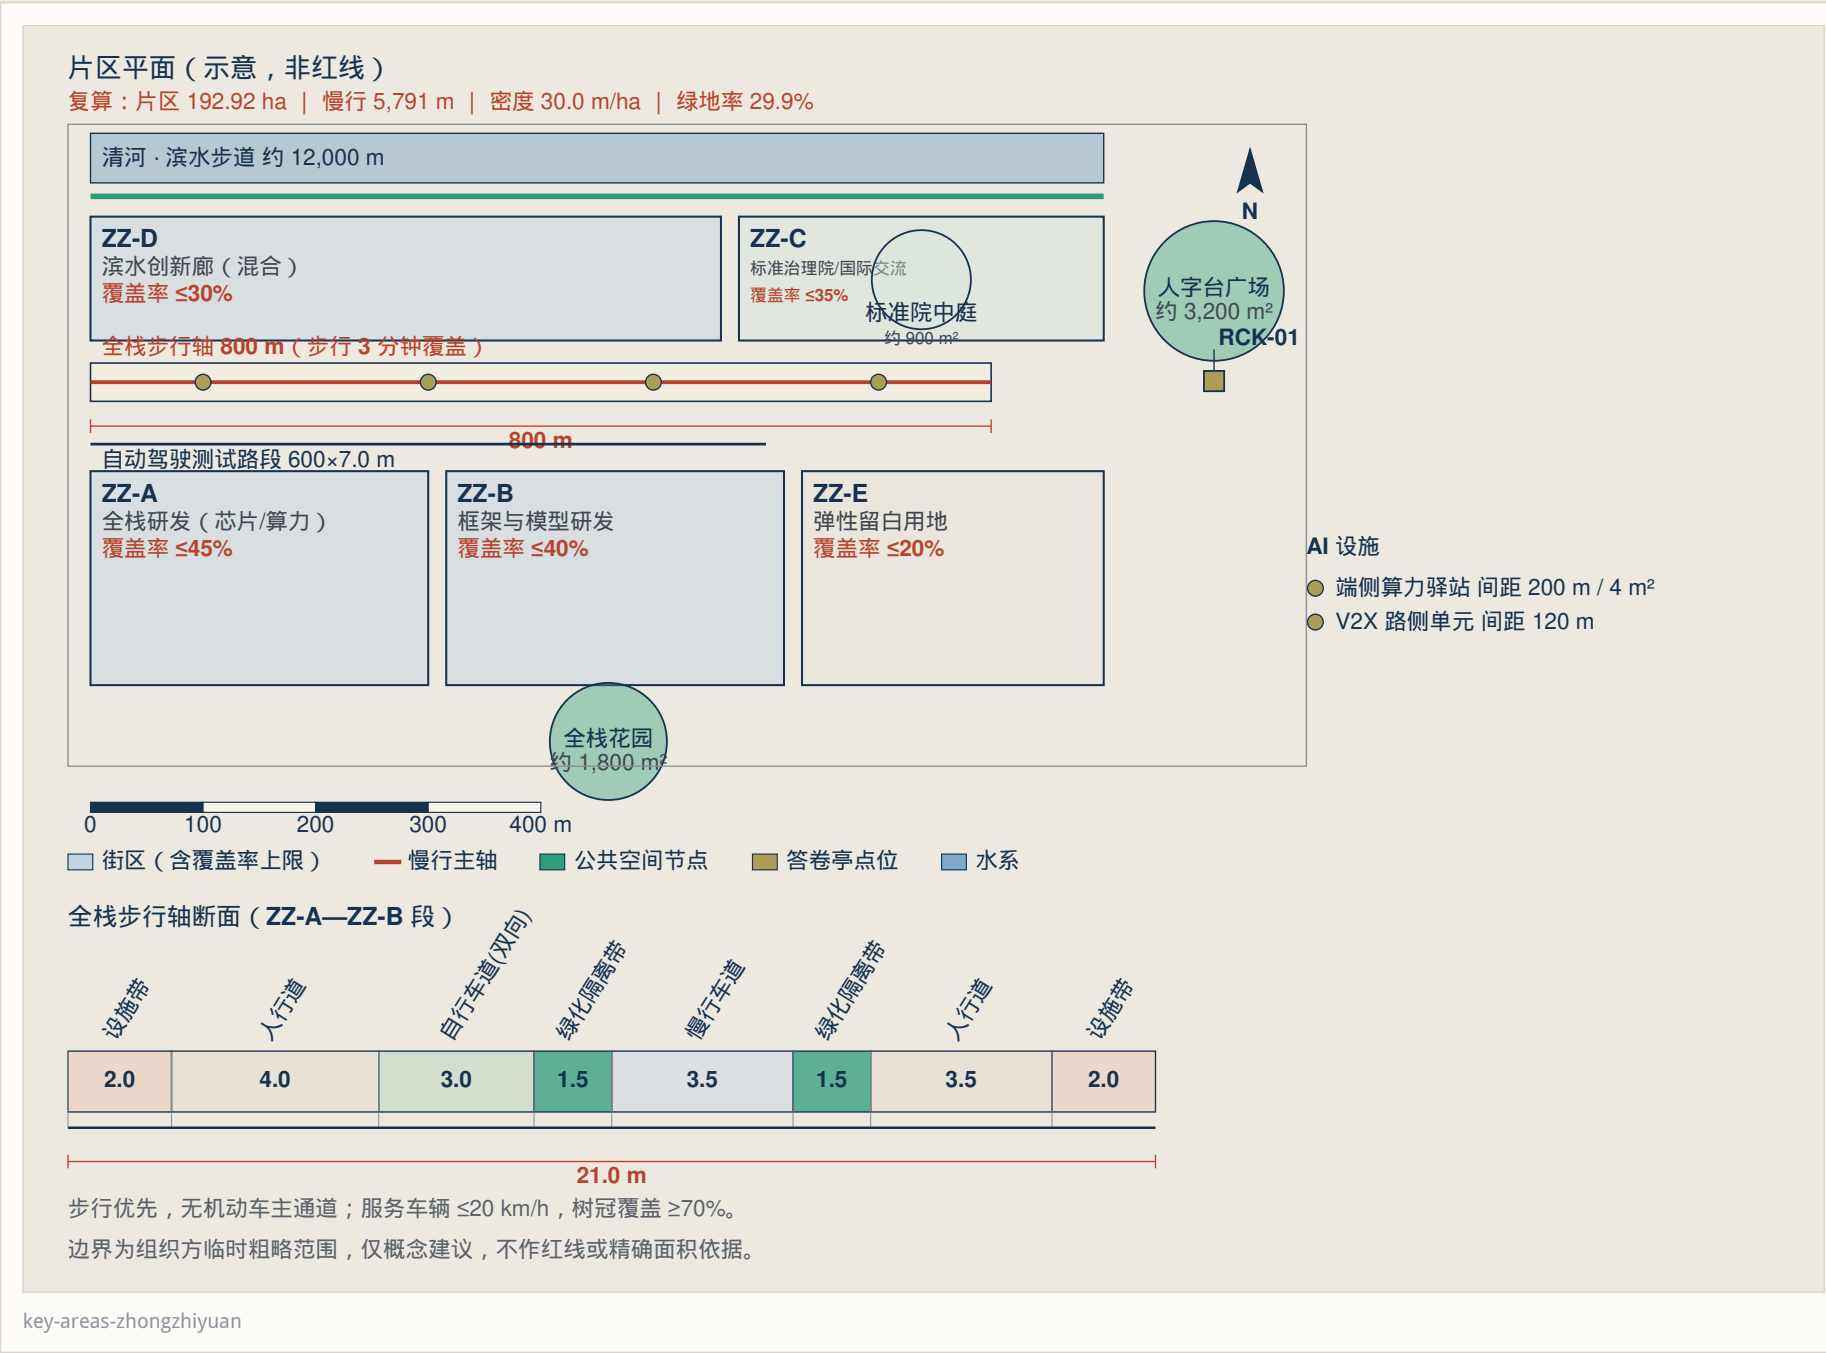


图 06 智源台 193 ha

复算：192.92 ha | 慢行 5,791 m | 密度 30.0 m/ha | 绿地率 29.9%

- 街区 ZZ-A—ZZ-E：全栈研发（芯片/算力）、框架与模型研究、标准治理院与国际交流、滨水创新走廊、弹性预留地。
- 全栈步行轴 800 m（三分钟步行圈），标准断面 21.0 m。
- 公共锚点：人字广场约 3,200 m²、全栈花园约 1,800 m²、RCK-01 答卷亭。
- 自动驾驶测试段 600 × 7.0 m；边缘算力点位间距 200 m / 4 m²。

清河滨水步道约 12,000 m，与主脉绿道形成双线并行。

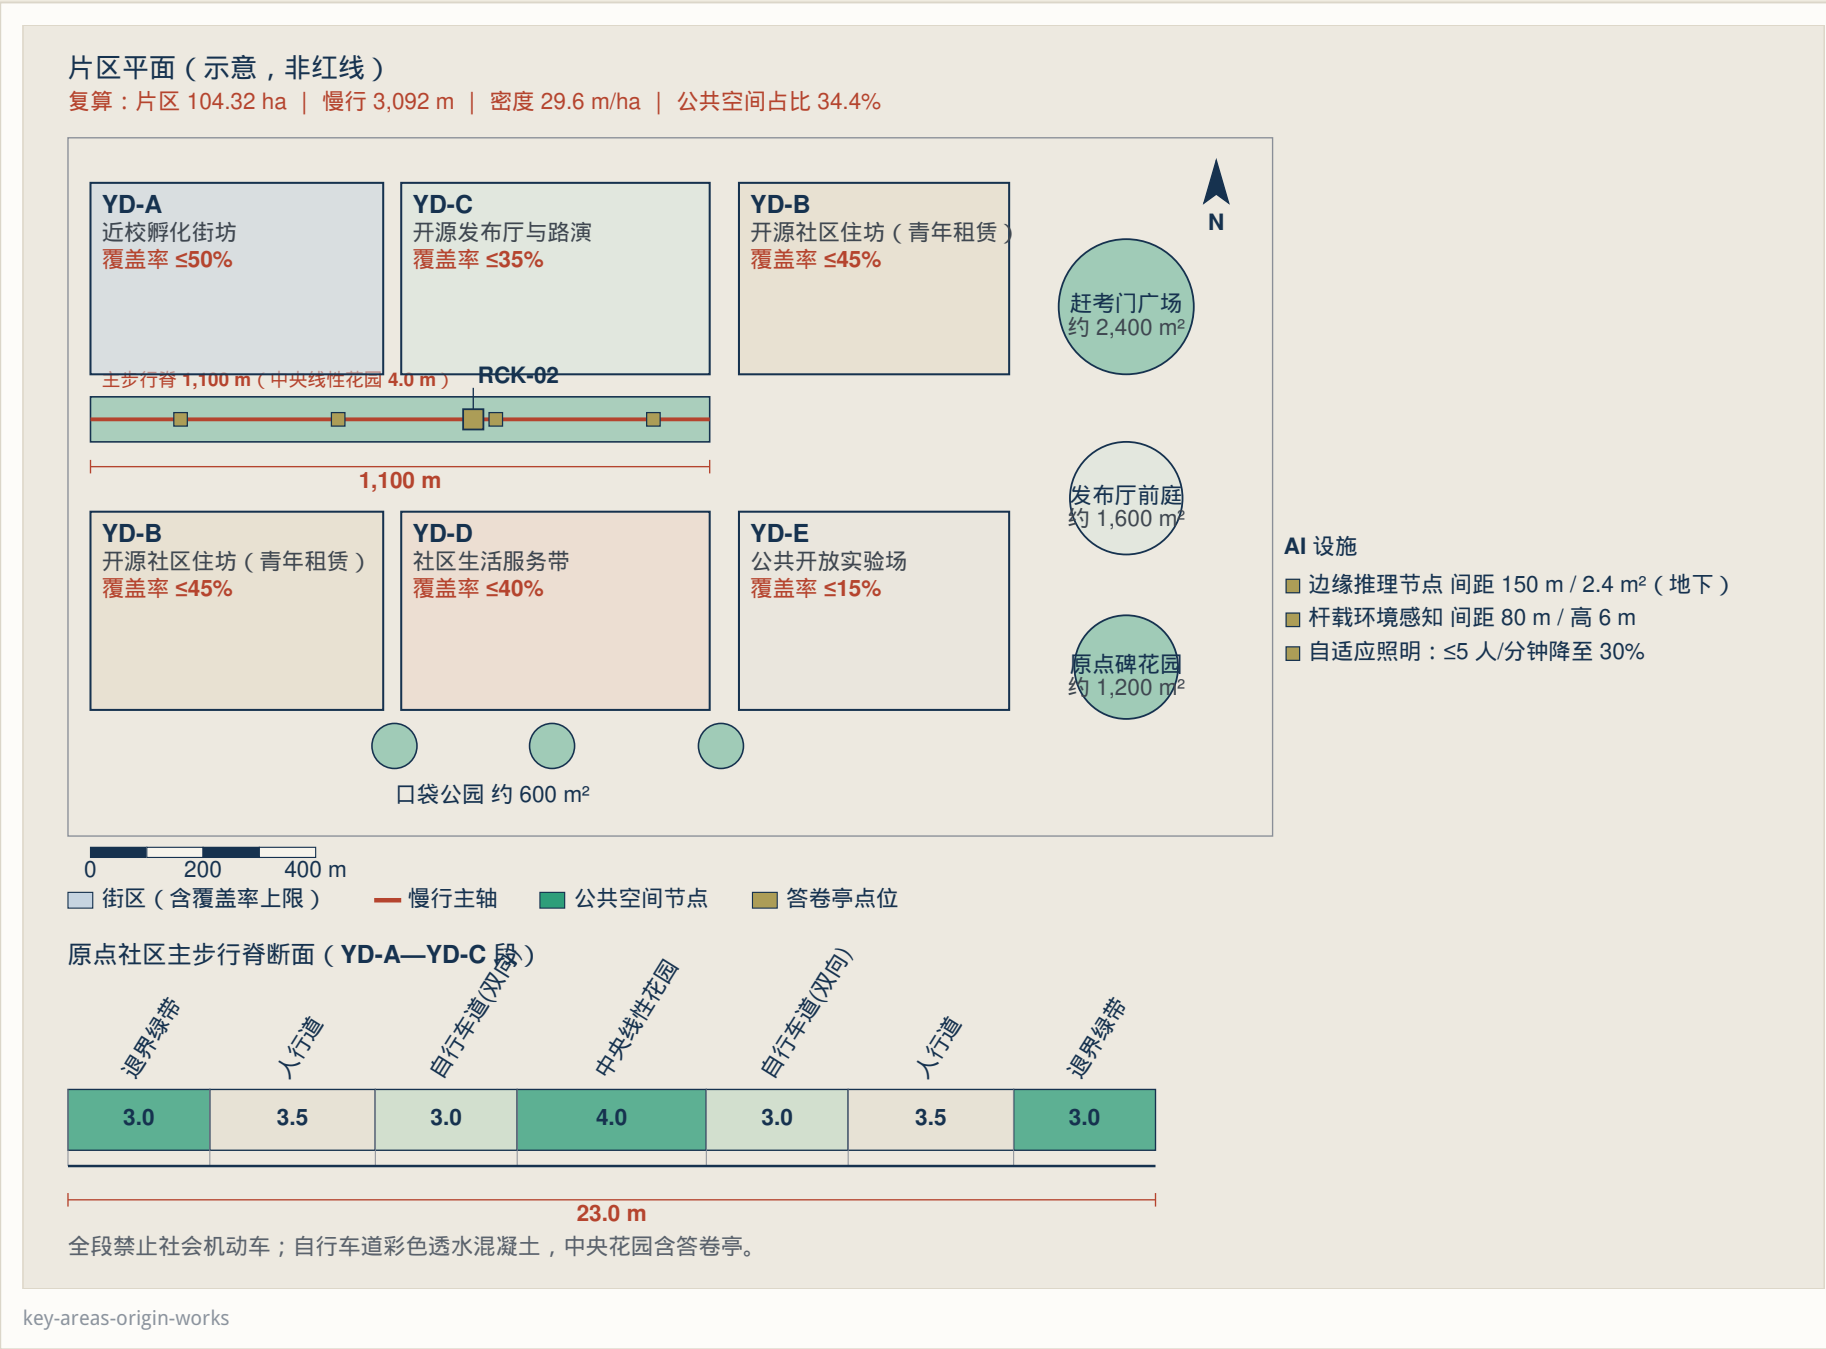


图 07 原点坊 104 ha

复算：104.32 ha | 慢行 3,092 m | 密度 29.6 m/ha | 公共空间 34.4%

- 街区 YD-A—YD-E：邻校孵化、开源发布厅与 Demo Day、开源人才租赁住房、社区服务带、开放实验场。
- 主步行脊 1,100 m，中央线性花园 4.0 m；标准断面 23.0 m。
- 公共锚点：赶考门广场约 2,400 m²、原点碑花园约 1,200 m²、RCK-02 答卷亭。

口袋公园每处约 600 m²，串联三条南北向步行支线。

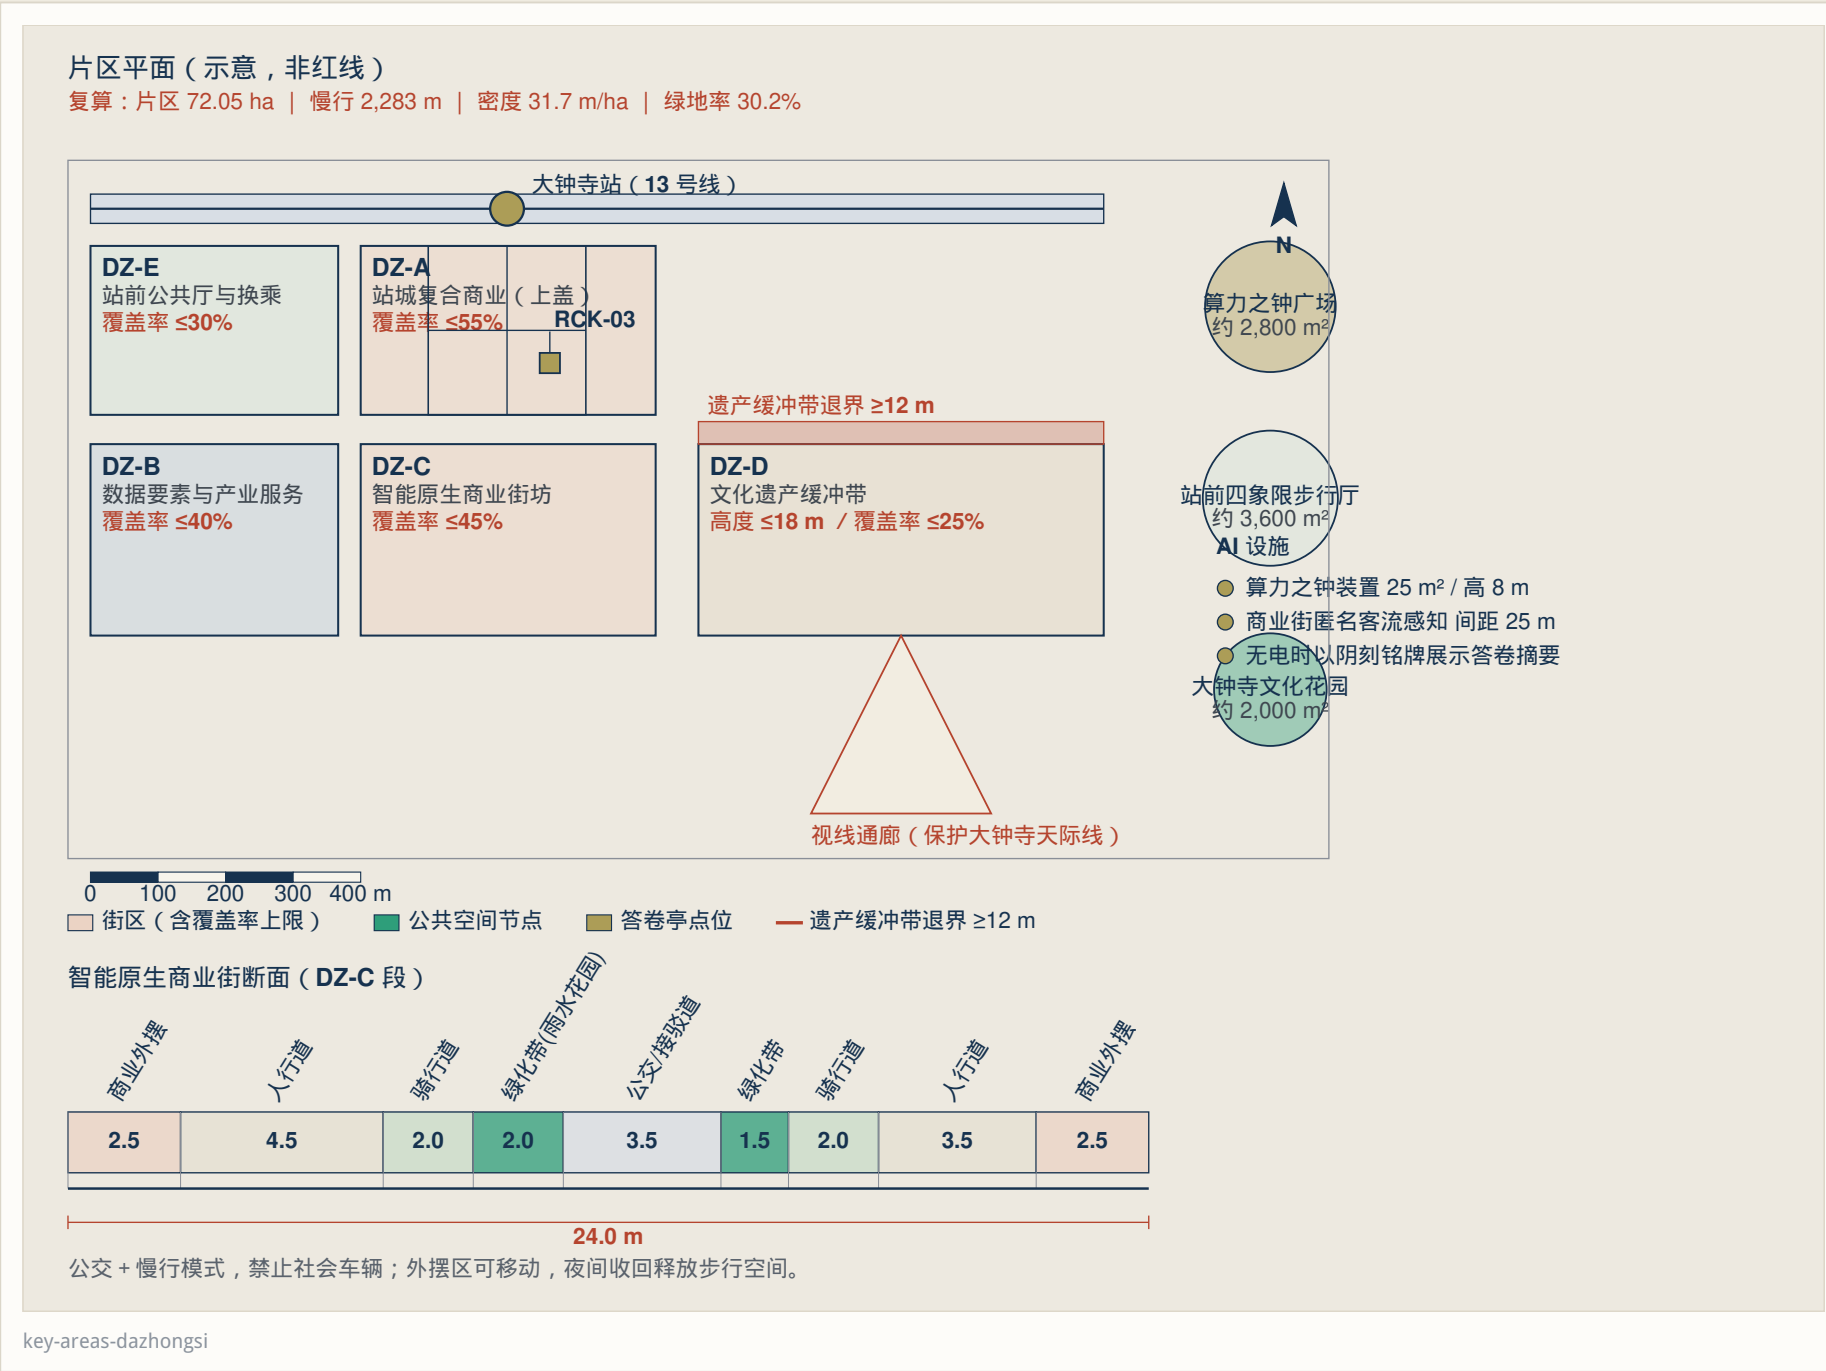


图 08 智汇钟 72 ha

复算：72.05 ha | 慢行 2,283 m | 密度 31.7 m/ha | 绿地率 30.2%

- 街区 DZ-A—DZ-E：绿色算力、产业引擎、智能原生商业、生活居住、四象限公园。
- 智能原生商业街标准断面 24.0 m；大钟寺文物本体退让 ≥ 12 m。
- 公共锚点：算力之钟、大钟寺智站四象限站厅、RCK-03 答卷亭。
- 公交 + 慢行模式，禁止社会车辆；外摆区可移动，夜间收回释放步行空间。

文物保护范围与建设控制地带须待官方资料发布后复核。


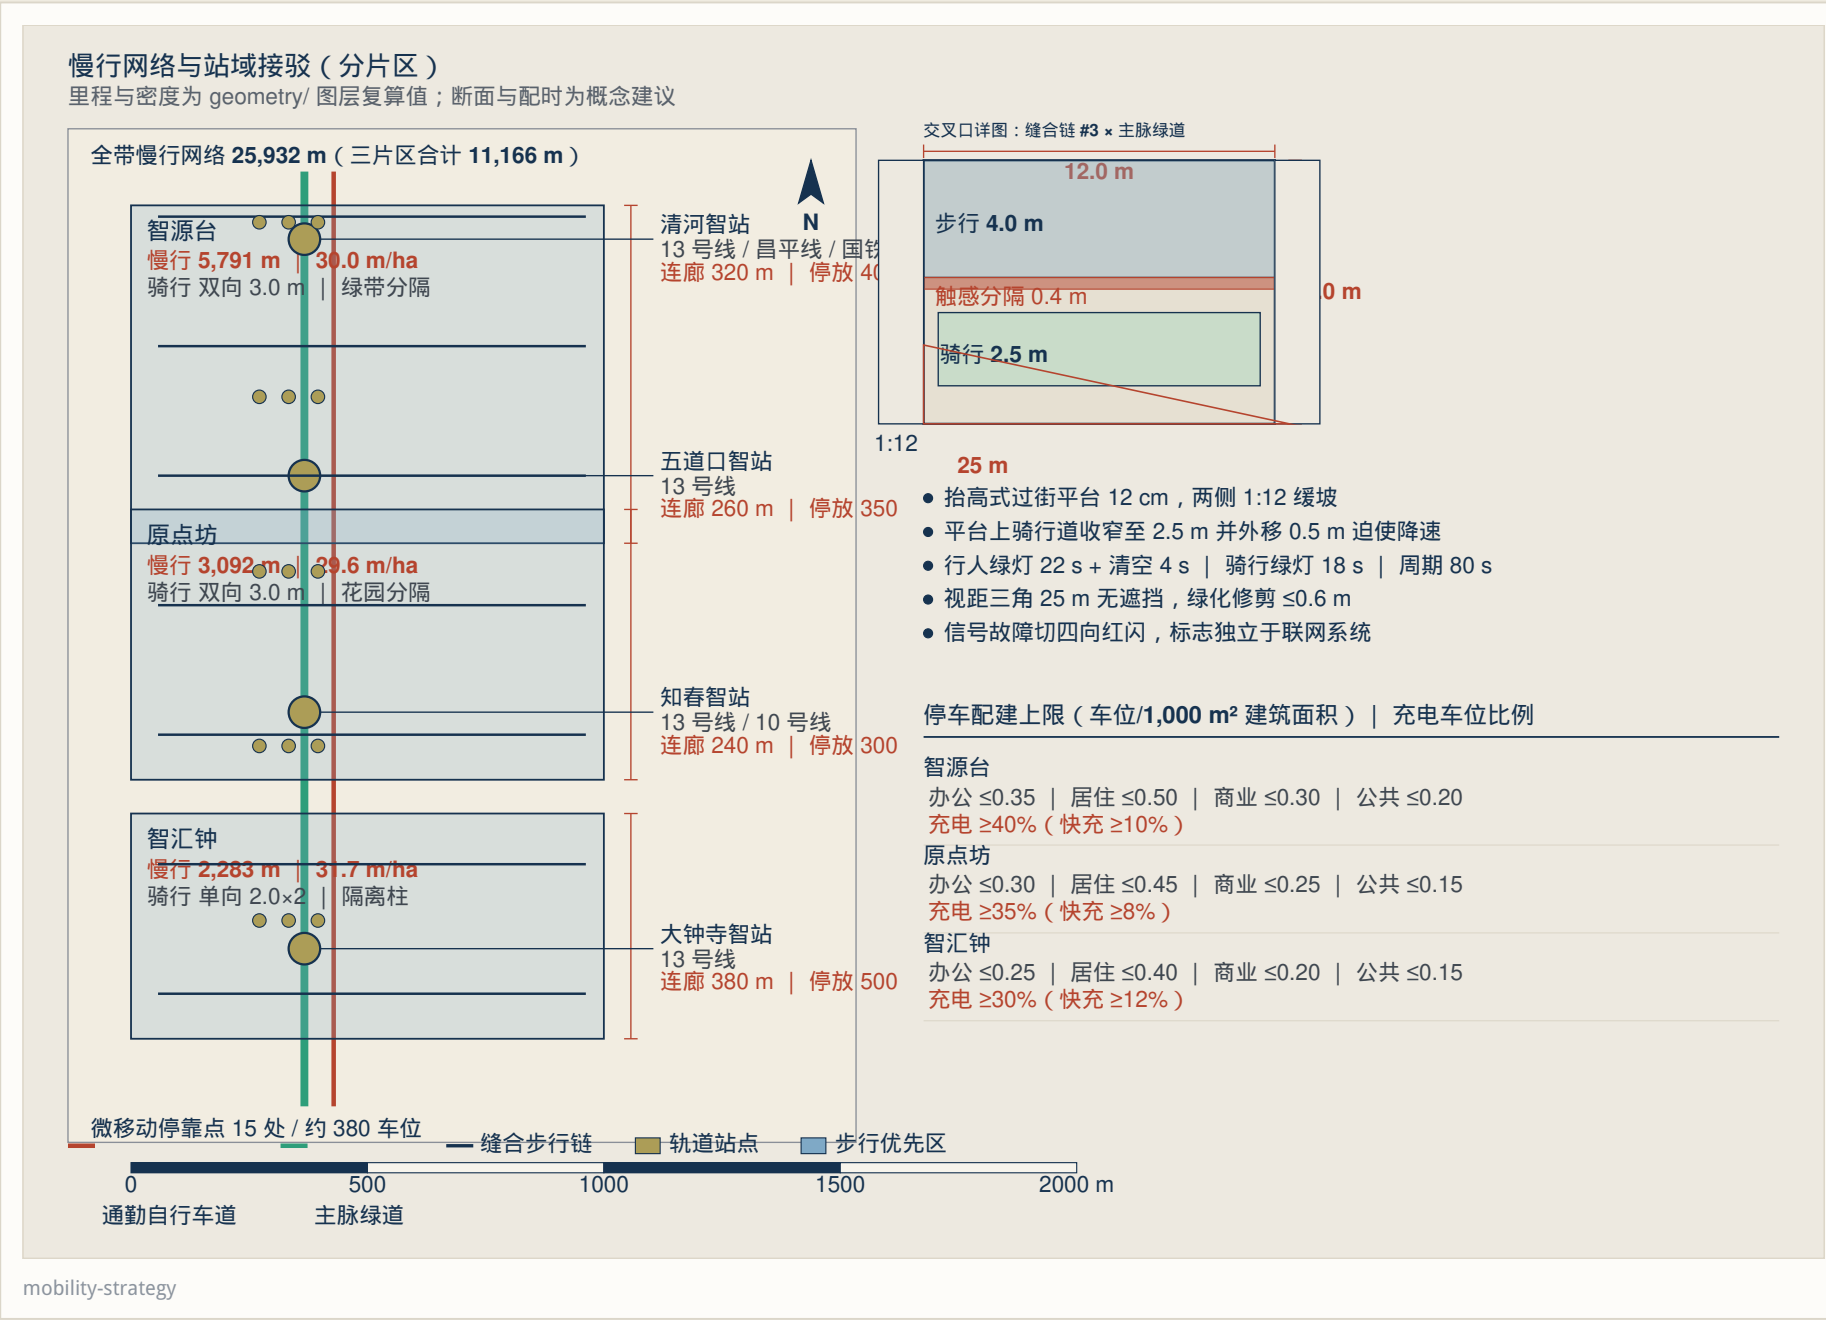


图 09 交通策略

全带慢行网络 25,932 m（其中三处重点区内 11,166 m）。

- 站域接驳：清河、五道口、知春、大钟寺，风雨连廊 240–380 m。
- 交叉口详图：抬升过街平台 12 cm，配 1:12 坡道；25 m 无遮挡视距三角。
- 信号失效时切换四向红闪；标识在离线状态下仍然有效。
- 分片区停车供给上限，快充车位比例 ≥ 30–40%。

当前交通尺寸与分担率均为概念建议，须待交通流量、站点 OD 与轨道工程接口资料到位后校准。

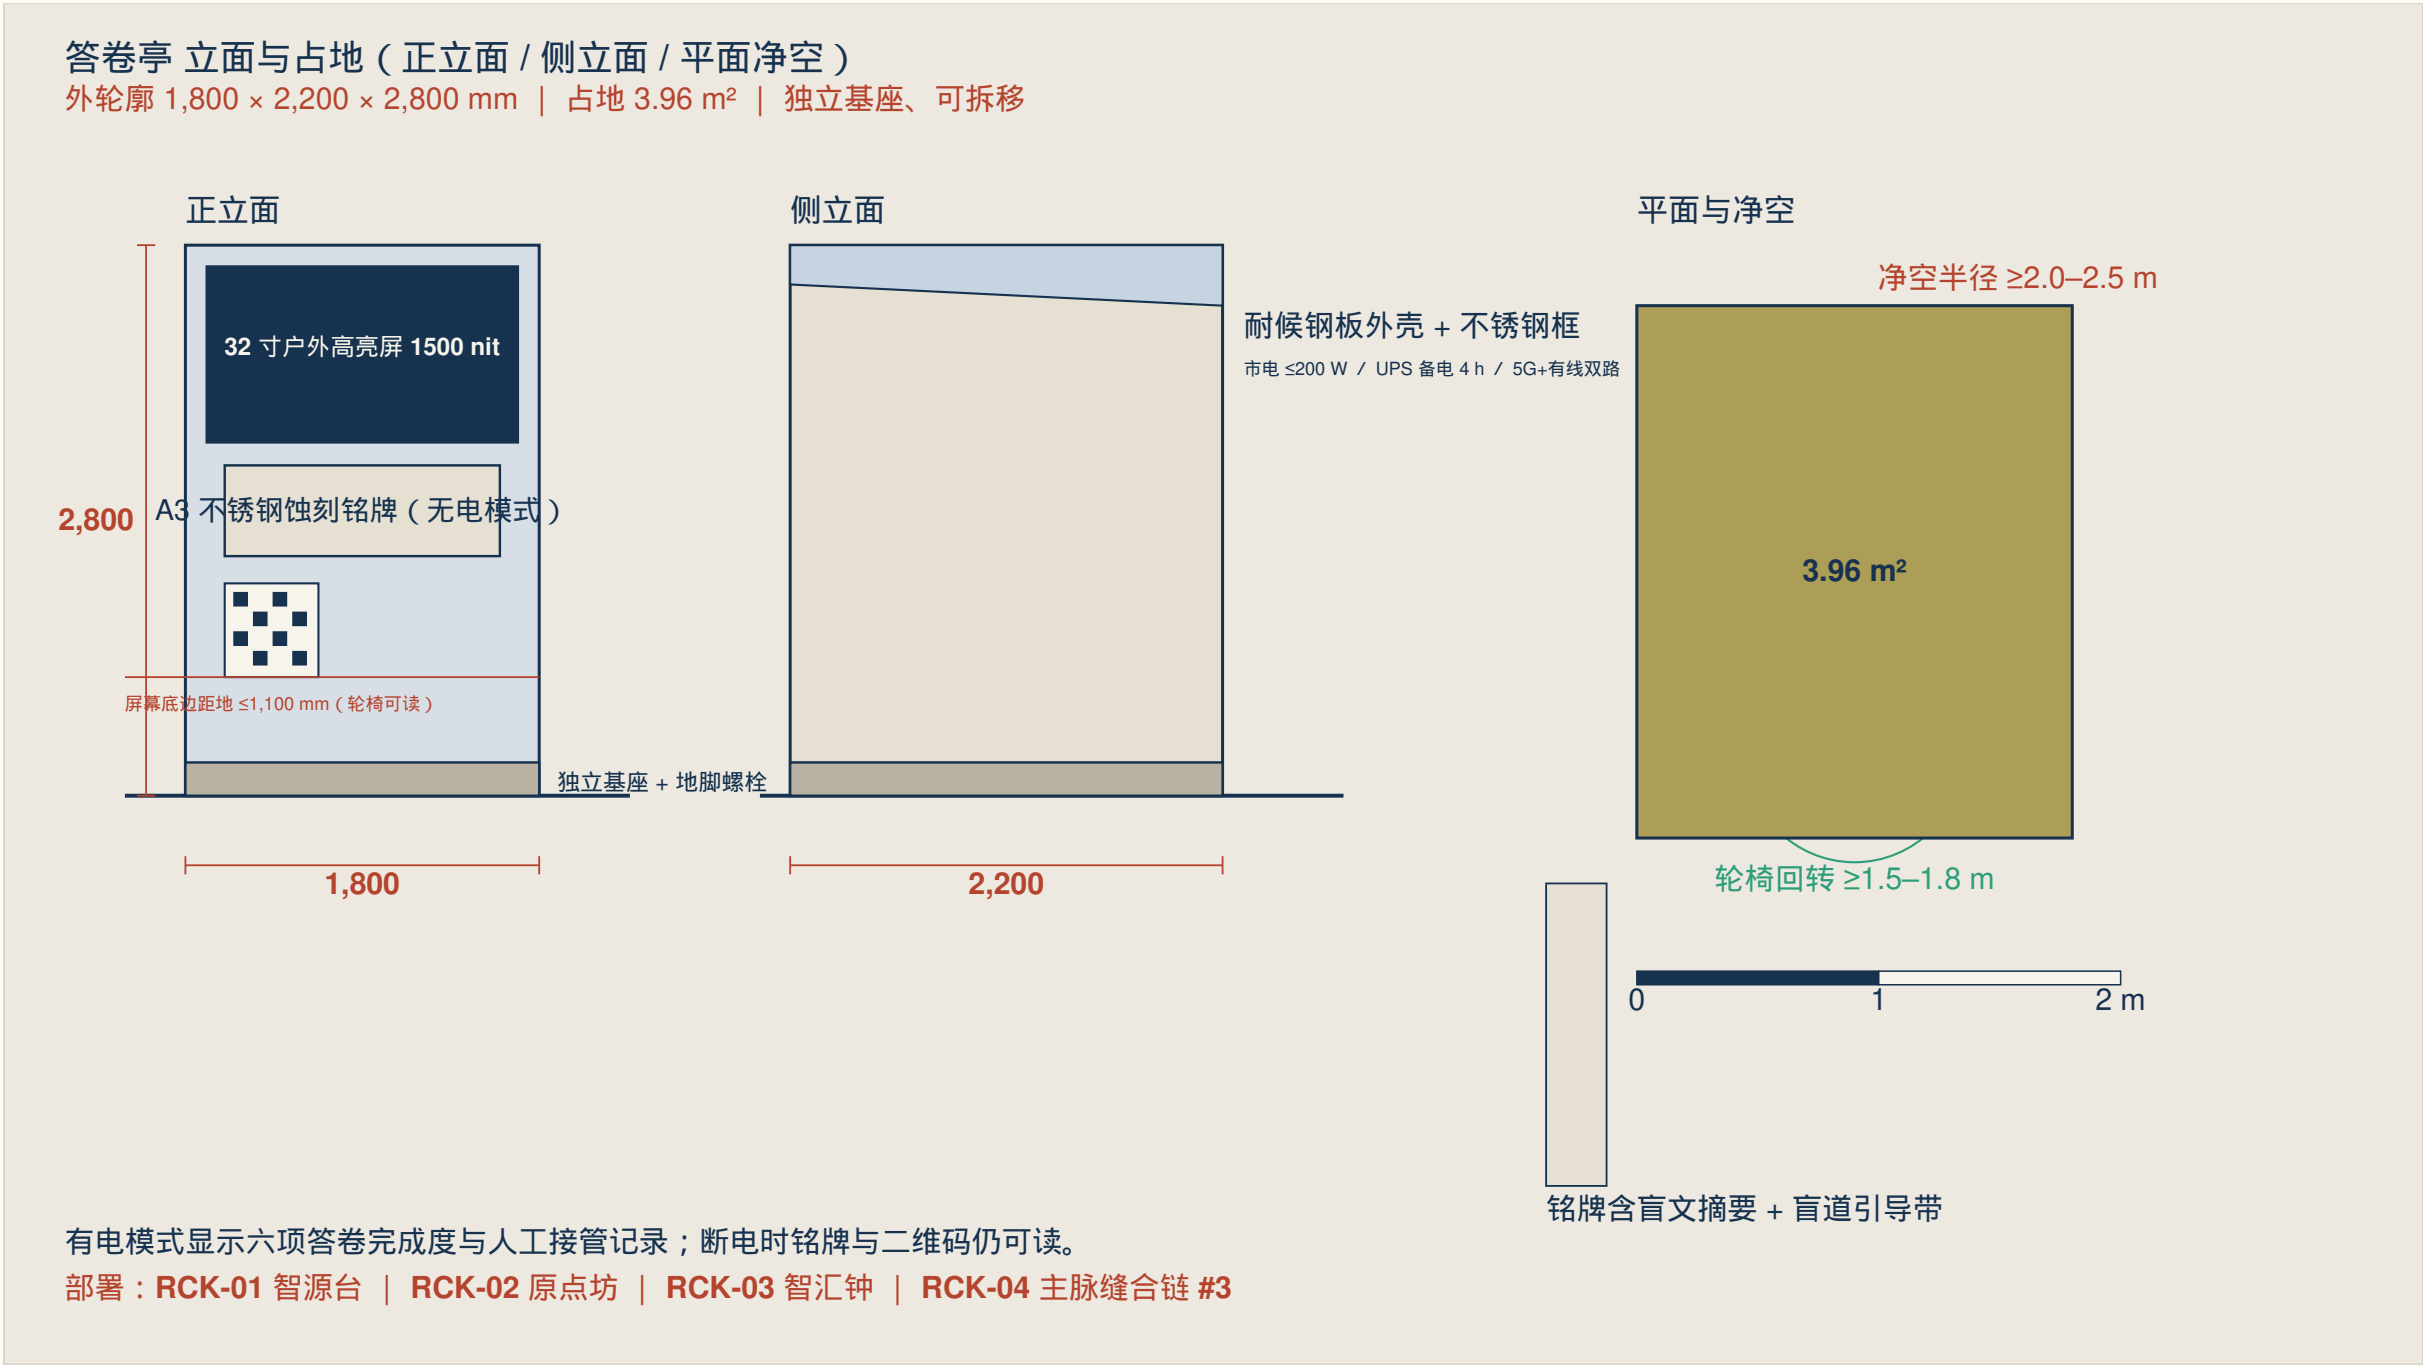

report-card-kiosk

图 10 答卷亭（概念设计目标）

1,800 × 2,200 × 2,800 mm | 占地 3.96 m² | 独立可拆卸基座

- 有电模式：32 英寸高亮室外屏（1,500 nit），实时显示 F1–F6 状态。
- 无电模式：A3 不锈钢蚀刻铭牌 + 实体二维码，指向静态清单。
- 无障碍概念目标：净操作区 ≥ 2.0 m，轮椅回转半径 ≥ 1.5 m，屏幕中心高度 1,000–1,200 mm；须经适用技术标准与专业核验，不构成点位已合规结论。

范围与三处重点区均采用组织方发布的临时粗略替代边界（provisional），仅为概念建议，不得作为正式红线、审批依据或精确面积依据；官方 polygon 发布后必须整体重算几何、指标、图纸与 HTML。

- 布点：RCK-01 智源台 | RCK-02 原点坊 | RCK-03 智汇钟 | RCK-04 主脉缝合链 #3。
- 铭牌同时提供盲文摘要与触感导引条，不依赖智能手机即可获取信息。

1. 六类人才画像

- 原始创新科学家：安静、长周期探索，低电磁噪声专用实验室。
- 开源工程师：低成本弹性联合办公，贡献可在原点碑被看见。
- AI 创业者：快速迭代，便捷接入测试沙盒与风险资本。
- 产业工程师：真实工业数据与边缘部署环境。
- 国际人才：双语标识与无缝国际生活服务。
- 本地社区居民：绿色公园与带人工兜底的智能服务的首要受益者。

2. 12 张场景卡与 4 类产业沙盒

- 12 张场景卡：涵盖智能交通调度、自适应公园照明、AI 健康驿站、环境微气候感知与智慧街具。
- 4 类产业测试沙盒：
 - 具身机器人沙盒（智源台）
 - 无人配送与物流走廊（遗址公园）
 - 生成式城市设计沙盒（原点坊）
 - 绿色算力与能源调度沙盒（智汇钟）

每张场景卡均写明用户任务、空间、责任组合、最小数据、非 AI 路径、放行证据与退出条件。

百年京张 AI 创新带城市设计 | 提交包：cf3901646 | 临时粗略边界（provisional）

1. 三期实施路径

- 一期（2026–2028）原点启动：
 - 主脉绿道贯通、开源发布厅、人字台、首批 4 类沙盒。
- 二期（2029–2031）智网扩展：
 - 7 条缝合链全线贯通、4 处智站 TOD、答卷亭全域覆盖。
- 三期（2032–2035）全球引领：
 - 世界级自主 AI 生态与国际治理对话平台。

2. 标准与合规矩阵

- 住房和城乡建设部《城市设计管理办法》
 - 详细规划编制技术指引
 - 《建筑与市政工程无障碍通用规范》GB 55019-2021
 - 《生成式人工智能服务管理暂行办法》
 - 《智慧助老技术产品及服务推广目录》（仅作参考）
 - 严格隐私协议：不向云端传输原始人脸生物特征数据。
- 权属、许可、控规、市政与文保资料为现场启动的前置条件。