



JINGZHANG OPEN BELT

ONE LINE THREE COURTS SIX ROOMS

Bring the nine-kilometre park back to daily life

01 MASTERPLAN ATLAS


Nine kilometres folded into three urban plans: built works, public plans and this proposal




03 THREE KEY AREAS

Plans, cut lines and everyday edges at the same scale


01 Zhongzhiyuan Test Court

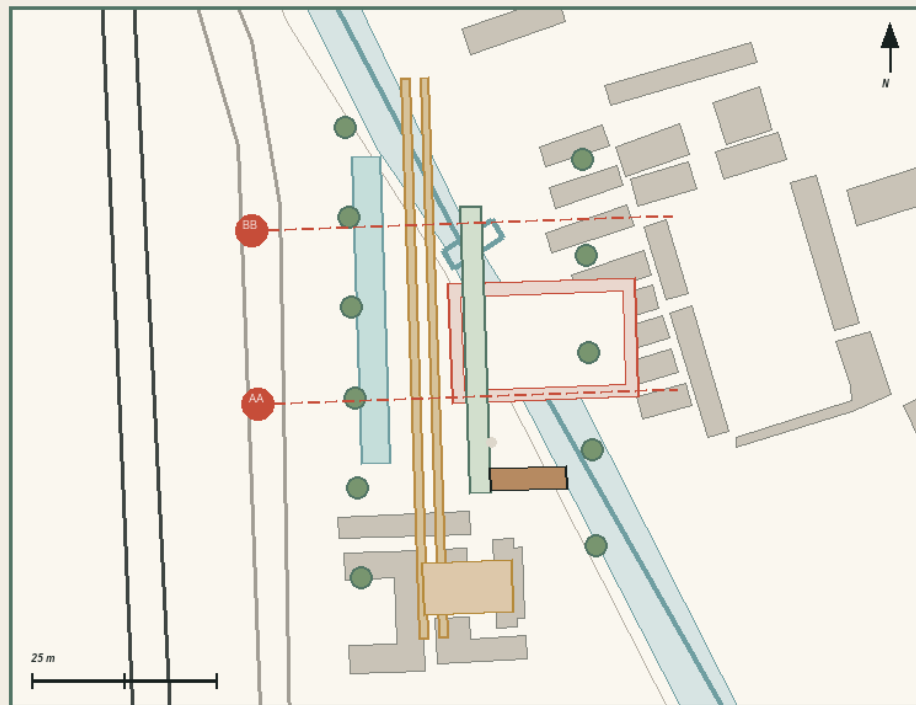


AA Public edge at the test court

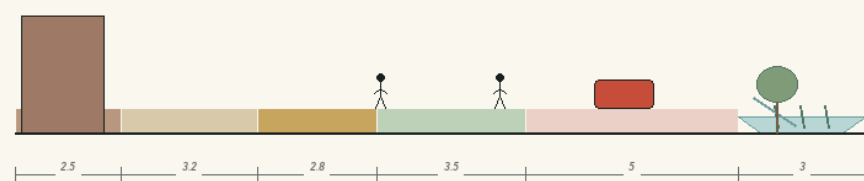


BB Xiaoyuehe link

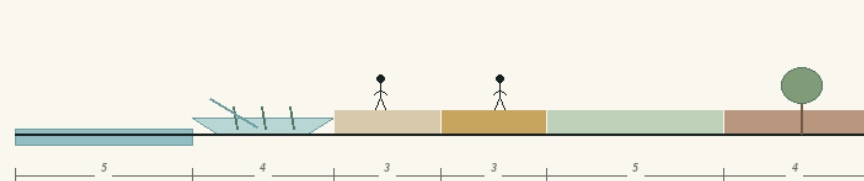


02 AI Origin Service Court

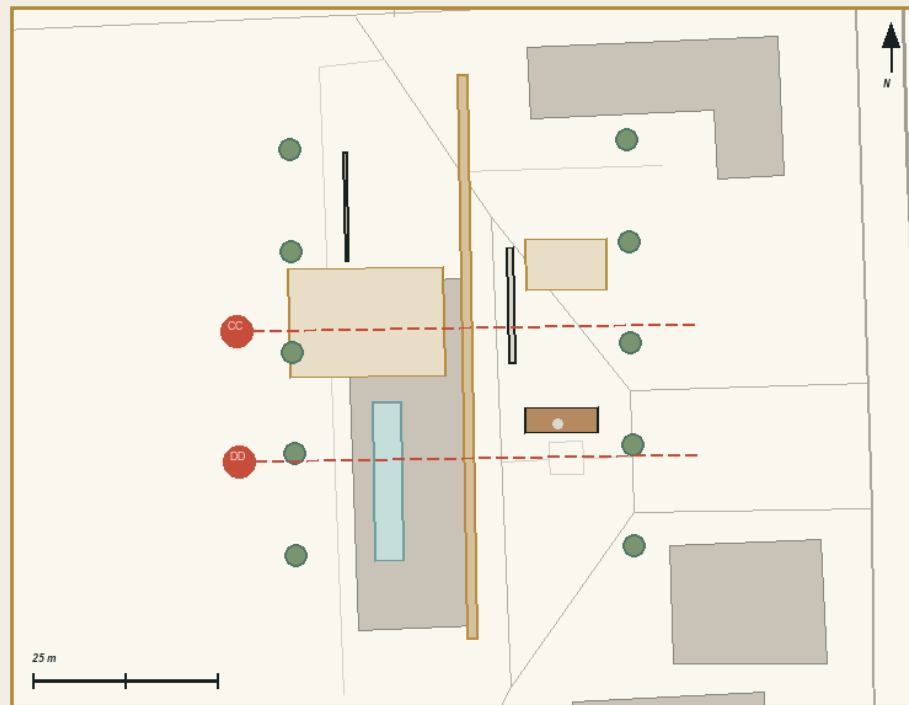


CC Old forecourt

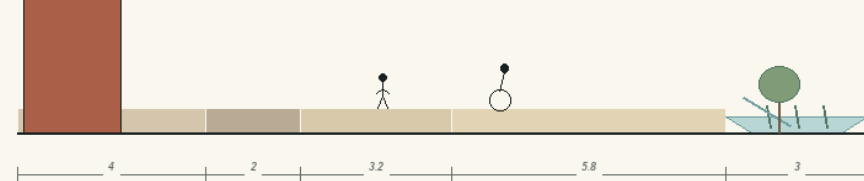


DD Service street court

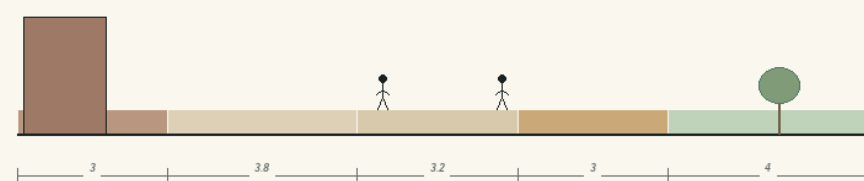


03 Dazhongsi Exchange Court

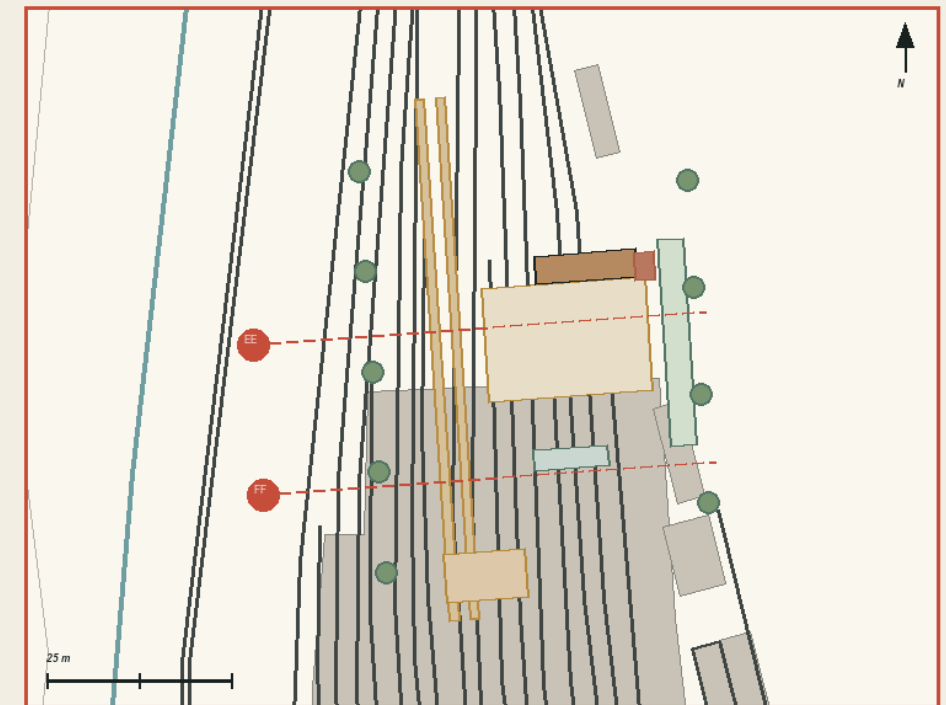

EE Daily edge at the exchange court

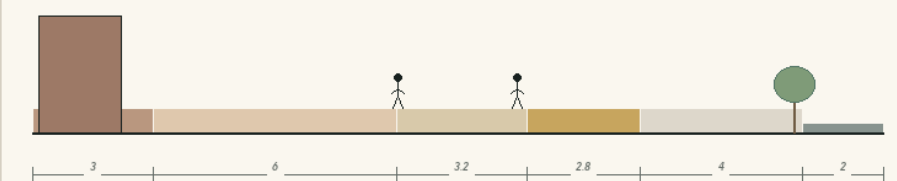

FF Step-free crossing

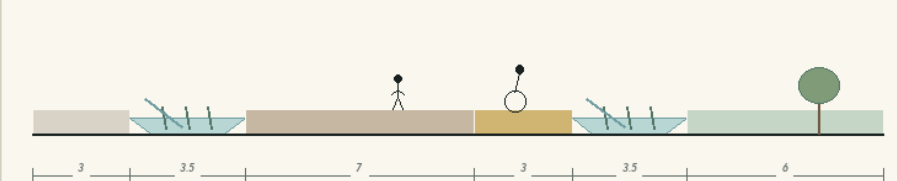


PUBLIC WALK SLOW CYCLE RAIN GARDEN REVERSIBLE TEST EDGE

CONCEPT DESIGN PROVISIONAL BOUNDARY OSM FOR CONTEXT ONLY


Working dimensions Concept design 1:200 section logic

04 MOVEMENT, WATER AND SIX SECTIONS


Join public routes and crossings before placing tests and services

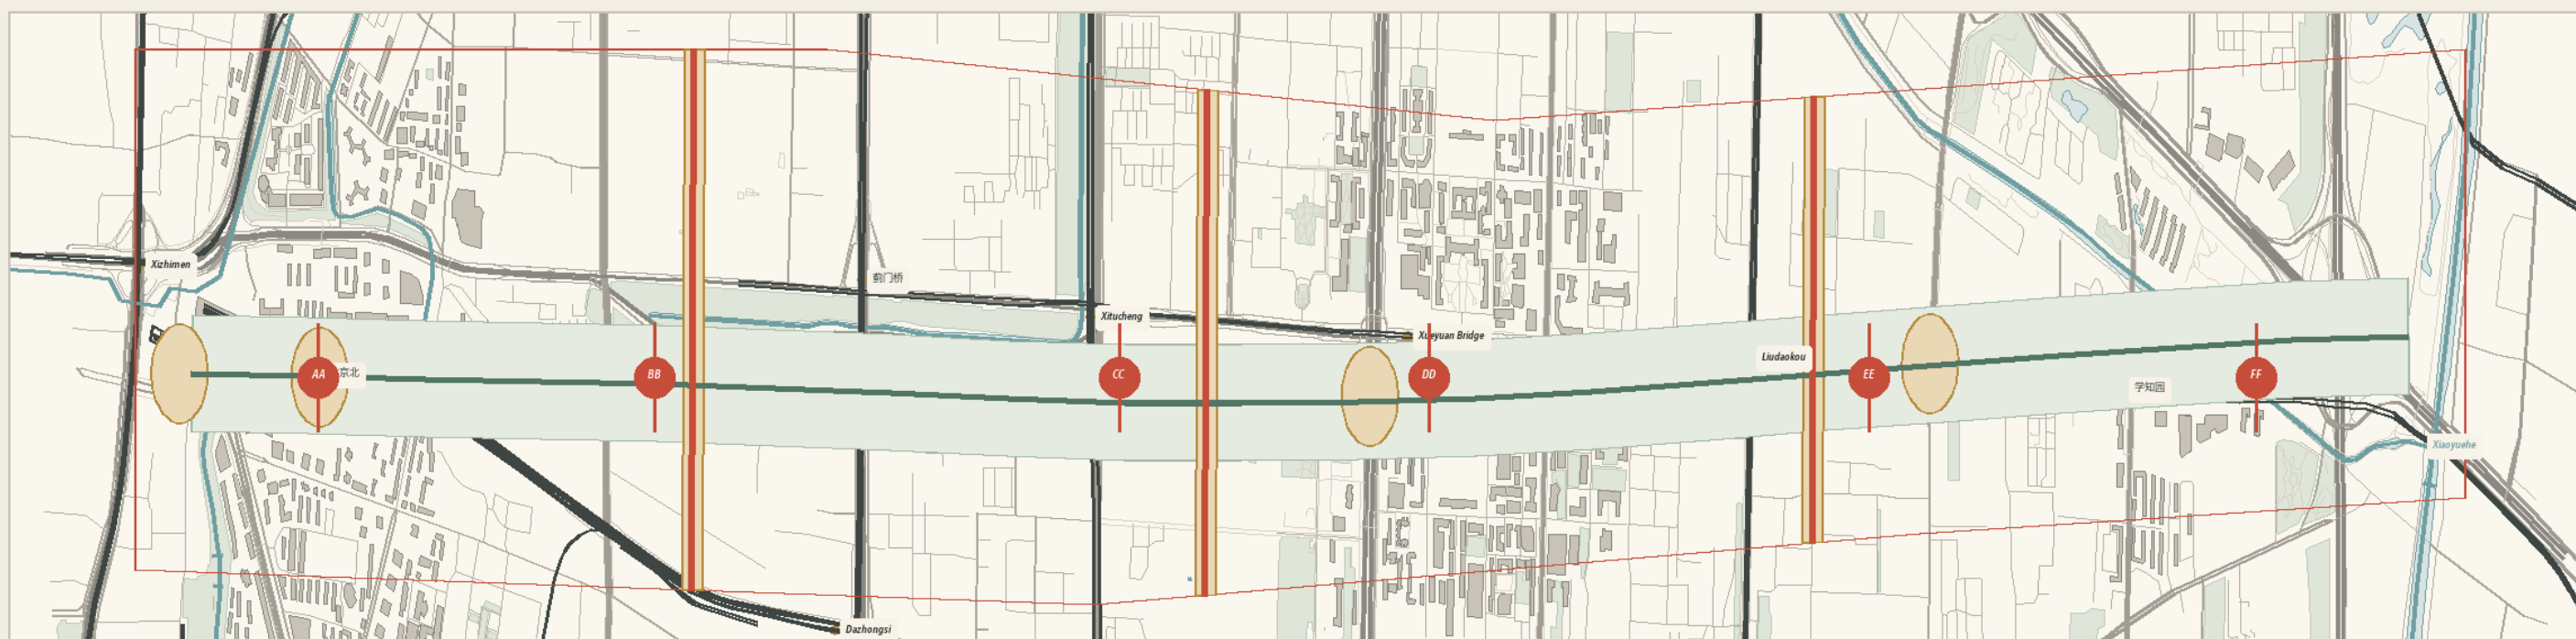


AA Public edge at the test court

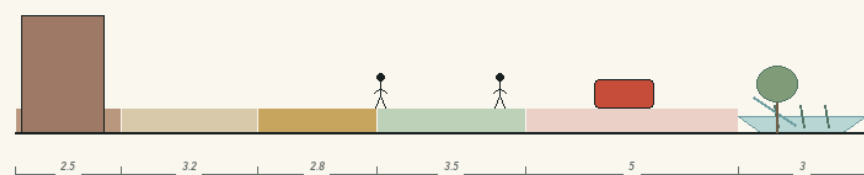


BB Xiaoyuehe link

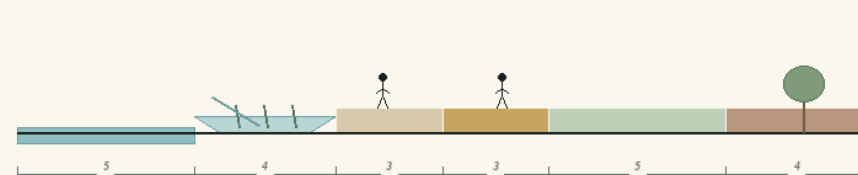


CC Old station forecourt

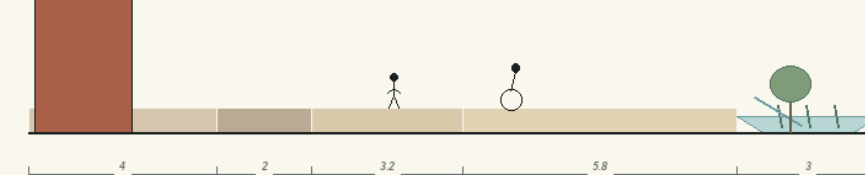


DD Service street court

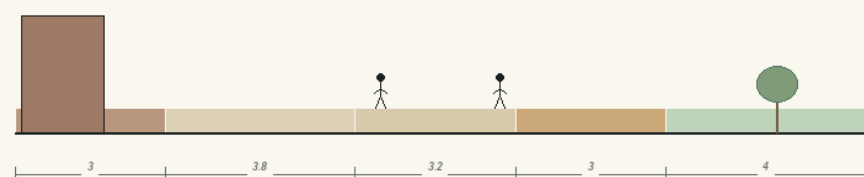

EE Daily edge at the exchange court

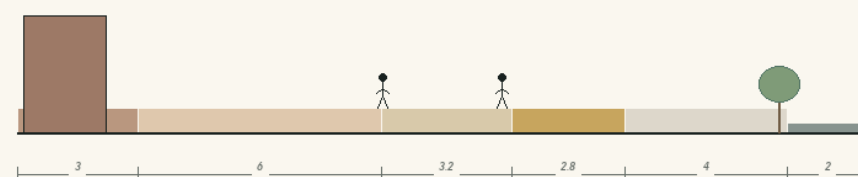


FF Step-free crossing

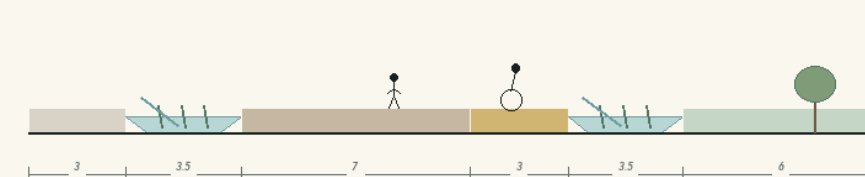

02 FROM NINE KILOMETRES TO ONE COURTYARD

One long line, three urban districts, three everyday scales

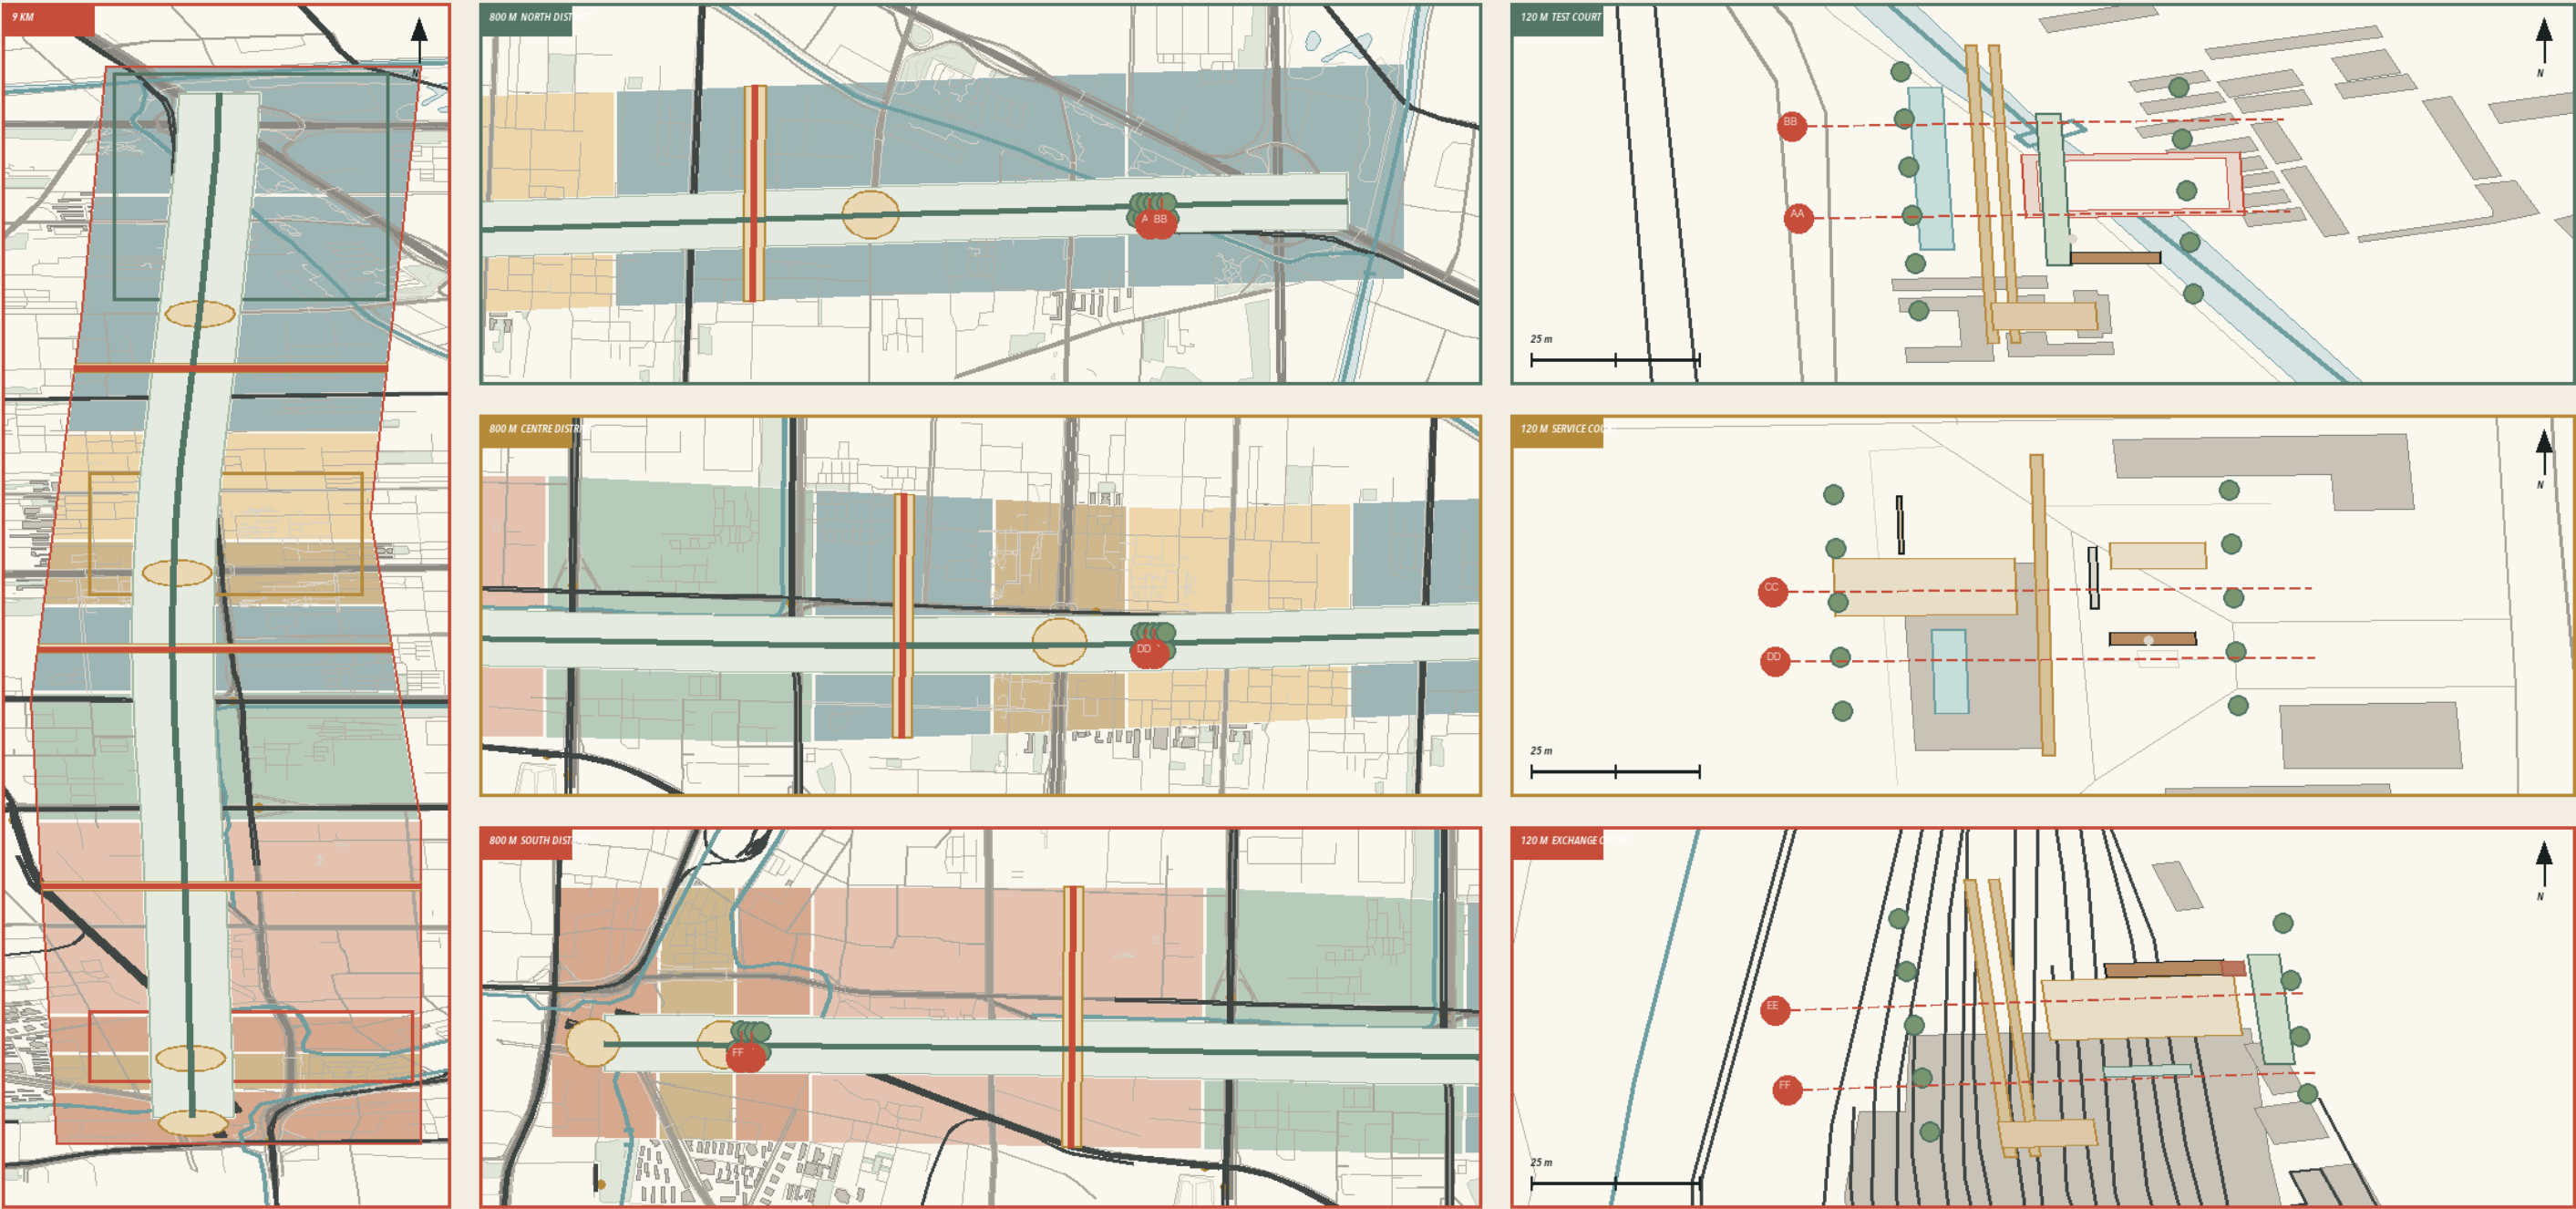


CONCEPT DESIGN PROVISIONAL BOUNDARY OSM FOR CONTEXT ONLY


Scale structure informed by REN AXIS (CC BY 4.0); redrawn for this proposal




01 Zhongzhiyuan Test Court

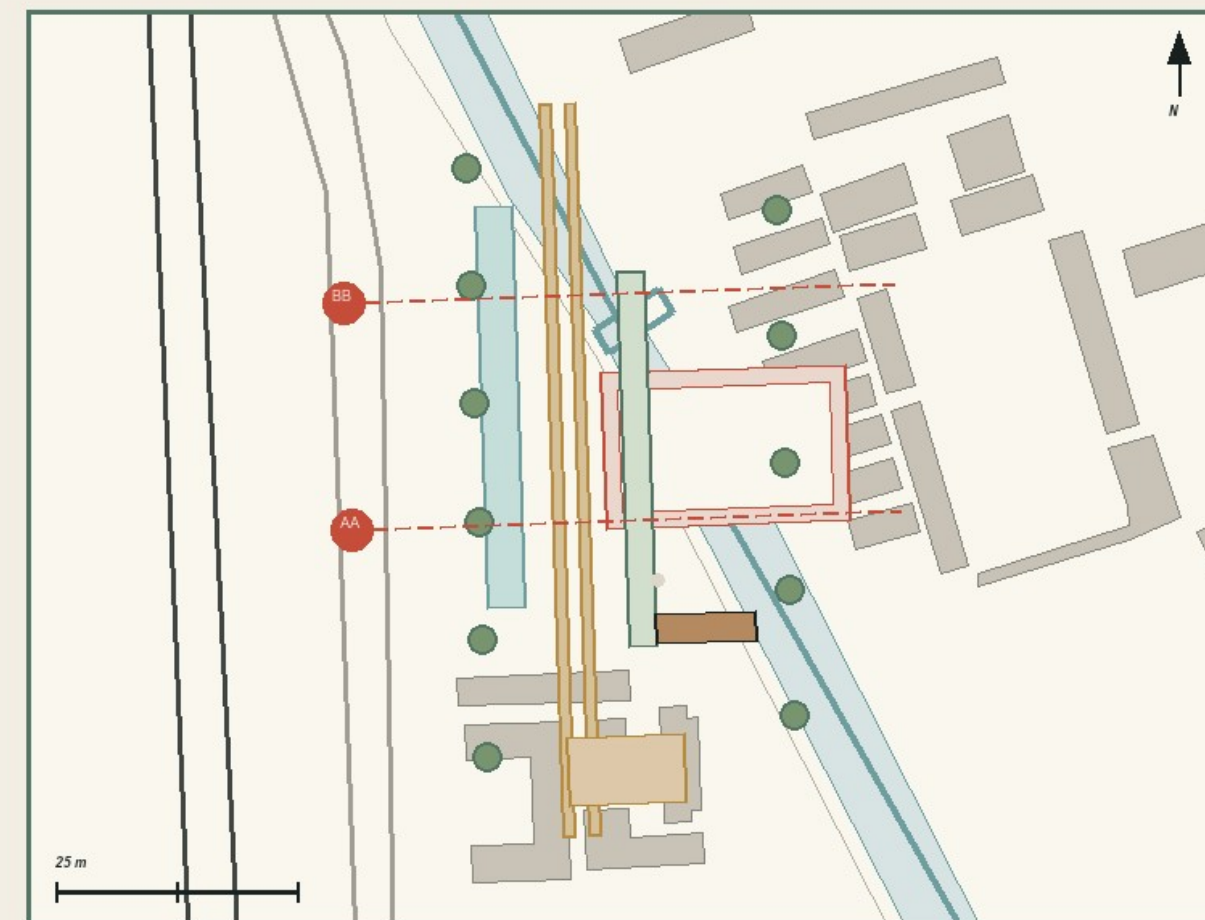

AA Public edge at the test court

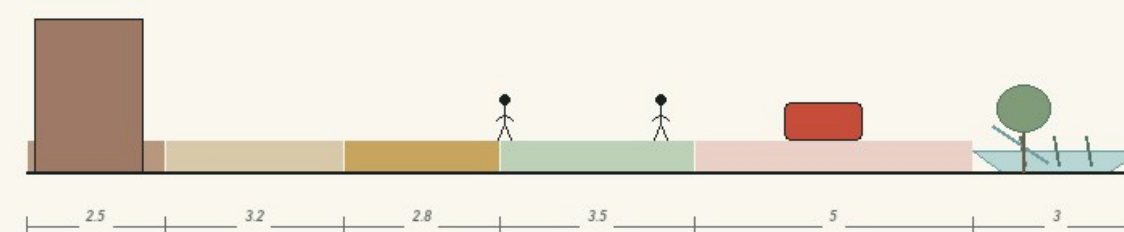

BB Xiaoyuehe link



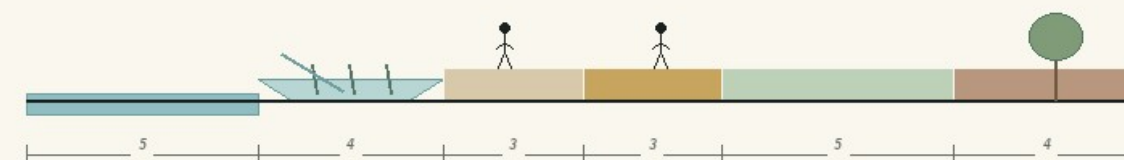


PUBLIC WALK SLOW CYCLE RAIN GARDEN REVERSIBLE

CONCEPT DESIGN. PROVISIONAL BOUNDARY. ONLY FOR REFERENCE ONLY.




02 AI Origin Service Court

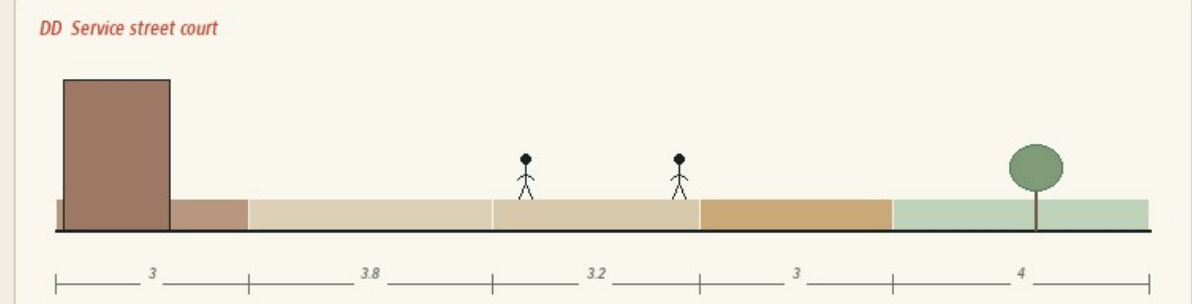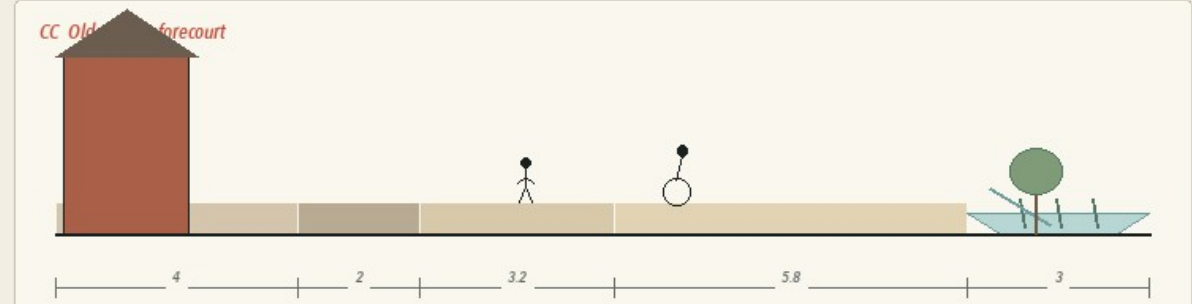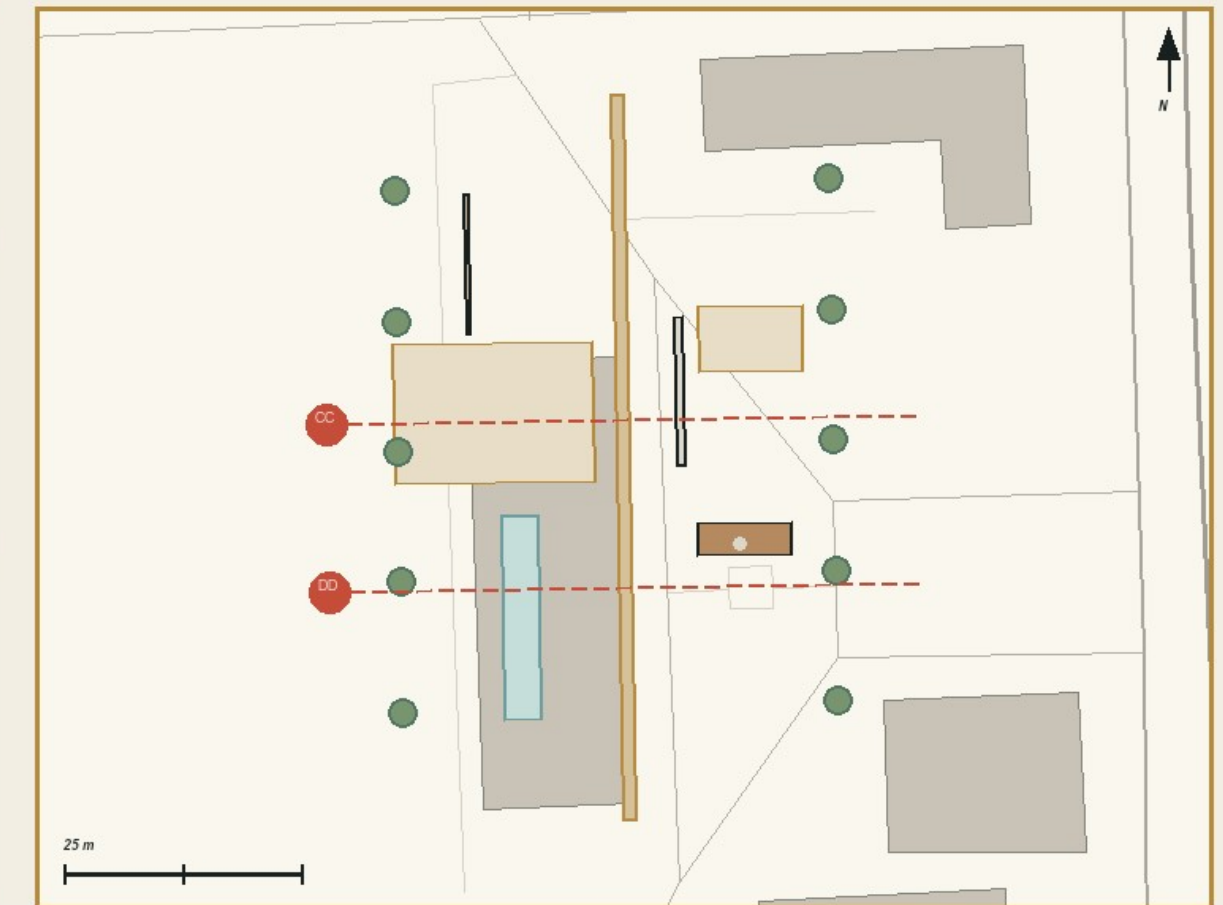


TEST EDGE




03 Dazhongsi Exchange Court

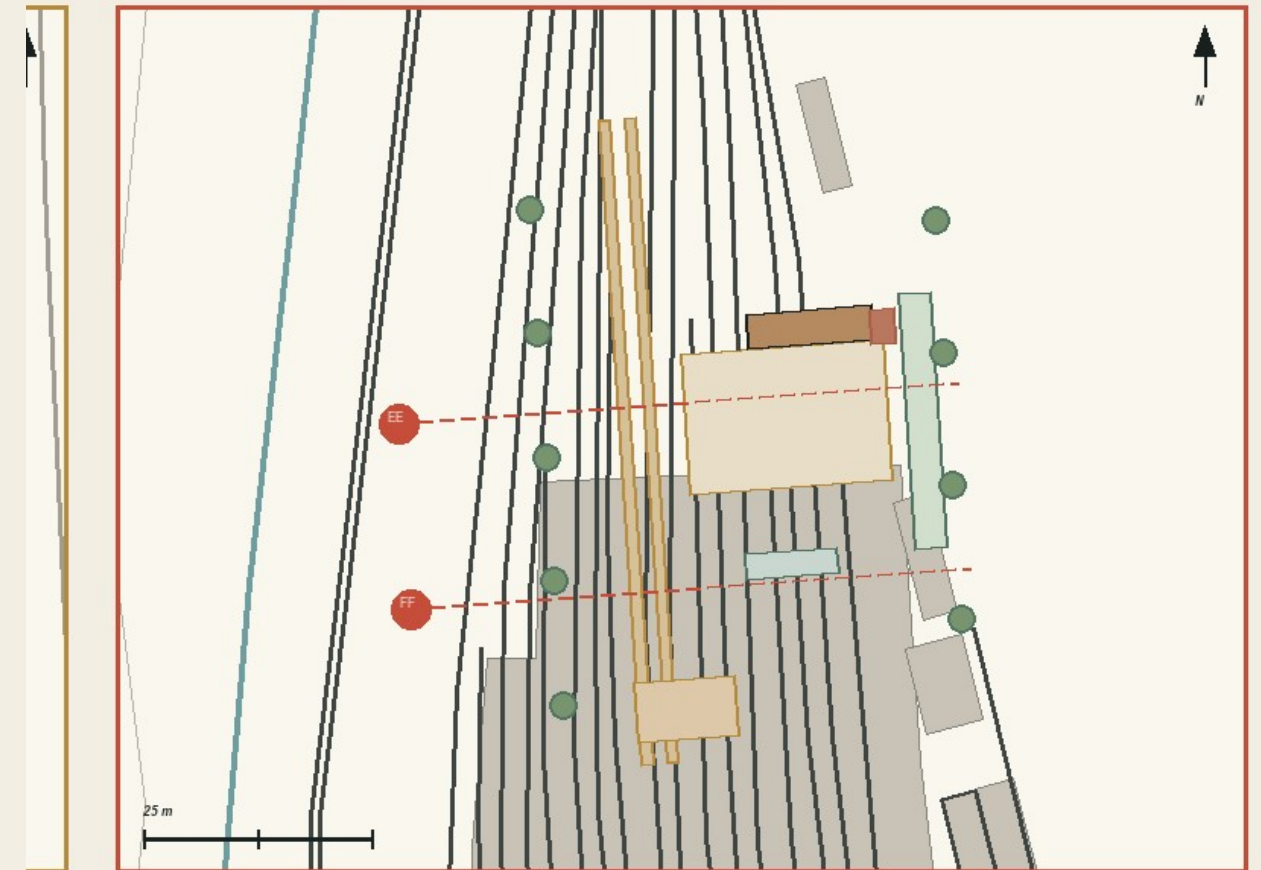

EE Daily edge at the exchange court

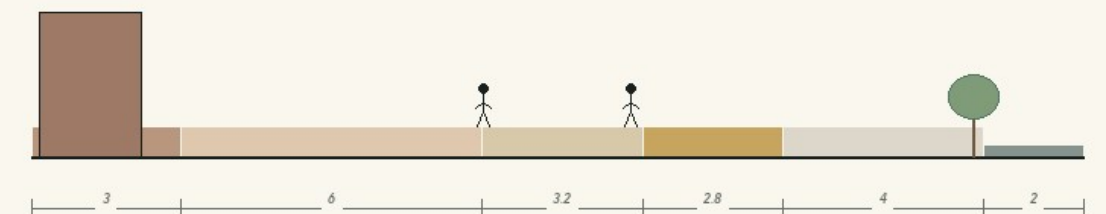

FF Step-free crossing

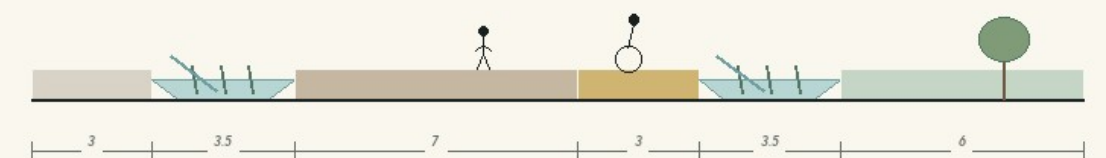



04 MOVEMENT, WATER AND SIX SECTIONS

Join public routes and encourage better planning for the future



CONCEPT DESIGN: PRELIMINARY BOUNDARY: CONCEPT ONLY

DESIGNER: JZ OPEN BELT


07 *EVERYDAY LIFE IN THREE COURTYARDS*

Three separate concept scenes tied to the viewpoints in the plans



PARK, THREE COURTYARDS

neighbourhood, water and stations meet along the public spine

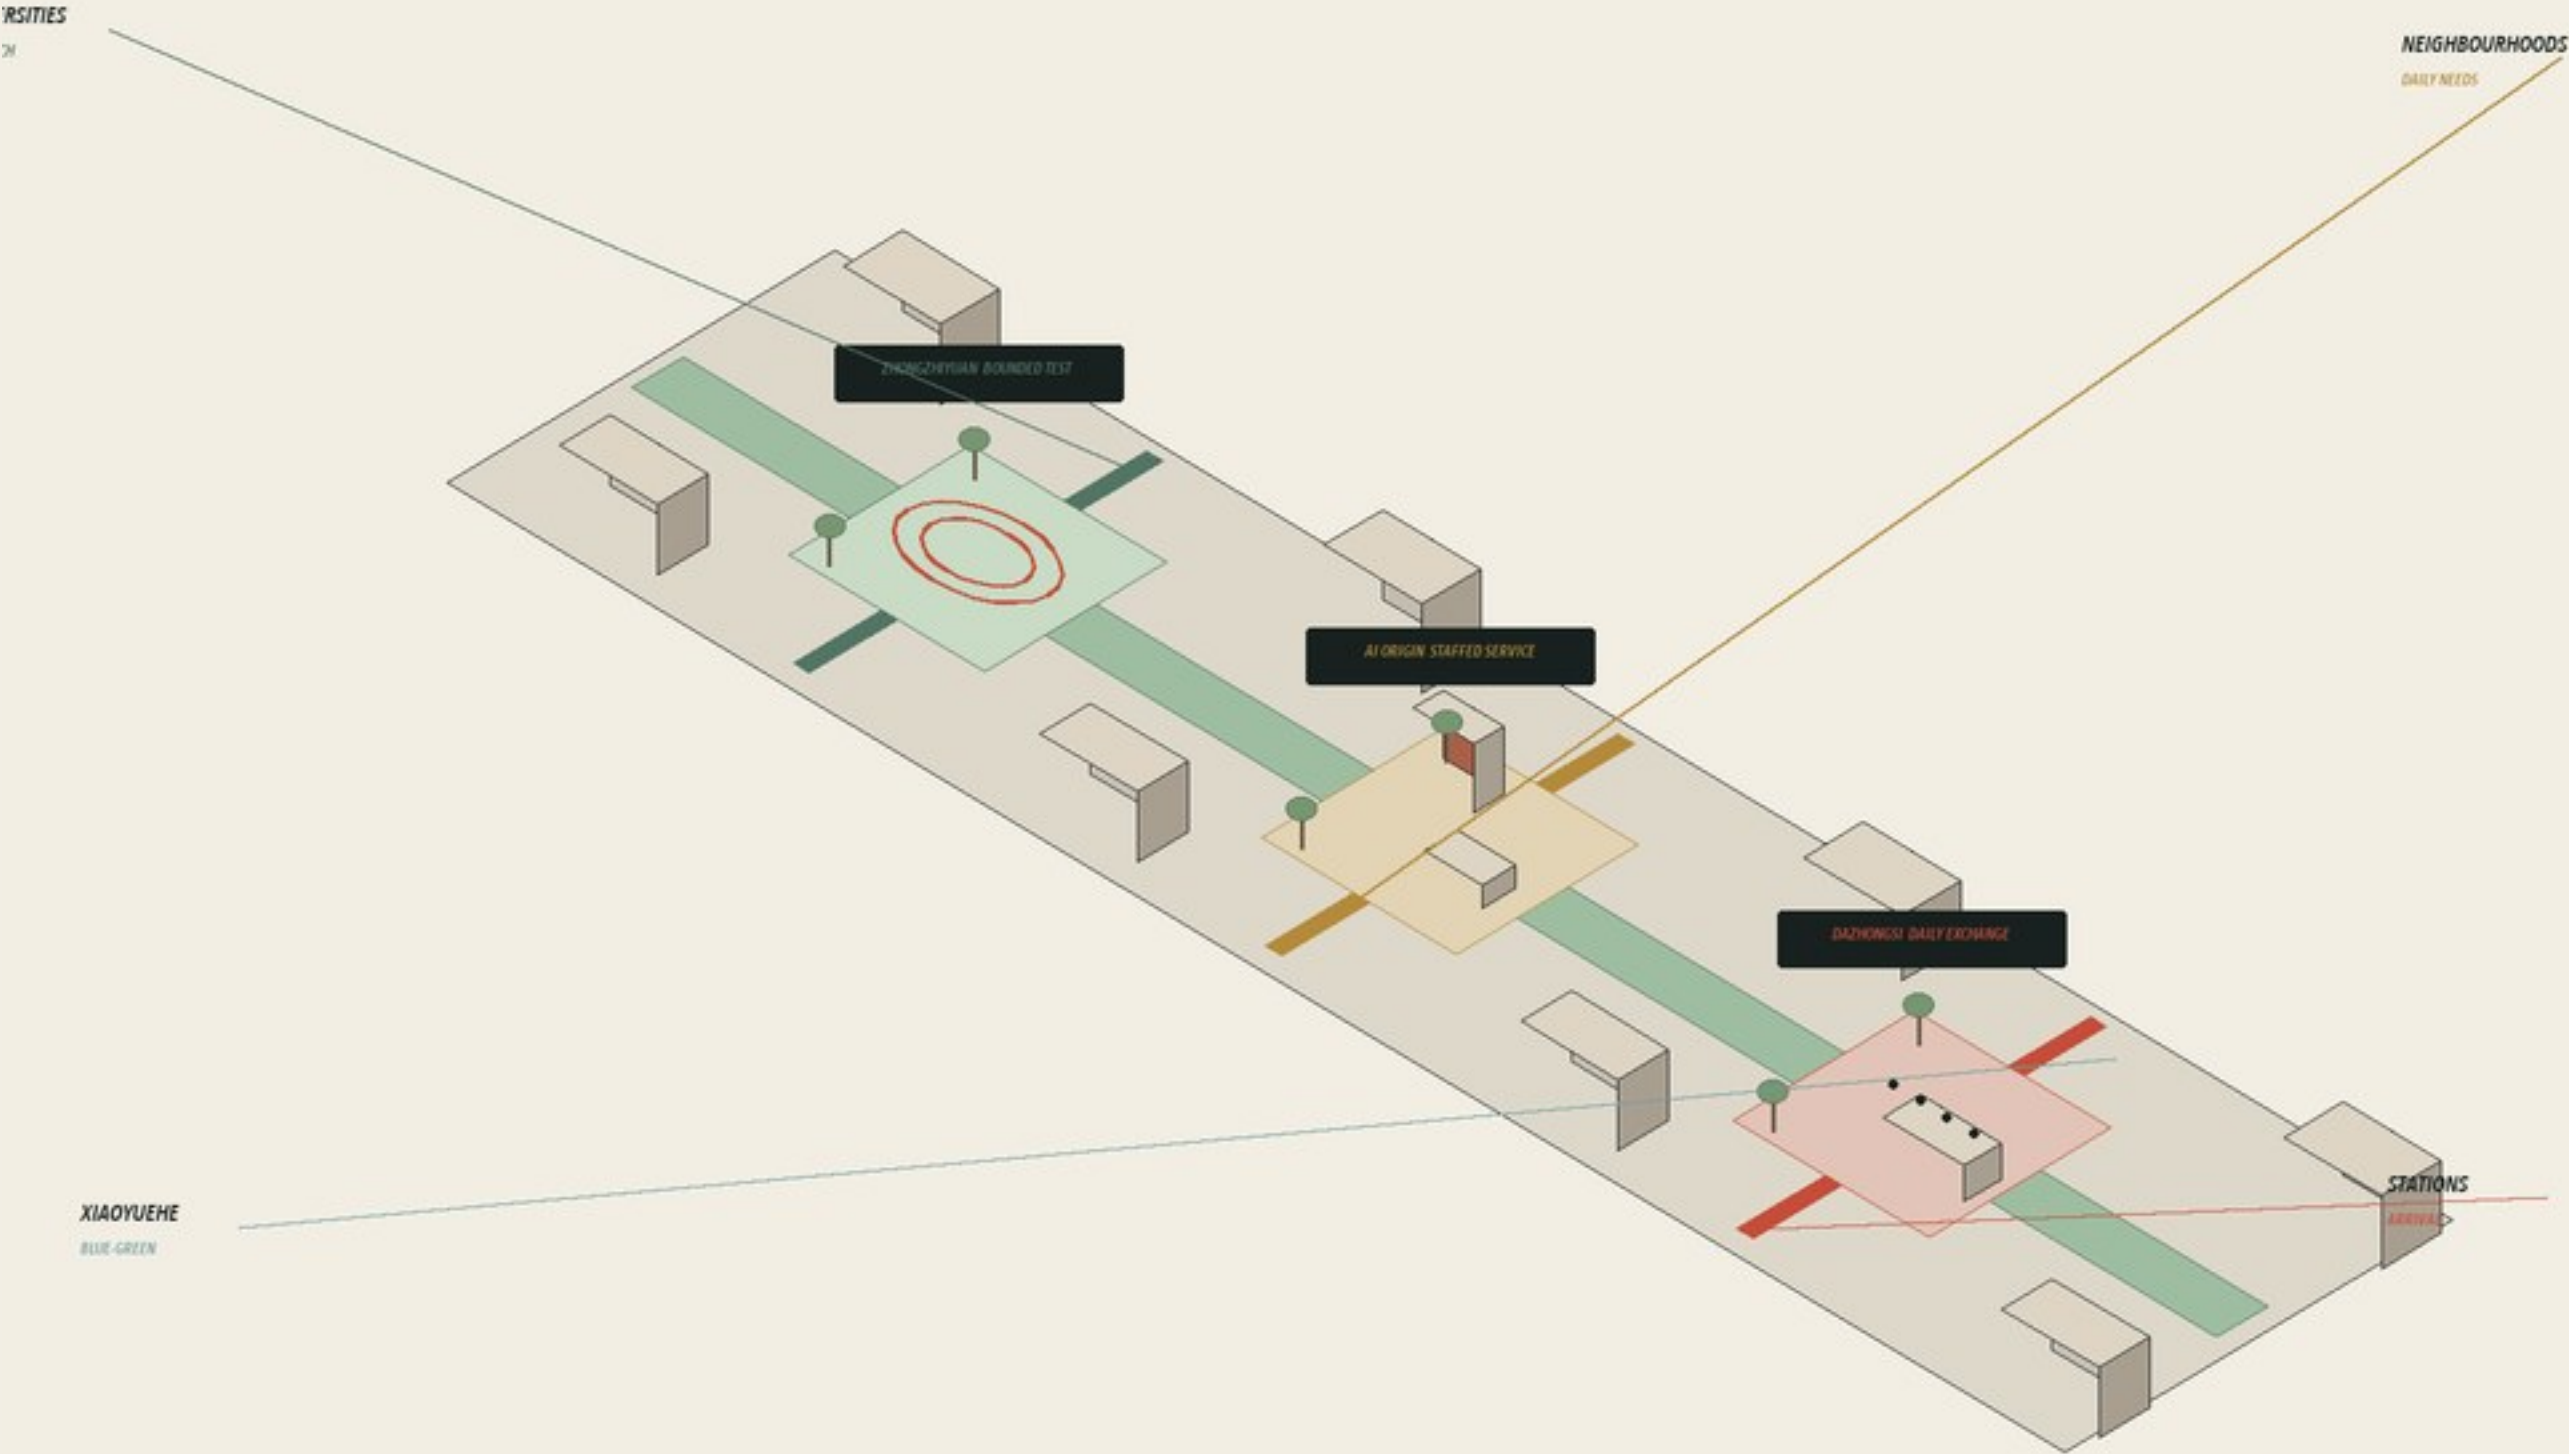


VISIONAL BOUNDARY OSM FOR CONTEXT ONLY

Spatial axonometric Concept relations

08 REVERSIBLE, REPAIRABLE, REPLACEABLE

Eight components drawn to dimensions, materials and connections

C01 Shade canopy

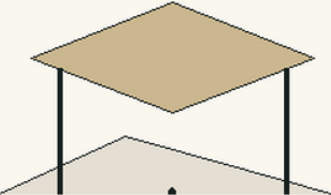

bolted steel columns, replaceable timber slats, screw piles

6 × 3 × 3.2 m

C02 Three-height bench



replaceable timber boards on galvanized frames

3.6 × 0.7 × 0.55 m


C03 Rain-garden edge



open curb, gravel trench, clean-out sump

6 × 2.4 × 0.45 m

C04 Heritage reading rail

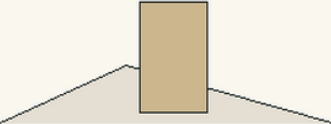

reused rail base and replaceable non-digital panel

2.4 × 0.45 × 1.15 m


C05 Staffed service table



lockable timber modules and movable stools

2.4 × 0.8 × 0.75 m


C06 Visible test edge

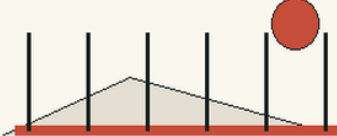

bolted low steel rail, red stop marker, no opaque fence

4 × 0.25 × 0.9 m


C07 Staff call post

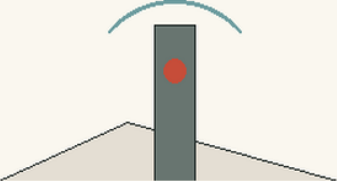

low-voltage button, tactile marker, staffed response





0.35 × 0.35 × 1.35 m

C08 Shielded night light

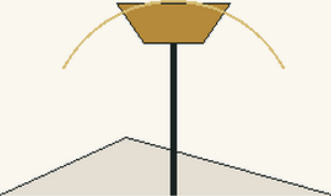

replaceable warm lamp, shielded optic, timed circuit

0.35 × 0.35 × 3.6 m

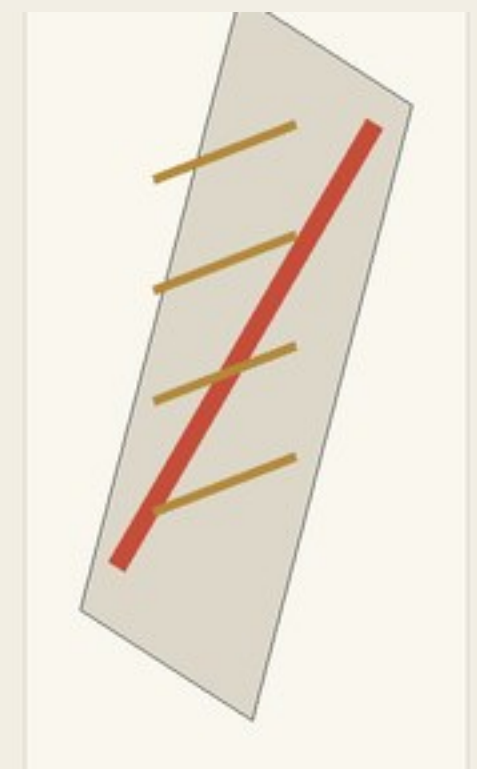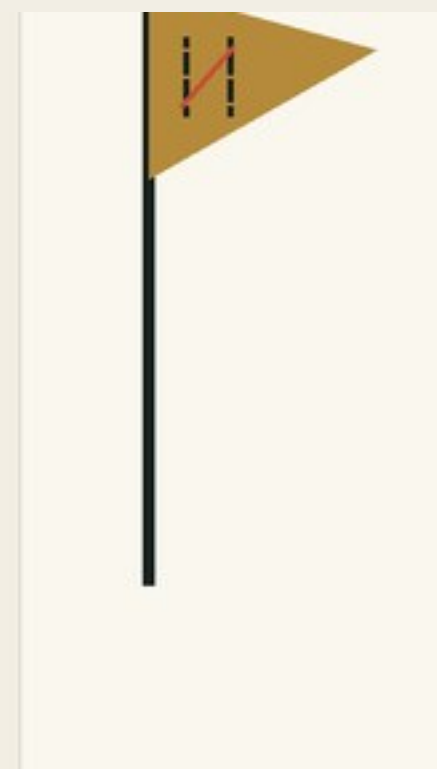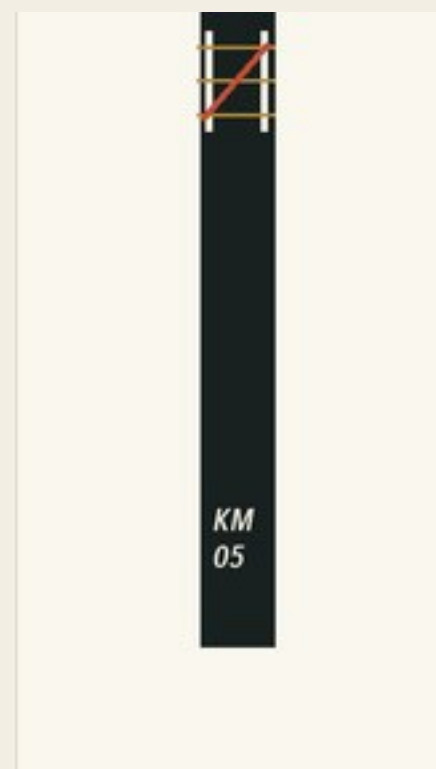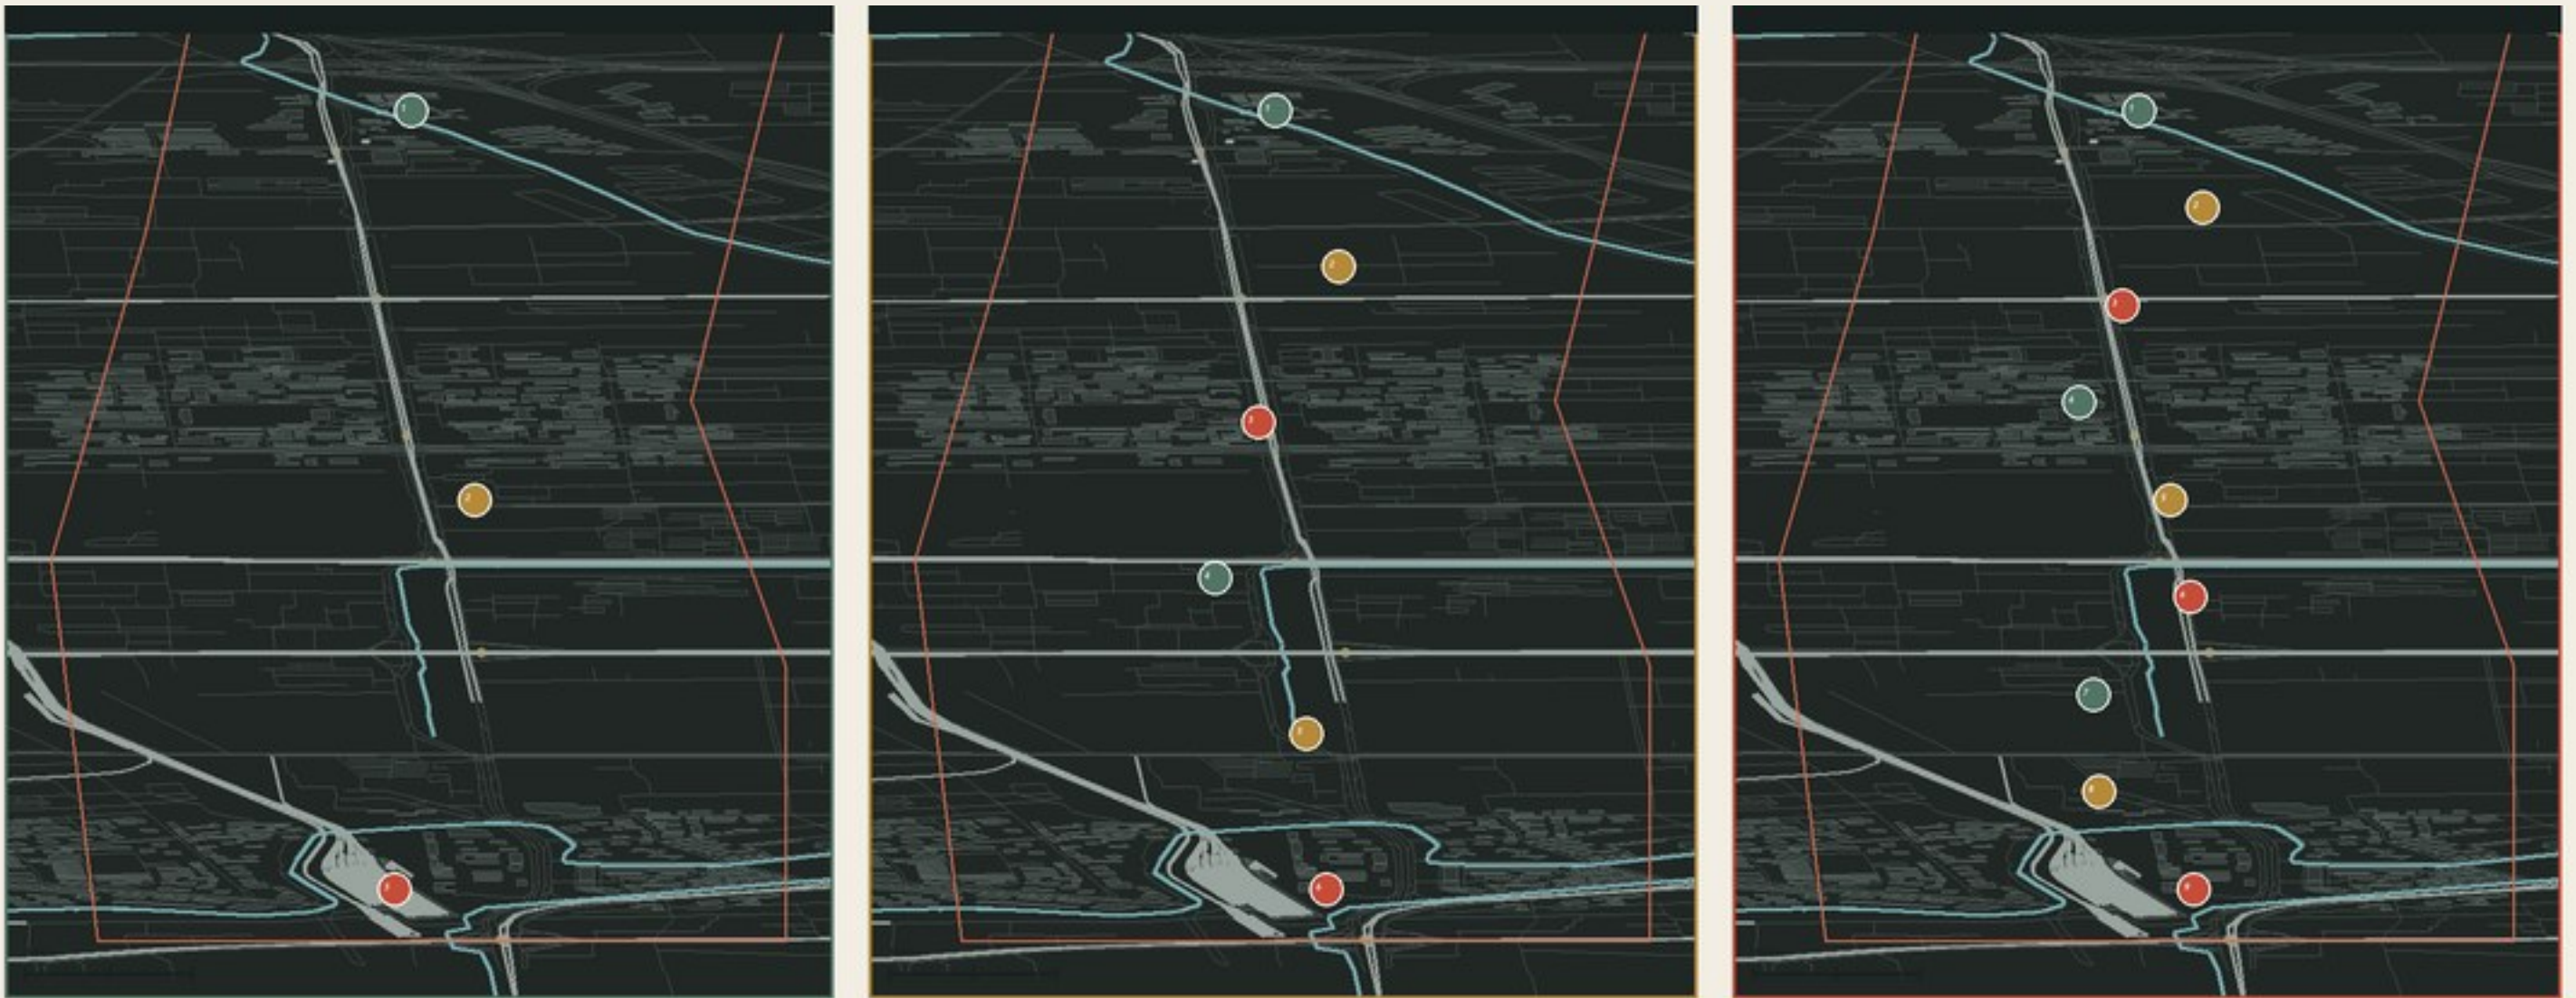

05

SPATIAL MEASUREMENT

Three pilots measured with one rule; numbers stay at the edge of the drawing



3.2 m	2.8 m	3.5 m	500 m	14 / 6	9
CLEAR WALK	SLOW CYCLE	TEST BUFFER	REST CHECK	SCENES / TESTS	FIRST PROJECTS

PUBLIC PROJECT STATUS ☐ OSM CONTEXT ☐ PROVISIONAL GEOJSON ☐ FIELD REMEASURE

TO VERIFY official boundary, title, utilities, exact heritage controls, statutory intensity