




ONE LINE THREE COURTS SIX ROOMS

把九公里公园接回日常

01 总体设计图册

九公里折成三幅城市图，已建、公开计划与本案增量同图阅读

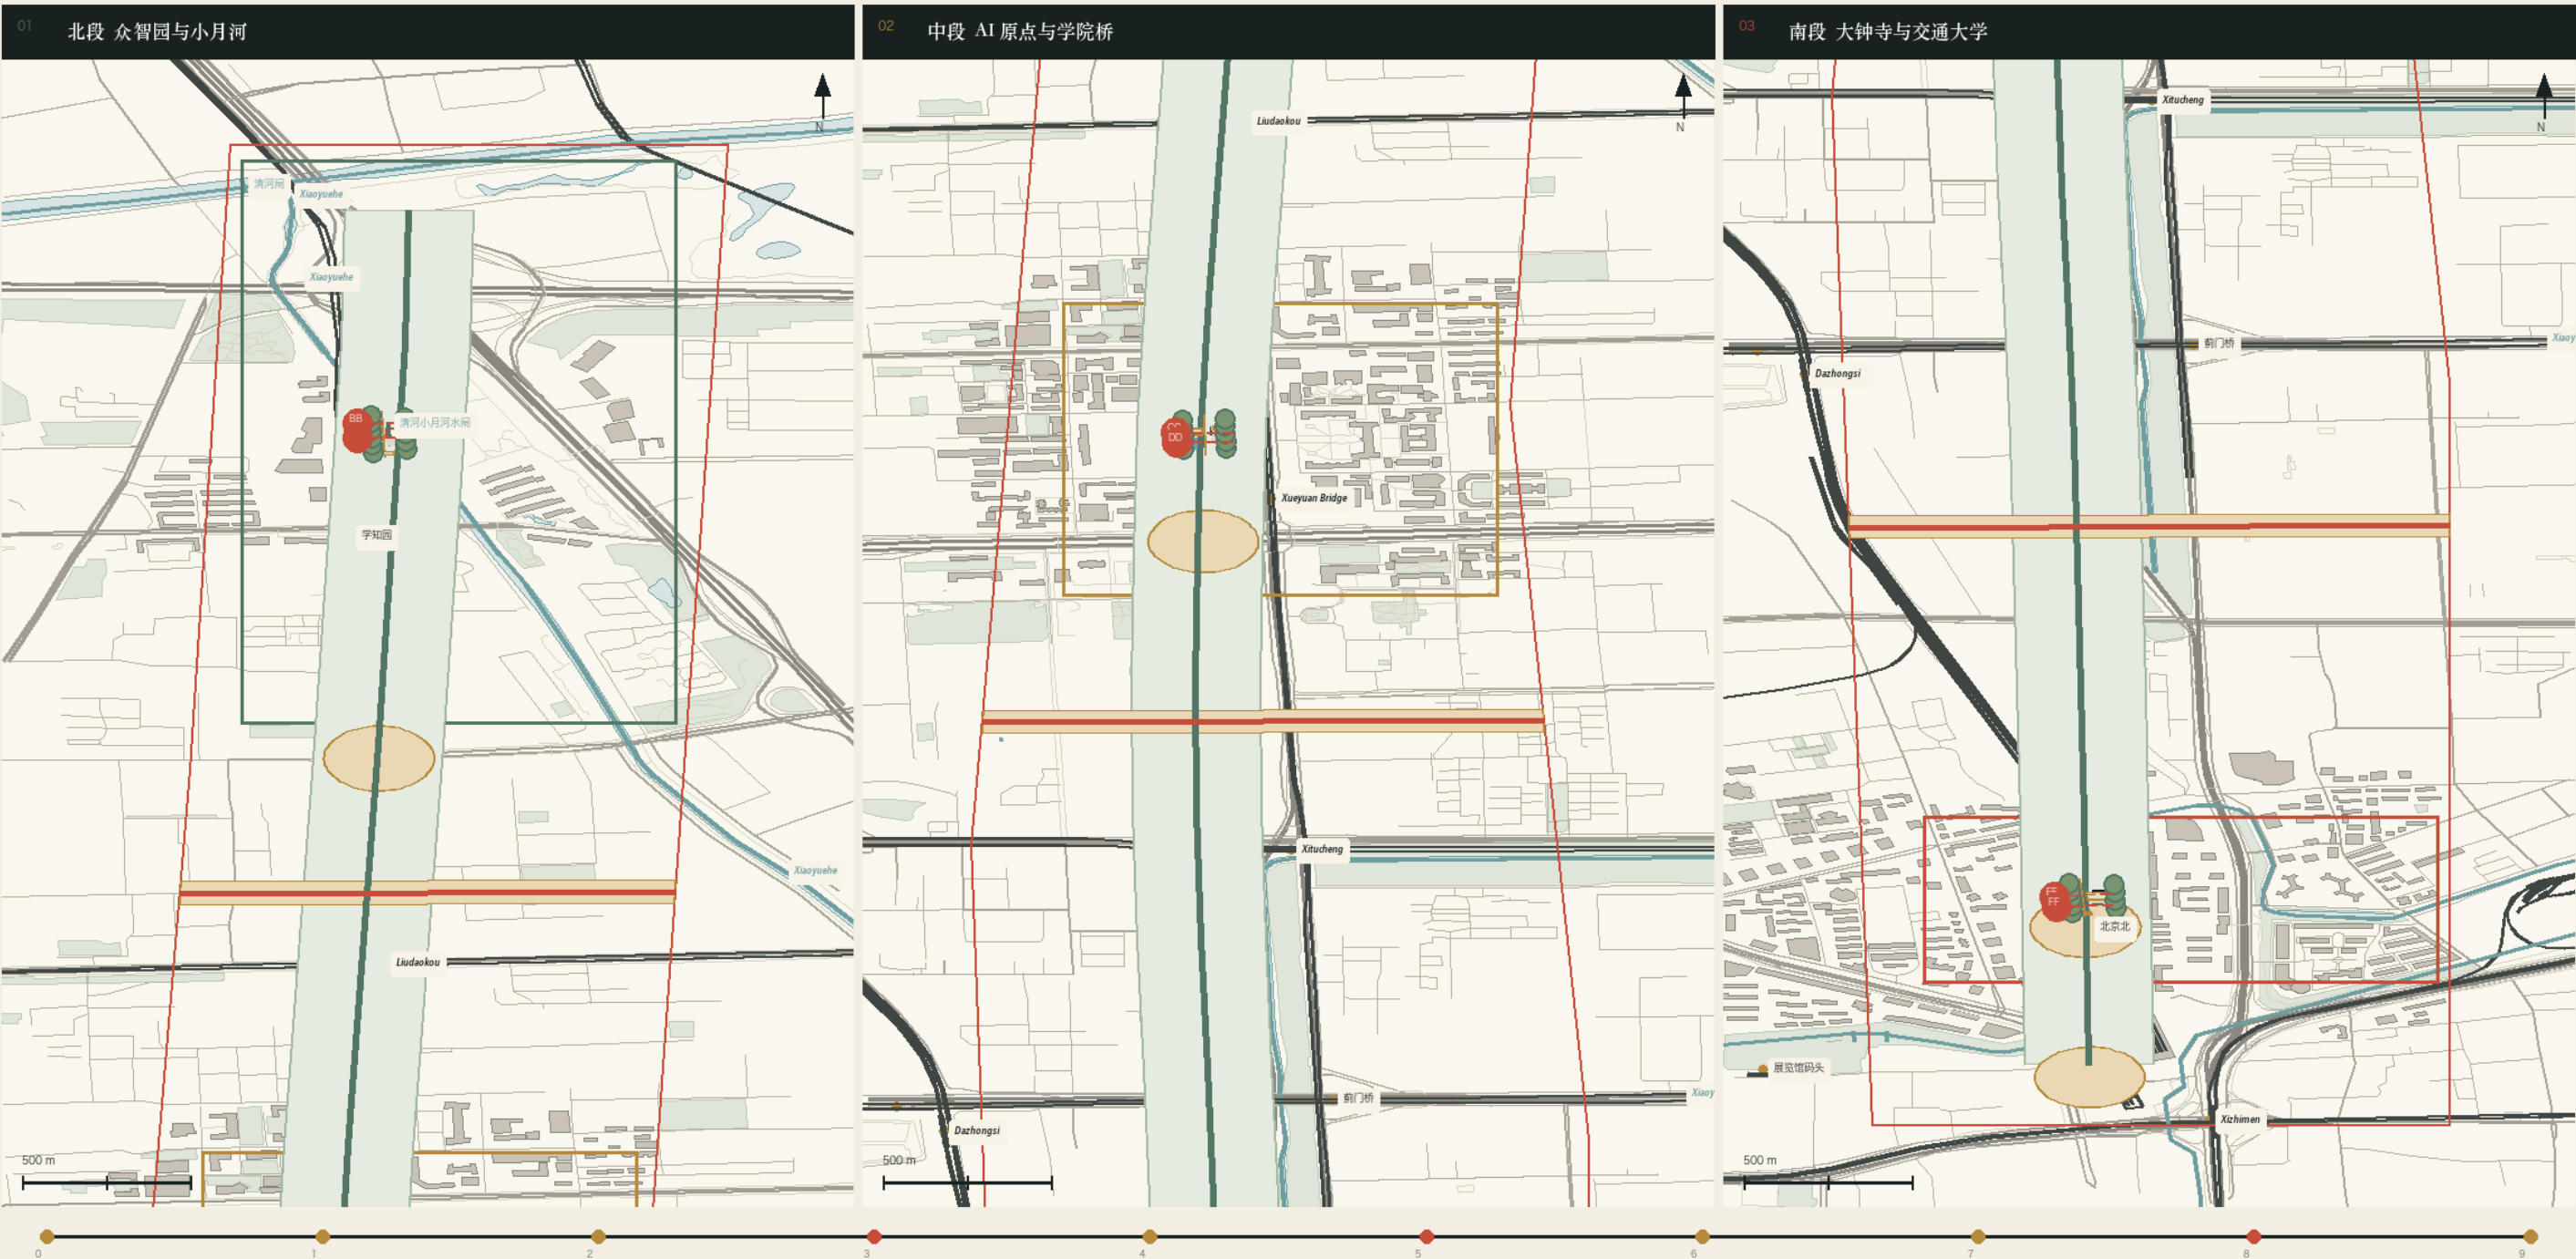




概念方案 暂定边界 OSM 仅作参考

© OpenStreetMap contributors ODbL 1.0

03 三处重点地区




同一比例尺的平面、剖切线与日常界面

01 众智园试验院

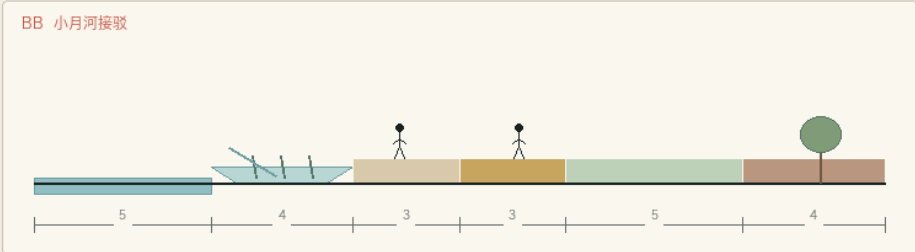
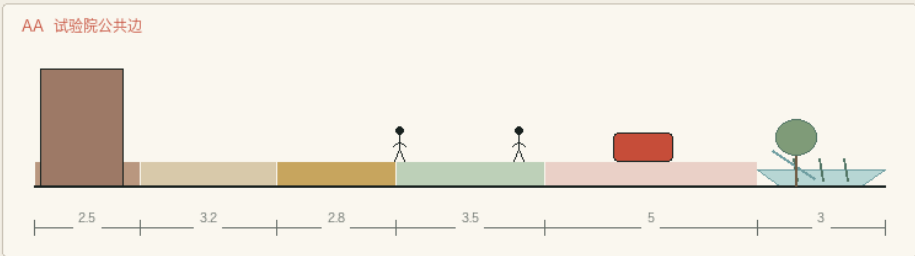
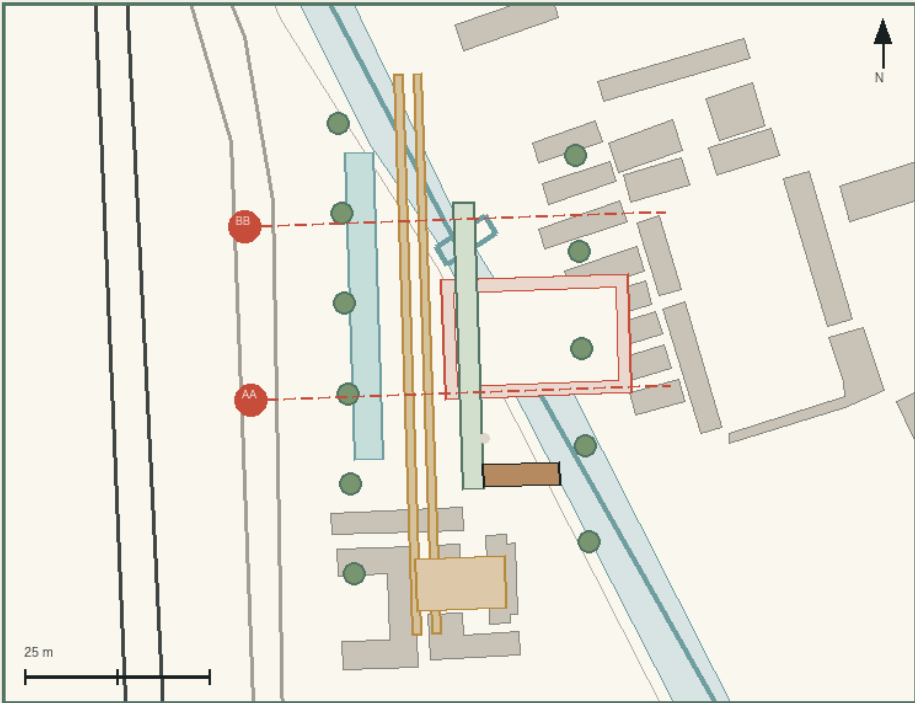


公共步行 慢骑 雨庭 可撤构筑 试验边

02 AI 原点服务院

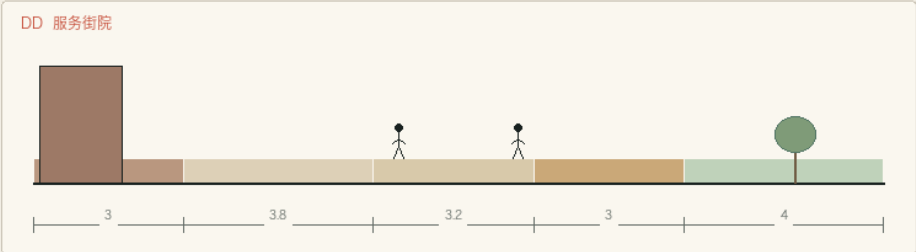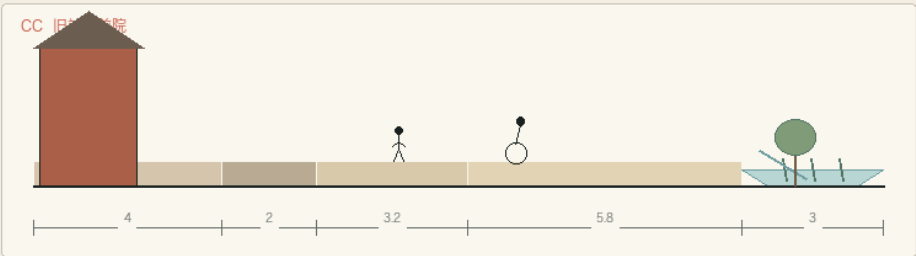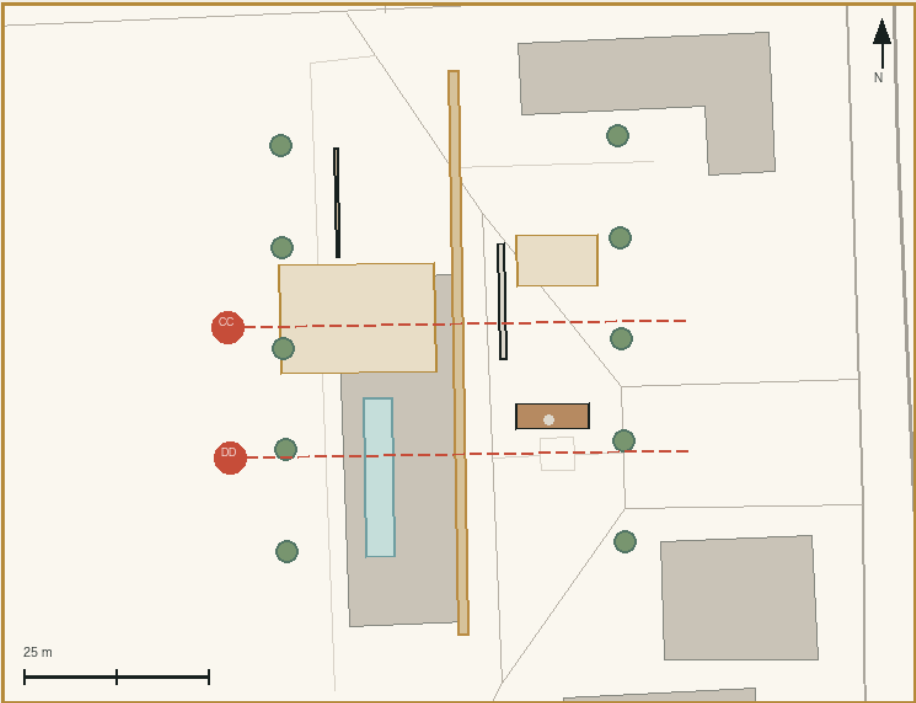

03 大钟寺交换院





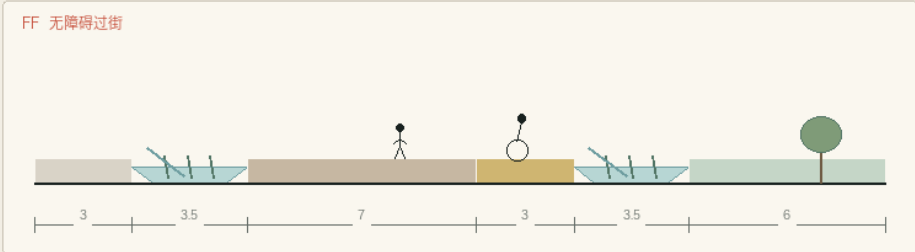
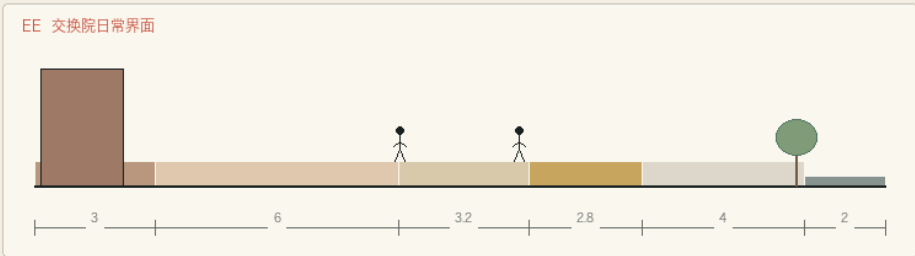
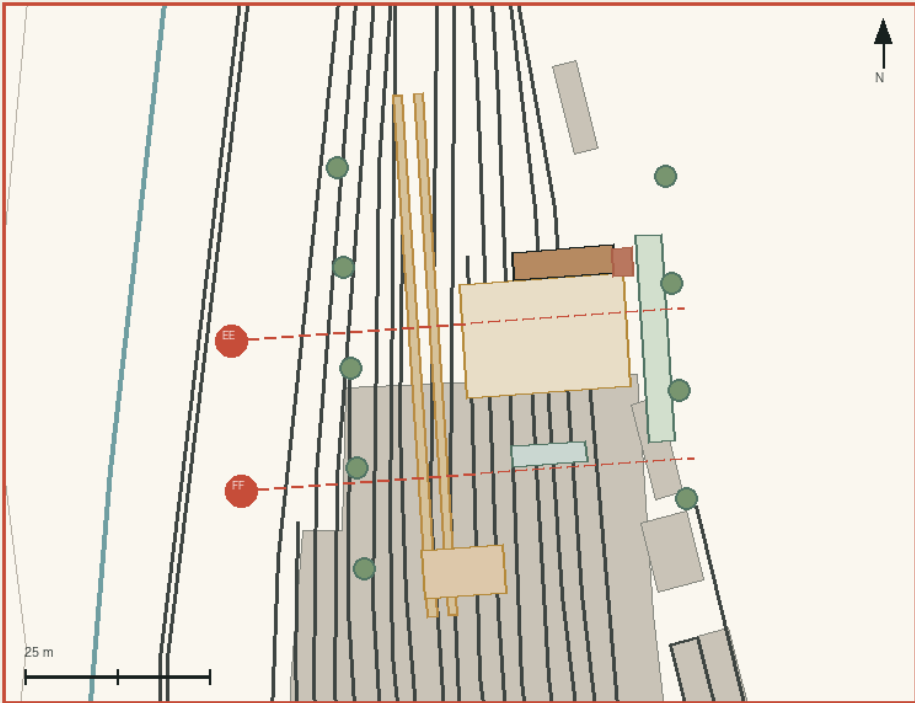


概念方案 暂定边界 OSM 仅作现状语境


Working dimensions Concept design 1:200 section logic

04 慢行、蓝绿与六条剖面

先把公共路线和过街接上，再布置试验与服务

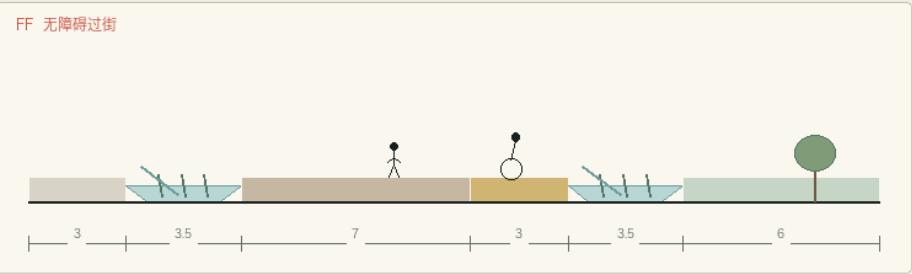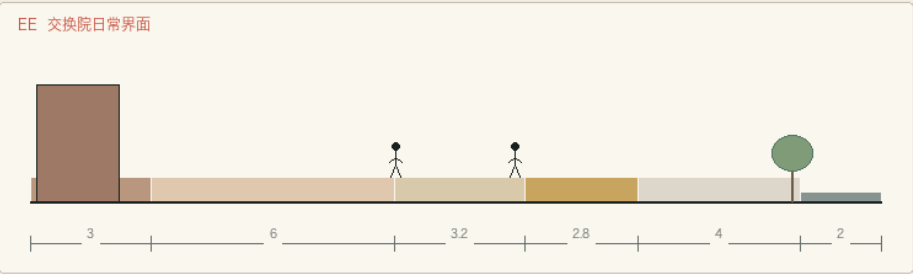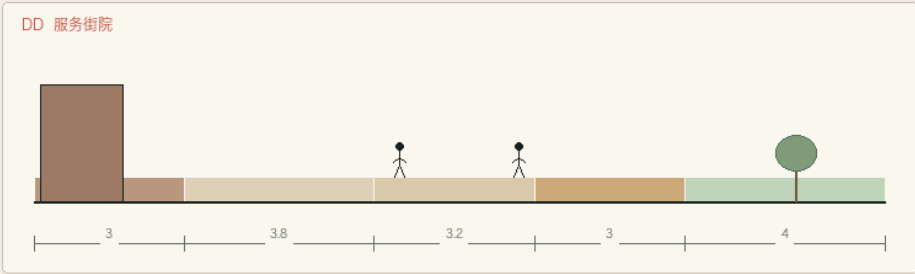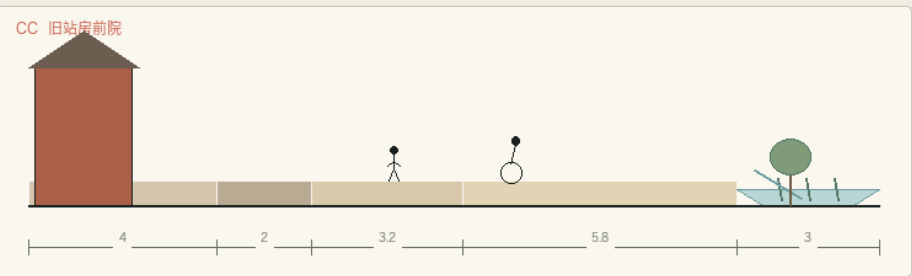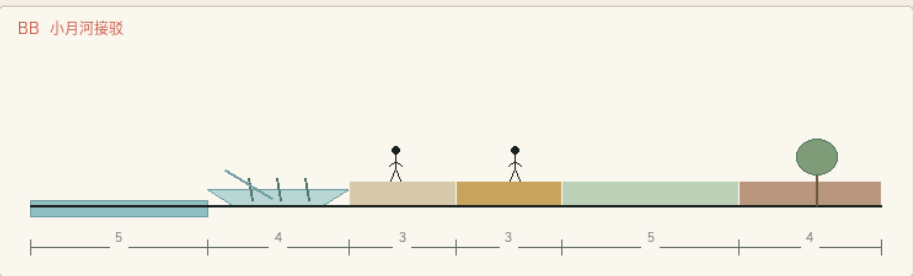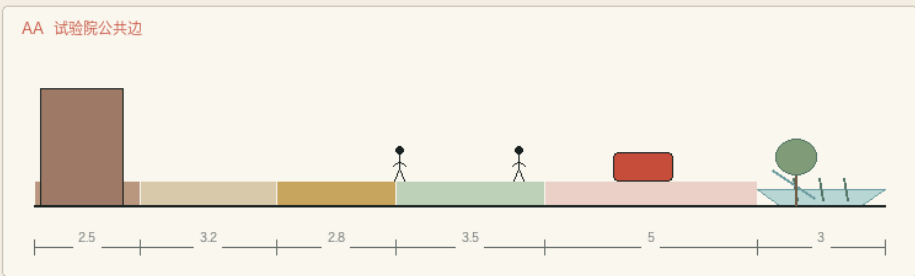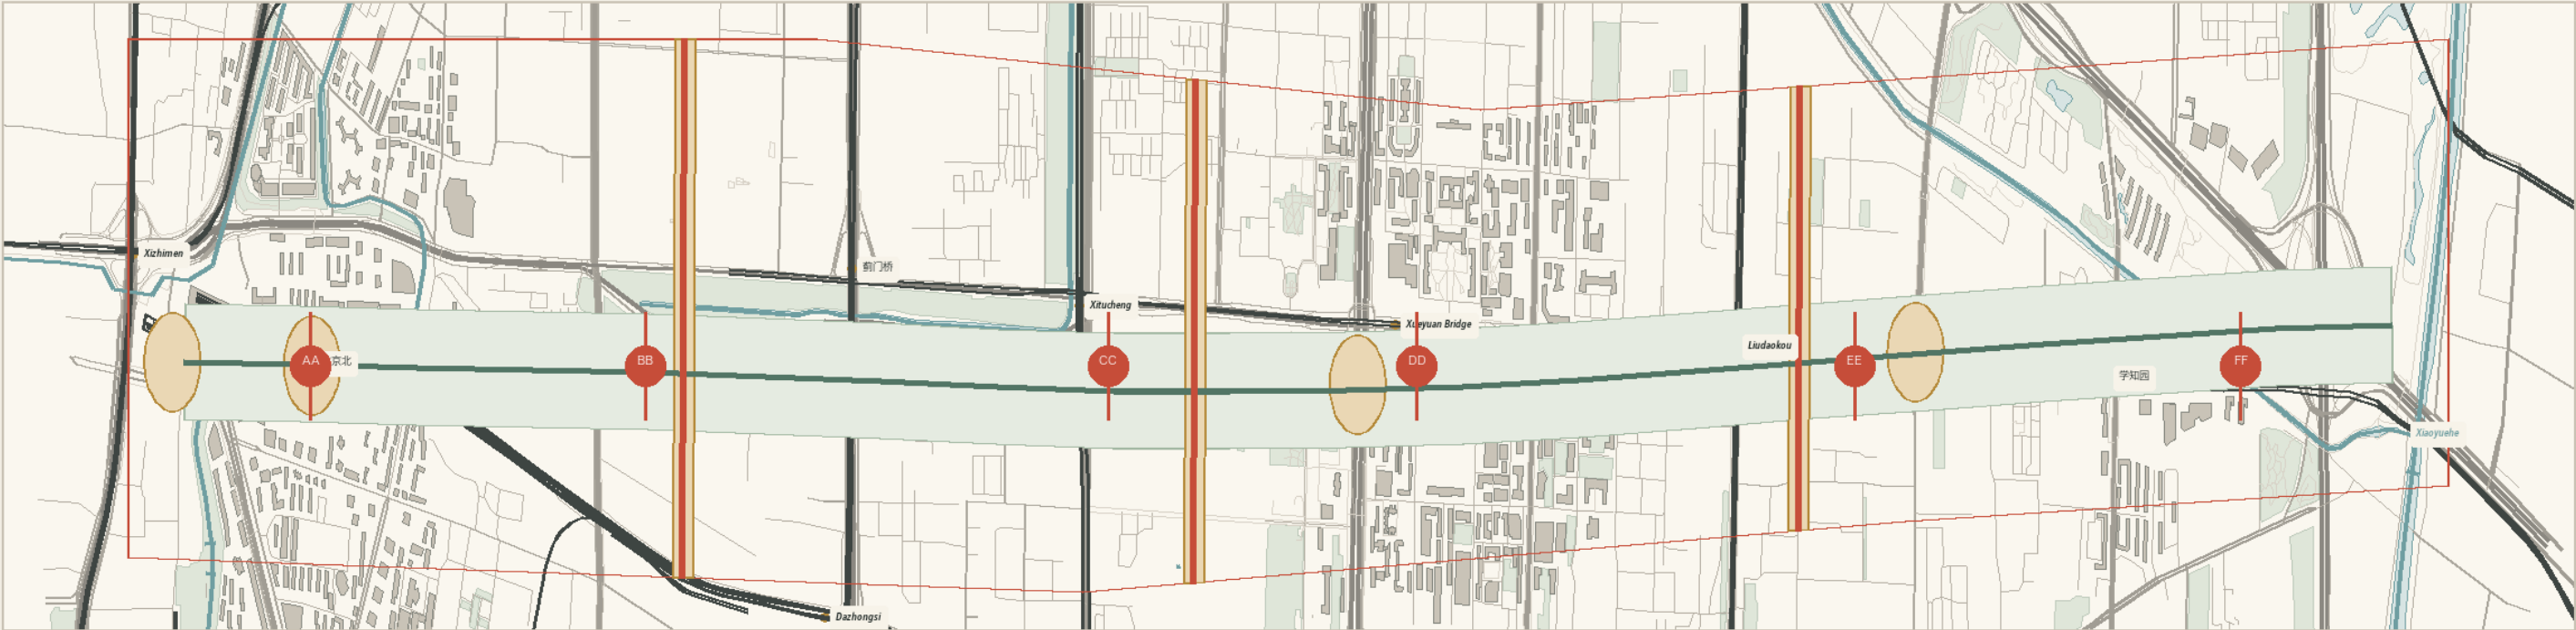

02 从九公里到一座院子
一张长线、三段街区、三个日常尺度

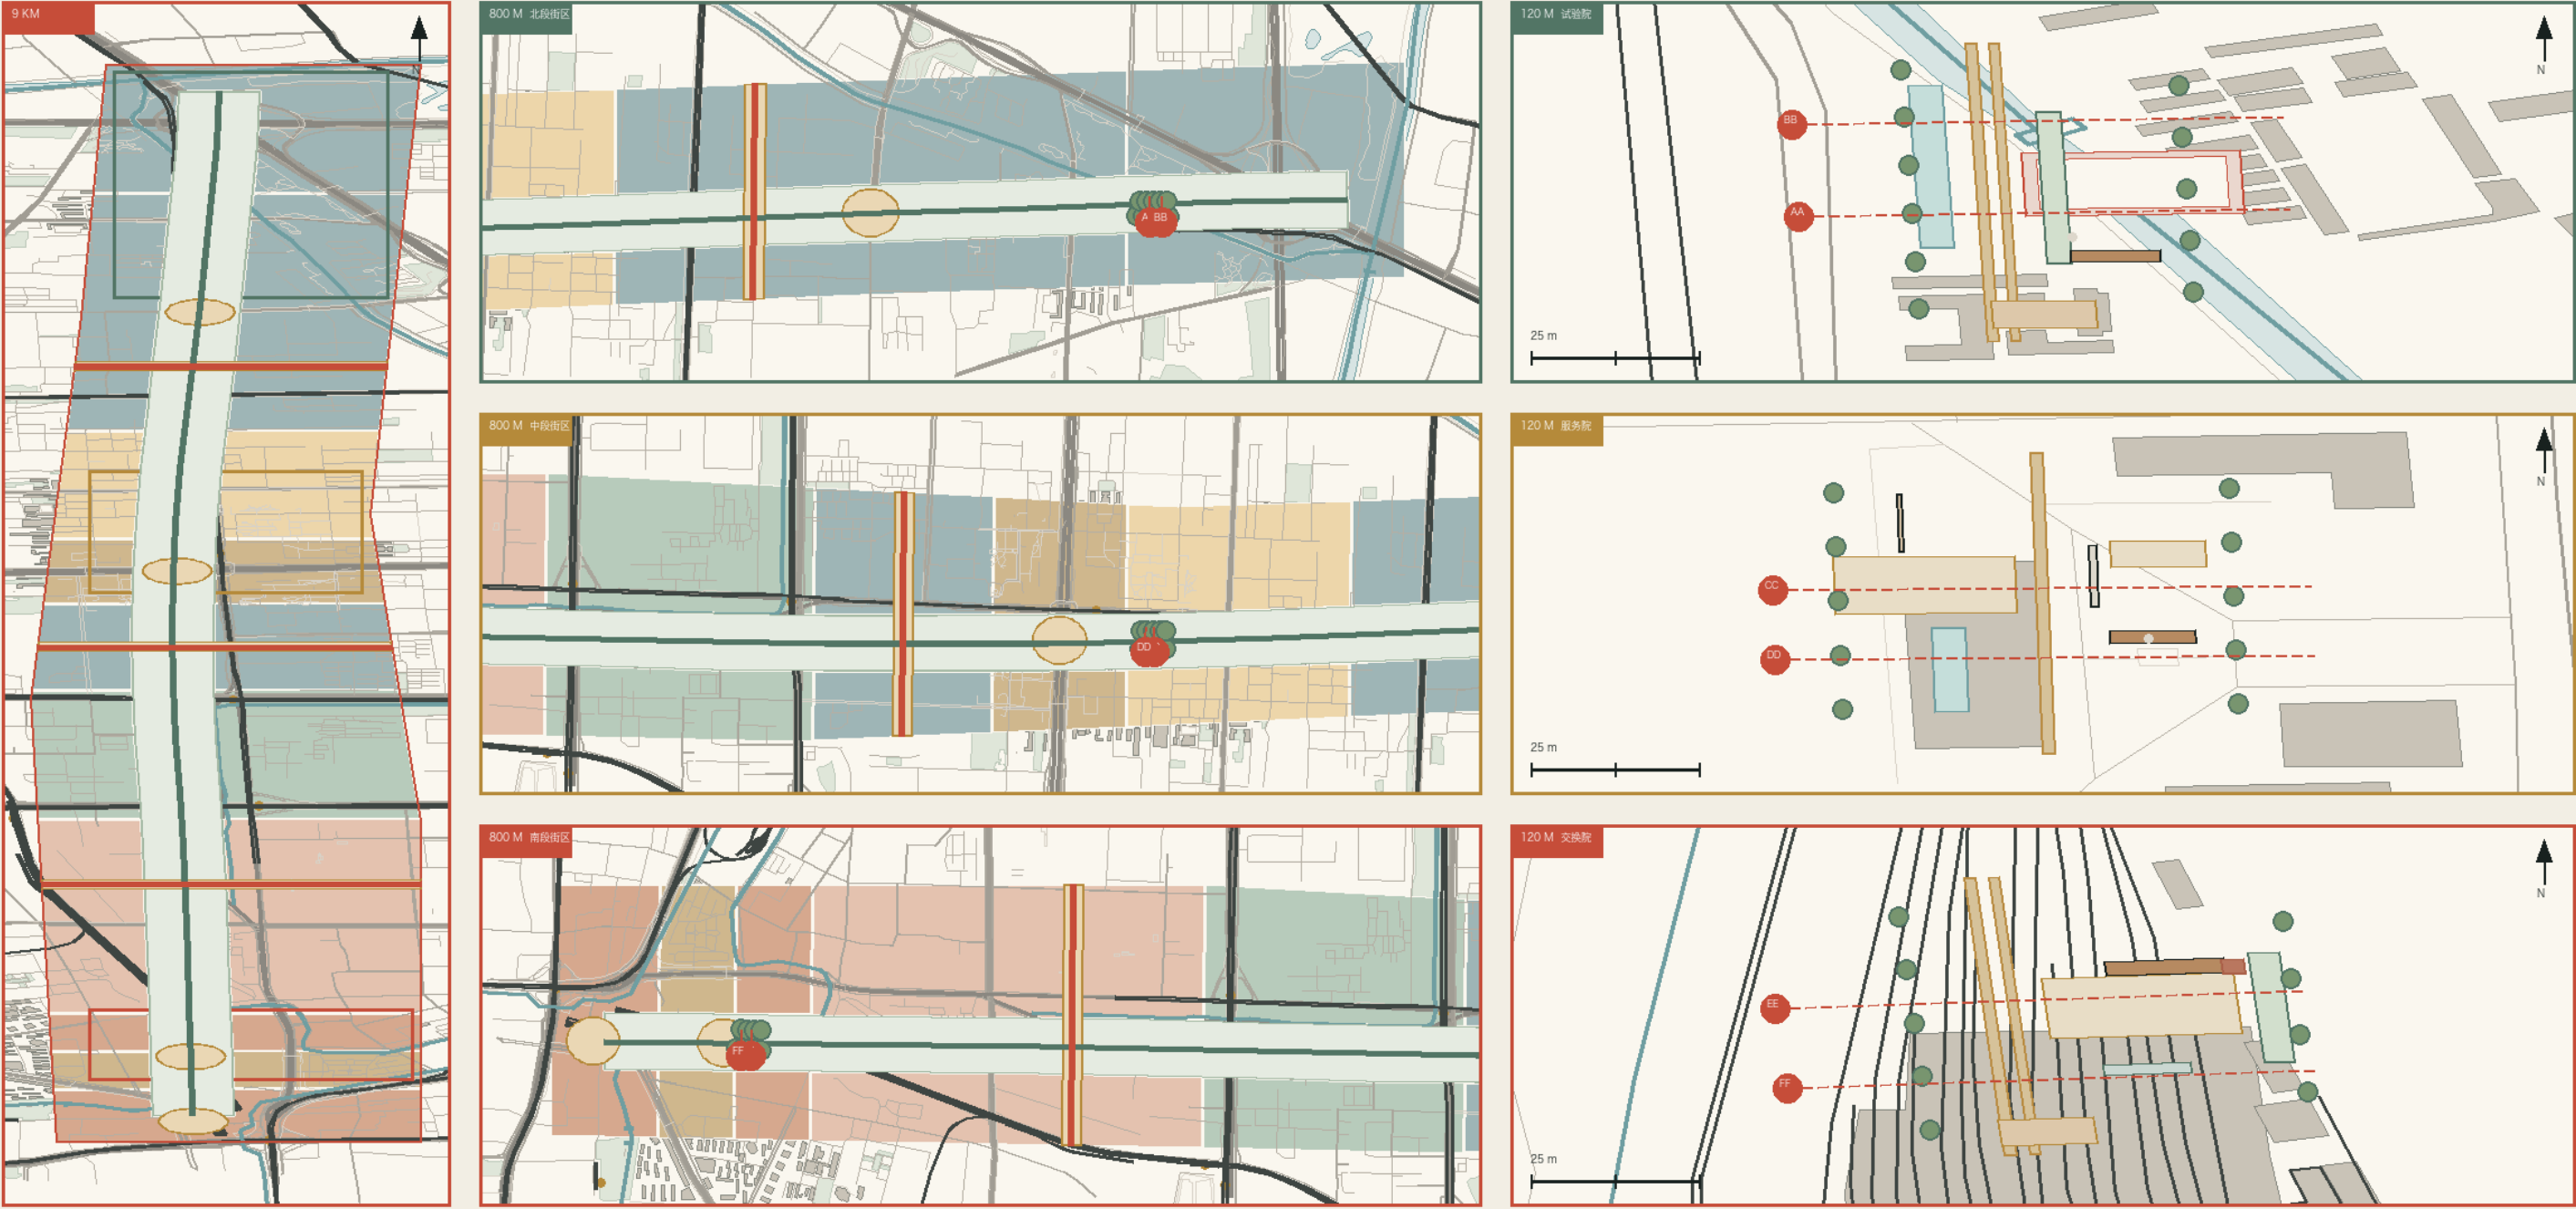


概念方案 暂定边界 OSM 仅作参考语境


Scale structure informed by REN AXIS (CC BY 4.0); redrawn for this proposal




01 众智园试验院

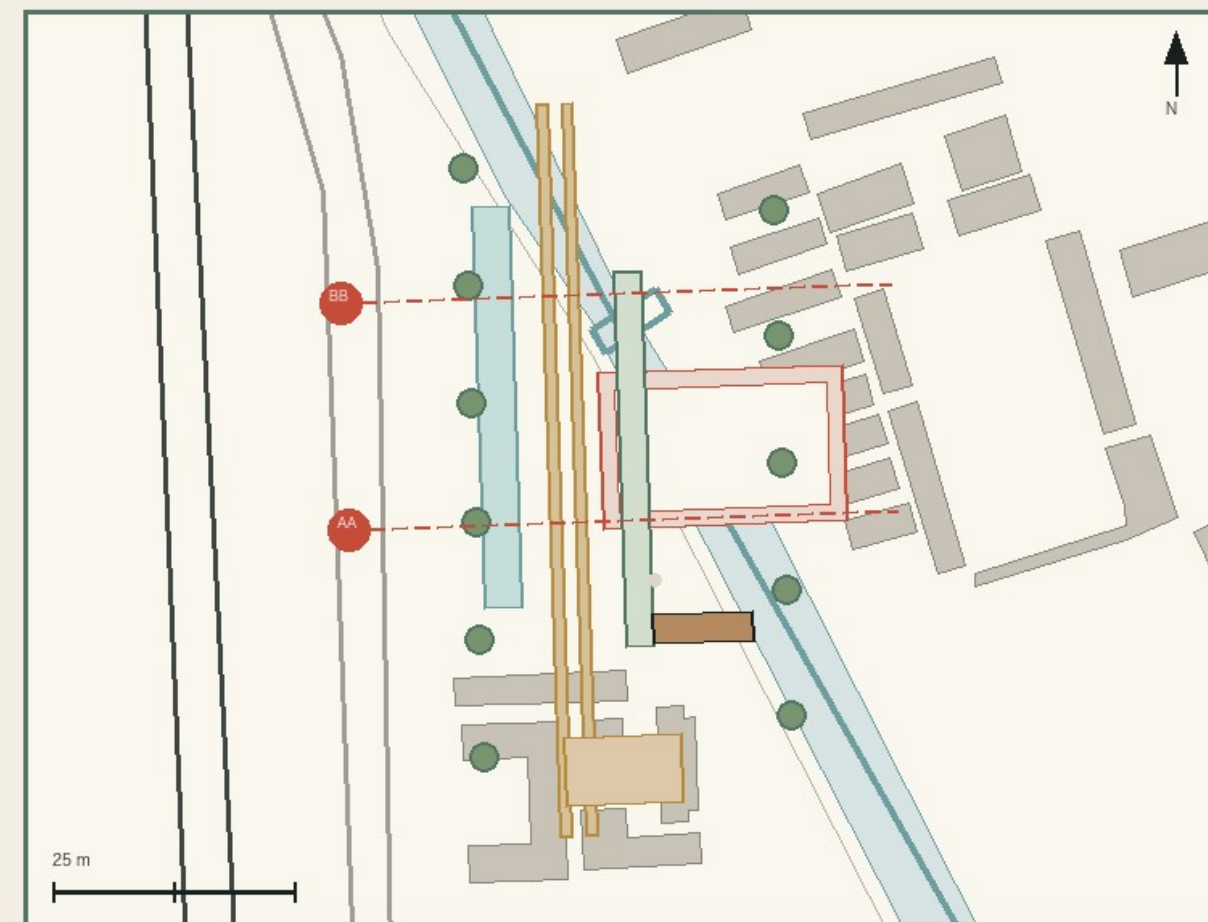

AA 试验院公共边

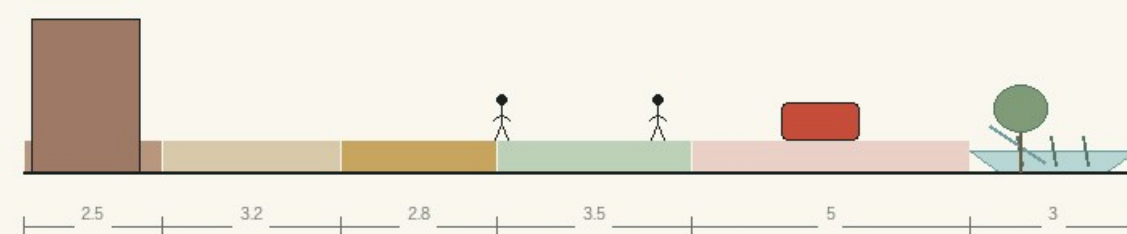

BB 小月河接驳



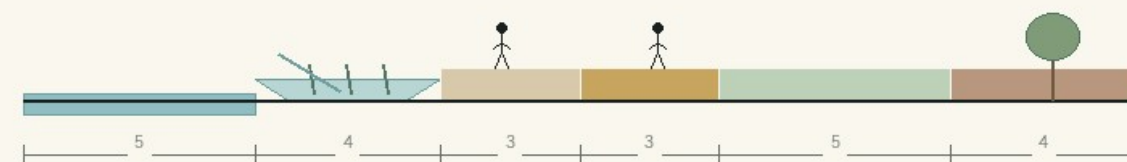


公共步行 慢骑 雨庭 可撤构筑 试验边

概念方案 众智园 众智园试验院




02 AI 原点服务院

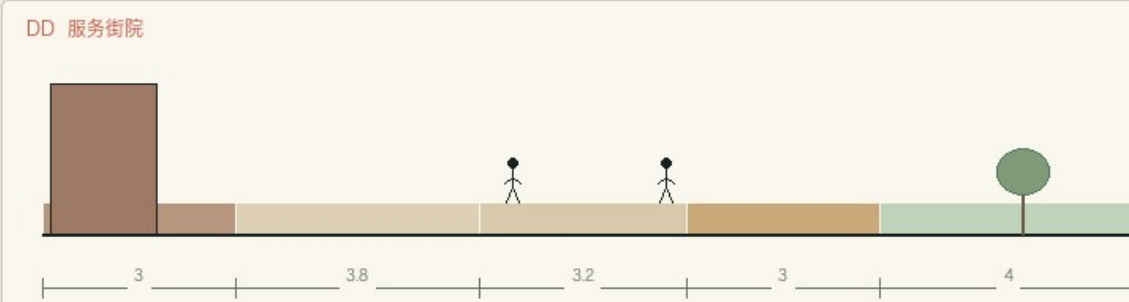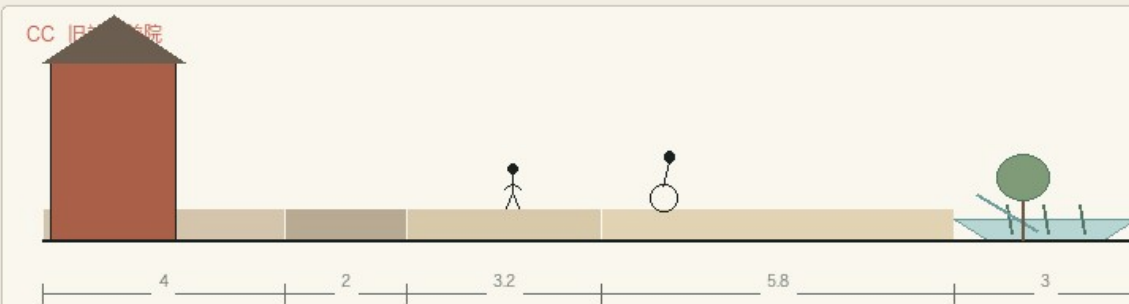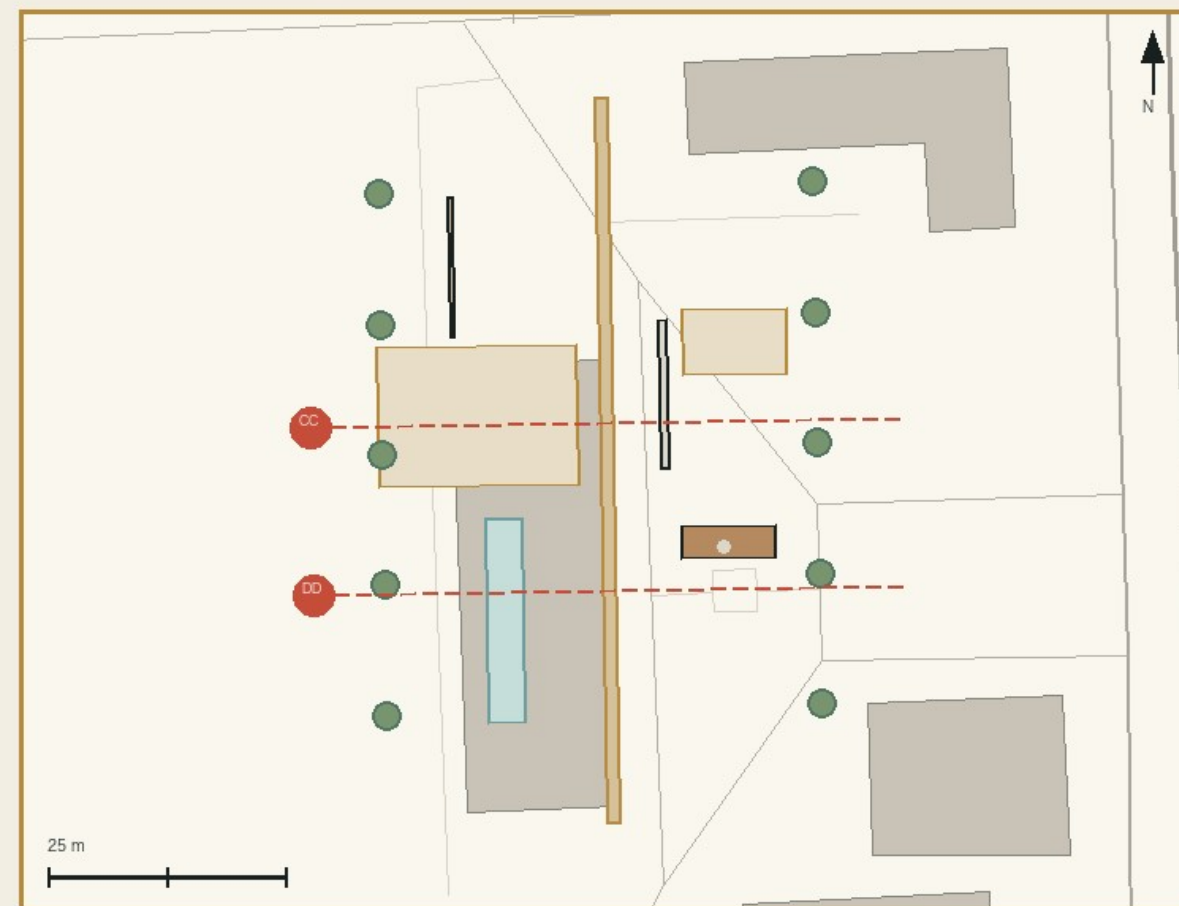





03 大钟寺交换院

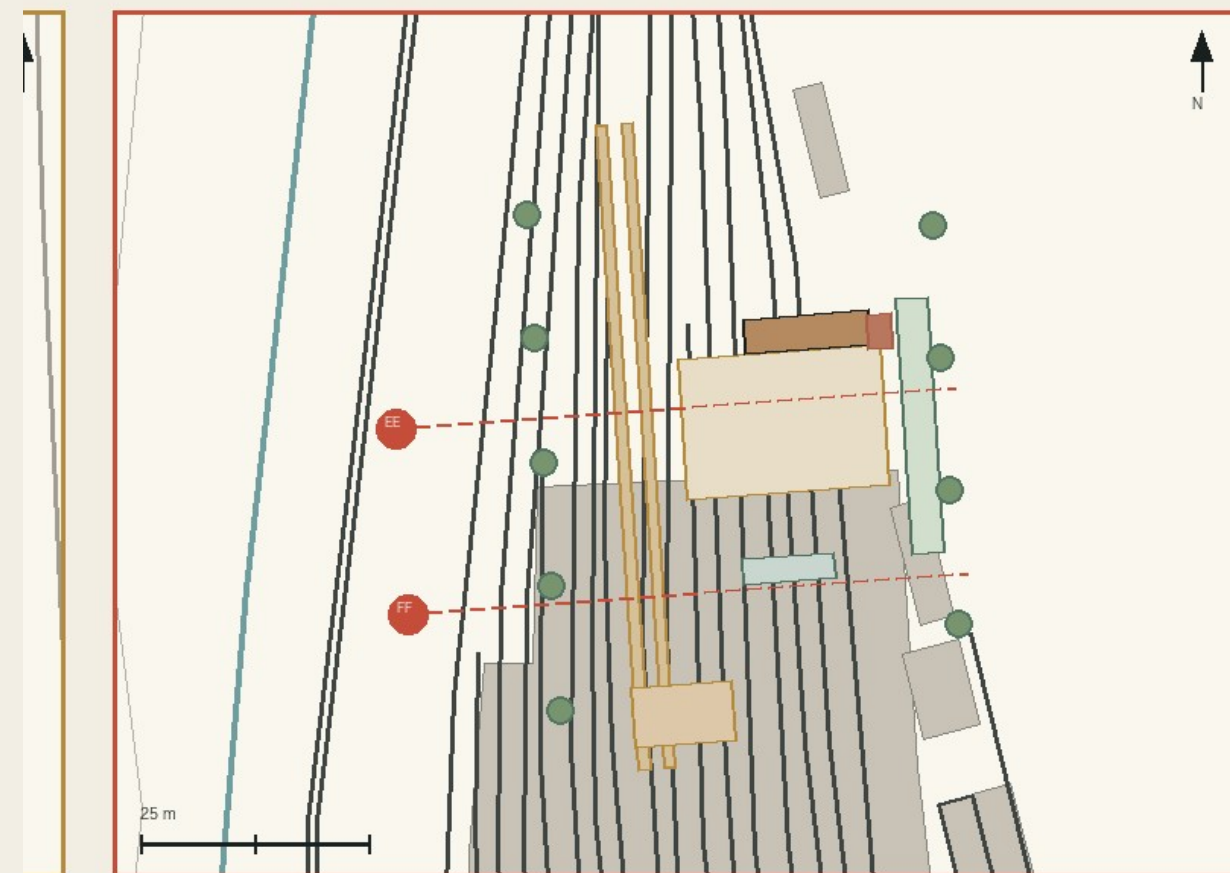

EE 交换院日常界面

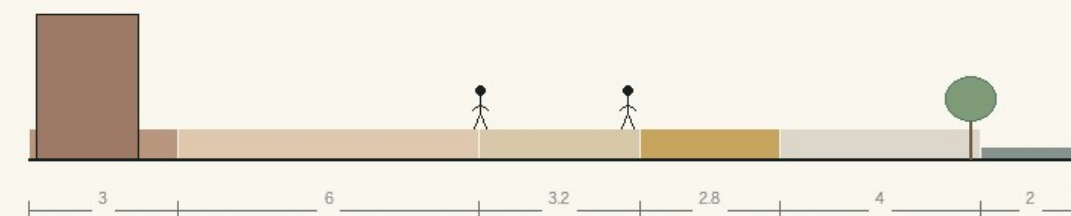

FF 无障碍过街

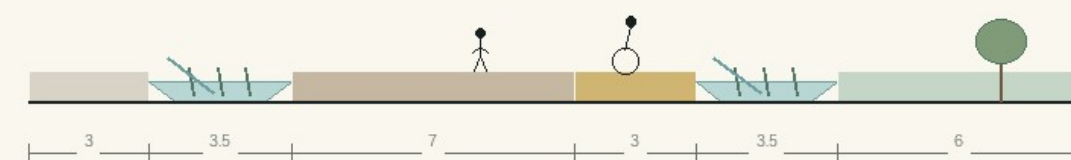

Working dimensions. Concept design. 1:200 section level



慢行、蓝绿与六条剖面



图例：慢行、蓝绿与六条剖面


三座院落的日常

三张独立的概念场景，对应三张平面里的真实视角



条公园，三座院落


1、河道与车站在公共脊上相遇

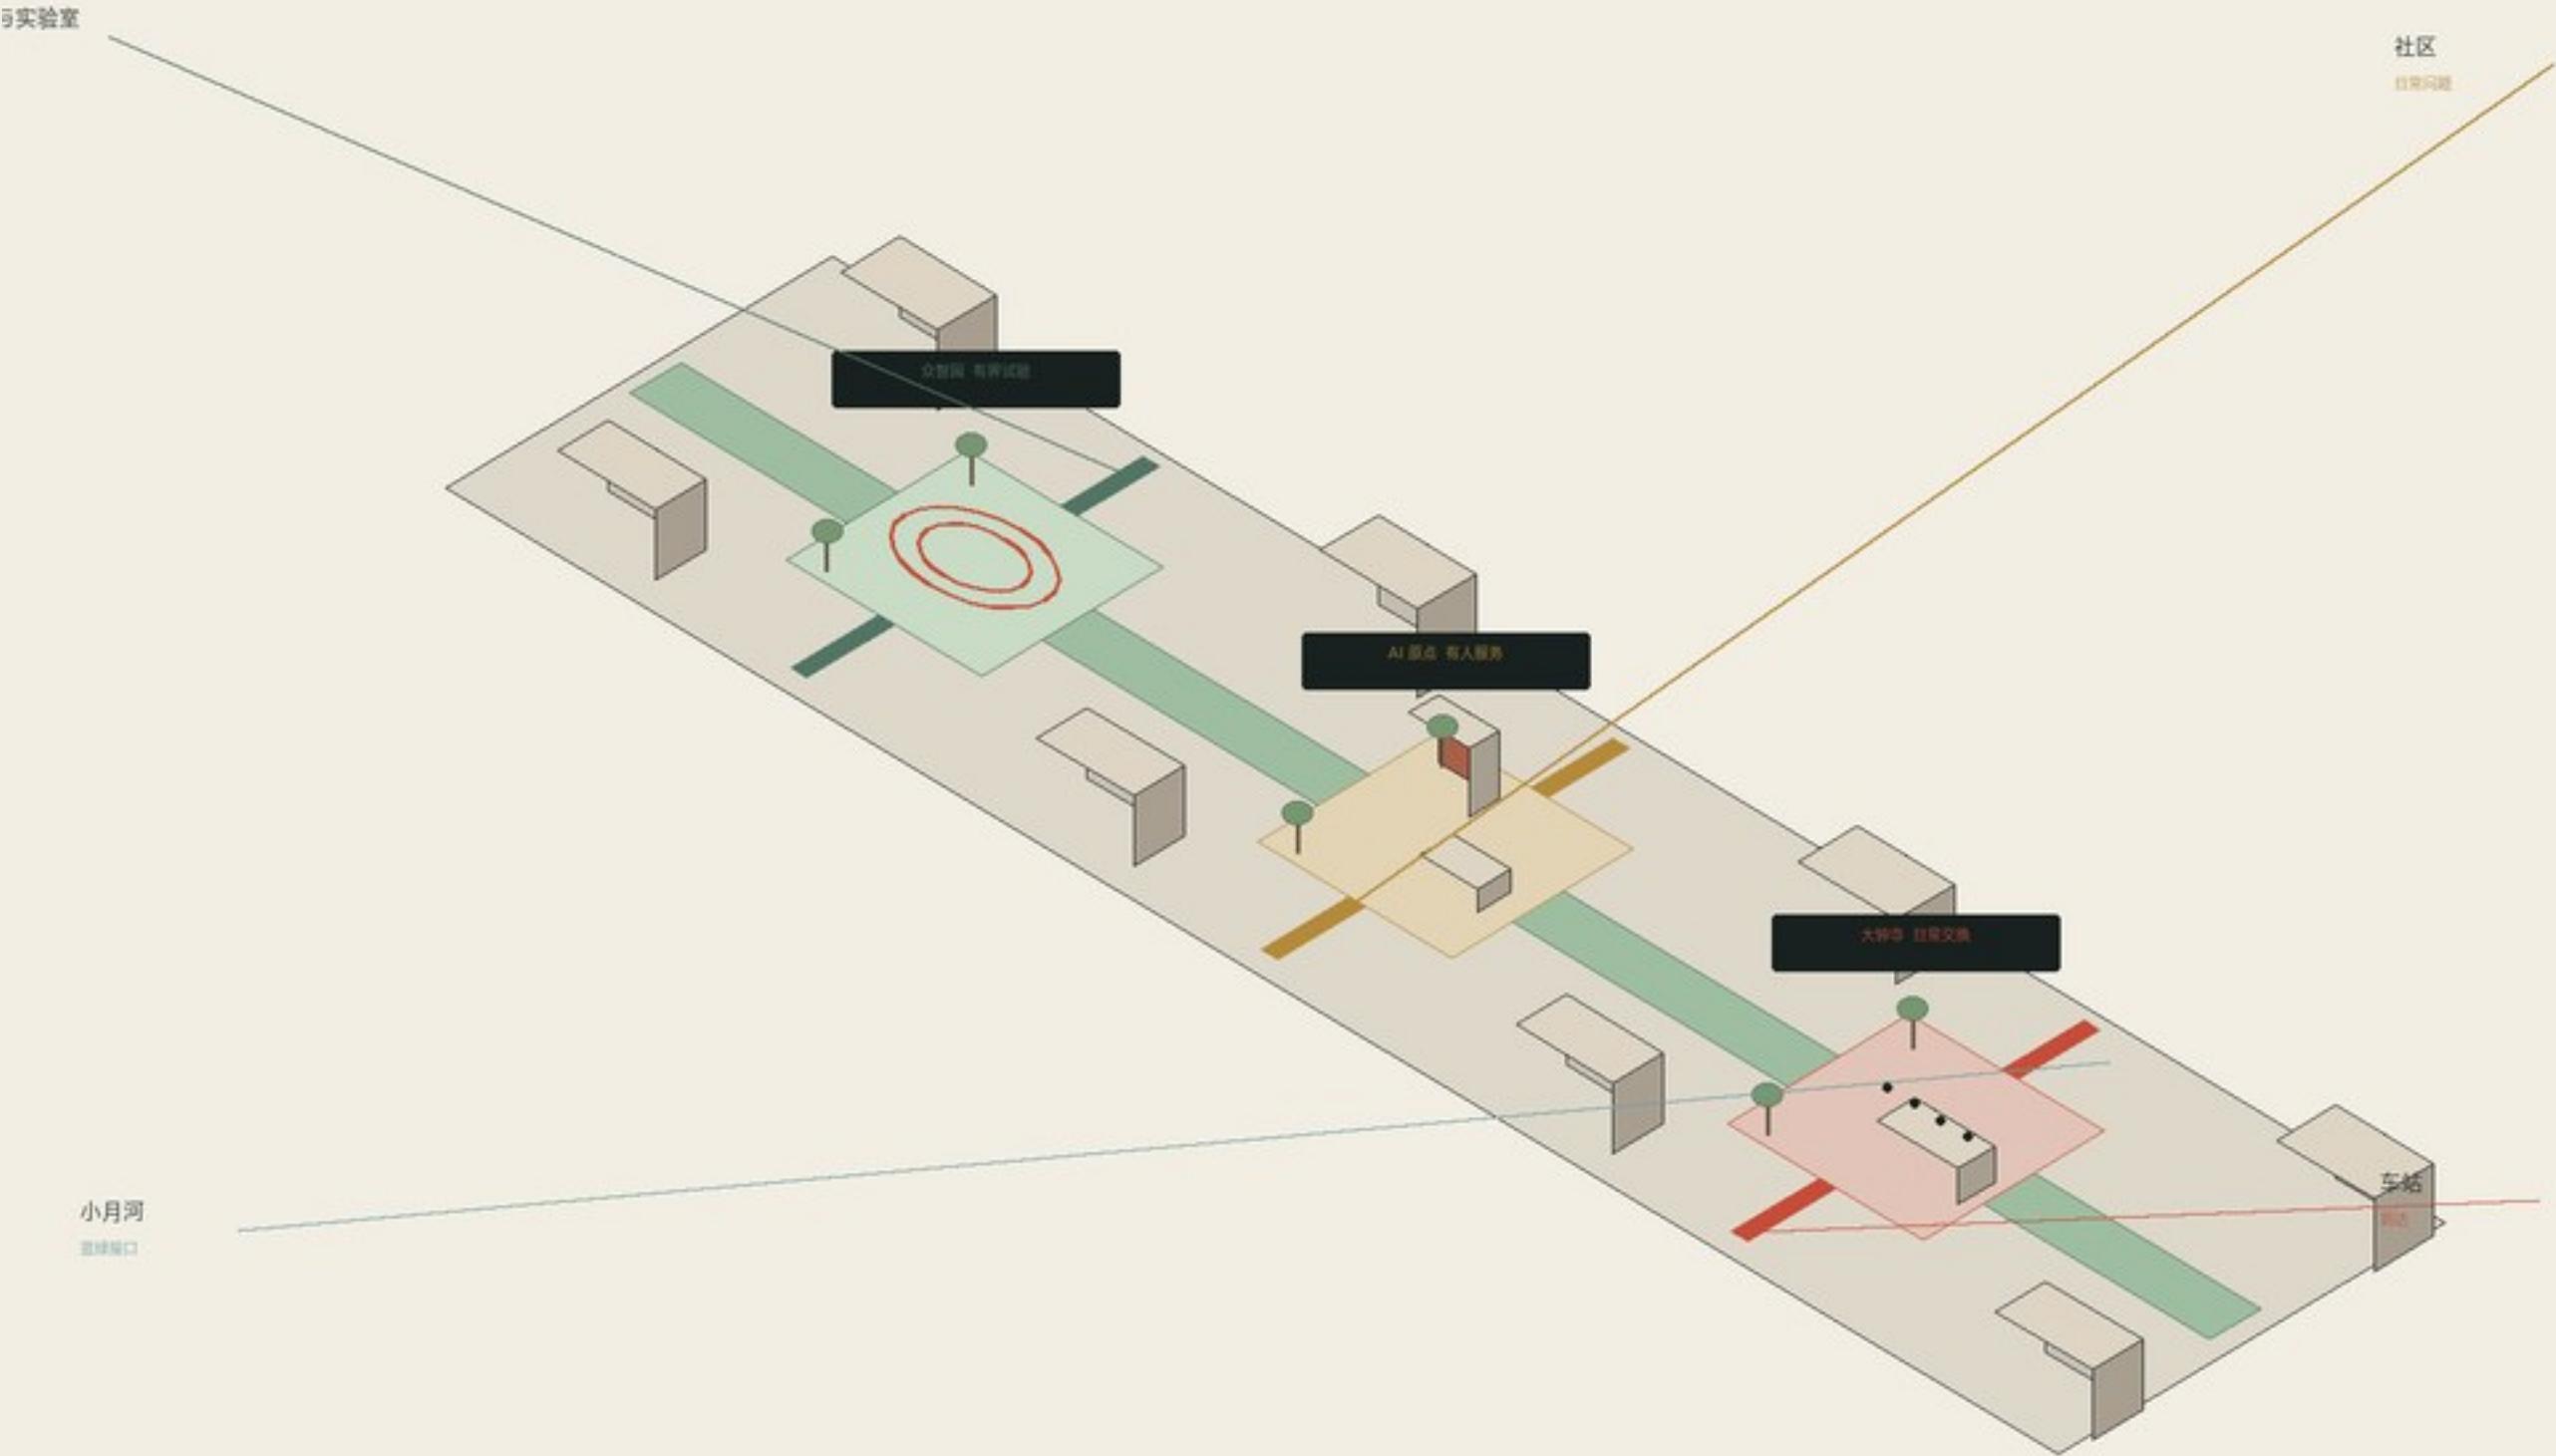

08 可拆、可修、可替换

八个构件画到尺寸、材料和连接关系

C01 树雨棚

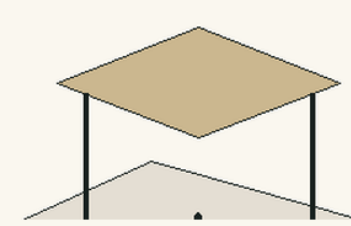

螺栓钢柱 / 可换木格栅 / 螺旋桩

6 × 3 × 3.2 m

C02 三种座高长凳



可换木板 / 镀锌框架

3.6 × 0.7 × 0.55 m


C03 雨庭边



开口砾石 / 碎石沟 / 排水口

6 × 2.4 × 0.45 m

C04 遗产阅读架

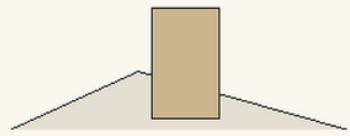

再用钢轨 / 可换展板

2.4 × 0.45 × 1.15 m


C05 有人服务桌



可锯木模块 / 活动凳

2.4 × 0.8 × 0.75 m


C06 可视试验边

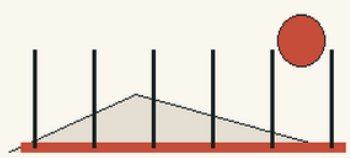

低矮钢栏 / 红色停机标记

4 × 0.25 × 0.9 m


C07 人工呼叫柱

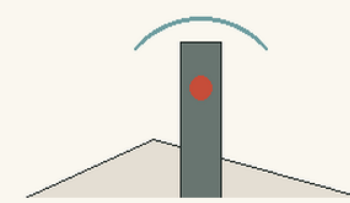

低压按钮 / 触觉标记 / 人工响应



0.35 × 0.35 × 1.35 m

C08 遮光夜灯

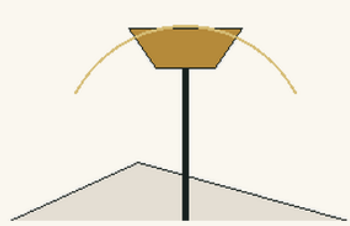

可换暖光灯 / 遮光灯罩 / 分时回路

0.35 × 0.35 × 3.6 m

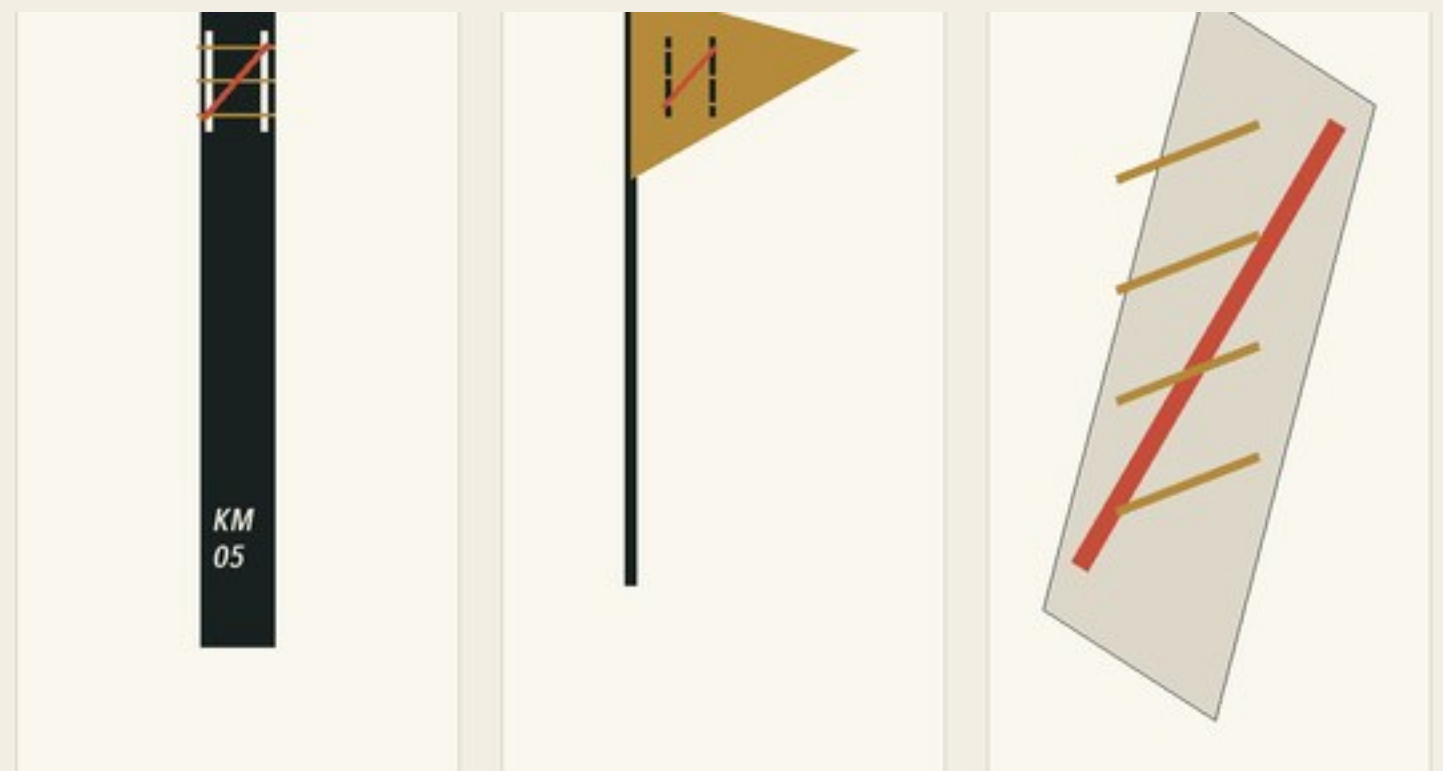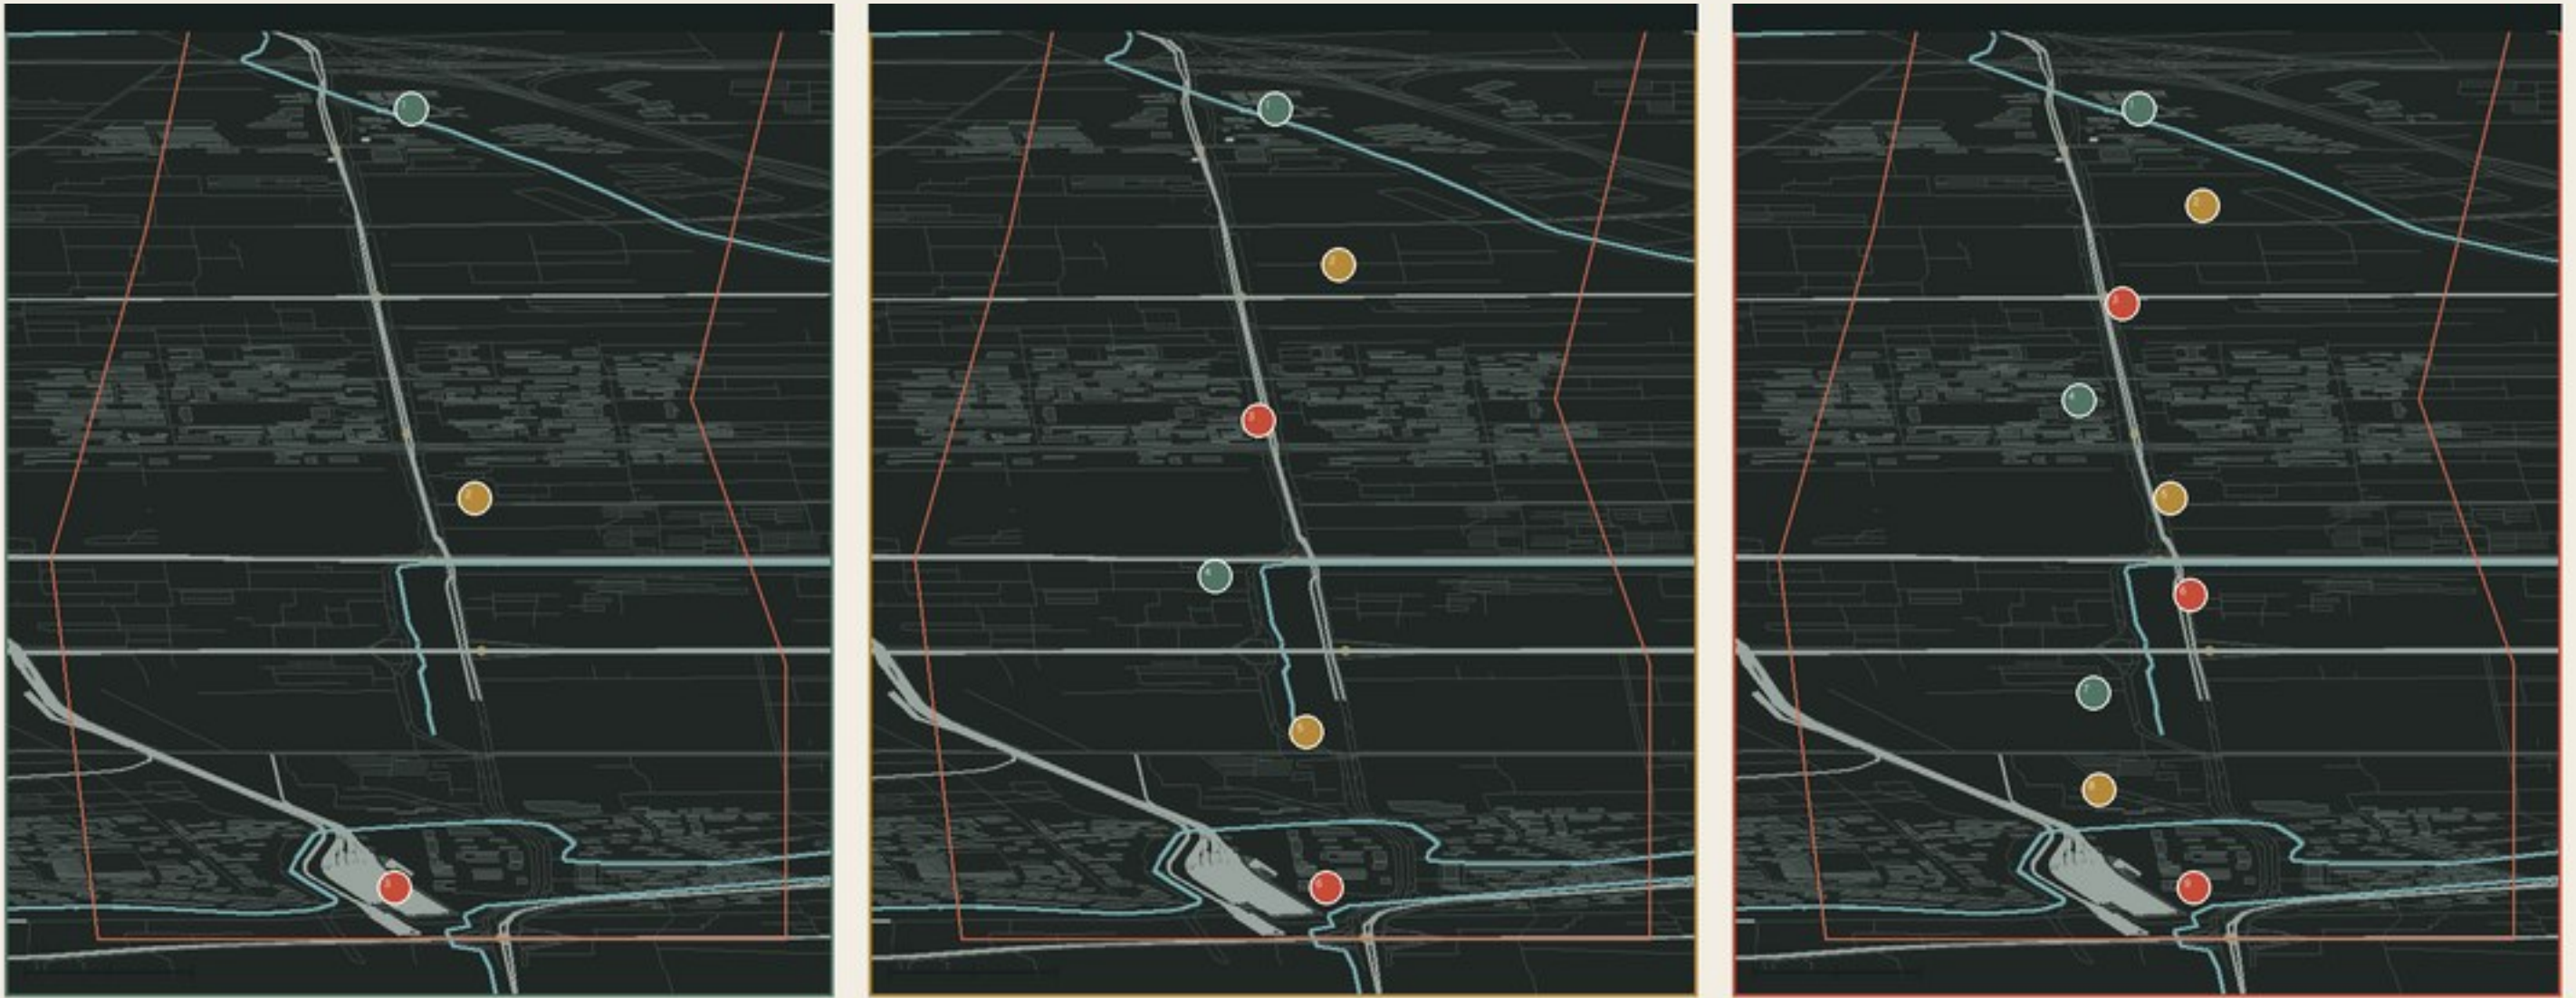

05

空间测量图

三处小样用同一把尺复测，数字退到图纸边缘



3.2 m	2.8 m	3.5 m	500 m	14 / 6	9
连续步行净宽	候骑道	试验缓冲	驿站检查半径	场景 / 测试	首批项目

公开项目状态 → OSM 语境 → 暂定 GeoJSON → 现场复测

待核 官方红线、权属、管线、精确文保线、法定强度