



何以京张：The Openline 100

海淀京张遗址公园走廊城市设计提案 · A3 图版册

本册为图版集：24 张图版，全部基于真实 OSM 城市肌理与提案几何数据重新渲染。
完整论述文本见 proposal.md / proposal.en.md 与 report/proposal.html。
图纸规范：Sasaki v1.2 图面标准（色板 / 字阶 / 比例尺 / 指北针 / 图签）。


Openline 100 Studio · kenshin-ai-101 · 2026-08 · v1.2

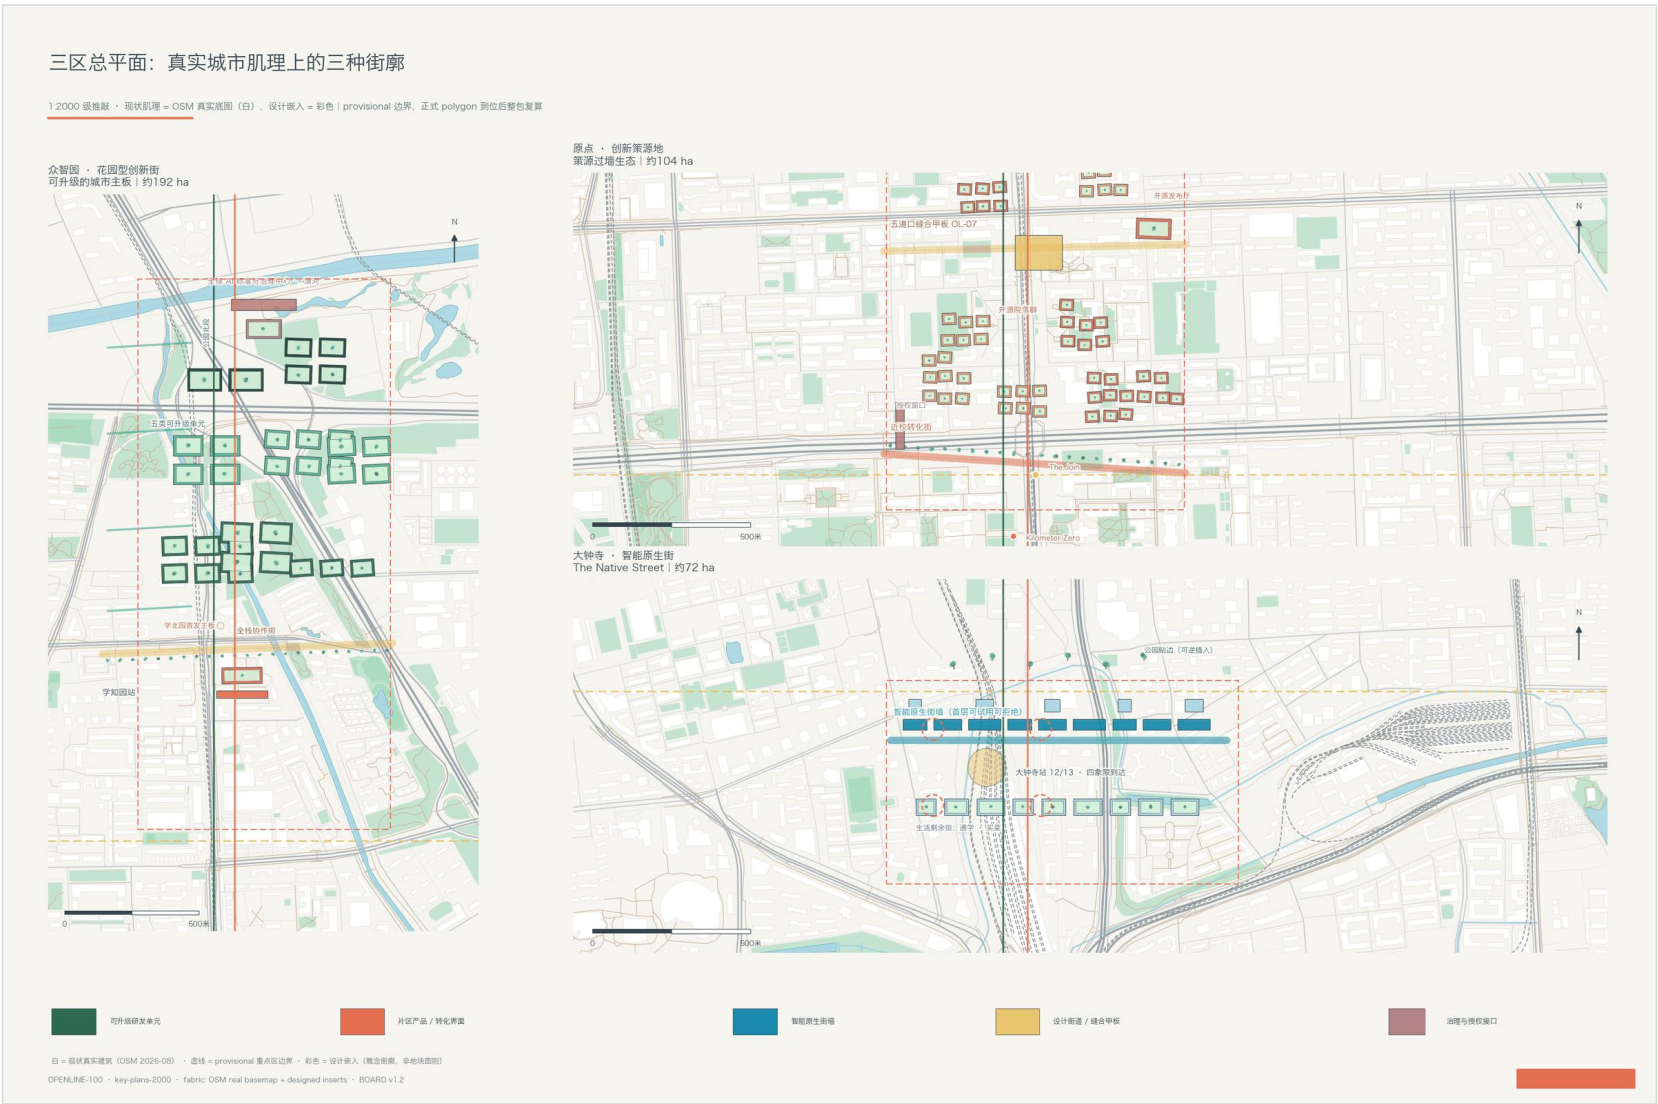

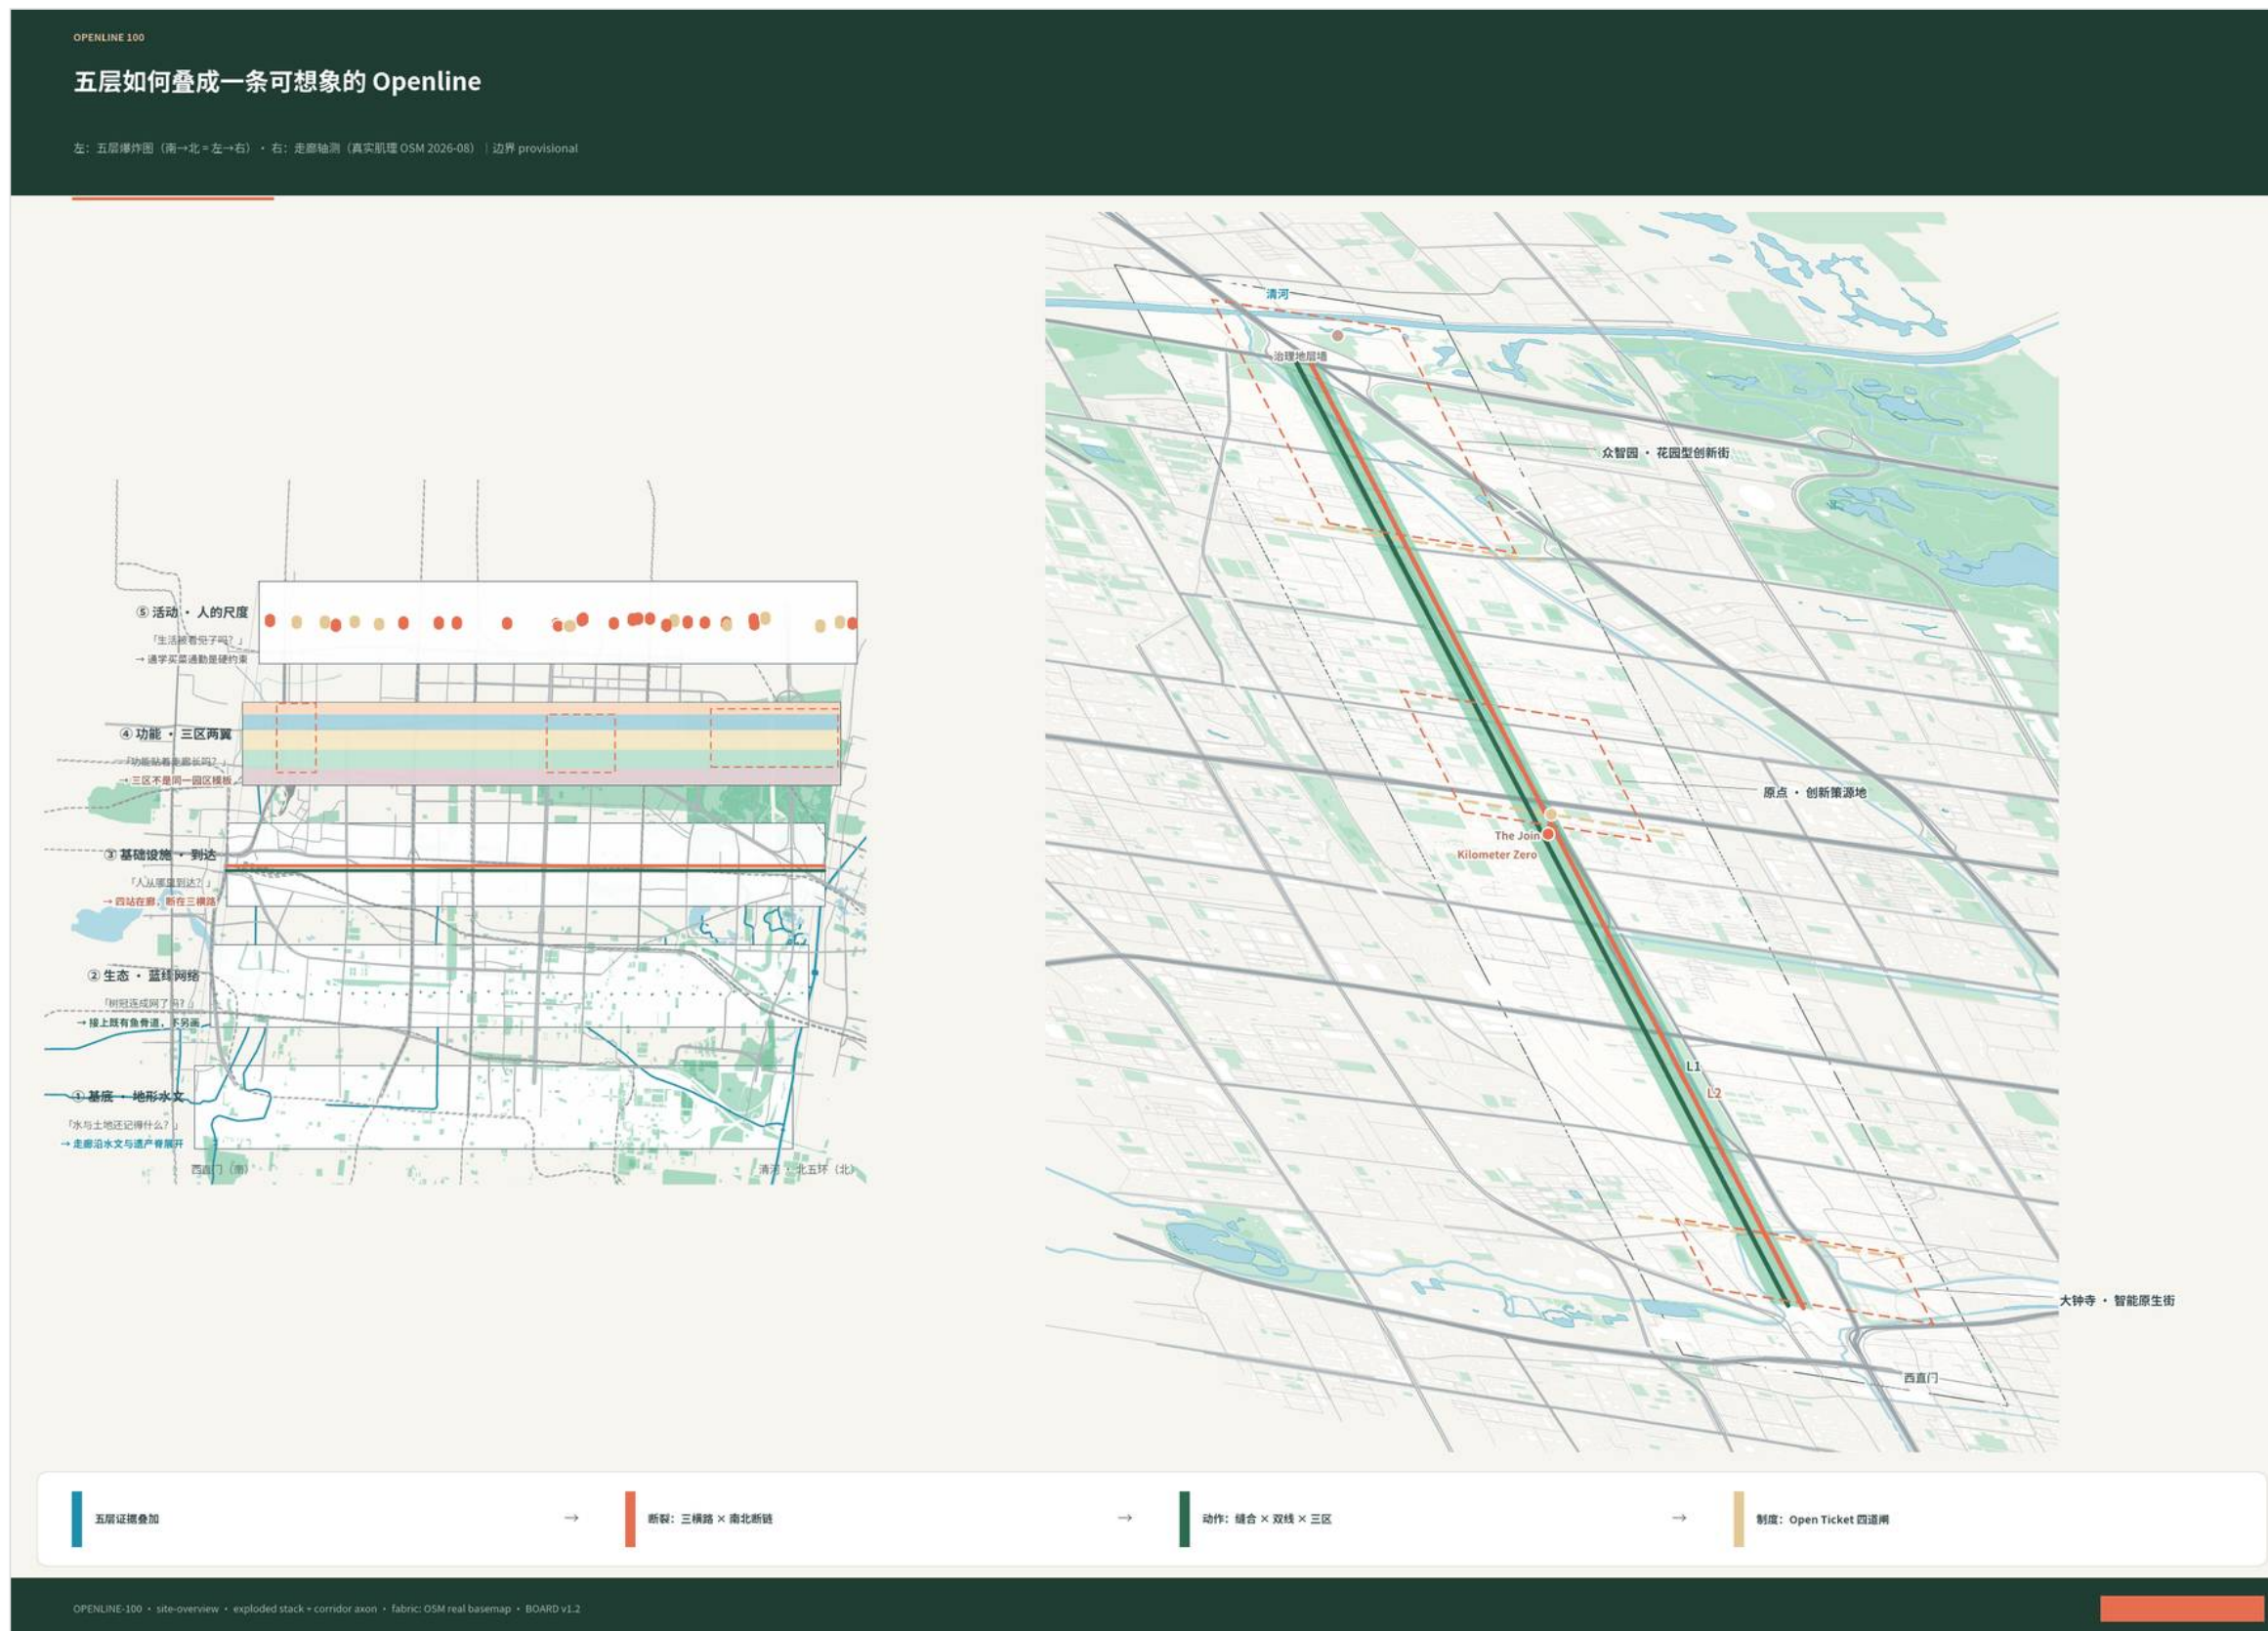


01 场地总览：五层结构 × 斜轴测走廊全貌

边界 provisional · 讨论级概念建议 · 非审批几何 · 正式数据到位后整包复算

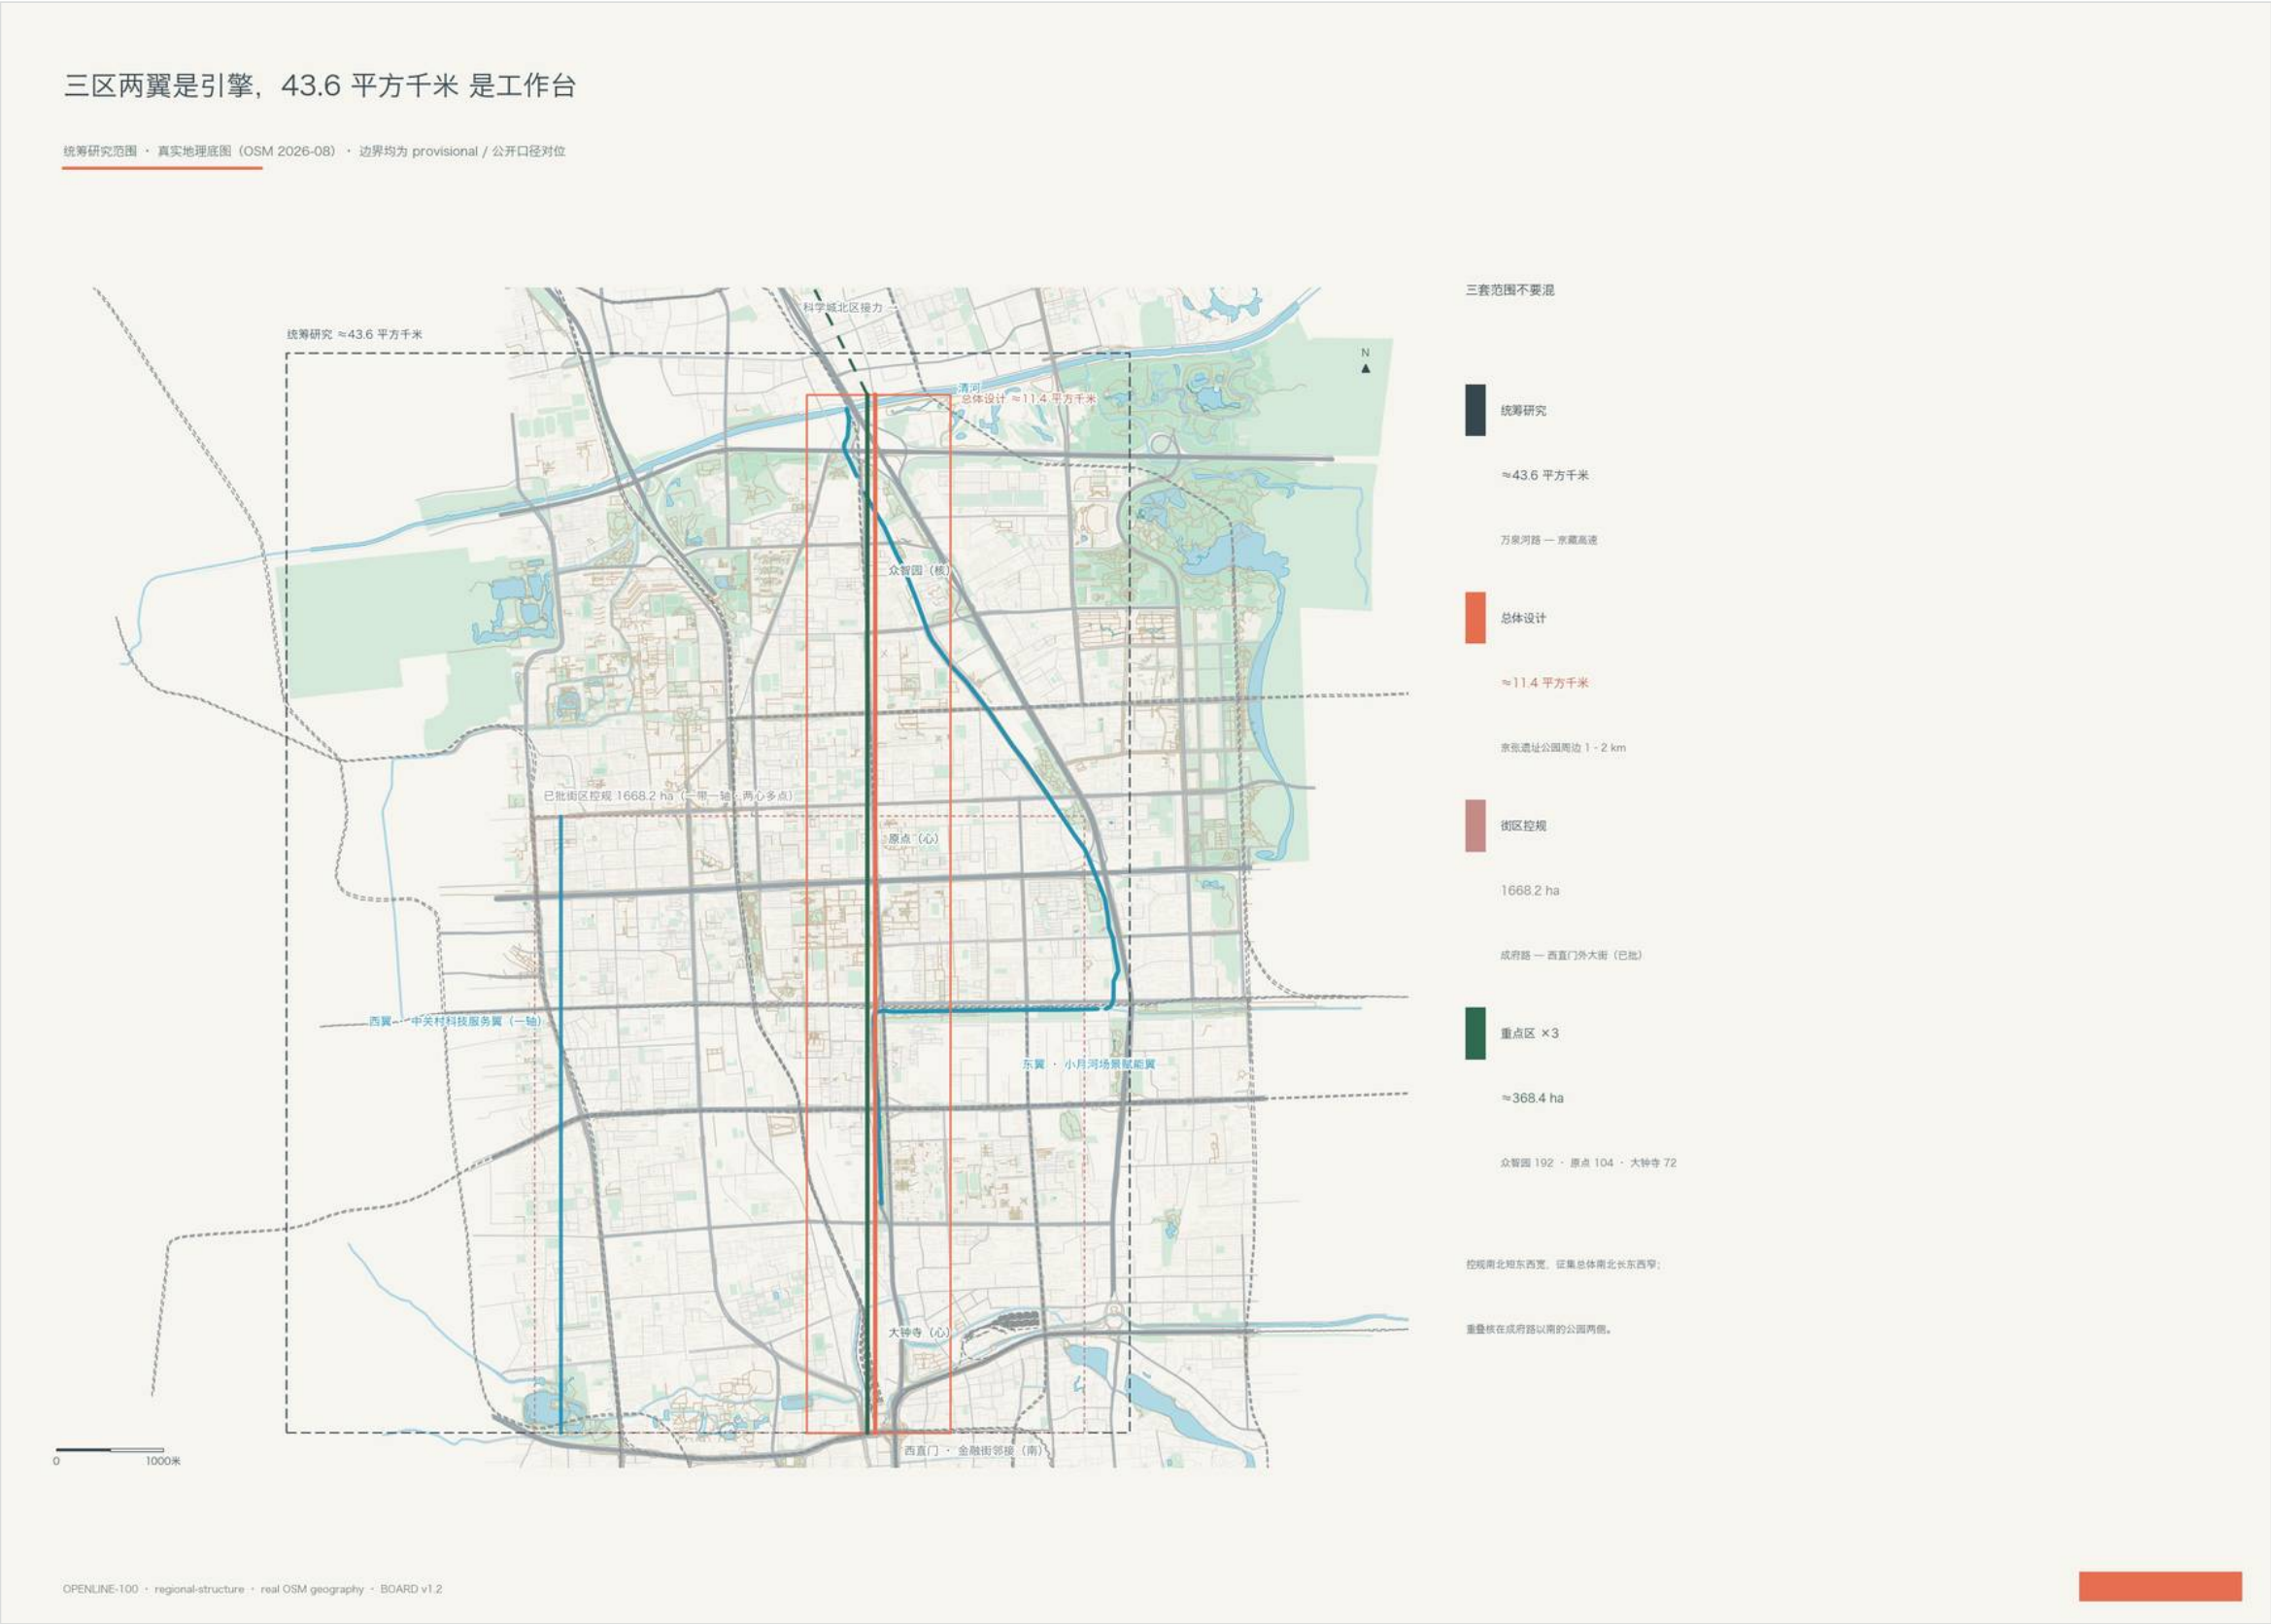

02 区域结构：京张走廊在北京西北的位置

边界 provisional · 讨论级概念建议 · 非审批几何 · 正式数据到位后整包复算

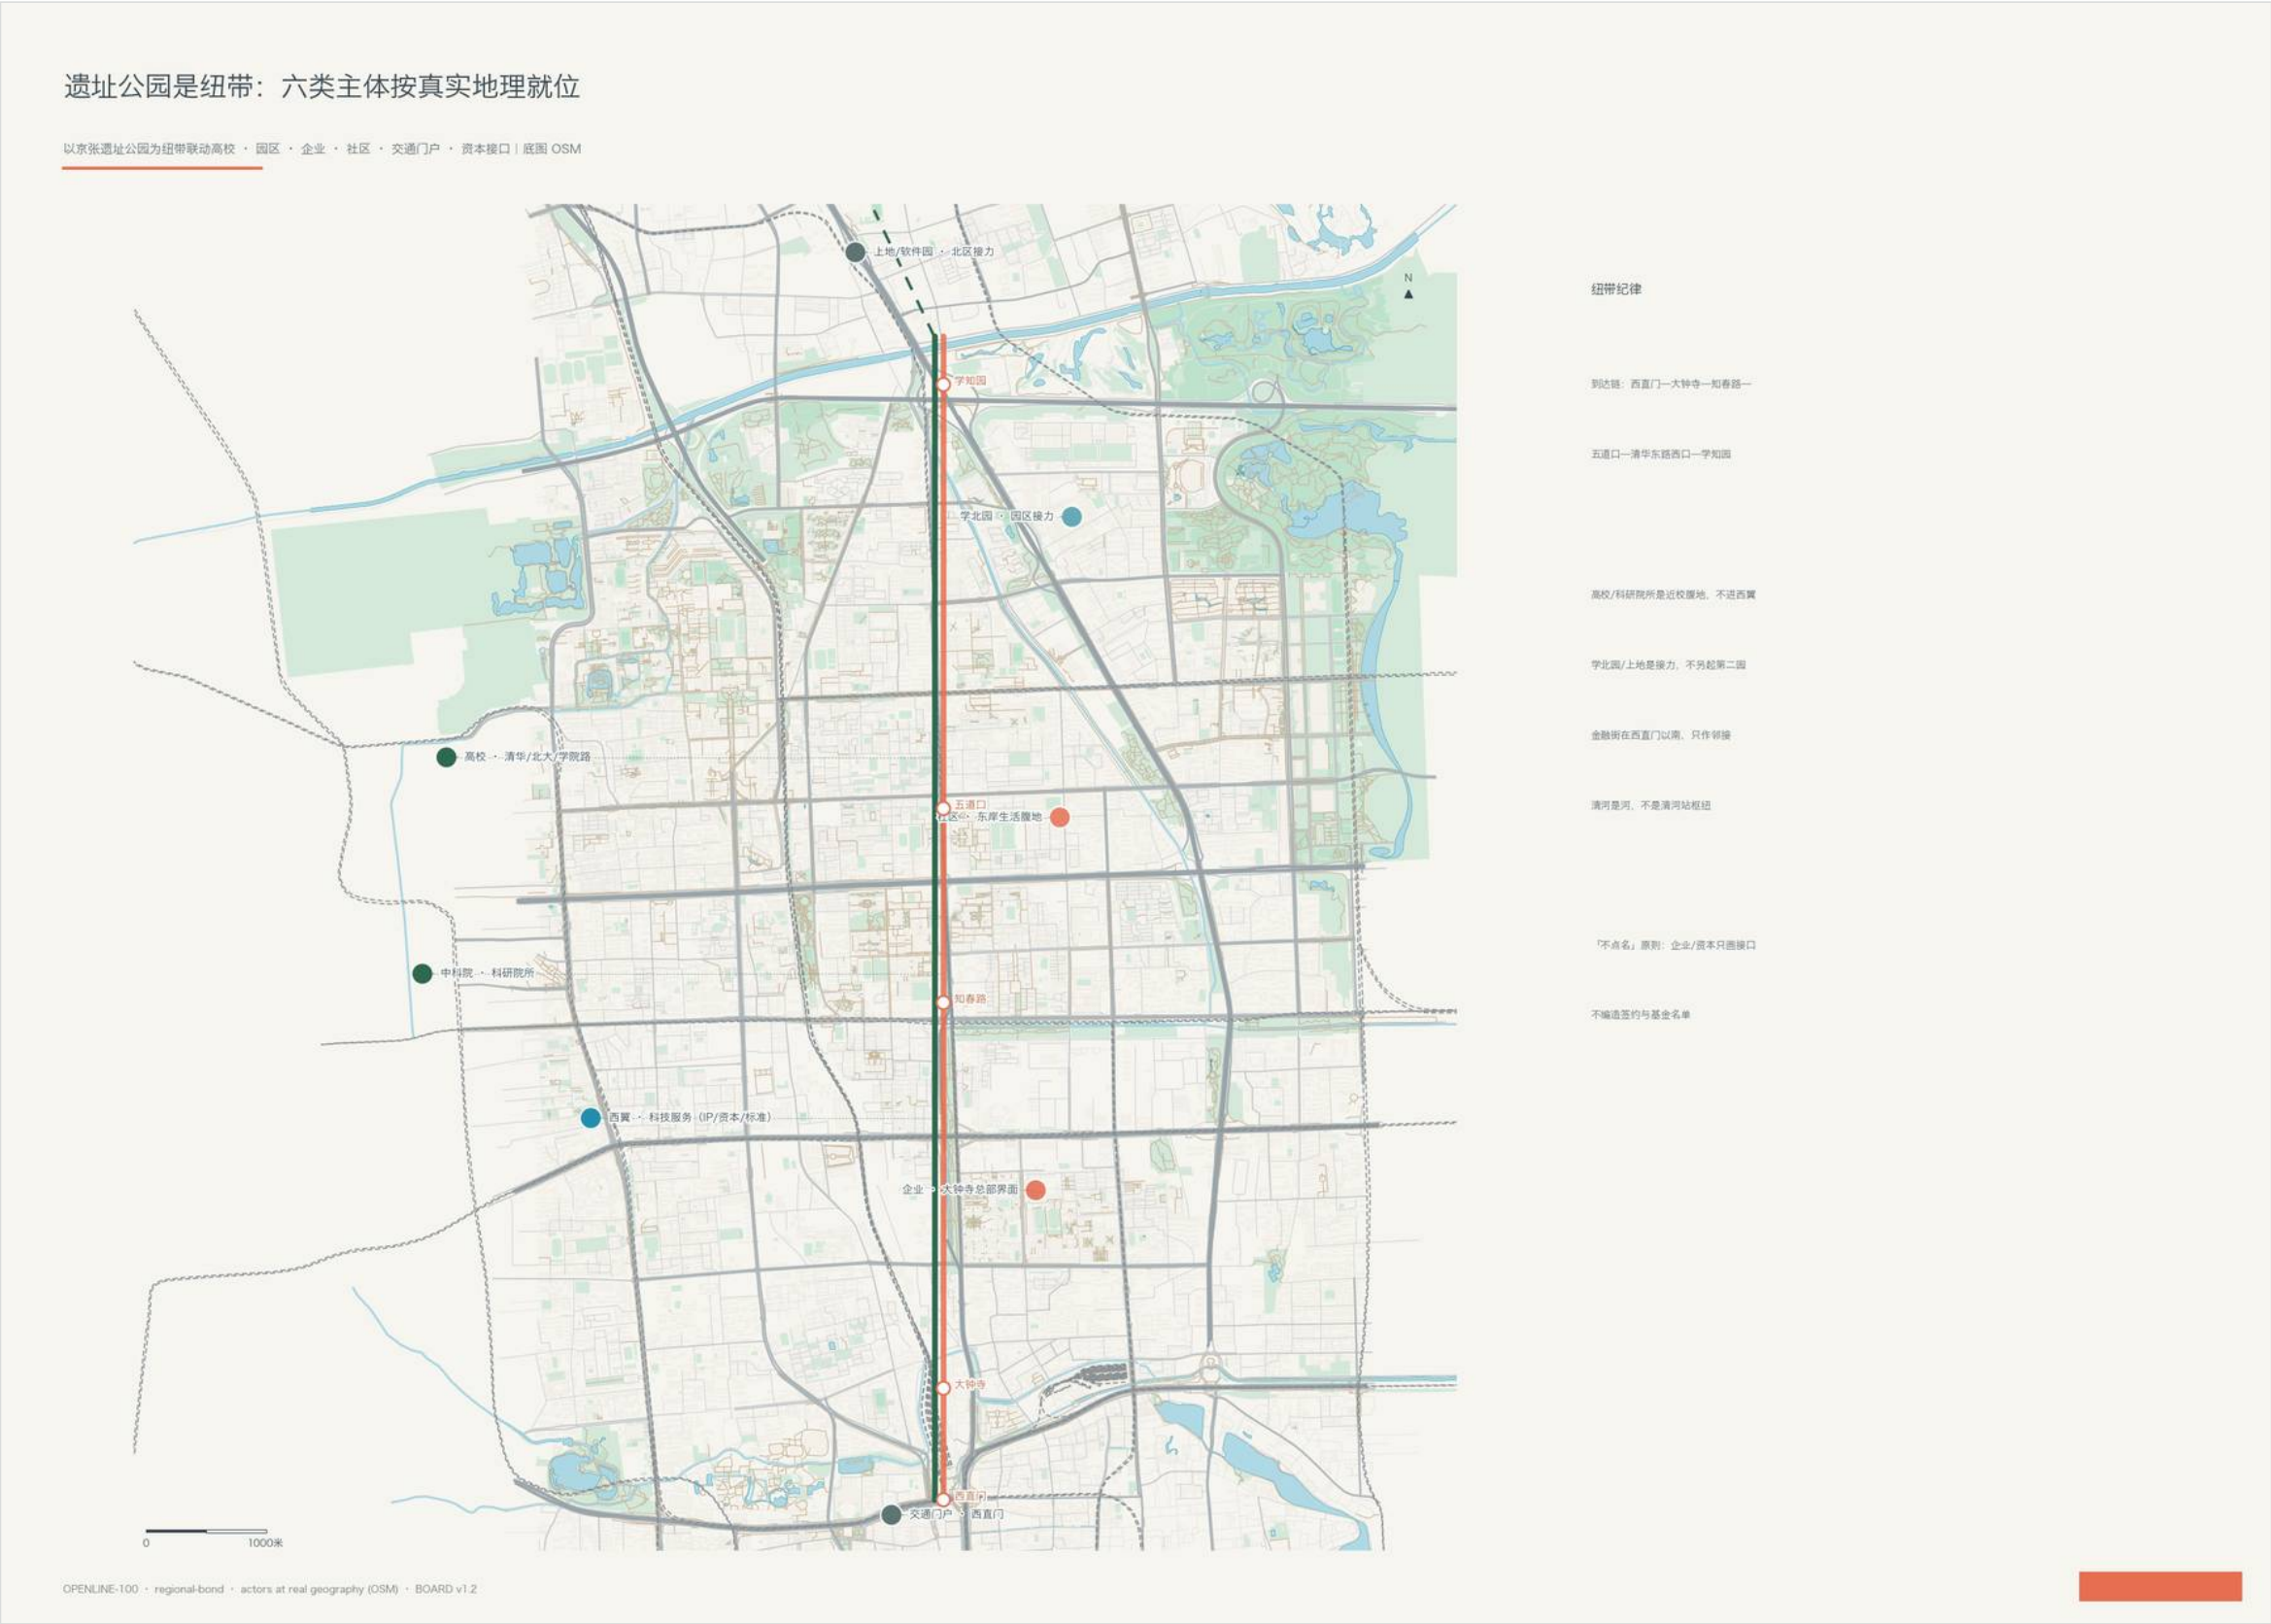



04 土地利用与结构：一轴三核五段

边界 provisional · 讨论级概念建议 · 非审批几何 · 正式数据到位后整包复算




05 三重点区落位：众智园 · 原点 · 大钟寺

边界 provisional · 讨论级概念建议 · 非审批几何 · 正式数据到位后整包复算


三区总平面：真实城市肌理上的三种街廓

1:2000 级推敲 · 现状肌理 = OSM 真实底图 (白), 设计嵌入 = 彩色 | provisional 边界, 正式 polygon 到位后整包复算


众智园 · 花园型创新街
可升级的城市主板 | 约192 ha

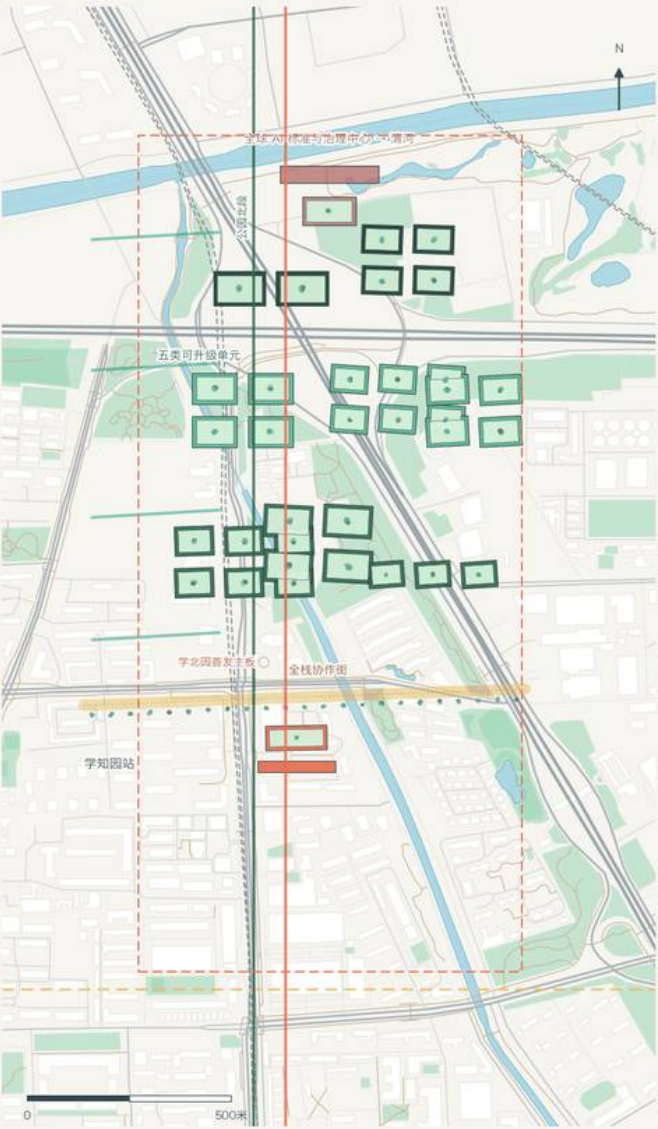

原点 · 创新策源地
策源过墙生态 | 约104 ha

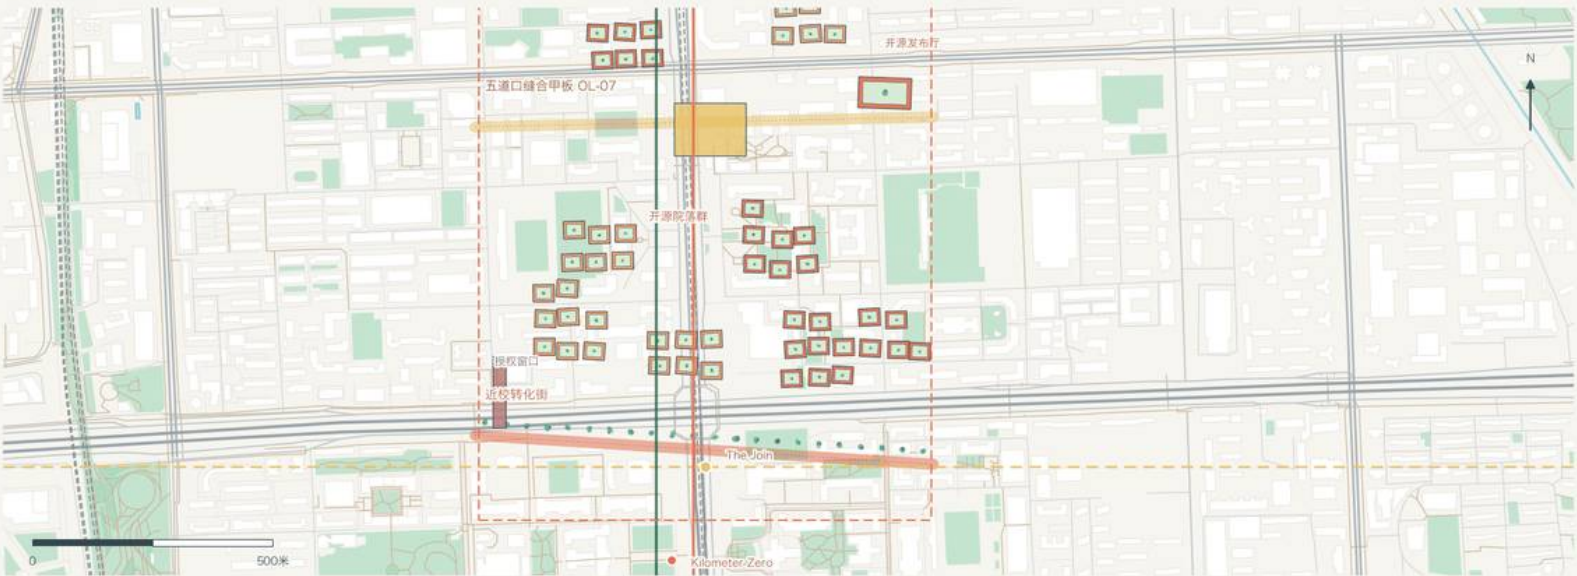

大钟寺 · 智能原生街
The Native Street | 约72 ha

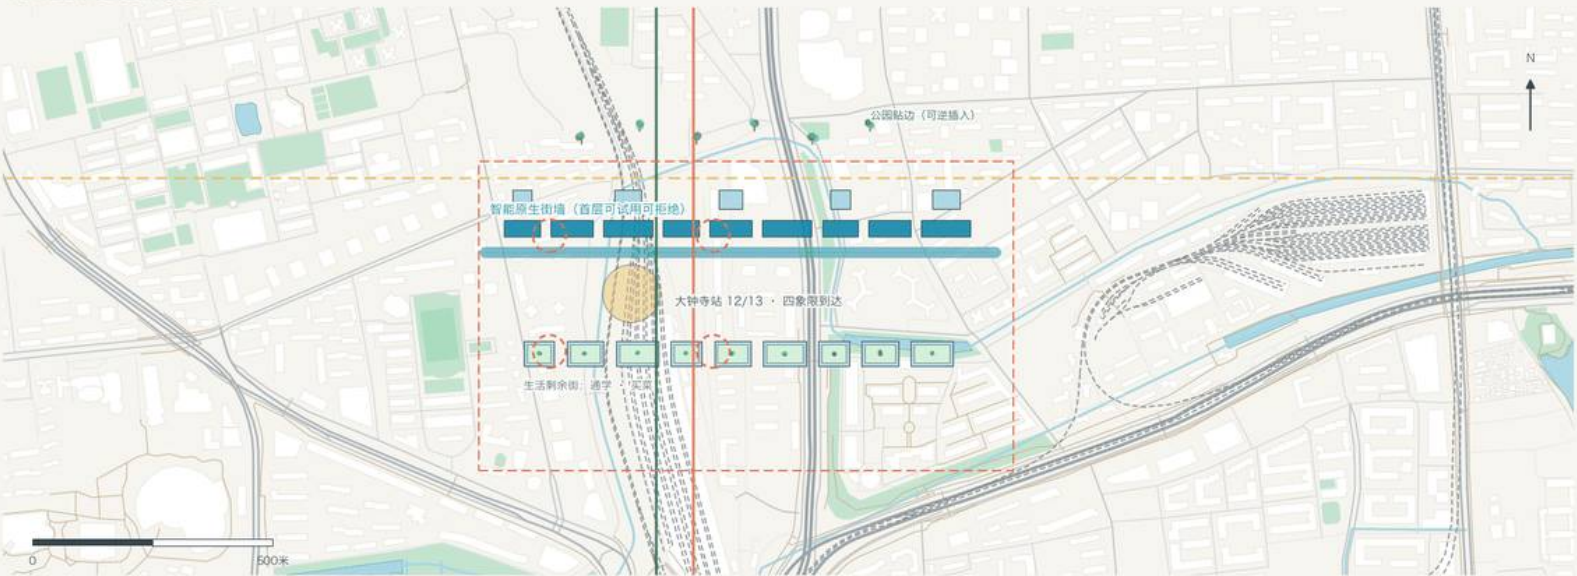

可升级研发单元

片区产品 / 转化界面

智能原生街墙

设计街道 / 缝合甲板

治理与授权接口

白 = 现状真实建筑 (OSM 2026-08) · 虚线 = provisional 重点区边界 · 彩色 = 设计嵌入 (概念街廓, 非地块面则)
OPENLINE-100 · key-plans-2000 · fabric: OSM real basemap + designed inserts · BOARD v1.2


06 1:2000 三重点区总平面 (真实 OSM 城市肌理)

边界 provisional · 讨论级概念建议 · 非审批几何 · 正式数据到位后整包复算


体量服从街廓，天际线不另立塔

上排：三区白模轴测（体量 = 概念区间，z 轴略夸张） · 下条：沿公园南→北天际线剖面

众智园 · 18 - 36 m 花园型院落（体量服从街廓）

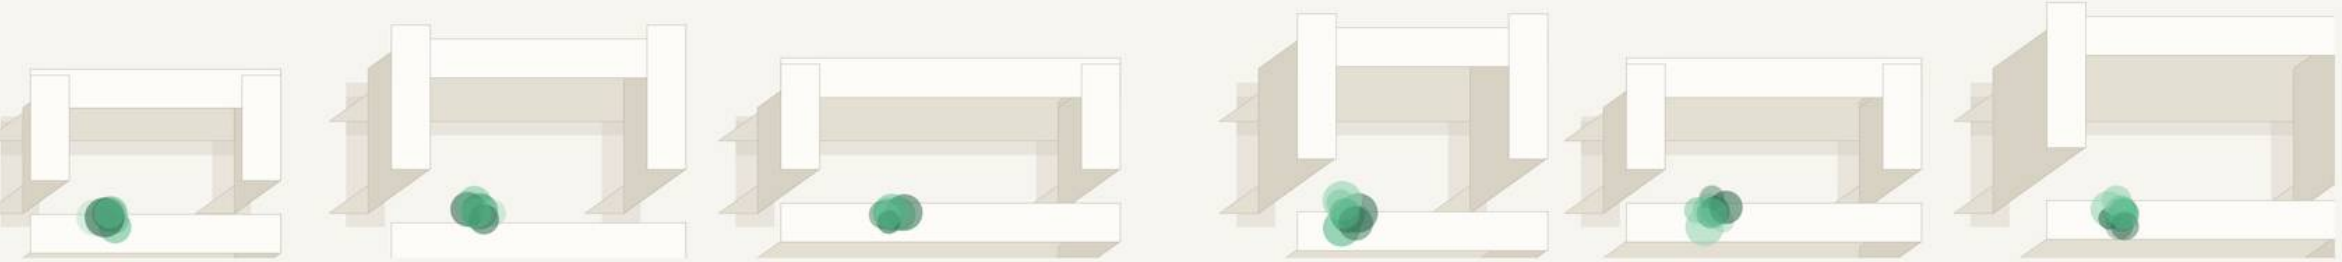

原点 · 近校压低 ≤45 m（小肌理开源院落）

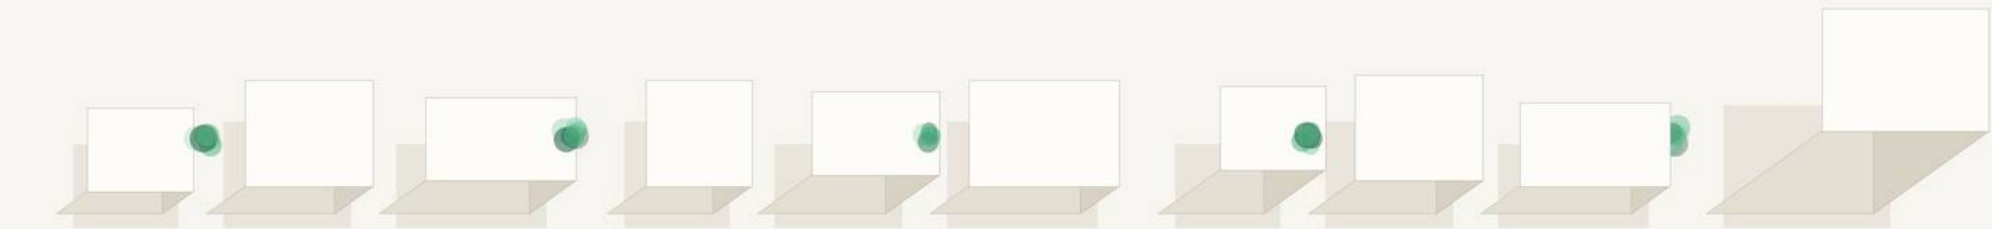


大钟寺 · 街墙连续 24 - 36 m，服从既有总部体量



原有总部 80 m
不另立塔

沿公园南 → 北：不另立塔，天际线让位树冠

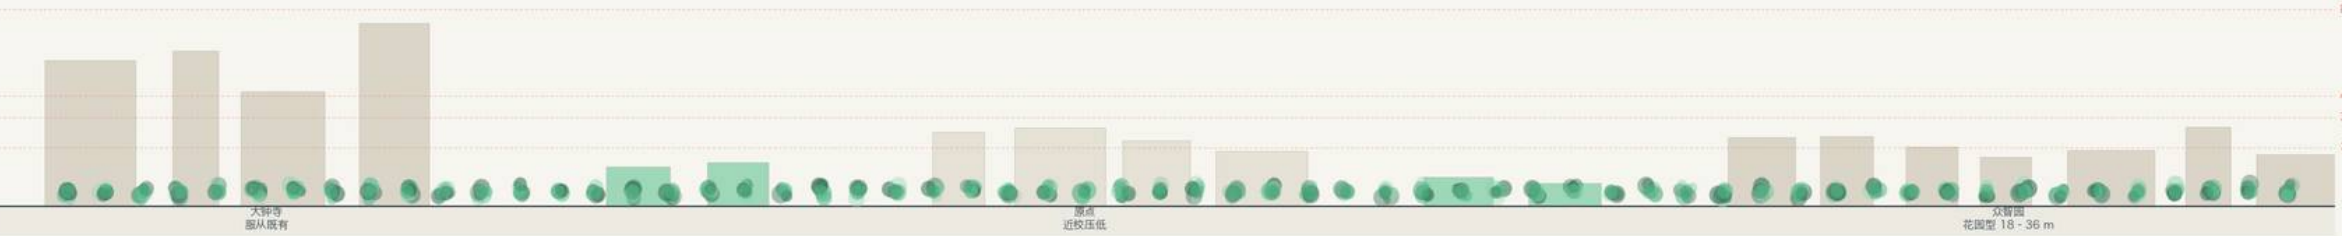

OPENLINE-100 · key-massing-skyline · concept heights, caps yield to official parcels · BOARD v1.2

07 体量与天际线控制

边界 provisional · 讨论级概念建议 · 非审批几何 · 正式数据到位后整包复算




08 六个典型断面

边界 provisional · 讨论级概念建议 · 非审批几何 · 正式数据到位后整包复算

五处地点，切开就能认

地点剖面（非符号街）：院落/授权窗口/三层甲板/站到达/清河界面，与「走进」氛围图对话


01 众智园 · 院落与公园带

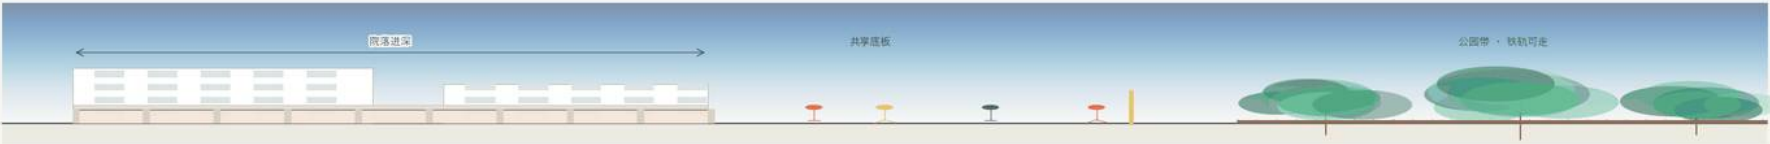


02 原点 · 授权窗口与 KMO



03 五道口 · 三层缝合甲板

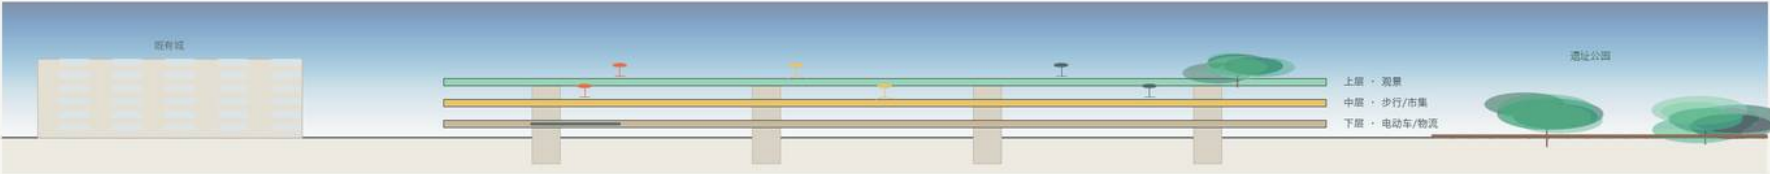

04 大神寺站 · 只做到达

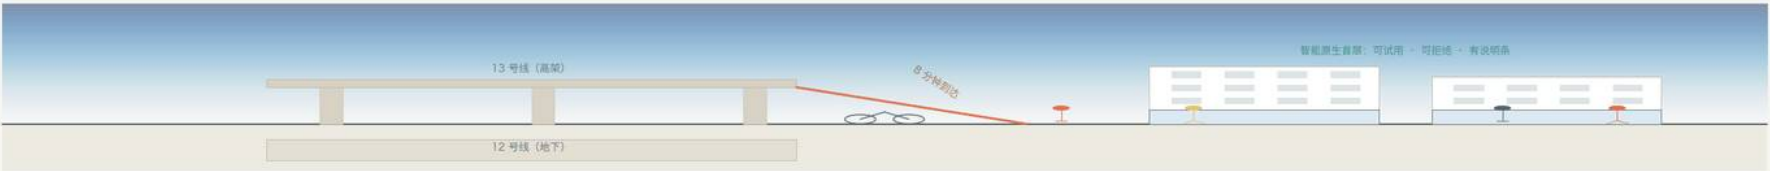

05 清河 · 治理面河界面



OPENLINE-100 · key-eyes · five place sections · BOARD v1.2

读法

每张都是

切开的地

有墙、有树、

有水、有人、

不是一点透视

的符号街。


深度 = 制度在

剖面里成立

可加入、可核造

可退出、可继承

09 五处「城市之眼」地点剖面

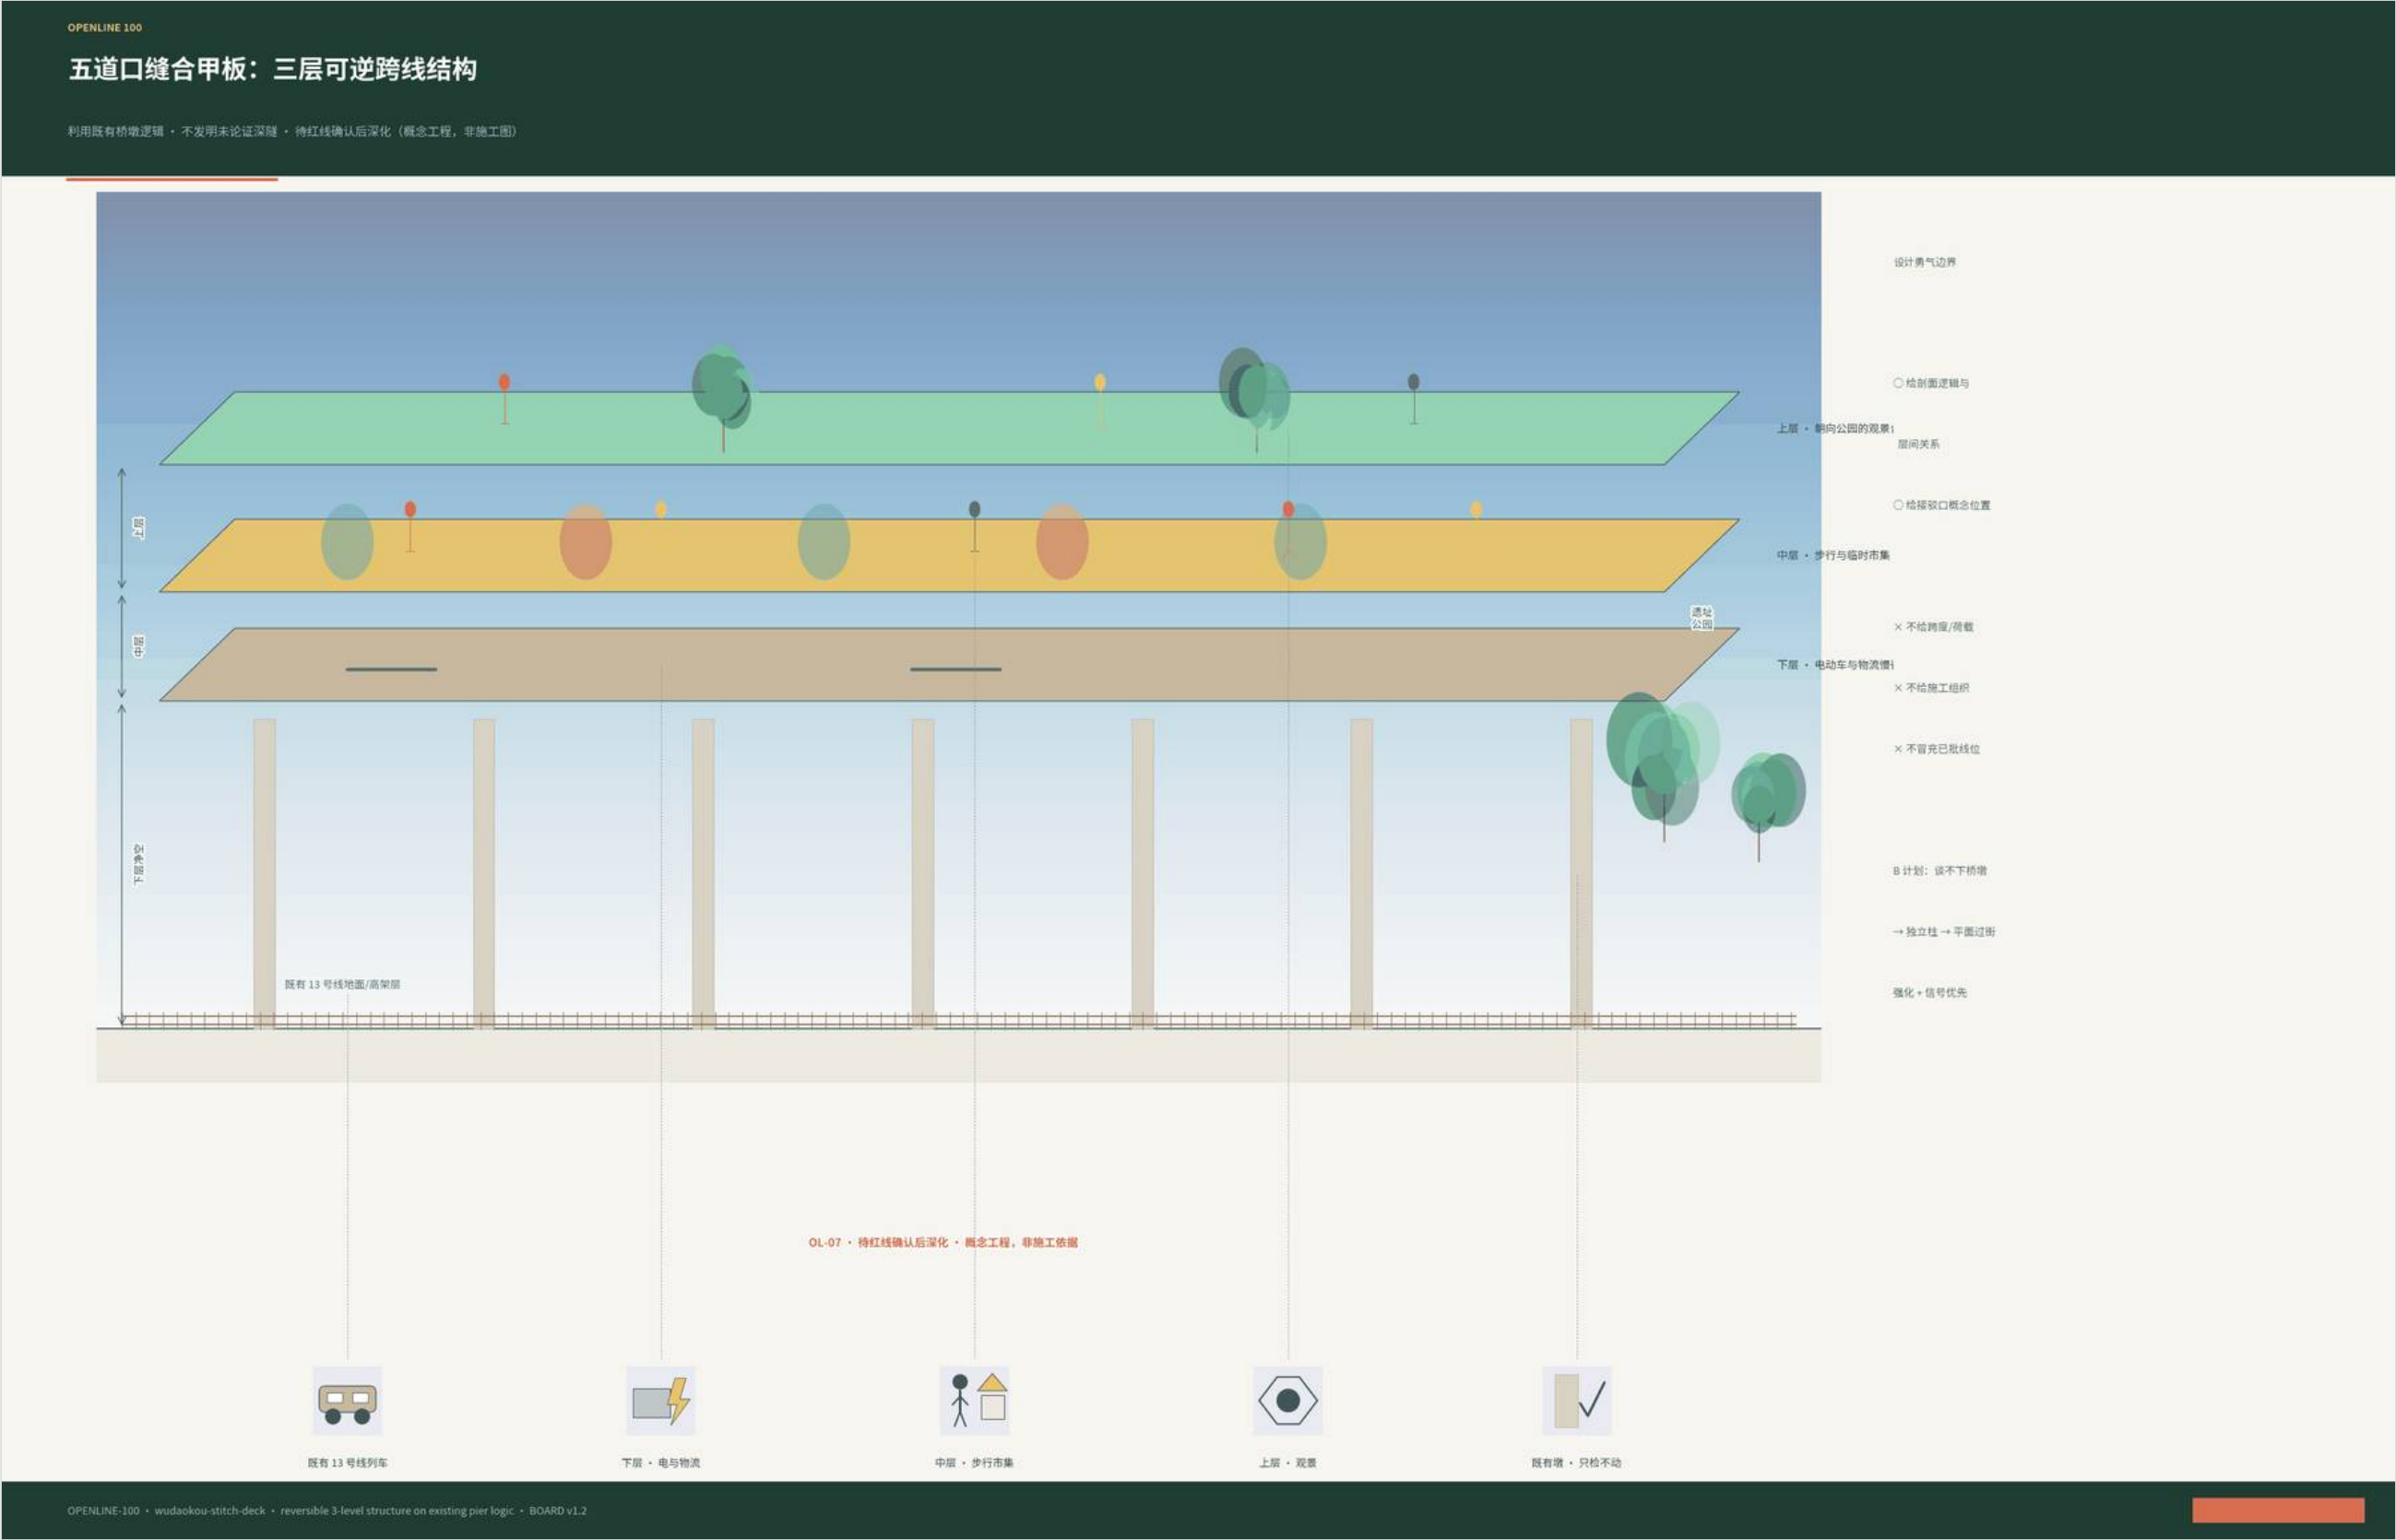

10 五道口缝合甲板：三层竖向

五道口缝合甲板：把最大胆的动作画成可信的日常

剖透视 · 材质 / 高差 / 真实人物 · 手绘边缘保留概念的不确定性，不冒充实景 | OL-07



11 镇版之图：缝合甲板剖透视 · 材质 / 高差 / 真实人物

边界 provisional · 讨论级概念建议 · 非审批几何 · 正式数据到位后整包复算



12 铁轨显形：京包线线位扎进真实街廓

让铁轨长进地面：五种物质转译

组件进公共空间组件库，随 Inherit 版本化 · 声景与碑文须许可与人工审核后试点

地面层 · 轨作铺装




禁忌：不做可达展品

叙事层 · 里程思辨碑




禁忌：不娱乐化京张史

剖面层 · 考古展示沟

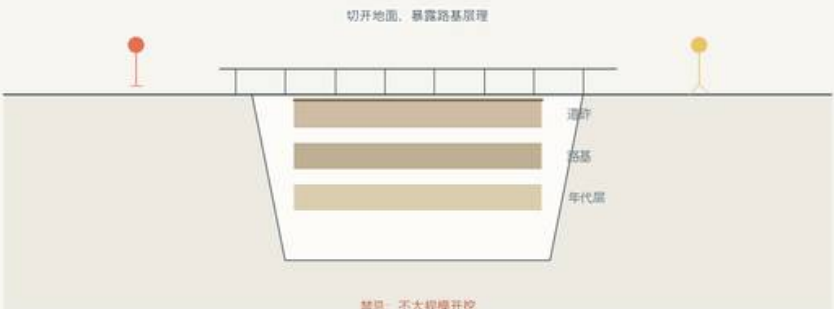

禁忌：不大规模开挖

声景层 · 蒸汽×白噪

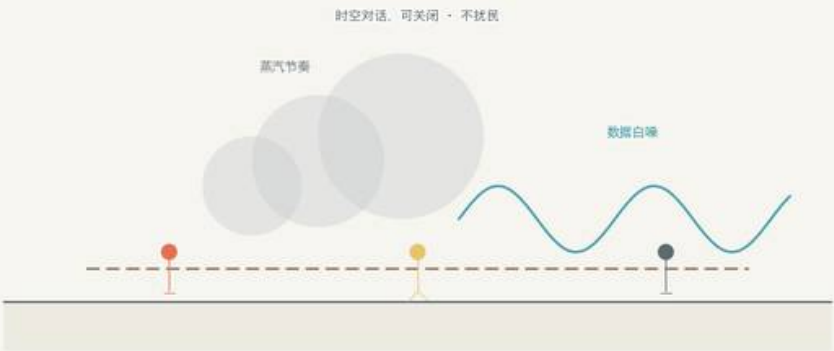

禁忌：不做噪声装置

设施层 · 轨成家具



禁忌：不伪造原址原件


进组件库的三条规则

- ① 清权 + 安全检测之后，才谈转用
- ② 随 Inherit 版本化：可加入 · 可退出 · 可继承
- ③ 声景与碑文先试点，许可与人工审核前置

五种转译共用一条地图：轨不离地，地不离街。

遗产显魂：分级 · 口述 · 以人为轨

从保护遗产到续写京张 | 考古三级 × 口述三声 × 人字坡三次转身 | A-HERITAGE-001 方法框架

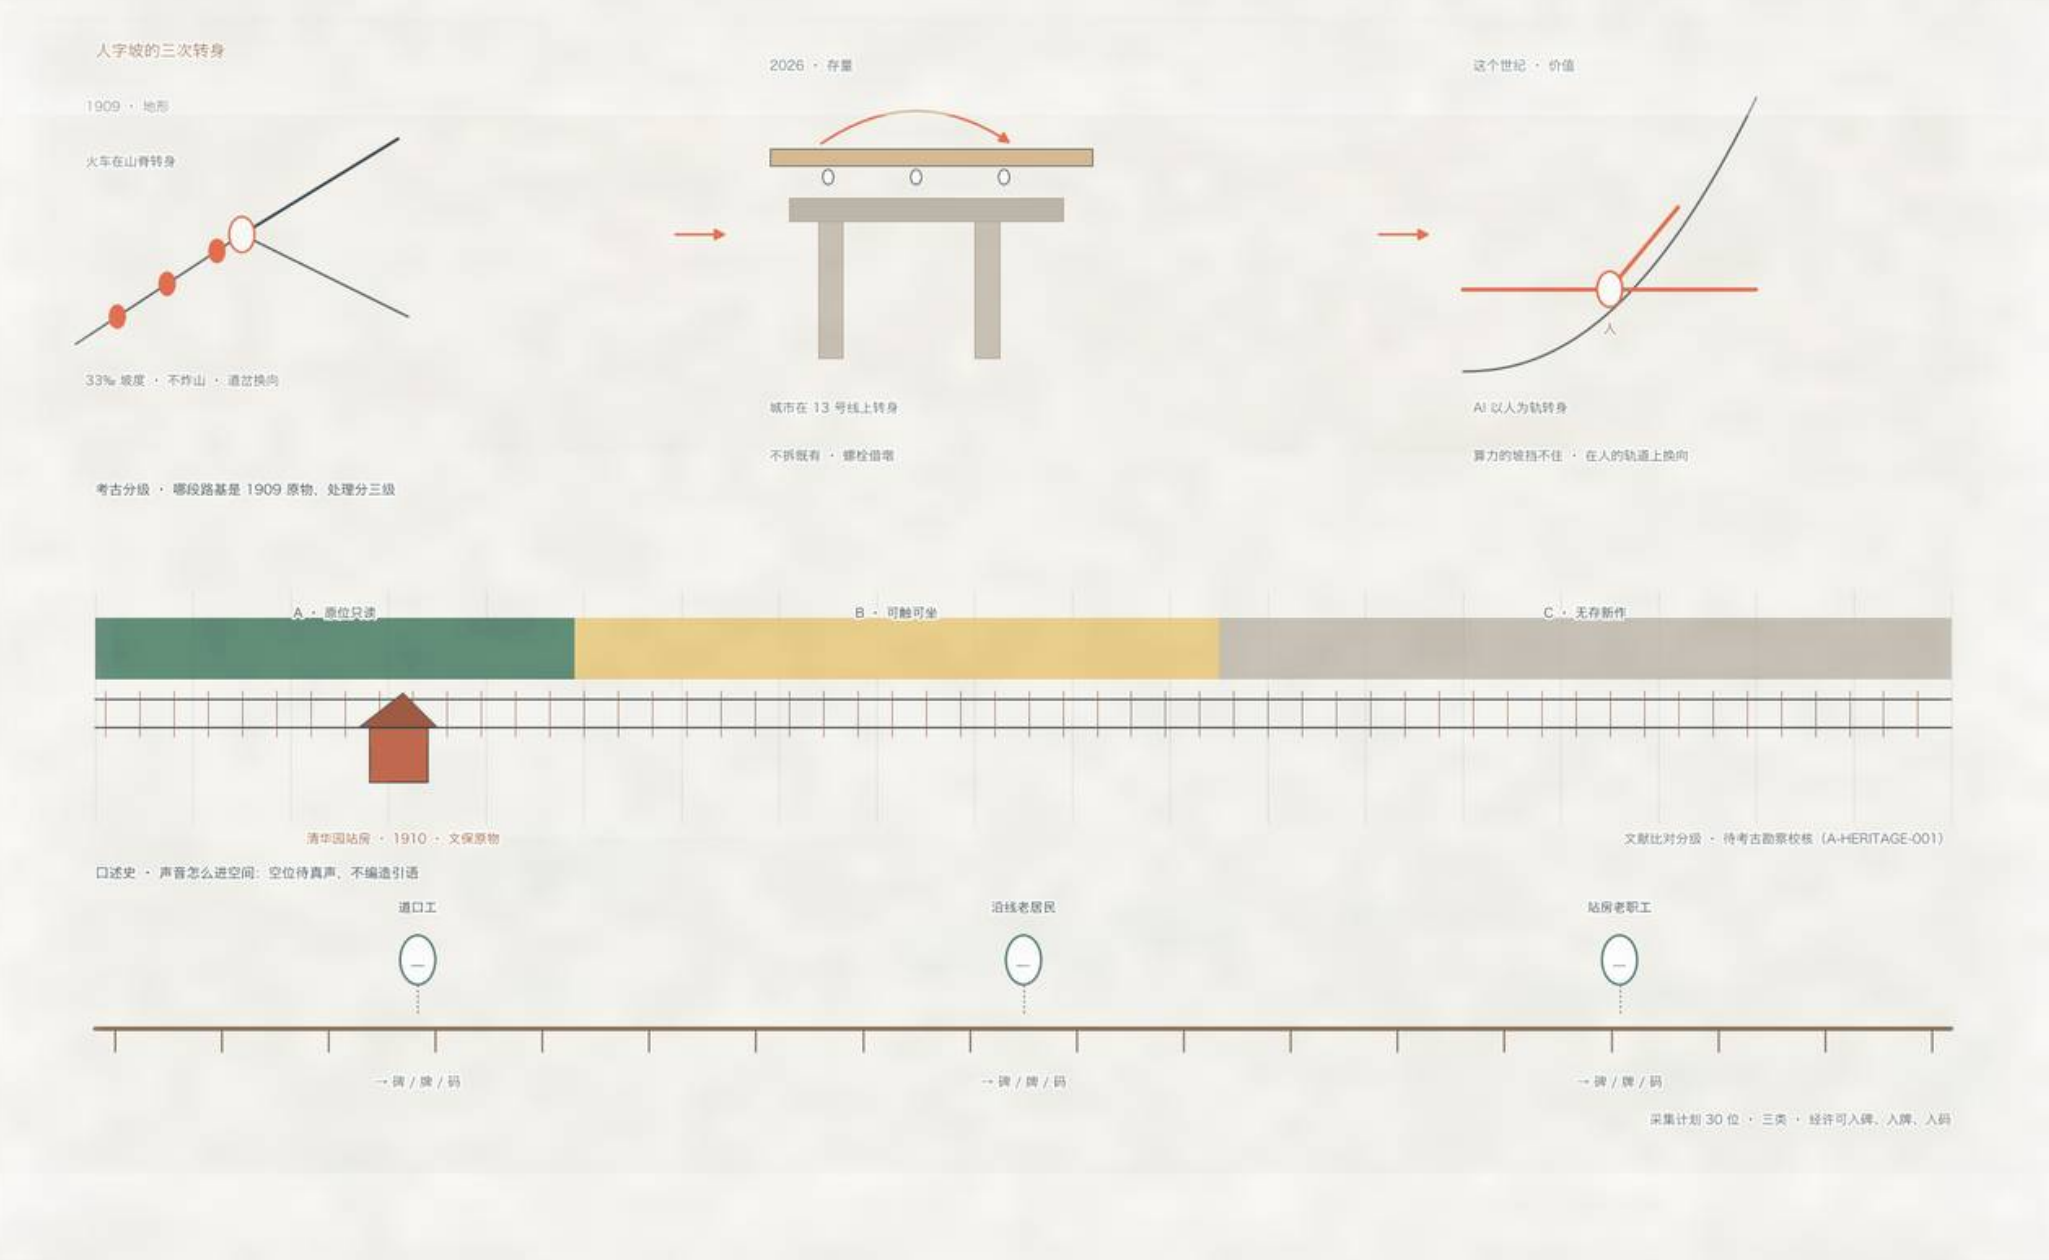

以人为轨

人字坡的「人」

1909 的「人」字，

写的是线路的形状。

这个世纪的「人」字，

写的是价值的归属。

铁路解剖学 → 当代对应物

道岔 (转向) = 核验 / 退出闸

避难线 (收容失控) = 失败案例库

试车段 (新车不上正线) = 治理沙盘

轨 = 人类价值观 (不是算力)

三层各就各位

分级 · 对物 (1909 原物分级处理)


口述 · 对人 (声音经许可进空间)

转身 · 对时代 (AI 以人为轨)

分级为文献比对框架 · 待勘察校核

口述为空白 · 待真实采集 (A-HERITAGE-001)

双线 Openline · 三条缝合 · 真实轨道与站点 · 断点只标问号进清单 (不画假桥隧) | 底图 OSM

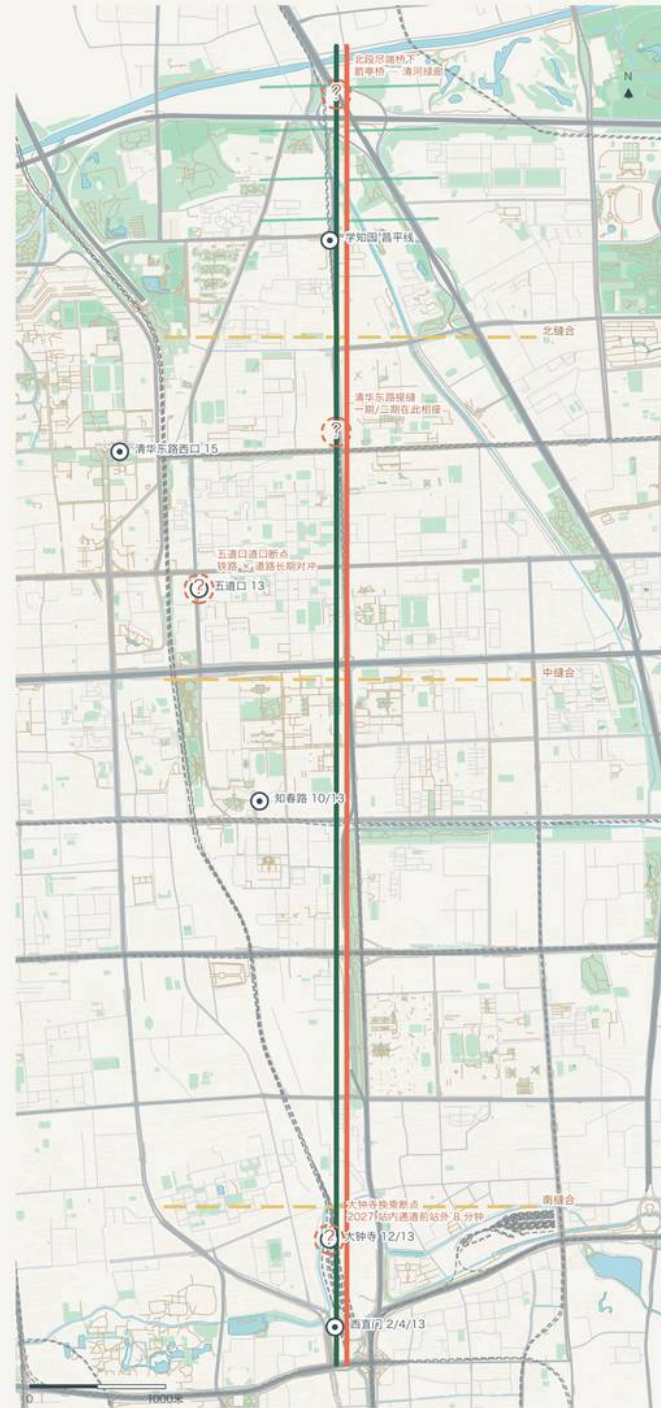

-
- The diagram illustrates the relationship between different types of lines and points in a research context. It consists of several horizontal lines of different colors and a red circle at the bottom left.
- L1 历史证路线：慢行优先 · 树冠连续** (L1 Historical Evidence Route: Slow travel priority · Tree canopy continuity) - Represented by a black line.
 - L2 Openline 服务线：驿站 · 场票入口** (L2 Openline Service Line: Station · Ticket entrance) - Represented by an orange line.
 - 三条东西缝合：接高校/社区/站点** (Three East-West Sutures: Connecting universities/community/stations) - Represented by a yellow line.
 - 二阶已建成鱼骨慢行（接上不重画）** (Second stage completed fishbone slow travel (connected to above, not redrawn)) - Represented by a green line.
 - 真实轨道：13/12/15/昌平线等（OSM）** (Real track: 13/12/15/Changping Line etc. (OSM)) - Represented by a grey line.
 - 蓝绿骨架：公园脊 + 清河/小月河** (Blue-green skeleton: Park spine + Qinghe/Xiaoyue River) - Represented by a blue line.
 - 断点 = 研究问号，进 OL-O1 清单** (Break point = Research question mark, enter OL-O1 list) - Represented by a red circle containing a question mark.

断圆逻辑（非工程设计）：

- L1 步行为主，骑行为辅，树冠连续
- L2 允许服务车与应急，仍慢行优先
- 步行路权全时 $\geq 50\%$ 断面（不完美）
- 缝合线交叉口人行过街与视距优先

最新断点已给概念性工程方案:

五道口三层结合甲板 OL-07 (待红线深化)

边界 provisional · 讨论级概念建议 · 非审批几何 · 正式数据到位后整包复算

生态的数字承诺：每期可核验的目标

碳预算 · 径流控制率 · 热岛降幅 · 生物多样性净增益 · 树冠覆盖 | 传感进信托。Verify 闸公开 | 目标承诺 A-ECO-001



承诺不是口号 · 每个数都要监测

怎么测

L1 传感杆 + 年度调查

径流计量 · 地表温度

材料台账 · 能耗分项

样方样线 · 树冠遥感

谁来验

数据信托只进不出

受托人持证开启

Verify 闸按季公开

不达标怎么办

组件库版本化整改

目标不悄悄改写

缺口写进公开纪要

为什么敢承诺

可逆先行 → 试铺成本低

目标取自公开实践区间


官方数据到位即复算

16 生态的数字承诺：每期可核验的目标 · 目标承诺

边界 provisional · 讨论级概念建议 · 非审批几何 · 正式数据到位后整包复算

谁在 Openline 上相遇：AI 创新生态关系图

角色类型 + 关系流 + 空间接口 · 不点名机构 · 不编造投资额与名单

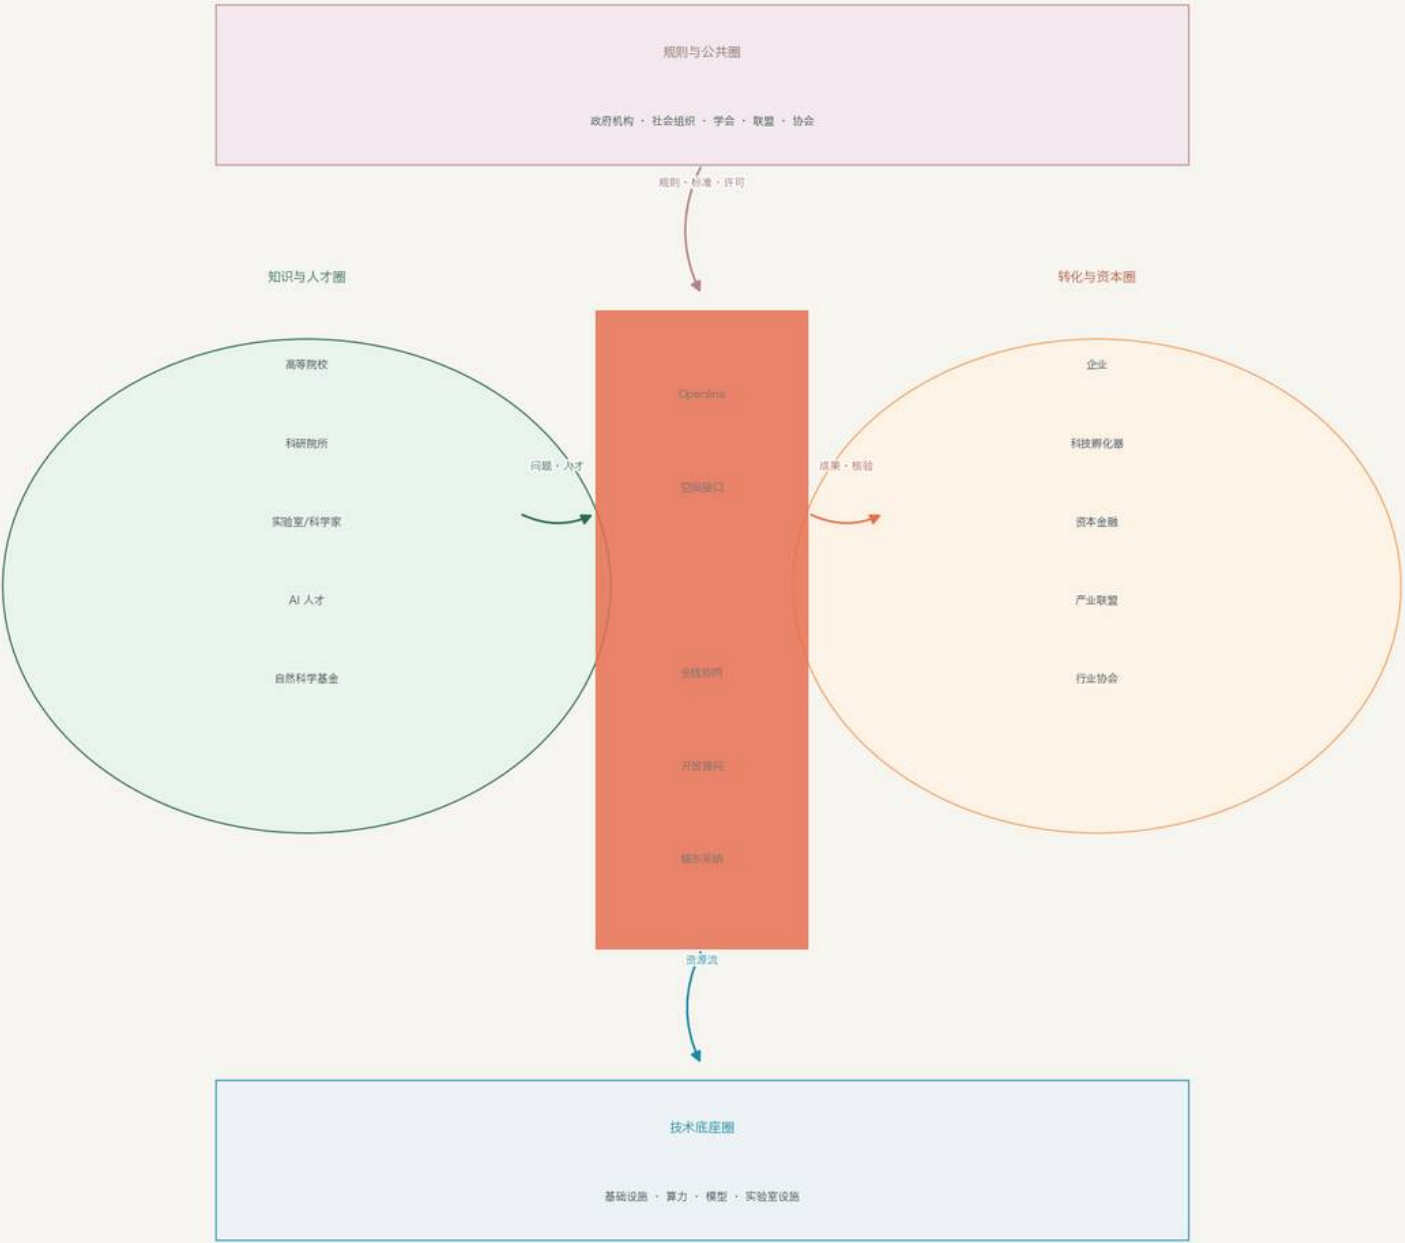

四条关系流（图谱的「边」）

问题—研发流

原点 → 众智圈：高校/科学家提问 → 全栈联合研发与治理复核

研发—采纳流

众智圈 → 大神寺：过治理门的能力上街；采用反馈与失败回流

资源流

底座 — 全带：算力经驿站进场景；资本只在对接界面出现

公共流


规则圈 — 公开议事：Join/Exit 进出，Inherit 沉淀组件与纪要

机制八要素：土地 · 空间 · 产业 · 资金

· 人才 · 算力 · 数据 · 场景

Open Ticket 制度剖面：Openline 的票制

路权在数字时代的续写 | 加入 · 核验 · 退出 · 继承 × 治理 / 空间 / 数据 / 时间 四层 | 治理概念图

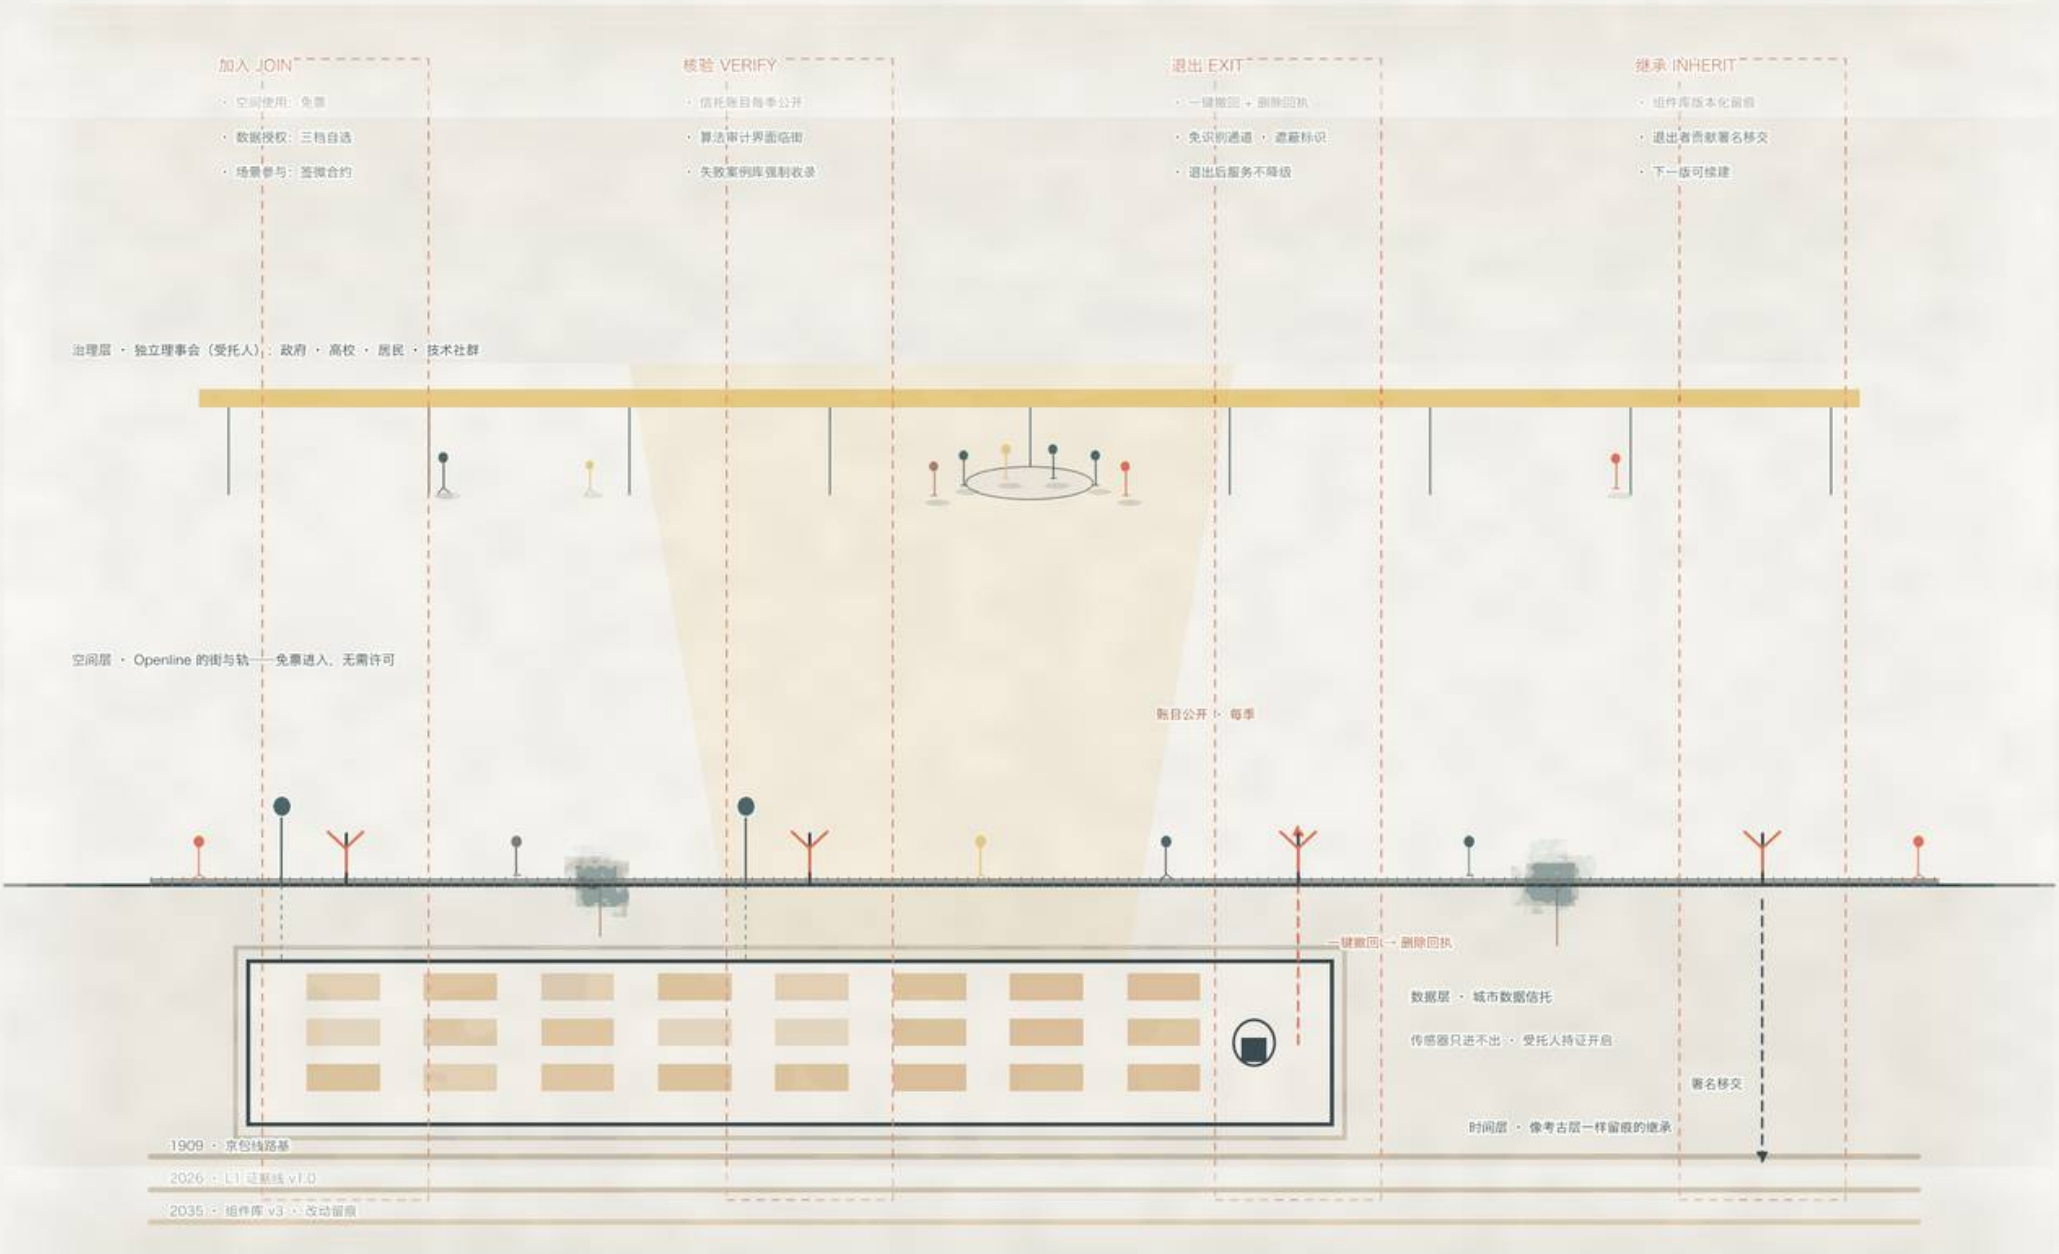

路是 Openline,

票是 Open Ticket。

- 1909: 京张争的是路权自立
- 2026: 续写数字时代的市民路权
- 路没有票制只是工程
- 有了票制才是公共服务

四层 × 四通闹

治理 谁在受托 · 空间 免费进入
数据 信托上锁 · 时间 留痕继承


治理概念图 · 非已定制度

机制待与衔接 / 数据主管部门共建

18 Open Ticket 制度剖面：加入 · 核验 · 退出 · 继承

哪些量已复算、哪些仍待正式数据

第一类可复算 (provisional 置信度) · 第二类街区结构已知/地块强度未知 · 第三类运营绩效入 assumptions

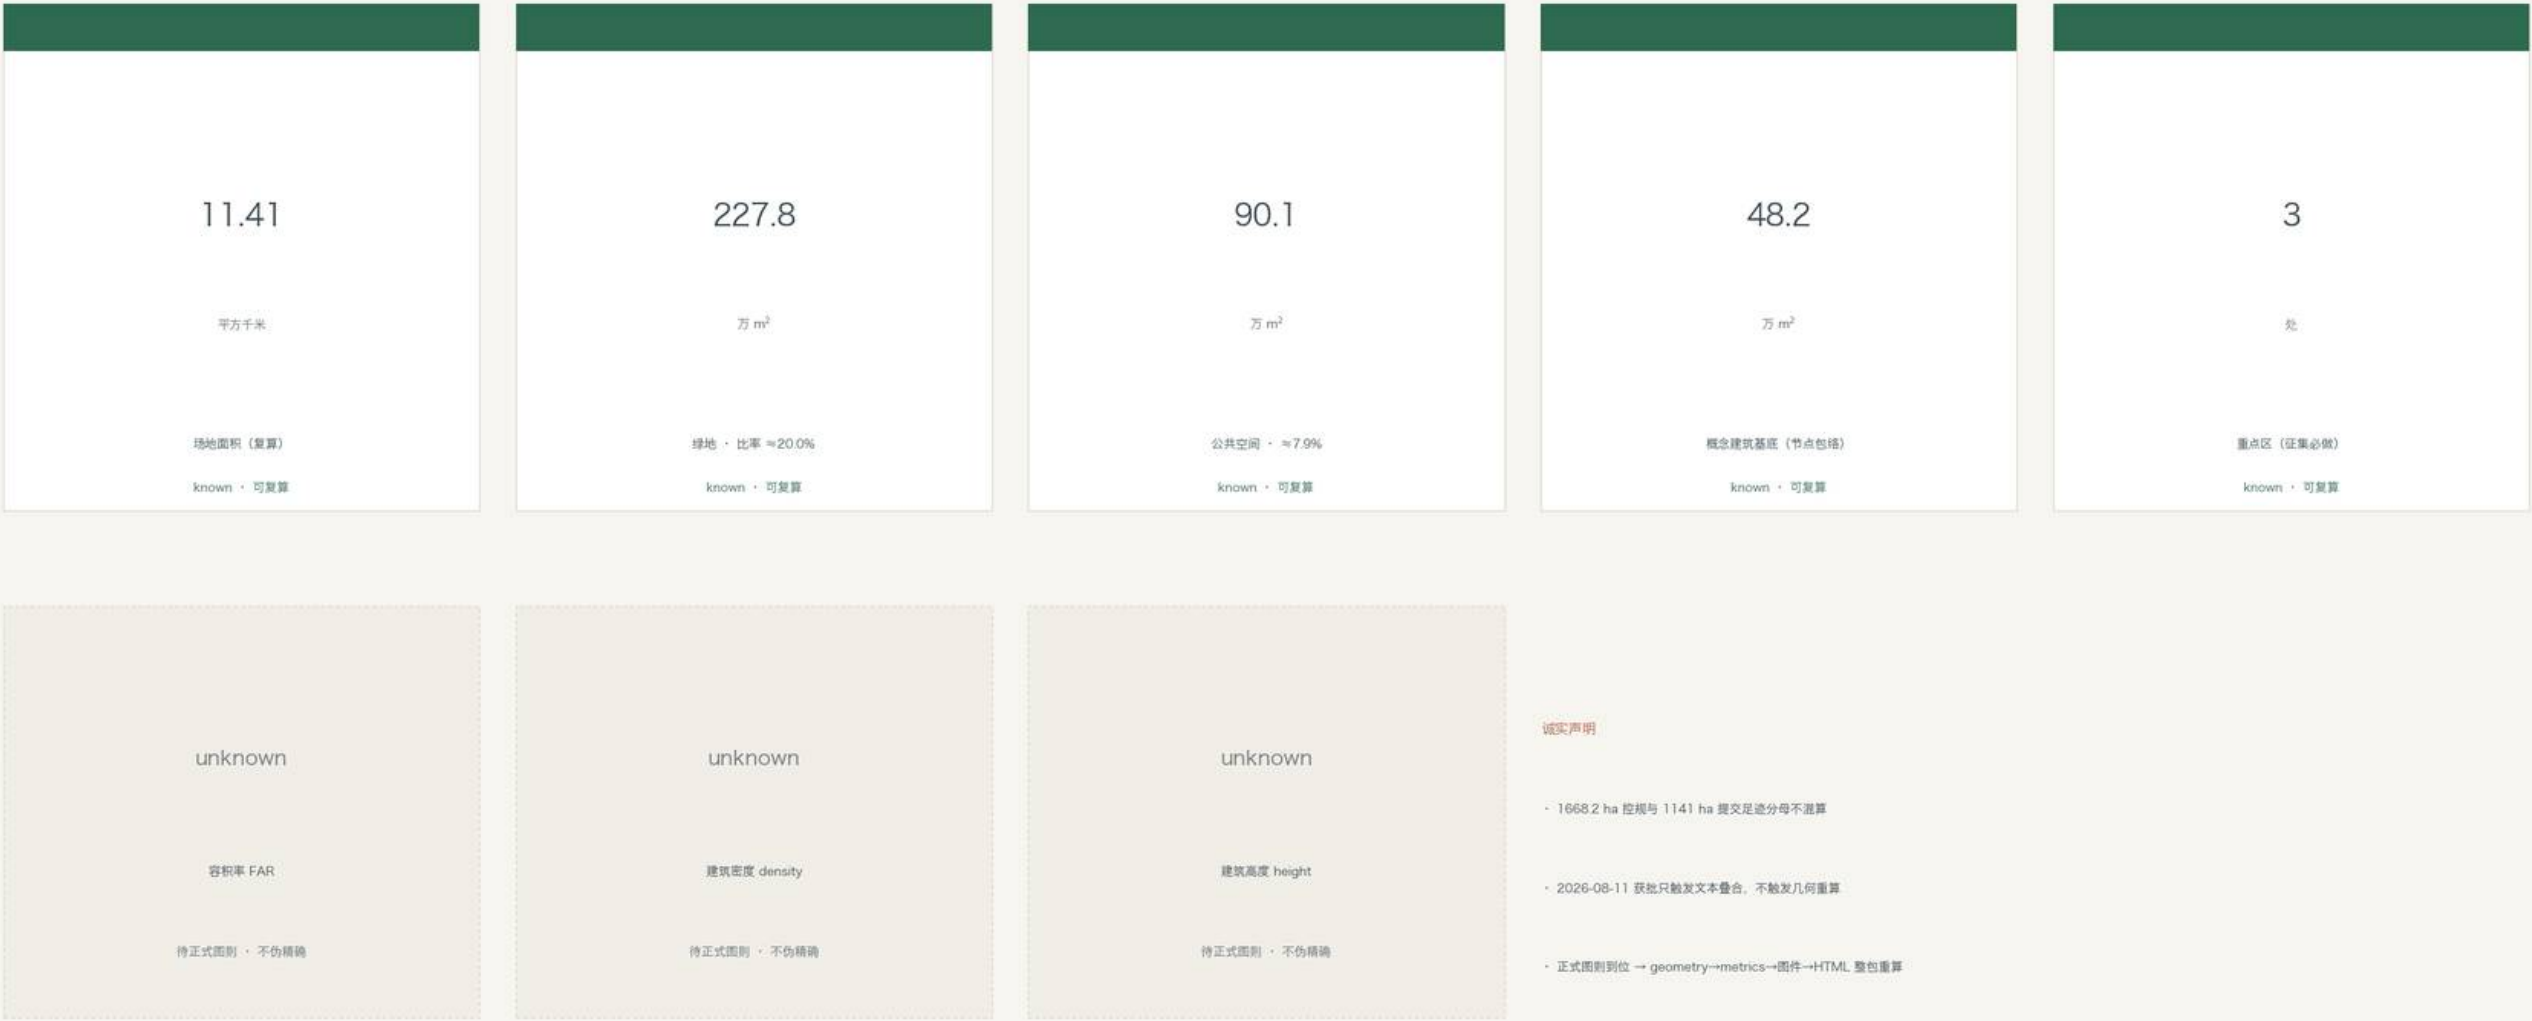

OPENLINE-100 · metrics-evidence · source: metrics.json recalculated in EPSG:4548 · BOARD v1.2

19 指标证据：全部数字可追溯 metrics.json

边界 provisional · 讨论级概念建议 · 非审批几何 · 正式数据到位后整包复算

公共空间先行，强度奖励跟进：0 - 1 · 1 - 3 · 3 - 10

与 OL-01 - 10 项目清单同一套动作 · 分期不是资金计划 | 底图 OSM 真实肌理 | 虚线 = 尚未落地

0 - 1 年 · 样板



1 - 3 年 · 成街



3 - 10 年 · 网络



0 - 1 年 · 样板

- 原点到达面先动
- KMO + 中缝合样板
- 驿站单点原型

1 - 3 年 · 成街

- 一组可升级单元成街
- 智能原生街道试点
- 授权窗口与发布厅

3 - 10 年 · 网络

- 三区协同网络展开
- OL-07 甲板进中期库
- 治理中心深化

OPENLINE-100 · key-phasing · 0 - 1 / 1 - 3 / 3 - 10 on real fabric · BOARD v1.2

20 分期实施：2026 → 2030 → 2035

边界 provisional · 讨论级概念建议 · 非审批几何 · 正式数据到位后整包复算

分期资本逻辑：可逆即低风险

每期同时回答 建设 / 出钱 / 运营 / 回流 | 专项债 → 片区统筹 → 企业认养 接力 | 量级估算 A-CAPITAL-001



21 分期资本逻辑：可逆即低风险 · 量级估算

边界 provisional · 讨论级概念建议 · 非审批几何 · 正式数据到位后整包复算



22 走进 ①：L1 地面步道晨景



23 走进去 ②：五道口甲板午后



24 走进 ③: 大钟寺段鸟瞰黄昏