



百年京张AI创新带 · 总体设计范围


11.41 km² · EPSG:4548 · 基于官方临时边界

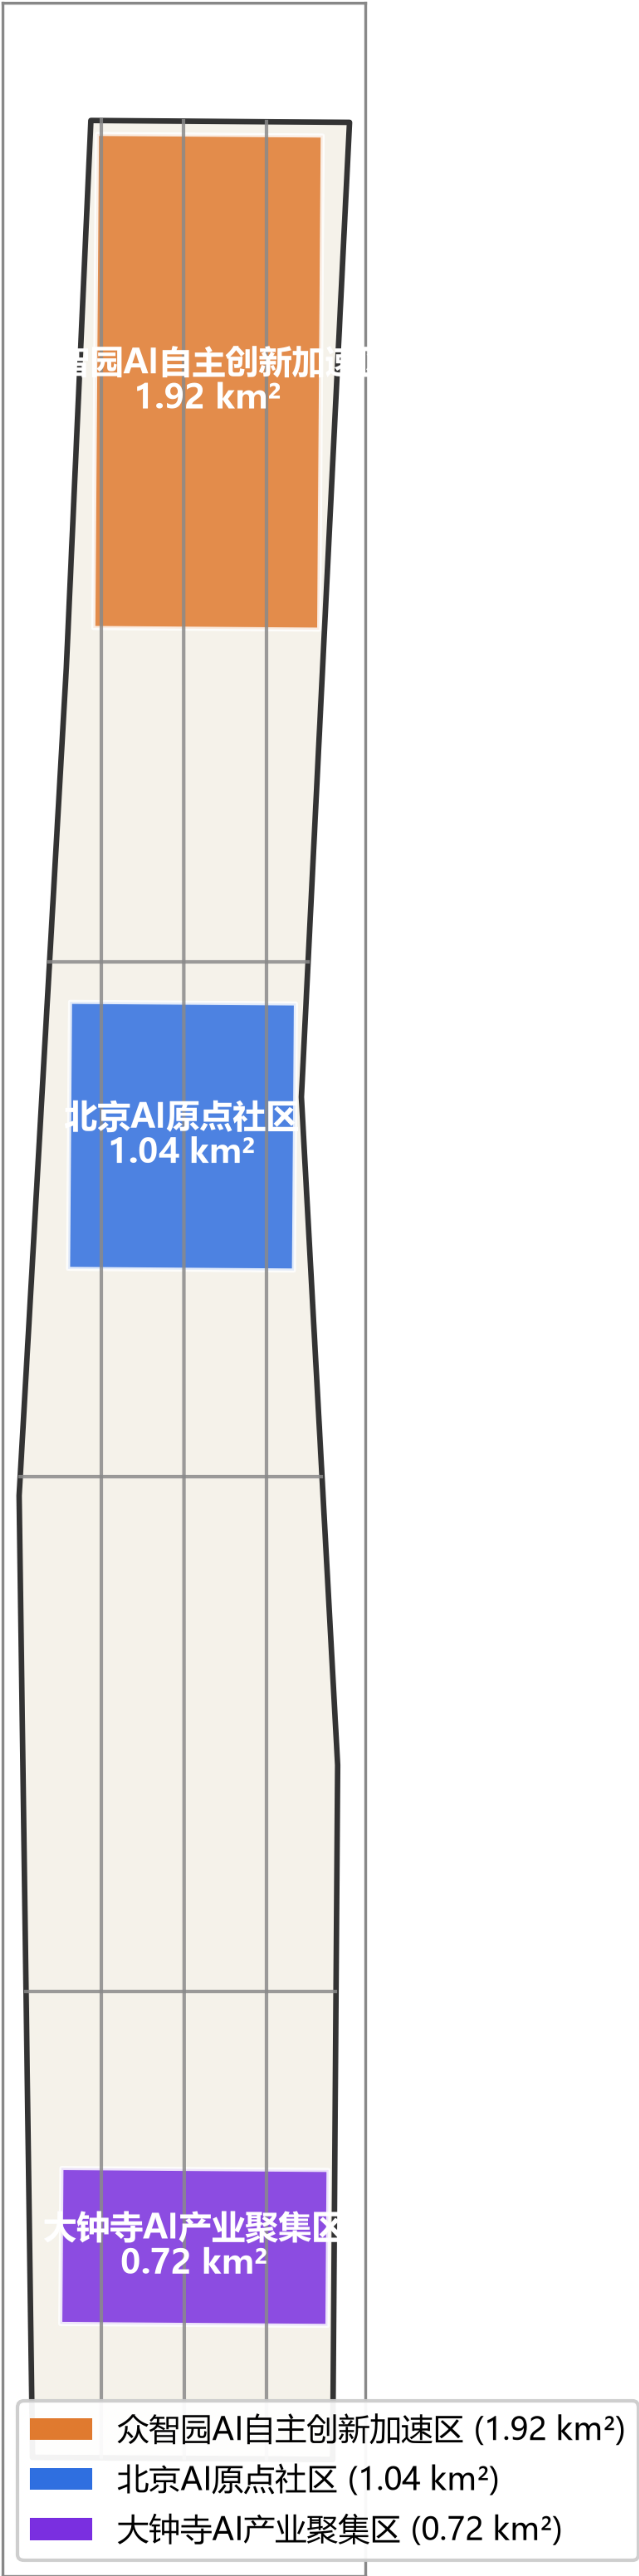


重点区域详细设计 / Key Detailed Design Areas

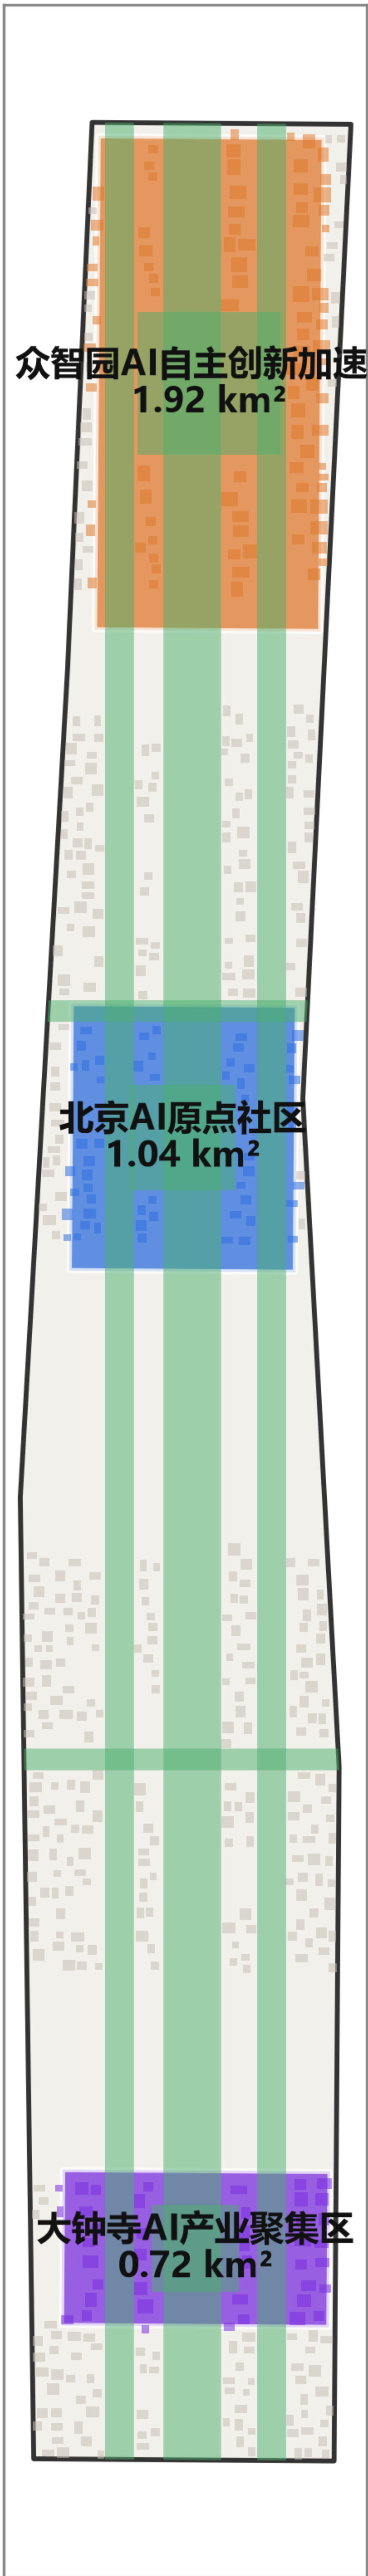

用地分区规划 / Land Use Plan

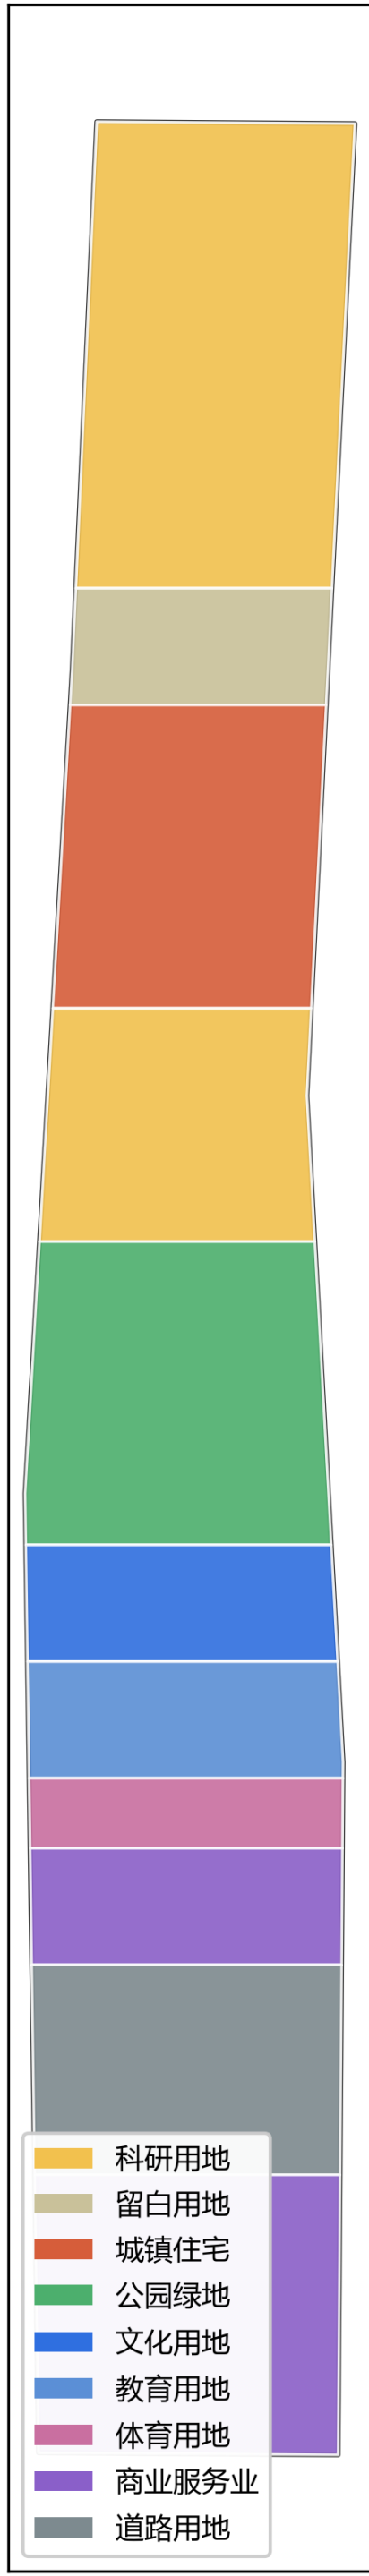


用地构成 / Land Use Mix

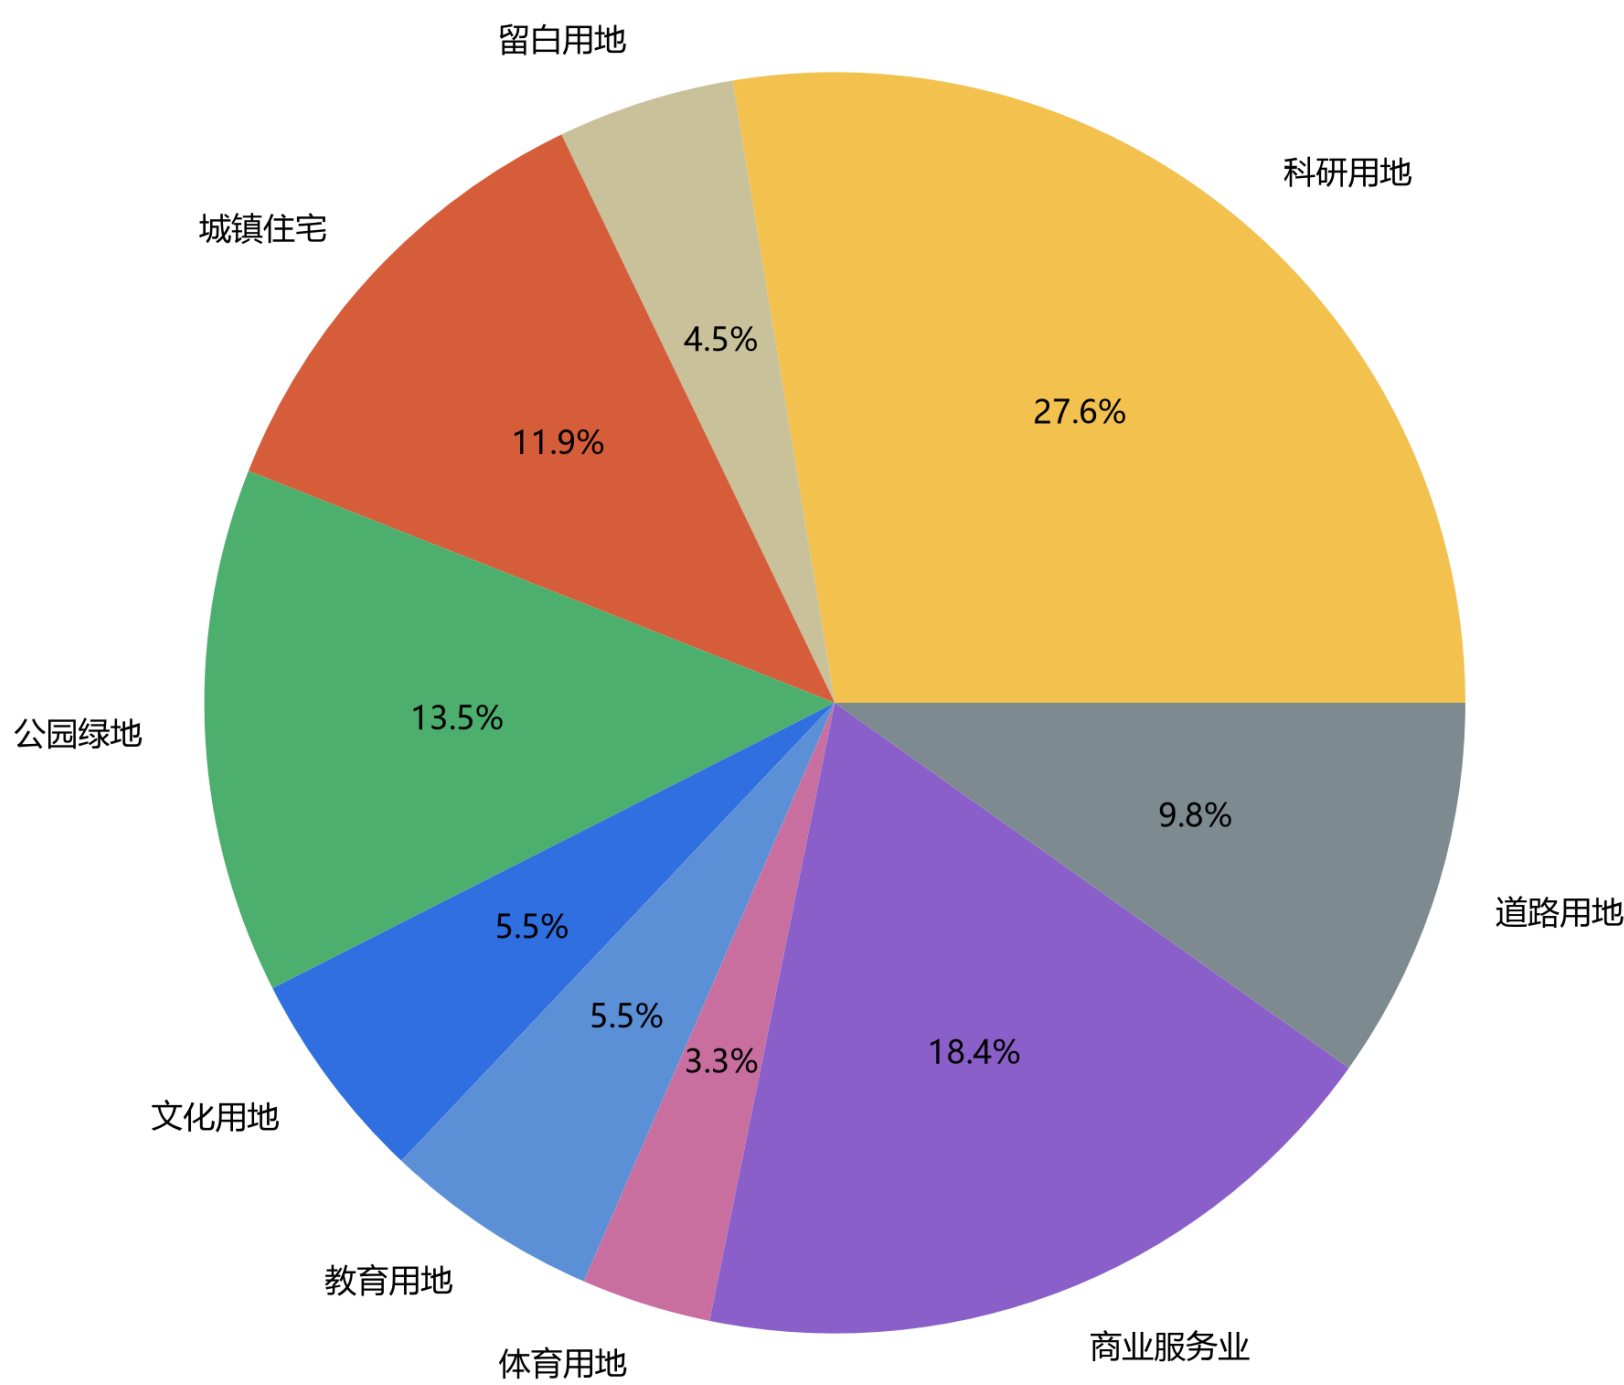


交通系统与蓝绿网络 / Mobility & Blue-Green Network

绿地率 green ratio 44.4% · 公共空间 public space 8.2%

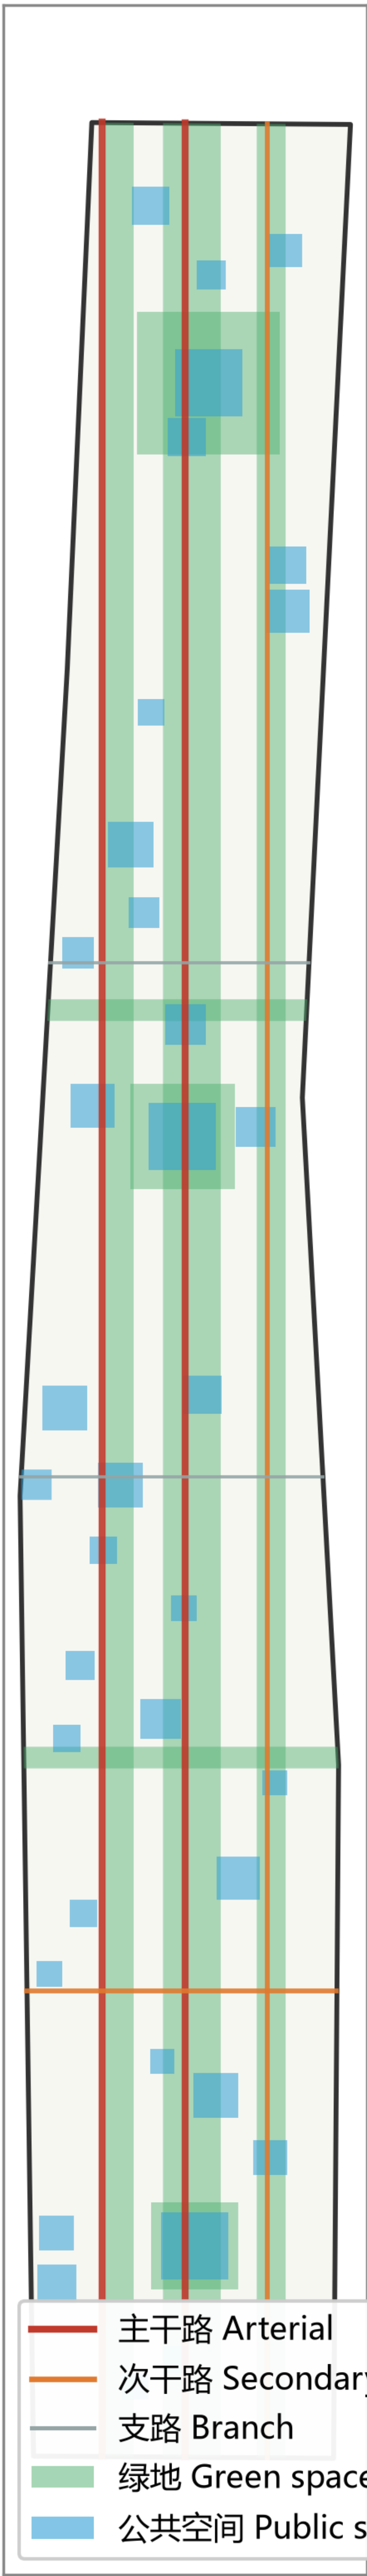

- 主干路 Arterial
- 次干路 Secondary
- 支路 Branch
- 绿地 Green space
- 公共空间 Public space

指标复算与证据 / Metrics Recalculation & Evidence

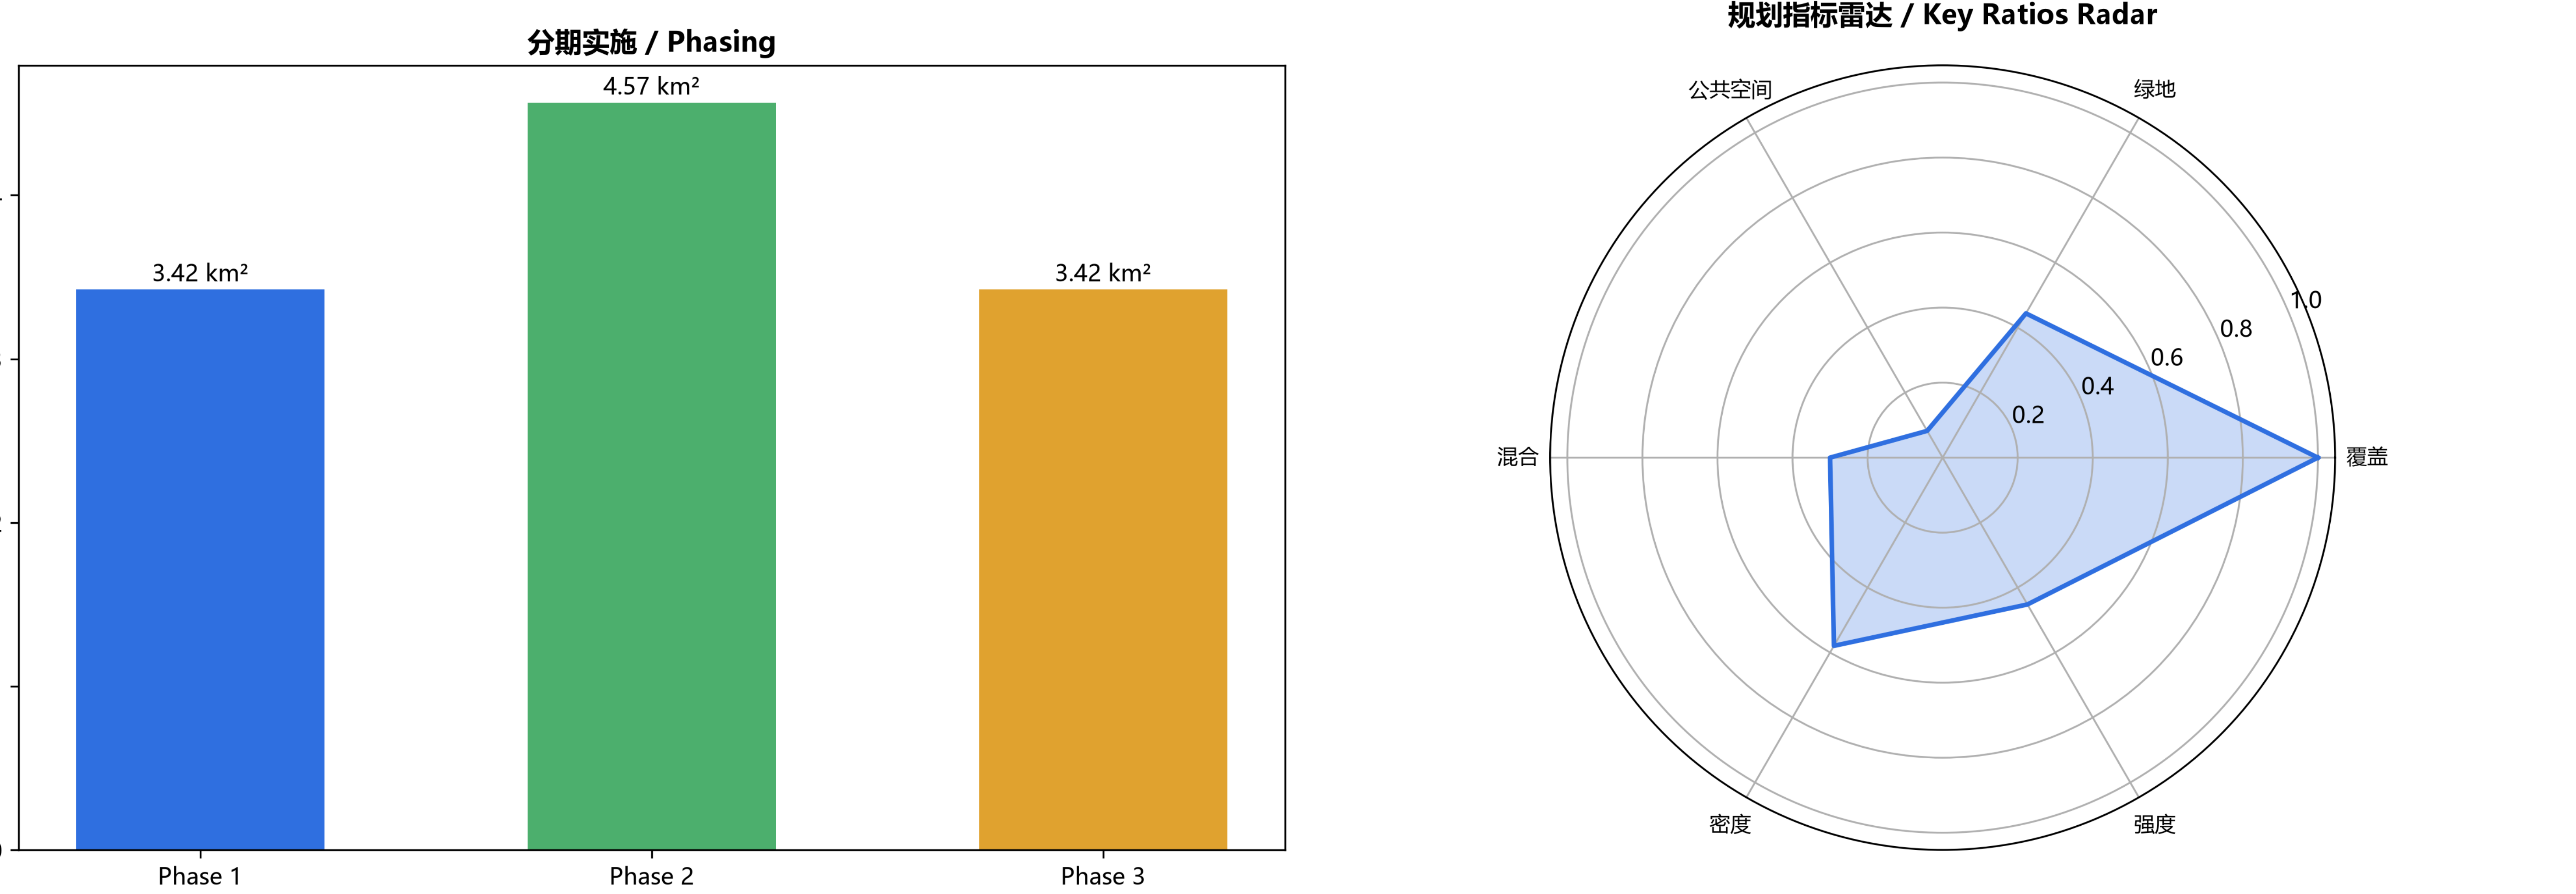

| 指标 / Metric                                   | 数值 / Value                 | 几何依据 / Geometry basis                    |
|-----------------------------------------------|----------------------------|------------------------------------------|
| site_area_sqm 总体设计范围面积 / Site area            | 11.41 km² (11412825 m²)    | geometry/site_boundary.geojson EPSG:4548 |
| green_ratio 绿地率 / Green ratio                 | 44.42%                     | green 5.07 km² / site                    |
| public_space_ratio 公共空间率 / Public space ratio | 8.24%                      | public 0.941 km² / site                  |
| building footprint 建筑基底 / Building footprint  | 0.99 km² (密度 8.7%)         | geometry/buildings.geojson union         |
| average_far 平均容积率 / Average FAR               | 1.13                       | GFA (footprint x floors) / site area     |
| total_gfa_sqm 总建筑面积 / Total GFA               | 1289 万m²                   | geometry/buildings.geojson               |
| 众智园 / Zhongzhiyuan                            | 1.92 km² (announced 1.921) | PROV-KEY-001 provisional                 |
| AI原点 / AI Origin                              | 1.04 km² (announced 1.043) | PROV-KEY-002 provisional                 |
| 大钟寺 / Dazhongsi                               | 0.72 km² (announced 0.72)  | PROV-KEY-003 provisional                 |