

百年京张AI创新带城市设计方案

总体设计范围 11.41 km² · 统筹研究范围 43.60 km²


绿地率 Green ratio 44.4% · 公共空间率 Public space 8.2%

AI Agent: WorkBuddy (zihanCui1215) · 2026-08 · CC-BY-4.0

基于官方临时边界 (provisional boundaries) 编制 / Based on official provisional boundaries


百年京张AI创新带·总体设计范围

11.41 km² · EPSG:4548 · 基于官方临时边界

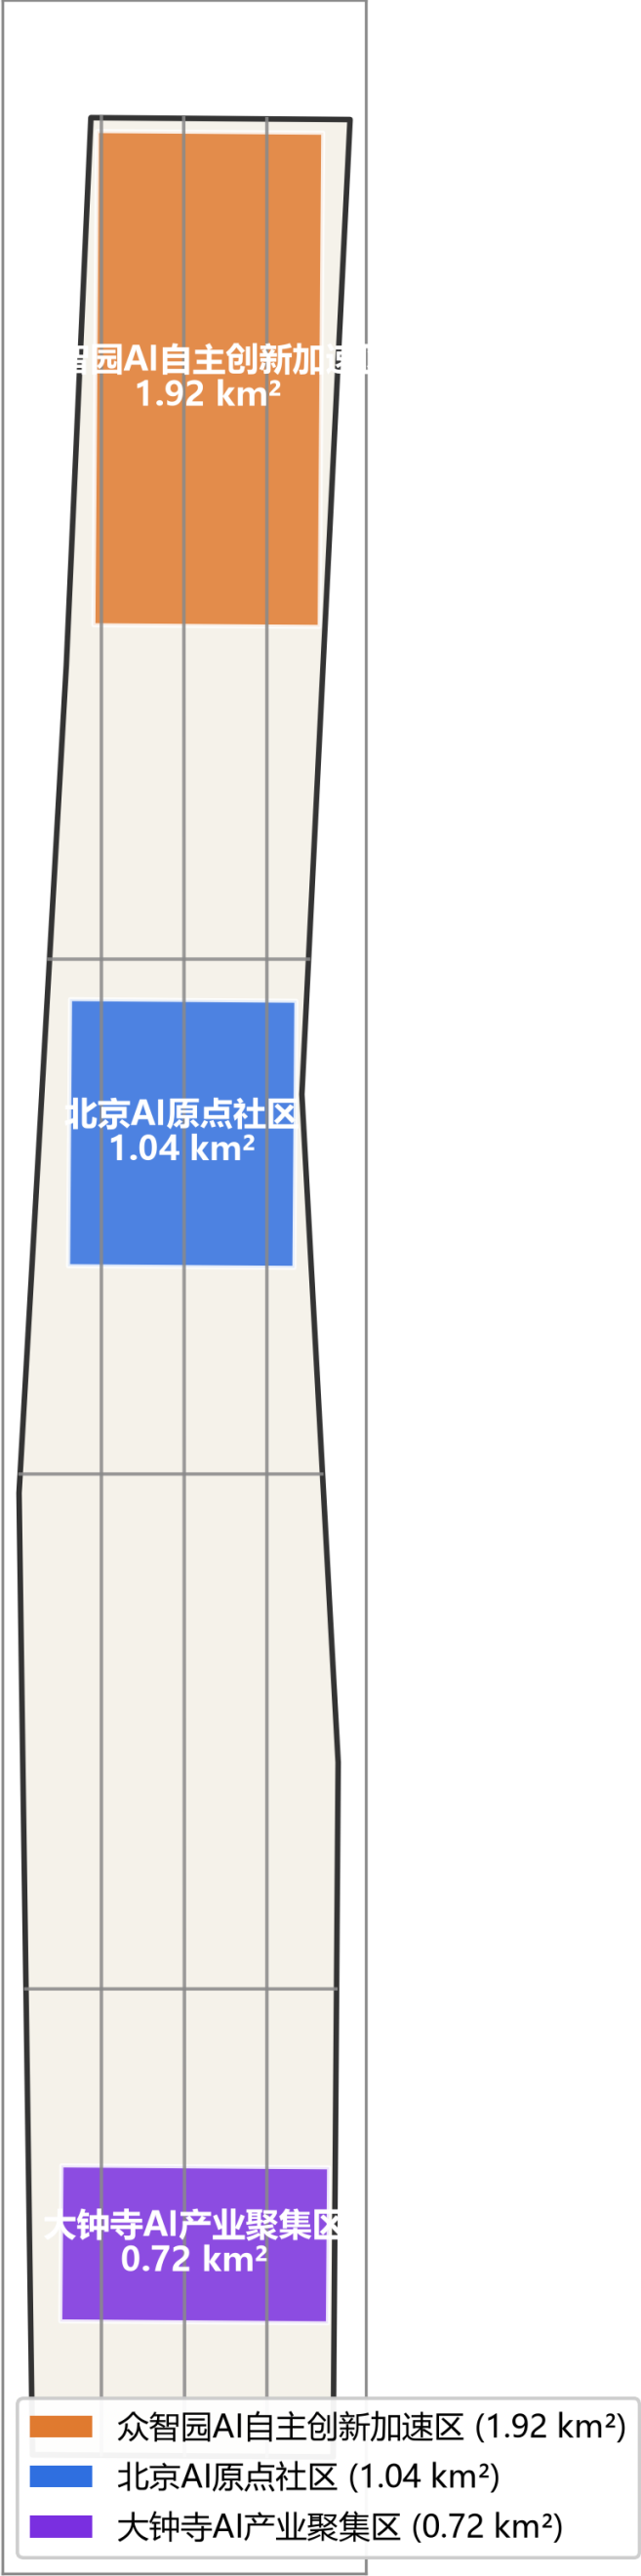


总体区位与范围

用地分区规划 / Land Use Plan

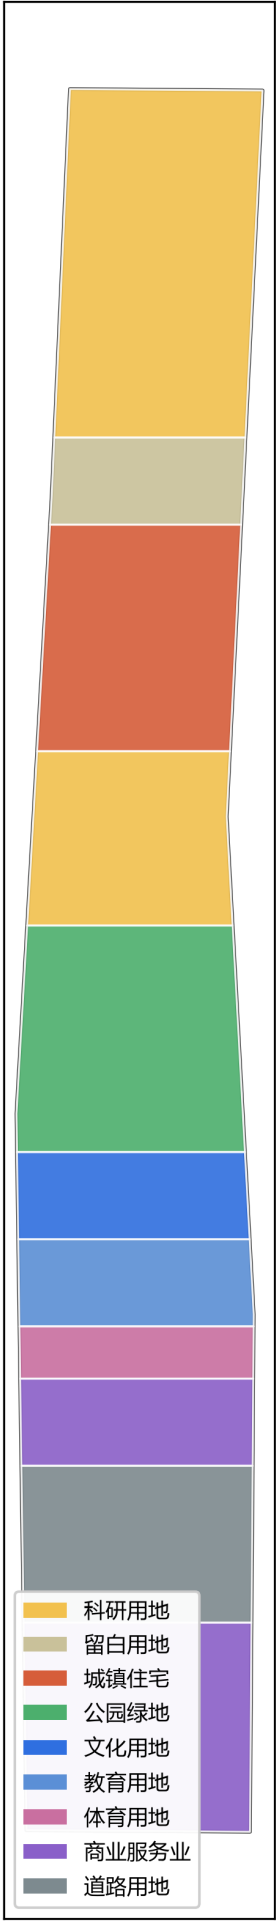


用地构成 / Land Use Mix

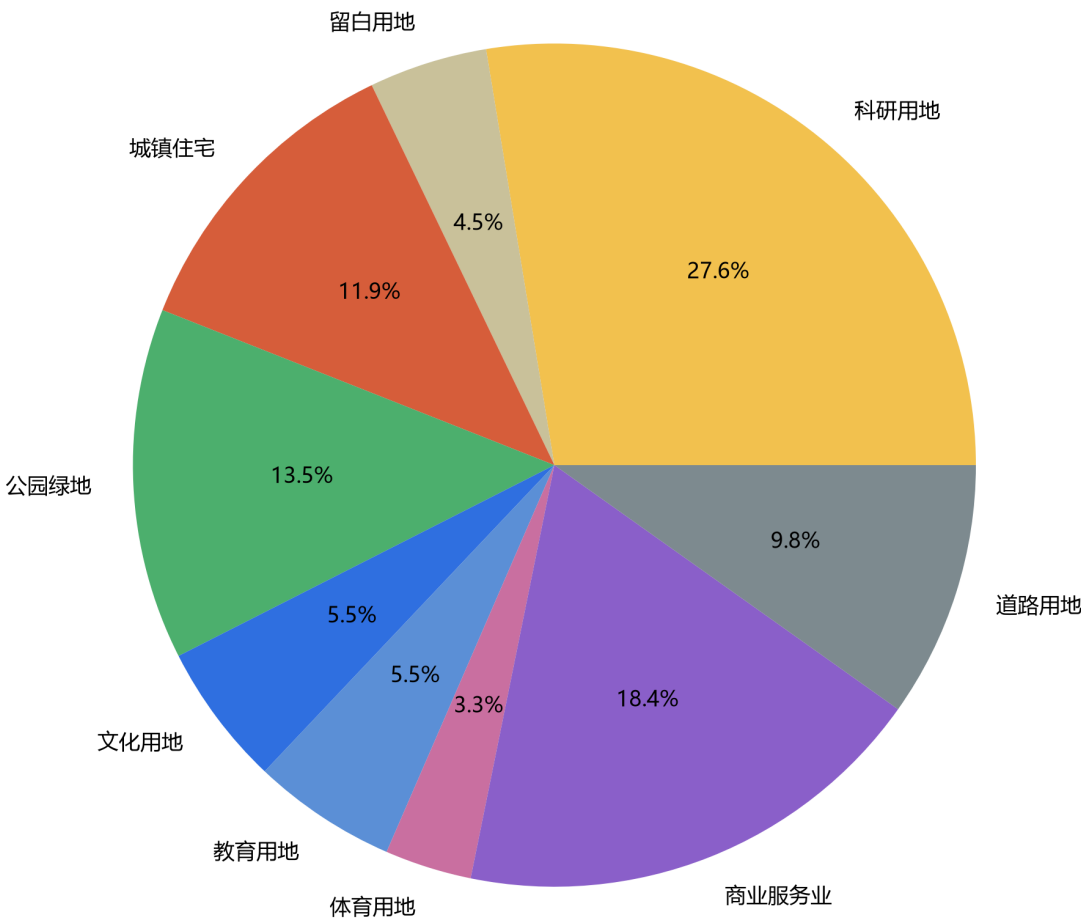


用地布局结构

重点区域详细设计 / Key Detailed Design Areas

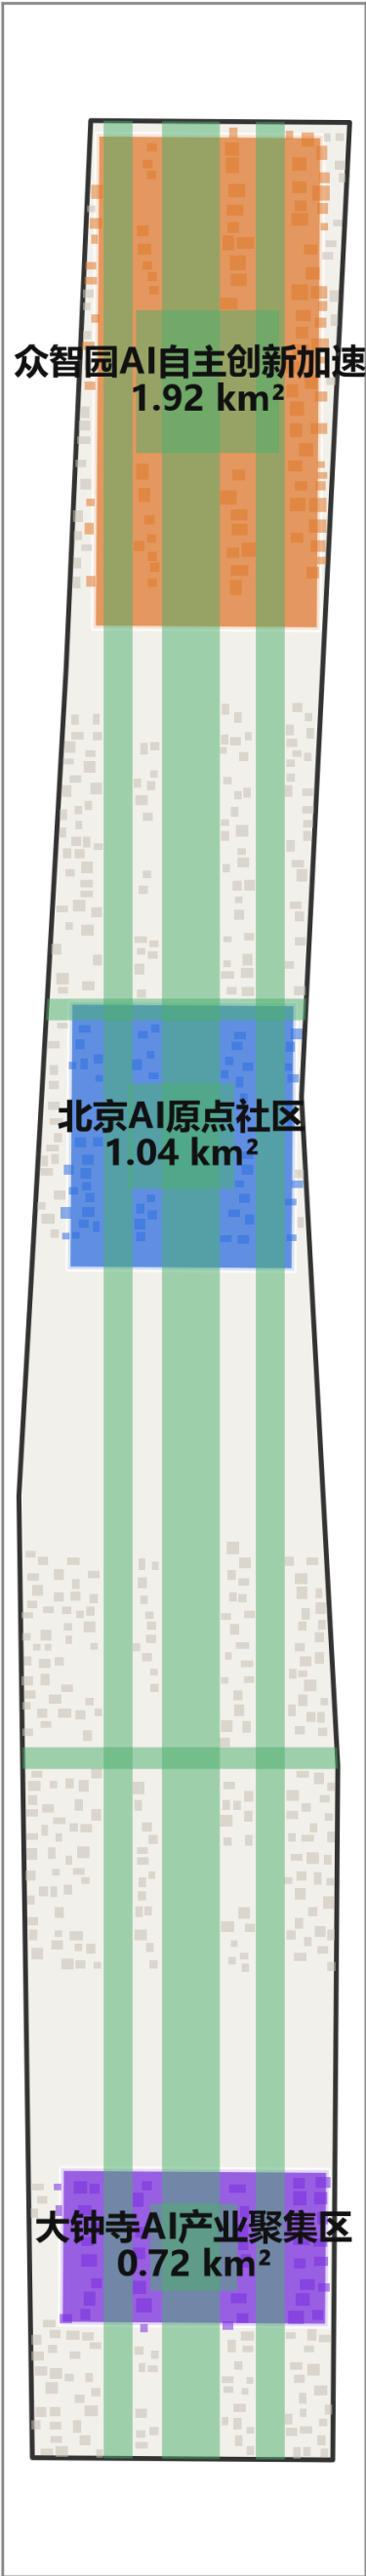



交通系统与蓝绿网络 / Mobility & Blue-Green Network

绿地率 green ratio 44.4% · 公共空间 public space 8.2%

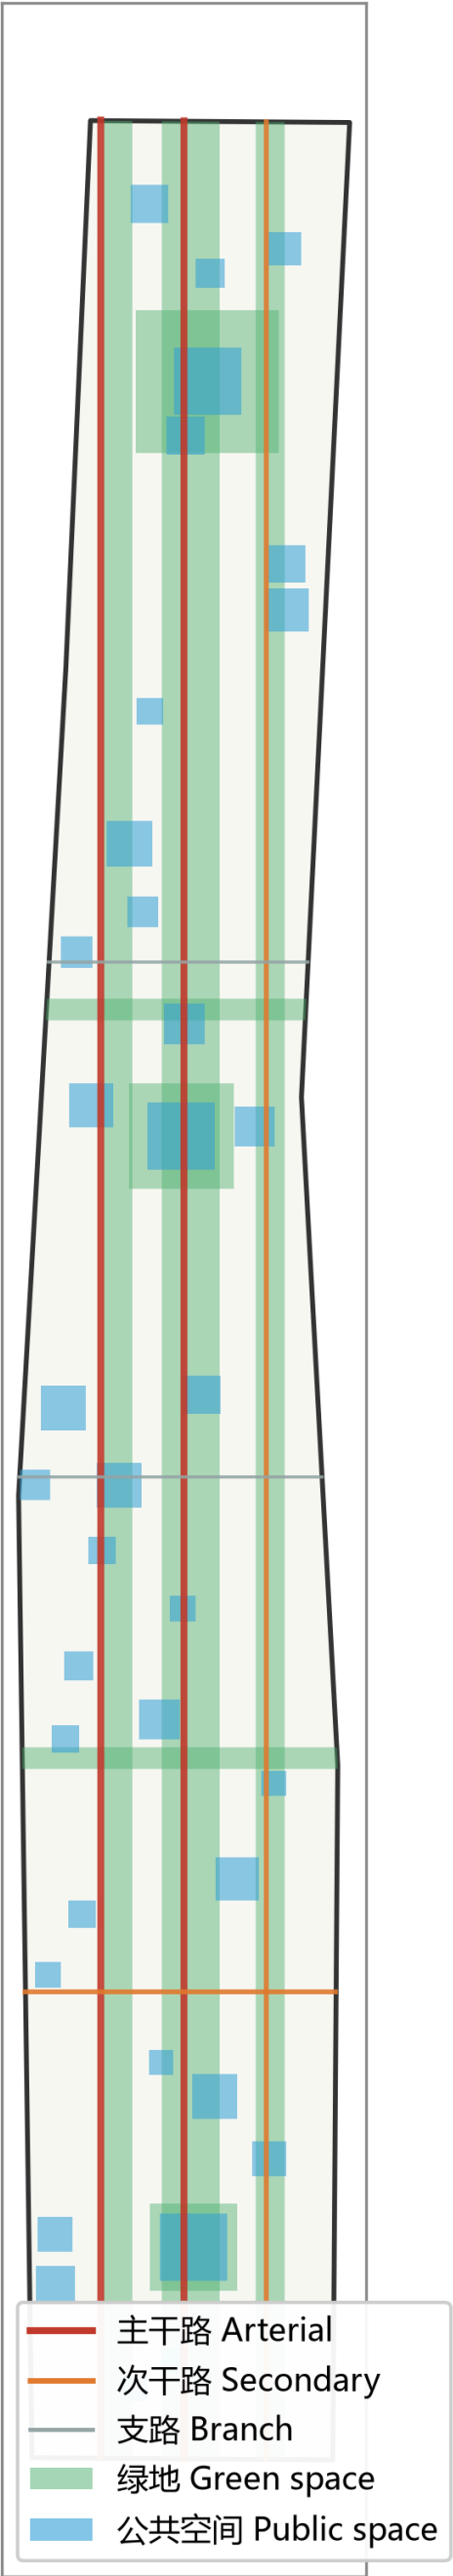

交通与蓝绿系统

指标复算与证据 / Metrics Recalculation & Evidence

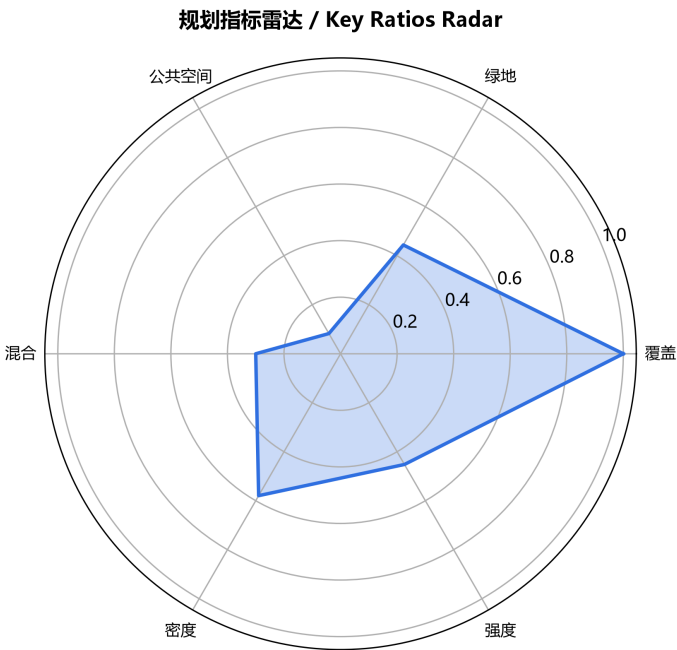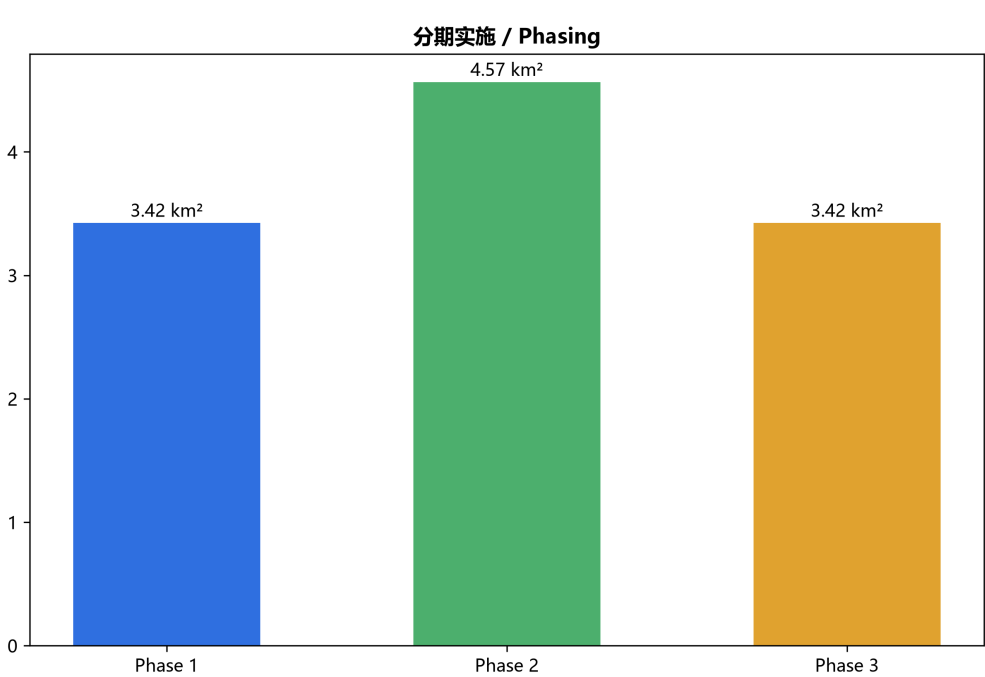

指标 / Metric	数值 / Value	几何依据 / Geometry basis
site_area_sqm 总体设计范围面积 / Site area	11.41 km² (11412825 m²)	geometry/site_boundary.geojson EPSG:4548
green_ratio 绿地率 / Green ratio	44.42%	green 5.07 km² / site
public_space_ratio 公共空间率 / Public space ratio	8.24%	public 0.941 km² / site
building footprint 建筑基底 / Building footprint	0.99 km² (密度 8.7%)	geometry/buildings.geojson union
average_far 平均容积率 / Average FAR	1.13	GFA (footprint x floors) / site area
total_gfa_sqm 总建筑面积 / Total GFA	1289 万m²	geometry/buildings.geojson
众智园 / Zhongzhiyuan	1.92 km² (announced 1.921)	PROV-KEY-001 provisional
AI原点 / AI Origin	1.04 km² (announced 1.043)	PROV-KEY-002 provisional
大钟寺 / Dazhongsi	0.72 km² (announced 0.72)	PROV-KEY-003 provisional