


43.6 km² 是城市网络，不是一条景观带

京张纵向公共骨架 × 八条真实横街 × 清河—小月河 × 西侧服务翼；灰虚线为临时研究范围。

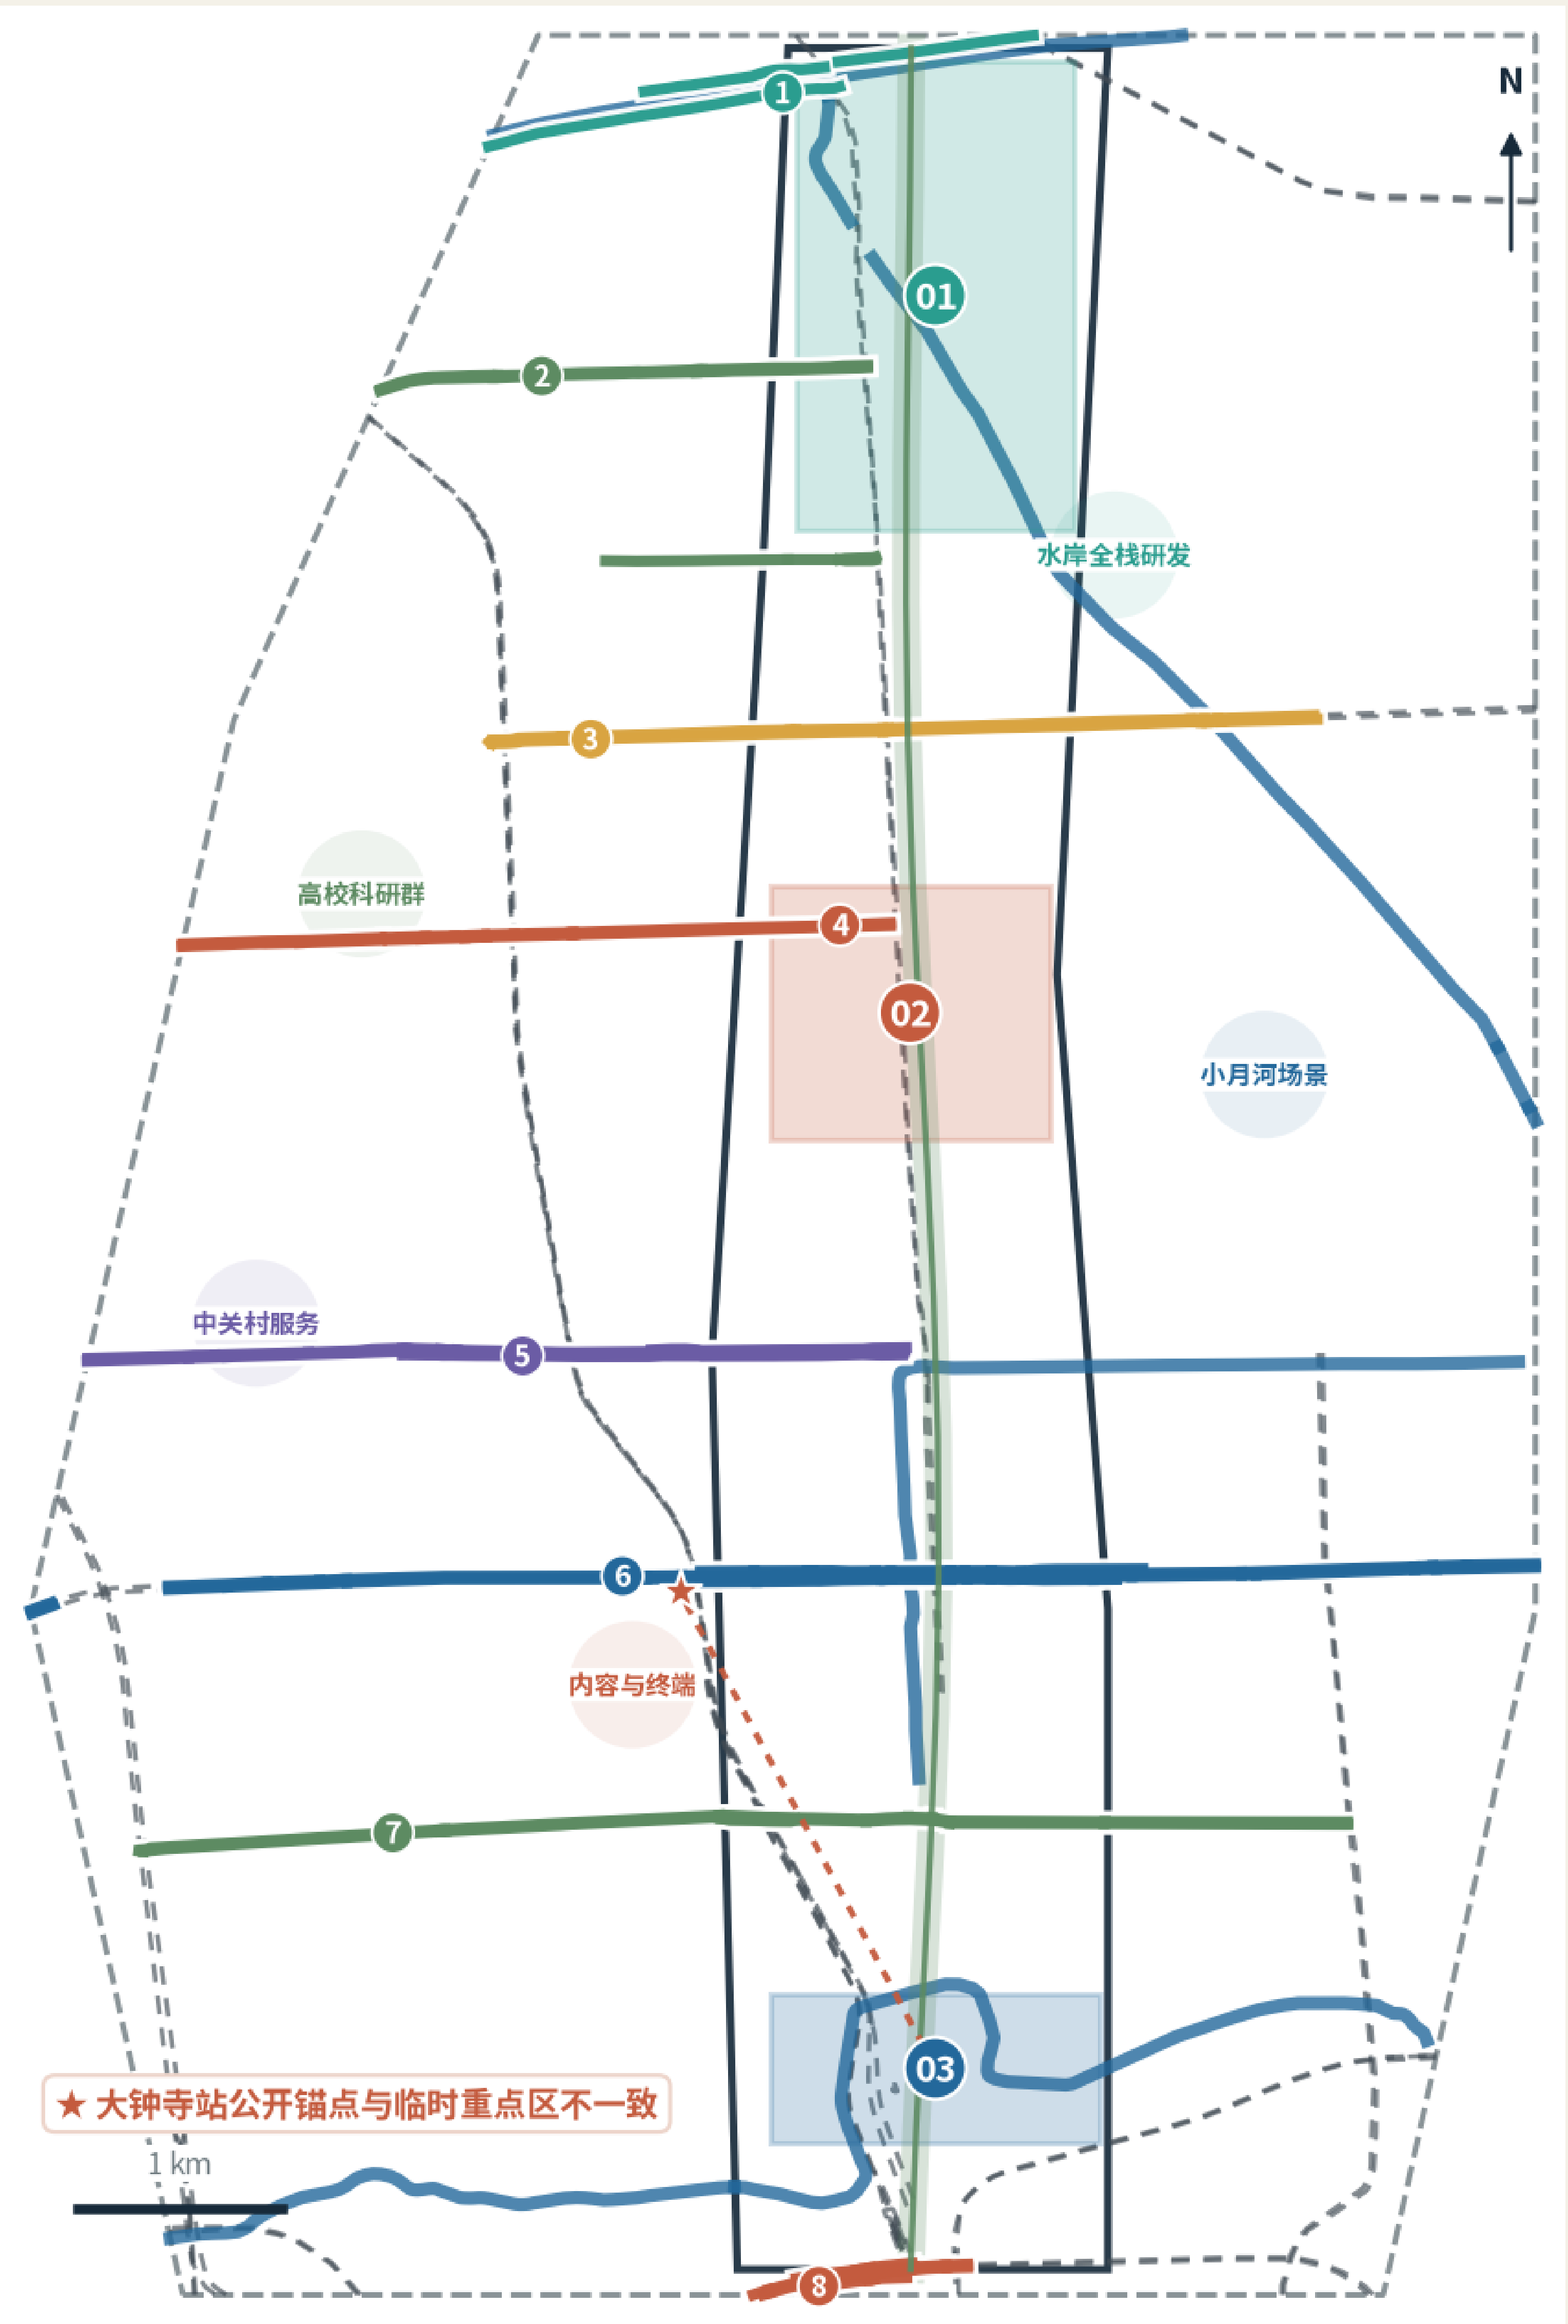

京张横街

让八条真实横向街道进入 43.6 平方公里创新城区

创新资源原本就在铁路两侧。设计的主角不是再造纵轴，而是让人横向穿过校园、社区、站口、产业首层与两条河。

43.6 km²

统筹研究

资源、交通、产业与蓝绿网络

11.4 km²

总体设计

用地、横街、街坊首层与公共空间

368.4 ha

三区详设

建筑前后台、站口、剖面与首批项目

三个可使用的地标

01 清河原型院


02 百桌评审厅

03 大钟寺四角台

现状→接口→街坊→运营

11.4 km² 概念用地不是留白

完整拓扑表达功能混合；非现状用地调查、非控规调整、非地块权利。

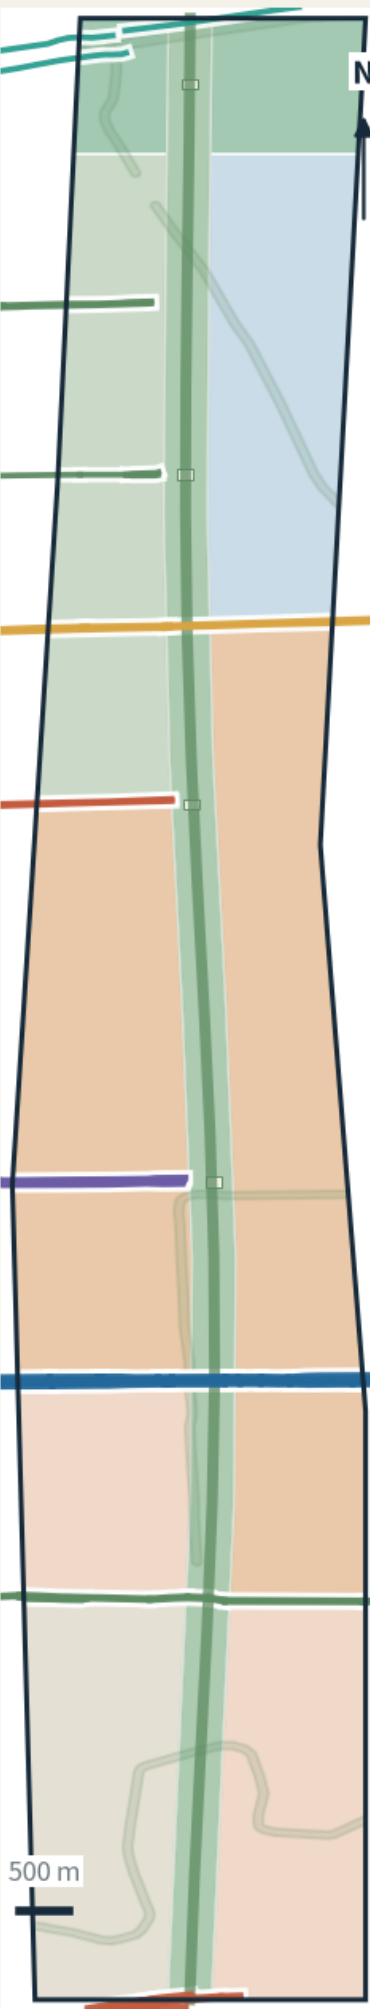

状态截点 2026-08-10 | 概念城市设计；临时边界与 OSM 仅供研究，不替代法定规划、权属或工程测绘。

五类城市材料

- 研发 / 孵化
0802
- 高校 / 科研
0804
- 居住 / 社区
0701/0702
- 商业 / 服务 / 文化
05/0803
- 公园 / 生态
1401/1402
- 横街 / 公共节点
1207/1403

首层动作只分四类

- 01 保留现状
- 02 首层改造
- 03 合作租赁
- 04 条件新增

水岸研发横街：从河岸到研发后场的完整梯度

研究区间：生境12~20m | 净步行≥3m | 需渠6~12m | 公开前场8~15m



近校转换横街：校园门到企业的五分钟短链

研究下段：净步行≥3m | 单向骑行≥2.5m | 工作间连渠6~9m | 入口≥2/100m



四象限站城：先连续地面，再比选桥下、连桥或地下


研究下段：每角到达面≥12×20m | 地面过街≤2信号阶段 | 车位150~300/角停核



FIG 02 / 05

纵向公园已经存在，设计重点是横向穿越与完整断面

八条横街以真实水岸/道路命名；每条都必须连到建筑首层、站口、校园或社区，而不止于公园边。

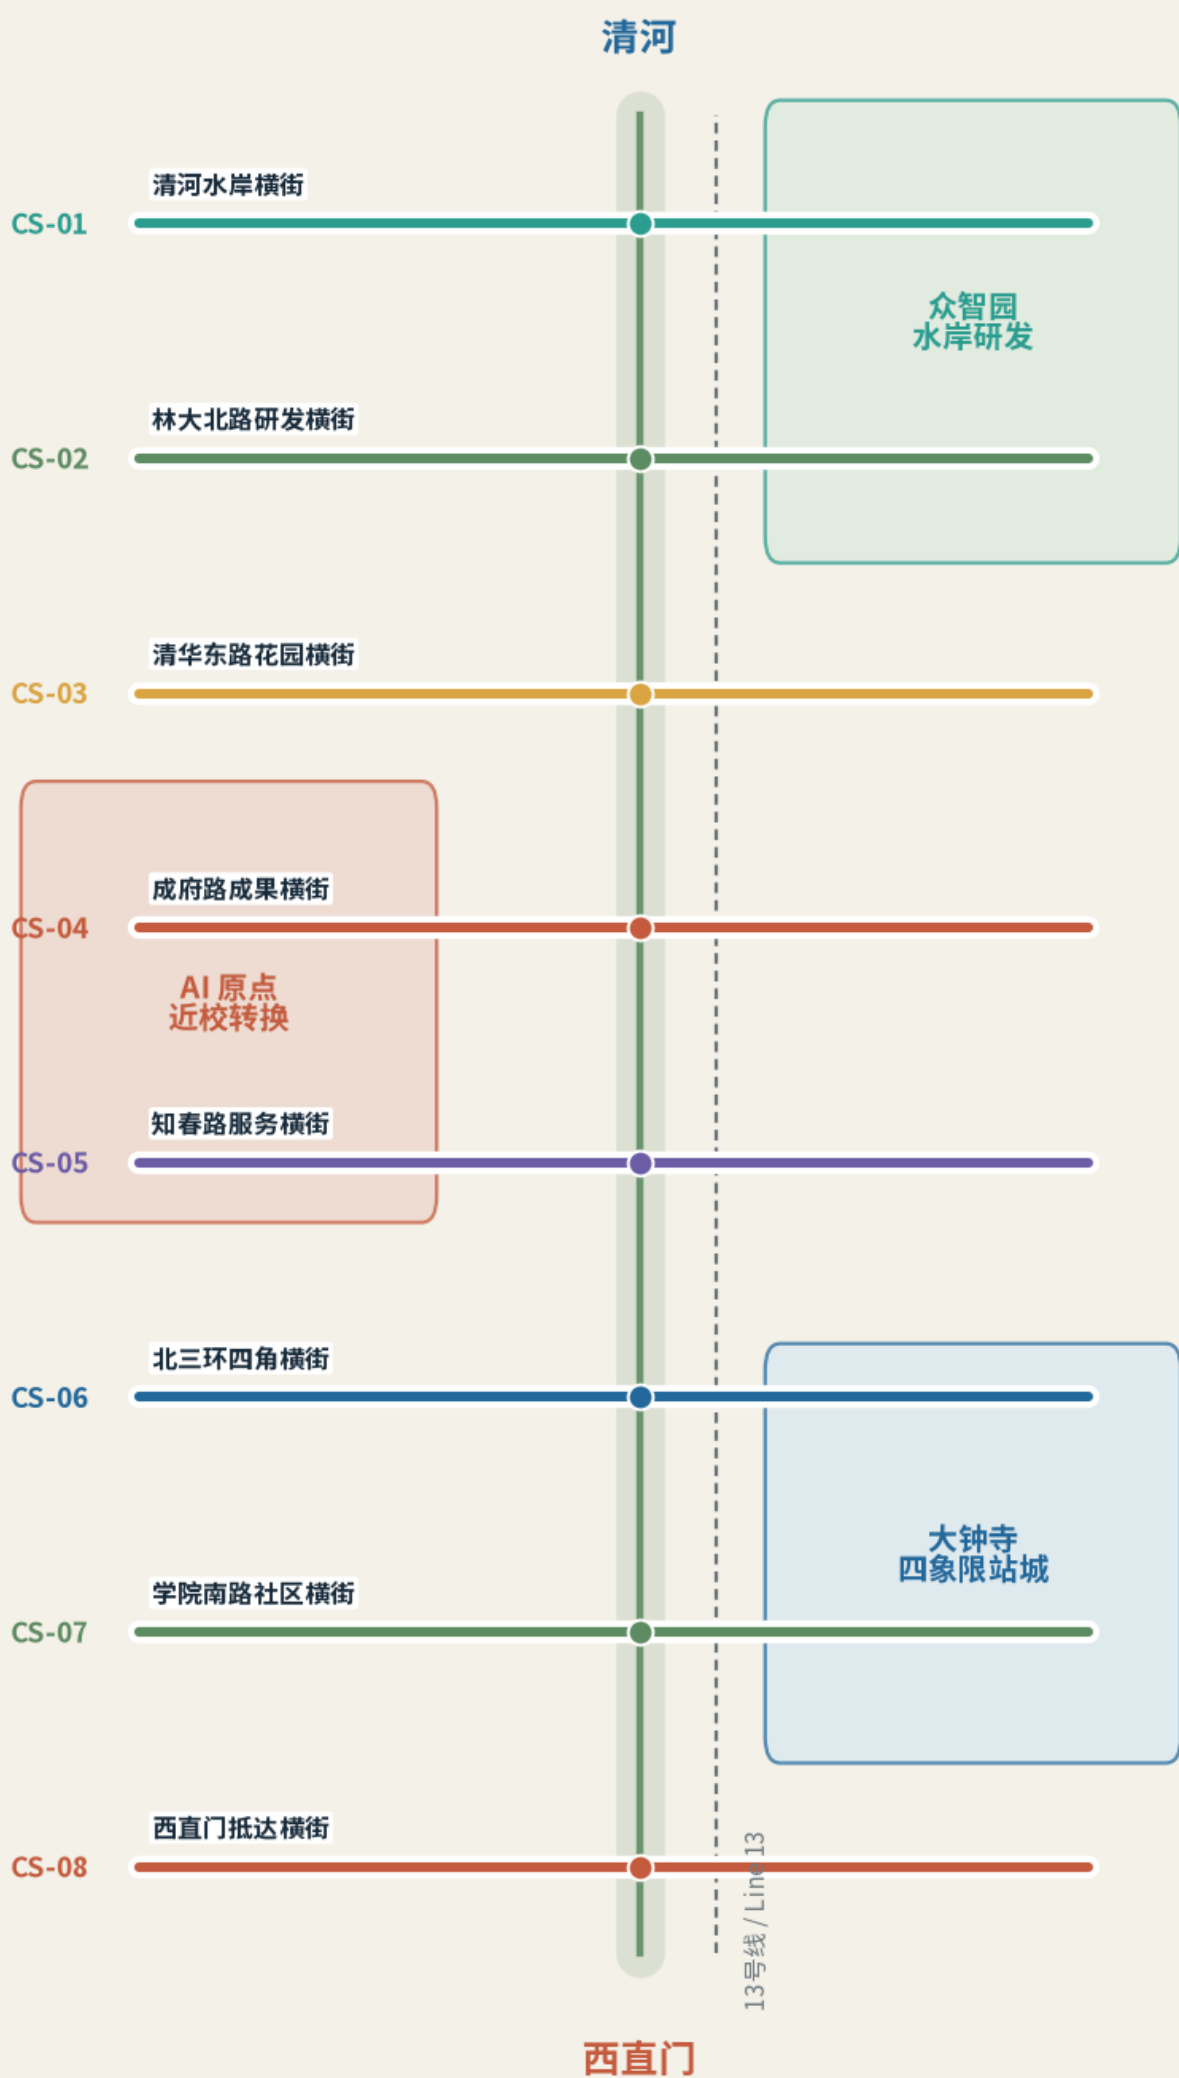

状态截点 2026-08-10 | 概念城市设计；临时边界与 OSM 仅供研究，不替代法定规划、权属或工程测绘。

水岸研发横街：从河岸到研发后场的完整梯度

研究区间：生境12~20m | 净步行≥3m | 需渠6~12m | 公开前场8~15m



近校转换横街：校园门到企业的五分钟短链

研究下段：净步行≥3m | 单向骑行≥2.5m | 工作间连渠6~9m | 入口≥2/100m



四象限站城：先连续地面，再比选桥下、连桥或地下

研究下段：每角到达面≥12×20m | 地面过街≤2信号阶段 | 车位150~300/角停核



FIG 04 / 05

三处重点区：三种街坊，不是三座孤立雕塑

工作视窗采用 OSM 现状建筑；彩色为首层改造，红色为条件新增，横线为主公共路径。

水岸研发街坊



01 众智园 AI 自主创新加速区

清河原型院

安全研发后场 + 可进入评审前场 + 清河生境边缘


日常

共享仪器预约、午间评审、通勤、河岸散步、餐饮

事件

季度原型开放日与国际标准工作坊

近校转换街坊

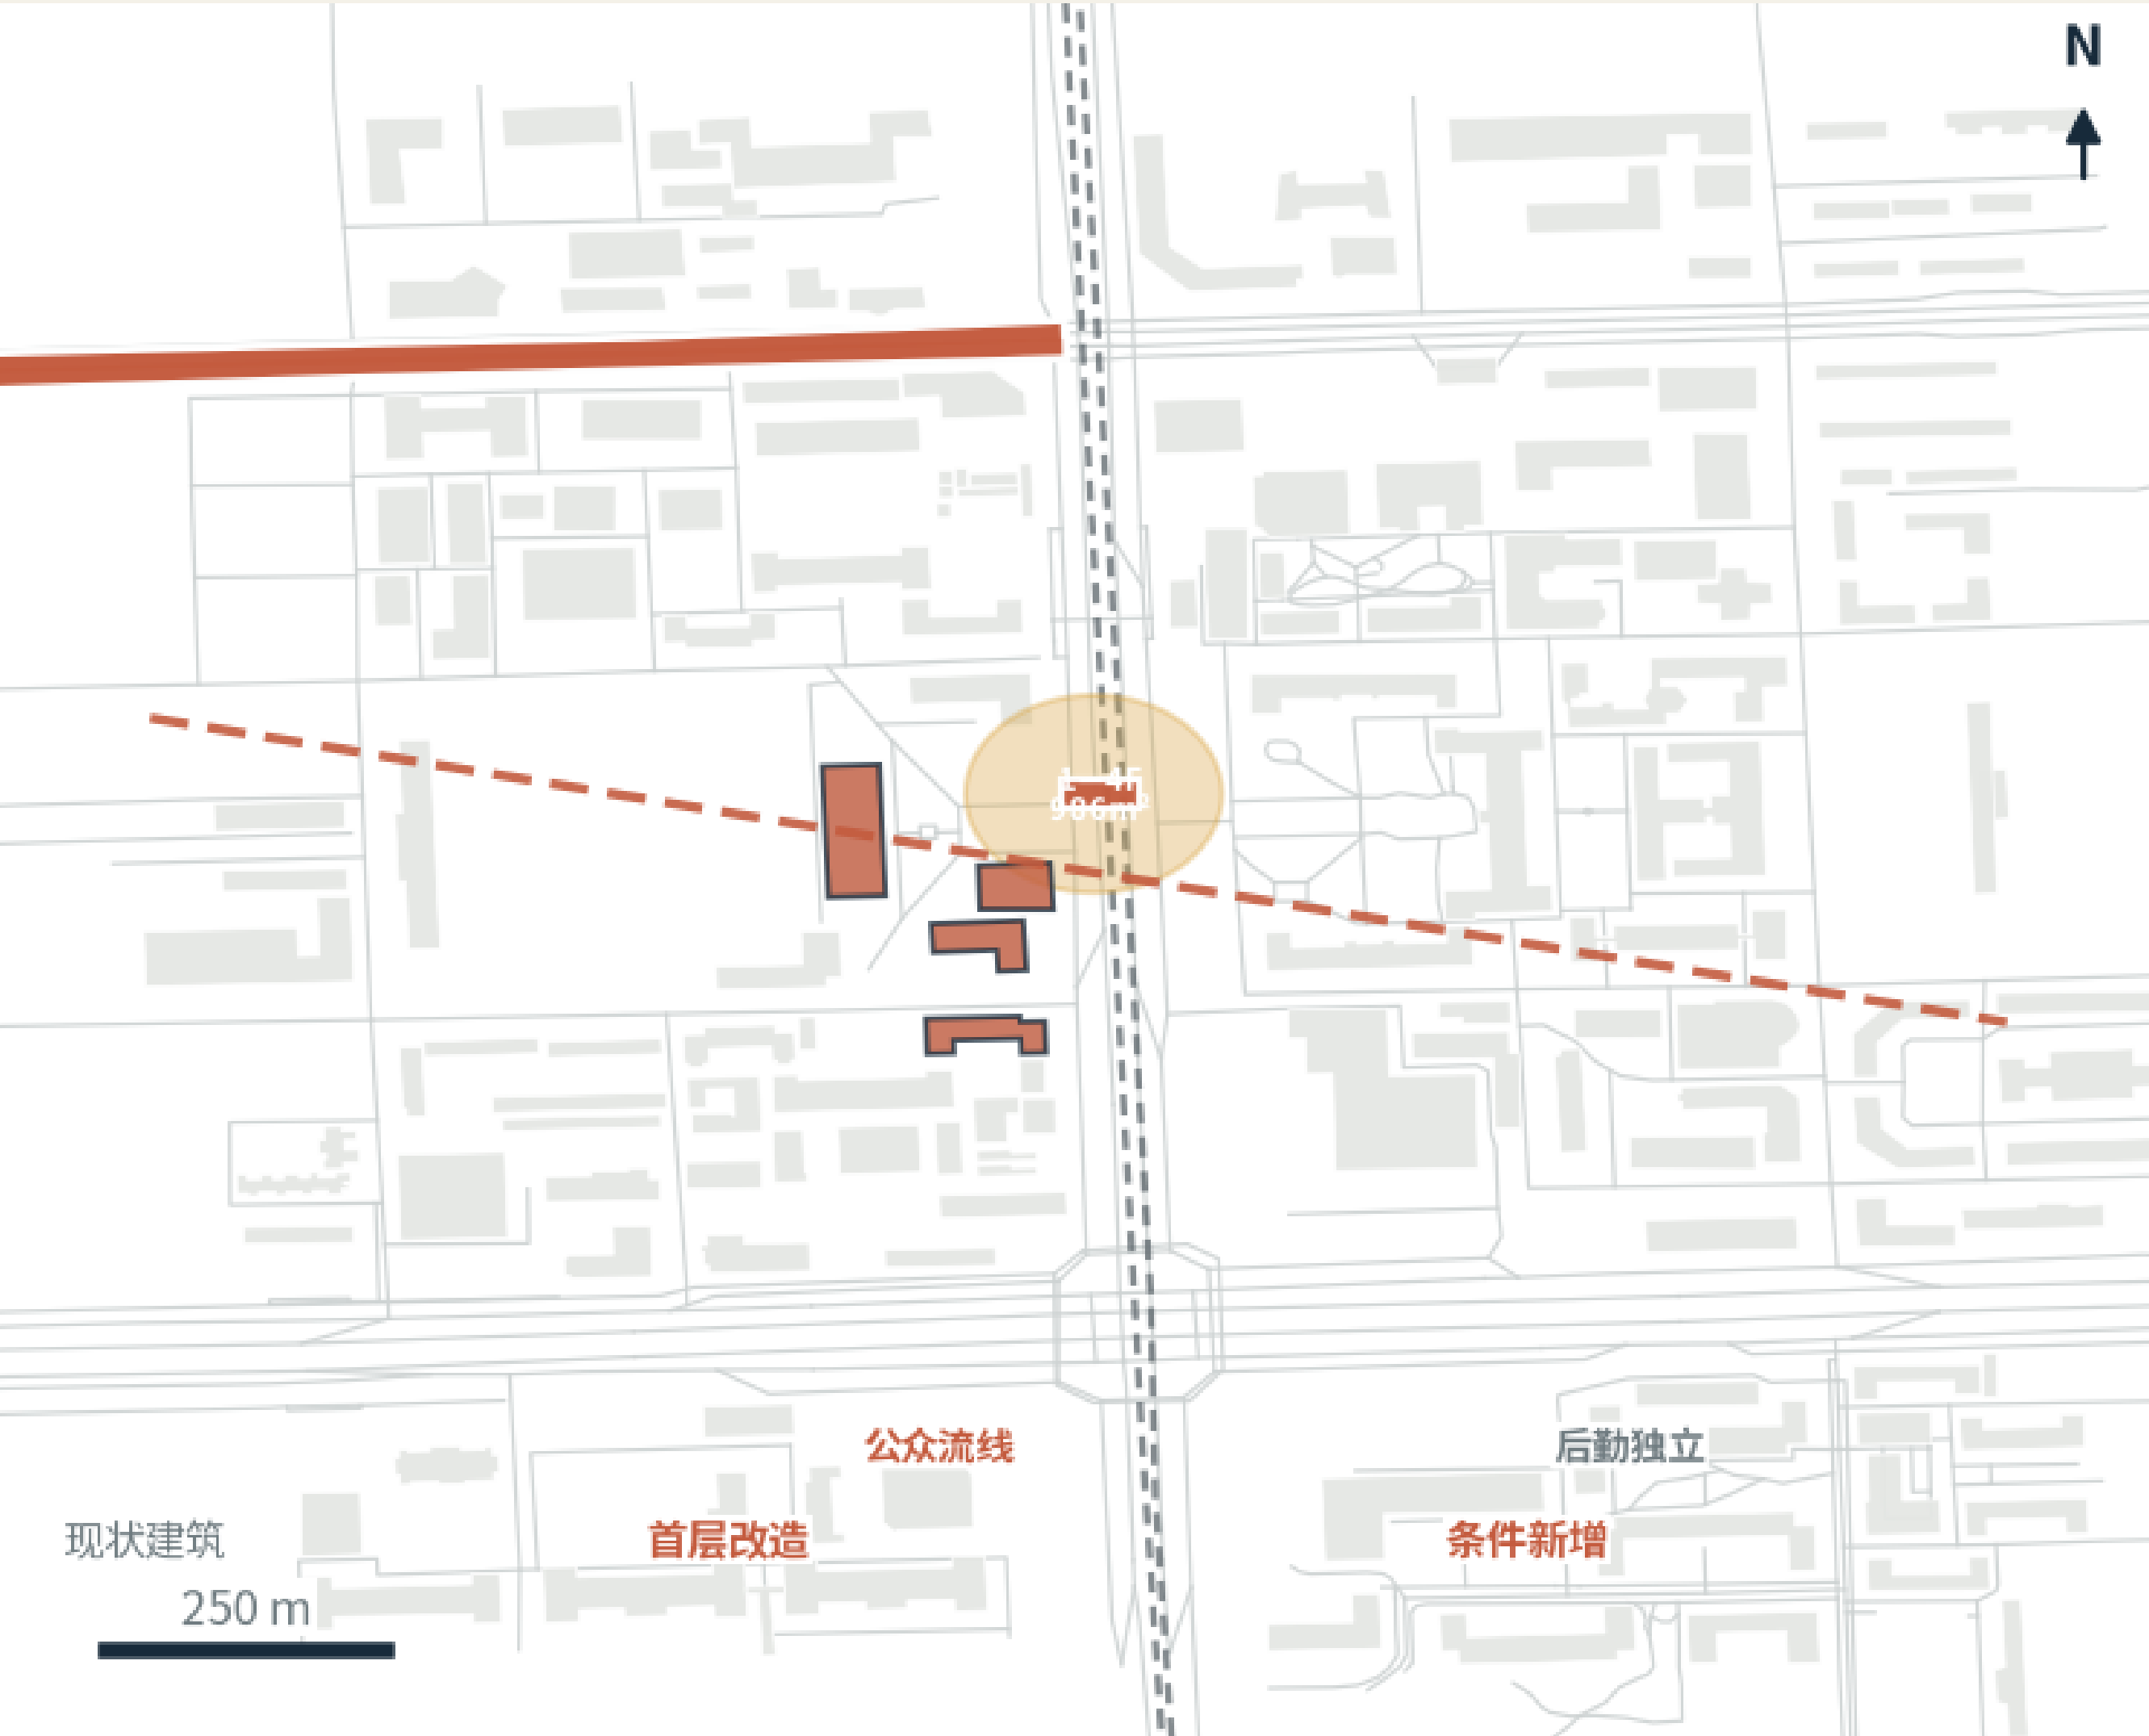

02 北京 AI 原点社区

百桌评审厅

校园门—小工作间—公开评审—孵化—生活服务的短链


日常

开放工位、法务算力门诊、夜间学习、托育与平价餐饮

事件

每周同行评审、每月成果上街、毕业季驻地

四象限站城街坊

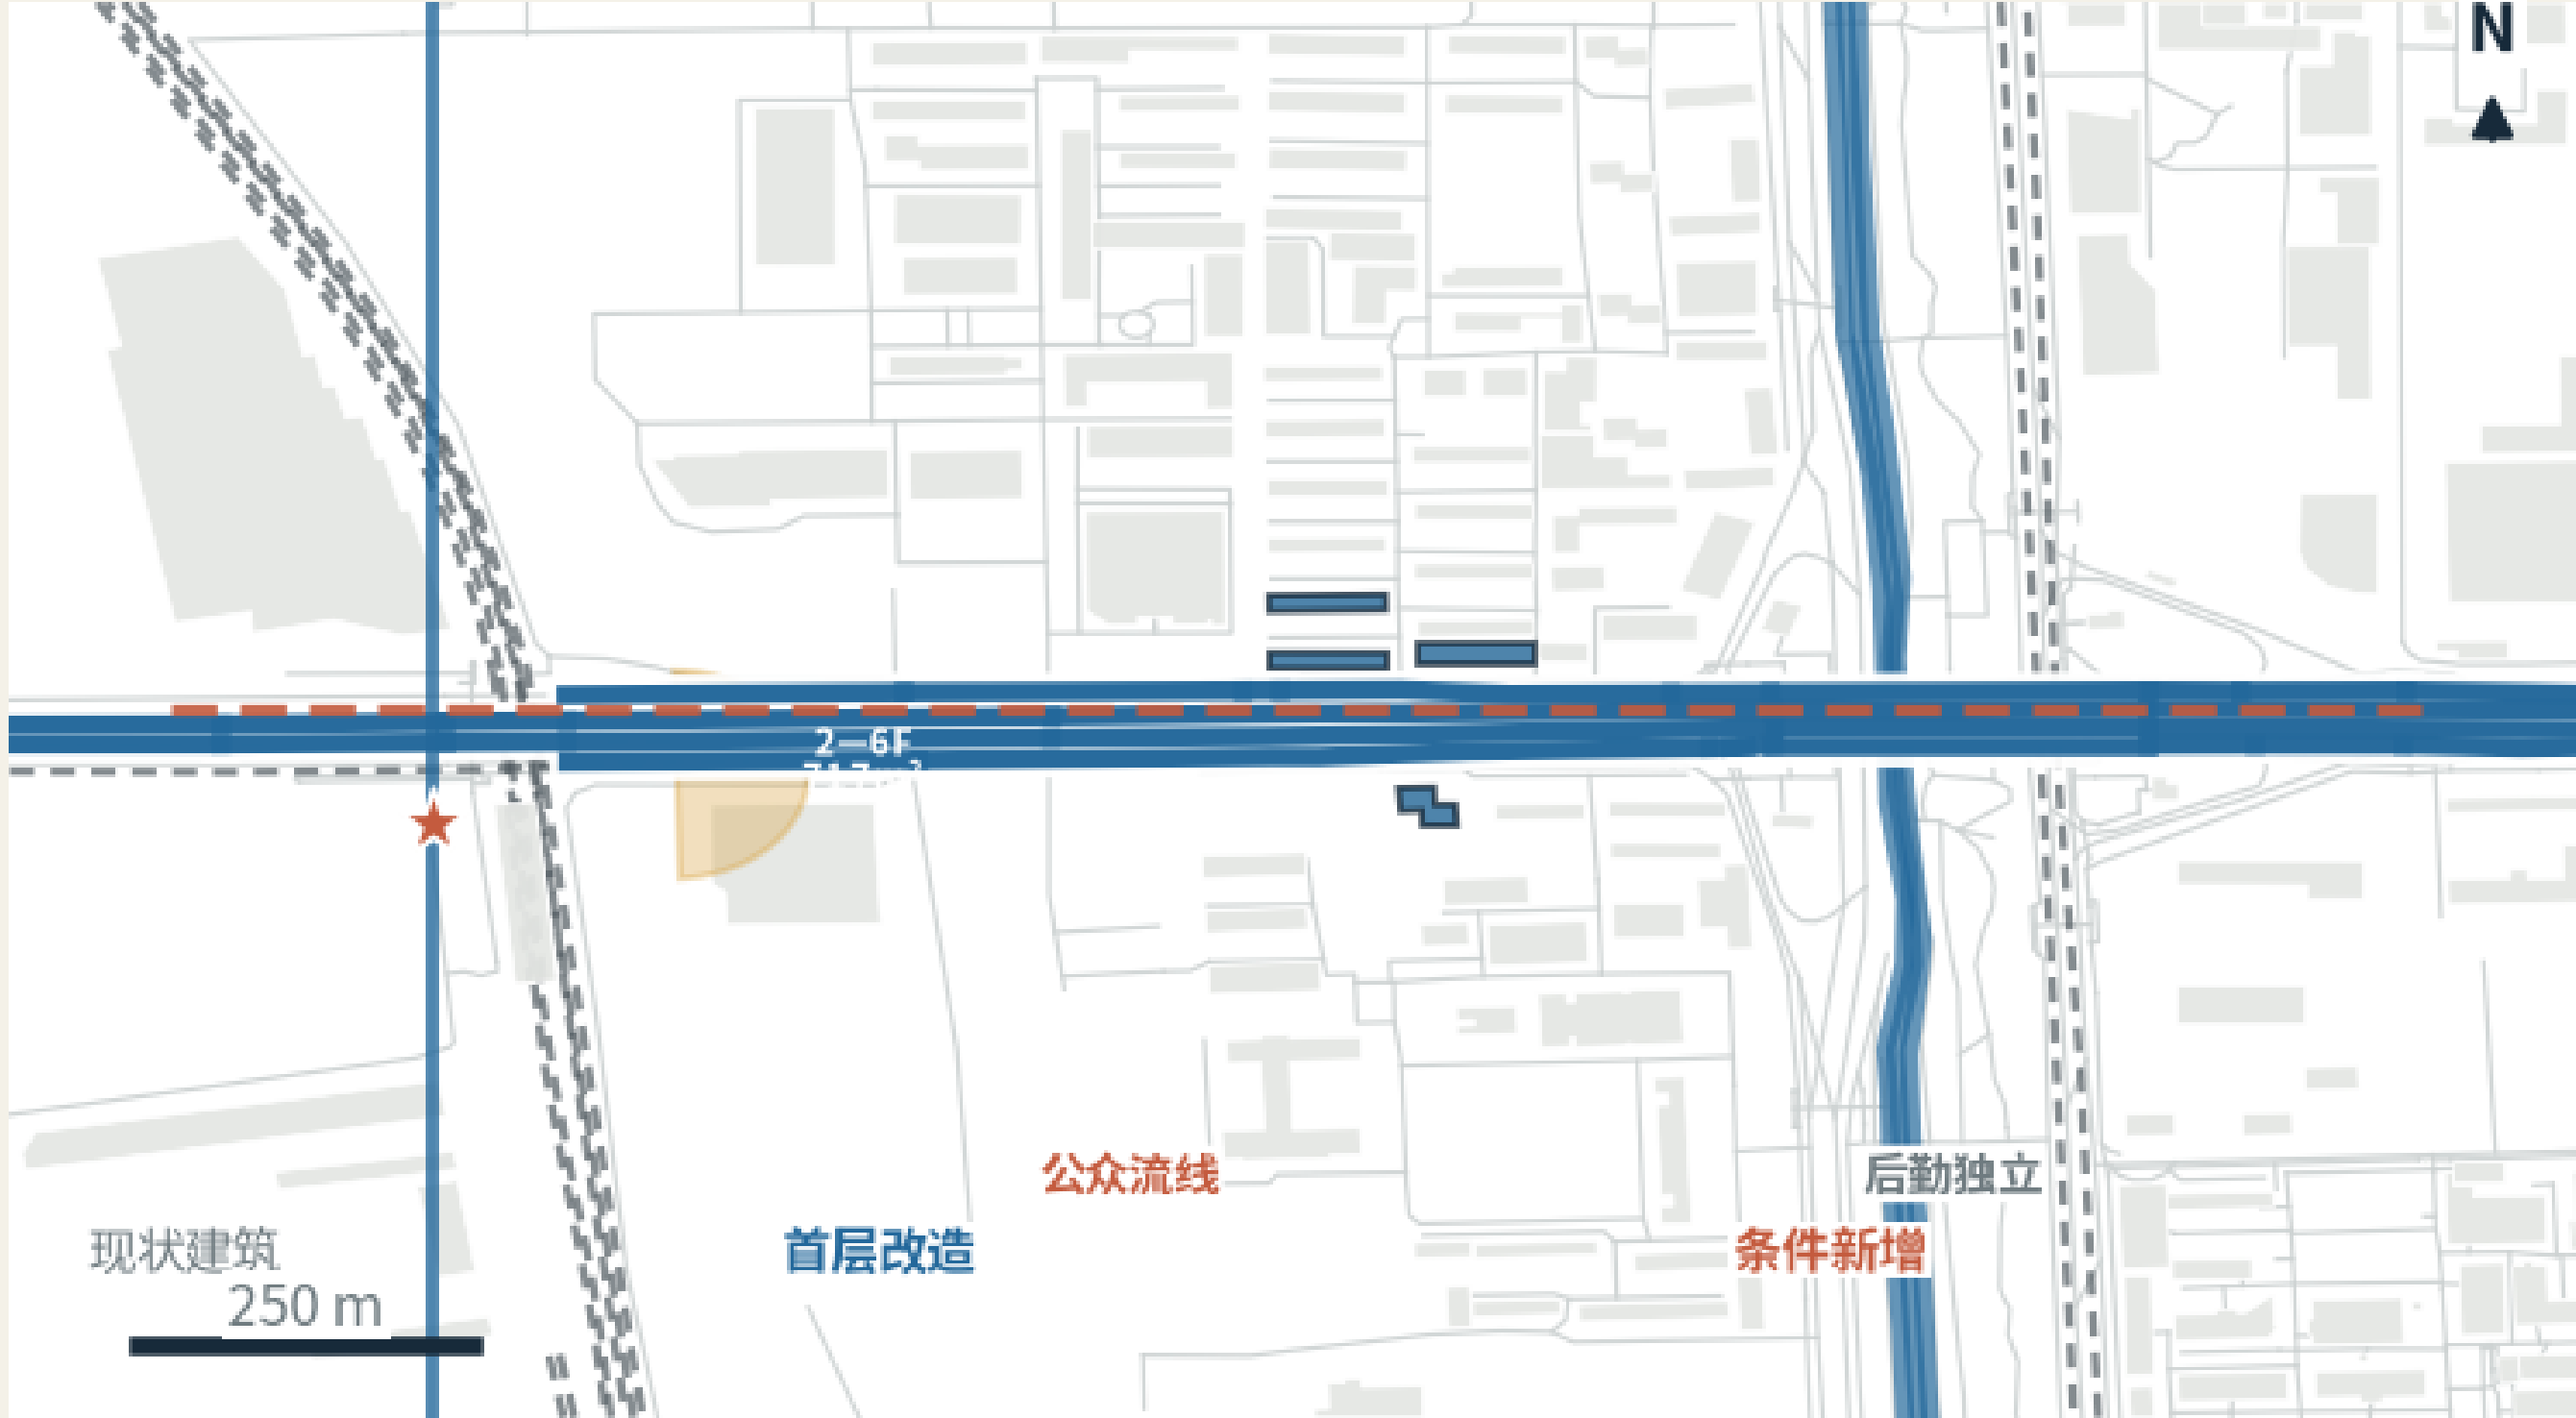

03 大钟寺 AI 产业聚集区

大钟寺四角台

地面连续优先的四象限站口 + 内容制作 + 智能终端 + 通勤生活

日常

换乘、骑行停放、维修退换、青年夜校、社区服务

事件

小型发布、公共放映、终端试用与声音文化夜

把设计、数据边界和实施权限放在同一张表

已知不等于官方控制；目标不等于现状；未知也不等于不做设计。

官方任务	本包推导	设计目标	保持未知
43.6 km² 统筹研究 11.4 km² 总体设计 368.4 ha 三区详设 9 km 京张公共骨架	8 条真实横街 535 个 OSM 建筑 15 个实施项目 12 张场景卡	- 八条横街连续性 8/8 - 无障碍横向通行 100% target - 首层入口密度 >= 2 / 100 m target - 公共首层开放 >= 60 h/week target	- 正式红线 / 地块 / 权属 - FAR / 高度 / 密度 - 结构 / 消防 / 市政容量 - 客流 / 工程投资 / 工期

15 个项目 × 三类实施权限

公共空间 / 0—18月	PJT-01 全 线现状竣工图与权属合图	PJT-02 八 条横街无障碍审计	PJT-03 知 春路—大钟寺跨 13 号线需求核 验	PJT-04 清 华东路项目接口协 调	PJT-05 横 街基础服务包	PJT-08 大 钟寺四角步行与骑 行包	PJT-11 清 河与小月河接口样 板
合作租赁 / 1—3年	PJT-06 清 河原型院一期	PJT-07 百 桌评审厅与 50 +50 工位	PJT-09 北 影内容制作首层	PJT-10 终 端维修与材料循环 柜台	PJT-12 首 层合作租赁条款	PJT-15 横 街运营基金与五年 复盘	
法定工程 / 3—10年	PJT-13 大 钟寺站城工程方案 比选			PJT-14 众 智园水岸街坊条件 更新			

停止条件 未取得正式边界与工程资料，不锁定 FAR、高度、拆除、桥隧或投资；未签租赁/维护责任，不宣称首层开放；无人工替代，不运行 AI 场景。