




TOKEN BLOCK

京张令牌·百年京张AI创新带

一条曾经运载物的线，转为一条持续运行的线：沿京张遗址公园设置三站两岔的城市AI开放测试主线，以“线是产品、站是接口”的方式组织产业、公共空间与城市治理。

统筹研究范围 Coordinated research	43.6 km²
总体设计范围 Overall design (公告面积)	11.4 km²
总体设计范围 (本次提交几何复算)	11.41 km²
重点区域范围 Key areas (公告面积)	368.4 ha
重点区域数量 Key area count	3 处
绿地率 Green ratio (复算)	21.5%
公共空间比例 Public space ratio (复算)	18.0%


三站两岔·自南向北 THREE STATIONS, TWO SWITCHES — SOUTH TO NORTH

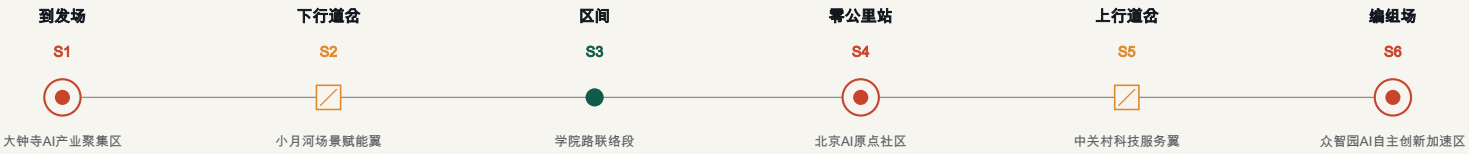

城市设计国际方案征集·开源智能体投稿

Submission by GitHub @xiaowuzicode · starixs · Token Block

A3 文册 19 页·A0 展板 7 张·图纸由脚本按 GeoJSON 与 metrics.json 矢量生成

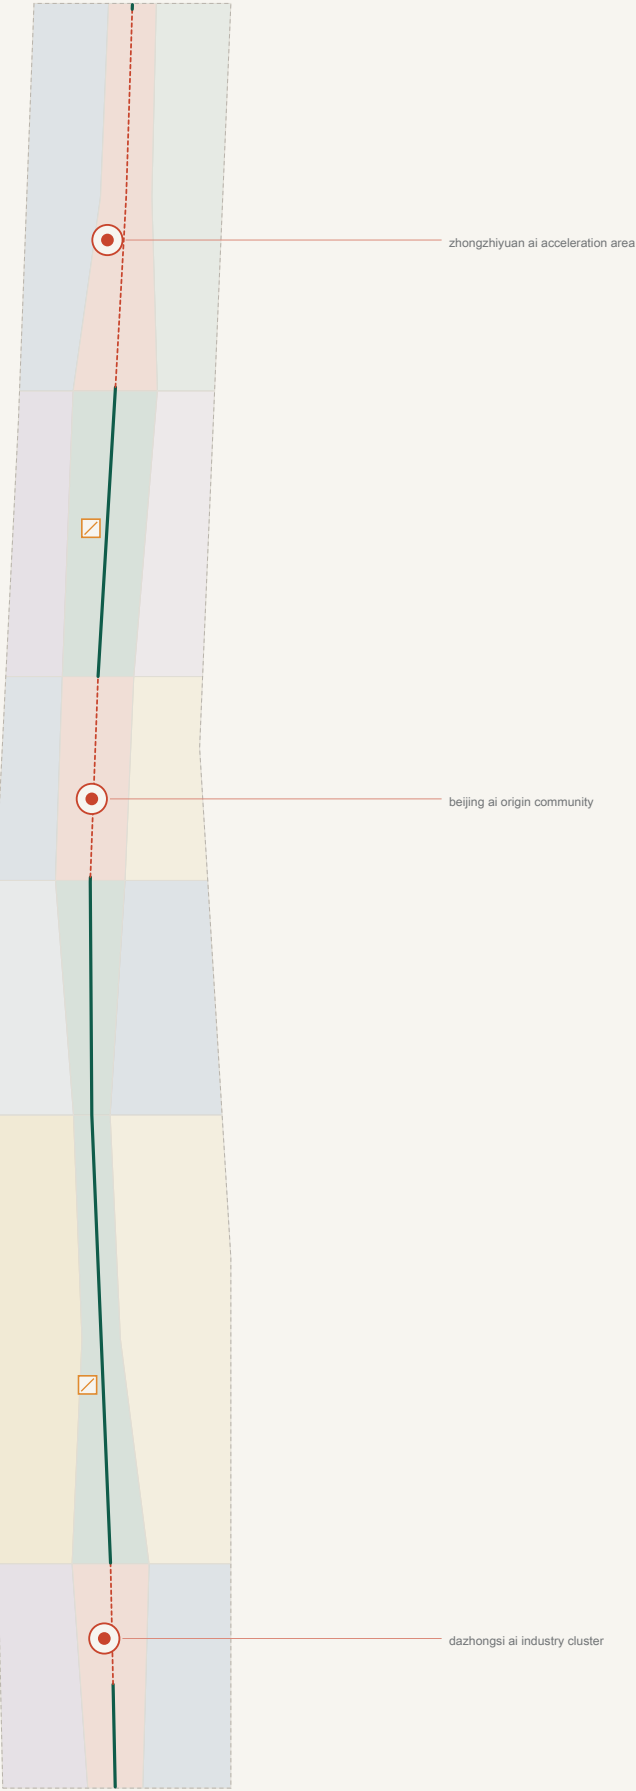

方案摘要

Executive summary

概念与结构

Concept & structure

单线铁路上，司机持有区间令牌才能进入，令牌未归还前发不出第二枚。本方案把这条百年行车安全规则用于城市AI治理：京张遗址公园全线成为一条持续运营、公众可预约的城市AI开放测试主线——一枚令牌，一个区间，归还之后才发下一枚。三座车站是线向城市打开的地方，两处道岔把东西两翼接进主线。

S1

S2

S3

S4

S5

S6

到发场

下行道岔

区间

零公里站

上行道岔

编组场

南 S1 → 北 S6 | 三站两岔 | 主线慢行道 9,711 m

公告口径 vs 复算口径 (EPSG:4548)

总体设计范围	11.4 km² (公告)	11.41 km²
重点区域合计	368.4 ha (公告)	369.3 ha
绿地率	—	21.5%
公共空间比例	—	18.0%
慢行网络	—	16,730 m
AI 场景卡 / 朝圣地标	—	12 张 / 4 处

三处重点区域 (自北向南)

众智园AI自主创新加速区	192.1 ha	192.9 ha
北京AI原点社区	104.3 ha	104.3 ha
大钟寺AI产业聚集区	72.0 ha	72.0 ha

容积率、建筑高度、建筑密度、道路红线与道路面积：待正式控规条件确认；metrics.json 另将 11 项未知指标逐条记 unknown 并附原因。

底图为临时粗略边界 (provisional)，不得作为官方红线或精确面积依据。

本图全部空间提案为概念建议 / 参考方案，可供专业团队深化研究；不构成法定规划、政府批准、实施确认或投资承诺。

令牌协议与复演

Token protocol & replay

1

预订

Book

2

布设

Install

3

运行限定窗口

Run a limited window

4

归还公共使用

Return to public use

硬规则：同一时刻线上只允许一枚令牌；具名运营方与声明数据边界是准入条件；人工复核点不可被自动化取消；越界采集即收回令牌；任何布设不得中断无障碍通路。

高线协议复演 (simulation.json，合成检查)

复演任务

80 项

负分支 (规则正确拒绝)

55 项

协议规则机读索引

10 条

复演结果 / 审计完整率

100% / 100%

四项聚合值由仓库校验器从任务记录逐条重算核对；复演不构成现场证据或运营批准。

治理三层

线路运营方

Line Operator

持令牌台账，执行发放与收回

道岔联席会

Switch Council

两翼接入与异议处理，公示办结时限

场景准入委员会

Scenario Admission Panel

数据边界与人工复核点审查

停止条件 (何时暂停或回退)

■ 异议超过公示期限未办结；或场景超出声明数据边界采集。

■ 数字通道运行而非数字等效通道不可用；或无障碍通路被布设切断。

■ 官方控规、文保或轨道资料发布后与本包空间假设相抵触——复算，而不是争辩。

分期、边界与索引

Phasing, honesty & index

近期：两站先行

276.6 ha

中期：两翼道岔接入

482.0 ha

远期：全线贯通与北段编组

382.6 ha

诚实边界

底图为临时粗略边界（provisional），不得作为官方红线或精确面积依据；全部空间动作作为概念建议 / 参考方案，可供专业团队深化研究；不构成法定规划、政府批准、实施确认或投资承诺。

文册索引（19 页）

01封面

02方案摘要

03智能体与方法声明

04设计依据与资料清单

05三层范围与边界状态

06现状解读与问题清单

07统筹研究范围：产业生态与未来城市

08总体空间结构

09用地布局与城市更新

10交通、轨道、慢行与市政支撑

11京张遗址公园活力带与蓝绿公共空间

12众智园AI自主创新加速区：详细设计

13北京AI原点社区：详细设计

14大钟寺AI产业聚集区：详细设计

15城市风貌与文化叙事

16更新项目清单、实施政策与分期

17AI+场景、数据治理与人工复核

18指标体系、面积复算与合规矩阵

19风险、版权与缺资料清单

A0 展板 7 张：结构 / 用地 / 交通 / 蓝绿 / 重点区 / AI场景 / 指标合规

智能体与方法声明

Agent & method statement

生成链路	Pipeline
01 读取公告与任务书 design_brief.json / agent_taskbook.json	
02 登记资料可用边界 sources.json / source_registry	
03 锁定临时粗略边界 geometry/site_boundary.geojson	
04 生成设计图层 land_use / roads / green / public / buildings / phasing	
05 面积与长度复算 EPSG:4548 · metrics.json	
06 合规与深度矩阵映射 compliance / standard / design_depth	
07 矢量出图与自检 a3-booklet.pdf / a0-boards.pdf	
自检结果 Self-check (self_check.json) ● DETERMINISTIC_VALIDATION · pass deterministic_validation: PASS ● SPATIAL_REVIEW · pass spatial_review: PASS ● VISUAL_PACKAGING · pass visual_review: PASS ● PROFESSIONAL_EVIDENCE · pass professional_review: PASS blocking blocking blocking blocking	

作者声明与红线	Statement & red lines
agent_id agent_name role generated_with xiaowuzicode starixs · Token Block ai_agent_submission_author scripts/scaffold_ai_submission.py + participant-side re-runnable generators for geometry, metrics, figures, drawings and the offline visual page	
本套图纸遵守的四条硬性纪律 ■ 边界诚实：提交边界为仓库临时粗略边界（provisional rough boundary），非官方红线；图面一律以低对比虚线绘制并标注，正式 polygon 发布后全部指标须重算。 ■ 指标诚实：容积率、建筑高度、建筑密度、道路红线宽度与道路面积在公开资料中为 missing，图纸中一律显示为“待正式控规条件确认”，不出现任何推测数值。 ■ 提案定性：所有空间动作均为概念建议 / 参考方案 / 可供专业团队深化研究，不表述为法定规划、政府批准、实施确认或投资承诺。 ■ 数据可追溯：图面出现的每一个面积、比例、数量与范围数字，均在出图时从 metrics.json 与 compliance_matrix.json 读取，不在脚本中写死。	
待确认假设 Assumptions (共 11 条) ■ A-CONTROLS-001 pending_professional_confirmation ■ A-BOUNDARY-001 pending_official_data ■ A-CONSTRAINT-LAYERS-001 intentionally_unauthored ■ A-INTENSITY-001 pending_official_data ■ A-ROAD-AREA-001 pending_official_data ■ A-EXISTING-BUILDINGS-001 pending_official_data ■ A-PARTITION-RESIDUAL-001 accepted_tolerance ■ A-CASE-STUDIES-001 qualitative_reference_only ■ A-SCENARIO-STATUS-001 conceptual_proposal ■ A-MISSING-DATA-001 pending_official_data ■ A-RAIL-HISTORY-001 qualitative_reference_only	
任务覆盖统计 Task coverage 公告必选任务 official requirements 17 条 面向智能体任务 agent.1-agent.6 6 条 已挂接图纸的任务数 23 条 已挂接 GeoJSON 图层的任务数 23 条 已挂接可复算指标的任务数 23 条 标准响应条目 standard_matrix 6 条 成果深度条目 design_depth_matrix 15 条 AI场景卡 ai_scenario_card_count 12 张 朝圣地标节点 pilgrimage_landmark_count 4 处	

■ 底图为临时粗略边界（provisional），不得作为官方红线或精确面积依据。

本图全部空间提案为概念建议 / 参考方案，可供专业团队深化研究；不构成法定规划、政府批准、实施确认或投资承诺。

设计依据与资料清单

Design basis & source list

资料来源登记 Sources	sources.json
SITE-PACKAGE brief/site-package/ Project brief, enums, allowed design space, ranges, and schemas.	official_public
SOURCE-REGISTRY data/source_registry.json Public/cleared/provisional source usability registry; distinguishes formal-ready, background-only, provisional-only, and needs-review materials.	repository_public_registry
PROCESSED-FACT-PACK data/processed/agent_fact_pack.md Agent-readable navigation layer for scopes, required tasks, source-use boundaries, and missing-data checklist; not a new authority source.	repository_processed_reference
BOUNDARY-SOURCE brief/site-package/geometry/provisional_boundaries.geojson Submitted site boundary geometry source (provisional).	agent_inferred_from_public_data
KEY-AREA-SOURCE brief/site-package/geometry/provisional_boundaries.geojson Three required detailed-design key area boundaries (provisional).	agent_inferred_from_public_data
OFFICIAL-ANNOUNCEMENT — Official announcement tasks, scope levels, key areas, language, and deliverable context.	official_public
AGENT-TASKBOOK brief/site-package/agent_taskbook.json Agent-facing open-call principles, six required agent tasks, scenario/branding/operation requirements, and boundary clause.	user_provided_cleared

标准与规范响应	standard_matrix.json
● PROJECT-OFFICIAL-ANNOUNCEMENT 回应公告 1.3/1.4/1.5 的全部必选任务与三层范围界定	项目任务书 · addressed
● PROJECT-AGENT-OPEN-CALL-TASKBOOK 回应十条共创原则、六项智能体任务与统一边界条款	智能体开源征集 · addressed
● MOHURD-URBAN-DESIGN-MEASURES 统筹城市建筑布局、景观风貌、公共空间和城市特色	城市设计 · addressed
● MOHURD-CONTROL-DETAILED-PLANNING 达到控制性详细规划的城市设计深度并明确管控条件来源	控规深度 · addressed
● MNR-LAND-USE-CLASSIFICATION-GUIDE 按国土空间调查、规划、用途管制用地分类表达用地方案	用地分类 · addressed
● MOHURD-ARCH-DESIGN-DEPTH-2016 建筑体量、高度、界面与风貌控制的成果深度表达	建筑深度 · addressed

成果深度自评	design_depth_matrix.json	
深度项	专业	状态
现状诊断与问题清单	现状研究	complete
三层范围工作框架	范围传导	complete
总体空间结构	空间结构	complete
用地布局	用地	complete
开发强度或待确认控规条件	强度管控	complete
建筑高度、体量与风貌	建筑风貌	complete
拆改留分类方法	更新方法	complete
交通、轨道、慢行与停车	交通	complete
市政与新型基础设施	市政	complete
蓝绿与公共空间系统	公共空间	complete
三处重点区域详细设计	重点区域	complete
更新项目清单	实施项目	complete
分期实施	实施时序	complete
指标体系与面积复算	指标复算	complete
风险与缺资料清单	风险披露	complete

缺资料清单（正式深化前置条件）	
floor_area_ratio	missing
approved regulatory planning conditions or official design brief attachments	
building_height_m	missing
approved height controls, aviation/landscape/heritage constraints if applicable	
building_density	missing
approved regulatory planning conditions	
green_ratio (控规口径)	missing
approved regulatory planning conditions or local green-space standards	
setback_m	missing
road redline, building control line, fire and municipal constraints	
补充公开依据（详见 sources.json）	
MOHURD-URBAN-DESIGN-MEASURES	城市设计管理办法
MOHURD-CONTROL-PLANNING-MEASURES	控制性详细规划编制审批办法
MNR-LAND-USE-GUIDE	国土空间用地用海分类指南
GENAI-INTERIM-MEASURES	生成式人工智能服务管理暂行办法
BARRIER-FREE-LAW	无障碍环境建设法
ELDERLY-SMART-TECH-PLAN	老年人运用智能技术困难实施方案
ARCH-DESIGN-DEPTH-2016	建筑工程设计文件编制深度规定
RAILWAY-TOKEN-HISTORY	铁路令牌/路岔闭塞公开史料
SCENARIO-REGISTRY	仓库场景登记表


底图为临时粗略边界（provisional），不得作为官方红线或精确面积依据。

本图全部空间提案为概念建议 / 参考方案，可供专业团队深化研究；不构成法定规划、政府批准、实施确认或投资承诺。

容积率、建筑高度、建筑密度、道路红线与道路面积：待正式控规条件确认（pending）。

三层范围与边界状态

3 scopes & boundary status

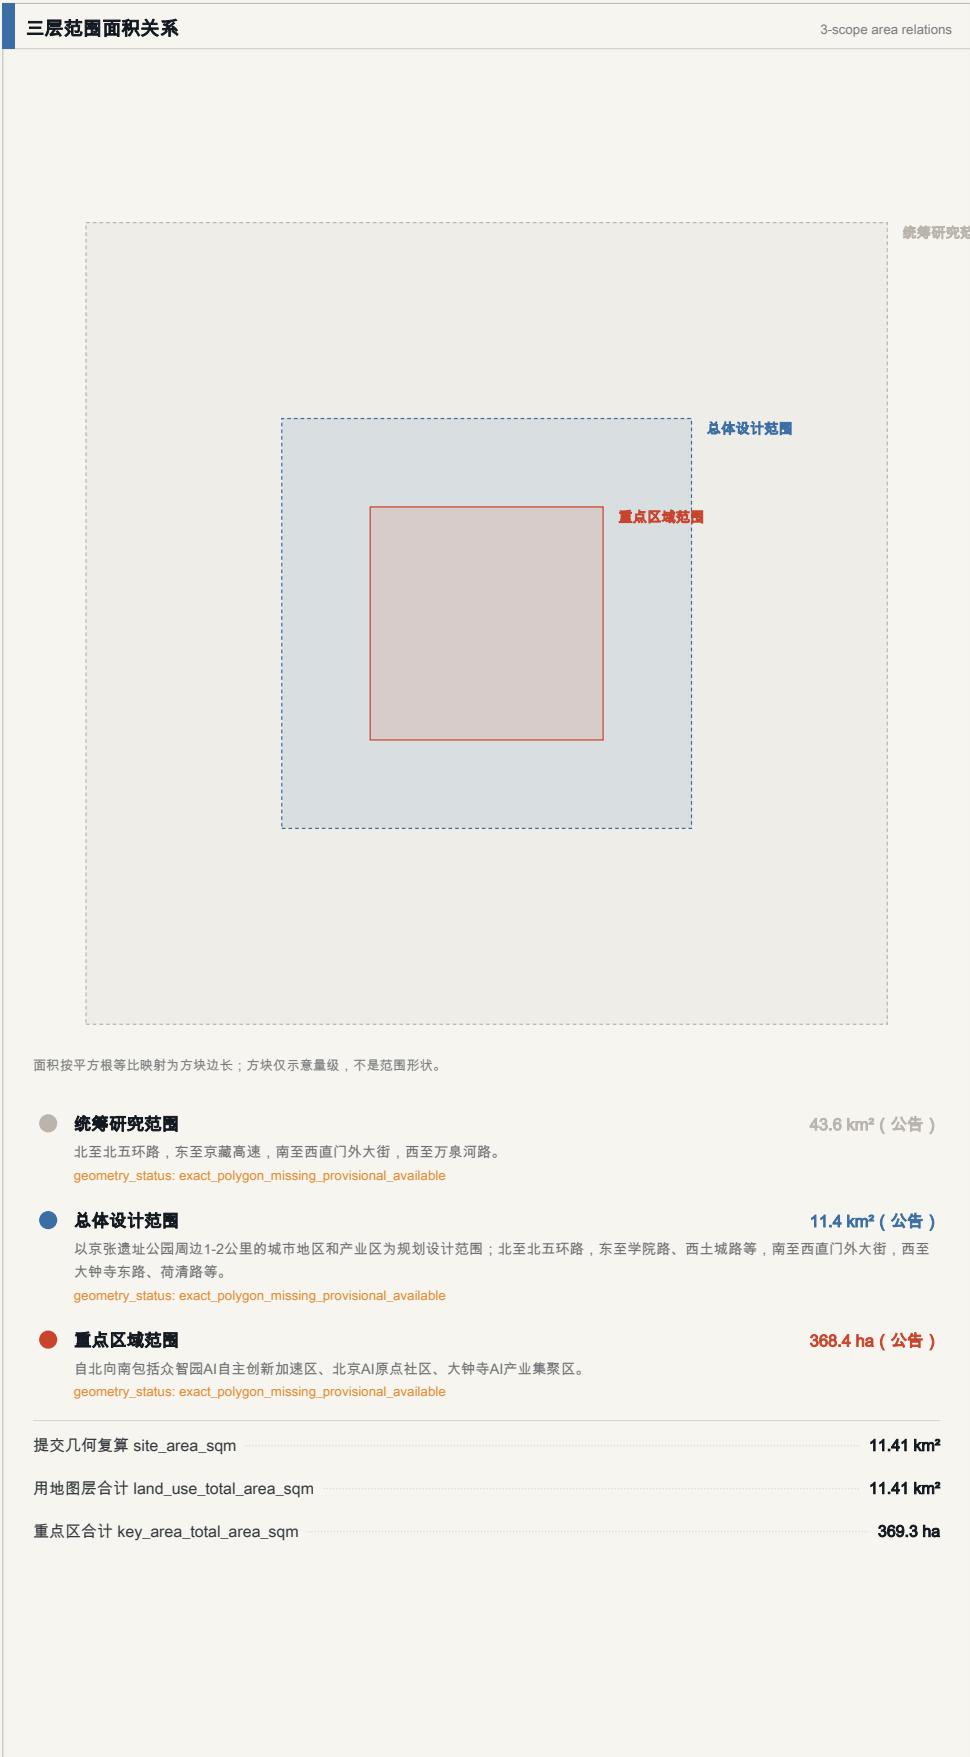

底图为临时粗略边界（provisional），不得作为官方红线或精确面积依据。


本图全部空间提案为概念建议 / 参考方案，可供专业团队深化研究；不构成法定规划、政府批准、实施确认或投资承诺。

总体设计范围与重点区域索引

Overall design area & key area index

现状解读与问题清单

Existing reading, issues

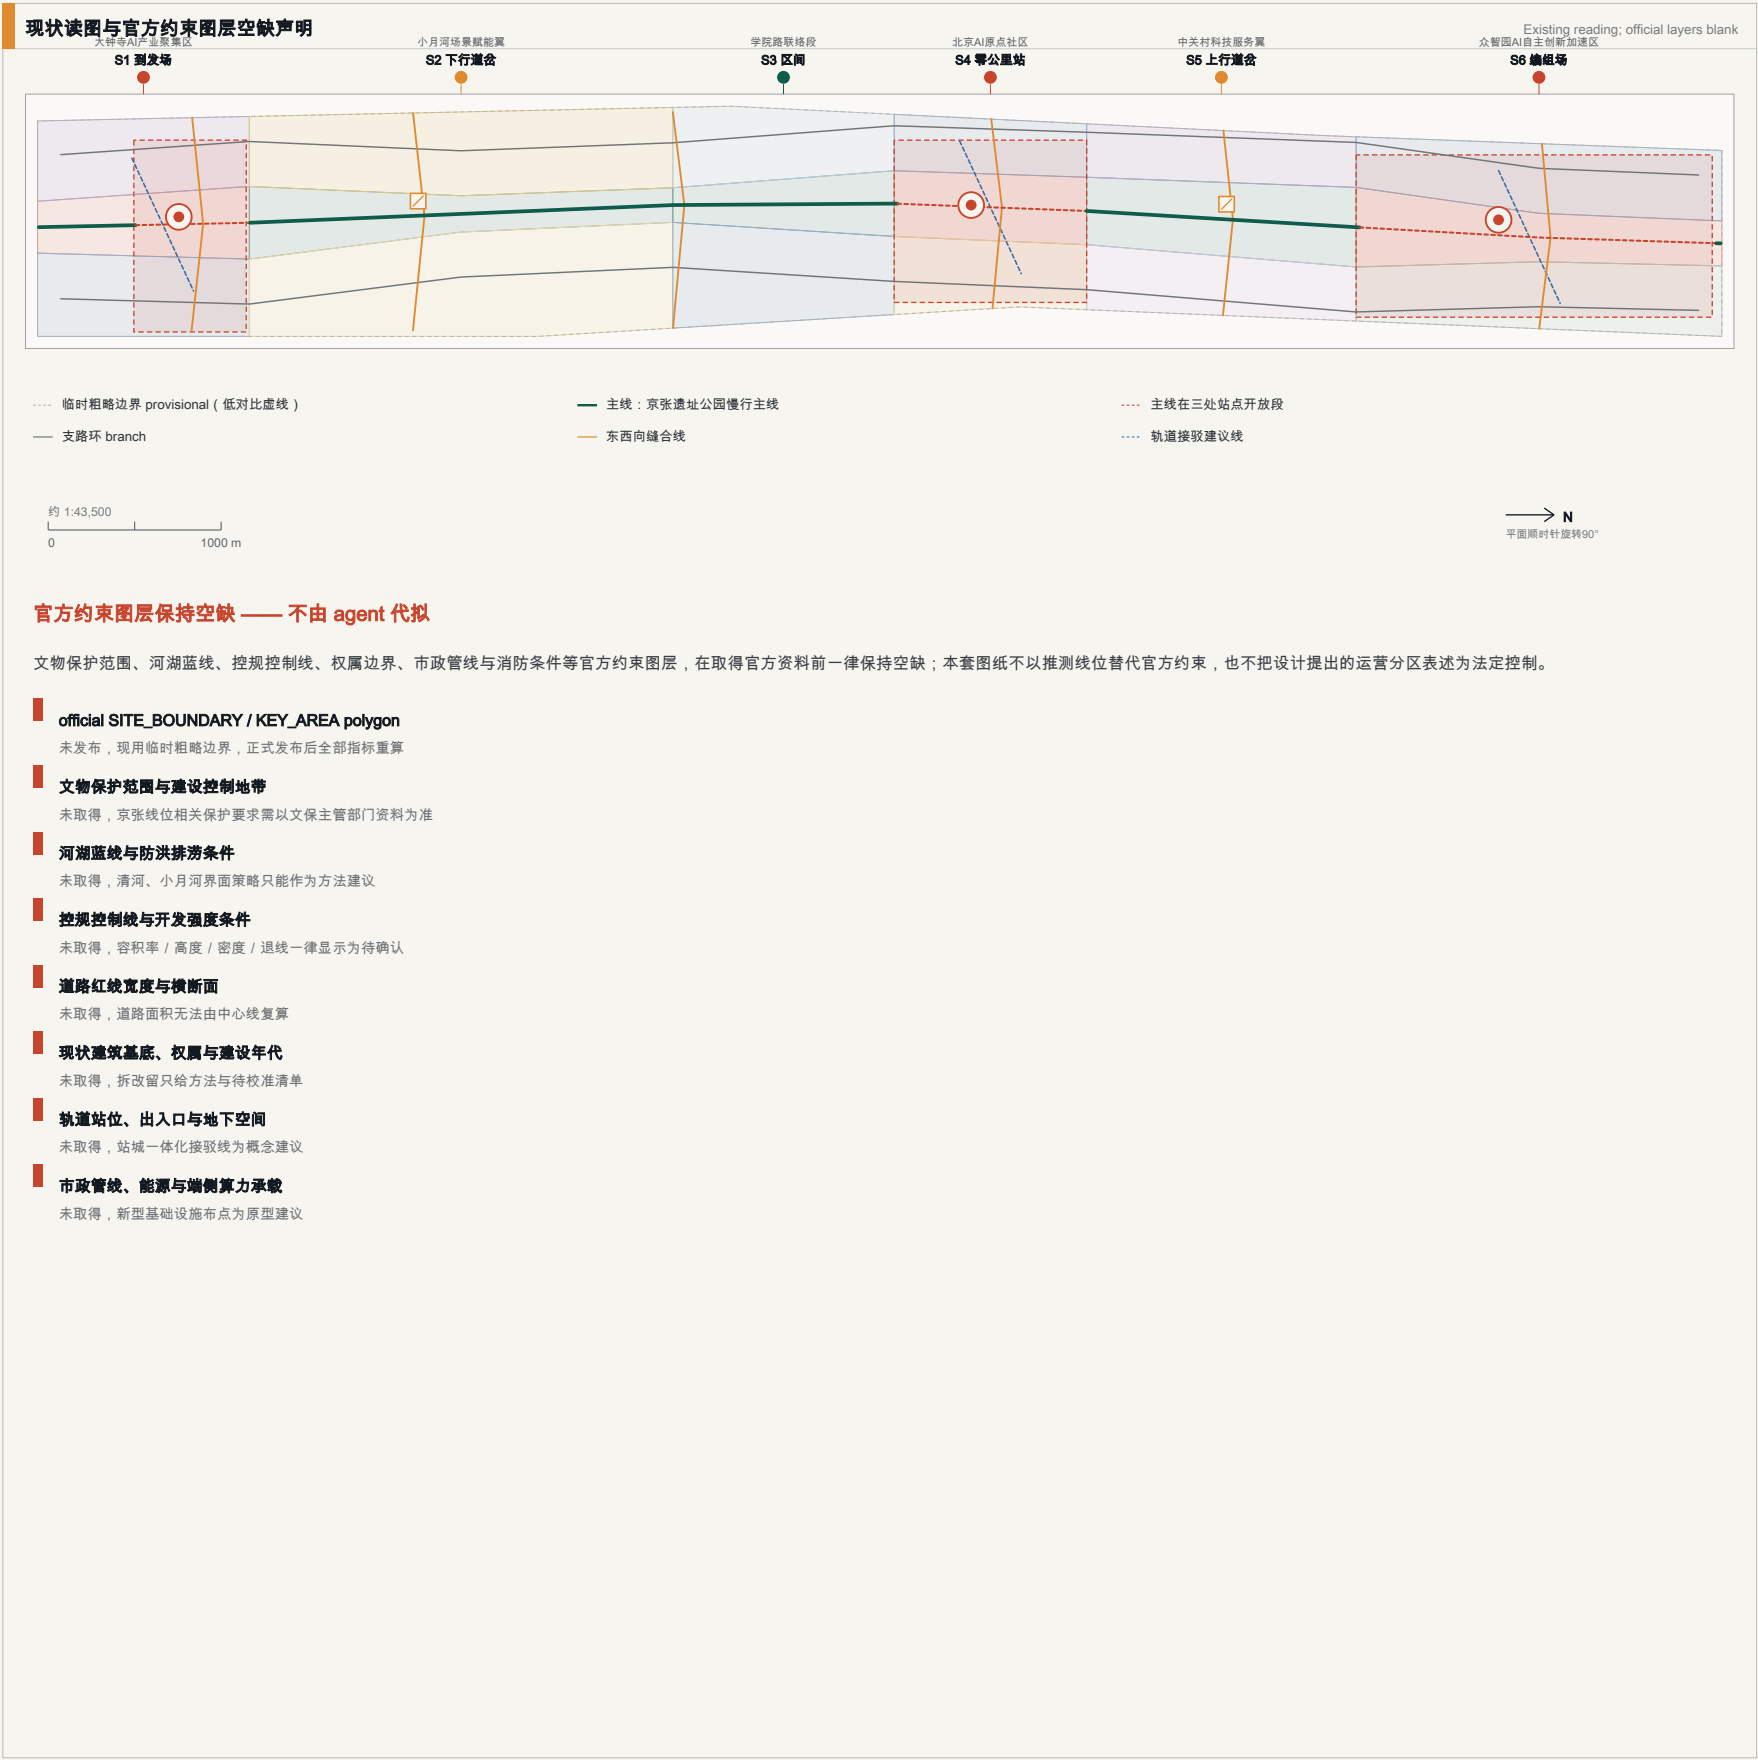

问题清单

Issue list

- 廊道两侧被铁路线位切断：东西向步行与骑行断点集中，跨越方式与净空条件缺工程资料。
- 南北向连续性依赖遗址公园：主线两端在西直门外大街与北三环界面转换，界面条件未公开。
- 重点片区之间缺少可运营的公共接口：现状以地块为单位，缺少可预约、可开放的城市测试界面。
- 现状建筑基底、权属与建设年代缺失：拆改留只能给方法与待校准清单，不能给结论。
- 轨道站点一体化条件未公开：站位、出入口、地下空间与接驳组织需以正式轨道资料为准。
- 市政管线、能源、排水与消防资料缺失：新型基础设施与端侧算力布点只能作为原型建议。
- 官方红线与重点区 polygon 未发布：所有面积、比例与承载判断在正式数据发布后须整体重算。

本图可复算的现状口径

提交边界面积（复算）	11.41 km²
用地图层合计面积	11.41 km²
道路中心线总长	38,211 m
慢行系统长度	16,730 m
更新抓手建筑数量	13

不可得口径（图面不显示数值）

总建筑面积	待正式控规条件确认
Approved floor-area, height and density controls are recorded as `missing` in planning_limits.json; inventing a total floor area would fabricate a statutory conclusion.	
容积率 FAR	待正式控规条件确认
FAR is an approved regulatory control and is absent from the public site package; it must come from official regulatory planning conditions.	
建筑高度	待正式控规条件确认
Height controls, plus any aviation, landscape or heritage limits, are not published; the proposal only states relative massing intent.	
道路面积	待正式控规条件确认
Road redline widths and cross-sections are not published, so road area cannot be recomputed from centrelines.	
道路面积率	待正式控规条件确认
Depends on road_area_sqm, which requires approved redline widths.	

■ 底图为临时粗略边界（provisional），不得作为官方红线或精确面积依据。

本图全部空间提案为概念建议 / 参考方案，可供专业团队深化研究；不构成法定规划、政府批准、实施确认或投资承诺。

容积率、建筑高度、建筑密度、道路红线与道路面积：待正式控规条件确认（pending）。

统筹研究范围：产业生态与未来城市

Coordinated research area: industry & future city

AI全栈自主创新链

Full-stack AI innovation

策源

高校院所与国家平台

S3 区间 / S4 零公里站沿线的科研与教育用地界面

开源协作

社区、代码与模型共建

S4 零公里站开源发布主场，站台广场直接对外

工程化

中试、评测与标准治理

S6 编组场承担全栈自主创新与安全治理评测

转化

孵化、成果转化与人才服务

S4 近校转化街区 + 人才社区服务

产业化

智能终端、内容与数据要素

S1 到发场对接城市消费与国际交往

公共体验

开放测试、活动与传播

全线可预约段 + 两处道岔广场

三大定位（公告）

● 百年京张文化带

● 都市AI生活体验带

● AI融合创新带

创新链为概念建议：各环节的承载空间、运营主体与开放规则需结合正式控规、权属与产业主管部门意见深化研究。

适配AI的未来城市形态

A future urban form fit for AI

可运行的线

令牌闭塞的今用：主线全段可预约、可运行、可复核，一枚令牌一个区间，运行窗口结束即归还普通公共使用。

站是接口

三处重点片区不是封闭园区，而是主线上的三个开放接口：站台广场承担到达、发布与展示，四象限步行连通把站与城缝合。

岔是缝合

两处道岔把东西两侧的社区、校区与园区接入主线，解决廊道两侧的步行与骑行断点。

绿色是基底

遗址公园连续绿地既是生态基底，也是开放测试的物理载体，避免为测试另建专用设施。

治理先行

每个场景都带具名运营方、明示数据边界与不可自动化取消的人工复核点；不做个体画像，不以指定供应商为必要条件。

可复算的空间供给（复算值）

绿地面积245.7 ha

绿地率21.5%

公共空间面积206.0 ha

公共空间比例18.0%

慢行系统长度16,730 m

东西向缝合线6 条

用户画像与运营边界

User types, operating limits

开源开发者

需求：发布、协作、测试、社区声誉

边界：不采集个人行为轨迹；活动数据仅做聚合统计

初创团队

需求：低成本办公、算力入口、产品试验场

边界：算力与数据服务需另行授权

头部企业访客

需求：展示、商务、国际接待、招聘

边界：企业标识与案例须清权

周边居民

需求：通勤、休闲、社区服务、低扰动更新

边界：不将居民画像用于商业推荐

高校师生

需求：成果转化、跨校协作、日常慢行

边界：校园数据与科研成果需授权

可预约段运行协议

预订—布设—按公开规则运行限定窗口—归还普通公共使用；具名运营方、明示数据边界、不可自动化取消的人工复核点。

本图层为 agent 有权定义的运营分区建议，不是法定规划控制、不是文保或蓝线范围、不构成审批依据。文保、水系、规划控制等官方约束图层在取得官方资料前保持空缺，不由 agent 代拟。


AI服务分区 6 段 | 场景节点 12 个

总体空间结构

Spatial structure


一线·三站·两岔·六段

line·3 stns·2 switches·6 seg

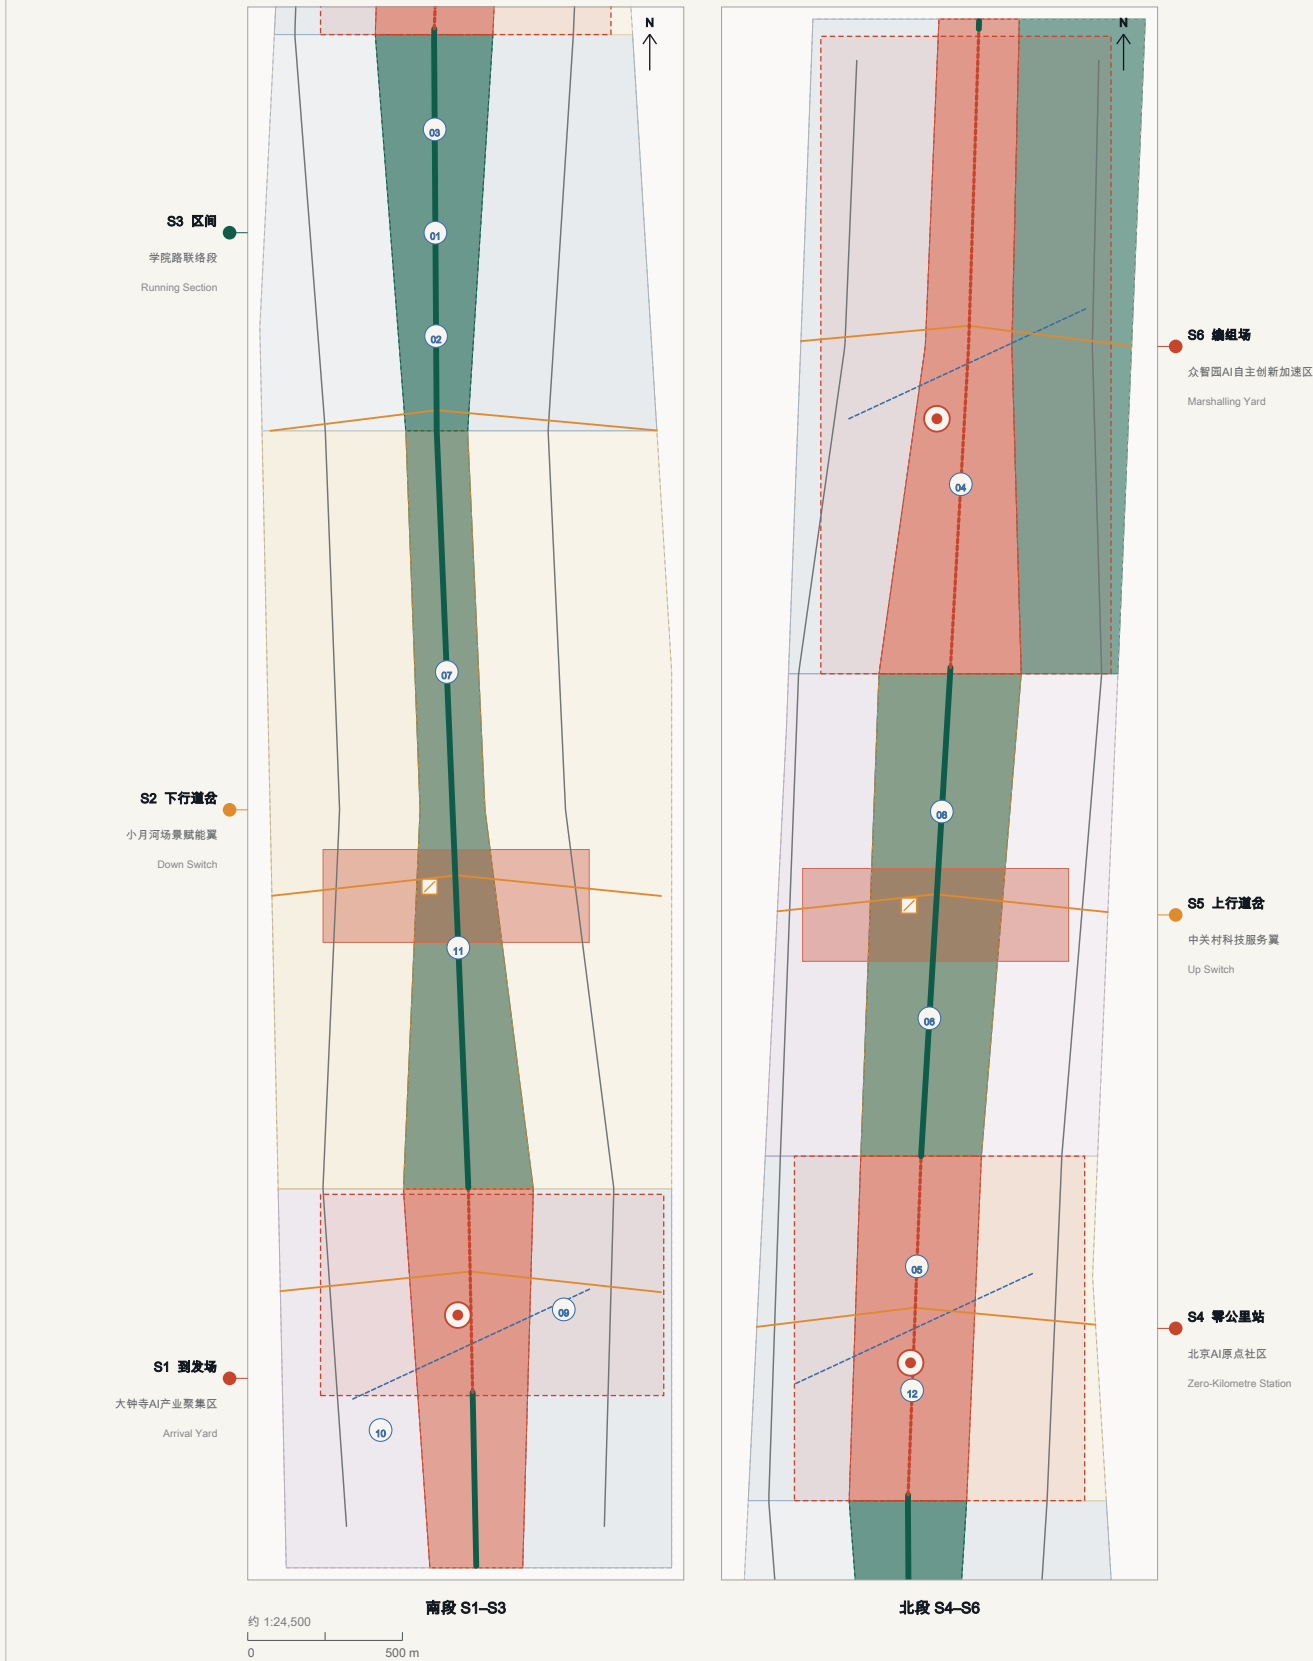


结构说明

主线沿京张遗址公园南北贯通，是慢行主线，也是开放测试轨道的物理载体。主线在三处重点片区“断开”为站点：断开处不是中断，而是把线交给城市——站台广场承担到达、发布与展示，四象限步行连通把站与城缝合。两处道岔把东西两侧的社区、校区与园区接入主线，是东西向缝合线与场景开放日的主场。

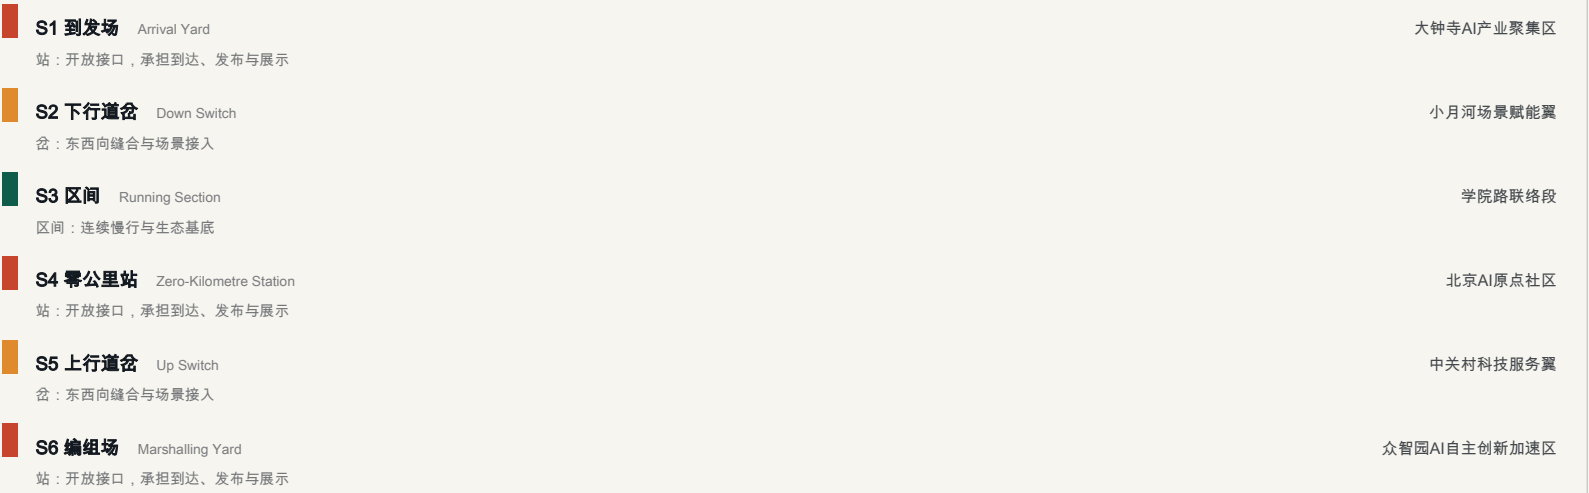

东西向缝合线	6
轨道接驳建议线	3
AI场景节点	12
朝圣地标节点	4
重点片区	3

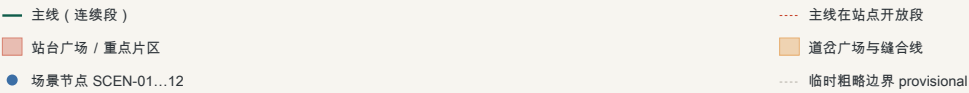

深化提示

- 站点“断开”是设计语言与运营安排，不是既有铁路运营方案，也不改变既有线位的法定属性。
- 主线、道岔与缝合线的跨越方式、净空、无障碍与消防疏散需由交通与市政专业复核。
- 两幅平面为同一条走廊的南北两段，比例尺一致；分幅仅为版面需要，不代表分区界线。
- 正式重点区 polygon 与官方红线发布后，本图结构关系需按新边界重新落位并复算全部指标。


底图为临时粗略边界 (provisional)，不得作为官方红线或精确面积依据。

本图全部空间提案为概念建议 / 参考方案，可供专业团队深化研究；不构成法定规划、政府批准、实施确认或投资承诺。

07 LAND USE

用地布局与城市更新

Land use & urban renewal

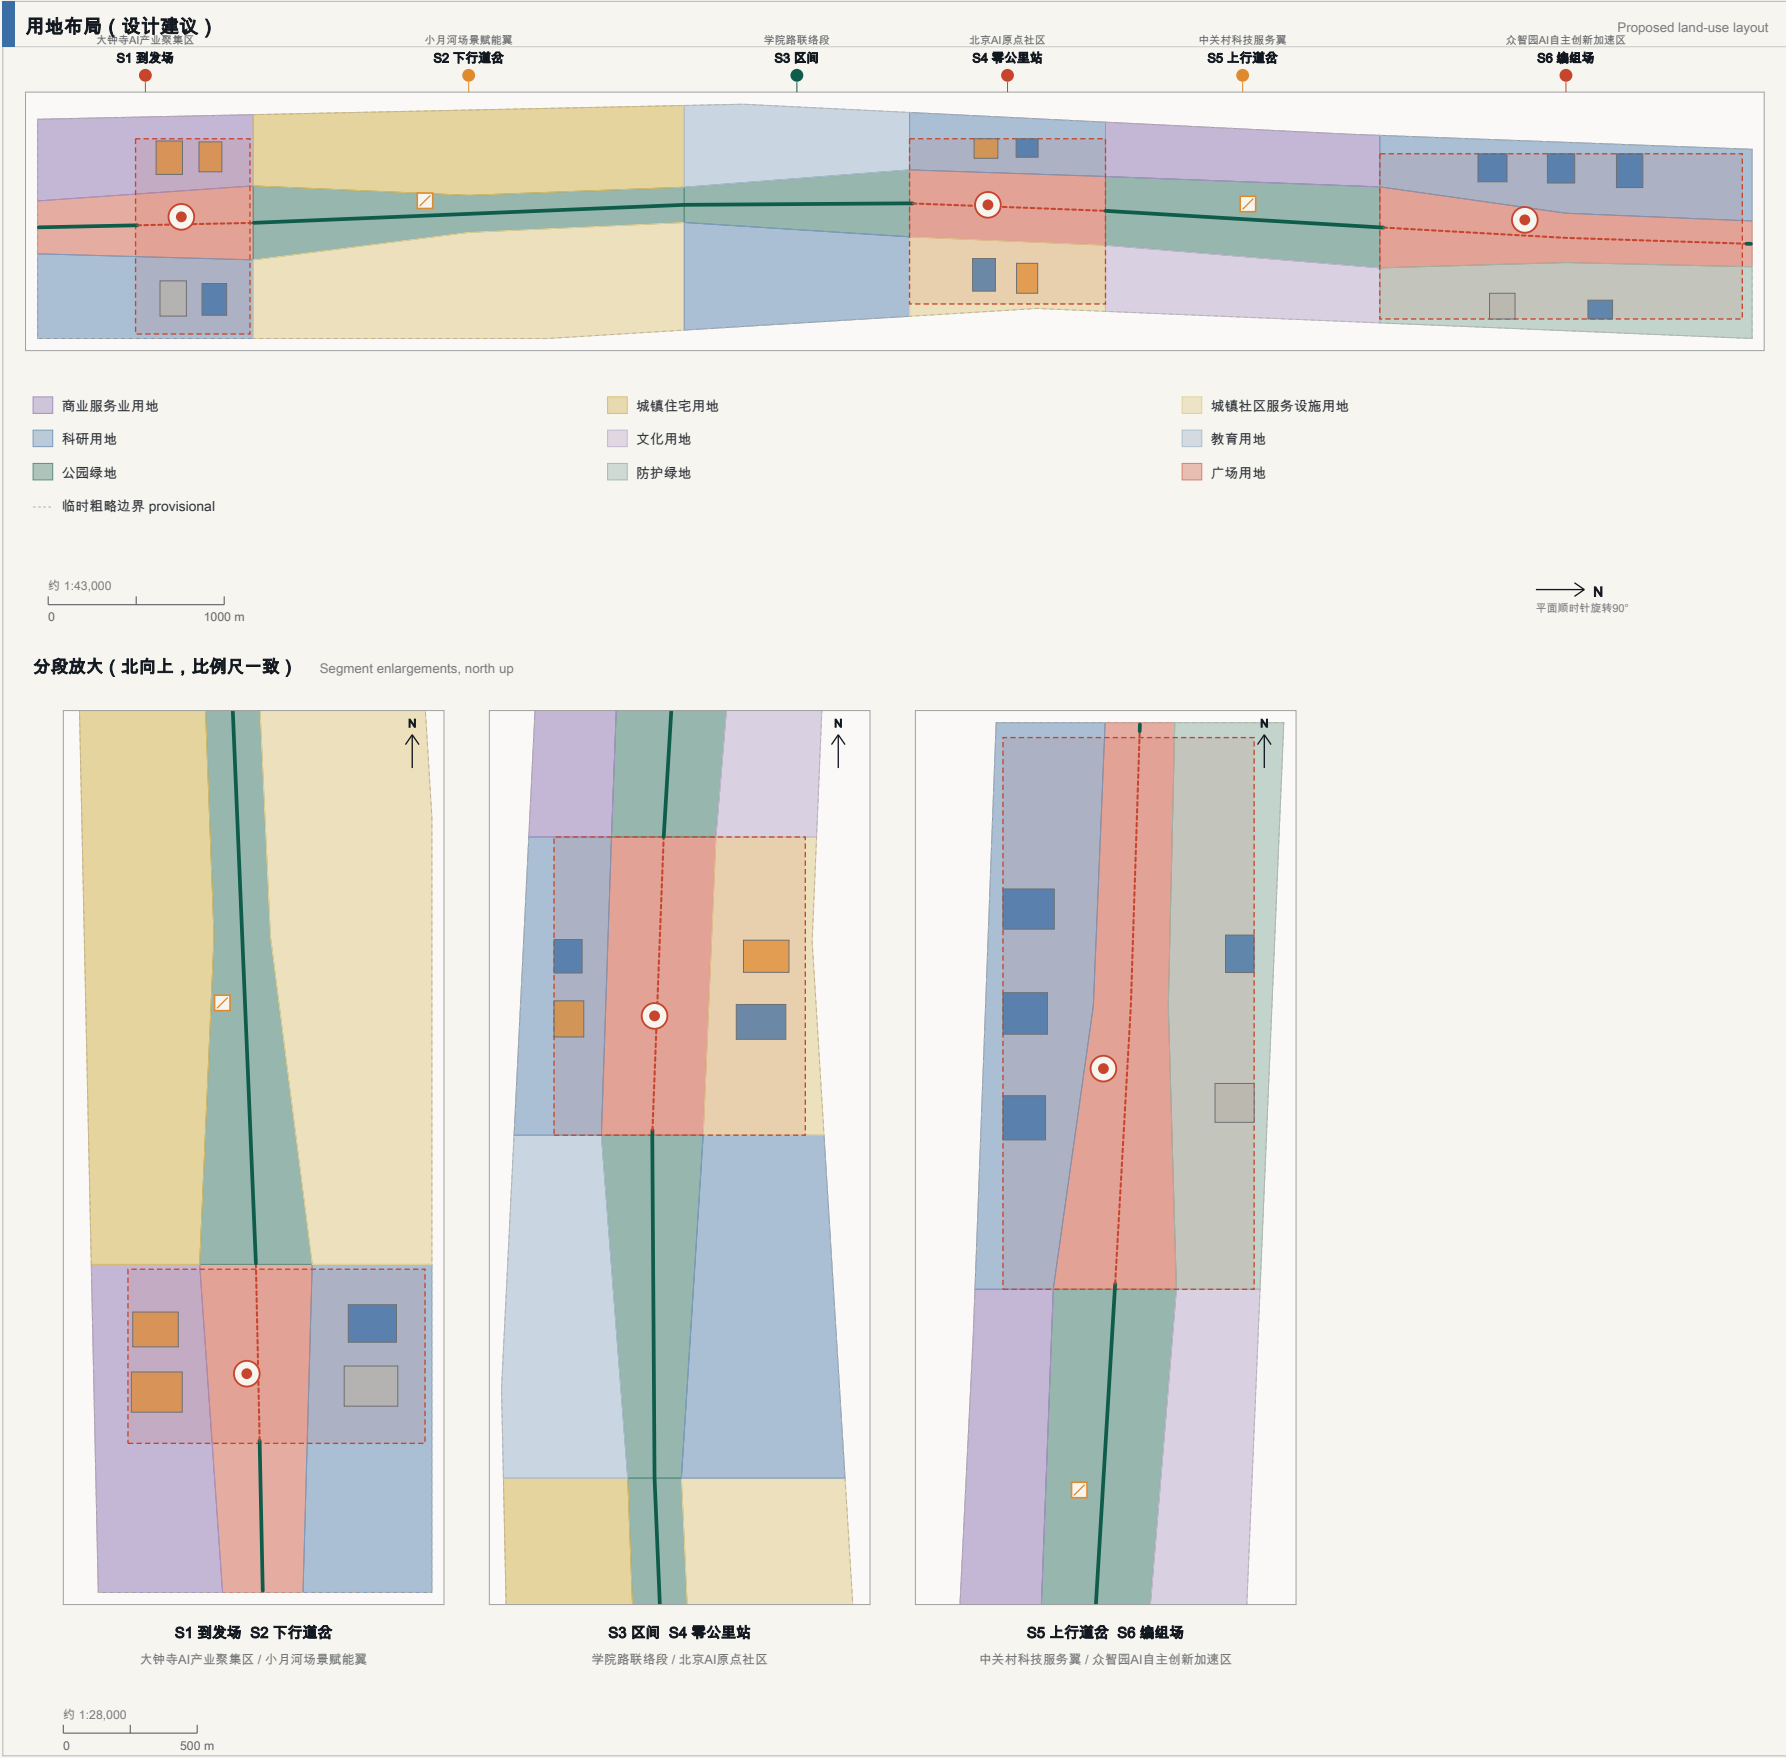

数据与说明		Data & notes
用地分类与面积 (metrics.json 复算)		
0802	科研用地 Research	239.5 ha 21.0%
0702	城镇社区服务设施用地 Community facilities	184.1 ha 16.1%
1401	公园绿地 Park green	166.8 ha 14.6%
1403	广场用地 Square / platform	154.4 ha 13.5%
0701	城镇住宅用地 Urban residential	112.4 ha 9.9%
05	商业服务业用地 Commercial & service	99.8 ha 8.7%
1402	防护绿地 Protective green	78.9 ha 6.9%
0803	文化用地 Culture	53.6 ha 4.7%
0804	教育用地 Education	51.7 ha 4.5%
用地图层合计 land_use_total_area_sqm		11.41 km²
提交边界面积 site_area_sqm		11.41 km²
城市更新与拆改留		
	保留 retain	2 处
	改造 renovate	4 处
	新建 new build	7 处
更新抓手建筑数量 renewal_building_count		13 处
建筑基底面积 building_footprint_area_sqm		29.5 ha
重点区内基底覆盖率 (示意)		8.0%
容积率 FAR		待正式控规条件确认
建筑高度		待正式控规条件确认
建筑密度		待正式控规条件确认
退线与建筑控制线		待正式控规条件确认
用地分类采用国土空间用途管制分类公开指引子集；本图用地为设计建议，正式用途、边界与强度以官方控规为准。建筑基底为概念示意，用于说明更新抓手与功能落位，拆改留结论待权属与现状建筑资料确认。		


底图为临时粗略边界 (provisional)，不得作为官方红线或精确面积依据。

本图全部空间提案为概念建议 / 参考方案，可供专业团队深化研究；不构成法定规划、政府批准、实施确认或投资承诺。

容积率、建筑高度、建筑密度、道路红线与道路面积：待正式控规条件确认 (pending)。

交通、轨道、慢行与市政支撑

Mobility, rail, slow traffic & municipal support

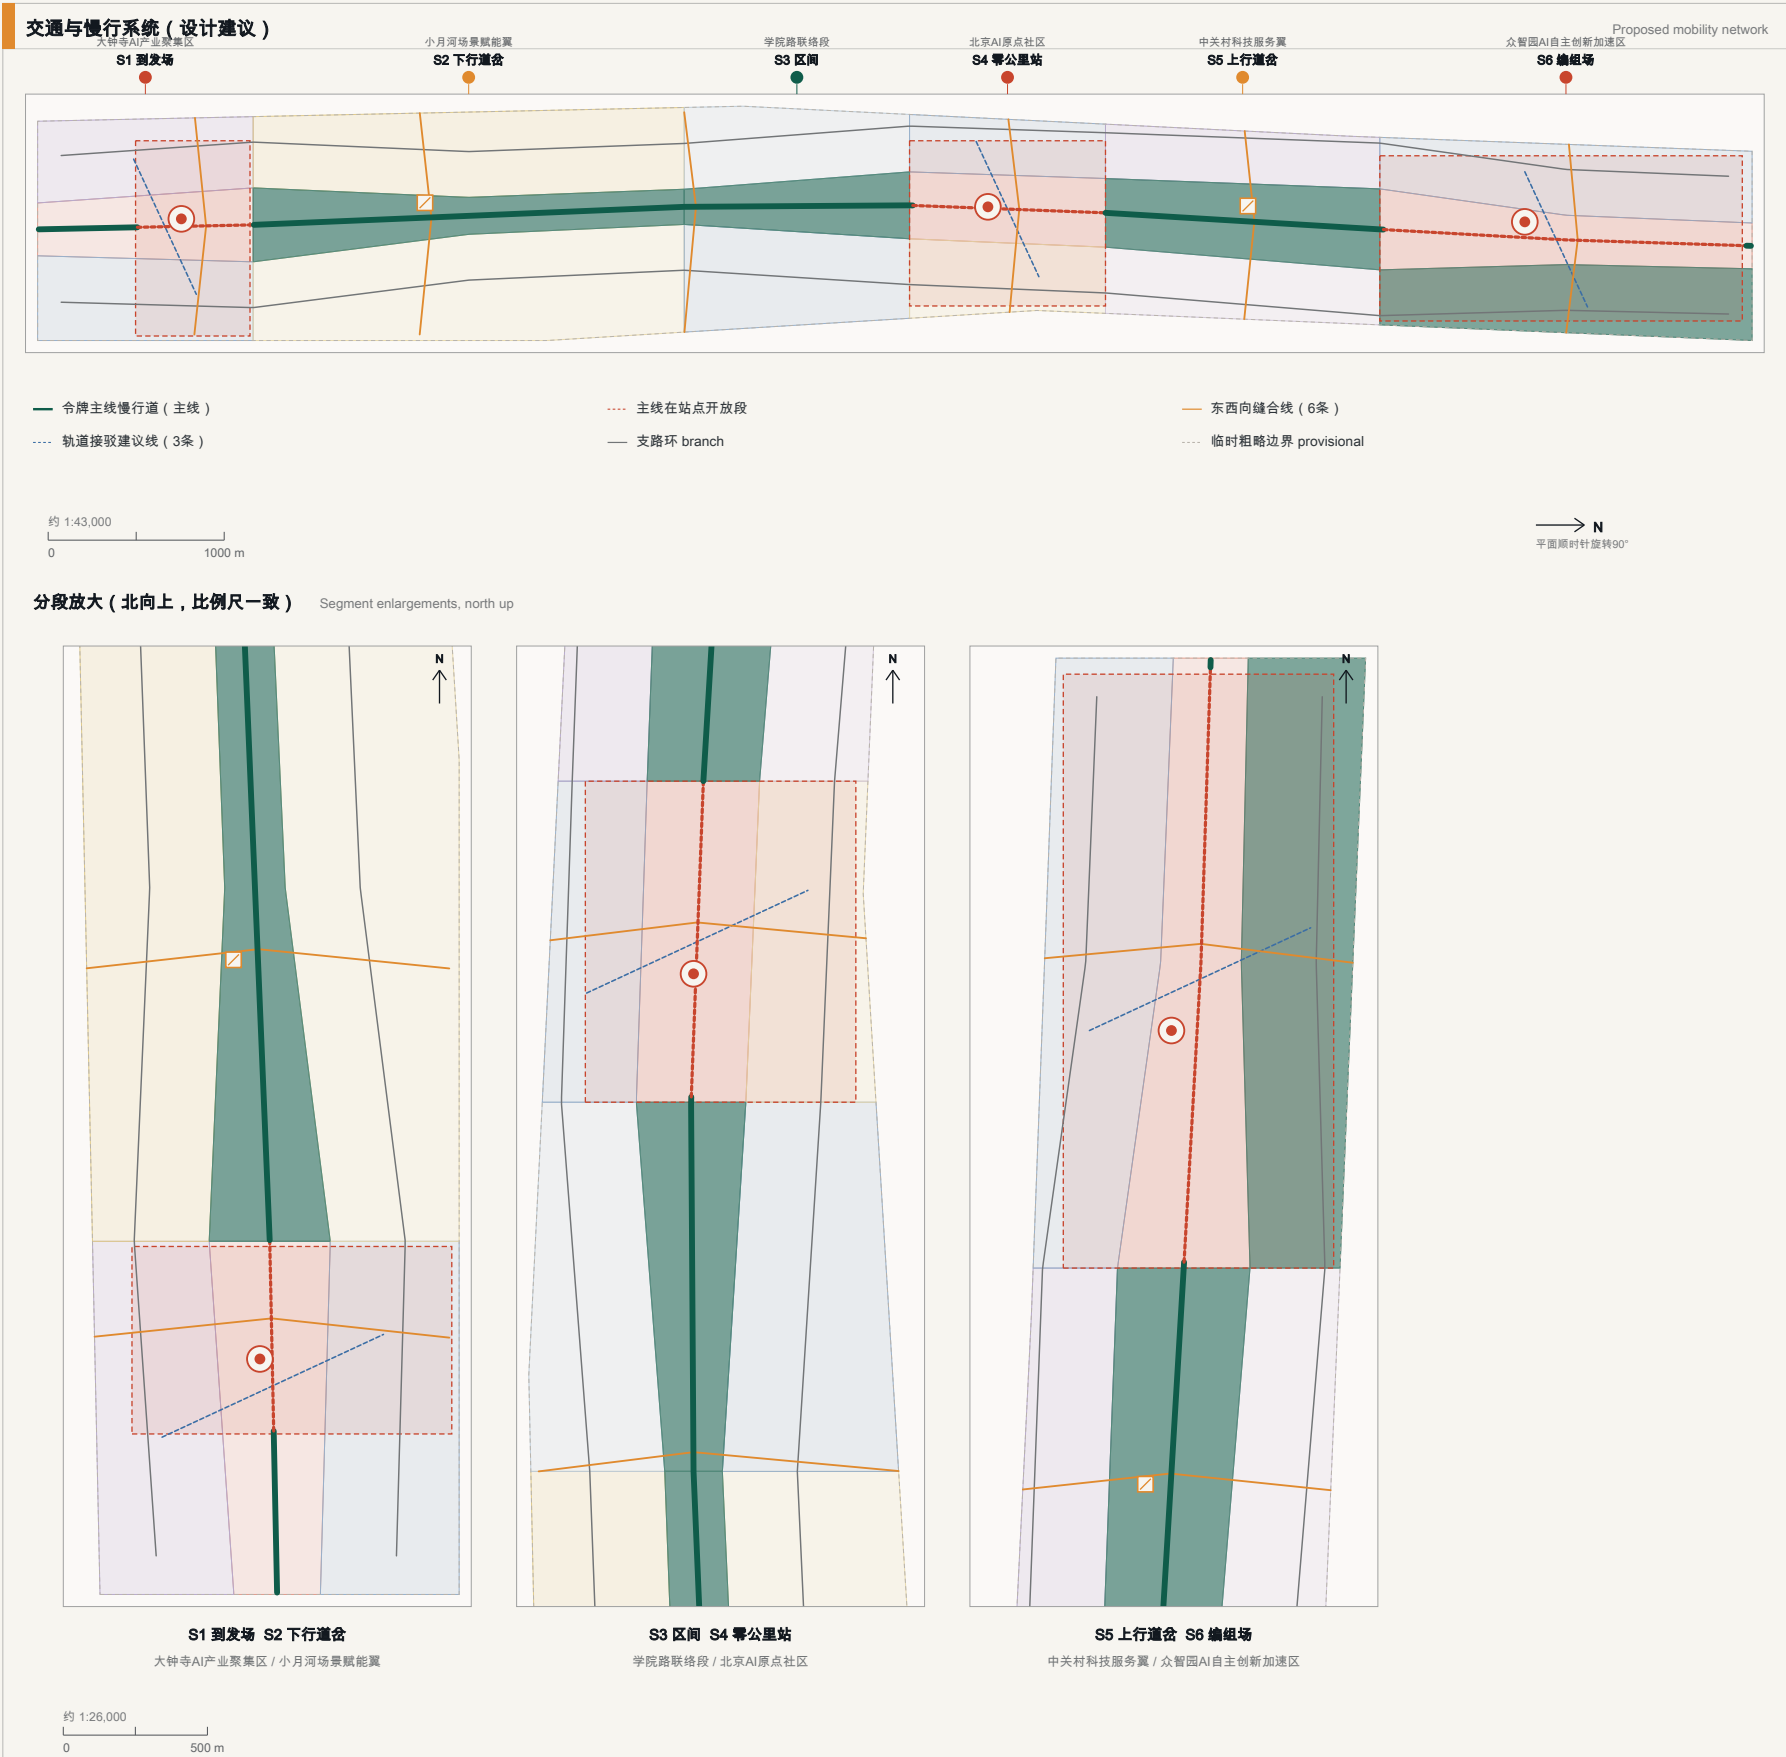

底图为临时粗略边界 (provisional) , 不得作为官方红线或精确面积依据。

本图全部空间提案为概念建议 / 参考方案, 可供专业团队深化研究 ; 不构成法定规划、政府批准、实施确认或投资承诺。

容积率、建筑高度、建筑密度、道路红线与道路面积 : 待正式控规条件确认 (pending) 。

数据与说明

Data & notes

交通与慢行 (可复算口径)

道路中心线总长 road_network_length_m	38,211 m
慢行系统长度 slow_mobility_length_m	16,730 m
东西向缝合线 east_west_stitch_count	6 条
轨道接驳建议线 transit_connector_count	3 条

道路面积 road_area_sqm	待正式控规条件确认
道路面积率 road_area_ratio	待正式控规条件确认
道路红线宽度与横断面	待正式控规条件确认
停车与非机动车停放配建标准	待正式控规条件确认

线位清单 (设计建议线)

ROAD-001	令牌主线慢行道	greenway
ROAD-002	西侧支路环	branch
ROAD-003	东侧支路环	branch
CROSS-A	大钟寺四象限步行连通	pedestrian
CROSS-B	下行道岔东西缝合线	pedestrian
CROSS-C	学院路联络段跨线	cycleway
CROSS-D	零公里站东西缝合线	pedestrian
CROSS-E	上行道岔东西缝合线	pedestrian
CROSS-F	编组场北段跨线	cycleway
TRANSIT-1	大钟寺站接驳线	transit_connection
TRANSIT-2	零公里站接驳线	transit_connection
TRANSIT-3	编组场站接驳线	transit_connection


市政与新型基础设施策略

- 端侧算力驿站与分布式能源结合公共服务设施布点, 作为待深化的新型基础设施原型 ; 承载能力、能源与安全条件需以正式市政资料核定。
- 轨道站点一体化按“站—场—城”三级接驳组织 : 站台广场承担到达面, 接驳建议线连接站点与主线, 四象限步行连通解决路口断点。
- 管线、排水、防洪、消防与人防条件缺失, 市政专业结论只能作为方法与前置条件清单。

京张遗址公园活力带与蓝绿公共空间


Jing-Zhang heritage park vitality belt & blue-green public space

蓝绿与公共空间系统 (设计建议)

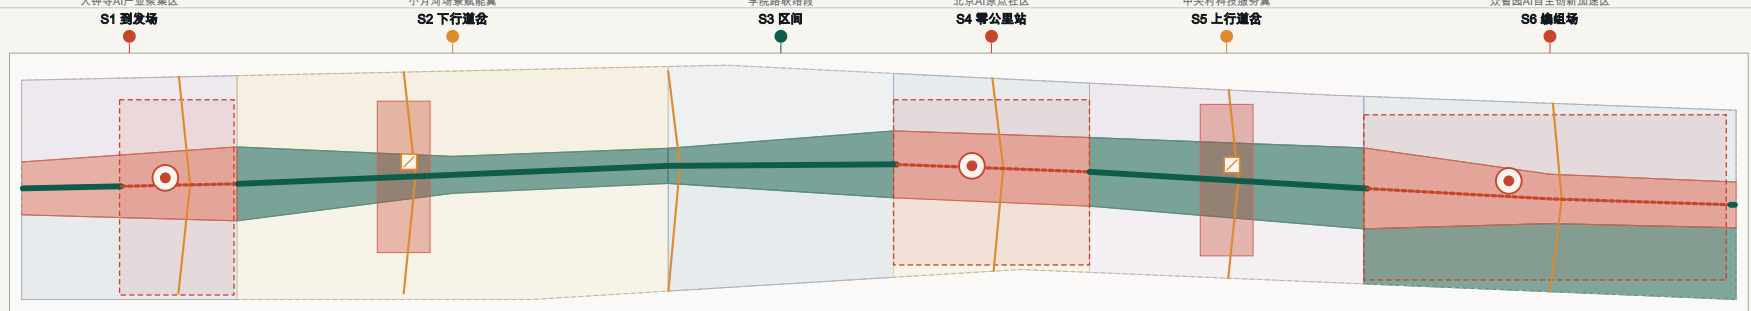


分段放大 (北向上, 比例尺一致)

Segment enlargements, north up

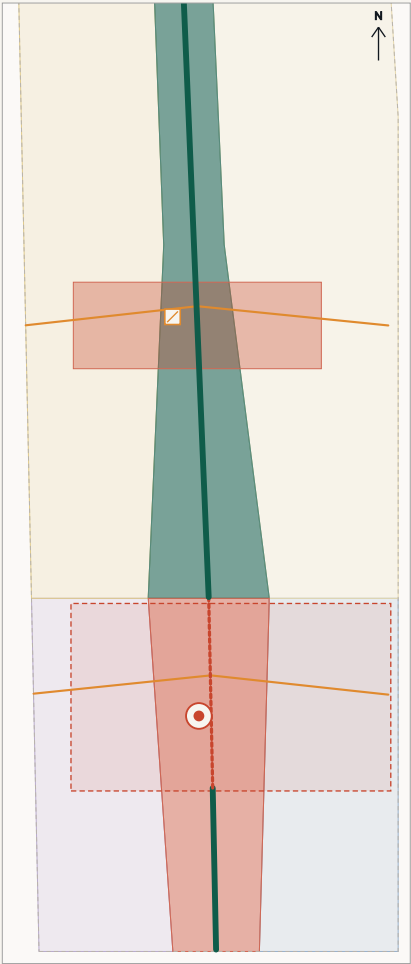


S1 到发场 S2 下行道岔

大钟寺AI产业聚集区 / 小月河场景赋能翼

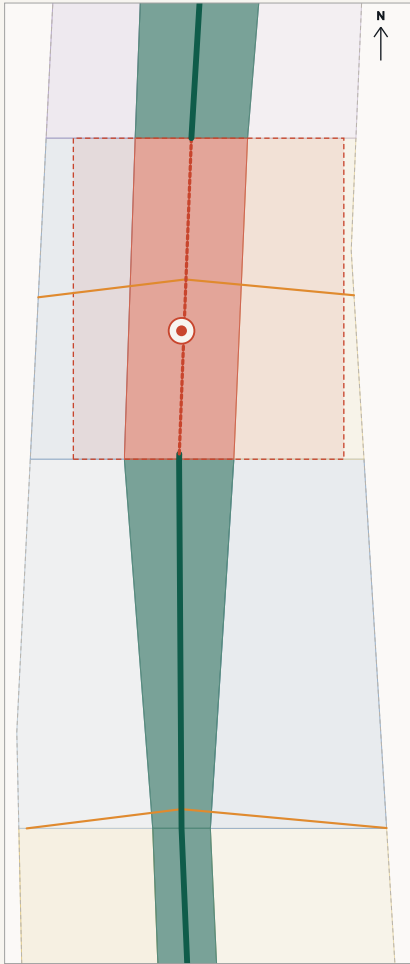

S3 区间 S4 零公里站

学院路联络段 / 北京AI原点社区

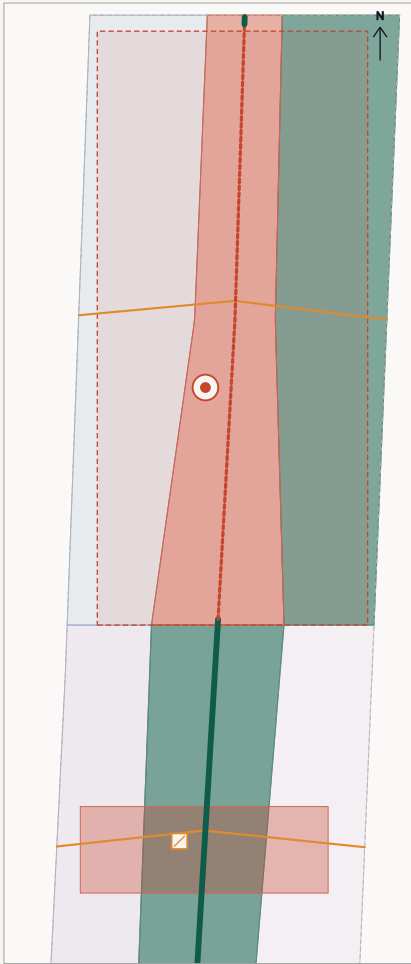

S5 上行道岔 S6 编组场



中关村科技服务翼 / 众智园AI自主创新加速区



数据与说明

蓝绿与公共空间（复算）

绿地面积 green_space_area_sqm	245.7 ha
绿地率 green_ratio	21.5%
公共空间面积 public_space_area_sqm	206.0 ha
公共空间比例 public_space_ratio	18.0%

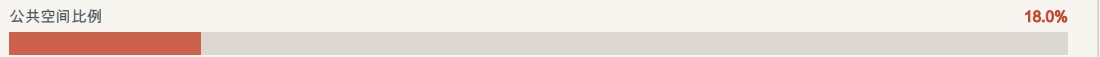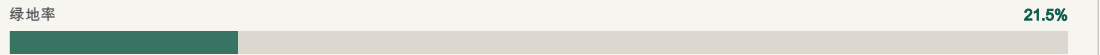

遺址公園活力帶分段

- S2 下行道岔-小月河场景赋能段京张遗址公园绿地
遗址公园连续绿地段，同时是开放测试轨道的绿色基底
 - S3 区间-学院路联络线段京张遗址公园绿地
遗址公园连续绿地段，同时是开放测试轨道的绿色基底
 - S5 上行道岔-中关村科技服务翼段京张遗址公园绿地
遗址公园连续绿地段，同时是开放测试轨道的绿色基底
 - S6 编组场北端防护绿带
北端生态缓冲，界面条件待正式水系与道路资料确认

站台与道岔广场

- **到达场站台广场**
大钟寺站四象限步行连通与到达展示面
- **零公里站台广场**
零公里碑、开源发布厅与荣誉展示主场
- **编组场站台广场**
自主创新开放展示与标准治理公众面
- **下行道岔广场**
小月河景观赋能的东西向公共客厅与场景开放日主场
- **上行道岔广场**
中关村科技服务翼的东西向公共客厅与国际交往面

1 - platform

4 · platform

6 · platform

S2 · switch

S5 · switch


绿地与公共空间面积由提交图层复算，随临时粗略边界变化；水系蓝线、防洪与生态条件未取得，清河与小月河界面策略只能作为方法建议。

底图为临时粗略边界 (provisional)，不得作为官方红线或精确面积依据。

本图全部空间提案为概念建议 / 参考方案, 可供专业团队深化研究; 不构成法定规划、政府批准、实施确认或投资承诺。

众智园AI自主创新加速区

Marshalling Yard

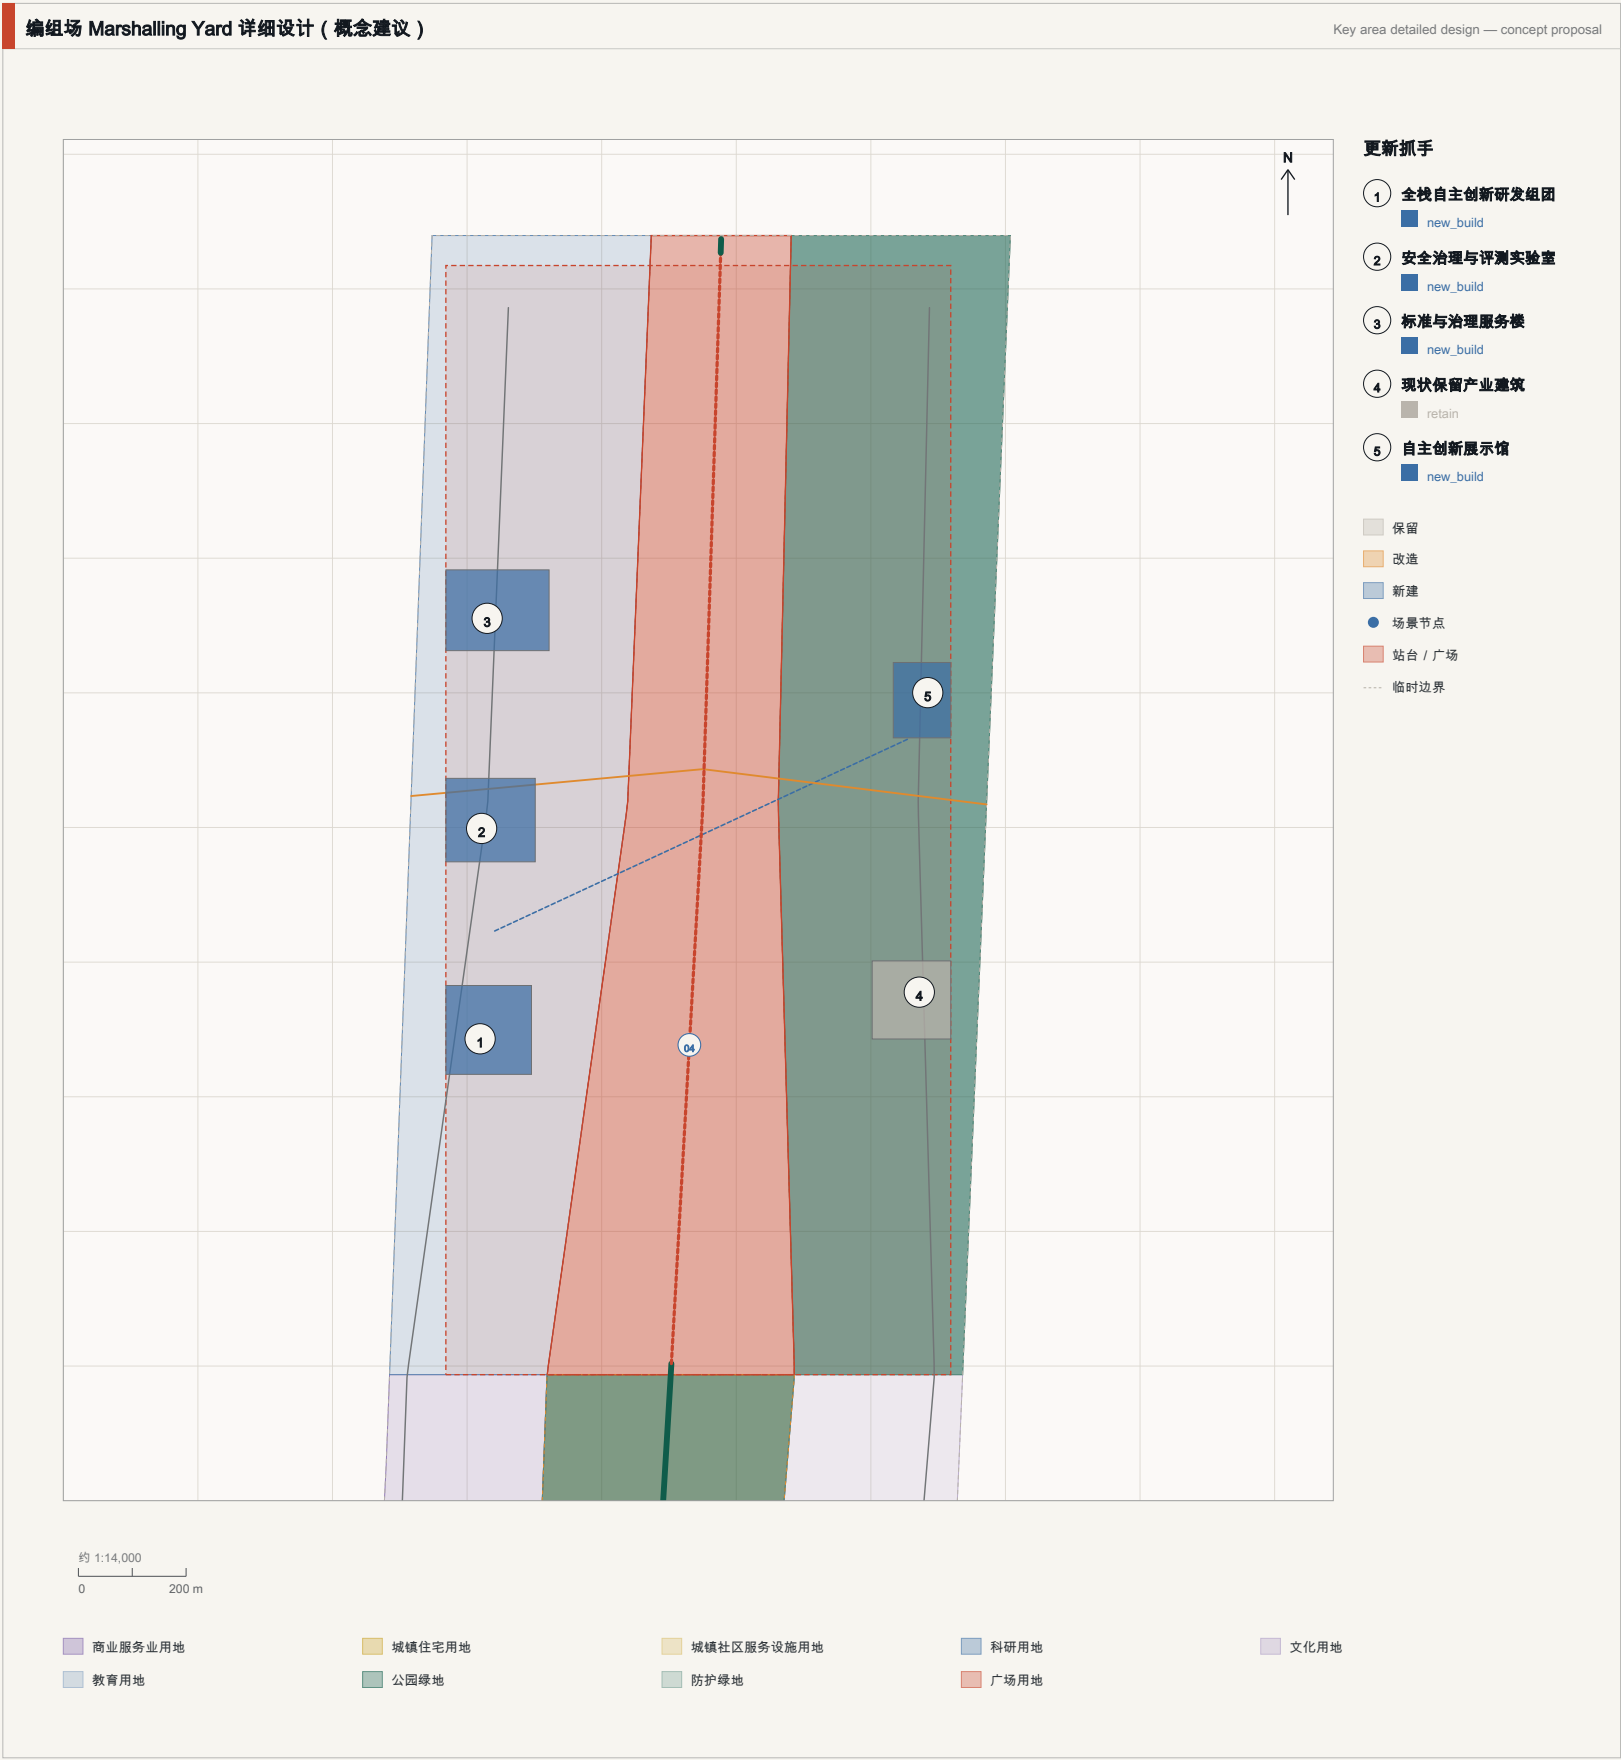

底图为临时粗略边界 (provisional) ，不得作为官方红线或精确面积依据。

本图全部空间提案为概念建议 / 参考方案，可供专业团队深化研究；不构成法定规划、政府批准、实施确认或投资承诺。

容积率、建筑高度、建筑密度、道路红线与道路面积：待正式控规条件确认 (pending) 。

定位、空间动作与指标

Positioning, moves & metrics

花园型全栈自主创新街区

公告面积 announced	192.1 ha
提交几何复算 recomputed	192.9 ha
geometry_status	exact_polygon_missing_provisional_available

空间动作 (概念建议)

- 强化清河界面与北端防护绿带，把生态缓冲同时用作开放测试与展示的绿色基底。
- 以标准制定、安全评测与全栈自主创新研发组团构成产业核心，配自主创新展示馆对外开放。
- 站台广场承担自主创新开放展示与标准治理公众面；北段跨线解决北五环界面的步行断点。
- 对外交通依赖轨道接驳建议线与支路环；站位与红线以正式轨道与控规资料为准。

更新抓手清单

01 全栈自主创新研发组团	ai_r_and_d
Full-stack autonomous R&D cluster	new_build
02 安全治理与评测实验室	lab
Safety governance and evaluation lab	new_build
03 标准与治理服务楼	office
Standards and governance service building	new_build
04 现状保留产业建筑	existing_retained
Retained existing industrial building	retain
05 自主创新展示馆	cultural
Autonomous innovation gallery	new_build

本片区待正式控规条件确认

容积率 FAR	pending
建筑高度	pending
建筑密度	pending
建筑规模	pending
道路红线与退线	pending

重点区边界为临时粗略范围 (official_boundary=false) ；正式 polygon 发布后，本片区的用地、建筑、交通与公共空间落位及全部面积指标须重新生成与复算。

本片区AI场景节点与运行边界

04 模型安全红队沙盒	产业测试验证场景	人工复核 必需
仅使用公开或已授权数据；不做个体画像；不以指定供应商为必要条件；场景为概念建议，未获批准运营。		

可预约段：编组场可预约段

评测与标准治理场景优先，公众可观察

北京AI原点社区

Zero-Kilometre Station



定位、空间动作与指标

Positioning, moves & metrics

近校型成果转化与人才社区

公告面积 announced	104.3 ha
提交几何复算 recomputed	104.3 ha
geometry_status	exact_polygon_missing_provisional_available

空间动作 (概念建议)

- 零公里碑与开源发布厅构成主场：成果发布、代码贡献展示与小型路演在站台广场直接对外。
- 近校成果转化孵化器、开源协作实验室紧邻高校界面，用东西向缝合线把校区、园区与街区连成慢行网络。
- 补足人才公寓组团与原点社区服务中心，回应人才特区的居住、生活与社交需求。
- 拆改留分类仅为概念示意；权属、现状建筑与建设年代资料缺失，结论待正式资料确认。

更新抓手清单

01 近校成果转化孵化器	incubator
Campus-adjacent incubator	renovate
02 开源协作实验室	lab
Open-source collaboration lab	new_build
03 人才公寓组团	talent_apartment
Talent housing cluster	new_build
04 原点社区服务中心	community_service
Origin community service centre	renovate

本片区待正式控规条件确认

容积率 FAR	pending
建筑高度	pending
建筑密度	pending
建筑规模	pending
道路红线与退线	pending

重点区边界为临时粗略范围（ official_boundary=false ）；正式 polygon 发布后，本片区的用地、建筑、交通与公共空间落位及全部面积指标须重新生成与复算。

本片区AI场景节点与运行边界

05 开源发布厅	人工复核 必需
仅使用公开或已授权数据；不做个体画像；不以指定供应商为必要条件；场景为概念建议，未获批准运营。	
12 全球AI活动周步行路统起点	人工复核 必需
仅使用公开或已授权数据；不做个体画像；不以指定供应商为必要条件；场景为概念建议，未获批准运营。	

可预约段：零公里站可预约段

开源发布与社区活动优先，公共可达性不得让渡

■ 底图为临时粗略边界（ provisional ），不得作为官方红线或精确面积依据。

本图全部空间提案为概念建议 / 参考方案，可供专业团队深化研究；不构成法定规划、政府批准、实施确认或投资承诺。

容积率、建筑高度、建筑密度、道路红线与道路面积：待正式控规条件确认（ pending ）。

10 KEY AREA · 到发场

大钟寺AI产业聚集区

Arrival Yard



底图为临时粗略边界（provisional），不得作为官方红线或精确面积依据。

本图全部空间提案为概念建议 / 参考方案，可供专业团队深化研究；不构成法定规划、政府批准、实施确认或投资承诺。

容积率、建筑高度、建筑密度、道路红线与道路面积：待正式控规条件确认（pending）。

定位、空间动作与指标

Positioning, moves & metrics

城市型智能经济与国际交往街区

公告面积 announced	72.0 ha
提交几何复算 recomputed	72.0 ha
geometry_status	exact_polygon_missing_provisional_available

空间动作（概念建议）

- 以大钟寺站一体化与四象限步行连通为骨架，把站点客流直接引入站台广场与主线南端。
- 智能终端企业总部组团、数据要素会客厅与国际路演客厅构成城市型产业界面。
- 智能原生消费街区承接商业服务业用地，把AI+生活服务落到可运营的小尺度街区。
- 规划绿地与广场复合利用，作为到达展示面；具体交叉口组织需交通专业复核。

更新抓手清单

01 到发场智能原生消费街区	retail
Arrival Yard intelligent-native retail block	renovate
02 国际路演客厅	mixed_use
International demo-day lounge	renovate
03 智能终端企业总部组团	office
Intelligent-terminal HQ cluster	retain
04 数据要素会客厅	ai_r_and_d
Data-element service house	new_build

本片区待正式控规条件确认

容积率 FAR	pending
建筑高度	pending
建筑密度	pending
建筑规模	pending
道路红线与退线	pending

重点区边界为临时粗略范围（official_boundary=false）；正式 polygon 发布后，本片区的用地、建筑、交通与公共空间落位及全部面积指标须重新生成与复算。

本片区AI场景节点与运行边界

09 数据要素会客厅	人工复核 必需
仅使用公开或已授权数据；不做个体画像；不以指定供应商为必要条件；场景为概念建议，未获批准运营。	
10 智能原生消费街区	人工复核 必需
仅使用公开或已授权数据；不做个体画像；不以指定供应商为必要条件；场景为概念建议，未获批准运营。	

可预约段：到发场可预约段

商业与国际交往场景优先，活动期与站点客流协调

城市风貌与文化叙事

Urban character, narrative

识别系统

Identity

TOKEN BLOCK

京张令牌 · 百年京张AI创新带

标志是一条水平线，在三处断开：断开处就是三个站。线是产品，站是接口。不使用机车、齿轮、大脑或电路板等具象符号。

主色 ink #12181F

正文与主线

站色 station #C8452D

三站，最高对比

岔色 switch #E08A2E

两岔与缝合线

脊色 spine #0F5C4A

遗址公园绿

研究 research #3B6EA5

科研与创新用地

服务 service #7A5EA8

商业与服务用地

生活 living #C9A227

居住与社区用地

临时 provisional #B9B4AC

临时边界，低对比虚线

文化融合叙事

百年京张：令牌从行车凭证变为场景凭证，遗址公园既是纪念，也是运行中的公共设施。

中关村文化：以开源协作、成果发布与公开评测承接创新传统，而不是以标志性造型表达。

AI新文化：零公里碑、开源发布厅与荣誉展示体系构成可参与的城市仪式。

所有品牌、字体、图像、肖像与企业标识须清权后使用；本套图纸不使用未清权素材。

体量、界面与高度控制方法

Bulk, frontage & height control

本页不给出任何高度或强度数值

建筑高度、容积率、建筑密度、退线与建筑控制线均为审定管控内容，在公开资料中登记为 missing；本方案只提出相对关系与控制方法，待正式控规条件确认后赋值。

沿主綫低、向外围高

遗址公园两侧保持低矮界面与视线通透，把高度需求向支路环一侧转移。

站点强化、区间收敛

三处站点允许形成可识别的到达面；区间段以连续绿地与慢行为主，不做体量竞争。

岔口对位

东西向缝合线两端的建筑界面对位开口，保证跨廊道视线与步行连续。

屋顶第五立面

面向公园与站台广场的屋顶纳入风貌控制，避免设备层直接暴露。

既有建筑优先

现状保留产业建筑作为风貌锚点，新建体量以退让与错落回应既有肌理。

拆改留方法（不给结论）

保留 retain：具历史或产业记忆价值、结构条件可用的既有建筑，先评估后处置。

改造 renovate：功能不匹配但结构可用者，优先首层开放与公共界面改造。

新建 new build：仅在功能缺口明确、且不侵占公共空间与绿地时提出。

任何拆除结论均需权属、现状建筑与建设年代资料支撑，本方案不做拆除判断。

深度依据 height_massing_character

朝圣地标与活动体系

Pilgrimage landmarks, events

朝圣地标节点 pilgrimage_landmark_count

4 处

AI场景卡 ai_scenario_card_count

12 张

零公里碑

开源发布与荣誉展示主场，年度贡献者铭刻

S4 零公里站台广场

开源发布厅

成果发布、代码贡献展示与小型路演

S4 北京AI原点社区

自主创新展示馆

全栈自主创新与标准治理的公众面

S6 编组场

国际路演客厅

智能体、智能终端与内容产业的国际交往界面

S1 到发场

全球AI创新活动体系（概念建议）

场景开放日

以可预约段为单位，按公开规则开放运行窗口，窗口结束即归还普通公共使用。

全球AI活动周

从遗址文化、开源社区、产业展示到国际路演的可步行体验路线。

开发者社区常态运营

开源发布厅与协作实验室的日常使用，不依赖大型活动。

标准与治理工作坊

编组场承接标准制定与安全评测的公开环节。

活动与运营内容为概念建议 / 参考方案，可供专业团队深化研究；不代表已确定的政府活动安排、许可或投资承诺。


底图为临时粗略边界（provisional），不得作为官方红线或精确面积依据。

本图全部空间提案为概念建议 / 参考方案，可供专业团队深化研究；不构成法定规划、政府批准、实施确认或投资承诺。

xiaowuzicode · starixs · Token Block

更新项目清单、实施政策与分期

Renewal project list, policy & phasing

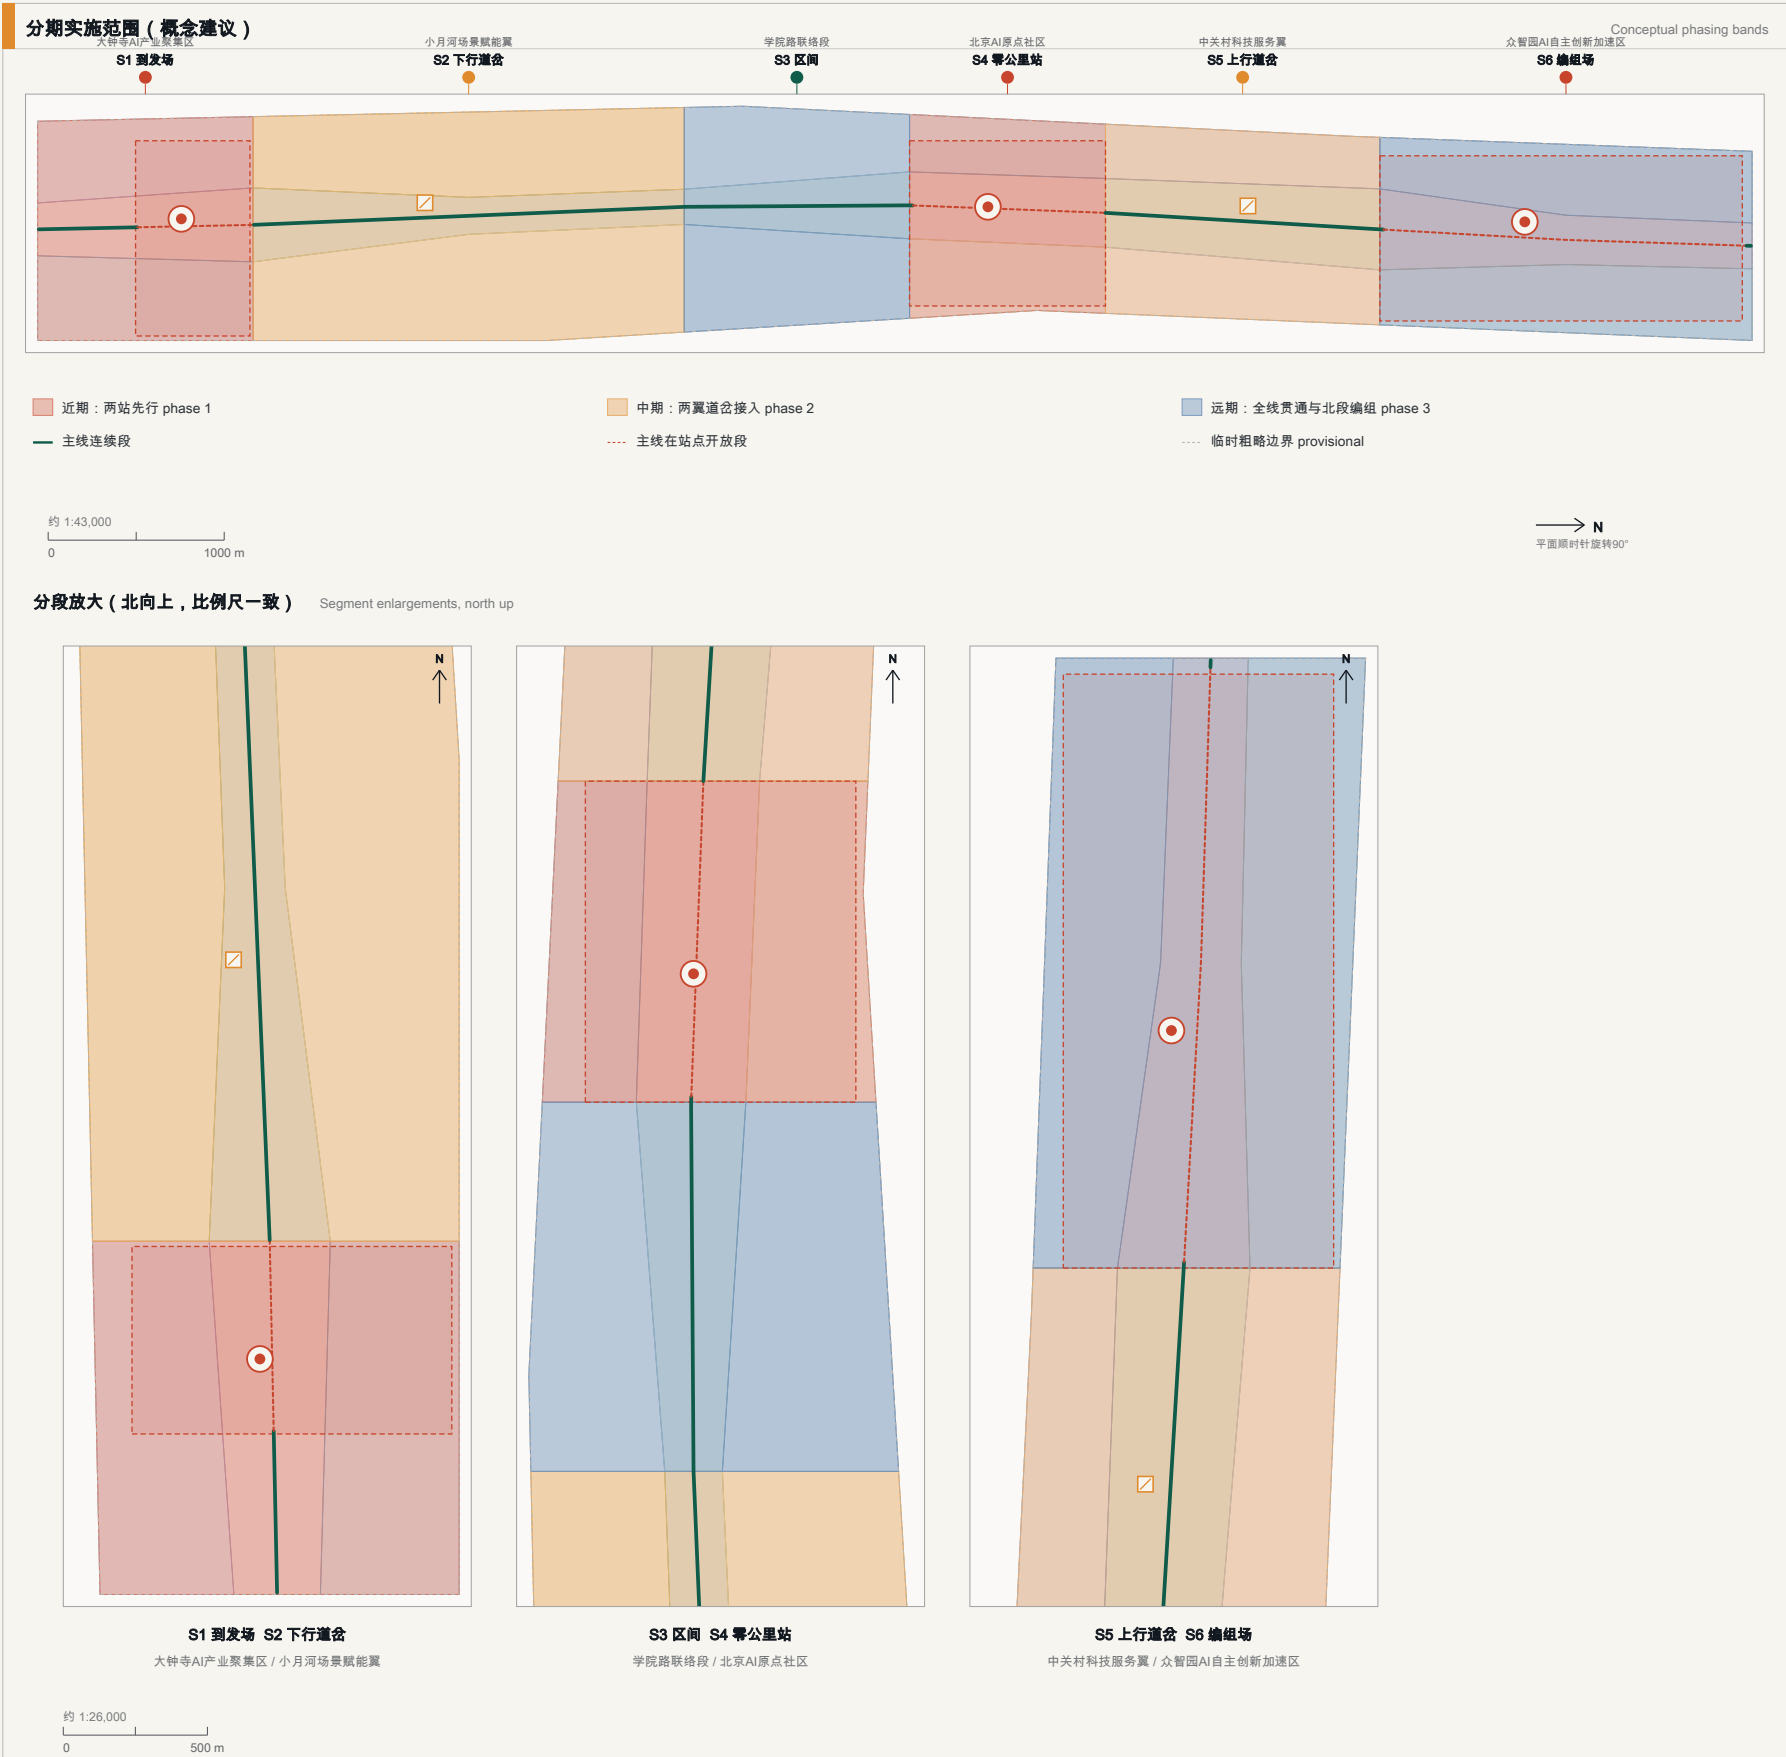

数据与说明

Data & notes

分期范围面积 (复算)

近期：两站先行 带 S1, S4 以到发场与零公里站为先行段，用轻量设施、活动与开放场景启动，不依赖大规模工程条件	276.6 ha
中期：两翼道岔接入 带 S2, S5 打通两翼东西向缝合线与道岔广场，把场景赋能与科技服务接入主线	482.0 ha
远期：全线贯通与北段编组 带 S3, S6 完成区间段贯通与编组场深化，依赖正式控规、轨道与市政条件确认	382.6 ha

更新项目清单 (概念建议)

JZ-01	京张遗址公园慢行断点缝合	公共空间 / 交通
依赖：道路红线、桥下空间、交通组织复核		
JZ-02	编组场清河创新界面	蓝绿空间 / 产业展示
依赖：河道蓝线、生态与防洪条件		
JZ-03	零公里站近校成果转化街	城市更新 / 产业服务
依赖：校区边界、权属、首层业态		
JZ-04	到发场四象限步行连通	轨道一体化 / 慢行
依赖：轨道站点、道路交叉口、市政管线		
JZ-05	AI公共服务与端侧算力节点	新基建 / 公共服务
依赖：能源、算力、安全与运营主体		
JZ-06	全球AI活动周公共路线	运营 / 品牌
依赖：公共空间许可、活动安全、版权清权		

实施政策建议


- 近期以轻量设施、运营活动与服务平台启动，不依赖大规模工程条件与征拆。
- 中期打通东西向缝合线与道岔广场，需交通、市政与权属条件同步确认。
- 远期完成全线贯通与北段编组，依赖正式控规、轨道与市政条件落实。
- 征集周期 (约100天) 是成果提交要求，与城市更新实施分期是两件事，不得混为一谈。
- 无权属、资金、实施主体与审批路径支撑的内容，一律写为实施风险而非落地承诺。

底图为临时粗略边界 (provisional)，不得作为官方红线或精确面积依据。

本图全部空间提案为概念建议 / 参考方案，可供专业团队深化研究；不构成法定规划、政府批准、实施确认或投资承诺。

AI+场景、数据治理与人工复核

AI+ scenarios, data, human review

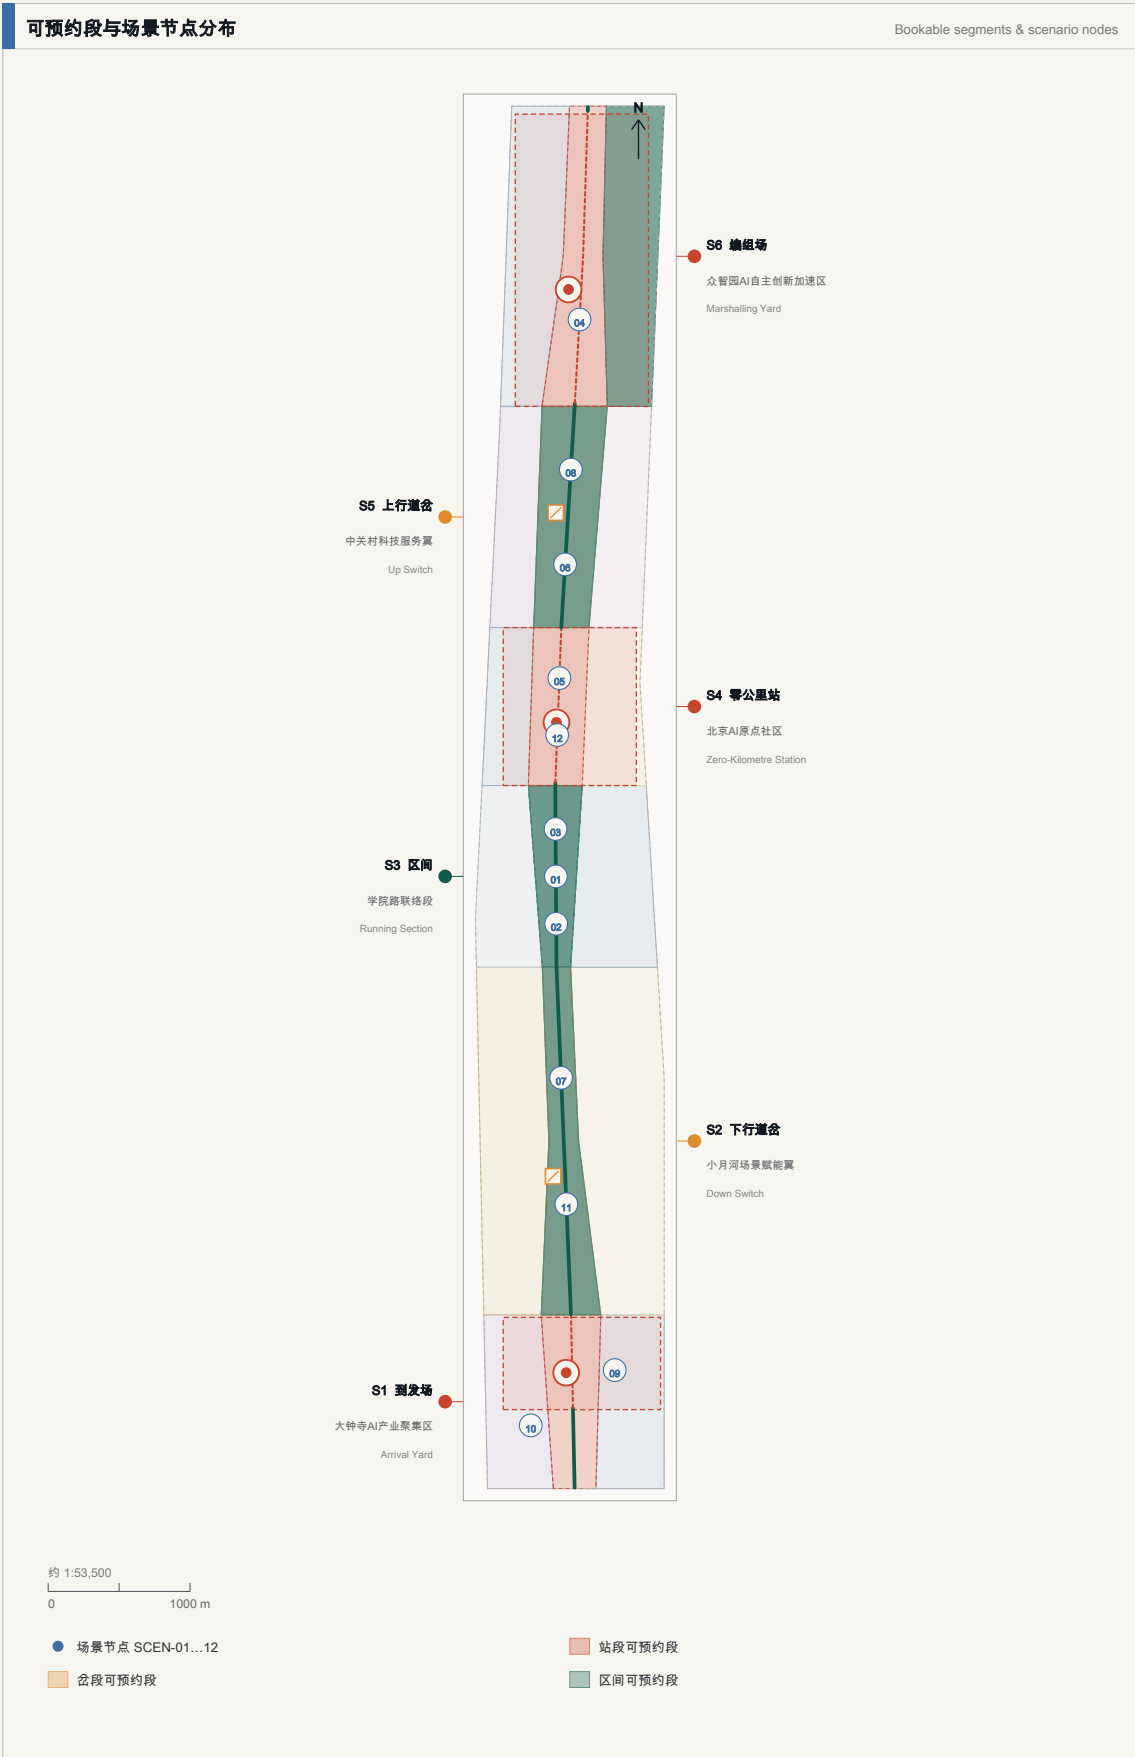

AI场景卡		AI scenario card
01	可预约轨道段 Bookable track segment 人工复核必需	S3
02	低速机器人配送验证 Low-speed robot delivery validation 产业测试验证场景 人工复核必需	S3
03	自主慢行体验评估 Autonomous slow-mobility assessment 产业测试验证场景 人工复核必需	S3
04	模型安全红队沙盘 Model safety red-team sandbox 产业测试验证场景 人工复核必需	S6
05	开源发布厅 Open-source release hall 人工复核必需	S4
06	沿线AI文化导览 AI cultural guide along the line 人工复核必需	S5
07	AI+医疗健康服务导航点 AI+ health service navigation point 人工复核必需	S2
08	企业服务Copilot窗口 Enterprise service copilot counter 人工复核必需	S5
09	数据要素会客厅 Data-element service house 人工复核必需	S1
10	智能原生消费街区 Intelligent-native retail street 人工复核必需	S1
11	公共安全与活动运营复核 Public safety and event operations review 人工复核必需	S2
12	全球AI活动周步行路线起点 Global AI Week route start 人工复核必需	S4

数据治理与人工复核		Data rules & human review
统一数据边界（全部场景适用）		仅使用公开或已授权数据；不做个体画像；不以指定供应商为必要条件；场景为概念建议，未获批准运营。
可预约段运行协议		预订—布设—按公开规则运行限定窗口—归还普通公共使用；具名运营方、明示数据边界、不可自动化取消的人工复核点。
六段可预约段与优先场景		
S1 到发场可预约段		商业与国际交往场景优先，活动期与站点客流协调
S2 下行道岔可预约段		生活服务与低速配送验证优先，居民知情与撤销权前置
S3 区间可预约段		连续路径类验证优先，窗口最长、干扰最低
S4 零公里站可预约段		开源发布与社区活动优先，公共可达性不得让渡
S5 上行道岔可预约段		企业服务与国际交往场景优先
S6 编组场可预约段		评测与标准治理场景优先，公众可观察
治理红线		- 城市智能体可辅助识别慢行断点、公共空间热力、设施维护与活动安全风险，但不替代规划审批，不输出未经授权的个人画像。 - 每个场景须有具名运营方、明示数据边界与不可自动化取消的人工复核点。 - 不以指定供应商、指定模型或指定终端为必要条件；场景为概念建议，未获批准运营。 - 场景数据只做聚合统计；居民、师生与访客画像不得用于商业推荐。

底图为临时粗略边界（provisional），不得作为官方红线或精确面积依据。

本图全部空间提案为概念建议 / 参考方案，可供专业团队深化研究；不构成法定规划、政府批准、实施确认或投资承诺。

14 METRICS

指标体系、面积复算与合规矩阵

Metrics, areas recomputed, compliance

指标复算表			Metrics recomputation (metrics.json)	
指标	置信度	值		
site_area_sqm	high	11.41 km²		
land_use_total_area_sqm	high	11.41 km²		
land_use_area_commercial_services_05_sqm	medium	99.8 ha		
land_use_area_urban_residential_0701_sqm	medium	112.4 ha		
land_use_area_community_facilities_0702_sqm	medium	184.1 ha		
land_use_area_research_0802_sqm	medium	239.5 ha		
land_use_area_culture_0803_sqm	medium	53.6 ha		
land_use_area_education_0804_sqm	medium	51.7 ha		
land_use_area_park_green_1401_sqm	medium	166.8 ha		
land_use_area_protective_green_1402_sqm	medium	78.9 ha		
land_use_area_square_1403_sqm	medium	154.4 ha		
green_space_area_sqm	medium	245.7 ha		
green_ratio	medium	21.53%		
public_space_area_sqm	medium	206.0 ha		
public_space_ratio	medium	18.05%		
building_footprint_area_sqm	low	29.5 ha		
building_footprint_ratio_key_areas	low	7.99%		
key_area_count	high	3		
key_area_total_area_sqm	medium	369.3 ha		
key_area_beijing_ai_origin_community_sqm	medium	104.3 ha		
key_area_dazhongsi_ai_industry_cluster_sqm	medium	72.0 ha		
key_area_zhongzhiyuan_ai_acceleration_area_sqm	medium	192.9 ha		
phasing_area_phase_1_sqm	medium	276.6 ha		
phasing_area_phase_2_sqm	medium	482.0 ha		
phasing_area_phase_3_sqm	medium	382.6 ha		
road_network_length_m	medium	38,211 m		
slow_mobility_length_m	medium	16,730 m		
east_west_stitch_count	medium	6		
transit_connector_count	medium	3		
renewal_building_count	low	13		
ai_scenario_card_count	high	12		
pilgrimage_landmark_count	high	4		
unknown (11) · 待正式控规条件确认				
total_floor_area_sqm			scenario_admission_turnaround_days	
floor_area_ratio			step_free_continuity_breaks	
building_height_m			non_digital_equivalence_ratio	
road_area_sqm			objection_resolution_days	
road_area_ratio			public_space_return_compliance_ratio	
booked_window_utilisation_ratio				
协议复演与治理覆盖 (simulation.json 高统合成)				
simulation_task_count	80		tool_schema_pass_rate	100%
simulation_negative_branch_count	55		audit_completeness	100%
token_protocol_rule_count	10		scenario_data_boundary_count	12
simulation_success_rate	100%		scenario_human_review_count	12

底图为临时粗略边界 (provisional) ，不得作为官方红线或精确面积依据。

本图全部空间提案为概念建议 / 参考方案，可供专业团队深化研究；不构成法定规划、政府批准、实施确认或投资承诺。

容积率、建筑高度、建筑密度、道路红线与道路面积：待正式控规条件确认 (pending) 。

合规矩阵：任务→章节 / 图层 / 指标 / 图纸							compliance_matrix.json	
任务号	任务名称	图层	指标	图纸	来源			
1.3.1	构建世界级AI创新生态体系	2	2	2	2			
1.3.2	建设适配AI新质生产力的新型城市形态	2	2	1	2			
1.3.3	打造全球AI创新人才向往的高品质城区	2	3	1	2			
1.4.1	统筹研究范围	1	1	1	2			
1.4.2	总体设计范围	2	2	2	2			
1.4.3	重点区域范围	1	5	1	2			
1.5.1.1	统筹研究范围：AI创新生态体系	2	2	1	2			
1.5.1.2	统筹研究范围：适配人工智能的未来城市形态	2	2	2	2			
1.5.2.1	总体设计范围：产业目标与功能布局	2	3	1	2			
1.5.2.2	总体设计范围：城市更新总体框架	3	3	2	2			
1.5.2.3	总体设计范围：轨道交通市政配套设施	2	4	1	2			
1.5.2.4	总体设计范围：京张遗址公园活力带	3	4	1	2			
1.5.2.5	总体设计范围：城市风貌	2	2	2	2			
1.5.3.required	重点区域详细设计必选项	4	2	2	2			
1.5.3.1	众智园AI自主创新加速区	3	2	1	2			
1.5.3.2	北京AI原点社区	3	3	1	2			
1.5.3.3	大钟寺AI产业聚集区	3	2	1	2			
agent.1	一带总体概念与功能统筹方案设计	3	2	2	2			
agent.2	AI全栈自主创新体系与世界级AI创新生态设计	3	2	1	2			
agent.3	AI+场景赋能新范式与智能化AI活力城市设计	3	3	2	2			
agent.4	AI公共空间、智能原生新业态与朝圣地标设计	3	4	1	2			
agent.5	百年京张文化、中关村文化与AI新文化融合叙事设计	2	2	1	2			
agent.6	一带全球AI创新活动体系与长期运营设计	3	4	1	2			
口径说明								
第一类：可由提交几何直接复算的空间指标（边界面积、绿地率、公共空间比例、建筑基底面积、分期面积），全部已复算并写入 metrics.json。								
第二类：需官方控规或任务书附件支撑的管控指标（容积率、建筑高度、建筑密度、退线、道路红线与设施标准），一律登记为 unknown 并给出原因。								
第三类：需运营或产业数据持续校准的绩效指标（创新指数、人才密度、慢行可达性、活动参与度、场景使用频次），进入 assumptions 与后续观测，不写入本次结论。								
所有 known 指标均可由 geometry/*.geojson 在 EPSG:4548 下重算；官方 polygon 发布后须整体重算，不能只替换单个文件。								
面积一致性校核								
用地图层合计 - 提交边界面积							12.0 sqm (0.0001%)	
重点区复算 - 公告面积							+8,893.0 sqm (+0.24%)	
提交边界复算 - 公告面积							+12,825 sqm	

15 RISK

风险、版权与缺资料清单

Risk, copyright, missing data

缺资料清单	Missing data
floor_area_ratio 需自：approved regulatory planning conditions or official design brief attachments 正式提交必需：是 building_height_m 需自：approved height controls, aviation/landscape/heritage constraints if applicable 正式提交必需：是 building_density 需自：approved regulatory planning conditions 正式提交必需：是 green_ratio (控规口径) 需自：approved regulatory planning conditions or local green-space standards 正式提交必需：是 setback_m 需自：road redline, building control line, fire and municipal constraints 正式提交必需：是	missing missing missing missing missing
边界与范围缺口	
统筹研究范围	exact_polygon_missing_provisional_available
总体设计范围	exact_polygon_missing_provisional_available
重点区域范围	exact_polygon_missing_provisional_available
官方 SITE_BOUNDARY 与三处 KEY_AREA polygon 未发布；本包使用仓库临时粗略边界生成，替换官方 polygon 后，site boundary、key areas、land use、roads、green space、public space、buildings、phasing 与 metrics 均需重算。	

实施与运营风险	Delivery & ops risk
边界风险 临时粗略边界与官方红线不一致，将导致全部面积、比例与承载判断变化。 控规风险 容积率、高度、密度与退线未定，建筑规模与形态结论不可提前锁定。 工程风险 跨廊道连通的净空、结构与消防疏散条件未核，缝合线可行性待复核。 权属风险 权属与实施主体不明，更新项目清单不构成实施安排。 市政风险 管线、能源、排水与算力承载缺资料，新型基础设施只能作为原型。 运营风险 可预约段与活动体系需许可、安全与保险安排，运营主体未定。 数据风险 场景数据来源、授权与最小化边界需在正式实施前独立审查。 版权风险 品牌、字体、图像、肖像与企业标识须清权后方可使用。	等级 高 等级 高 等级 中 等级 高 等级 中 等级 中 等级 中
假设登记 assumptions.json (共 11 条)	
A-CONTROLS-001 · pending_professional_confirmation Detailed regulatory controls, road redlines, ownership, municipal utilities, and engineering constraints must be confirmed from official attachments before statutory use. A-BOUNDARY-001 · pending_official_data The submitted site boundary and the three key-area polygons are the repository's provisional rough boundaries, not an official redline. All areas, ratios and the land-use partition must be recomputed together once official polygons are published. A-CONSTRAINT-LAYERS-001 · intentionally_unauthored Water system, heritage protection, regulatory control and existing road/rail layers are marked editable_by_agent=false in the site package enum. This package leaves them unauthored rather than inventing them; geometry/constraints.geojson carries only agent-definable bookable track segments and located scenario nodes. A-INTENSITY-001 · pending_official_data Floor area ratio, total floor area, building height and building density are recorded as unknown because planning_limits.json records them as missing official controls. Only a relative massing intent is stated. A-ROAD-AREA-001 · pending_official_data Road area and road area ratio cannot be recomputed from centrelines because approved redline widths and cross-sections are not published. Whether each east-west stitch crosses at grade, over or under is an engineering question this package does not answer. A-EXISTING-BUILDINGS-001 · pending_official_data No current-building survey, ownership record or official parcel geometry exists in the public package. The thirteen building footprints are indicative renewal handles whose suggested retain/renovate/new-build action derives from the structural role of their band, not from any judgement about a real existing building. No demolition conclusion is issued for any real parcel. A-PARTITION-RESIDUAL-001 · accepted_tolerance The land-use partition is generated by slicing the submitted boundary, so its area equals the site area by construction. A residual of about 12 sqm (1.1e-6 relative) remains between land_use_total_area_sqm and site_area_sqm as a floating-point artefact of reprojection to EPSG:4548. It is not a topological gap; measured gap and overlap are 1.8e-16 and 0 square degrees respectively. 其余 4 条见 assumptions.json (本页不截断内容，仅限于版面)	

版权、合规与不声称事项	Copyright, compliance, no-claims
本方案不声称 ■ 不声称获得官方批准、审定控规或法定规划地位。 ■ 不声称最终土地权属、最终建设规模或保证实施。 ■ 不声称任何政府活动安排、投资承诺或运营授权。 ■ 不把 provisional 边界表述为 official redline 或精确面积依据。 ■ 不把 agent 推测值冒充审定指标或工程结论。	
资产与许可 ■ 本套 A3 / A0 图纸由脚本以矢量方式生成，未使用外部图片、截图、地图瓦片或第三方素材。 ■ 字体为系统随附字体，按子集嵌入 PDF；不加载远程字体、脚本或 API。 ■ 全部空间数据来自提交包 geometry/*.geojson，指标来自 metrics.json，范围面积来自公告与 site-package 登记值。 ■ 许可与来源说明见 sources.json 与 report/copyright_statement.md。	
自检结论 DETERMINISTIC_VALIDATION · pass · blocking deterministic_validation: PASS SPATIAL_REVIEW · pass · blocking spatial_review: PASS VISUAL_PACKAGING · pass · blocking visual_review: PASS PROFESSIONAL_EVIDENCE · pass · blocking professional_review: PASS	
AI agent 对事实、来源、版权、空间数据、指标与表达负责；维护者与专业评审可依据自检结果、空间复核与合规矩阵要求返修或拒绝。	

底图为临时粗略边界 (provisional)，不得作为官方红线或精确面积依据。

本图全部空间提案为概念建议 / 参考方案，可供专业团队深化研究；不构成法定规划、政府批准、实施确认或投资承诺。

容积率、建筑高度、建筑密度、道路红线与道路面积：待正式控规条件确认 (pending)。