


总体概念与空间结构 · 京张红榜 JINGZHANG RED LIST

图 · 1

总体概念图 · 一脊双廊三核三站

区位与三层范围：总体设计范围（临时约束） / 三处重点区（临时约束） / 站点一体化影响圈

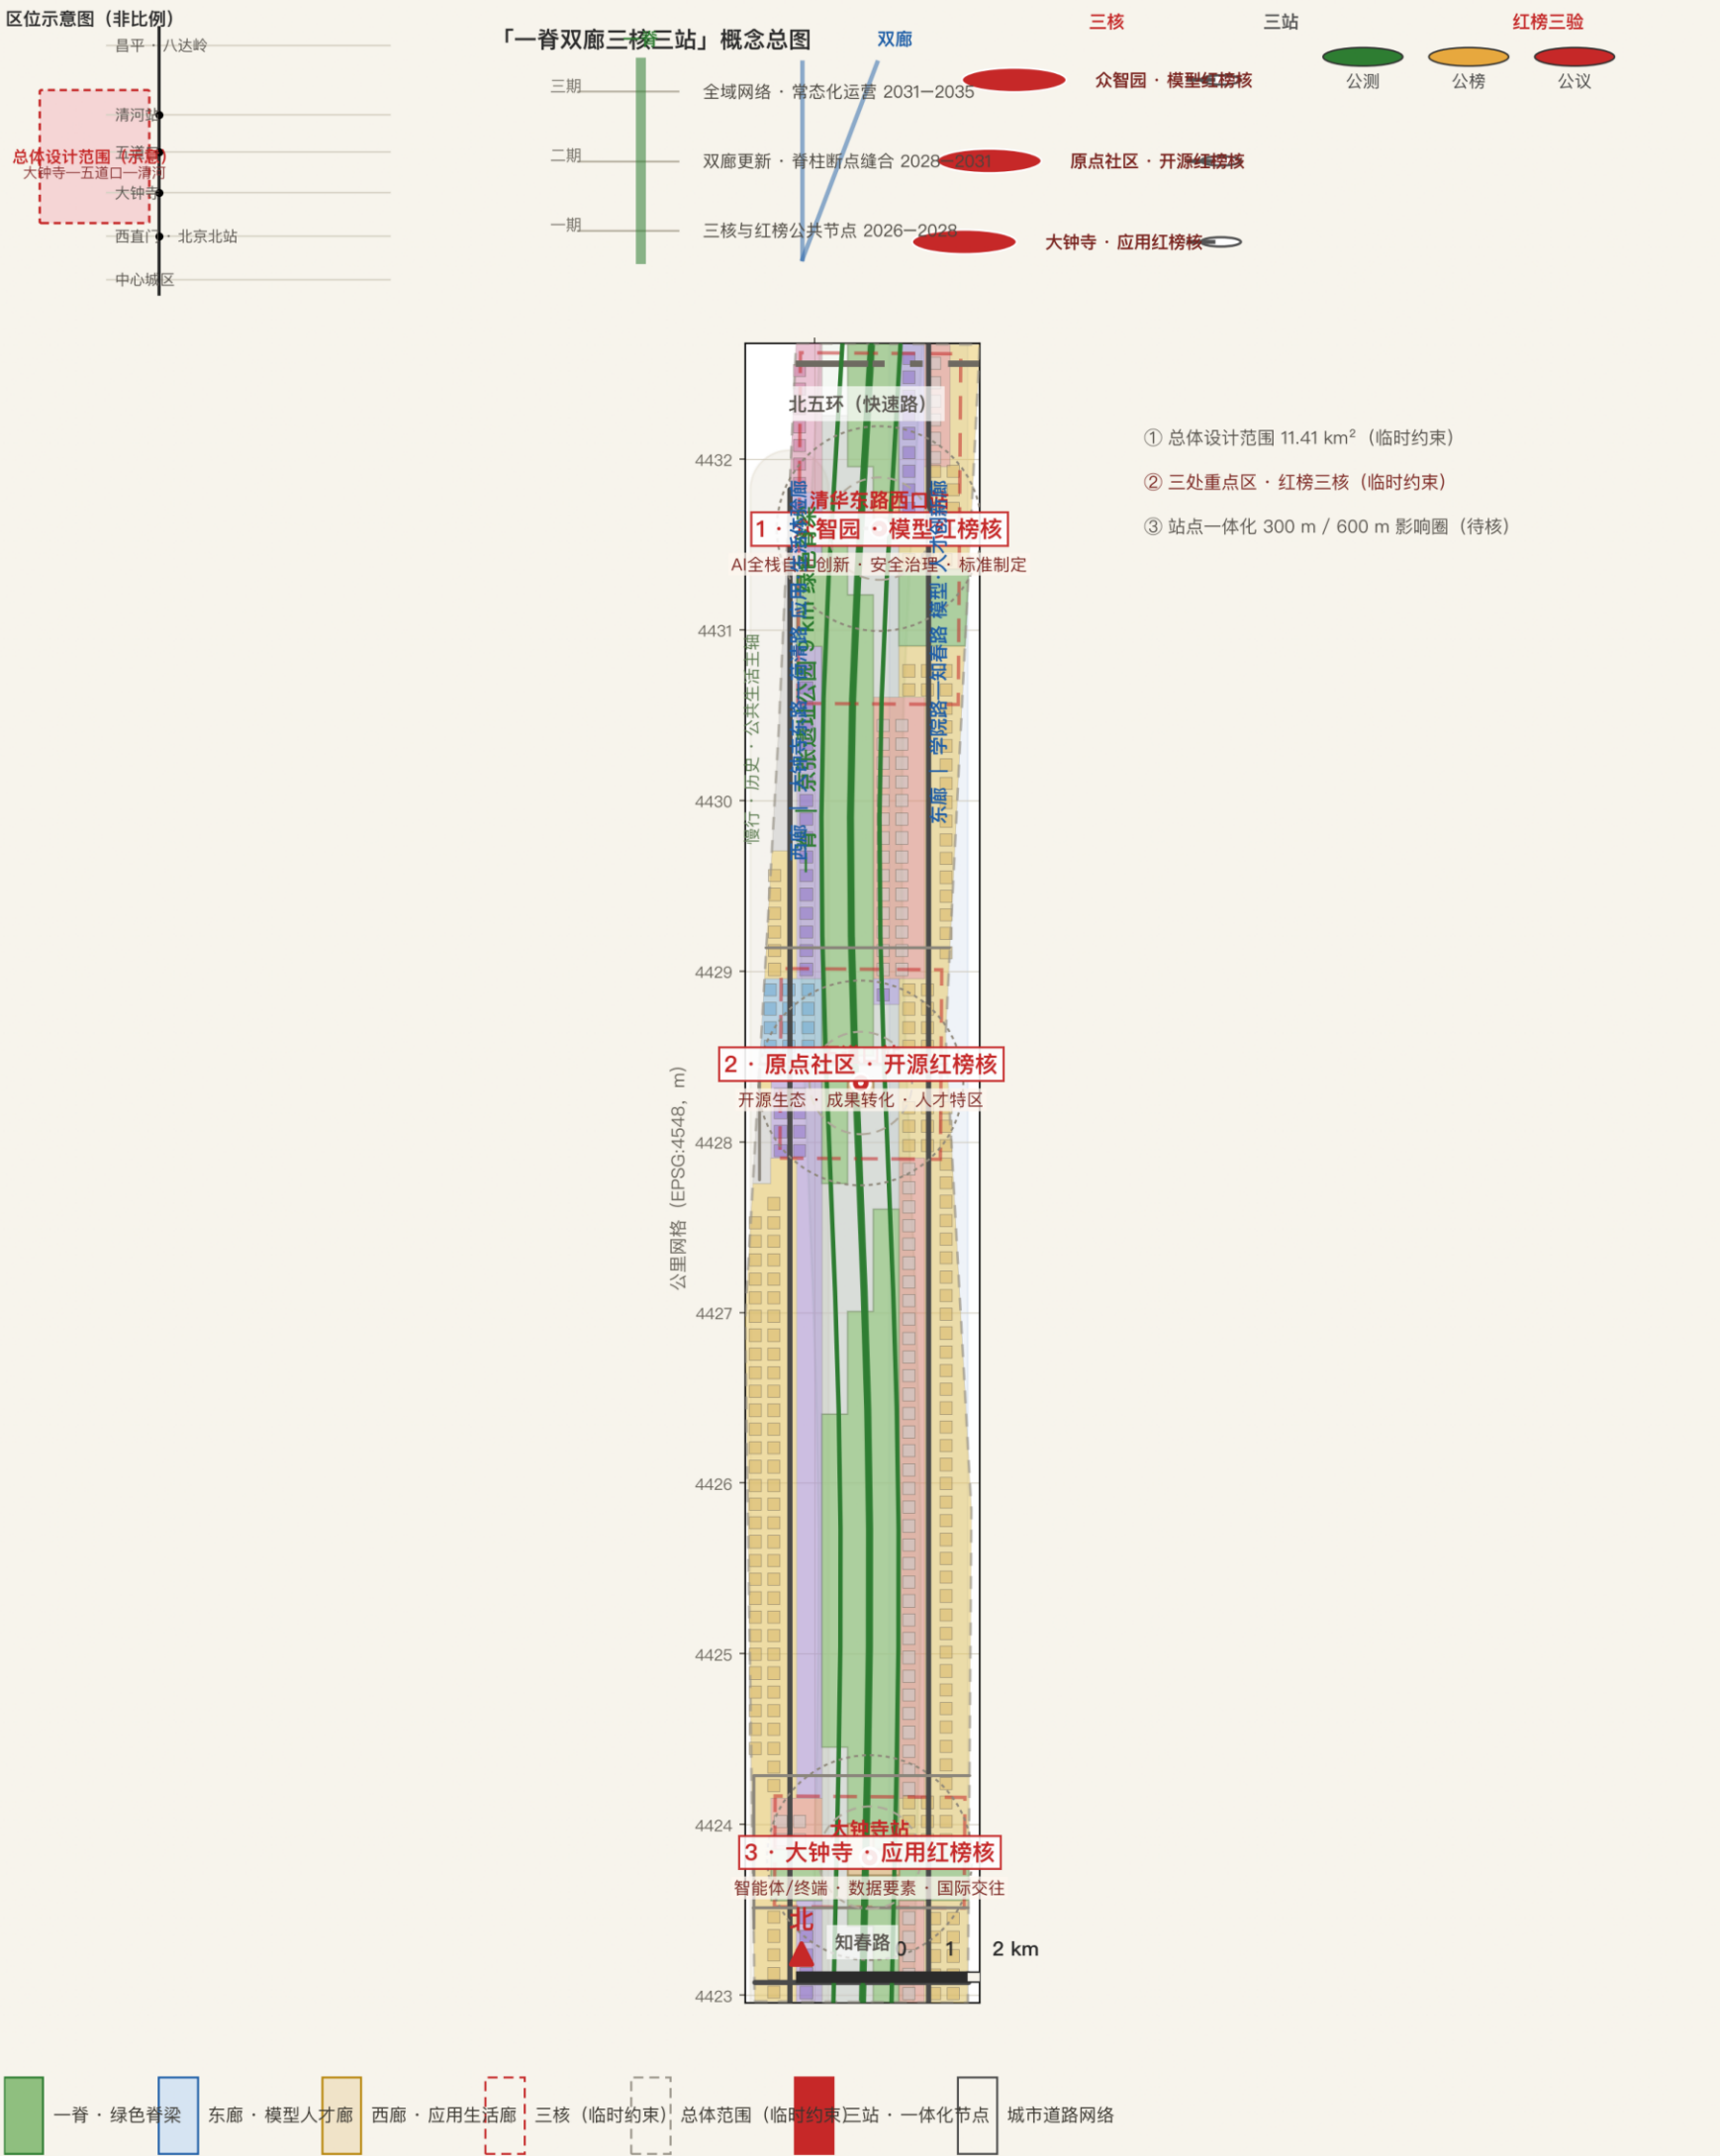


临时约束范围，仅供设计讨论 | 坐标系：CGCS2000 高斯投影 EPSG:4548（局部公里网格） | 仅表达设计意图，不构成法定规划图则
数据来源：京张红榜几何数据包 v0.1 (site_boundary / constraints / land_use / roads / green_space / public_space / buildings / phasing / metrics.json)

图 · 2

用地结构图 · MNR 分类与红榜三核耦合

总体设计范围 11.41 km² | 9 类用地分区（临时约束范围） | 红榜三核标注

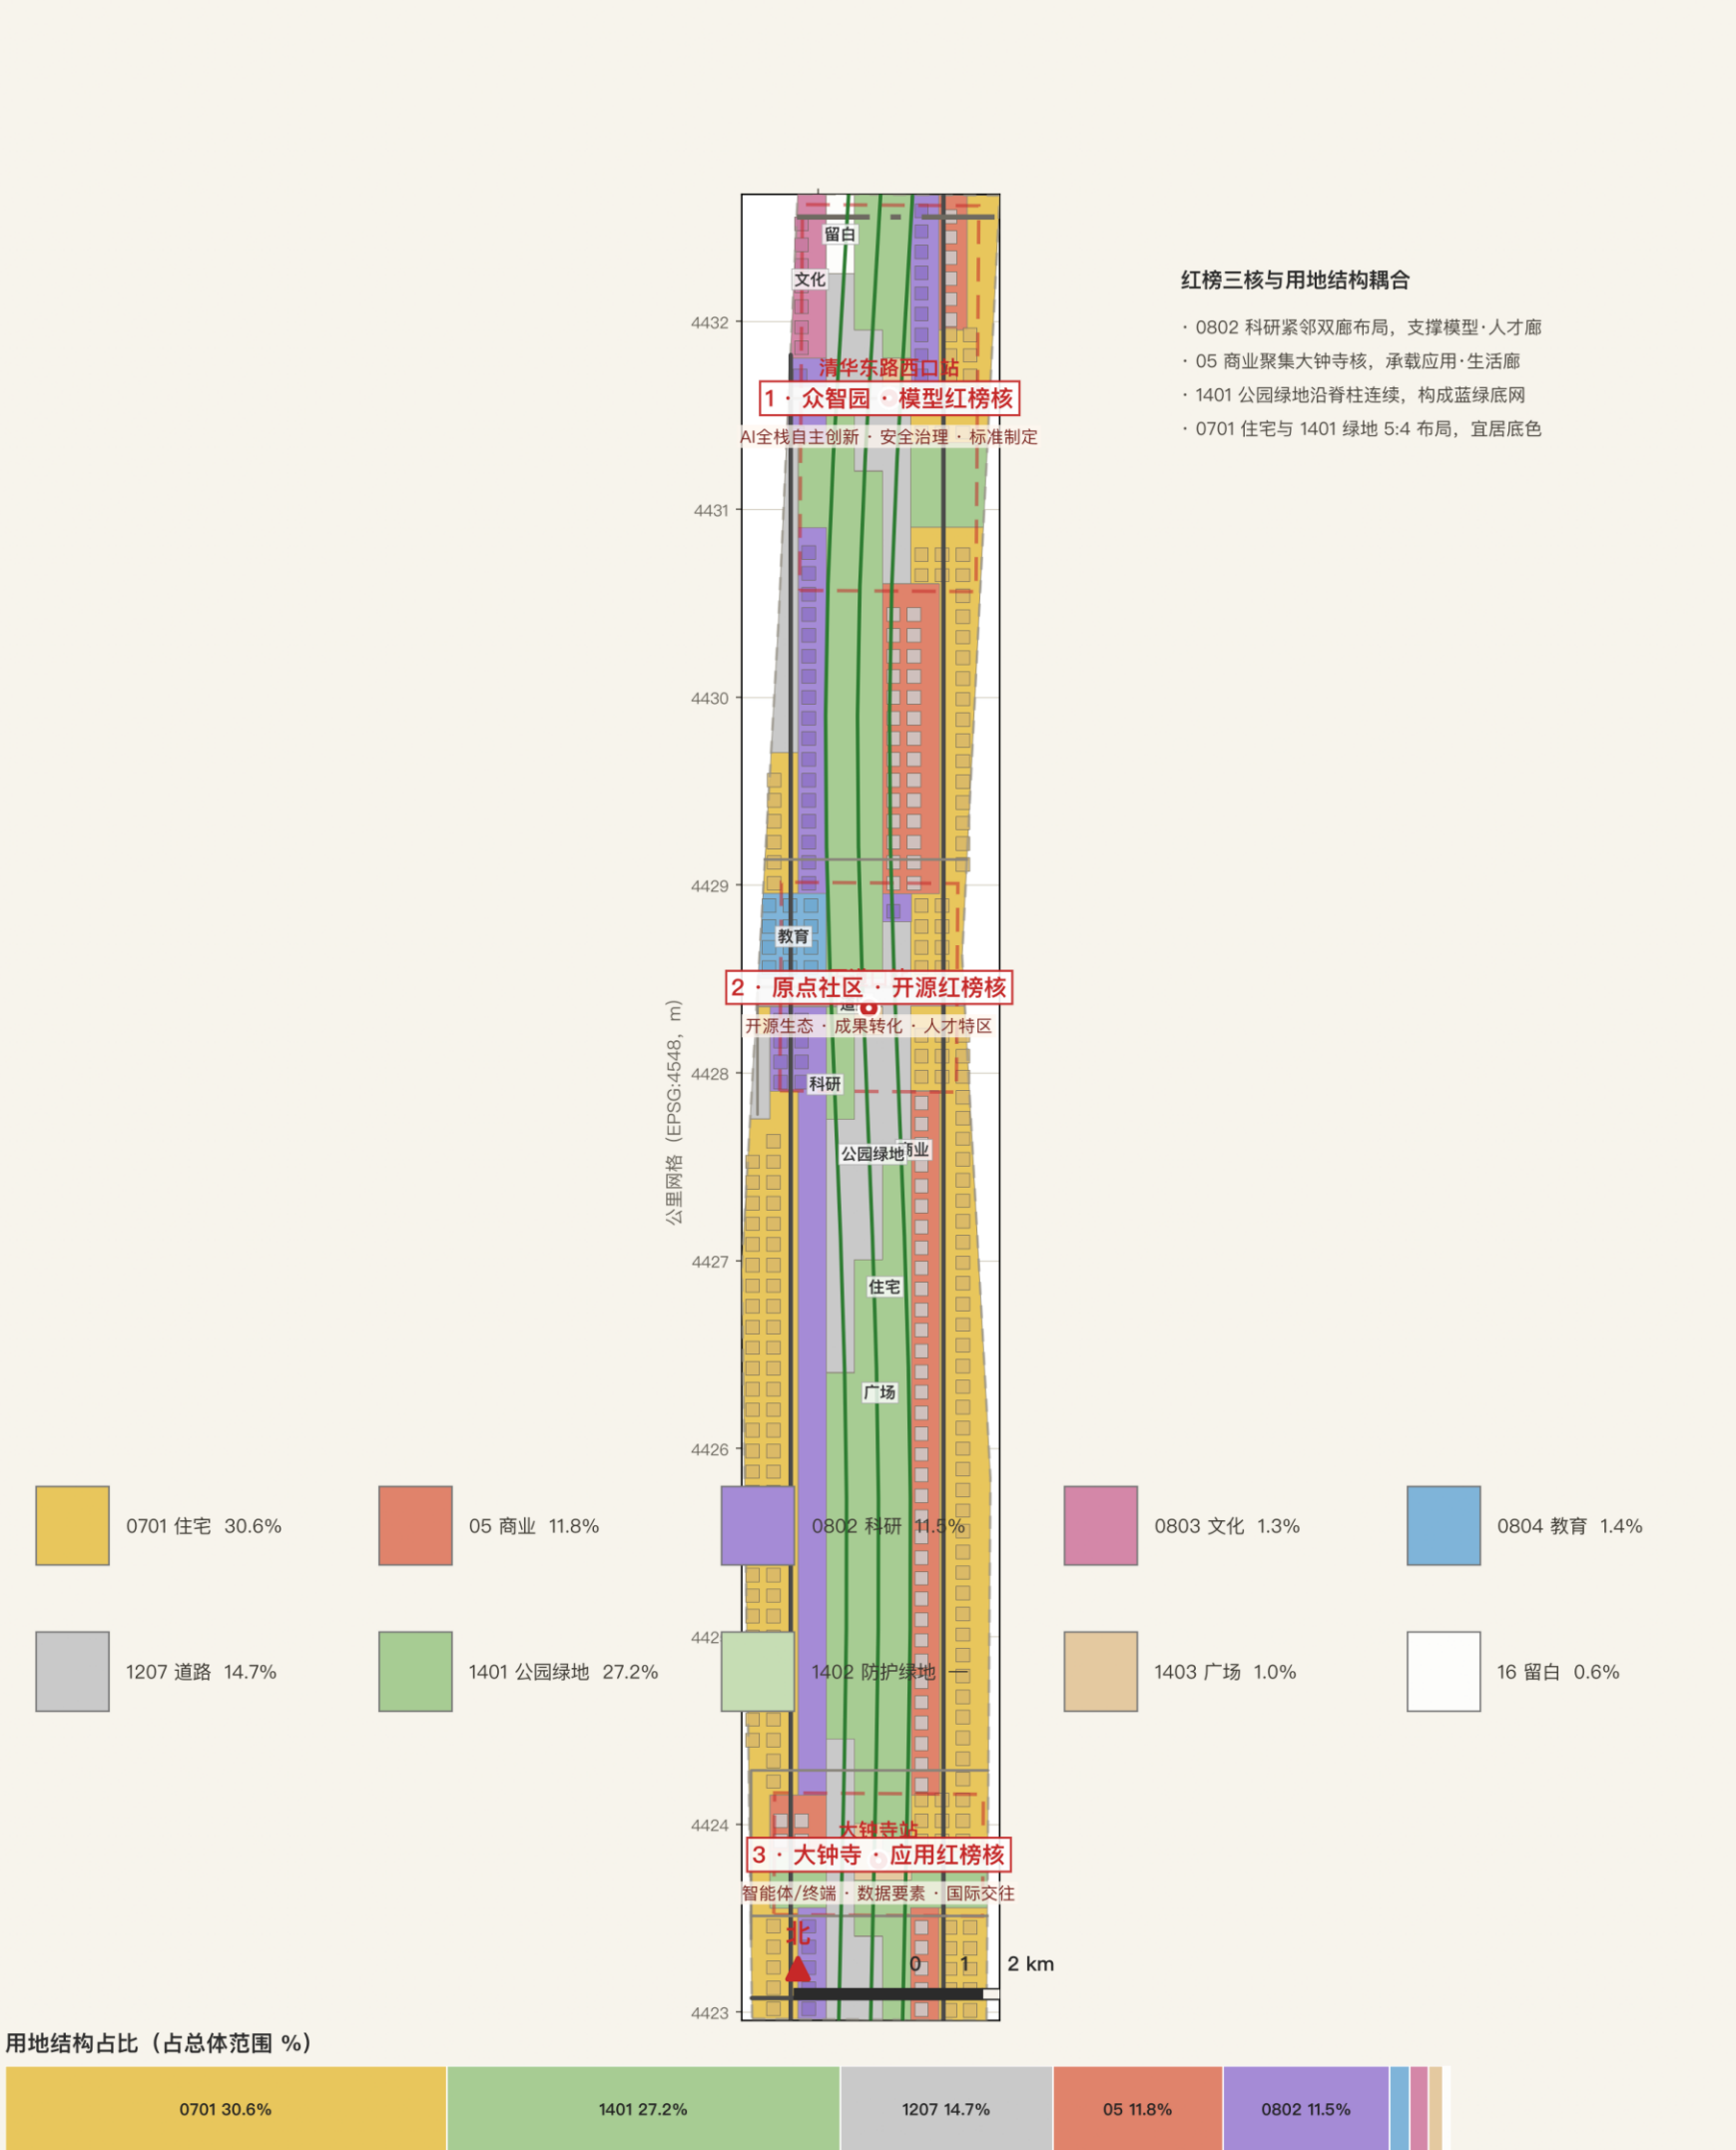

临时约束范围，仅供设计讨论 | 坐标系：CGCS2000 高斯投影 EPSG:4548（局部公里网格） | 1402 防护绿地为规划预留类别，本卷数据并入 1401
数据来源：京张红榜几何数据包 v0.1 (site_boundary / constraints / land_use / roads / green_space / public_space / buildings / phasing / metrics.json)

三核详细设计与实施路径 · 京张红榜 JINGZHANG RED LIST


图 · 3

京张红榜 · JINGZHANG RED LIST (JZ-RL)

红榜三验 · 公测 / 公榜 / 公议

三处重点区域详细设计 · 红榜三核

临时约束范围示意 | 分区概念与更新项目清单 (JZ-01 ~ JZ-10) 对应标注

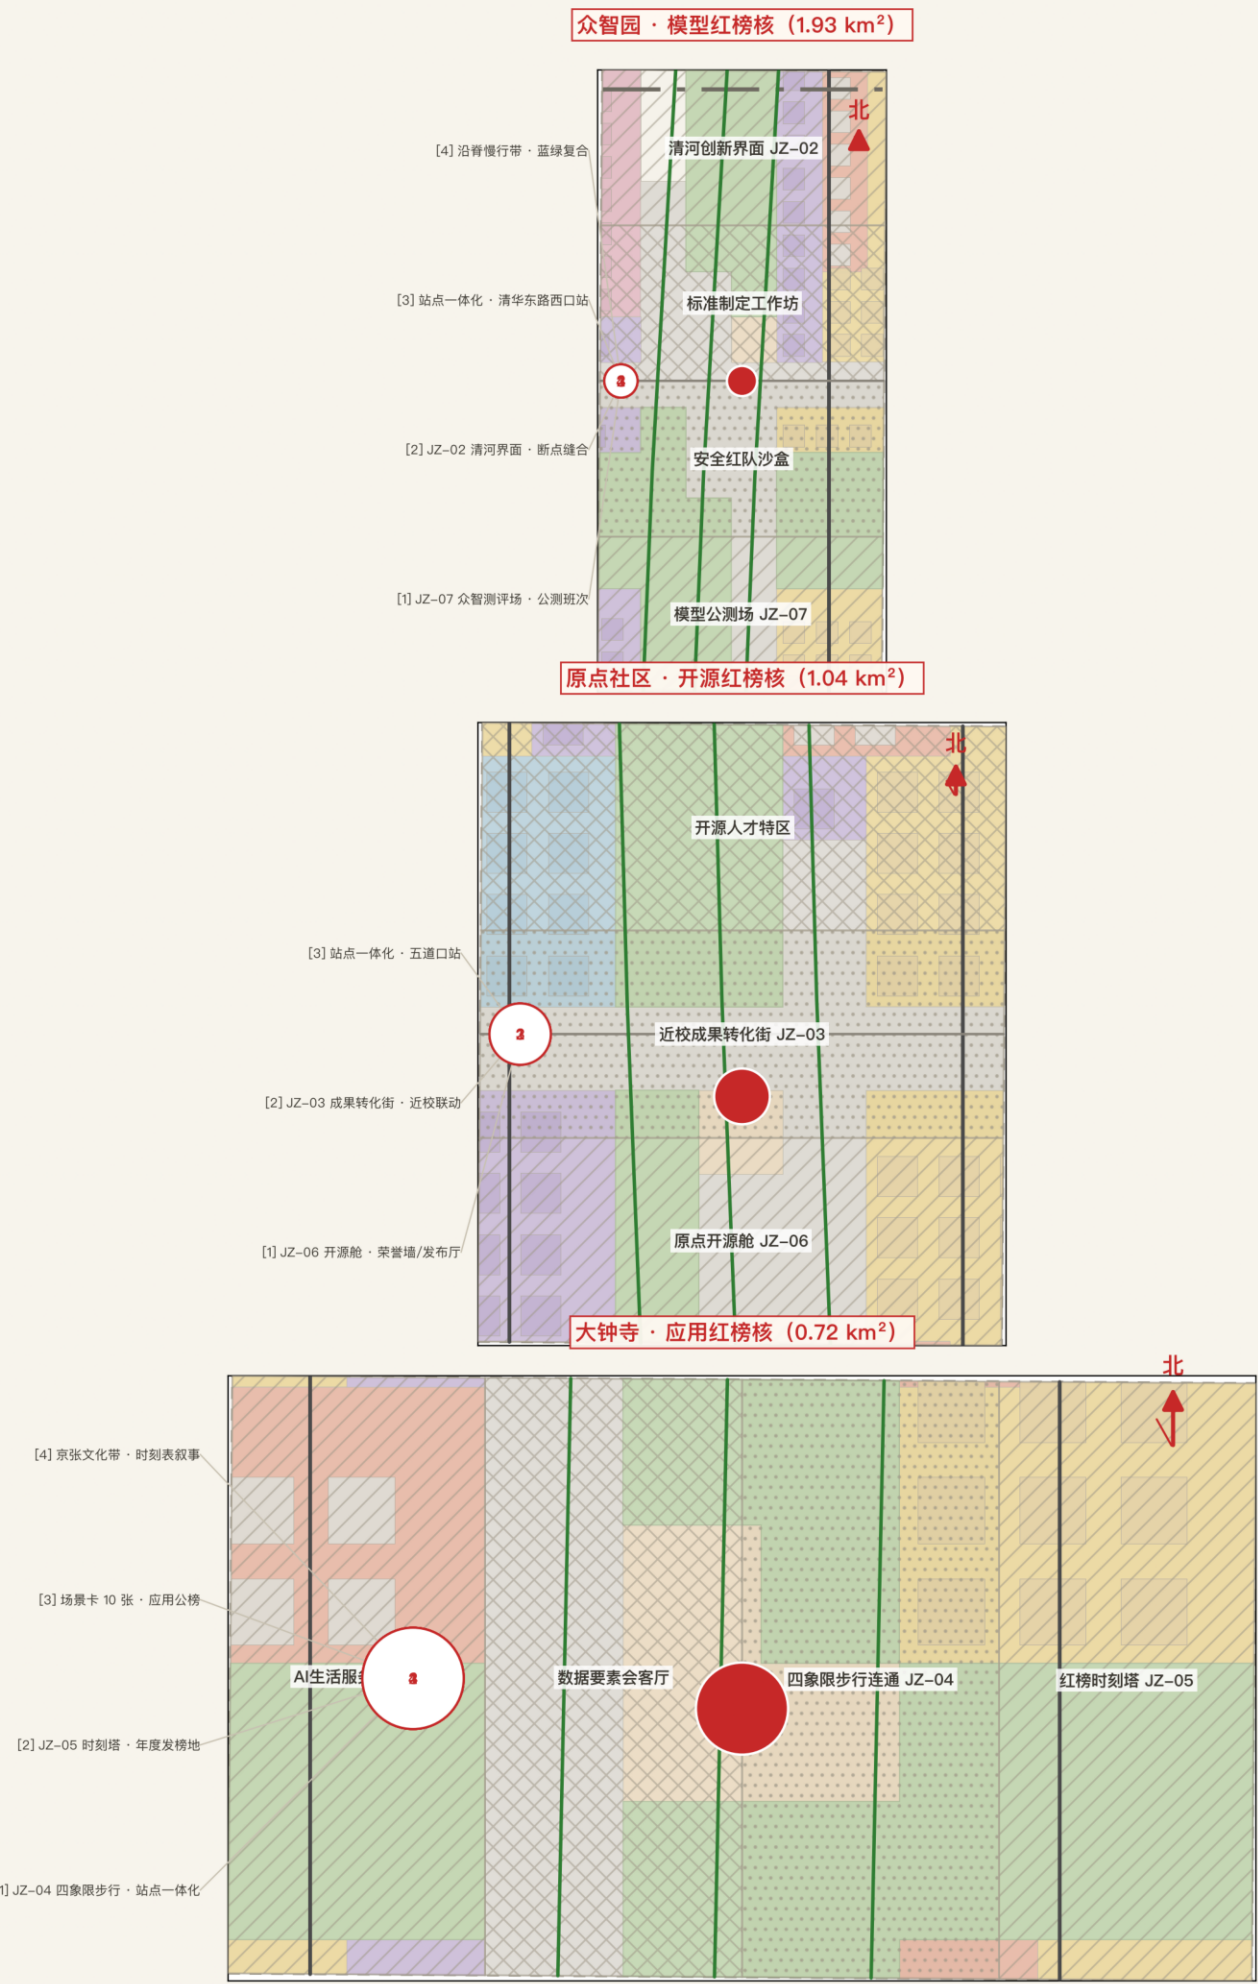

分区填充为概念示意 (由临时范围派生), 更新项目编号对应 JZ 清单
临时约束范围, 仅供设计讨论 | 坐标系: CGCS2000 高斯投影 EPSG:4548 (局部公里网格) | 重点区域范围与分期为概念建议
数据来源: 京张红榜几何数据包 v0.1 (site_boundary / constraints / land_use / roads / green_space / public_space / buildings / phasing / metrics.json)


图 · 4

京张红榜 · JINGZHANG RED LIST (JZ-RL)

红榜三验 · 公测 / 公榜 / 公议

交通慢行与蓝绿公共空间复合系统

道路分级 | 绿道脊线 | 公园绿地与广场 | 站点 300 m / 600 m 步行圈 | 红榜节点

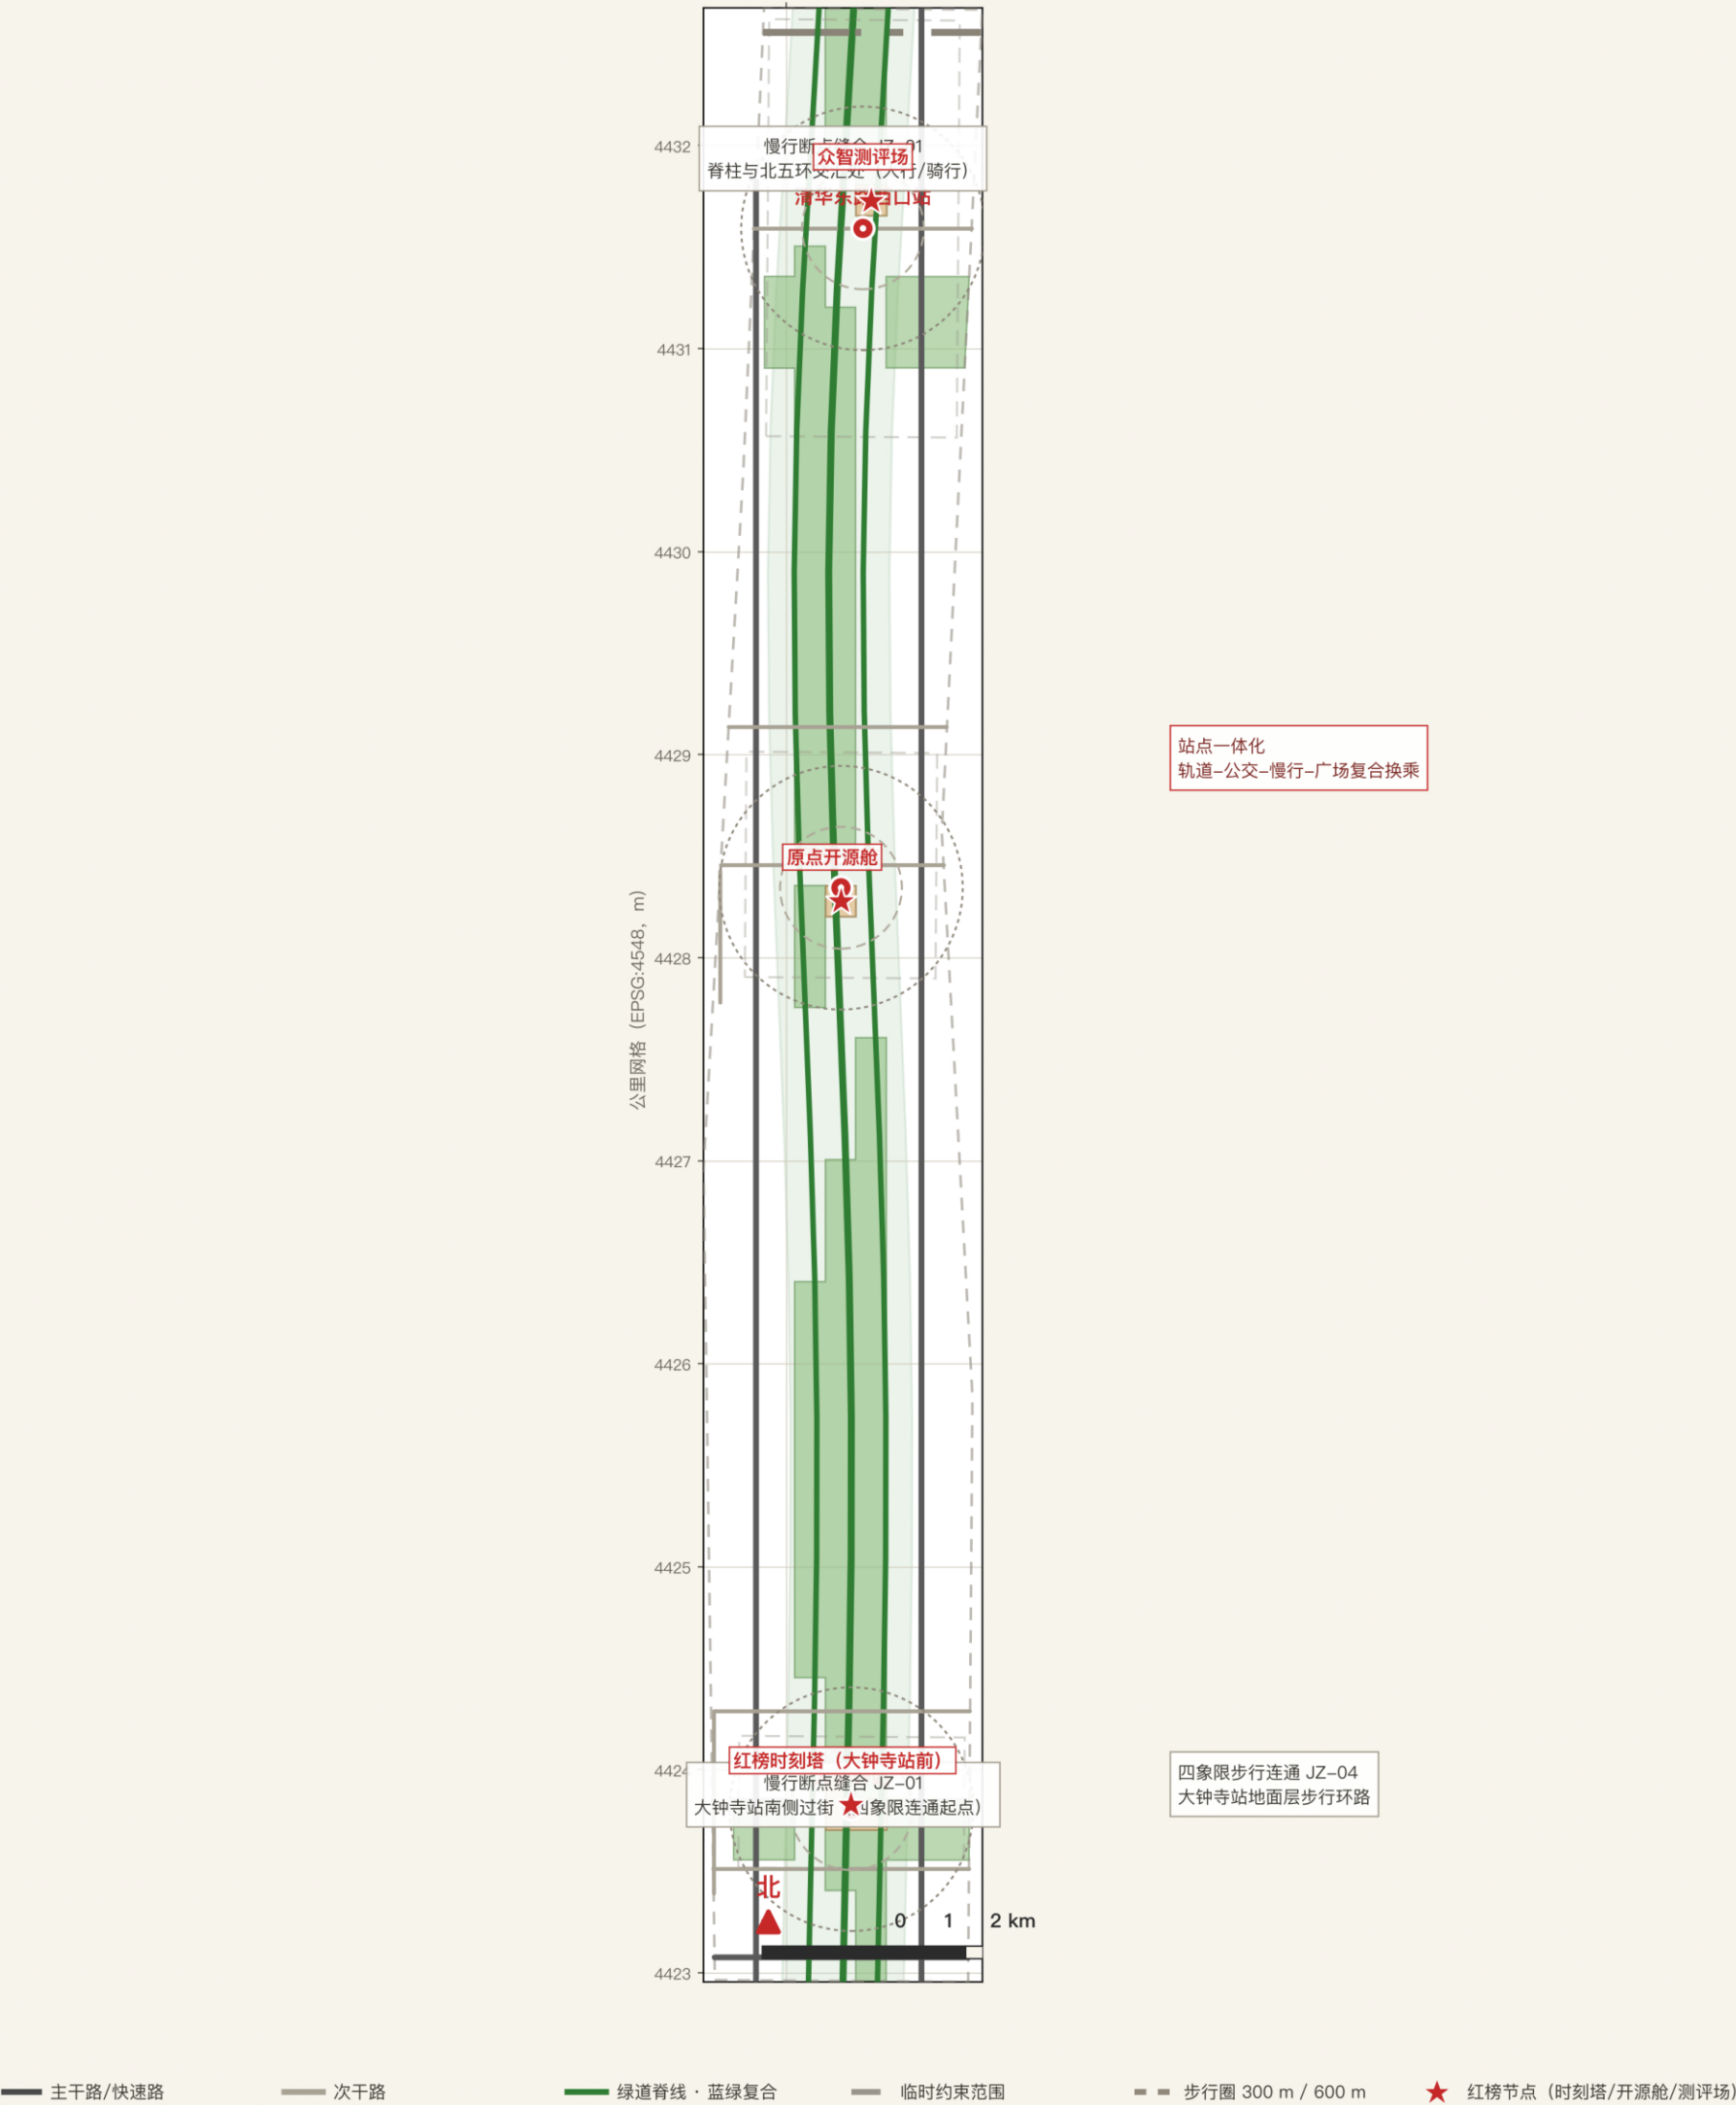

临时约束范围, 仅供设计讨论 | 坐标系: CGCS2000 高斯投影 EPSG:4548 (局部公里网格) | 道路宽度与红线为设计建议值
数据来源: 京张红榜几何数据包 v0.1 (site_boundary / constraints / land_use / roads / green_space / public_space / buildings / phasing / metrics.json)