

JINGZHANG RED LIST

Urban Design Proposal for the Centennial Jing-Zhang AI Innovation Belt · Open-Evaluation Corridor



通过 Pass



复测 Retest




回滚 Rollback

一脊双廊三核三站 · 红榜三验（公测—公榜—公议）

One spine · two corridors · three cores · three stations · Red-List three verification

Overall design area and evidence chain

Provisional constraint, design discussion only; not a statutory plan or implementation commitment

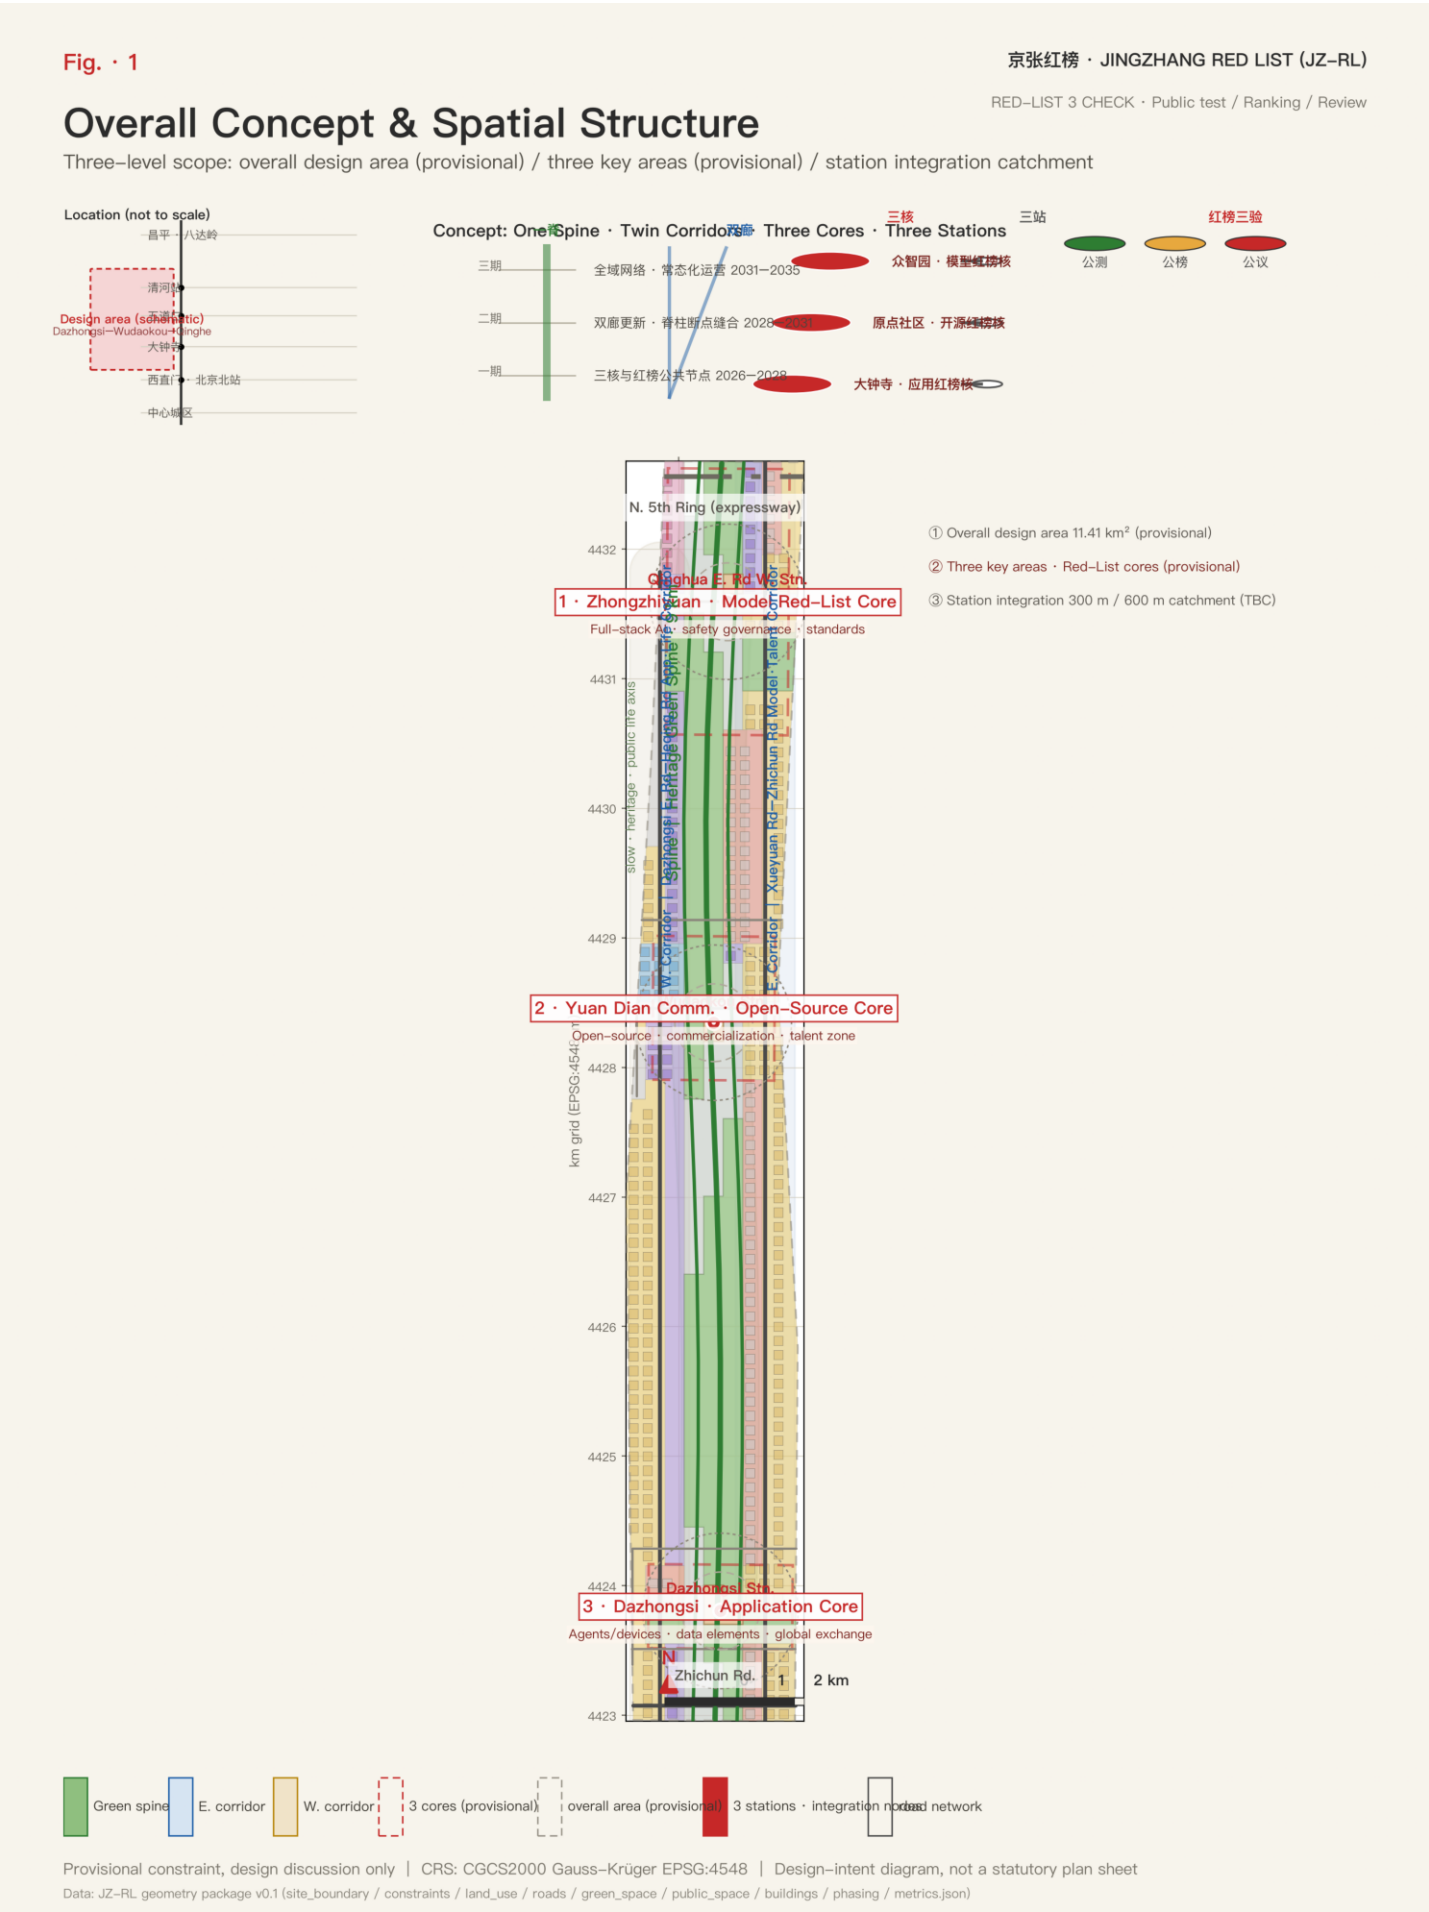

Three-level scope and land-use structure

Provisional constraint, design discussion only; not a statutory plan or implementation commitment


Fig. · 2

京张红榜 · JINGZHANG RED LIST (JZ-RL)

RED-LIST 3 CHECK · Public test / Ranking / Review

Land-Use Structure · MNR Codes vs Cores


Overall design area 11.41 km² | 9 land-use categories (provisional) | red-list core callouts

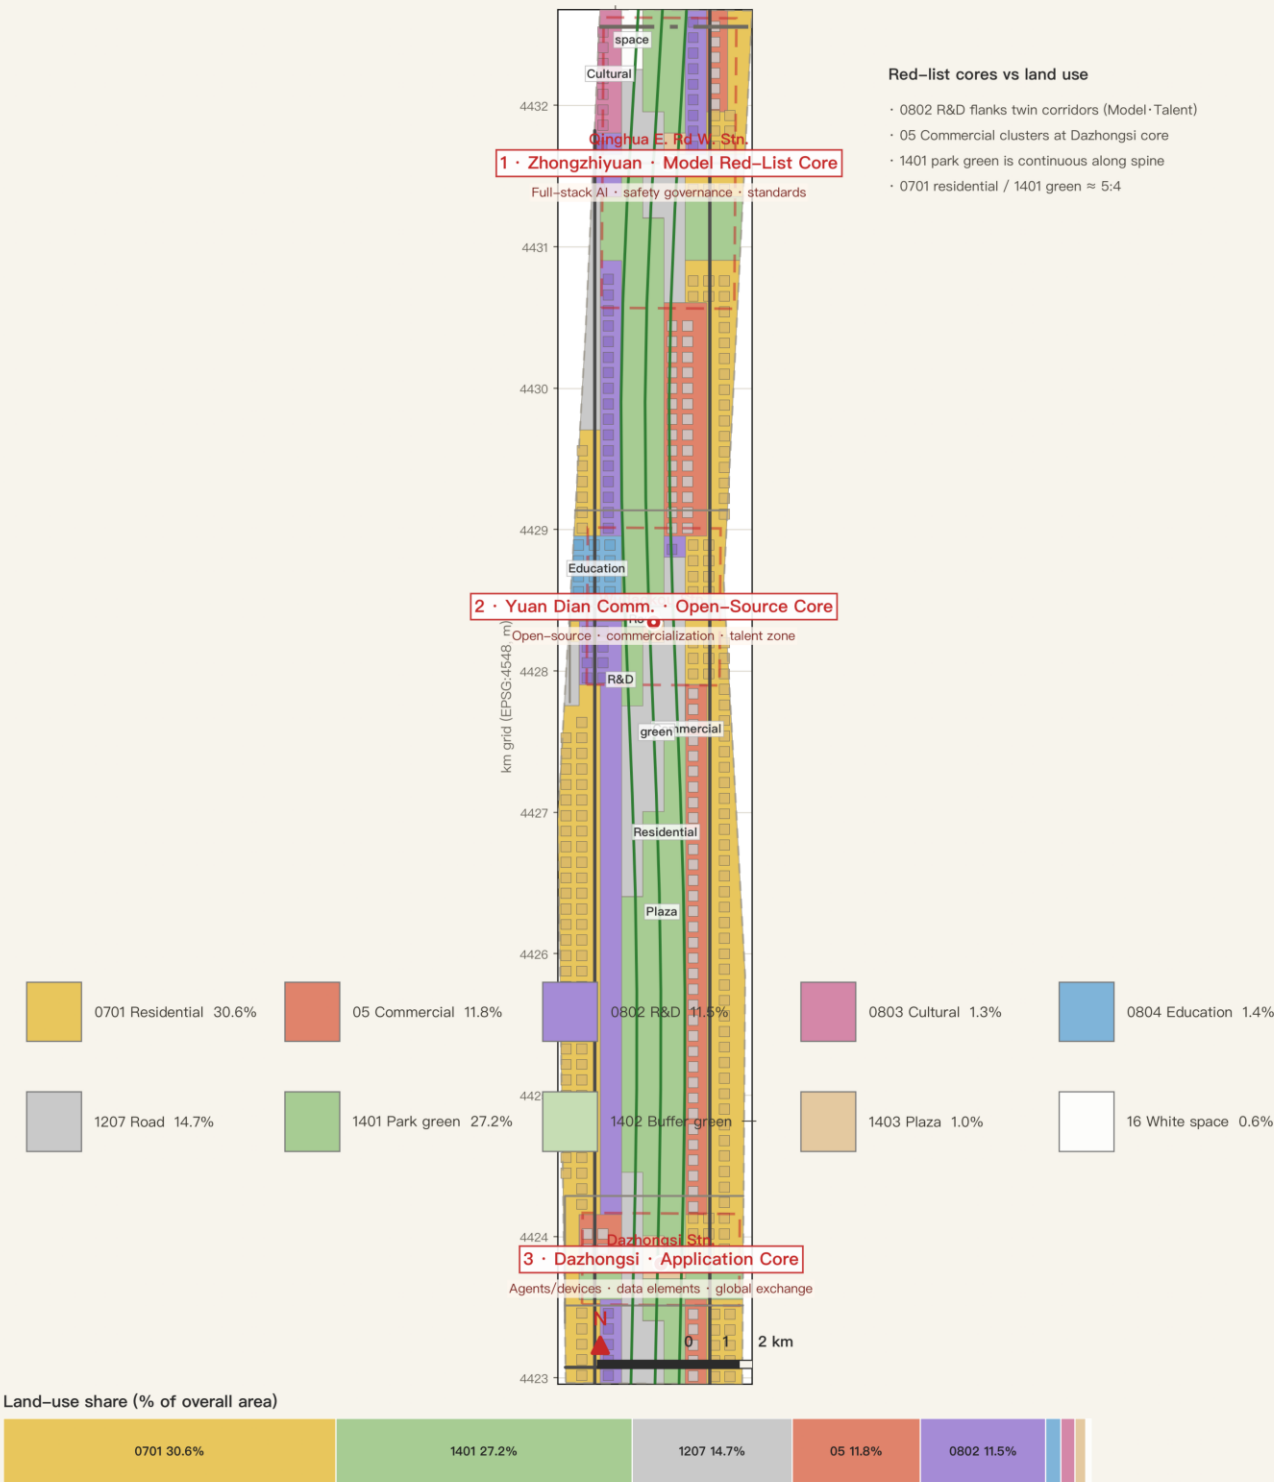

Provisional constraint, design discussion only | CRS: CGCS2000 Gauss-Krüger EPSG:4548 | 1402 buffer green reserved in the MNR scheme; merged into 1401
Data: JZ-RL geometry package v0.1 (site_boundary / constraints / land_use / roads / green_space / public_space / buildings / phasing / metrics.json)

Three key areas: detailed design

Provisional constraint, design discussion only; not a statutory plan or implementation commitment

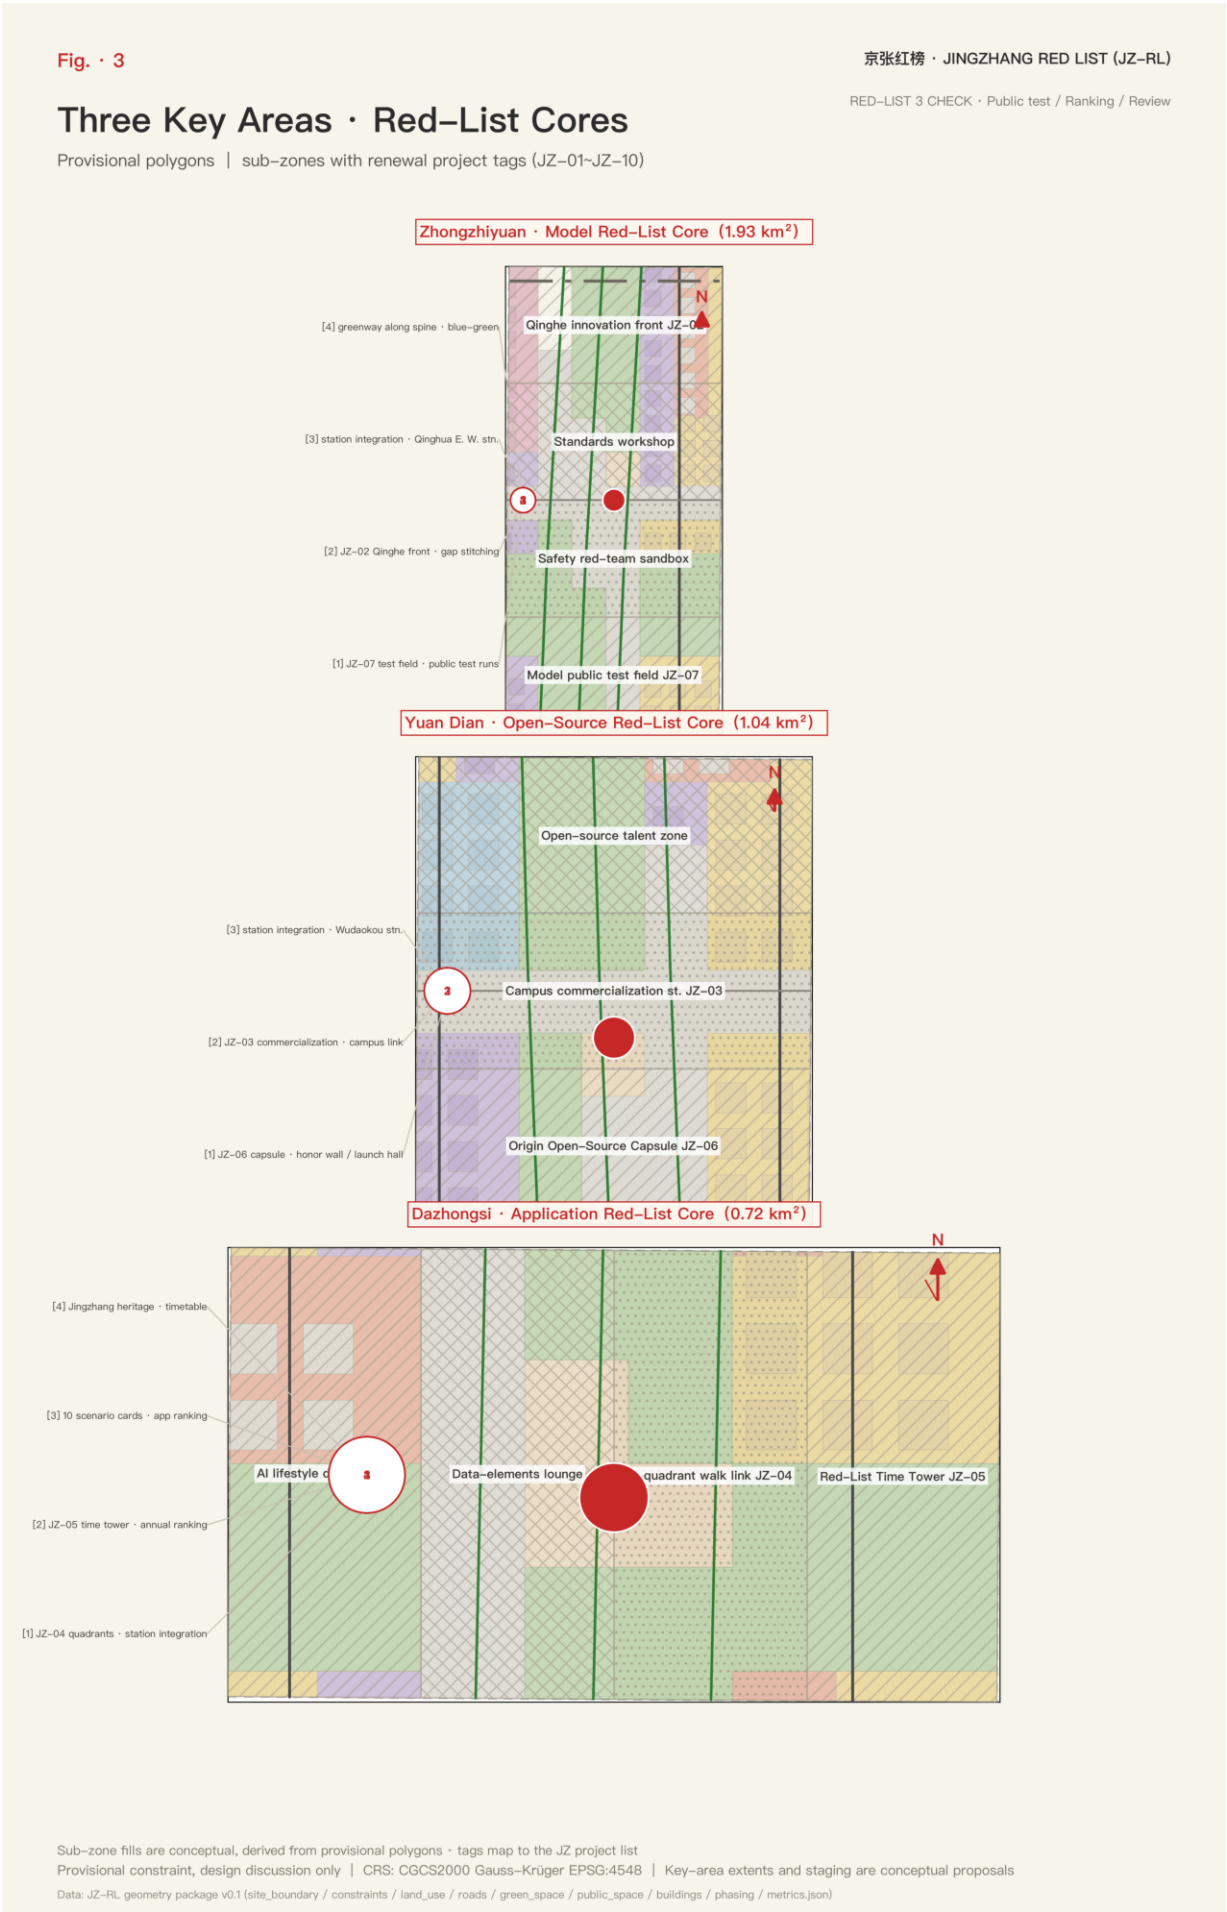

Slow mobility and blue-green public space

Provisional constraint, design discussion only; not a statutory plan or implementation commitment


Fig. · 4

Mobility · Slow Traffic & Blue-Green Spaces

Road hierarchy | greenway spine | parks & plazas | 300/600 m walk rings | red-list nodes

京张红榜 · JINGZHANG RED LIST (JZ-RL)

RED-LIST 3 CHECK · Public test / Ranking / Review

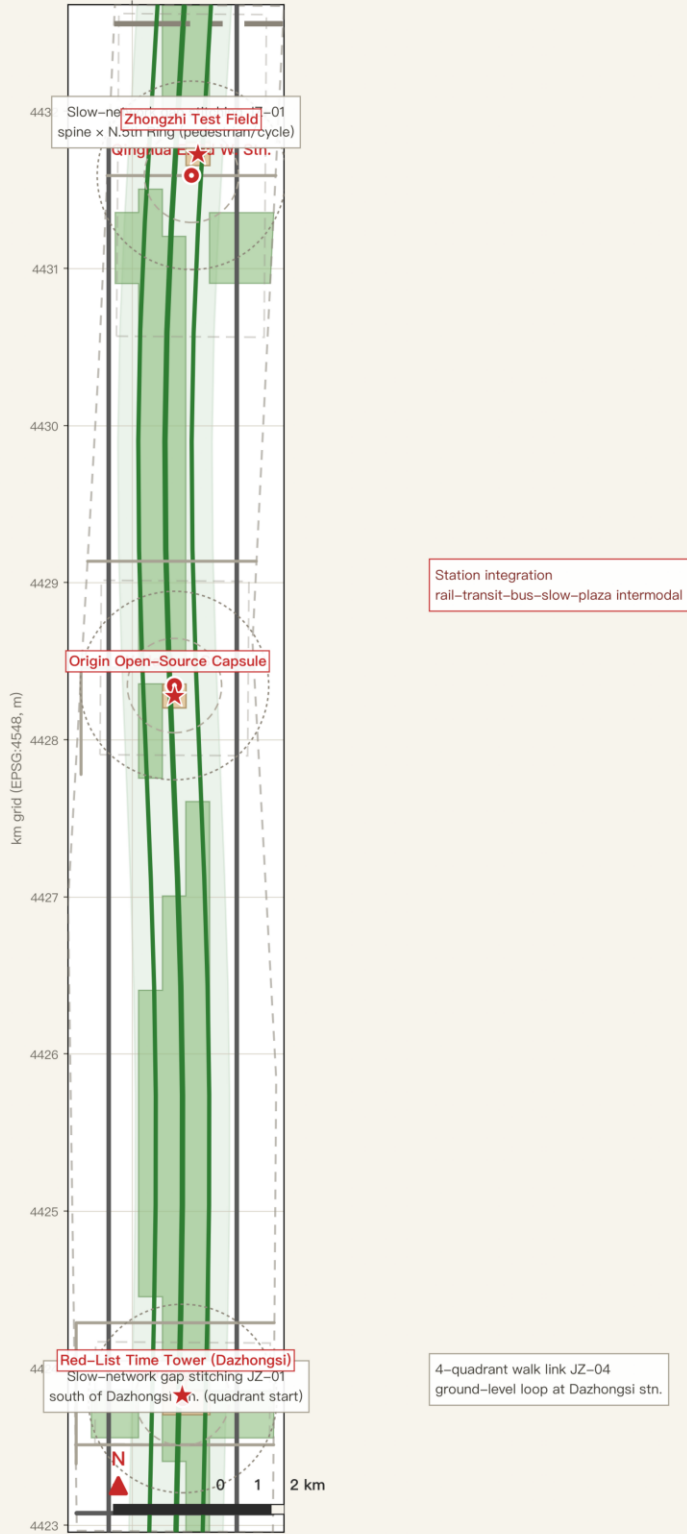

arterial/expressway collector greenway spine · blue-green provisional boundary walk ring 300/600 m red-list nodes (3 sites)

Provisional constraint, design discussion only | CRS: CGCS2000 Gauss-Krüger EPSG:4548 | Road widths are design suggestions, not statutory redlines
Data: JZ-RL geometry package v0.1 (site_boundary / constraints / land_use / roads / green_space / public_space / buildings / phasing / metrics.json)


Core metric recalculation and evidence chain

Provisional constraint, design discussion only; not a statutory plan or implementation commitment

Fig. · 5

Key Metrics Recalculation & Evidence Chain

All values recalculated from geometry/*_geojson in EPSG:4548 (metrics.json)

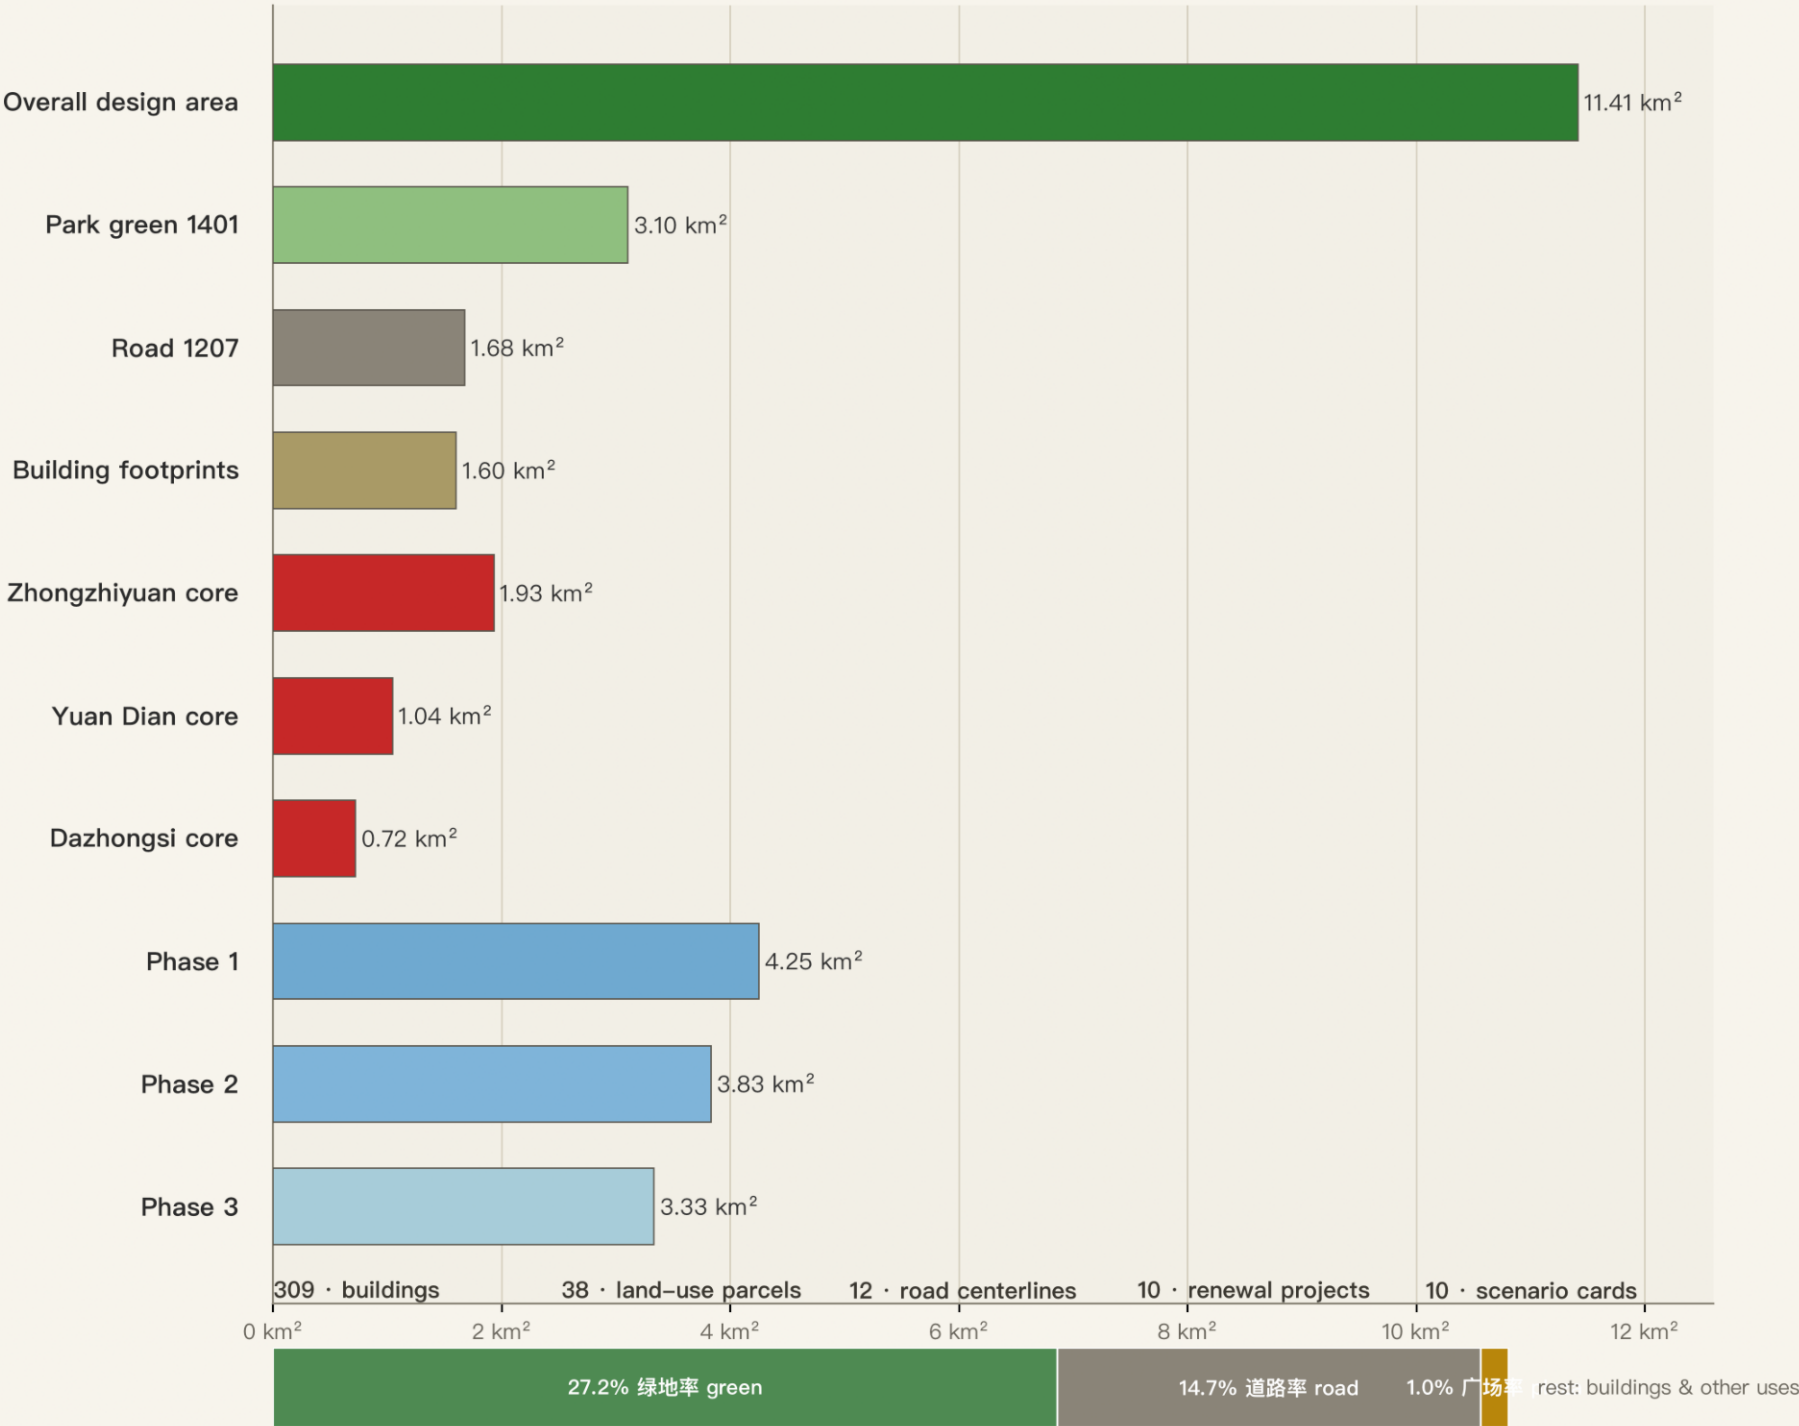

京张红榜 · JINGZHANG RED LIST (JZ-RL)

RED-LIST 3 CHECK · Public test / Ranking / Review

Evidence Chain

① Provisional boundary

site_boundary.geojson #SITE-001
Overall design area 11.41 km²

② Land-use zones

land_use.geojson #LU-*
9 codes · 38 parcels

③ Feature layers

buildings/roads/green/public
309 bldgs · 12 centerlines · green 3.10 km²

④ Metric recalculation

metrics.json
areas / ratios / counts · EPSG:4548

⑤ Drawing deliverables

assets/figures/*_png
5 figures in this volume


Note: FAR, building height, density and green-ratio controls pending official regulatory planning conditions (metrics.json status=unknown)

Provisional constraint, design discussion only | CRS: CGCS2000 Gauss-Krüger EPSG:4548 | Extent & metrics based on the provisional boundary
Data: JZ-RL geometry package v0.1 (site_boundary / constraints / land_use / roads / green_space / public_space / buildings / phasing / metrics.json)

Core metrics recalculation (EPSG:4548, provisional scope)

指标 Metric	值 Value	单位 Unit	状态 Status
总体设计范围面积 Overall design area	11,412,825.386	sqm	known
绿地率 Green ratio	0.272	ratio	known
广场比例 Plaza ratio	0.010	ratio	known
道路比例 Road ratio	0.147	ratio	known
建筑基底面积 Building footprint area	1,601,856	sqm	known
建筑栋数 Building count	309	count	known
重点区数量 Key area count	3	count	known
AI场景卡 Scenario cards	10	count	known
产业测试场景 Industry test scenarios	3	count	known
用户画像 User personas	5	count	known
朝圣地标 Pilgrimage landmarks	3	count	known
AI生态案例 AI ecosystem cases	6	count	known
更新项目 Renewal projects	10	count	known
用地地块数 Land-use parcels	38	count	known
道路中心线 Road centre lines	12	count	known

Phasing and renewal projects

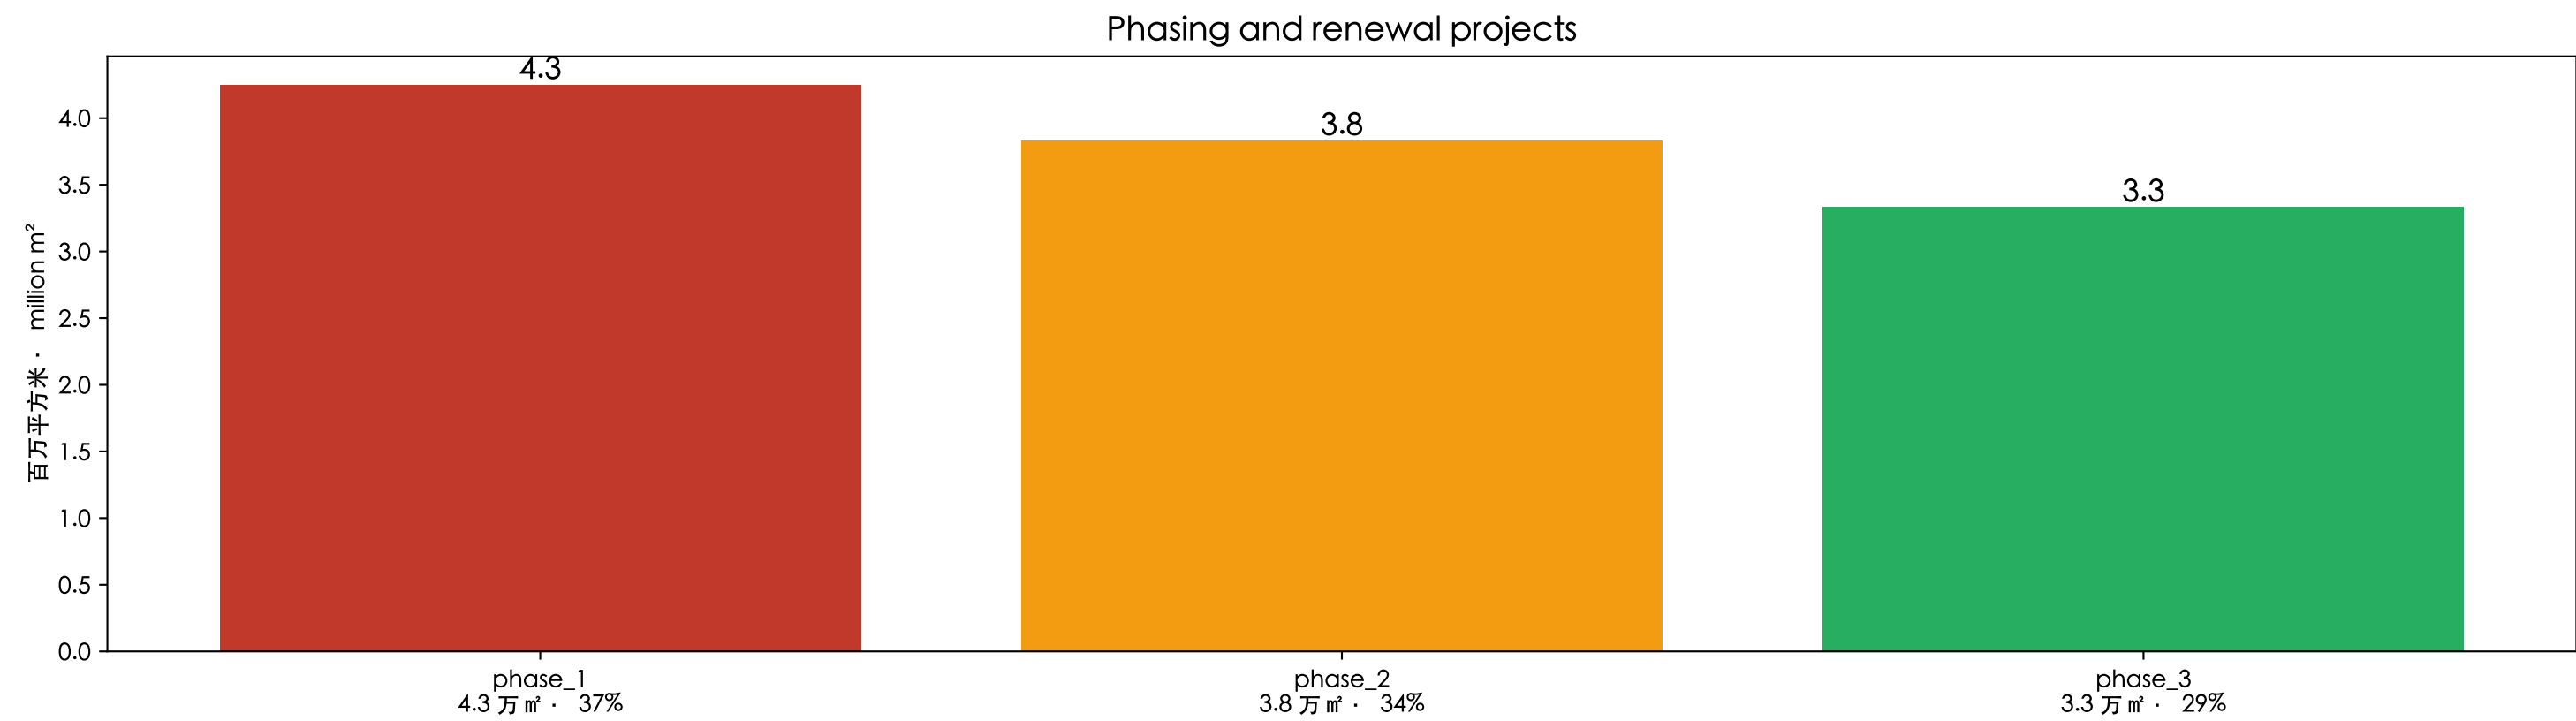

Renewal projects JZ-01…JZ-10

JZ-01 慢行断点缝合 · JZ-02 清河创新界面 · JZ-03 成果转化街 · JZ-04 站四象限步行连通 · JZ-05 红榜时刻塔网络 · JZ-06 原点开源舱 · JZ-07 众智测评场 · JZ-08 数据要素会客厅 · JZ-09 AI生活服务样板街 · JZ-10 红榜大会公共路线