


人字线 THE SWITCHBACK LINE

百年京张的第二次爬坡 · 总体概念与空间结构板

人字线 THE SWITCHBACK LINE · 总体概念图

百年京张的第二次爬坡 —— 一脊三折 · 六廊缝合 · 两翼联动（方案总览 / 概念建议）

一撇一捺两条轨道在折返点交汇：历史轨（砖红）与数据轨（靛蓝）。三处重点区即三次换向加速的折返站。

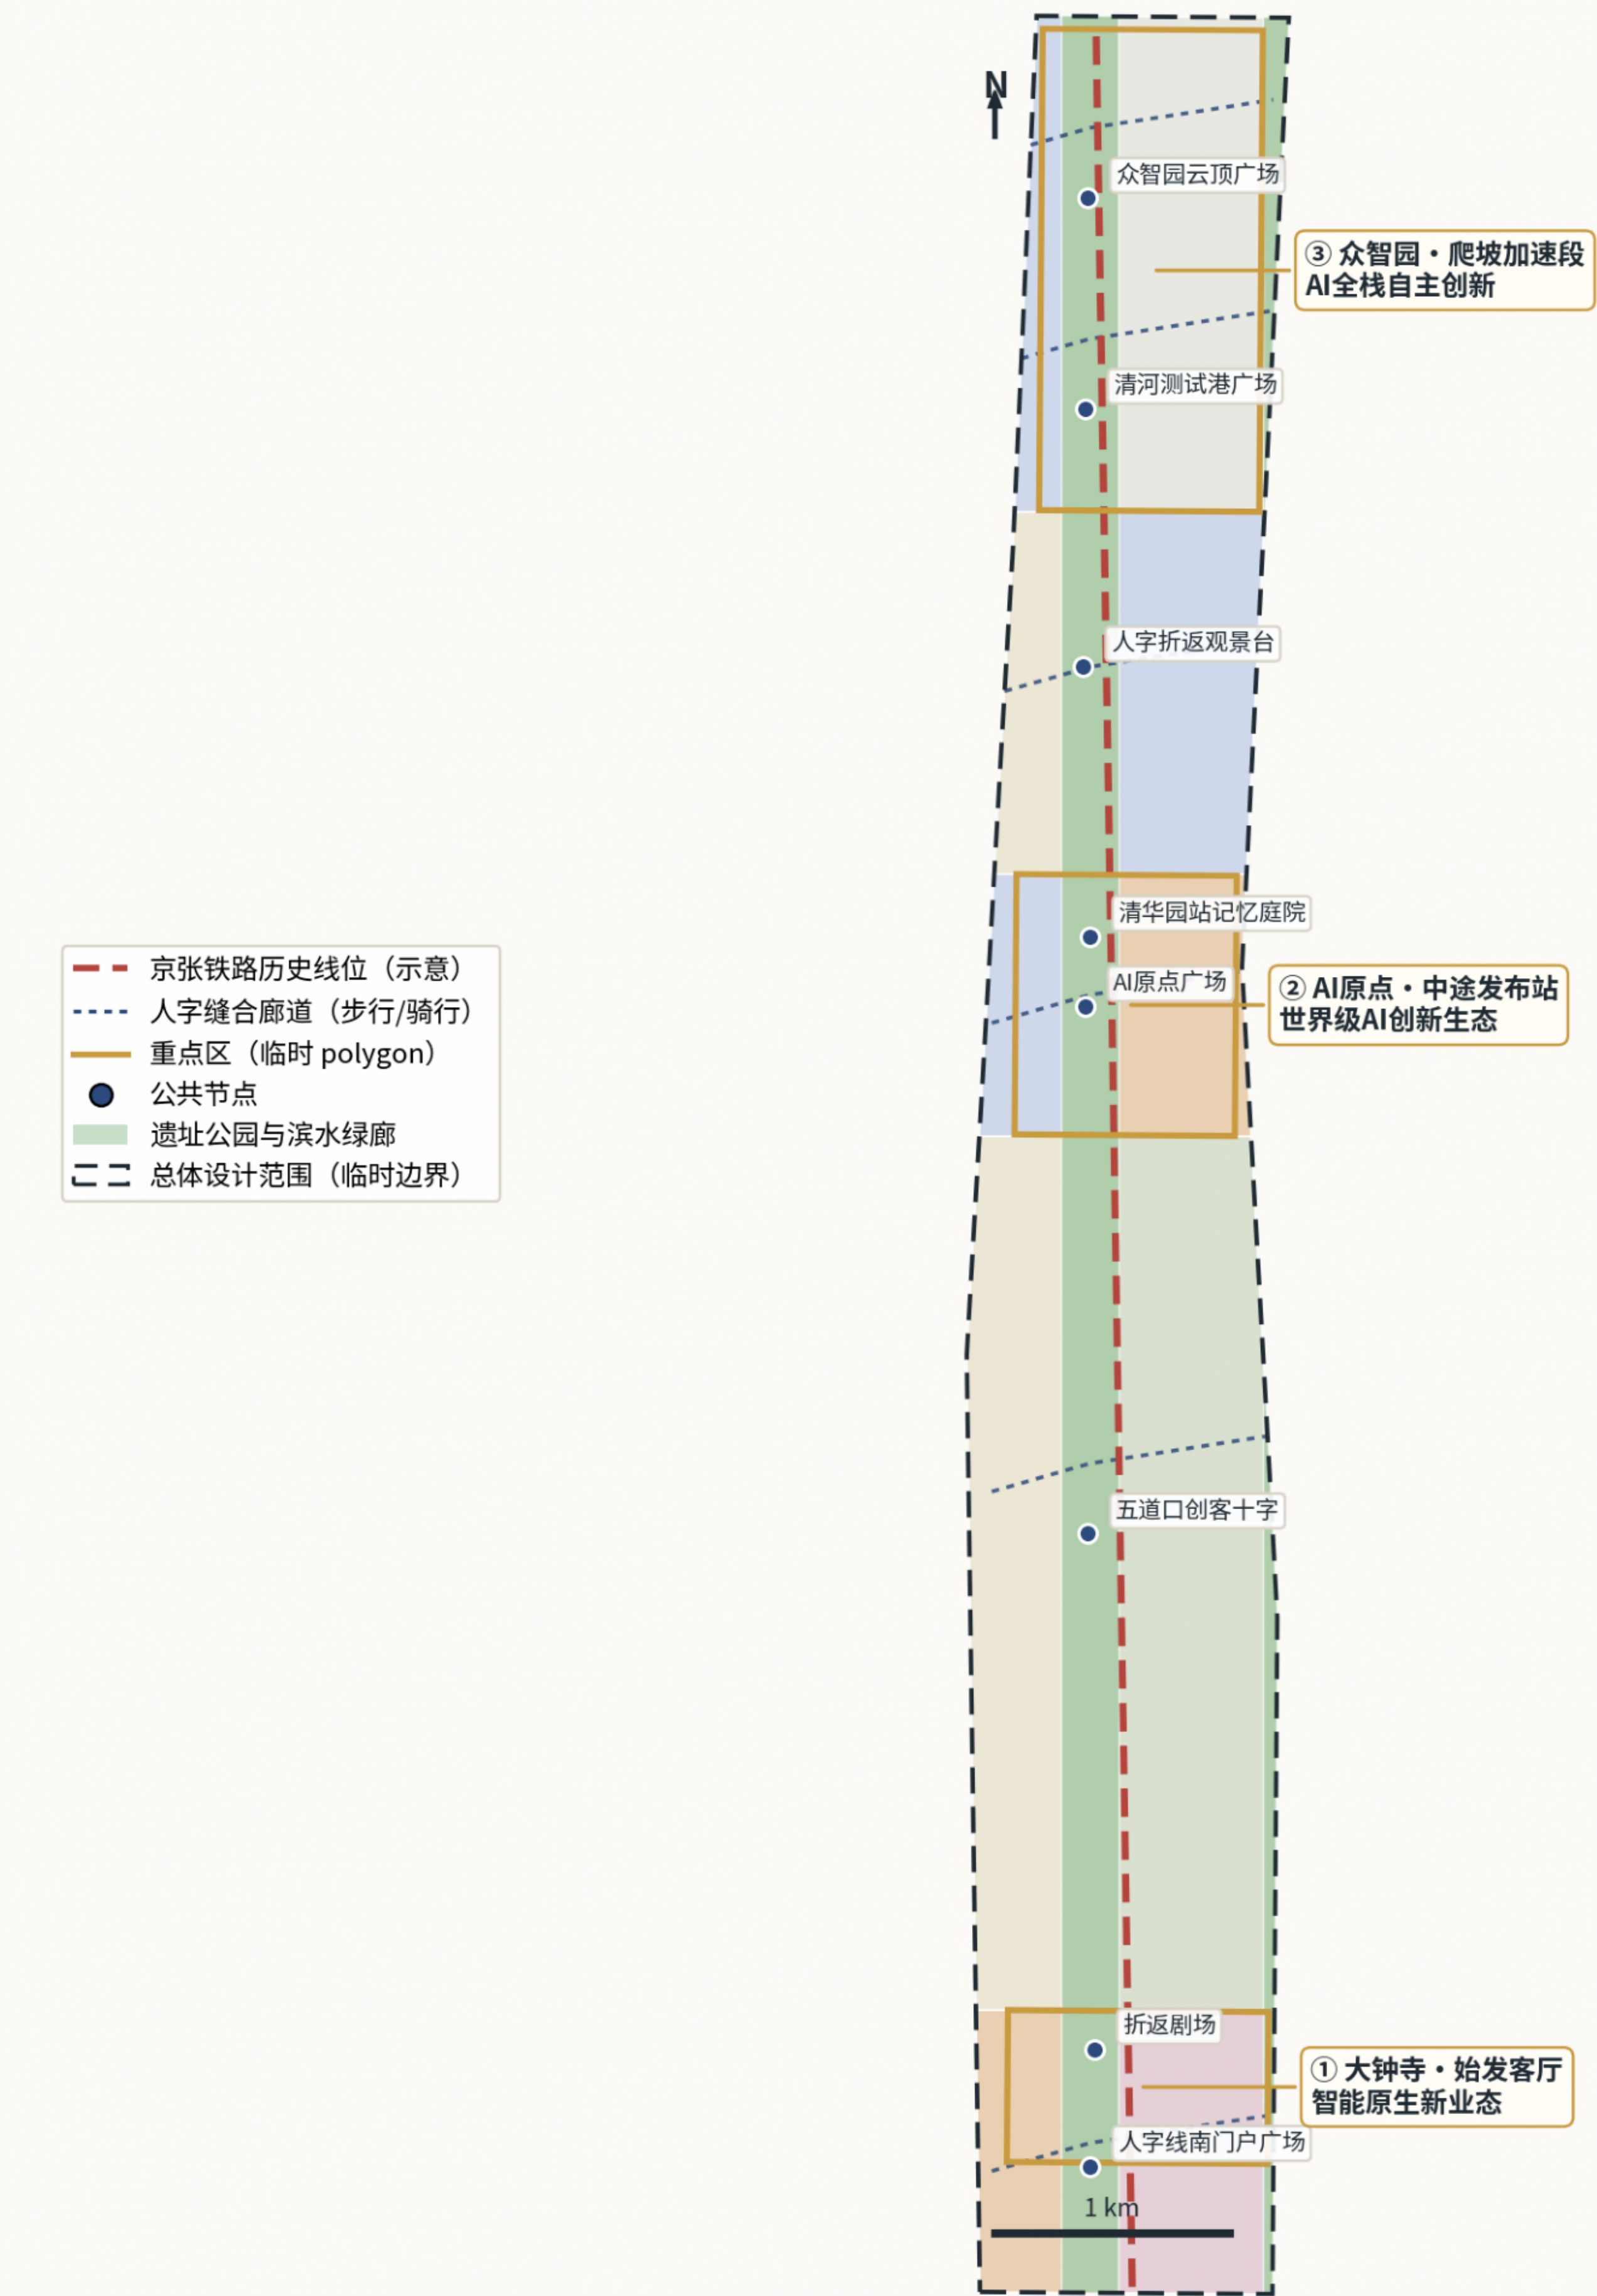


一脊：京张遗址公园活力带（中央绿脊，公园绿地 262 ha）；三折：大钟寺始发客厅 / AI原点中途发布站 / 众智园爬坡加速段；六廊：六条人字形东西缝合廊道（步行骑行优先，5-8 分钟间距）；两翼：中关村科技服务翼 / 小月河场景赋能翼。

空间结构与用地构成

一脊（遗址公园绿脊）· 三折（三处重点区）· 六廊（东西缝合）· 两翼（服务翼/场景翼）

用地分区（拓扑安全划分 · 19 单元 · 国标代码）

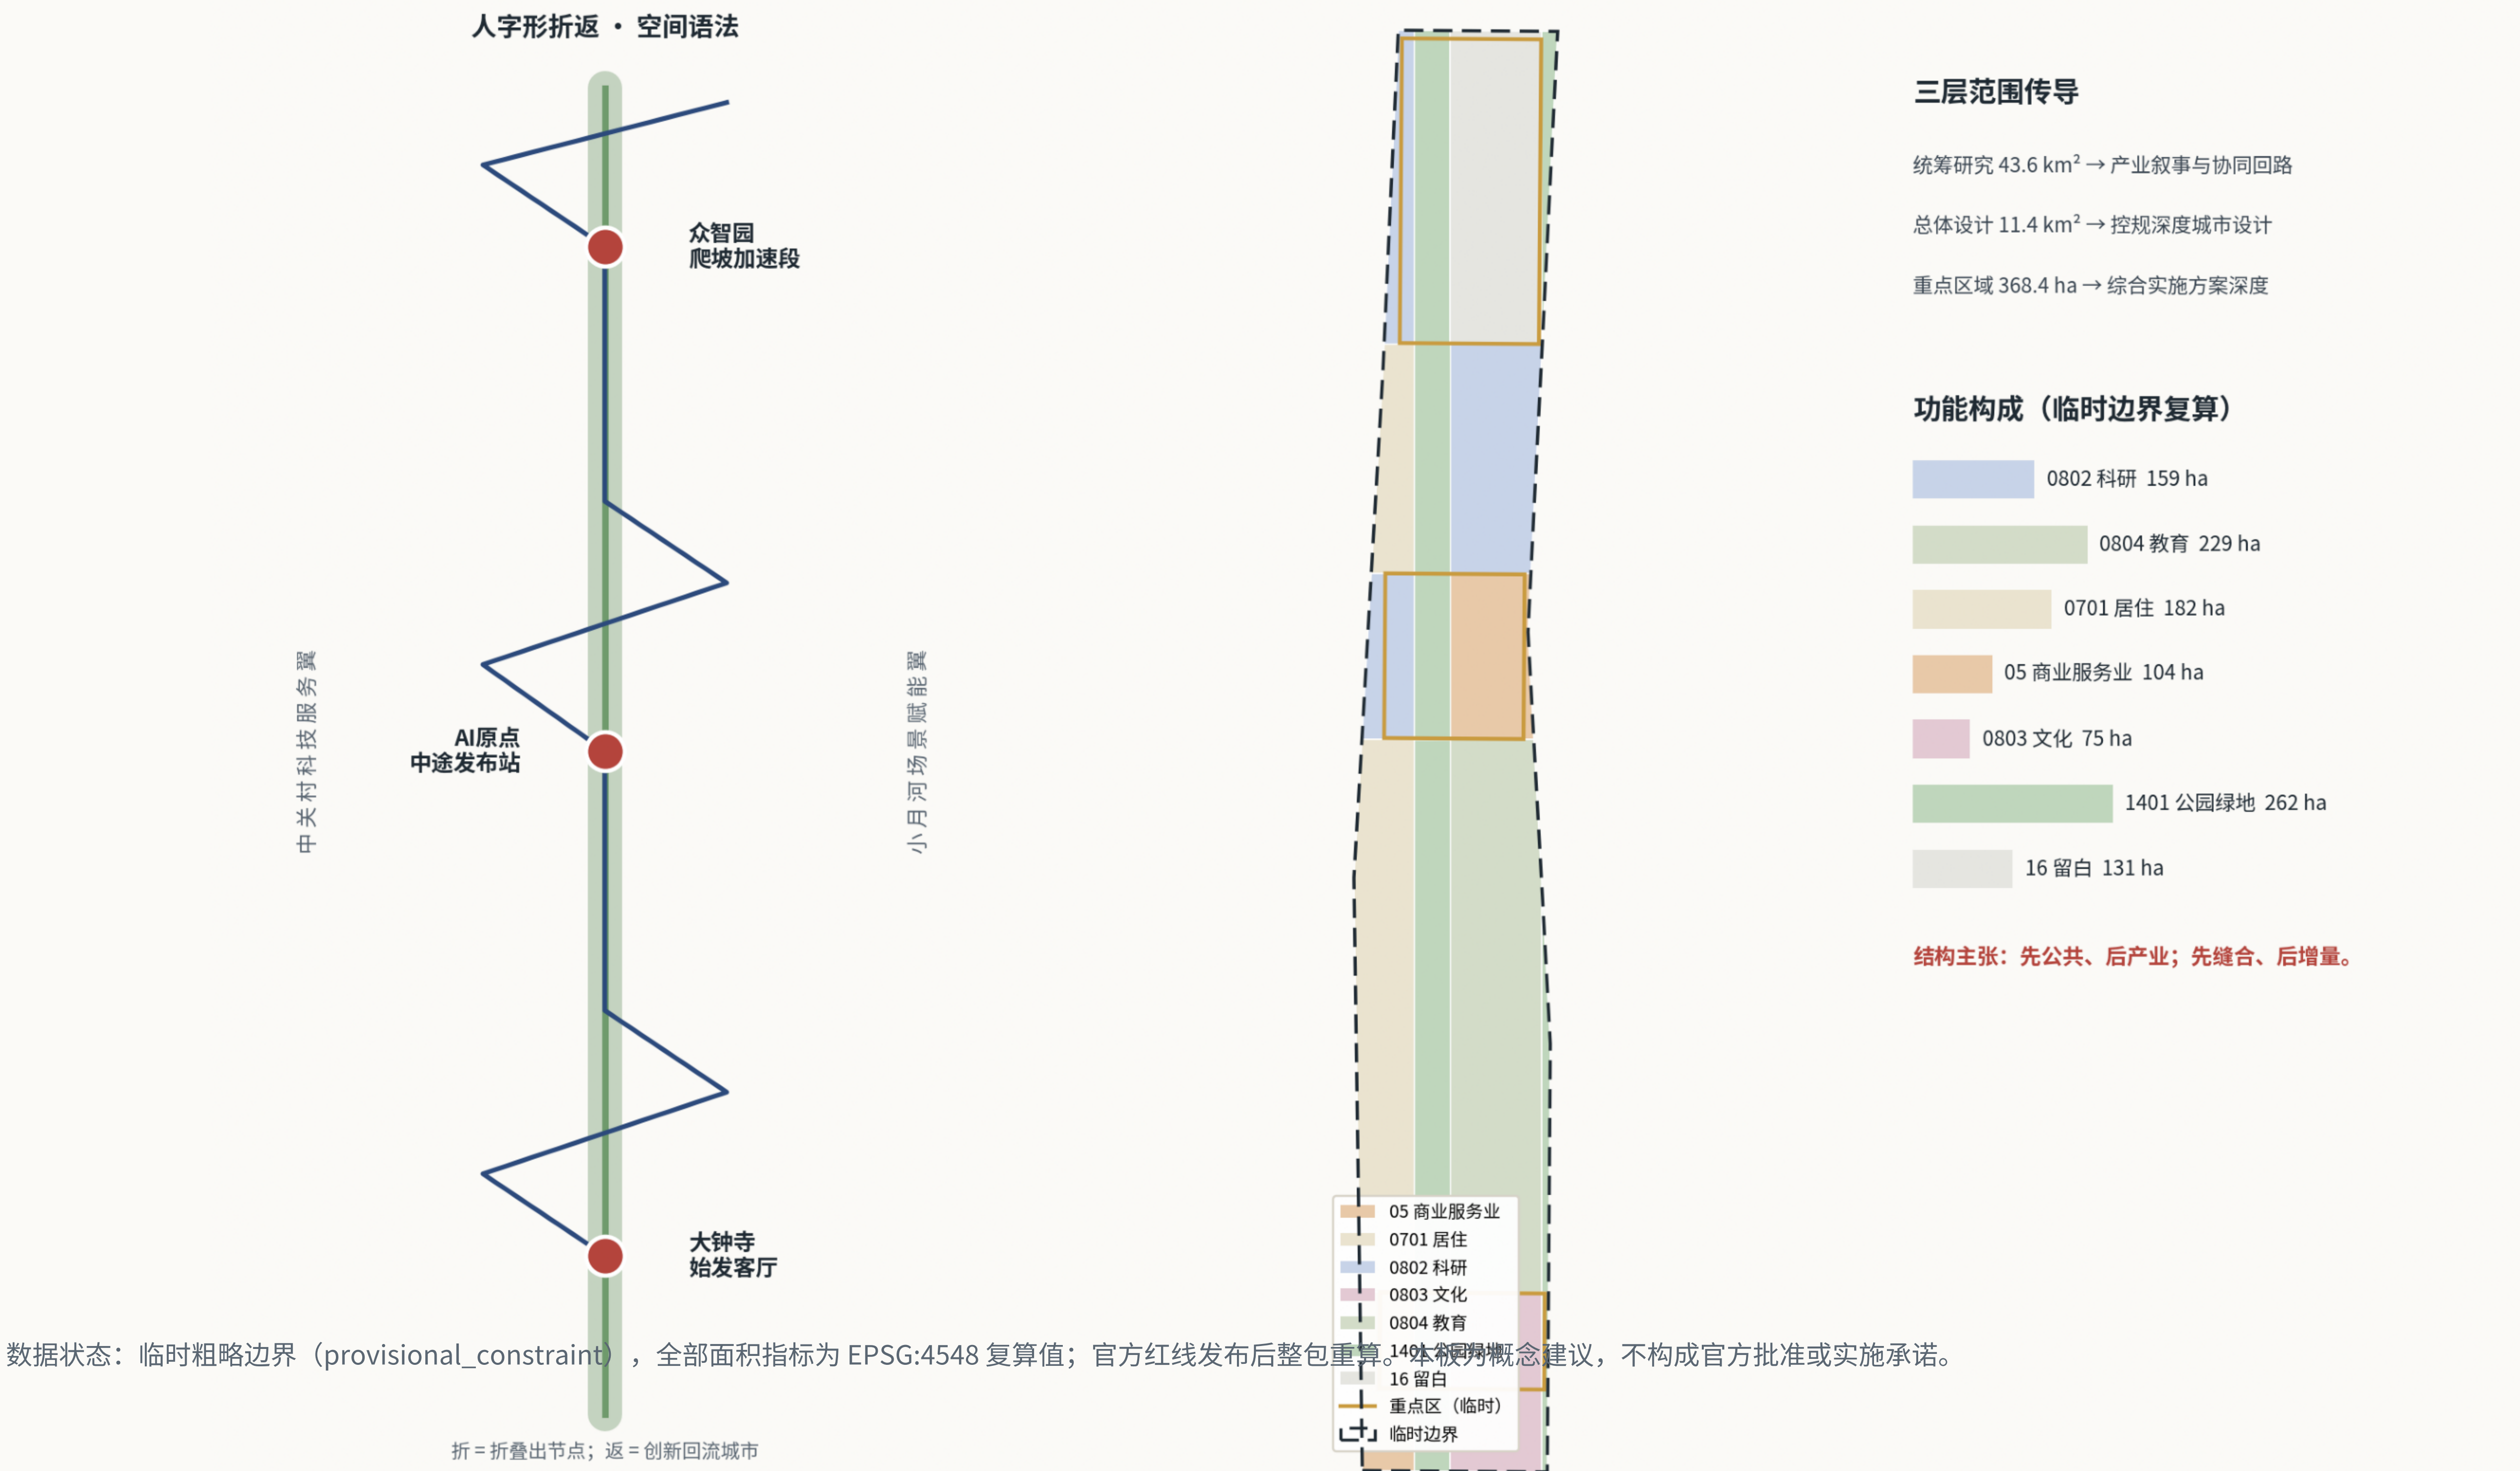

边界与重点区为临时粗略 polygon（provisional_constraint），仅用于概念表达与自检复算；面积复算 CRS: EPSG:4548。来源: SRC-PROVISIONAL-BOUNDARIES-2026。

边界与重点区为临时粗略 polygon（provisional_constraint），仅用于概念表达与自检复算；面积复算 CRS: EPSG:4548。来源: SRC-PROVISIONAL-BOUNDARIES-2026。

三层范围传导

统筹研究 43.6 km² → 产业叙事与协同回路

总体设计 11.4 km² → 控规深度城市设计

重点区域 368.4 ha → 综合实施方案深度

功能构成（临时边界复算）

0802 科研 159 ha

0804 教育 229 ha

0701 居住 182 ha

05 商业服务业 104 ha

0803 文化 75 ha

1401 公园绿地 262 ha

16 留白 131 ha



结构主张：先公共、后产业；先缝合、后增量。

重点区 · 场景 · 指标证据板

三次折返的详细设计 / 12 张场景卡 / 可复算指标链

三处重点区详细设计索引


三次折返：始发（大钟寺）→ 发布（AI原点）→ 加速（众智园）；金色为临时重点区 polygon，设计均为概念建议

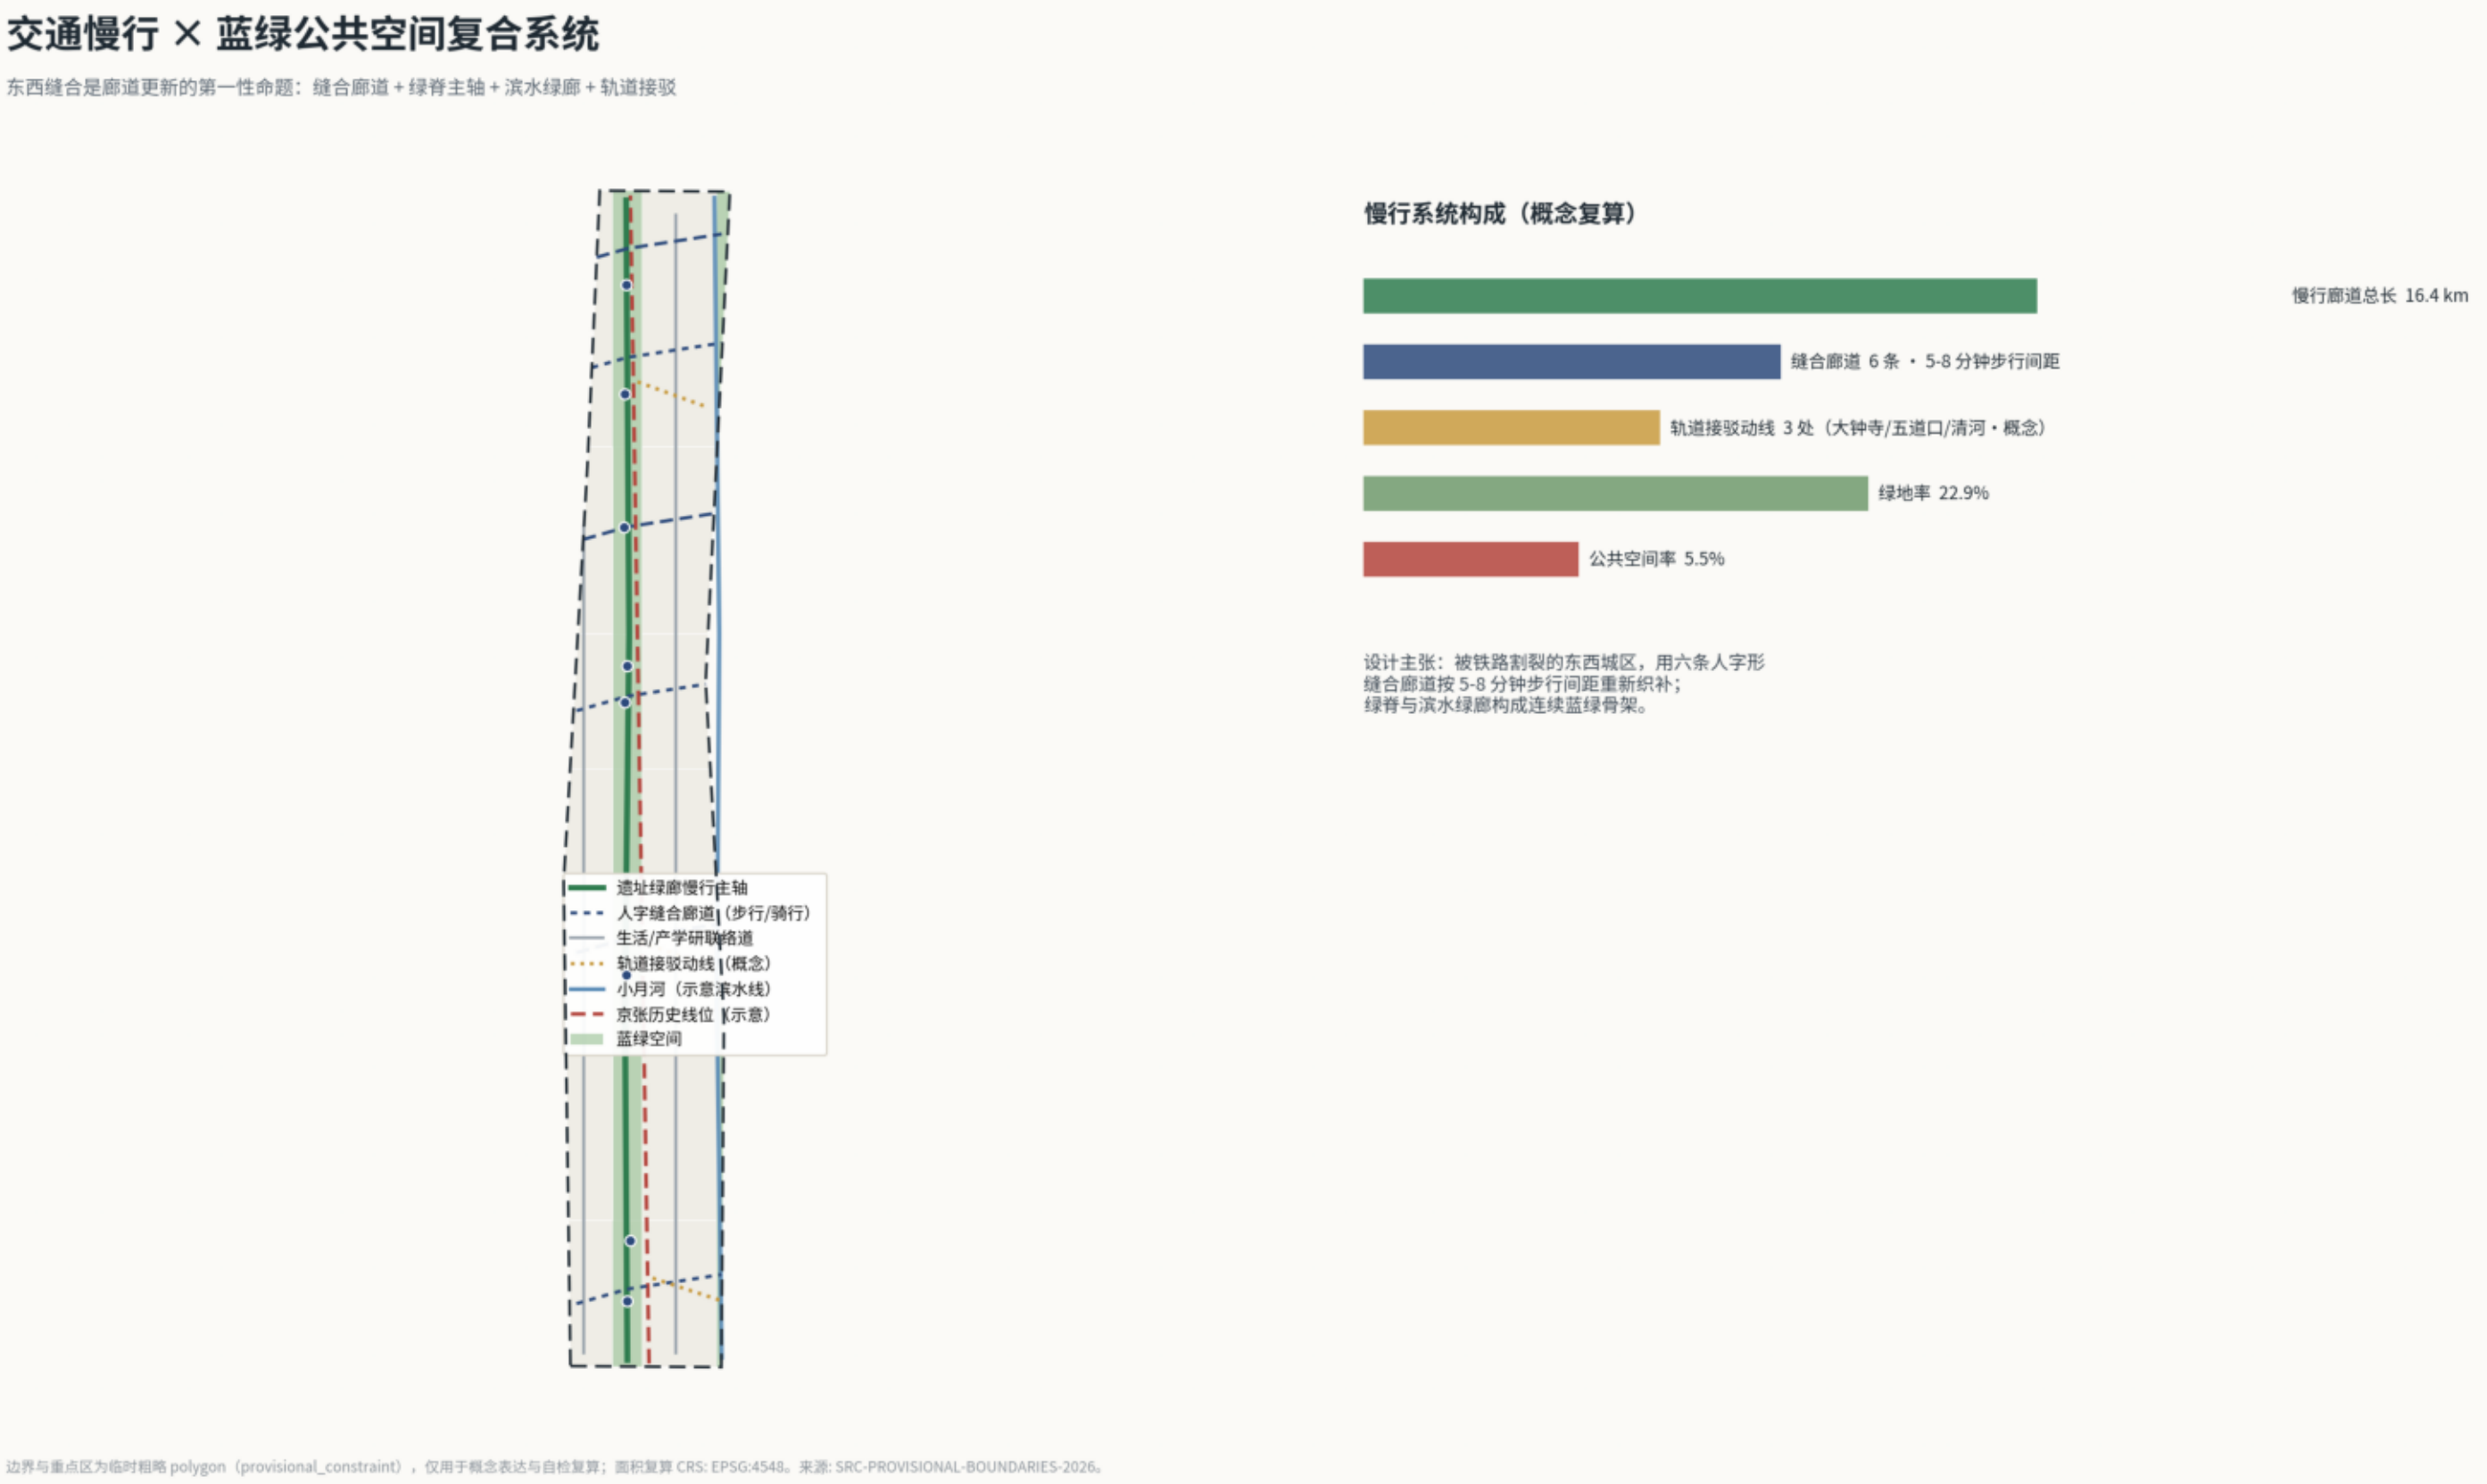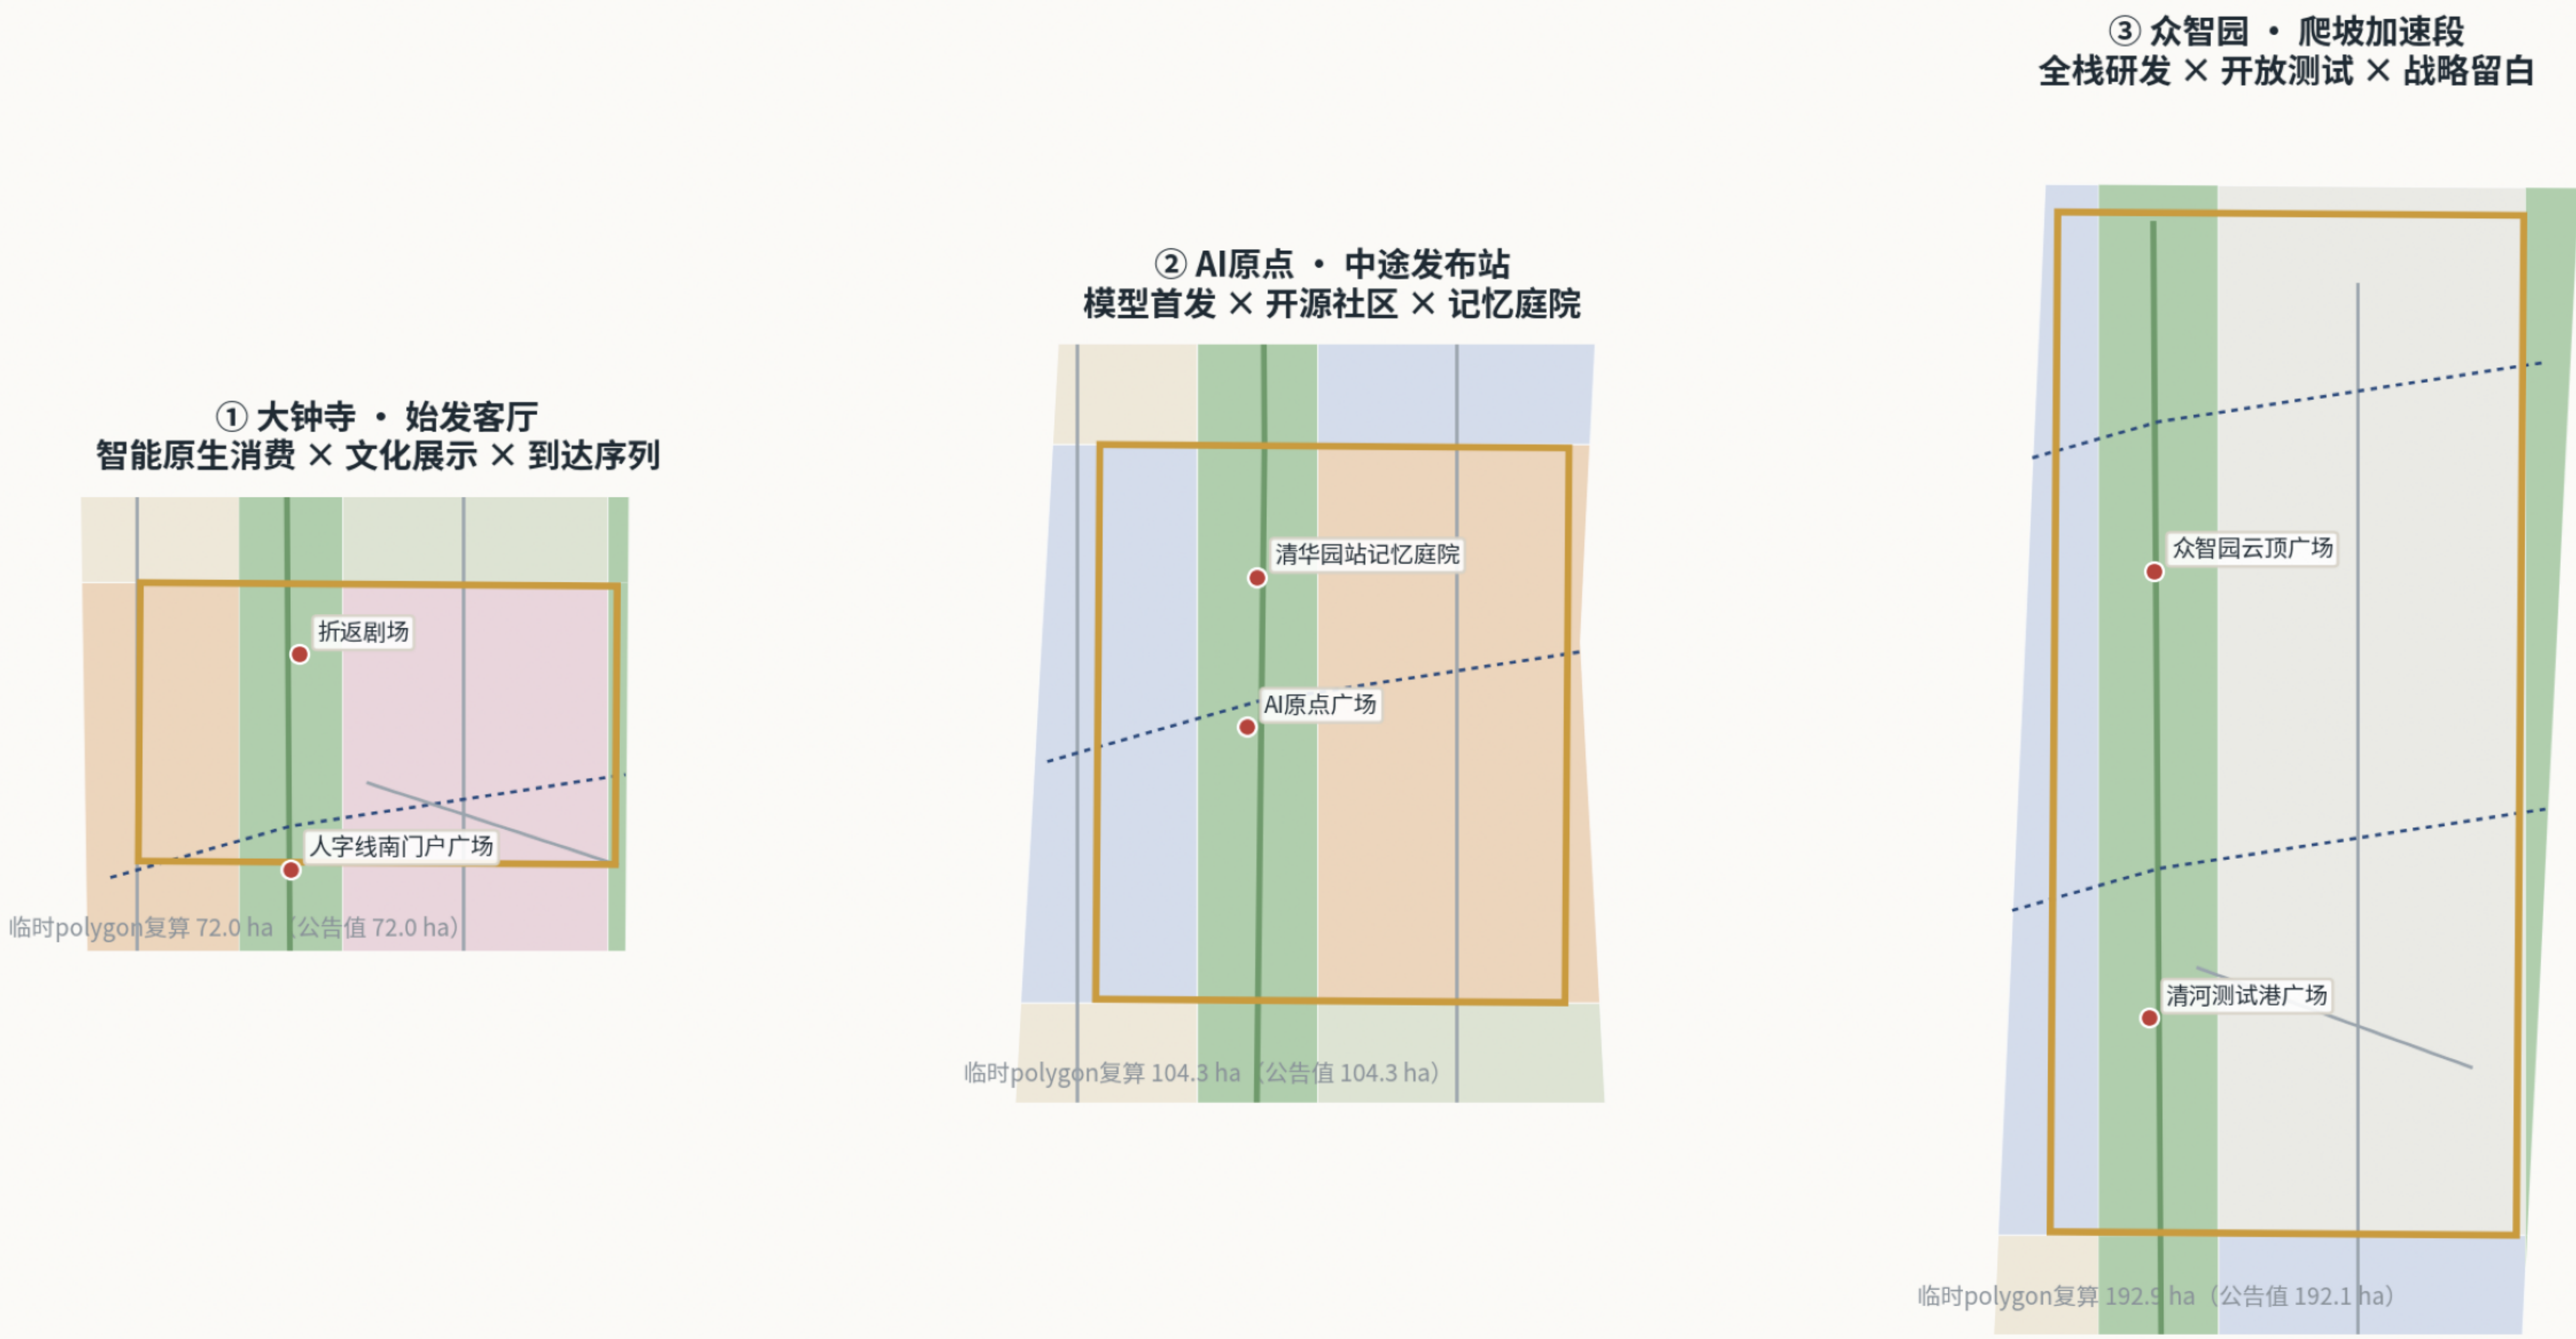

边界与重点区为临时粗略 polygon（provisional_constraint），仅用于概念表达与自检复算；面积复算 CRS: EPSG:4548。来源: SRC-PROVISIONAL-BOUNDARIES-2026。

核心指标复算与证据链

所有面积与比例可由 GeoJSON 独立复算；临时边界与概念估算均已标注

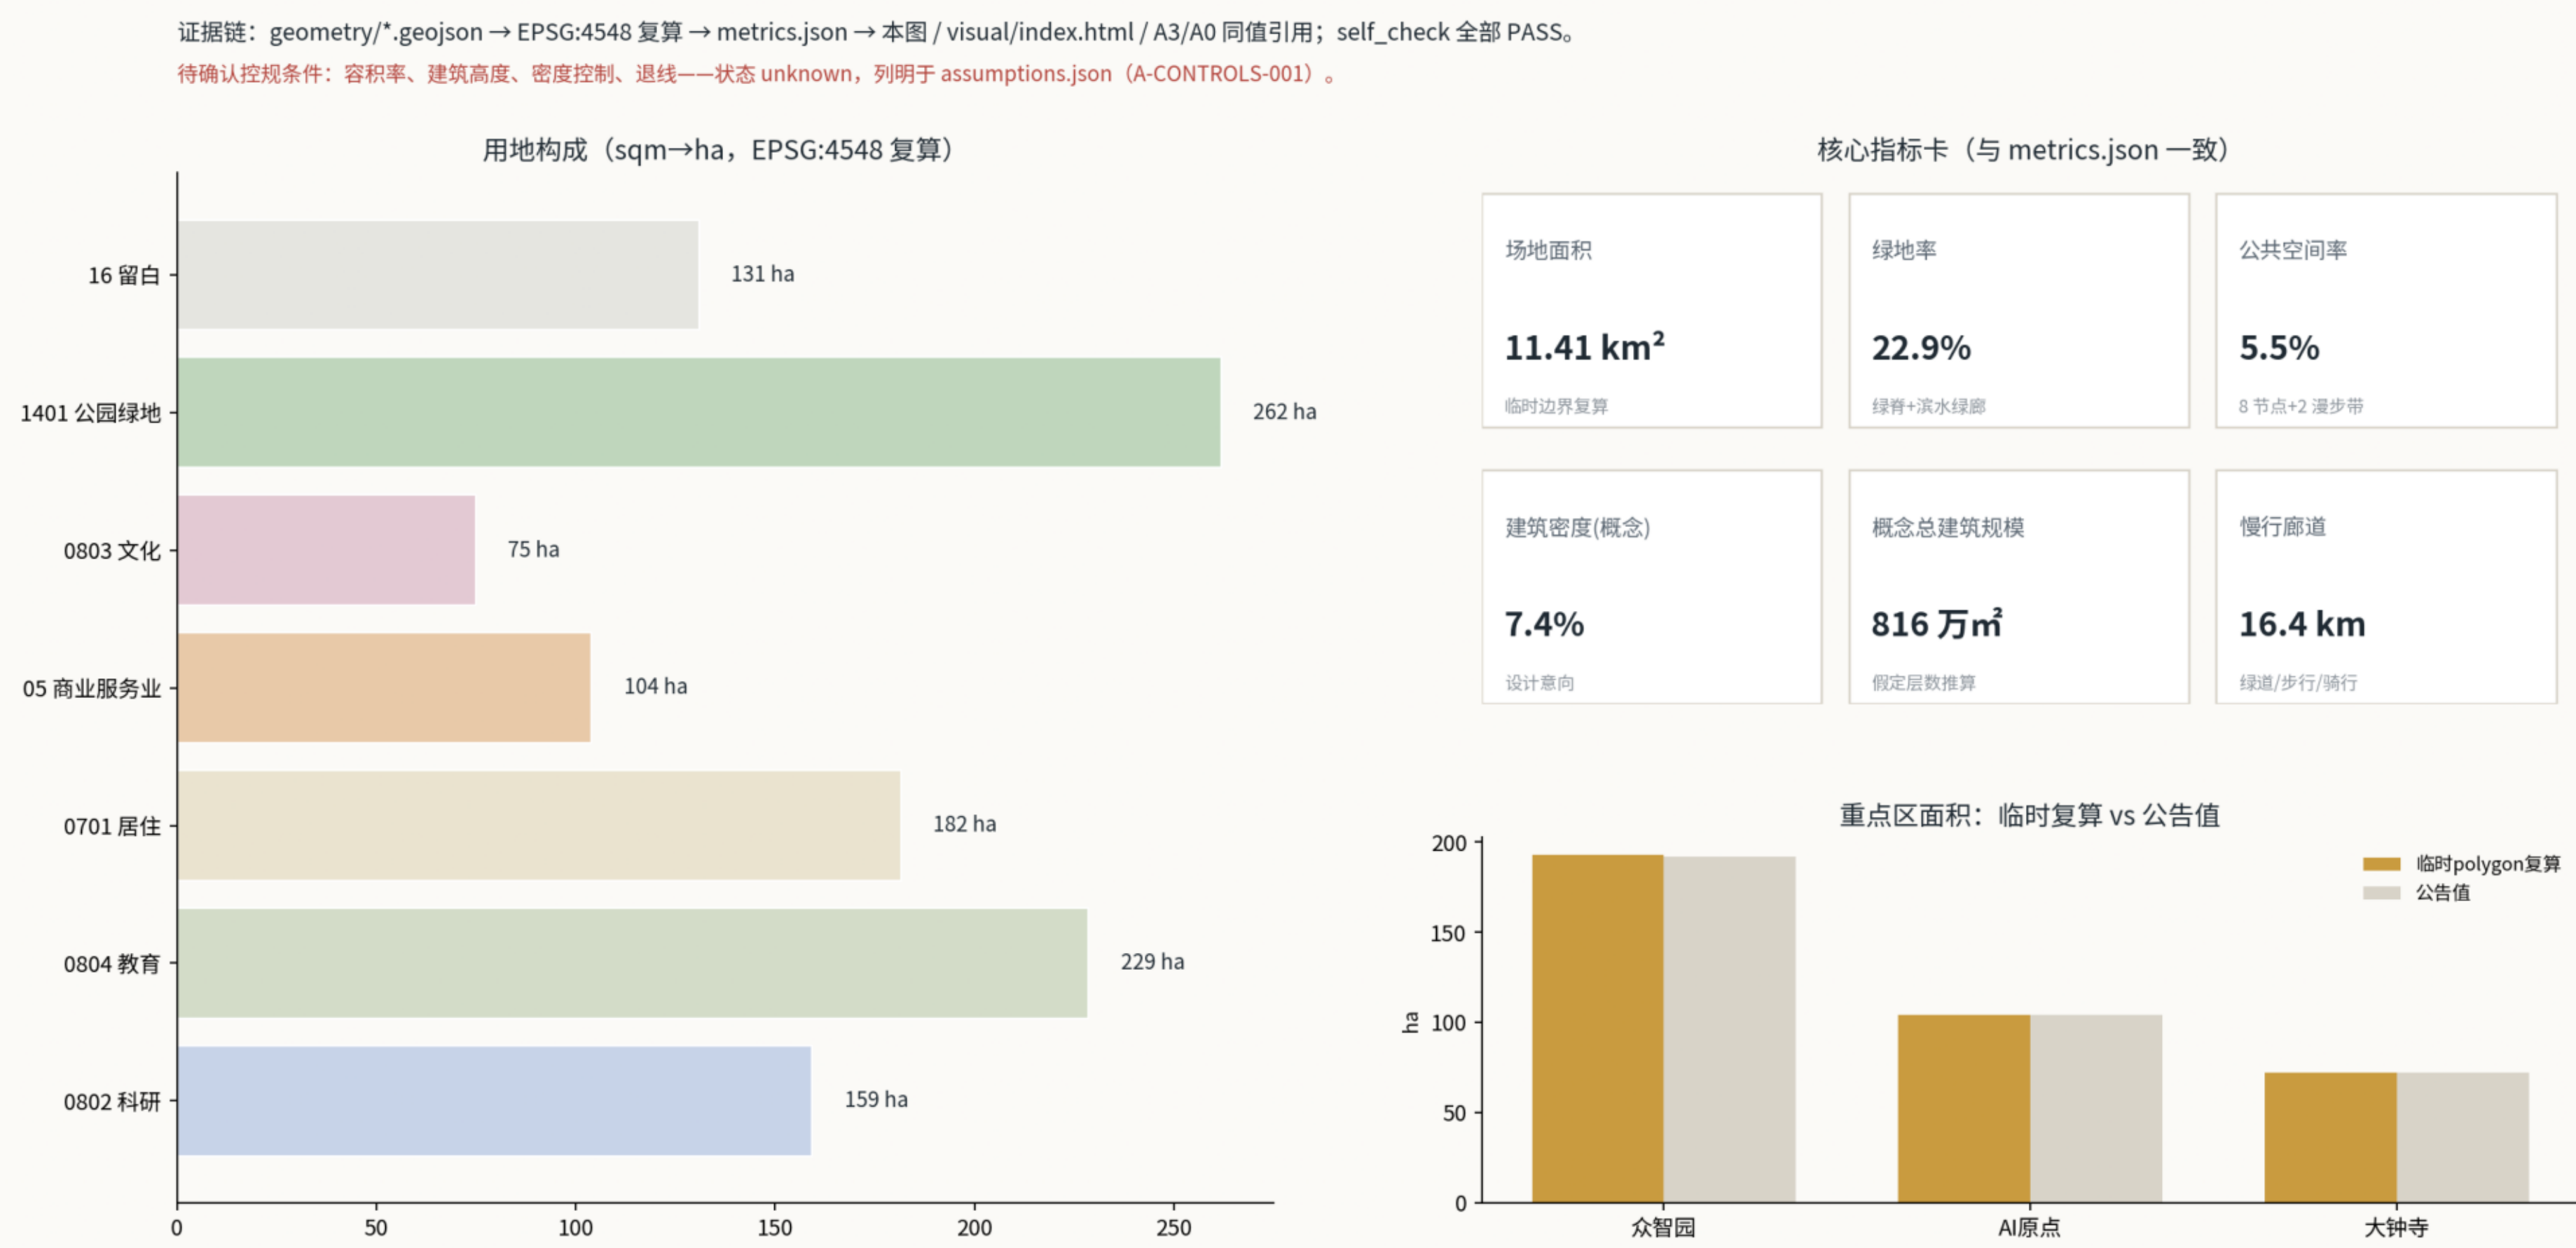

边界与重点区为临时粗略 polygon（provisional_constraint），仅用于概念表达与自检复算；面积复算 CRS: EPSG:4548。来源: SRC-PROVISIONAL-BOUNDARIES-2026。

场景卡（12 张，★产业测试验证）：SC-01 时空叠映导览 / SC-02 AR夜跑伴行 / SC-03 创客市集匹配 / SC-04★模型首发公开评测 / SC-05★机器人开放测试港 / SC-06★端侧算力沙箱 / SC-07 智算消费实验室 / SC-08 养老陪伴试点 / SC-09 生态感知管护 / SC-10 接驳MaaS / SC-11 人字工单 / SC-12 国际创新导览。

核心指标：场地 11.41 km² · 绿地率 22.9% · 公共空间率 5.5% · 慢行 16.4 km · 概念总建筑面积 816 万 m²。