


京张尺规线 / Jingzhang The Gauge Line

众智园 · 众智园 · Zhongzhiyuan · Slogan · 三纵三带 · 三重点区 · 慢行主带 · 蓝绿网络

图01 资料证据链与三带总览

Fig.01 Evidence Chain & Three-Belt Overview

京张尺规线 / Jingzhang The Gauge Line — Dual Gauge, not Slogan

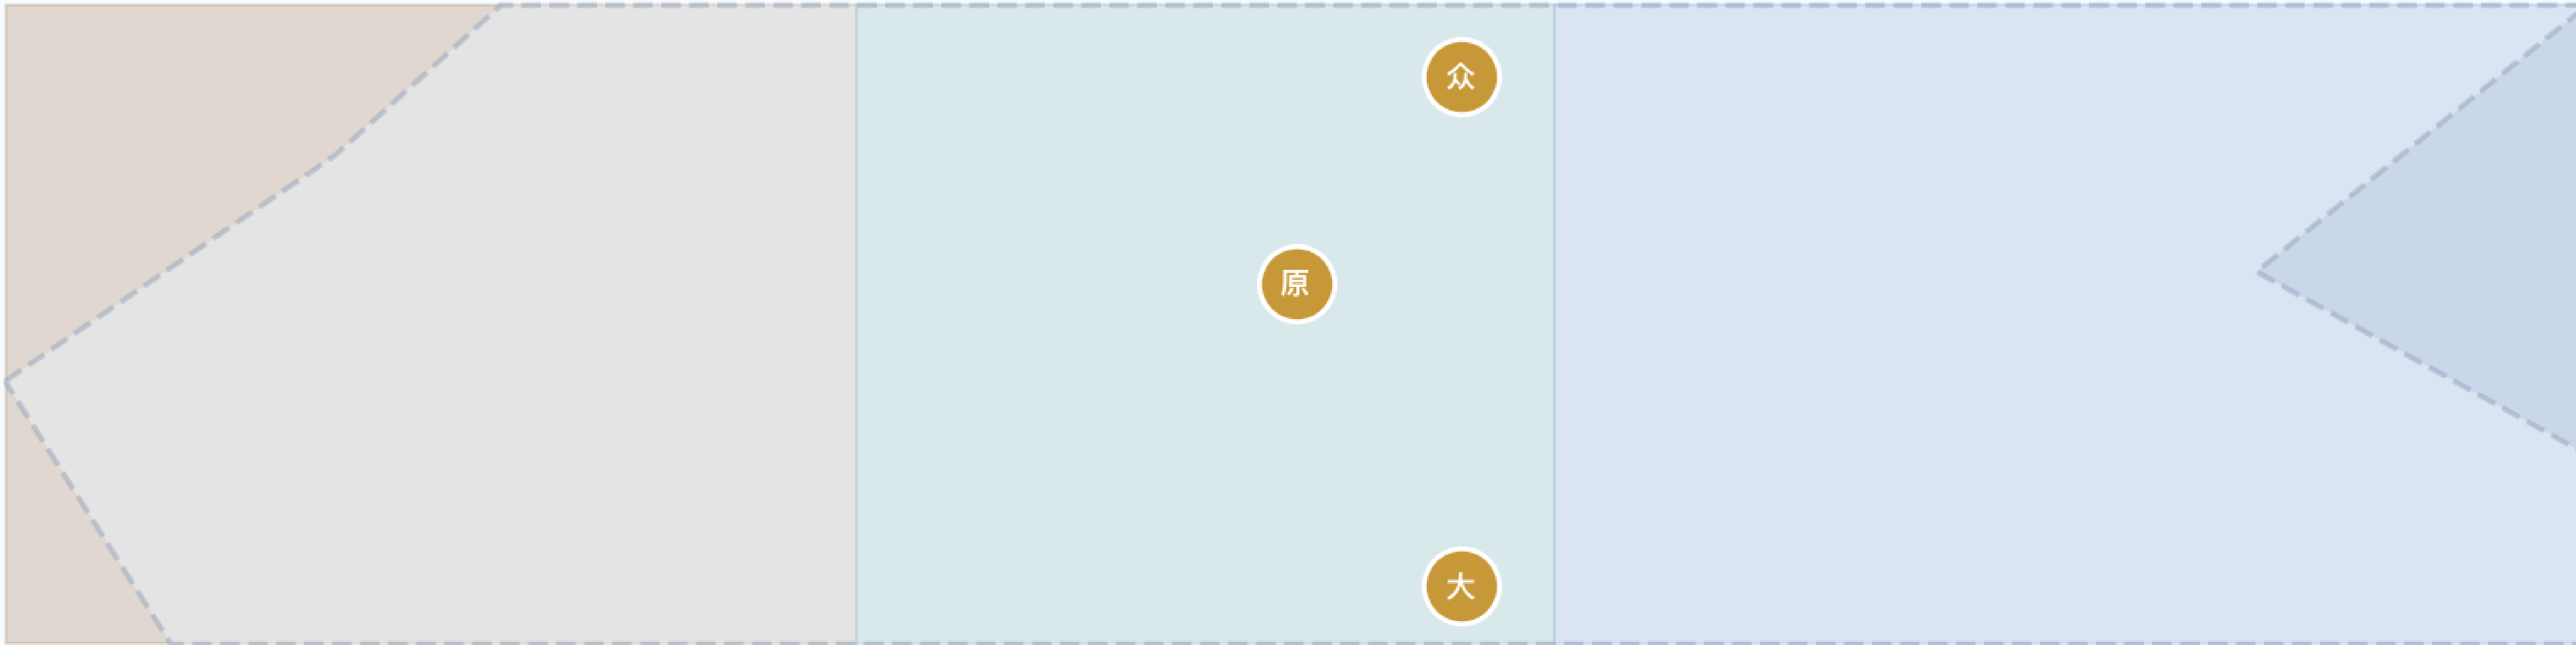

Provisional boundary · 临时粗略边界，仅用于设计讨论与自检，非官方红线 / Not an official redline | 示意图·非等比·仅示意 / Schematic, not to scale | Source: provisional_boundaries.geojson (EPSG:4548)

证据层级 / Evidence layers

① 公告 + Agent 任务书 / Brief

④ metrics 指标复算 (EPSG:4548)

② provisional 边界 + 三重点区

⑤ 合规·标准·深度矩阵 + 自检

③ 用地·建筑·道路·绿地·公共空间

总览：三带结构 + 三重点区 + 证据链 / Overview: three-belt structure + key areas + evidence chain

空间主轴：人本尺度步行主轴串联京张遗址公园绿轴；东西缝合次干路重连被铁路切割的城市肌理。三重点区——众智园（自主创新）、AI 原点社区（开源转化）、大钟寺（智能经济）——沿轴落位。

图03 三处重点区域索引与设计任务

Fig.03 Three Key Areas Index

每个重点区：定位 + 空间结构 + 建筑更新 + 交通慢行 + 公共空间 + AI场景 + 实施风险



Provisional boundary · 临时粗略边界，仅用于设计讨论与自检，非官方红线 / Not an official redline | 示意图·非等比·仅示意 / Schematic, not to scale | Source: provisional_boundaries.geojson (EPSG:4548)

设计动作摘要 / Design moves

[众] 众智园 Zhongzhiyuan

自主模型测试·标准制定

安全治理展示·低碳算力

图例 / Legend

众智园 AI 自主创新加速区 大钟寺 AI 产业聚集区

北京 AI 原点社区 --- provisional 边界

[原] AI原点社区 Origin Community

开源协作·成果发布

人才特区·近校孵化

[大] 大钟寺 Dazhongsi

领军企业·智能体新业态

数据要素·四象限连通

三处重点区域详细设计 / Three key areas detailed design

图05 核心指标复算与证据链

Fig.05 Metrics Recalculation & Evidence

空间指标由提交几何复算；管控指标（FAR/高度）因官方控规缺失标 unknown




拆改留为概念建议，非权属或工程结论 · Provisional boundary; recalculate when official geometry supplied

核心指标复算与证据链 / Metrics & evidence

图02 总体设计范围用地结构

Fig.02 Land-Use Structure of Overall Design Area

用地全覆盖、无重叠；用地代码依《国土空间调查、规划、用途管制分类》

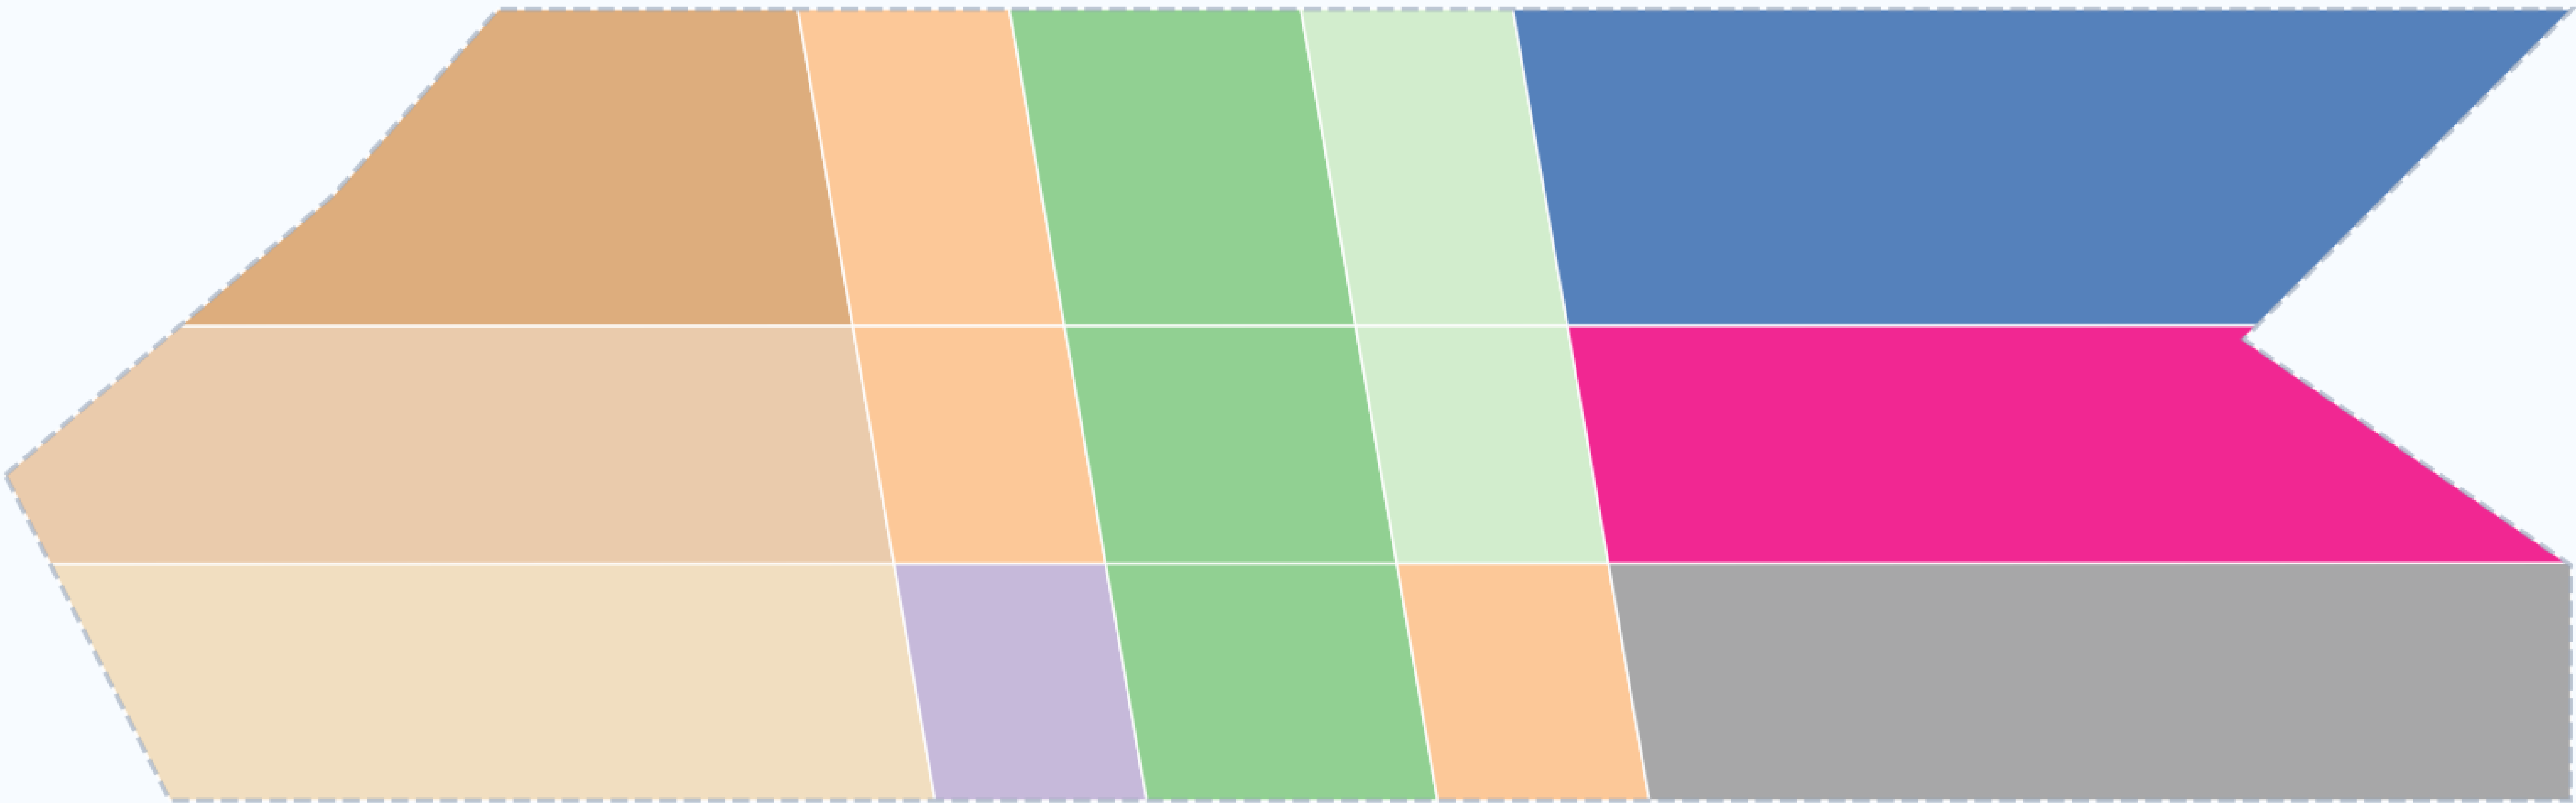

Provisional boundary · 临时粗略边界，仅用于设计讨论与自检，非官方红线 / Not an official redline | 示意图·非等比·仅示意 / Schematic, not to scale | Source: provisional_boundaries.geojson (EPSG:4548)




总体设计范围用地结构 / Land-use structure

图04 交通慢行与蓝绿公共空间复合系统

Fig.04 Mobility & Blue-Green Public Space

人本尺度步行主轴 + 东西缝合 + 蓝绿网络 + 朝圣地标

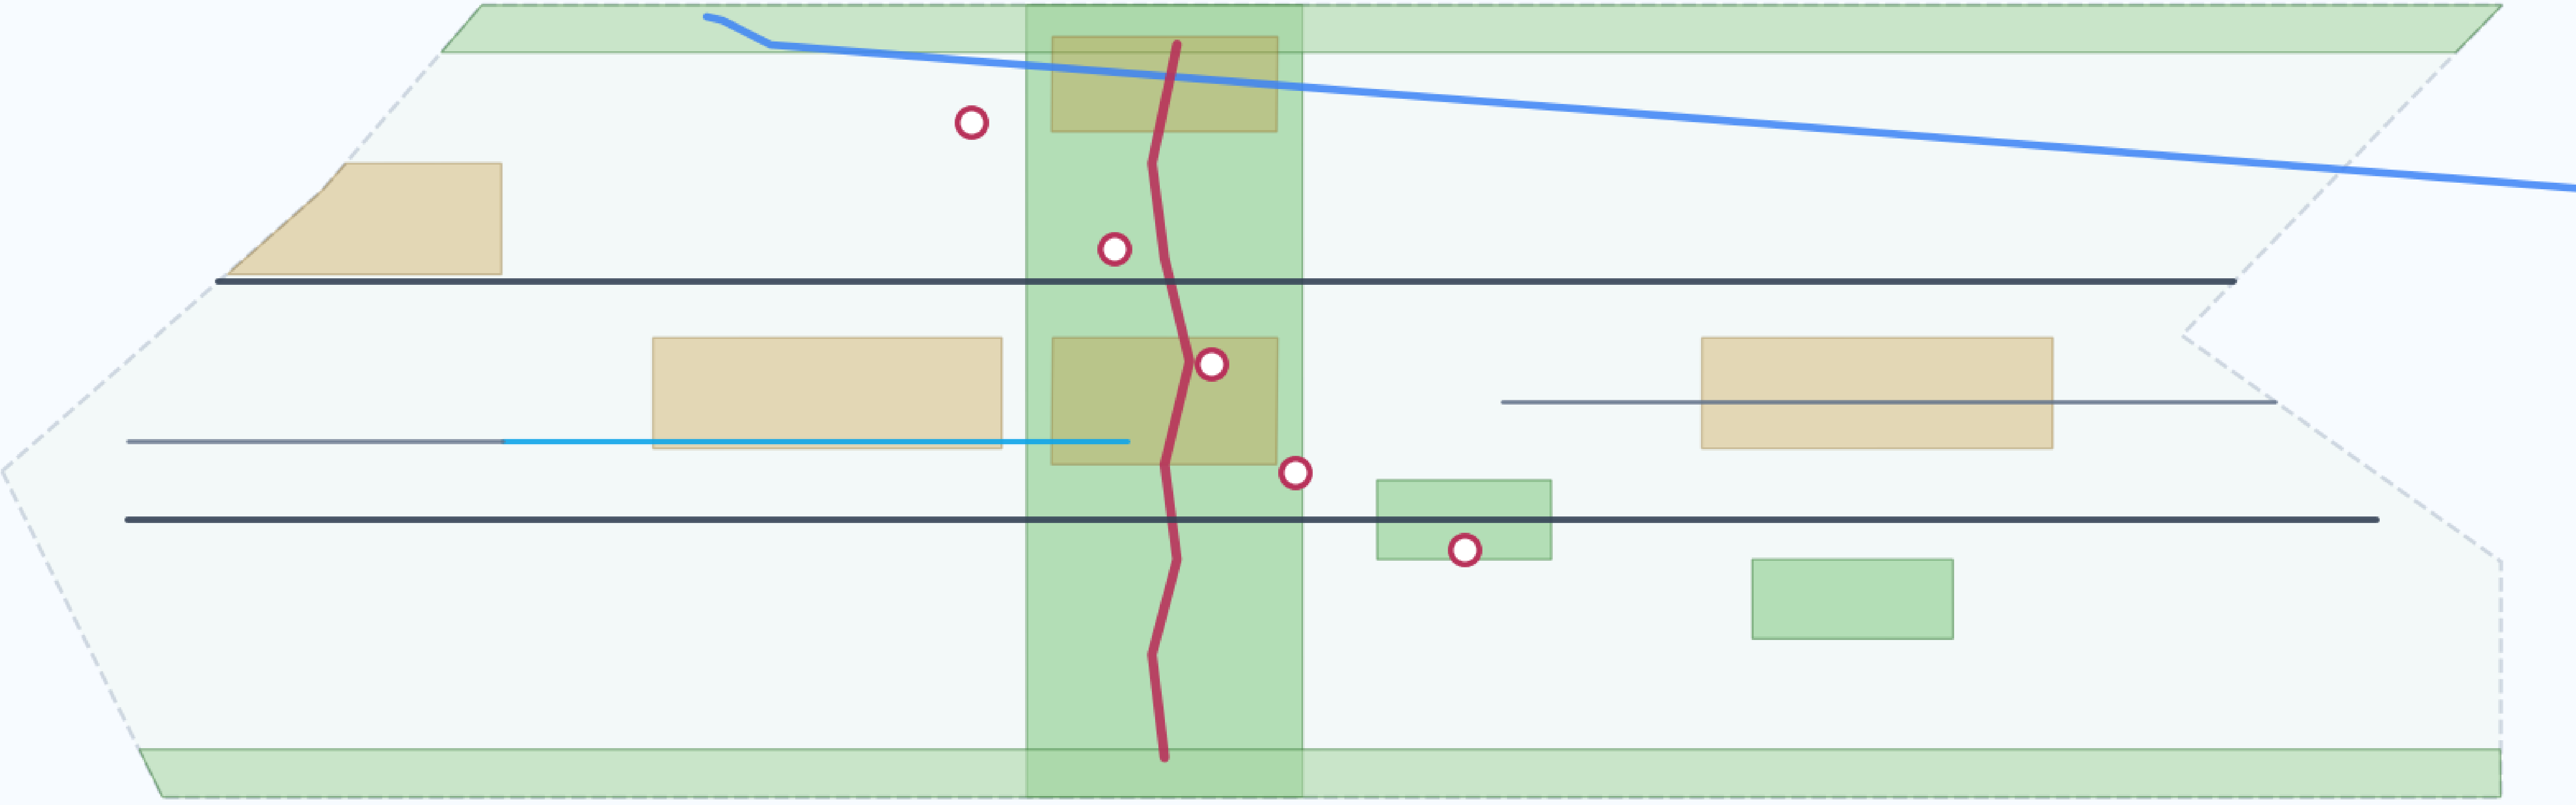

Provisional boundary · 临时粗略边界，仅用于设计讨论与自检，非官方红线 / Not an official redline | 示意图·非等比·仅示意 / Schematic, not to scale | Source: provisional_boundaries.geojson (EPSG:4548)

图例 / Legend				
 现状水系 / Waterway (OSM)	 缝合次干路 / Stitching road	 自行车道 / Cycleway	 公园绿地 / Park	 公共空间·地标前场 / Public
 步行主轴 / Pedestrian spine	 支路 / Branch	 地铁站 / Metro station	 防护绿地 / Buffer green	 provisional 边界