


京张1909 · AI创新带

总体方案 — 一轨两河三站 · 六轴多点

总览地图 · 总体空间结构（北向图右）

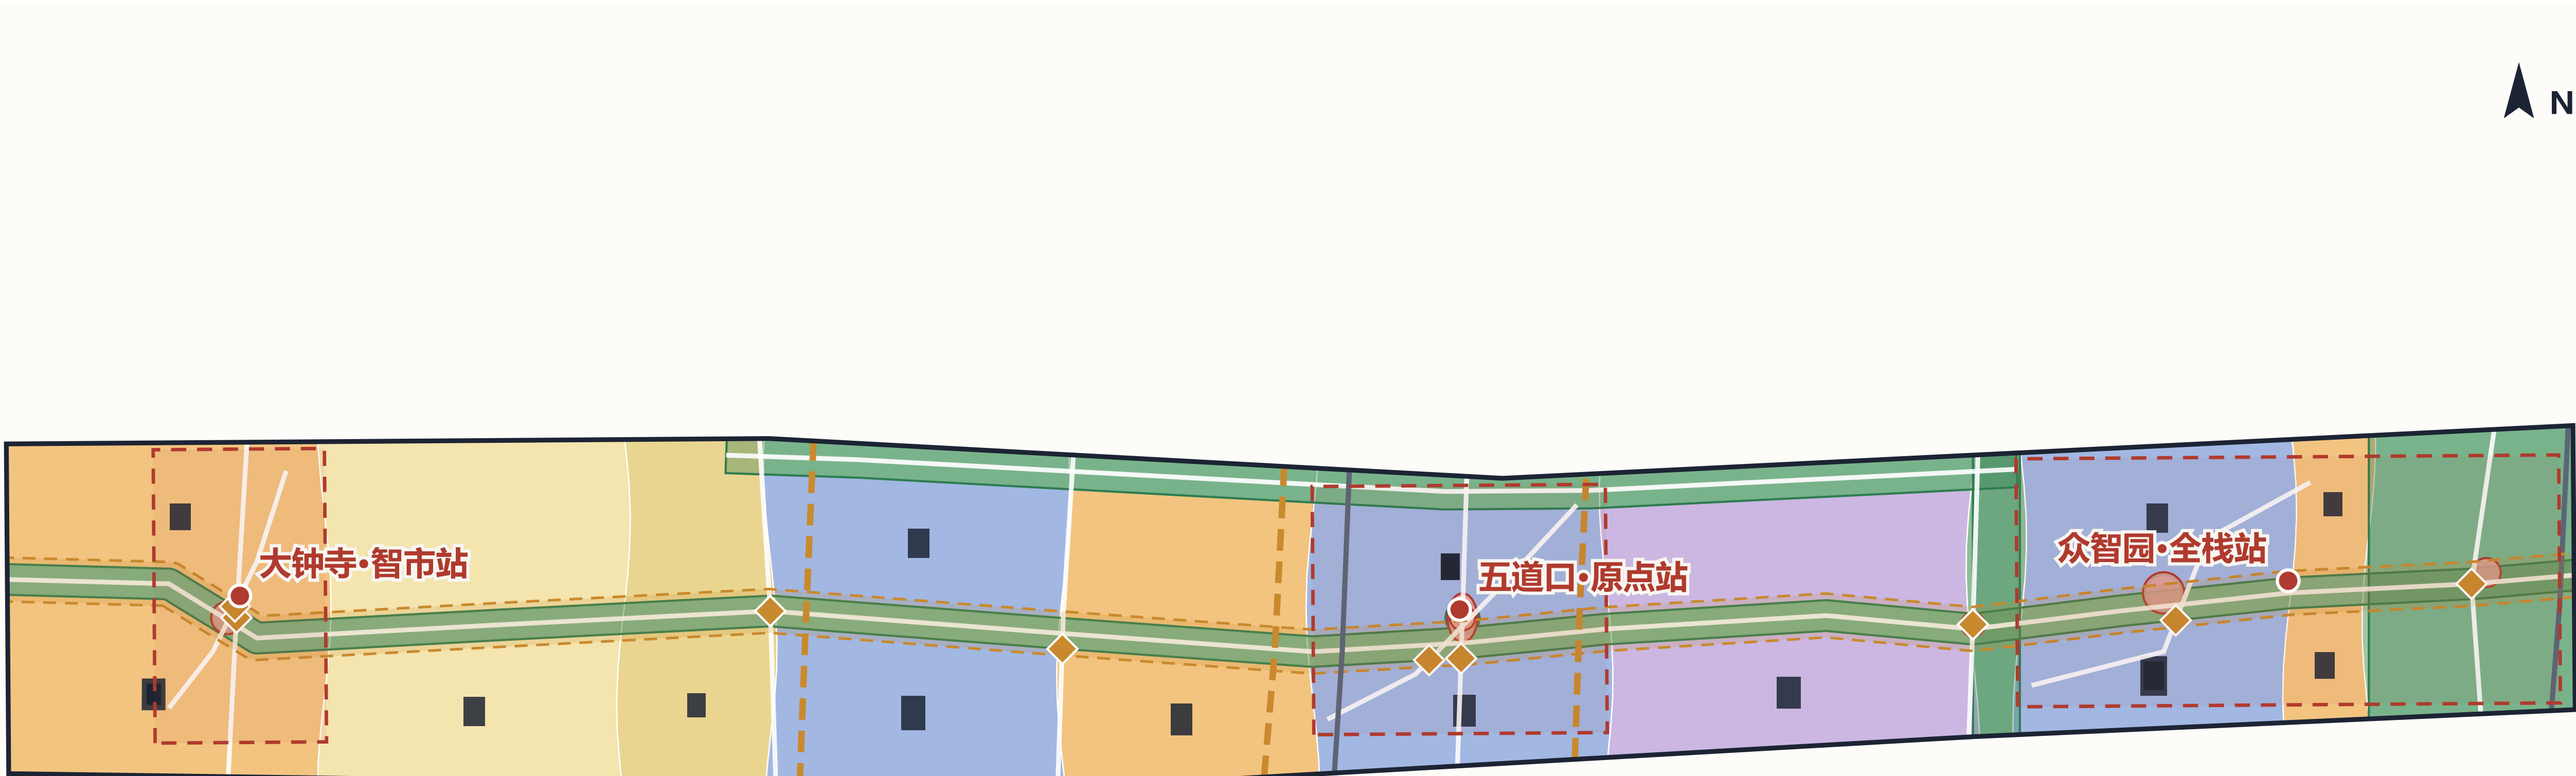

商业服务业 05 256 ha 居住 0701 132 ha 社区服务 0702 66 ha 科研 0802 306 ha 教育 0804 113 ha 公园绿地 1401 245 ha 防护绿地 1402 18 ha 广场 1403 5 ha 既有京张铁路线位（遗产轨线脊） 现状主干道 重点区域（临时约束） 站前广场与公共空间 示范更新建筑基底 蓝绿开敞空间

临时约束边界：本带全部图面与面积指标基于仓库登记的临时范围线，仅供方案讨论与自验；官方边界发布后整体重置。

一轨

京张遗产轨线慢行文化脊：沿 1909 年线位设置约 9.8 公里、宽约 116 米遗产公园脊，慢行、文化展示与 AI 场景复合轴（控规“一带”核心段）。

两河

清河生态客厅（北端约 83.4 公顷滨水界面）× 小月河场景连接绿廊（场地内接驳段，沿东边线内缩约 62 米，河道本体在场地外），衔接控规景观结构“三带”。

六轴多点

六条东西缝合轴（大钟寺/学院路/知春路/五道口/五环上跨/清河流水）响应控规“南北贯通、东西连通”；遗产脊与 9 条横向线路 18 处穿廊交点按“一线一点”设 9 处缝合广场，对位控规“多点”体系。

核心指标

约 1,141.3 公顷

总体设计范围
公估约 11.4 平方公里。临时边界复算一致

23.5%

绿地率（复算）
green_space 图层开集 / 提交范围；口径对照见正文

约 9.8 公里

遗产轨线慢行文化脊
串联三站与全部文化节点

63 个

用地单元
同一切割线平面切分，无缝无重叠全覆盖

19 处

示范性更新建筑
新建 8 + 改造 9 + 保留 2；拆除待现状调查

3 处 / 约 368.4 公顷

重点区域
众智园-原点社区-大钟寺（临时范围）

分期实施

一期

约 748.9 公顷
三站首开区与遗产轨线指示范段

二期

约 167.6 公顷
原点社区从源与清河界面，众智园概念先行区启动

三期

约 224.7 公顷
众智园核心区与两河客厅全面建成

京张1909 · AI创新带

证据与运营 — 可复算、可审计、可迭代

AI+ 场景体系

编号	场景	空间载体	摘要
01	AI慢行导航	遗产轨线脊全线	可解释导航与低侵入传感识别断点与衔接节点，输出人工可复核建议
02	企业服务Copilot	三站服务驿站	政策检索、空间匹配与申报导航，结论附来源与置信度
03	公共安全与活动运营复核	站前广场群	人流与活动风险只微聚合预警，处置决定由人工作出
04	低速无人配送测试	原点社区内街	限定路线、限速、可回退的配送试点，数据分级开放
05	AI文化导览	1909记忆线路	多语导览讲述京张铁路与中关村创新史，史实经文献复核
06	AI健康服务导航	社区服务节点	连接周边医疗与健康资源，不提供诊断结论；医疗等公共服务场所保留现场指导与人工办理通道，传统服务与智能服务并行按图力发（2020）45号政策背景把握（其阶段性目标已到期，仅作参考设计参考）
07	安全治理沙盘（测试）	众智园实验楼	标准制定、可信评测与模型红队测试的可参观协作节点
08	边缘算力驿站（测试）	三站公共服务点	分布式算力与低碳能源融合的新基建原型，供专业团队深化
09	开源发布厅	原点站广场	成果发布、代码贡献展示与小型路演
10	低碳运行监测（测试）	清河凉水客厅	雨洪、能耗与碳排放监测，指标口径公开
11	数据要素会客厅	大钟寺片区	以合规、授权、可审计为前提的数据流通城市界面
12	1909全球活动周路线	一带公共空间	开发者节、场景开放日与朝圣路线的年度运营组合

指标复算

提交范围面积	1,141.3 公顷
蓝绿开敞空间面积	267.9 公顷
蓝绿开敞空间占比	23.5%
公共空间面积	6.3 公顷
公共空间占比	0.6%
示范建筑基底面积	13.0 公顷
示范建筑基底占比（设计值）	1.1%
道路中心线总长	25,471 m
遗产轨线脊长度	9,800 m
一期面积	748.9 公顷
二期面积	167.6 公顷
三期面积	224.7 公顷
重点区域数量	3
用地单元数量	63

数据缺口（待正式数据补齐）：容积率、建筑高度上限、法定建筑密度、法定绿地率管控、退线控制 — 待正式数据补齐

任务覆盖与专业矩阵

- 公告任务 17/17 全覆盖
- 智能体任务 6/6 全覆盖
- 正式设计深度 15/15 完成
- 专业标准响应 9 条（含 3 条非强制新增标准）

来源分层

- SITE-PACKAGE** — 任务书、收单、设计空间、限值、模式与临时边界等场地包材料。
- SOURCE-REGISTRY** — 区分 formal 可用、背景、临时与待审资料的登记册。
- PROCESSED-FACT-PACK** — 范围、任务、资料用途与缺资料清单的导航图，非新权威来源。
- BOUNDARY-SOURCE** — 提交总体设计范围（临时约束），仅用于生成、展示与临时自信。
- KEY-AREA-SOURCE** — 三处重点区域范围（临时约束），仅用于生成、展示与临时自信。
- OFFICIAL-ANNOUNCEMENT** — 公告 1.3/1.4/1.5 的任务、范围、面积、语言与成果最终主控依据。
- AGENT-TASKBOOK** — 十条共创原则、六项智能体任务、场景/品牌/运营要求与边界条款。
- GLOBAL-CASE-BACKGROUND** — 全球创新生态案例为背景研究（匹兹堡、伦敦国王十字、Kista、Kendall Square、深圳南山、杭州城西、慕尼黑 Werksviertel），仅作参考参照，不作为正式证据。
- KG-DRAFT-2024** — 《北京海淀区京张铁路遗址公园沿线（人工智能创新街区重点地区）HD00-1601等街区控制性详细规划（街区层面）（2022-2035年）（草案）》公示图则（北京市规划和自然资源委员会海淀分局，2024-12-20 公示）；空间结构“一带一轴、两心多点”、三大目标定位、规模控制（常住约36.4万人、城乡建设用地约1648.1公顷、建筑规模约2369.3万平方米）、九类主导功能分区、配套设施（公共服务298处等）、整体景观结构“三带六轴、多廊多中心”、交通体系（道路网密度约8.0公里/平方公里、绿色出行80%）等结构性衔接依据。
- KG-APPROVAL-2026** — 北京日报报道（2026-08-12）：市规划自然资源委于 2026-08-11 批复《北京海淀区京张铁路遗址公园沿线（人工智能创新街区重点地区）HD00—1601等街区控制性详细规划（街区层面）（2024年—2035年）》；范围东至新街口外大街、西至中关村大街、北至成府路、南至西直门外大街，共 9 个街区约 1668.2 公顷；以绿色公共空间建设引领区域城市更新，发展大模型、智能体、具身智能等新业态，构建生活圈与创新圈融合的一刻钟社区服务圈。