


开源轨道 OPEN RAIL

京张AI共同体 · 百年京张AI创新带城市设计

板 1 | 总体设计结构

开源轨道 OPEN RAIL · 京张AI共同体

总体概念：一廊·六站·三区·两翼

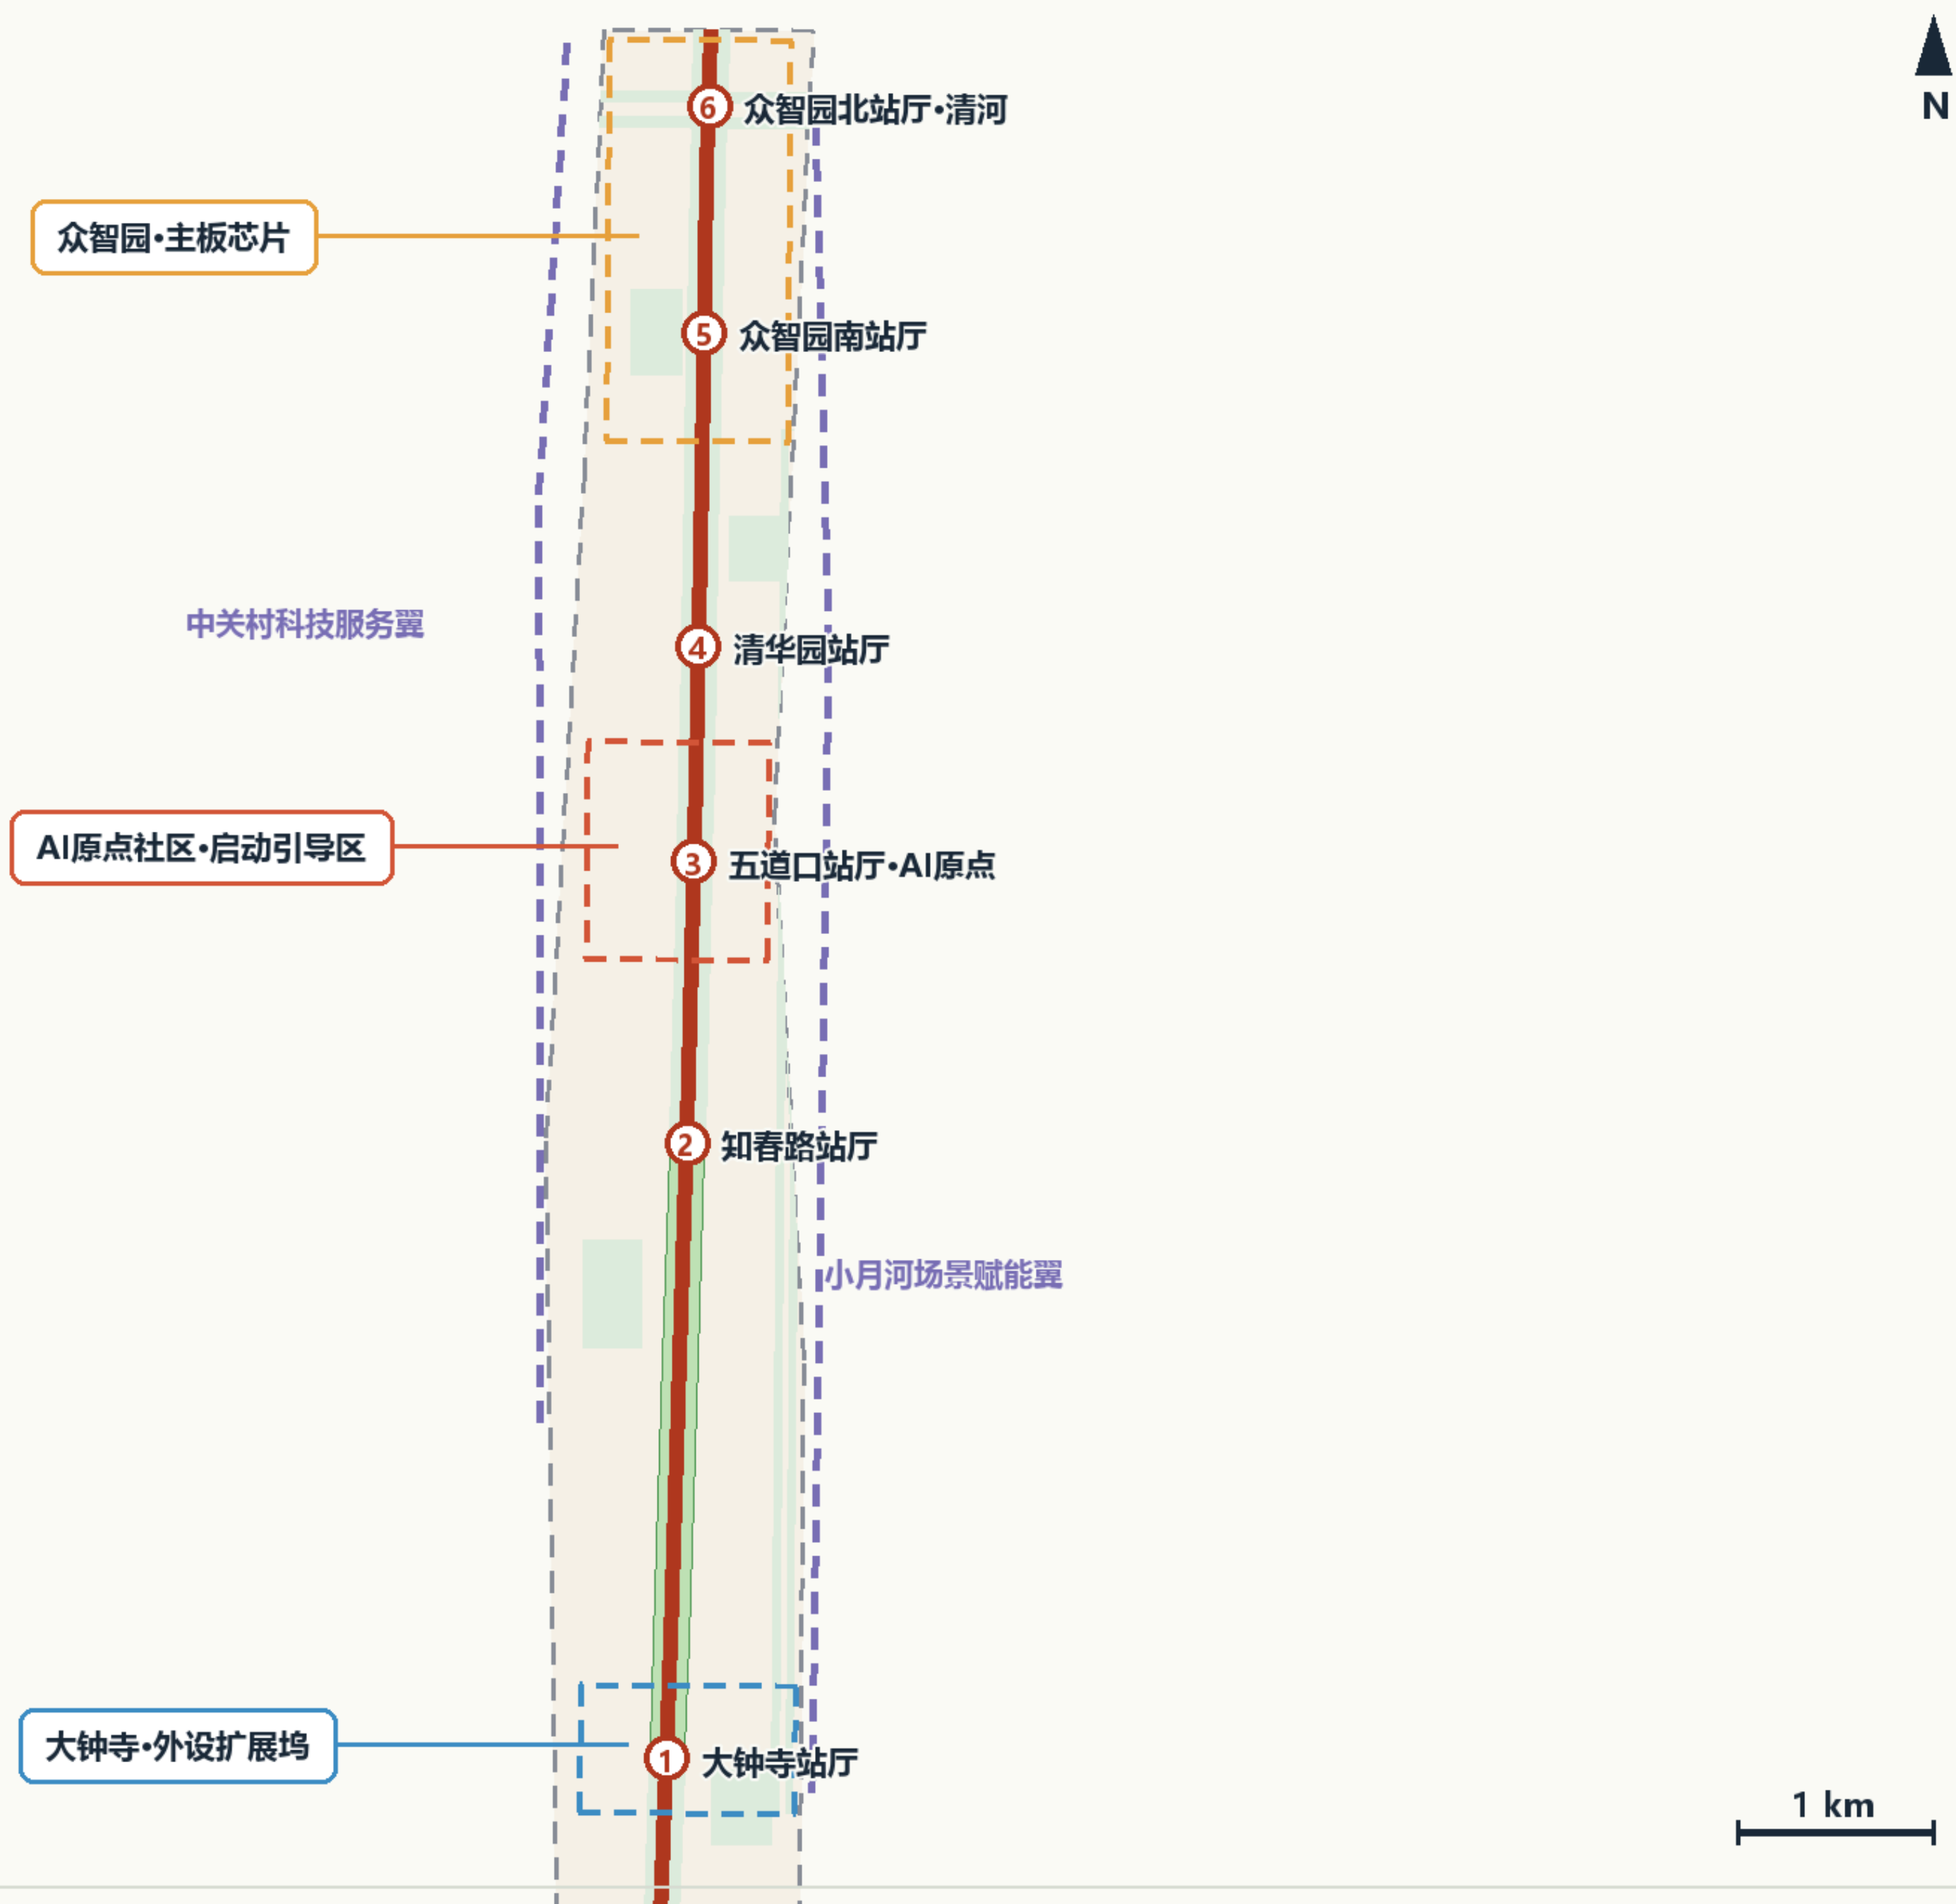

来源：场地包 provisional_boundaries.geojson / 官方公告 / 本方案设计图层 | 面积复算: -EPS:4548 - |
边界：临时粗略边界 (provisional_constraint, 依据公告文字四至推定, 非官方红线)
所有空间落地均为概念建议 / 参考方案, 可供专业团队深化研究

总体概念

一条主线

百年京张铁轨 → 开源步道, 9.7km 连续城市主板

六个站厅

大钟寺/知春路/五道口/清华园/众智园南北, 车站是节点

三区两翼

众智园·原点社区·大钟寺 + 中关村翼/小月河翼

百年转译

詹天佑“人”字铁路 → 开源“人”字网络


AI共同体

开发者、居民、企业与智能体共享的开源城市

一廊 · 六站 · 三区 · 两翼


- 9.7km 遗址廊道 = 城市主板；铁轨 = 数据与慢行总线
- 六站厅：大钟寺/知春路/五道口/清华园/众智园南北
- 三区：众智园(主板芯片)/原点社区(引导区)/大钟寺(扩展坞)
- 两翼：中关村科技服务翼 + 小月河场景赋能翼

概念建议 · 临时边界 (provisional), 非官方红线

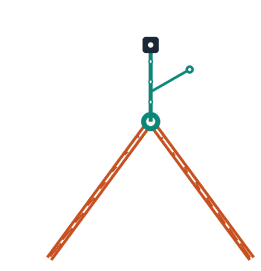

开源轨道 OPEN RAIL · 京张AI共同体

用地结构与空间传导：廊道为轴、地块为群

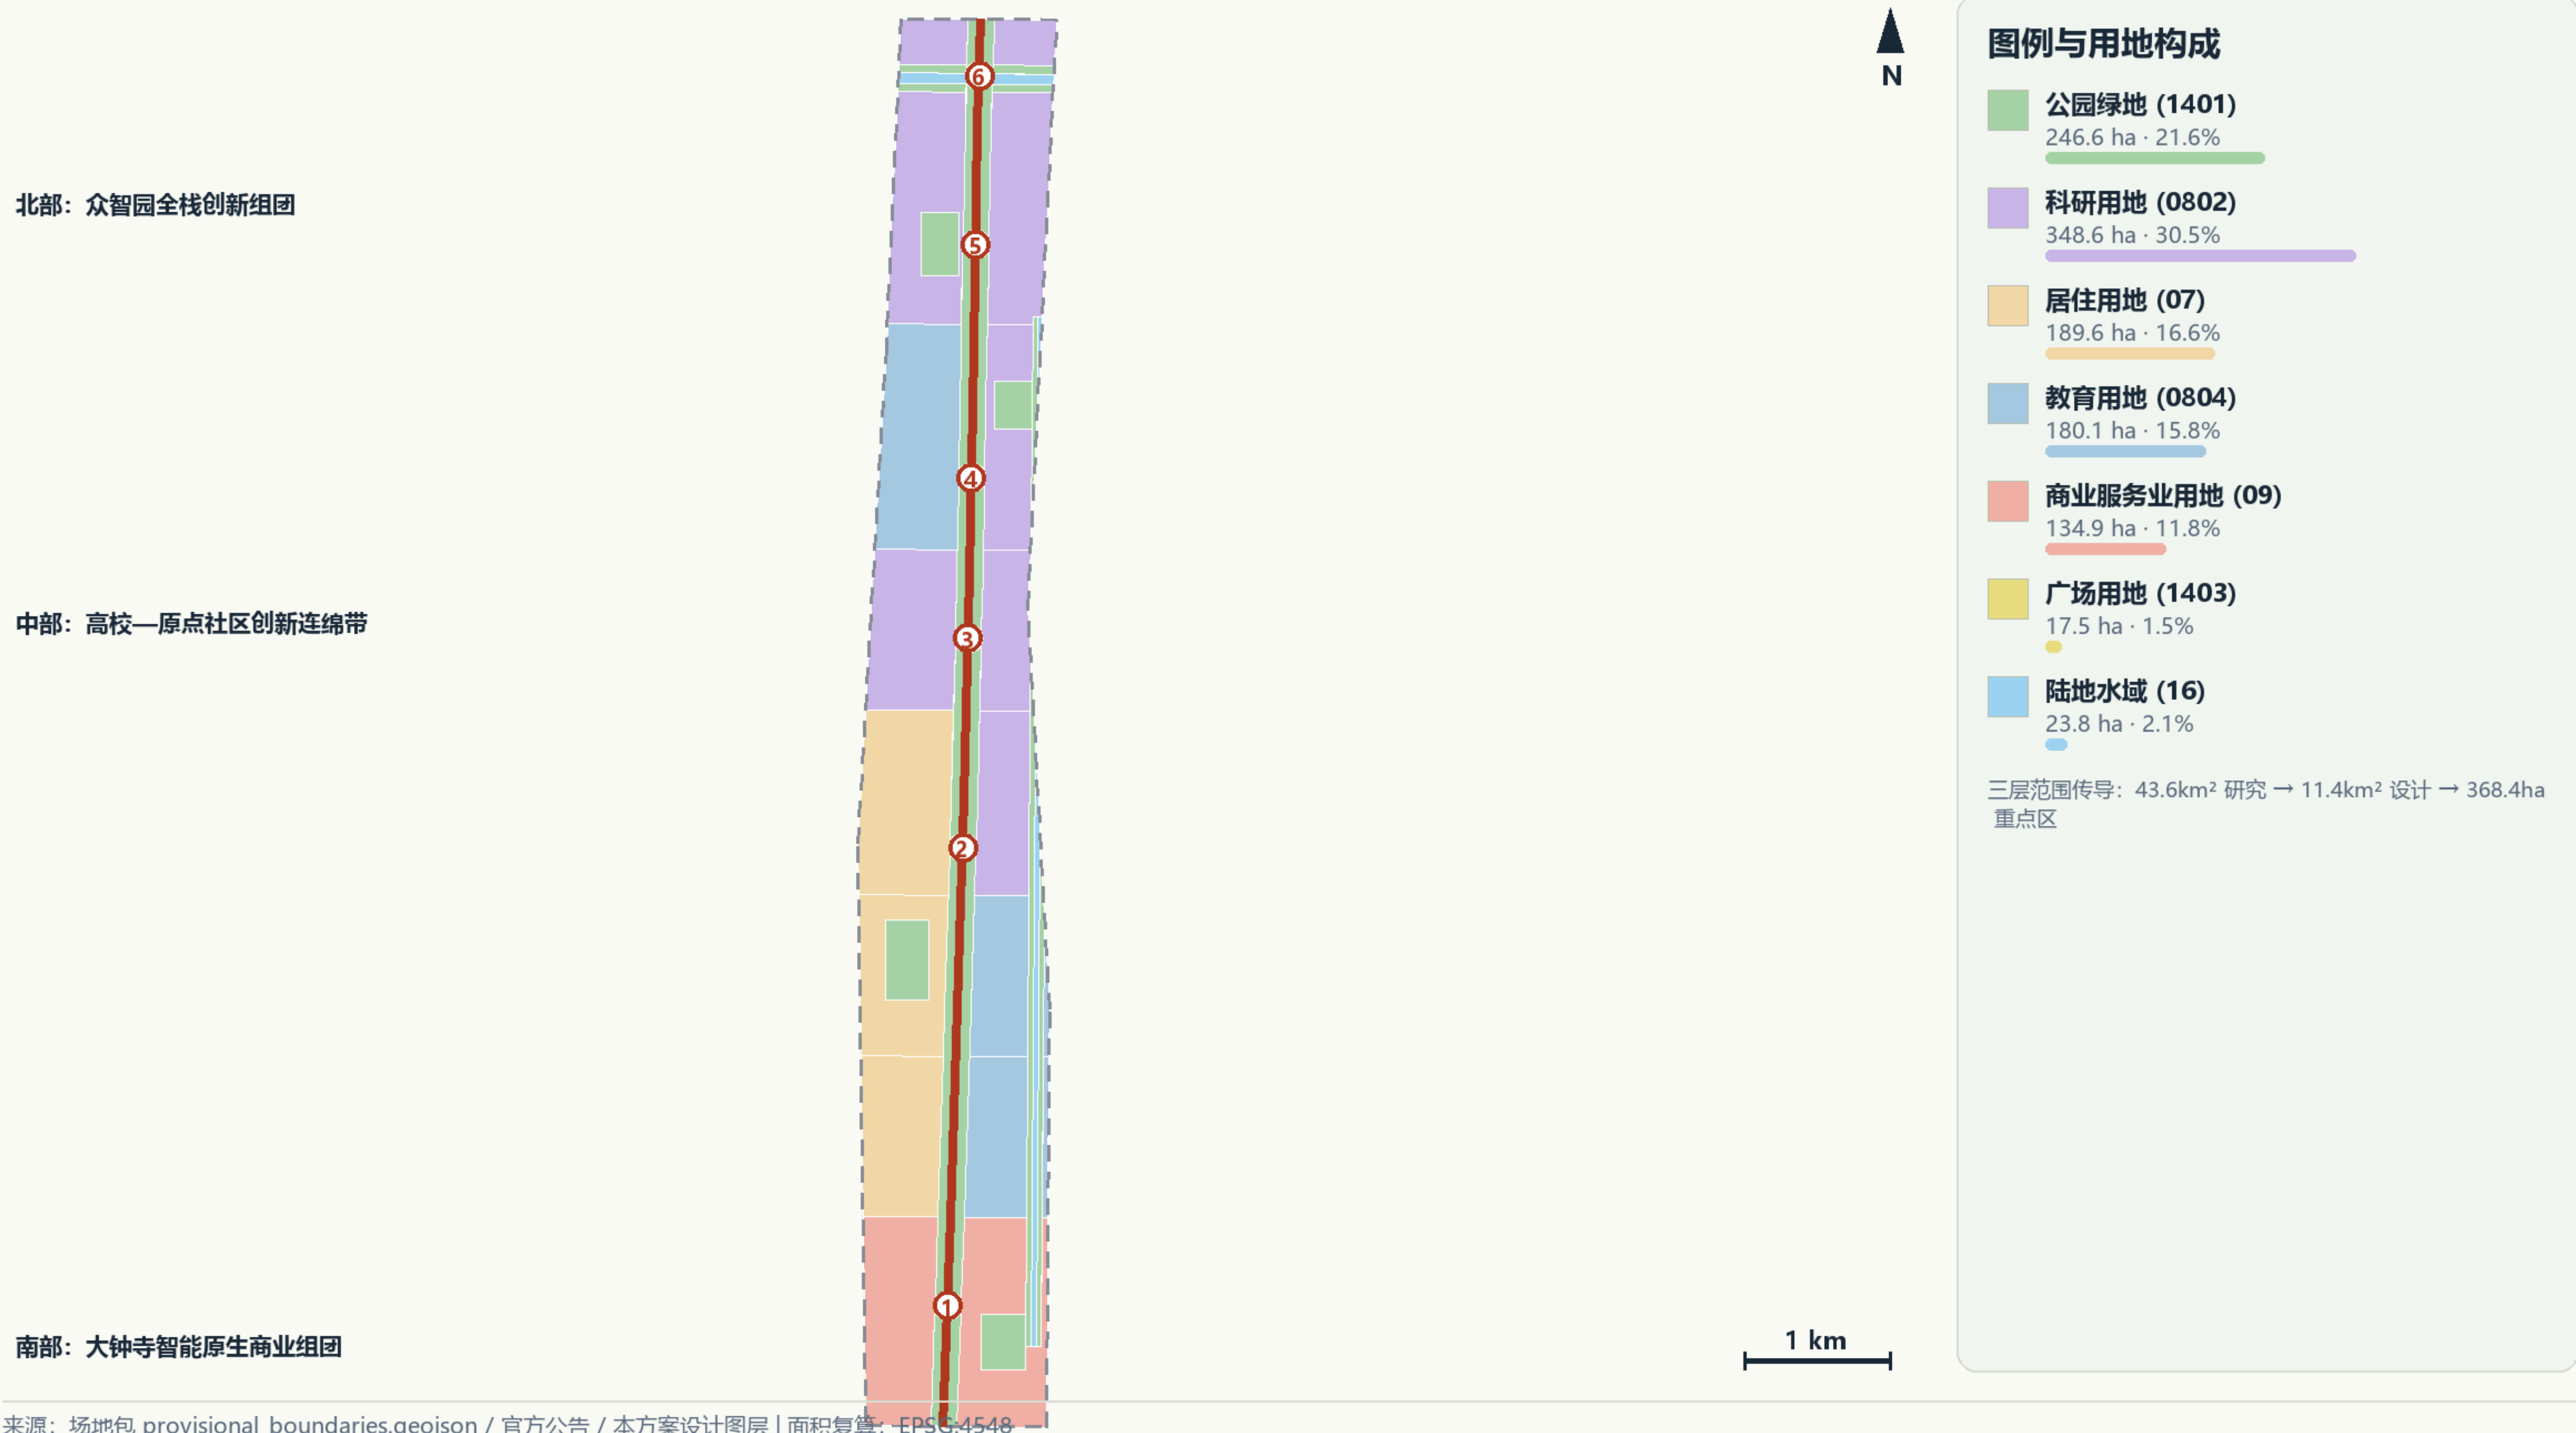

来源：场地包 provisional_boundaries.geojson / 官方公告 / 本方案设计图层 | 面积复算：EPS 6.4548


边界：临时粗略边界（provisional_constraint，依据公告文字四至推定，非官方红线）

所有空间落地均为概念建议 / 参考方案，可供专业团队深化研究

用地构成（复算）

用地	ha	%
科研 0802	348.6	30.5
绿地 1401	246.6	21.6
居住 07	189.6	16.6
教育 0804	180.1	15.8
商业 09	134.9	11.8

更新框架：中部居住以留为主，高校界面以改为主，三重重点区留改拆结合；地块级分类待现状底数。

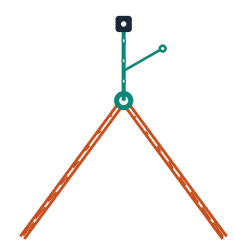


开源轨道 OPEN RAIL

京张AI共同体 · 百年京张AI创新带城市设计

板 3 | 交通、轨道、慢行与市政支撑

开源轨道 OPEN RAIL · 京张AI共同体

交通慢行 × 蓝绿网络：三线织补、两河串珠

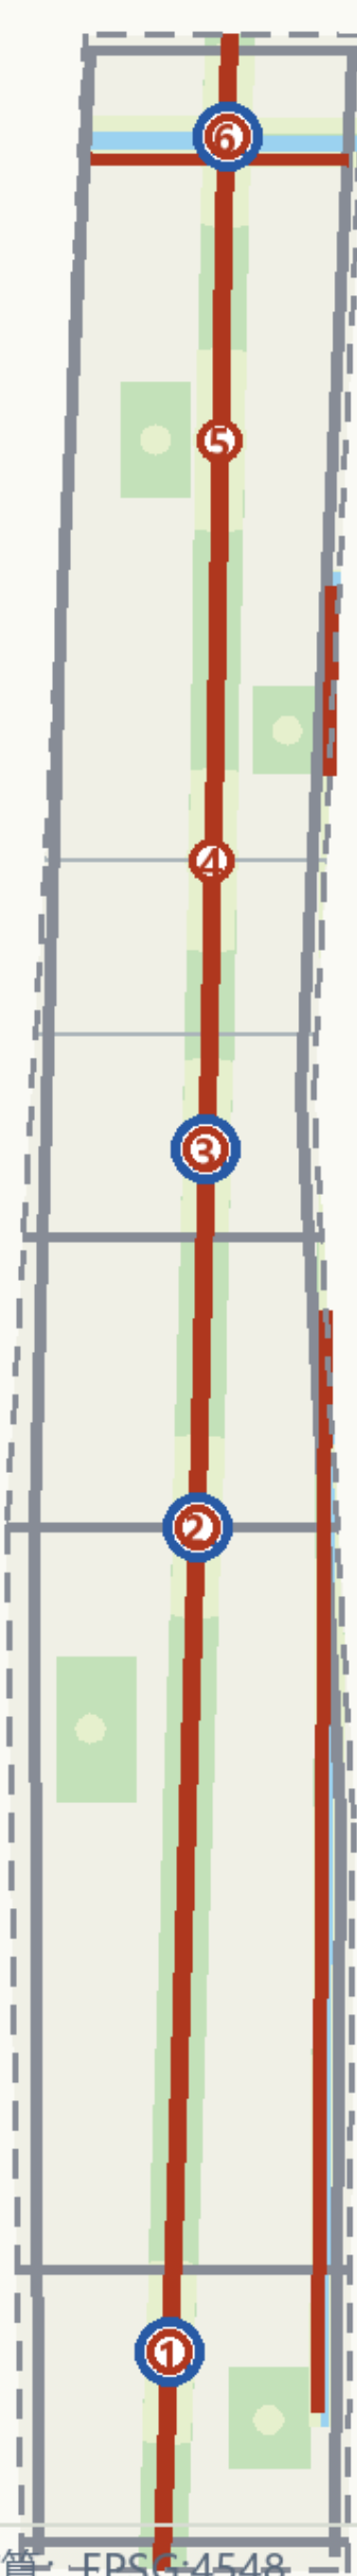

图例与系统要点

- 开源步道 京张遗址慢行主线 9.7km
- 轨道站点一体化 (M, 概念接驳)
- 城市干路界面 (西土城-学院路/荷清路等)
- 清河 / 小月河水面
- 遗址廊道与滨水绿带
- 公共空间网络 (站厅广场/活力段/滨水界面)

· 慢行断点织补：跨干路 6 处站厅节点全龄友好接驳

· 蓝绿连续：廊道—清河—小月河构成 N 字形生态骨架

· AI 场景节点沿主轴布置，步行 5 分钟可达站厅

· 轨道线位/道路红线以官方为准，本图为概念组织


来源：场地包 provisional_boundaries.geojson / 官方公告 / 本方案设计图层 | 面积复算: EPS 6.4548

边界：临时粗略边界 (provisional_constraint, 依据公告文字四至推定, 非官方红线)

所有空间落地均为概念建议 / 参考方案, 可供专业团队深化研究

三线织补 · 两河串珠

- 开源步道 9.72km：步行+骑行主线，六站厅全龄接驳
- 轨道一体化：大钟寺/知春路/五道口/上地（概念接驳）
- 端侧算力节点进公园；分布式能源+海绵设施结合滨水绿带
- 轨道线位与道路红线以官方为准

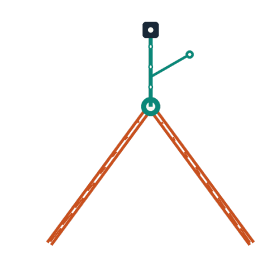

蓝绿骨架


- 主线廊道 156.7 万㎡ 连续公园绿地
- 清河/小月河滨水绿带 + 4 社区公园
- 绿地率 21.61%（设计模型值）

公共空间网络

- 6 站厅广场 + 6 段廊道活力段
- 滨水开放空间 + 5 口袋广场
- 公共空间率 10.56%（不与绿地率相加）


AI 朝圣地标

- 开发者散步道（全线）
- 智能体贡献荣誉墙（清华园）
- 开源成果展示廊（清华园）
- AI原点纪念碑（五道口）

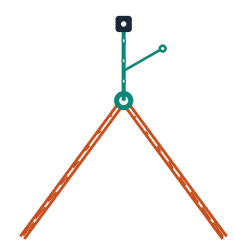

开源轨道 OPEN RAIL · 京张AI共同体

三处重点区域：定位差异 · 空间抓手 · 风险条件

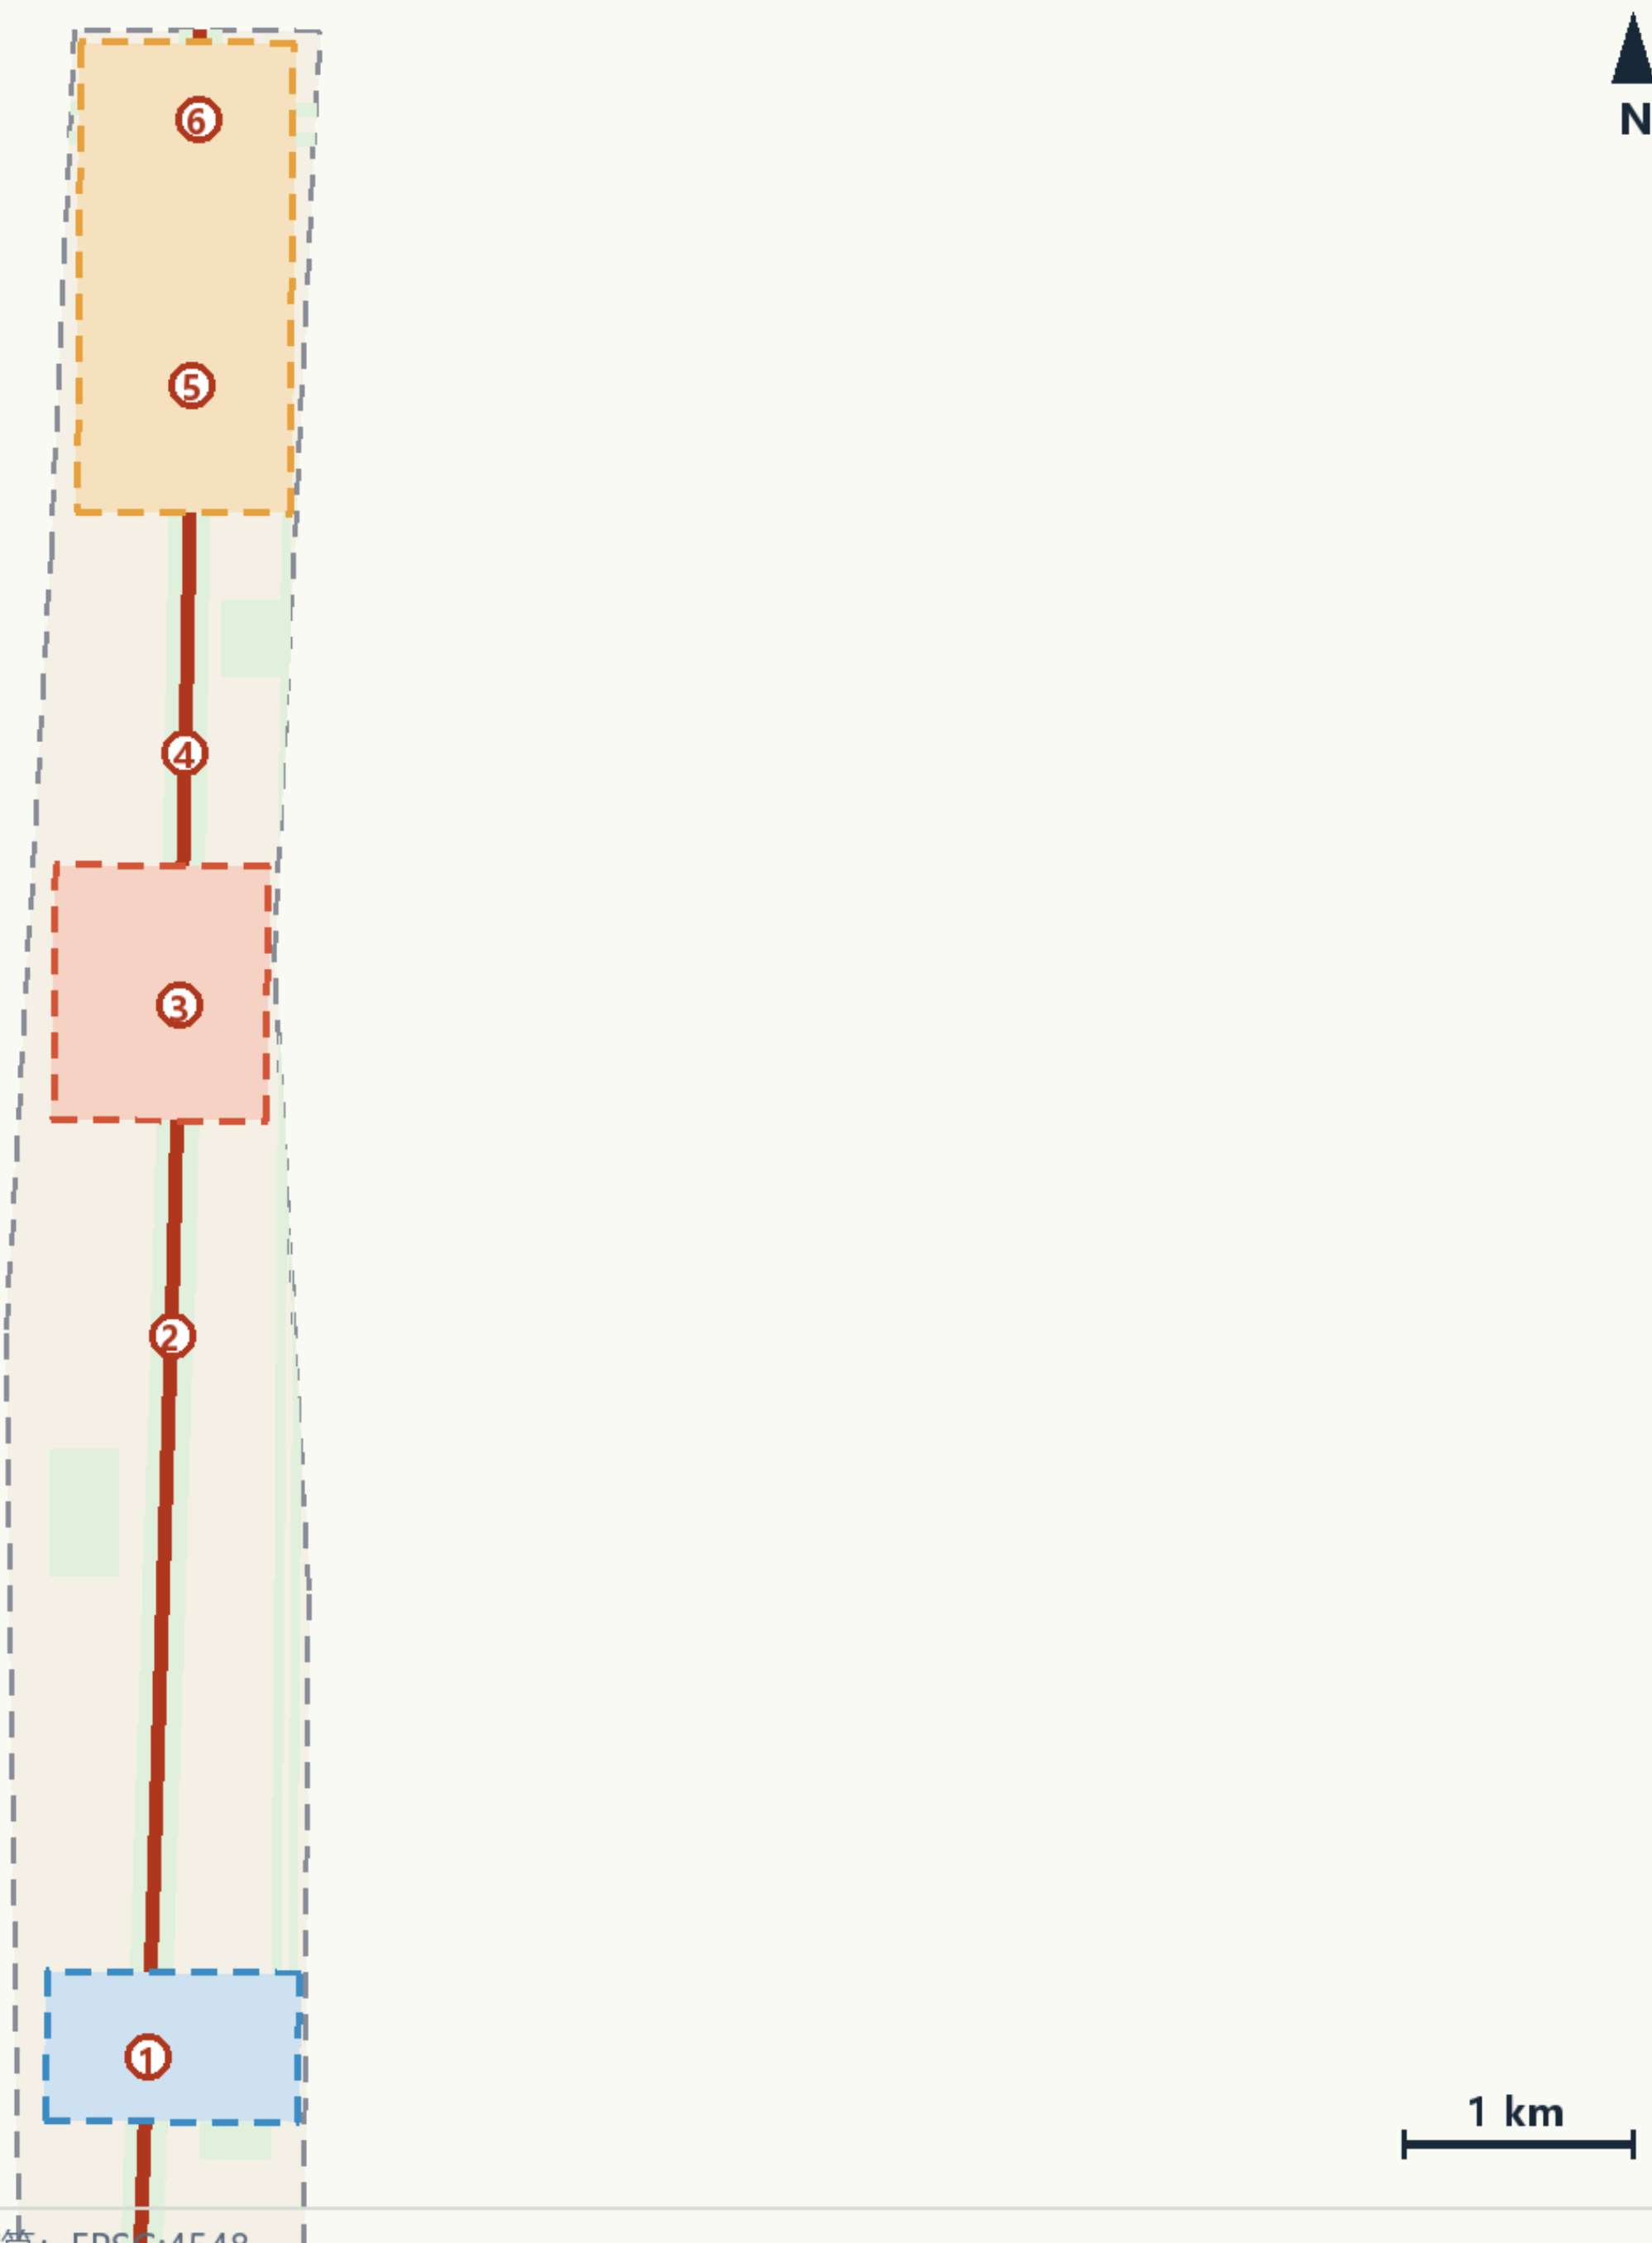

来源：场地包 provisional_boundaries.geojson / 官方公告 / 本方案设计图层 | 面积复算: 4548
边界：临时粗略边界 (provisional_constraint, 依据公告文字四至推定, 非官方红线)
所有空间落地均为概念建议 / 参考方案, 可供专业团队深化研究

重点区域详细设计

众智园AI自主创新加速区

主板芯片 · 全栈自主创新体系

约192.1ha (公告口径)

- 全栈算力—模型—工具链院落
- AI治理标准试验场
- 中央绿谷开放创新界面

空间落地均为概念建议, 须待官方精确边界与控规条件后深化

北京AI原点社区

启动引导区 · 世界级AI创新生态

约104.3ha (公告口径)

- 清华园站厅-开源成果展示廊
- 开发者混合创新街区
- 五道口站厅国际交往门户

空间落地均为概念建议, 须待官方精确边界与控规条件后深化

大钟寺AI产业聚集区

外设扩展坞 · 智能原生新业态

约72.0ha (公告口径)


- 智能原生消费与商务场景
- 大钟寺站厅城市展示窗口
- AI+商业测试验证街区

空间落地均为概念建议, 须待官方精确边界与控规条件后深化

定位差异与空间抓手

重点区	定位	抓手
众智园 192.1 ha	主板芯片	全栈院落 · 治理试验场 · 绿谷
原点社区 104.3 ha	启动引导区	展示廊 · 开发者街区 · 门户
大钟寺 72.0 ha	扩展坞	智能原生商业 · 测试街区

空间落地均为概念建议, 待官方边界与控规条件深化。

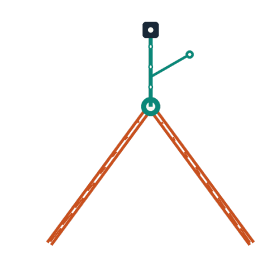

13 张场景卡（3 测试验证须许可）

- AI+交通慢行
- AI文化游览
- AI健康导航
- 企业副驾
- 安全复盘
- 测试:机器人配送
- AI+开放课堂
- AI+商业导购
- 算力公测
- 公园养护
- 测试:自动接驳
- 测试:治理沙箱

画像（6 类）


研究员/开发者/高校师生/居民/访客/长者与无障碍需求者；公共空间组件库 10 类可组合

年度活动

春大会/夏测试季/秋文化季/冬贡献年会

分期

近期南段示范 → 中期北段+众智园南 → 远期众智园北+清河

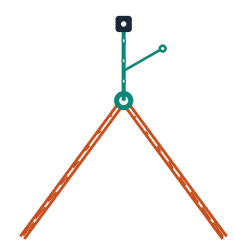

开源轨道 OPEN RAIL

京张AI共同体 · 百年京张AI创新带城市设计

板 7 | 指标复核与合规响应

11,412,825

m² 设计范围

21.61%

绿地率

10.56%

公共空间

1107

概念基底

9.72 km


主线

23

合规条目全覆盖

开源轨道 OPEN RAIL · 京张AI共同体

指标复算与证据链：所有数字可从包内几何重算

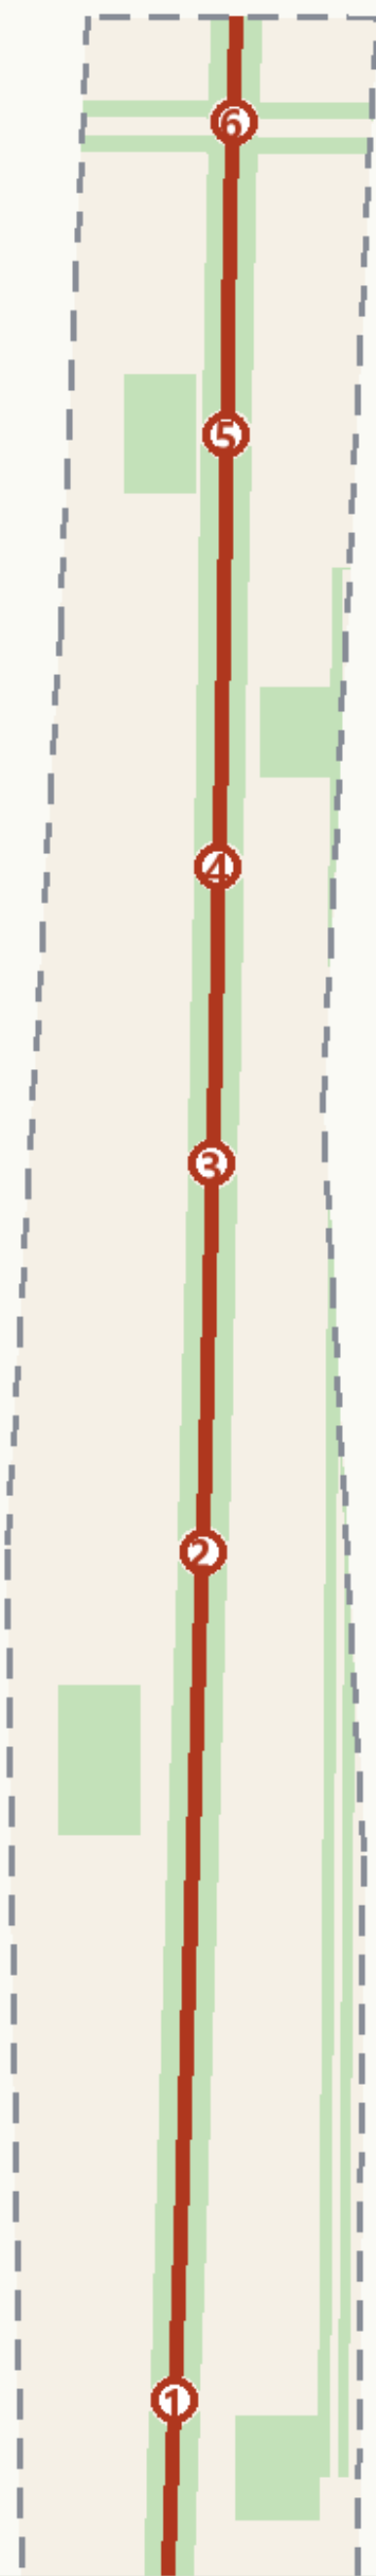

N

核心指标卡

总体设计范围面积

11,412,825 m²

≈ 11.41 km² (公告口径 11.4 km², 偏差 0.11%)

□ site_boundary.geojson → polygon_area(EPSG:4548)

绿地率 green_ratio

21.61%

绿地 246.6 ha / 总用地

□ green_space → site_boundary

公共空间率 public_space_ratio

10.56%

公共空间 120.6 ha / 总用地

□ public_space → site_boundary

建筑基底面积 (概念量)

221.6 ha

1107 个基底 · 基底率 19.4%

□ buildings.geojson 求和

开源主线长度

9.72 km

六站厅串联 · 步行约 2 小时

□ roads.geojson 中线长度

重点区域

3 处 · 368.4 ha

众智园 192.1 / 原点社区 104.3 / 大钟寺 72.0 (公告口径)

□ key_areas.geojson

来源：场地包 provisional_boundaries.geojson / 官方公告 / 本方案设计图层 | 面积复算: EPSG:4548


边界：临时粗略边界 (provisional_constraint, 依据公告文字四至推定, 非官方红线)

所有空间落地均为概念建议 / 参考方案, 可供专业团队深化研究 | 证据链: GeoJSON 图层 → EPSG:4548 复算 → metrics.json → 本图与 visual/index.html data-value 一致; 容积率/高度等待官方控规补齐 (status=unknown)

证据链

- GeoJSON → EPSG:4548 复算 → metrics.json → 图纸/展示页一致
- 合规矩阵 23 条全覆盖; 标准矩阵覆盖强制标准; 深度 15 项 complete
- 容积率/高度: unknown, 待官方控规
- 自检四门全过后方可提交 (见 self_check.json)

概念建议 / 参考方案 · 不替代正式规划 · 不构成政府审定结论

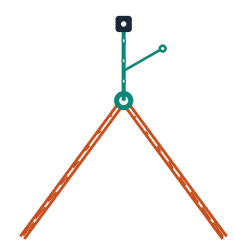

开源轨道 OPEN RAIL

京张AI共同体 · 百年京张AI创新带城市设计


板 8 | 场所设计深化与实施治理

开源轨道 OPEN RAIL · 京张AI共同体

六站厅场所意象：从概念条带到可感场所（概念剖面示意）

大钟寺站厅


■ 外设扩展坞 · 测试街区

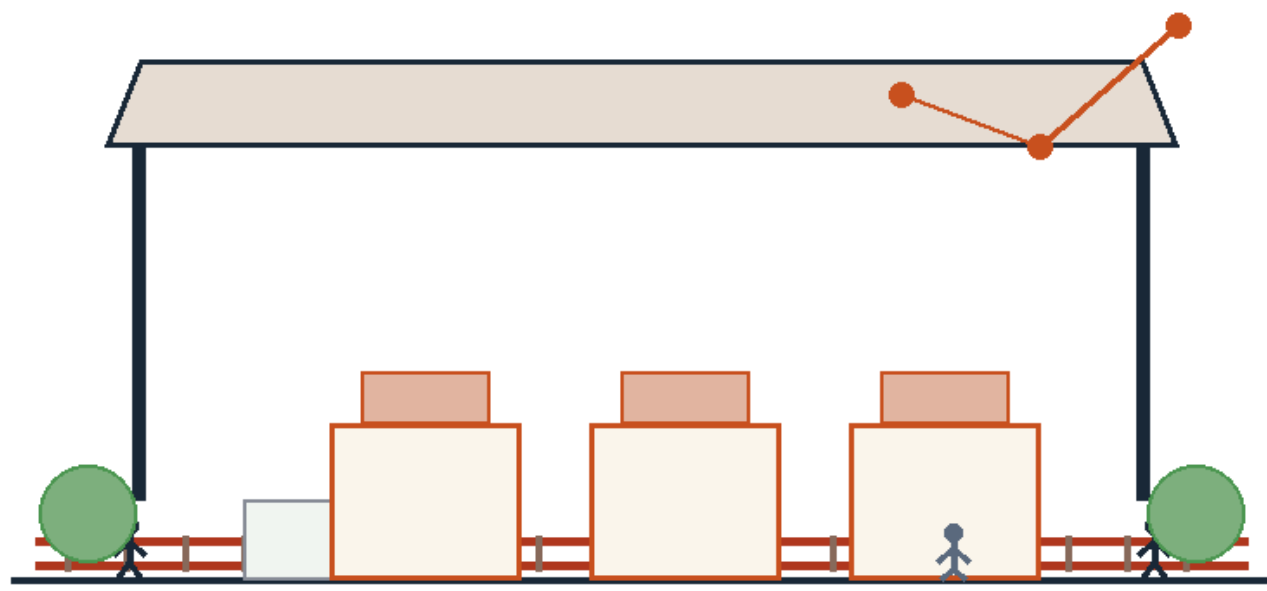

概念剖面 · 比例示意

知春路站厅


■ 全时服务 · 社区补给

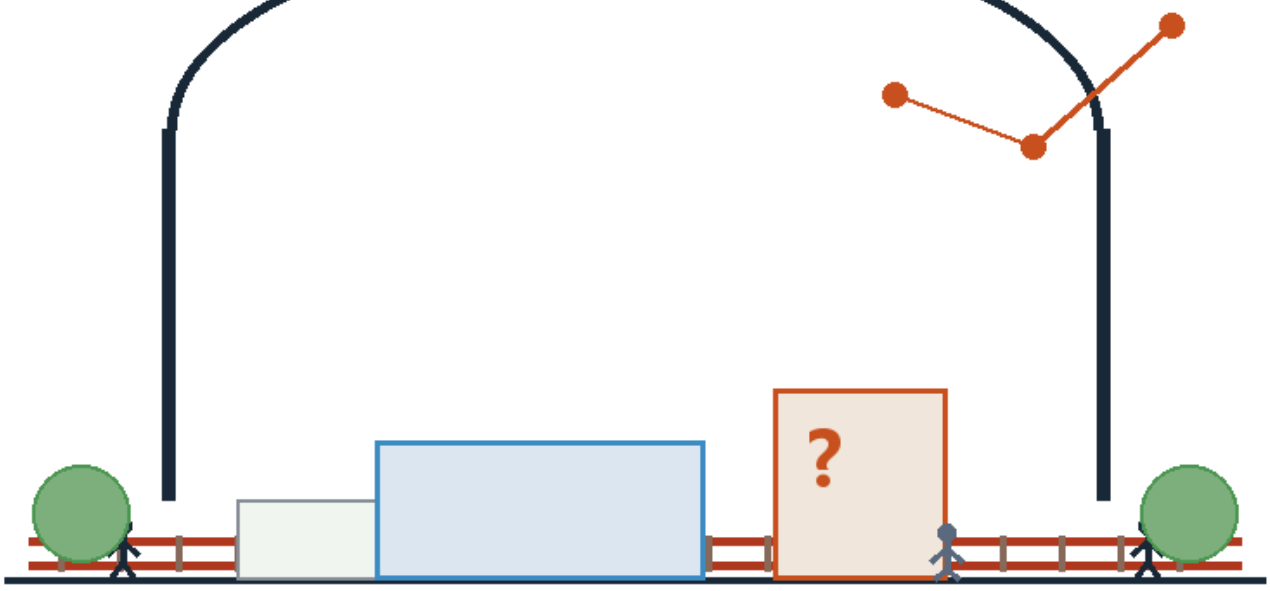

概念剖面 · 比例示意

五道口站厅·AI原点


■ 原点广场 · 城市客厅

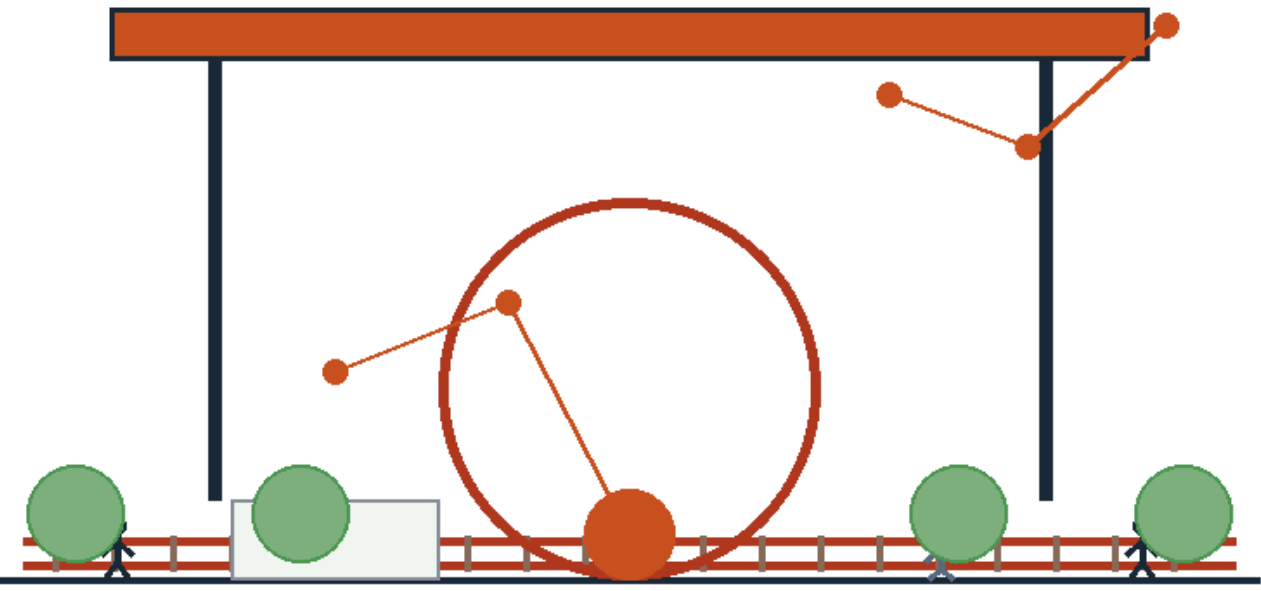

概念剖面 · 比例示意

清华园站厅


■ 遗产展示 · 荣誉长墙

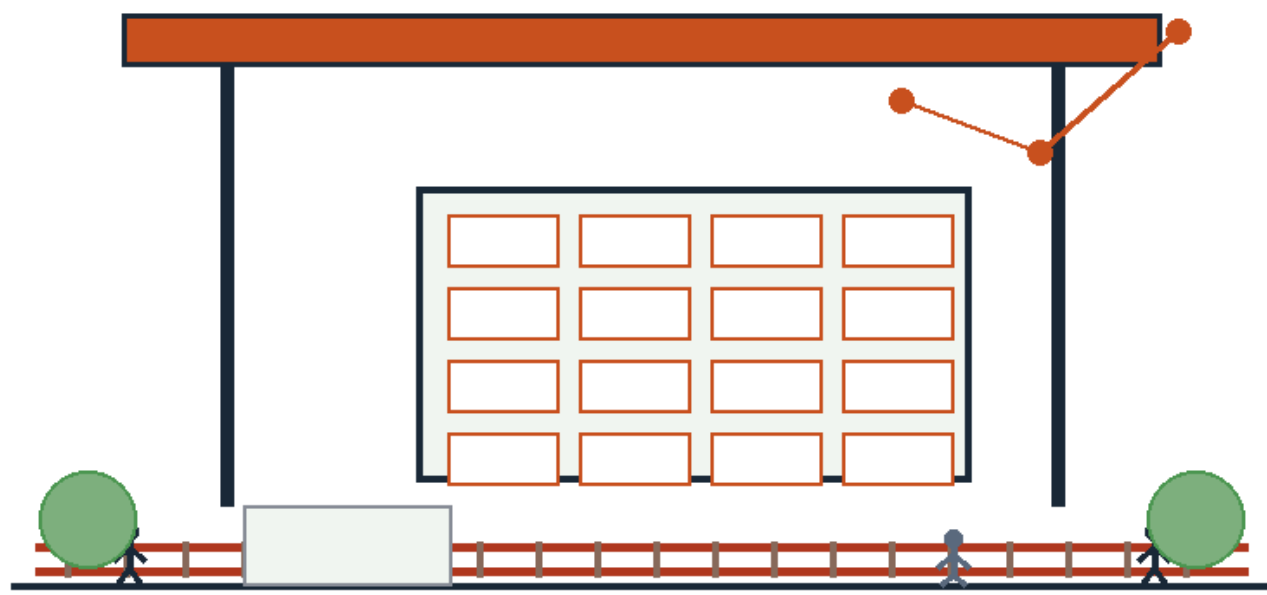

概念剖面 · 比例示意

众智园南站厅


■ 主极客厅 · 共享实验

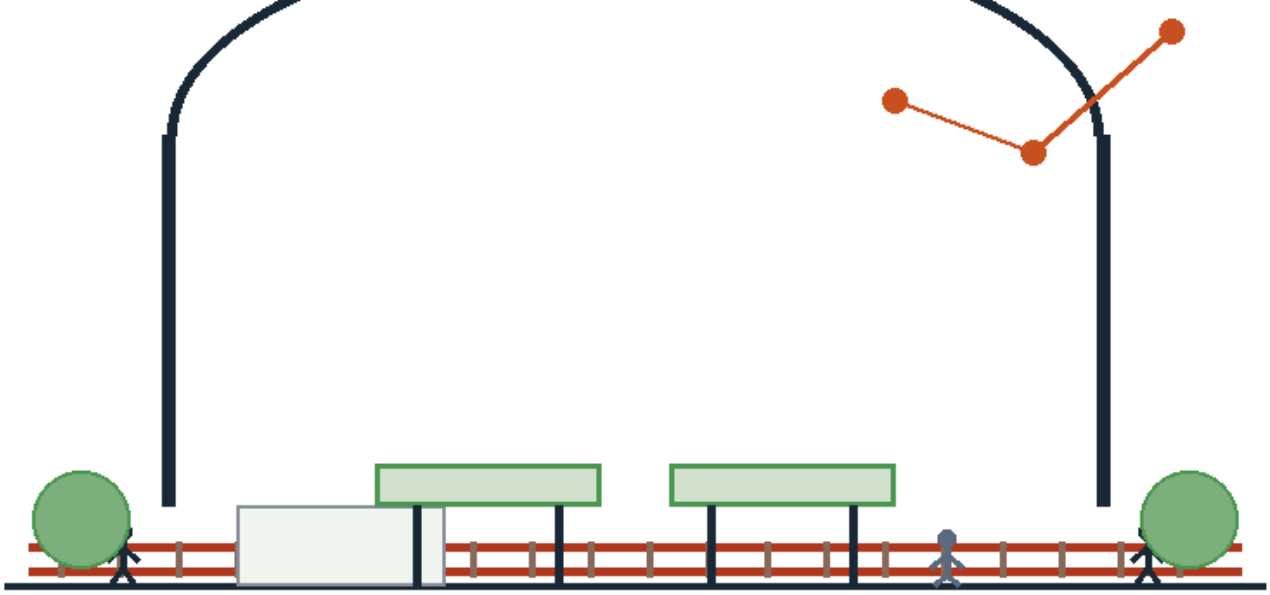

概念剖面 · 比例示意

众智园北站厅·清河

■ 北门户 · 换乘接驳

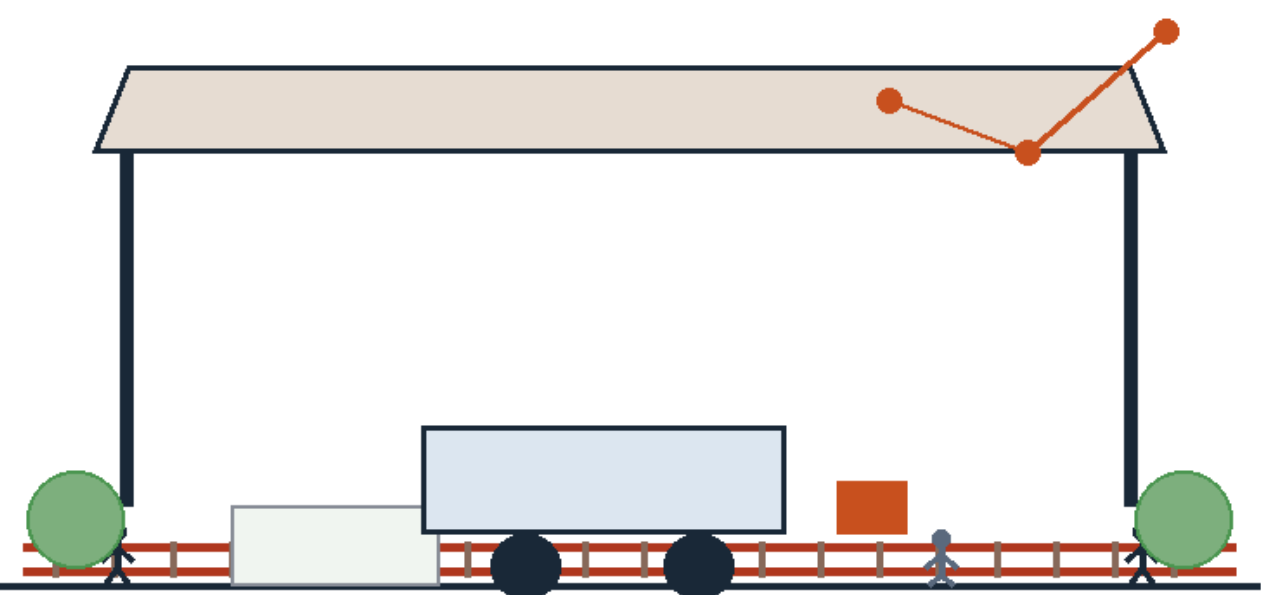


概念剖面 · 比例示意

概念性场所设计示意，非工程图纸，总体边界为 provisional（非官方红线），实施前须经控规校核与专业深化

开源轨道 OPEN RAIL · 京张AI共同体

众智园「commit 广场」节点放大平面：场所设计深化（概念示意）

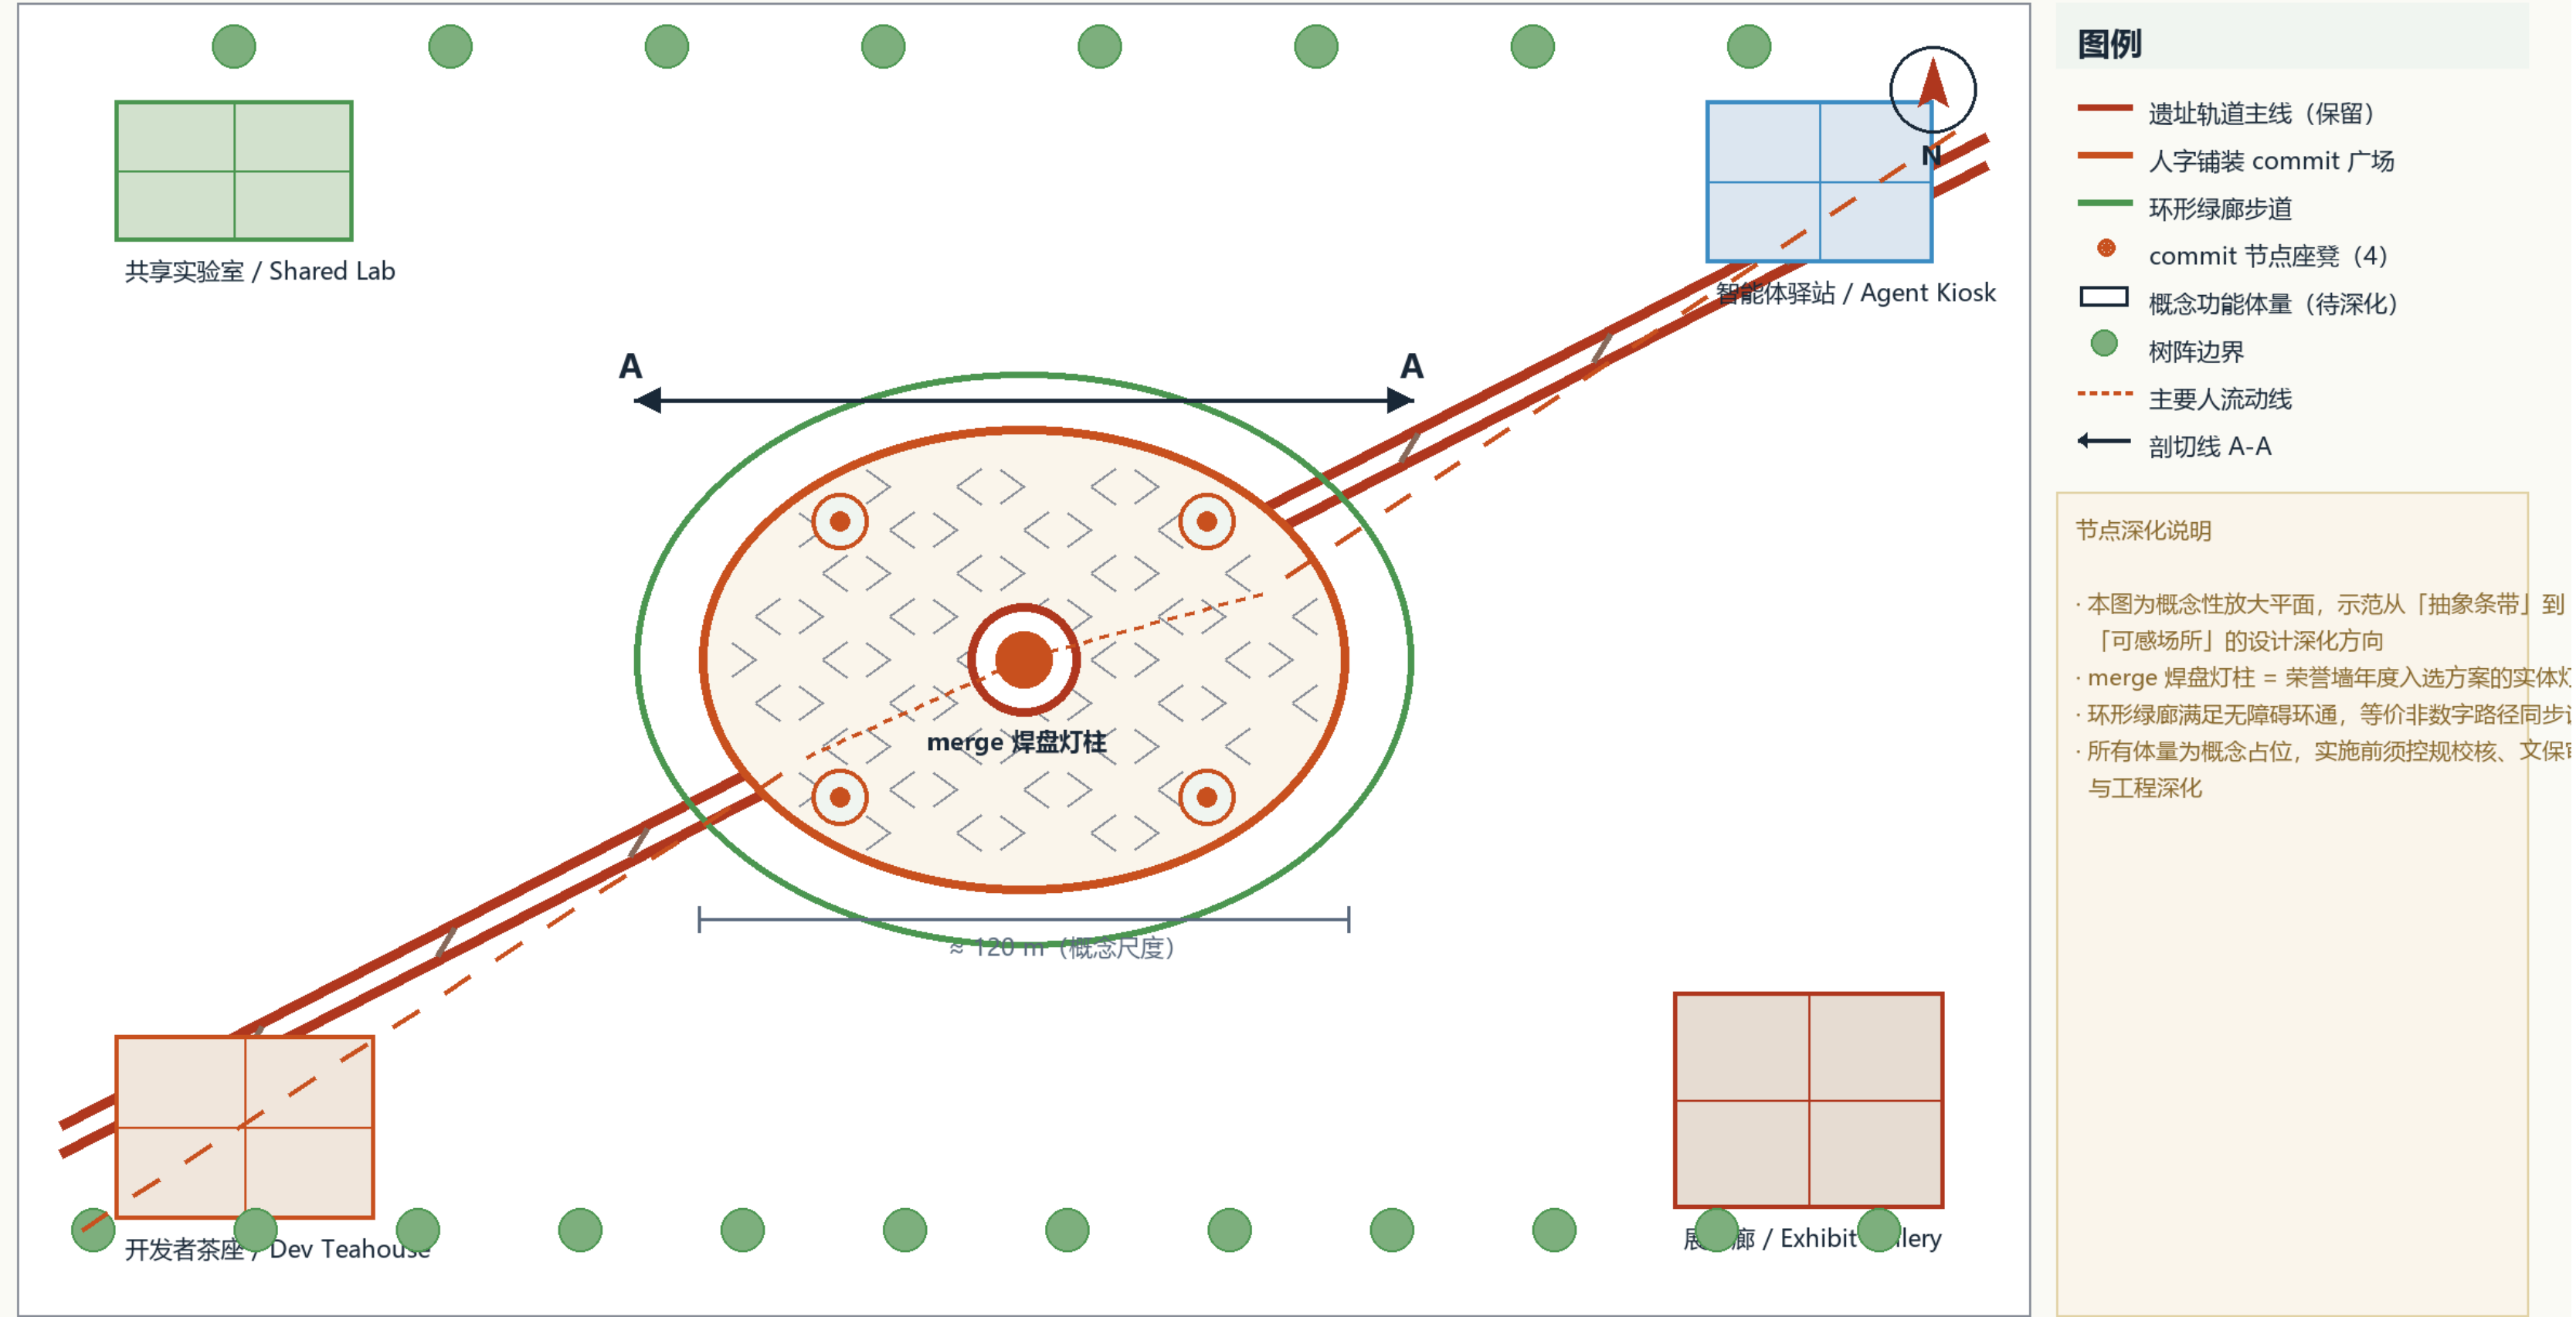

概念性场所设计示意，非工程图纸，总体边界为 provisional（非官方红线），实施前须经控规校核与专业深化

场所深化（概念）


- 六站厅概念剖面：从条带到场所
- 品牌应用：铺装/栏杆/座椅/灯柱/地刻
- commit 广场放大平面（概念占位体量）

资金类型（建议）

- 市区财政与专项 / 市场主体投资
- 产业基金 / 公益基金会 / 社区微更新
- 运营收益反哺（复审公开）

基线测量协议

- P1 无障碍覆盖率 / P2 等价路径 / P3 响应时长
- P4 慢行断点 / P5 第三方无障碍审查
- 失败样本全保留；无实测 = 待基线

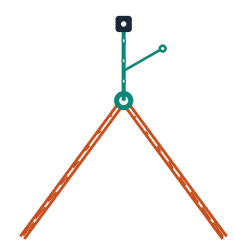


开源轨道 OPEN RAIL

京张AI共同体 · 百年京张AI创新带城市设计

板 9 | 沿街界面、节点构造与排序方法论

开源轨道 OPEN RAIL · 京张AI共同体


沿街建筑界面与典型街道剖面：三类街道断面 + 底层界面节奏（概念示意）

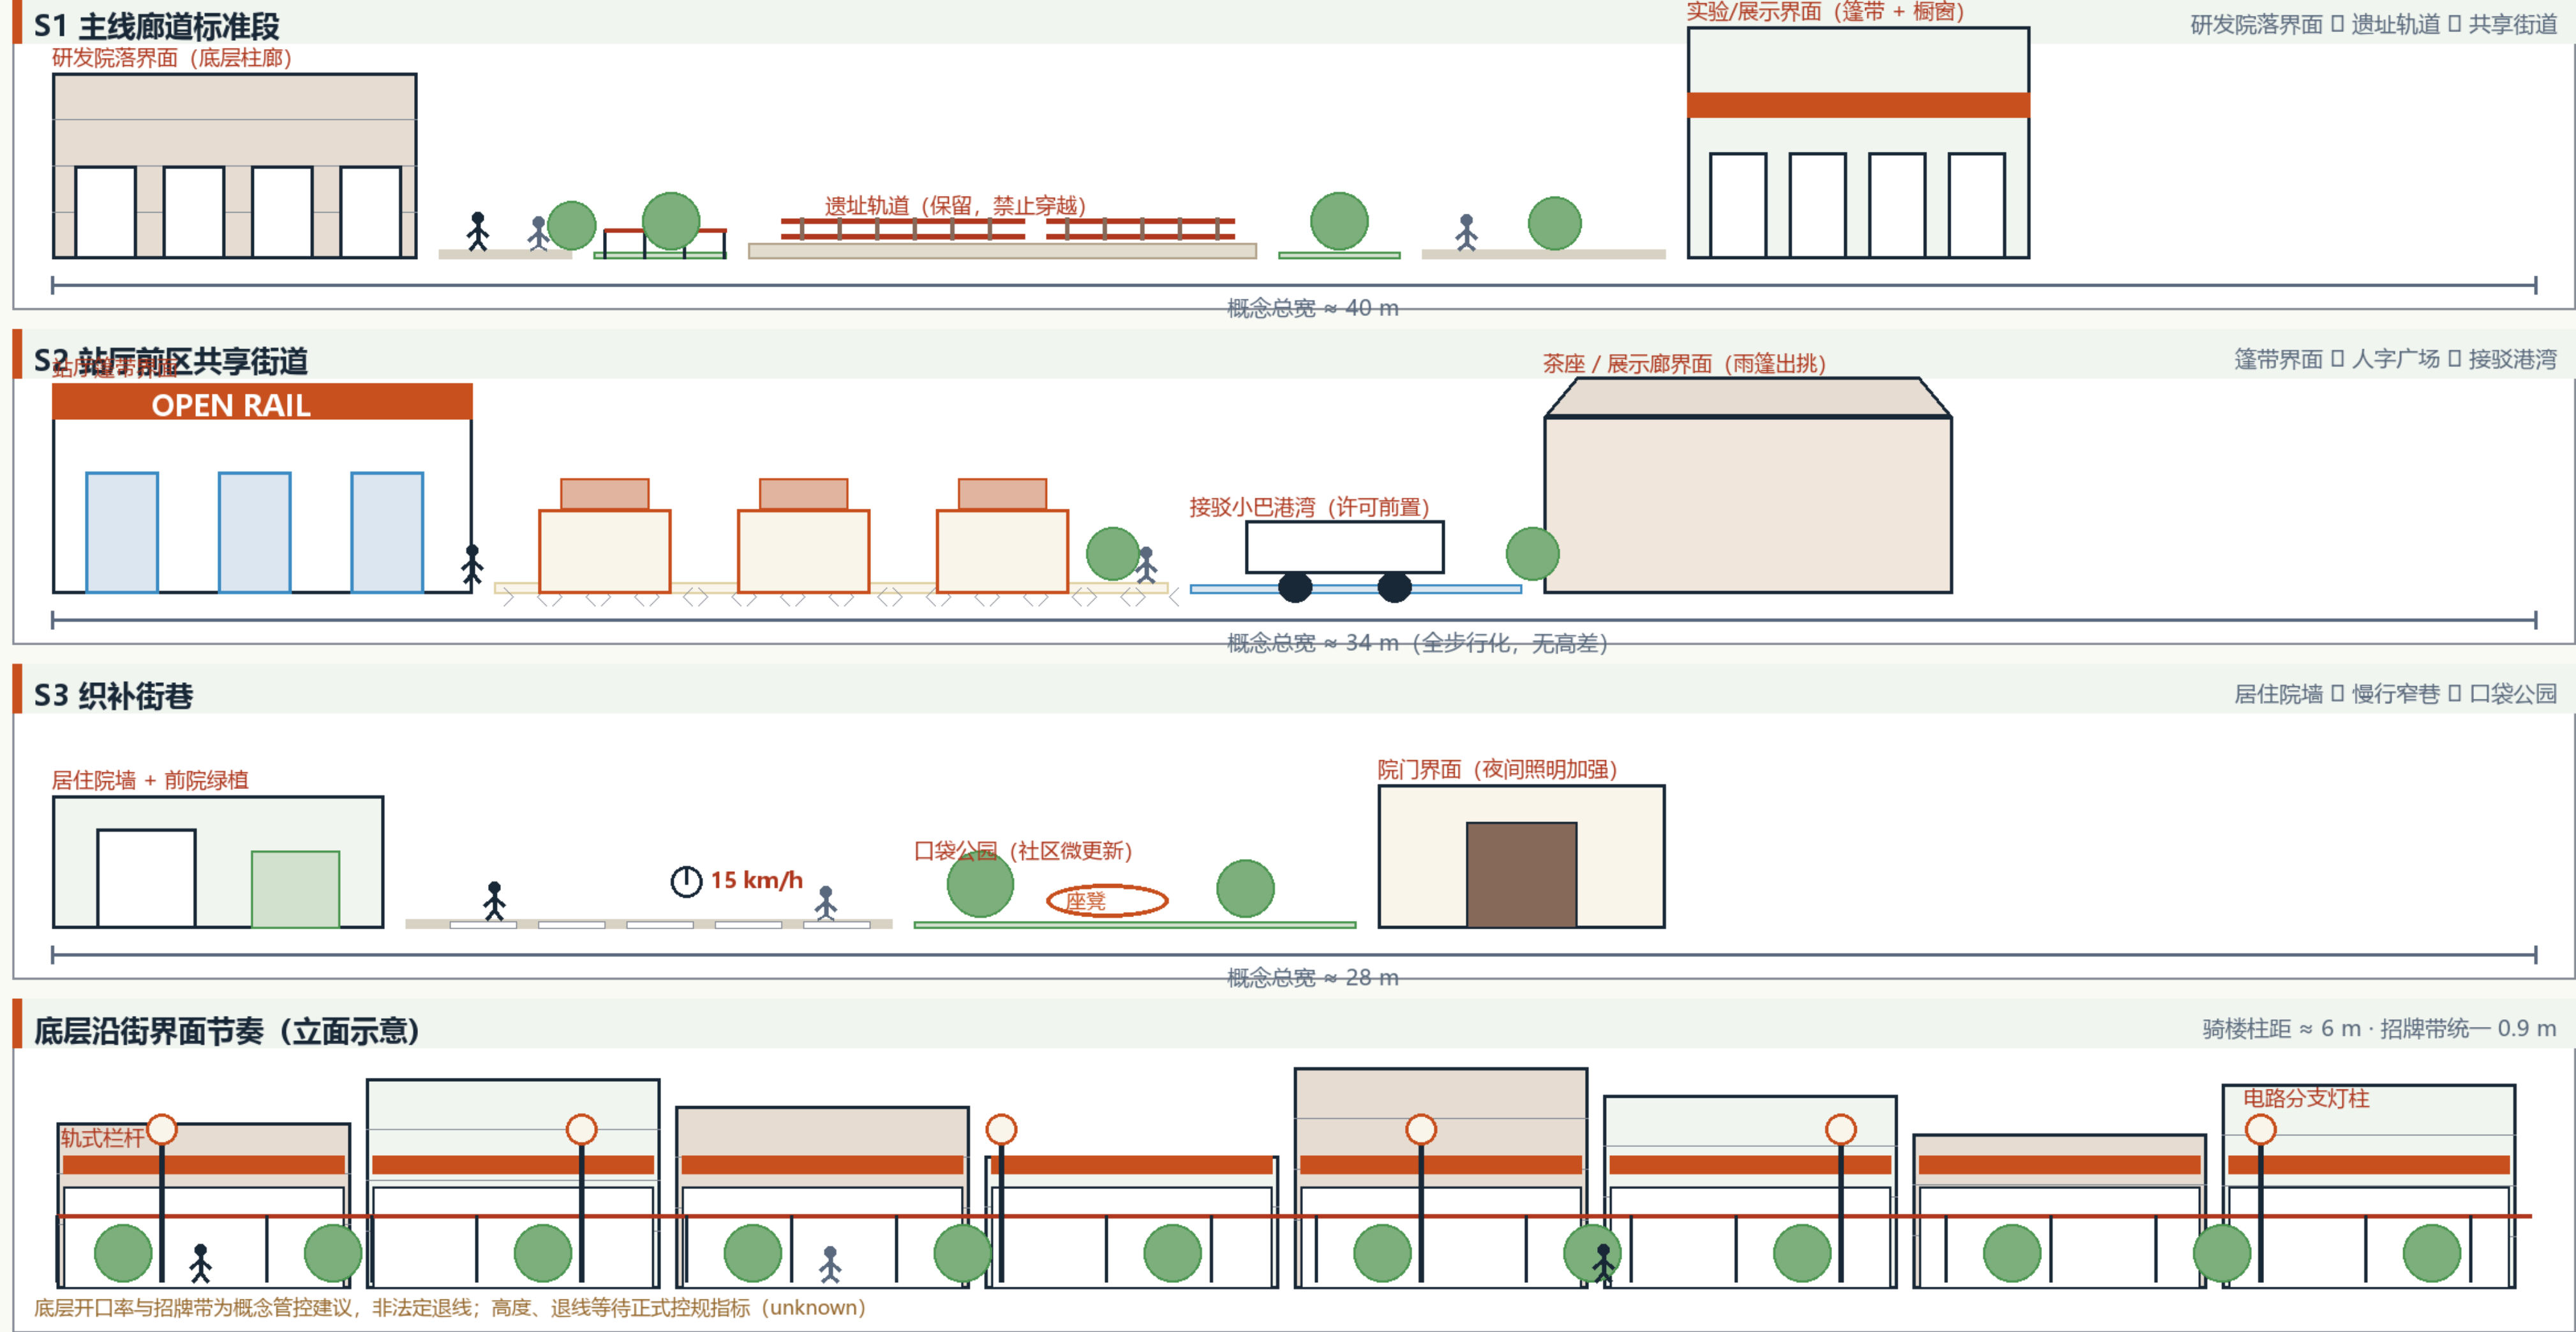

概念性构造与界面意向，非施工图；总体边界为 provisional（非官方红线），材质、工艺与结构以控规校核及专业深化为准

开源轨道 OPEN RAIL · 京张AI共同体

节点构造详图：铺装分层 / commit 座凳 / 电路灯柱 / merge 地刻（概念意向）

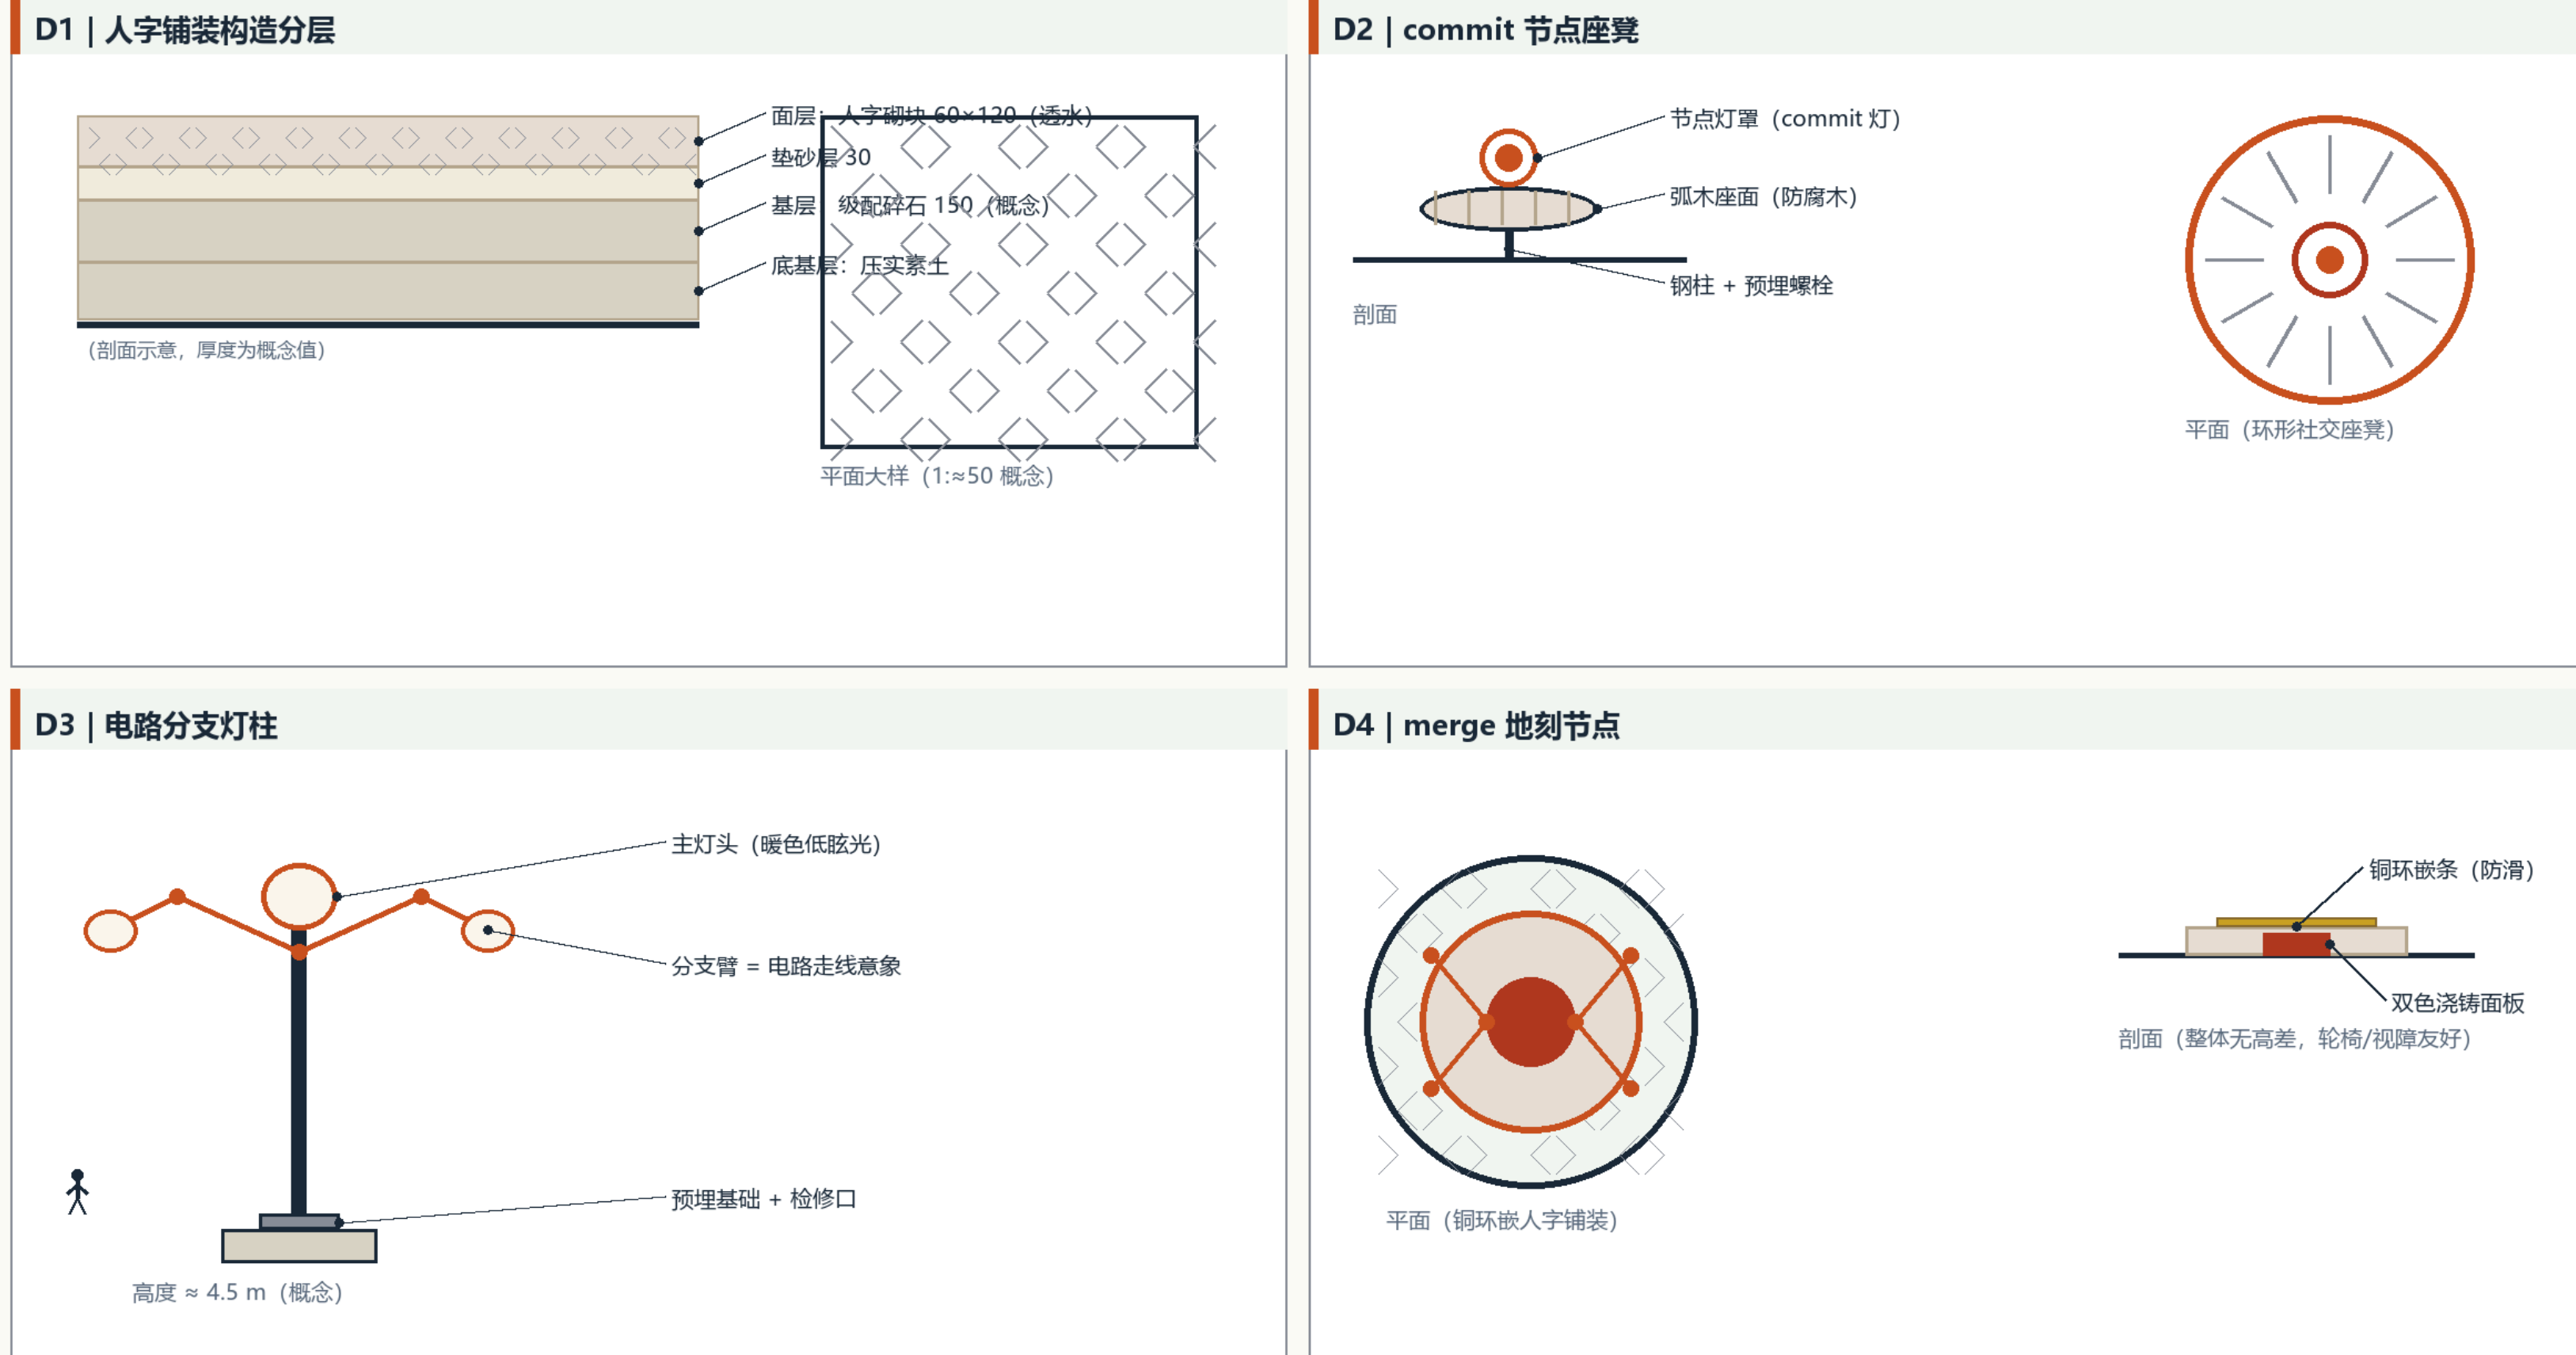

概念性构造与界面意向，非施工图；总体边界为 provisional（非官方红线），材质、工艺与结构以控规校核及专业深化为准

沿街界面（概念）

- S1 廊道段：院落柱廊—绿缓冲—轨道—共享街
- S2 站厅前区：全步行无高差 + 接驳港湾
- S3 织补街巷：15 km/h 慢行 + 口袋公园
- 骑楼柱距 ≈ 6 m · 招牌带 0.9 m（非法定）

节点构造（意向）

- 人字铺装分层（透水砌块/垫砂/级配/素土）
- commit 座凳：弧木 + 钢柱 + 节点灯
- 电路灯柱 ≈ 4.5 m 暖色低眩光
- merge 地刻：铜环防滑、整体无高差

排序方法论（触发式）

- 数据基线 → 优先级评分 → 成本科目
- 效益维度（P1-P5）→ 敏感性检验
- 无实测与官方数据前不产出数值结论
- 结论随 90 天公开复审滚动更新