


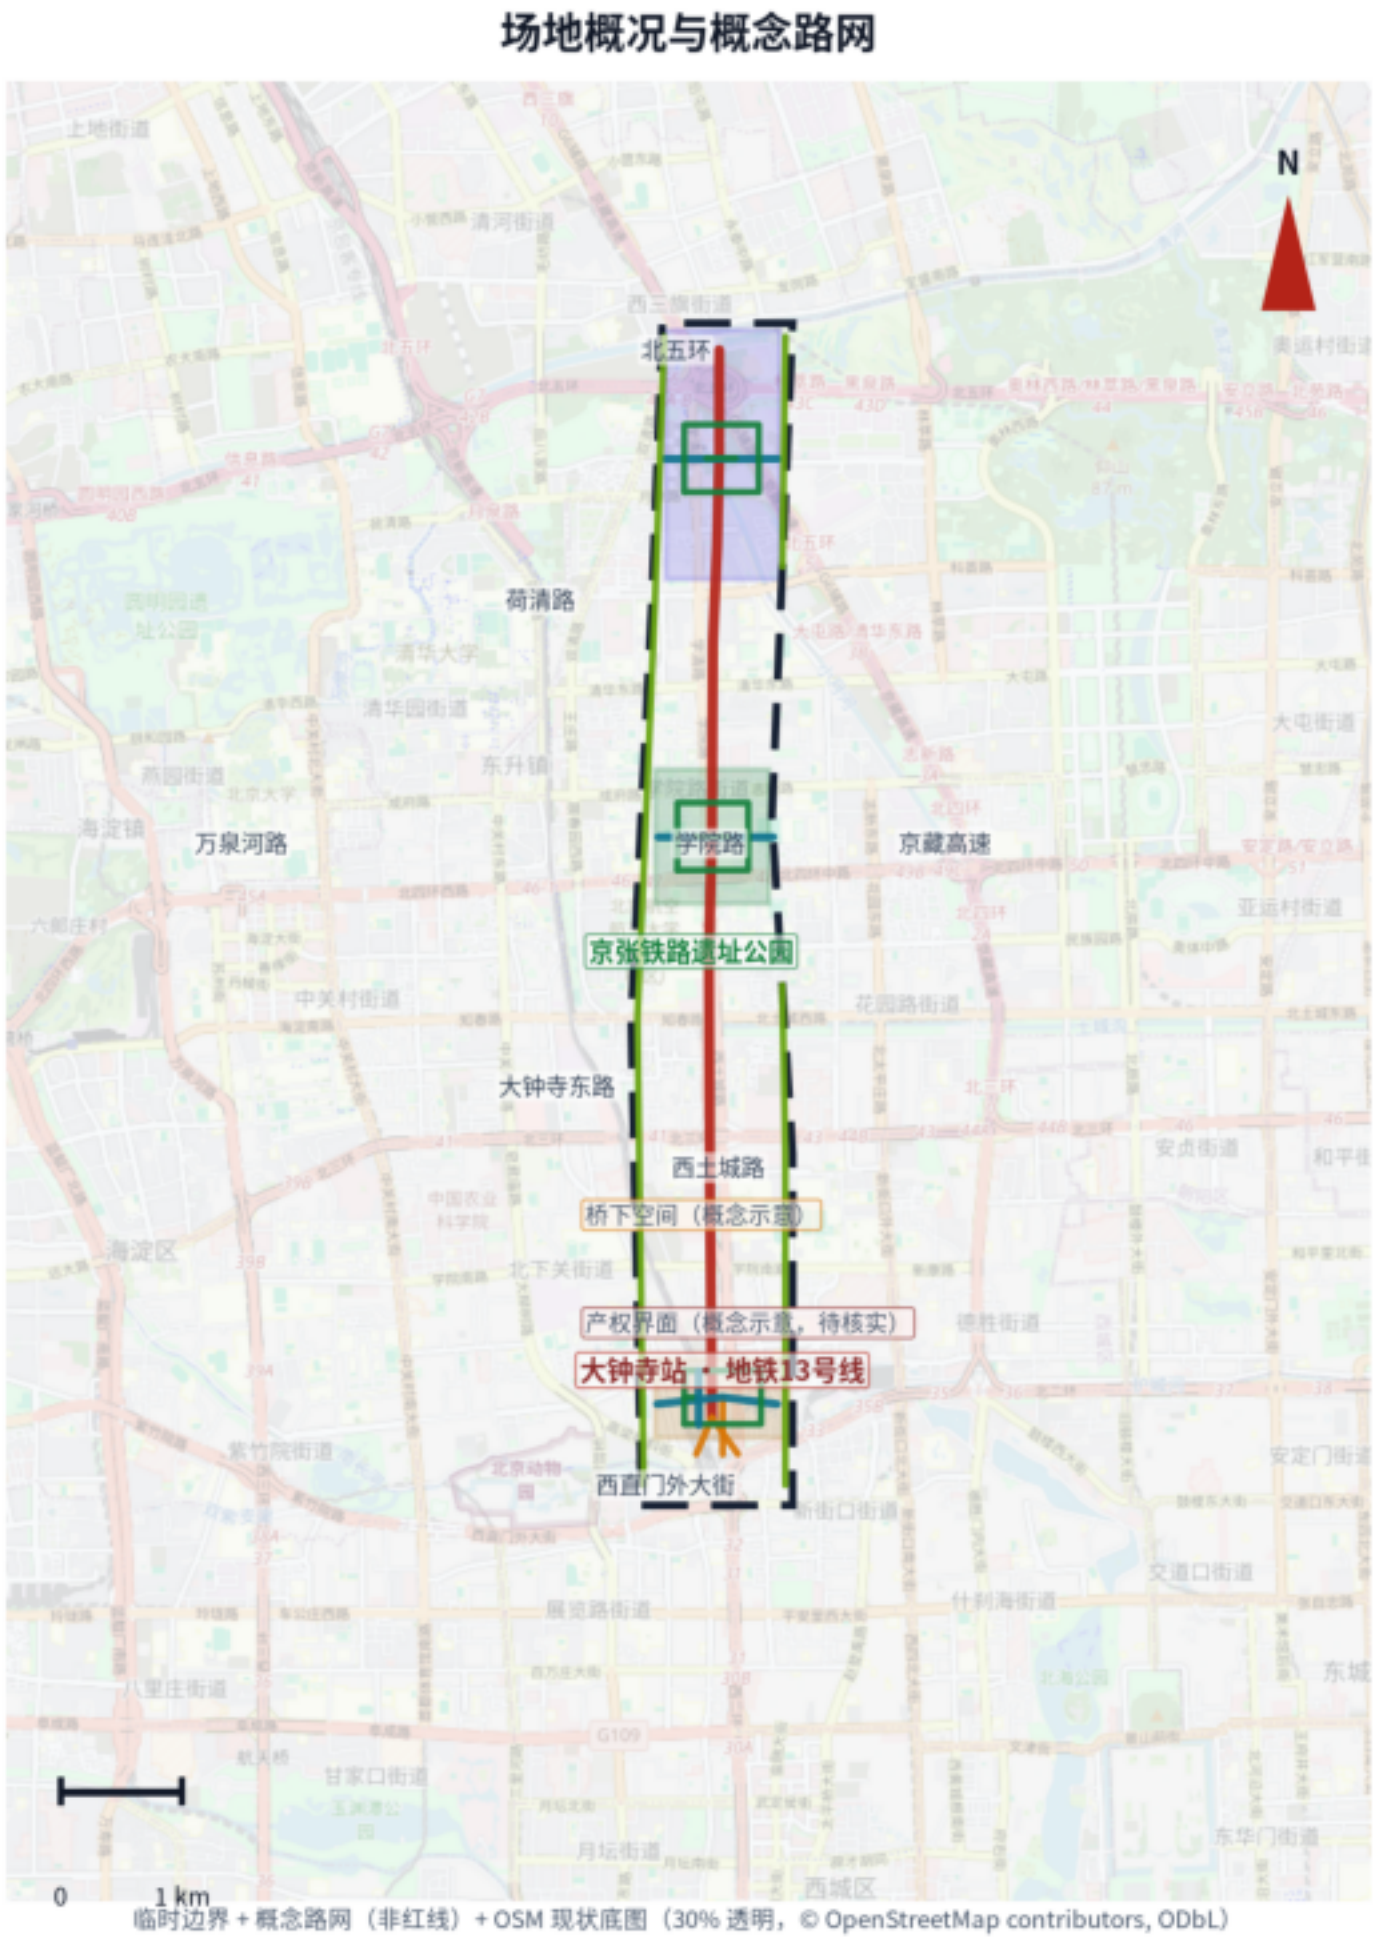

图例

- 黏菌主静脉
- 次级支脉
- 慢行环
- 京张绿廊
- 站点接驳
- 众智园片区
- 北京AI原点社区
- 大钟寺AI产业集聚区

边界/路网/片区为算法模拟概念与临时范围（非实测、非审批几何）；道路/站点/公园名称基于 OSM 公开数据与公告文字四至（位置示意）




19.20 2.802 8813 m 17/18 80.34 69.1% 25.2%

最优效率 Run7 冻结 骨架总长 关键节点覆盖 Plan03 UDS 透水铺装率 绿色渗透率

方法：生物黏菌自适应网络 + NSGA-II 多目标优化

真实 Physarum 167 边骨架（方法验证）

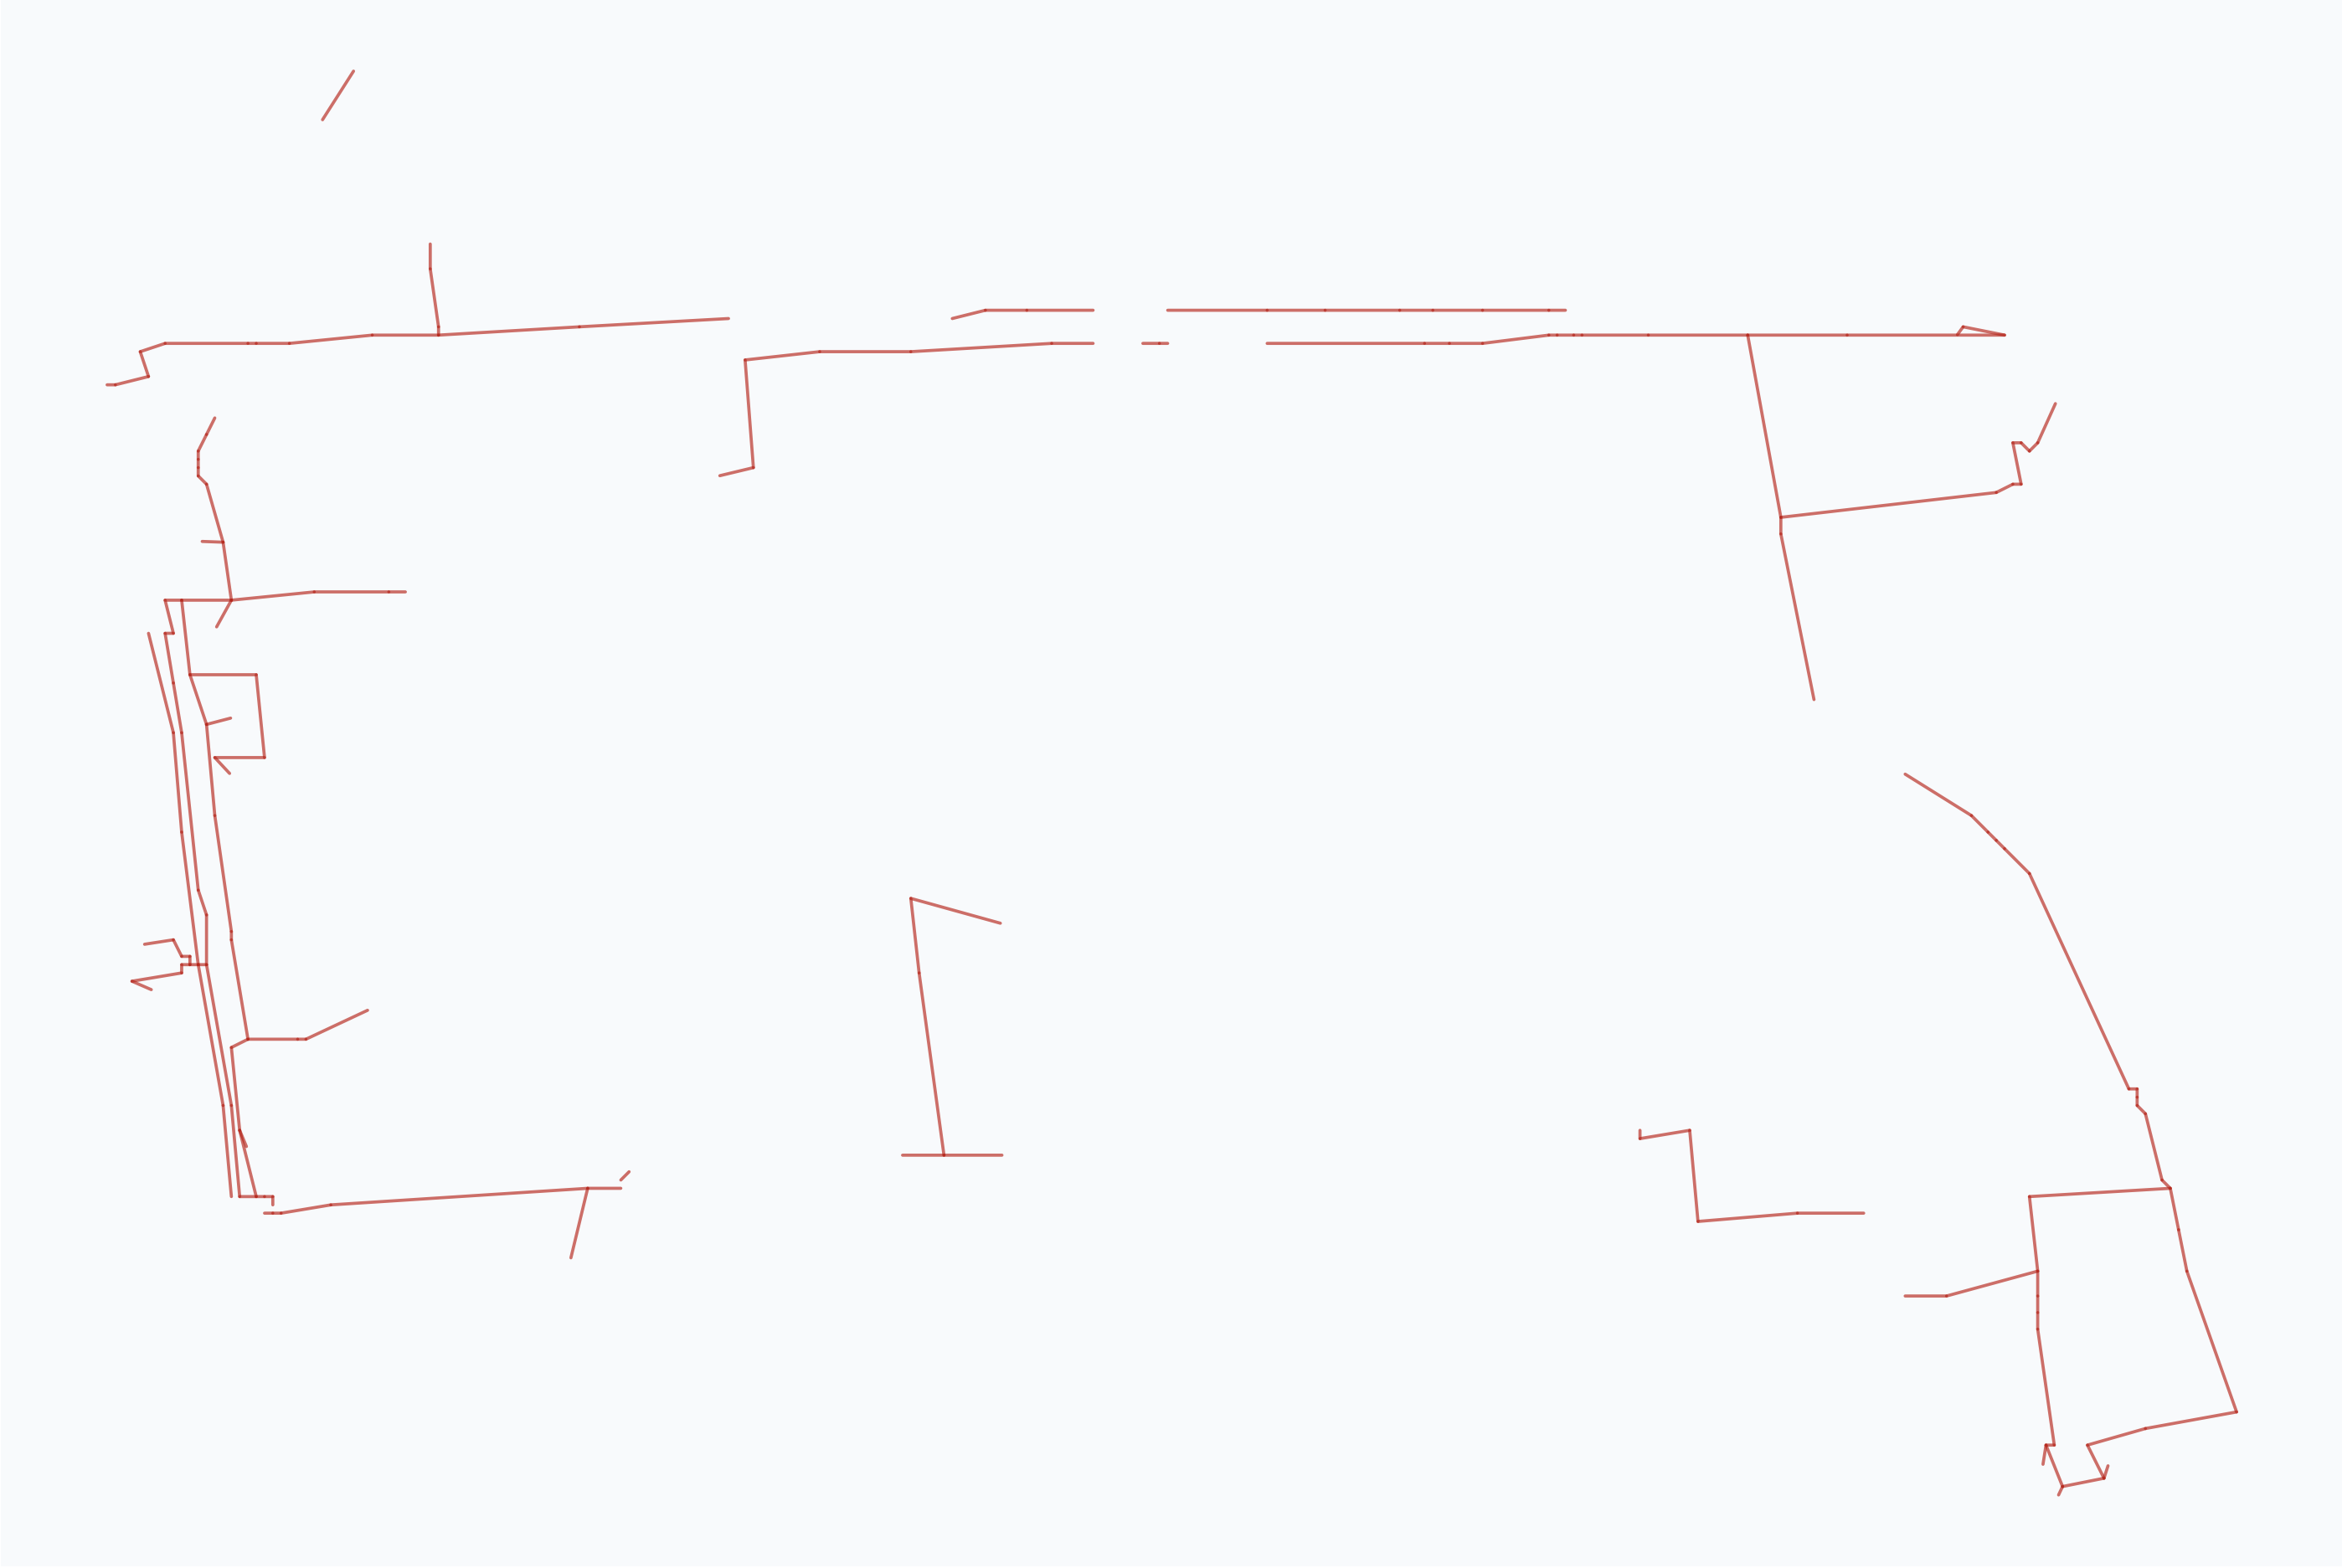


核心指标复算（同屏同级 · 场外方法验证）

OFF-SITE 场外 · 非场地正式几何

0	19.20	167
遗产硬穿越	最优效率	网络边数
g1 硬约束 · 场外	Run7 冻结 2.802 · 基线 1.143 · 场外	真实黏菌骨架 · 场外

方法验证证据（真实 Physarum 运行）：167 边网络 / 效率 19.20 / 遗产目标 f3=f2（退化为造价，非场地内独立遗产合规结论）

三处重点区域与全球标杆案例

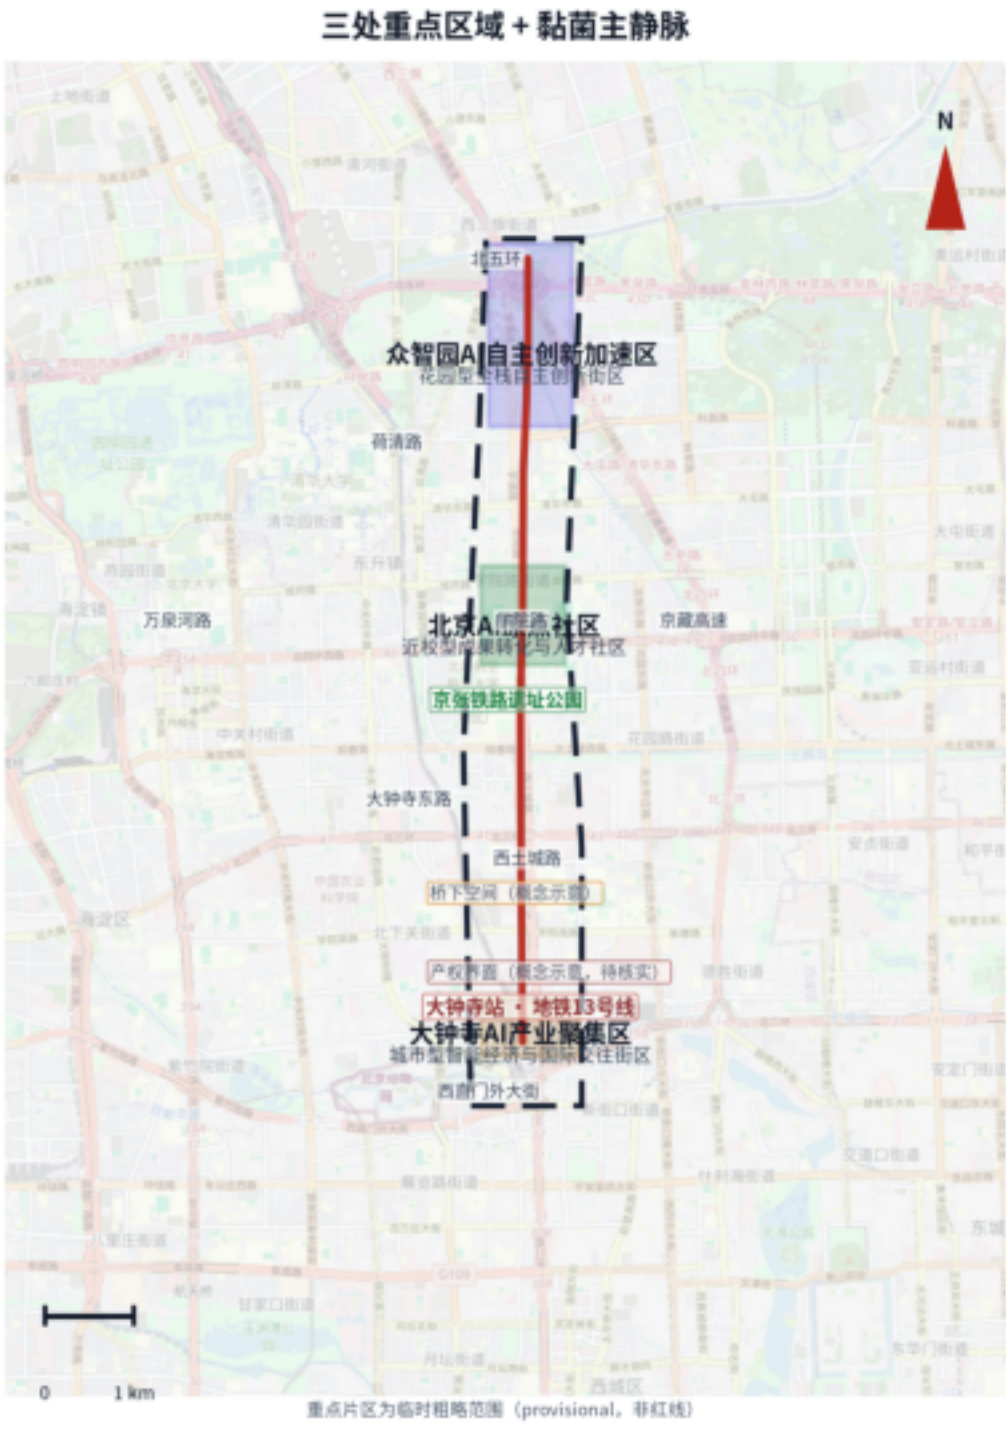

图例

- 众智园AI自主创新加速区
- 北京AI原点社区
- 大钟寺AI产业聚集区
- 黏菌主静脉
- 场地临时边界 (虚线)

三处片区边界为公告面积+文字四至推定的临时范围，非官方 polygon。非红线；站点坐标为 OSM 公开数据。

全球标杆案例（公开信息）

案例	地点	核心做法（公开报道）	借鉴/警示
Sidewalk Labs Quayside	多伦多	传感网络、数据信托试点（2017–2020）	数据治理 / 隐私警示
马斯达尔城	阿布扎比	低排放街区、被动降温、PRT 试点	低碳街区 + 接驳
松岛 IBD	仁川	填海新城、U-City 传感	新基建预留
阿姆斯特丹	荷兰	政企民协作、living lab	渐进更新 + 治理
雄安新区	河北	CIM 数字孪生、蓝绿网络、管廊	数字孪生 + 蓝绿

测试验证场景与实施矩阵

测试验证场景

实施矩阵（建议性框架）

场景	验证对象	检验依据	关键目标	项目	建议责任主体	建议周期	暂停/退出
T-01 大钟寺站 TOD	四象限步行连通与接驳	GB 50763-2012 / GB/T 51328	换乘全程无障碍	JZ-01 慢行断点	区交通委 + 公园	近期	权属未定则暂停
T-02 小月河雨洪	蓝绿廊道 + 透水铺装	海绵城市指南 / GB 50014	透水 69.1% / 绿滞 25.2%	JZ-02 清河界面	区水务局 + 园区	中期	防洪不满足则退出
T-03 AI 原点可达性	校区-园区-街区慢行	GB 50763-2012	慢行环覆盖 + 无障碍连续	JZ-03 成果转化街	高校 + 区科信局	中期	权属争议则暂停
				JZ-04 四象限连通	轨道单位 + 区交通委	中期	时序不匹配则顺延
				JZ-05 端侧算力	区科信局 + 运营主体	长期	运营缺位则退出
				JZ-06 路网深化复算	设计方 + 高校	长期	数据未发布则待确认


无障碍与包容性（GB 50763-2012）

无障碍服务矩阵（GB 50763-2012）

画像	无障碍与包容性需求	空间响应
开源开发者	夜间协作可达与安全	无障碍出入口/卫生间、分级照明
初创团队	团队含残障成员	无障碍办公/共享测试空间
头部企业访客	国际/行动不便接驳	多语言标识、无障碍电梯
周边居民	老人/儿童/残障通行	缘石坡道、盲道、休息座椅
高校师生	残障师生连通	无障碍慢行缝合、体验点

风险、版权与合规说明

- 真实 Physarum 运行位于临时边界以西约 2-3 公里，仅 140 米交叠；未平移坐标、未编造红线。
- 遗产保护为 editable_by_agent=false 锁定图层；官方遗产几何缺失，f3≡f2（遗产影响退化为造价）。
- 本方案不声称官方批准、审定控规、最终权属或实施保证。
- HTML 不加载远程脚本/瓦片/字体/iframe/表单/API。
- 申诉救济：发现—登记—整改—回访闭环（建议性框架，待主管部门与运营单位批复）。

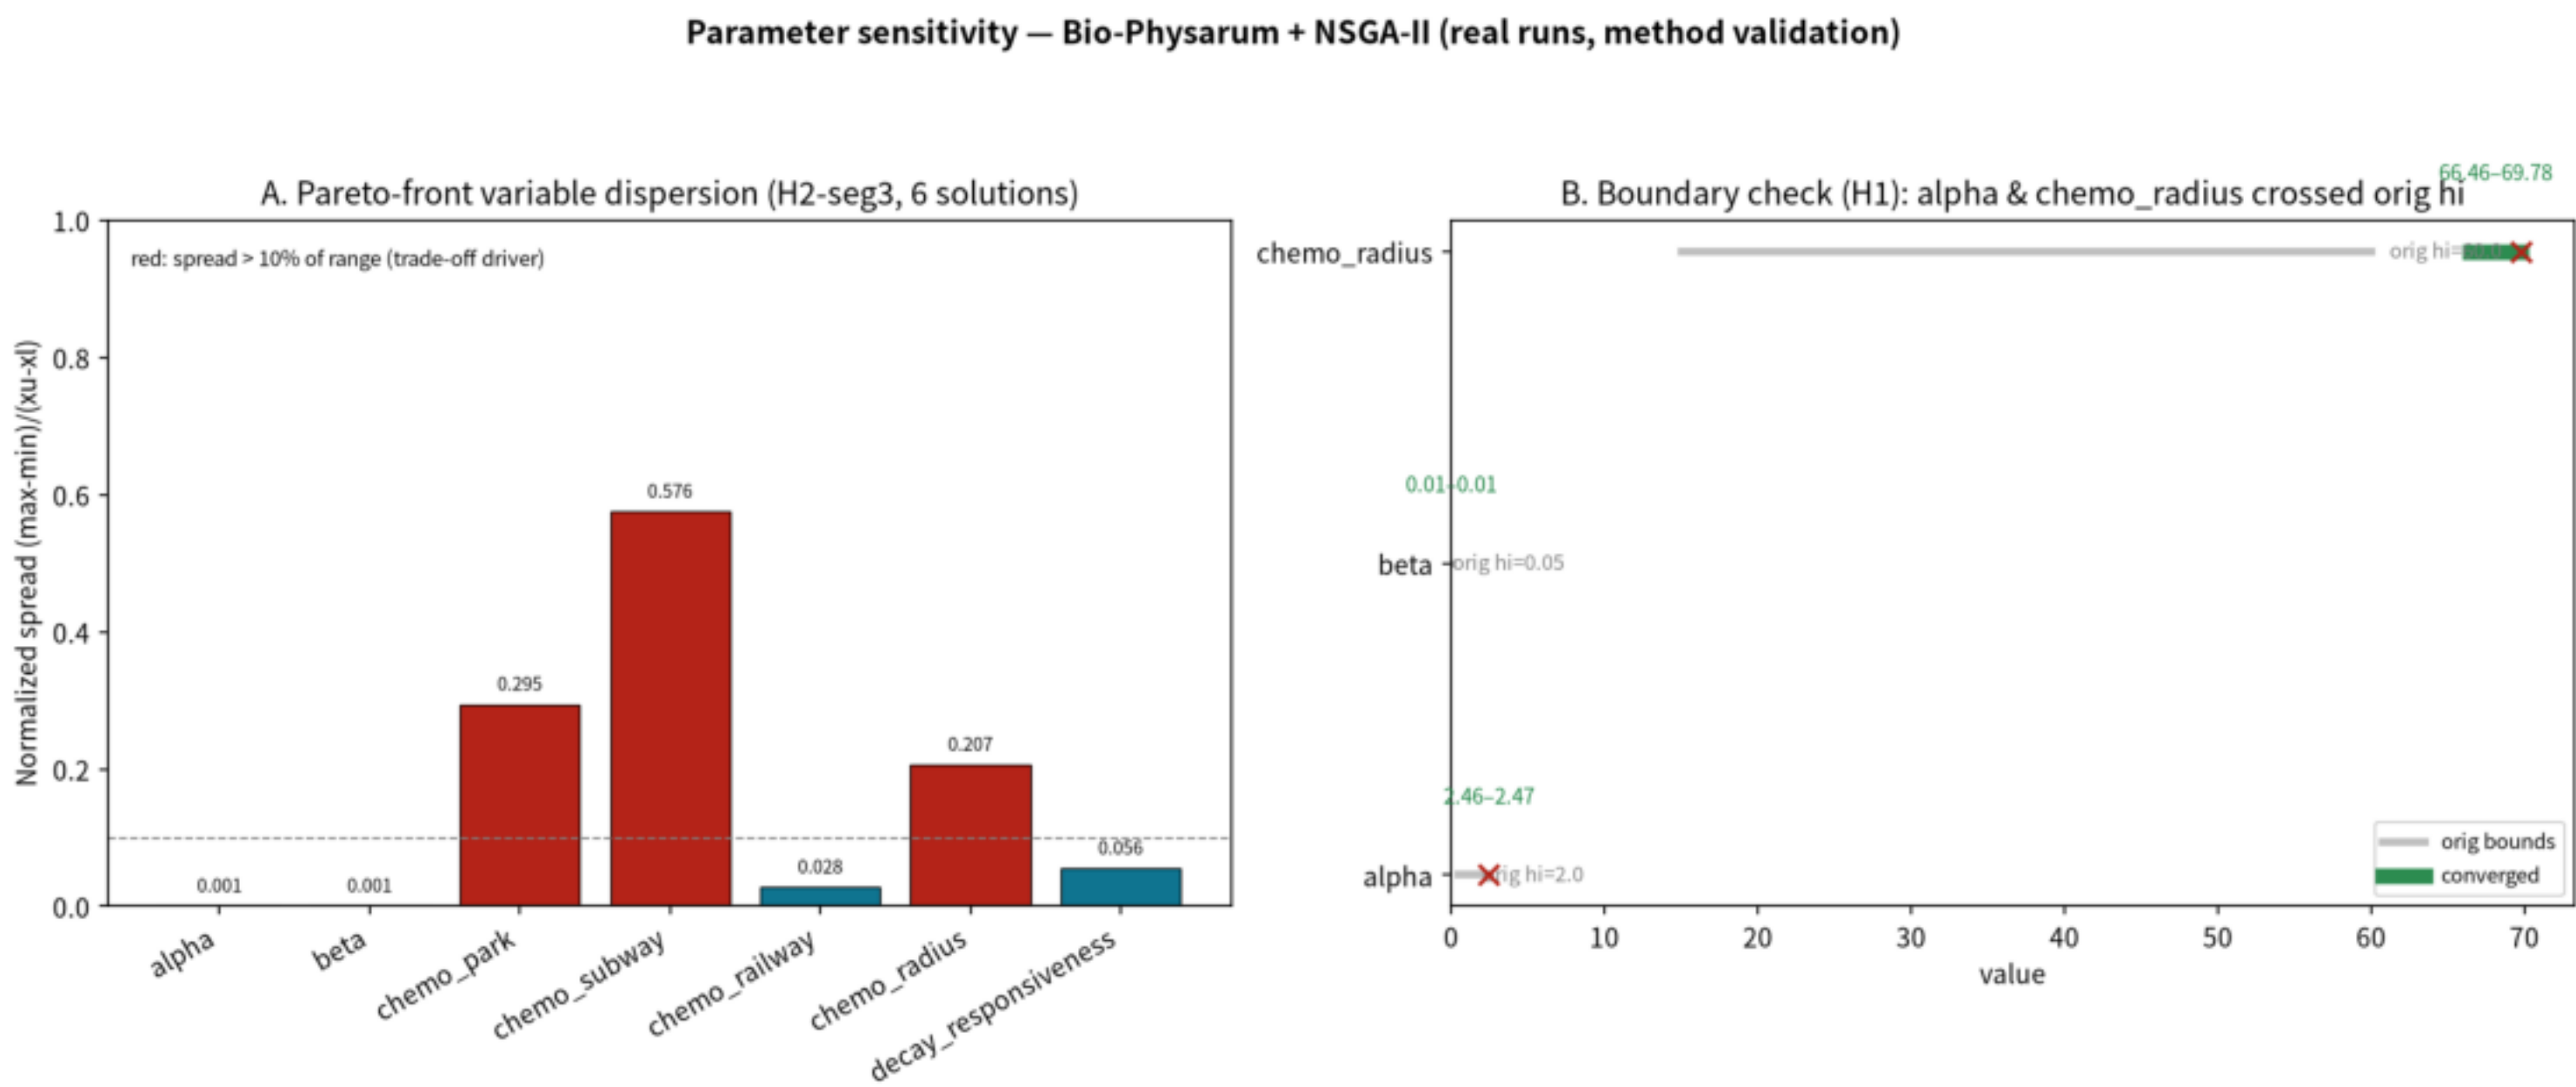

造价细目 (建议性框架)

等级	长度(m)	单价(元/m)	造价(万元)
主干路	740.2	8000	592.2
次干路	1744.1	5000	872.0
支路	3679.9	3000	1104.0
微循环	2648.8	1500	397.3
合计	8813.0	—	2965.5

平均 3365 元/m；仅路网市政造价，不含管线迁改/轨道土建/拆迁 (建议性框架)

政策衔接矩阵 (建议性框架)

项目	政策/标准依据 (真实)	待确认
JZ-01	GB 50763-2012 / 无障碍条例	桥下权属
JZ-02	海绵城市指南 / GB 50014	蓝线/防洪
JZ-03	北京城市更新条例 (建议性)	条款/权属
JZ-04	GB/T 51328 / GB 50763	站点/管线
JZ-05	新基建政策 (待确认)	监管主体
JZ-06	京政发 (1984) 128号	图则/红线

