

⑤ 总体概念：人字形展线（1909）→ 人字链创新带；命名与Logo方向见proposal.md。


⑤ 一脊：京张遗址公园活力脊（概念绿地廊道，南北贯通）；活力脊二期2025年与京张遗址公园连接报道；双翼（中关村科技服务翼 / 小月河场景赋能翼）

⑤ 三链节：众智园「研」、原点社区「创」、大钟寺「业」。

⑤ 双翼：中关村科技服务翼（要素/IP/资本）、小月河场景赋能翼（场景/试验/体验）。

⑤ 三层范围逐级传导：43.6平方千米研究 → 11.4平方千米设计 → 368.4公顷重点区。

⑤ 边界为临时粗略边界（provisional），仅用于设计讨论；官方polygon发布后重算。

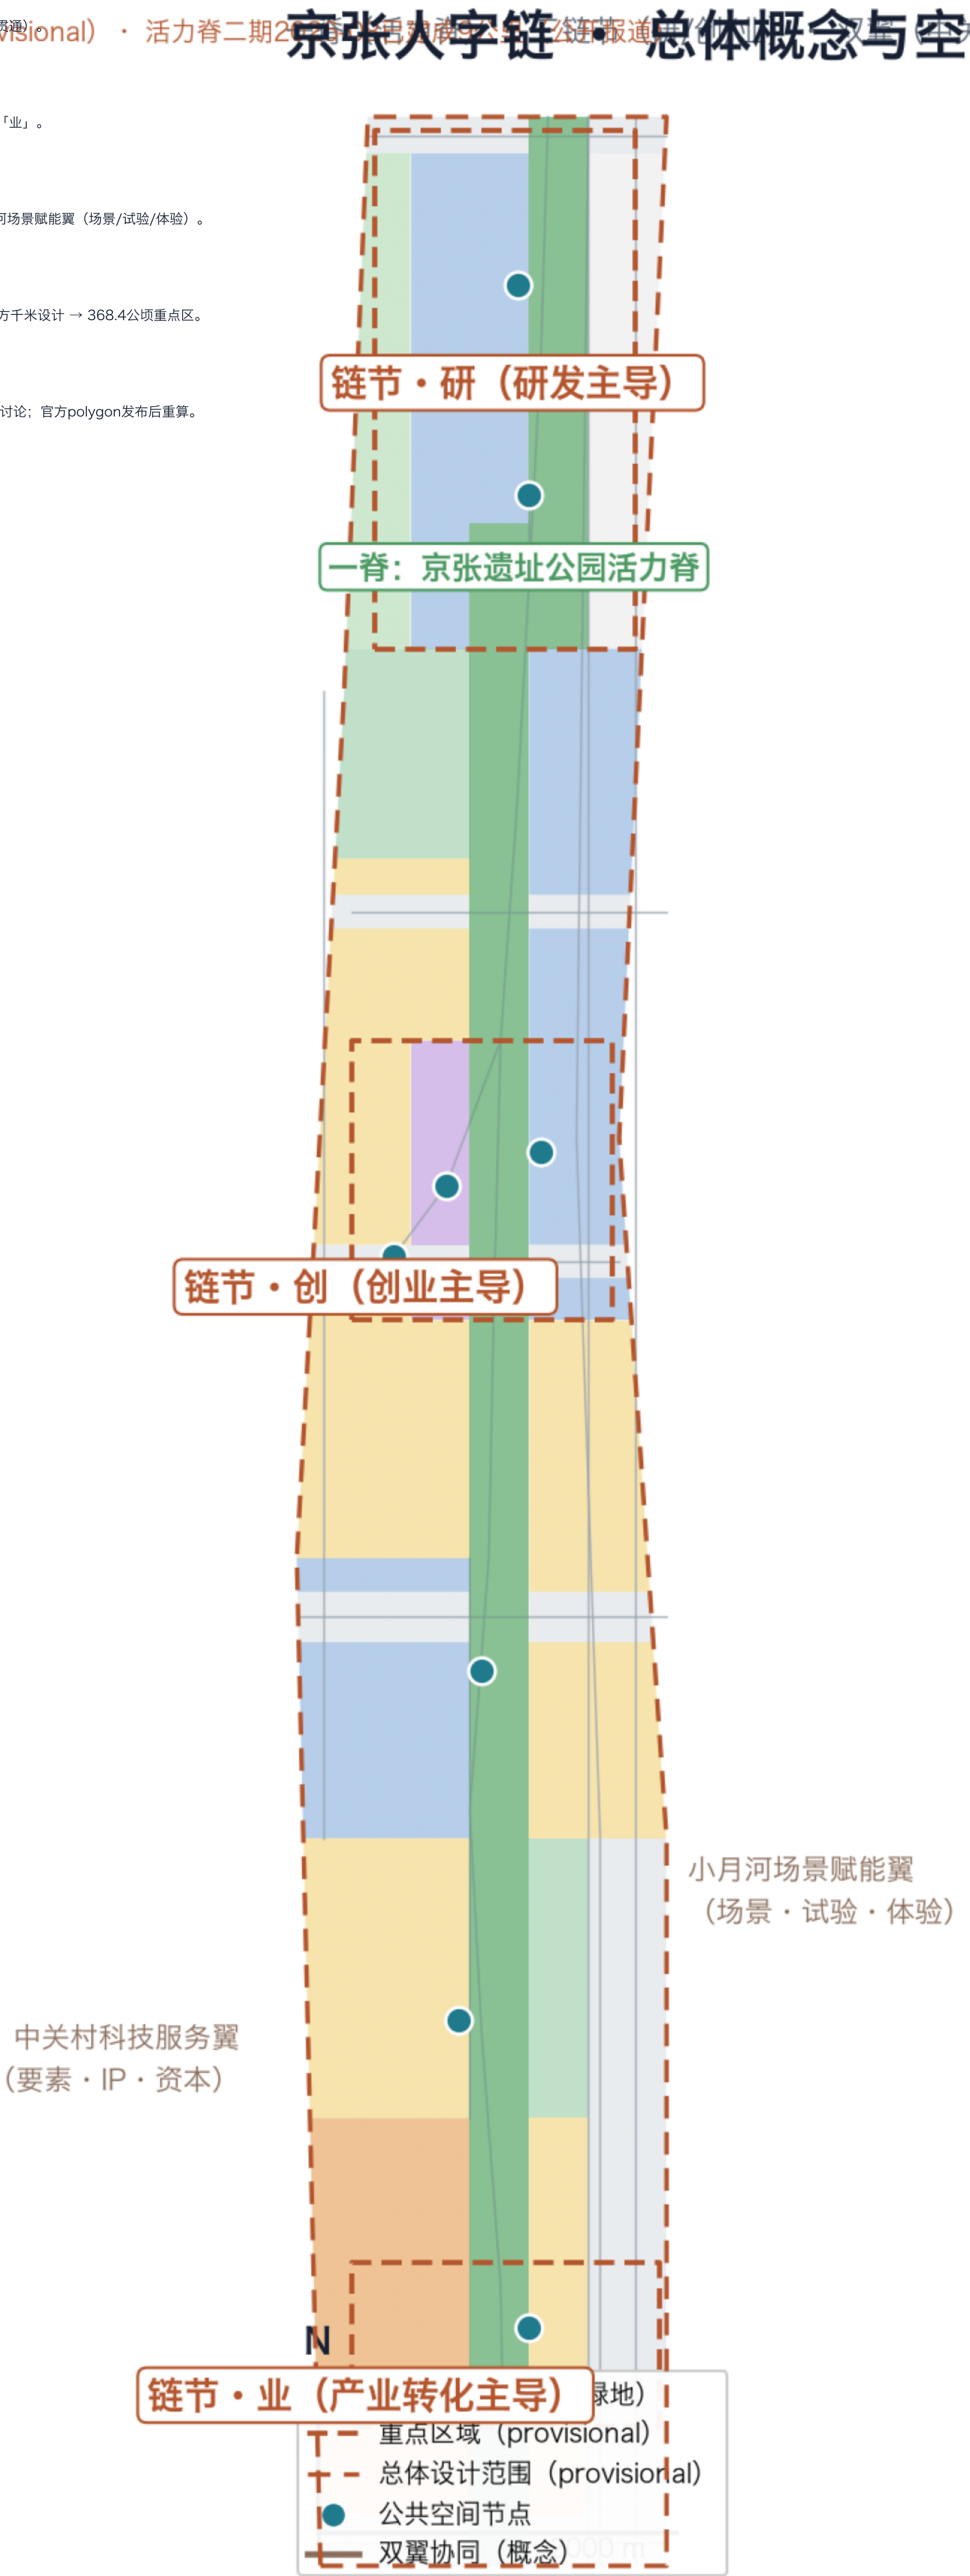


📌 科研18.9%+商业8.1%=产业空间27%；居住25.8%；绿地22.5%；道路13.5%；留白4.0%。


📌 概念总建筑面积约206万平方米（含地下空间）；概念容积率约0.8；用地代码遵循国土空间用地用海标准（GB 50217-2023）；用地结构：居住（25.8%）· 产业（36.9%）· 绿地（22.5%）· 道路（13.5%）· 留白（4.0%）


📌 拆改留概念示意：新建约60%／改造约24%／保留约16%（需现状普查修正，非地块级结论）。

📌 官方控规指标缺失，floor_area_ratio登记unknown待补。

京张人字链 · 用地结构与功能分区

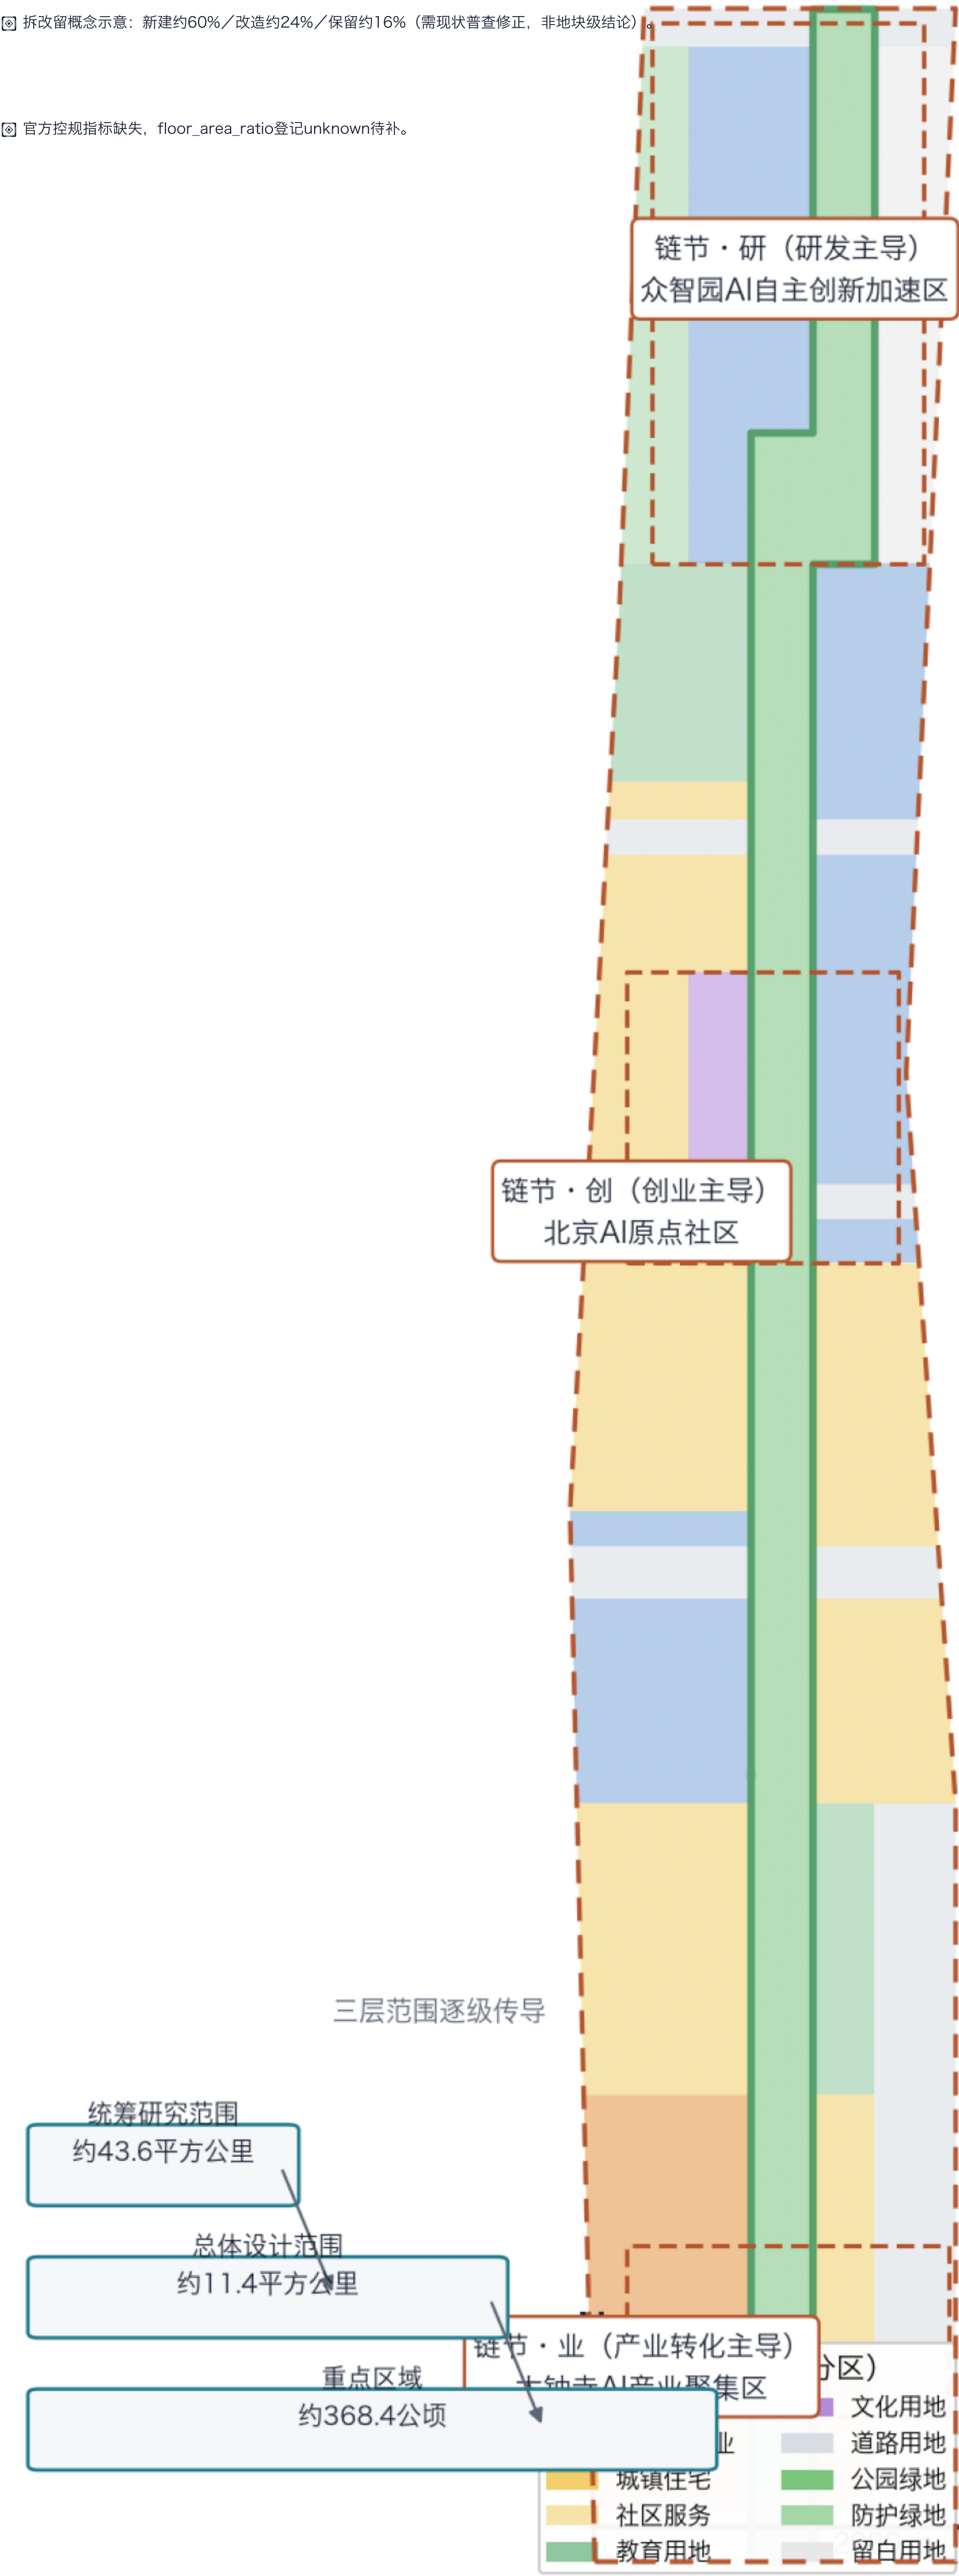

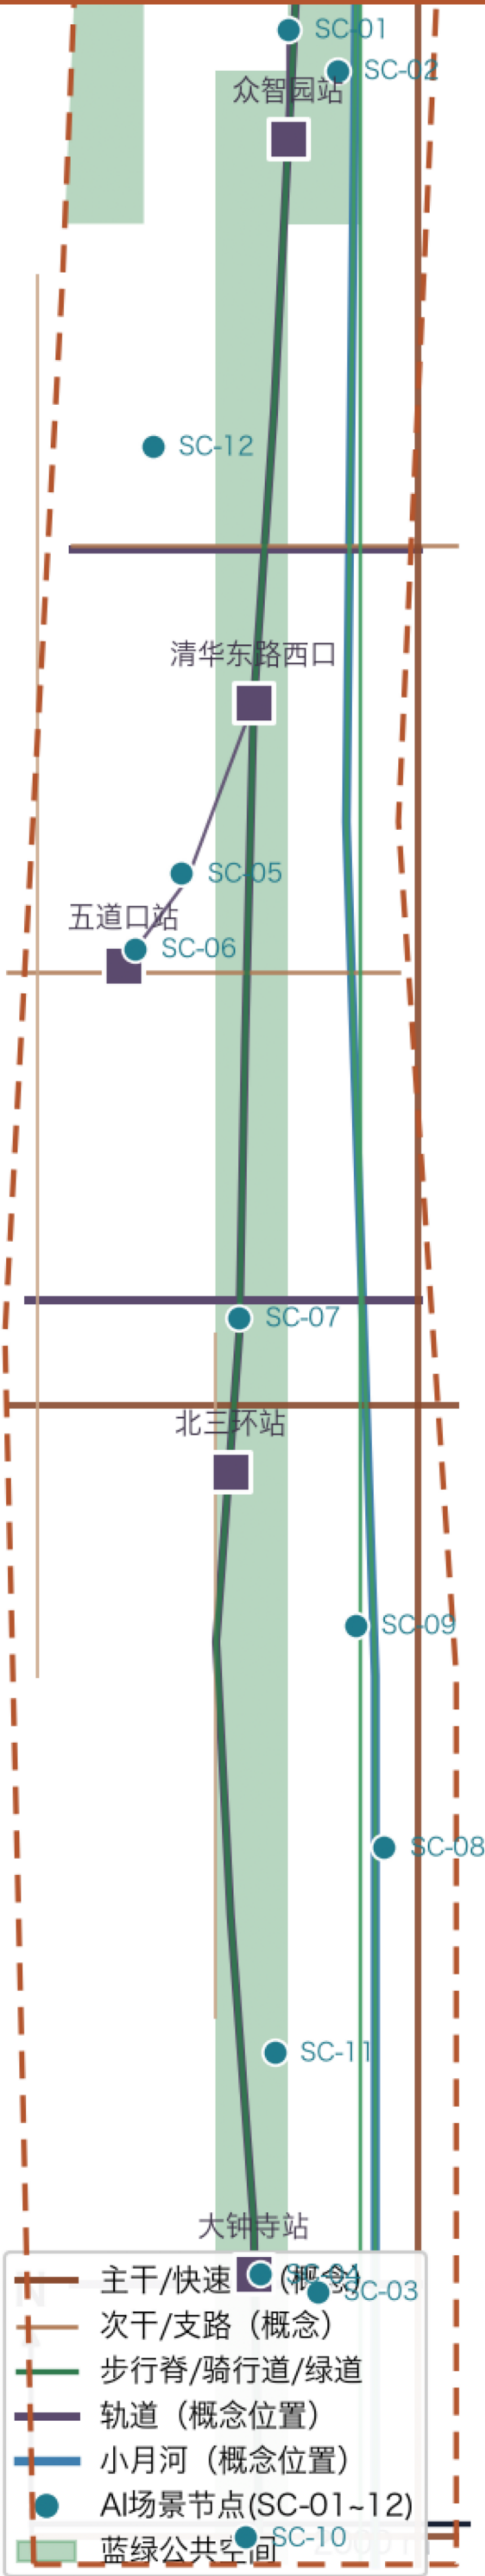

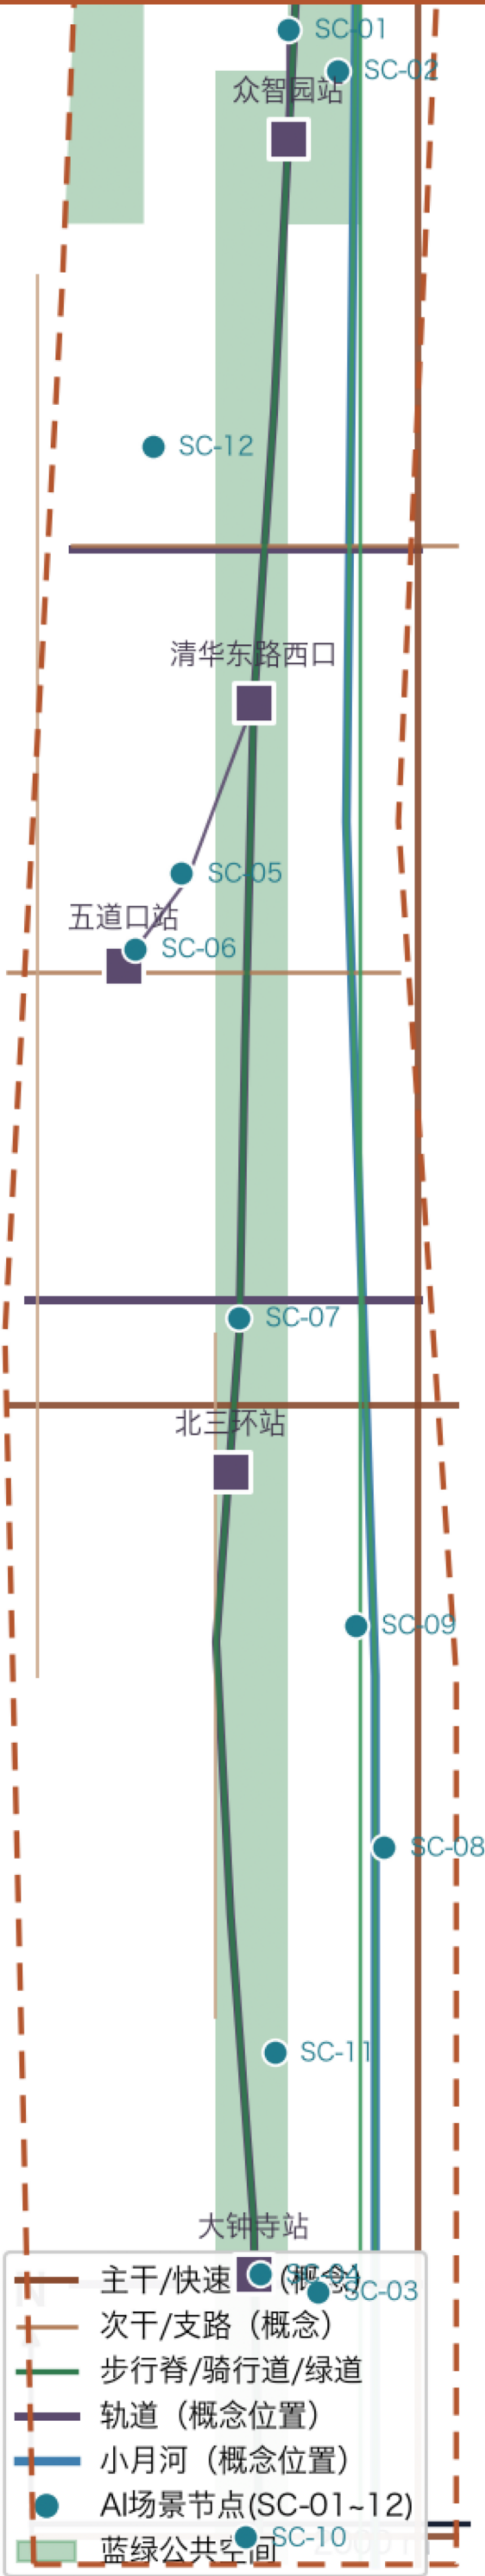

📍 研 · 众智园（约192.1公顷）：一园两轴三组团；实验室—中试—展示垂直复合；治理沙盒。

📍 创 · 原点社区（约104.3公顷）：清华园车站—原点之心；低扰动有机更新；开源工坊。

📍 业 · 大钟寺（约72.0公顷）：一站四象限；具身中试、数据要素流通试验床。

📍 三区面积均为provisional复算值，待官方polygon更新。

链节 · 研（研发主导）

链节 · 创（创业主导）

链节 · 业（产业转化主导）

N

2000 m

链节 · 研 | 众智园AI自主创新加速区（约192.1公顷）

定位：花园型AI创新街区，AI全栈自主创新与治理话语权

空间结构：一园两轴三组团（科技广场为园心）

建筑更新：实验室—中试—展示垂直复合（概念）

交通：五环一体化对外交通方向、园区绿道

场景：算力之芯(SC-01)、治理沙盒(SC-02)

风险：国家平台政策依赖、五环工程条件待确认

链节 · 创 | 北京AI原点社区（约104.3公顷）

定位：近校型AI创新街区，世界级AI创新生态

空间结构：一轴一心两翼（清华园车站文化区为原点之心）

建筑更新：低扰动有机更新，保留改造为主（概念）

交通：五道口/清华东路西口站点一体化

场景：开源工坊(SC-05)、AI体验街(SC-06)

风险：校地协同与权属关系待确认

链节 · 业 | 大钟寺AI产业聚集区（约72.0公顷）

定位：城市型AI创新街区，智能原生新业态

空间结构：一站四象限（大钟寺站为核）

建筑更新：领军企业牵引的产业载体（概念）

交通：站点四象限步行连通、静态交通组织

场景：具身中试(SC-03)、数据市集(SC-04)

风险：政策试点与权属条件待确认

📄 场景14张（4个测试验证）：算力之芯、治理沙盒、具身中试、数据市集、开源工坊、AI体验街、文化导览、慢行评估、健康导航、企业协办、低速配送、运营复核、学院路AI教育共创站、西土城路AI法律服务站。

📄 六类画像：研究员/创业者/开发者/投资人服务者/居民/全球访客。

📄 运营：京张AI创新大会+链节开放日+开发者之夜+社区活动；沙盒申报一季度评审一脱敏开放一人工复核。

📄 全部活动与招商表述为概念建议。

场地约1141公顷；绿地率22.5%；公共空间比例0.8%；概念容积率0.18；三重点区面积复算见metrics.json。


京张人字链 · 核心指标复算与证据链（自 geometry/* .geojson 与 metrics.json 派生）

总体设计范围面积	概念绿地率	公共空间比例	概念容积率	建筑概念密度
compliance_matrix覆盖公告1.3/1.4/1.5、自选区域场景与agent.1-6共24项；standard_matrix覆盖6项标准；design_depth_matrix覆盖15项深度项。				
1141.3	22.5%	0.8%	0.18	1.9%
风险与版权：公开/清权资料、原创素材、AI生成责任披露、官方批准承诺禁用、缺资料清单完整登记。				
公顷	ratio	ratio	ratio	ratio
site_area_sqm · EPSG:4548 复算	green_ratio · 活力脊+防护绿地	public_space_ratio · 8处广场节点	concept_floor_area_ratio · 非控规指标	building_density · 概念基底


自检与证据状态

确定性校验（结构/引用/占位）	PASS
空间校验（拓扑/覆盖/面积复算）	PASS
可视化封装校验（离线/指标一致）	PASS
专业证据校验（标准/深度/指标引用）	PASS
provisional 边界警示	如实披露 · 待官方polygon后重算

分期范围占比（概念）

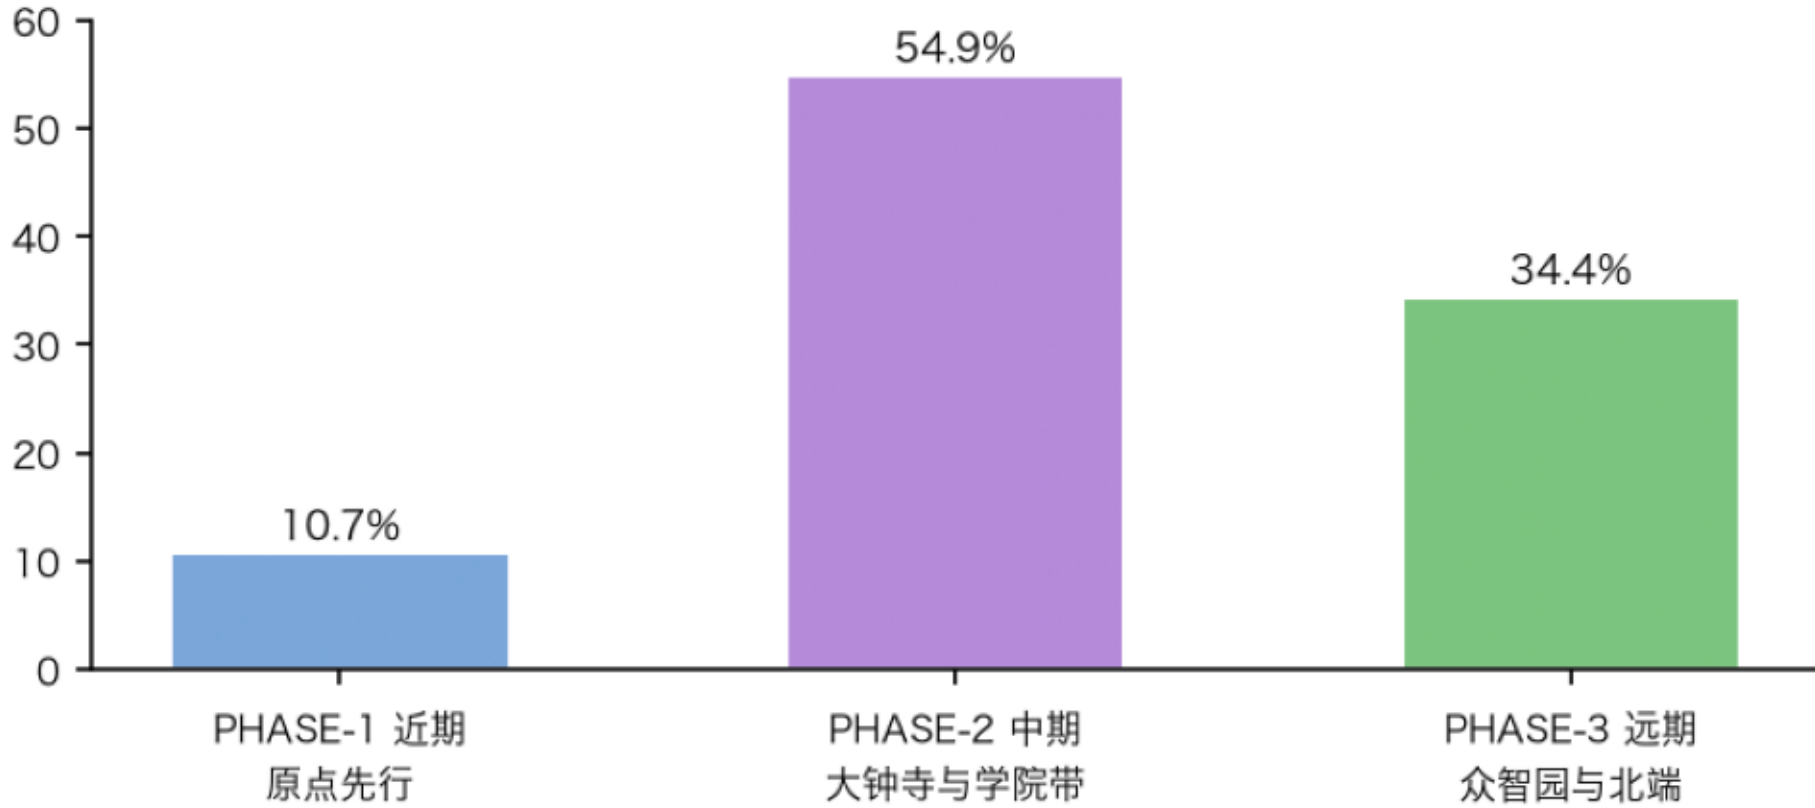

用地结构（占总体设计范围%）

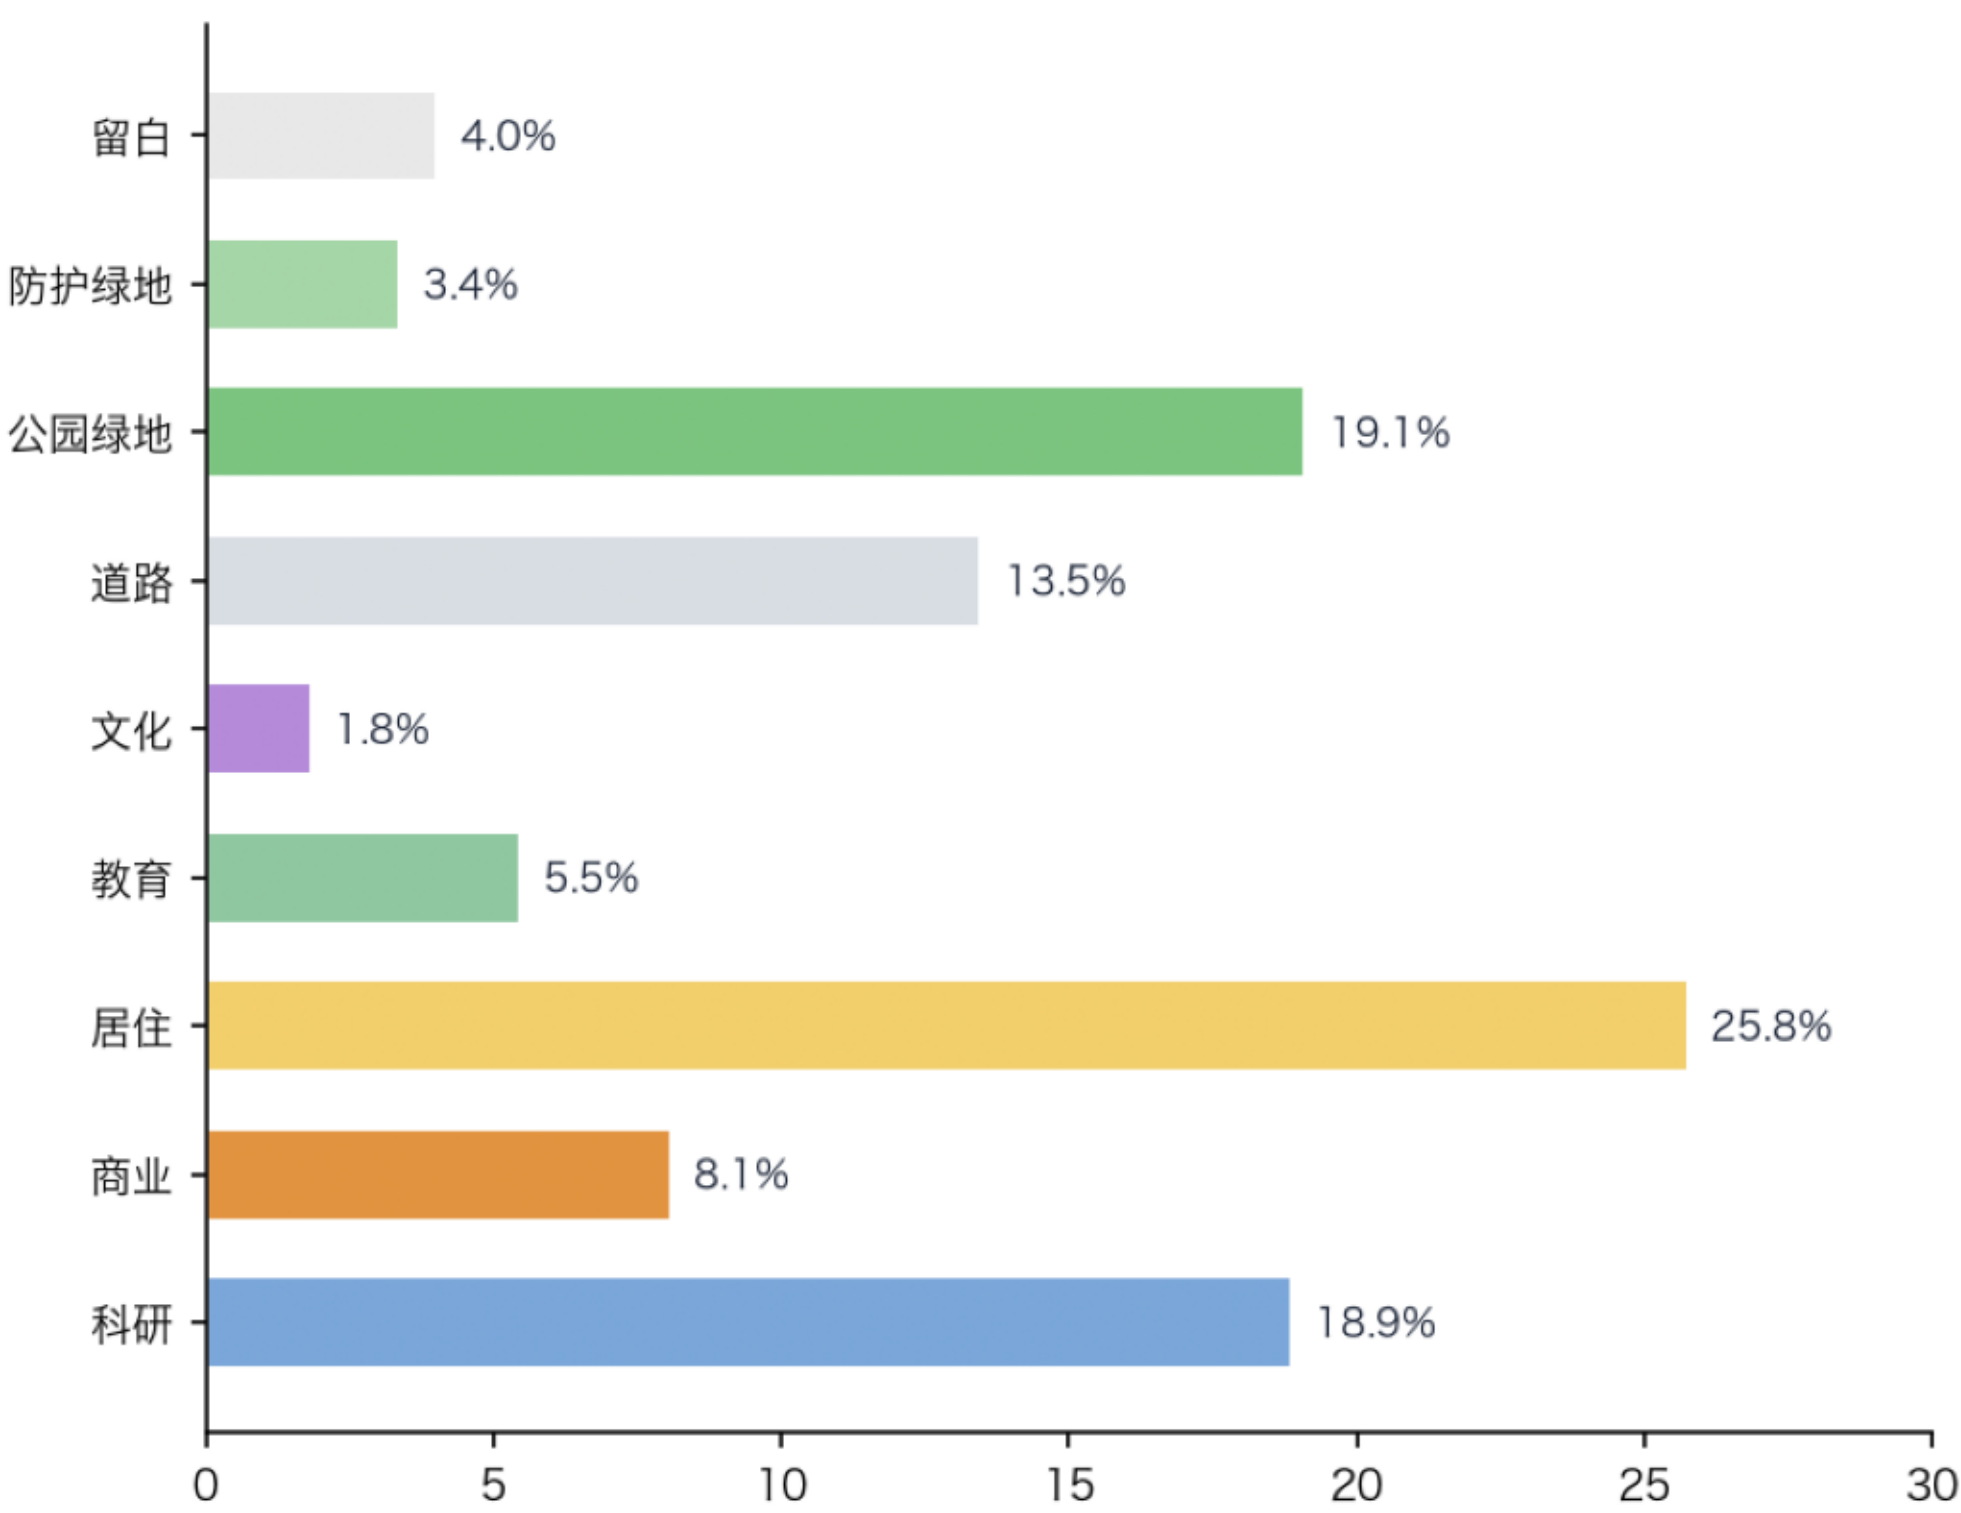

注：全部面积在 EPSG:4548 投影下复算；概念指标（容积率/密度/高度）为设计量级假设，官方控规指标（floor_area_ratio 等）待补；数值与 metrics.json 一致，可在 visual/index.html 复核。