


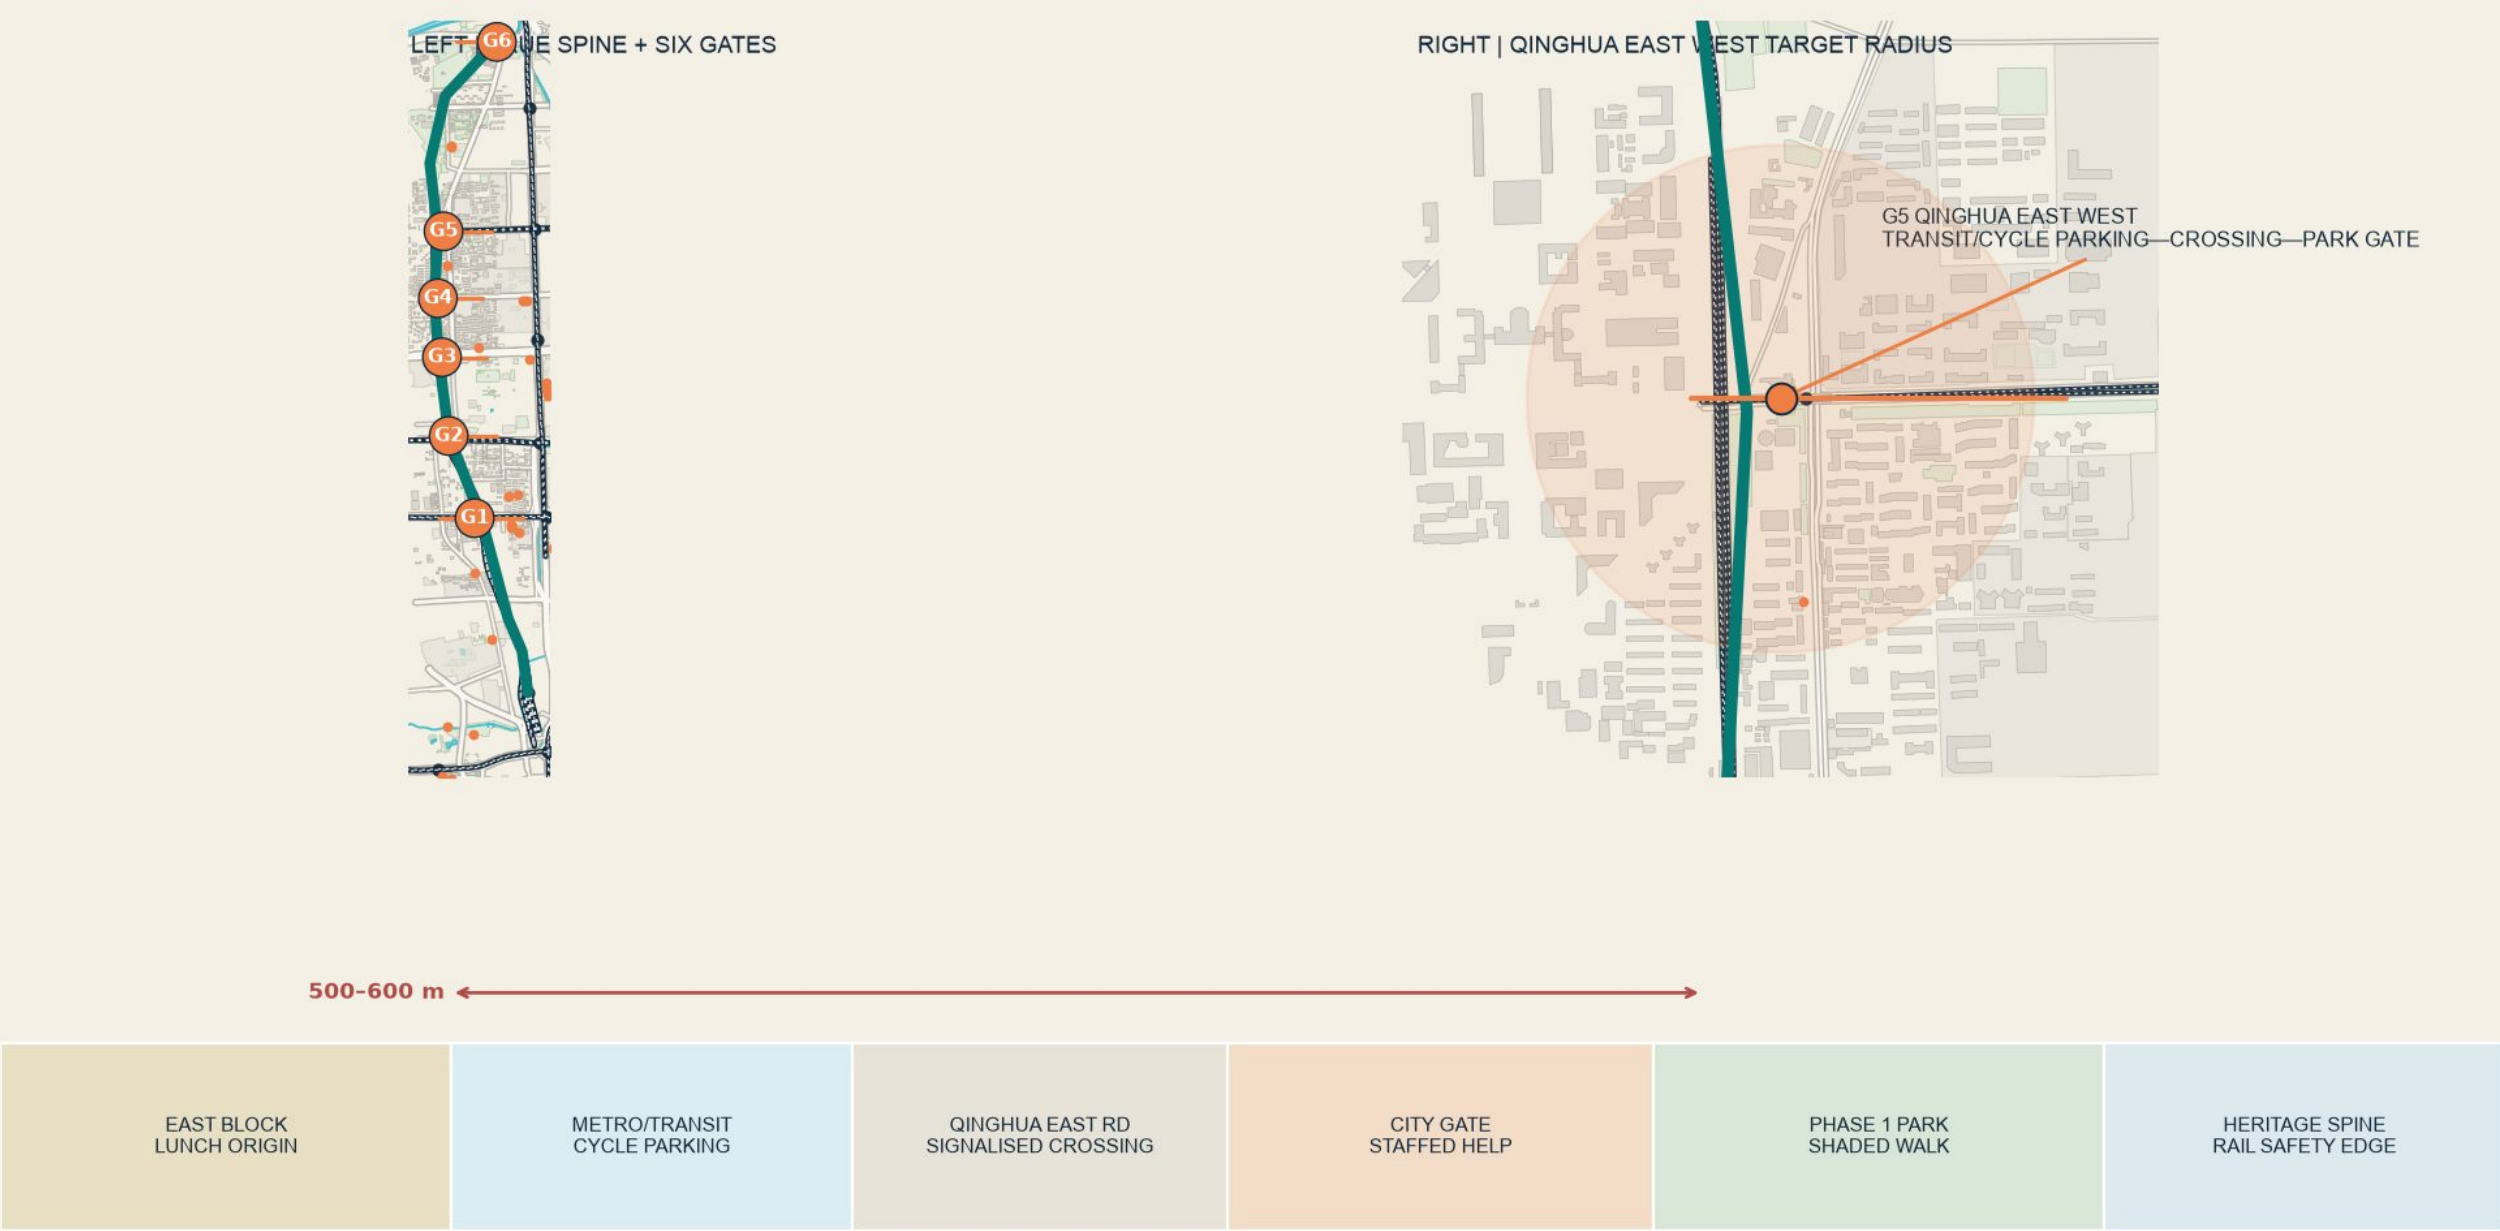

LUNCH WALK INTO THE PARK: CORRIDOR + QINGHUA EAST WEST GATE AT TWO SCALES

500-600 M IS A TARGET SERVICE RADIUS AROUND REAL PHASE 1 GATES, NOT A SURVEYED ROUTE



THE EAST-WEST SEGMENT IS A DESIGN RELATIONSHIP, TO BE REPLACED BY FIELD WALK, CROSSING-TIME, CLEAR-WIDTH + ACCESS AUDITS.
CONCEPT DESIGN - PROVISIONAL BOUNDARY - NOT AN OFFICIAL REDLINE

JING-ZHANG COMMON VERANDA - CONCEPTUAL URBAN DESIGN

REAL JING-ZHANG CORRIDOR + DELIVERY STATUS

OVERALL DESIGN LIMITS: XIZHIMEN OUTER ST—NORTH FIFTH RING; DAZHONGSI EAST/HEQING—XUEYUAN/XITUCHENG



CONCEPT DESIGN · PROVISIONAL BOUNDARY · NOT AN OFFICIAL REDLINE

- 01
PHASE 1 OPEN: ZHICHUN—QINGHUA EAST, APPROX. 2.5 KM
- 02
EXISTING SPORTS + RUN/WALK/CYCLE: AUDIT FIRST, DO NOT DUPLICATE
- 03
QINGHUA EAST SOUTH PROJECT APPROVED: ADD ACCOUNTABILITY, NOT DUPLICATE LANDSCAPE
- 04
PHASE 2 UNDER CONSTRUCTION: DO NOT PRE-CLAIM CONTINUITY
- 05
BOUNDARY + KEY AREAS REMAIN NON-OFFICIAL VECTORS

JING-ZHANG COMMON VERANDA · CONCEPTUAL URBAN DESIGN

MASTERPLAN: TRUE SPINE, SIX REAL INTERFACES, THREE VERANDA TYPES

ACTIVITY POCKETS SIT OFF THROUGH-FLOWS; BUILT PROJECTS ARE BASELINE; NO UNVERIFIED CROSS-RAIL SHORTCUTS




CONCEPT DESIGN · PROVISIONAL BOUNDARY · NOT AN OFFICIAL REDLINE

- G6 N. 5TH RING—QINGHE SOUTH EDGE
 - G5 QINGHUA EAST WEST
 - G4 CHENGFU—WUDAOKOU
 - G3 N. 4TH RING HERITAGE BRIDGE
 - G2 ZHICHUN SOUTH
 - G1 DAZHONGSI 4 QUADRANTS
- SOUTH → NORTH STATUS
STATION / PHASE 1 OPEN / APPROVED PROJECT / PHASE 2 WORKS


JING-ZHANG COMMON VERANDA · CONCEPTUAL URBAN DESIGN

THREE OFFICIAL SCALES: 43.6 KM² / 11.4 KM² / 368.4 HA

AREAS + TEXTUAL LIMITS FOLLOW THE OFFICIAL NOTICE; SUBMITTED POLYGONS REMAIN PROVISIONAL, NOT OFFICIAL VECTORS

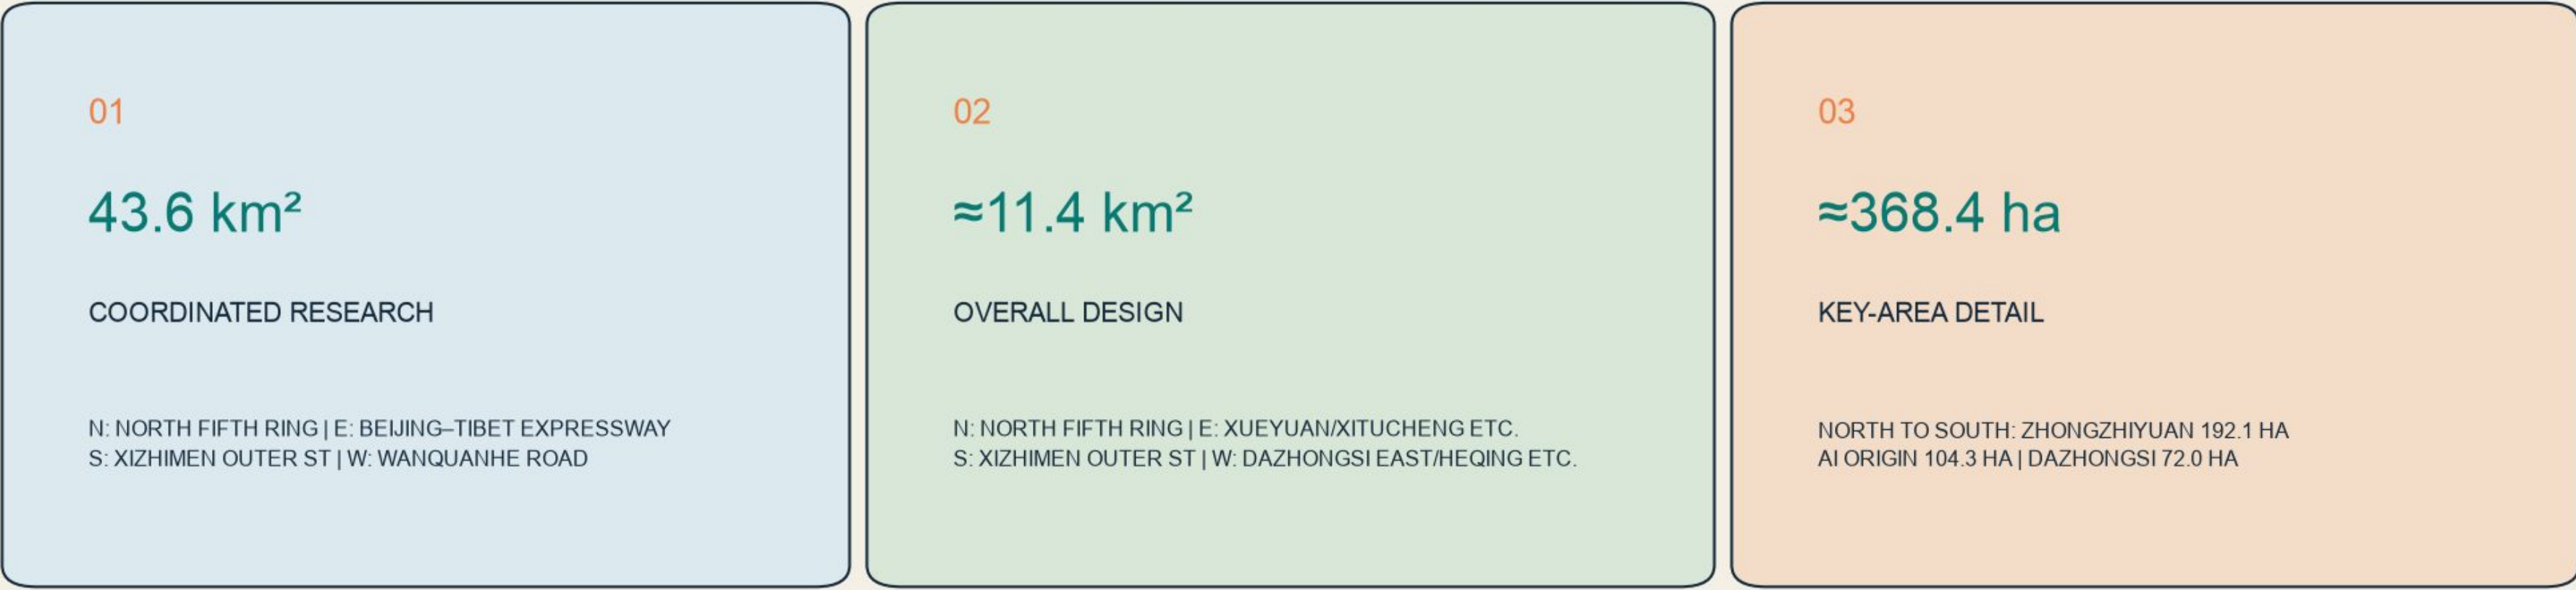

SIX OVERALL-DESIGN CIVIC CAPABILITIES, NORTH TO SOUTH

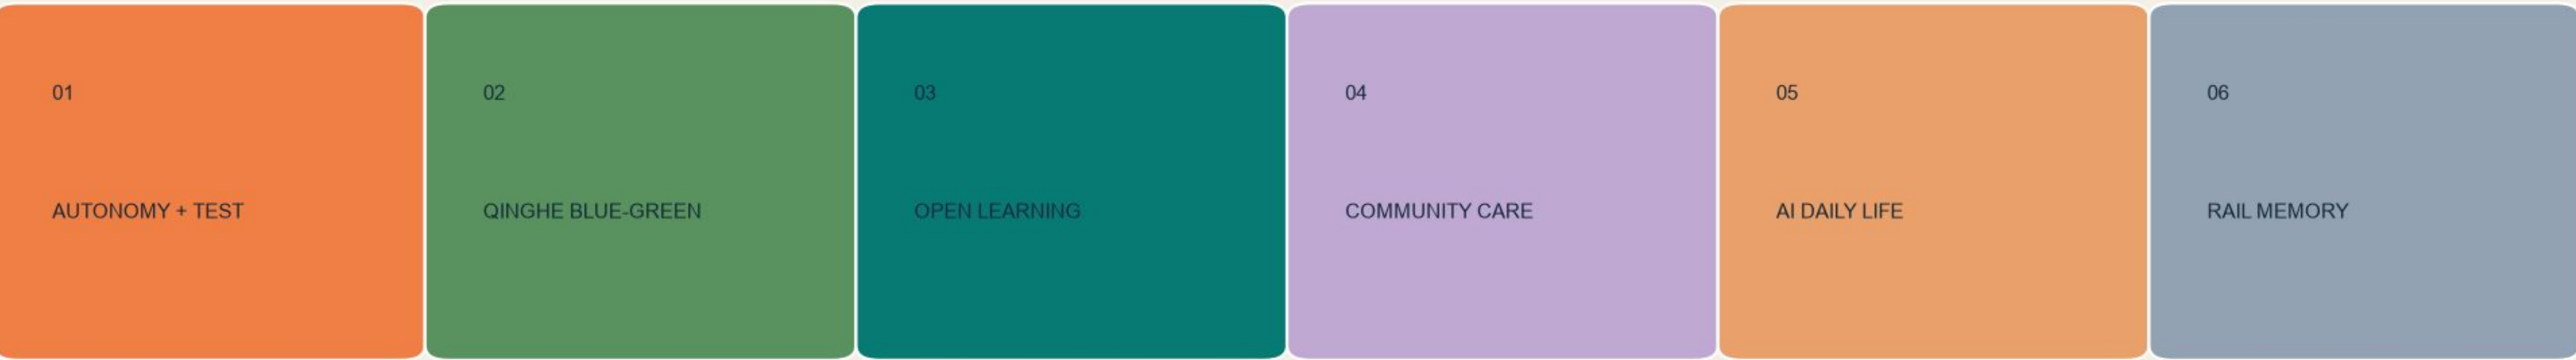

SCOPE LOGIC: 43.6 KM² FOR STRATEGIC COORDINATION; APPROX. 11.4 KM² FOR URBAN DESIGN; THREE KEY AREAS FOR SITE-LEVEL DETAIL. REPLACE ALL PROVISIONAL GEOMETRY WHEN OFFICIAL GIS/CAD ARRIVES.

CONCEPT DESIGN · PROVISIONAL BOUNDARY · NOT AN OFFICIAL REDLINE

JING-ZHANG COMMON VERANDA · CONCEPTUAL URBAN DESIGN

EXISTING BUILDING CONTEXT ≠ CONCEPTUAL RENEWAL CAPACITY

OSM BUILDINGS ORIENT THE READER; 22 STUDY UNITS TEST CAPACITY ONLY, NOT DEMOLITION OR APPROVAL



GREY=PUBLIC OSM CONTEXT (NOT A SURVEY) · TEAL=90×64 M CONCEPT STUDY UNITS · ORANGE=PROVISIONAL KEY AREA


CONCEPT DESIGN · PROVISIONAL BOUNDARY · NOT AN OFFICIAL REDLINE

JING-ZHANG COMMON VERANDA · CONCEPTUAL URBAN DESIGN

THREE KEY AREAS: REAL LOCATIONS, REAL INTERFACES, CONCEPT MOVES

NORTH TO SOUTH: ZHONGZHIYUAN—AI ORIGIN—DAZHONGSI; BASE MAP ORIENTS, COLOURED MOVES REMAIN REPLACEABLE

01 ZHONGZHIYUAN TEST VERANDA

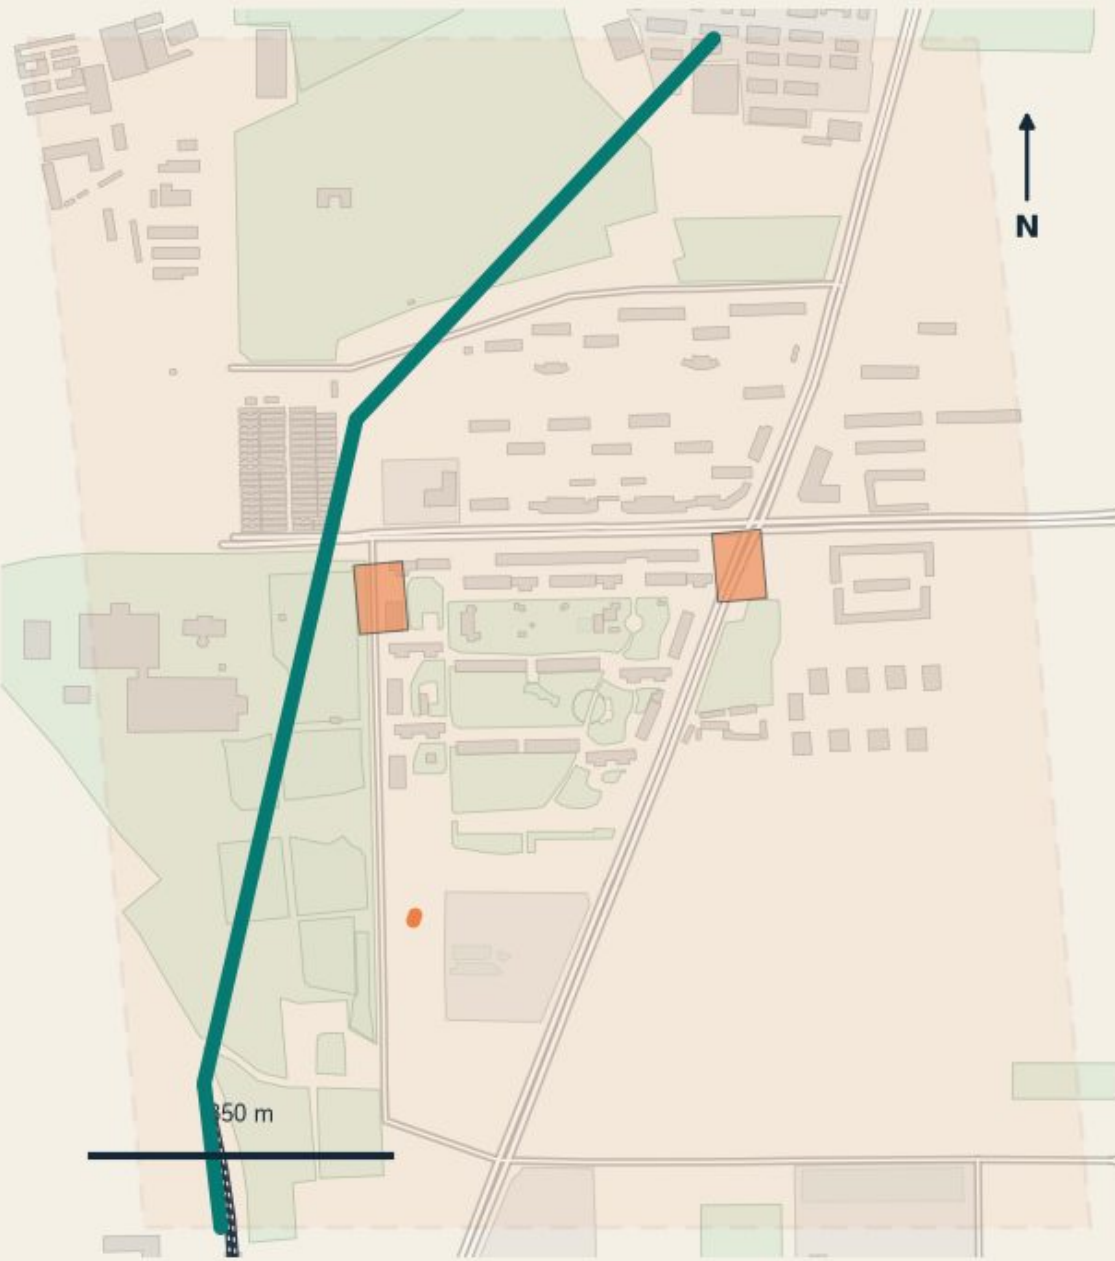

CONTROLLED TESTING, QINGHE ECOLOGY + PHASE 2 INTERFACE SOUTH OF THE FIFTH RING

CONCEPT DESIGN · PROVISIONAL BOUNDARY · NOT AN OFFICIAL REDLINE

02 AI ORIGIN LEARNING VERANDA



WUDAOKOU—QINGHUA EAST WEST: REAL STATIONS, CITY STREETS + PHASE 1 PARK

03 DAZHONGSI LIVING VERANDA



DAZHONGSI FOUR QUADRANTS: RAIL TRANSFER, ACTIVE GROUND FLOORS + COMMUNITY WALKING

JING-ZHANG COMMON VERANDA · CONCEPTUAL URBAN DESIGN

ZHONGZHIYUAN TEST VERANDA

CONTROLLED TESTING, QINGHE ECOLOGY + PHASE 2 INTERFACE SOUTH OF THE FIFTH RING



CONCEPT DESIGN · PROVISIONAL BOUNDARY · NOT AN OFFICIAL REDLINE

- 01 TEST INTAKE + EXPLANATION
- 02 LOW-SPEED ROBOTICS SANDBOX
- 03 RED-TEAM COURTYARD
- 04 ENERGY + SAFETY AUDIT
- 05 PUBLIC OBSERVATION VERANDA
- 06 HUMAN TAKEOVER DESK


PHYSICAL RELATION
TEST VEHICLES ARE PHYSICALLY SEPARATED FROM PUBLIC WALKING; STOP ON BOUNDARY BREACH, LOST LINK OR MISSING HUMAN TAKEOVER.

GREY+OSM CONTEXT (NOT SURVEY) | DARK+RAIL | ORANGE+REAL STREET INTERFACE | COLOUR+CONCEPT CAPACITY

JING-ZHANG COMMON VERANDA · CONCEPTUAL URBAN DESIGN

AI ORIGIN LEARNING VERANDA

WUDAOKOU—QINGHUA EAST WEST: REAL STATIONS, CITY STREETS + PHASE 1 PARK

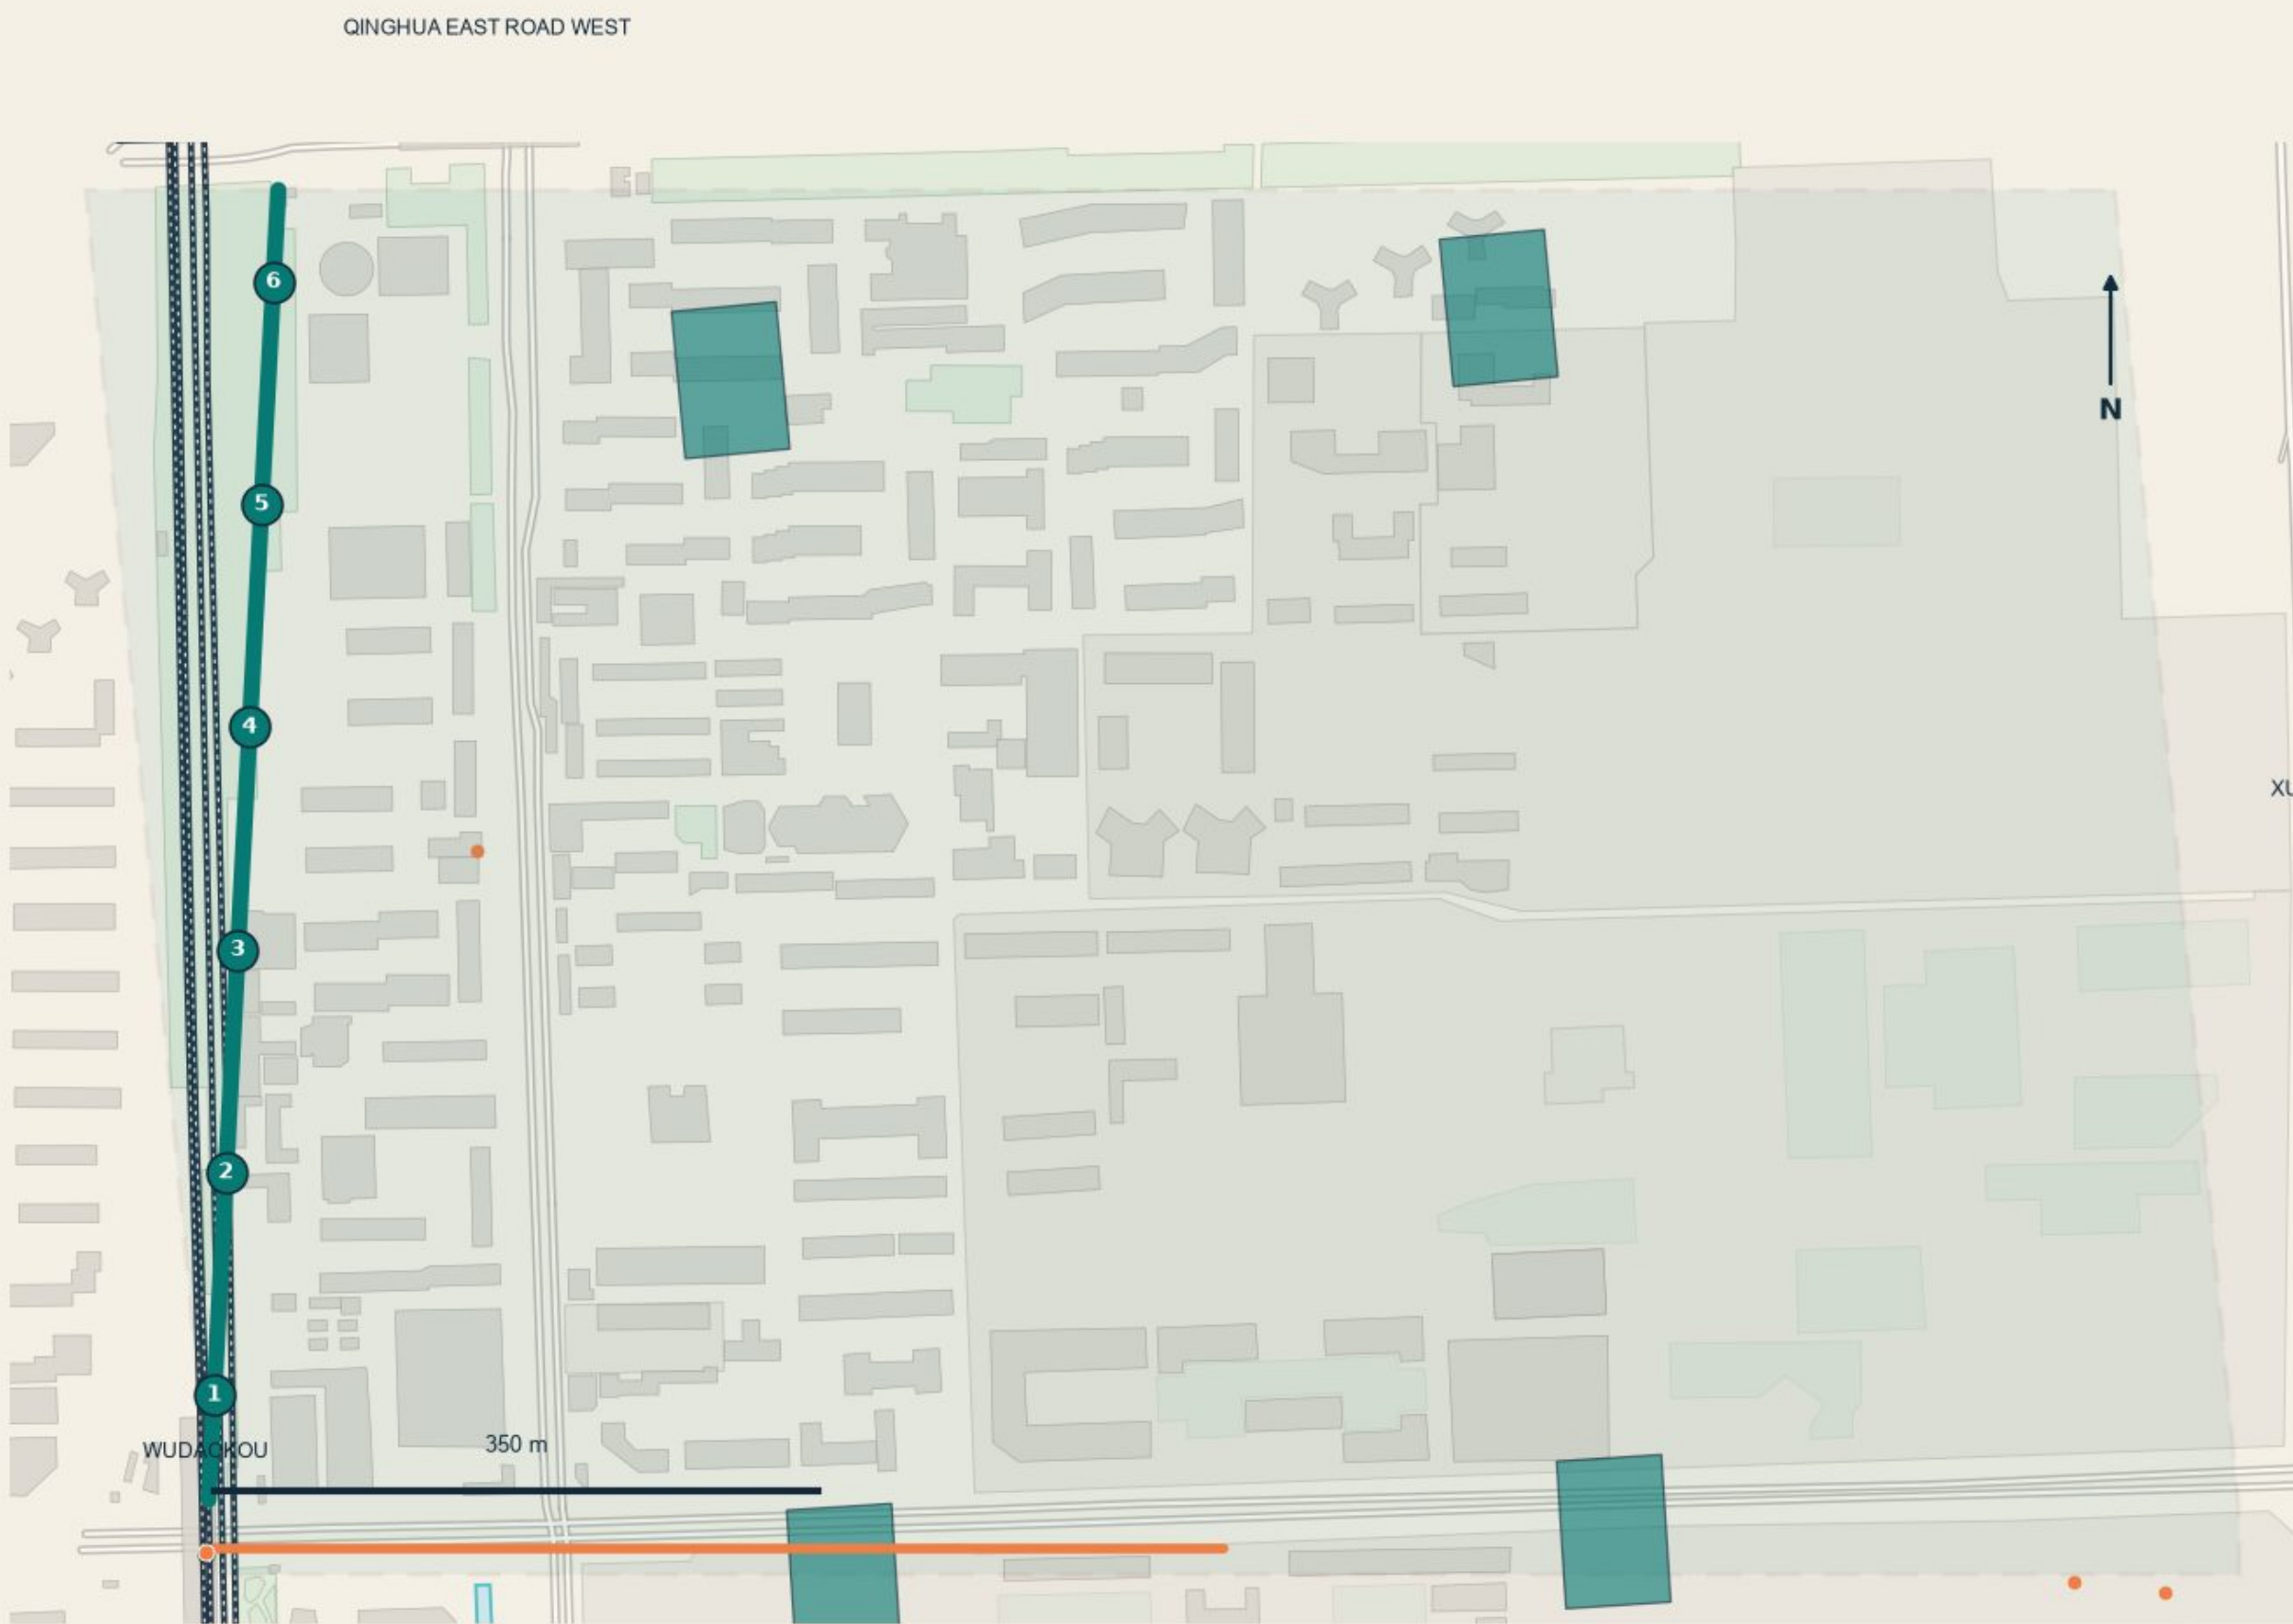

CONCEPT DESIGN · PROVISIONAL BOUNDARY · NOT AN OFFICIAL REDLINE

- 01 OPEN-SOURCE RELEASE GATE
- 02 PUBLIC LEARNING STEPS
- 03 RESEARCH-TO-CIVIC TABLE
- 04 ACCESSIBLE LEARNING LOOP
- 05 RAIL RAIN GARDEN
- 06 COMMUNITY REVIEW DESK


PHYSICAL RELATION
EAST-WEST LINKS USE REAL INTERFACES SUCH AS CHENGFU AND QINGHUA EAST; NO AT-GRADE CROSSING OF OPERATING RAIL.

GREY+OSM CONTEXT (NOT SURVEY) | DARK+RAIL | ORANGE+REAL STREET INTERFACE | COLOUR+CONCEPT CAPACITY

JING-ZHANG COMMON VERANDA · CONCEPTUAL URBAN DESIGN

DAZHONGSI LIVING VERANDA

DAZHONGSI FOUR QUADRANTS: RAIL TRANSFER, ACTIVE GROUND FLOORS + COMMUNITY WALKING

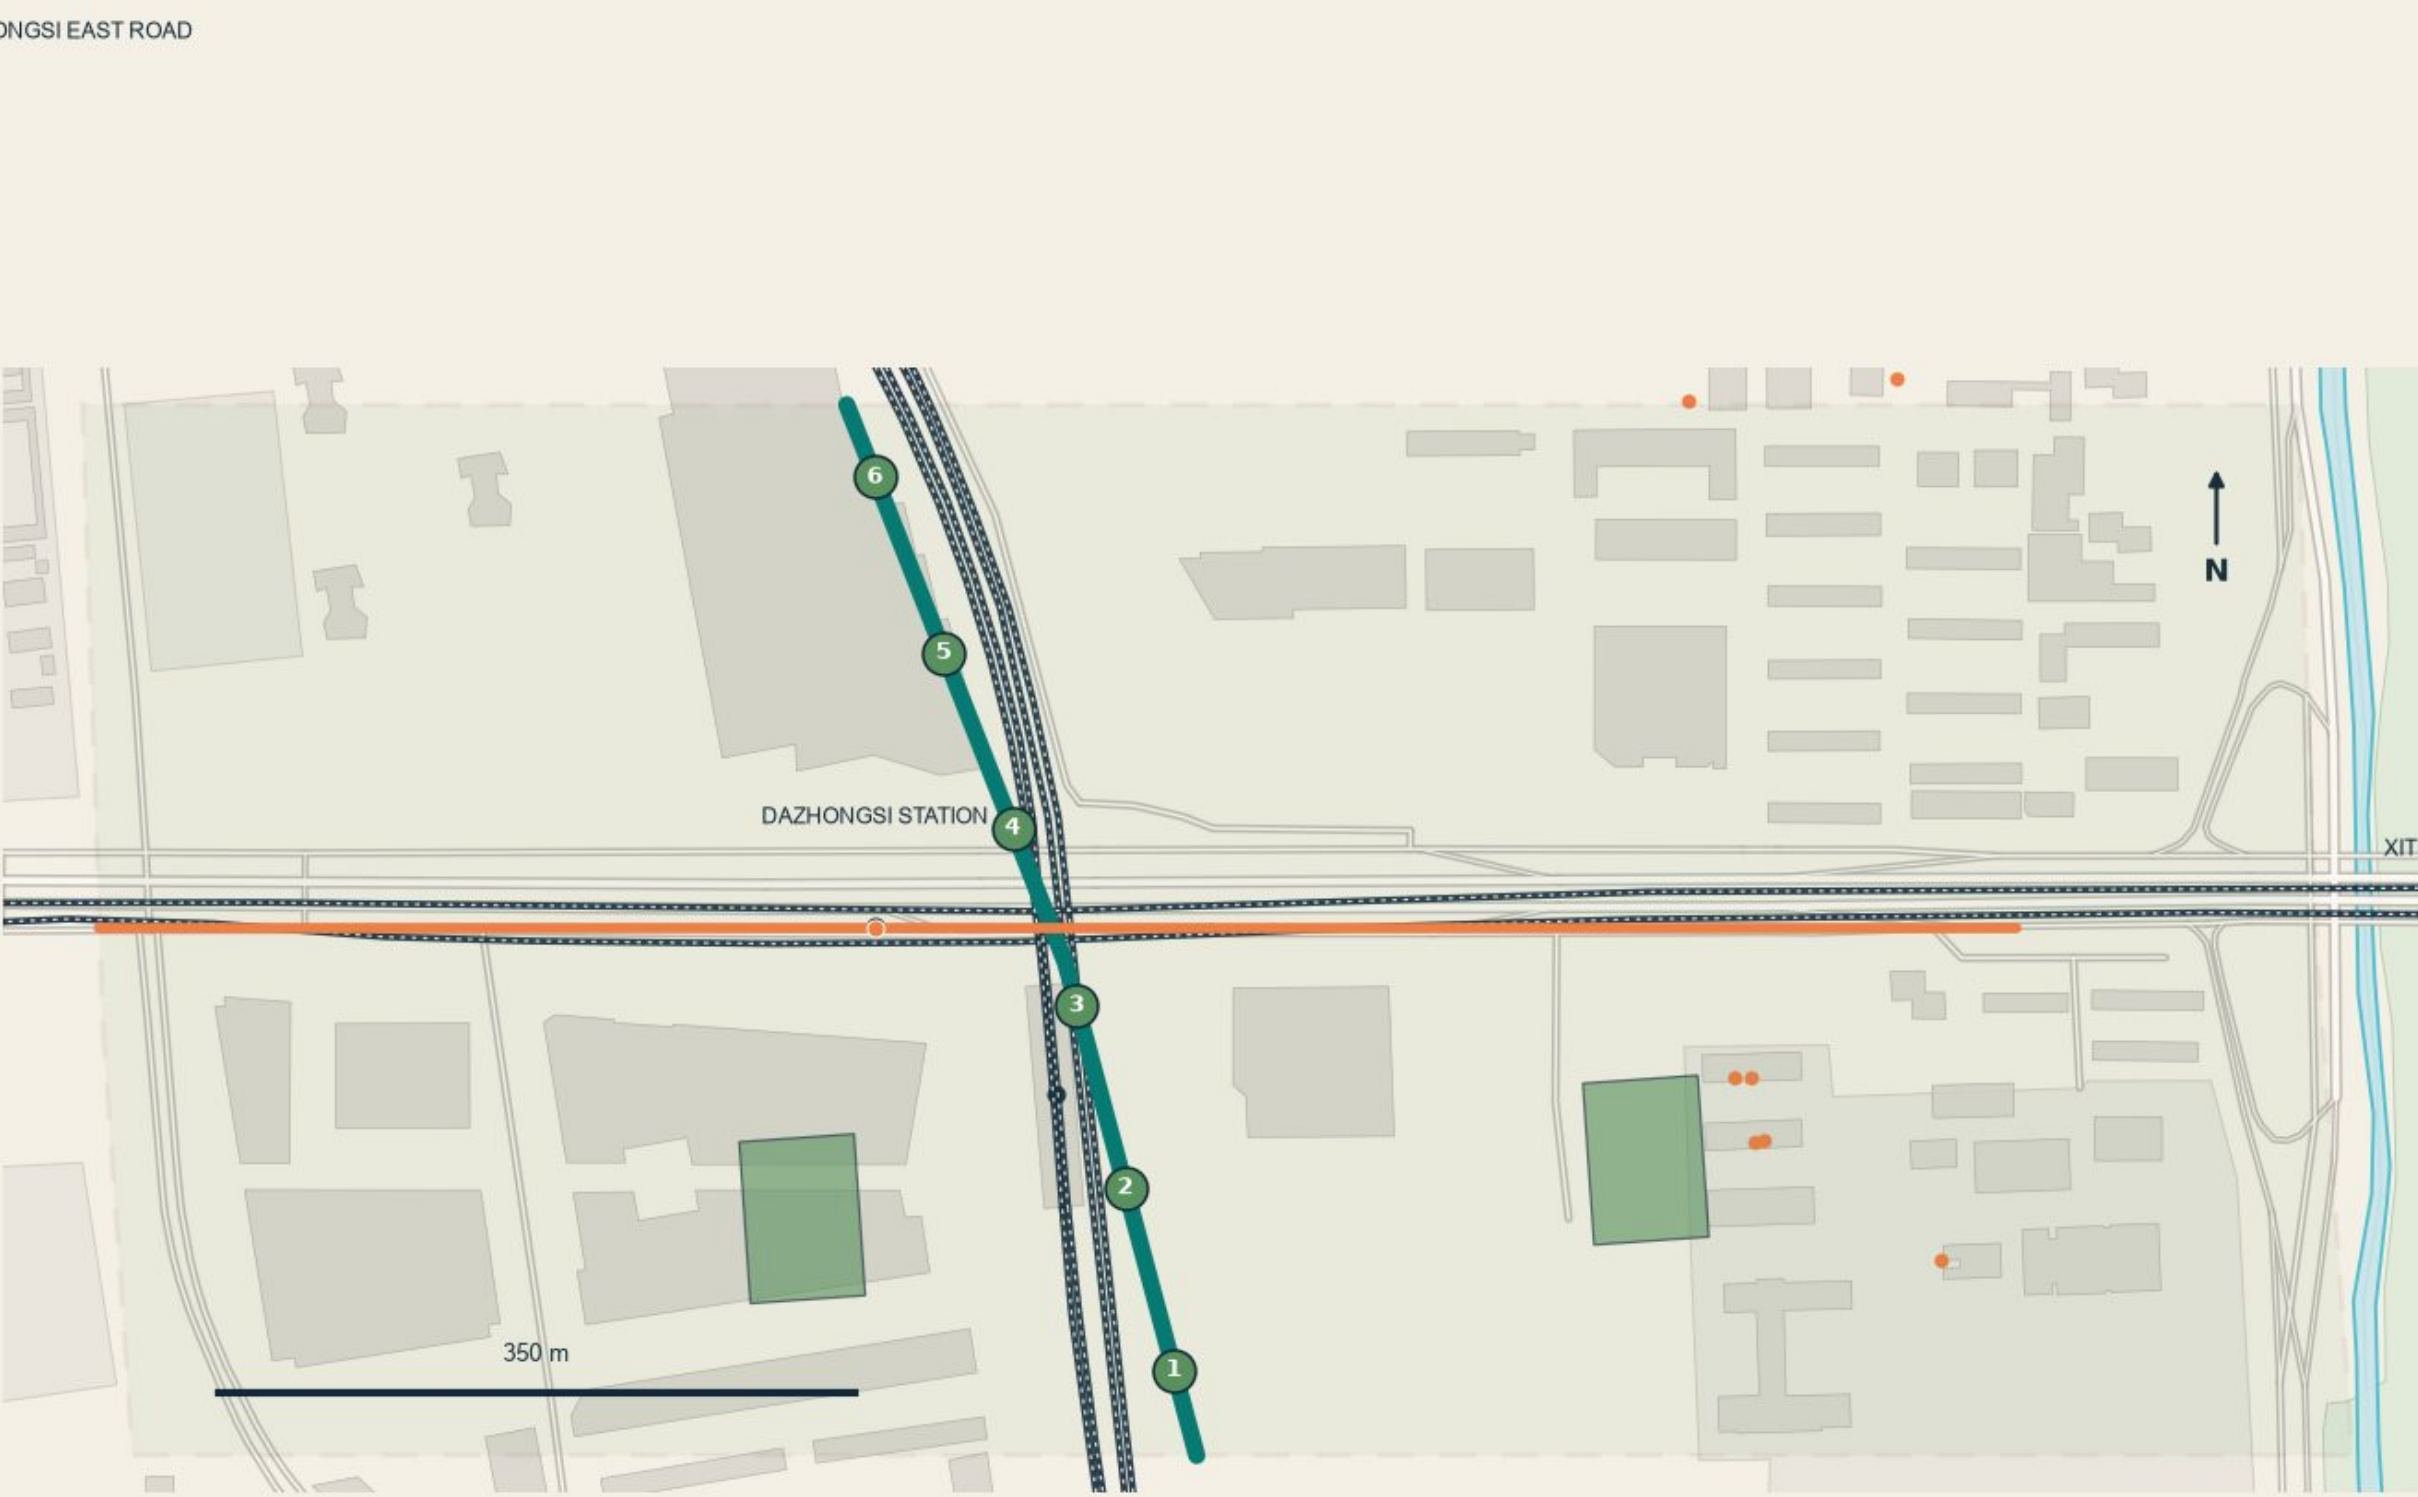

CONCEPT DESIGN · PROVISIONAL BOUNDARY · NOT AN OFFICIAL REDLINE

- 01 TRANSIT ARRIVAL LIVING ROOM
- 02 RESPONSIBLE RETAIL DESK
- 03 ELDER SERVICE NAVIGATION
- 04 CENTENNIAL CIVIC LEDGER CLOCK
- 05 NIGHT CO-GOVERNANCE GARDEN
- 06 COMMUNITY APPEAL DESK


PHYSICAL RELATION
AUDIT EXISTING FOUR-QUADRANT ROUTES, ENTRANCES + CYCLE PARKING FIRST, DO NOT INVENT A CROSS-RAIL SHORTCUT.

GREY+OSM CONTEXT (NOT SURVEY) | DARK+RAIL | ORANGE+REAL STREET INTERFACE | COLOUR+CONCEPT CAPACITY

JING-ZHANG COMMON VERANDA · CONCEPTUAL URBAN DESIGN

LUNCH WALK INTO THE PARK: CORRIDOR + QINGHUA EAST WEST GATE AT TWO SCALES

500–600 M IS A TARGET SERVICE RADIUS AROUND REAL PHASE 1 GATES, NOT A SURVEYED ROUTE

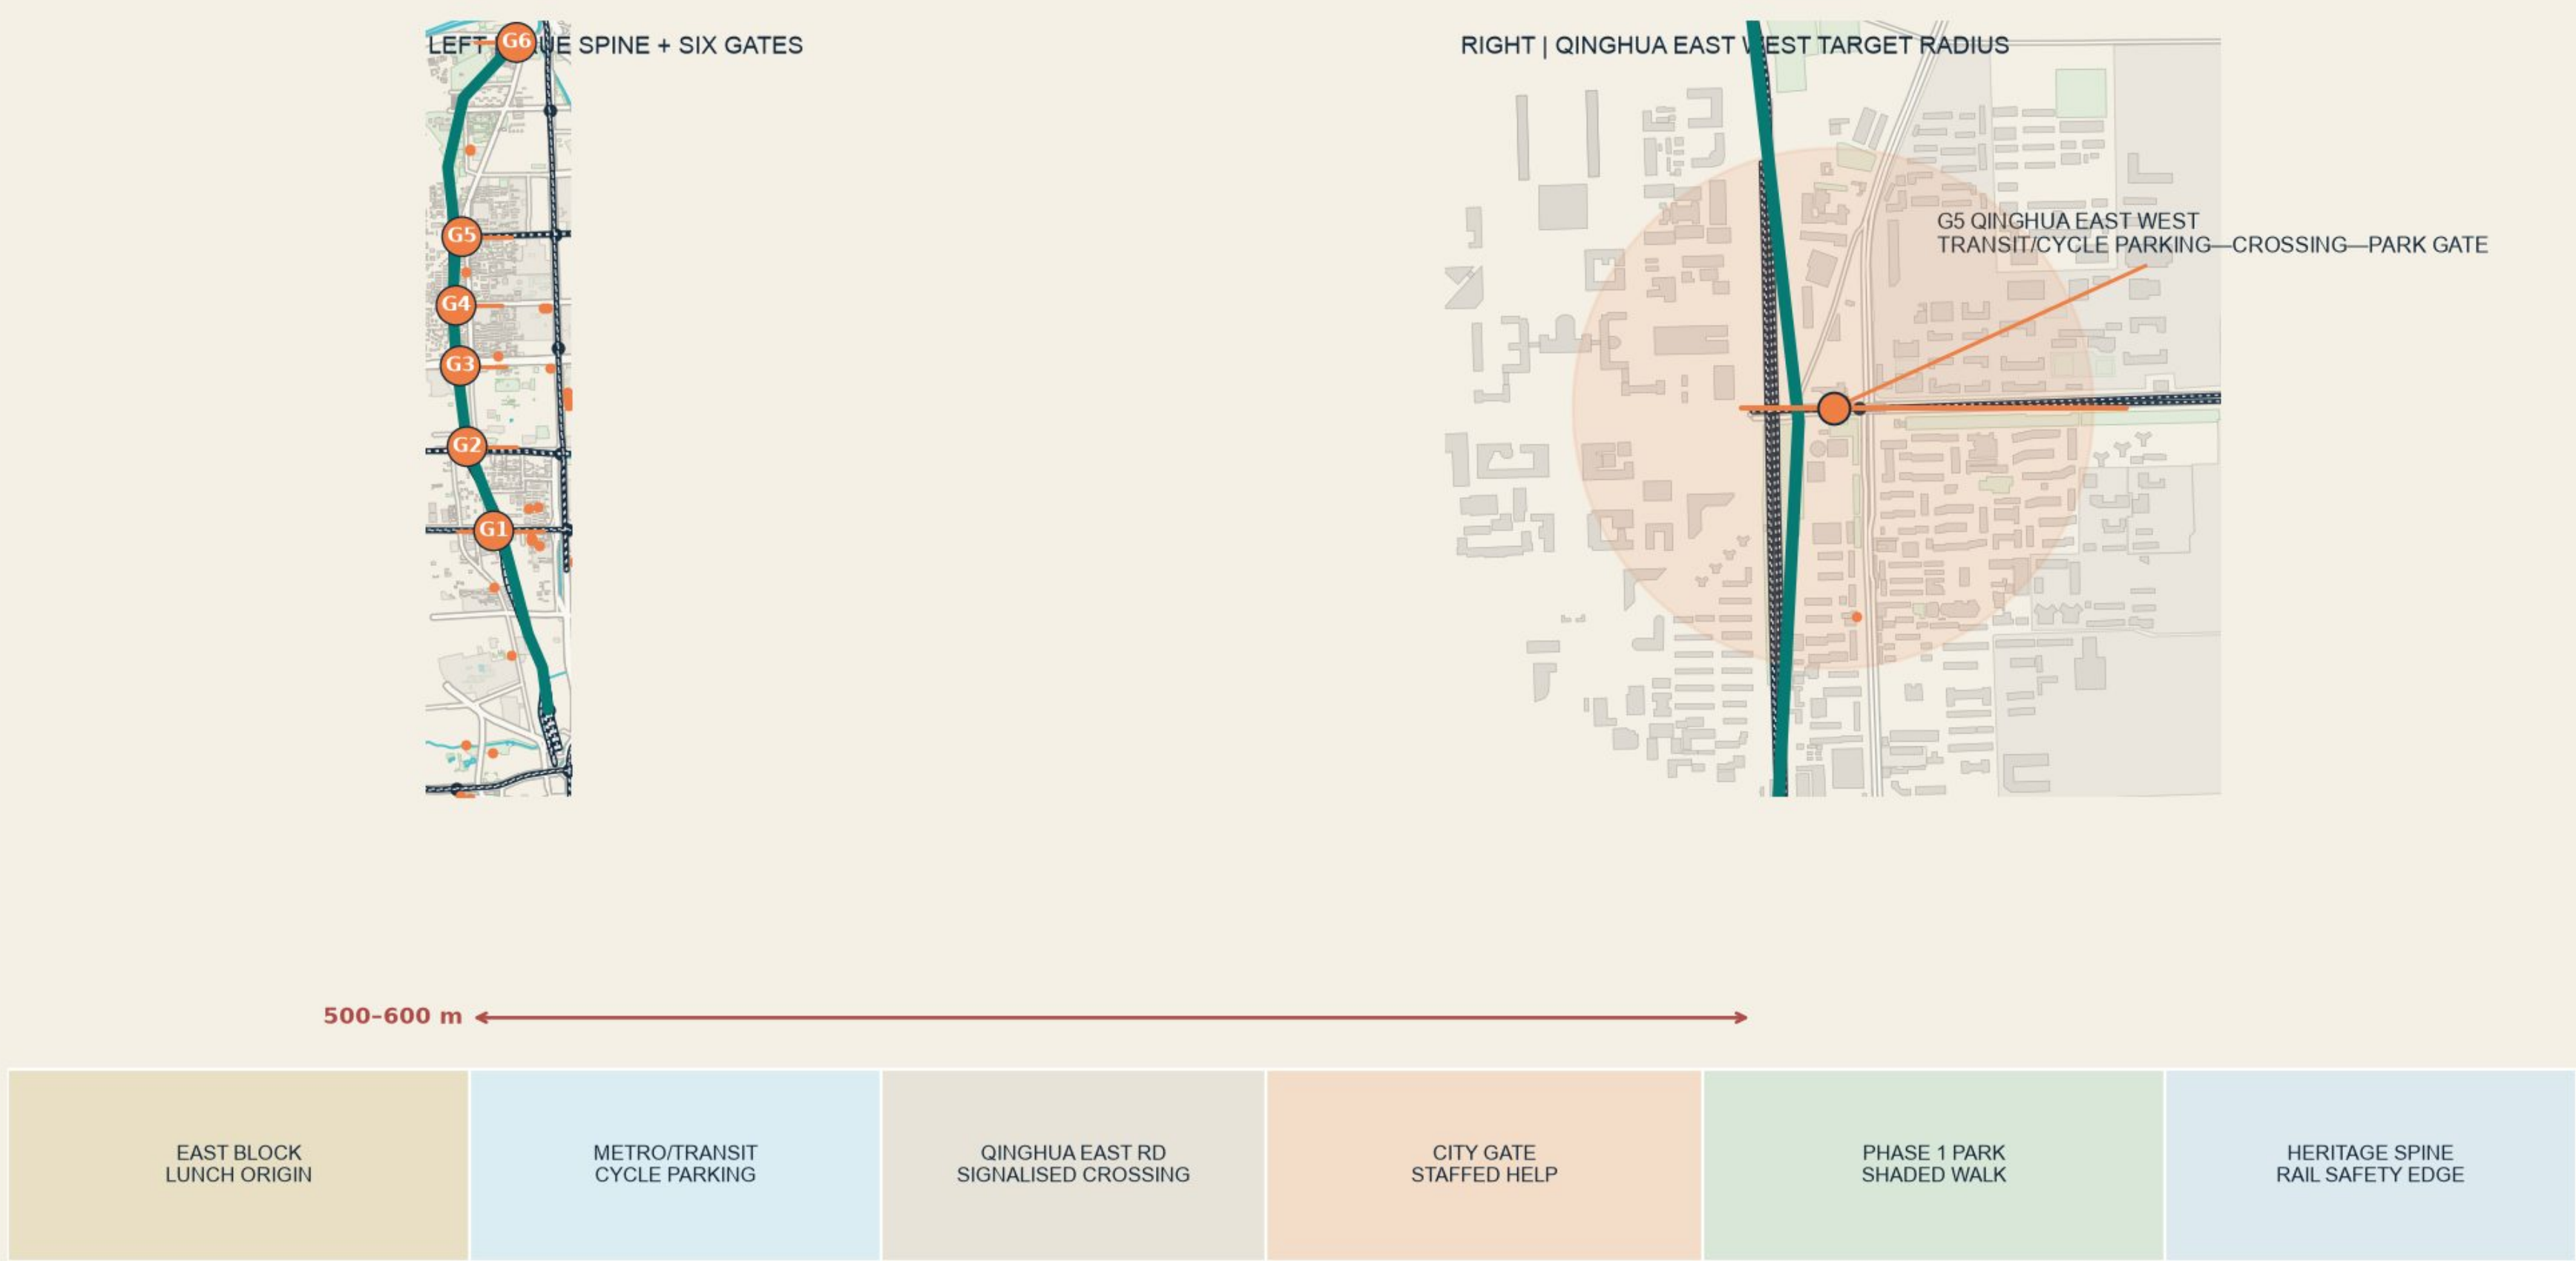


THE EAST–WEST SEGMENT IS A DESIGN RELATIONSHIP, TO BE REPLACED BY FIELD WALK, CROSSING-TIME, CLEAR-WIDTH + ACCESS AUDITS.
CONCEPT DESIGN · PROVISIONAL BOUNDARY · NOT AN OFFICIAL REDLINE

JING-ZHANG COMMON VERANDA · CONCEPTUAL URBAN DESIGN

PUBLIC-REALM SECTION: THROUGH-MOVEMENT, ACTIVITY + RAIL SAFETY DO NOT COLLIDE

CONCEPT MODULES SHOW RELATIONSHIPS + PRIORITY ONLY, VERIFY CLEAR WIDTH, TREES, UTILITIES, FIRE + RAIL CONDITIONS

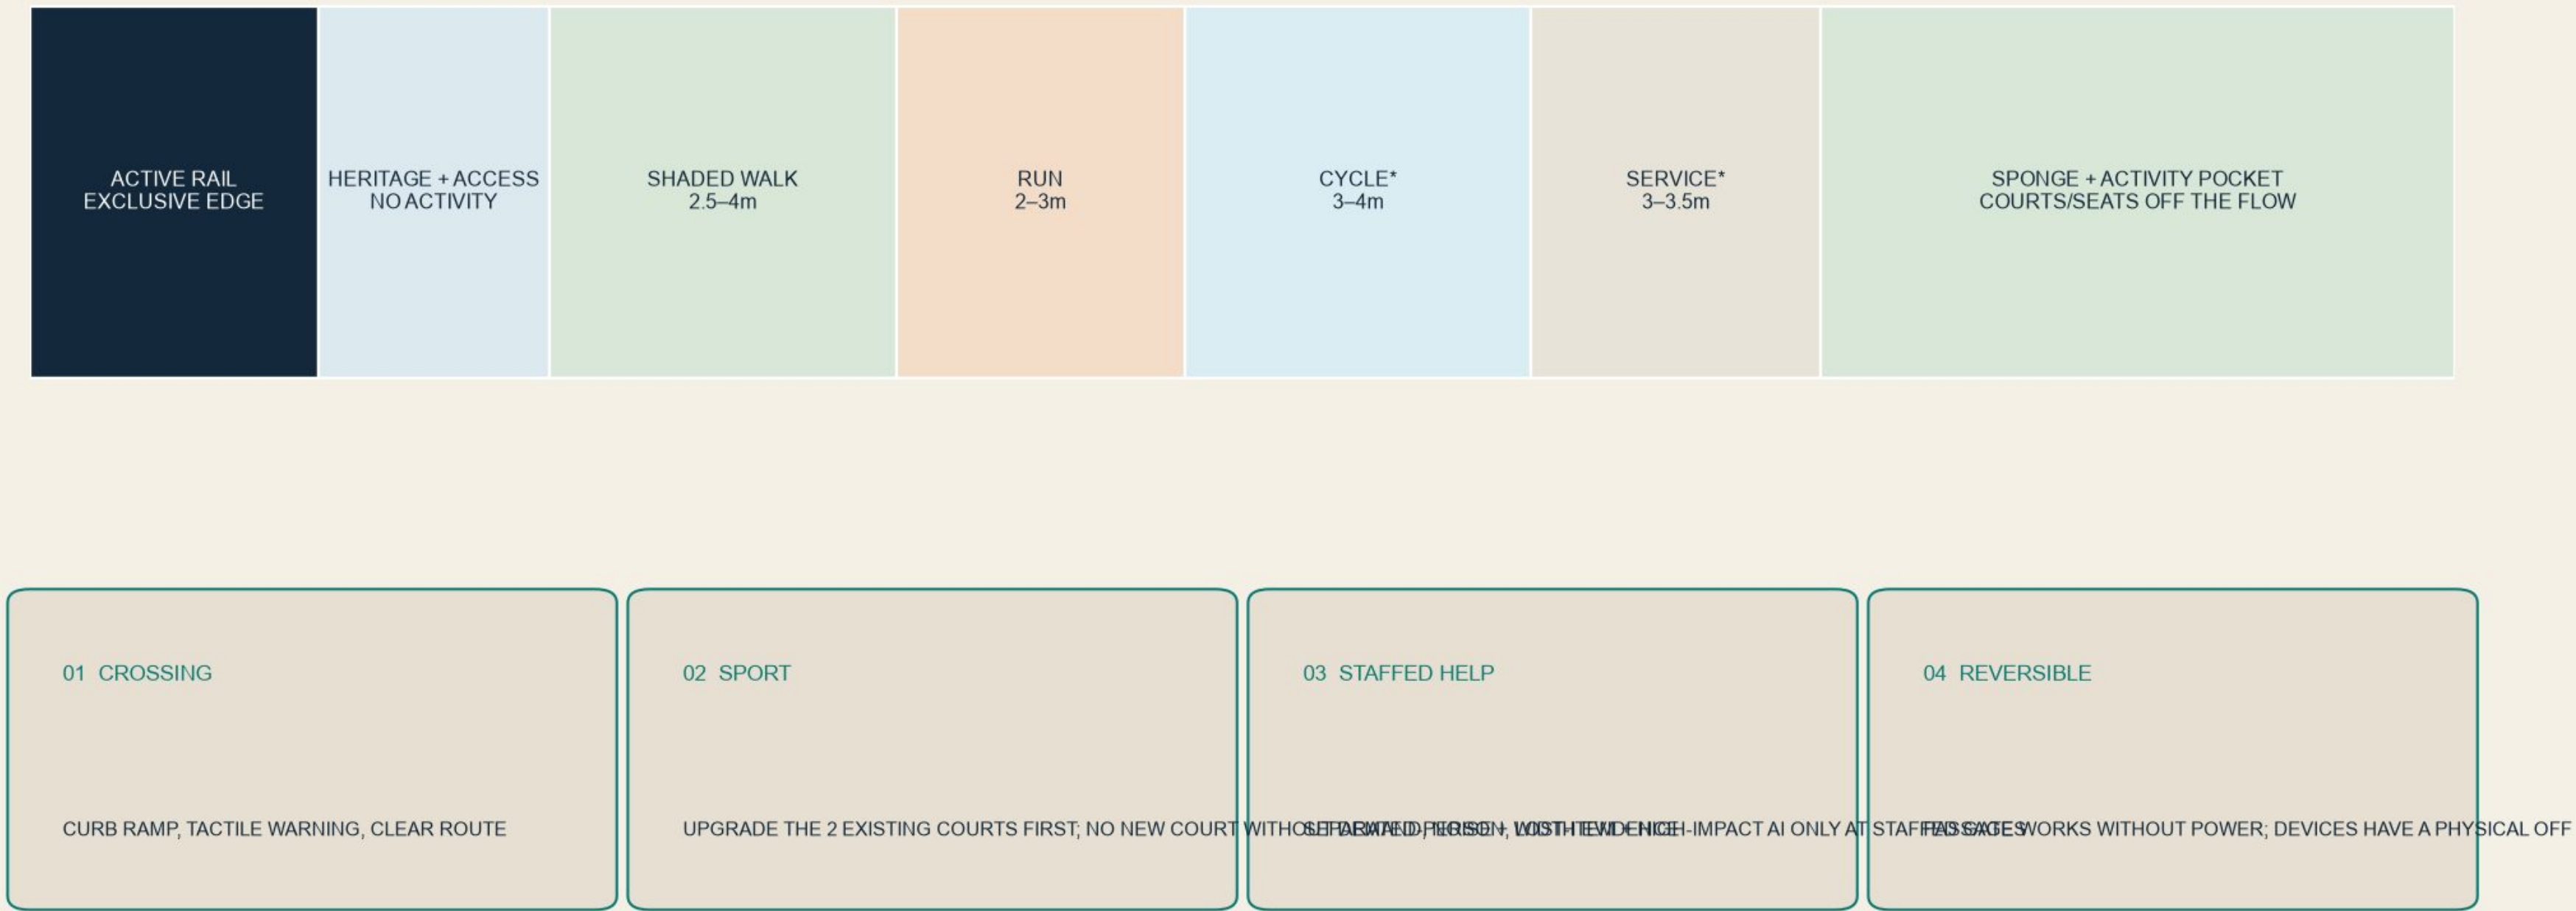

CONCEPT DESIGN · PROVISIONAL BOUNDARY · NOT AN OFFICIAL REDLINE

JING-ZHANG COMMON VERANDA · CONCEPTUAL URBAN DESIGN

PEOPLE, VEHICLES + RAIL: ONE PATH CANNOT DO EVERYTHING

WALK, RUN, CYCLE, SERVICE + RAIL ARE SEPARATED BY SPEED AND RISK; CYCLES BYPASS ON CITY STREETS WHERE WIDTH FAILS




* NOT MANDATORY ALONG THE WHOLE LINE; CYCLES USE CITY STREETS WHERE WIDTH FAILS; SERVICE VEHICLES ENTER ONLY IN MAINTENANCE WINDOWS. COURTS, SEATS + QUEUES STAY OFF THE THROUGH-BANDS.
CONCEPT DESIGN · PROVISIONAL BOUNDARY · NOT AN OFFICIAL REDLINE

JING-ZHANG COMMON VERANDA · CONCEPTUAL URBAN DESIGN

BLUE-GREEN CIVIC REALM: A SHADED, SPONGE-LIKE, INHABITABLE HERITAGE CORRIDOR

THE LOW-TECH BASE WORKS WITHOUT POWER; SMART FACILITIES REMAIN A SEPARATE SWITCHABLE SERVICE LAYER

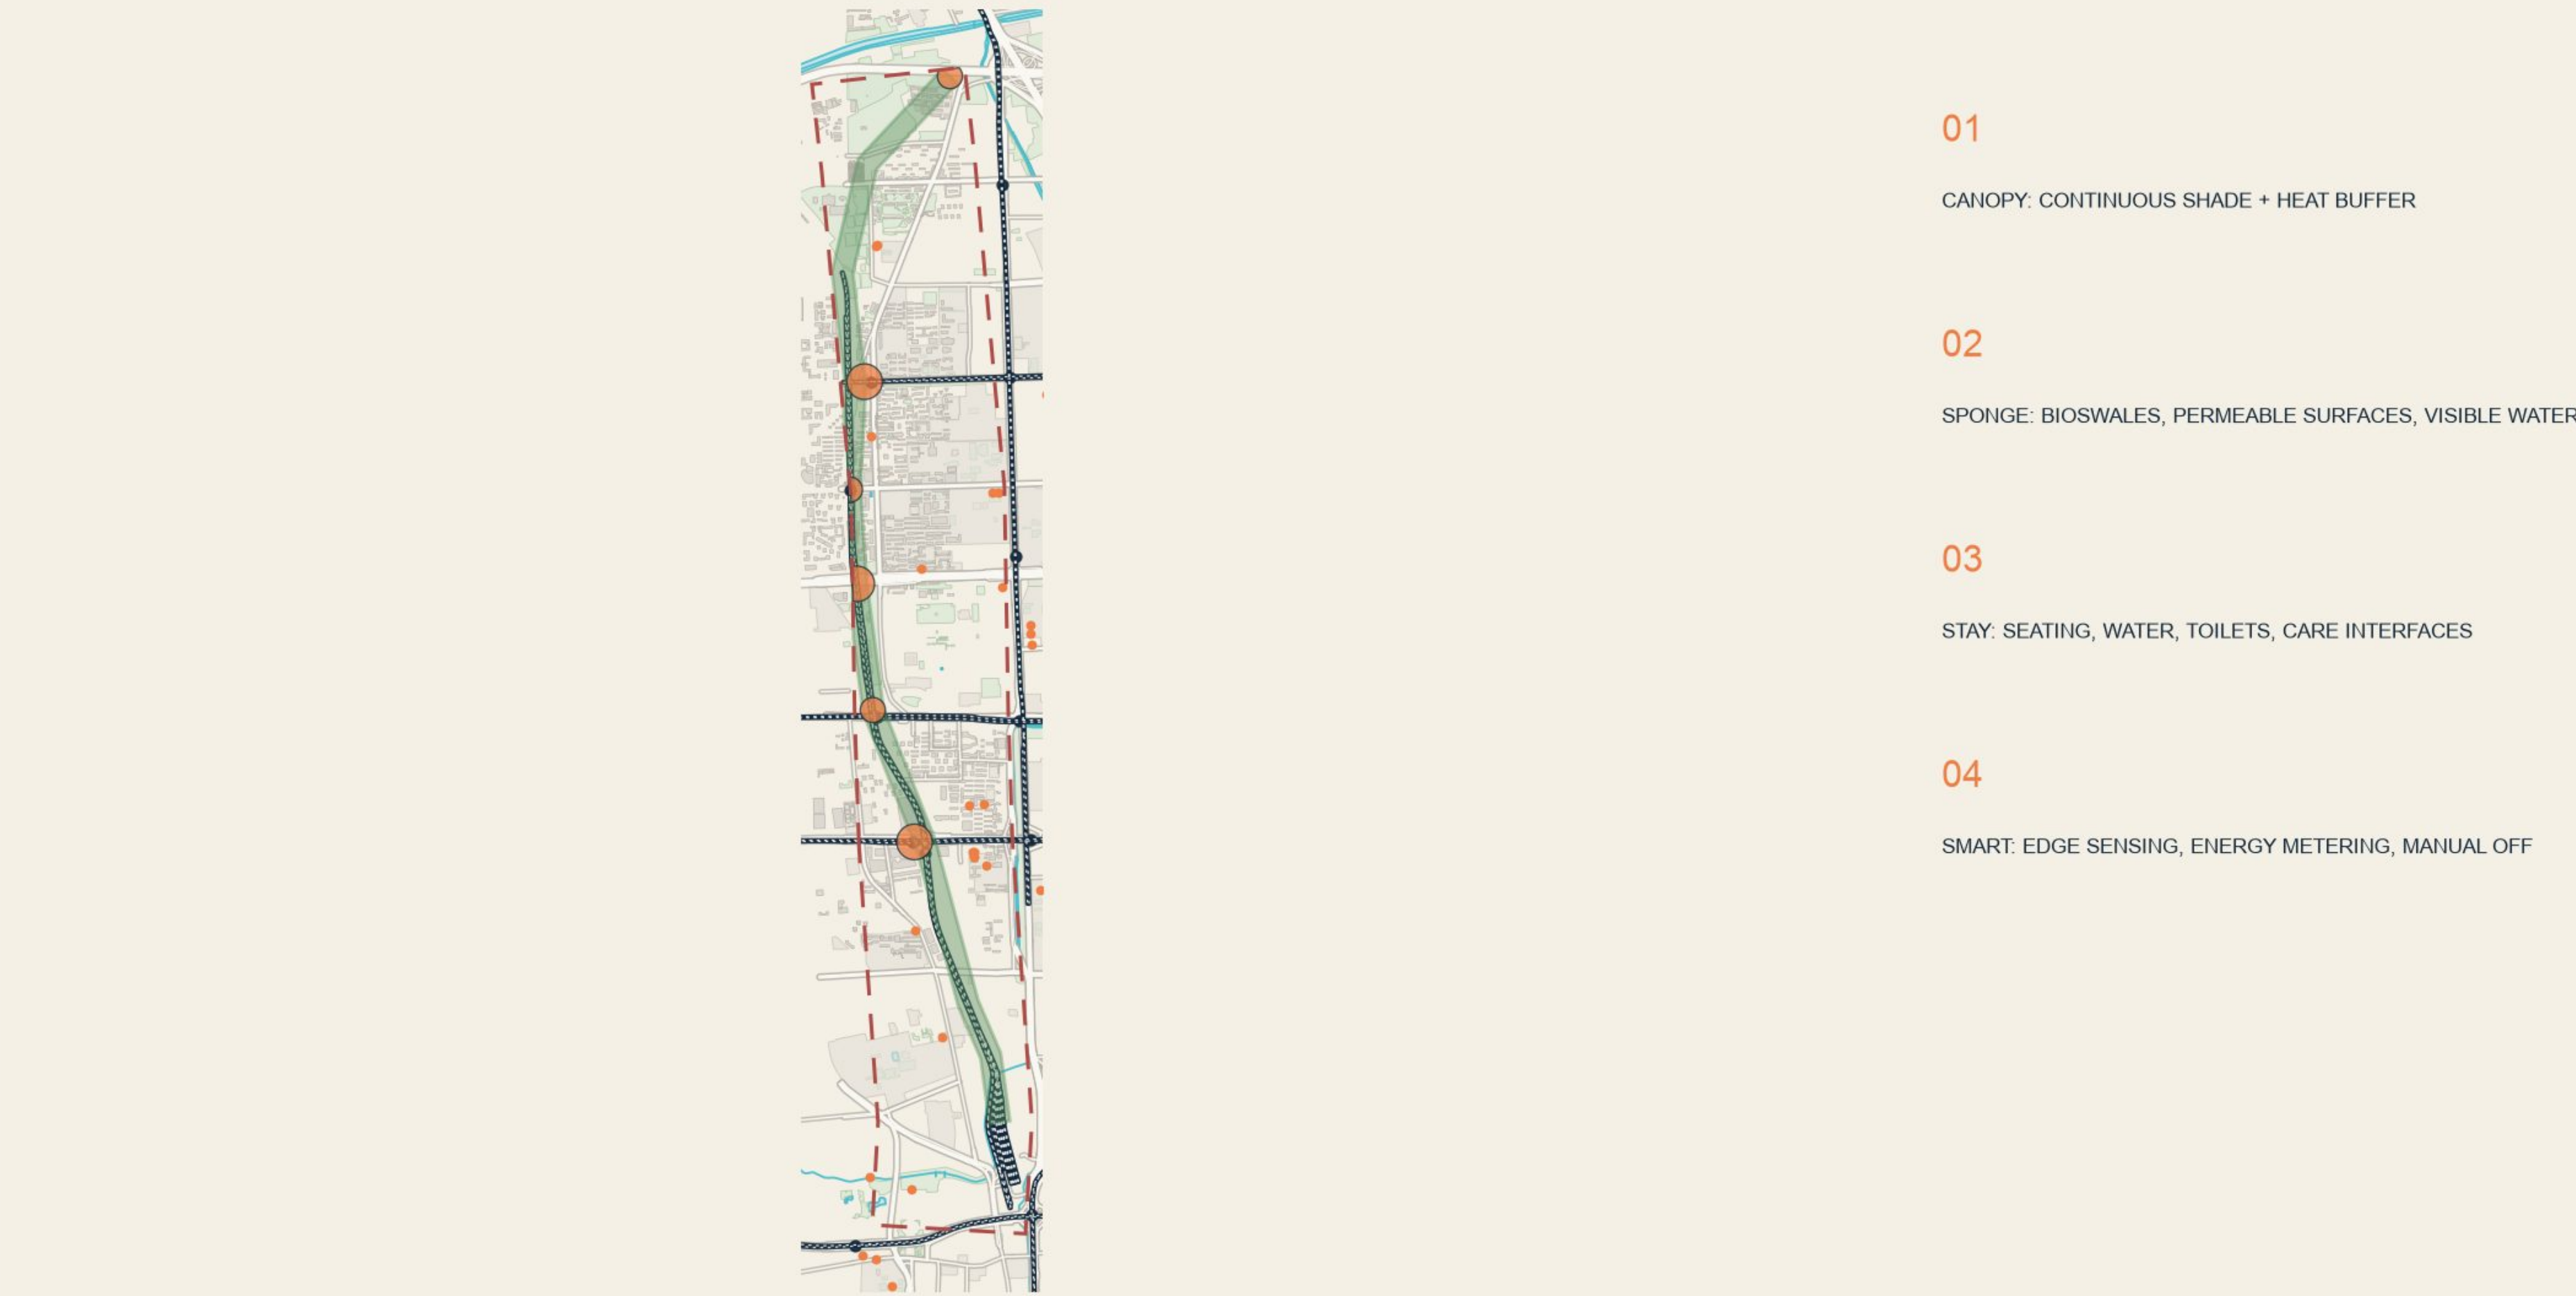

CONCEPT DESIGN · PROVISIONAL BOUNDARY · NOT AN OFFICIAL REDLINE

JING-ZHANG COMMON VERANDA · CONCEPTUAL URBAN DESIGN



TWELVE PERCEPTIBLE SCENARIOS: SPACE—DATA—HUMAN—EXIT

SCENARIOS ARE NOT A FEATURE LIST, EACH IS A CIVIC SERVICE CONTRACT WITH PLACE, OWNER AND STOP CONDITION




CONCEPT DESIGN · PROVISIONAL BOUNDARY · NOT AN OFFICIAL REDLINE

JING-ZHANG COMMON VERANDA · CONCEPTUAL URBAN DESIGN

AI ECOSYSTEM: RESEARCH—TEST—ADOPTION—PUBLIC RETURN

INNOVATION SERVICES MUST PRODUCE VISIBLE, VERIFIABLE CIVIC VALUE—NOT ONLY FIRM-LEVEL BENEFITS

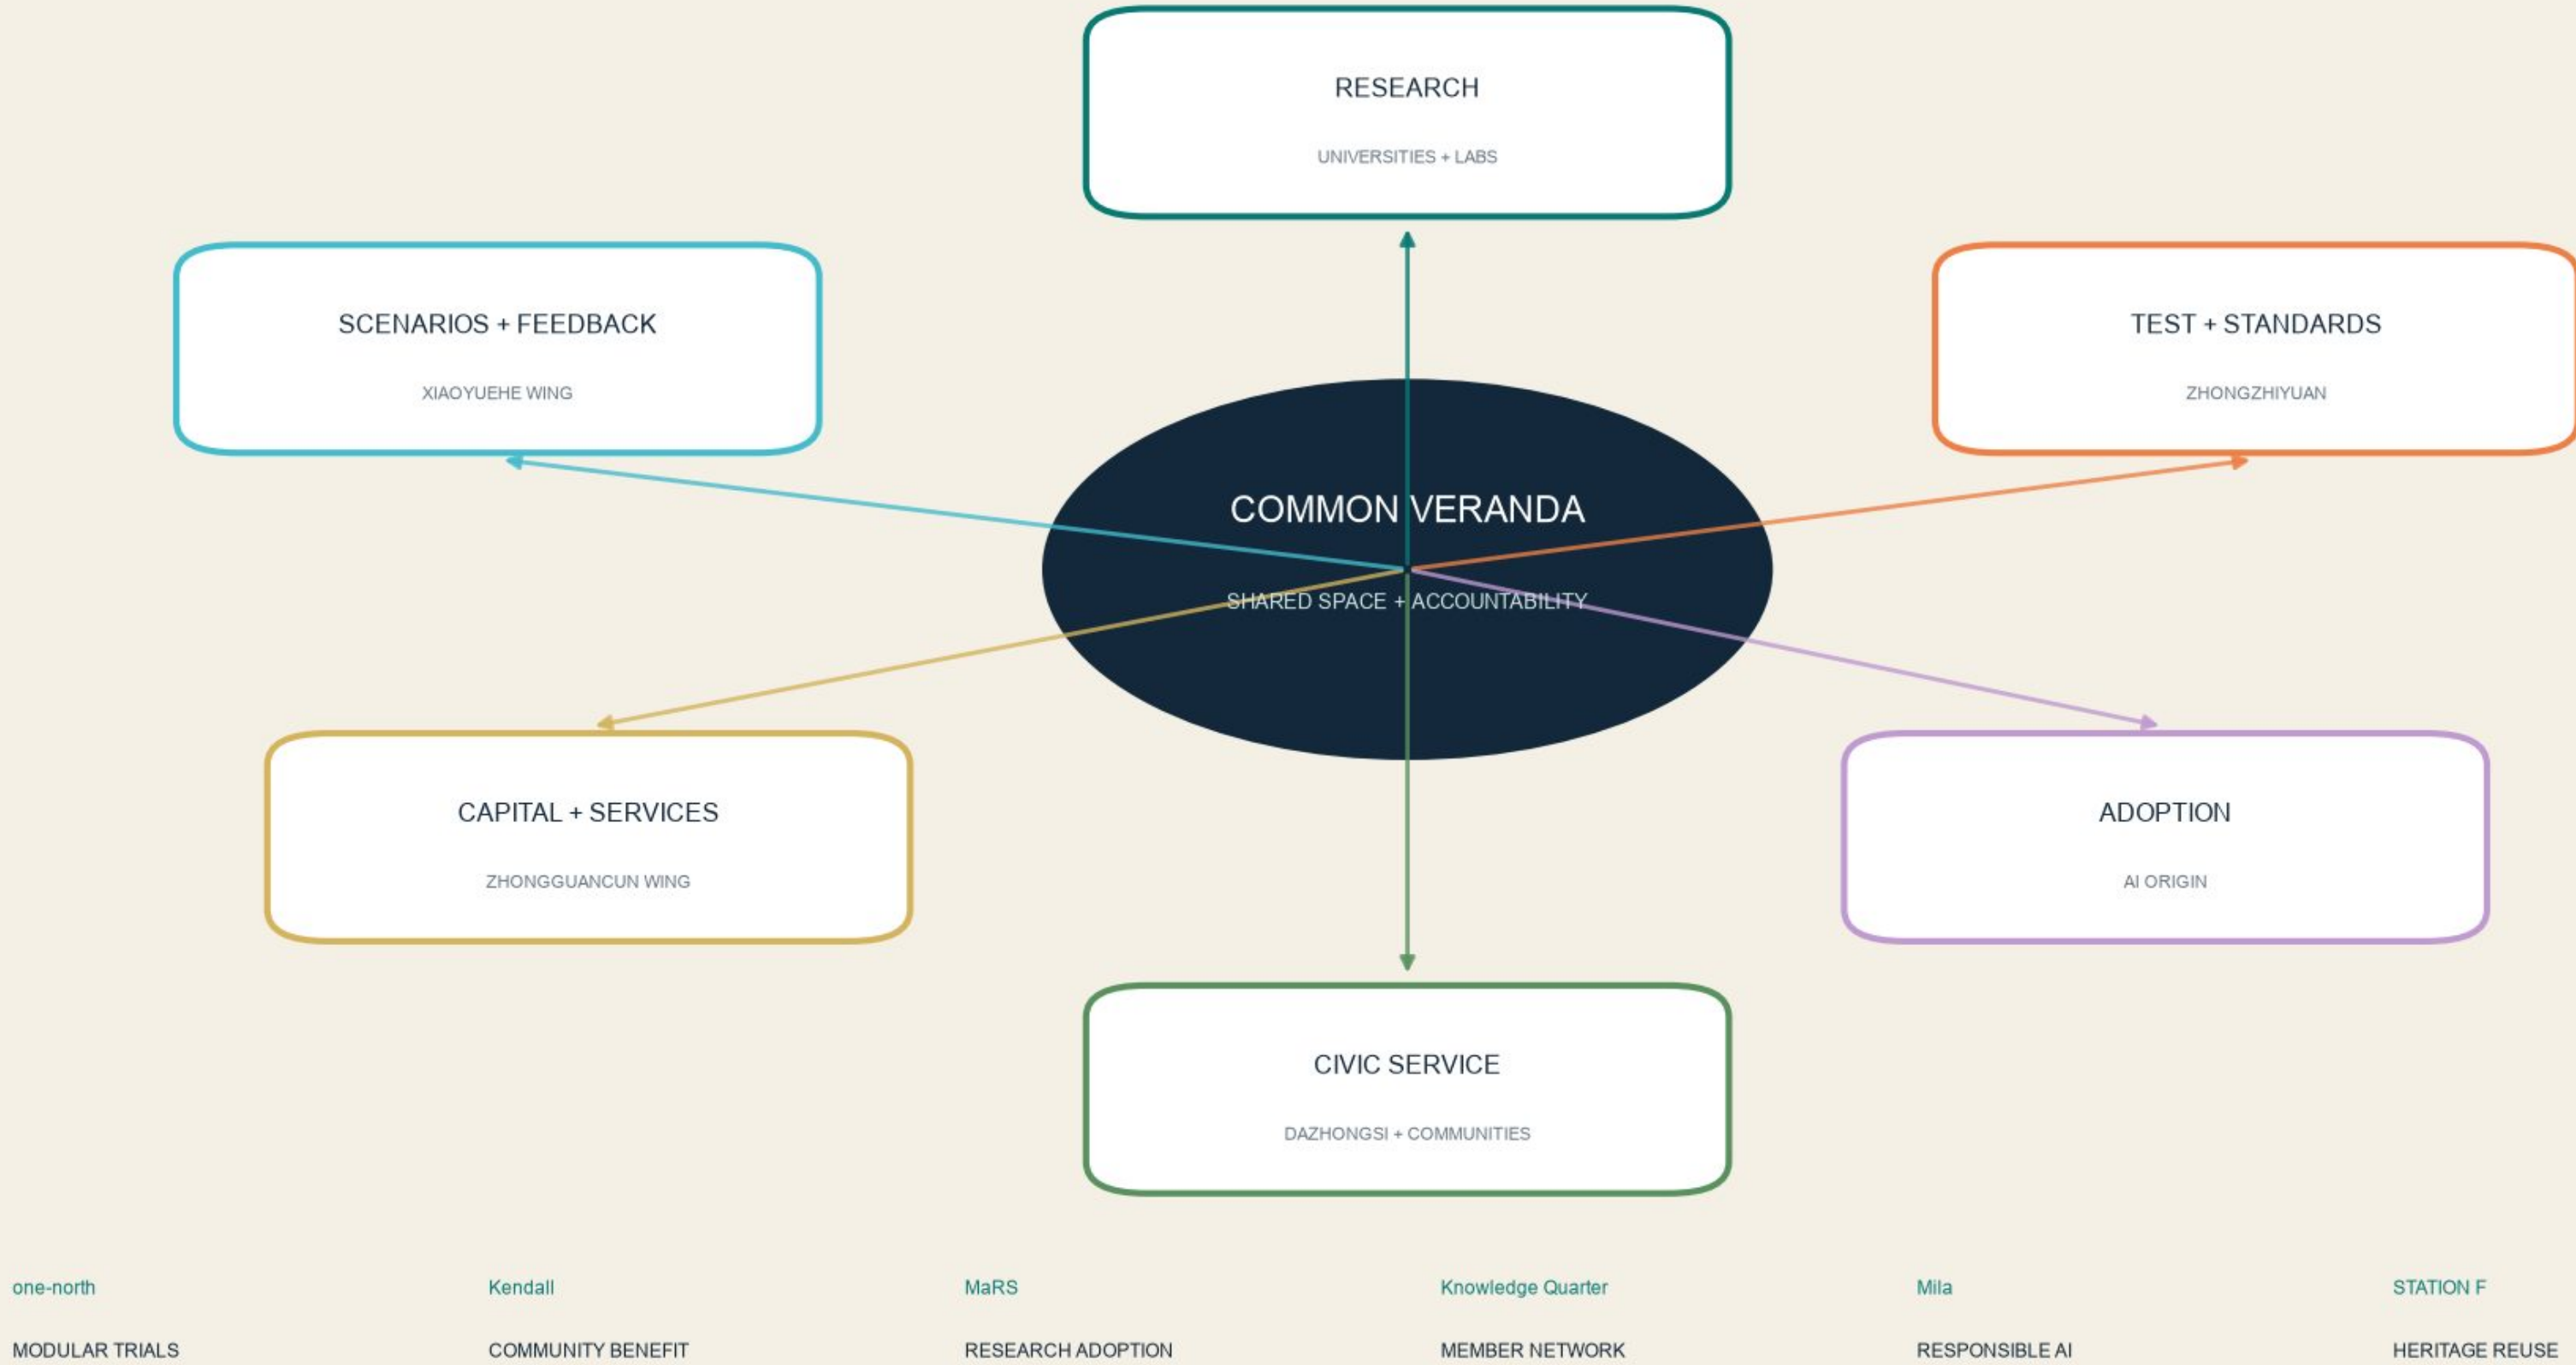


CONCEPT DESIGN · PROVISIONAL BOUNDARY · NOT AN OFFICIAL REDLINE

JING-ZHANG COMMON VERANDA · CONCEPTUAL URBAN DESIGN

CULTURE + IDENTITY: FROM ENGINEERING SELF-RELIANCE TO OPEN ACCOUNTABILITY

IDENTITY IS NOT DECORATION; IT IS A PUBLIC GRAMMAR THAT MAKES SPACE AND AI SERVICES LEGIBLE

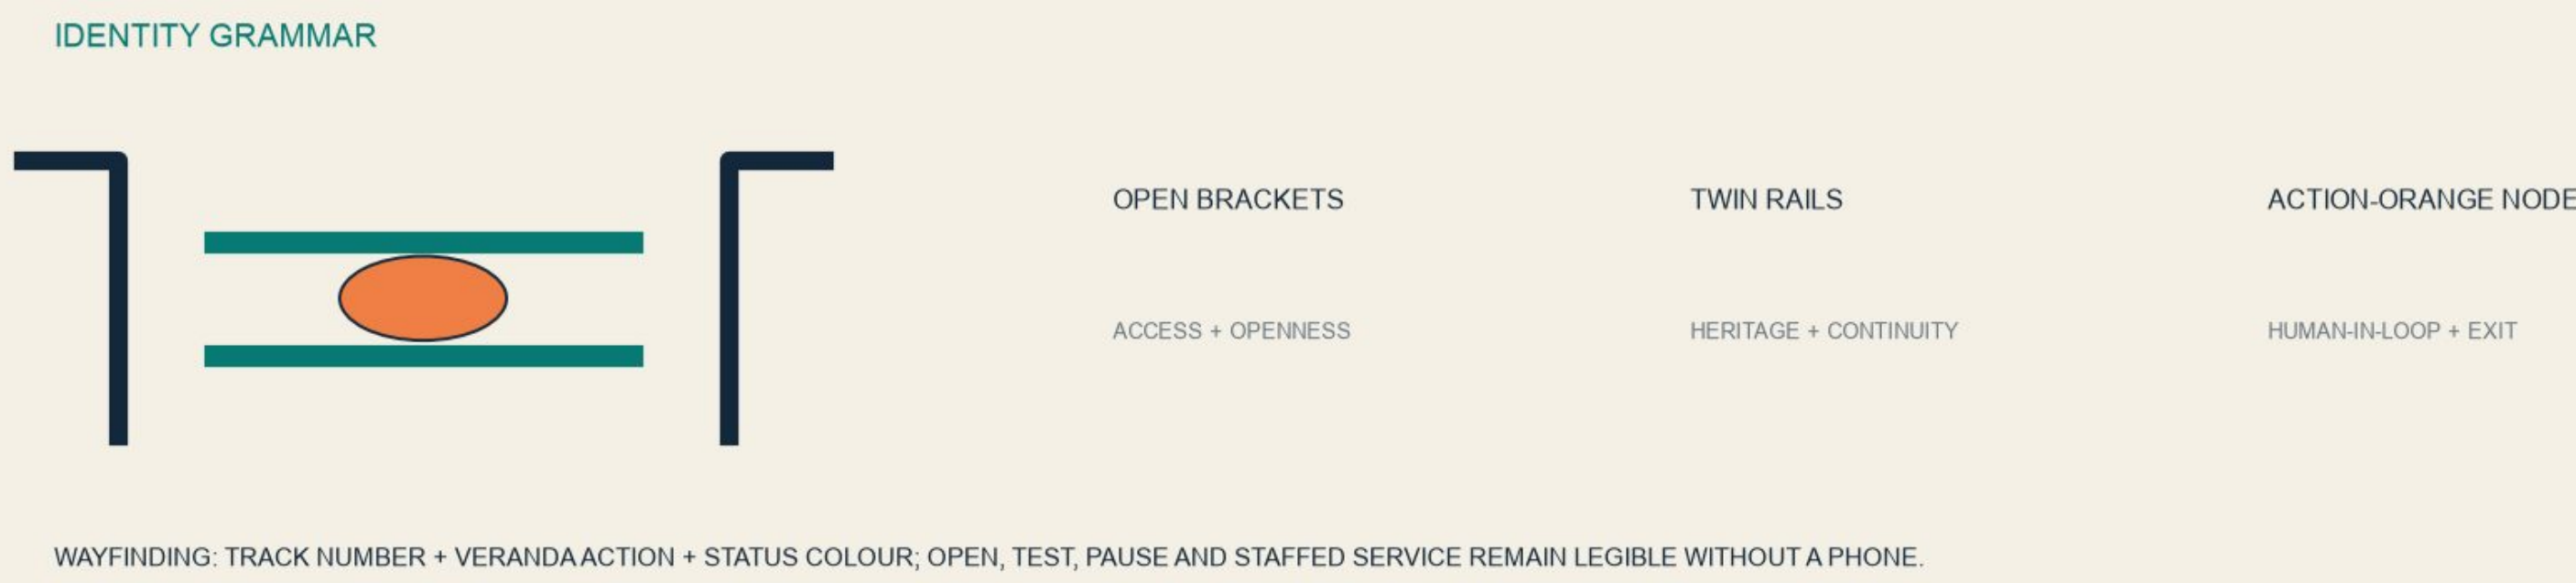


CONCEPT DESIGN · PROVISIONAL BOUNDARY · NOT AN OFFICIAL REDLINE

JING-ZHANG COMMON VERANDA · CONCEPTUAL URBAN DESIGN

VERANDA RECEIPT: A PAUSABLE 90-DAY CIVIC TABLETOP

PROVES STRUCTURE, STOP AND EXIT LOGIC ONLY; NOT AUTHORIZED OR RUN ON SITE

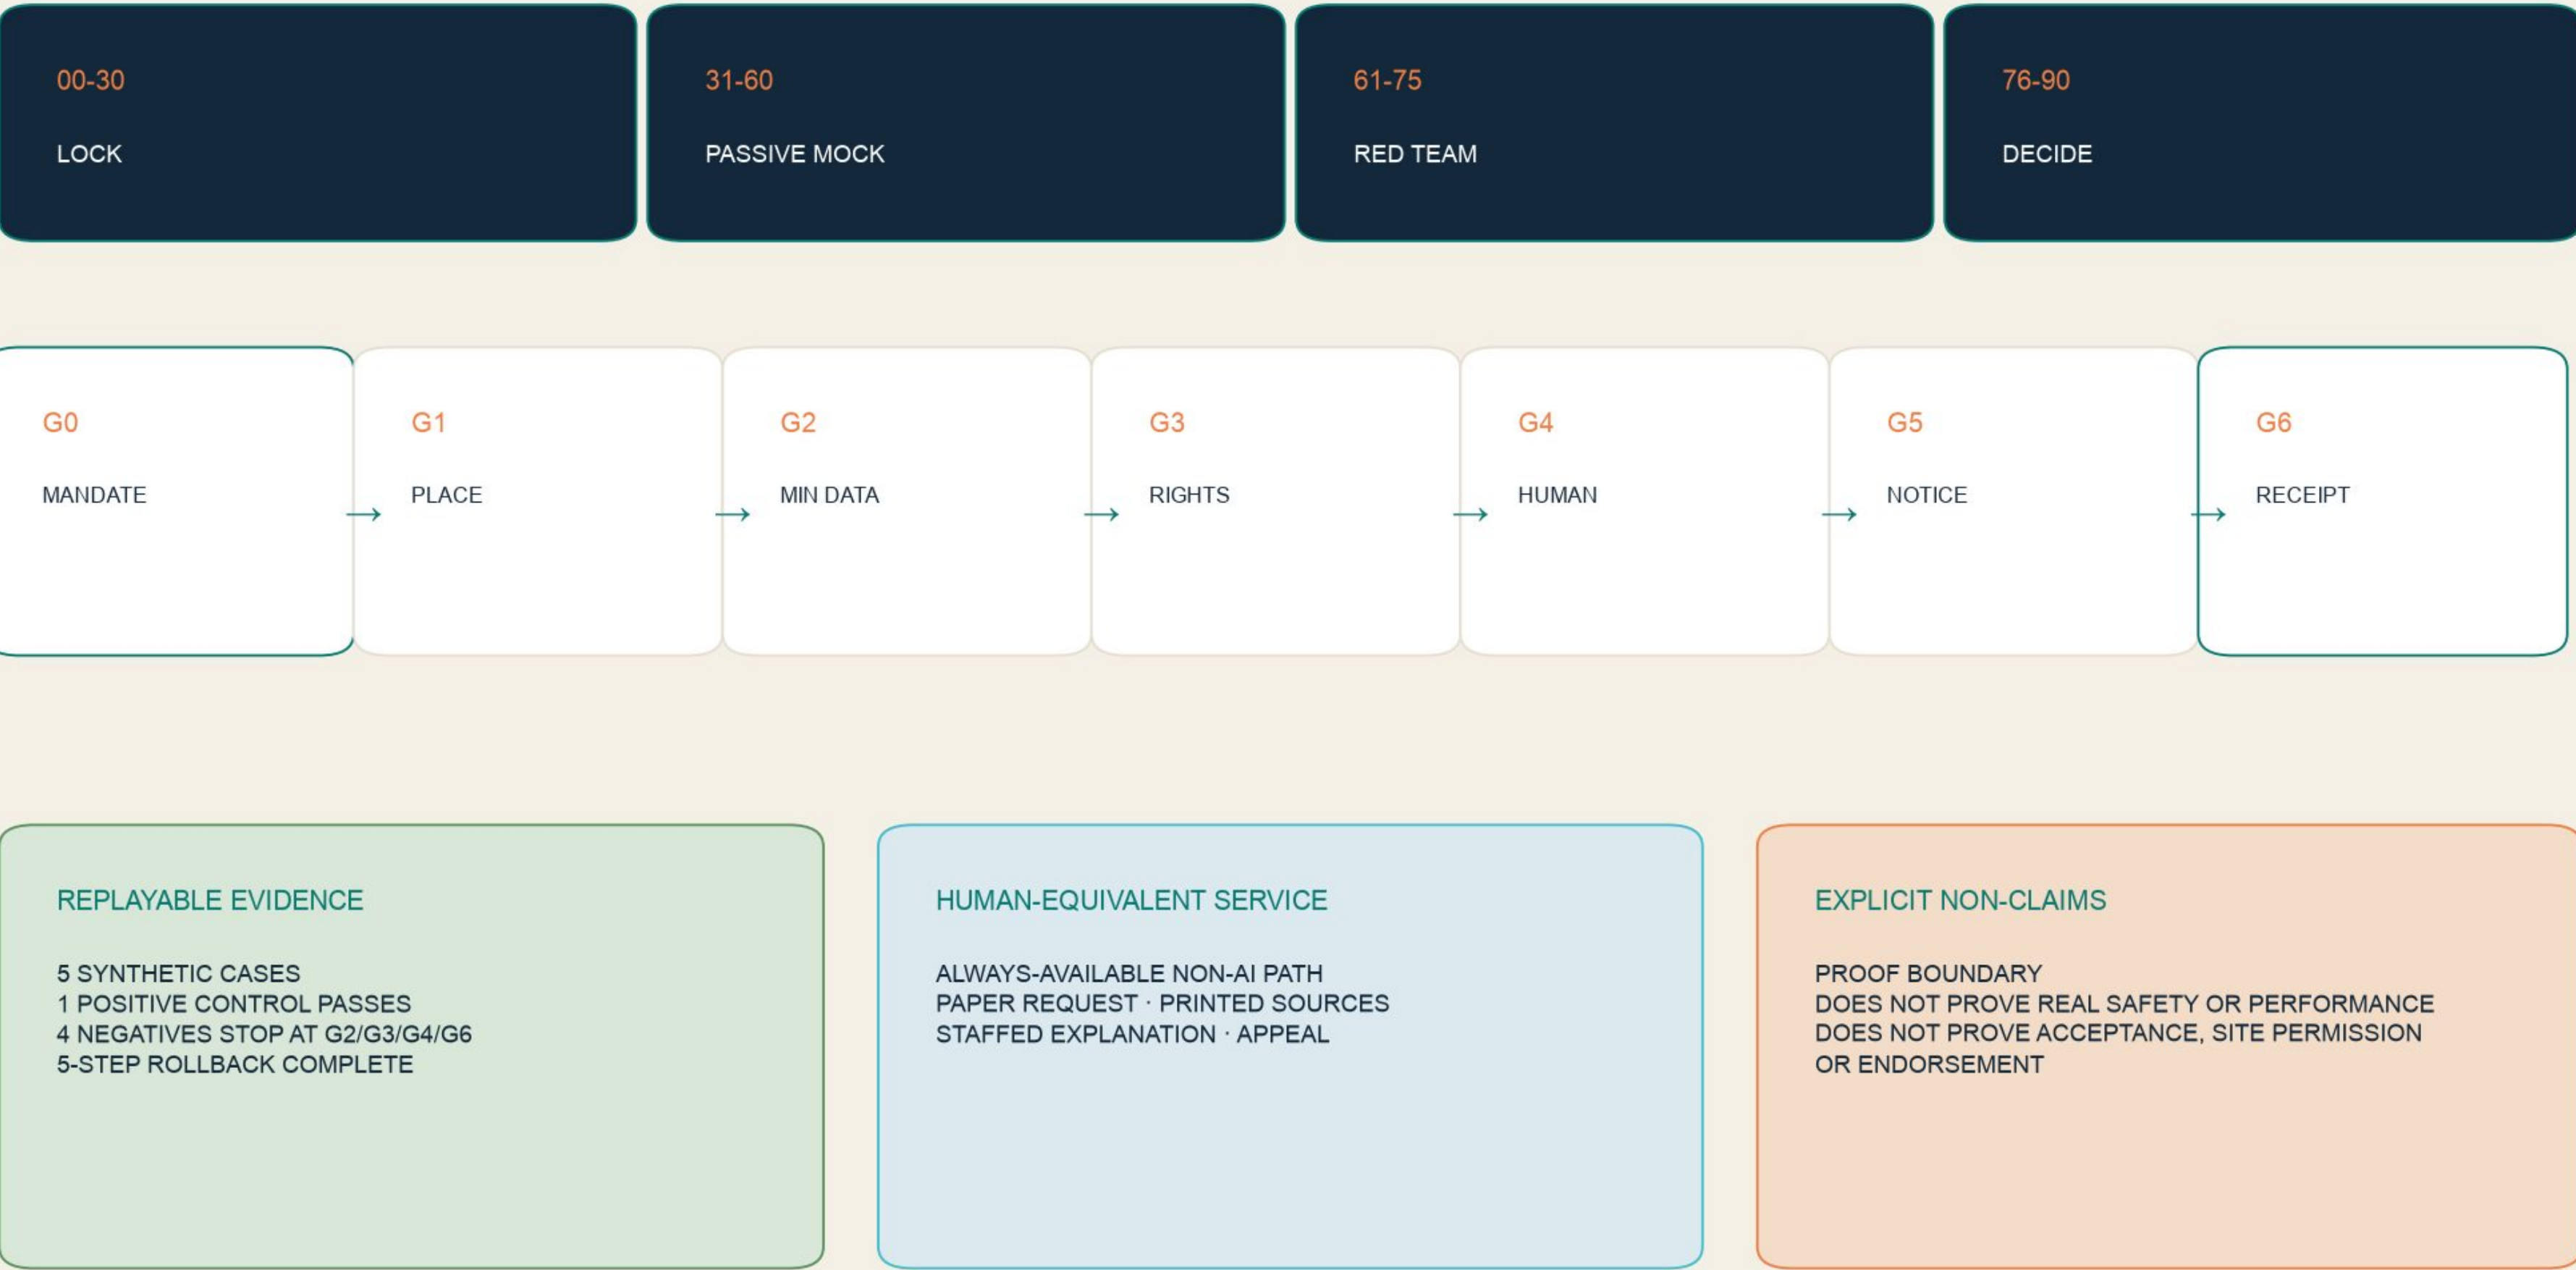

CONCEPT DESIGN · PROVISIONAL BOUNDARY · NOT AN OFFICIAL REDLINE

JING-ZHANG COMMON VERANDA · CONCEPTUAL URBAN DESIGN

FEASIBILITY VERDICT: CIVIC BASELINE FIRST, REVERSIBLE PILOT SECOND

READINESS IS NOT A DESIGN SCORE; IT RECORDS THE EVIDENCE GAP TO A SITE DECISION

NOW	0—6 MONTHS	6—18 MONTHS	AFTER OFFICIAL EVIDENCE
CONCEPT + TABLETOP	SITE AUDIT + CIVIC BASELINE	ONE 90-DAY REVERSIBLE PILOT	PERMANENT WORKS + CROSSINGS
01	BUILT BASELINE + SIX-GATE SITE AUDIT ACTIONABLE NOW	OWNER: RENEWAL LEAD + ACCESS CO-REVIEW RELATIVE COST: S	DEPENDENCY: SITE PERMISSION · SURVEY GATE: ISSUE / RIGHTS / SAFETY REGISTER
02	SHADE, SEATING, WAYFINDING + STAFFED BASE CONDITIONALLY FEASIBLE	OWNER: SITE OPERATOR + PUBLIC-REALM TEAM RELATIVE COST: S—M	DEPENDENCY: FIRE · UTILITIES · MAINTENANCE GATE: NO OWNER, NO WORK
03	VERANDA RECEIPT: TABLETOP TO SITE PILOT TABLETOP READY / SITE NOT AUTHORIZED	OWNER: SPONSOR + STEWARD + DATA/IP RELATIVE COST: M	DEPENDENCY: ALL G0—G6 SIGNED GATE: ANY FAILED GATE → HUMAN + ROLLBACK
04	RAIL CROSSINGS, TUNNELS + PERMANENT BUILDINGS NOT BUILD-READY	OWNER: AUTHORITY + RIGHTS HOLDERS + DISCIPLINE LEADS RELATIVE COST: L	DEPENDENCY: OFFICIAL GIS · RIGHTS · SURVEY · APPROVAL GATE: KEEP CONCEPTUAL UNTIL EVIDENCE EXISTS

BOTTOM LINE: NO OFFICIAL GEOMETRY, RIGHTS, SURVEY OR APPROVAL—NO CONSTRUCTION DRAWING, NO OPERATIONS, STAFFED EQUIVALENT OR EXIT FUND—NO SMART LAYER.

CONCEPT DESIGN · PROVISIONAL BOUNDARY · NOT AN OFFICIAL REDLINE

JING-ZHANG COMMON VERANDA · CONCEPTUAL URBAN DESIGN

TWELVE WORK PACKAGES: EVERY SPATIAL MOVE CARRIES ACCOUNTABILITY + EXIT

S/M/L ARE RELATIVE COST BANDS, NOT BUDGET ESTIMATES

ZHONGZHIYUAN · TEST	AI ORIGIN · LEARN	DAZHONGSI · LIVE
4 HAND-OFF-READY PACKAGES	4 HAND-OFF-READY PACKAGES	4 HAND-OFF-READY PACKAGES
01 TEST INTAKE HALL M G0-G3	05 OPEN-SOURCE GATE S G2-G3	09 TRANSIT ARRIVAL ROOM L G1-G5
02 LOW-SPEED SANDBOX L G1-G4	06 90-DAY RECEIPT M G0-G6	10 RESPONSIBLE RETAIL M G2-G6
03 RED-TEAM COURT M G2-G6	07 PUBLIC LEARNING STEPS S G1-G5	11 ELDER NAVIGATOR M G1-G6
04 ENERGY/SAFETY KIOSK S G3-G6	08 ACCESSIBLE LOOP M G1-G6	12 CIVIC LEDGER CLOCK S G3-G6

EACH PACKAGE: LEAD ROLE · PROFESSIONAL DEPENDENCIES · RELATIVE COST · MAINTENANCE WINDOW · ACCEPTANCE GATE · STOP/REMOVE CONDITION · P1/P2/P3 WINDOW


CONCEPT DESIGN · PROVISIONAL BOUNDARY · NOT AN OFFICIAL REDLINE

JING-ZHANG COMMON VERANDA · CONCEPTUAL URBAN DESIGN

PROVISIONAL / NOT AN OFFICIAL REDLINE / NOT AN ENGINEERING ALIGNMENT

DELIVERY + OPERATIONS: BUILD THE CIVIC BASELINE BEFORE SMART SERVICES

EVERY PHASE HAS ENTRY CONDITIONS, PUBLIC EVIDENCE, AN ACCOUNTABLE OWNER AND A ROLLBACK GATE

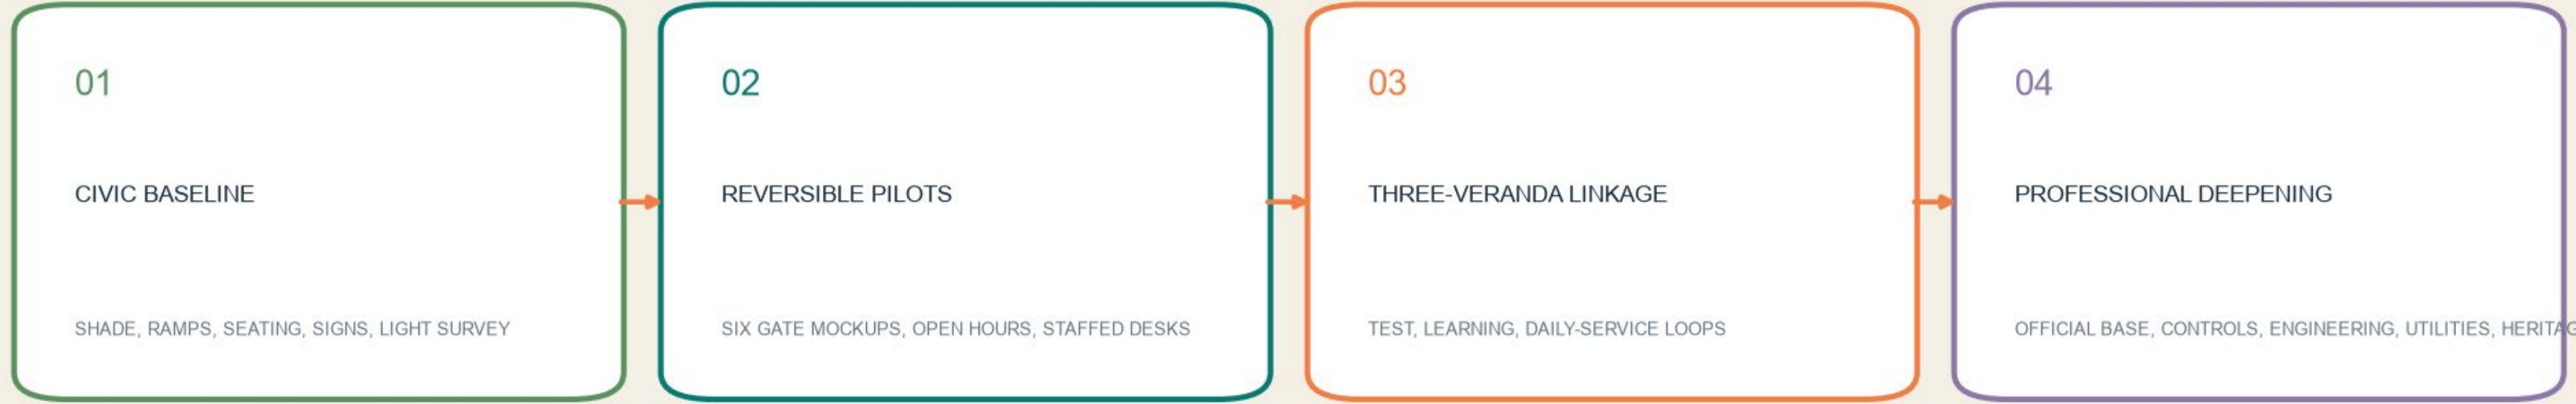

OPERATING RHYTHM

DAY	MONTH	QUARTER	YEAR
SERVICE + CARE	MAINTAINER SALON	OPEN EVALUATION	OPEN VERANDA WEEK

ROLLBACK GATES

STALE SOURCE / BOUNDARY / LINK LOSS / UNTRACEABLE COMPLAINT / NO HUMAN OWNER / NOT REPRODUCIBLE

CONCEPT DESIGN · PROVISIONAL BOUNDARY · NOT AN OFFICIAL REDLINE

JING-ZHANG COMMON VERANDA · CONCEPTUAL URBAN DESIGN

LONG-TERM OPERATIONS: WHO MAINTAINS, RESPONDS AND RETIRES

NO MAINTENANCE WINDOW, STAFFED EQUIVALENT OR EXIT FUNDING — NO SMART LAYER

DAILY	MONTHLY	QUARTERLY	ANNUAL
OPEN · ACCESS · NOTICE · STAFF · INCIDENT	MAINTAINER SALON · REPAIR · DISSENT	RUN/PAUSE/APPEAL/REPAIR RECEIPTS	OPEN VERANDA WEEK · ASSET/LICENSE AUDIT

FUNDING FIRST	PUBLIC LEDGER	OPEN BRAND GOVERNANCE
OPERATIONS OWNER MAINTENANCE + SPARES STAFFED FALLBACK INSURANCE + EXIT FUND	OPEN / TEST / PAUSED COMPLAINT + APPEAL REPAIR + REVIEW CONTINUE / REVISE / RETIRE	ATTRIBUTED REUSE STATUS COLOURS STAY AI CONTENT STAYS LABELLED EVERY CHANGE DATED + VERSIONED

IF A QUARTER CANNOT PUBLISH OWNER, REPAIR AND EXIT EVIDENCE, THE SCENARIO DEFAULTS TO PAUSED; TWO UNCLOSED QUARTERS TRIGGER A RETIREMENT DECISION.

CONCEPT DESIGN · PROVISIONAL BOUNDARY · NOT AN OFFICIAL REDLINE

JING-ZHANG COMMON VERANDA · CONCEPTUAL URBAN DESIGN

SIX-GATE EVIDENCE: NO FICTIONAL SHORTCUT ACROSS ACTIVE RAIL

EACH GATE STARTS WITH ITS REAL INTERFACE, PHYSICAL CONFLICT + DESIGN RULE


G1	DAZHONGSI	FOUR QUADRANTS, PARKING, TRANSFER + VENT CONFLICT	AUDIT EXISTING ROUTES, NO AT-GRADE RAIL CROSSING
G2	ZHICHUN	PHASE 1 SOUTH, ROAD + RAIL OVERLAP	EXISTING OR PROFESSIONALLY VERIFIED CROSSING ONLY
G3	NORTH FOURTH RING	UNDER-BRIDGE ACTIVITY VS THROUGH-FLOW	COURTS, QUEUES + SEATS OFF THROUGH-BANDS
G4	CHENGFU—WUDAOKOU	RETAIL, METRO + CYCLE PEAK	CONTINUOUS WALK, CYCLE BYPASS
G5	QINGHUA EAST ROAD WEST	APPROVED PUBLIC SPACE + CYCLE PARKING	ADD ACCOUNTABILITY, NOT DUPLICATE LANDSCAPE
G6	NORTH FIFTH RING—QINGHE SOUTH EDGE	PHASE 2 UNDER CONSTRUCTION	NO CONTINUITY CLAIM BEFORE ACCEPTANCE

CONCEPT DESIGN · PROVISIONAL BOUNDARY · NOT AN OFFICIAL REDLINE

JING-ZHANG COMMON VERANDA · CONCEPTUAL URBAN DESIGN

REGIONAL COLLABORATION AS EXITABLE EVIDENCE INTERFACES

EACH NODE DEFINES INPUT, MINIMUM OUTPUT, OWNER TYPE AND STOP GATE

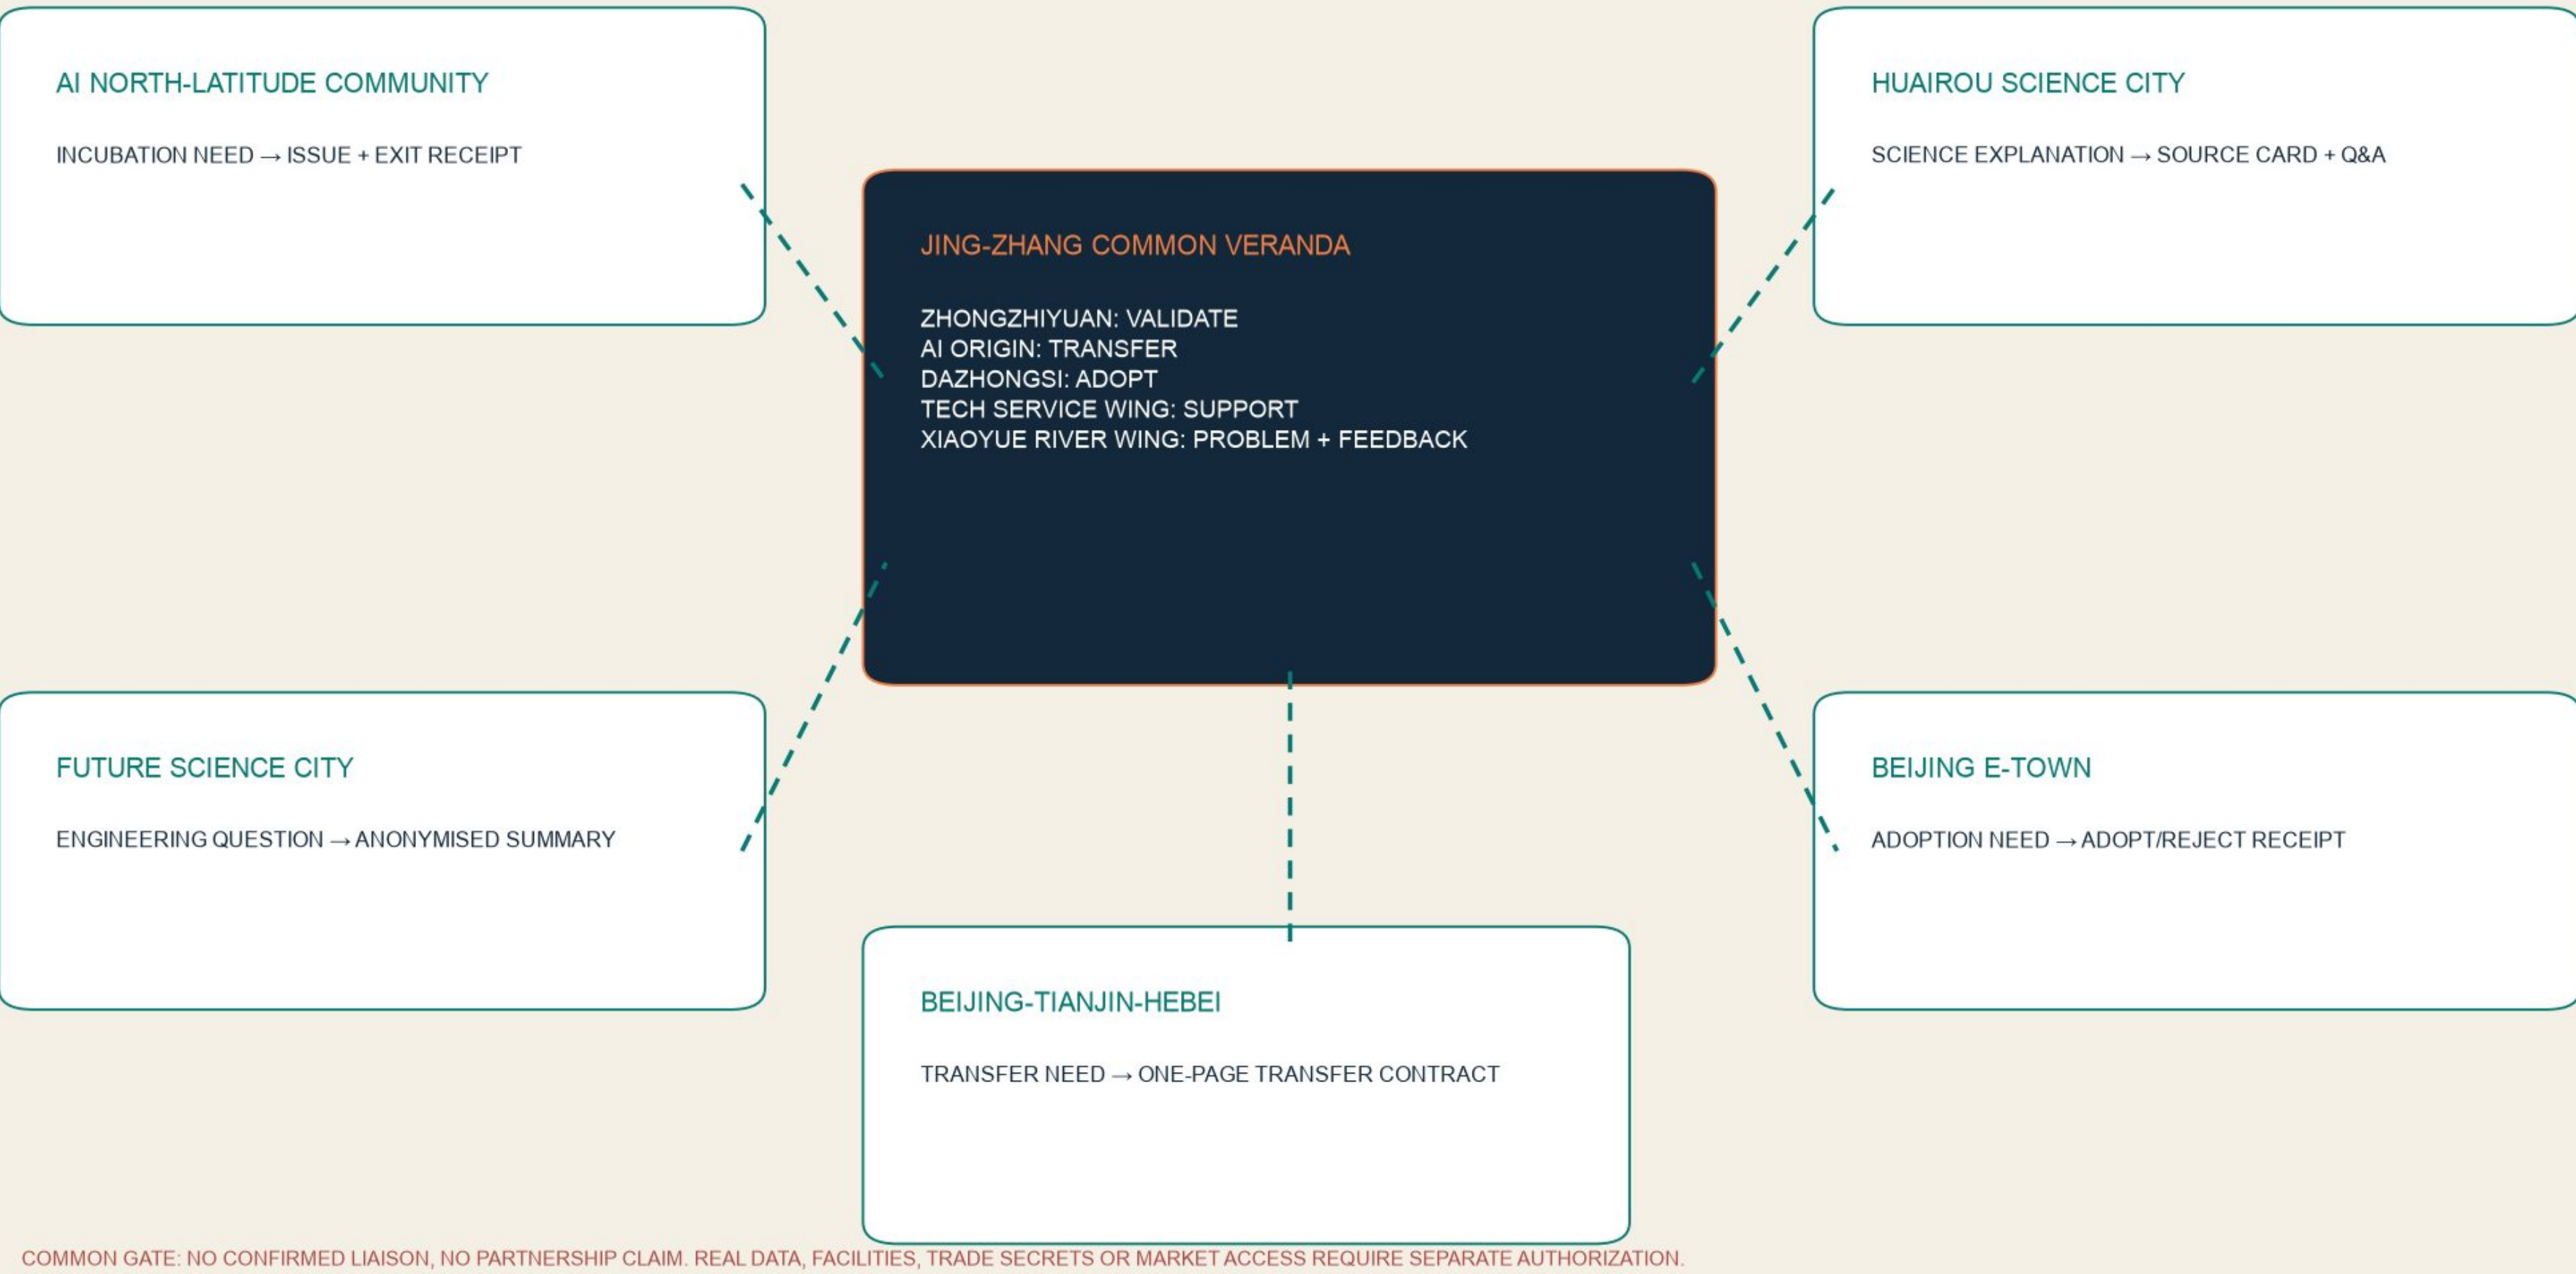

COMMON GATE: NO CONFIRMED LIAISON, NO PARTNERSHIP CLAIM. REAL DATA, FACILITIES, TRADE SECRETS OR MARKET ACCESS REQUIRE SEPARATE AUTHORIZATION.

CONCEPT DESIGN · PROVISIONAL BOUNDARY · NOT AN OFFICIAL REDLINE

JING-ZHANG COMMON VERANDA · CONCEPTUAL URBAN DESIGN

METRICS, EVIDENCE + RISK: QUANTIFY WHAT CAN BE RECALCULATED; TRIGGER WHAT CANNOT

CURRENT VALUES COMPARE INTERNAL CONCEPT ALLOCATION ONLY; THEY ARE NOT STATUTORY PLANNING CONTROLS



QUALITY NOTE: DETERMINISTIC VALIDATION ONLY ENABLES CONTENT REVIEW, SPATIAL QUALITY STILL DEPENDS ON REAL CONTEXT, DESIGN JUDGEMENT, DRAWING QUALITY AND PROFESSIONAL REVIEW.

CONCEPT DESIGN · PROVISIONAL BOUNDARY · NOT AN OFFICIAL REDLINE

JING-ZHANG COMMON VERANDA · CONCEPTUAL URBAN DESIGN

DESIGN CONCLUSION: ONE CIVIC VERANDA, SIX CITY GATES, THREE EVIDENCE LAYERS

EXISTING BASELINE, CONCEPTUAL RECOMMENDATION + PROFESSIONAL-DEEPENING ITEMS ARE EXPLICITLY SEPARATED



CONCEPT DESIGN · PROVISIONAL BOUNDARY · NOT AN OFFICIAL REDLINE

JING-ZHANG COMMON VERANDA · CONCEPTUAL URBAN DESIGN