


一脊 · 三区 · 十八断面 · 低速智能设备试验网络

总体空间结构: 约 9.3 公里公共空间主轴串联三处重点地区与 18 处评估断面; 紫色虚线为低速配送试验线路 (限速 6 公里/小时), 方块为 3 处服务驿站


图 01 / SITE OVERVIEW

可感京张 SENSIBLE JING-ZHANG v0.6.0

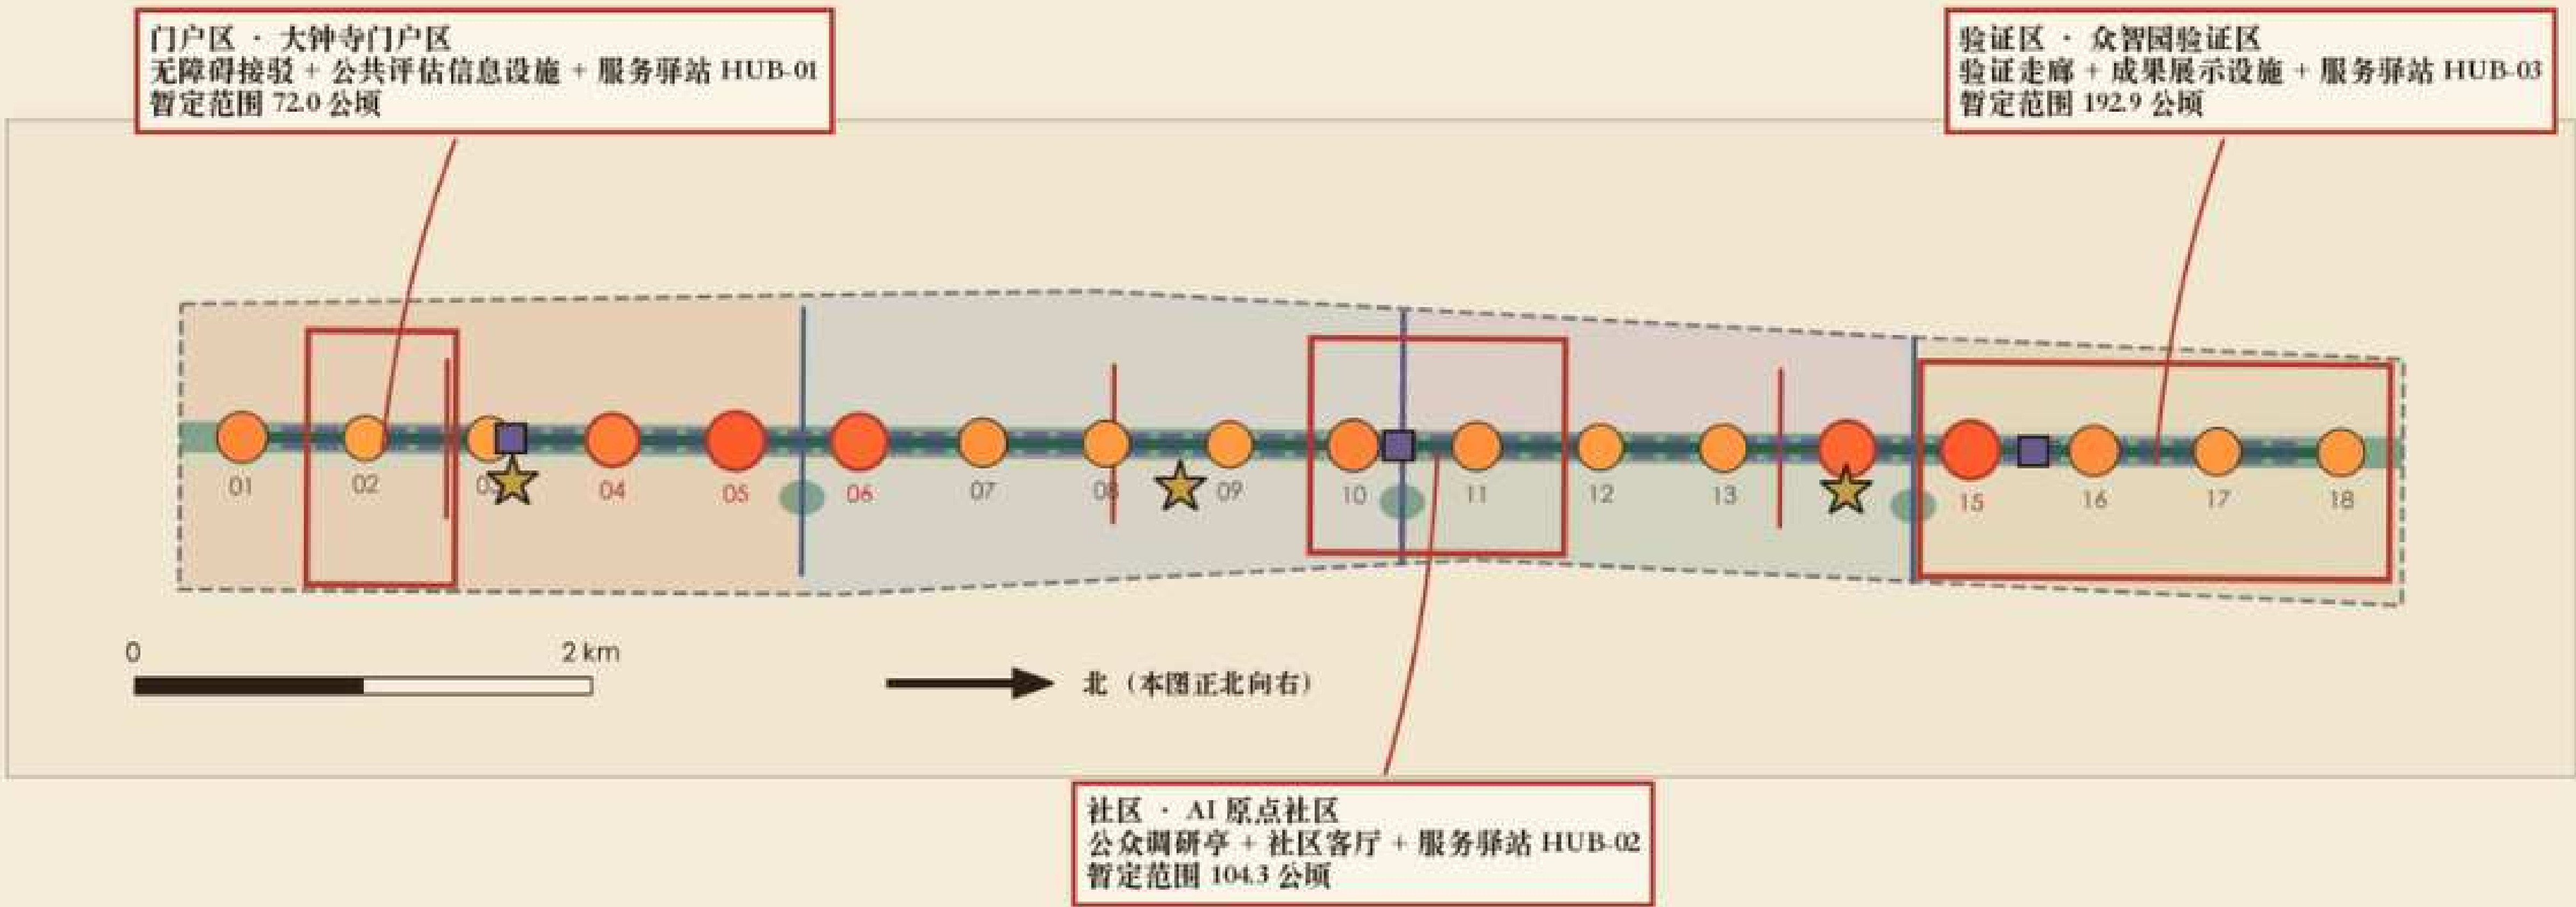

三层范围 · 空间关系

统筹研究层 约 43.6 平方公里

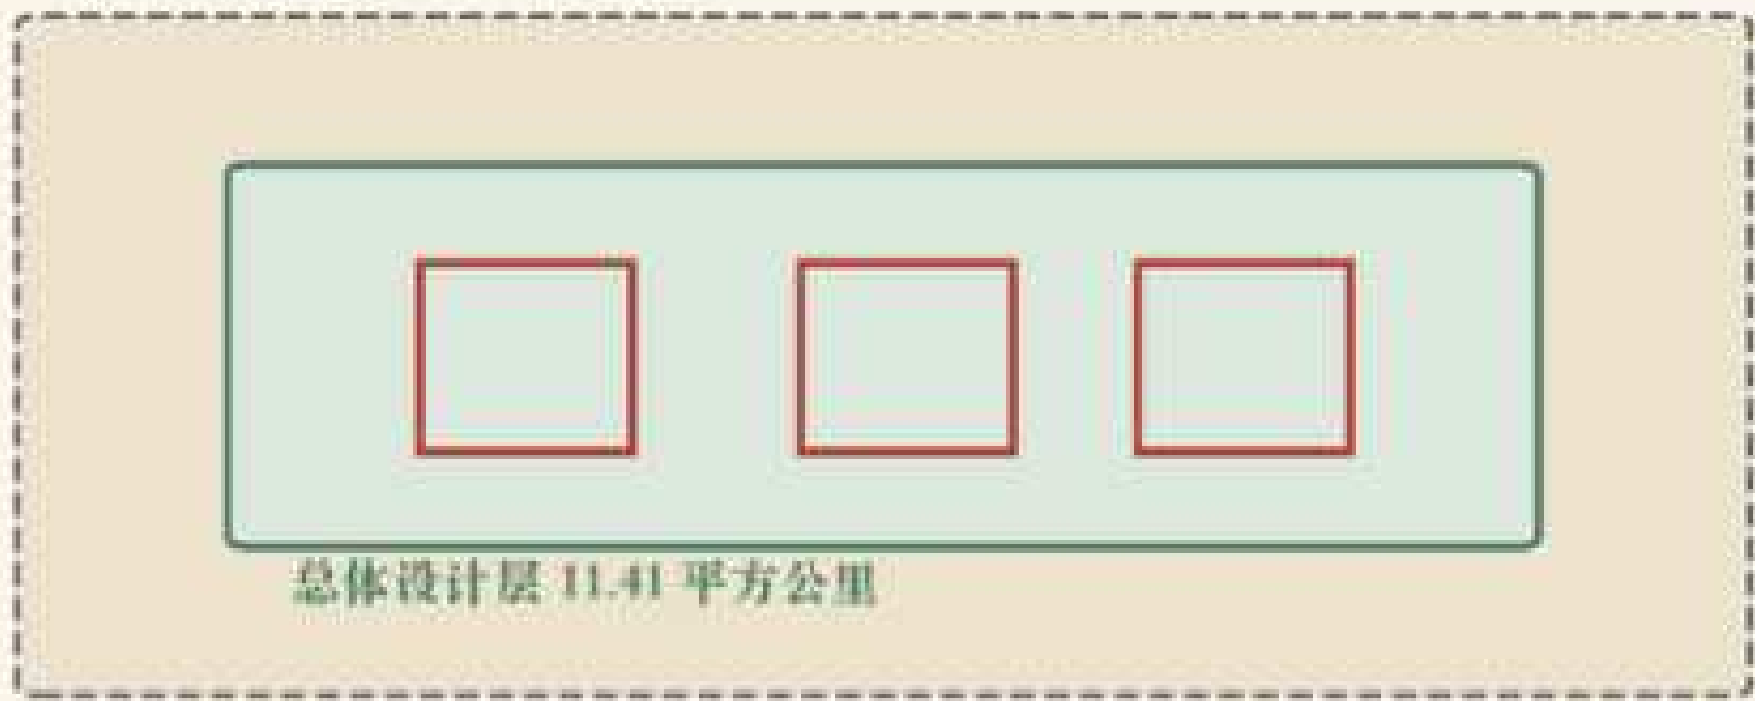

重点地区层 3 处

低速智能设备 · 运行规则 (概念)

- 运行速度上限 6 公里/小时
- 不得占用无障碍通道与驻留空间
- 驿站承担充换电与末端交接
- 碰撞、超速或持续投诉即暂停试验

主要技术指标 (复算)

11.41	12.27	18
平方公里	% 绿地几何面积比	处评估断面
5	18.8	3
处高短板断面	公里试验线路	处服务驿站

数据来源: 本方案空间数据 (EPSG:4326 交换, 面积于 EPSG:4548 复算) 与指标附件; 图面由脚本自空间数据直绘。

范围为暂定研究边界, 不作为法定规划边界或审批依据。公共空间感知指标为模型估算; 低速配送试验线路与服务驿站为概念性建议 (限速 6 公里/小时), 非法定车道。

图说: 一脊、三区、十八断面与低速智能设备试验网络; 橙点大小反映模型估算短板程度。

概念性建议 · 非法定规划边界 · 效果图非实景

规划导图：技术路线、空间体系与成果结构

图 06 / PLANNING ROADMAP

可感京张 SENSIBLE JING-ZHANG v0.6.0

自资料核定至年度复核的八步闭环；左栏为目标与定位，右栏为成果构成，底部为公告任务与章节对照

目标与三项发展定位

文化传承带

京张铁路遗产连续可达、可讲述

智能服务体验带

面向日常生活的智慧服务与低速设备试验

融合创新带

创新功能与公共空间品质同步提升

五项主要功能

- 众智园：受控测试与设备交接
- AI 原点社区：青年创新与公众调研
- 大钟寺：门户接驳与产业服务
- 十八断面：分类更新与整治
- 公共信息平台：年度监测与评估

技术路线（八步闭环）

01	核定资料与边界	公告、任务书、暂定边界	✓
02	建立评估维度	遮阴、绿视、驻留、夜间安全	✓
03	复算空间指标	EPSG:4548 面积与长度复算	✓
04	确定总体结构	一脊、三区、十八断面	✓
05	划分断面族与措施	六族分类与整治标准做法	✓
06	布置场景与设施	16 项场景、驿站与感知设施	✓
07	编制分期与运营	三期项目库与年度运营	✓
08	建设后评估与复核	90 日复测、年度监测回写	

第八步结论回到第二步评估维度：指标口径随现场踏勘与公众调研结果修正。

复核回写

成果构成

规划说明书	十四章、逐图配图说
规划图纸	6 张规划图版
概念效果图	9 张，统一标注非实景
文化主视觉	1 张，古典风格
空间数据	9 个图层
指标附件	21 项可复算指标

公众沟通与文化叙事

- 京张十二幕：叙事与空间锚点一一对应
- 微短剧共创：许可、授权与退出规则
- 公共评估信息设施：基线与整改公开
- 年度复测活动：公众确认下一轮清单

章节对照：一 设计依据 | 二 三层范围 | 三 统筹研究 | 四 总体设计 | 五 重点地区 | 六 场景与叙事 | 七 智慧设施 | 八 用地与拆改留 | 九 交通市政 | 十 蓝绿风貌 | 十一 项目分期 | 十二 指标复算 | 十三 风险合规 | 十四 参考附录

数据来源：本方案空间数据（EPSG:4326 交换，面积于 EPSG:4548 复算）与指标附件；图画由脚本自空间数据直绘。

范围为暂定研究边界，不作为法定规划边界或审批依据。公共空间感知指标为模型估算；低速配送试验线路与服务驿站为概念性建议（限速 6 公里/小时），非法定车道。


图说：八步闭环技术路线、成果构成与章节对照；导图为方法示意，不含空间比例。

用地布局：主轴绿地与科研、居住功能带状复合

9个概念用地单元；建筑基底仅为界面研究原型；右侧为用地构成与西—东典型横断面（含低速设备通行层位置）

图 02 / LAND USE

可感京张 SENSIBLE JING-ZHANG v0.6.0

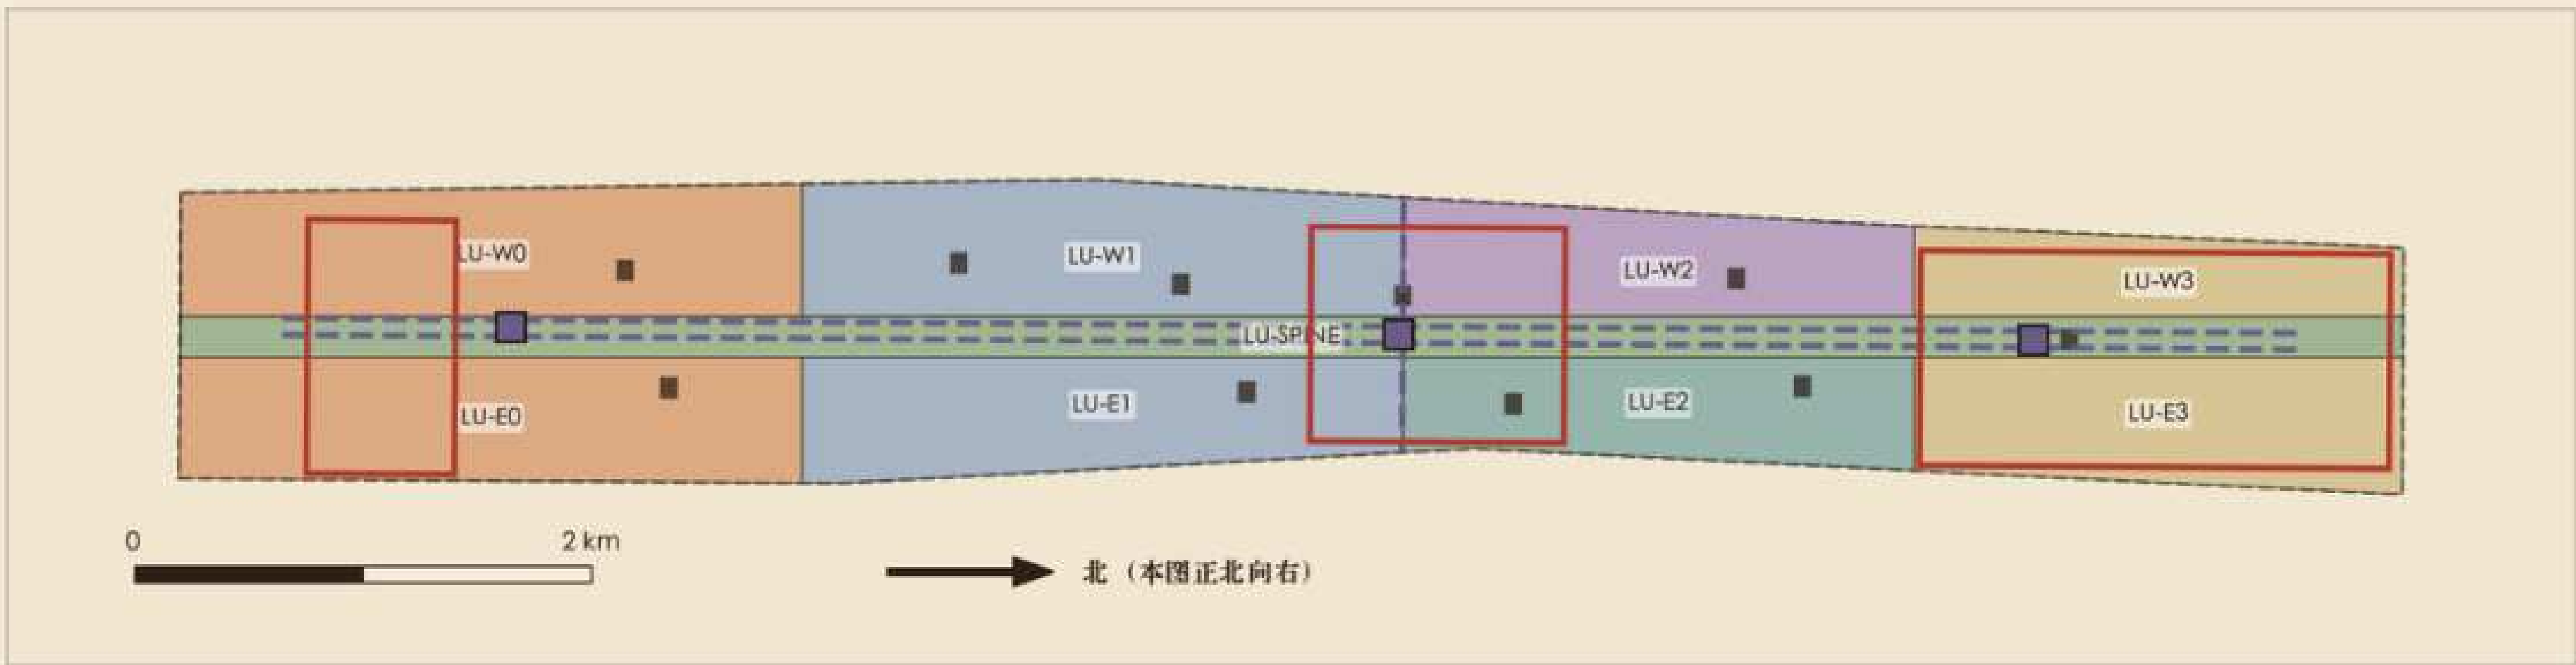

公园绿地 商业服务业用地 科研用地 低速配送试验线路 概念建筑基底（界面原型）


数据来源：本方案空间数据（EPSG:4326 交换，面积于 EPSG:4548 复算）与指标附件；图画由脚本自空间数据直绘。
范围为暂定研究边界，不作为法定规划边界或审批依据。公共空间感知指标为模型估算；低速配送试验线路与服务驿站为概念性建议（限速 6 公里/小时），非法定车道。

用地构成（几何复算）



典型横断面（西→东，概念）


低速设备通行层贴主轴绿道外侧设置，不得进入无障碍通道与断面驻留带

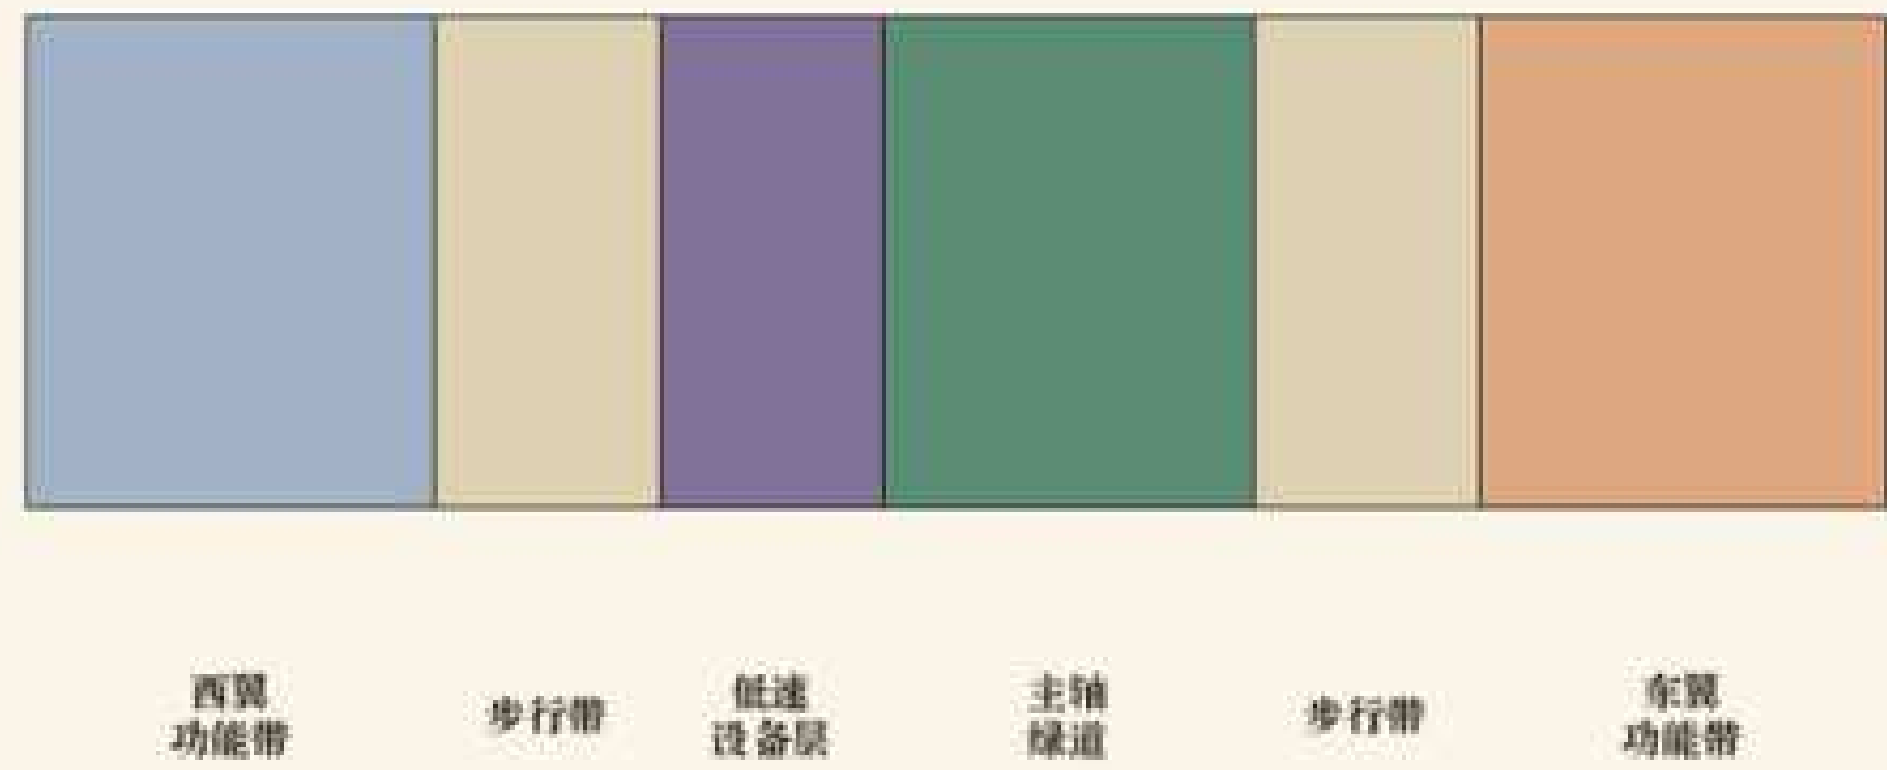

图说：九个概念用地单元与西—东横断面；低速设备层贴主轴绿道外侧设置。

南北贯通 · 东西缝合：慢行网络与蓝绿公共空间体系

主轴绿道南北贯通；东西向联系廊与轨道接驳构成可达网络；紫色虚线为低速配送试验线路（概念层）

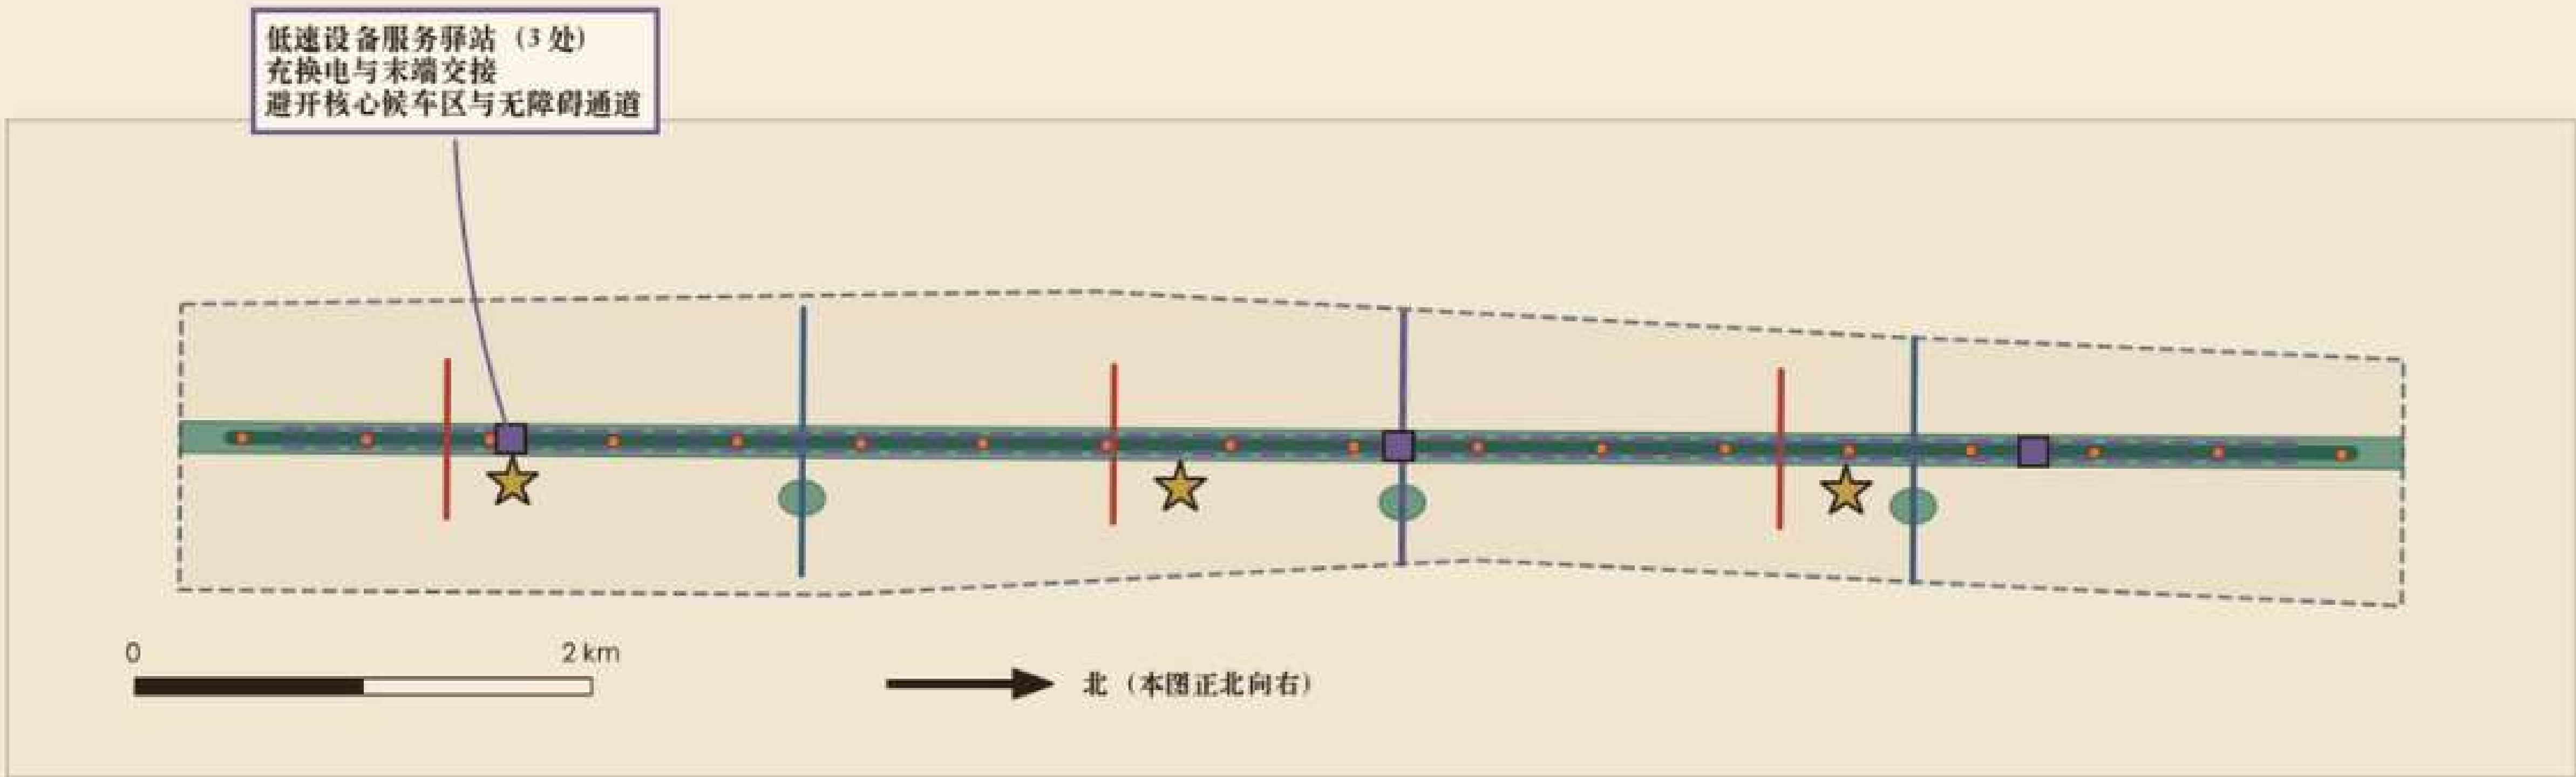

—— 主轴绿道 —— 东西向联系廊 - - - 低速配送试验线路 ■ 服务驿站 ■ 概念绿地

数据来源：本方案空间数据（EPSG:4326 交换，面积于 EPSG:4548 复算）与指标附件；图画由脚本自空间数据直绘。
范围为暂定研究边界，不作为法定规划边界或审批依据。公共空间感知指标为模型估算；低速配送试验线路与服务驿站为概念性建议（限速 6 公里/小时），非法定车道。

图 04 / MOBILITY & BLUE-GREEN

可感京张 SENSIBLE JING-ZHANG v0.6.0

公共空间层级

- 带级**
主轴绿道 + 主题标志节点
- 段级**
东西向联系廊 + 轨道接驳通道
- 邻里级**
口袋公园 + 断面驻留带 + 驿站节点

蓝绿、慢行与试验线路指标

概念绿地面积	140.0 公顷
绿地几何面积比	12.27 %
主轴长度	9.3 公里
公共空间节点面积比	1.34 %
试验线路累计	18.8 公里
服务驿站	3 处 / 972 平方米

图说：主轴绿道、东西向联系廊与低速配送试验线路的空间关系。

三处重点地区：门户区 · 社区 · 验证区


以模型估算高短板断面为一期优先整治对象；公共评估信息设施与低速设备服务驿站为智慧服务落点

图 03 / KEY AREAS

可感京张 SENSIBLE JING-ZHANG v0.6.0


门户区 · 大钟寺门户区

无障碍接驳 + 公共评估信息设施 + 服务驿站 HUB-01 · 暂定 72.0 公顷

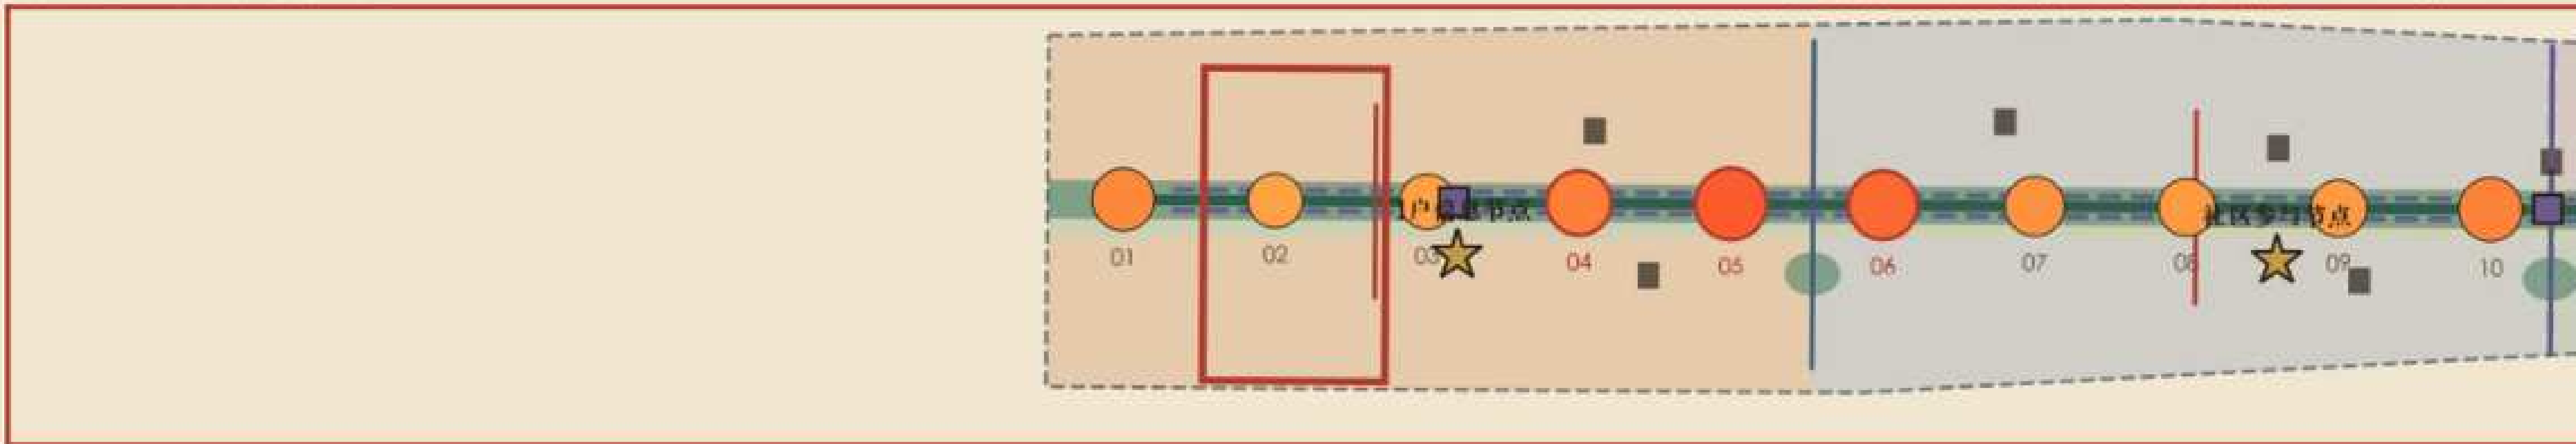


社区 · AI 原点社区

公众调研亭 + 社区客厅 + 服务驿站 HUB-02 · 暂定 104.3 公顷

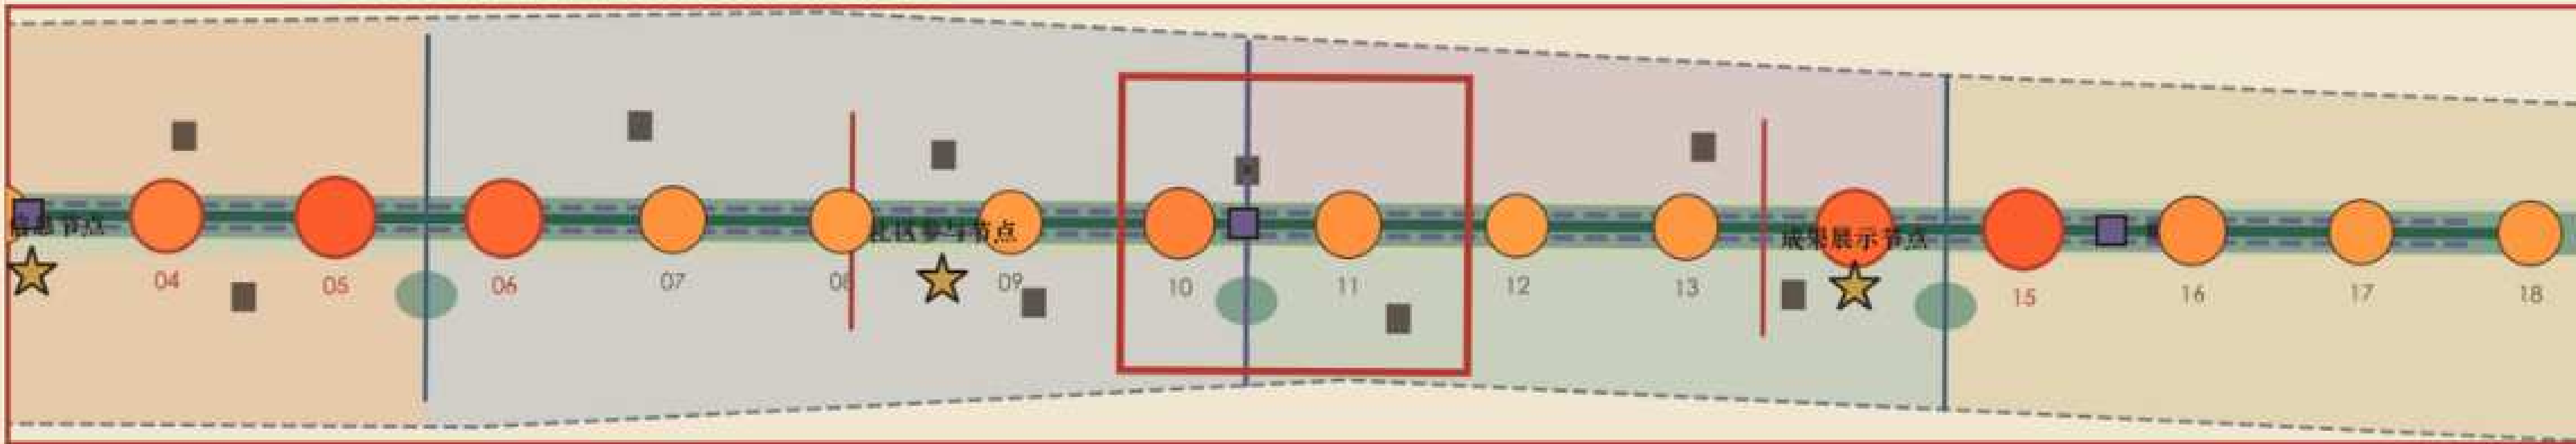

验证区 · 众智园验证区

验证走廊 + 成果展示设施 + 服务驿站 HUB-03 · 暂定 192.9 公顷

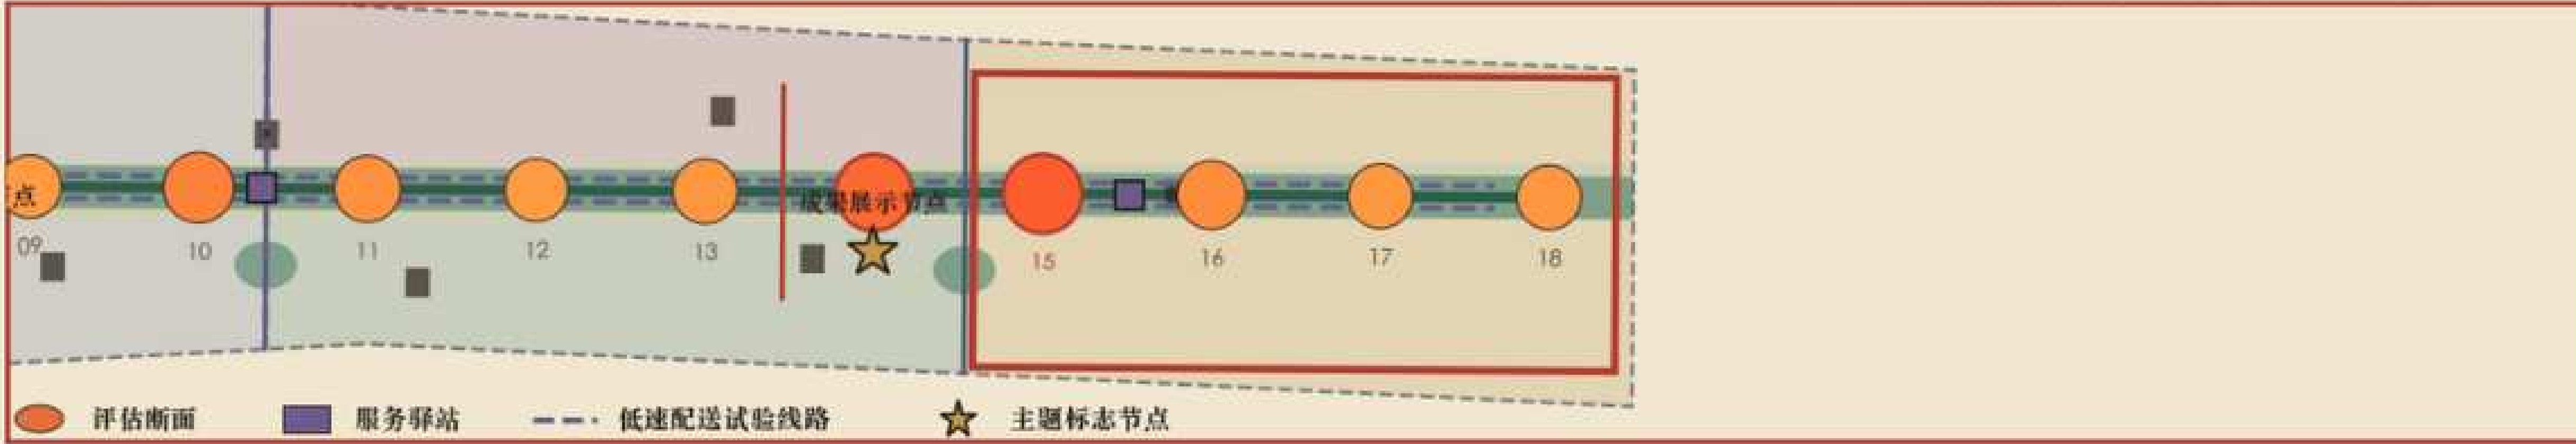

数据来源：本方案空间数据（EPSG:4326 交换，面积于 EPSG:4548 复算）与指标附件；图画由脚本自空间数据直绘。

范围为暂定研究边界，不作为法定规划边界或审批依据。公共空间感知指标为模型估算；低速配送试验线路与服务驿站为概念性建议（限速 6 公里/小时），非法定车道。

一期优先断面（短板指数 ≥ 0.45 ）

断面	街段	短板	遮阴	夜安
PS-SEC-05	ST-JZ-05	0.554	0.52	0.51
PS-SEC-15	ST-JZ-15	0.548	0.53	0.42
PS-SEC-14	ST-JZ-14	0.518	0.51	0.33
PS-SEC-06	ST-JZ-06	0.515	0.53	0.36
PS-SEC-04	ST-JZ-04	0.457	0.78	0.62


详细设计深化任务

- 01 大钟寺：无障碍接驳连续体、公共评估信息设施、HUB-01 接口
- 02 原点社区：公众调研亭、社区客厅、HUB-02 交接
- 03 众智园：验证走廊、成果展示设施、HUB-03 交接
- 04 断面整治包：遮阴、座椅、照明与铺装标准做法
- 05 运行规则：限速、避让与停止条件纳入运营协议

图说：门户区、社区与验证区三窗同比例比较，并列一期优先断面清单。

A0-6 概念效果图精选

《京张醒来之后》· 可感京张 Sensible Jing Zhang · v0.6.0 · 暂定研究边界

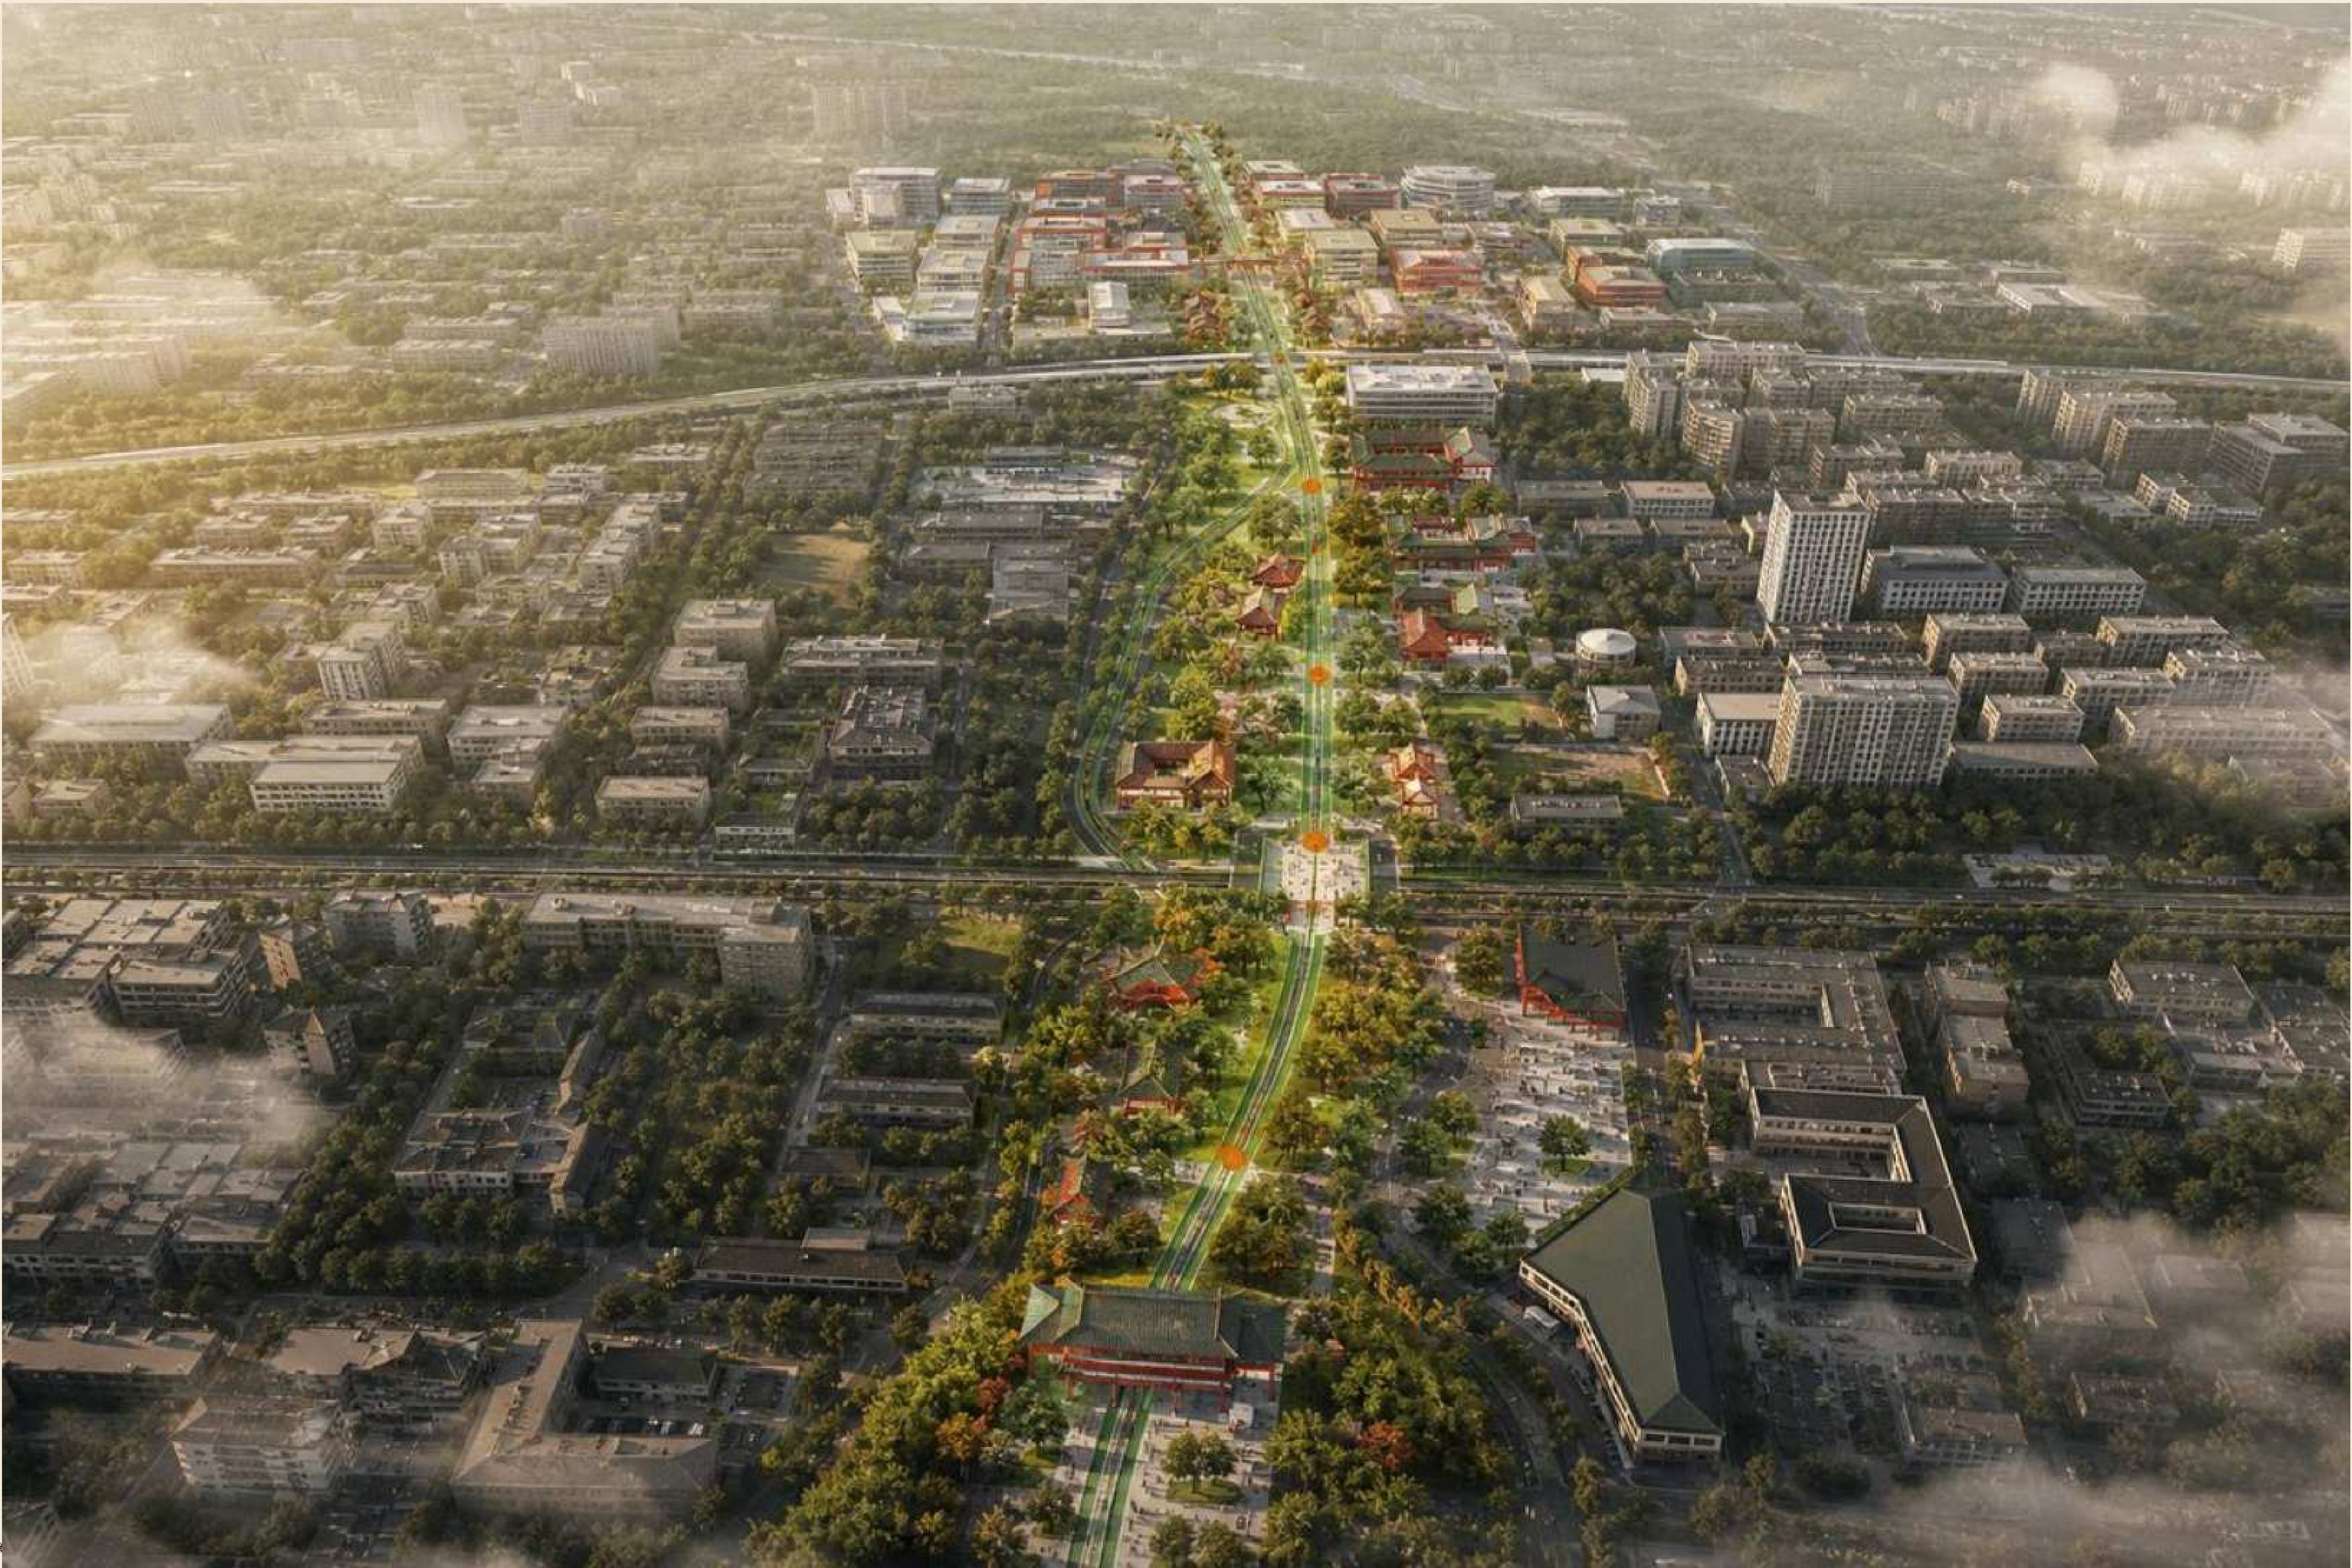

图说：全带鸟瞰概念效果图

概念性建议 · 非法定规划边界 · 效果图非实景

A0-7 京张十二幕分镜长卷

《京张醒来之后》· 可感京张 Sensible Jing Zhang · v0.6.0 · 暂定研究边界



第1幕：铁路苏醒——感知节点点亮绿脉



第2幕：第一节轨道——枕木化身座椅



第3幕：缓坡共融——轮椅与慢递机器人同行



第4幕：穿越记忆——轨下通廊静谧点亮



第5幕：车站·城门——从站台走向城市客厅



第6幕：校园边界——人潮广场因座而静



第7幕：暴晒等待——以树荫还时间以温度



第8幕：夜行安心——柔光守护每一段步行



第9幕：社区共创——民意亭里听见需求



第10幕：AI校园试验场——低速机器人共行走廊



第11幕：基线门庭——城市基线的文化门户



第12幕：触摸基线——测量权回归市民

图说：十二幕叙事与空间轴

概念性建议 · 非法定规划边界 · 效果图非实景

Board 7/8

指标证据链与建设后评估：可复算 · 可复测 · 可追溯

以公共空间短板排序确定分期；低速设备指标与场景停止条件同步登记；空间数据与指标附件为技术校核依据

图 05 / METRICS & EVIDENCE

可感京张 SENSIBLE JING-ZHANG v0.6.0

主要技术指标

研究范围	绿地几何面积比
1141.3	12.27%
公顷	
公共空间节点面积比	评估断面
1.34%	18
	高短板 5 处
试验线路	应用场景
18.8	16
公里	含测试类 6
国际案例	服务驿站
7	3
机制借鉴	处

公共空间短板排序（前十，模型估算）

PS-SEC-05		0.554
PS-SEC-15		0.548
PS-SEC-14		0.518
PS-SEC-06		0.515
PS-SEC-04		0.457
PS-SEC-10		0.446
PS-SEC-01		0.430
PS-SEC-16		0.420
PS-SEC-11		0.395
PS-SEC-07		0.390

建设后评估机制 · 全过程闭环



设施巡检结果仅用于设施状态判断，不得替代人工验收与公众反馈。

技术校核要点

规划边界	暂定研究边界
面积复算	EPSG:4548
感知类指标	模型估算待复测
强度与红线	待法定资料明确
公众调研	协议可部署 · 未实施
低速设备路权	概念建议 · 待审批

分期实施安排

一期 · 补短板

一期

5 处高短板断面整治 + 主辅贯通 + 公共评估信息设施 + 试验线路接口预留

二期 · 织网络

二期

东西向联系廊 + 口袋公园 + 公众调研亭 + 3 处驿站 + 验证走廊

三期 · 成体系

三期

建设后评估常态化运行 + 年度监测 + 多运营主体规则（经审批后）

数据来源：本方案空间数据（EPSG:4326 交换，面积于 EPSG:4548 复算）与指标附件；图画由脚本自空间数据直绘。

范围为暂定研究边界，不作为法定规划边界或审批依据。公共空间感知指标为模型估算；低速配送试验线路与服务驿站为概念性建议（限速 6 公里/小时），非法定车道。

图说：指标复算、短板排序、评估闭环与分期实施安排。

概念性建议 · 非法定规划边界 · 效果图非实景

Board 8/8