

京张智脉

Jingzhang Flowlines

骨架—毛细双相自适应流网络城市设计

百年京张AI创新带 · 概念建议 · 不替代法定规划

数据来源：临时粗略边界（非法定红线）+ 自适应流网络生成 | 面积在 EPSG:4548 复算

01 场地与证据链总览


临时边界 + 三处重点区 + 骨架相主轴



--- 临时边界 (非红线) 重点区域 (临时)
—— 骨架相主轴 绿地骨架

02 用地结构 (流网络分区生成)

覆盖提交边界 100.00%，无缝隙无重叠

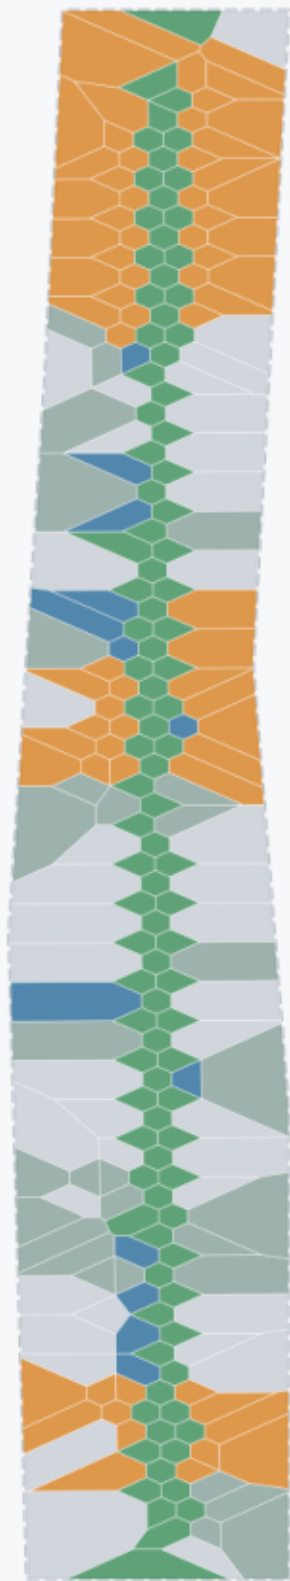

- 用地分类
- 城镇住宅

商业服务业


公园绿地

留白用地

科研用地


03 重点区域详细设计：三种流角色

众智园·源点

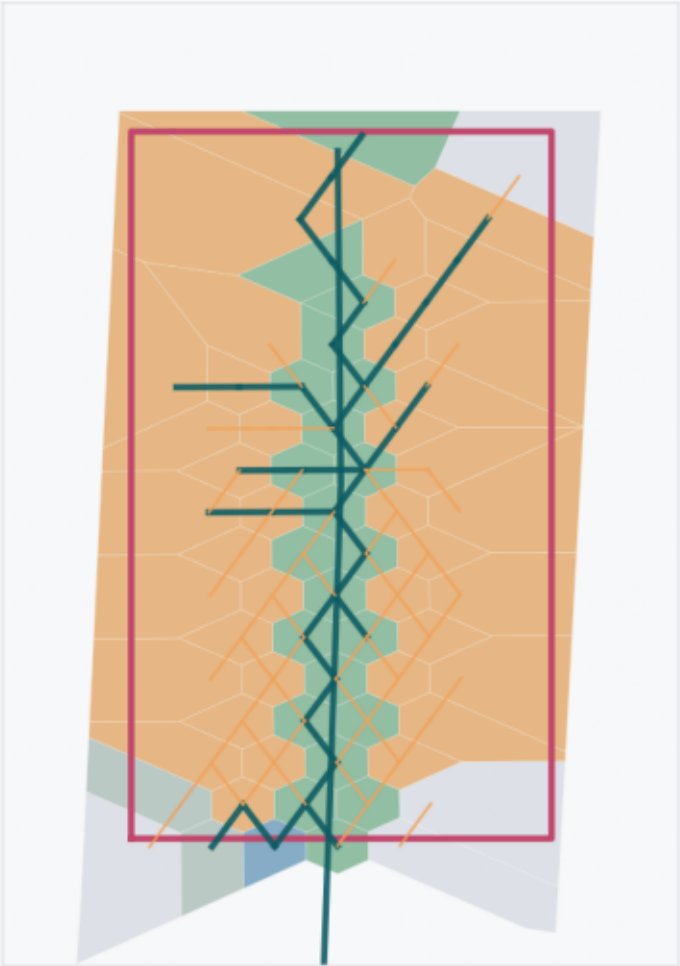


公告面积约 192.1 公顷 (临时范围)

AI原点社区·原点

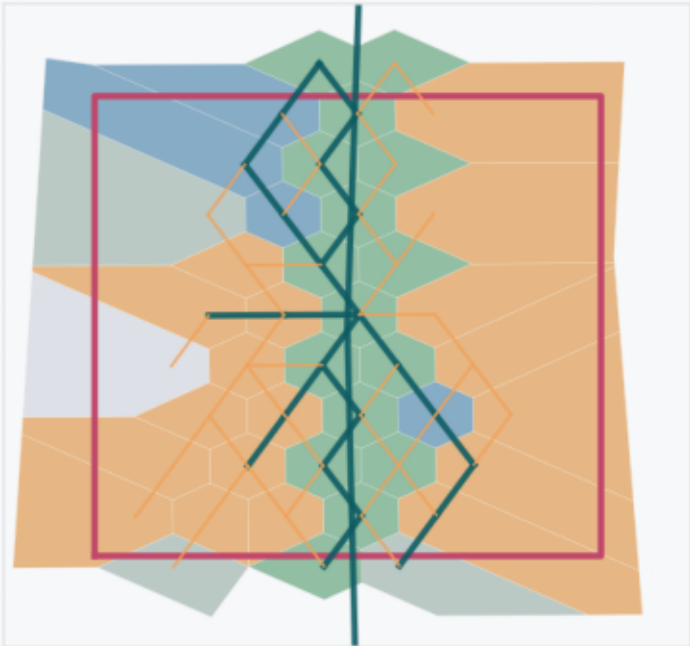

公告面积约 104.3 公顷 (临时范围)

大钟寺·枢点

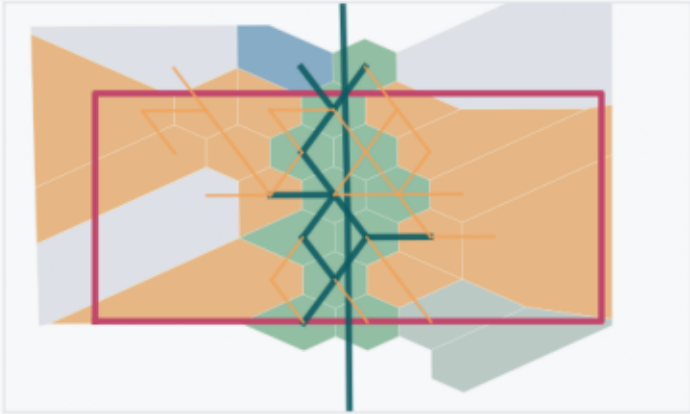


公告面积约 72.0 公顷 (临时范围)

数据来源：临时粗略边界（非法定红线）+ 自适应流网络生成 | 面积在 EPSG:4548 复算

04 骨架—毛细网络与蓝绿空间

骨架 149 段 / 毛细 216 段 / 独立环 109 个

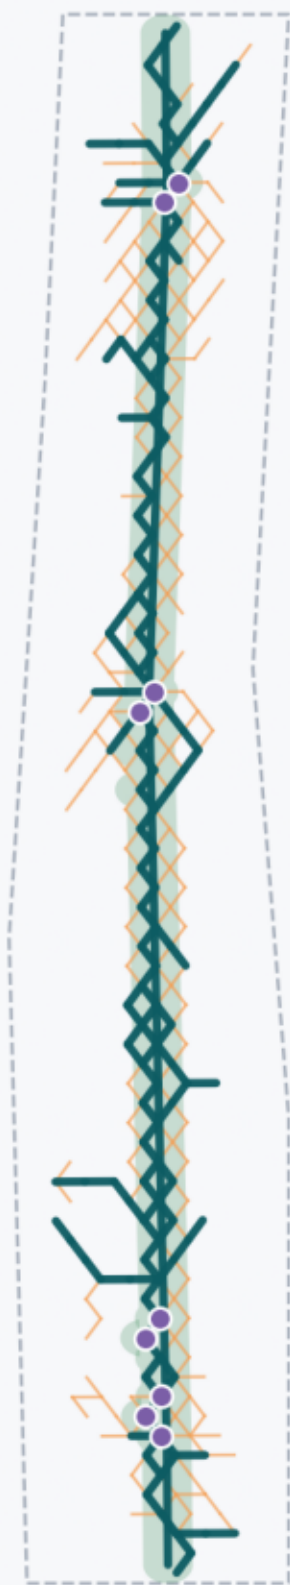

- 骨架相 ($\gamma \geq 1$, 层级)
- 脉点广场
- 毛细相 ($\gamma < 1$, 含环)
- 绿地骨架

05 指标复算与基准检验（含反面结果）

复算指标



场地面积
11.41 km²

绿地率
20.64%

公共空间
1.28%

重点区数
3

容积率
待正式数据补齐

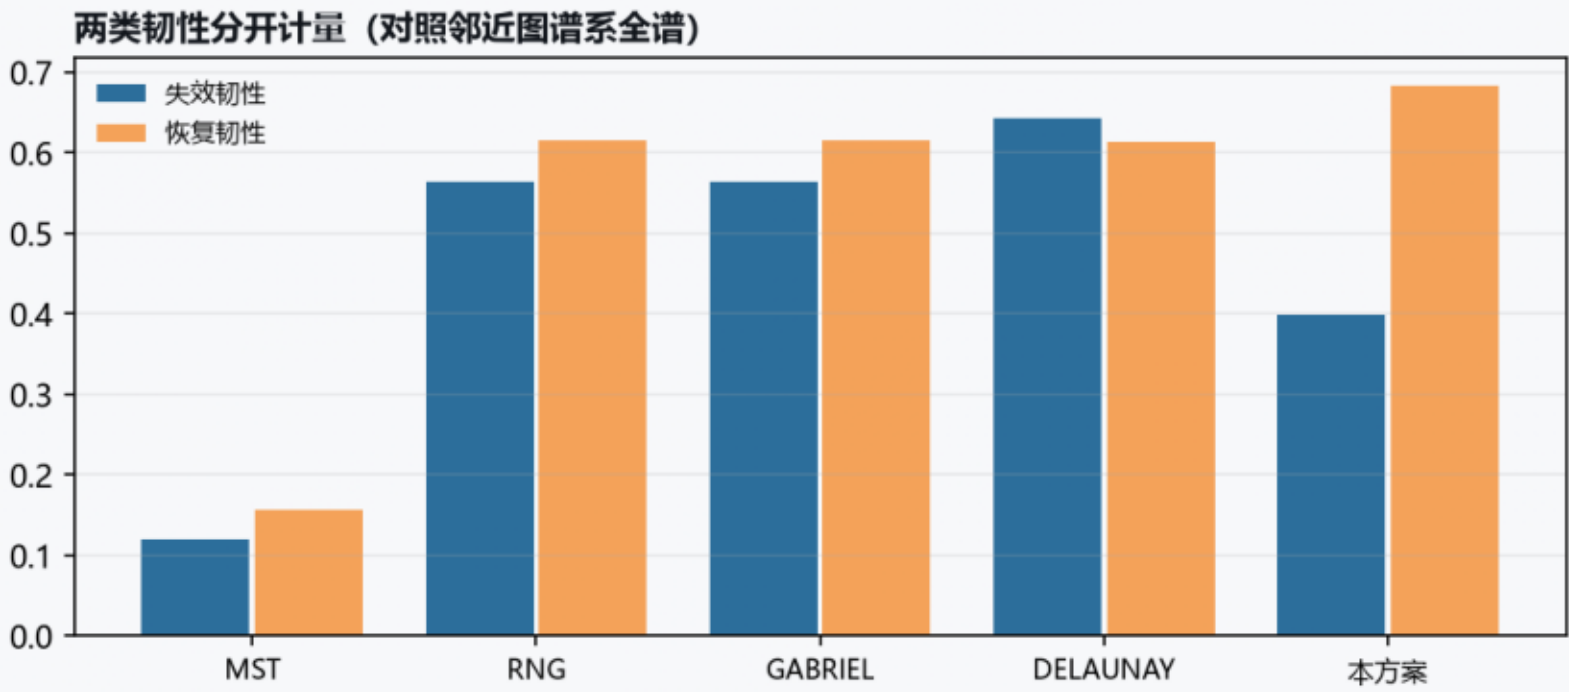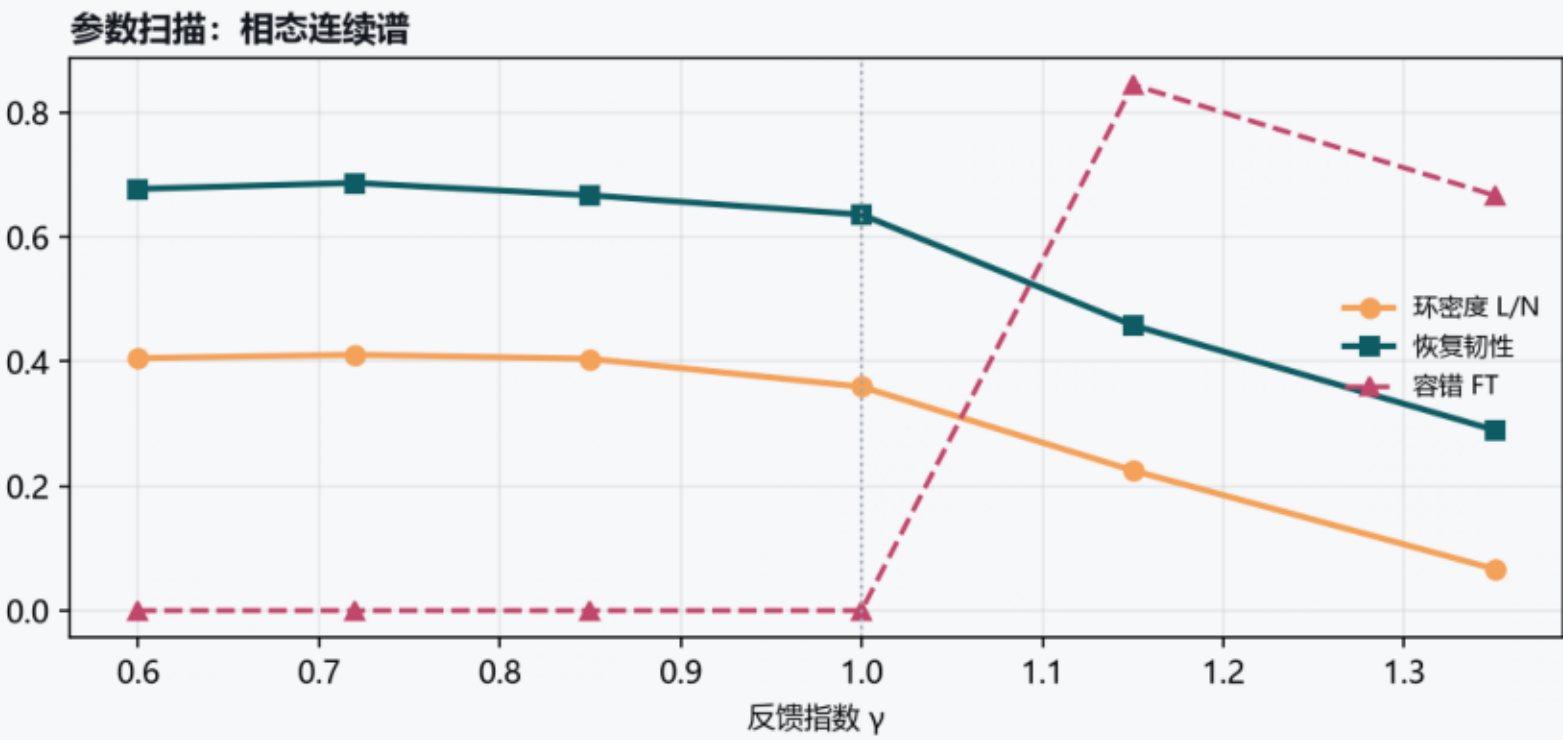

诚实读法：
本方案节点覆盖 0.3865，
是一层建议网络，非最小生成树替代品，
因此总长低于 1 不等于更便宜。

更密的基准在失效韧性上仍占优；
本方案以更低造价换取更高恢复韧性。