


# 京张1909 · AI创新带

## 总体方案 — 一轨两河三站 · 六轴多点

总览地图 · 总体空间结构：一轨两河三站 · 六轴多点（北向图右）

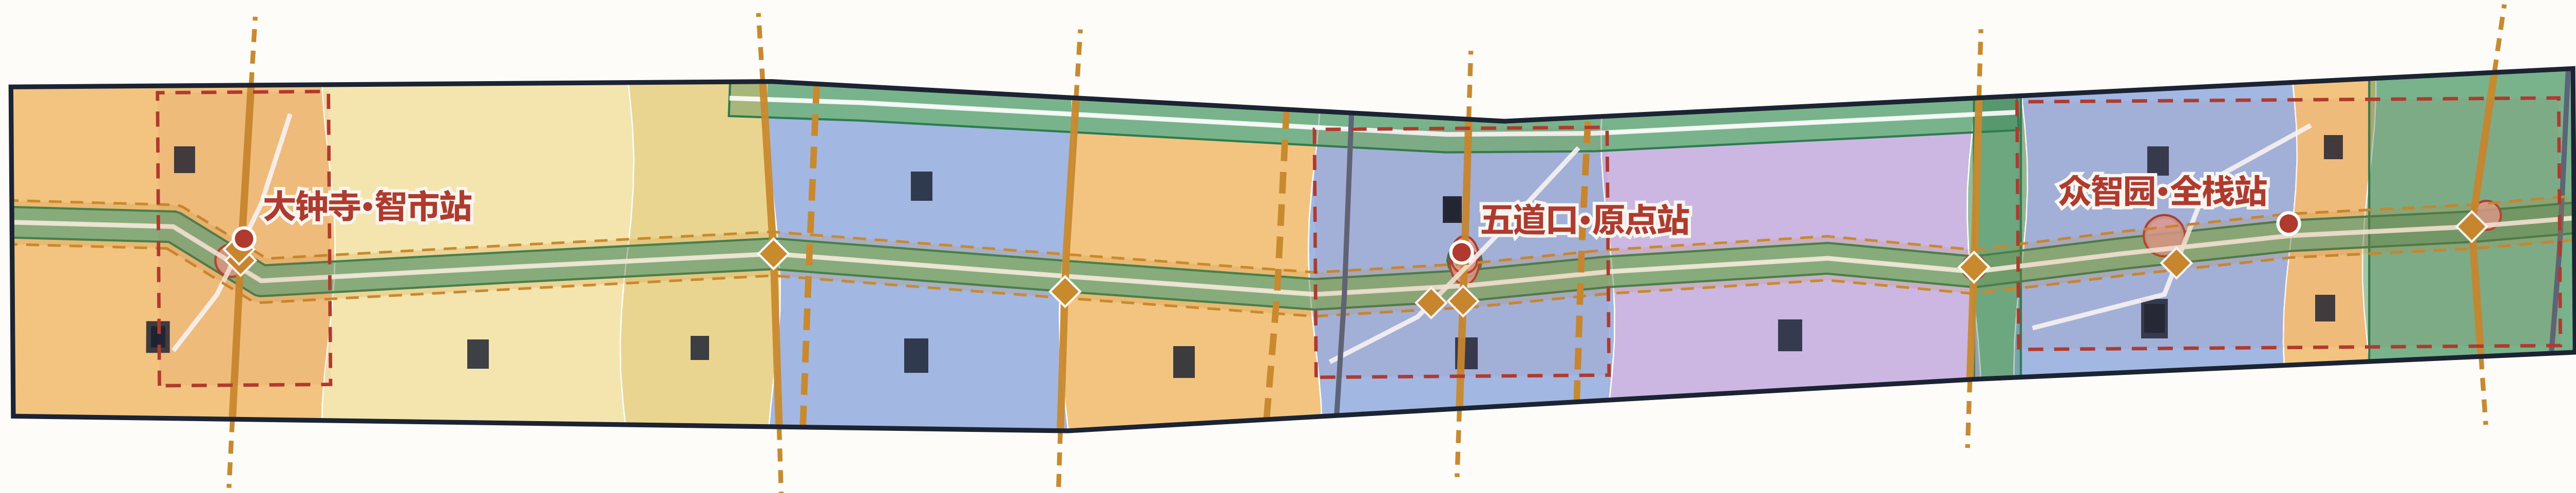

商业服务业 05 256 ha 居住 0701 132 ha 社区服务 0702 66 ha 科研 0802 306 ha 教育 0804 113 ha 公园绿地 1401 245 ha 防护绿地 1402 18 ha 广场 1403 5 ha 既有京张铁路线位（遗产轨线脊） 现状主干道 重点区域（临时约束） 站前广场与公共空间 示范更新建筑基底 蓝绿开敞空间

临时约束边界：本带全部图面与面积指标基于仓库登记的临时范围线，仅供方案讨论与自验；官方边界发布后整体重置。

### 一轨

京张遗产轨线慢行文化脊：沿 1909 年线位设置约 9.8 公里、宽约 116 米遗产公园脊，慢行、文化展示与 AI 场景复合轴（控规“一带”核心段）。

### 两河

清河生态客厅（北端约 83.4 公顷滨水界面）× 小月河场景连接绿廊（场地内接驳段，沿东边线内缩约 62 米，河道本体在场地外），衔接控规景观结构“三带”。

### 六轴多点

六条东西缝合轴（大钟寺/学院路/知春路/五道口/五环上跨/清河流水）响应控规“南北贯通、东西连通”；遗产脊与 9 条横向线路 18 处穿廊交点按“一线一点”设 9 处缝合广场，对位控规“多点”体系。

### 核心指标

约 1,141.3 公顷

总体设计范围  
公估约 11.4 平方公里。临时边界复算一致

23.5%

绿地率（复算）  
green\_space 图层开集 / 提交范围；口径对照见正文

约 9.8 公里

遗产轨线慢行文化脊  
串联三站与全部文化节点

63 个

用地单元  
同一切割线平面切分，无缝无重叠全覆盖

19 处

示范性更新建筑  
新建 8 + 改造 9 + 保留 2；拆除待现状调查

3 处 / 约 368.4 公顷

重点区域  
众智园 - 原点社区 - 大钟寺（临时范围）

### 分期实施

#### 一期

约 748.9 公顷

三站首开区与遗产轨线指示范段

#### 二期

约 167.6 公顷

原点社区从源与清河界面，众智园概念先行区启动

#### 三期

约 224.7 公顷

众智园全栈区与两河客厅全面建成



# 京张1909 · AI创新带

证据与运营 — 可复算、可审计、可迭代

## AI+ 场景体系

| 编号 | 场景          | 空间载体     | 摘要                                                                                            |
|----|-------------|----------|-----------------------------------------------------------------------------------------------|
| 01 | AI慢行导航      | 遗产轨线脊全线  | 可解释导航与低侵入传感识别断点与衔接节点，输出人工可复核建议                                                                |
| 02 | 企业服务Copilot | 三站服务驿站   | 政策检索、空间匹配与申报导航，结论附来源与置信度                                                                      |
| 03 | 公共安全与活动运营复核 | 站前广场群    | 人流与活动风险只微聚合预警，处置决定由人工作出                                                                       |
| 04 | 低速无人配送测试    | 原点社区内街   | 限定路线、限速、可回退的配送试点，数据分级开放                                                                       |
| 05 | AI文化导览      | 1909记忆线路 | 多语导览讲述京张铁路与中关村创新史，史实经文献复核                                                                     |
| 06 | AI健康服务导航    | 社区服务节点   | 连接周边医疗与健康资源，不提供诊断结论；医疗等公共服务场所保留现场指导与人工办理通道，传统服务与智能服务并行按图力发（2020）45号政策背景把握（其阶段性目标已到期，仅作参考设计参考） |
| 07 | 安全治理沙盘（测试）  | 众智园实验楼   | 标准制定、可信评测与模型红队测试的可参观协作节点                                                                      |
| 08 | 边缘算力驿站（测试）  | 三站公共服务点  | 分布式算力与低碳能源融合的新基建原型，供专业团队深化                                                                    |
| 09 | 开源发布厅       | 原点站广场    | 成果发布、代码贡献展示与小型路演                                                                              |
| 10 | 低碳运行监测（测试）  | 清河凉水客厅   | 雨洪、能耗与碳排放监测展示，指标口径公开                                                                          |
| 11 | 数据要素会客厅     | 大钟寺片区    | 以合规、授权、可审计为前提的数据流通城市界面                                                                        |
| 12 | 1909全球活动周路线 | 一带公共空间   | 开发者节、场景开放日与朝圣路线的年度运营组合                                                                        |

## 指标复算

|               |            |
|---------------|------------|
| 提交范围面积        | 1,141.3 公顷 |
| 蓝绿开敞空间面积      | 267.9 公顷   |
| 蓝绿开敞空间占比      | 23.5%      |
| 公共空间面积        | 6.3 公顷     |
| 公共空间占比        | 0.6%       |
| 示范建筑基底面积      | 13.0 公顷    |
| 示范建筑基底占比（设计值） | 1.1%       |
| 道路中心线总长       | 25,471 m   |
| 遗产轨线脊长度       | 9,800 m    |
| 一期面积          | 748.9 公顷   |
| 二期面积          | 167.6 公顷   |
| 三期面积          | 224.7 公顷   |
| 重点区域数量        | 3          |
| 用地单元数量        | 63         |

数据缺口（待正式数据补齐）：容积率、建筑高度上限、法定建筑密度、法定绿地率管控、退线控制 — 待正式数据补齐

## 任务覆盖与专业矩阵

- 公告任务 17/17 全覆盖
- 智能体任务 6/6 全覆盖
- 正式设计深度 15/15 完成
- 专业标准响应 9 条（含 3 条非强制新增标准）

## 来源分层

- SITE-PACKAGE** — 任务书、校毕、设计空间、限值、模式与临时边界等场地包材料。
- SOURCE-REGISTRY** — 区分 formal 可用、背景、临时与待审资料的登记册。
- PROCESSED-FACT-PACK** — 范围、任务、资料用途与缺资料清单的导航图，非新权威来源。
- BOUNDARY-SOURCE** — 提交总体设计范围（临时约束），仅用于生成、展示与临时自信。
- KEY-AREA-SOURCE** — 三处重点区域范围（临时约束），仅用于生成、展示与临时自信。
- OFFICIAL-ANNOUNCEMENT** — 公告 1.3/1.4/1.5 的任务、范围、面积、语言与成果归属主控依据。
- AGENT-TASKBOOK** — 十条共创原则，六项智能体任务、场景/品牌/运营要求与边界条款。
- GLOBAL-CASE-BACKGROUND** — 全球创新生态案例为背景研究（匹兹堡、伦敦国王十字、Kista、Kendall Square、深圳南山、杭州城西、慕尼黑 Werksviertel），仅作参考参照，不作为正式证据。
- KG-DRAFT-2024** — 《北京海淀区京张铁路遗址公园沿线（人工智能创新街区重点地区）HD00-1601等街区控制性详细规划（街区层面）（2022-2035年）（草案）》公示图则（北京市规划和自然资源委员会海淀分局，2024-12-20 公示）；空间结构“一带一轴、两心多点”、三大目标定位、规模控制（常住约36.4万人、城乡建设用地约1648.1公顷、建筑规模约2369.3万平方米）、九类主导功能分区、配套设施（公共服务298处等）、整体景观结构“三带六轴、多廊多中心”、交通体系（道路网密度约8.0公里/平方公里、绿色出行80%）等结构性衔接依据。
- KG-APPROVAL-2026** — 北京日报报道（2026-08-12）：市规划自然资源委于 2026-08-11 批复《北京海淀区京张铁路遗址公园沿线（人工智能创新街区重点地区）HD00—1601等街区控制性详细规划（街区层面）（2024年—2035年）》；范围东至新街口外大街、西至中关村大街、北至成府路、南至西直门外大街，共 9 个街区约 1668.2 公顷；以绿色公共空间建设引领区域城市更新，发展大模型、智能体、具身智能等新业态，构建生活圈与创新圈融合的一刻钟社区服务圈。