


ONE PUBLIC BASELINE • THREE VERIFIABLE CIVIC PROTOTYPES

ONE PUBLIC BASELINE • THREE VERIFIABLE CIVIC PROTOTYPES


Urban fabric, continuous space, six stitches and three landmark archetypes

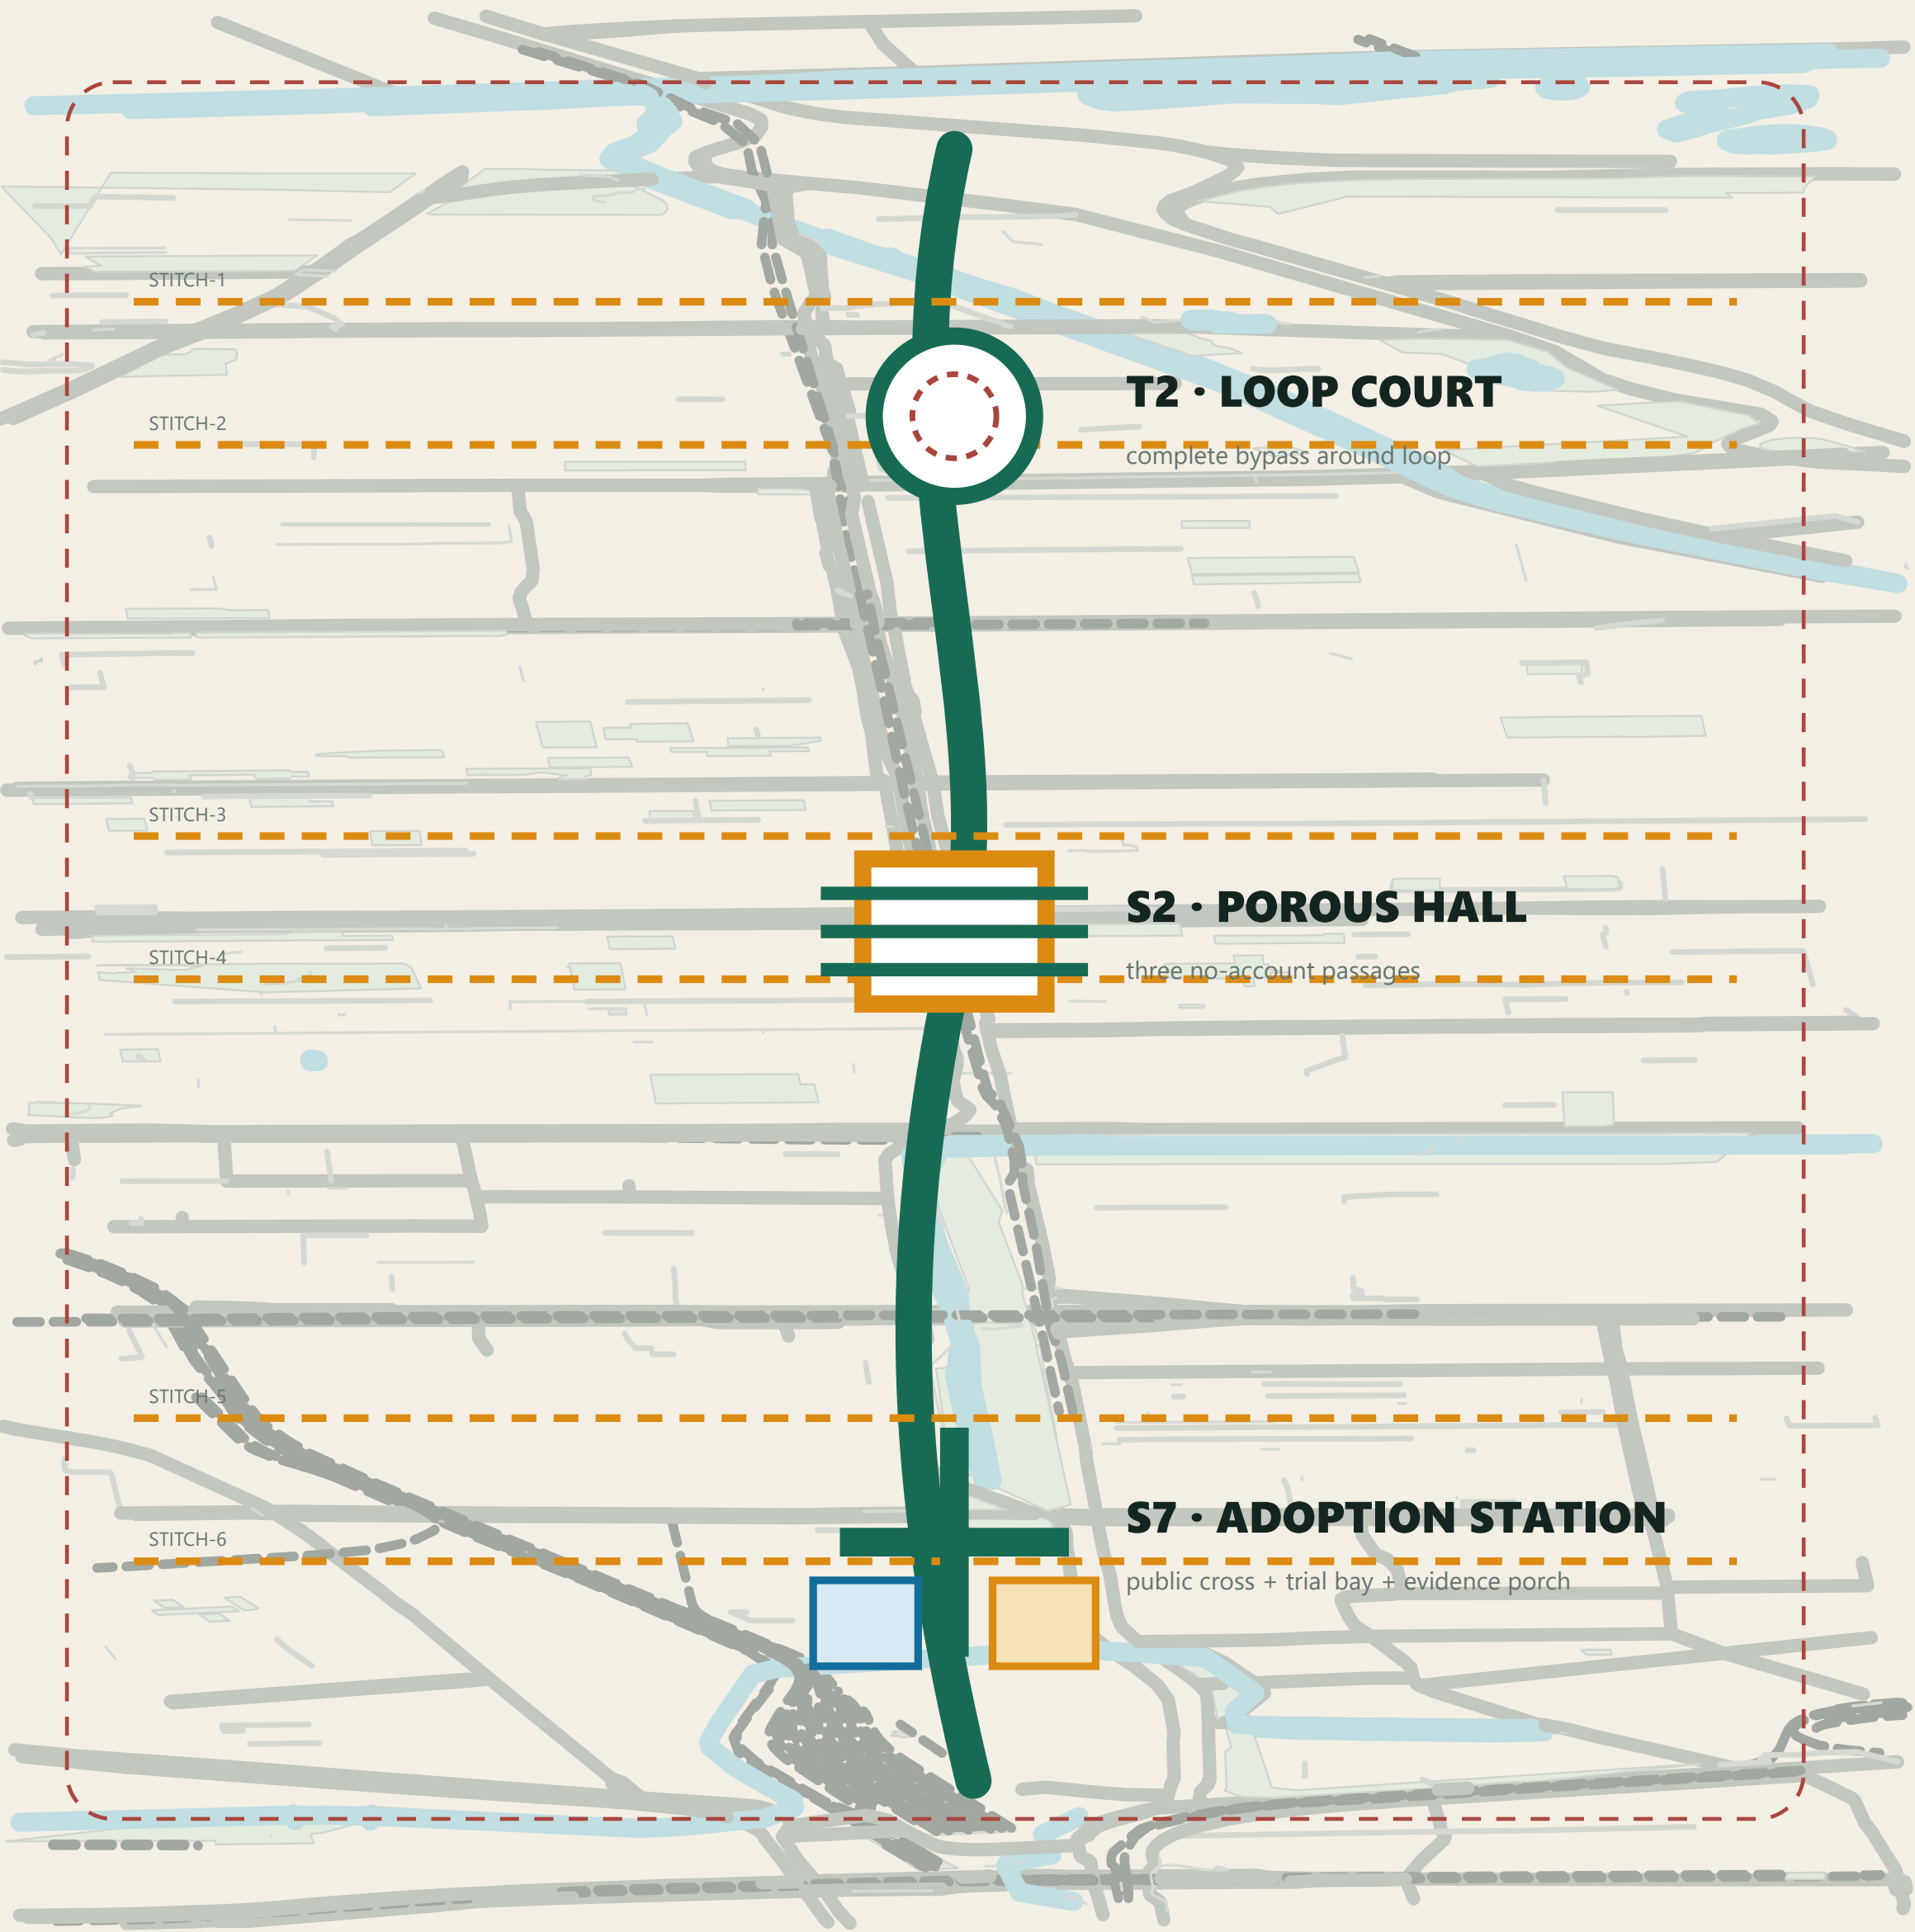

Map data © OpenStreetMap contributors · ODbL · 2026-08-13

SPINE • STATIONS • WINGS

THREE DISTINCT SPATIAL TYPES

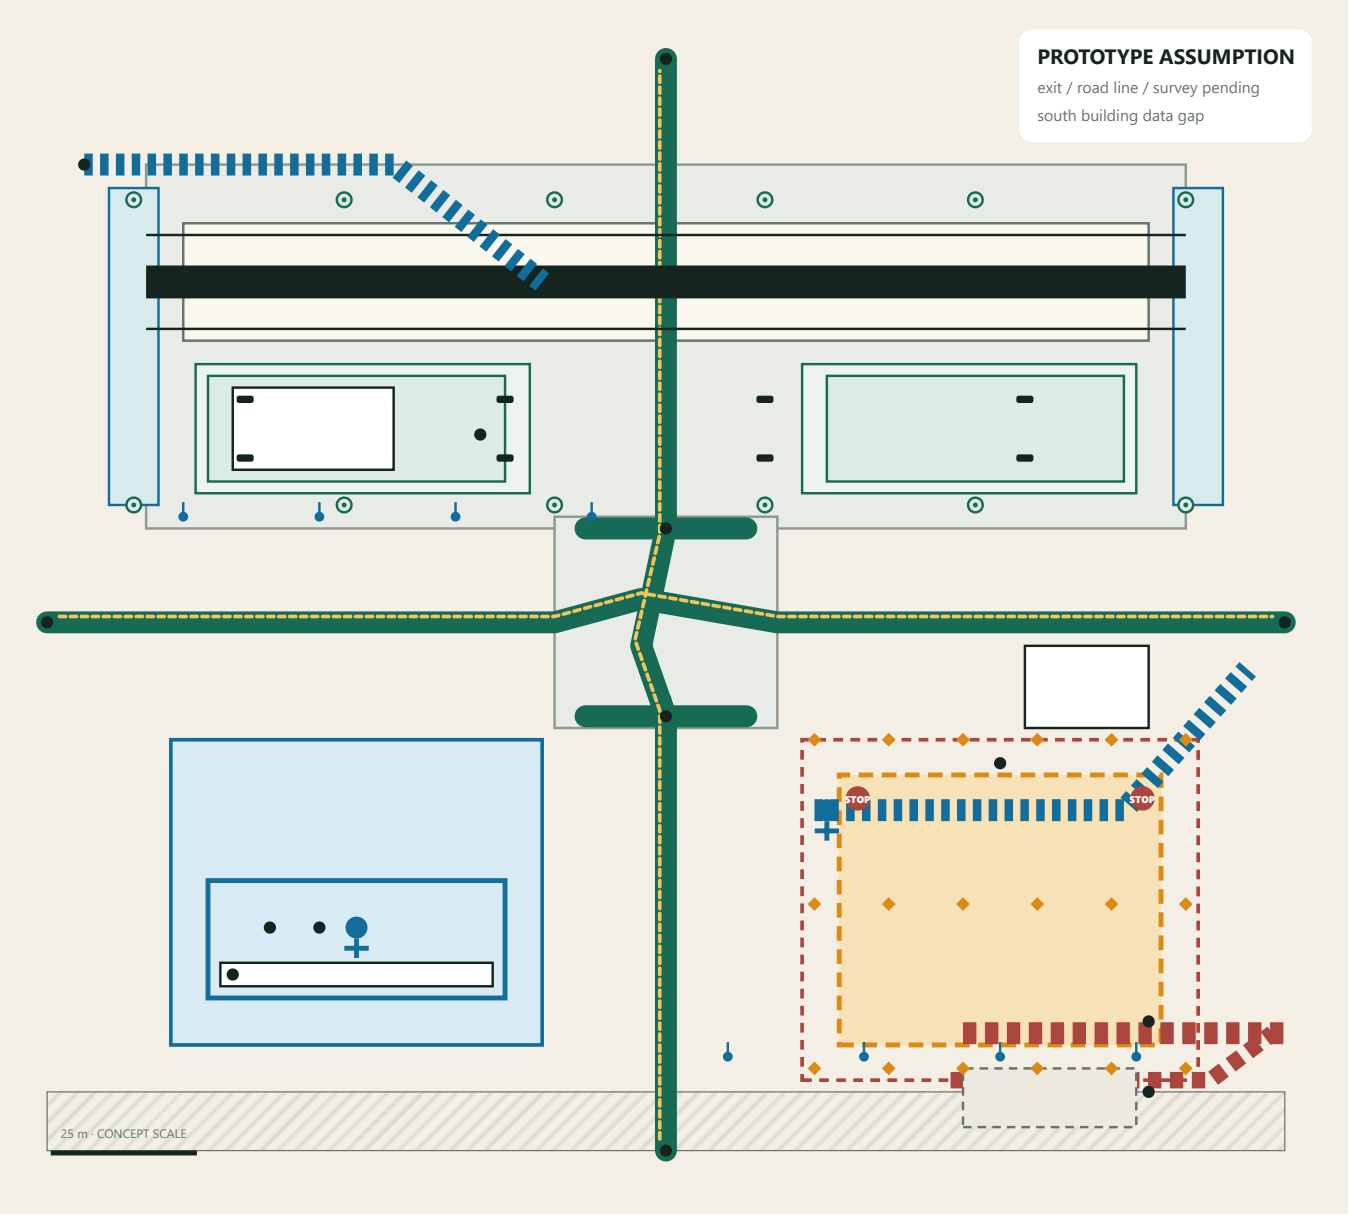


PUBLIC CROSS STAYS OPEN
AI ENTERS ONE REVERSIBLE BAY
DECISION REMAINS AT THE PORCH
E2 DOCUMENTED • NOT BUILT • NOT FIELD-RUN

Dazhongsi OSM has one building feature; no existing fabric is invented.

FIVE-SECOND CLAIM

BASELINE STANDS FIRST


AI THEN ENTERS PAIRED PROOF

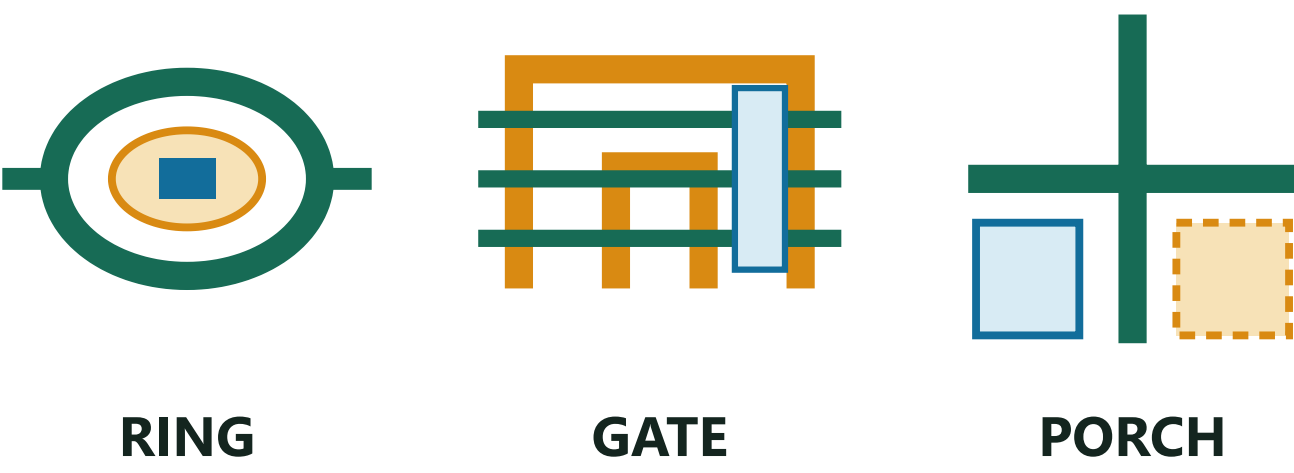

REGIONAL ADOPTION LOOP

- 01 PUBLIC PROBLEM
- 02 REPRODUCE
- 03 PAIRED TEST
- 04 HUMAN DECIDE
- 05 ARCHIVE

E2 DOCUMENTED • NOT BUILT • NOT FIELD-RUN

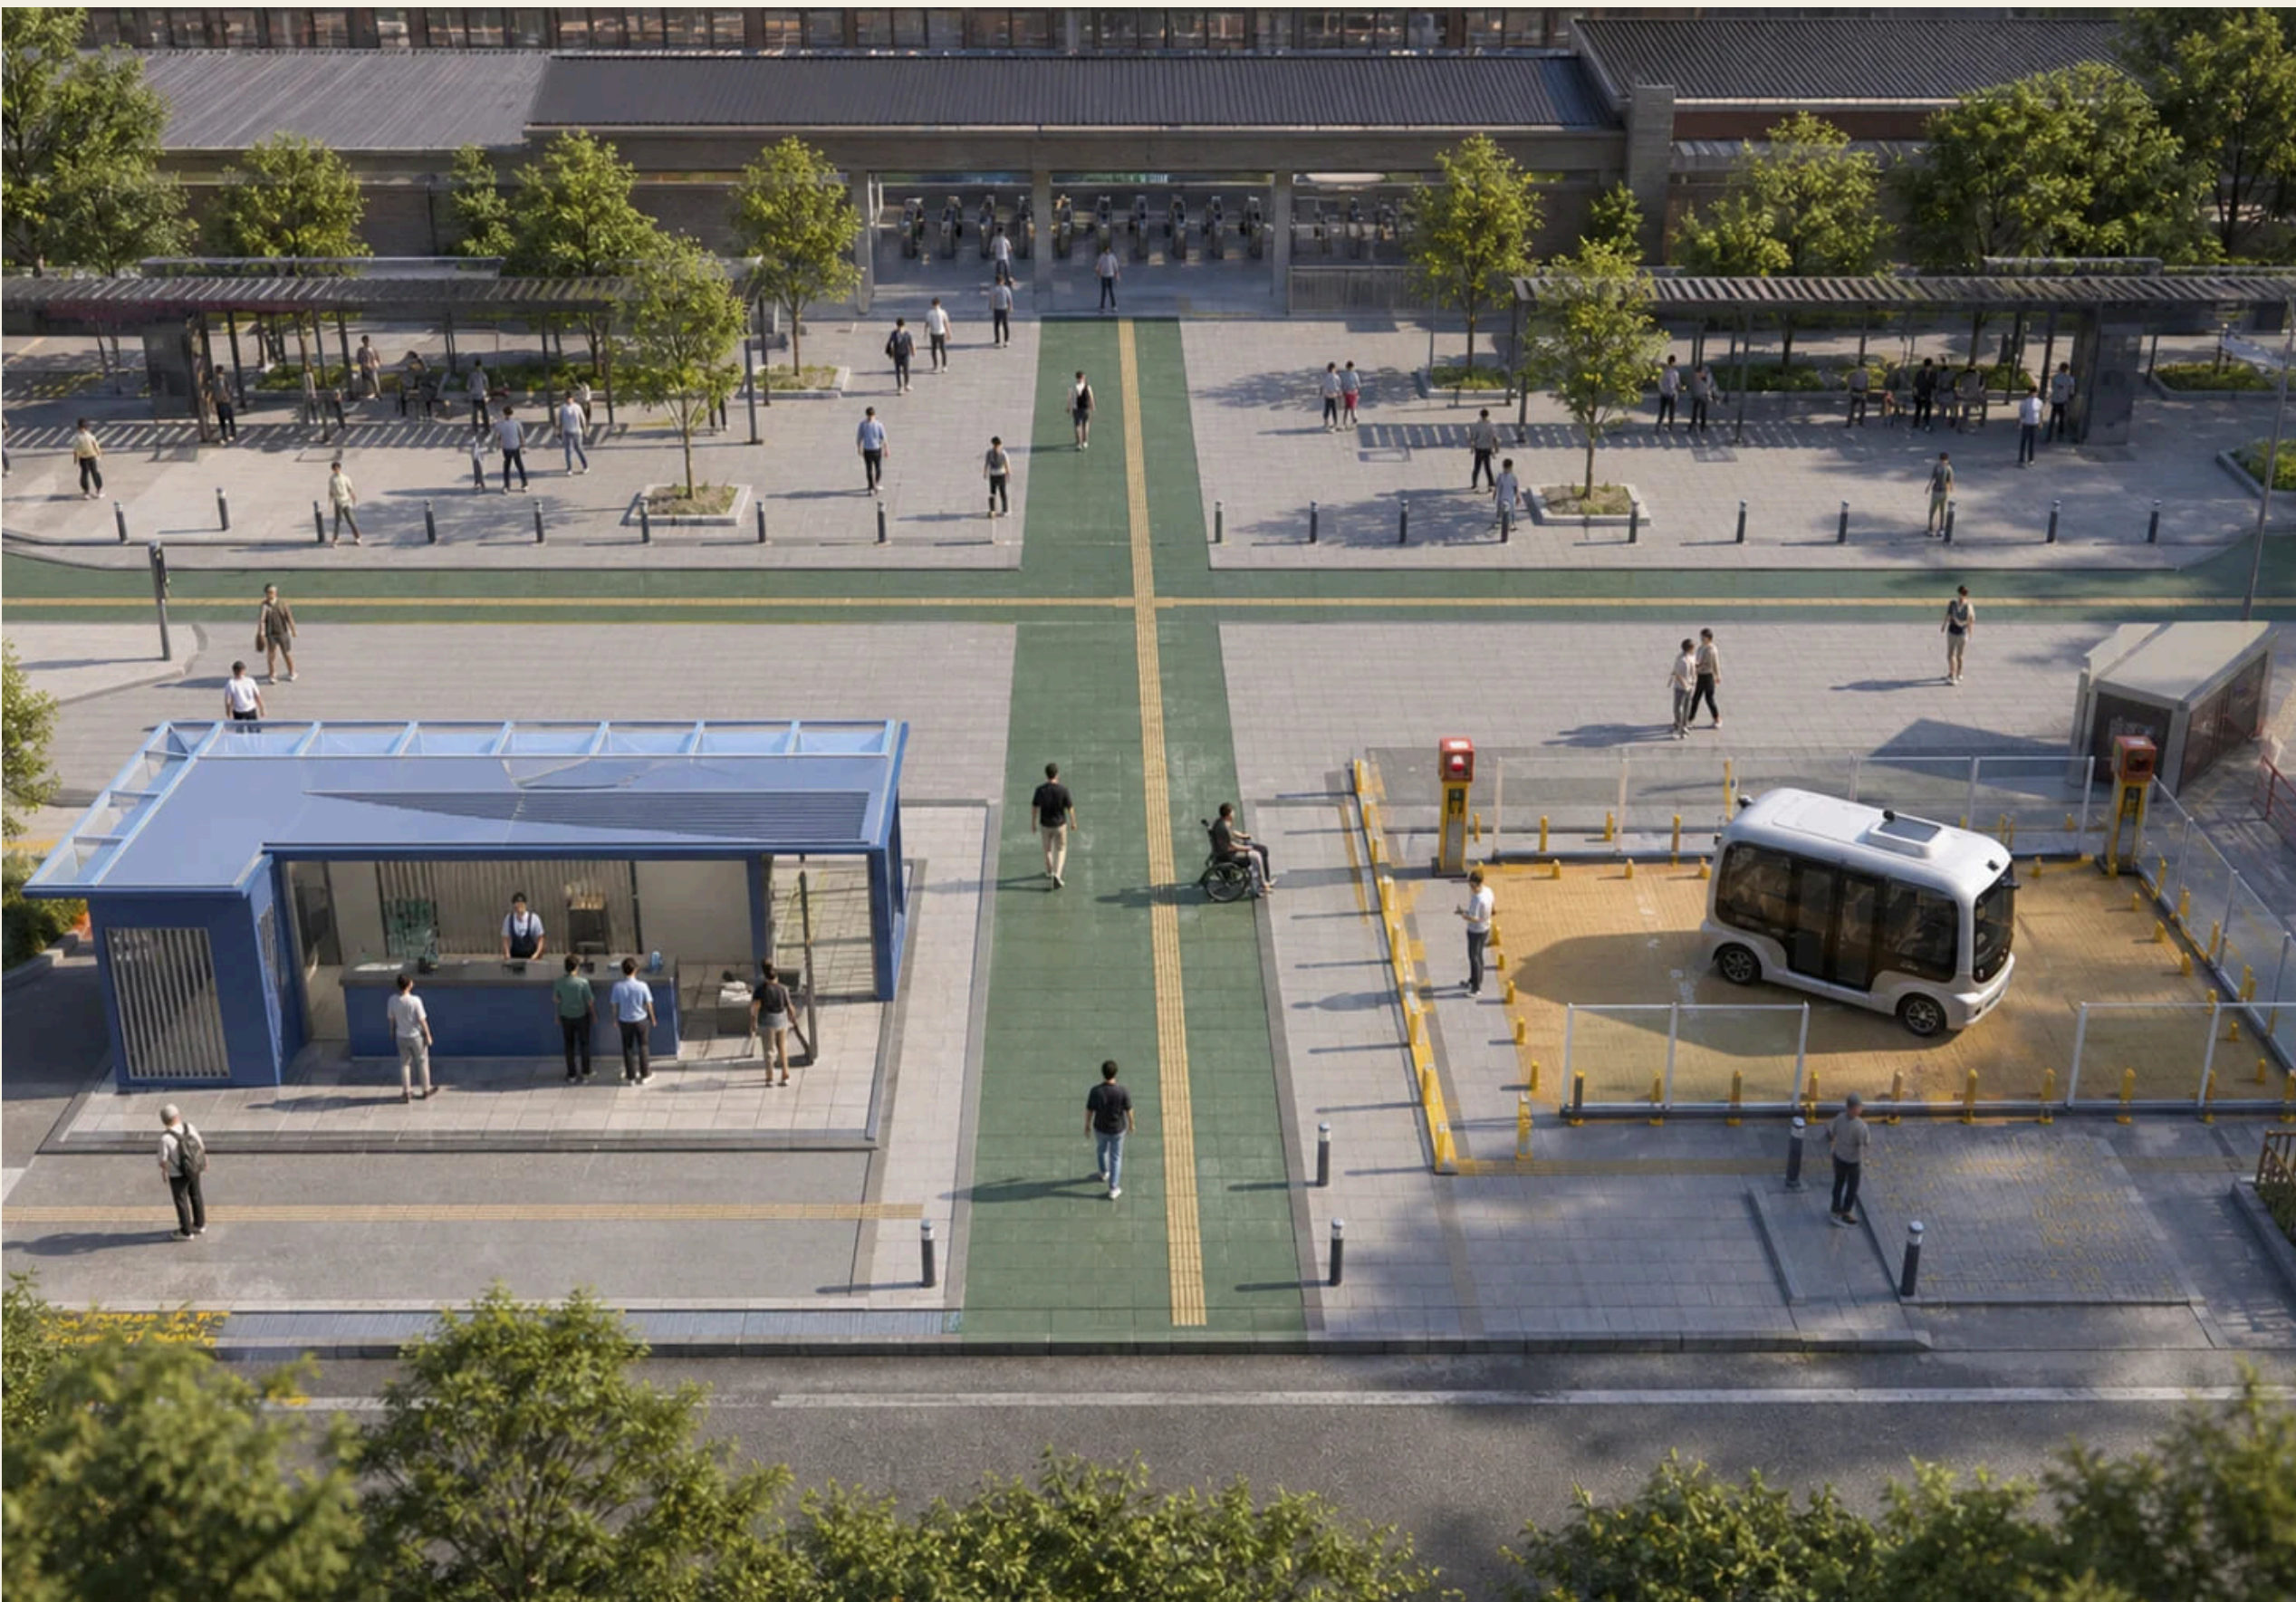

BASELINE STANDS FIRST

AI THEN PROVES VALUE

RECEIPT DECIDES ADOPT / REVISE / STOP


E2 DOCUMENTED • NOT BUILT • NOT FIELD-RUN

Map data © OpenStreetMap contributors · ODbL · 2026-08-13 · concept layout pending official base

PUBLIC PROBLEM TO KNOWLEDGE ASSET • INPUT, OWNER + FAILURE EXIT AT EVERY STEP






Annual receipts return to the public problem ledger; no promotional ranking

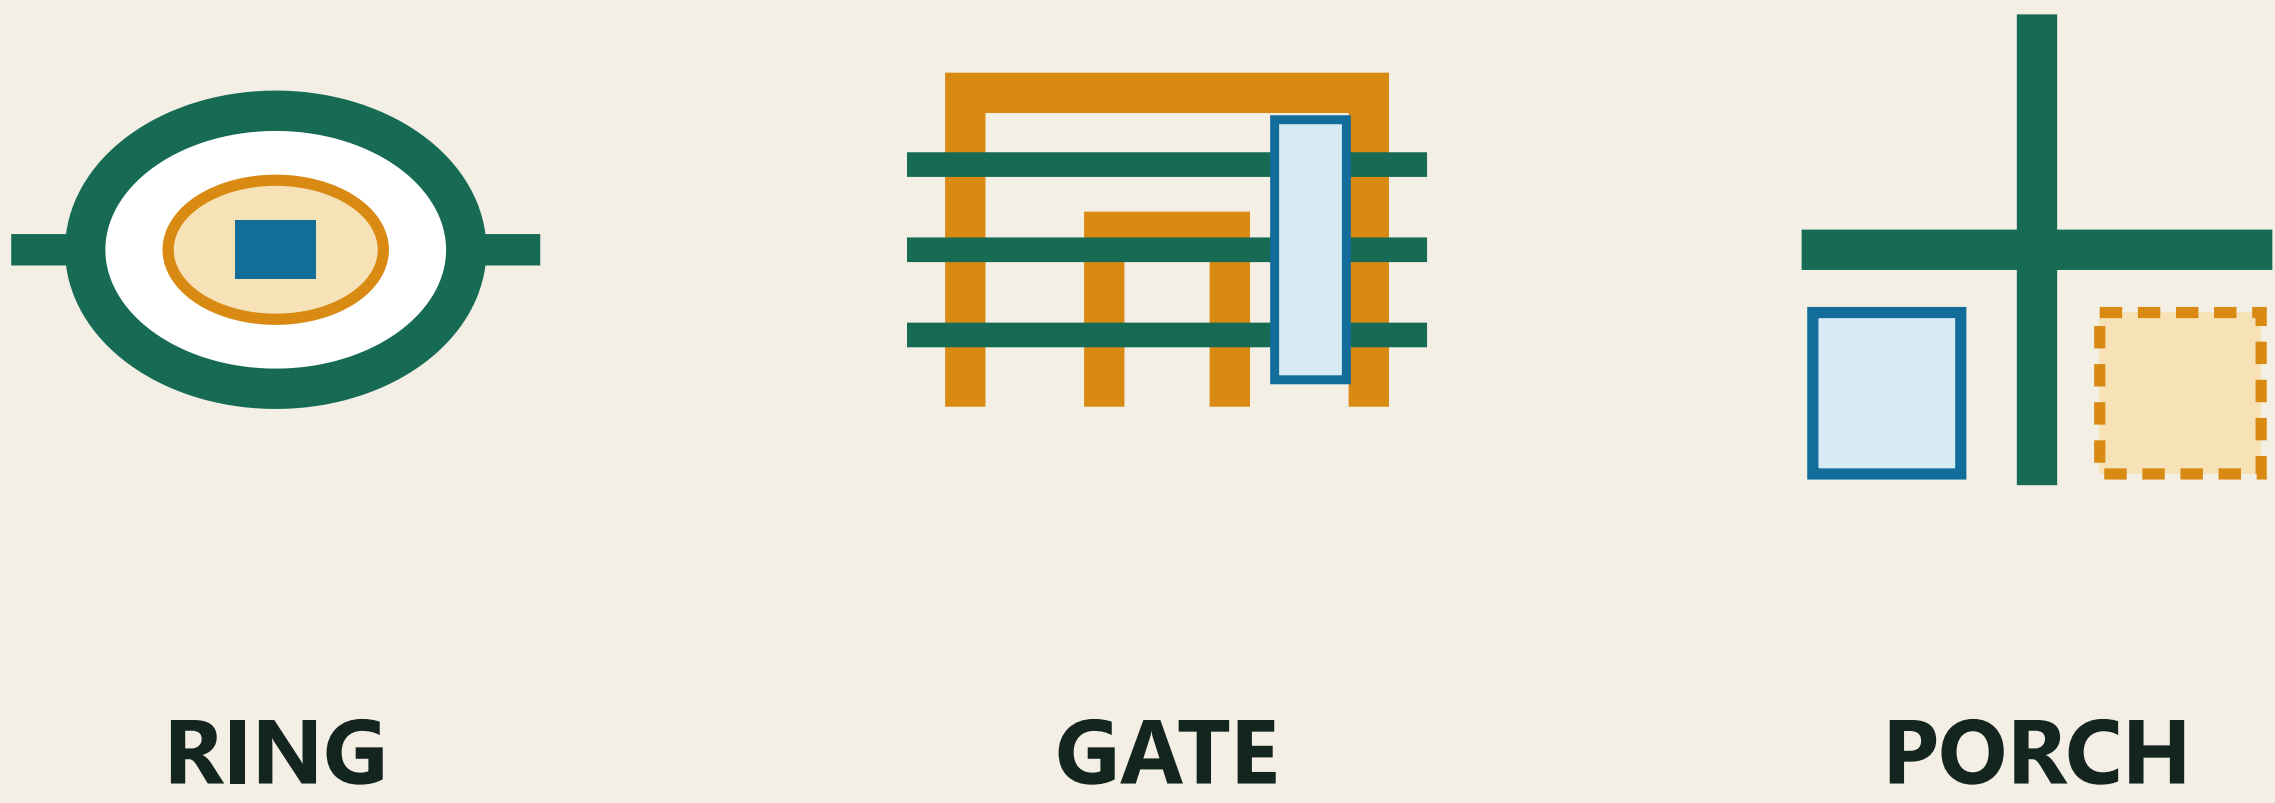

DAZHONGSI RECEIPT PORCH • THE TRIAL NEVER CAPTURES THE PUBLIC CROSS


THREE LANDMARKS • S7 LAYERED CUTAWAY AS FLAGSHIP EVIDENCE

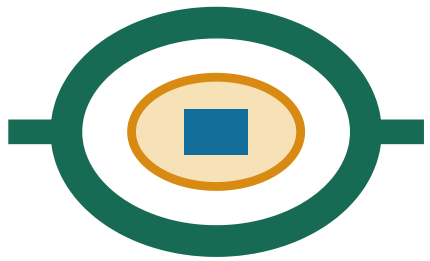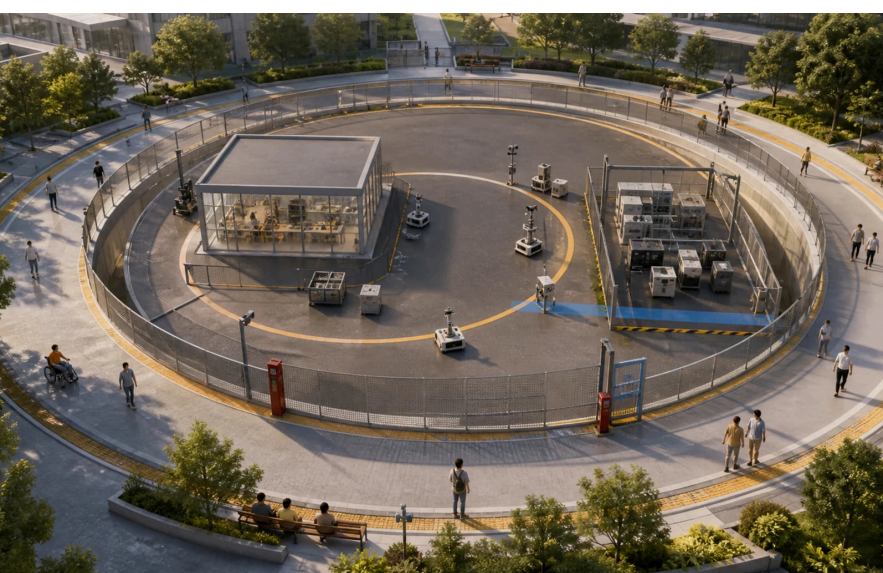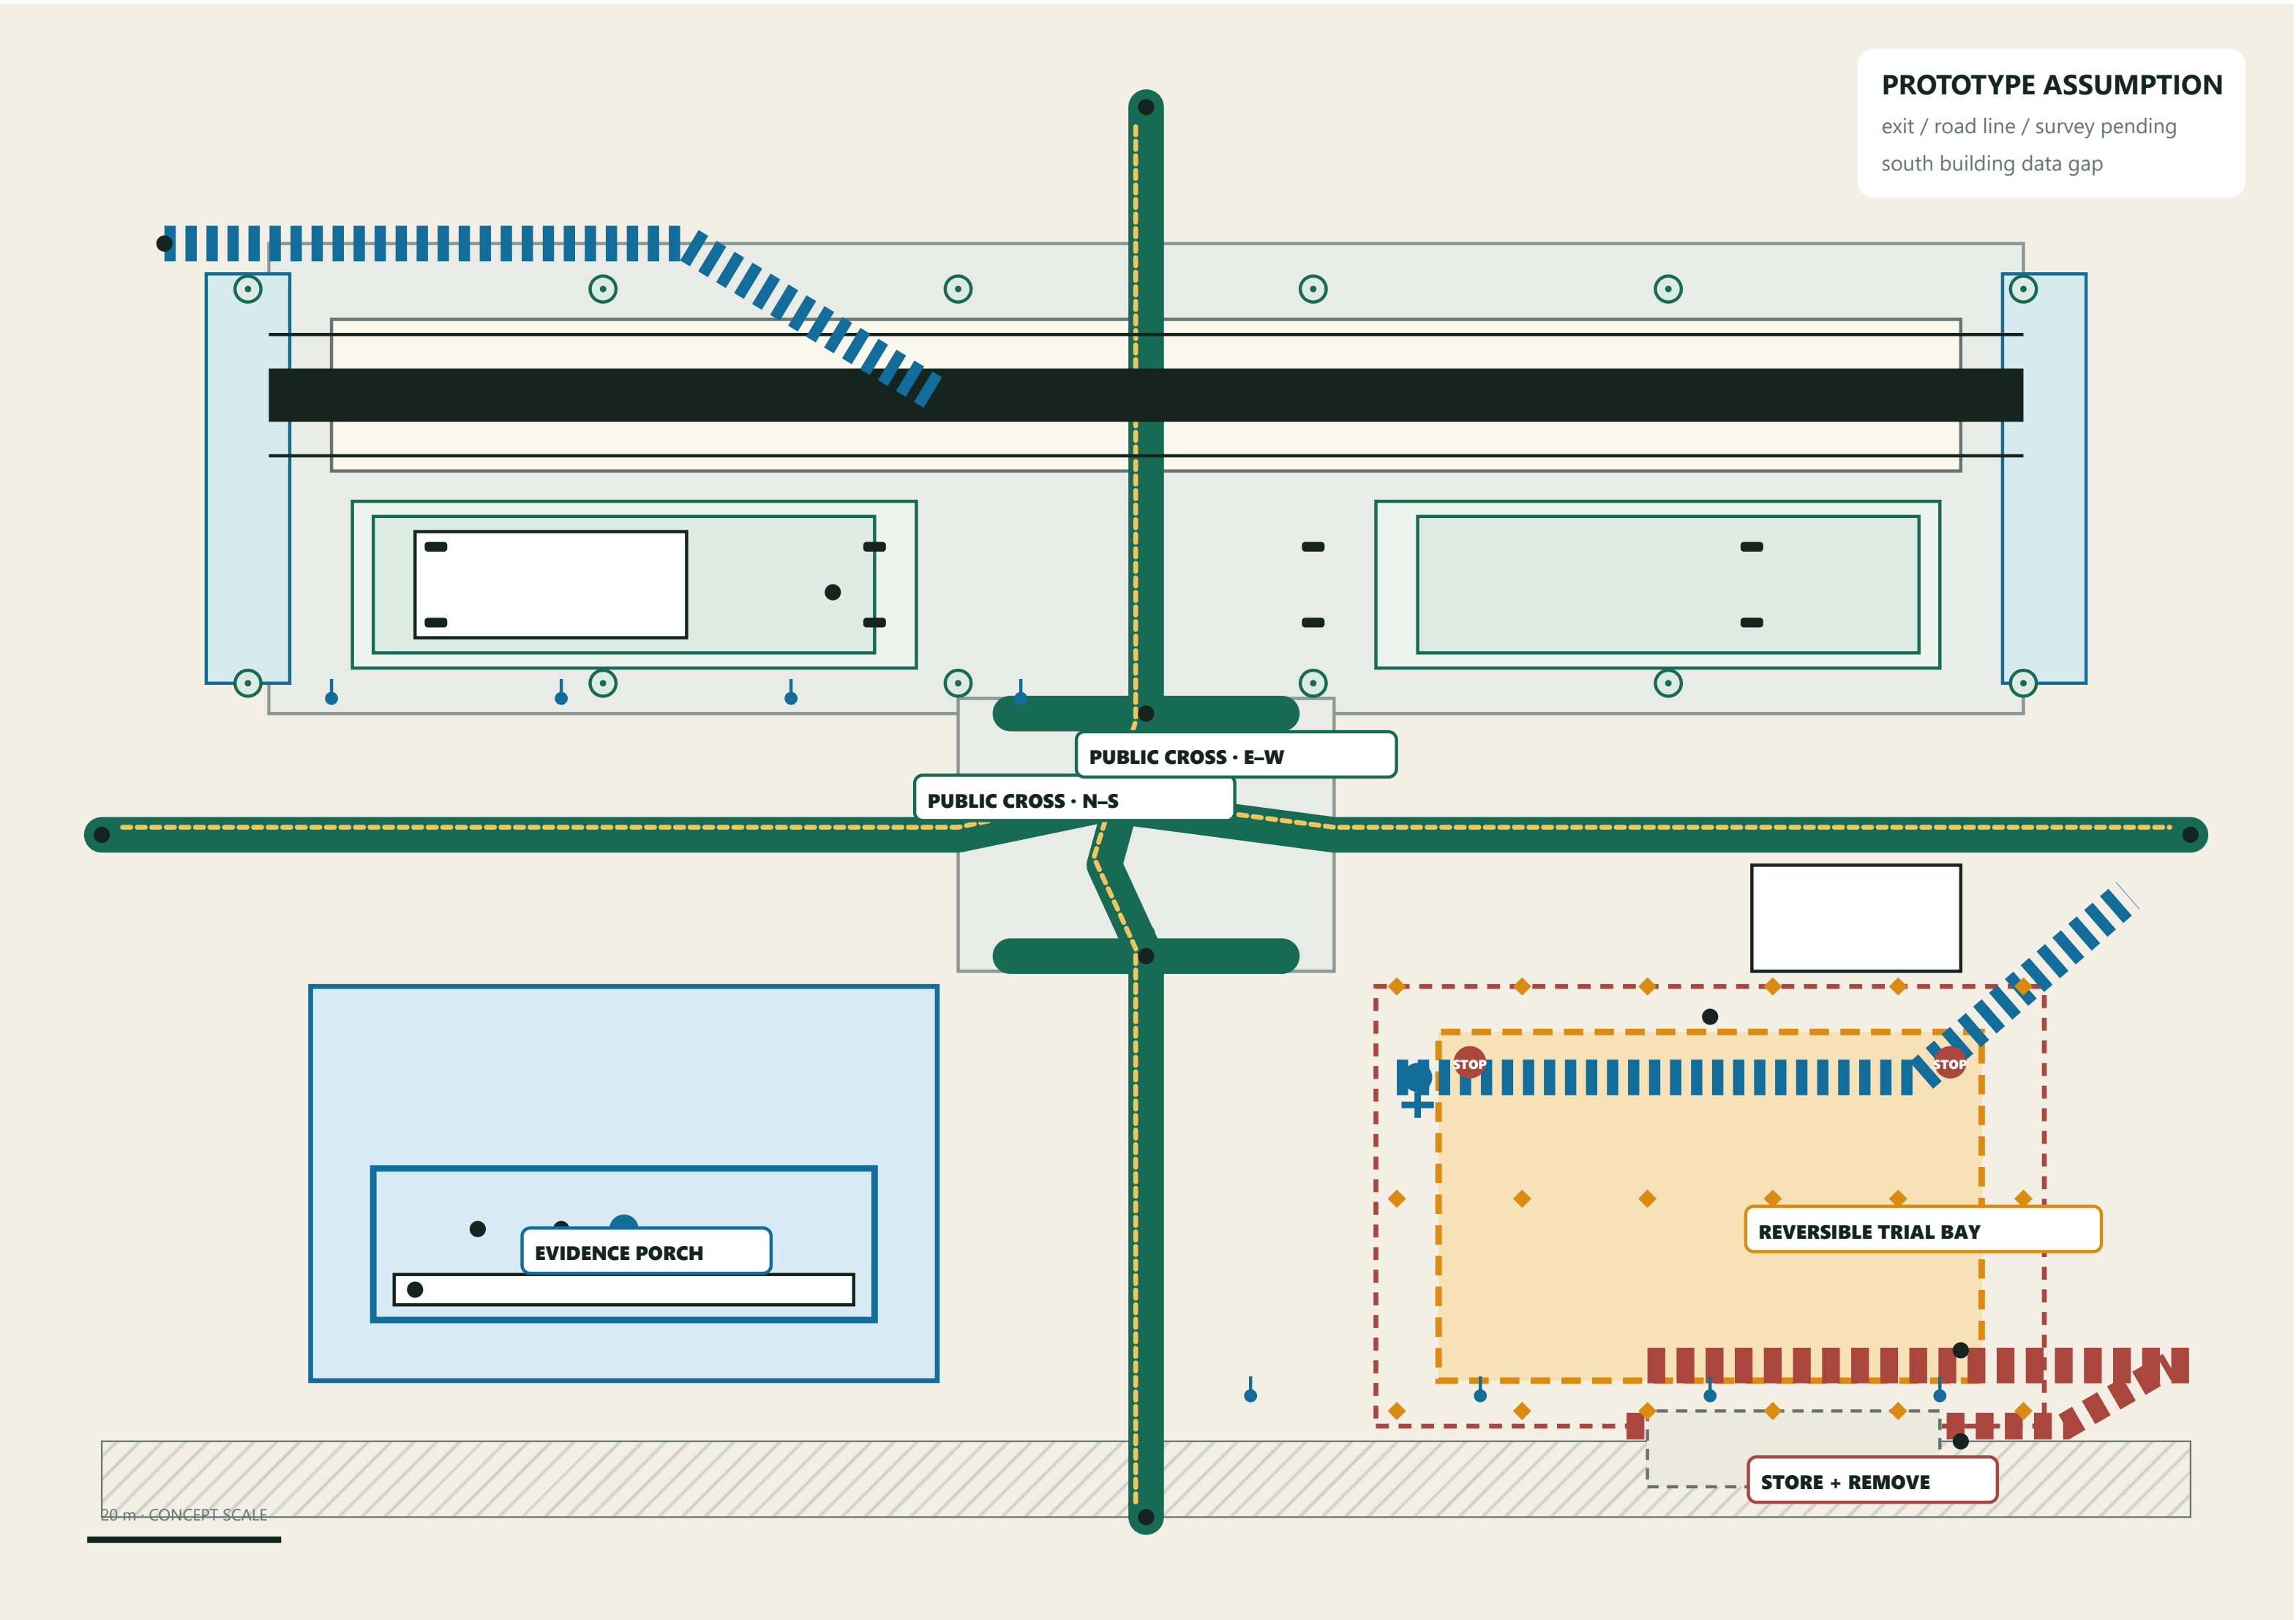

T2 • VERIFICATION RING

Complete bypass around controlled ring

E1 • survey + permits pending

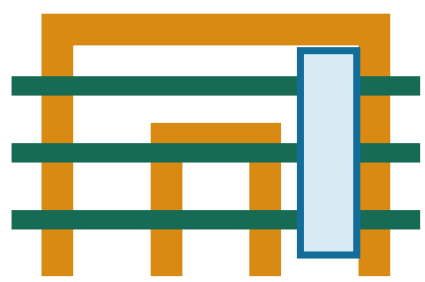


S2 • TRANSLATION GATE


Three passages + human review

E1 • ground-floor fit pending

1:200 SECTION • THE TRIAL NEVER CAPTURES THE PUBLIC ROUTE

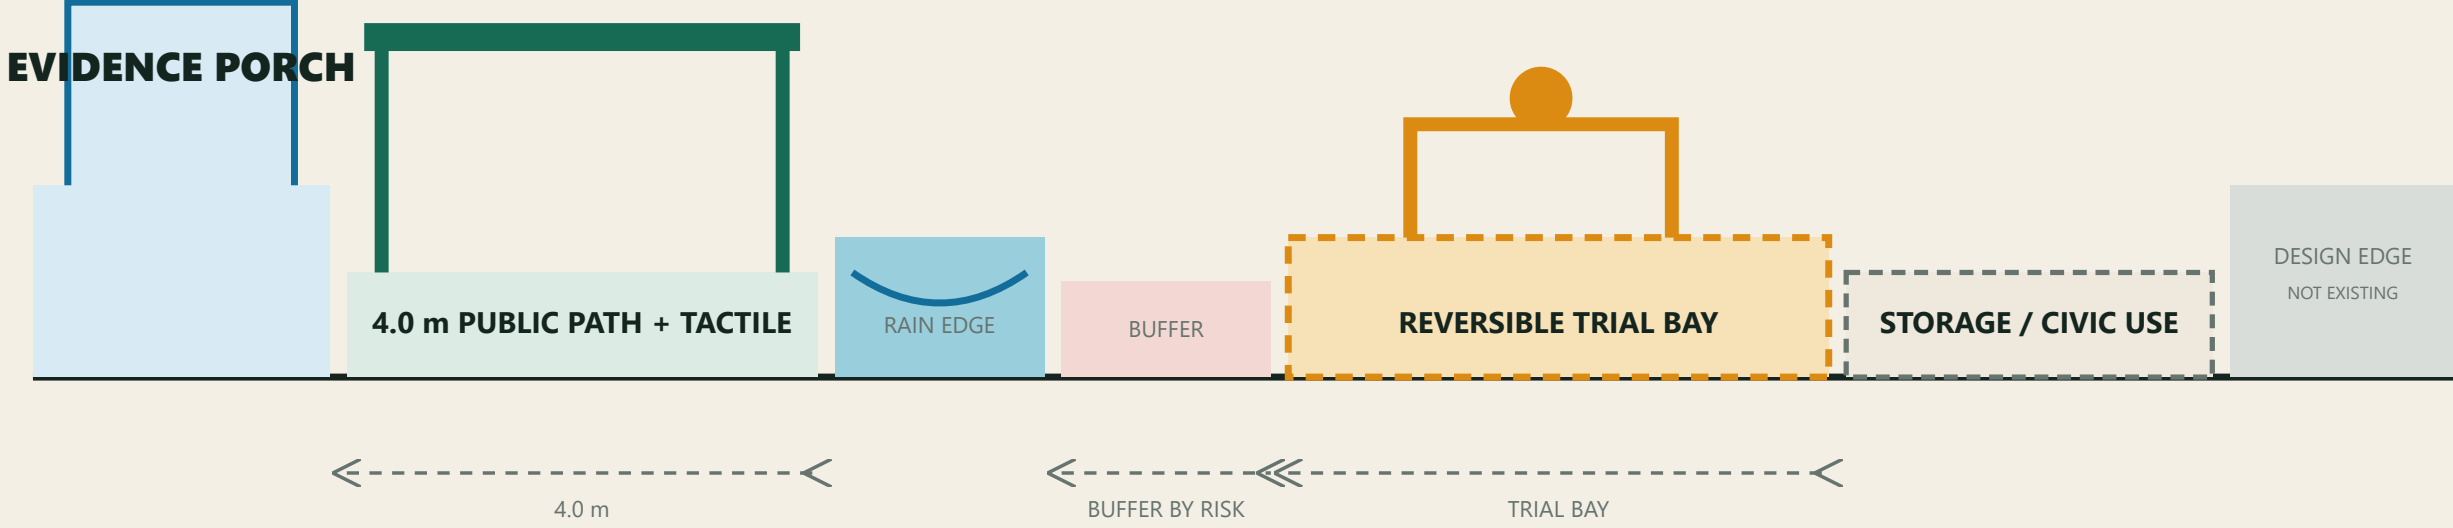

ASSEMBLY AXON • ROUTE, BAY, PORCH, BLUE-GREEN EDGE

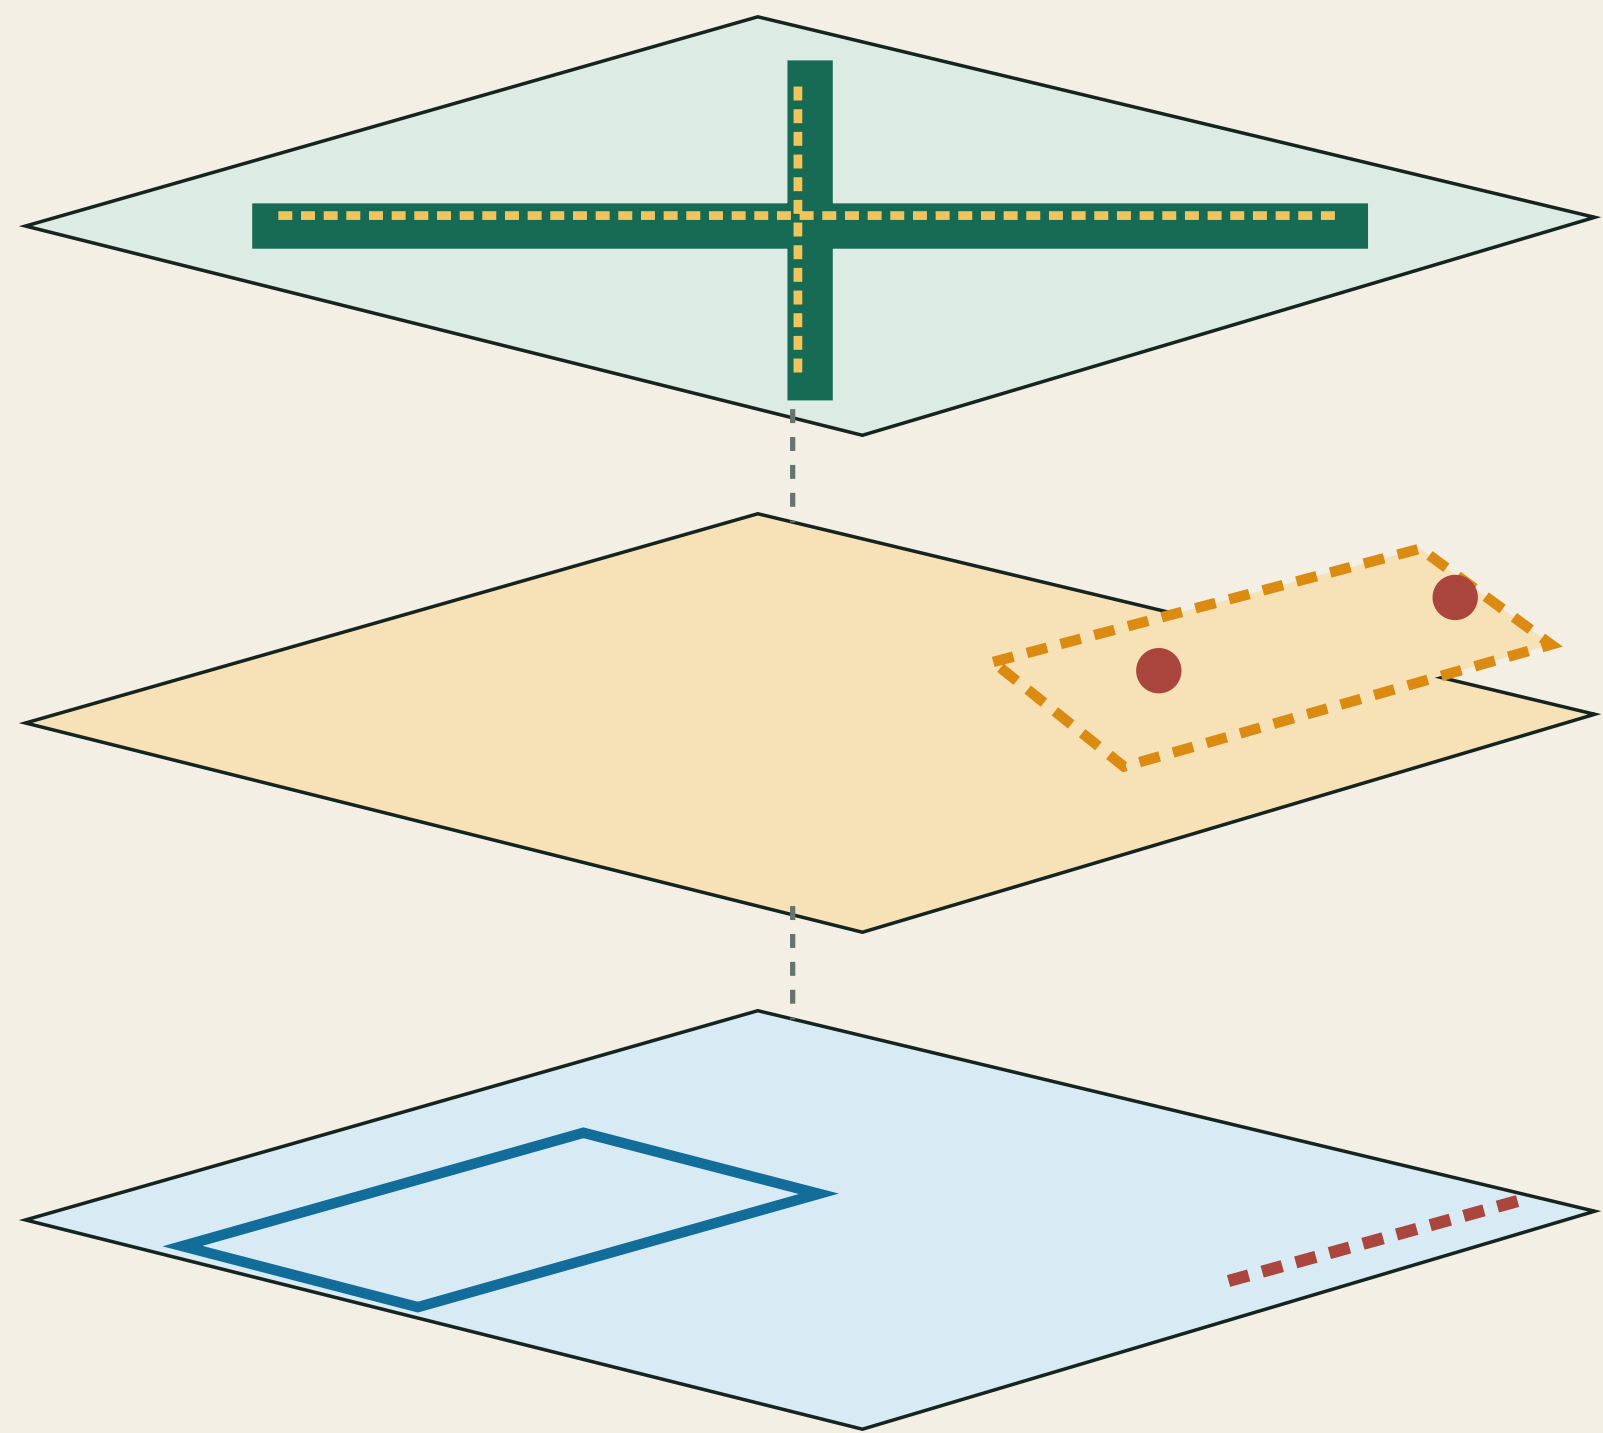

01 PERMANENT BASELINE

cross, tactile, ramps, shade, rain



02 REVERSIBLE AI TRIAL

separate bay, barriers, control, two E-stops

03 PUBLIC EVIDENCE + EXIT

staffed porch, status, appeal, storage and restoration

Reviewable prototype proposal; quantities calculated, formal unit and total prices pending quotation.

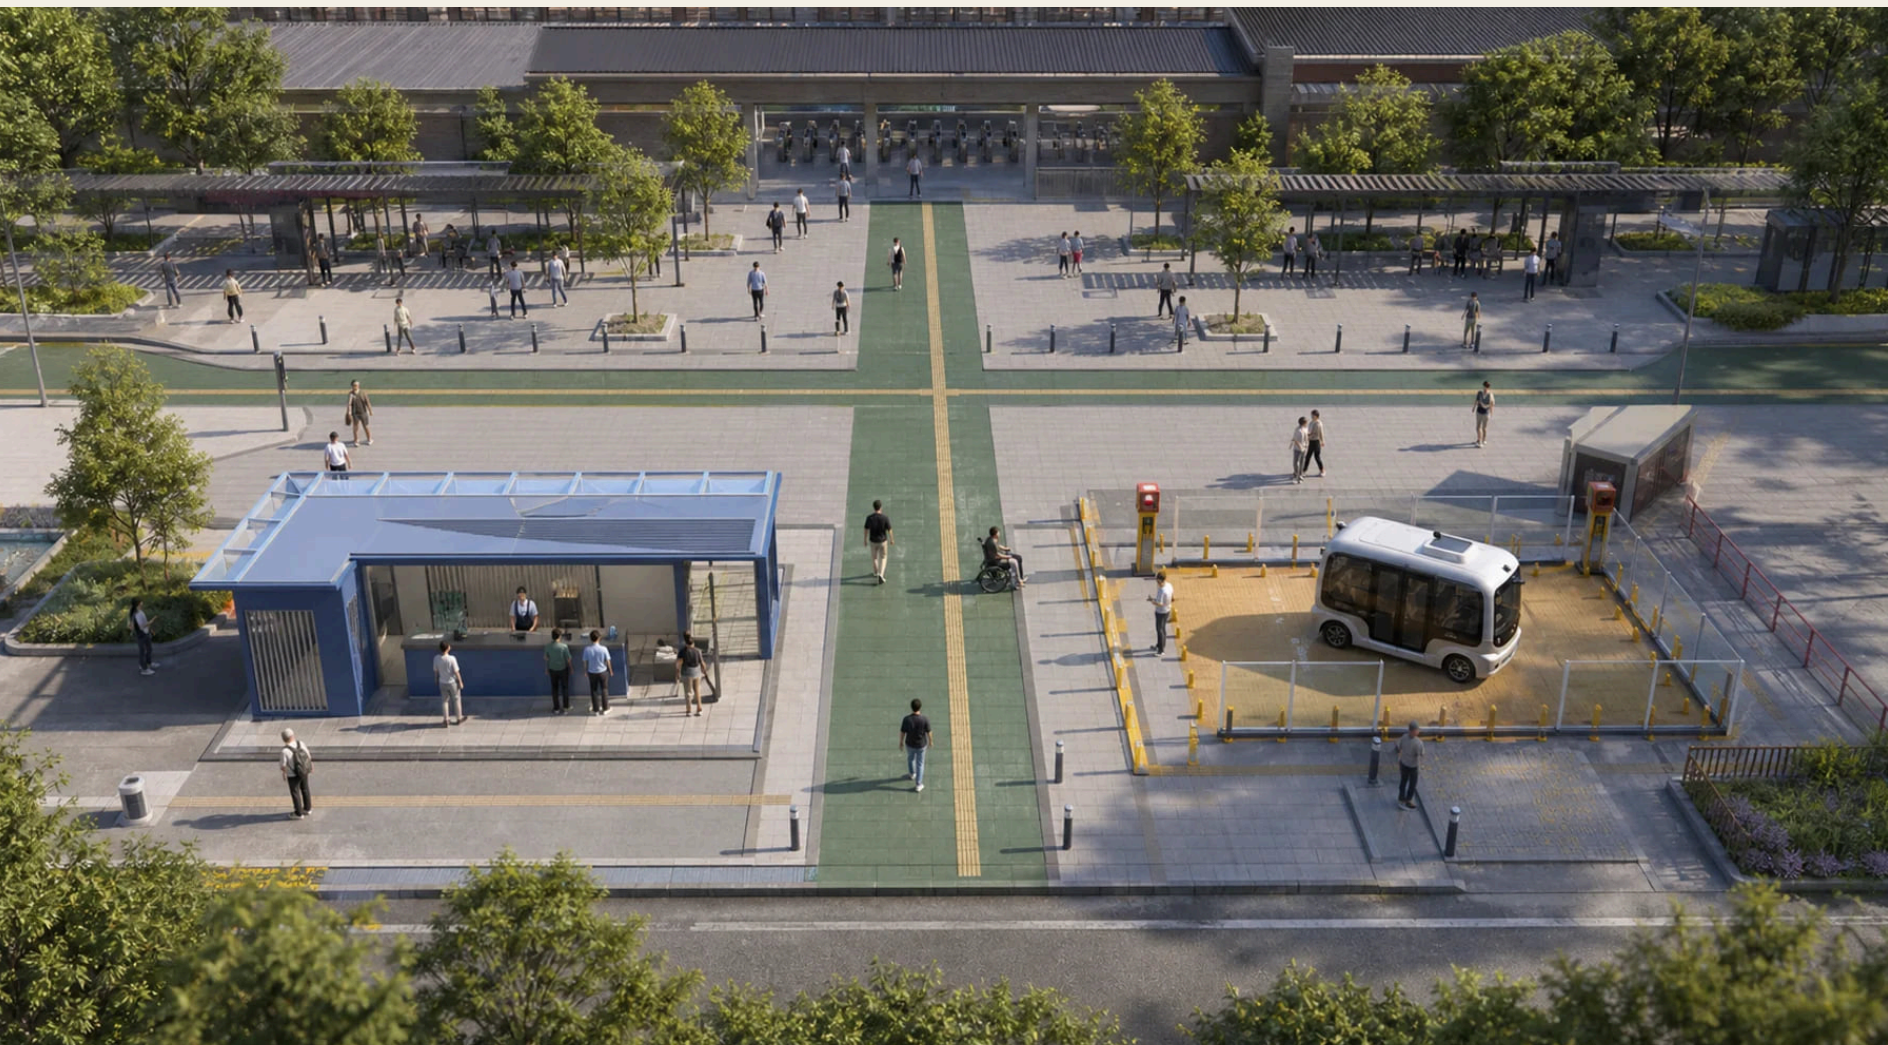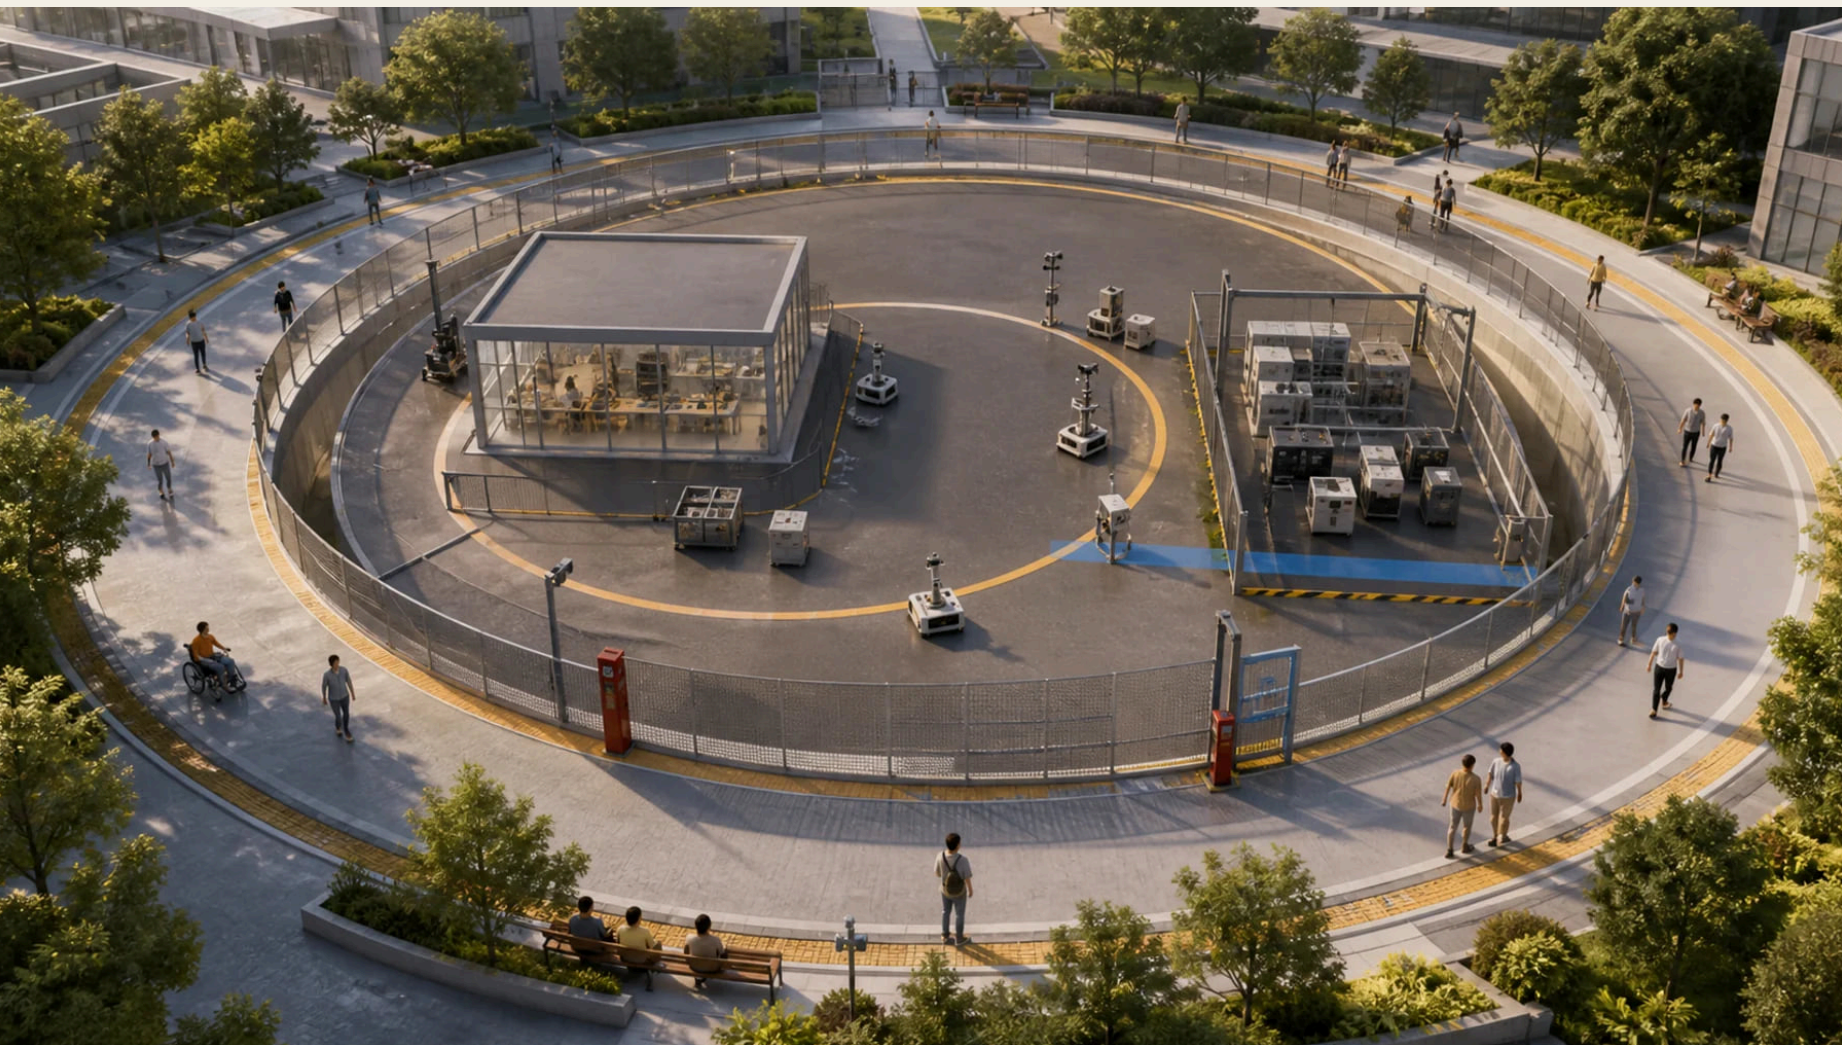

OPEN → TRIAL → PAUSE → RETIRE

both public routes remain open in all states

bay, E-stops and removal stay on one side

experience views are concept images / not site evidence

E2 PROTOTYPE READINESS • PERMITS, KIT, FORMS, ROLES + EXIT

E2 PROTOTYPE READINESS • PERMITS, QUANTITIES, FORMS, ROLES + RECEIPT

01 • EIGHT PERMIT GATES

Written site-use and asset-owner consent	PENDING
Ownership, boundary and existing-condition survey	PENDING
Fire access, egress apron and temporary-structure review	PENDING
Audit of accessible routes, ramps, tactile guidance and staffed service	PENDING
Temporary power, protection and isolation responsibility	PENDING
Isolated network, data minimisation and log-retention rule	PENDING
Conventional-interchange priority, operating window and traffic approval	PENDING
Equipment safety, insurance, emergency stop and supplier removal duty	PENDING

02 • REPRODUCIBLE KIT / QUOTE PENDING

KIT-PAV-01	Permeable paving	920 sqm
KIT-ACC-01	Continuous tactile guidance	168 linear_m
KIT-ACC-02	Accessible ramps	4 unit
KIT-BGR-01	Rain gardens	240 sqm
KIT-SHA-01	Shade bays	6 bay
KIT-FUR-01	Public benches	12 unit
KIT-WAT-01	Drinking-water points	2 unit
KIT-LGT-01	Low-level lighting	16 unit
KIT-SAF-01	Removable barriers	48 module
KIT-SAF-02	Dual emergency-stop posts	2 unit
TOTAL = DESIGN QUANTITY × PENDING MARKET QUOTE		

03 • FIVE BLANK FORMS

FORM-BASELINE

Baseline service log

date_time · weather · user_profile_optional · task_attempt

FORM-TRIAL

Controlled trial log

permit_gate_complete · four_posts_present · trial_start · trial_end

FORM-INCIDENT

Incident and stop-event form

event_time · trigger · stop_authority · equipment_isolated

FORM-RECOVERY

Recovery drill and space-restoration form

clock_start · ordinary_task_completed · north_south_route_open · east_west_route_open

FORM-RECEIPT

Civic adoption receipt

task · same_users · ordinary_baseline · ai_increment

E2 = DOCUMENTED READINESS

NOT PERMITTED • NOT BUILT

NOT FIELD-RUN

04 • CIVIC ADOPTION RECEIPT

S7 / SCN-010 • TEMPLATE ONLY

TASK

S7 SAME-TASK INTERCHANGE

BASELINE

public cross + interchange + staff

AI INCREMENT

southeast timed reversible bay

DENOMINATOR

100 eligible passages / mode

ZERO TOLERANCE

collision / intrusion / E-stop / route loss

RACI

01 • asset / site

02 • baseline service

03 • safety (independent)

04 • data recorder


05 • public representative

ADOPT


REVISE

STOP

ONE OPERATING DAY • SIX STEPS CONNECT SPACE, OWNER + EXIT

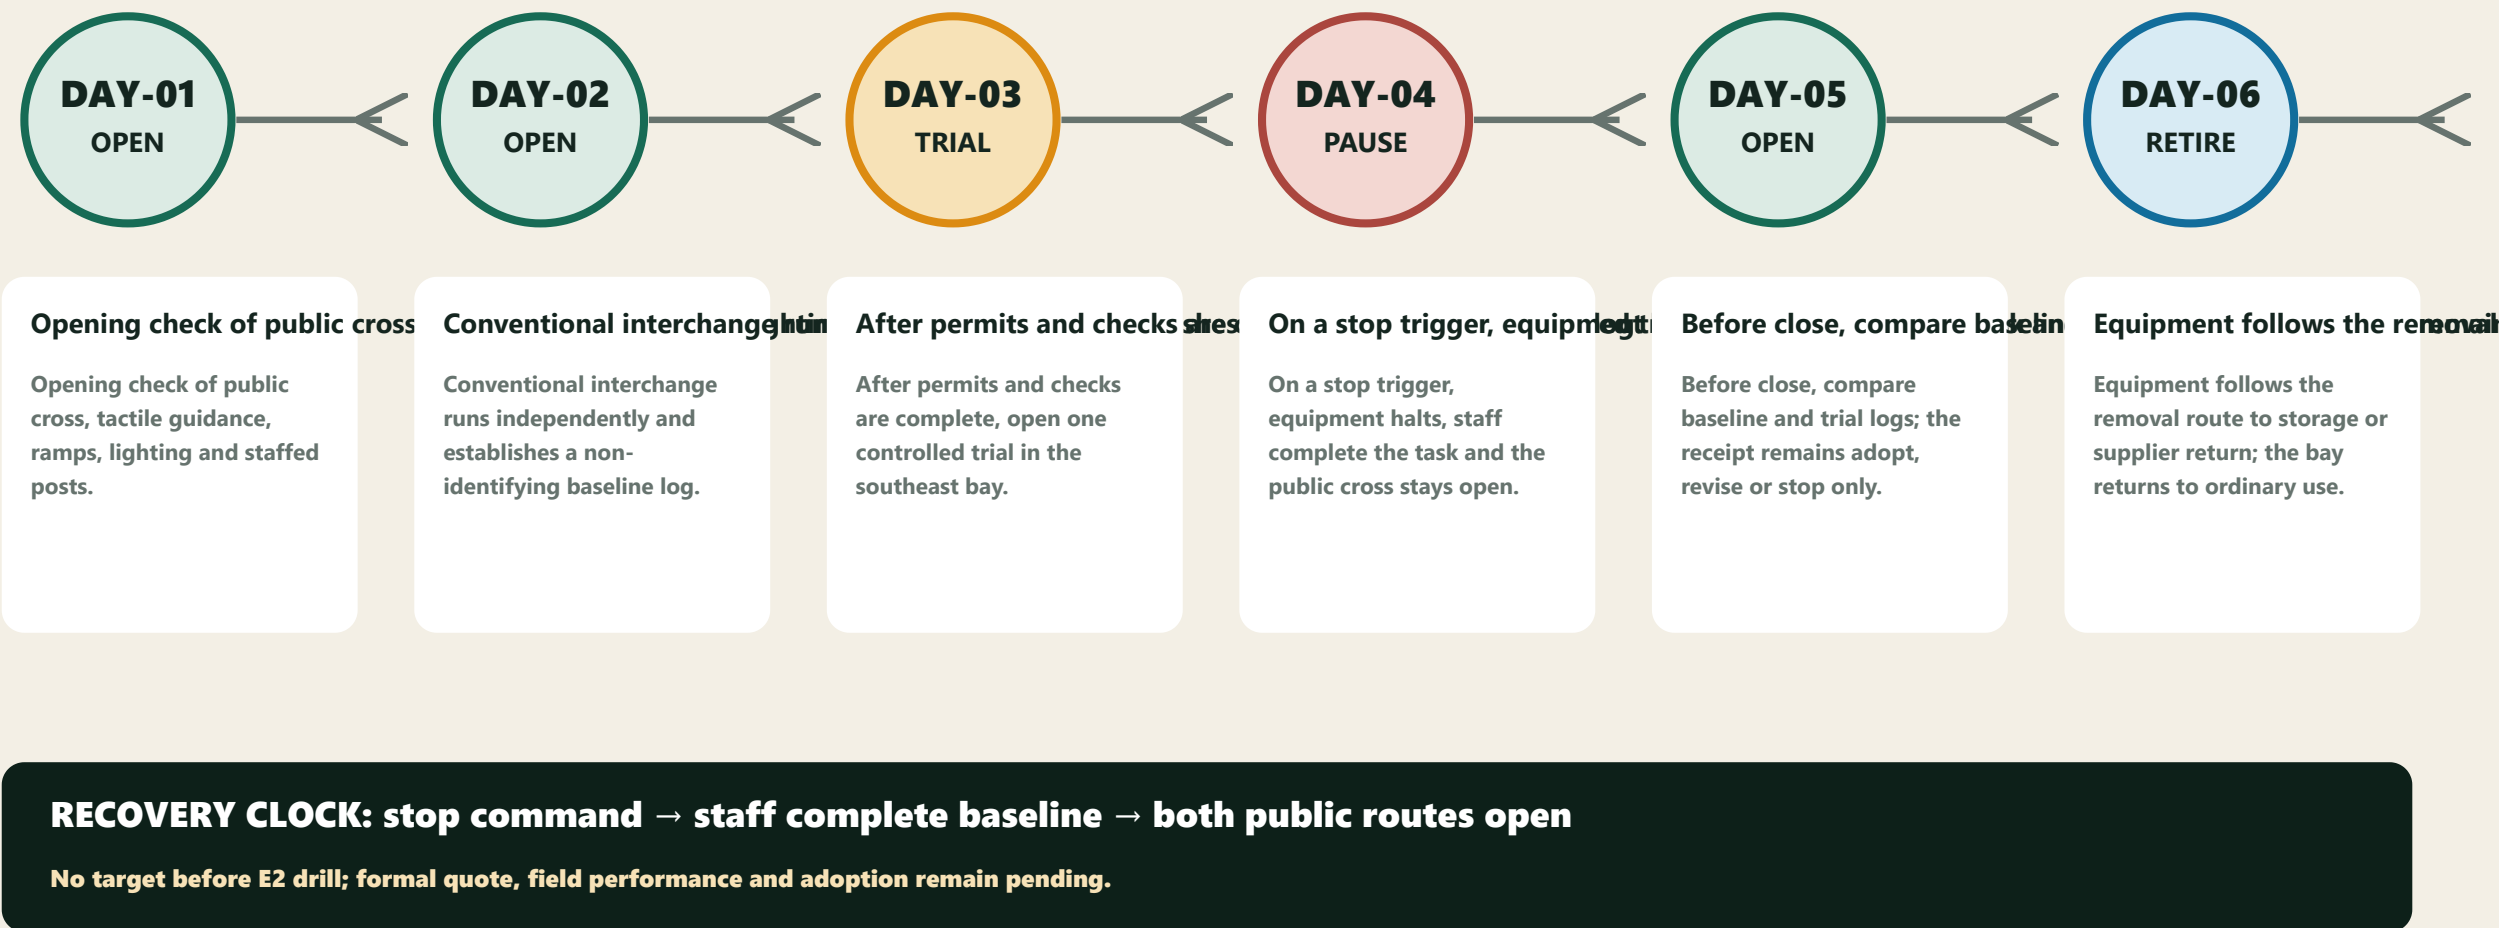

PUBLIC PROBLEM TO KNOWLEDGE ASSET • INPUT, OWNER + FAILURE EXIT AT EVERY STEP

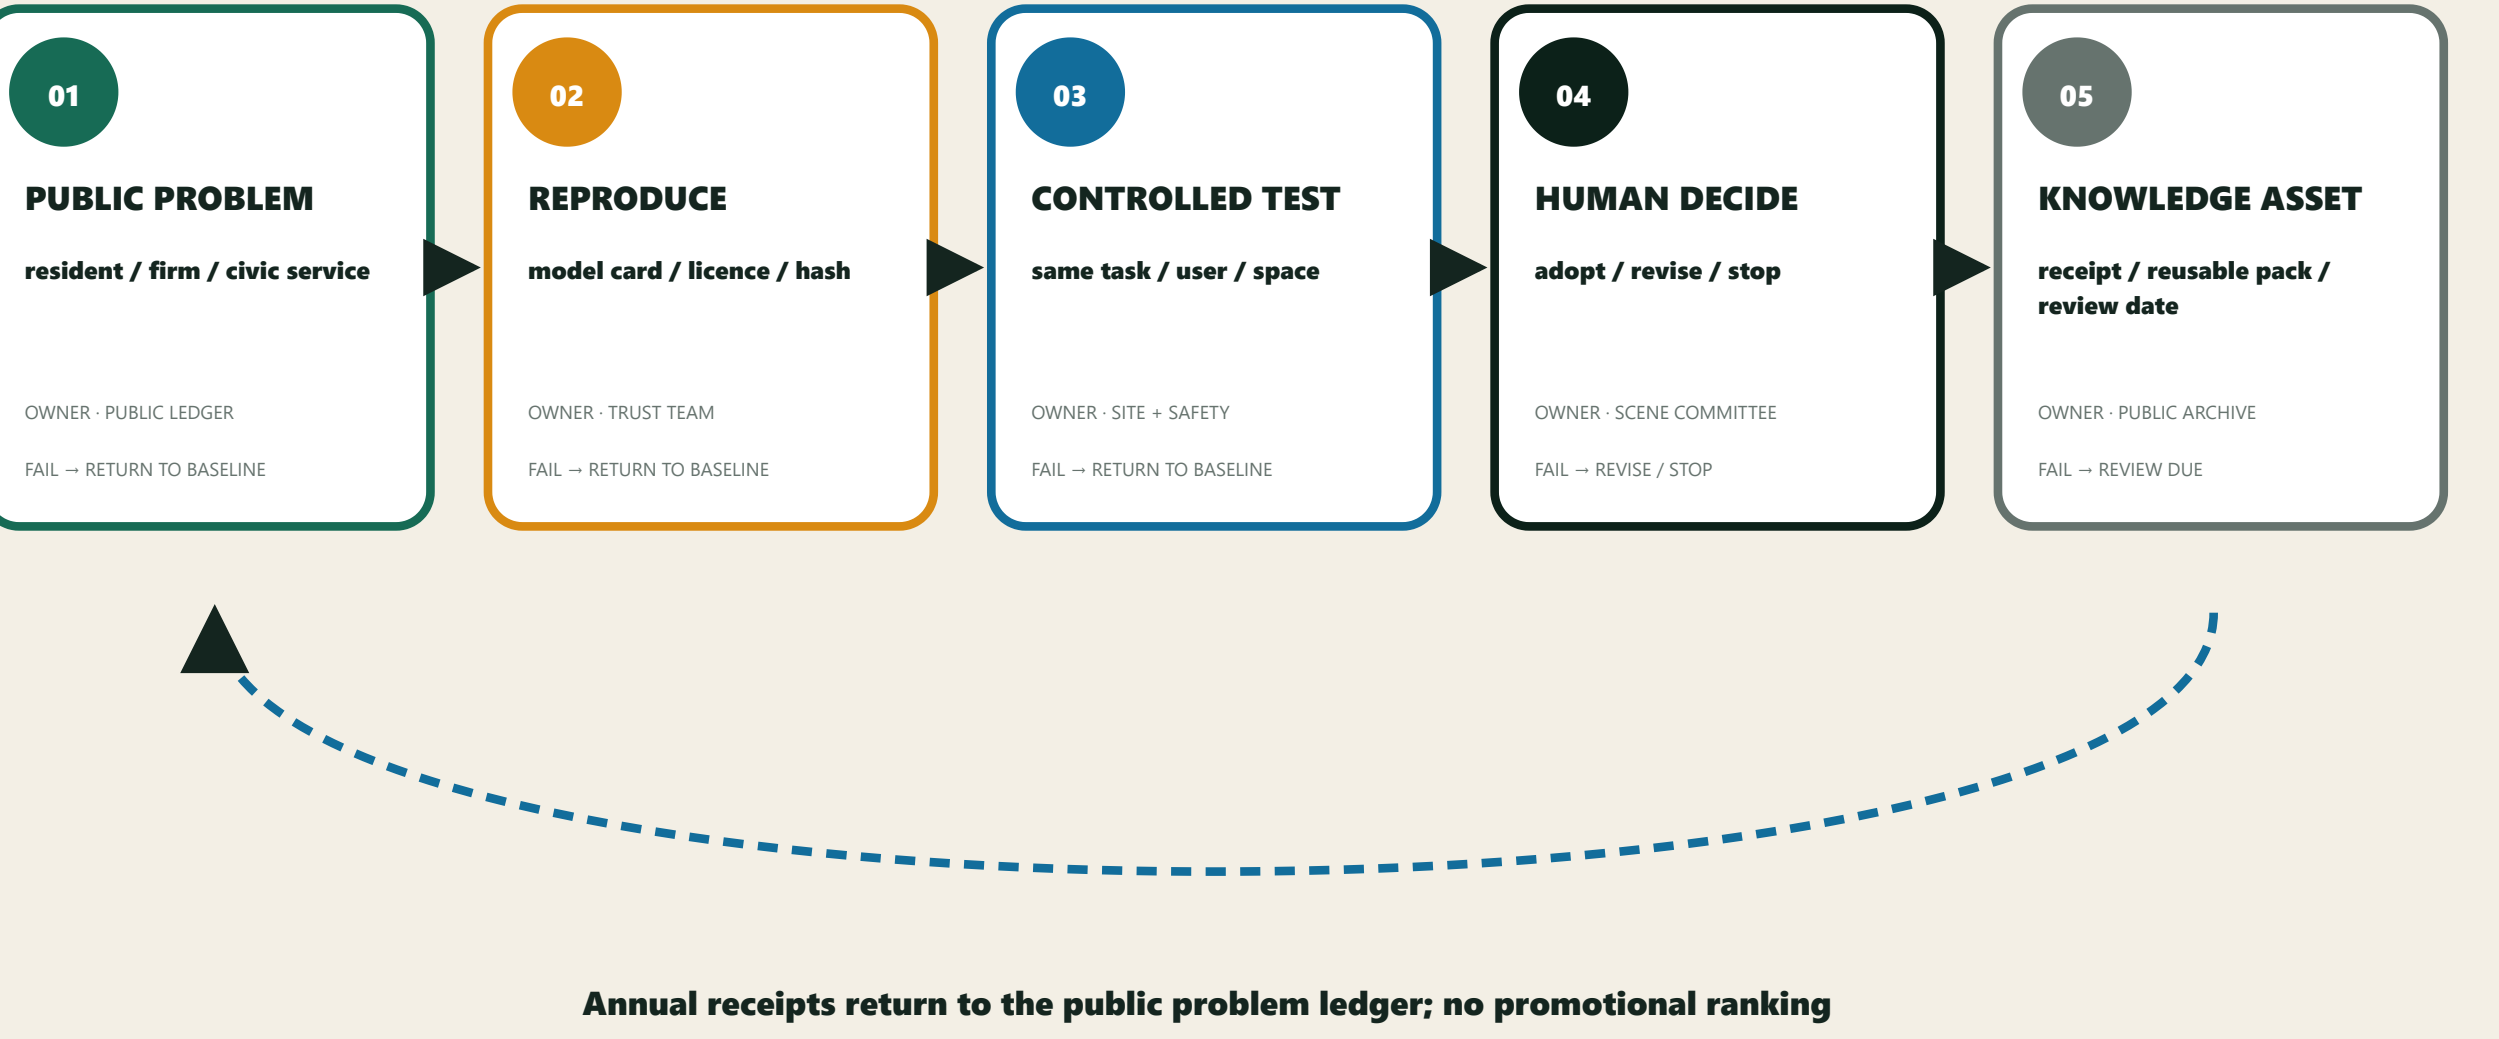

E2 = DOCUMENTED READINESS

not permitted • not built • not field-run

ADOPT • REVISE • STOP

every failed gate returns to the complete baseline