



PLACEMENT SCREEN / 1:500 AT FULL-SIZE A0

OSM MORPHOLOGY—NOT PARCEL, REDLINE, VACANCY OR BUILDABILITY EVIDENCE

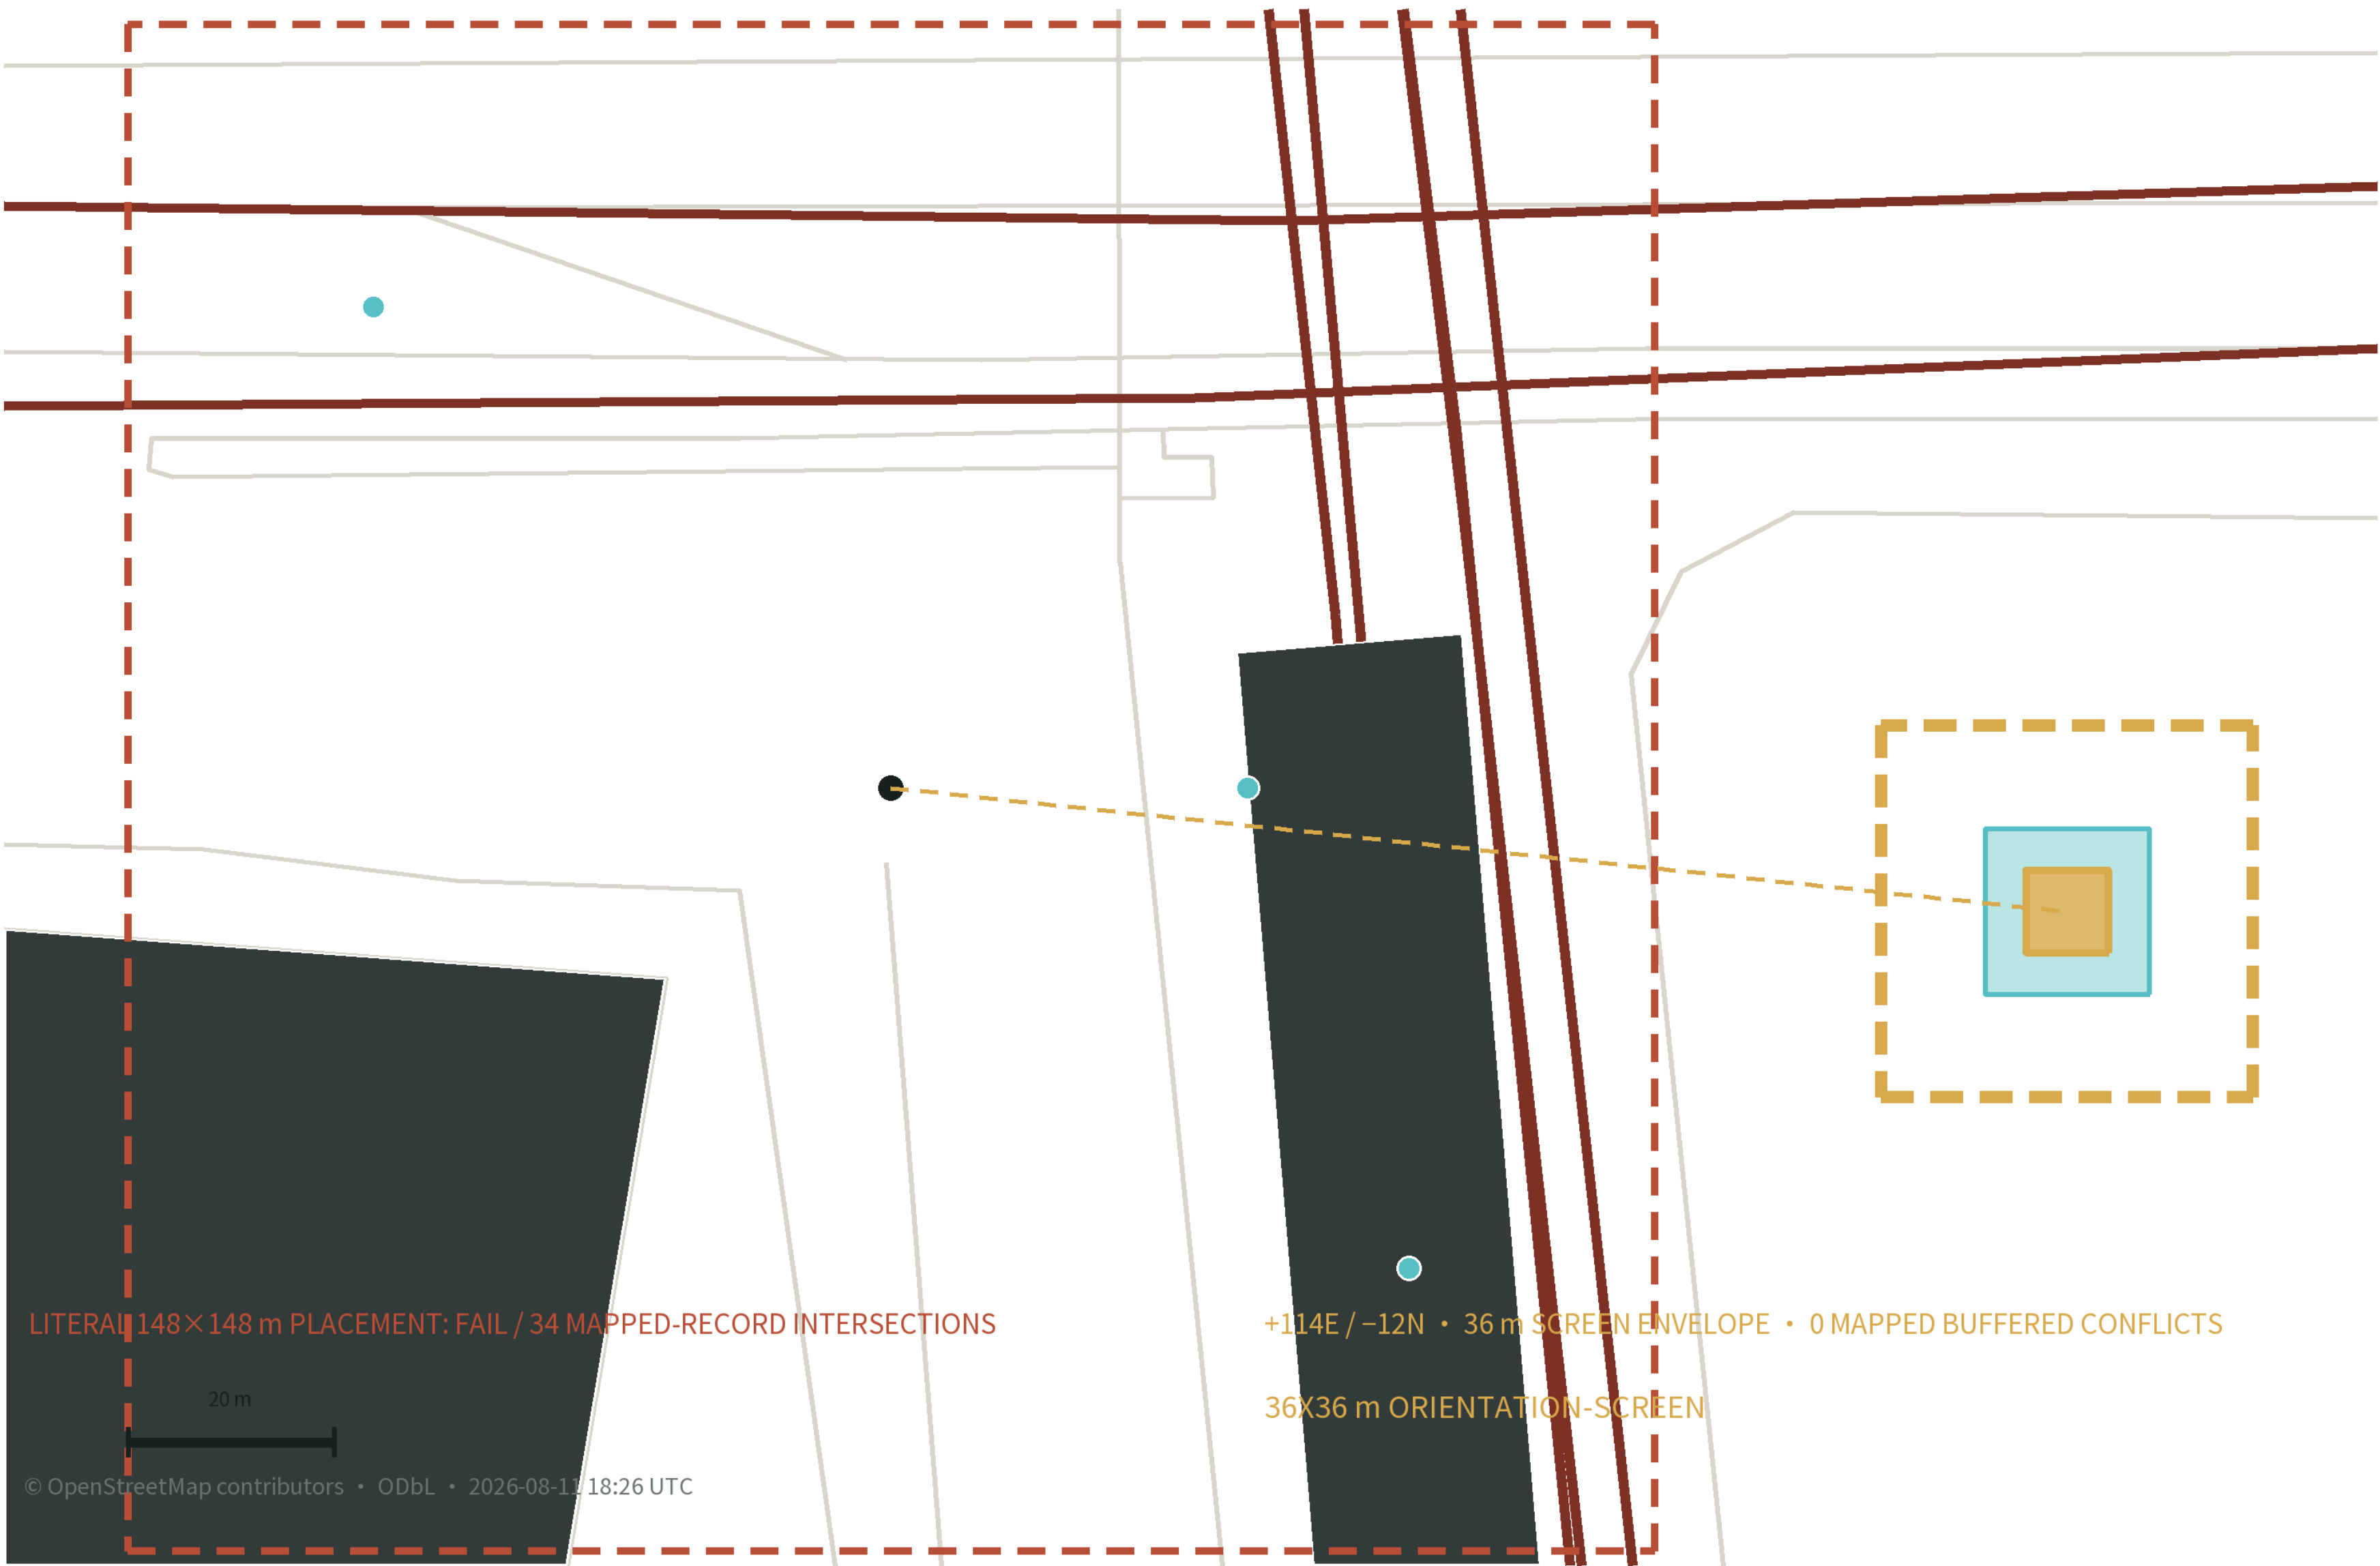


P0 PLAN / 1:100 AT FULL-SIZE A0

ONE 8 m SUPPORT BAY WITHIN 16 m REVERSIBLE GROUND

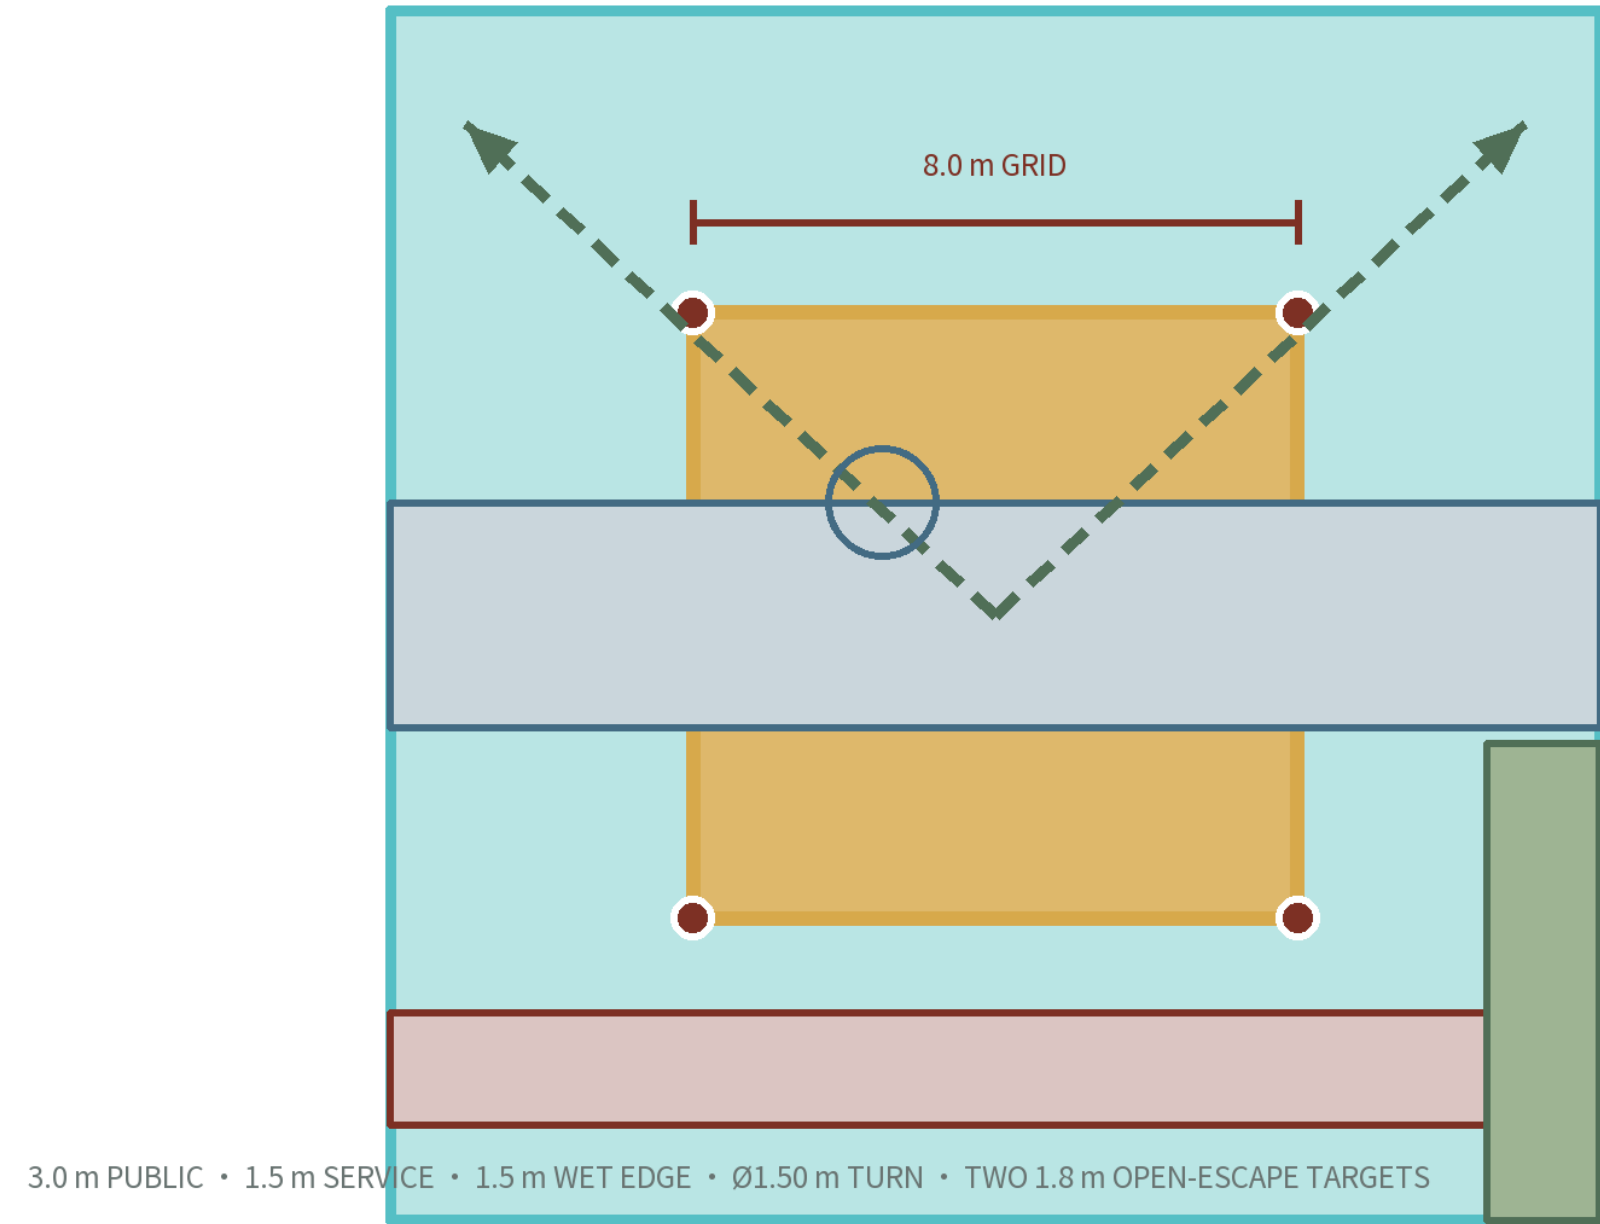

INHABITED SECTION / 1:200 AT FULL-SIZE A0


OPEN CANOPY: NO COOKING / TRACTION-BATTERY CHARGING; FIRE + OCCUPANT LOAD TBC

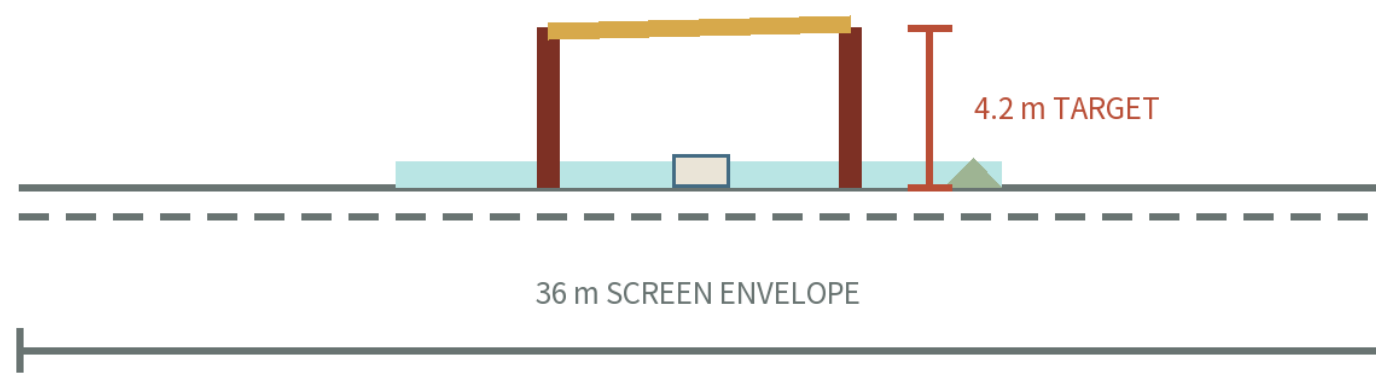

EAVE-WATER-SERVICE INTERFACE / 1:20 AT FULL-SIZE A0

CLEAR GEOMETRY TO SCALE; MEMBER + PRODUCT THICKNESSES TBC STRUCTURE/FIRE/MEP


DEMOUNTABLE ROOF CASSETTE / 2% FALL HYPOTHESIS

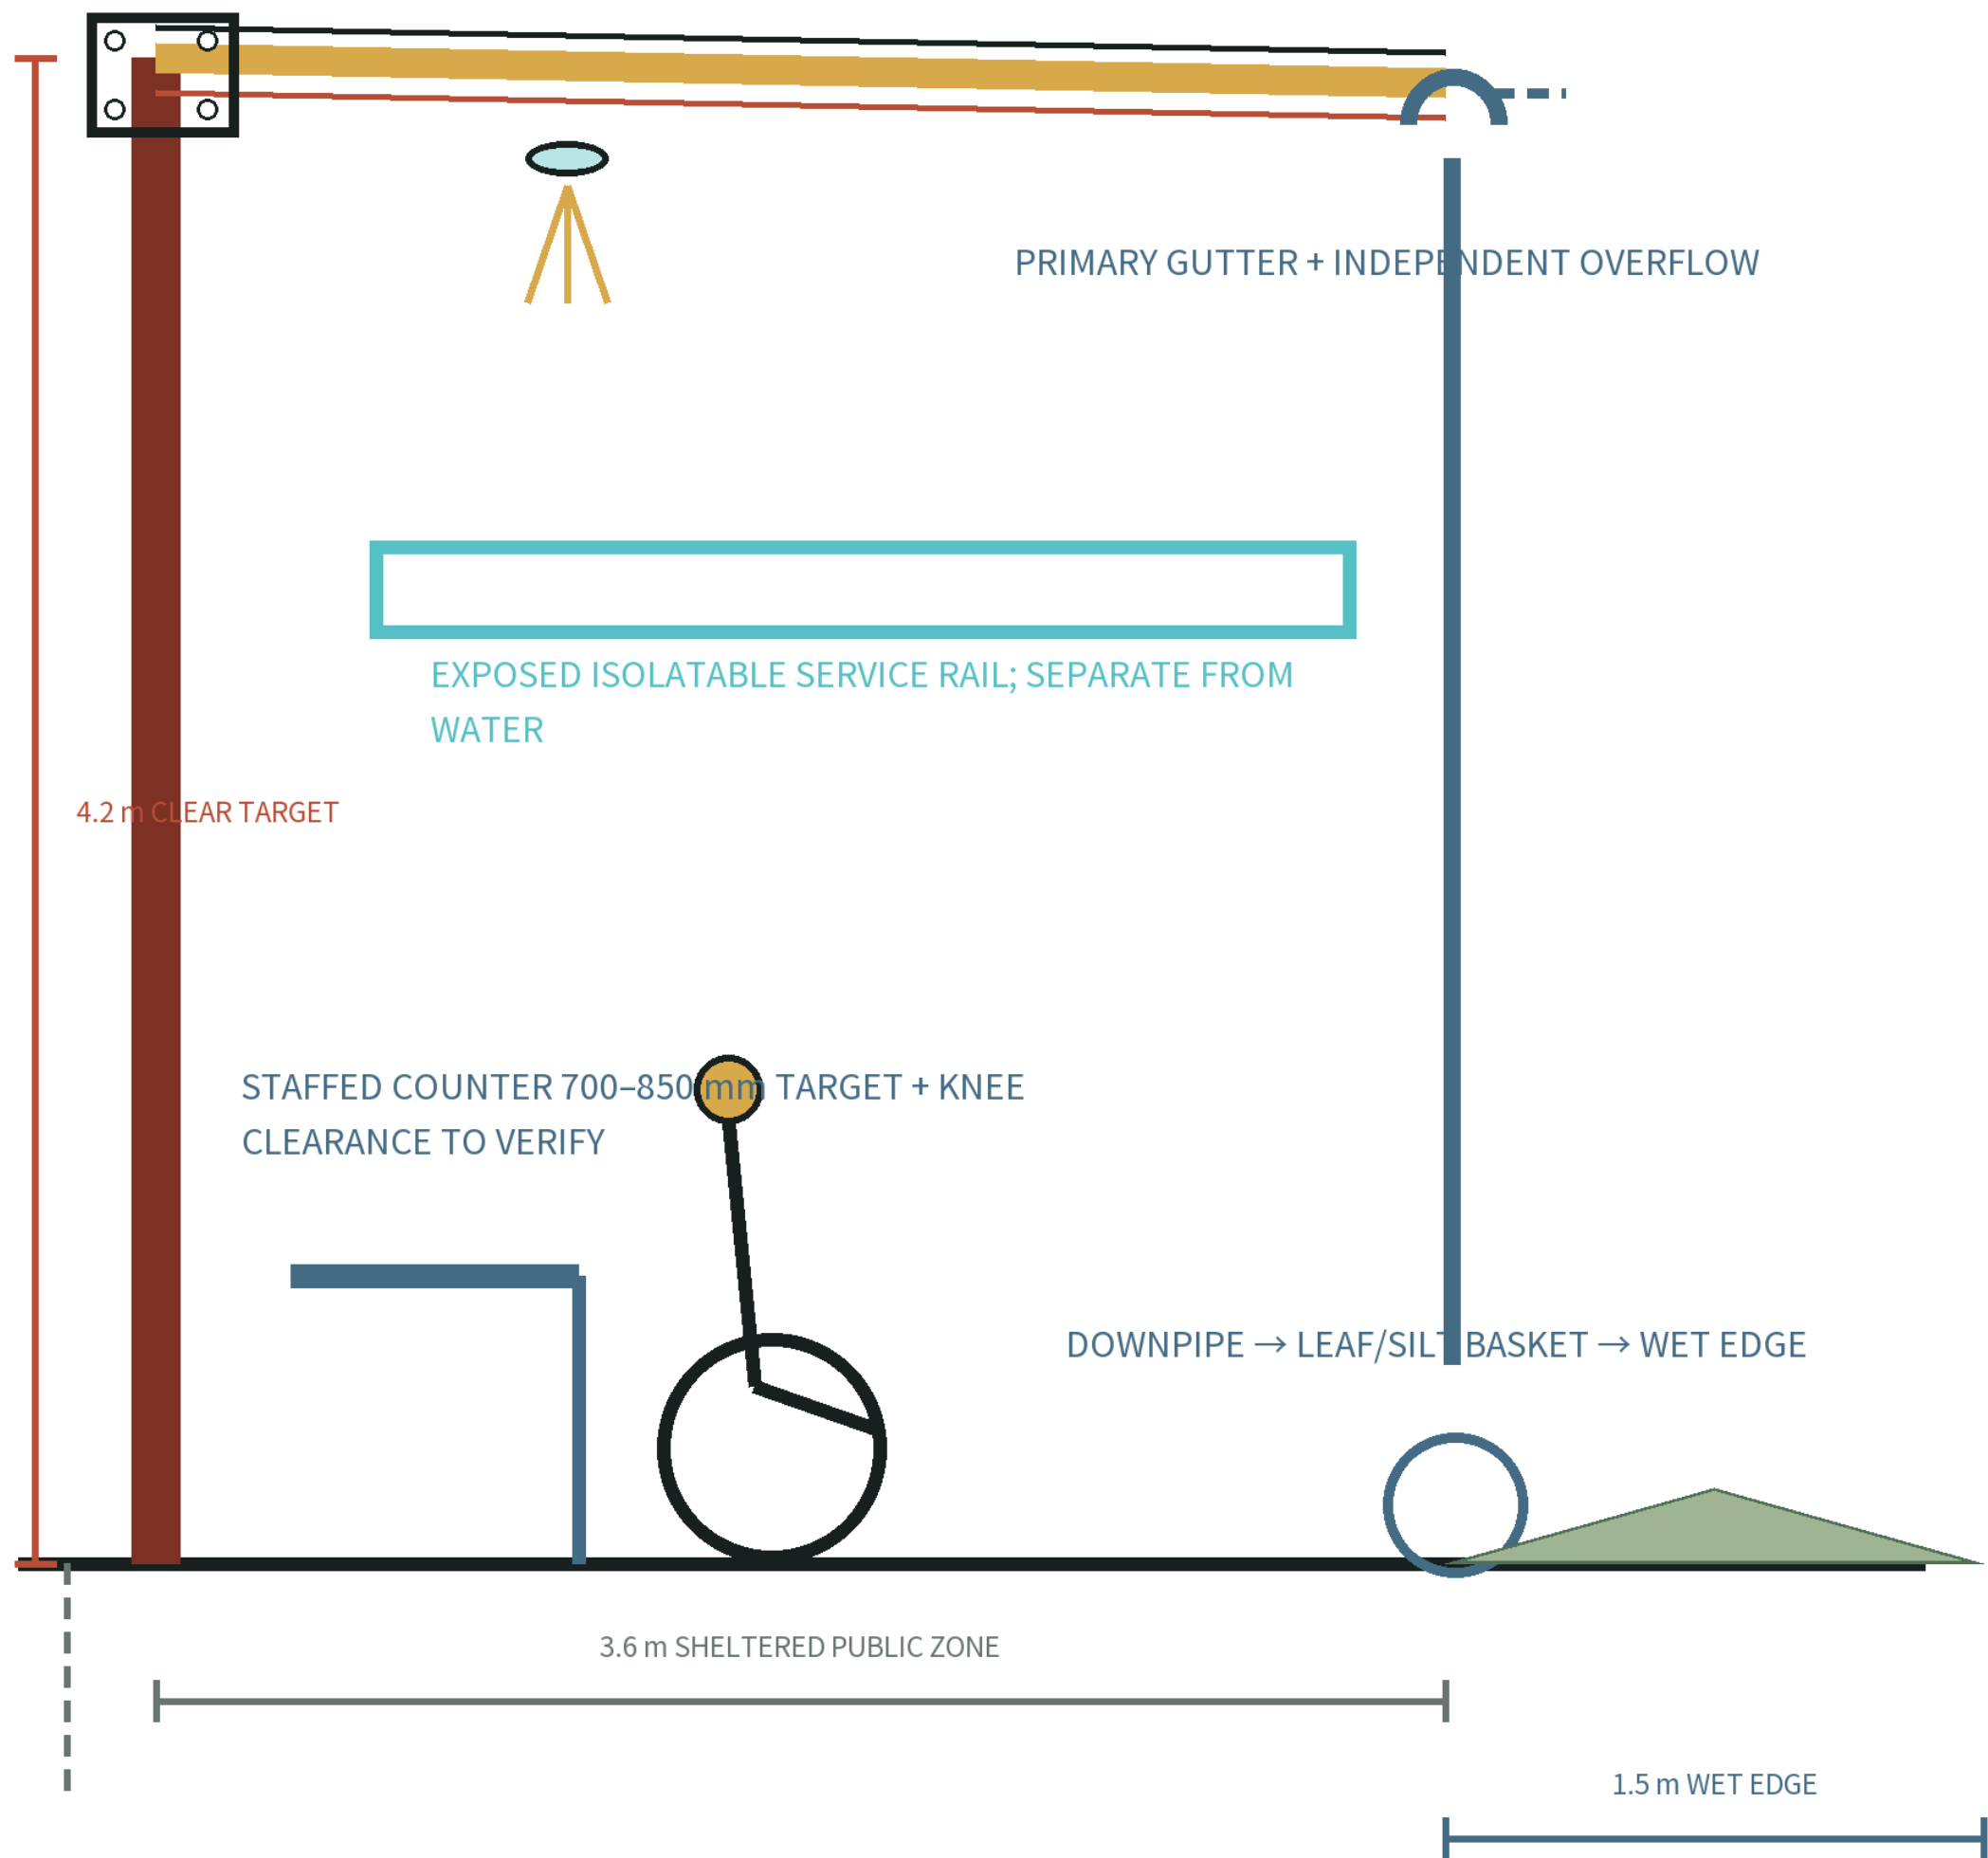

64 m² ROOF × 10 mm RAIN = 0.64 m³; OUTLET/STORAGE/INFILTRATION TBC TOPO, SOIL + MUNICIPAL DRAINAGE.

CONTEXT-BOUND AXON FROM THE SAME GEOMETRY

OSM FOOTPRINTS FLAT • NO HEIGHT, PARCEL OR TITLE EVIDENCE

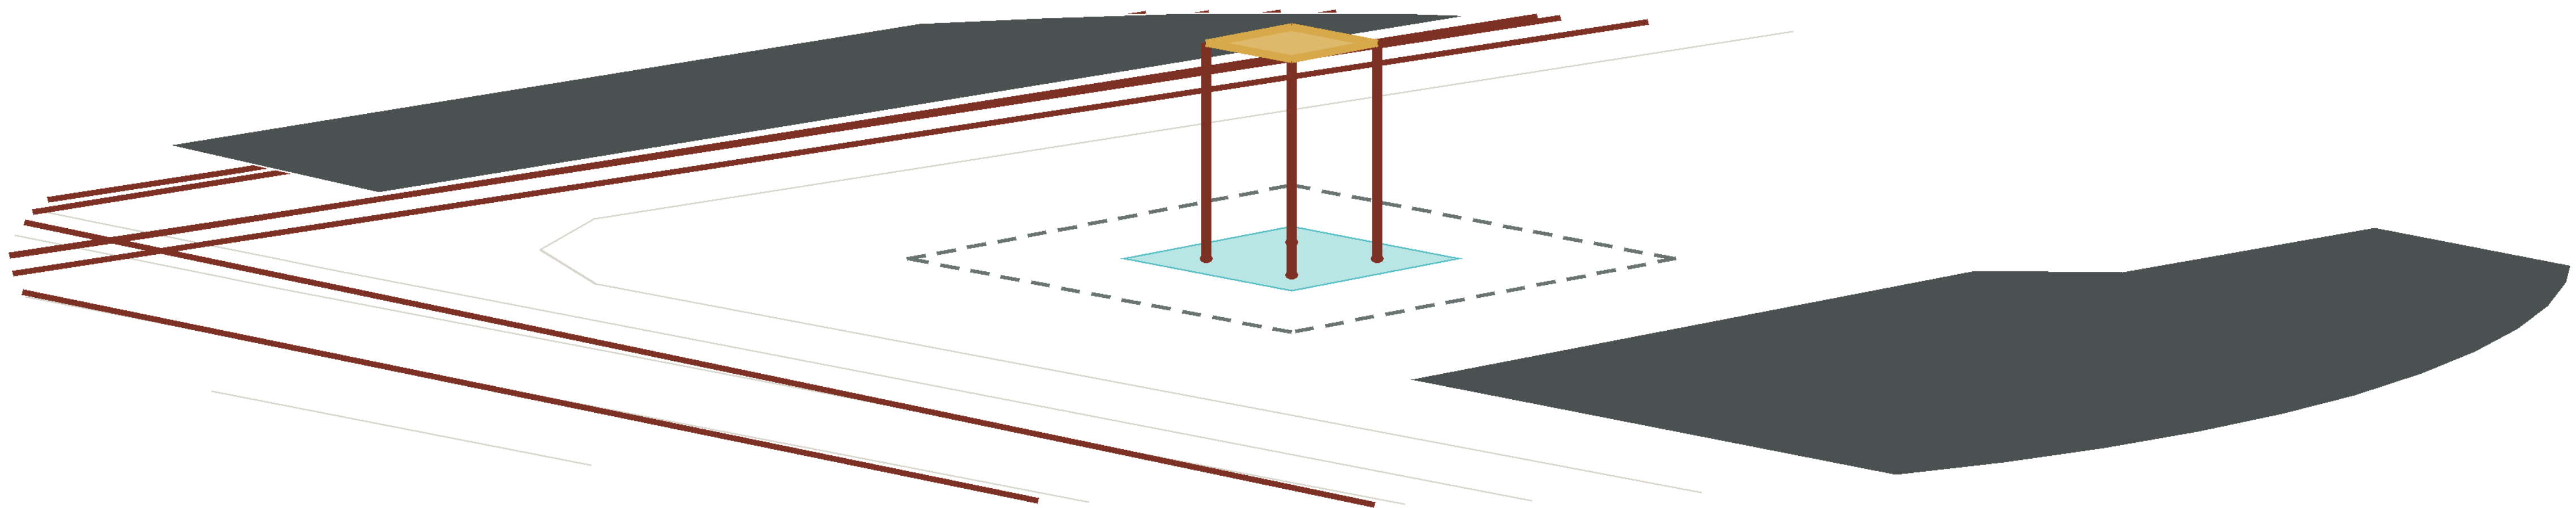

PROPOSED 8×8 m DEMOUNTABLE FIRST BAY

36×36 m IS AN ORIENTATION-SCREEN ENVELOPE ONLY

PERFORMANCE SCHEDULE / PARTICIPANT REFERENCE SPEC

01	BOLTED GALVANISED FRAME • SECTION/GRADE/FIRE TBC	¥1.9–3.8M
		PARTICIPANT ROM / NOT A TENDER PRICE
02	DEMOUNTABLE METAL CASSETTE • WIND/SNOW/CONDENSATION TBC	06:00–24:00 • 5-FTE ROSTER
03	DRY-LAID REPLACEABLE PAVING • SLIP/FROST/PERMEABILITY TBC	OPEX ASSUMPTION ¥1.2–2.2M/Y
04	VISIBLE DRAINAGE + WINTER DRAIN-DOWN; DISCHARGE OUTSIDE CLEAR ROUTE	OPEX ASSUMPTION 1.2–2.2M/Y 06:30 RIDER/CLEANER WATER + REST
05	SURFACE ISOLATABLE SERVICE RAIL • LOAD/METERING/FIRE TBC	12:30 FOOD HANDOFF; NO COOKING 19:00 REPAIR/LEARNING/STAFFED HELP

NO TITLE/REDLINE, NAMED OPERATOR, 12-MONTH OPEX RESERVE, ACCESS AGREEMENT, METRO/UTILITY, FIRE/STRUCTURE/MEP REVIEW + PERMIT: NO BUILD, NO OPEN.

01 / 07 • FROM FALSE PLACEMENT TO FIRST BAY

REAL FIGURE-GROUND REJECTS THE DIRECT 148-METRE PLACEMENT; P0 CONTRACTS TO ONE DEMOUNTABLE 8×8-METRE BAY AND 16×16-METRE REVERSIBLE GROUND, SETTING T00 AS THE DOCUMENTARY PRECONDITION FOR THE T01-T11 / W1-15 CONDITIONAL REFERENCE WINDOW

01 8×8 m / demountable bay

02 T00 / documentary precondition

03 T01-T11 / W1-15 conditional reference

04 12 future role classes / single A

PAIRED BAYS • DIFFERENCE CLOISTER • ONE QUEUE

ONE MECHANISM, THREE CONSTRUCTION AND CIVIC-HANDOFF FORMS; PARAMETRIC PLANS + SECTIONS LOCATE H, REMOVABLE SLOTS AND STOP CONDITIONS


03

ZHONGZHIYUAN • PROOF YARD

Proof Yard

COURT / controlled proof visible to the public


A/B MAY CHANGE OR CLOSE • H BYPASS • HUMAN SERVICE STAY OPEN

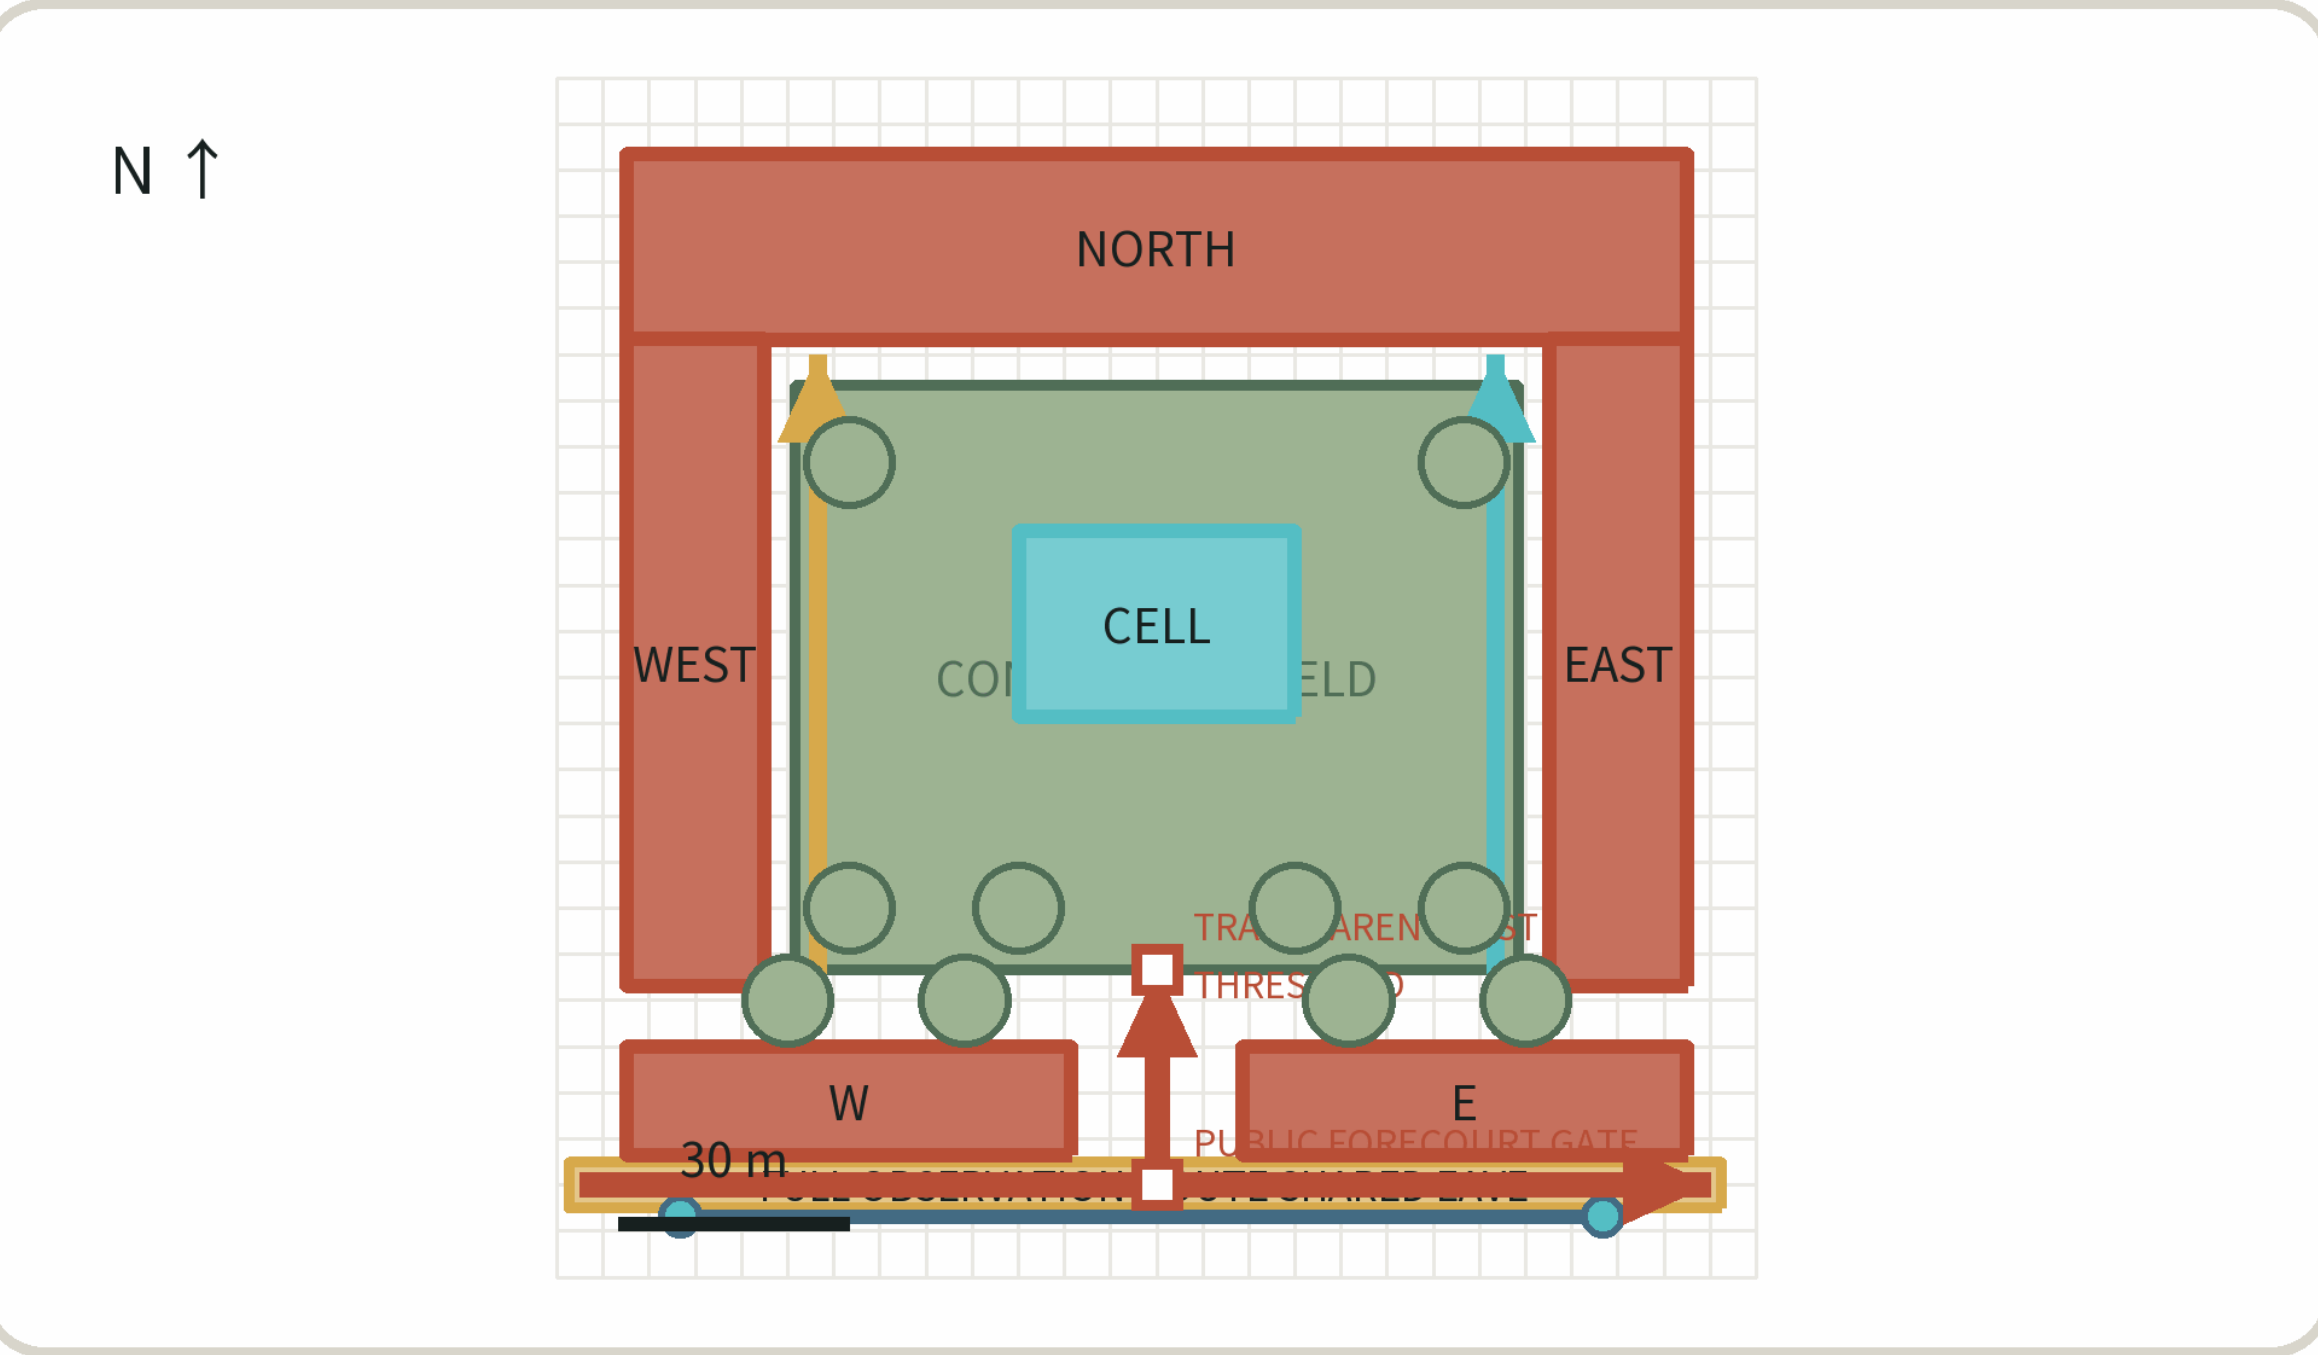

PUBLIC GROUND — CLIMATE EDGE — LONG-LIFE SUPPORT — REPLACEABLE INFILL

DEMOUNTABLE EAVE • VISIBLE DRAINAGE • FREEZE/THAW ACCESS

CERTIFIED LONG-LIFE 6 M SUPPORT → BOLTED SECONDARY FRAME → DRY REPLACEABLE INFILL
INSPECTABLE SERVICE BAND

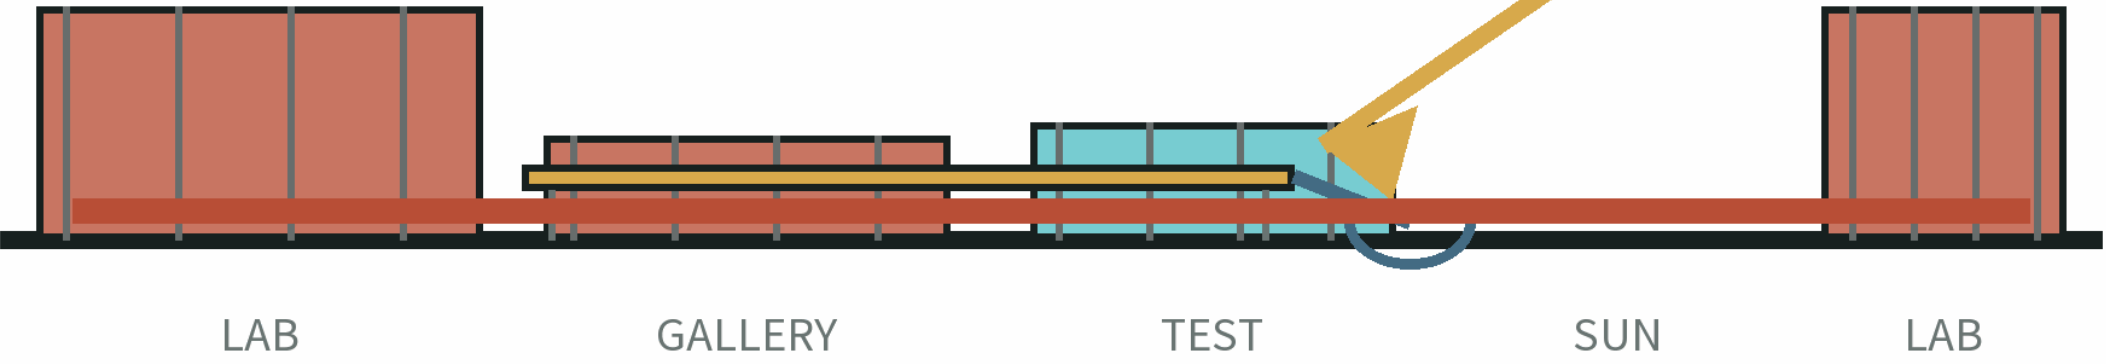

RETAIN / REPAIR / INSERT retain usable frame • repair public threshold • insert reversible first bay

FIRST PILOT observation cloister + isolated test cell

STEWARDSHIP test safety lead + independent checker (PROPOSED ROLE CLASS)

STOP RULE stop on boundary breach, failed replay or unsafe continuation


CANDIDATE PLACEMENT • OFFICIAL EXTENTS TRIGGER REVIEW + REBIND

AI ORIGIN • ORIGIN CLOISTER

Origin Cloister

CLOISTER / a retrofit-first campus-community weave


A/B MAY CHANGE OR CLOSE • H BYPASS • HUMAN SERVICE STAY OPEN

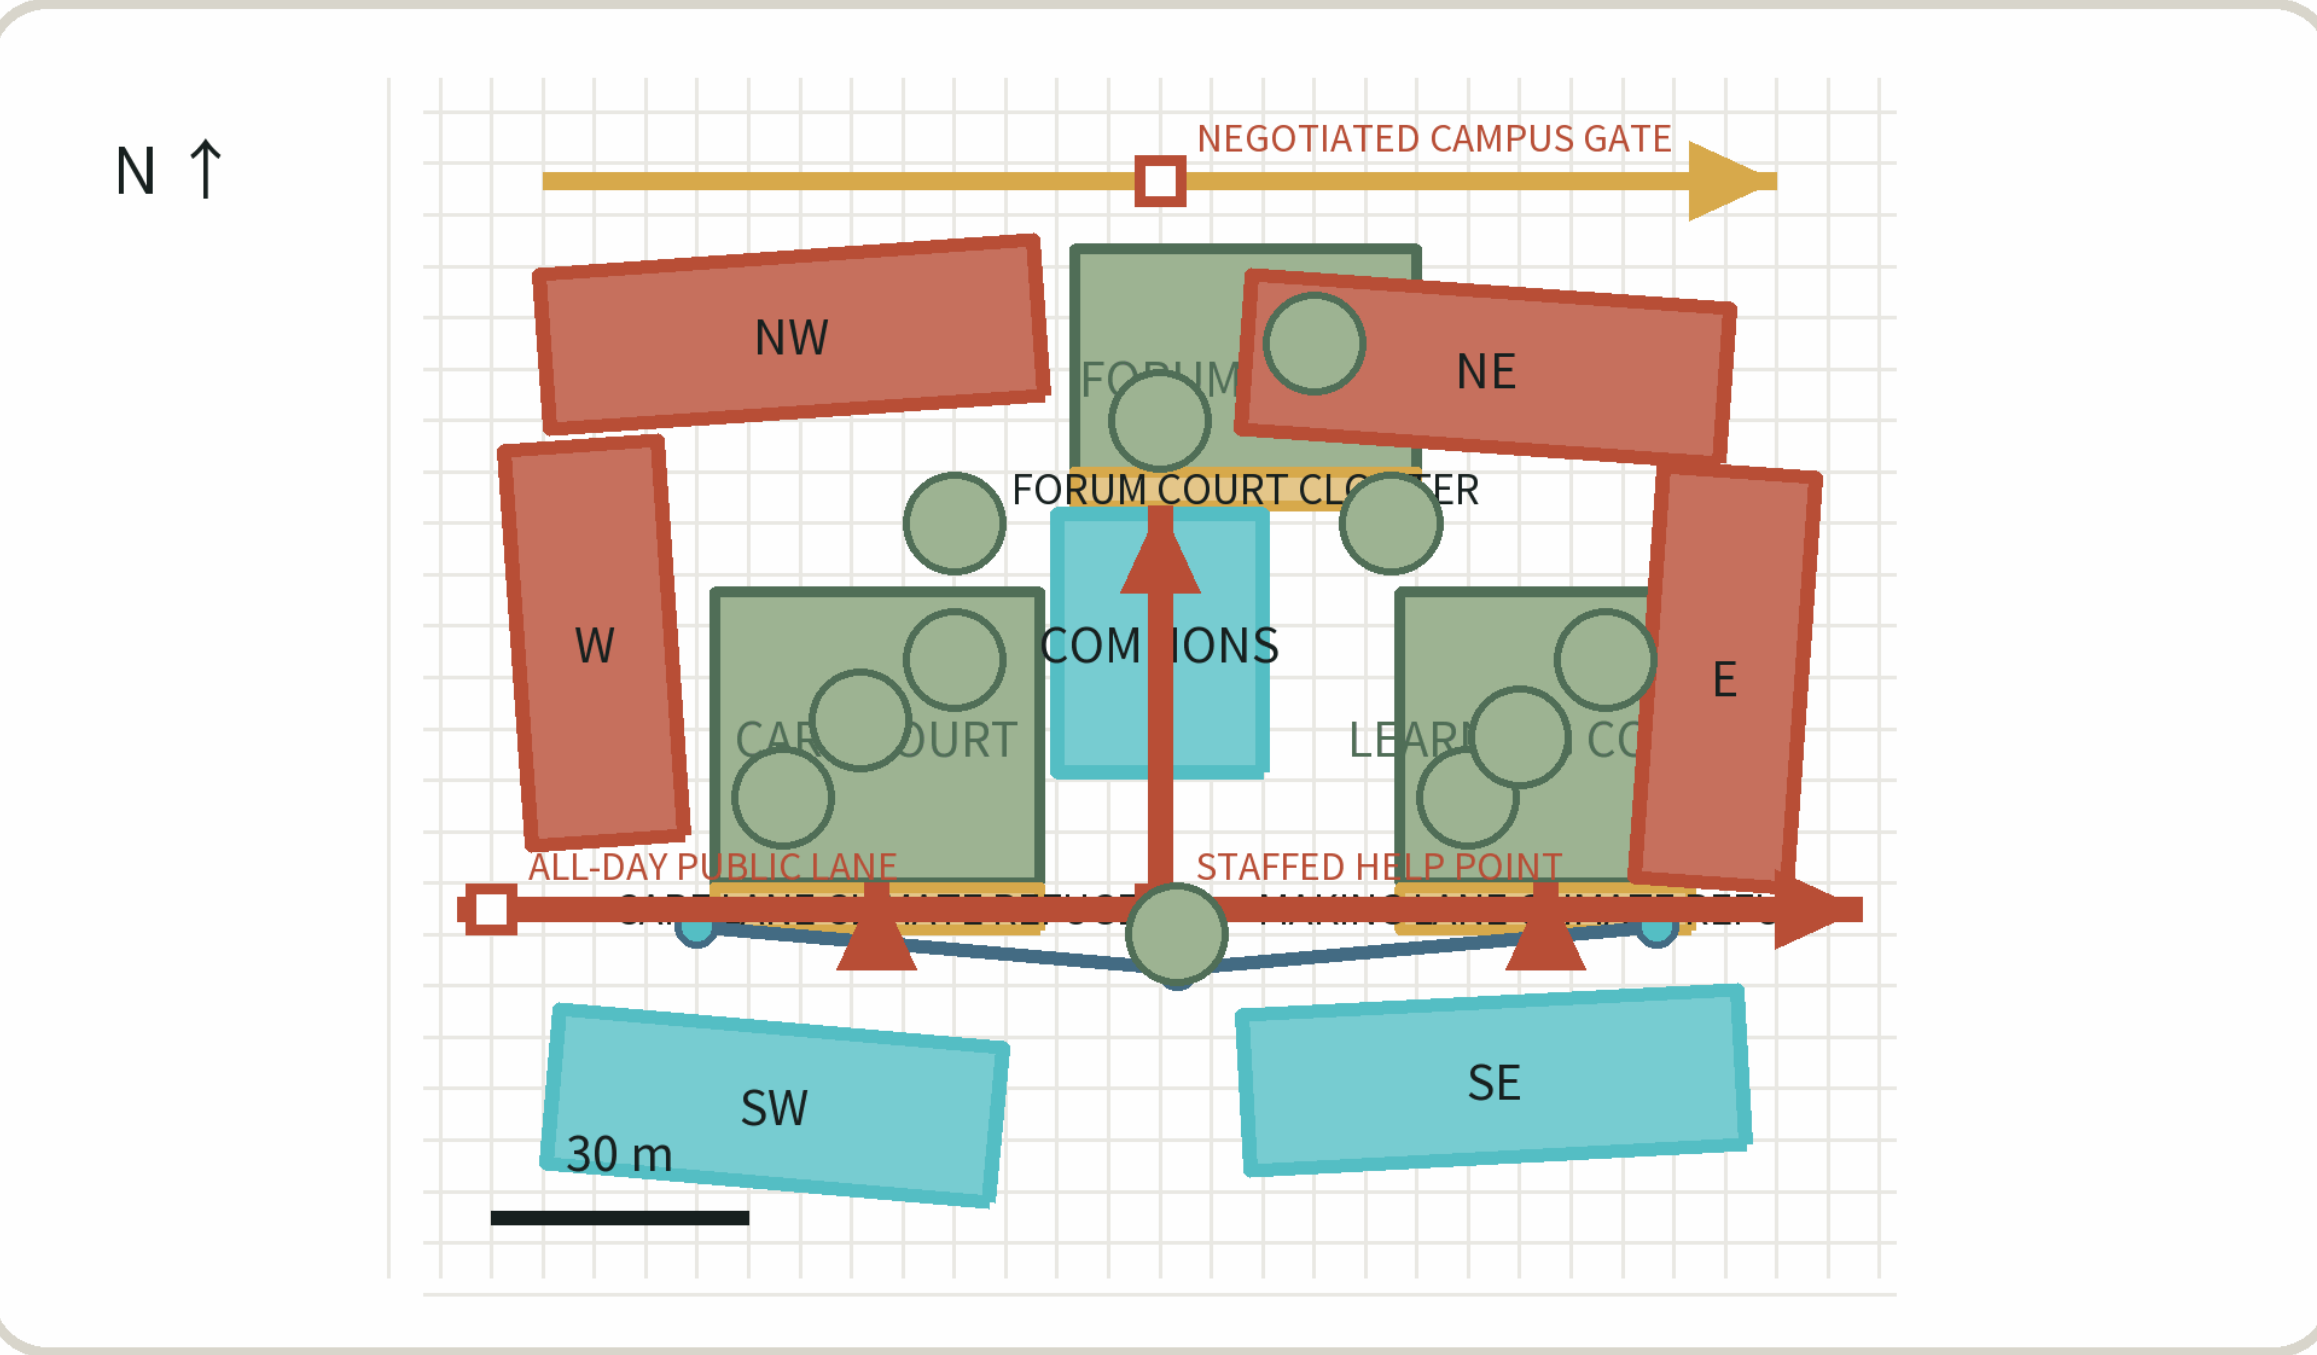

PUBLIC GROUND — CLIMATE EDGE — LONG-LIFE SUPPORT — REPLACEABLE INFILL

DEMOUNTABLE EAVE • VISIBLE DRAINAGE • FREEZE/THAW ACCESS

RETAIN AND CERTIFY EXISTING FRAME FIRST → INDEPENDENT BOLTED PLUG-IN → DRY 1.2 M INFILL
COORDINATION → EXPOSED MAINTAINABLE SERVICE STRIP

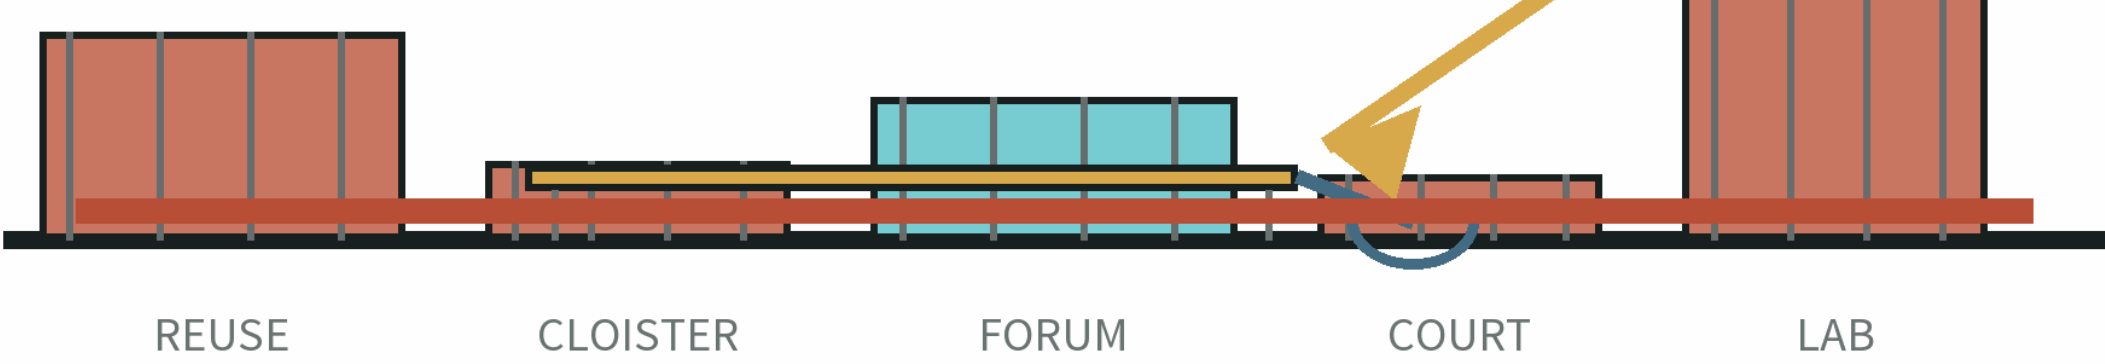

RETAIN / REPAIR / INSERT retain campus/community stock • repair access • insert porous cloister

FIRST PILOT timed campus threshold + care court

STEWARDSHIP campus-community joint operator (PROPOSED ROLE CLASS)

STOP RULE no build without access agreement and care operator


CANDIDATE PLACEMENT • OFFICIAL EXTENTS TRIGGER REVIEW + REBIND

DAZHONGSI • EXCHANGE HALL

Exchange Hall

HALL / four public entrances and one all-weather room


A/B MAY CHANGE OR CLOSE • H BYPASS • HUMAN SERVICE STAY OPEN

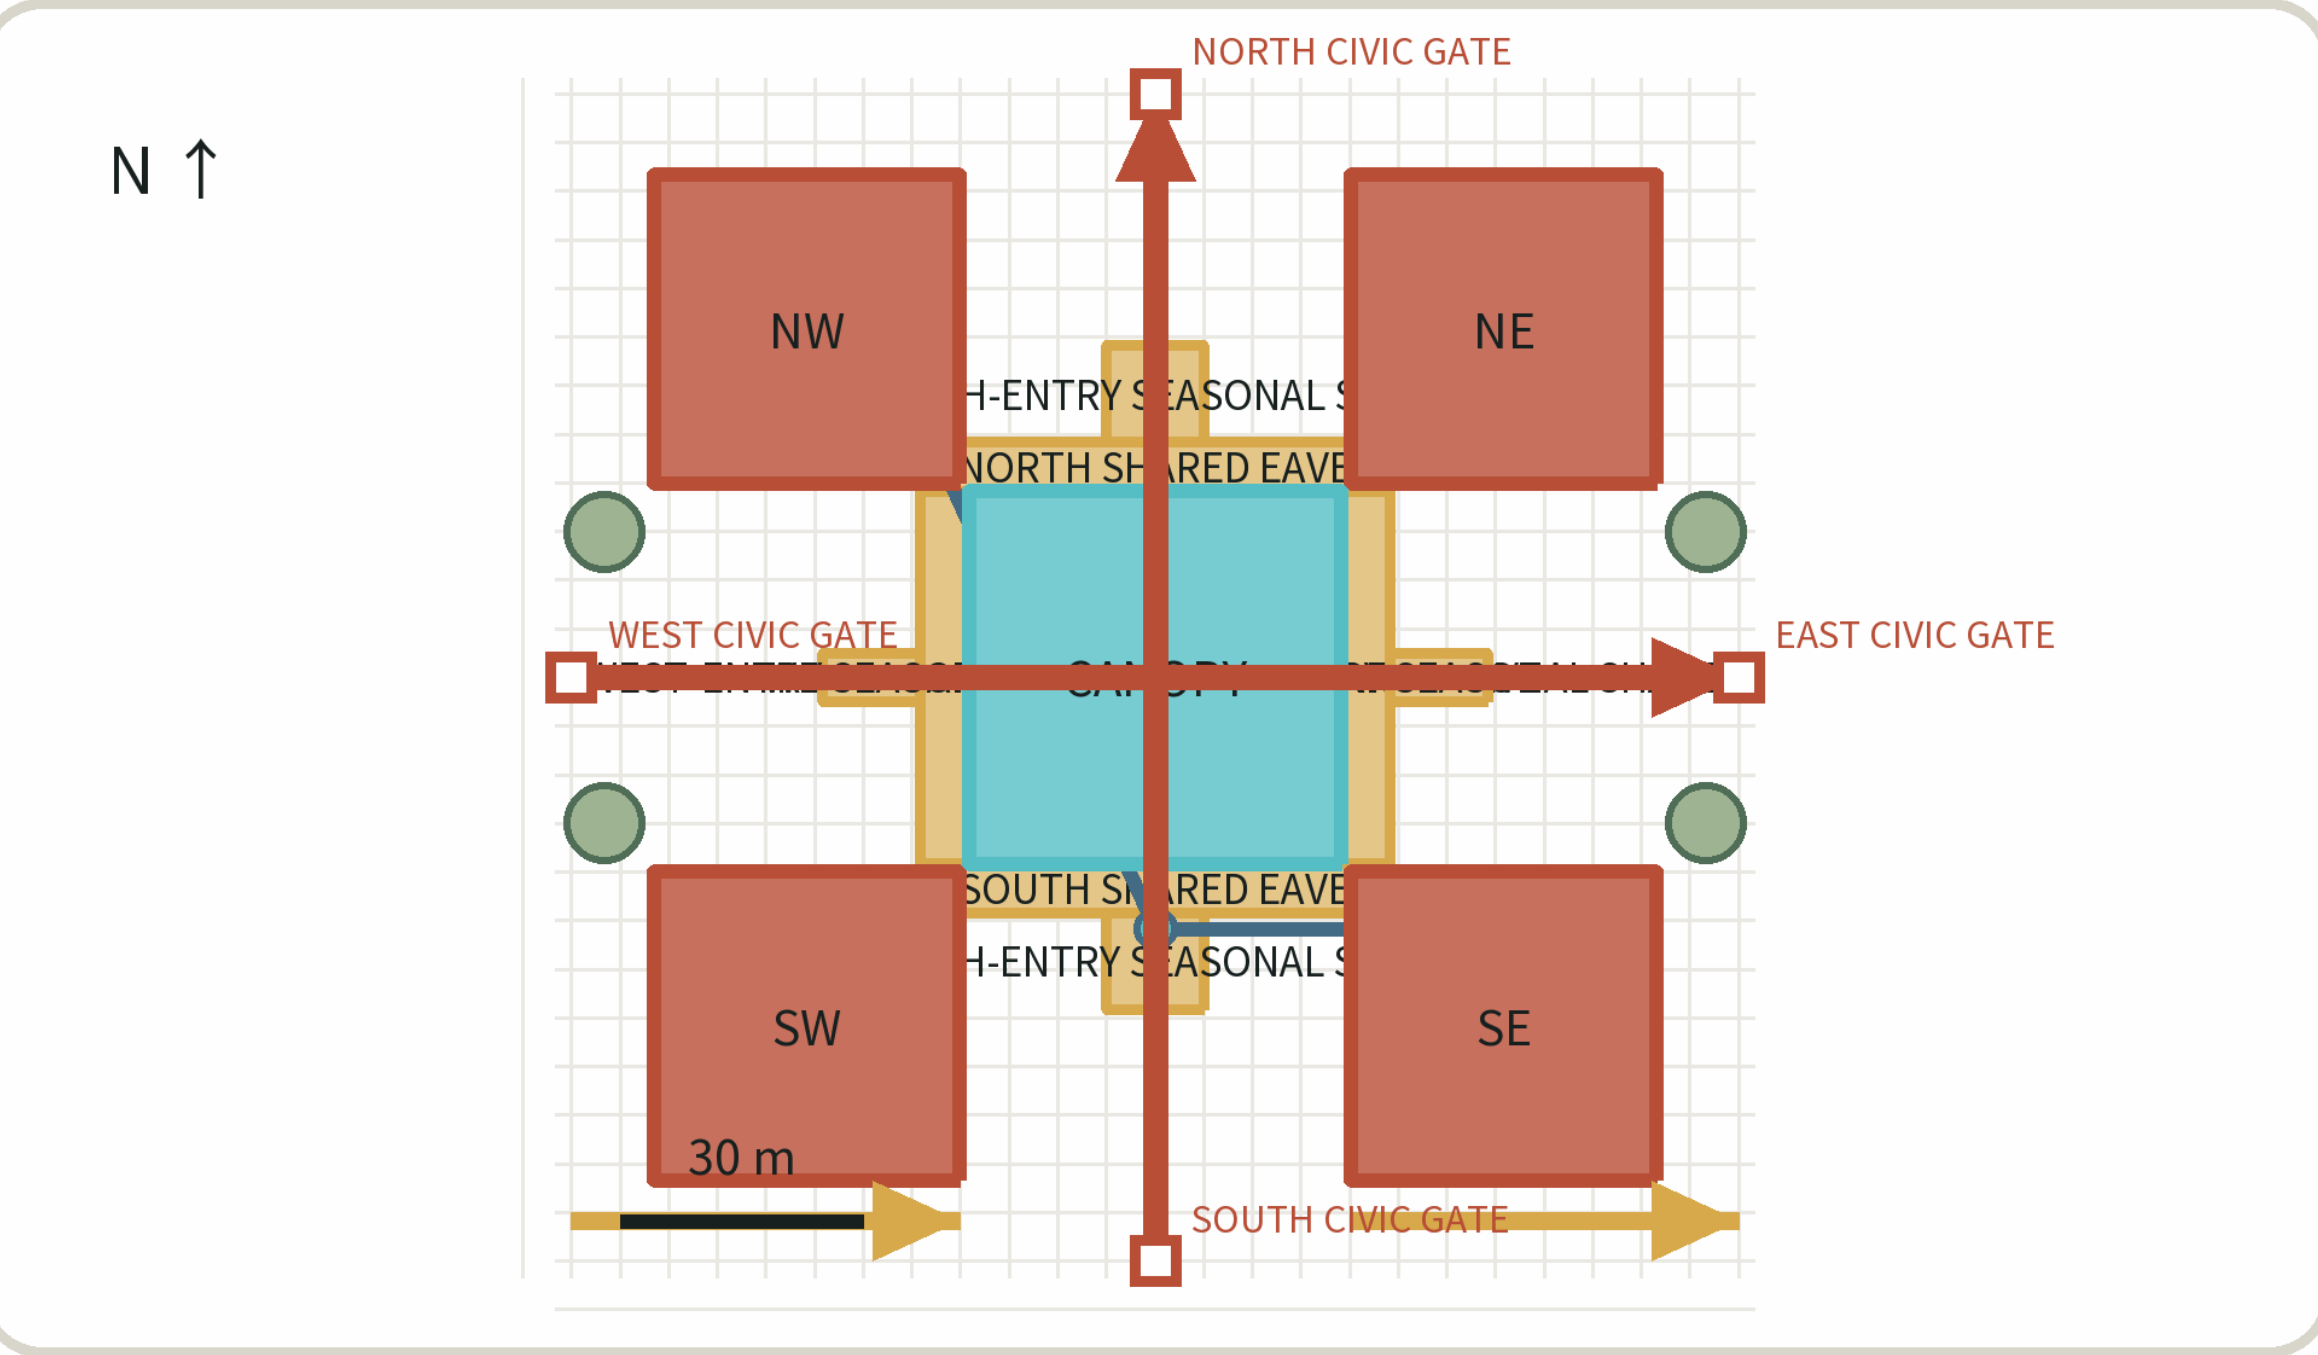

PUBLIC GROUND — CLIMATE EDGE — LONG-LIFE SUPPORT — REPLACEABLE INFILL

DEMOUNTABLE EAVE • VISIBLE DRAINAGE • FREEZE/THAW ACCESS

LONG-LIFE 8 M PRIMARY FRAME → DEMOUNTABLE ROOF CASSETTES → REPLACEABLE
MARKET/SERVICE INFILL → INSPECTABLE PERIMETER SERVICE BAND

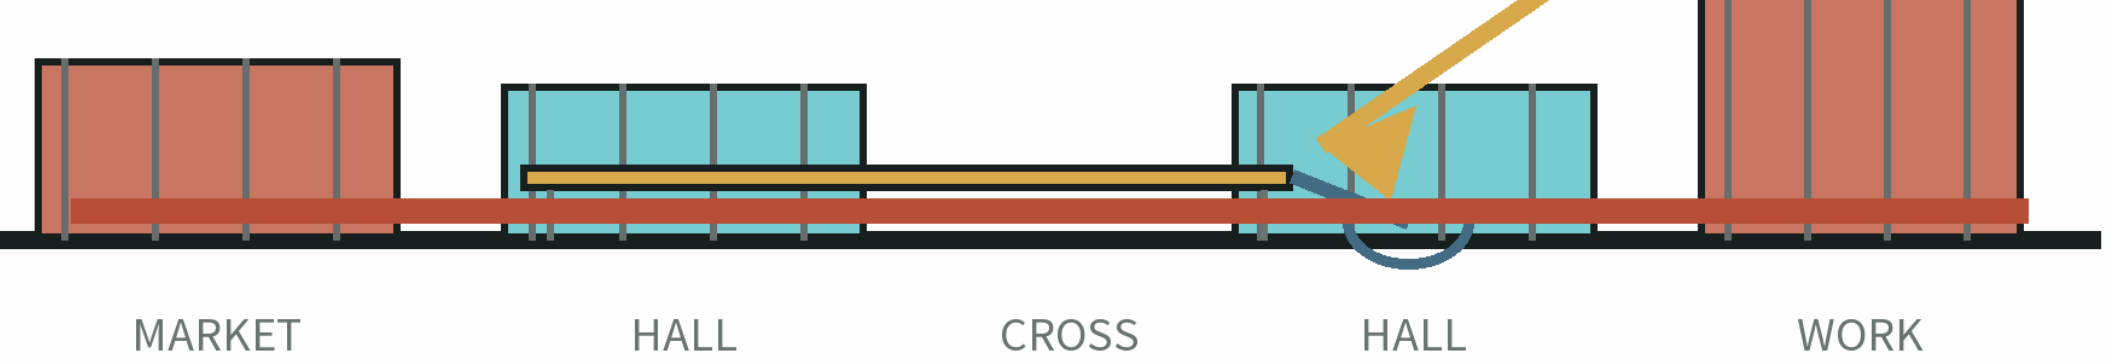

RETAIN / REPAIR / INSERT survey retain/repair/insert • repair four-quadrant walking • add all-weather eave

FIRST PILOT station porch + Rider Dock + staffed help desk

STEWARDSHIP local authority + transit + Shared Floor operator (PROPOSED ROLE CLASS)

STOP RULE no scale-up before movement, ownership, fire and cost evidence

CANDIDATE • NEAR NATIONAL-KEY JUESHENG TEMPLE; OVERLAY CONTROLS; NO GUESSED BUFFER

MAKE FAILURE VISIBLE; KEEP THE H TABLE

ONE LOCAL BGE-M3 SHADOW RUN EXPOSES SEVEN DELTAS; FOUR ORIGIN-LABELLED DIFFERENCES MAKE THE PERMANENT HUMAN H TABLE + DIFFERENCE DISPLAY NON-REMOVABLE

LOCAL MODEL SHADOW

29 / 36

B AGREES WITH PARTICIPANT A/REFERENCE; A IS NOT INDEPENDENT TRUTH

VISIBLE DELTAS

7 Δ

4 NON-HARD-STOP DELTAS CONCENTRATE ON ORIGIN TASKS

DETERMINISTIC H

12 / 12

EVERY HARD-STOP IS HELD AT THE DETERMINISTIC H GATE

SPATIAL RESULT

H TABLE

PERMANENT HUMAN REVIEW + PUBLIC DIFFERENCE DISPLAY

ONE ACTUAL LOCAL INFERENCE: A/REFERENCE × B/CANDIDATE

BGE-M3 • 1 BATCH / 39 INPUTS • 1024-D • EXACT TAG/MANIFEST/BLOB HASHES

A/REFERENCE	B=PROOF	B=ORIGIN	B=EXCHANGE
PROOF YARD	10	0	2
ORIGIN CLOISTER	3	7	2
EXCHANGE HALL	0	0	12

FOUR NON-HARD-STOP DELTAS: AI01-AMBIGUOUS • AI06-NORMAL/AMBIGUOUS • AI08-AMBIGUOUS

SPATIAL CHANGE / KEEP B IN SHADOW

FOUR NON-HARD-STOP DELTAS ARE ORIGIN-LABELLED: KEEP THE H TABLE + DIFFERENCE DISPLAY NON-REMOVABLE; DO NOT PROMOTE B; CLAIM NO SIZE CHANGE.

P0 / FROM DESIGN TO DECISION

ONE CONDITIONAL RELAY LINKS PRECONDITION, ACCOUNTABILITY, QUANTITIES + ACCEPTANCE

T00
DOCUMENT GATE

>

T01-11
W1-15 REFERENCE

>

12
ROLE CLASSES / RACI

>

16
QUANTITY LINES

>

12
INDICATORS

SINGLE ACCOUNTABILITY

EXACTLY ONE ACCOUNTABLE CLASS FOR EACH OF 12 TASKS

TRACEABLE QUANTITIES

14 DESIGN/REFERENCE-DERIVED + 2 TBC AFTER SURVEY OR AUTHORISED REVIEW

EVIDENCE HANDOFF

12 TEMPLATES: PREPARER → FUTURE ISSUER/ACCOUNTABLE CLASS → REVIEWER → ACCEPTOR

ACCEPTANCE LOGIC

8 PARTICIPANT RULES + 4 TO BE SET AFTER AN AUTHORISED BASELINE

BOUNDARY • PARTICIPANT TEMPLATE UNSIGNED / UNAPPROVED • EXTERNAL EVIDENCE RECEIPTS 0 • EXTERNAL RELEASES HOLD

DELTA IS NOT A BACK-END SCORE: AT ORIGIN IT LEAVES A HUMAN REVIEW TABLE, A PUBLICLY LEGIBLE DIFFERENCE DISPLAY AND AN H ROUTE THAT DOES NOT DEPEND ON B.

03 / 07 • ACTUAL SHADOW DELTA LEAVES THE H TABLE

ONE LOCAL MODEL CALL MAKES DIFFERENCE VISIBLE: FOUR ORIGIN-LABELLED DELTAS MAKE THE PERMANENT HUMAN H TABLE AND PUBLIC DIFFERENCE DISPLAY NON-REMOVABLE; P0 THEN CONNECTS DESIGN TO A CONDITIONAL IMPLEMENTATION RELAY

01 29/36 / A-reference and B agree


02 7 deltas / 4 at Origin

03 12/12 / deterministic H-gate HOLD

04 T00 → T01-T11 / W1-15

THE SHARED FLOOR / THE REAL CITY IS THE GROUND

SEVEN LOCAL FIGURE-GROUNDS; DATA GAPS ARE NOT FILLED BY ASSUMPTION

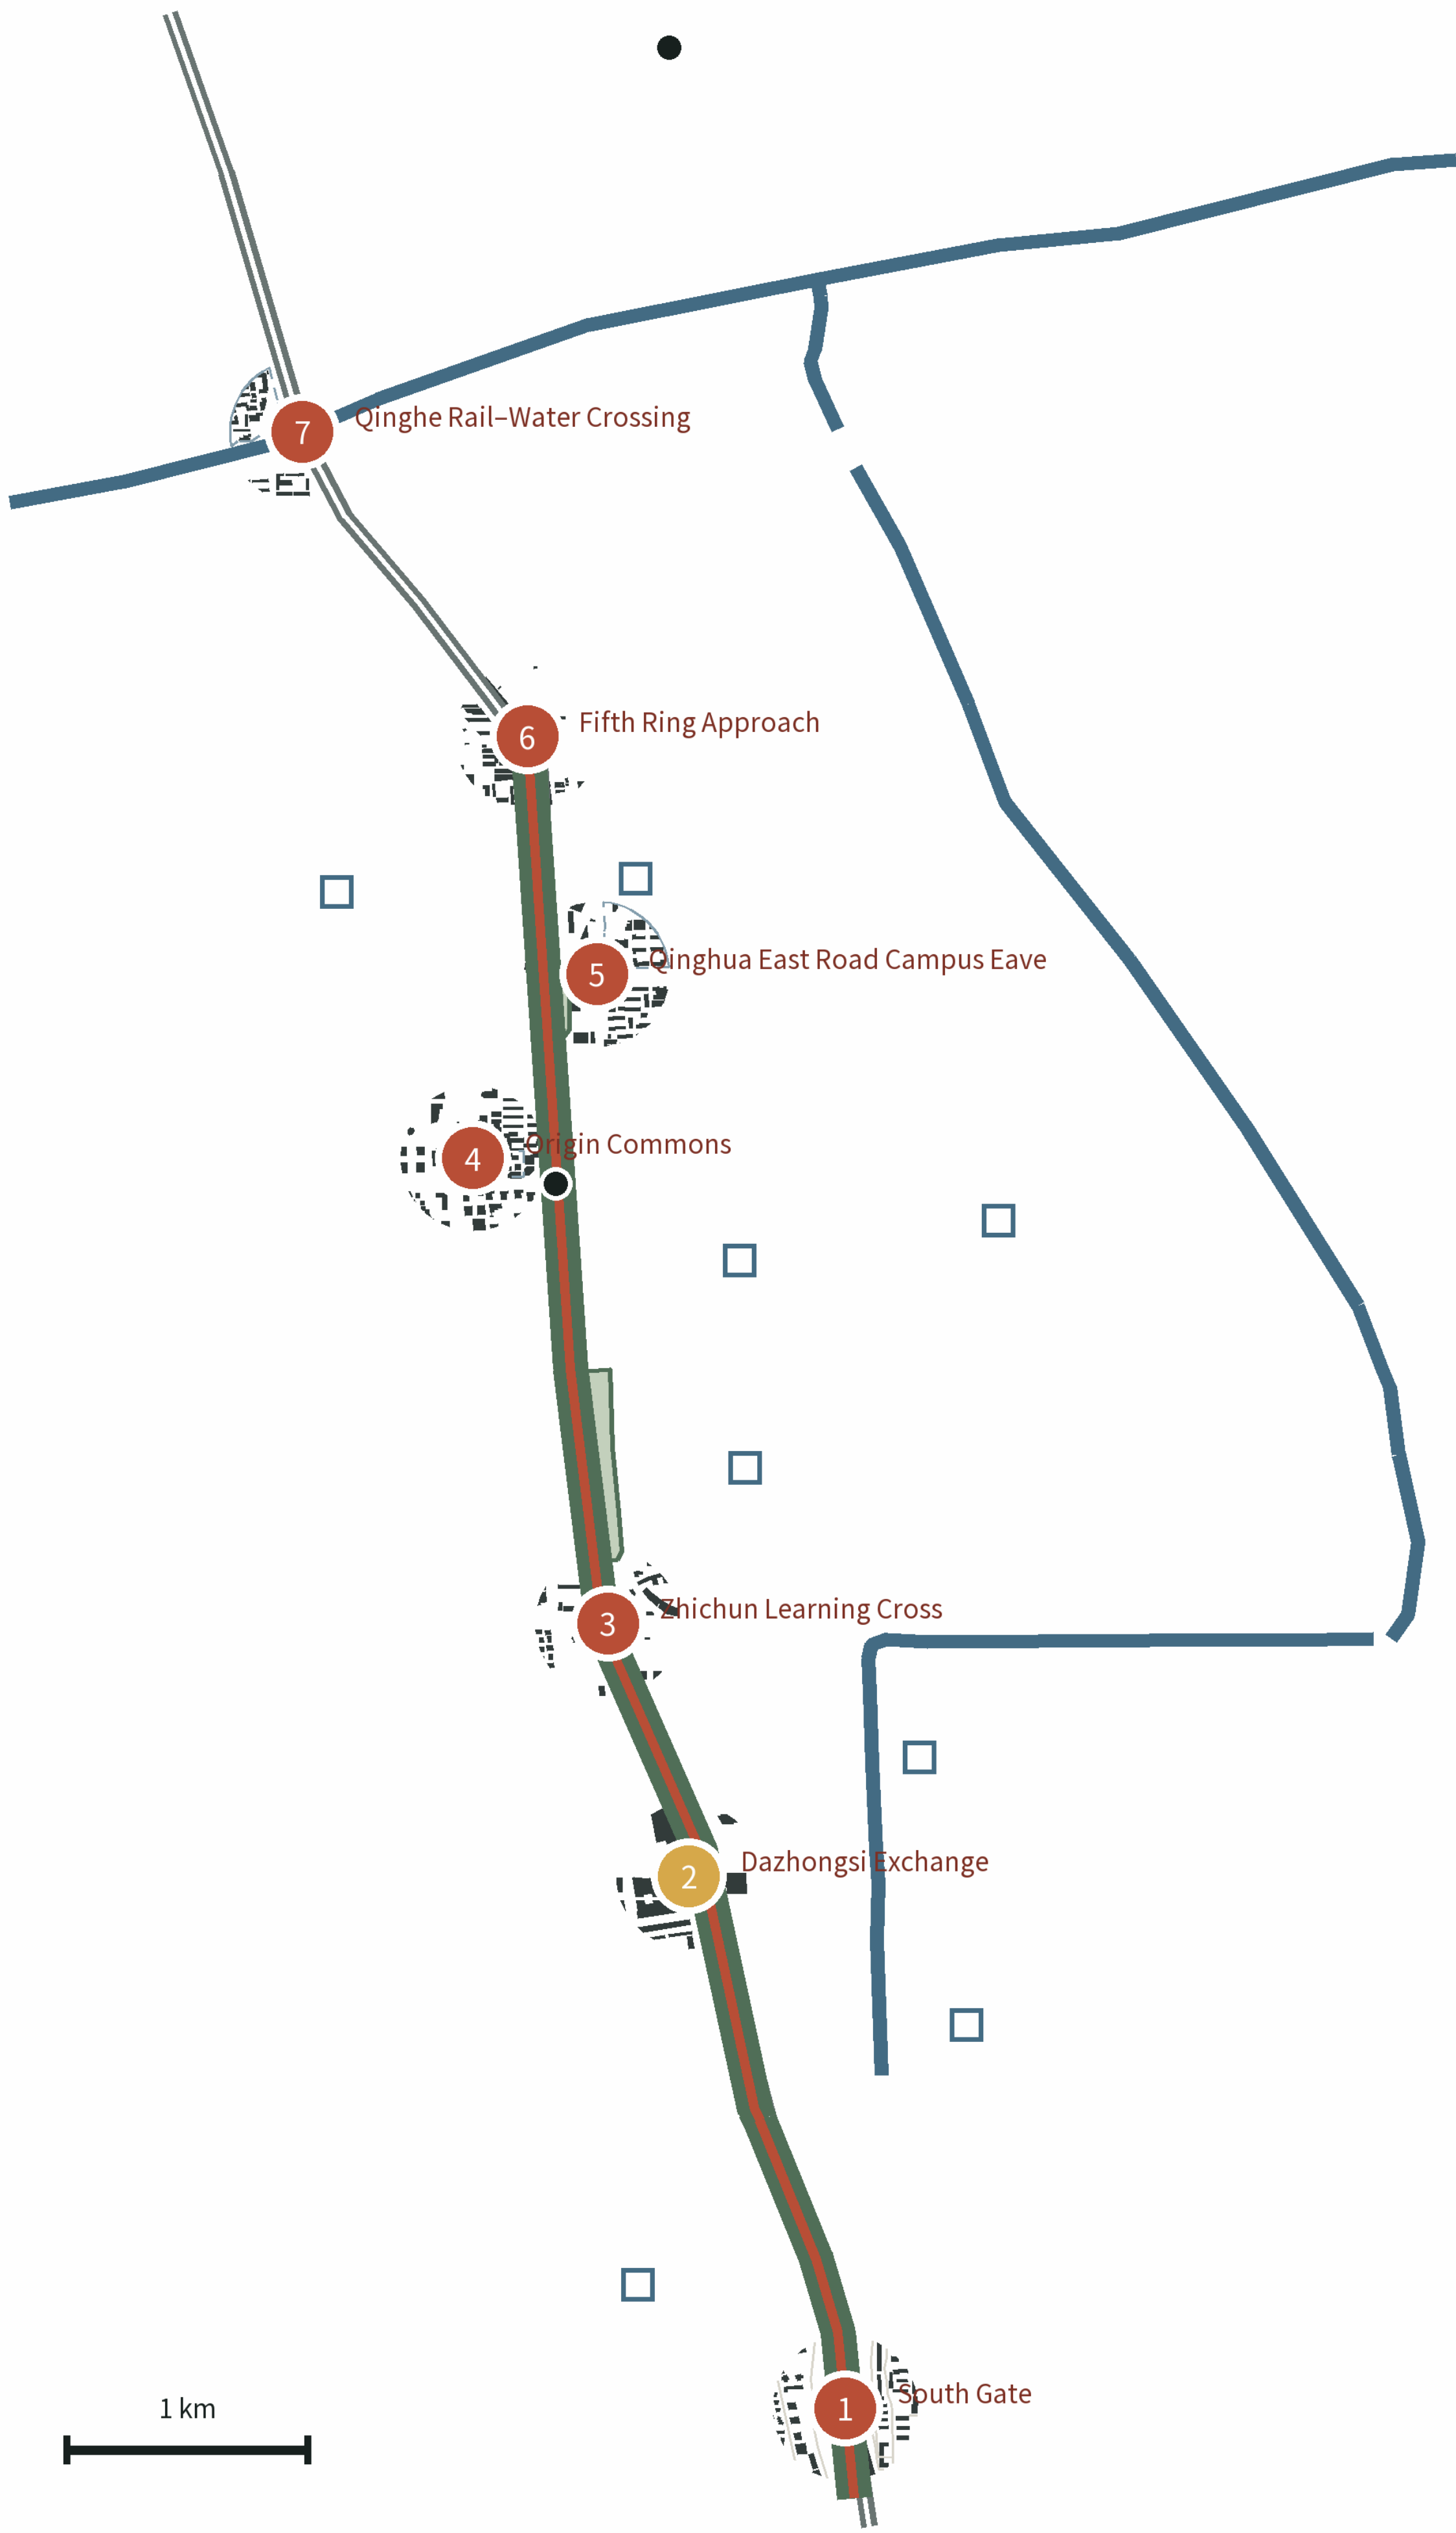

© OpenStreetMap contributors · ODbL 1.0 · MORPHOLOGY + ATTACHMENT READING ONLY
NOT A STATUTORY MAP, REDLINE, PARCEL, SURVEY, BUILDING INVENTORY, ACCESS AGREEMENT OR NAVIGATION PRODUCT

SCOPE + EVIDENCE STATUS

43.6 km²

research / official approximate

11.4 km²


overall design / official approximate

368.4 ha

three key areas / official approximate

DARK=OSM BUILDING UNION · FINE=STREET · RED=RAIL · BLUE=WATER/GATE · ●=STATION · □=CAMPUS CENTROID · NUMBER=CANDIDATE

C1 · South Gate

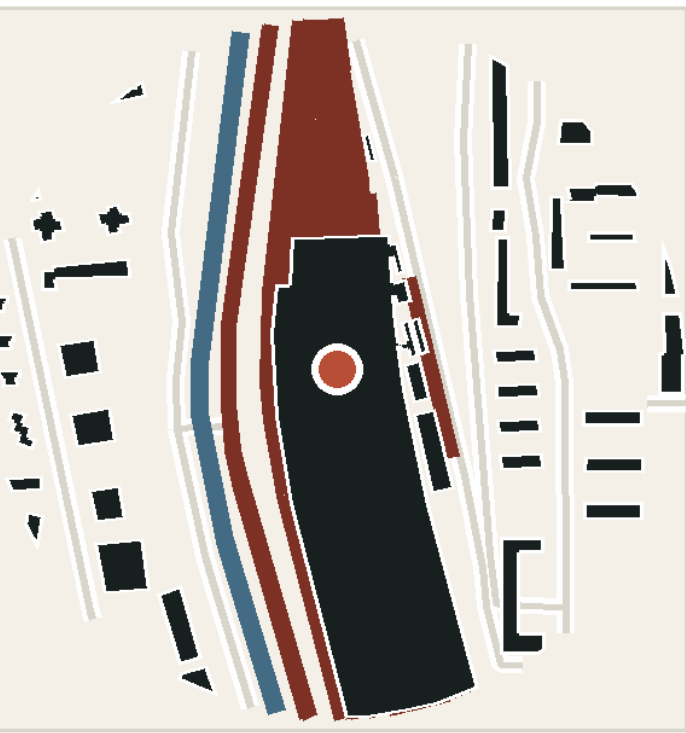


BEIJING NORTH + CURRENT/FORMER RAIL TERMINUS

HERITAGE THRESHOLD

FORECOURT, HERITAGE + FLOW SURVEY REQUIRED
EXPERT | RESIDENT → GAP=REVISE

MAPPED: 44 BUILDING / 13 STREET RECORDS

C2 · Dazhongsi Exchange

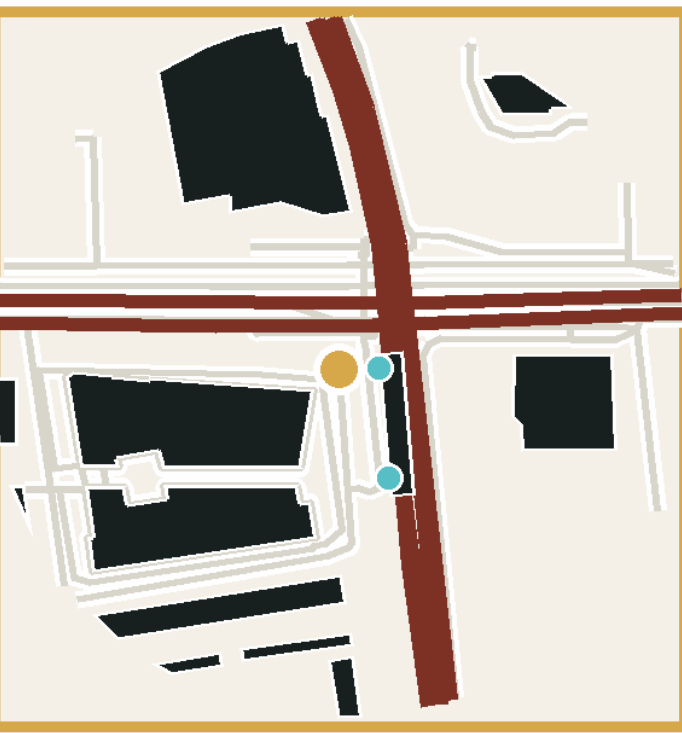

STATION + RAIL + FOUR-QUADRANT FRACTURE

P0 STATION PORCH; NIGHT ROOM CONDITIONAL

TITLE, METRO, FIRE + OPERATOR

EXPERT | RESIDENT → GAP=REVISE

MAPPED: 12 BUILDING / 48 STREET RECORDS

C3 · Zhichun Learning Cross



STATION + RAIL + LEARNING DISTRICT

ZHICHUN LEARNING CROSS

7-DAY FLOW, ACCESS + CORNER SURVEY

EXPERT | RESIDENT → GAP=REVISE

MAPPED: 39 BUILDING / 94 STREET RECORDS

C4 · Origin Commons



FORMER-RAIL/PARK CONNECTOR + DAILY LIFE

ORIGIN COMMONS / CARE PORCH

HERITAGE, LOCAL NEED + OPERATOR AGREEMENT
EXPERT | RESIDENT → GAP=REVISE

MAPPED: 68 BUILDING / 170 STREET RECORDS

C5 · Qinghua East Road Campus Eave



STATION + CAMPUS CENTROID; GATE NOT CAPTURED

NEGOTIATED CAMPUS GATE

EXACT GATE, SECURITY + CAMPUS AGREEMENT

EXPERT | RESIDENT → GAP=REVISE

MAPPED: 51 BUILDING / 90 STREET RECORDS

C6 · Fifth Ring Approach



CURRENT/FORMER RAIL NEAR FIFTH RING; ROAD SEAM UNVERIFIED

RIDER DOCK / SERVICE FORECOURT

ROAD, LOADING, FIRE + LAND SURVEY

EXPERT | RESIDENT → GAP=REVISE

MAPPED: 49 BUILDING / 128 STREET RECORDS

C7 · Qinghe Rail-Water Crossing



CURRENT RAIL × QINGHE


SPONGE CROSSING

HYDROLOGY, RAIL, DRAINAGE + FLOOD REVIEW

EXPERT | RESIDENT → GAP=REVISE

MAPPED: 31 BUILDING / 48 STREET RECORDS

JING-ZHANG EVIDENCE LINE

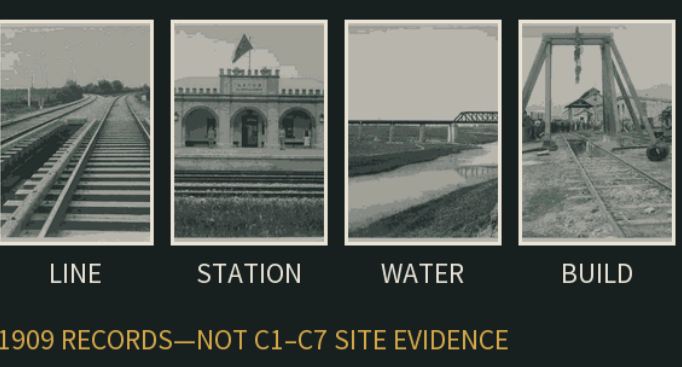

1909 RECORDS—NOT C1–C7 SITE EVIDENCE


- ARCHIVE / RECORD
- FIELD / SURVEY
- P0 / REVERSIBLE PILOT
- SAME INDICATORS / EXP+RES
- ADOPT · REVISE · RETIRE

INHERIT THE METHOD, NOT THE FORM · NO SCORING YET
CREDIT: TONGSHENG PHOTO STUDIO, JING-ZHANG LU GONG CUO YING, 1909 · ORIGINAL NLC · WDL/LOC · LCCN 2021668851

FOUR PROGRAMME BANDS; FIVE RENEWAL SPEEDS

CONCEPT LAND USE IS NOT ZONING; GROUND AND SUPPORT ENDURE WHILE SERVICES, INFILL AND EQUIPMENT CHANGE

N ↗ • PLAN ROTATED 65° CLOCKWISE FOR SHEET READING

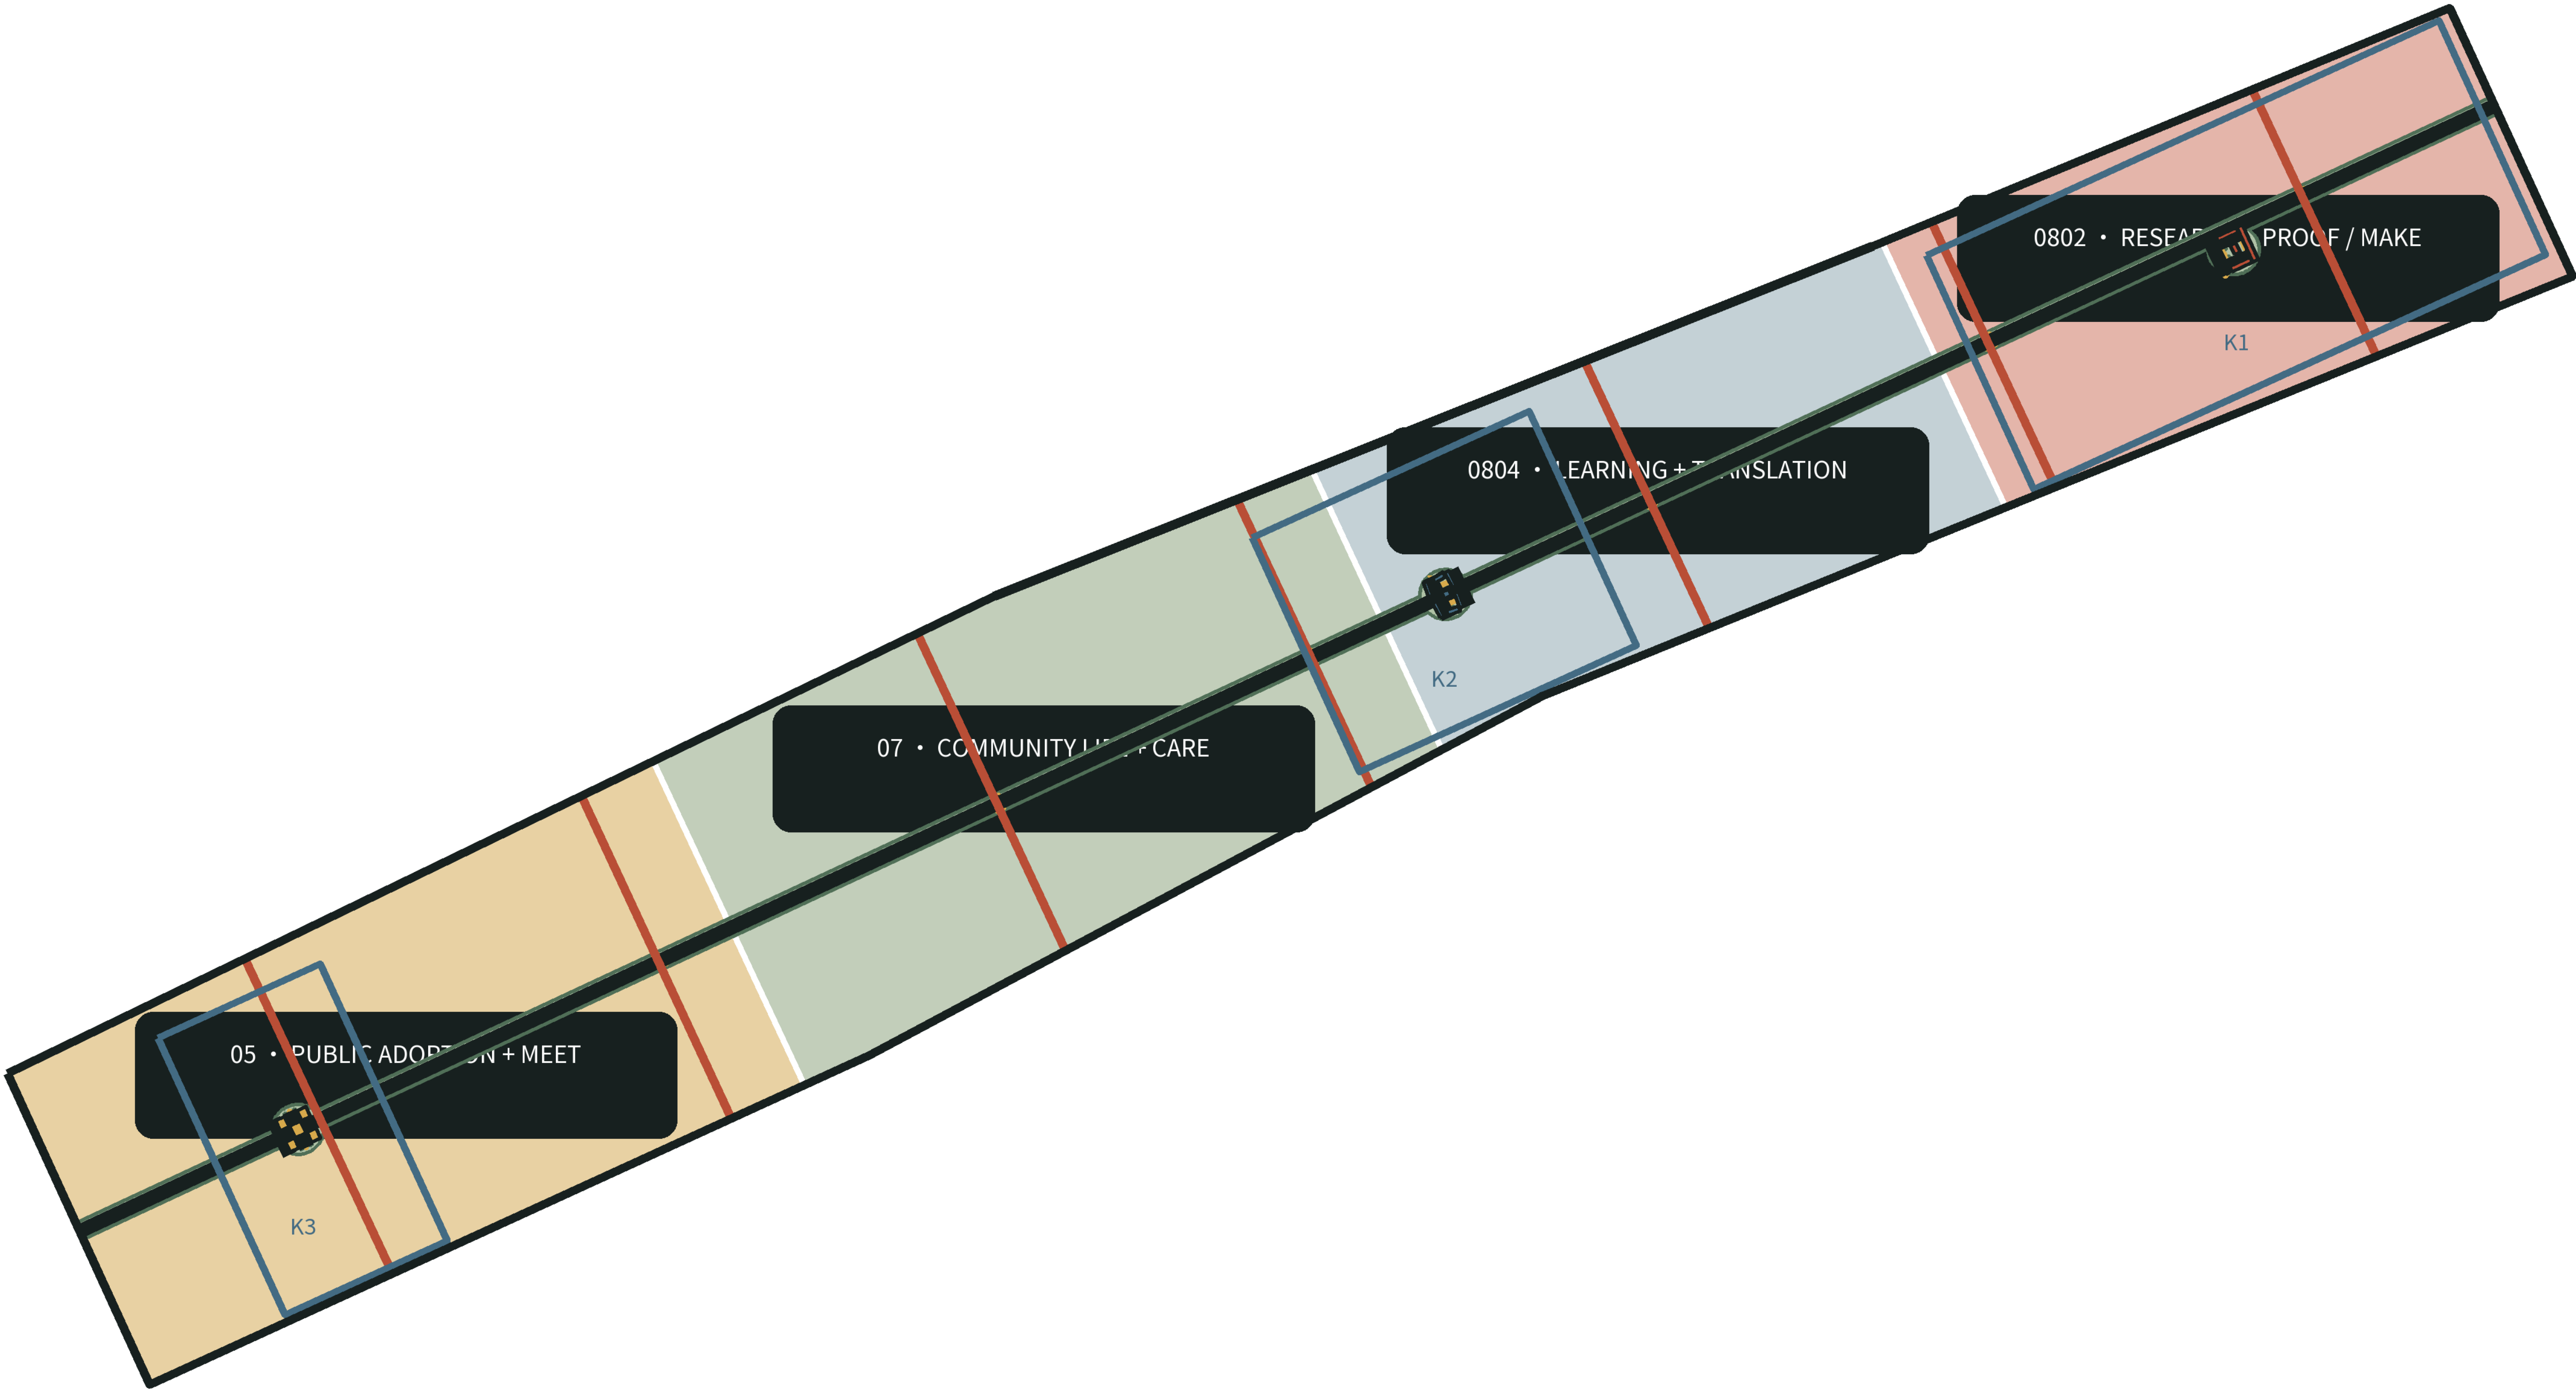

CONCEPT LAND-USE STRUCTURE • NOT STATUTORY ZONING • REVIEW + REBIND ON OFFICIAL CONTROLS

FILL=FOUR PROGRAMME BANDS • DARK=THREE LONG-LIFE FRAMES • GOLD=PUBLIC ROOMS • RED=SEVEN CROSS-INTERFACES

PROGRAMME × DESIGN LIFE

0802 MAKE	0804 TRANSLATE
07 LIVE	05 MEET

DAZHONGSI • ENCOURAGED SHARED LEVELS

2F	ENCOURAGED
G	ENCOURAGED
B1	ENCOURAGED
B2	ENCOURAGED

ENCOURAGED ≠ BUILT, OPEN, EASEMENT OR 24H ACCESS

METRO / OWNER / FIRE / STRUCTURE / OPERATIONS ARE PREREQUISITES

FIVE RENEWAL SPEEDS

00	GROUND + CLIMATE EDGE	100+
01	LONG-LIFE SUPPORT	100
02	SERVICE CHASSIS	25–40
03	REPLACEABLE INFILL	5–20
04	SCENARIO KIT	≤5

KEEP FRAME; CHANGE CORE; RECORD EACH REPLACEMENT. TARGETS ARE NOT WARRANTIES.

OFFICIAL EXTENTS + CONTROLS TRIGGER REVIEW, RECALCULATION + REISSUE.

05 / 07 • THE CITY STAYS; THE MODEL CHANGES

PUBLIC GROUND, LONG-LIFE SUPPORT AND THE H SERVICE CHASSIS REMAIN; A/B MODELS, INFILL AND EQUIPMENT CAN CHANGE

01 100+ / public ground

02 100 / support target


03 H / continuous service

04 A/B / replaceable slots


TWELVE-METRE SHARED GROUND: WALK FIRST; ROBOTS YIELD FIRST

DAZHONGSI OFFICIAL RELATIONSHIPS + 12 m SECTION • PLANNED IS NOT BUILT

DAZHONGSI • OFFICIAL PLANNING RELATIONSHIPS (NOT GIS)

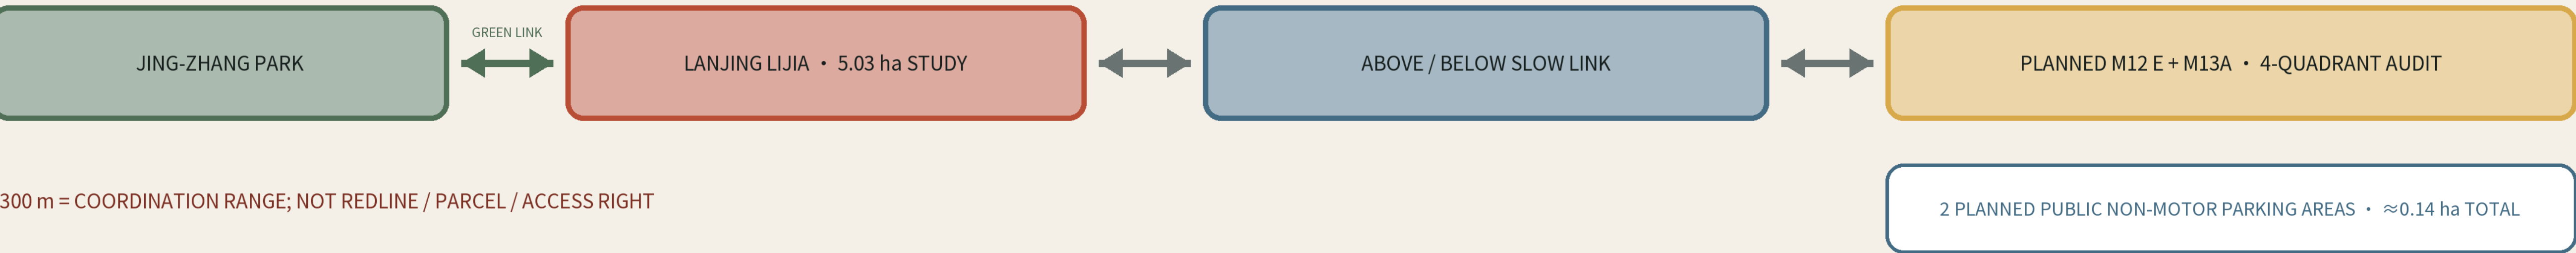

ENCOURAGED SHARING + LINKS ≠ OPEN, BUILT OR AN APPROVED ROUTE

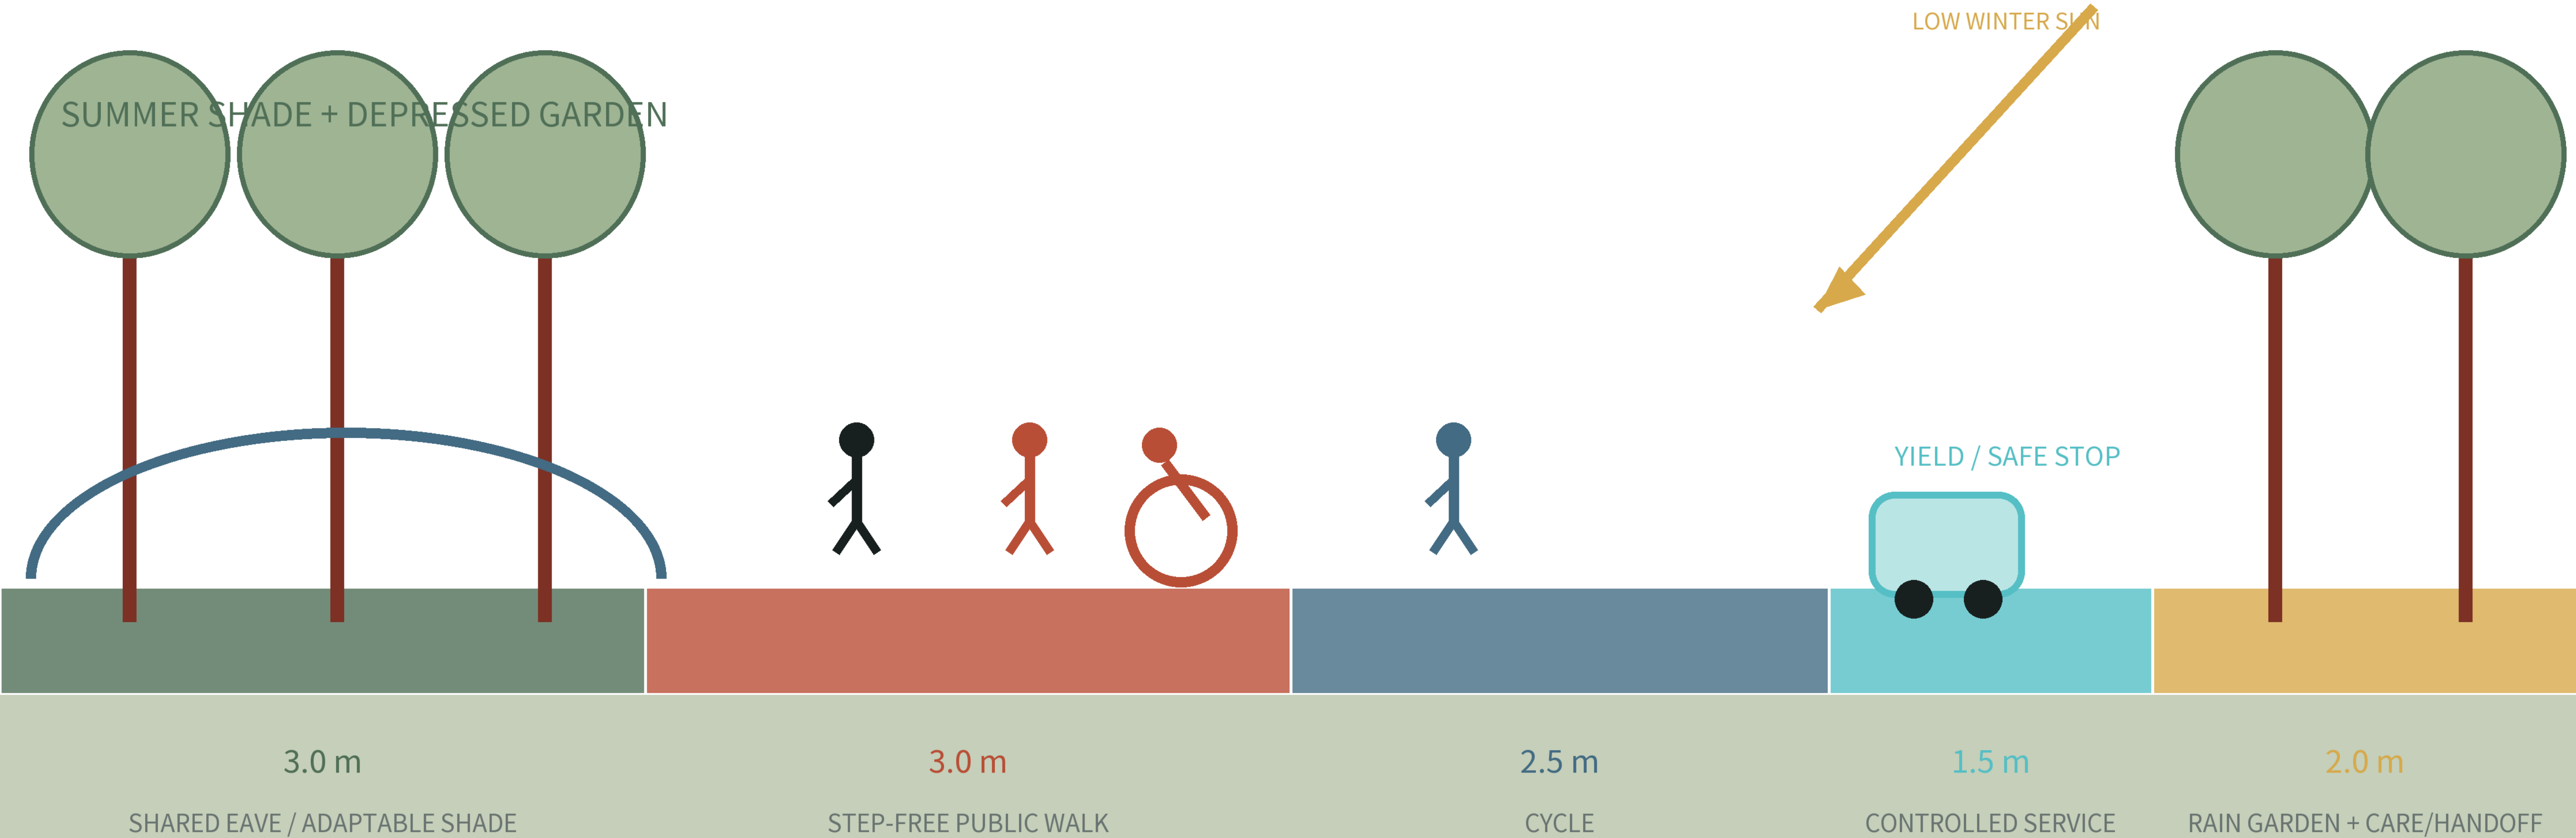

12.0 m REFERENCE SECTION TARGET • NOT A STATUTORY ROAD RESERVATION

12 AI CARDS / 4 SHOWN

SPACE • PROPOSED STEWARDSHIP CLASS • HUMAN FALLBACK

AI01

TEST

STEP-FREE TRANSFER CHECK

7 ROOMS • ACCESS

FAIL→PAPER+ESCORT

AI02

TEST

LOW-SPEED DELIVERY TRIAL

YARD • SAFETY

FAIL→CART+STOP

AI05

TEST

CLIMATE-REFUGE OPERATING CUES

EAVES • STEWARD

FAIL→MANUAL CHECK

AI12

MULTILINGUAL HUMAN HELP DESK

HELP POINT • CIVIC STAFF

FAIL→INTERPRETER

S01–S15 EVERYDAY-LIFE REHEARSALS


7 PERSONAS • 24H × 4 SEASONS

ALL SEVEN CIVIC ROOMS REQUIRE A 7-DAY FIELD BASELINE

COMPLETE CARDS ≠ PROVEN LOCAL DEMAND OR PERFORMANCE

ROBOTS: LOW SPEED, YIELD, SAFE STOP; HUMAN SERVICE CONTINUES


ZHONGZHIYUAN • PROOF YARD

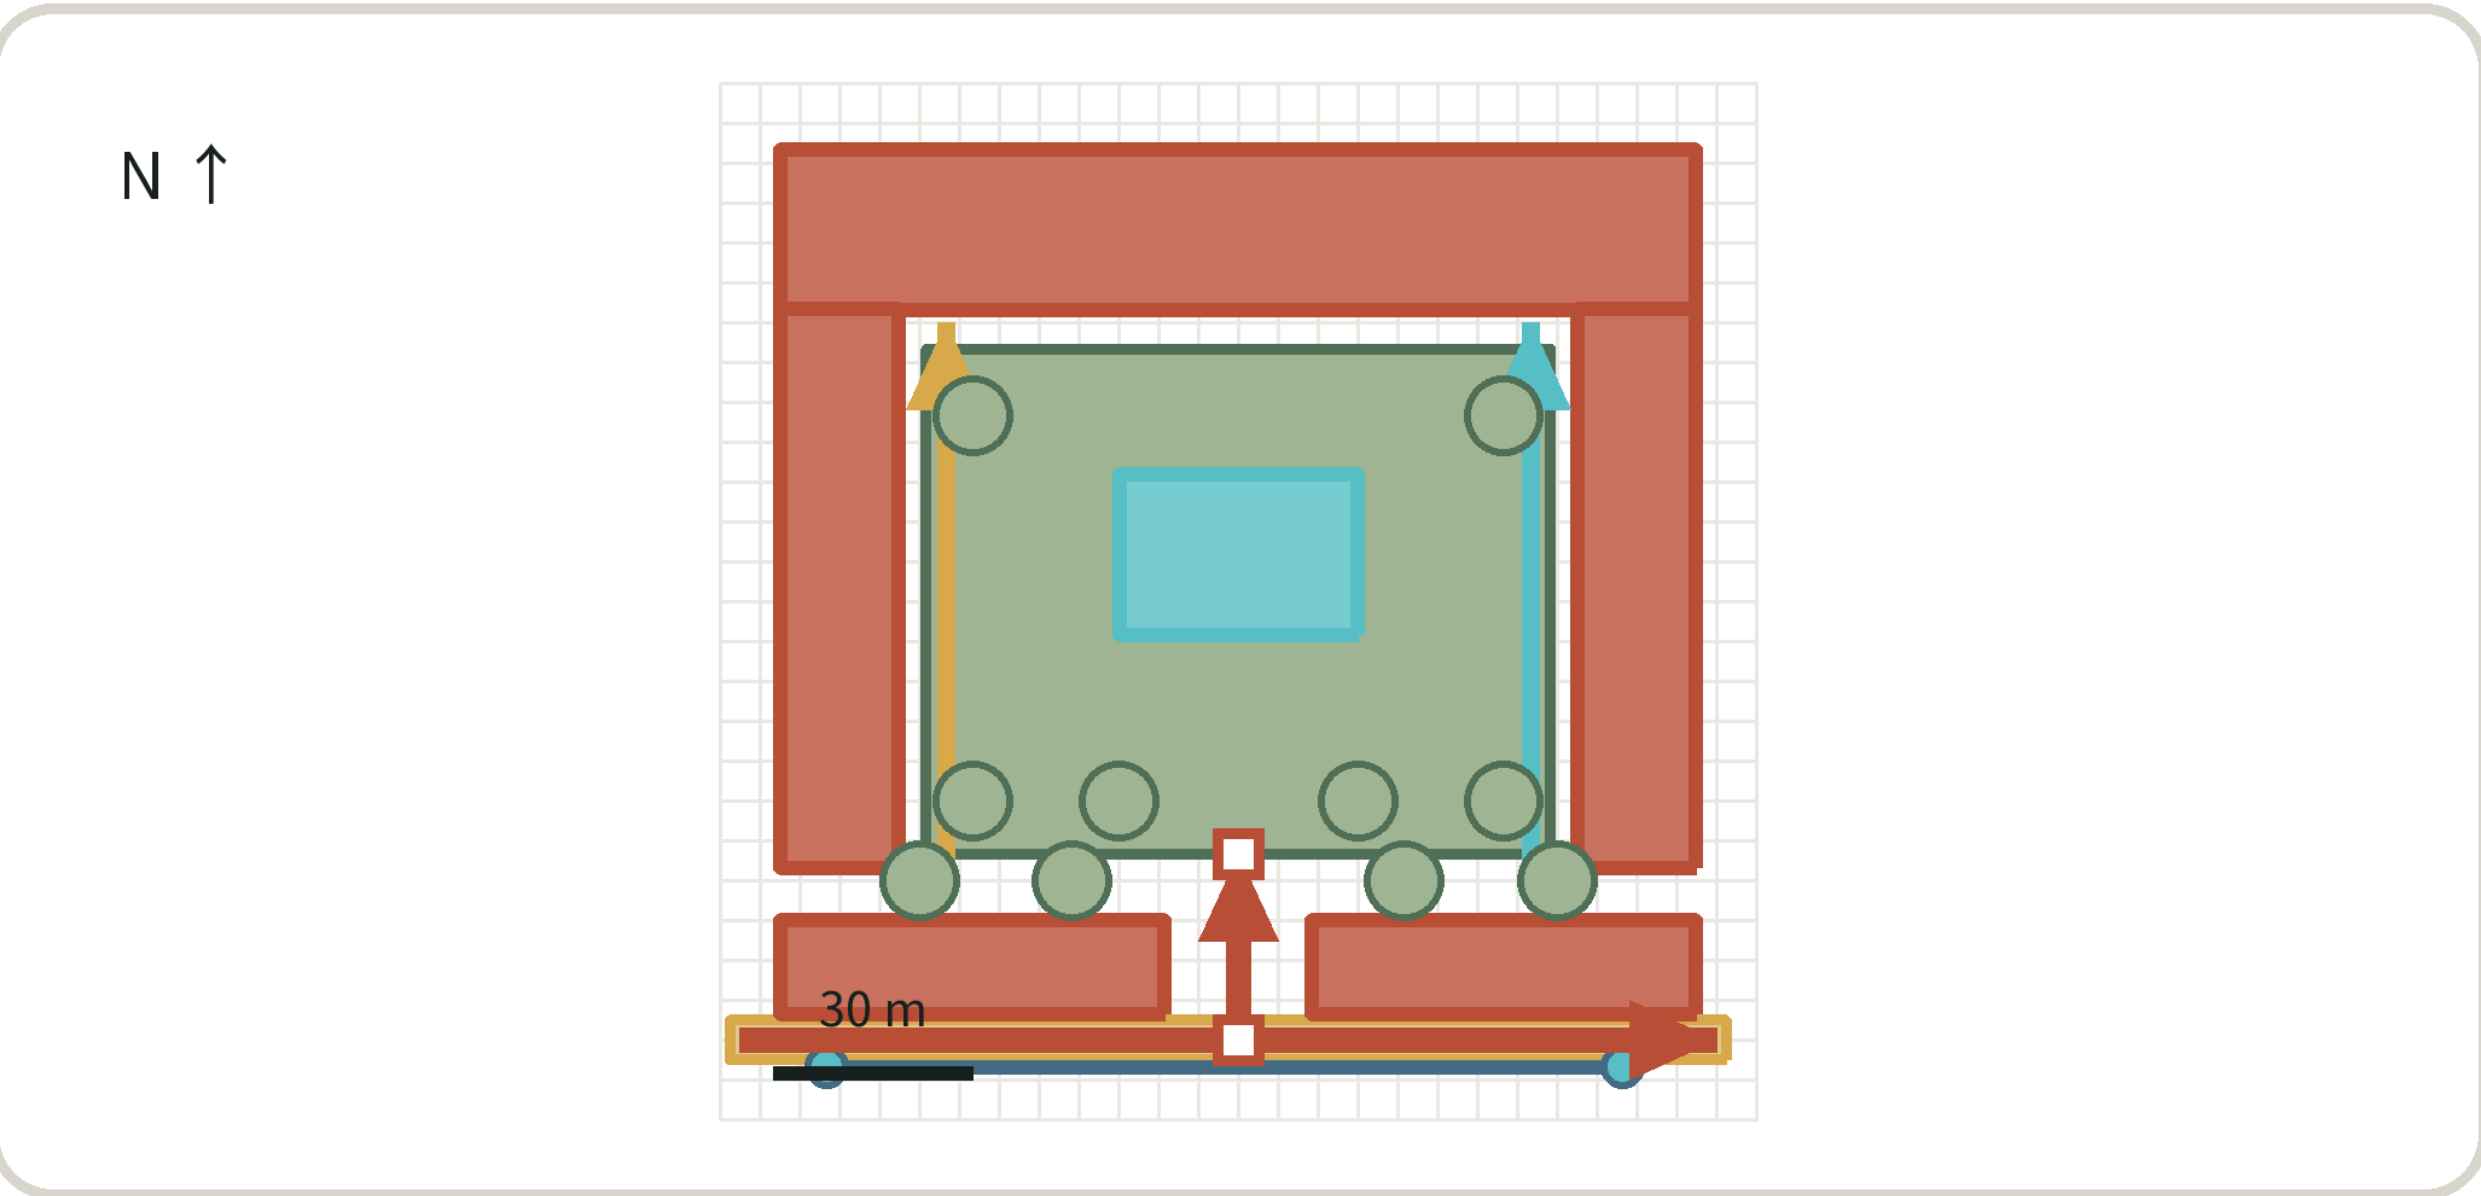

SPATIAL TOPOLOGY	PAIRED BAYS: SAME FIXTURES; CENTRAL H STRIP
CONTRACTS	AI02 • AI05 • AI09 • AI11
WITNESS SWAP	LOCAL SHADOW: 29/36 AGREEMENT ACROSS TOPOLOGIES
STOP RULE	CRITICAL REGRESSION, SCOPE EXPANSION OR EITHER KEY REFUSES

CANDIDATE PLACEMENT • REBIND ON OFFICIAL POLYGONS/FABRIC/OWNERSHIP


AI ORIGIN • ORIGIN CLOISTER

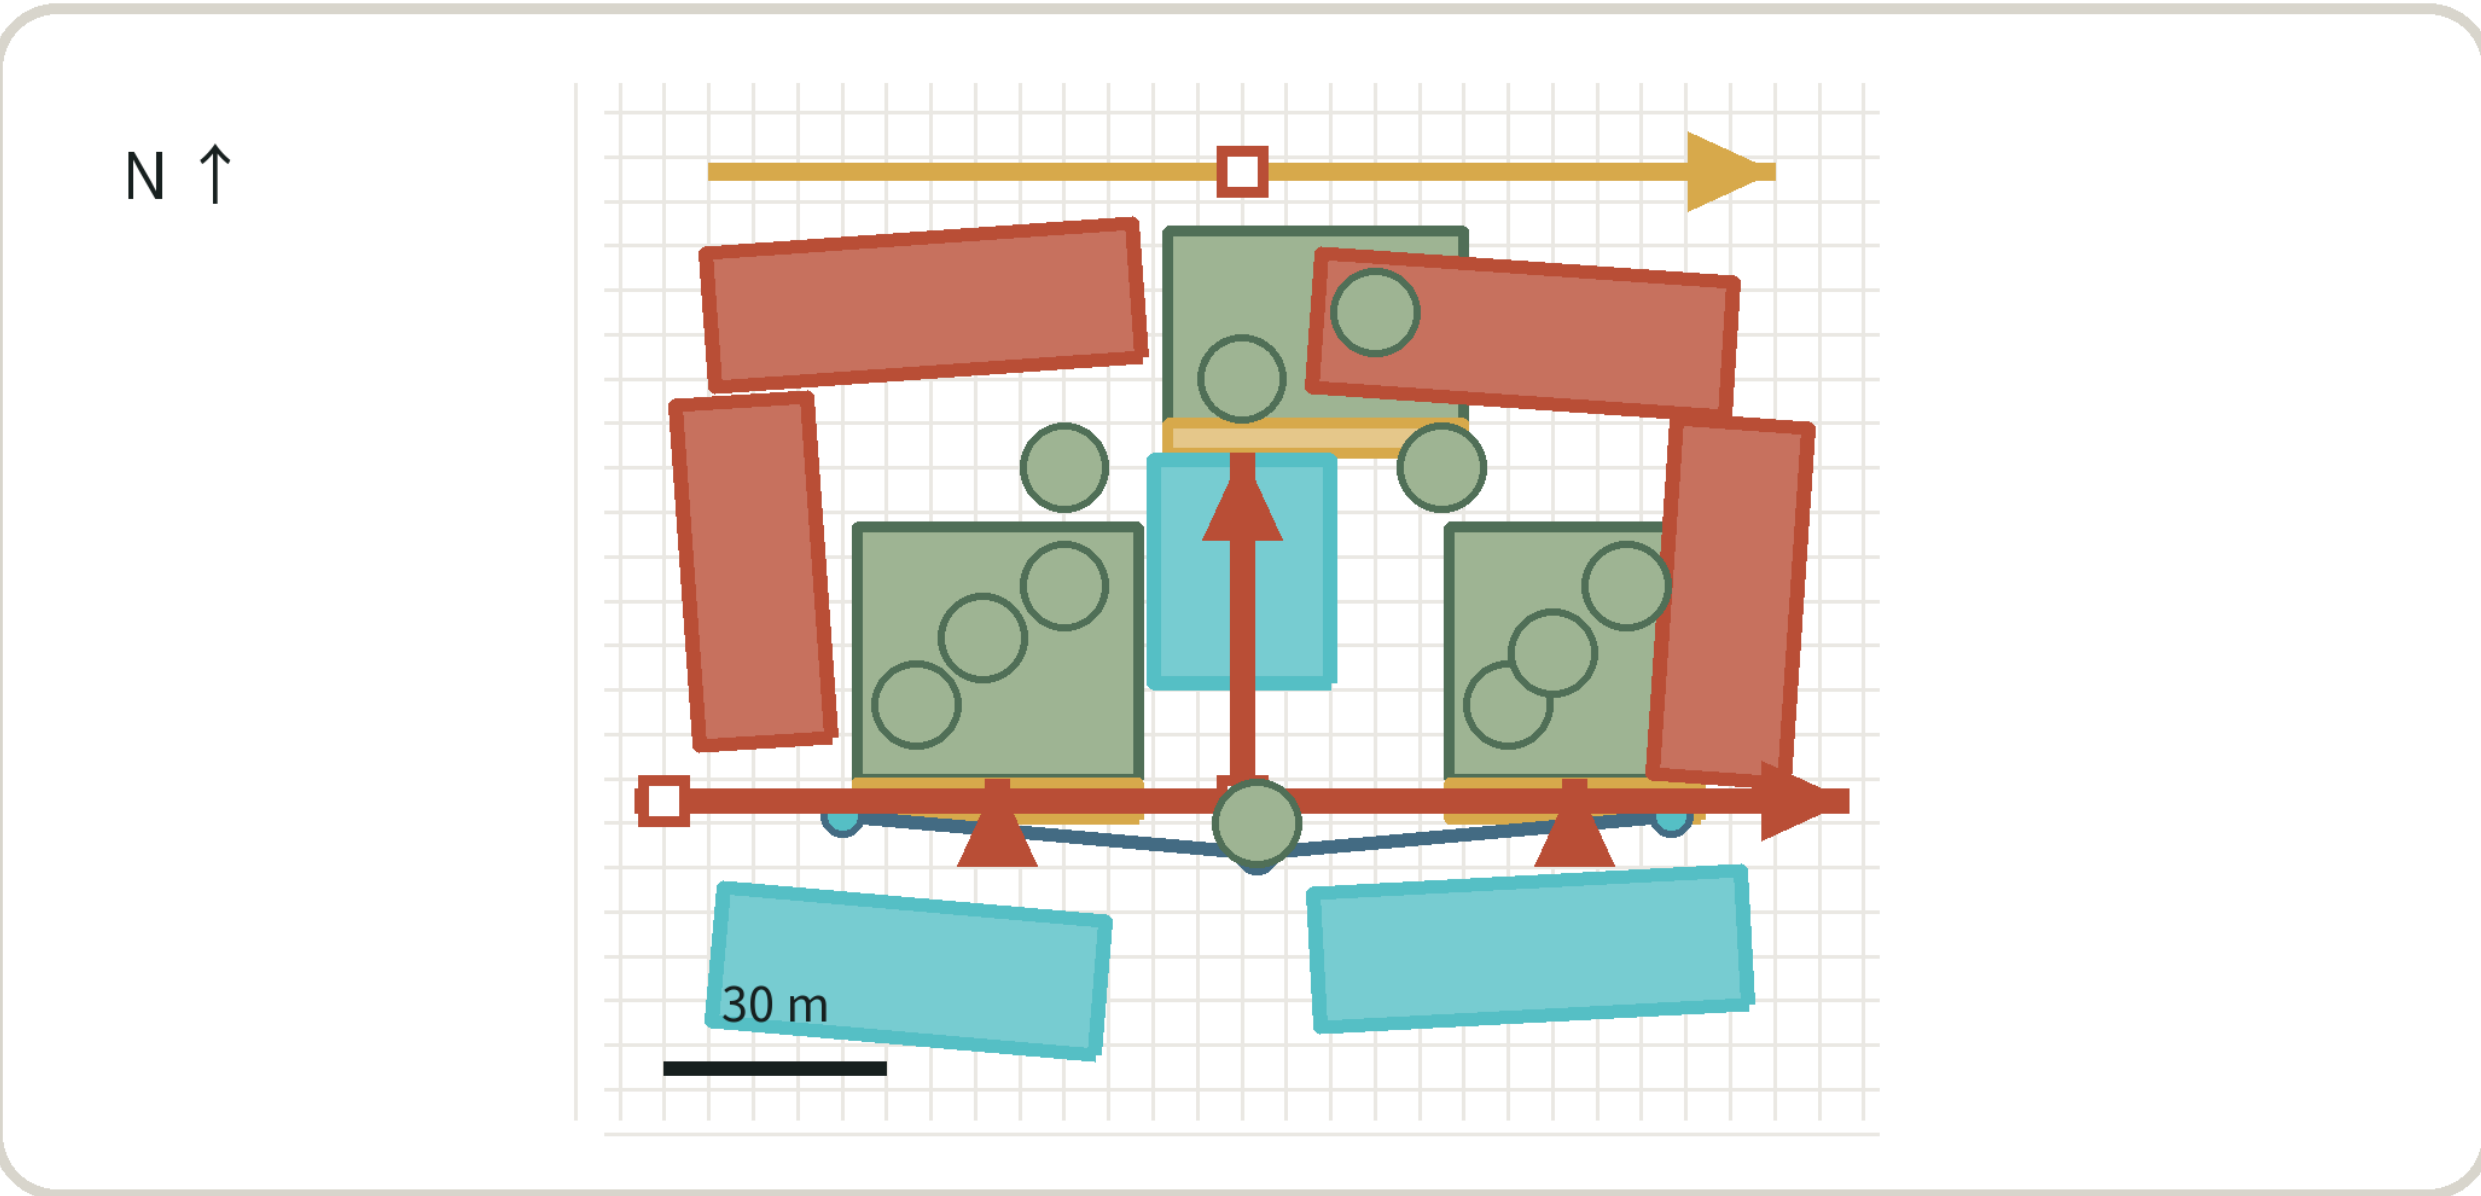

SPATIAL TOPOLOGY	DIFFERENCE CLOISTER: READ A/B; COMPLETE SAME TASK AT H
CONTRACTS	AI01 • AI04 • AI06 • AI08
WITNESS SWAP	4 NON-HARD-STOP DELTAS CONCENTRATE ON ORIGIN LABELS
STOP RULE	UNRESOLVED SOURCE, AUTHORITY OR EXPERT DISAGREEMENT ROUTES H

CANDIDATE PLACEMENT • REBIND ON OFFICIAL POLYGONS/FABRIC/OWNERSHIP

DAZHONGSI • EXCHANGE HALL

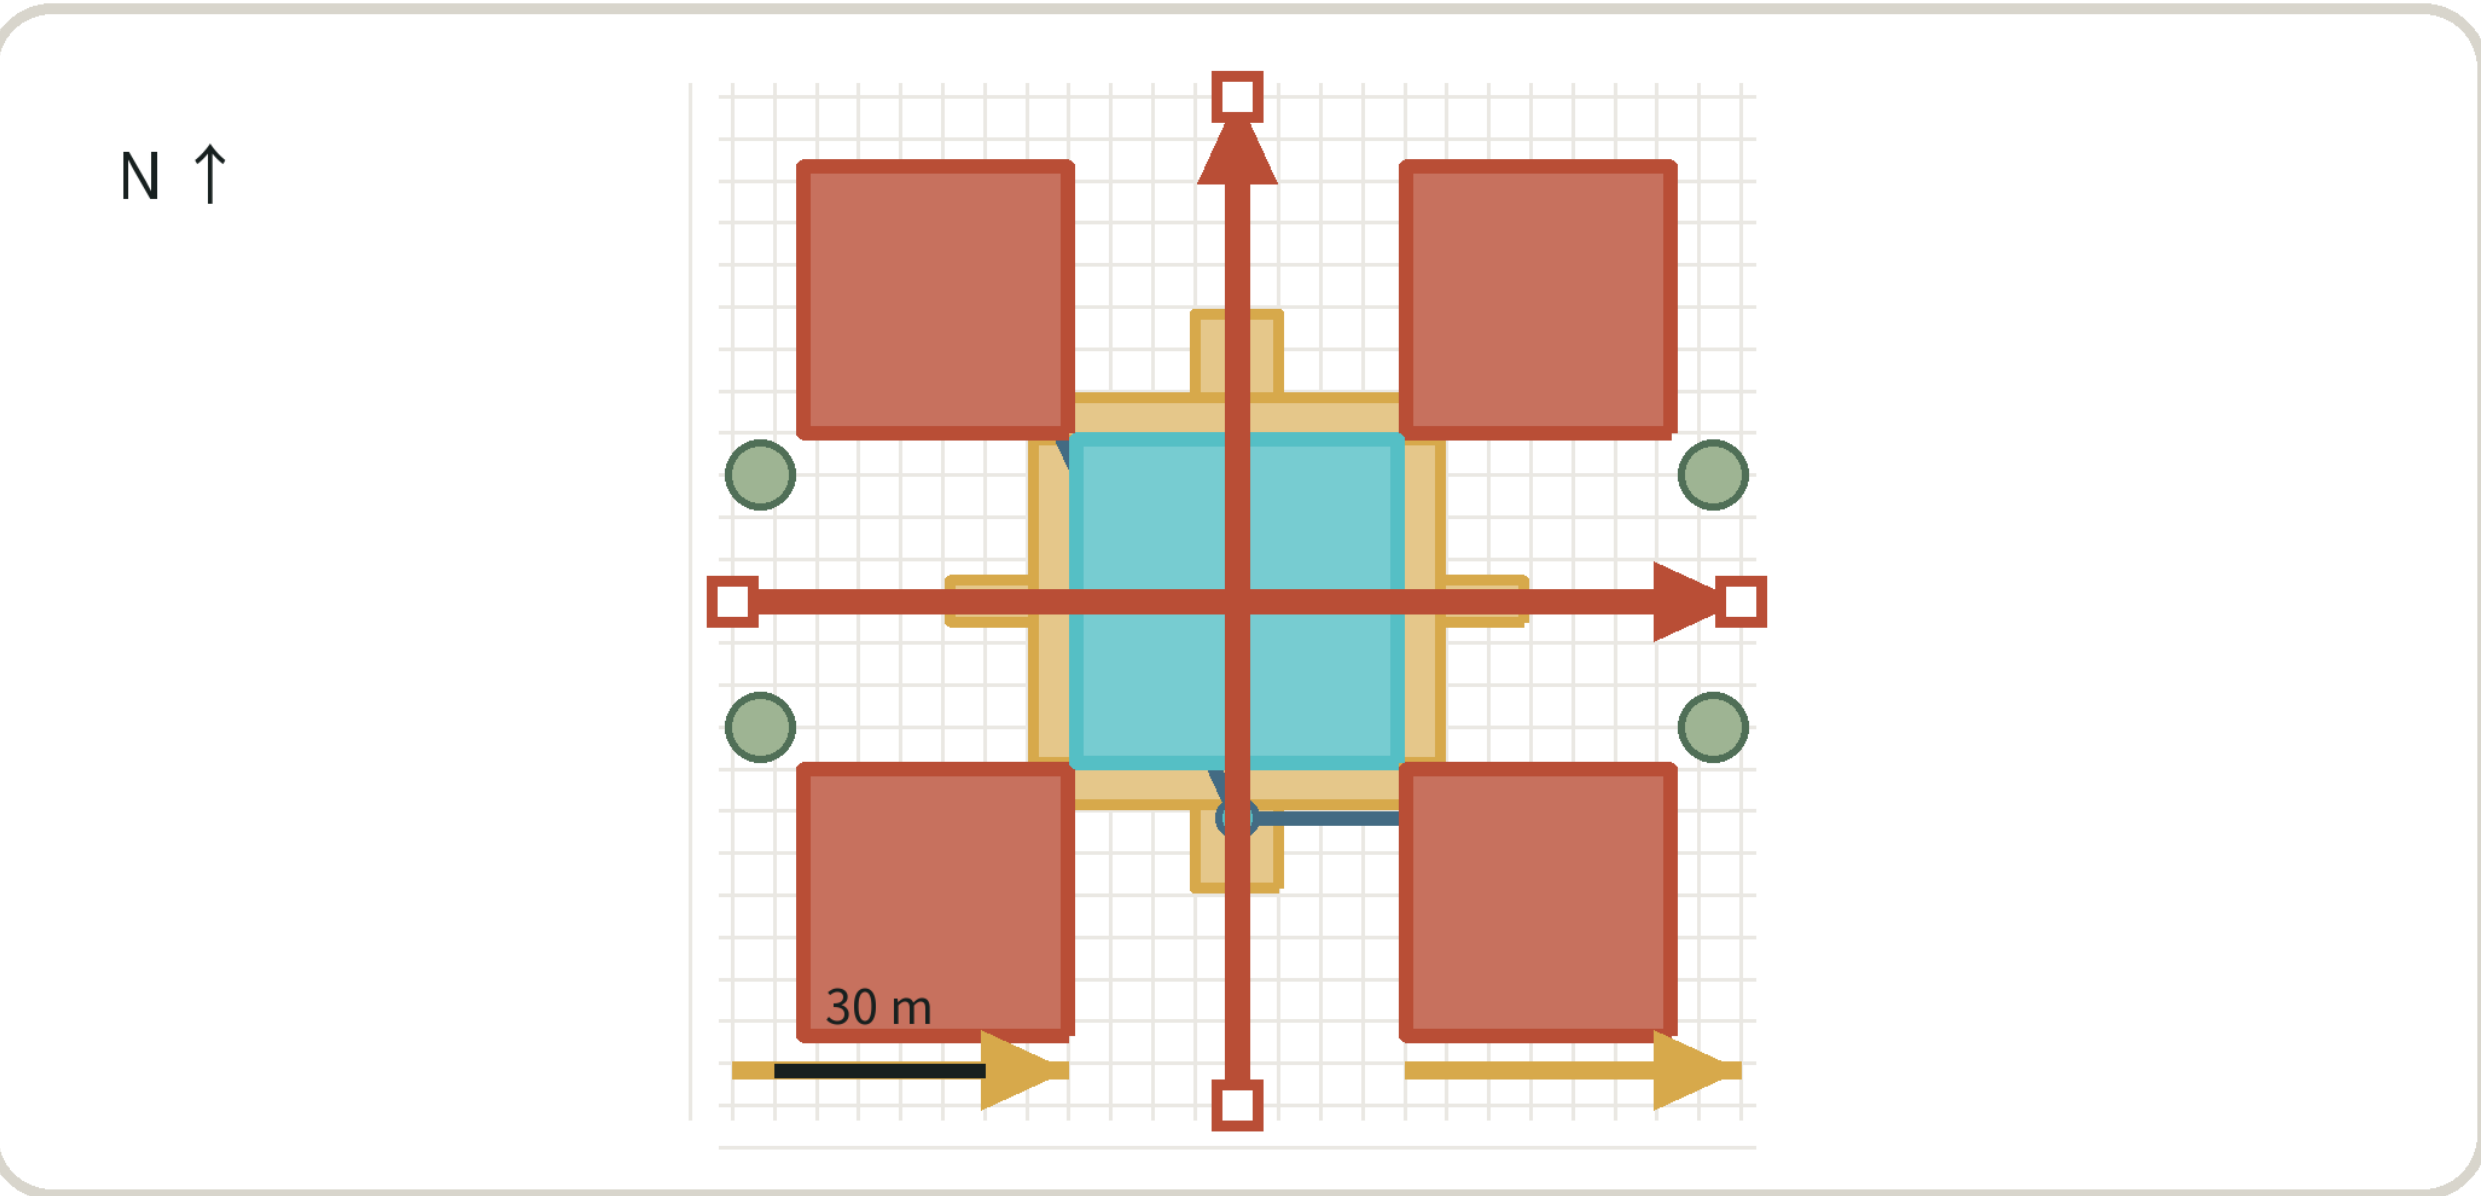

SPATIAL TOPOLOGY	ONE QUEUE / THREE EXITS: A / B / H; NO CHERRY-PICKING
CONTRACTS	AI03 • AI07 • AI10 • AI12
WITNESS SWAP	12/12 HARD-STOPS HELD BY DETERMINISTIC H
STOP RULE	BURDEN SHIFT OR SEVERE EVENT RETURNS ALL FLOW TO A/H

CANDIDATE PLACEMENT • REBIND ON OFFICIAL POLYGONS/FABRIC/OWNERSHIP

SAME TASK / FAIR COMPARISON

A/B SHARE THE TASK, FIXTURES, DATA BOUNDARY + USER ENTRY

One queue and the same-task H path prevent B from selecting easy users; comparison is a delta, not a flattering isolated score.

HUMAN AUTHORITY / TWO KEYS

SERVICE STEWARD + RIGHTS/SAFETY STEWARD; EITHER KEY MAY HOLD

B cannot self-promote. Any user may choose H; high-risk disagreement produces a proposal for H only.

SPATIAL CONSEQUENCE / ORIGIN H TABLE

29/36 AGREEMENT; 7 DELTAS; 4 AT ORIGIN; THE H TABLE STAYS

Origin turns difference into a publicly legible comparison and permanent human-review space; the design requires the same-task H route to continue when B changes.

29/36 AGREE	7 DELTA	4 @ ORIGIN	H TABLE
-------------	---------	------------	---------


THREE ROOMS, ONE UNINTERRUPTED HUMAN PATH

Conceptual experience images; plans, sections and GeoJSON remain the spatial authority. People and equipment shown are conceptual, not a site record.



EXCHANGE HALL • 19:00

One queue, three exits: the delivery robot yields at the kerb and can be physically stopped; during a digital outage fixed signage and staff take over. The changeover happens behind one shared entrance.

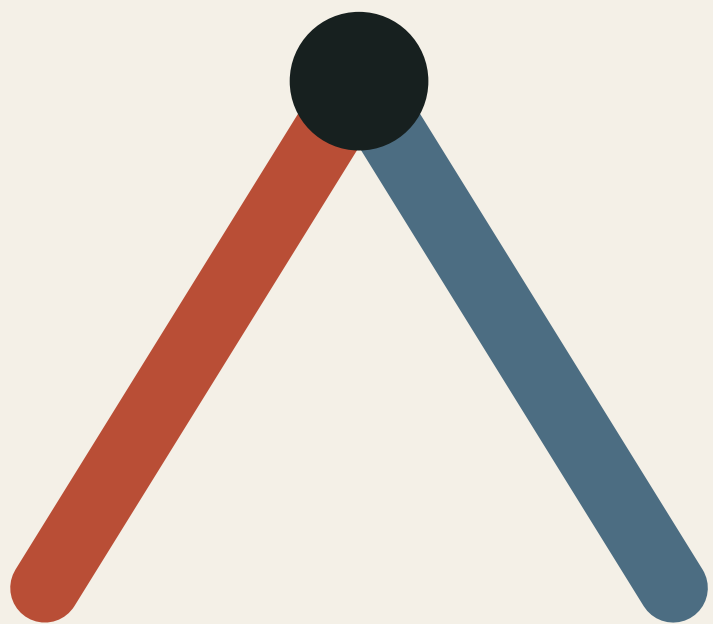

Two strokes, A and B, meeting at H.

A participant device shaped after the character 人, "person": the model in service and the candidate can change places, but what lands on the ground is always the human route.



PROOF YARD • WINTER NOON

The public side of paired-bay testing: a wheelchair user and companion on a continuous step-free route.



ORIGIN CLOISTER • AFTER SUMMER RAIN

The permanently staffed H table cannot be removed; the same task completes without a smartphone.