


Site Overview & Conceptual Network

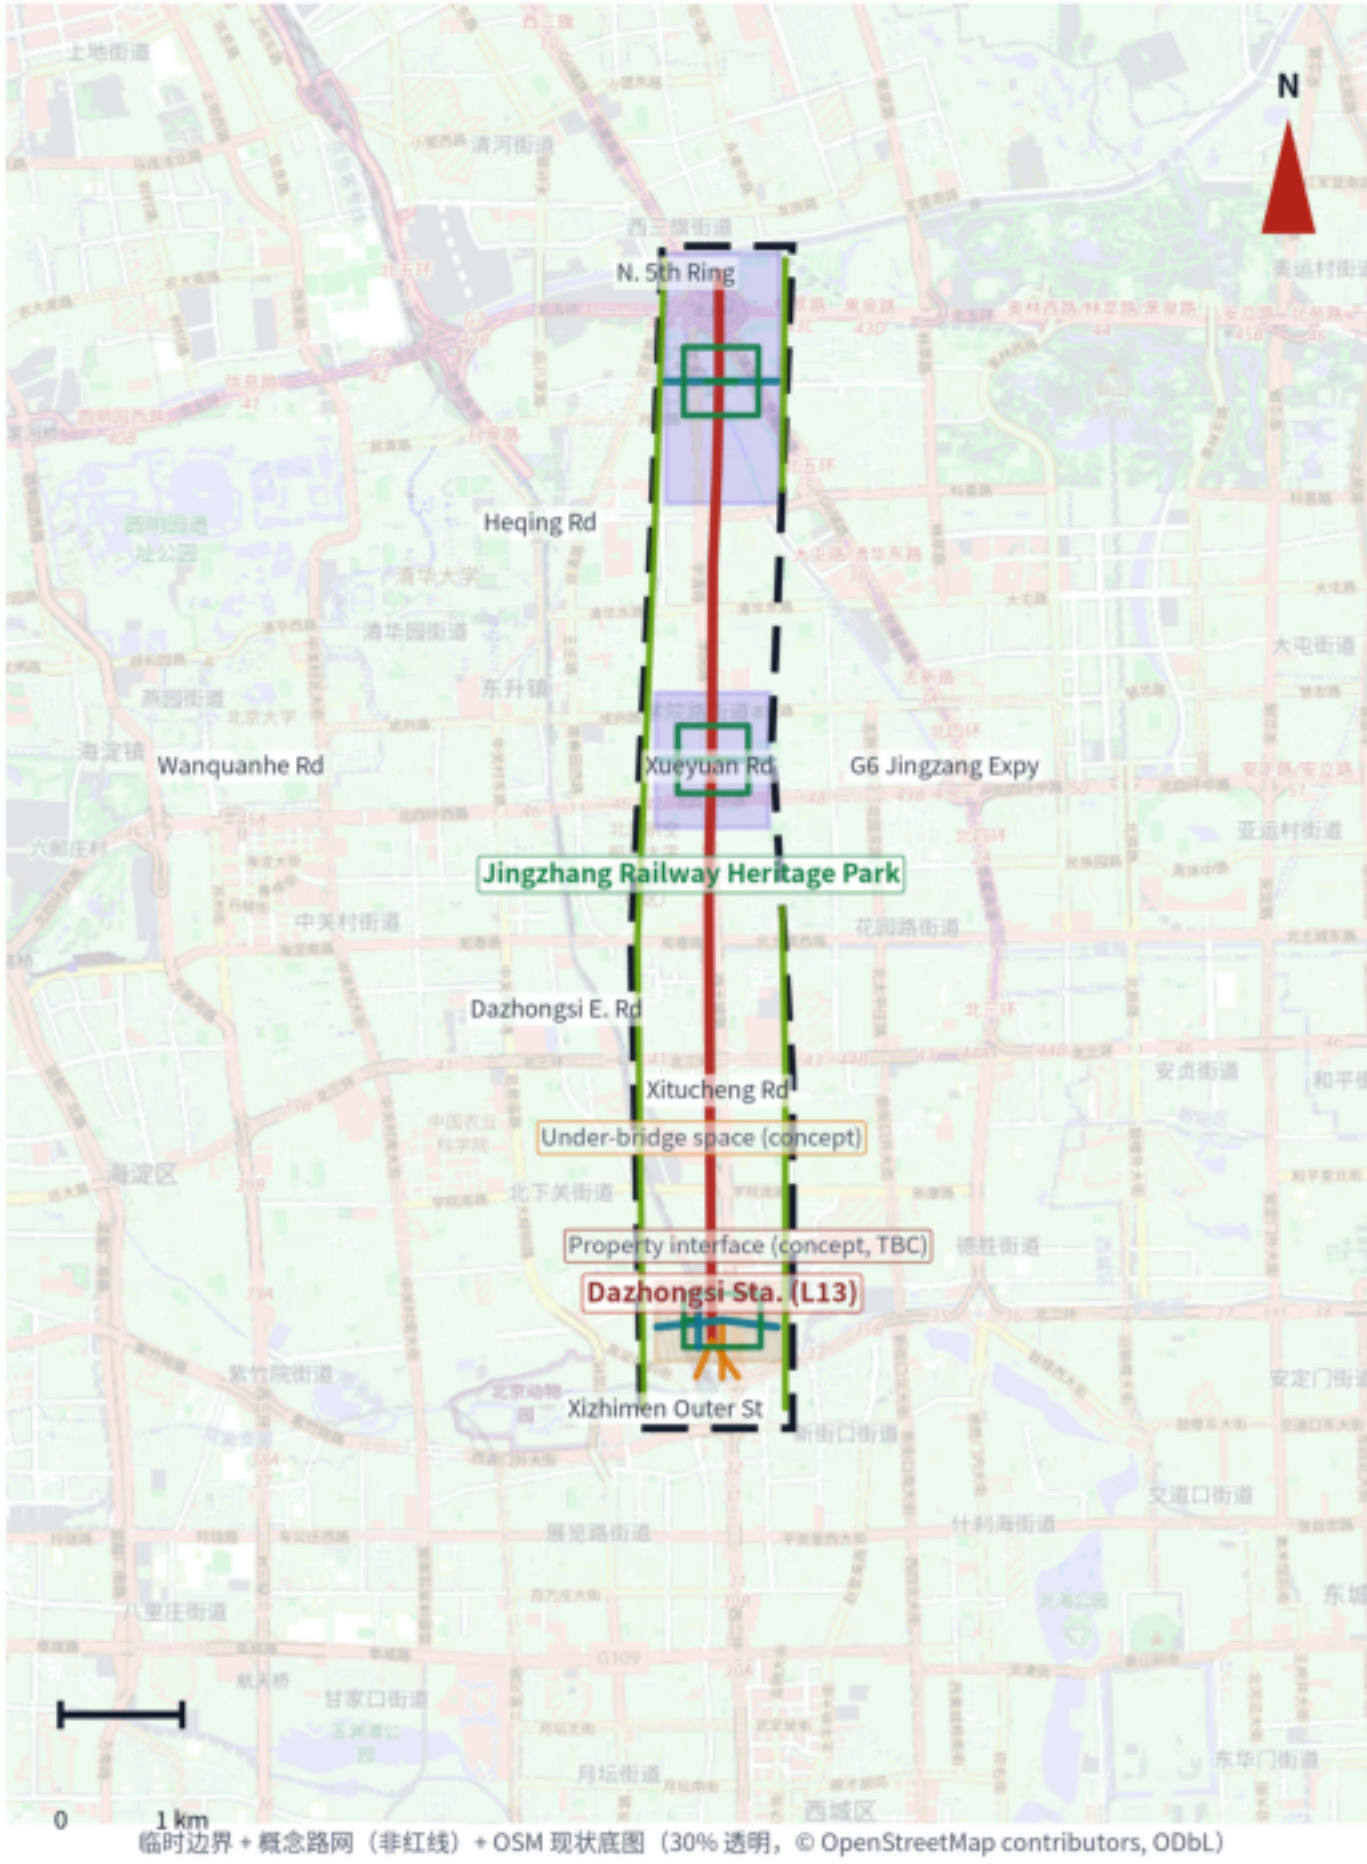

临时边界 + 概念路网（非红线）+ OSM 现状底图（30% 透明，© OpenStreetMap contributors, ODbL）

图例 Legend

- 黏菌主静脉 primary vein
- 次级支脉 secondary branch
- 慢行环 local loop
- 京张绿廊 green corridor
- 站点接驳 station feeder
- 众智园片区
- 北京AI原点社区
- 大钟寺AI产业聚集区

边界/路网/片区为算法模拟概念与临时范围（非实测、非审批几何）；道路/站点/公园名称基于 OSM 公开数据与公告文字四至（位置示意）；




最优效率 optimal eff. Run7 冻结 frozen 骨架总长 skeleton 关键节点覆盖 cover Plan03 UDS 透水铺装率 permeable 绿色渗透率 green pen.


PROVISIONAL BOUNDARY — CONCEPTUAL DESIGN ONLY
临时边界 — 概念设计 — 非审批范围
NOT FOR OFFICIAL USE OR ANY OTHER PLANNING DOCUMENT

Method: Bio-Physarum + NSGA-II

Real Physarum 167-edge skeleton (method validation)

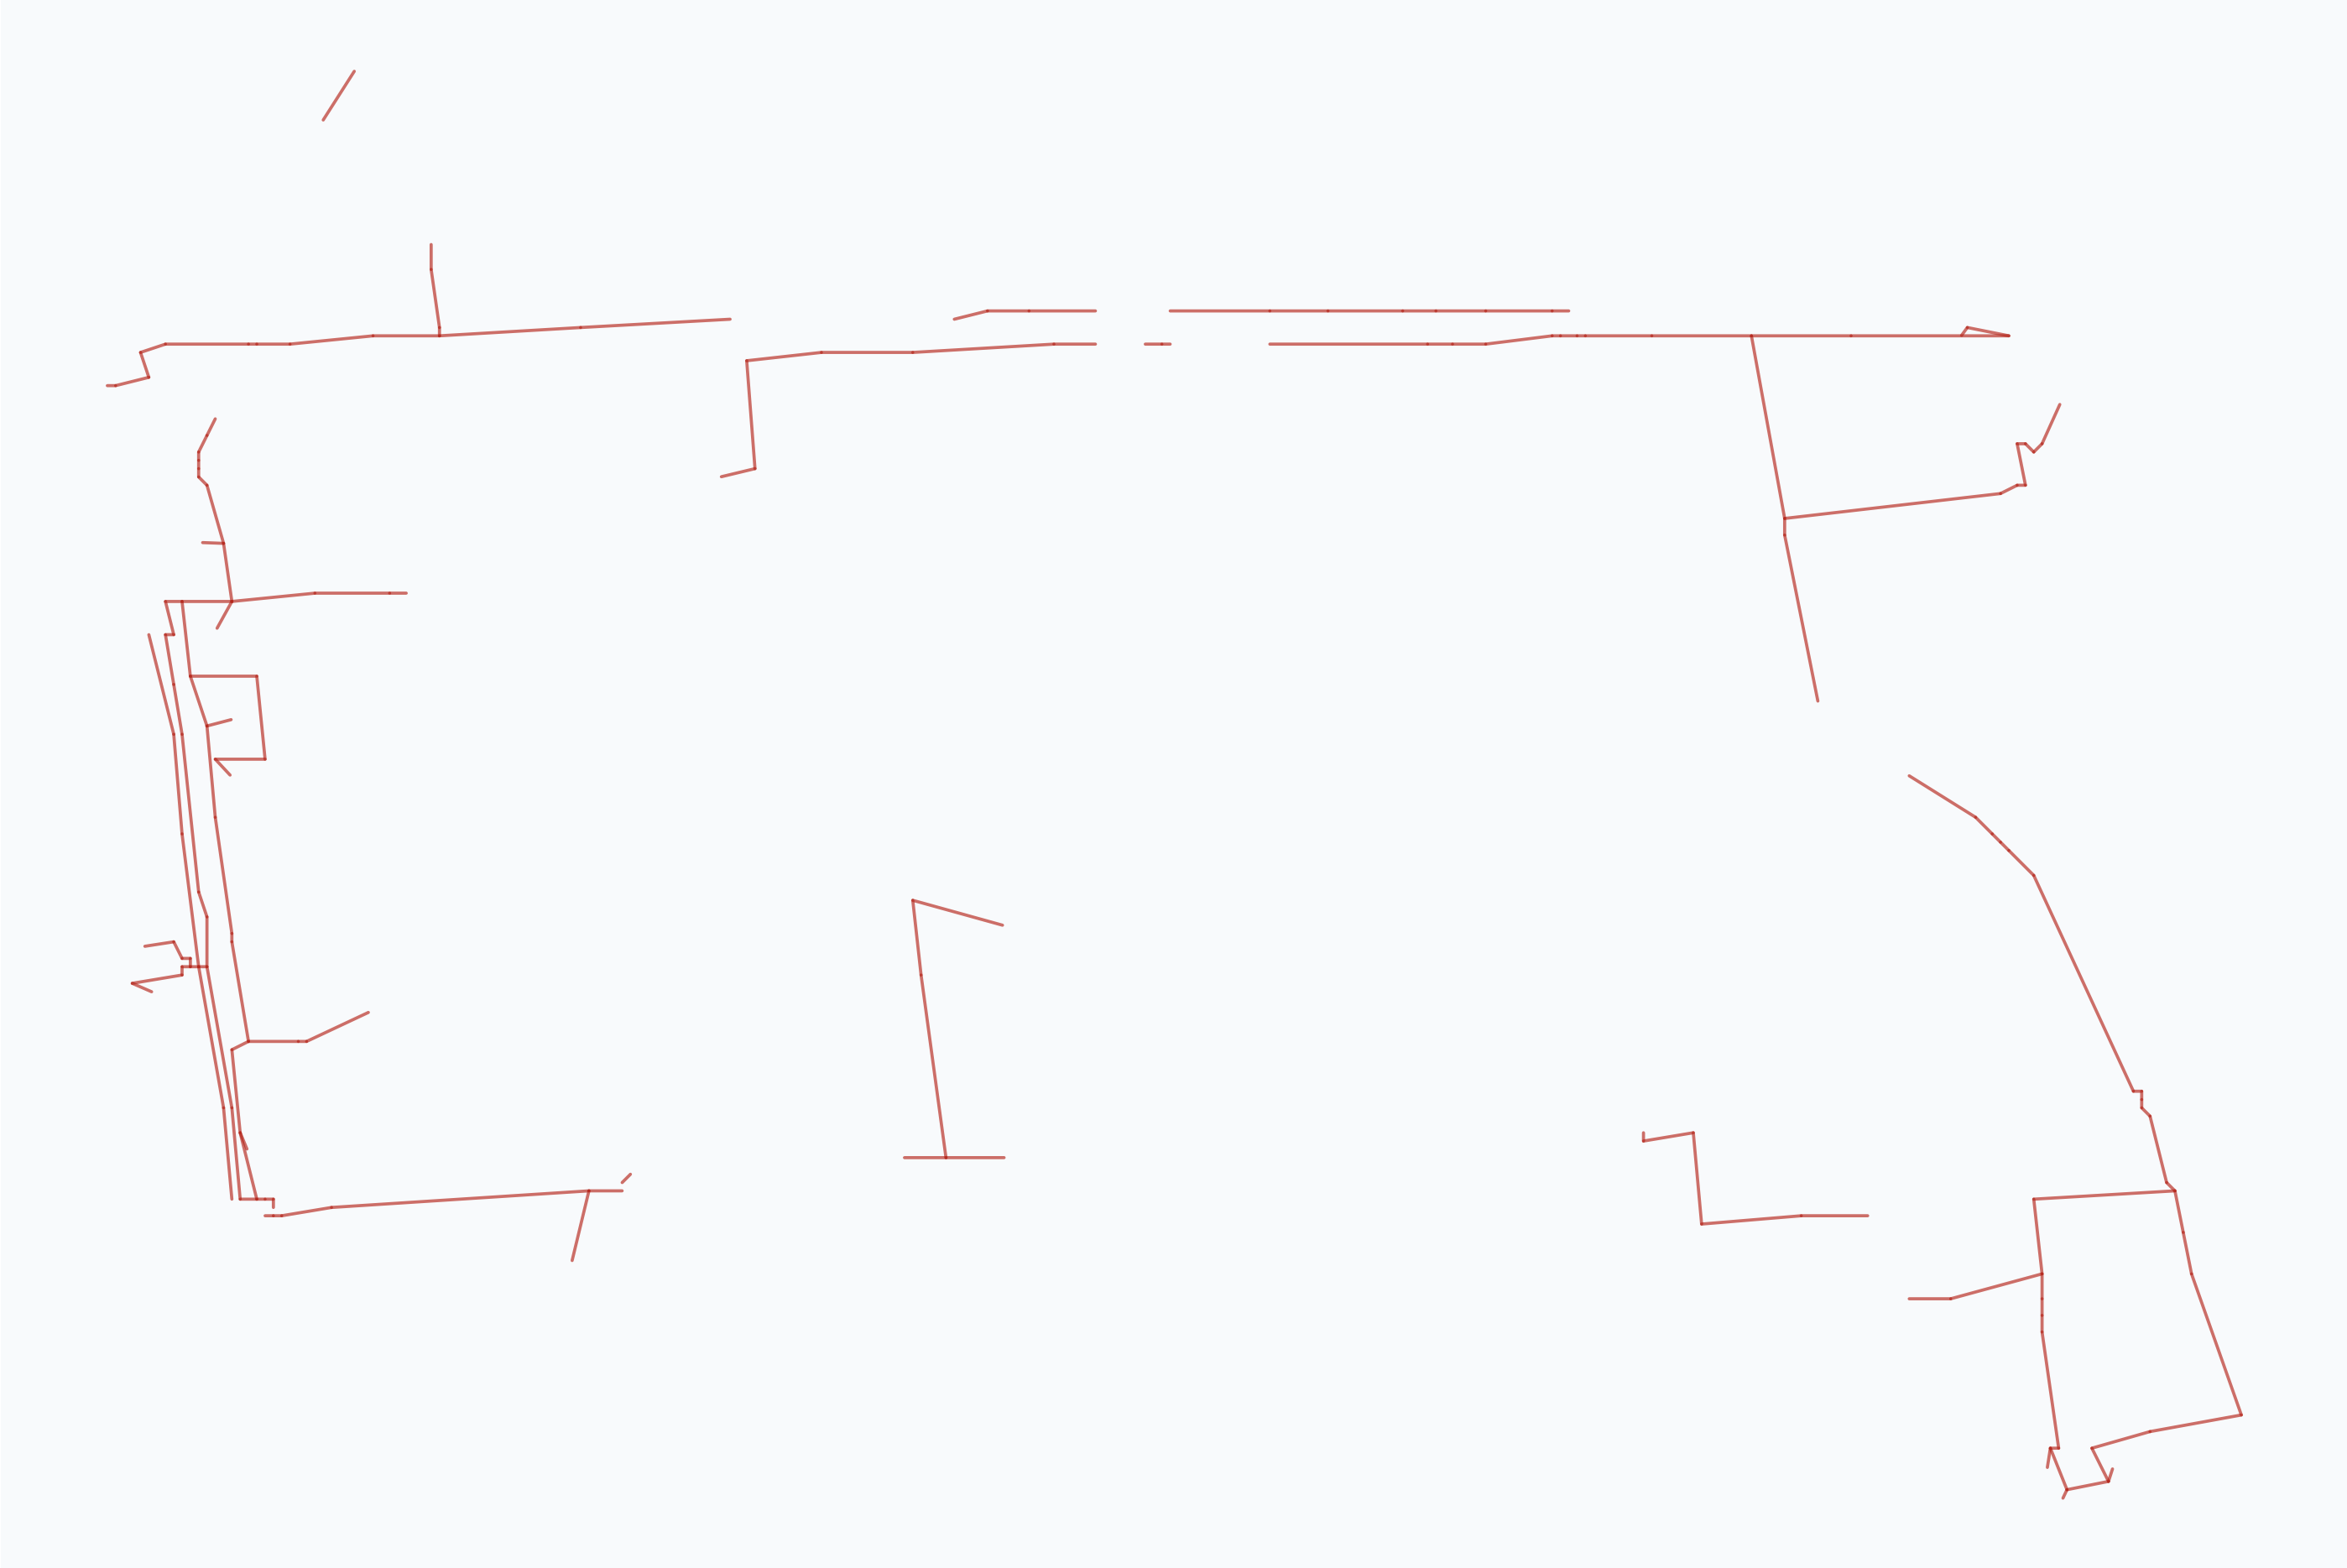

Metrics recalculation: efficiency (single axis)

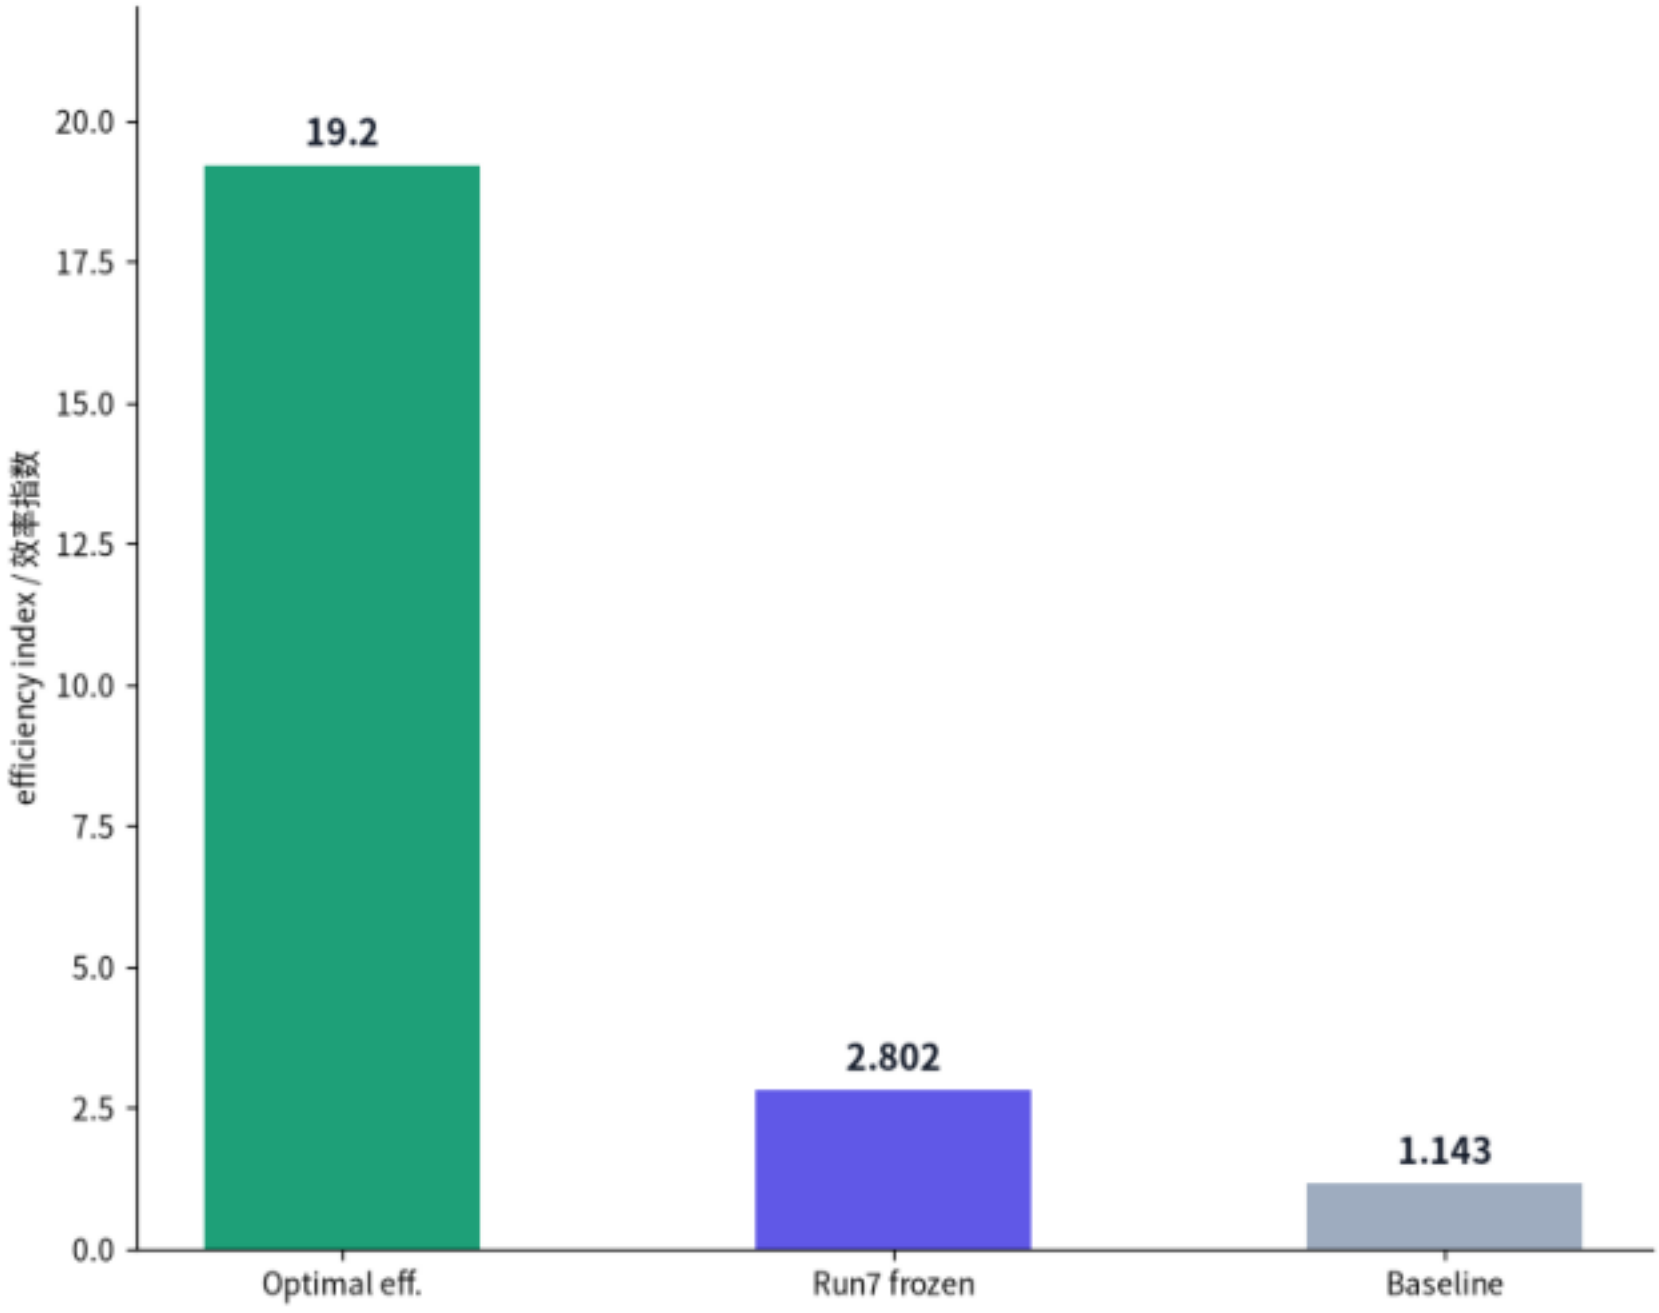

Plan03 urban-integration UDS 80.34 recommended; heritage objective f3≡f2 degenerates to cost
Method validation (real Physarum run): 167-edge network / efficiency 19.20 / heritage objective f3≡f2 (degenerates to cost; no independent

Heritage g1 hard-constraint gate (count)

0 crossings


constraint satisfied
(count, separate axis)

not an efficiency metric;
no independent site
heritage conclusion

PROVISIONAL BOUNDARY — CONCEPTUAL DESIGN ONLY
NOT AN OFFICIAL REDLINE OR APPROVED PLANNING DOCUMENT
临时边界 — 概念设计 — 非审批红线

Global Benchmark Cases

案例	地点	核心做法（公开报道）	借鉴/警示
Sidewalk Labs Quayside	Toronto	Sensing, data trust (2017-2020)	Governance / caution
Masdar City	Abu Dhabi	Low-emission, passive cooling, PRT	Low-carbon + feeder
Songdo IBD	Incheon	Reclaimed town, U-City sensing	New infra reserve
Amsterdam	Netherlands	PPP, living-lab	Incremental + governance
Xiong'an	Hebei	CIM twin, blue-green, tunnels	Twin + blue-green

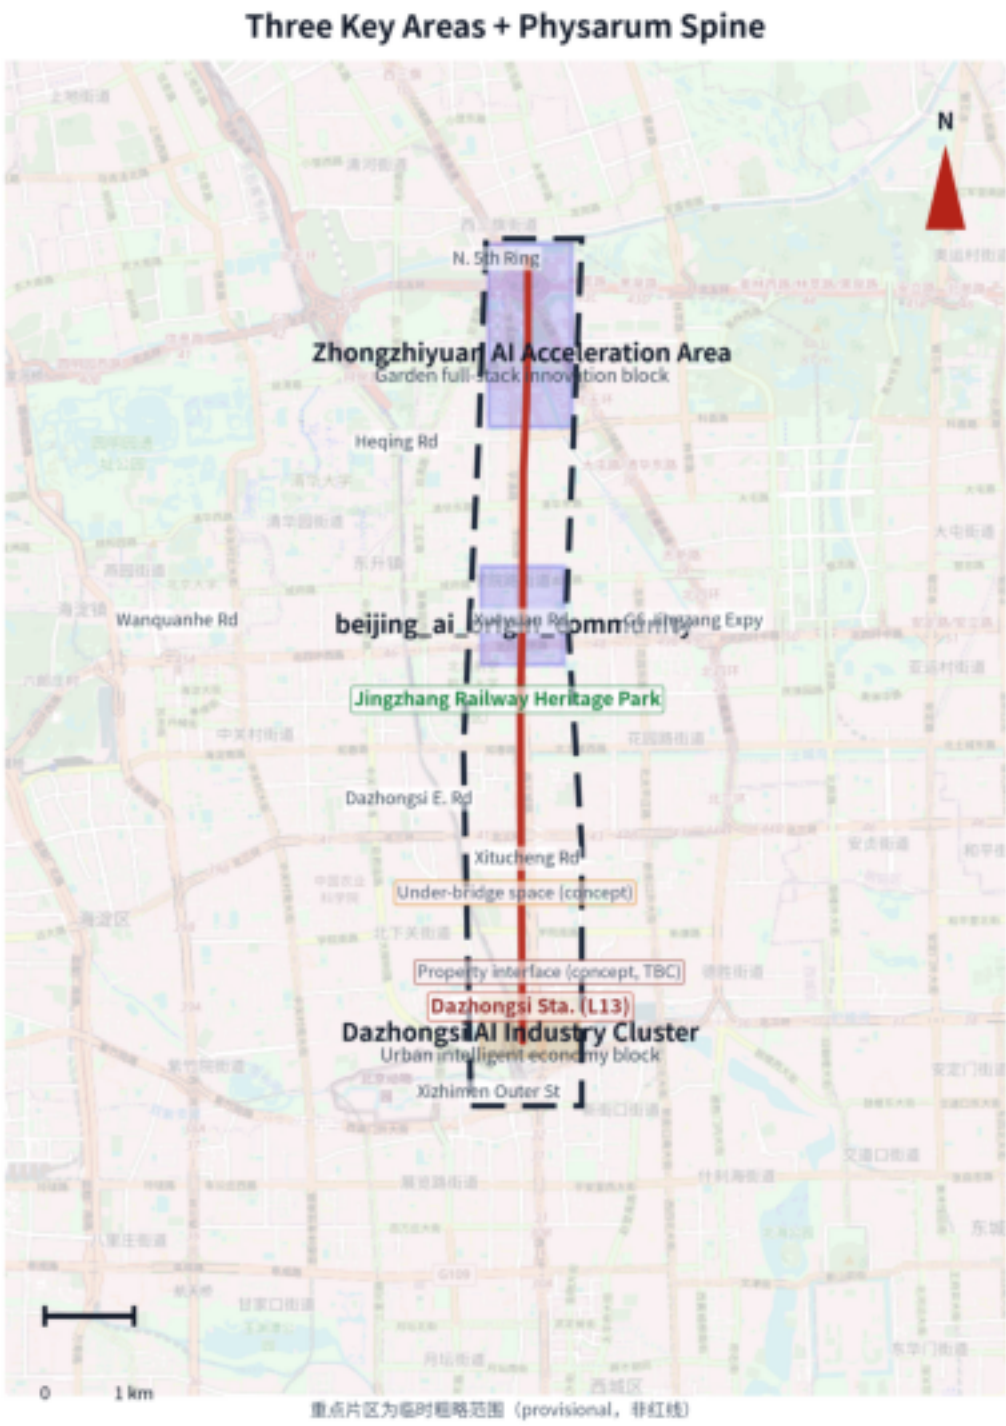

图例 Legend

- 众智园AI自主创新加速区
- 北京AI原点社区
- 大神寺AI产业聚集区
- 黏菌主静脉 primary vein
- 场地临时边界（虚线）

三处片区边界为公告面积+文字四至推定的临时范围，非官方 polygon、非红线；站点坐标为 OSM 公开数据。

PROVISIONAL BOUNDARY, CONCEPTUAL DESIGN ONLY
临时边界 — 概念设计 — 非规划红线

Test Validation Scenarios

场景	验证对象	检验依据	关键目标
T-01 Dazhongsi TOD	Four-quadrant link & feeder	GB 50763-2012 / GB/T 51328	Barrier-free flow
T-02 Xiaoyue stormwater	Blue-green + permeable	Sponge guide / GB 50014	Permeable 69.1% / 25.2%
T-03 AI Origin access	Campus-park stitching	GB 50763-2012	Loop covers + continuous

Implementation Matrix (suggestive)

项目	建议责任主体	建议周期	暂停/退出
JZ-01 Slow stitching	Transport + park	Near	Pause if unsettled
JZ-02 Qinghe interface	Water + park	Mid	Exit if flood unmet
JZ-03 Conversion street	University + bureau	Mid	Pause if dispute
JZ-04 Four-quadrant	Rail + transport	Mid	Postpone if mismatch
JZ-05 Edge computing	Bureau + operator	Long	Exit if absent
JZ-06 Recalibration	Design + university	Long	Keep 'to be confirmed'

Accessibility Matrix (GB 50763-2012)

画像	无障碍与包容性需求	空间响应
Open-source dev	Night collaboration safety	Barrier-free entrance/toilet, lighting
Startup team	Members with disabilities	Barrier-free office/test space
Enterprise visitor	International / reduced mobility	Multilingual signage, elevator
Nearby resident	Elderly/children/disabled	Curb ramps, tactile, seats
Univ. teacher/student	Disabled connectivity	Barrier-free stitching, point

Risk, Copyright & Compliance

• Real Physarum lies ~2-3 km west of provisional boundary (~140 m overlap); no translation, no fabricated redline.


• Heritage protection is editable_by_agent=false; official geometry missing, f3≡f2 (heritage degenerates to cost).

• No claim of official approval, approved plan, final ownership, or guaranteed implementation.

• HTML loads no remote scripts/tiles/fonts/iframes/forms/APIs.

• Appeal/redress: discover-register-rectify-revisit loop (suggestive).

Parameter sensitivity — Bio-Physarum + NSGA-II (real runs, method validation)

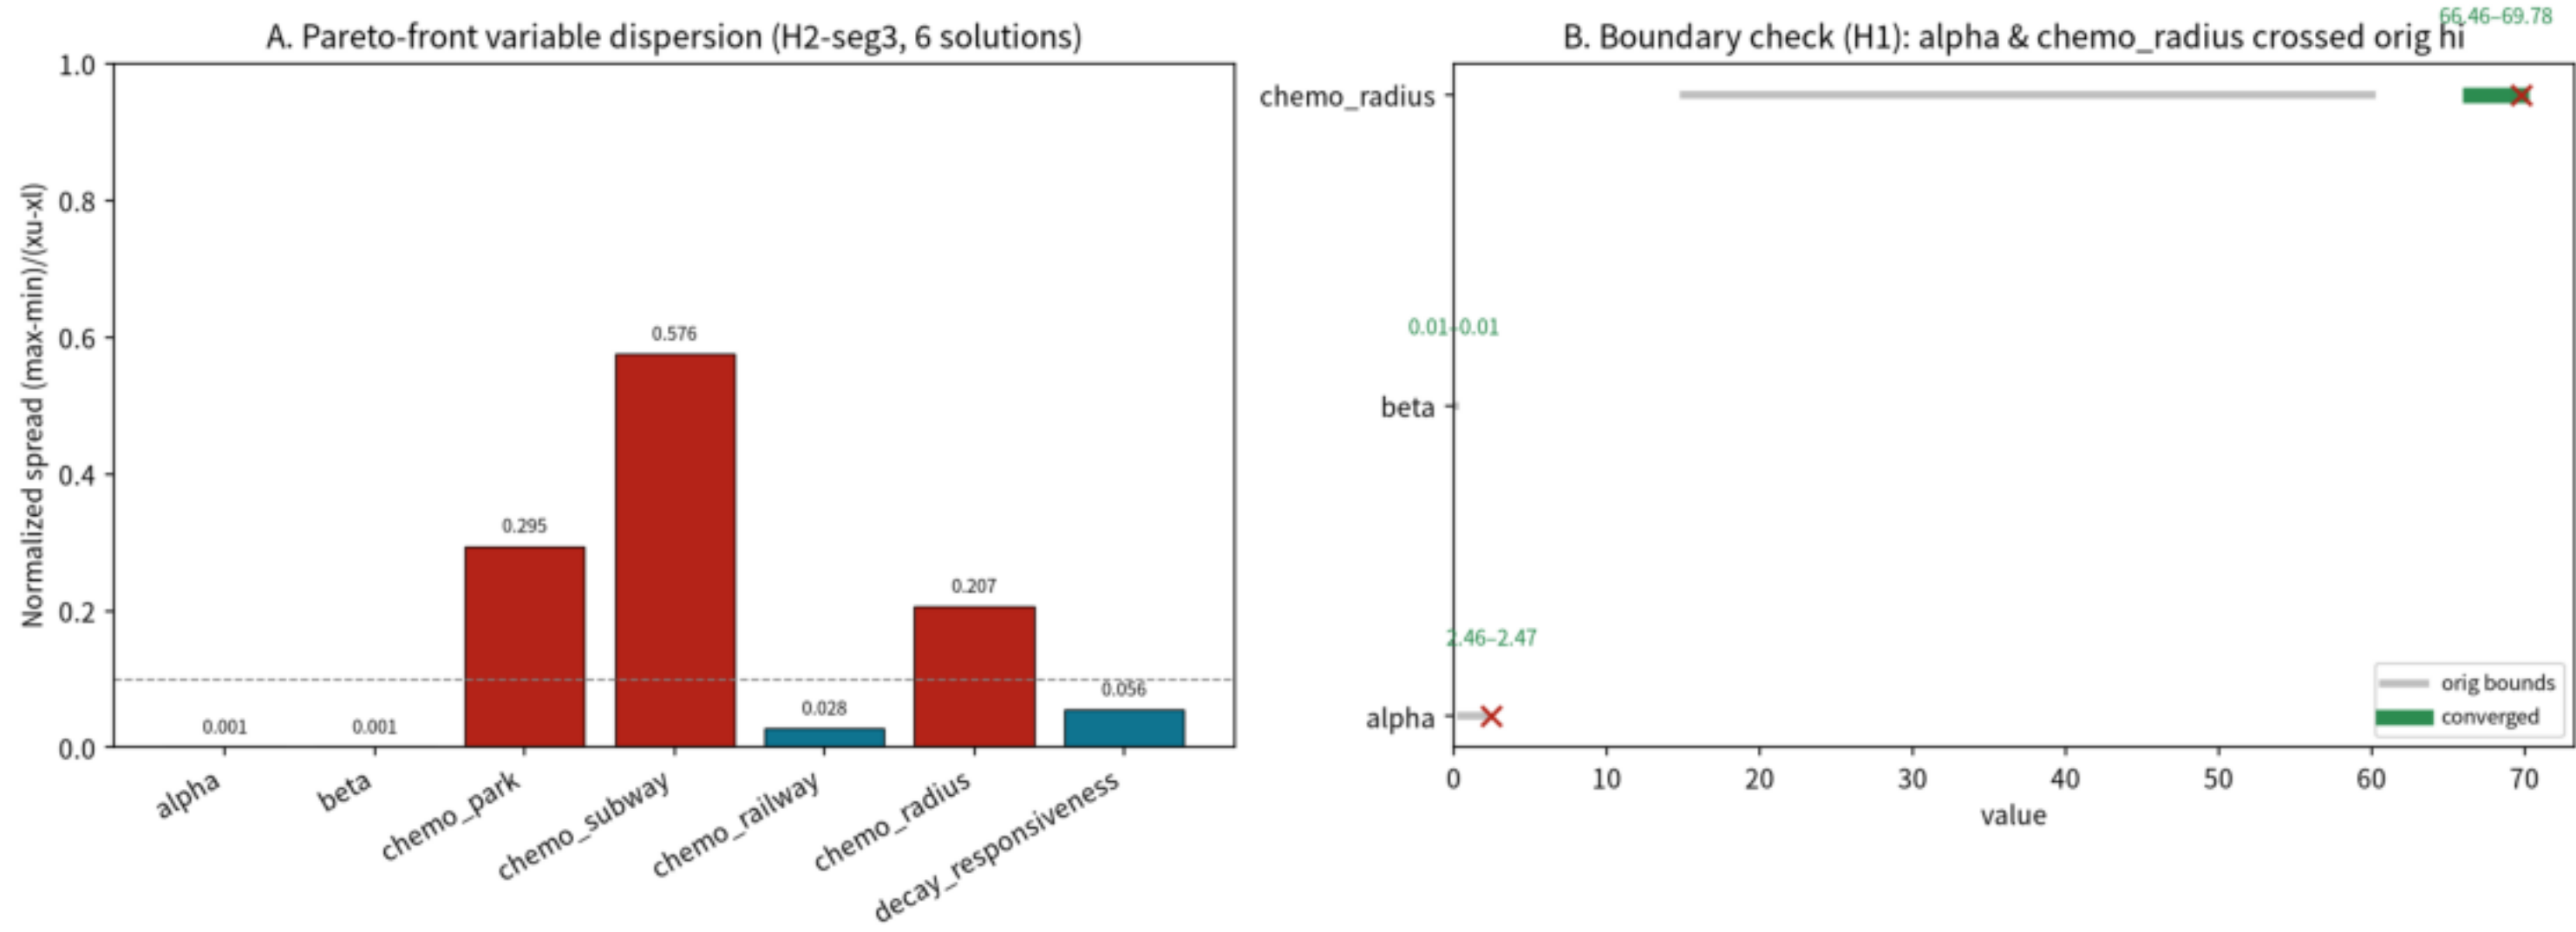

Cost Breakdown (suggestive)


等级	长度(m)	单价(元/m)	造价(万元)
Arterial	740.2	8000	592.2
Secondary	1744.1	5000	872.0
Branch	3679.9	3000	1104.0
Micro	2648.8	1500	397.3
Total	8813.0	—	2965.5

Avg 3365 CNY/m; municipal road only, excl. utility/rail/demo (suggestive)

Policy Alignment (suggestive)

项目	政策/标准依据 (真实)	待确认
JZ-01	GB 50763-2012 / barrier-free reg	ownership
JZ-02	Sponge guide / GB 50014	blue line
JZ-03	Beijing renewal reg (suggestive)	clauses
JZ-04	GB/T 51328 / GB 50763	station
JZ-05	New-infra policy (to confirm)	regulator
JZ-06	京政发〔1984〕128号	map/redline

Suggestive phasing gantt (6 projects x 3 phases)

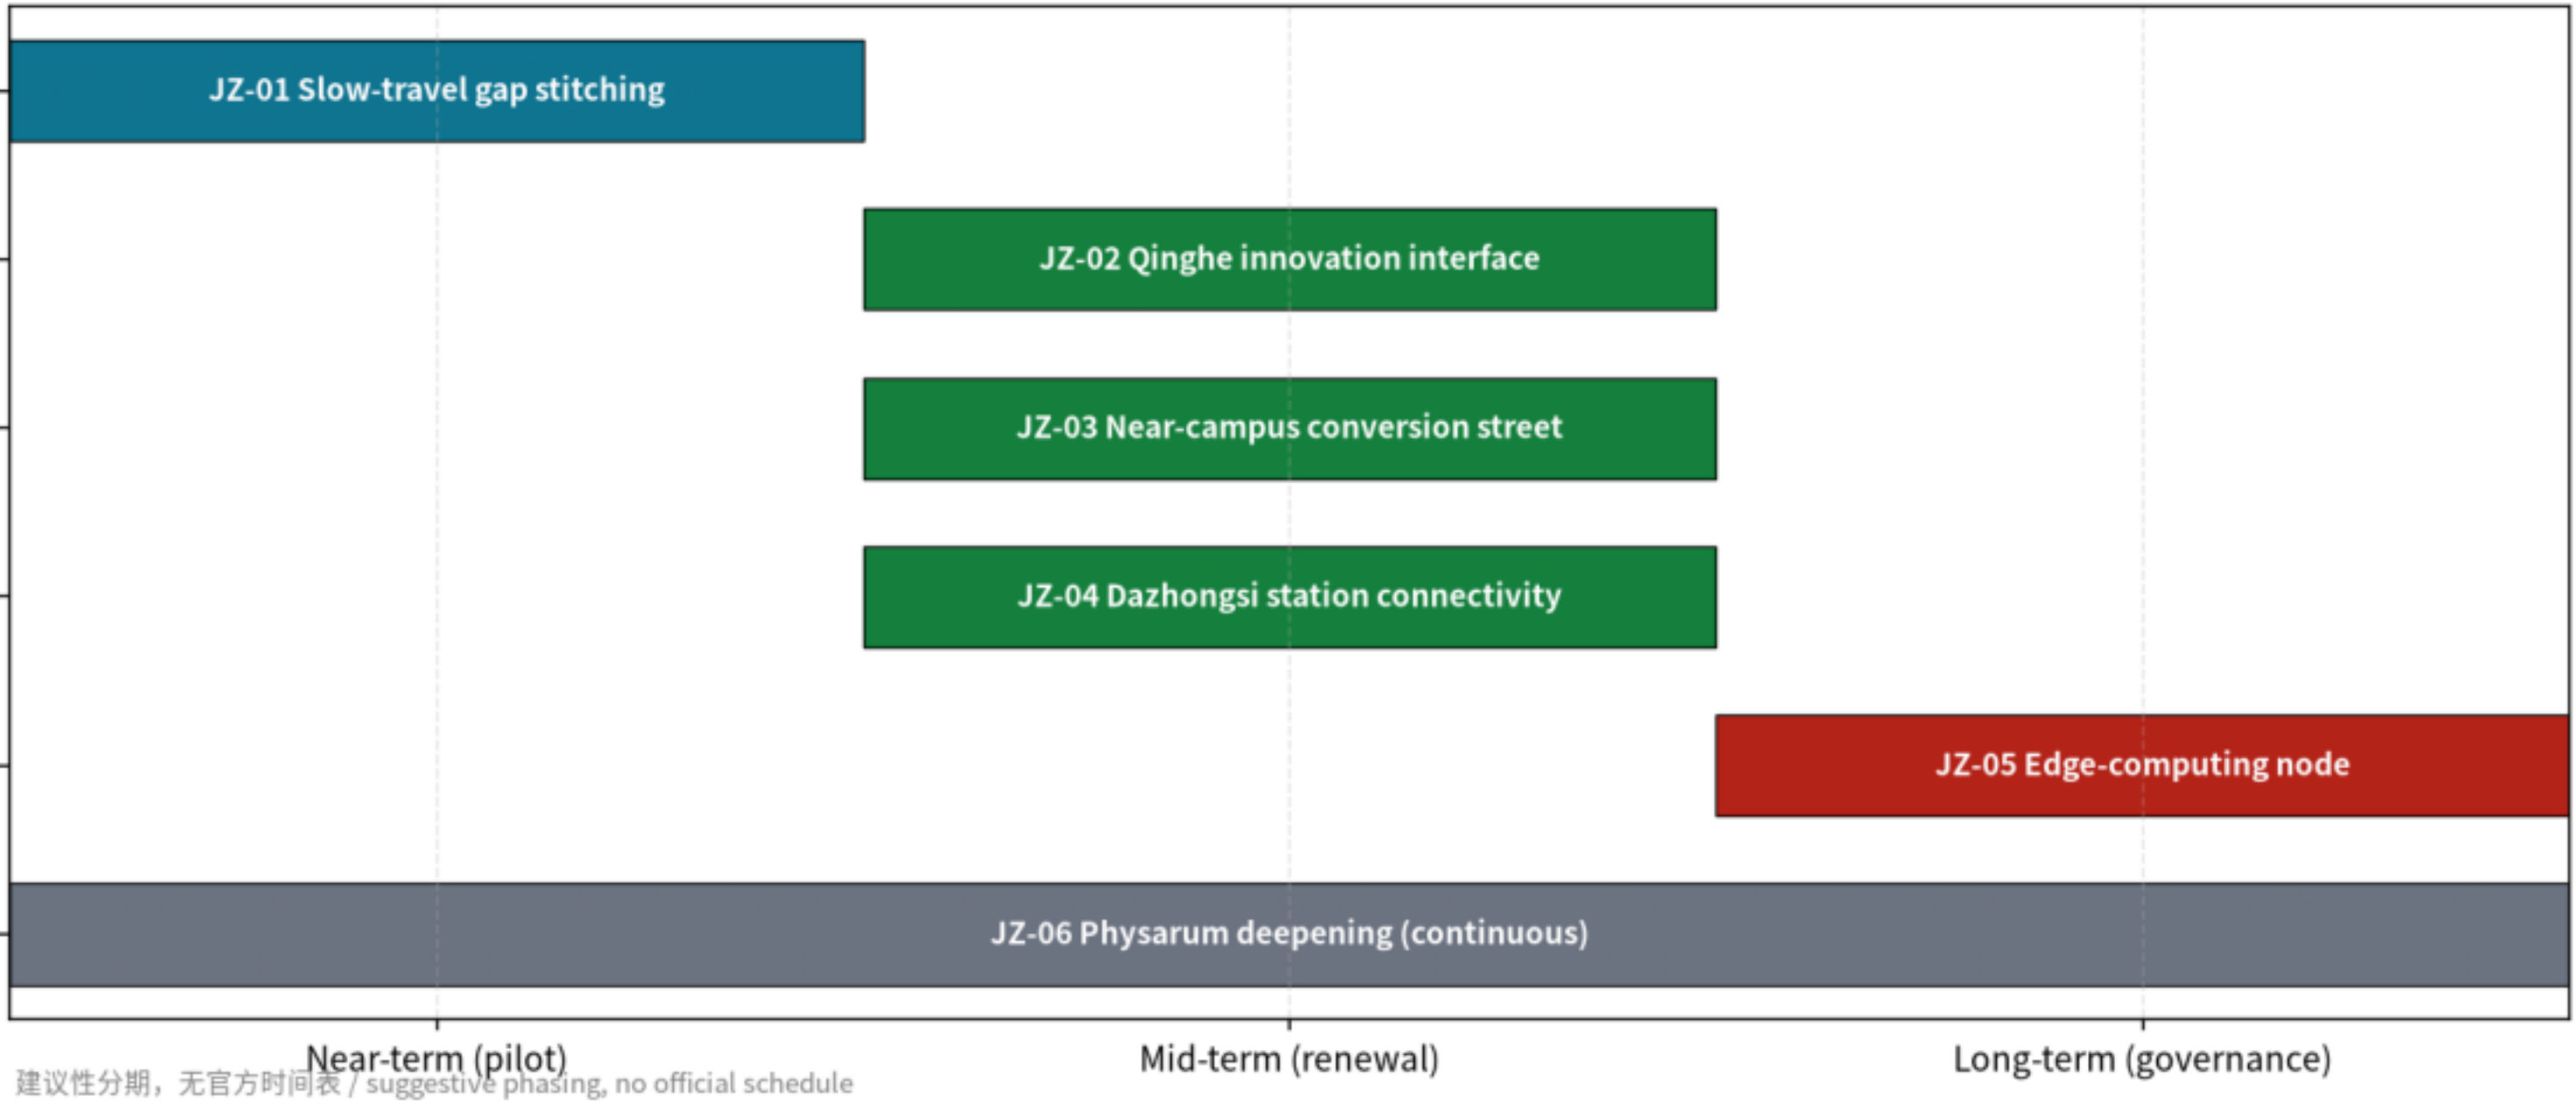

建议性分期，无官方时间表 / suggestive phasing, no official schedule