


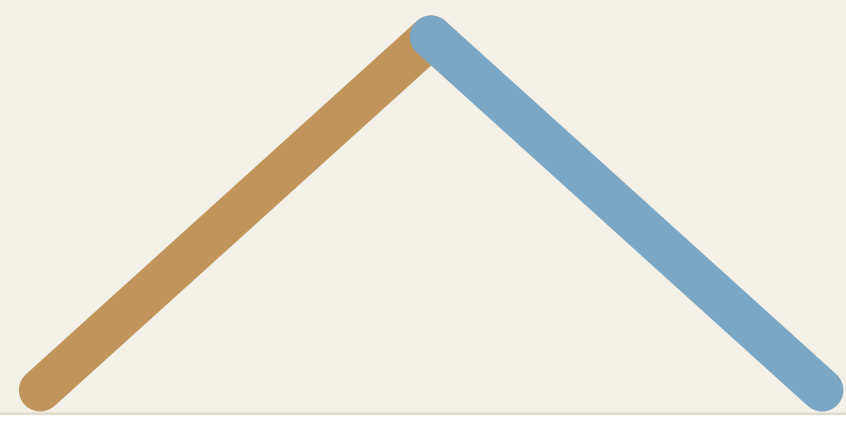

「人」字形双轨合流
AI以人为原点

一句话方案


把铁路留下的线性空间升级为一条可乘坐、
可实测、可纪念的城市智脉：六环缝合城市，
三枢驱动创新，十站承载记忆与场景。

三大定位

百年京张文化带 · 都市AI生活体验带
AI融合创新带——文轨讲历史，
智轨跑场景，鸣钟为里程碑。

五大功能回路

策源（原点）→ 加速与治理（众智园）
→ 业态化（大钟寺）→ 场景反馈（小月河翼）
→ 要素配置（中关村翼）

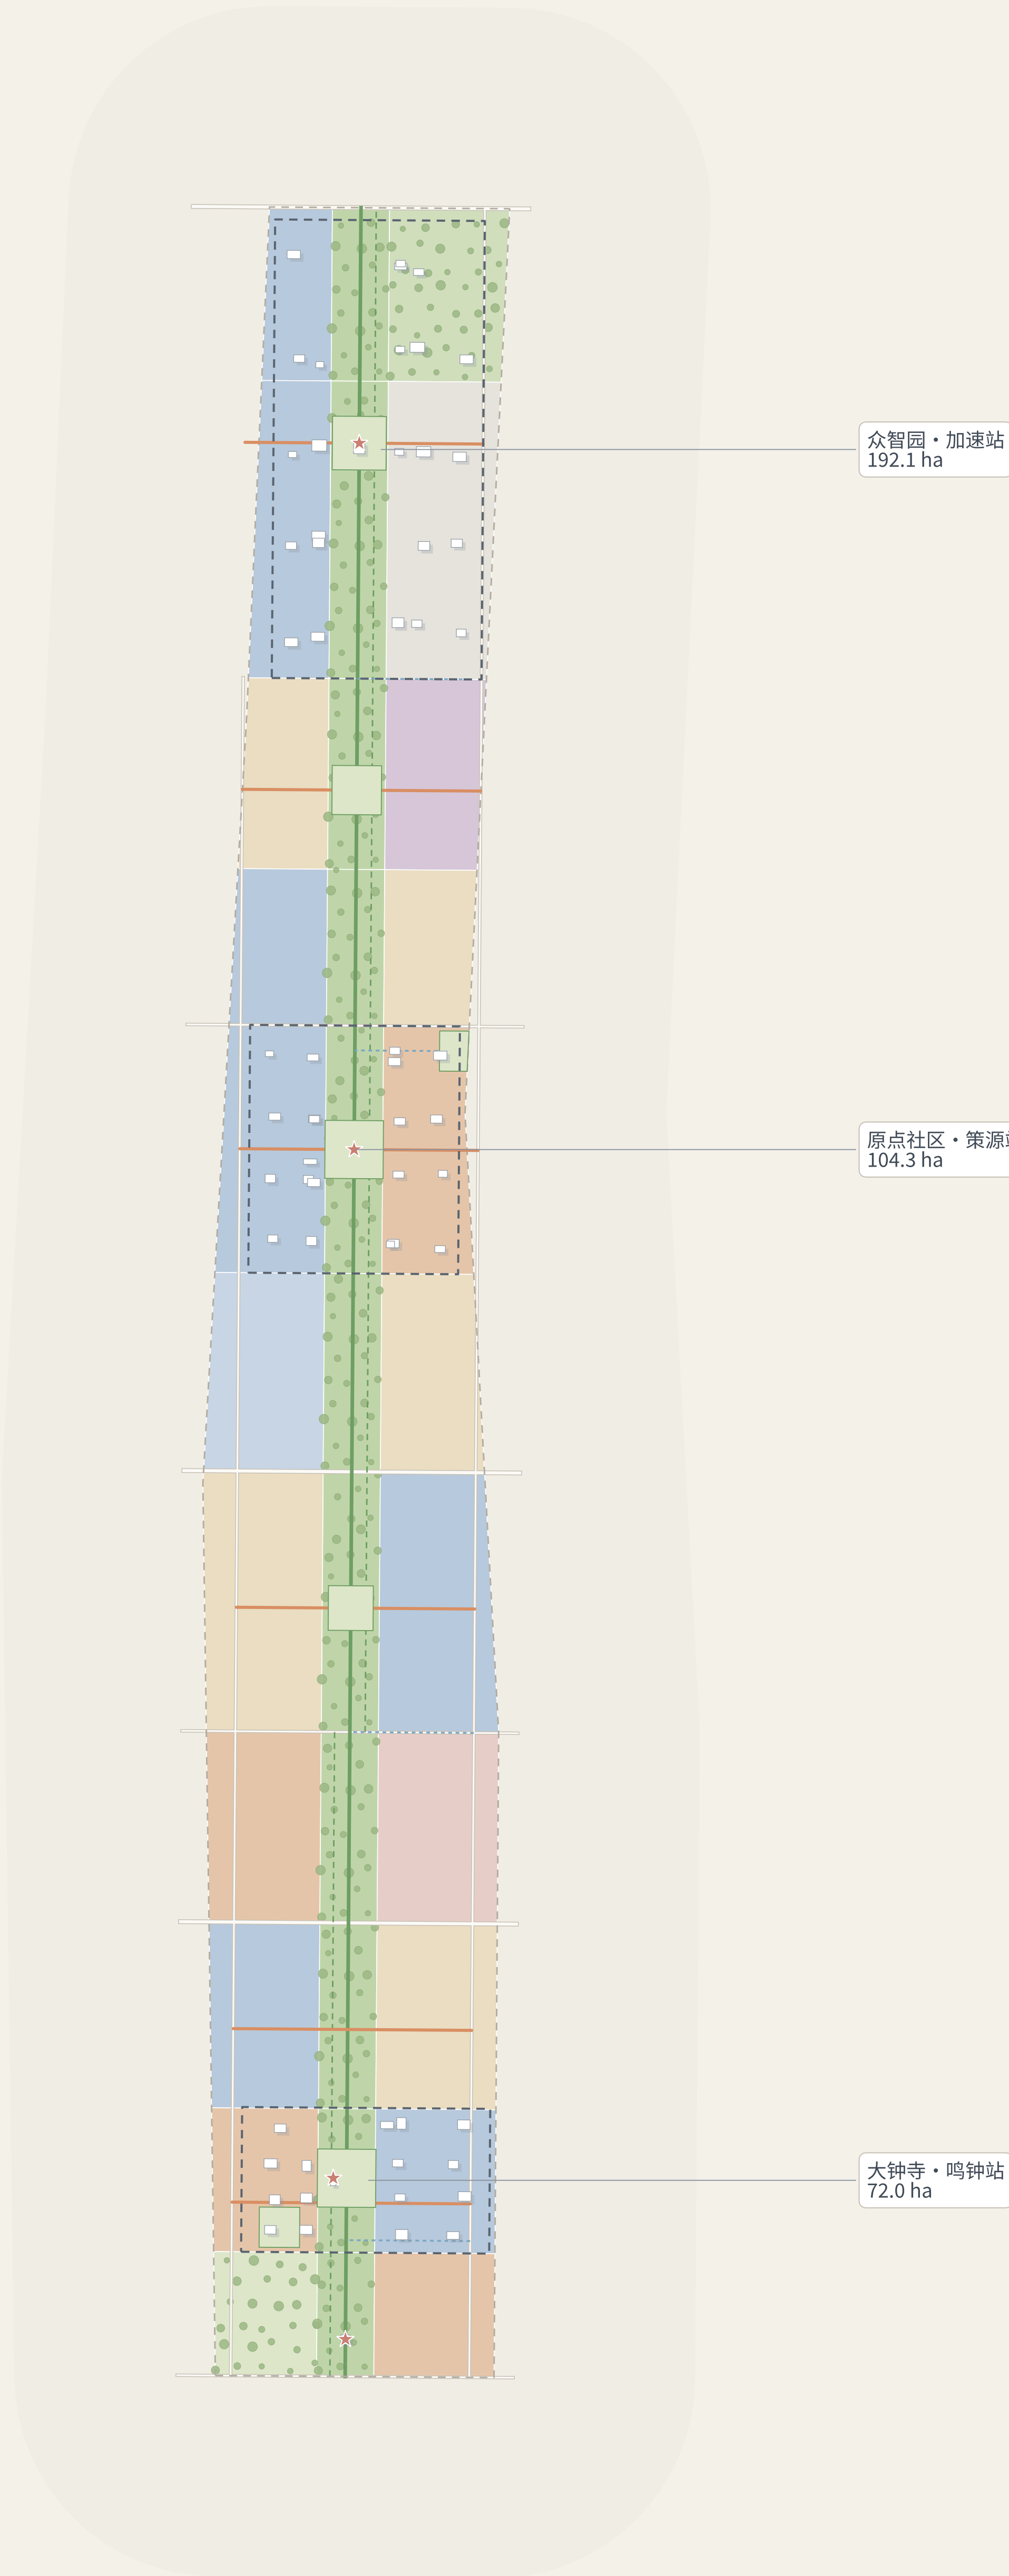

11.41 km²

总体设计范围 · 复算Δ0.11%

369.3 ha

三处重点区 · Δ0.24%

27.6% / 28.1%

绿地率 / 复合公共空间

25.8 km · 6环

慢行网络与缝合环


12卡 · 6像 · 4标


场景卡/画像/朝圣地标

23/23 · PASS

任务覆盖 · 四重本地审查

用地配比（33单元完整分区）

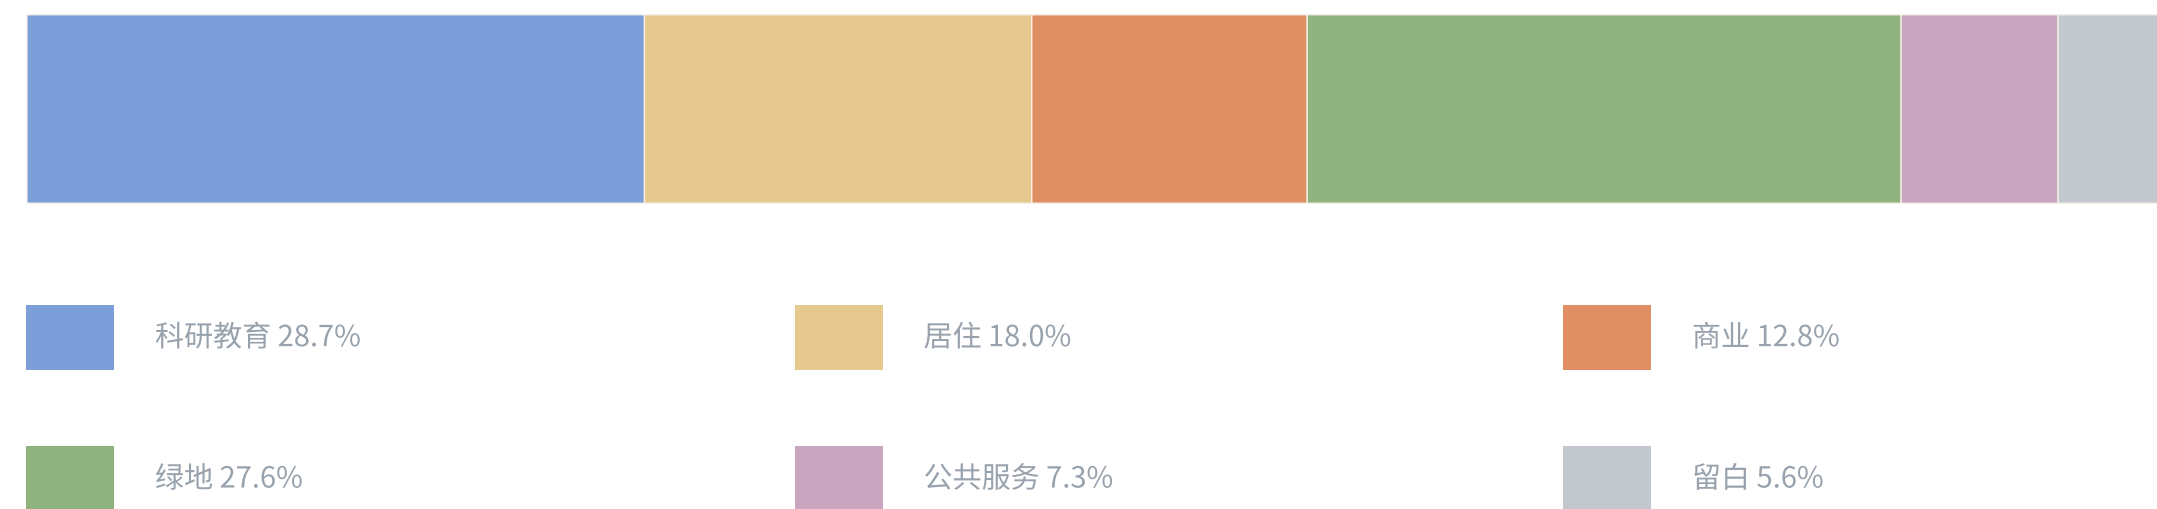


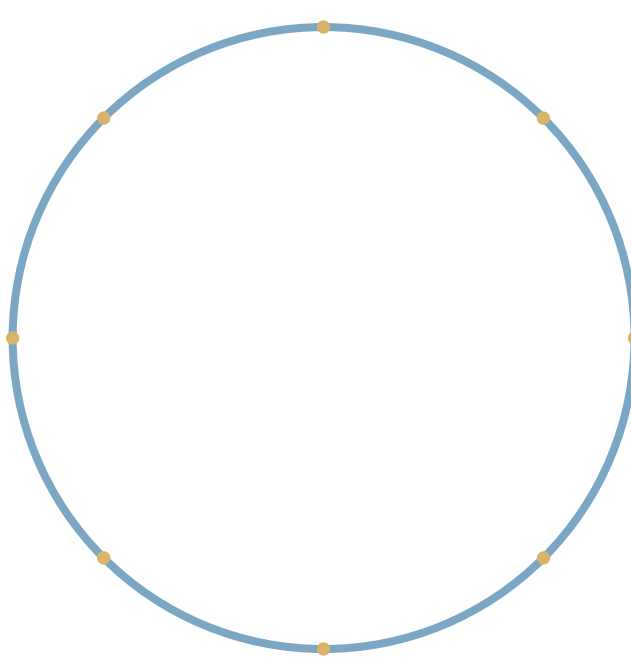

众智园 · 加速站

K7-K8 · 192.1 ha


- 环名园：治理论坛+全栈组团
- 战略留白 63.6ha 弹性启用
- 端侧算力×能源微网试验 ▲
- 五环之门国际发布台

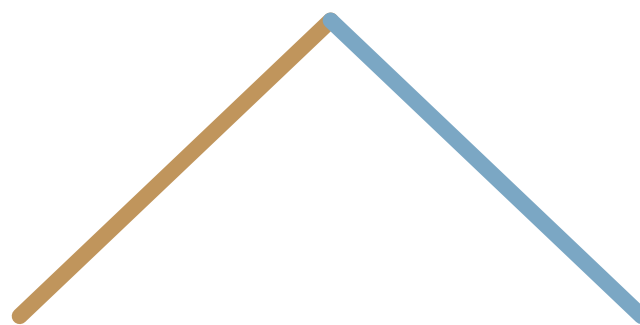

原点社区 · 策源站

K5 · 104.3 ha

- 人字桥缝合校-园-社
- 低扰动更新，保留街区肌理
- 五道口智能原生体验街
- 清华园站旧址展廊（待文保审批）

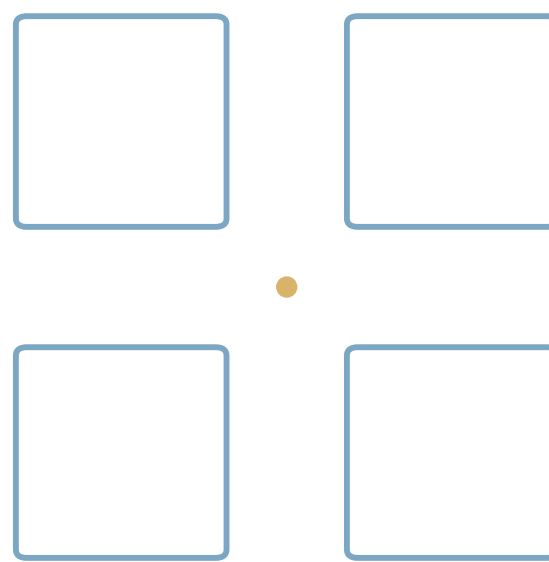


大钟寺 · 鸣钟站


K2 · 72.0 ha

- 站点四象限步行连通
- 存量楼宇智能化改造
- 自动驾驶接驳试验线 ▲
- 鸣智塔：为开源里程碑鸣钟

断面 A-A · 众智园段 (K7-K8)：低多层研发院落 × 240米绿轴 × 留白单元

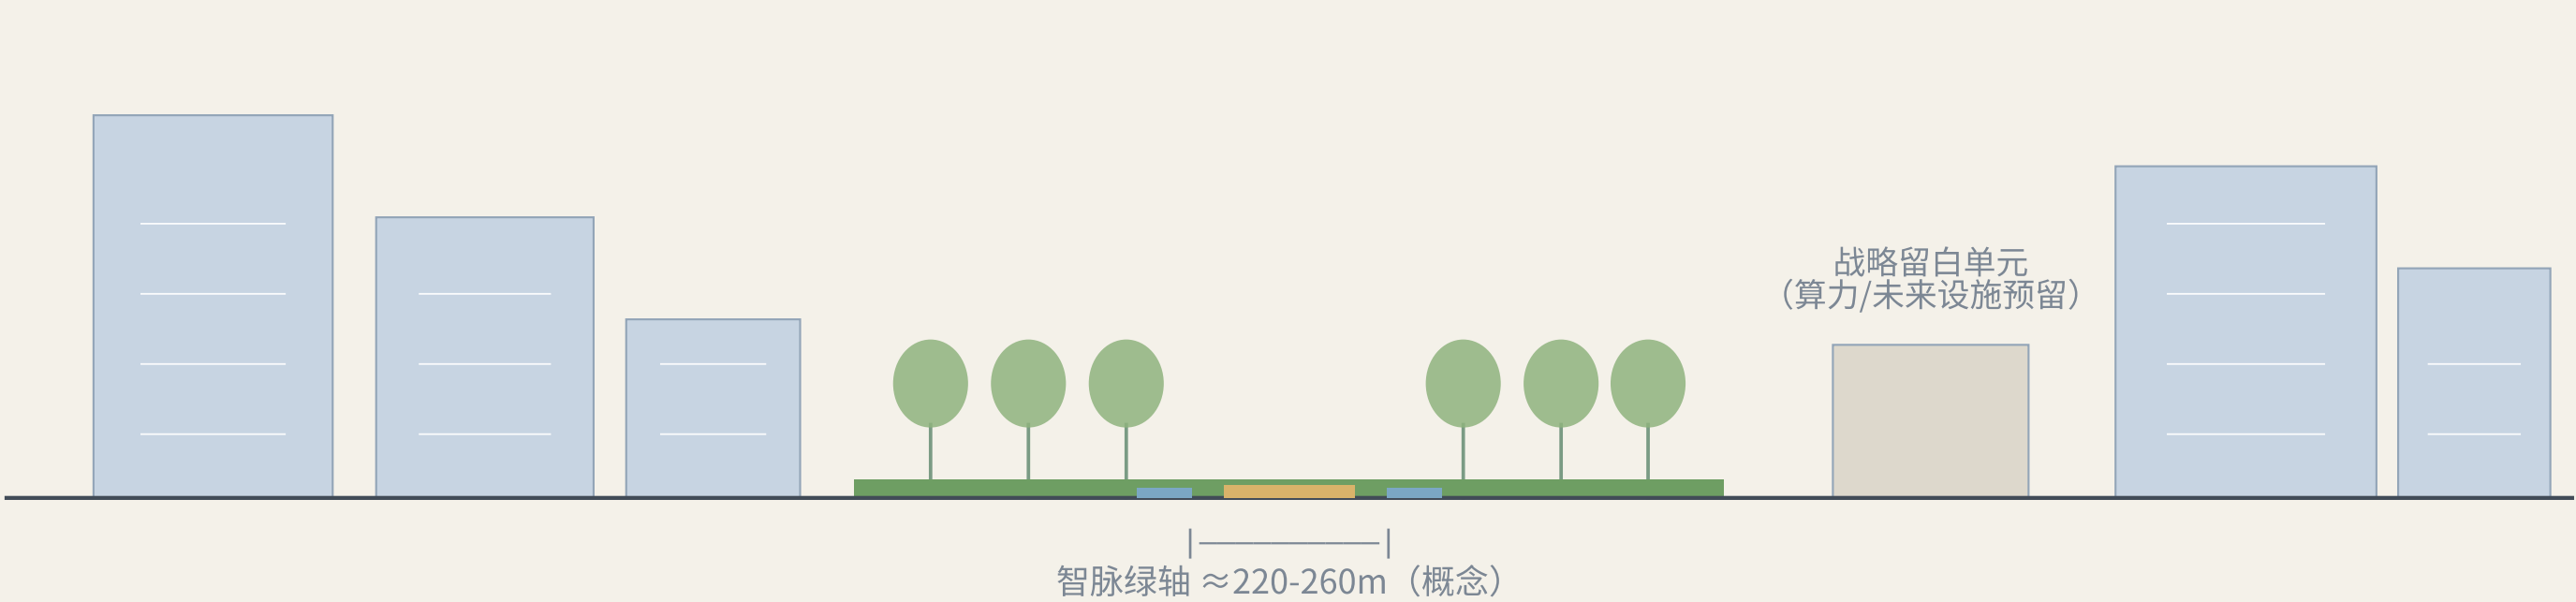

断面 B-B · 原点社区段 (K5)：小尺度混合院落 × 人字桥缝合 × 站点一体化

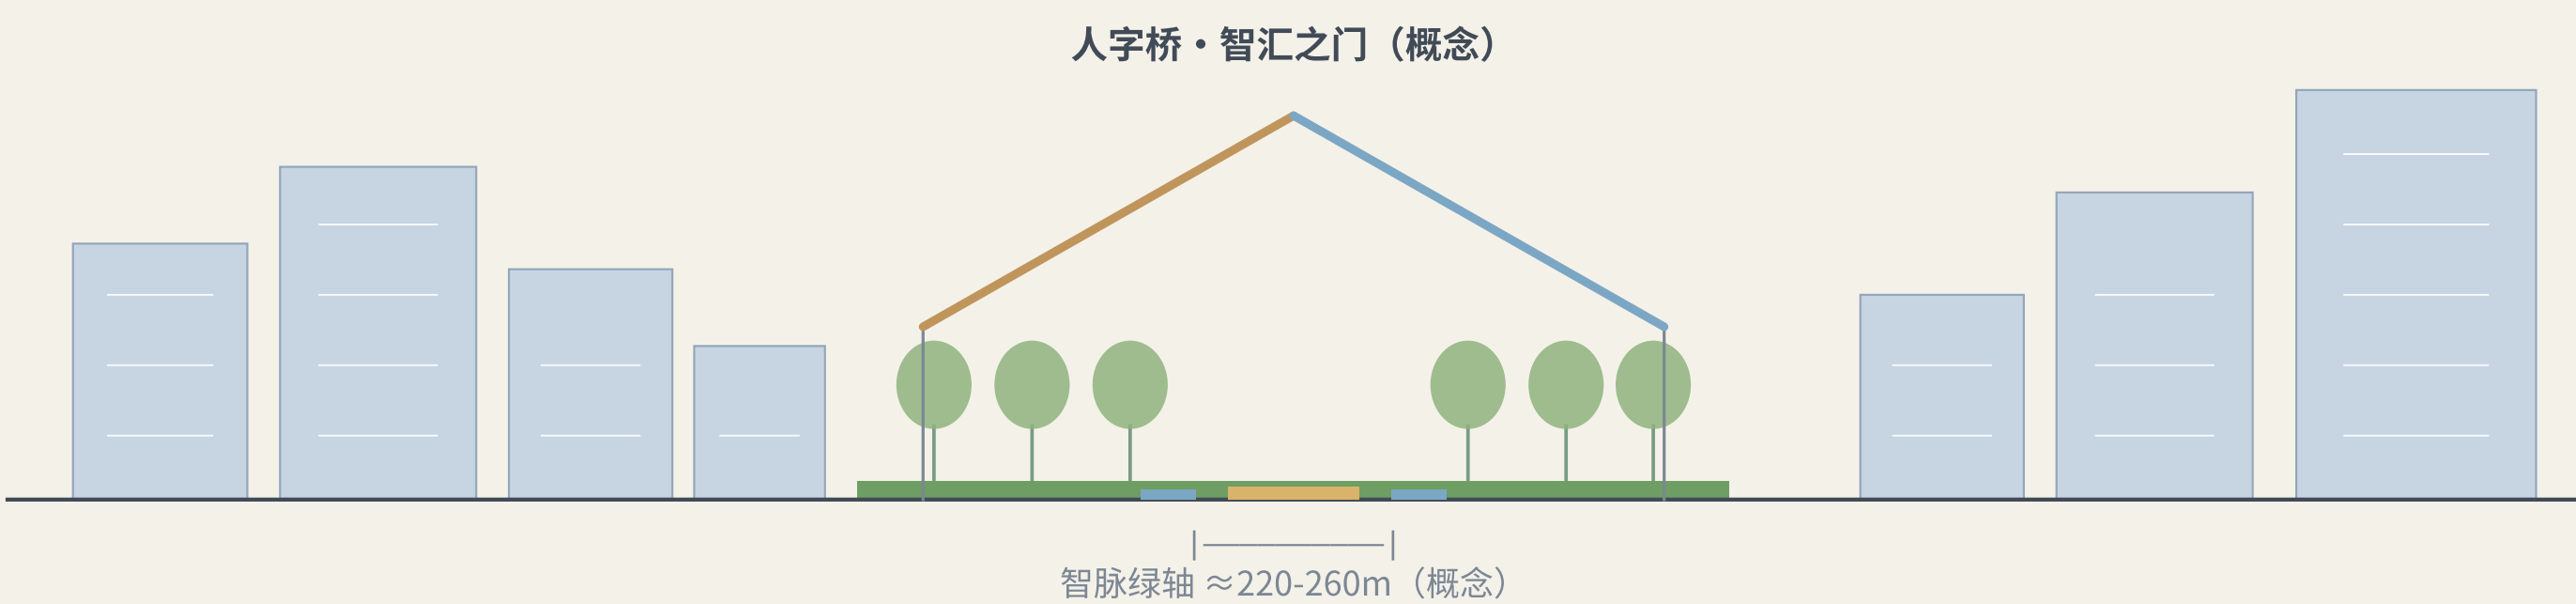

断面 C-C · 大钟寺段 (K2)：存量楼宇智能化改造 × 站点四象限连通



场景票卡墙（盖章=测试验证）

S01 K0-K9 智脉绿道AI伴行 P4 · P5	S02 L3 缝合智能过街 P4	S03 L4 无人低速配送 P2 · P4	S04 文筑 AI文化向导 P5
S05 K2 企业服务智能体 P3	S06 L4 社区健康导航 P4	S07 L1-L6 运营复盘智能体 P6	S08 K5东 智能原生消费街 P2 · P5
S09 K5西 成果转化撮合 P1 · P2	S10 K8 端侧算力微网 P2 · P6	S11 K2 自动驾驶接驳 P3 · P4	S12 K0 荣誉与城市记忆 P1 · P5

18项更新项目 × 三期时序（概念建议）

JZ-01	K0广场·贡献者墙	JZ-02	人字桥缝合环
JZ-03	大钟寺四象限	JZ-04	众智之环场地
JZ-05	绿道贯通成环	JZ-06	五道口体验街
JZ-07	原点转化组团	JZ-08	算力微网试验
JZ-09	清河文化带	JZ-10	学院桥人才社区
JZ-11	蓟门研发组团	JZ-12	五环之门
JZ-13	智能终端组团	JZ-14	知春微枢纽
JZ-15	学院路信软组团	JZ-16	社区有机更新
JZ-17	医养组团	JZ-18	留白启用机制