


京张·首班车 JZ FIRST TRAIN

百年京张铁路的AI首发站城市设计 · 一线三站两翼 · 总体概念

总体概念： 一线三站两翼 — 京张·首班车

总体概念： 一线三站两翼 — 京张·首班车

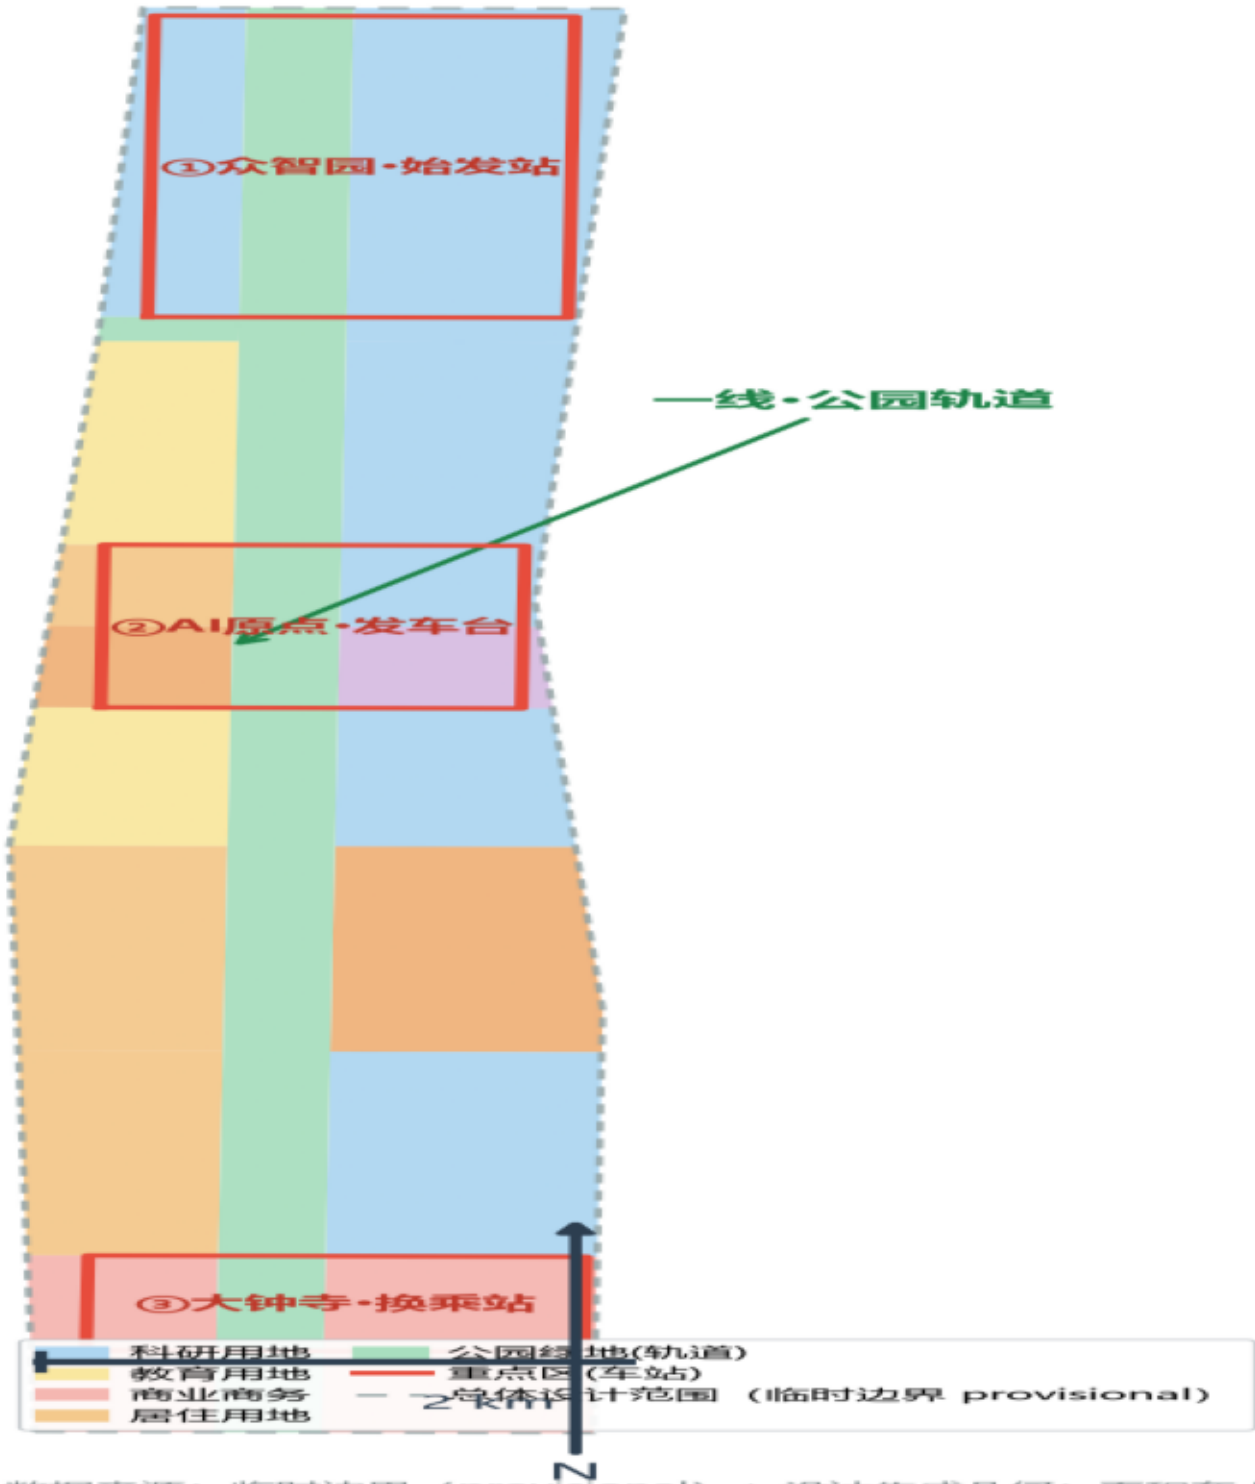

数据来源：临时边界（provisional）+ 设计生成几何；面积在 EPSG:4548 复算。空间为概念建议，非官方红线。


总体概念：遗址公园活力带=轨道，三处重点区=车站，中关村/小月河=信号所/风景线。

三层范围与用地结构

统筹研究 43.6km² · 总体设计 11.4km² · 重点区 368.4ha

三层范围与用地结构

统筹研究 43.6km² · 总体设计 11.4km² · 重点区 368.4ha

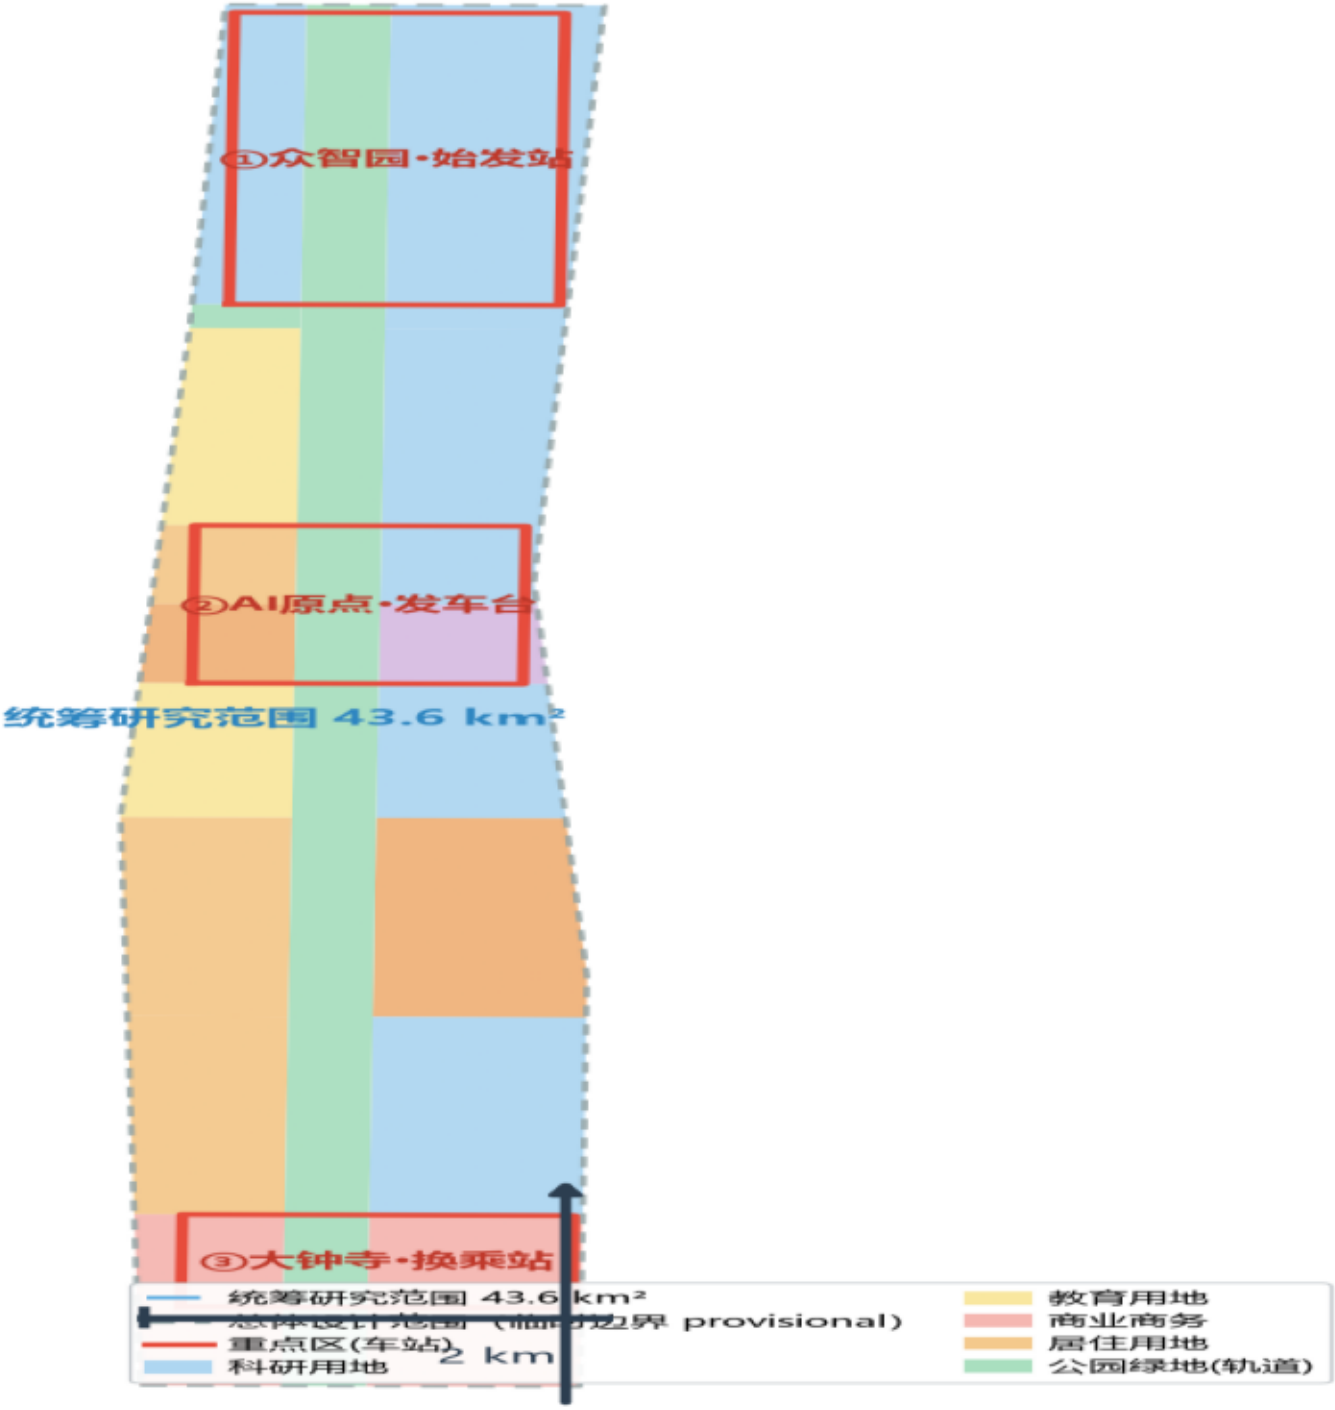

数据来源：临时边界 (provisional) + 设计生成几何；面积在 EPSG:4548 复算。空间为概念建议，非官方红线。


用地按走廊式分区：中央公园轨道贯穿，两侧科研/教育/商业/居住/文化用地沿带布局。

三处重点区域详细设计

众智园·始发站 / AI原点·发车台 / 大钟寺·换乘站


三处重点区域详细设计：定位 + 空间结构 + 场景 + 实施

① 众智园·始发站
创新机务段

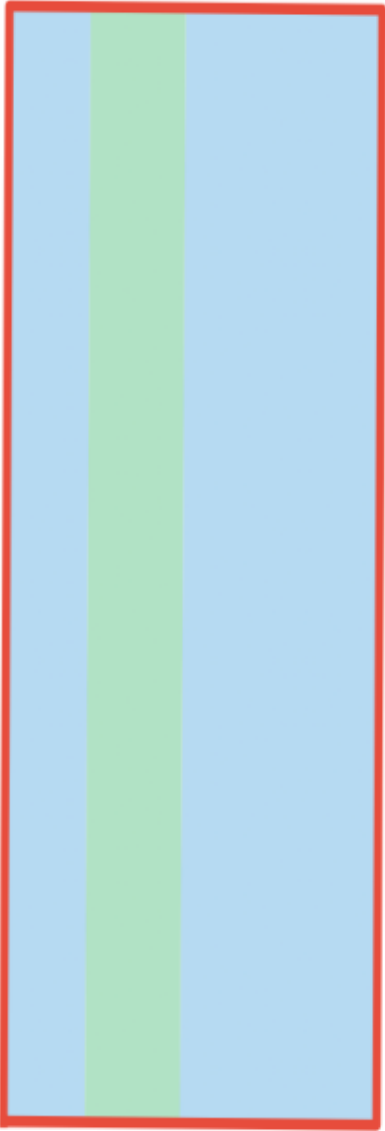


AI全栈自主创新加速
科研+中试+验证

② AI原点·发车台
世界首发站

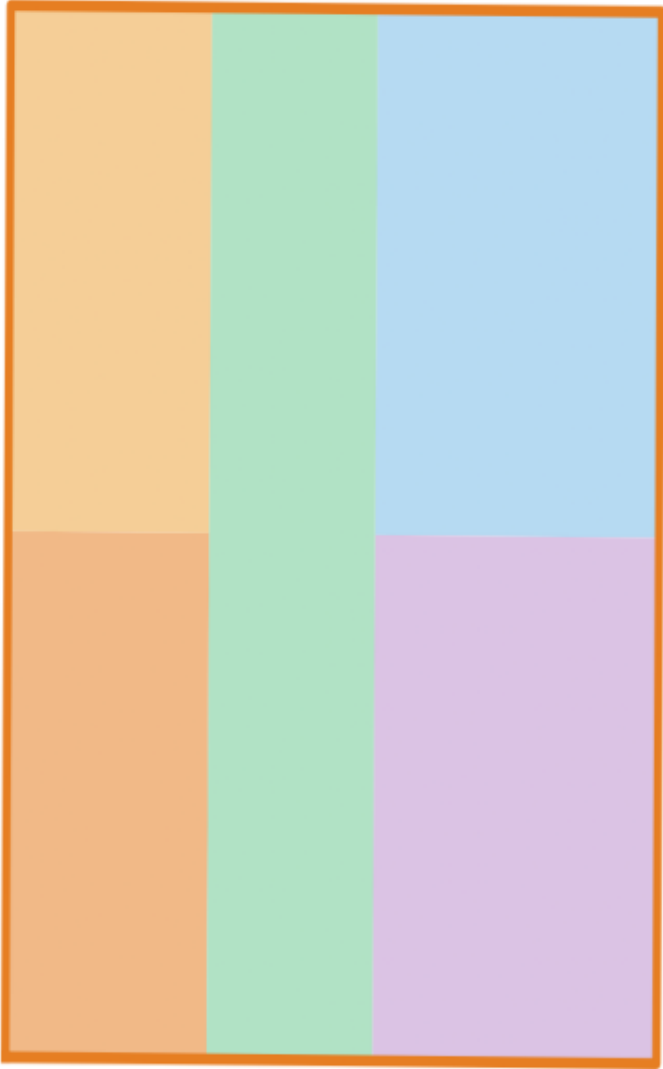

世界级AI创新生态
清华园站·发车纪念

③ 大钟寺·换乘站
智能枢纽

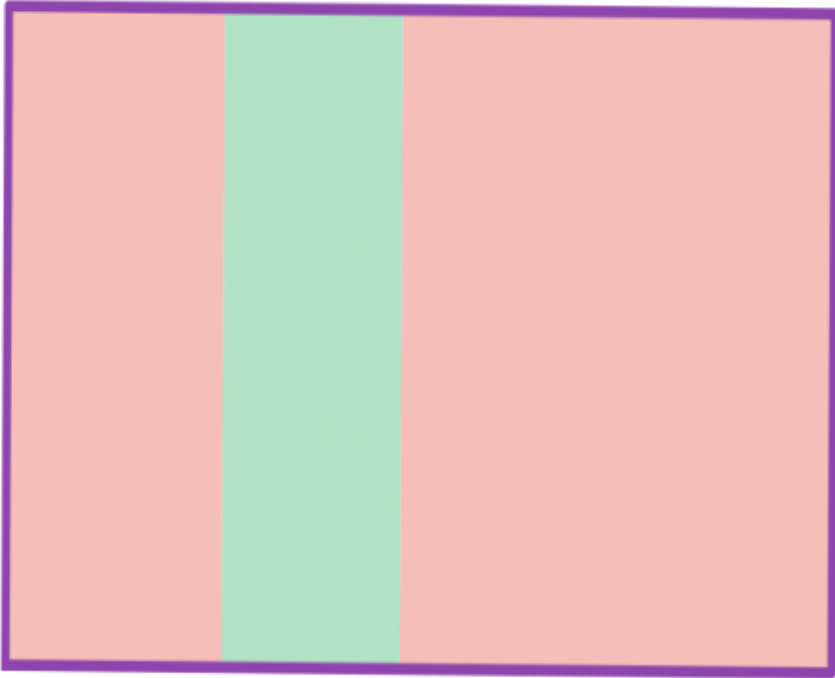


智能原生新业态
站城一体·南部门户

交通慢行与蓝绿公共空间复合系统

两纵多横+轨道·一轨多珠

交通慢行与蓝绿公共空间复合系统

交通慢行与蓝绿公共空间复合系统 两纵多横+轨道·一轨多珠

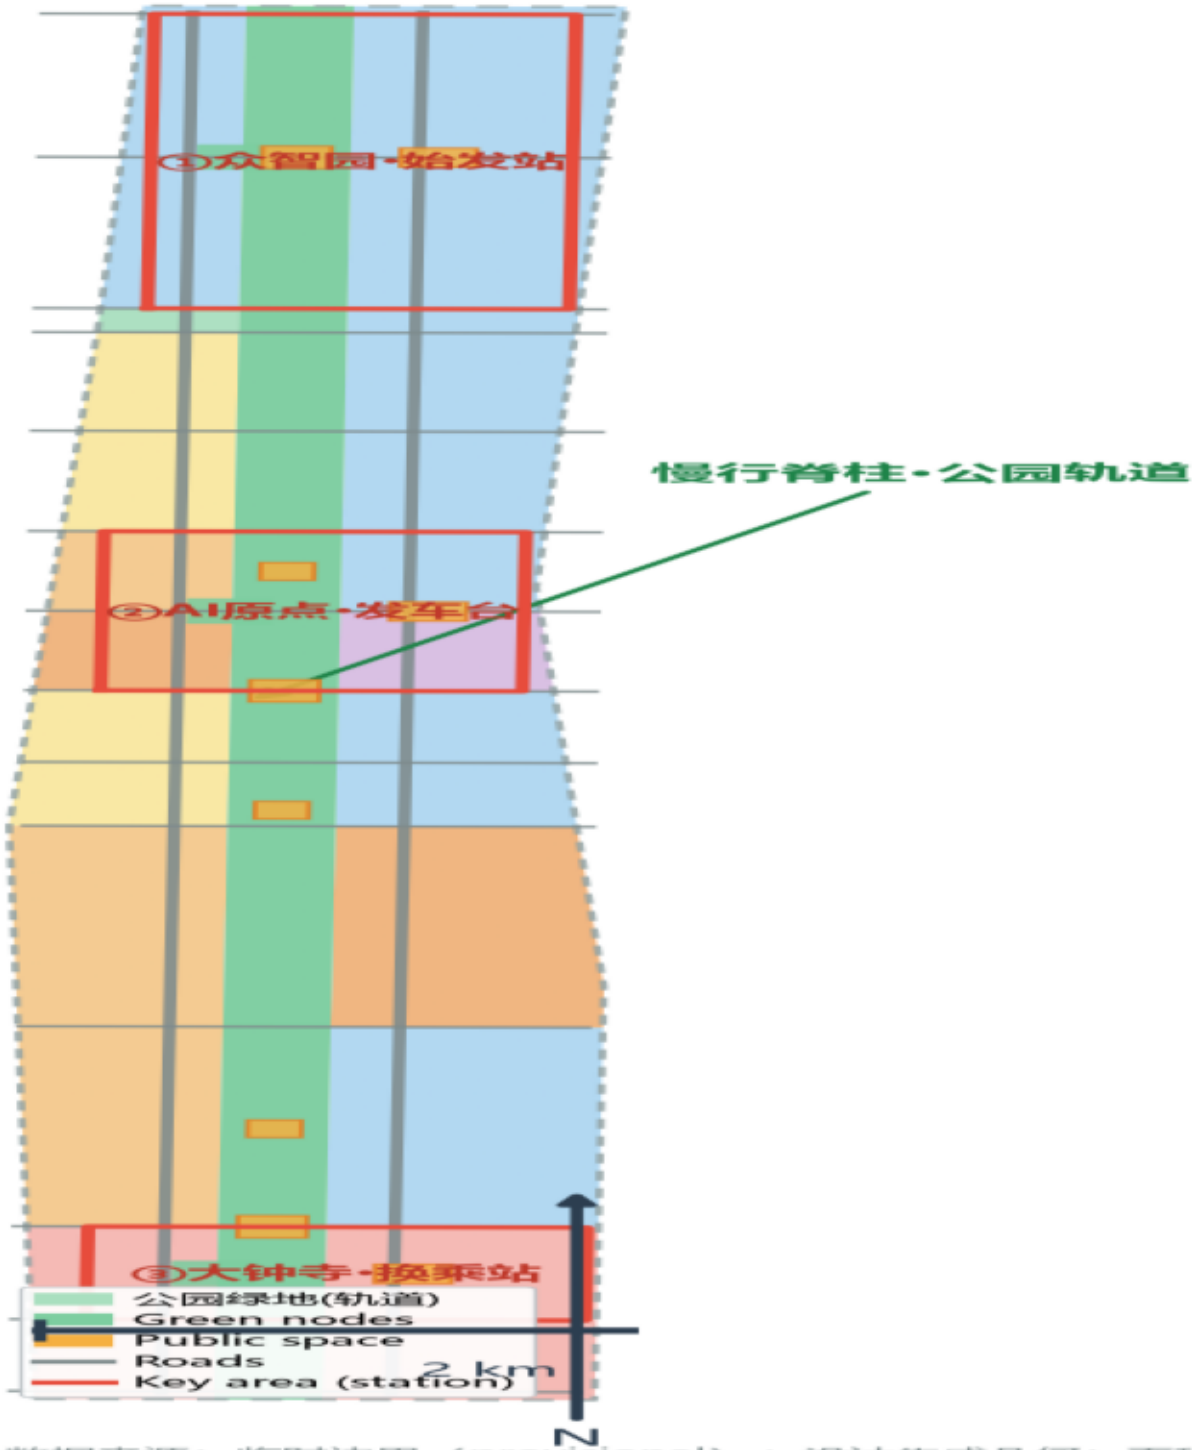

数据来源：临时边界（provisional）+ 设计生成几何；面积在 EPSG:4548 复算。空间为概念建议，非官方红线。

核心指标复算

由 geometry/*.geojson 在 EPSG:4548 复算

核心指标复算与证据链（由 geometry/*.geojson 在 EPSG:4548 复算）

总体设计范围

11.41

km²

公告值 11.4 km² · EPSG:4548 复算

绿地率

20.8%

绿地/范围

公园轨道+节点绿地

公共空间率

1.6%

公共空间/范围

三站广场+节点

估算容积率

1.65

总建面/范围

概念估算·非法定控规

建筑密度

15.1%

基底/范围

代表性建筑基底

道路里程

37.0

km

两纵+14横连接路